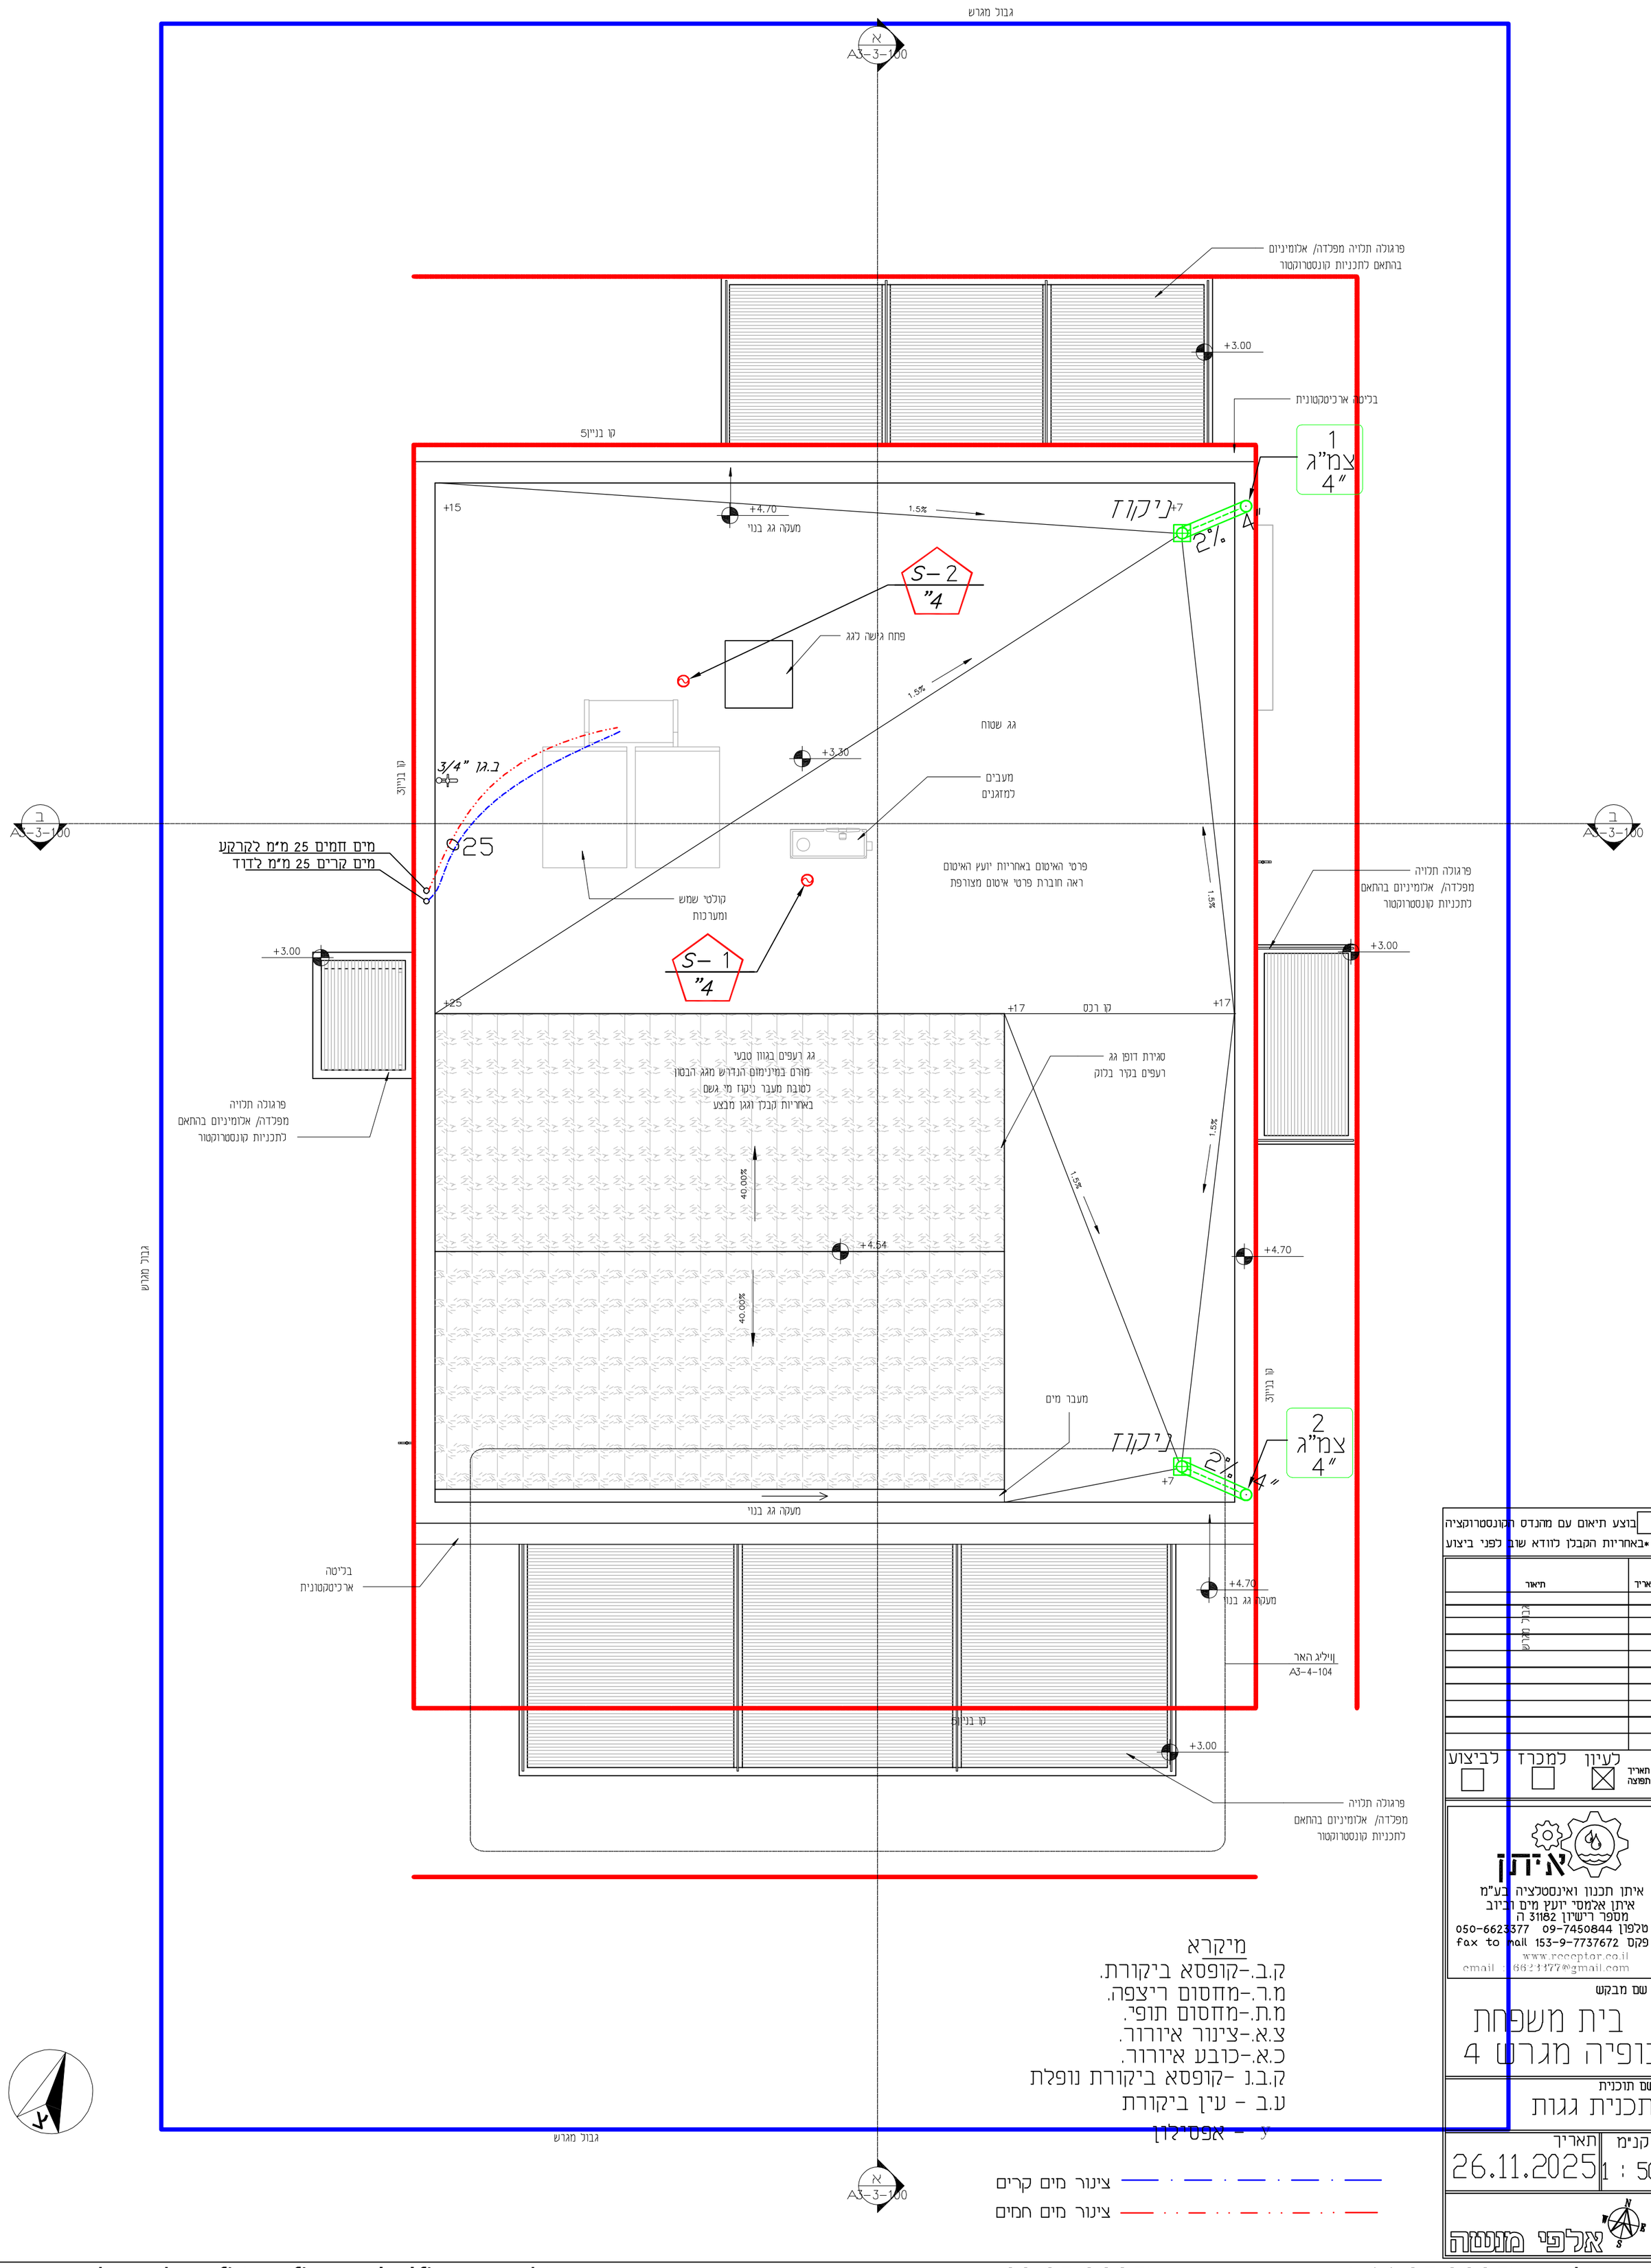

D:\autocad work yafit\nofia eyal alfi menash\הדובע תוינכותו סירטינס סיחפסינ 03.05.2025\שרגמ רשואמ 4 11.05.2025\work\work n

2 : 1 מדרגות

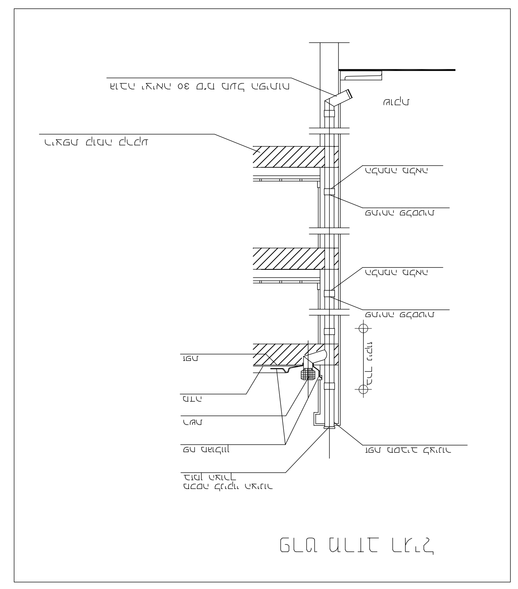
249
250
251
252
253
254
255
256
257
258
259
מפלס מדרכה
מפלס מרתף
מפלס מרתף
מפלס מרתף

לפני ביצוע עבודות האינסטלציה
הקבלן יחשוף את נקודת התחברות עירונית
כולל פתיחת מכסה שוחה עירונית
ובדיקה שעומק הצינור מתאים לתכנון
יש לדווח למתכנן במידה של אי התאמה

במידה ואין חיבור ביוב ציבורי
אסור לבצע עבודות צנרת ושוחות ביוב חיצוני
עד לקבלת החיבור ביוב הציבורי בפועל !

לפני קידוח כלונסאות של החומות או הבית
ובאופן כללי לפני תחילת עבודות
הקבלן יאתר את כל קווי הביוב הניקוז והמים במגרש
יסמנם וידווח למתכנן אינסטלציה על המצאותם
וינקוט בכל האמצעים הדרושים להגנתם

מכסה ביוב פרטי יהיה 20 סמ לפחות מעל מכסה תא ביוב עירוני
ו 20 ס"מ לפחות נמוך מריצפת ה 00 של הבית

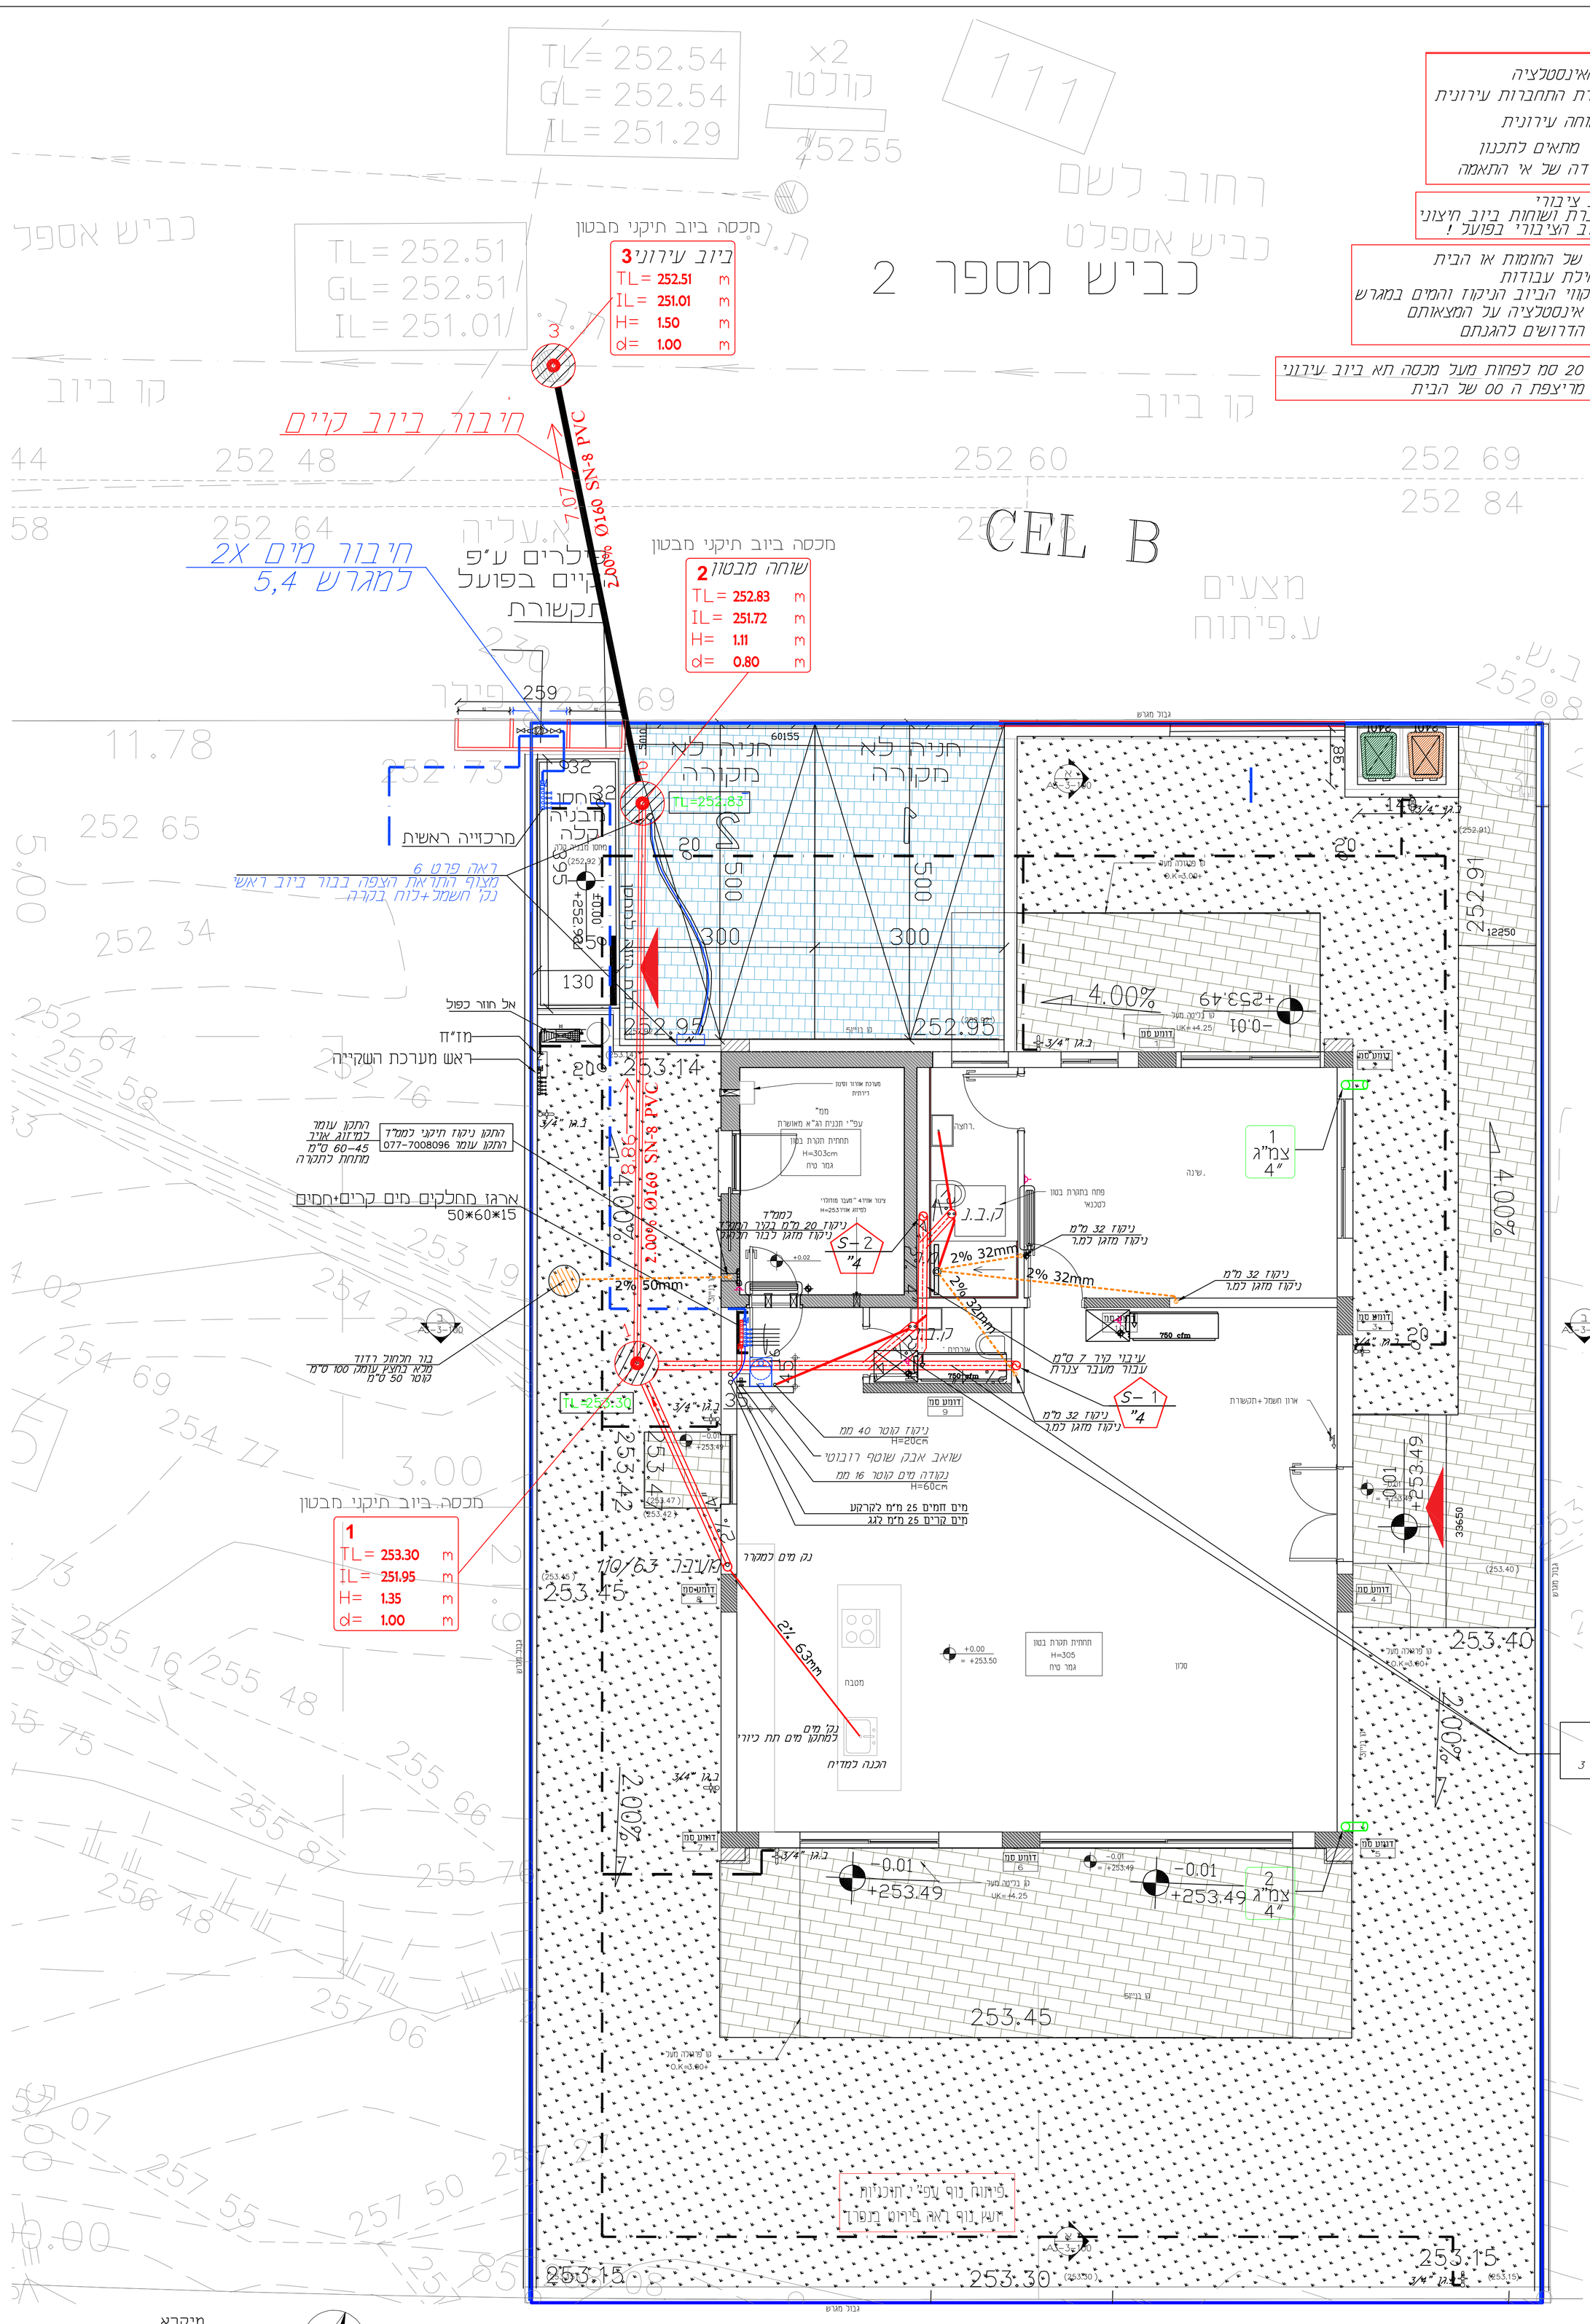

מיקרא
ק.ב.-קופסא ביקורת.
מ.ר.-מחסום ריצפה.
מ.ת.-מחסום תופי.
צ.א.-צינור איורור.
כ.א.-כובע איורור.
ק.ב.נ -קופסא ביקורת נופלת
ע.ב - עין ביקורת
y - אפסילון

ציור מים קרים
ציור מים חמים

יש לתאם מעבר צנרת בבטון עם מהנדס בניין לפני ביצוע

ניקוז מזגנים בתיאום קבלן מזגנים ואינסטלטור לפני ביצוע
יש לנקז מזגנים למקומות הבאים בלבד: בור חילחול,שפיכה חופשית לפיתוח,סיפון של כיור,מחסום ריצפה פעיל של מיקלחת,מחסום תופי של אמבטיה

בוצע תיאום עם מהנדס הקונסטרוקציה
*באחריות הקבלן לוודא שוב לפני ביצוע

תאריך	תיאור

תאריך הפצה: לעיון ☒ למכרז ☐ לביצוע ☐

איתן
איתן תכנון ואינסטלציה בע"מ
איתן אלמסי יועץ מים וביוב
מספר רישיון 31182 ה
טלפון 09-7450844 050-6623377
פקס 153-9-7737672 Fax to mail
www.receptor.co.il
email : 66231477@gmail.com

שם מבקש
בית משפחת
נופיה מגרש 4

שם תוכנית
תכנית קומת קרקע

קנ"מ	תאריך
1 : 50	26.11.2025

אלפי מנשה