תכנית פיתוח-מגרש 20

קנ"מ 1:100

תפוצה	תאריך
מנהל הפרויקט	
אדריכל	
ס.ביצוע/ים	
חשמל	
בזק	
שמש	
אינסטלציה	
מזגן	
אינסטלציה	
גז רכ. לבו	
מעבדים	
חברת חשמל	
חברת בזק	

מס'	שינויים	תאריך

עודכן ע"י: רחל

א. בסיס
הנדסת חשמל בע"מ
משרד: יד חרוצים 16, ירושלים 93420
טל: 074-7021015 נייד: 050-6550484
פקס: 077-5131015 דוא"ל: office@ebasis.co.il

שם הפרויקט:
נופיה-אלפי מנשה

שם הגיליון:
תוכנית פיתוח מגרש 20

קנה מידה: 1:100	○ לעיון	○ לאישור	● למכרז	○ לביצוע
תאריך: Date: 17.06.2024	מס' קובץ: File: 675P.dwg		
תכנן: איתן	שרטט: אילה	אישר: איתן	
מס' עדכון: 0	מס' הגליון: P20	מס' הפרויקט: 675	

לוח חשמל דירתי
מגרש 20

הנחיות לבניית לוח חשמל:
- מבנה לוח חשמל כלכסי חסין אש סדרת FW מחוצרת Hager
  דגם FW62US2 7–144 מודולים 2X(6x12) לפחות
- דלת כיס IP30 מחכתית
- כבידה כמיל Class–2
- צבע לבן
- מהדקי אפס והארקה עם חיבור מהיר
- ציוד חשמלי יהיה מסוג ABB שניידר הגר או EATON בלבד בעל זרם
- יש לשמור בלוח 30% מקום לתוספת עתידית בלוח

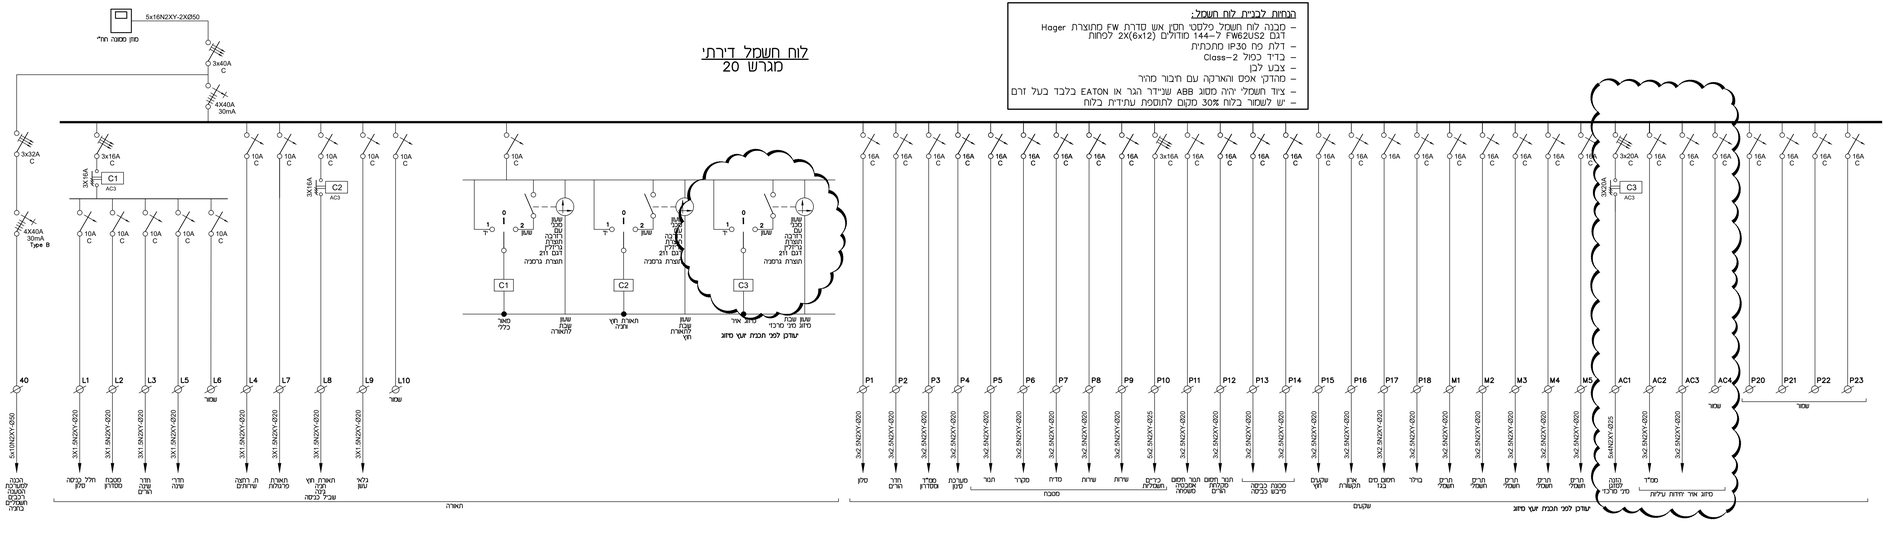

תמיצה	תאריך
ALL_SHEETS	
ALL_SHEETS	
TITLE_OF	
TITLE	
ELECTRICAL	
ELECTRICAL	
ELECTRICAL

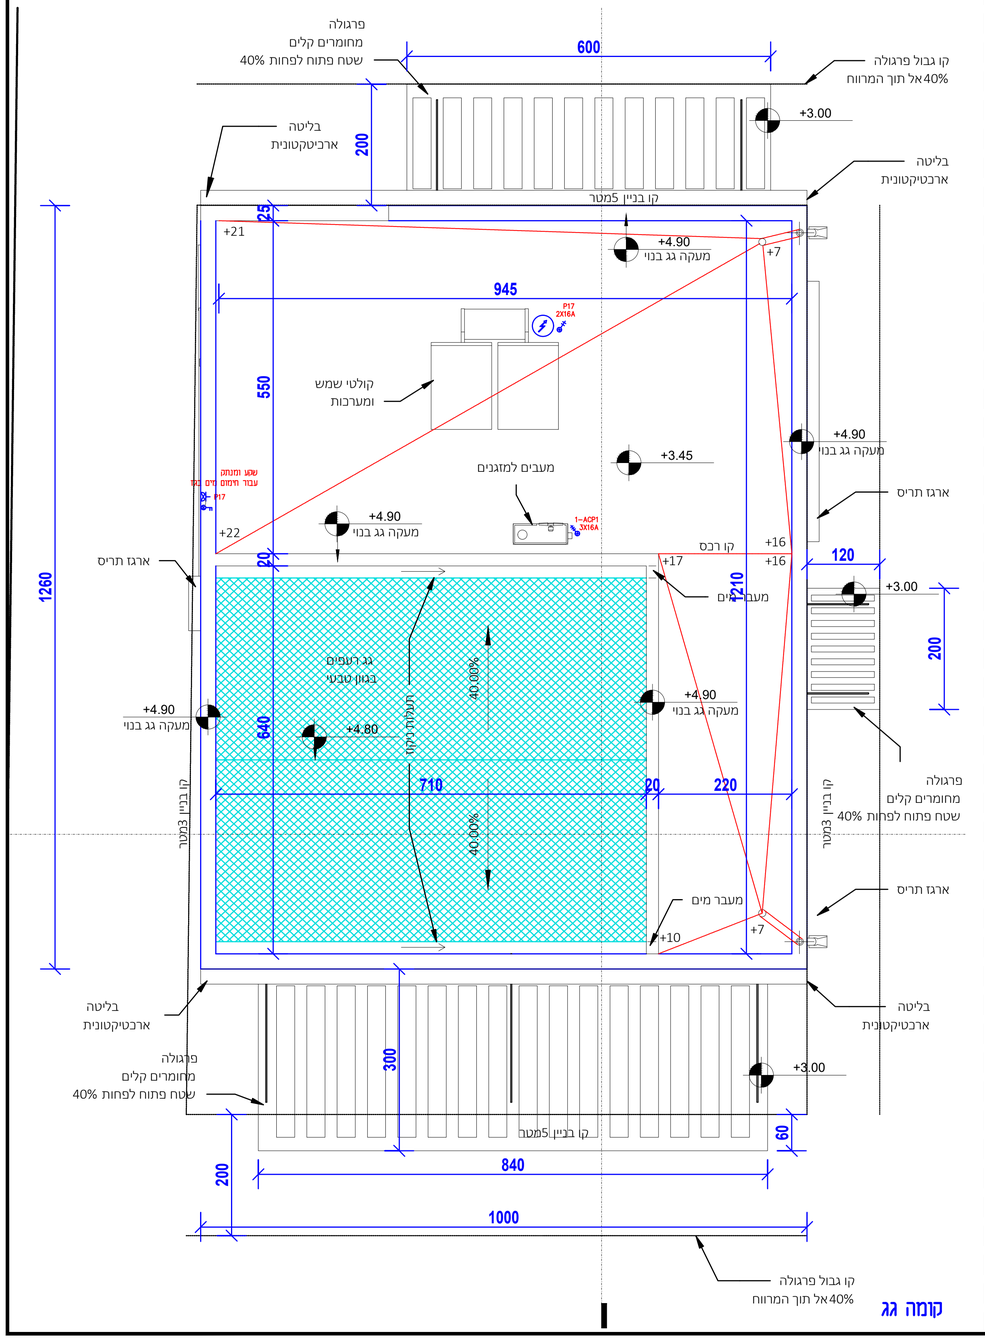

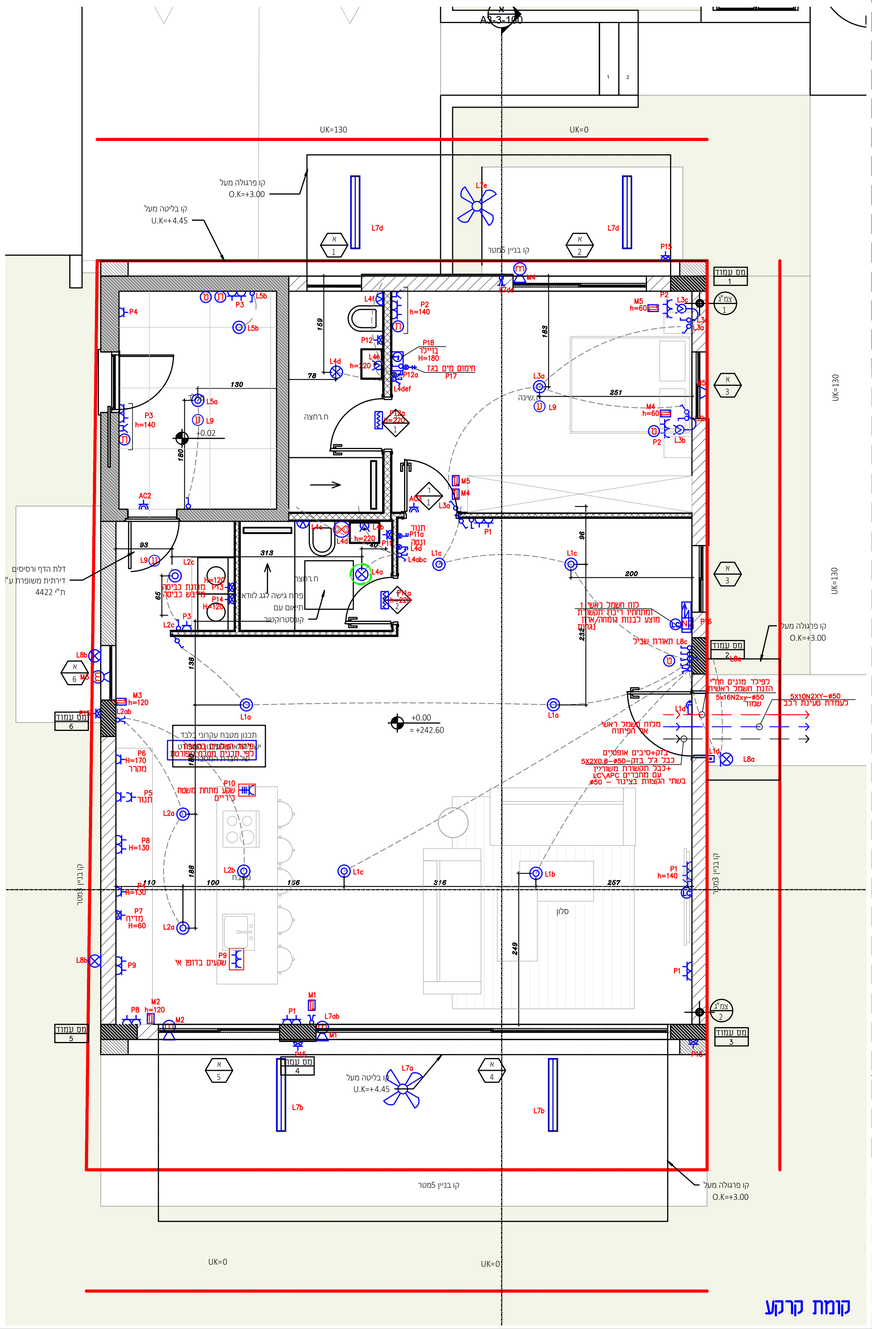

מקרא חשמל ותאורה:

כח חשמל		
	שקע 16A בודד H=60 אלא אם צוין אחרת	
	זוג שקעי 16A אלא אם צוין אחרת	
	מקבץ שקעים טיפוסי טיום באביזר N2 "ניסיסי" בארון תקשורת מתחת לוח חשמל	
	שקע חד פאזי מוגן מים H=60 אלא אם צוין אחרת	
	שקע ליחידת מ"א 16A H=220 מיקום סופי לפי תכנית מיזוג ובתיאום מול אדריכל	
	נקודת סכמטן מלאה-צנרת, כבילה ושקע סכמטן H=60	
	CIMA BOX הכולל: 4 שקעי שרות+2 תקשורת	
	נקודת תקשורת H=60, צינור #25 עם חוט משיכה מרכיבה תקשורת דירתי	
	נקודת סכריזיה מושלמת+צינור שמור #20 H=60	
	נקודת תקשורת מלאה הכולכלת: כבל תקשורת אופטי תקני מותקן בצינור #25 סיום בית תפוז אופטי LC\APC לפי דרישות מ"י 1-11801 עם רשים מוכנים מראש להתקנה בארון תקשורת דירתי ובסמוך עם חוט משיכה מרכיבה תקשורת דירתי	
	מנוע תשמלי H=200	
	הכנה לתרמוסטט מזגן- צינור 20 לחלל תקרה	
	תרמוסטט חימום תת רצפתי- יבוצע כפי הנחיות ספק	
	שקע לתנור חימום תשמלי 10 סמ מעל פתח דלת	
	בויילר	
	הכנה לזוגנה טיום בשקע	
	מפסק מאור בודד H=90	אלא אם צוין אחרת במפסקי הדלקה ליד מיטה H=60
	מפסק כפול H=90	
	מפסק מאור מתליף H=90	
	לחצן פעמון דלת H=90	
	מנתק מאור 2X16A / 3X16A	
	מפסק דו קוטבי מאור לחנור חימום תשמלי H=160	
	מפסק הרמה/הורדה לחדרים תשמלי 5 סמ מעל מפסק האורות ע"מ פרים	
	מפסק עם שעון בקיר לבויילר H=180	
	פכל צפיה (מוניטור) +לחצן פתיחה דלת H=120	
	תאורת חרום חד תכליתית 3w LED	
	גלאי עשן בתקרה	
	נקודת מאור בתקרה	
	גלית פנים תפרתי מוגן מים	
	גלית LED עגול שקוע בתקרה	
	גלית LED עגול קירי גובה H=220	
	גלית פנים קירי למנורת ליבה H=120	
	גלית פנים/חוץ קירי מוגן מים H=240 , במרחקי H=220	
	גלית קירי נמוך לתאורת המתאצת מדרגות/שרותים, h=15 מהרצפה /מדרגה	
	גלית מלבני IP65 להתקנה על פרגולה	
	מאוורר להתקנה בחוץ	
	פעמון דלת 220v (גונג) התקנה מעל דלת כניסה	
	הכנה מצלמה אבטחה, צינור 25 וחוט משיכה מארון תקשורת דירתי	

פרט לגבהים של הדלקות,
תאורה ותריסים:

ארון חשמל ותקשורת דירתי

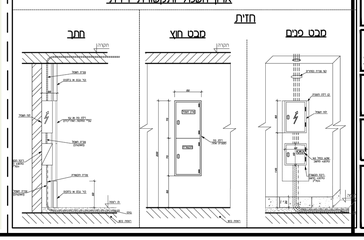

תפוצה	תאריך

מס'	שינויים	תאריך
1	עדכון תכנית	10.12.24
2	עדכון תכנית	15.12.24
3	עדכון תכנית	24.12.24
4	עדכון תכנית	22.4.25

עודכן ע"י: יפעת

א. בסיס
הנדסת חשמל בע"מ
משרד: רז זרוצים 16, ירושלים 93420
טל': 074-7021015 נייד: 050-6550484
פקס: 077-5131015 דוא"ל: office@ebasis.co.il

שם הפרויקט:
נופיה-אלפי מנשה מגרש 20

שם הגיליון:
תוכנית חשמל טיפוסית

קנה מידה: 1:50	לעיון ○ לאישור ○ למכרז ● לביצוע ○	
תאריך: 30.09.2024	מס' קובץ: 675-20.dwg	File:
תכנן: איתן	שרטט: שלומית	אישר: איתן
מס' עדכון: 4	מס' הגליון: 1	מס' הפרויקט: 675