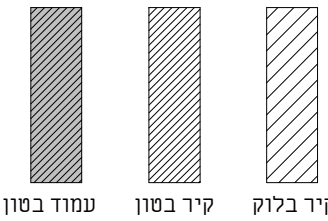


מתכונים:

ניהול פרויקט
מהיסוד - בן סלומון
פיקוח
מהיסוד - בן סלומון
קונסטרוקציה
ערן שילר
מיזוג אוויר
אייל ארז מהנדסים ויועצים בע"מ
אינסטלציה
איתן אלמסי
חשמל
איתן בסיס
אלומיניום
נוף
נתי בלוקא
חשמל חכם
חימום תת רצפתי
איטום
צבי טל
אקוסטיקה
מעליות
קרקע וביסוס
דיה הנדסת קרקע וביסוס
רישוי

[illegible]

מקרא קירות:

[illegible]

אדריכלות


CLIENT NAME:		המחלקה: 01	
PROJECT NAME:		הפרויקט: 02	
קבוצת רכישה נופיה			
DRAWING NAME:		התוכנית: 03	
נופיה - מגרש 1			
SHEET NUMBER:		הפרט: 04	
גליון שער			
SCALE:		EDITION:	
קנה מידה:		דיוור:	
TATUS:			
מסמט		1	
למכר		הילה כהנא	
בדק ע"י:		דפוס ע"י:	
DATE:		היום:	
22.09.2025			

NeumanHaynerArchitects

ניומן חיינר אדריכלים
מורד ההדריס 2, בית חירות
טל 09-9545842


office@nh-arch.com
www.nh-arch.com

נופיה - מגרש 1			
מס' גיליון	שם גיליון	מהדורה	תאריך הפצת המהדורה
A3-1-100	גליון שער	1	22/09/2025
A3-1-101	תכנית קומת קרקע	1	22/09/2025
A3-1-102	תכנית קומת גג	1	22/09/2025
A3-2-200	חזיתות 1	1	22/09/2025
A3-2-201	חזיתות 2	1	22/09/2025
A3-3-100	חתכים	1	22/09/2025
A3-4-101	פרטי פרגולה	1	22/09/2025
A3-4-103	פרטים	1	22/09/2025
A3-6-1000	רשימת פתחים	1	22/09/2025

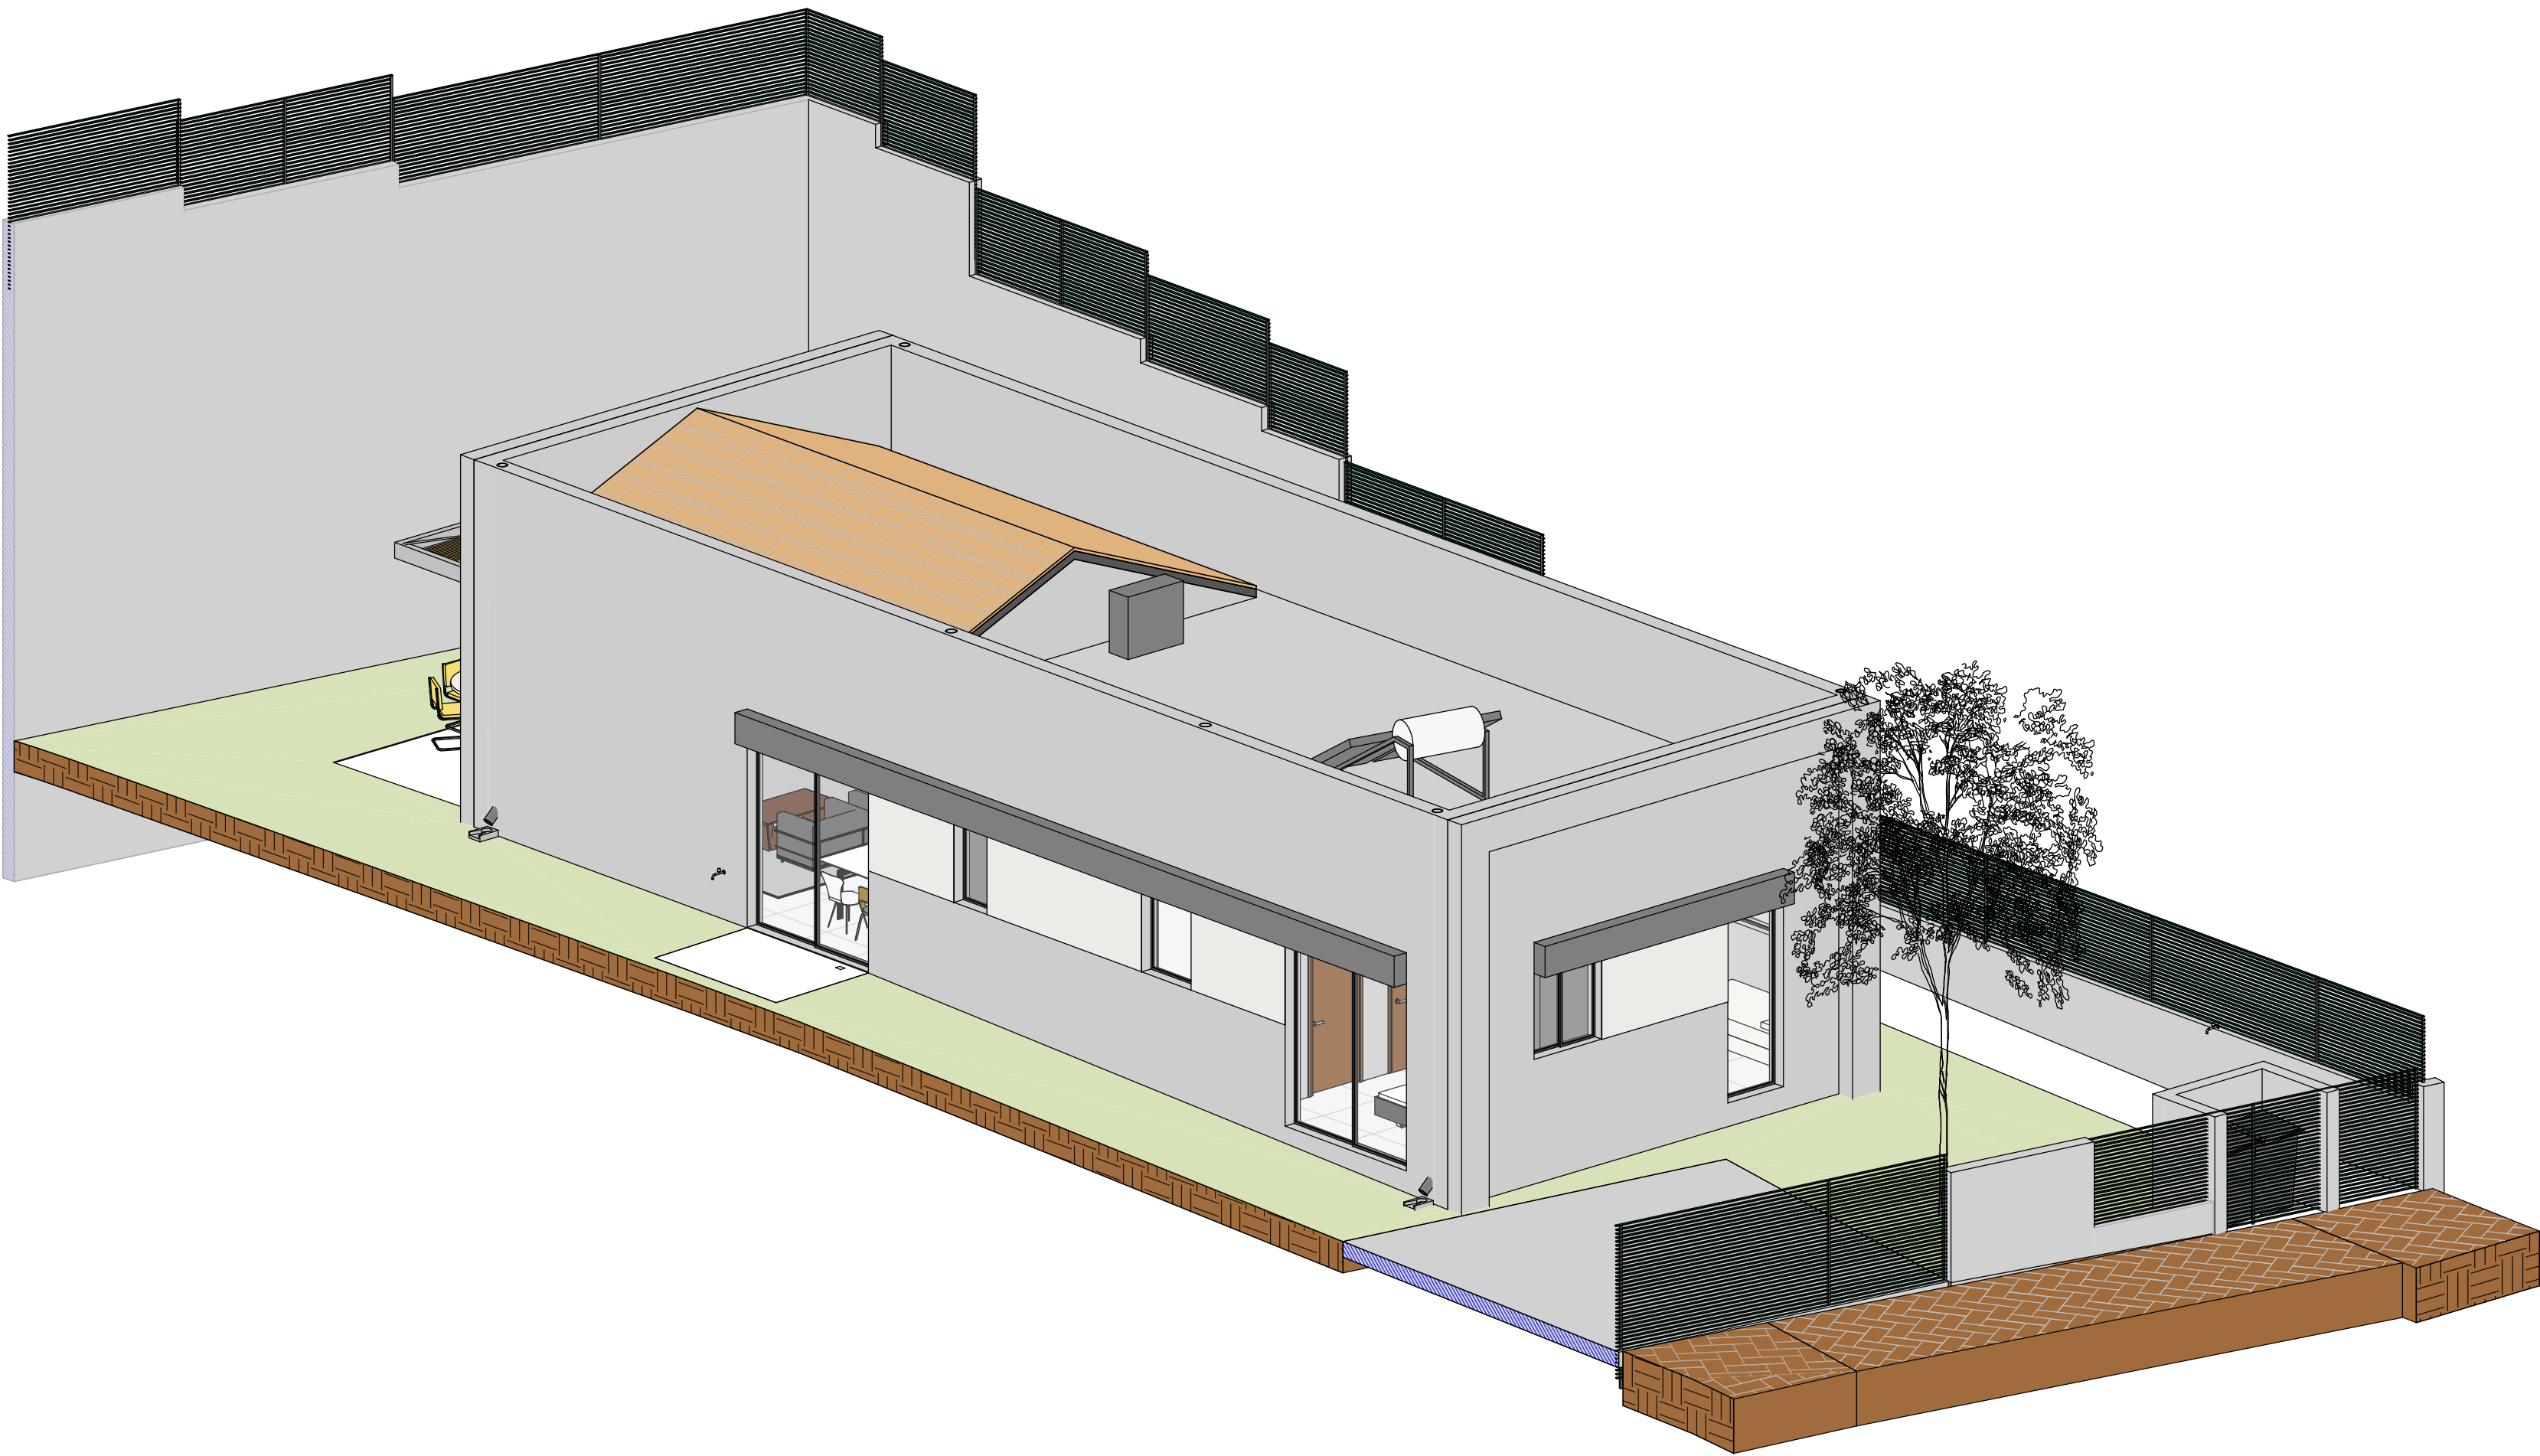

הערות:

- יש לעבוד במקביל לתכניות יועצים המאושרות על ידי האדריכל.
- פרטי ספי חלון - עפ"י חוברת אלומיניום של הספק הנבחר ובתיאום מול אדריכל.
- חימום תת רצפתי (במידה ויש במגרש זה) עפ"י פרטי הספק ובתיאום מול אדריכל.
- יש לעבוד במקביל לתכניות עיצוב פנים (במידה ויש מעצב פנים במגרש זה) המאושרות על ידי האדריכל.
- באחריות הקבלן לעדכן את האדריכל על אי התאמה בין התכניות יועצים לאדריכלות.
- כל הדלתות לפי מפרט מצורף.
- כל אלמנטי הבטון יקבלו התייחסות תרמית לפי הנחיות יועץ.
- פרטי איטום, בידוד וניקוז עפ"י תכניות יועצים ובאחריות הקבלן.

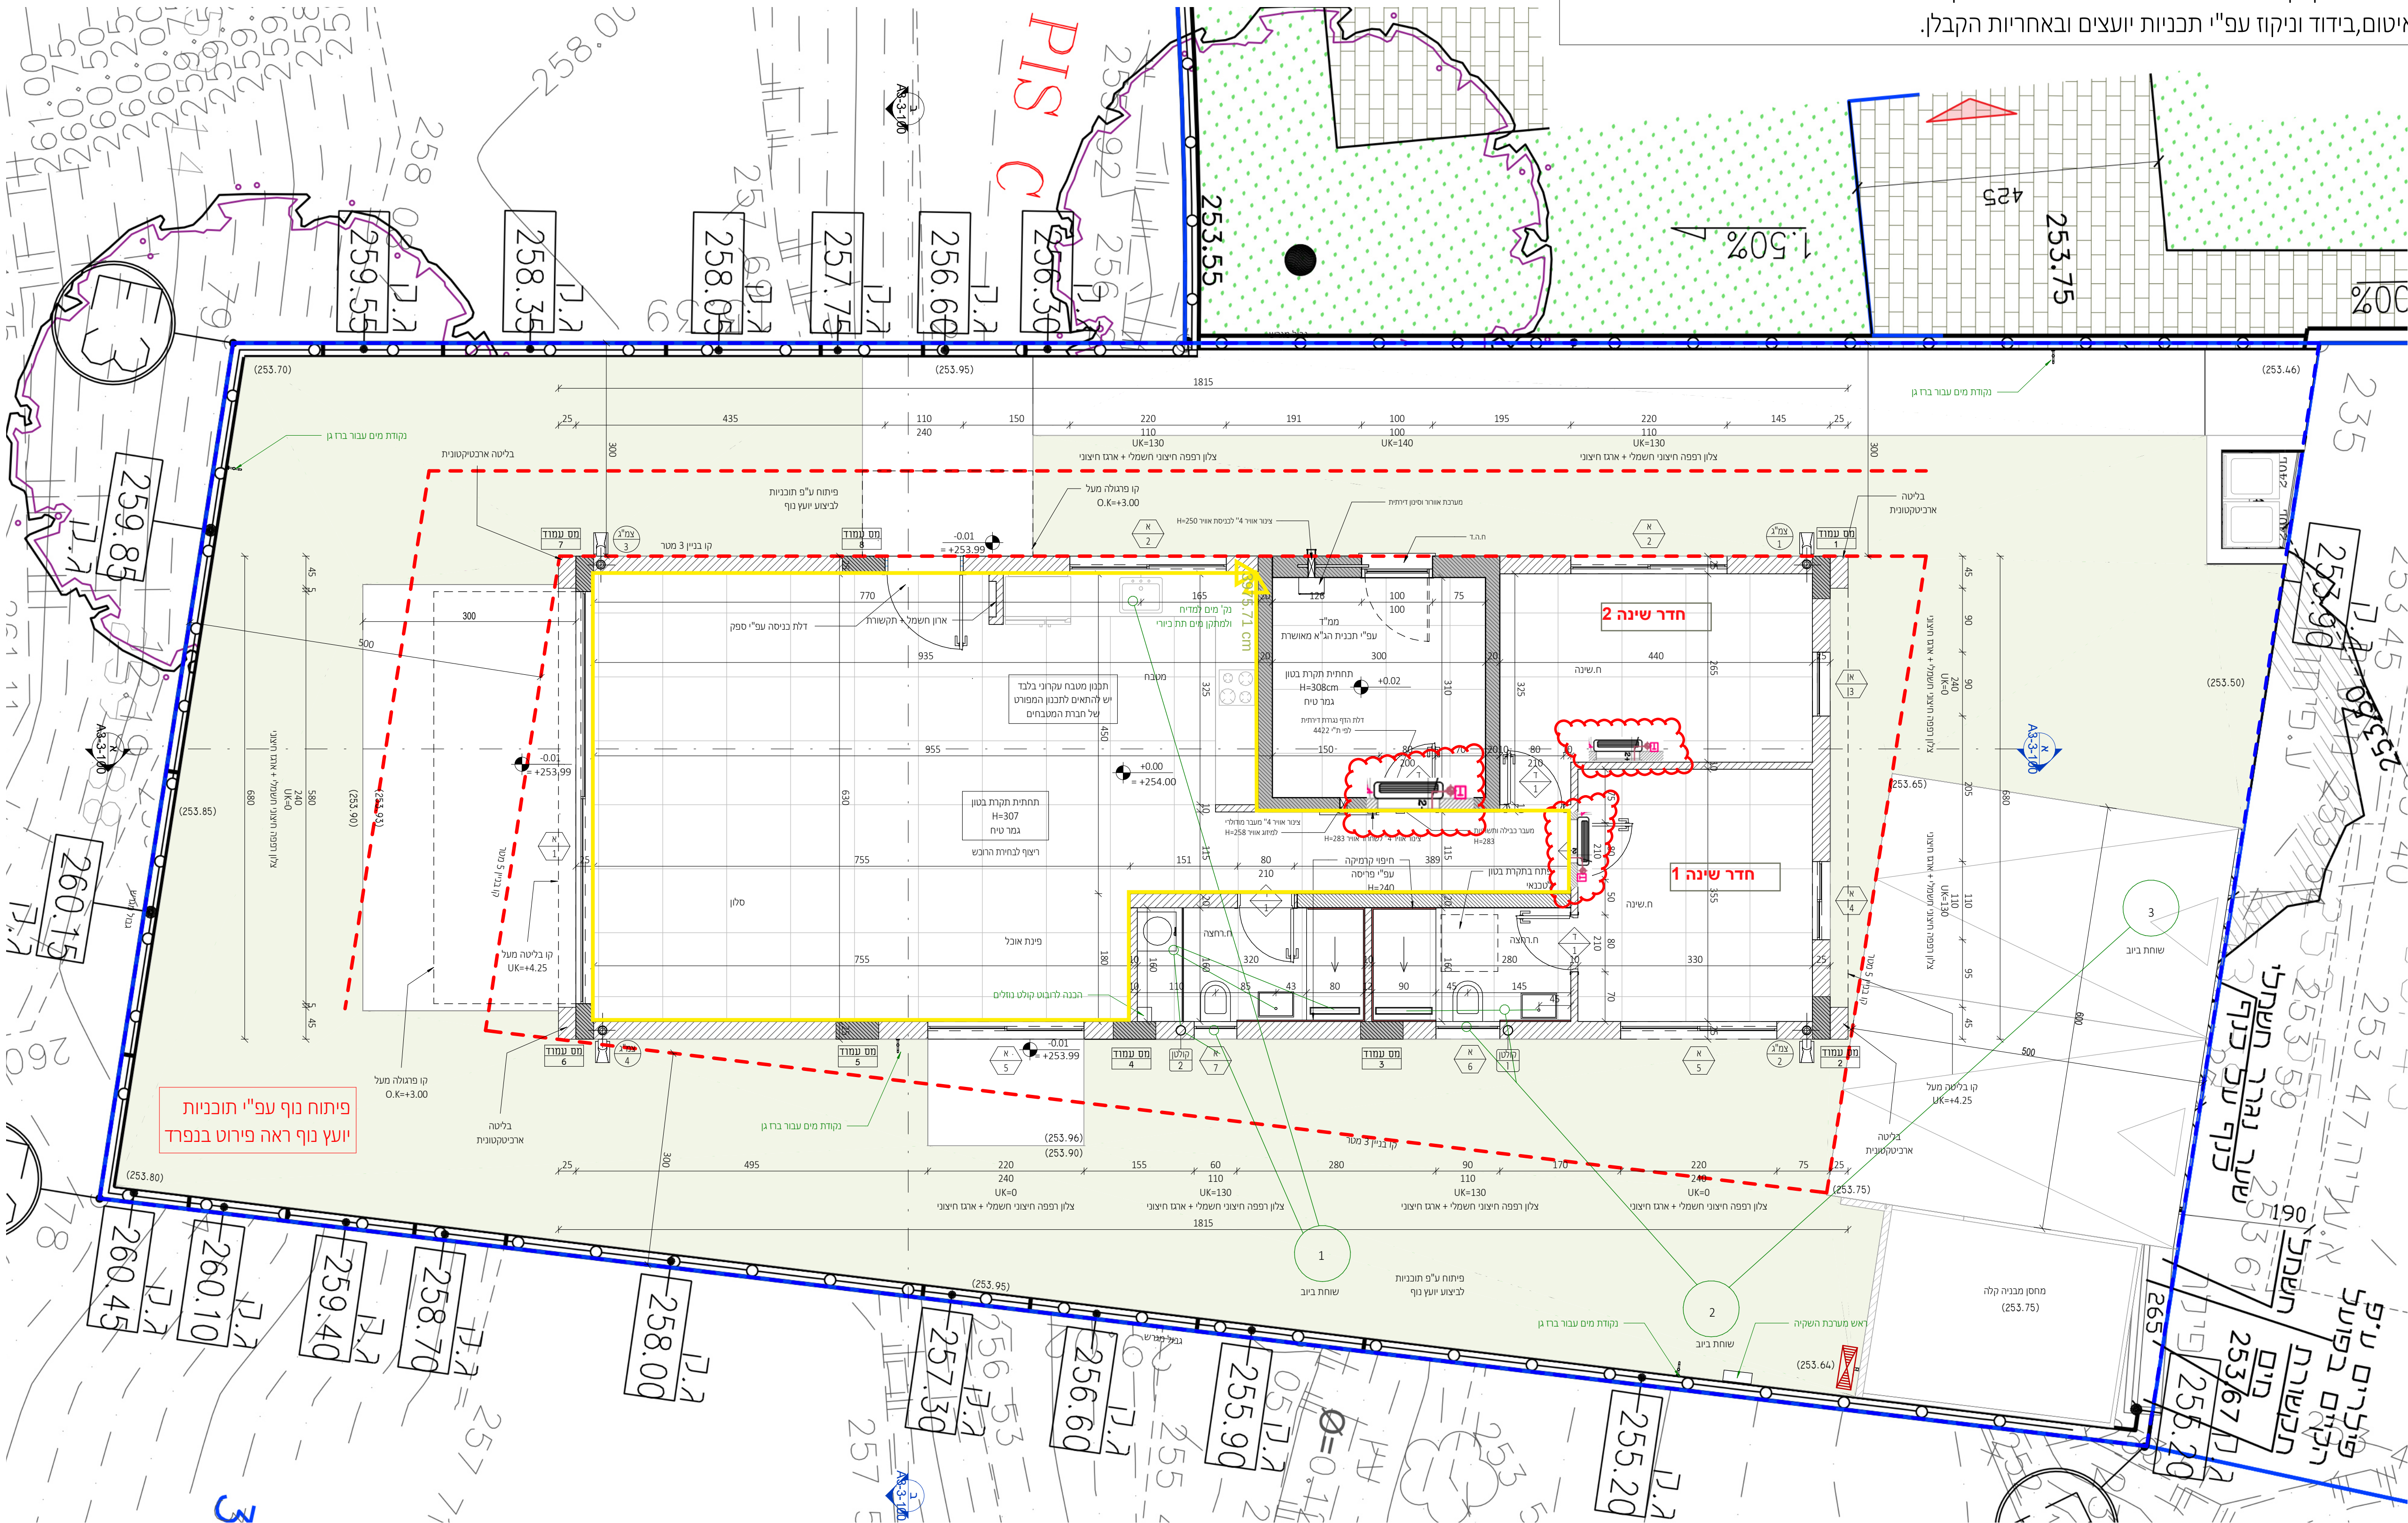

מתכנים:

ניהול פרויקט
מהיסוד - בן סלומון
פיקוח
מהיסוד - בן סולומון
קונסטרוקציה
ערן שילר
מיזוג אוויר
אייל ארז מהנדסים ויועצים בע"מ
אינסטליציה
איתן אלמסי
חשמל
איתן בסיס
אלומיניום
נוף
נתי בלוקא
חשמל חכם
חימום תת רצפתי
איטום
צבי טל
אקוסטיקה
מעליות
קרקע וביסוס
דיה הנדסת קרקע וביסוס
רישוי

± 0.00 = +254.00

- הערות:
- תכנית זו אינה קריאה יחד עם תכנית הרישוי.
 - התכנית אינה חייבת להיות חתומה על ידי המעצב.
 - התכנית אינה חייבת להיות חתומה על ידי המעצב.
התכנית אינה חייבת להיות חתומה על ידי המעצב.

משרד קירנות:

קיר בלוק
קיר בסוס
מגדל בסוס

תאריך	תיאור	מהדורה
22/09/2025	מכרז	1

אדריכלות

שם המוסד:

קבוצת רכישה נופיה

שם הפרויקט:

נופיה - מגרש 1

שם הגיליון:

תכנית קומת קרקע

מספר גיליון:

A3-1-101

חומרה:

EDITION: קנה מידה: SCALE:

STATUS: 1:50

שורש ע"י: הילה בהנא

תאריך: 22.09.2025

NeumanHaynerArchitects

נירן חיינר אדריכלים
מנכ"ל
office@nh-arch.com
www.nh-arch.com
09-9546842

זכויות יוצרים / ע"פ הנחיות ע"ד

פרטי איטום, בידוד וניקוז הגג עפ"י תכניות יועצים ובאחריות הקבלן

מתכונים:


ניהול פרויקט
מהיסוד - בן סלומון
פיקוח
מהיסוד - בן סלומון
קונסטרוקציה
ערן שילר
מיזוג אוויר
אייל ארז מהנדסים ויועצים בע"מ
אינסטלציה
איתן אלמסי
חשמל
איתן בסיס
אלומיניום
נוף
נתי בלוקא
חשמל חכם
חימום תת רצפתי
איטום
צבי טל
אקוסטיקה
מעליות
קרקע וביסוס
דיה הנדסת קרקע וביסוס
רישוי

$$\pm 0.00 = +254.00$$

הערות:
 1. תביתו ויש לקרוא יחד עם הכביות הוועצים.
 2. גובה אסכולים: ארבע תביות פחות.
 3. המידות הן בין קירות ואלו כולל מים.
 4. פחות השטח שמיני המבנה, כלכלי, מדורות, שבילים, רציפות,
 5. פשיטות בסיס, ארבע יתונות: ארבע תביות פחות.
 6. אסכולים: קירות ורצפות המבנה עם הקרקע ובידוד תרמי לאורך המעטרים
 7. והקורות על הקירות- גליות ויש מיני (יתון)- ארבע תביות קונסטרוקציה
 8. אף אף כי יבוצע כל מישור אופקי חמור. המבנה
 9. יש תרמי במסגרת עם מפרס מרמור, חמור. עיי פיקוד מרמור.

[illegible]

זקרא קירות:

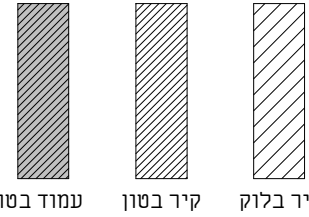[illegible]

אדריכלות

CLIENT NAME: _____ שם המזמין:

קבוצת רכישה נופיה


PROJECT NAME: _____: שם הפרויקט:

נופיה - מגרש 1

DRAWING NAME: ס הגליון:

SHEET NUMBER: 190 גליון:

A3-1-102

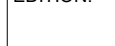SCALE:	קנה מידה:	EDITION:	חזרות:
1 : 50			
STATUS:	סטוס		
למכר			
	נבדק ע"י:	הילה כהנא	דפוס ע"י:
DATE:	22.09.2025		מ"ד:





NeumanHaynerArchitects

office@nh-arch.com
www.nh-arch.com

מזל 09-9545842

זכויות ייצור / ע"פ הנחיות עו"ד

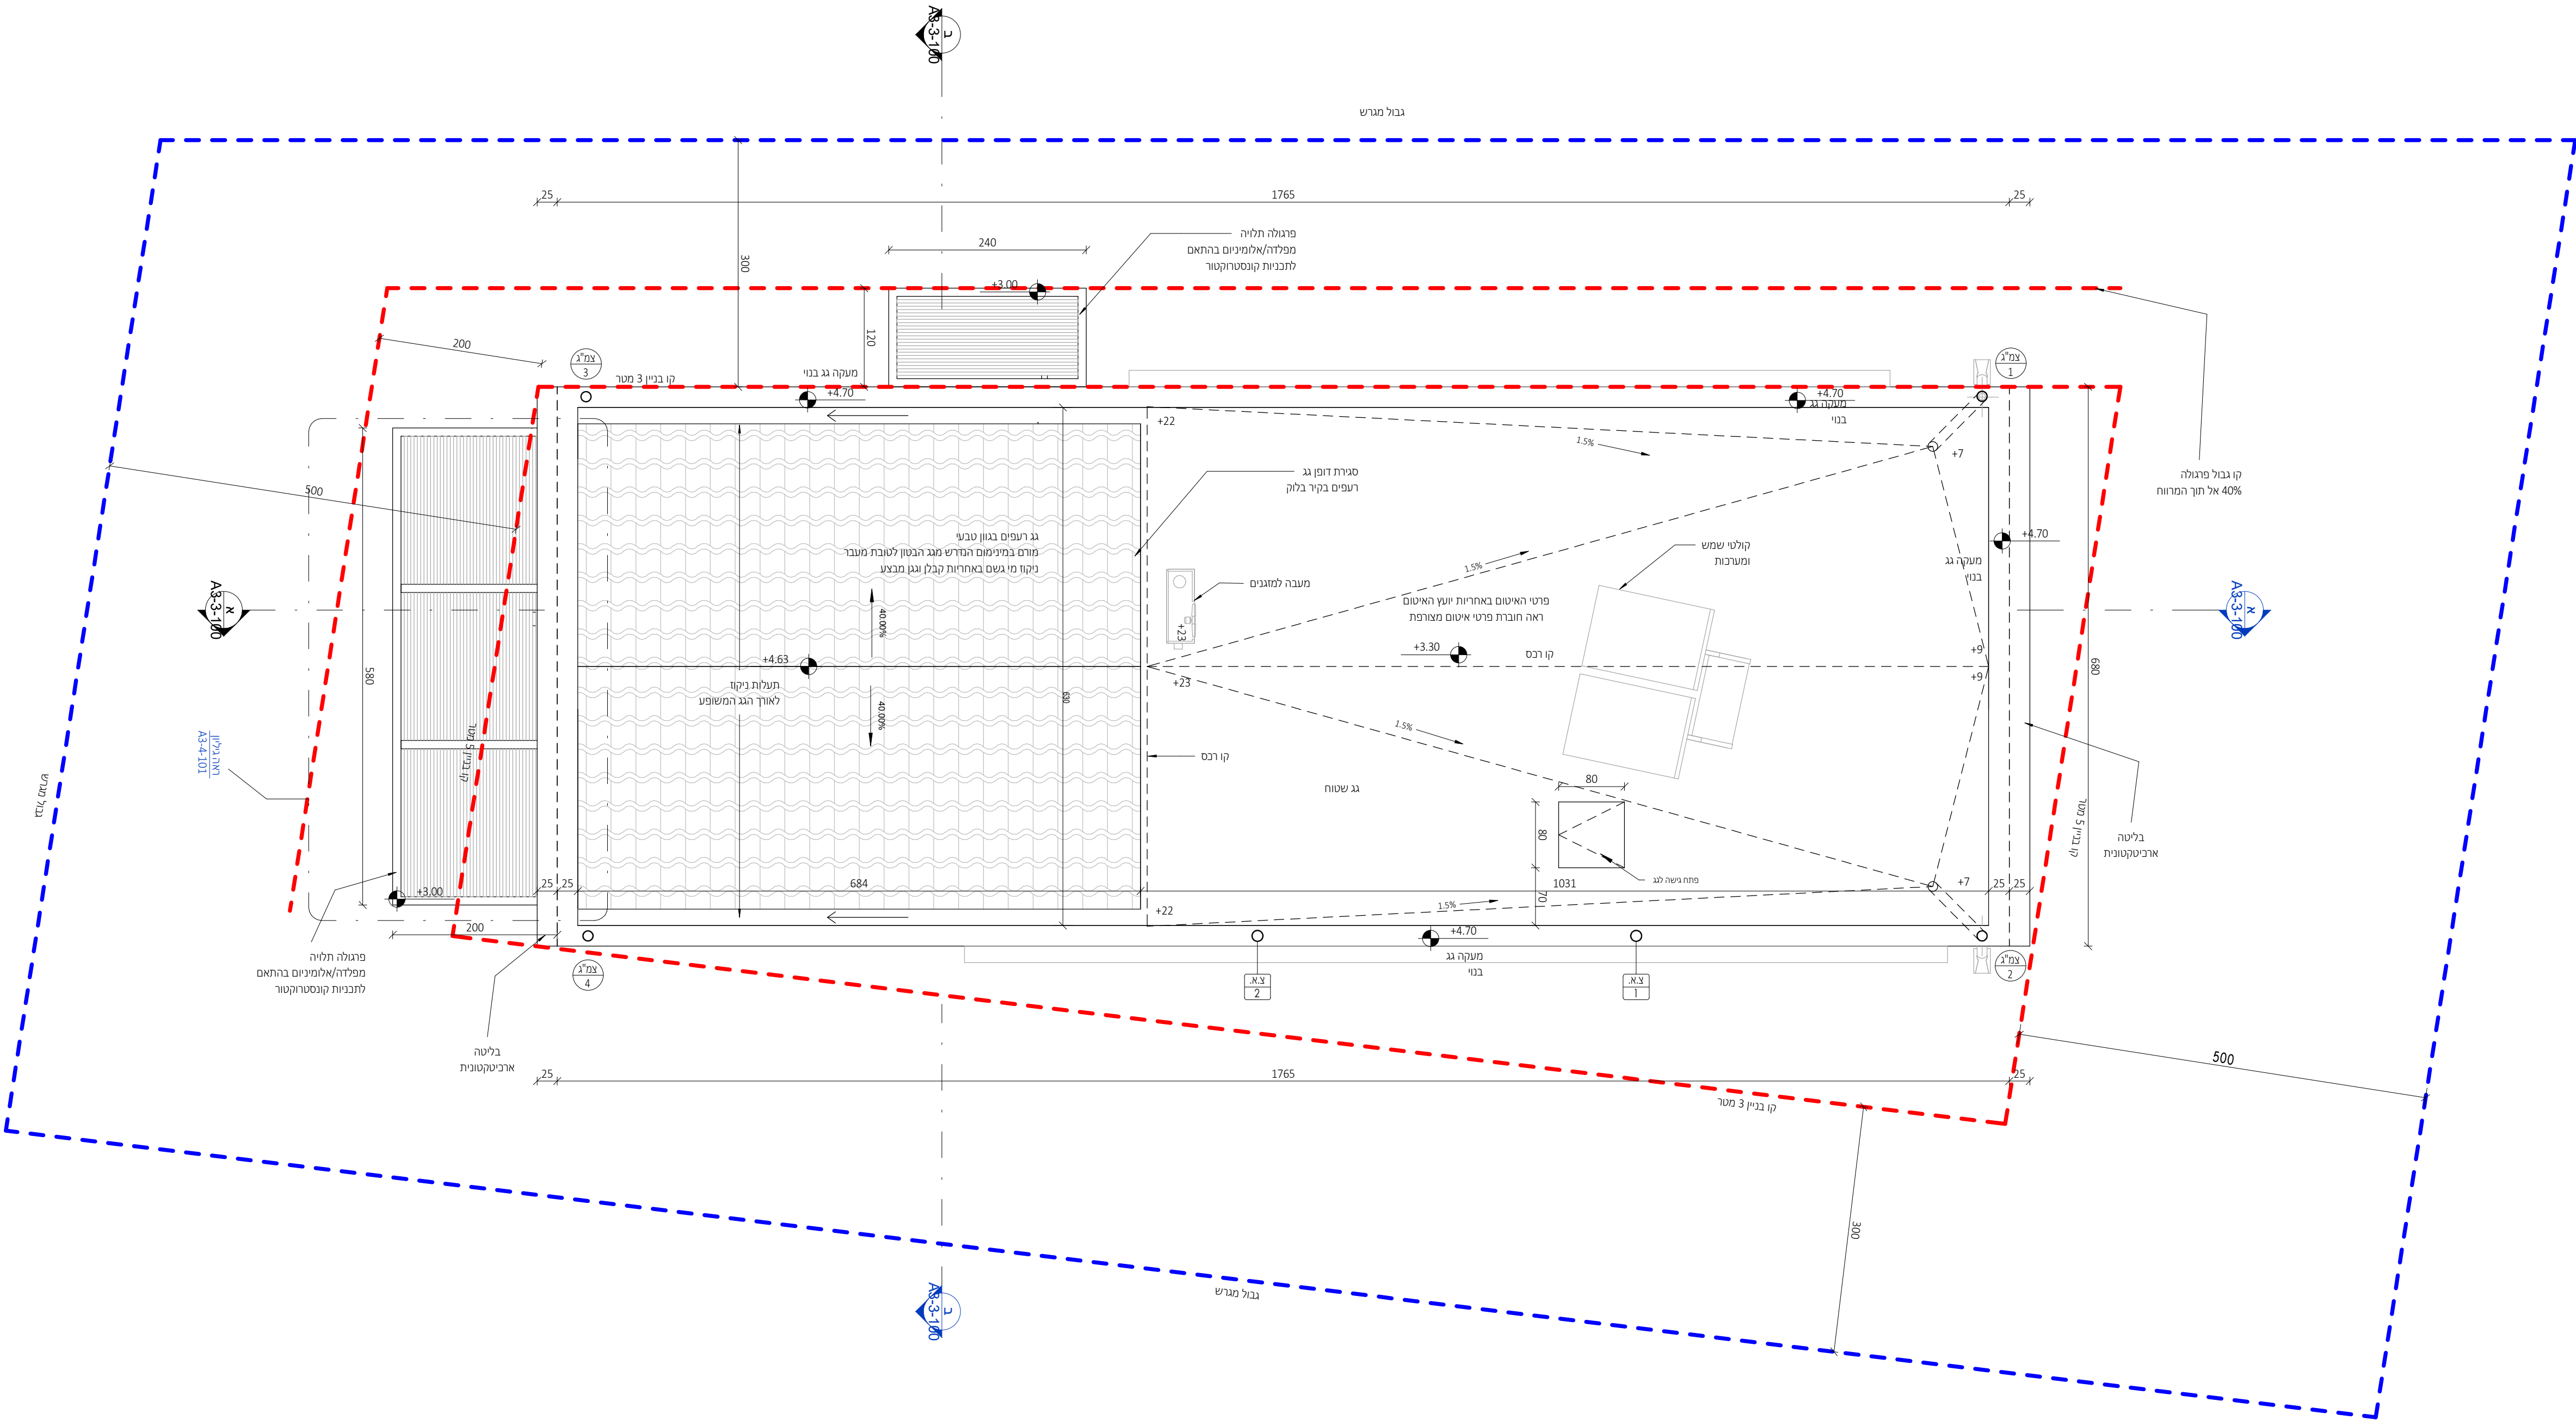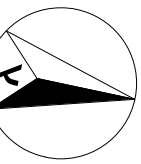


מתכננים:

ניהול פרויקט
מהיסוד - בן סלומון
פיקוח
מהיסוד - בן סולומון
קונסטרוקציה
ערן שילר
מיזוג אוויר
אייל ארז מהנדסים ויועצים בע"מ
אינסטלציה
איתן אלמסי
חשמל
איתן בסיס
אלומיניום
נוף
נתי בלוקא
חשמל חכם
חימום תת רצפתי
איטום
צבי טל
אקוסטיקה
מעליות
קרקע וביסוס
דיה הנדסת קרקע וביסוס
רישוי

± 0.00 = +254.00
הערות: 1. תכנית זו יש לקרוא יחד עם תכנית הרישום. 2. גובה אבטומיטי - ראה תכנית פיתוח. 3. הפירות הן בין קירות הבניה ולא כולל פחים. 4. פיתוח השטח סביב המבנה, כולל, מדרגות, גדרות, שבילים, ריצופים, שטחים גזרים, חניה וגן וא תכנית פיתוח. 5. איטום קירות ורצפות המבנה כמעט עם הקרקע ובידוד תרמי לאורך העמודים והקורות וגם על התקרות. כלירות או עם סימני גיטון- ראה תכנית קונסטרוקציה. 6. אף דים יבוצע בכל מישור אופקי הכולל מהבנין. 7. סיום תרמי במסד י"ד ע"פ מפרט תומקיר, מאושר ע"י פיקוד העורף.
המבצע אחראי למידות : עליו לבקר ולבדוק את כל המידות בתכנית ובקטע המבנה. במסגרת של מידות או אי התאמה בתכנית /או בבנין, עליו להודיע על כך מיד לאדריכל בסרט המשרד המשרד בעברות. המבצע יחזיק את רוק בתכנית שאושר לכניס. המבצע יחזיק אתה, בכל עת, של מידות של תכנית. אין לקבוע מידות על ידי חדיה בשום תכנית רחבה רחבה האדריכל ואין לשנות כל שימוש בה או ברעיונות הגלומים בה, אלא באישור בכתב מהאדריכל. מוחזקת /או יושב אשר שמו רשום בתכנית זו, נושא לכיד באחריות המקצועית והתקנית לתכנית. על המפקח והמבצע לודא התאמת התכנית האדריכלית "כניס" לתכנית זו, ויתר, המכר והתכנית האושרות ע"י כל גורמים הרשמיים. תכנית כוללת את כל האמצעים והידוע על ימים תוצאות.

משרד קירות:

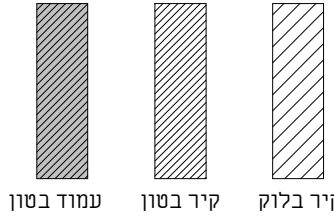

תאריך	תיאור	מהדורה
22/09/2025	מכר	1

אדריכלות

שם המסין:	CLIENT NAME:
קבוצת רכישה נופיה	
שם הפרויקט:	PROJECT NAME:
נופיה - מגרש 1	
שם הגליון:	DRAWING NAME:
חזיתות 1	
מספר גליון:	SHEET NUMBER:
A3-2-200	
מחזור:	EDITION:
SCALE:	קנה מידה:
1 : 50	
STATUS:	סטוס
למכר	
שורסס ע"י:	הילה בהנא
DATE:	22.09.2025
תאריך:	


NeumanHaynerArchitects

נויטן חיינר אדריכלים
מודד והנדס 2, בית חירות
09-954642 78
office@nh-arch.com
www.nh-arch.com

22/09/2025 9:58:59


זכיות ייצור / ע"פ הנחיות ע"ד

פיתוח נוף עפ"י תוכניות
יועץ נוף ראה פירוט בנפרד

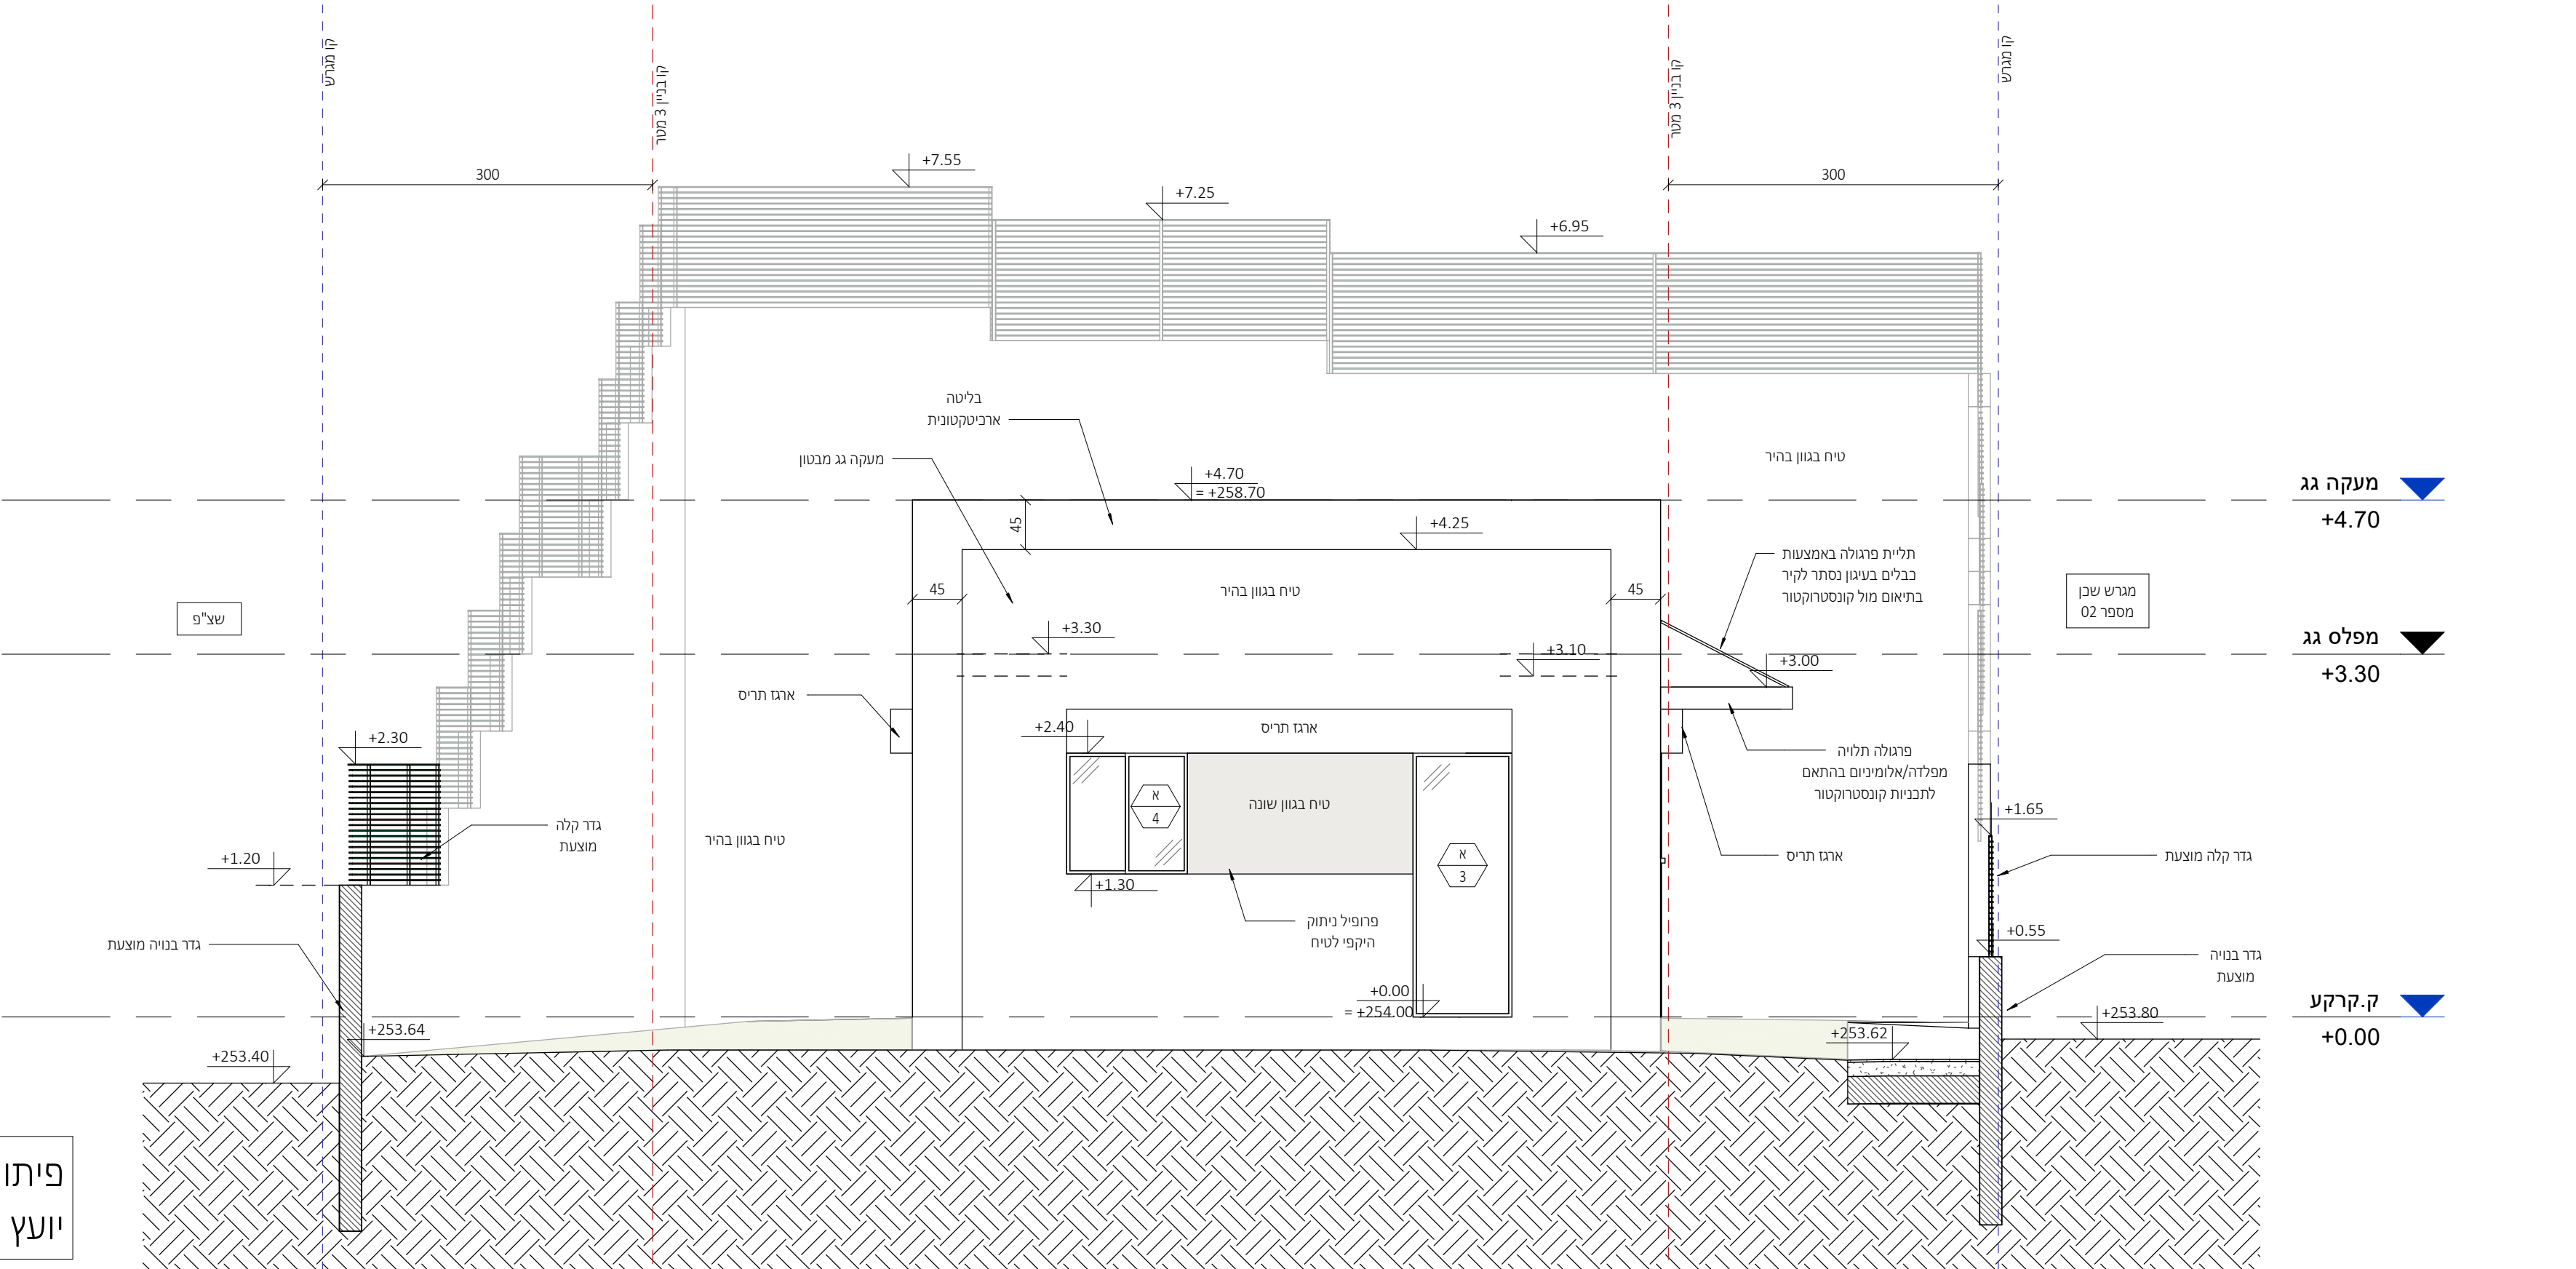

חזית צפונית

1 : 50

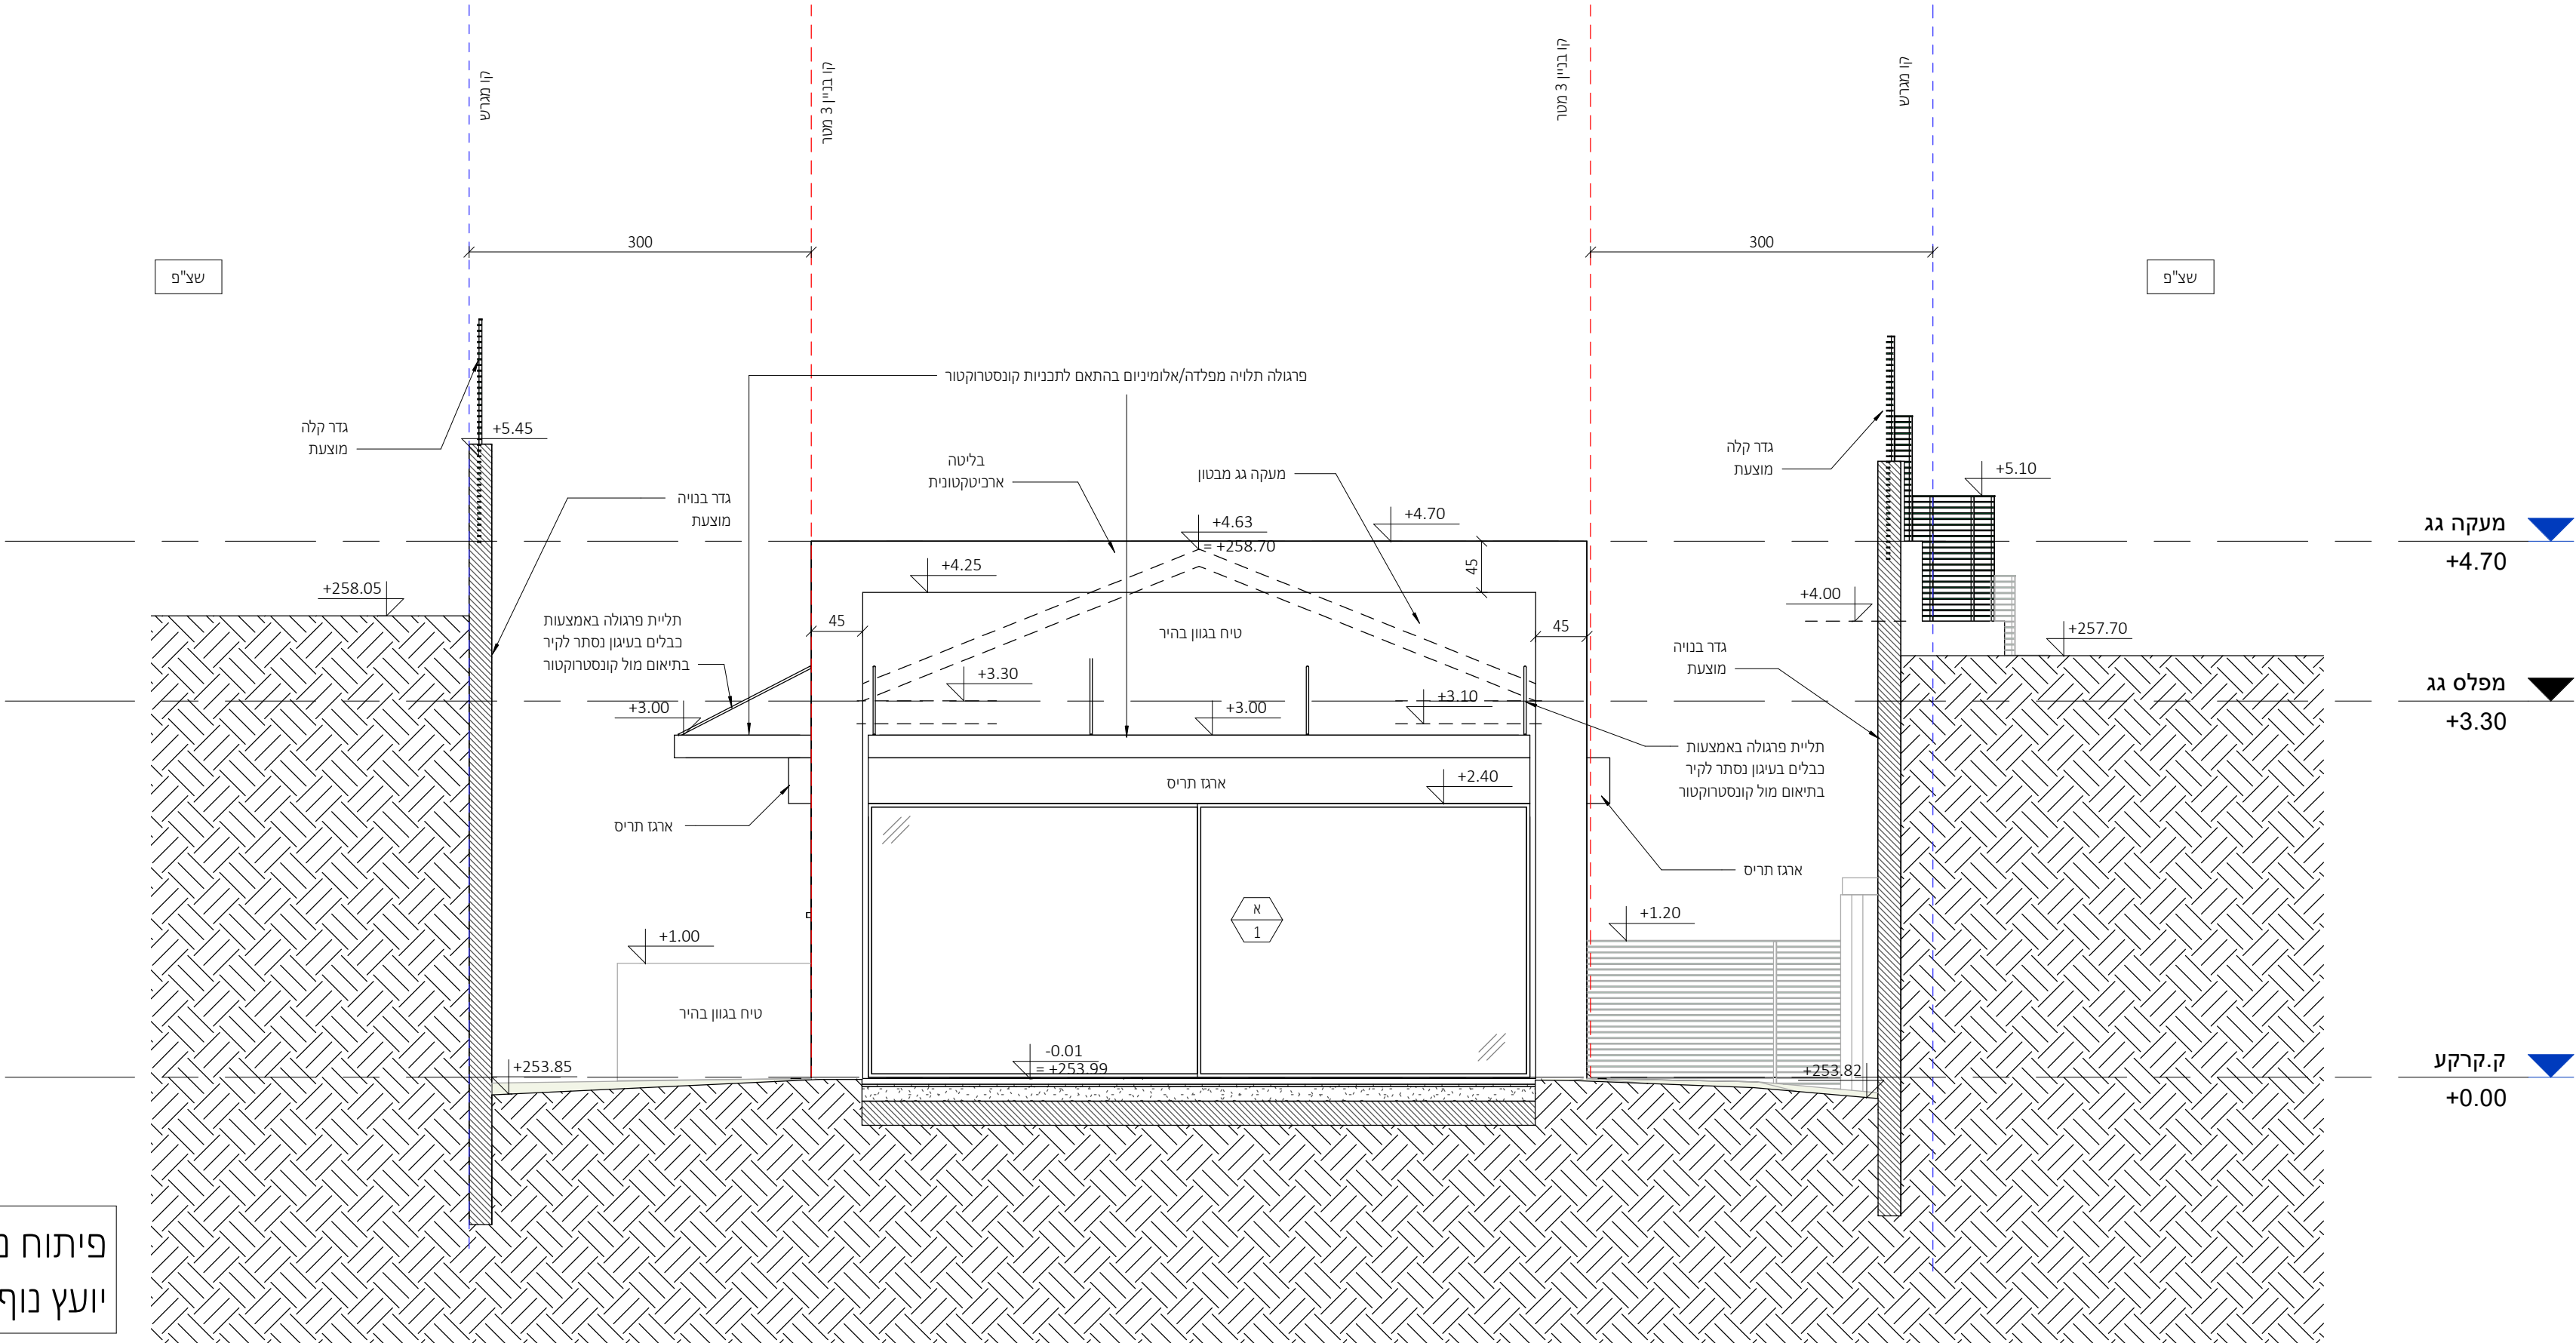

פיתוח נוף עפ"י תוכניות
יועץ נוף ראה פירוט בנפרד

חזית דרומית

1 : 50

מתכננים:

ניהול פרויקט
מהיסוד - בן סלומון
פיקוח
מהיסוד - בן סולומון
קונסטרוקציה
ערן שילר
מיזוג אוויר
אייל ארז מהנדסים ויועצים בע"מ
אינסטלציה
איתן אלמסי
חשמל
איתן בסיס
אלומיניום
נוף
נתי בלוקא
חשמל חכם
חימום תת רצפתי
איטום
צבי טל
אקוסטיקה
מעליות
קרקע וביסוס
דיה הנדסת קרקע וביסוס
רישוי

± 0.00 = +254.00
הערות: 1. תכנית זו אינה קריאה יחד עם תכנית הרישום. 2. גובה אבטומנטים: ראה תכנית פיתוח. 3. המידות הן בין קירות הבניה ולא כולל פיתוח. 4. פיתוח השטח סביב המבנה, כולל: מדרגות, גדרות, שבילים, ריצופים, שטחים גזירים, חניה וכו' ראה תכנית פיתוח. 5. איטום קירות ורצפות המבנה כמתנן עם הקרקע ובנידוד חורף לאורך המסדרים והקירות של המבנה. כליות לא עם סימני גיבוי. ראה תכנית קונסטרוקציה. 6. אין מים יבוצעו בכל מישור אופקי הכולל מחביון. 7. סייח חומי בממד"י ע"פ מפרט ותומקיר, מאושר ע"י פיקוד העורף. המבצע אחראי לסידור: עליו לבקר ולבדוק את כל המידות בתכנית ובקטע המבנה. במסגרת של מידות או אי התאמה בתכנית /או בבנין, עליו להודיע על כך מיד לאחריו בסדר המשיך בעבודתו. המבצע יושמש או ויקי בתכנית המשיך באישור לכניס. המבצע יחויב באחריות, בכל שלב, של מידות של תכנית. אין לקבוע מידות על ידי חידוש בשטח. תכנית היתה רכוש האדריכל ואין לשמש כל שימוש בה או ברעיונות הגלומים בה, אלא באישור בכתב מהאדריכל. מחברים /או יועץ אשר שמו רשום בתכנית זו, נושא לכך באחריות המקצועית והחוקית לתכנית. על התפתח והתקבל ליוזא התאמת התכנית האדריכלית "כניס" לתכנית כוללת את כל האחריות והידוע על ליום תחלפת.

משרד קירות:

קיר בלוק
קיר בסון
מחוד בסון

תאריך	תיאור	מהדורה
22/09/2025	מכרז	1

אדריכלות


שם המוסד:	CLIENT NAME:
קבוצת רכישה נופיה	
שם הפרויקט:	PROJECT NAME:
נופיה - מגרש 1	
שם הגיליון:	DRAWING NAME:
חזיתות 2	
מספר גיליון:	SHEET NUMBER:
A3-2-201	
תאריך:	EDITION:
שורה 1:	קנה מידה:
1	1 : 50
שורה 2:	סטוס:
למכרז	
שורה 3:	תאריך:
22.09.2025	

NeumanHaynerArchitects

נירן חיינו אדריכלים
מודד תודות 2, בית חירות
09-954642 78
www.nh-arch.com

office@nh-arch.com
www.nh-arch.com

זכיות ייצור / ע"פ הנחיות ע"ד

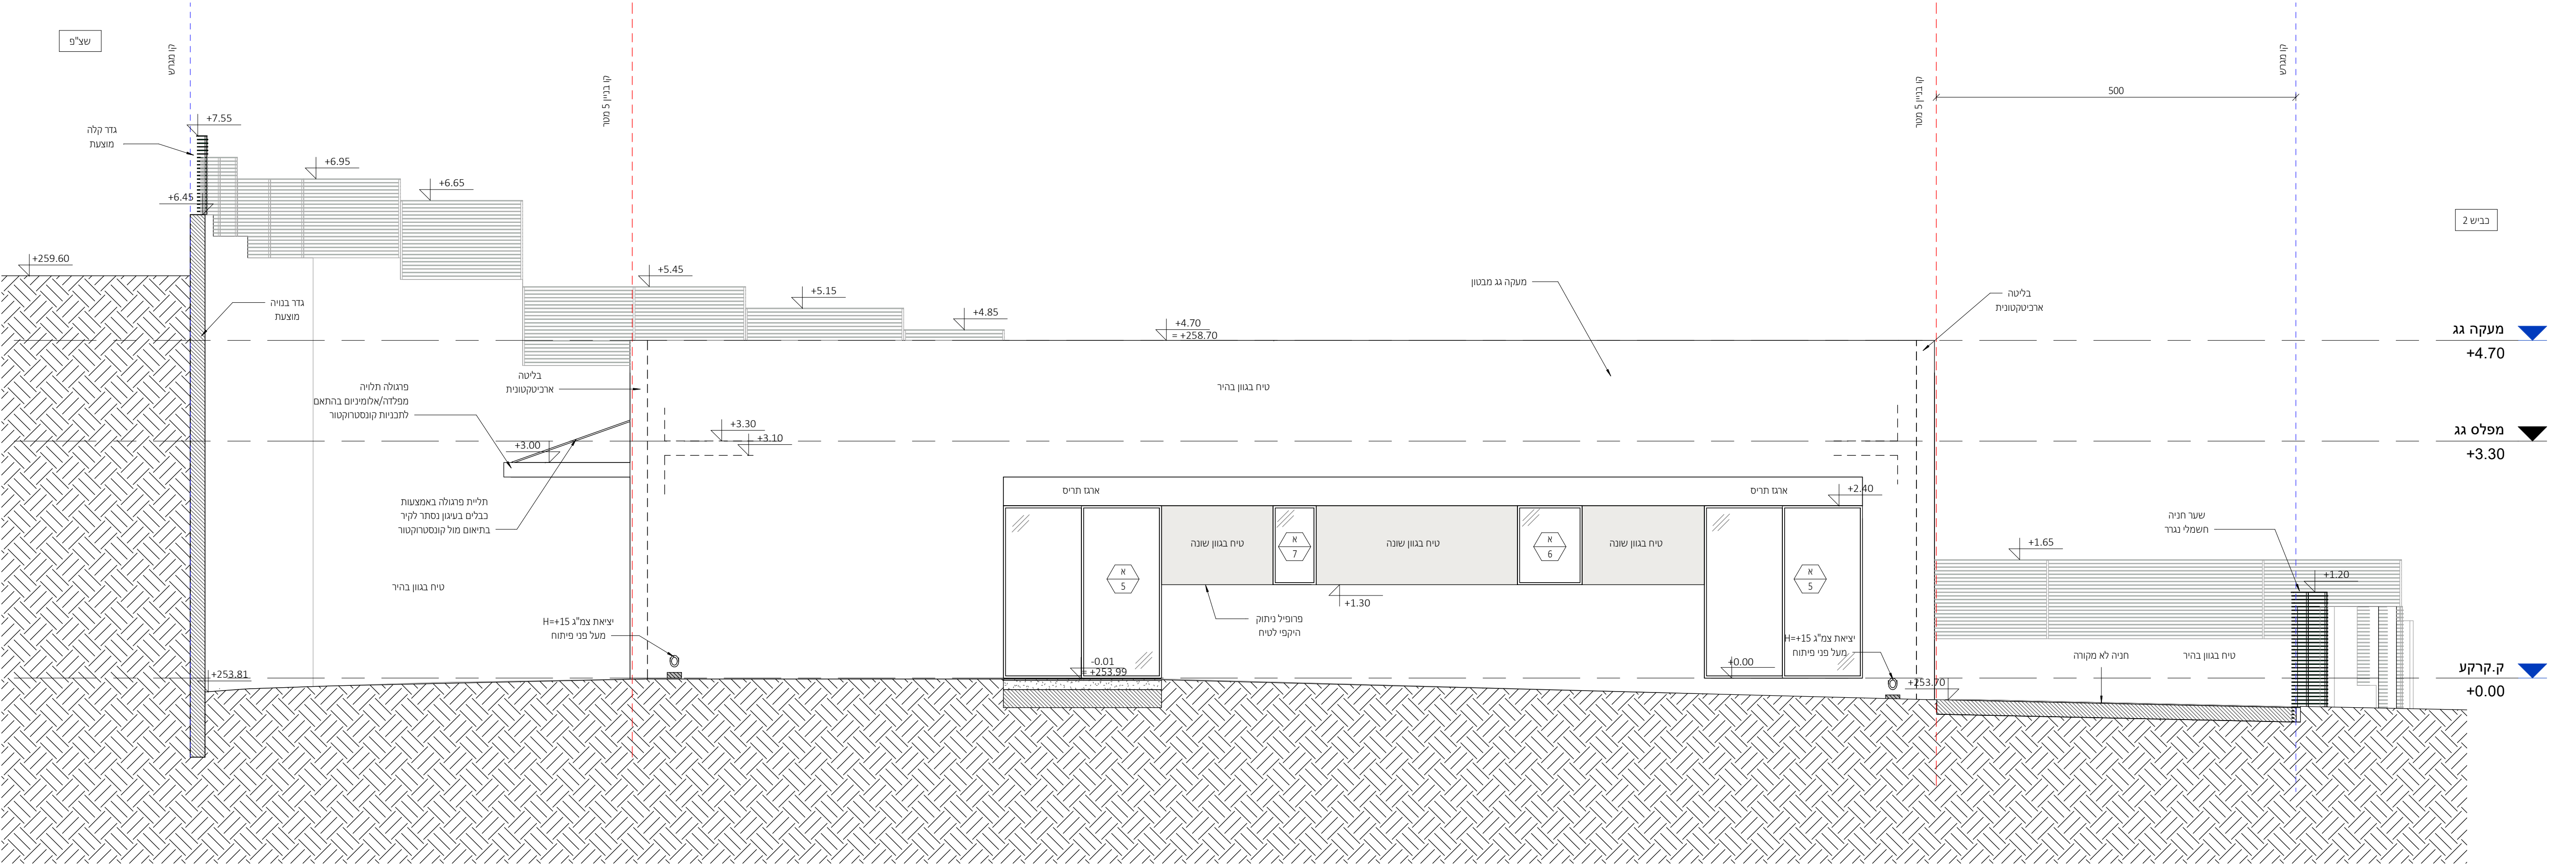

מתכונים:

ניהול פרויקט
מהיסוד - בן סלומון
פיקוח
מהיסוד - בן סלומון
קונסטרוקציה
ערן שילר
מיוזג אוויר
אייל ארז מהנדסים ויועצים בע"מ
אינסטלציה
איתן אלמסי
חשמל
איתן בסיס
אלומיניום
נוף
נתי בלוקא
חשמל חכם
חימום תת רצפתי
איטום
צבי טל
אקוסטיקה
מעליות
קרקע וביסוס
דיה הנדסת קרקע וביסוס
ירשני

[illegible]


קרא קירות:

ADRIKOLAT	
CLIENT NAME:	המסין:
קבוצת רכישה נופיה	
PROJECT NAME:	הפרויקט:
נופיה - מגרש 1	
ORDER NAME:	הזמין:
חתיכים	
SHEET NUMBER:	פר גזיון:
A3-3-100	
SCALE:	קנה מידה:
1 : 50	
EDITION:	דורד:
000000	
STATUS:	
למכר	
נבדק ע"י:	
09.02.2022	
DATE:	יורד:
22.09.2025	


NeumanHaynerArchitects

ימן חיינר אדריכלים
ורד ההדרים 2, בית חירות
09-9545842

office@nh-arch.com
www.nh-arch.com

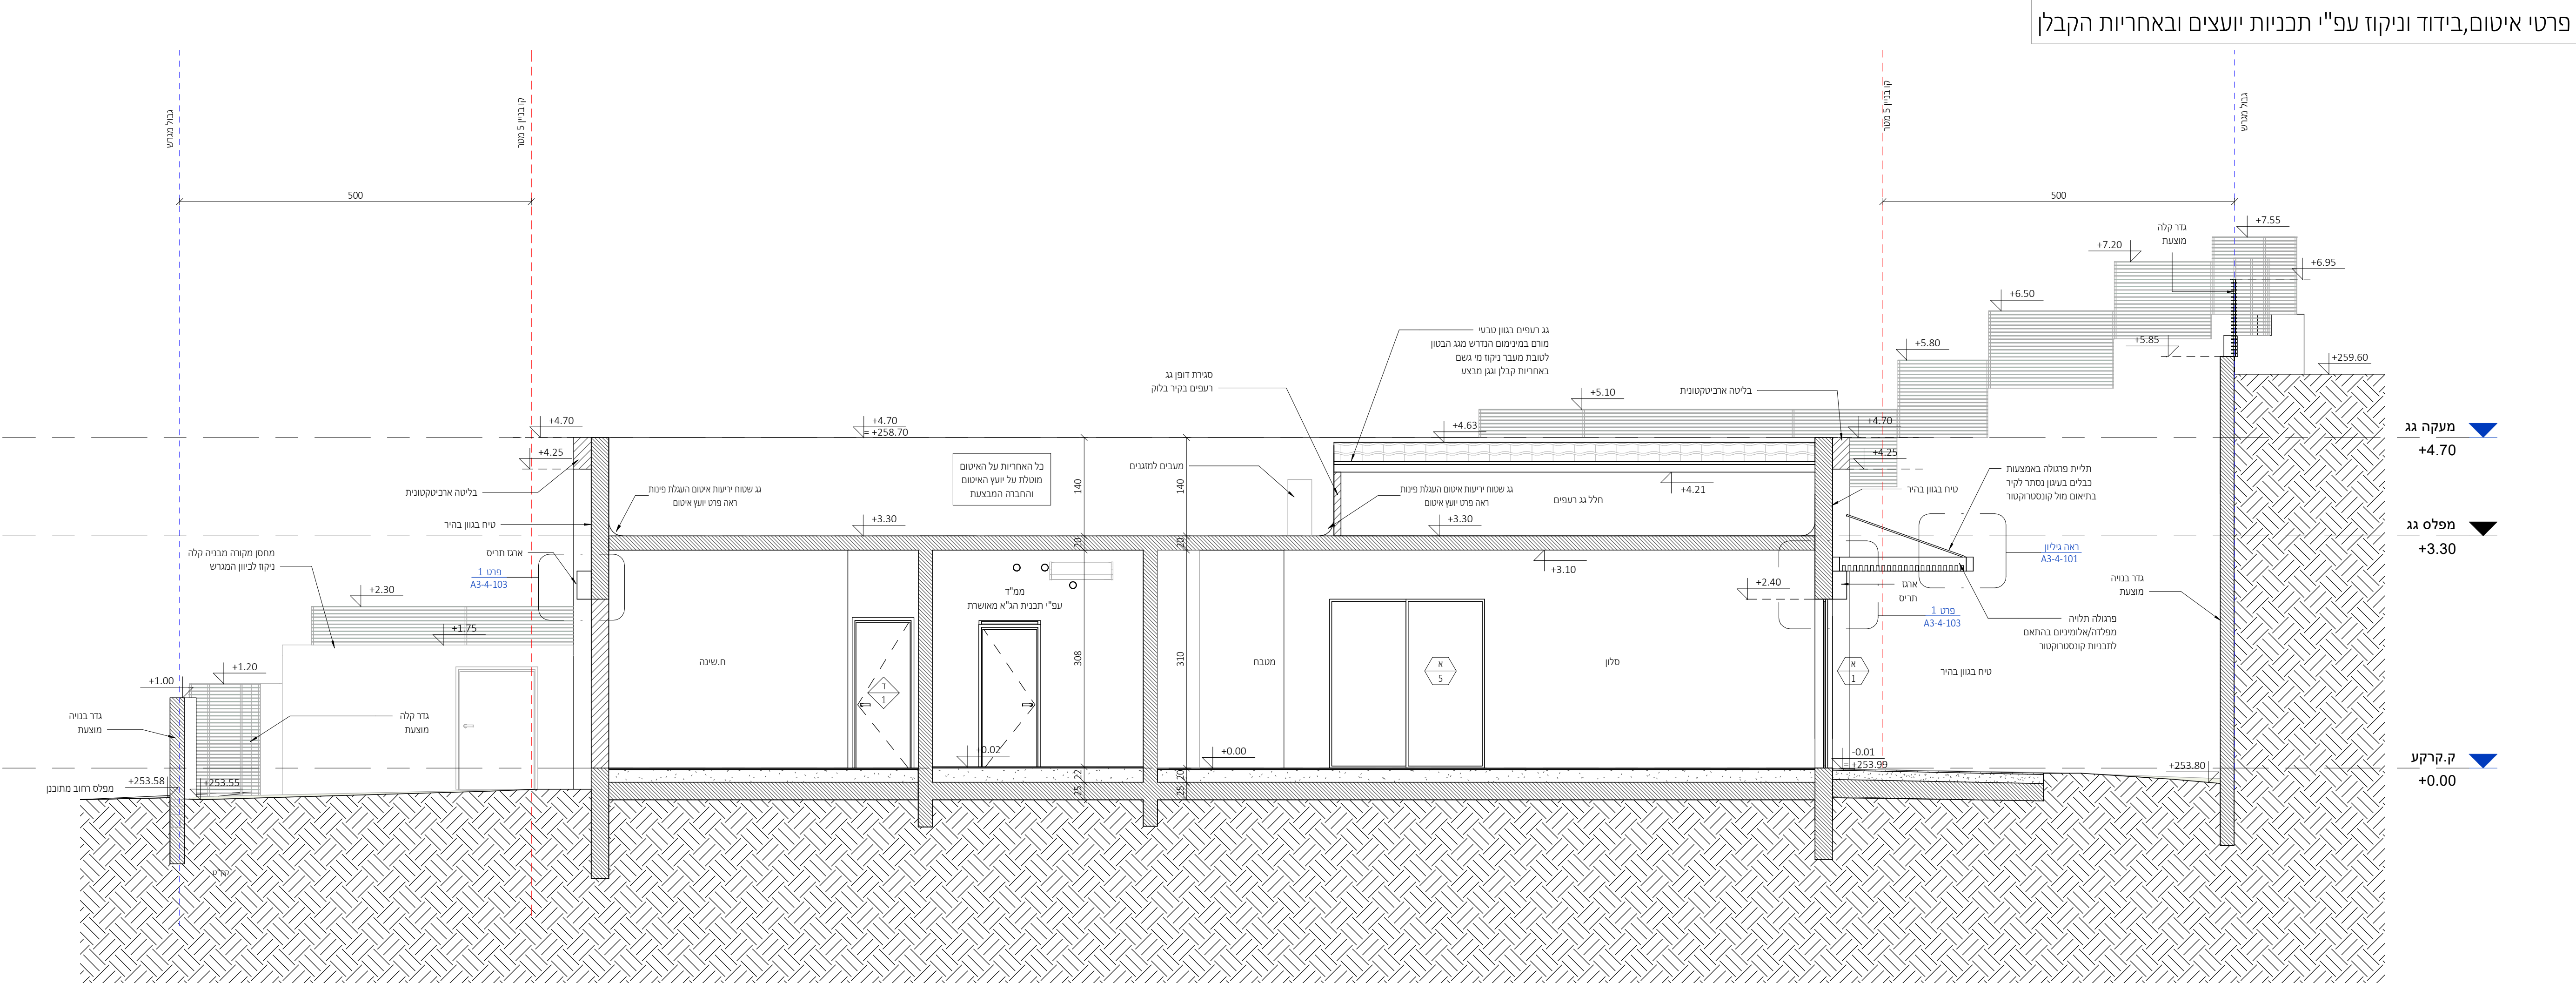

פיתוח נוף עפ"י תוכניות
יועץ נוף ראה פירוט בנפרד

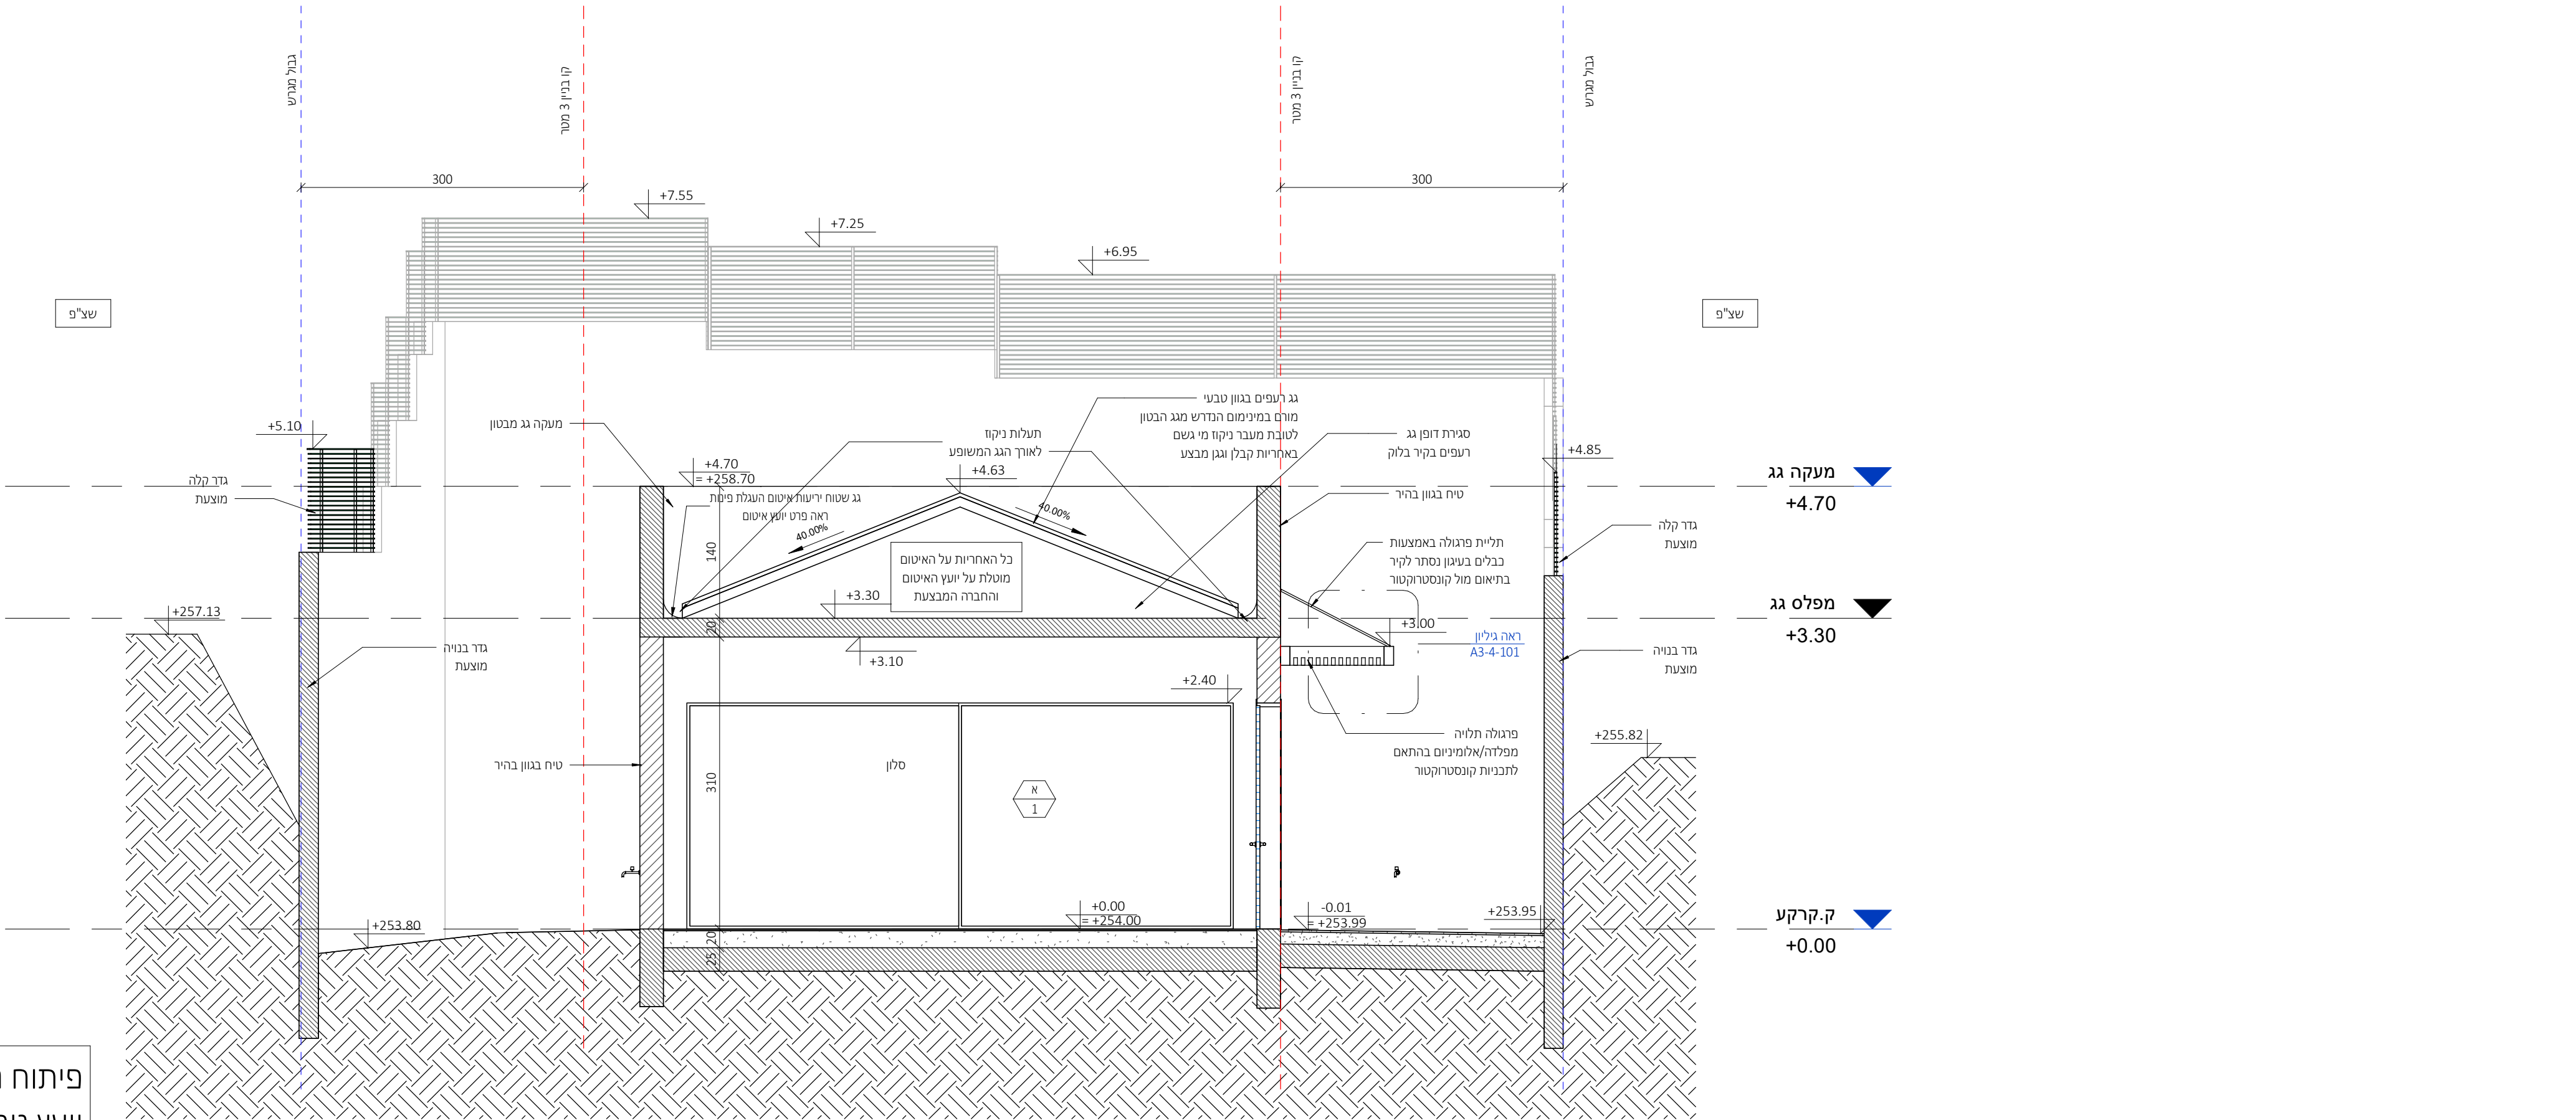

פיתוח נוף עפ"י תוכניות
יועץ נוף ראה פירוט בנפרד


חתך ב-ב

1 : 50

פרגולת אלומיניום




תמונה להמחשה בלבד

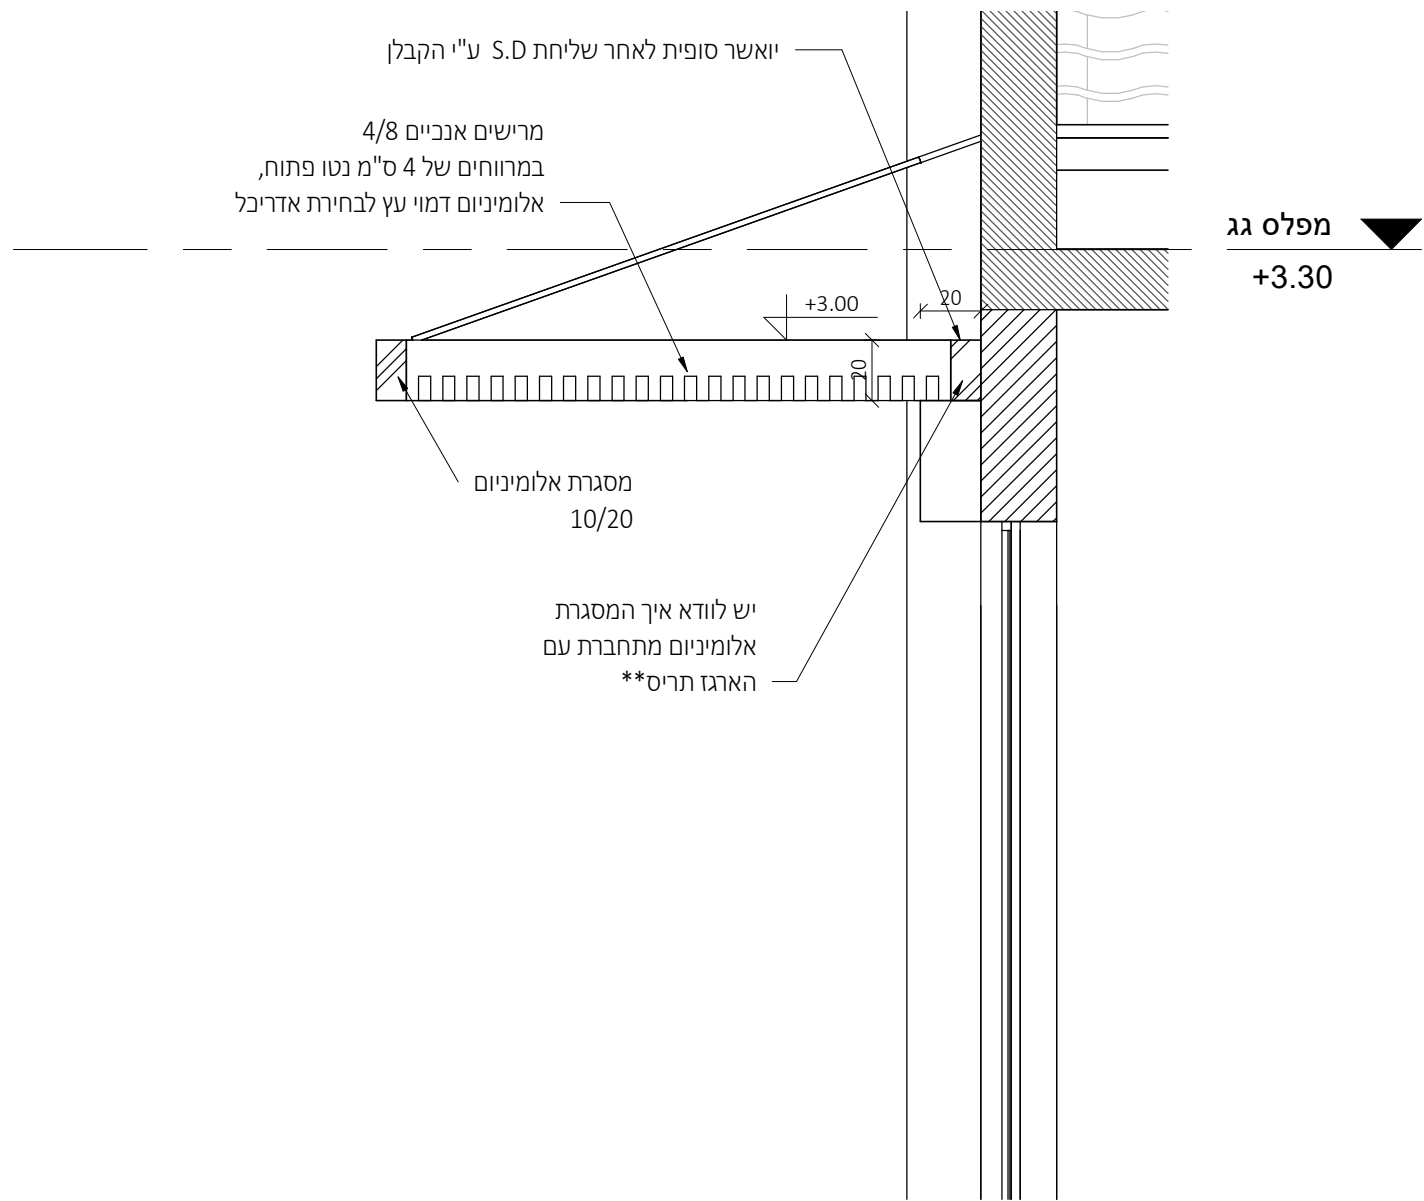

Section 15


1 : 25

להמשך תיאום

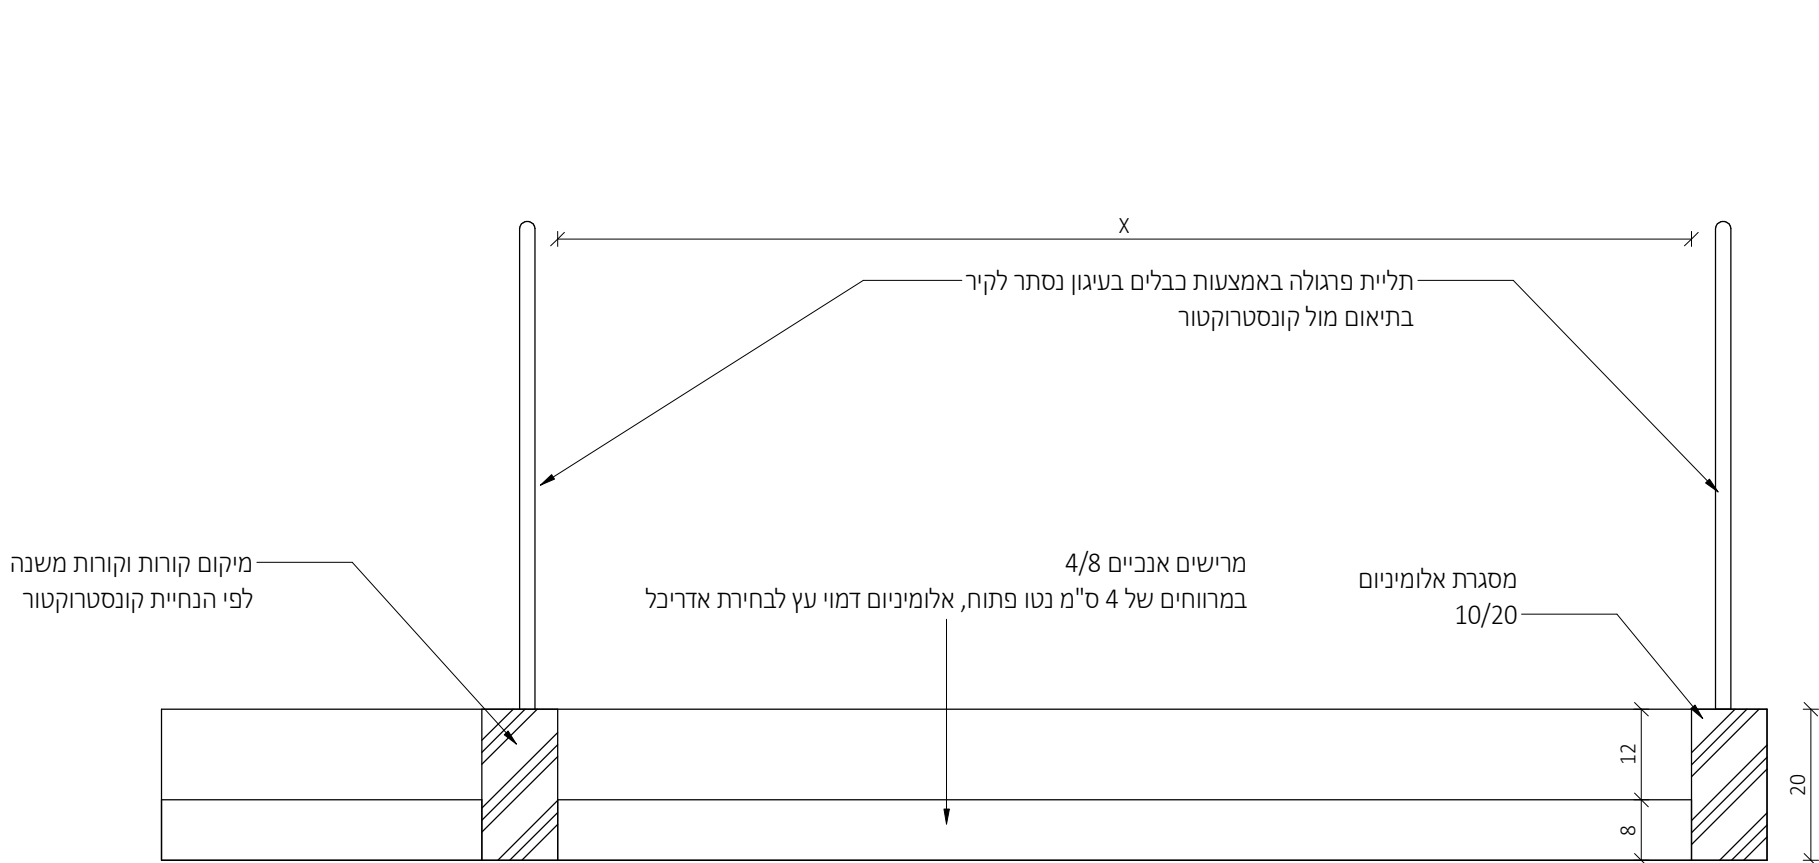

פרגולה - חתך אורך

1 : 10

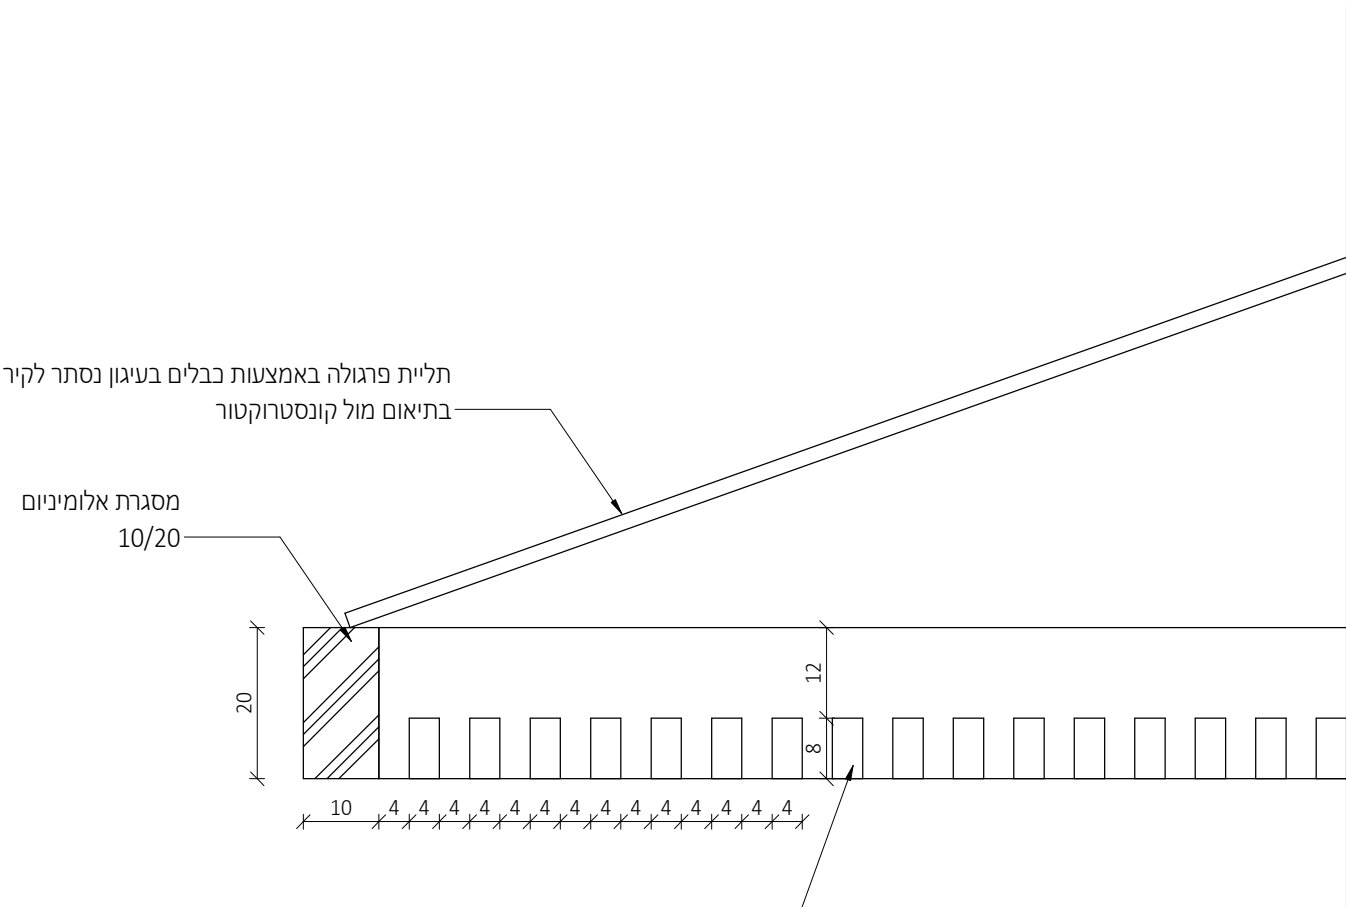

פרגולה - חתך רוחב


1 : 10

מתכננים:

ניהול פרויקט
מהיסוד - בן סלומון
פיקוח
מהיסוד - בן סולומון
קונסטרוקציה
ערן שילר
מיזוג אוויר
אייל ארז מהנדסים ויועצים בע"מ
אינסטלציה
איתן אלמסי
חשמל
איתן בסיס
אלומיניום
נוף
נתי בלוקא
חשמל חכם
חימום תת רצפתי
איטום
צבי טל
אקוסטיקה
מעליות
קרקע וביסוס
דיה הנדסת קרקע וביסוס
רישוי

± 0.00 = +254.00
הערות: 1. תכנית זו אינה לקראת ידע עם תכנית וריסטים. 2. גובה אבטומיסי - ראו תכנית פיתוח. 3. הפירות הן בין קירות הבניה ולא כולל פחים. 4. פיתוח השטח סביב הבנוה, כולל, מדרגות, גדרות, שטחים, ריצופים, שיפועים, גדרים, חניה וגובה ראו תכנית פיתוח. 5. איסוס קירות ורצפות הבנוה כמנוע עם הקרקע ובנידוד תרמי לאורך העמודים והקורות והקורות - כלירות או עם סימני (גובה) - ראו תכנית קונסטרוקציה. 6. אף דים יבוצע בכל מישור אופקי הבולם מהגובה. 7. סוף תרמי בממיד" ע"פ מפרט חומרים, מאושר ע"י פיקוח העורך. המבצע אחראי לסידות : עליו לבקר ולבדוק את כל המידות בתכנית ובקטע המבוצע. במסגרת של מידות או אי התאמה בתכנית /או בבנוי, עליו להודיע על כך מיד לאדריכל בסדר המשך העבודה. המבצע יישמש את ויקי בתכנית שמשך לכיצד. המבצע יחזיק באחר, כלל, את, של מידות של תכנית. אין לקבוע מידות על ידי מדידה בשטח. התכנית הינה רכוש האדריכל ואין לשנות כל שימוש בה או ברעיונות הגלומים בה, אלא באישור בכתב מהאדריכל. מחנדים /או יועץ אשר שמו רשום בתכנית זו, נושא לכיד באחריות המקצועית והמקצועית לתכנית. על המפקח והמבצע לודא התאמת התכנית האדריכלית "לכיצד" לתכנית ויחיד, המכר והתכנית המאושרות ע"י כל גורמים הרשמיים. התכנית כוללת את כל האחריות והידע עד ליום תחילת.

משרד קירות:

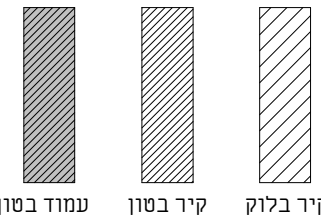

תאריך	תיאור	מהדורה
22/09/2025	מכרז	1

אדריכלות

שם המסין:	CLIENT NAME:
קבוצת רכישה נופיה	
שם הפרויקט:	PROJECT NAME:
נופיה - מגרש 1	
שם הגיליון:	DRAWING NAME:
פרטי פרגולה	
מספר גיליון:	SHEET NUMBER:
A3-4-101	
מחזור:	EDITION:
קנה מידה:	SCALE:
As indicated	
סטוס:	STATUS:
למכרז	
שורסע ע"י:	הילה בהנא
נבדק ע"י:	
תאריך:	DATE:
22.09.2025	

נירסן חיינר אדריכלים
מודד והנדס 2, בית חירות
99-9545642 78
www.nh-arch.com
office@nh-arch.com

22/09/2025 9:59:03


ניהול פרויקט
מהיסוד - בן סלומון
פיקוח
מהיסוד - בן סלומון
קונסטרוקציה
ערן שילר
מיזוג אוויר
אייל ארז מהנדסים ויועצים בע"מ
אינסטלציה
איתן אלמסי
חשמל
איתן בסיס
אלומיניום
בופ
נתי בלוקא
חשמל חכם
חימום תת רצפתי
איטום
צבי טל
אקוסטיקה
מעלות
קרקע וביסוס
דיה הנדסת קרקע וביסוס
רישוי

[illegible]


עמוד בטון קיר בטון יד בלוק

[illegible]


PROJECT NAME:		הפרויקט:	
DRAWING NAME:		שם התוכנית:	
A3-4-103			
SCALE:		מקנה מידה:	
As indicated		EDITION:	
TATUS:		סטוס:	
למכור		1	
DATE:		תאריך:	
22.09.2025		החלה מכירה	
NeumanHaynerArchitects			
יוסוף חיינר אדריכלים www.nh-arch.com 09-9545842			

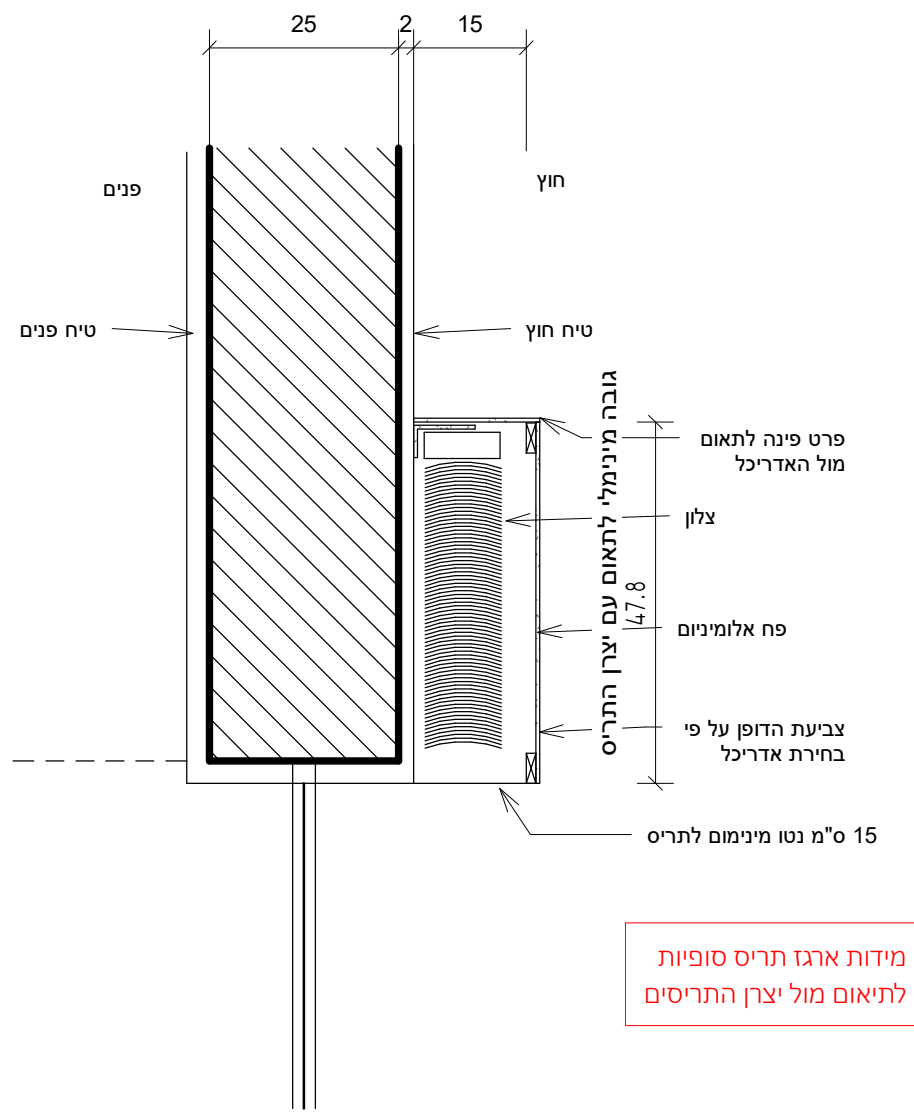


1 : 10

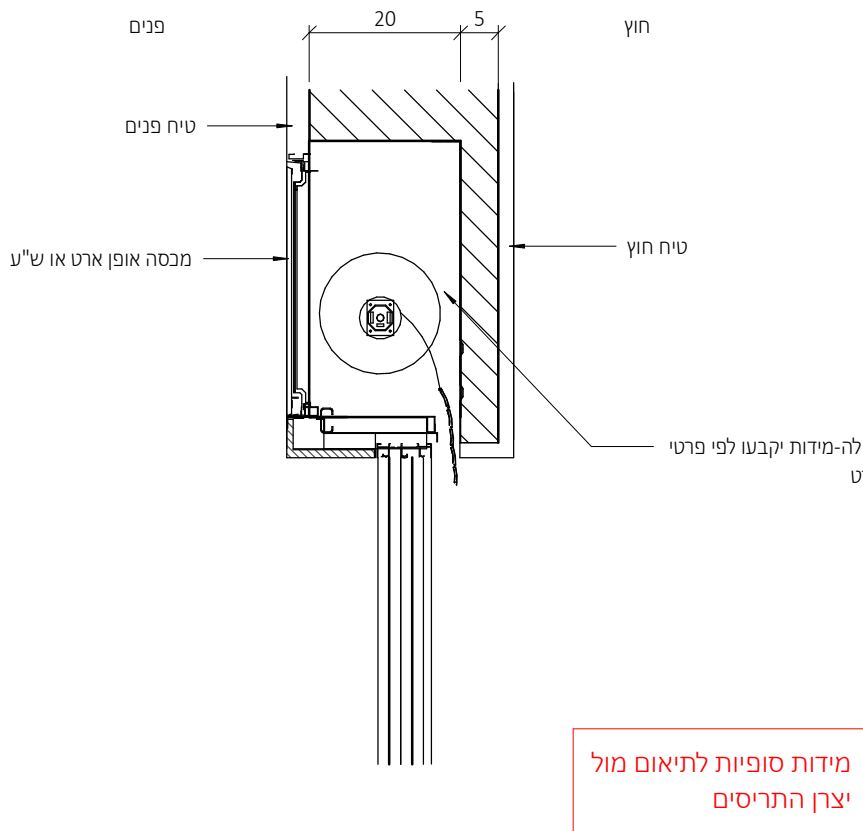


1 : 10

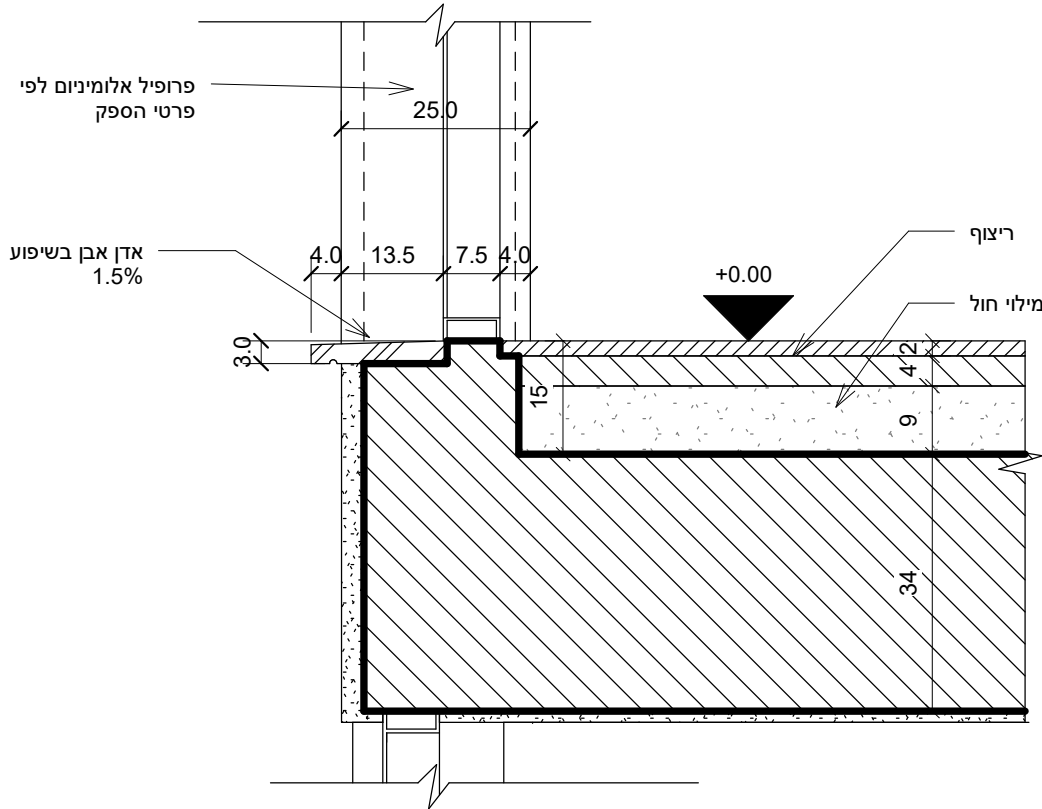

1 : 10

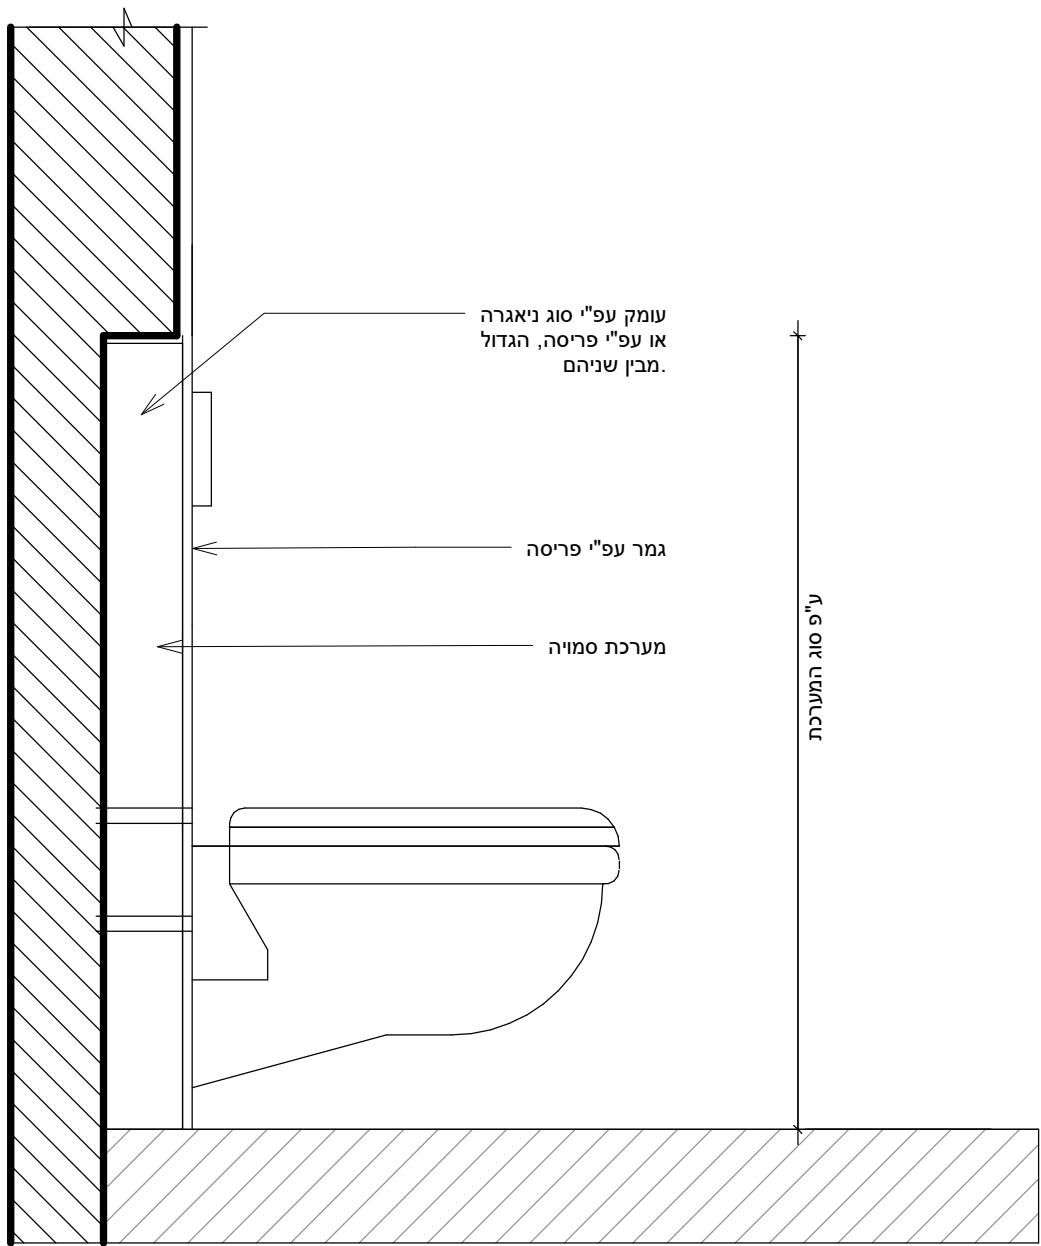

1 : 10

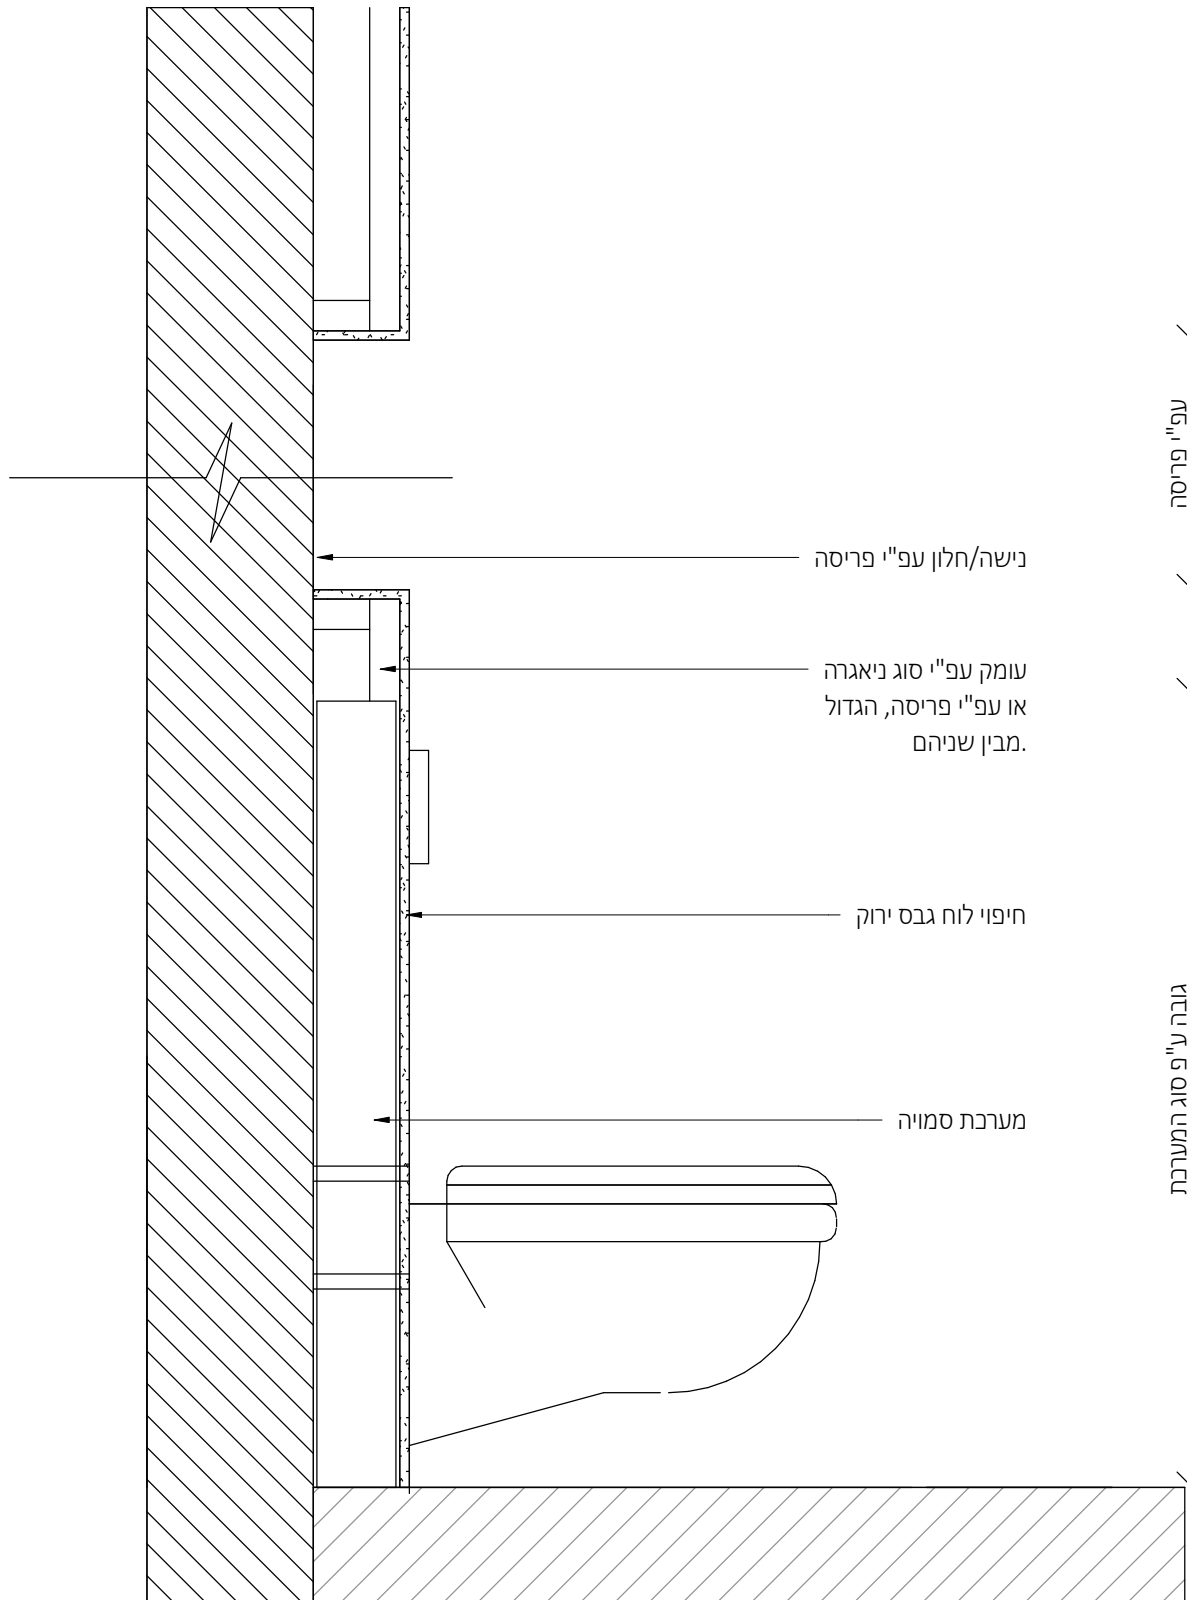

1 : 10

פרטי האיטום באחריות יועץ האיטום
ראה חוברת פרטי איטום מצורפת

להמשך תיאום

רשימת חלונות					
סוג	הערות	כמות	גובה	רוחב	מס פריט

קרקע

1	580	240	1	צלון רפפה חיצוני חשמלי + ארגז חיצוני	ויטרינה פרופיל 7500 קליל
2	220	110	2	צלון רפפה חיצוני חשמלי + ארגז חיצוני	חלון הזזה פרופיל 7000 קליל
3	90	240	1	צלון רפפה חיצוני חשמלי + ארגז חיצוני	דלת כנף פרופיל 4350 קליל
4	110	110	1	צלון רפפה חיצוני חשמלי + ארגז חיצוני	חלון הזזה פרופיל 7000 קליל
5	220	240	2	צלון רפפה חיצוני חשמלי + ארגז חיצוני	ויטרינה פרופיל 7500 קליל
6	90	110	1	צלון רפפה חיצוני חשמלי + ארגז חיצוני	חלון קיפ פרופיל 4500 קליל
7	60	110	1	צלון רפפה חיצוני חשמלי + ארגז חיצוני	חלון קיפ פרופיל 4500 קליל

סוג זכוכית – בהתאם למפורט בדו"ח התרמי (תנאי המינימום בעמוד 9 מתוך המפרט התרמי). כמו כן, הזכוכית תקבע בתיאום עם הקבלן לאחר אישור יועץ התרמי וחברת הניהול

כל פריט יחולק למינימום הכנפיים האפשרי (לתיאום מול ספק האלומיניום ובמסגרת שרטוטי shop drawing)

רשימת דלתות					
סוג	הערות	גובה	רוחב	כמות	מספר פריט

0	1	110	240	דלת כניסה	דלת חוץ דגם גארדה
1	4	80	210	דלת פנים	דלת פנים "אקוודור" תוצרת חמדיה
2	1	80	200	דלת נגרות ממ"ד	דלת פנים "אקוודור" תוצרת חמדיה

נוימן חיינר אדריכלים בע"מ

כל הזכויות שמורות
ט.ל.ח.

NeumanHaynerArchitects



רשימת פתחים

שם התכנית:

A3-6-1000

גליון מספר:

מהדורה:

22/09/2025



נופיה - מגרש 1

שם הפרויקט:

למכרז

סטטוס:

קבוצת רכישה נופיה

שם המממן:

קנה מידה:

22/09/2025 9:59:06

D:\NH-Arch-Dropbox\NH-Arch-Projects\NH-בתים ודירות\00\1\תכנית\001\

FILE NAME: כלל הפרויקטים להיתר\001\תכנית\001\