פרט יציאת צנרת חשמל בגג לבוילר וכדו'

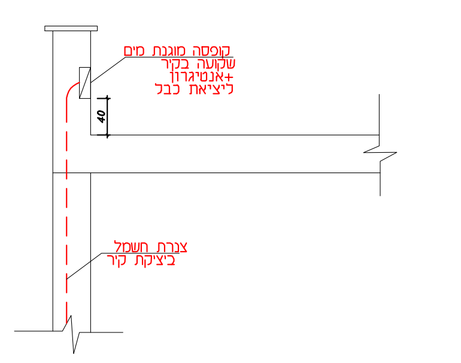

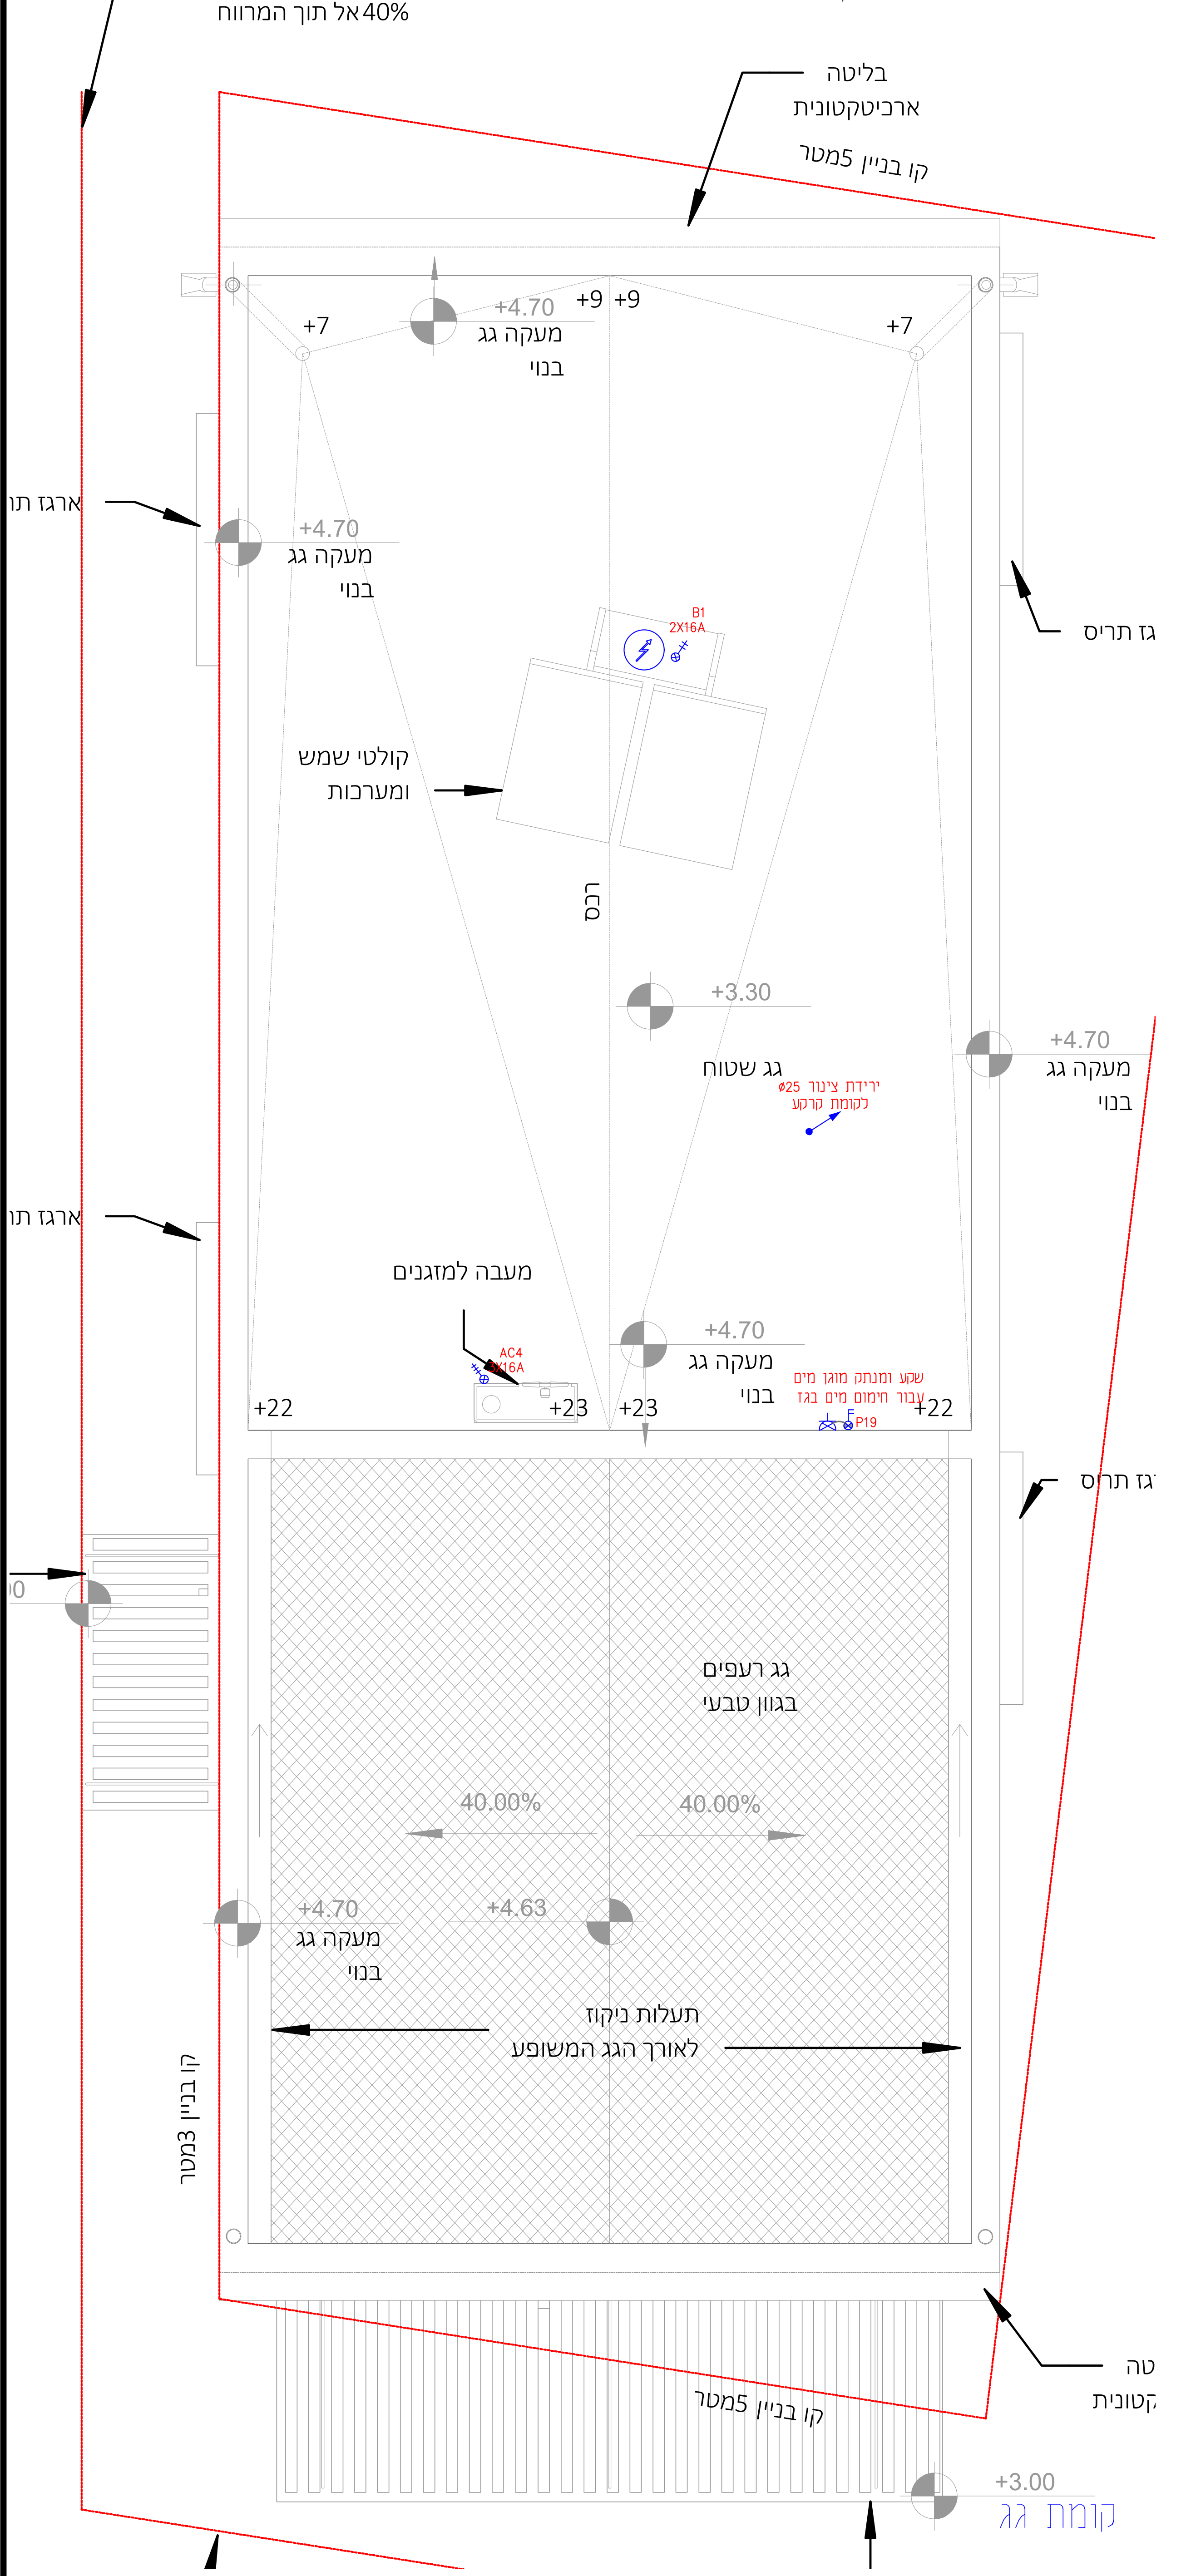

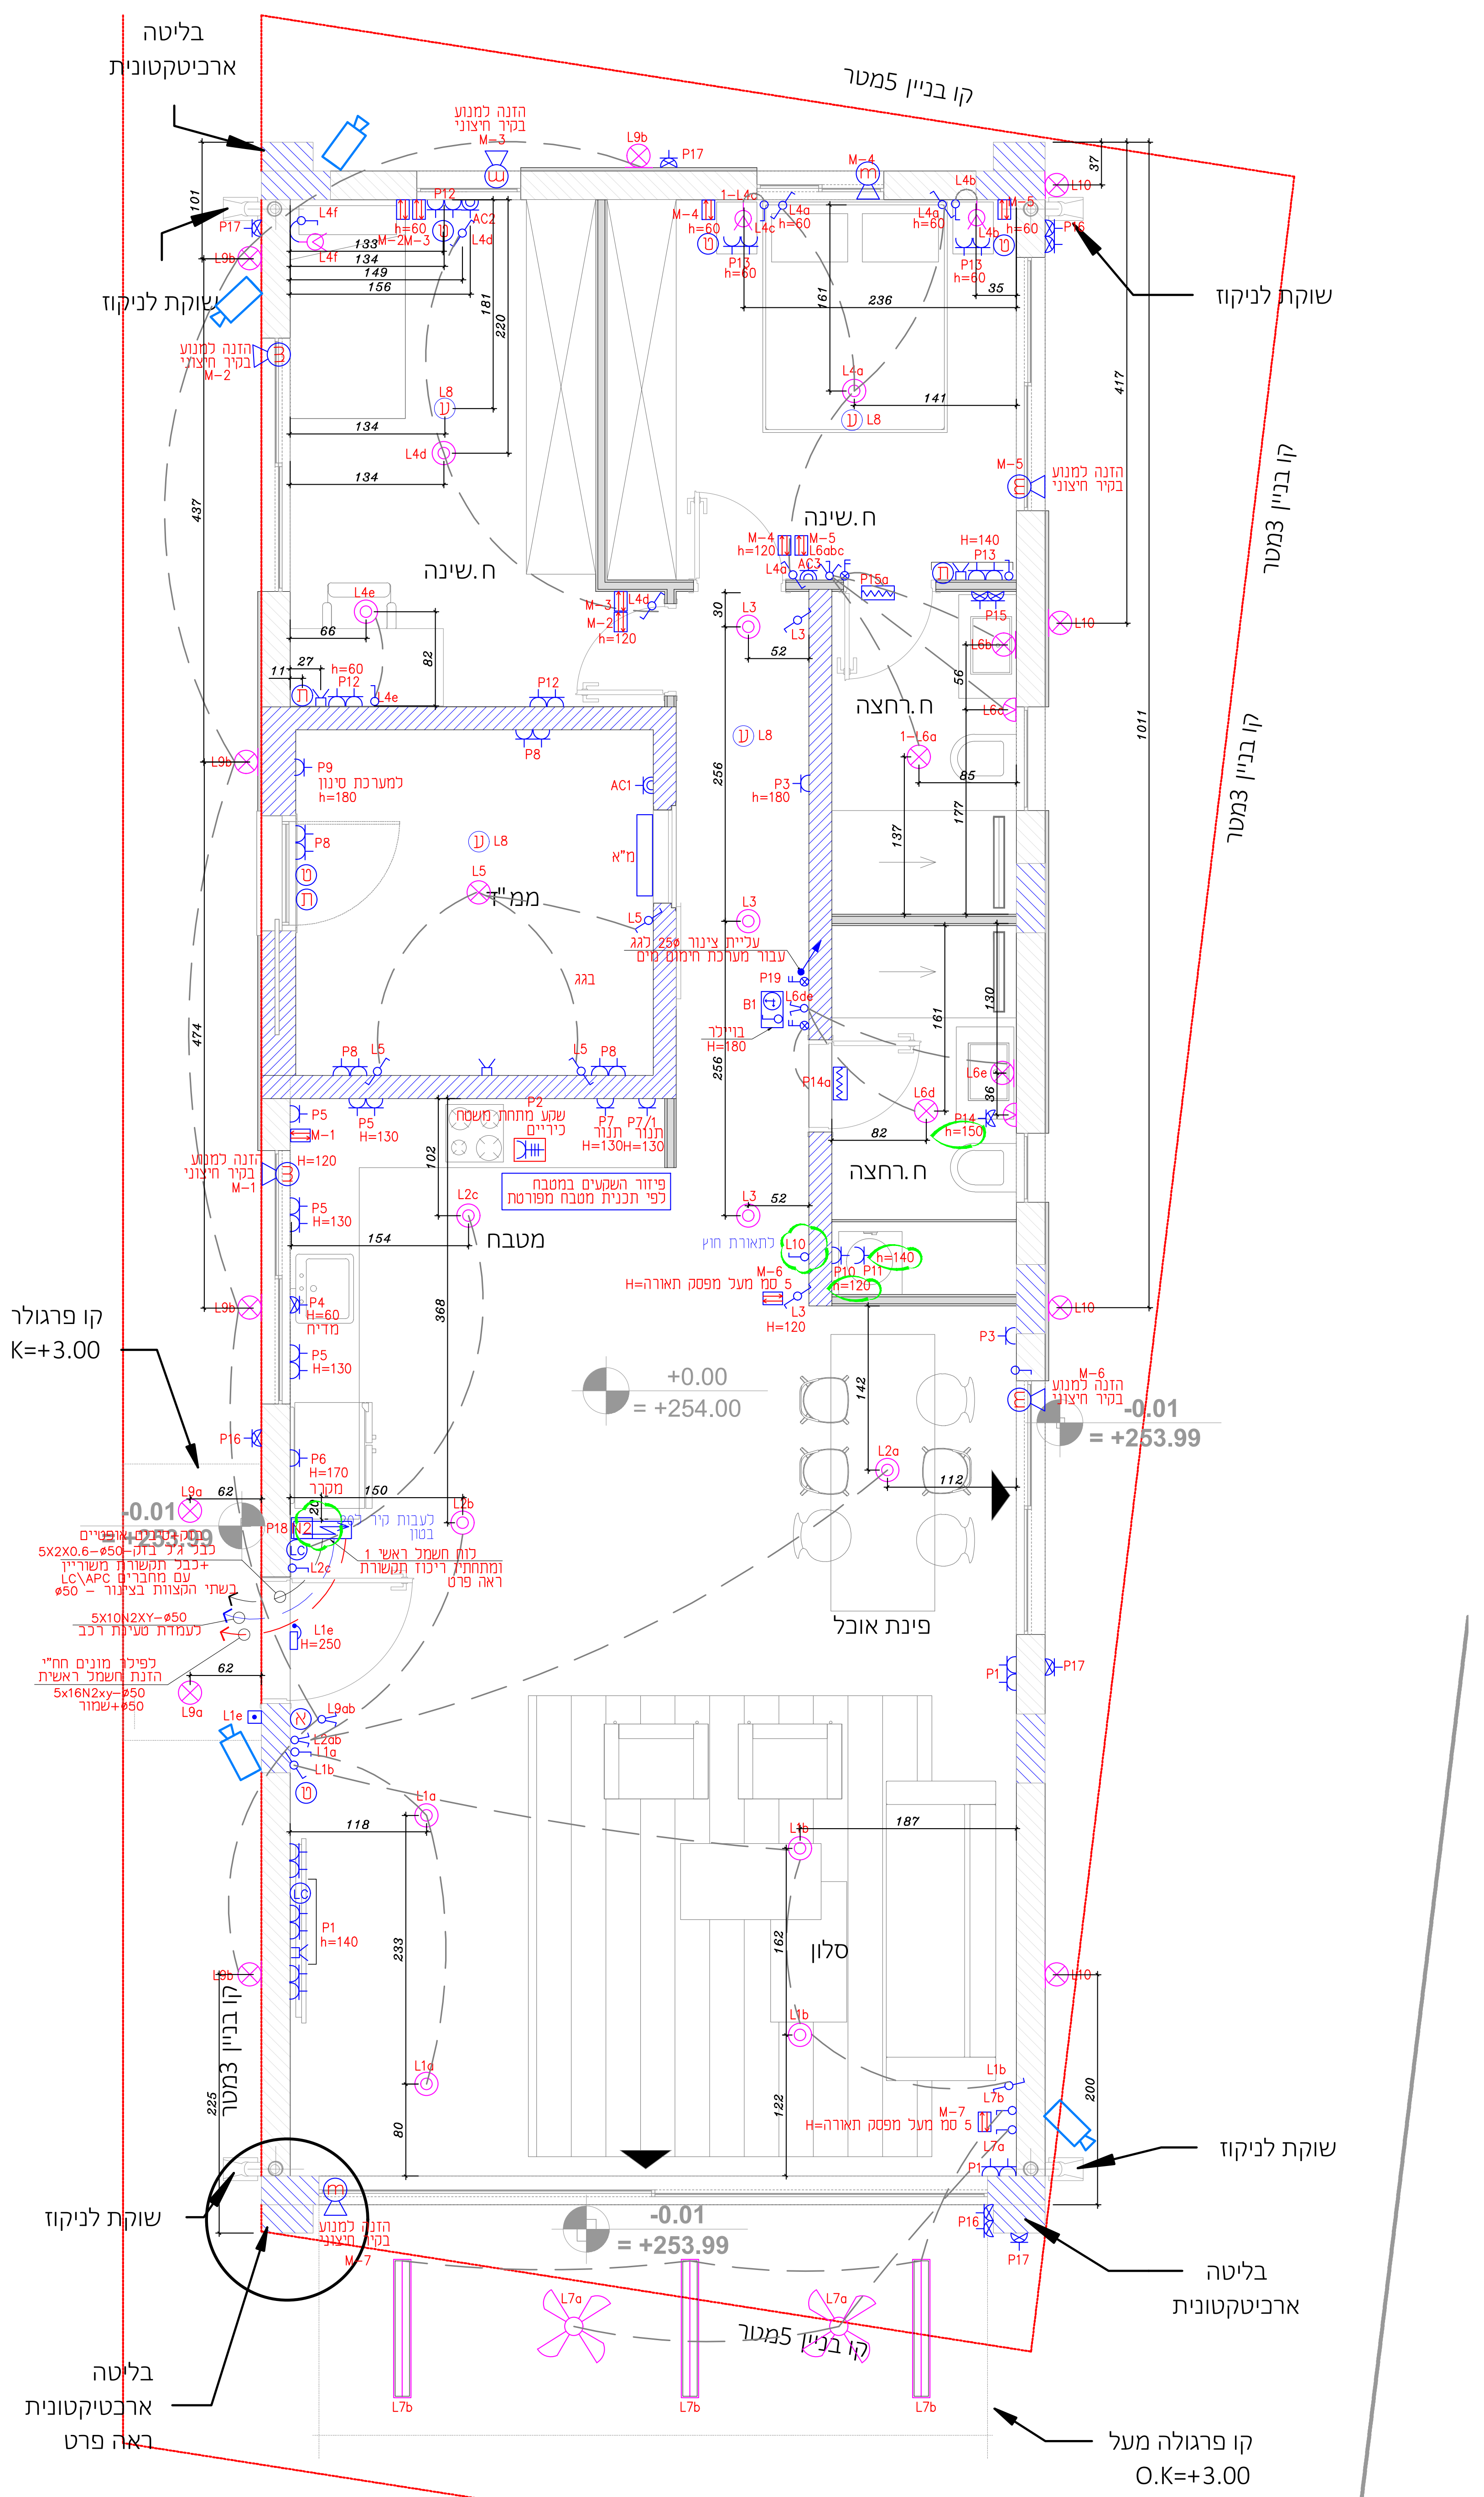

לוח	לוח חשמל
	שקע 16A בודד / זוג שקעי 16A — H=60 אלא אם צוין אחרת
	זוג שקעים בדופן אי
	מקבץ שקעים טיפוסי סיום באביזר N2\N6 "ניסקו" בארון תקשורת מתחת לוח חשמל
	שקע חד פאזי מוגן מים H=60 אלא אם צוין אחרת
	שקע ליחידת מ"א 16A H=220 מיקום סופי לפי תכנית מיזוג ובתיאום מול אדריכל?
	שקע תלת פאזי לכיריים חשמליות 3X16A
	נקודת טלפון מלאה-צנרת, כבילה ושקע טלפון H=60
	CIMA BOX הכולל: 4 שקעי שרות+2 תקשורת
	נקודת תקשורת H=60, צינור Ø25 עם חוט משיכה מריכוז תקשורת דירתי
	נקודת טלויזיה מושלמת+צינור שמור Ø20 H=60
	נקודת תקשורת מלאה הכוללת: כבל תקשורת אופטי תקני מותקן בצינור Ø25 סיום בית תקע אופטי LC\APD לפי דרישות ת"י 1-11801 עם ראשים מוכנים מראש להתקנה בארון תקשורת דירתי ובסלון עם חוט משיכה מריכוז תקשורת דירתי
	מנוע חשמלי H=200
	הכנה לתרמוסטט מזגן- צינור 20 לחלל תקרה
	תרמוסטט חימום תת רצפתי- יבוצע לפי הנחיות ספק
	שקע לתנור חימום חשמלי 10 סמ מעל פתח דלת
	בויילר
	הכנה לוונטה סיום בשקע
	NET
מפסקים	מפסק מאור בודד H=90 / מפסק כפול H=90 / מפסק מאור מחליף\מצליב H=90 — אלא אם צוין אחרת במפסקי הדלקה ליד מיטה H=60
	לחצן פעמון דלת H=90
	מנתק מואר 2X16A / 3X16A
	מפסק דו קוטבי מואר לתנור חימום חשמלי H=160
	מפסק מנתק עבור חימום מים בגז בגג
	מפסק הרמה/הורדה לתריס חשמלי 5 סמ מעל מפסק תאורה ע"פ פרט
	מפסק עם שעון בקיר לבויילר H=180
	פנל צפיה (מוניטור) +לחצן פתיחה דלת H=120
	תאורת חרום חד תכליתית LED 3w
	גלאי עשן בתקרה
	נקודת מאור בתקרה
	ג"ת פנים תקרתי מוגן מים
	ג"ת LED עגול שקוע בתקרה
	ג"ת LED עגול קירי גובה H=220
	ג"ת פנים קירי למנורת לילה H=120
	ג"ת פנים/חוץ קירי מוגן מים H=240 , במרתף H=220
	ג"ת קירי נמוך לתאורת התמצאות מדרגות/שירותים, h=15 מהרצפה /מרום מדרגה
	ג"ת מלבני IP65 להתקנה על פרגולה
	מאוורר להתקנה בחוץ
	פעמון דלת 220V (גונג) התקנה מעל דלת כניסה
	הכנה מצלמה אבטחה, צינור 25 וחוט משיכה מארון תקשורת דירתי

חזית לוח חשמל ראשי וארונות תקשורת

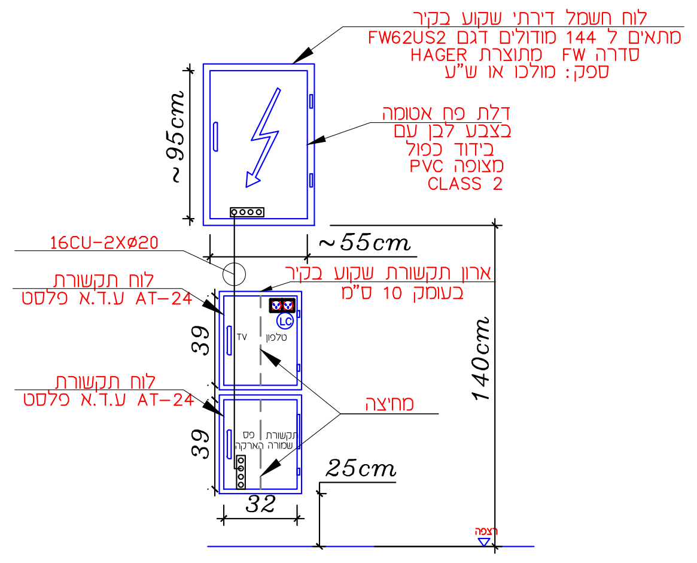

פרט לגבהים של הדלקות,
תאורה ותריסים:

תפוצה														תאריך
מנהל הפרויקט	אדריכל	מזמין/יזם	חשמל	קבלן	בטיחות	אקוסטיקה	אינסטלציה	קונסטרוקציה	אדריכל נוף	מטבחים	חברת חשמל	חברת בזק		

מס'	שינויים	תאריך
1	עדכון רקע אדריכלות	13.10.24
2	עדכון רקע תכנית	26.11.24
3	עדכון רקע תכנית	8.12.24
4	עדכון תוכנית	12.12.24
5	עדכון תוכנית	24.12.24
6	עדכון תוכנית	8.1.25
7	עדכון תוכנית	13.1.25
8	עדכון תוכנית	8.5.25
9	עדכון מעגלים בהתאם ללוח	17.6.25
10	עדכון מעגלים ומפסקים	23.6.25
11	עדכון תוכנית	17.9.25

עודכן ע"י: ליאל

הערות:

- * כל הגבהים בתכנית הינם למרכז אביזר אלא אם ציין במפורש אחרת
- * מיקום סופי לנקודות תאורה ייקבע ע"פ תכנית עיצוב פנים תאורת חוץ- ע"פ יועץ פיתוח
- * מיקום סופי לשקעי מיזוג עפ"י תוכנית יועץ מיזוג

הערות:

- מיקום סופי לנקודות תאורה ייקבע ע"פ תכנית עיצוב פנים תאורת חוץ- ע"פ יועץ פיתוח
- במידה והוחלט על הכנות לבית חכם:
כהכנה לבית חכם ולדלת חכמה יש להשחיל חוט 0 כחול נוסף בכל מפסק הדלקה
התכנון עצמו יעשה ע"י ספק בית חכם
- הכנות למיזוג אויר,חימום תת רצפתי, מערכות אבטחה, וחימום מים בחשמל יהיו עפ הנחיות יועץ לכל תחום
- יש לקרוא תכנית זו יחד עם תכנית אדריכלות למקרא בלוקים אדריכלות

מעגלים שמורים ליחידות
מ"א:
1-AC1 1-AC3
1-AC2 1-AC4

א. בסיס
הנדסת חשמל בע"מ
משרד: יד חרוצים 16, ירושלים 93420
טל: 074-7021015 נייד: 050-6550484
פקס: 077-5131015 דוא"ל: office@ebasis.co.il

שם הפרויקט:
נופיה-אלפי מנשה
מגרש 1

שם הגיליון:
תוכנית חשמל

קנה מידה: 1:50

○ לעיון ○ לאישור ● למכרז ○ לביצוע

מס' קובץ: File: 675-1.dwg
תאריך: Date: 15.08.2024

תכנן: איתן
שרטט: רחל
אישר: איתן

מס' עדכון: 11
מס' הגליון: E
מס' הפרויקט: 675