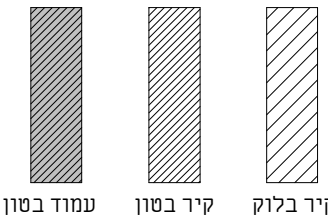


מתכונים:

ניהול פרויקט
מהיסוד - בן סולומון
פיקוח
מהיסוד - בן סולומון
קונסטרוקציה
ערן שילר
מיזוג אוויר
אייל ארז מהנדסים ויועצים בע"מ
אינסטלציה
איתן אלמסי
חשמל
איתן בסיס
אלומיניום
נוף
נתי בלוקא
חשמל חכם
חימום תת רצפתי
איטום
צבי טל
אקוסטיקה
מעליות
קרקע וביסוס
דיה הנדסת קרקע וביסוס
רישוי

[illegible]

מקרא קירות:

[illegible]

אדריכלות

קבוצת רכישה נופיה		שם הפרויקט:	
נופיה - מגרש 10		שם המדינה:	
גליון שער		שם העיר:	
A3-1-100		שם המדינה:	
קוד מידה:		EDITION:	
סטוס:		1	
למכור		סטוס ע"י:	
בדוק ע"י:		תאריך:	
22.09.2025		שם המדינה:	



NeumanHaynerArchitects

נוימן חיינר אדריכלים
מורד ההדרים 2, בית חירות
טל 09-9545842


מועד ההדפסה: 2, בית חירות
טל 09-9545842

מועד ההדפסה: 2, בית חירות
טל 09-9545842

זכויות ייצור / ע"פ הנחיות עו"ד

נופיה - מגרש 10			
מס' גיליון	שם גיליון	מהדורה	תאריך הפצת מהדורה

22.09.2025	1	גליון שער	A3-1-100
22.09.2025	1	תכנית קומת קרקע	A3-1-101
22.09.2025	1	תכנית קומה א	A3-1-102
22.09.2025	1	תכנית מפלס גג	A3-1-103
22.09.2025	1	תכנית תקרה ותאורה - קרקע	A3-1-104
22.09.2025	1	תכנית תקרה ותאורה קומה א	A3-1-105
22.09.2025	1	חזיתות 1	A3-2-200
22.09.2025	1	חזיתות 2	A3-2-201
22.09.2025	1	חתכים	A3-3-100
22.09.2025	1	גליון מדרגות	A3-4-100
22.09.2025	1	פרטים	A3-4-103
22.09.2025	1	פרטי פרגולה	A3-4-104
22.09.2025	1	רשימת פתחים	A3-6-1000

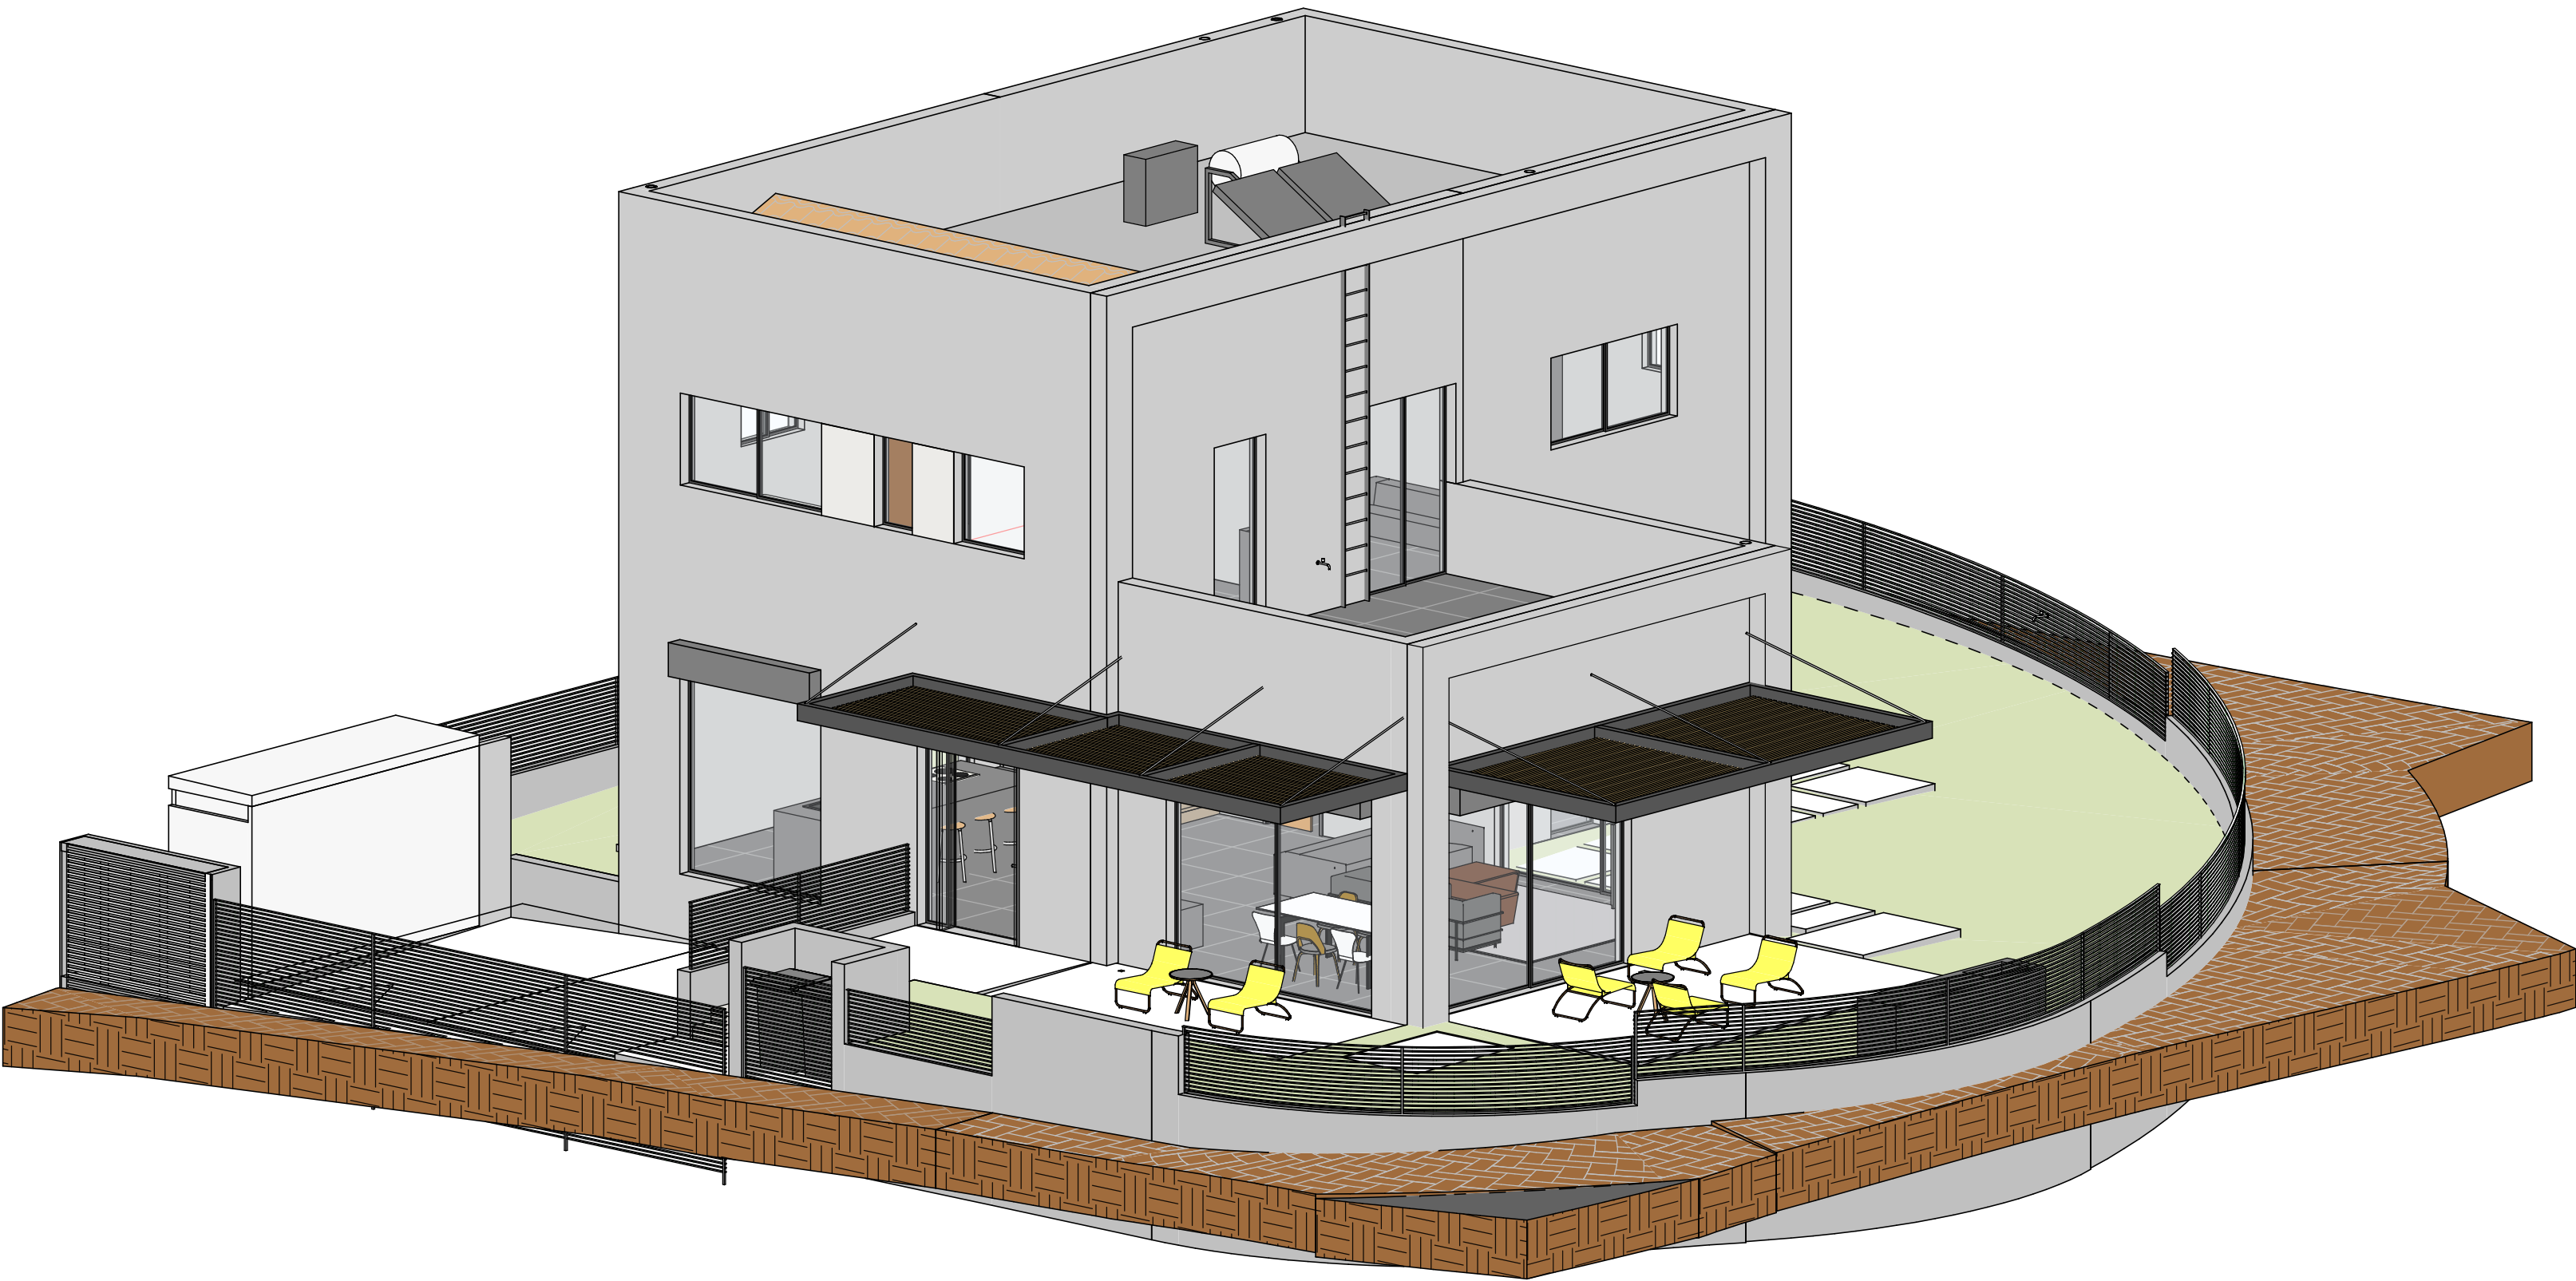

מתכונים:

ניהול פרויקט
מהיסוד - בן סולומון
פיקוח
מהיסוד - בן סולומון
קונסטרוקציה
ערן שילר
מיוזג אוויר
אייל ארז מהנדסים ויועצים בע"מ
אינסטלציה
איתן אלמסי
חשמל
איתן בסיס
אלומיניום
נוף
נתי בלוקא
חשמל חכם
חימום תת רצפתי
איטום
צבי טל
אקוסטיקה
מעליות
קרקע וביסוס
דיה הנדסת קרקע וביסוס
ירשני

+ 0.00 = 251.80

רות:

- הכניו וְ שֵׁי לְקוּרֹא יחד עם תכנית העיונים.
גובה אבטלוס – ראו תכנית פיתוח.
הימדות הובו בִּין הַקִּוּי הַבְּנִי (א כלל ש"ח).
הימדות השמש מביד המבנה, כולל, מדורות, שבי"ל, רציפים,
שפיעים גבוהים, חלונות הובו ראו תכנית פיתוח.
איסוף תרומות ורצפת המבנה בעם הערקע וכידור תמי לאור הממדים
הקורות ועל התקרות – נלדיה או עם מילי (ג'נון) ראו תכנית קונסטרקציה
אִתְּ חֵם יבוצע בעל משרד אפיקי הובל חובני.
אִתְּ חֵם תרומת גמטי – כ"פ חסידות גמטי, מאושר ע"י פיקד העורף.

[illegible]

קרא קירות:

עמוד בסון קיר בסון קיר בלוק

[illegible]

אדריכלות

CLIENT NAME: _____; המזמין:

קבוצת רכישה נופיה

PROJECT NAME: הפרויקט:

נופיה - מגרש 10

DRAFTING NAME: _____

תכנית קומת קרקע

מס' וליווי:

A3-1-101

SCALE:	קנה מידה:	EDITION:	דורה:
--------	-----------	----------	-------

1:50


STATUS: 0000 / 1 \

[illegible]

NeumanHaynerArchitects

ימן חיינר אדריכלים

www.nh-arch.com 09-9545842 7

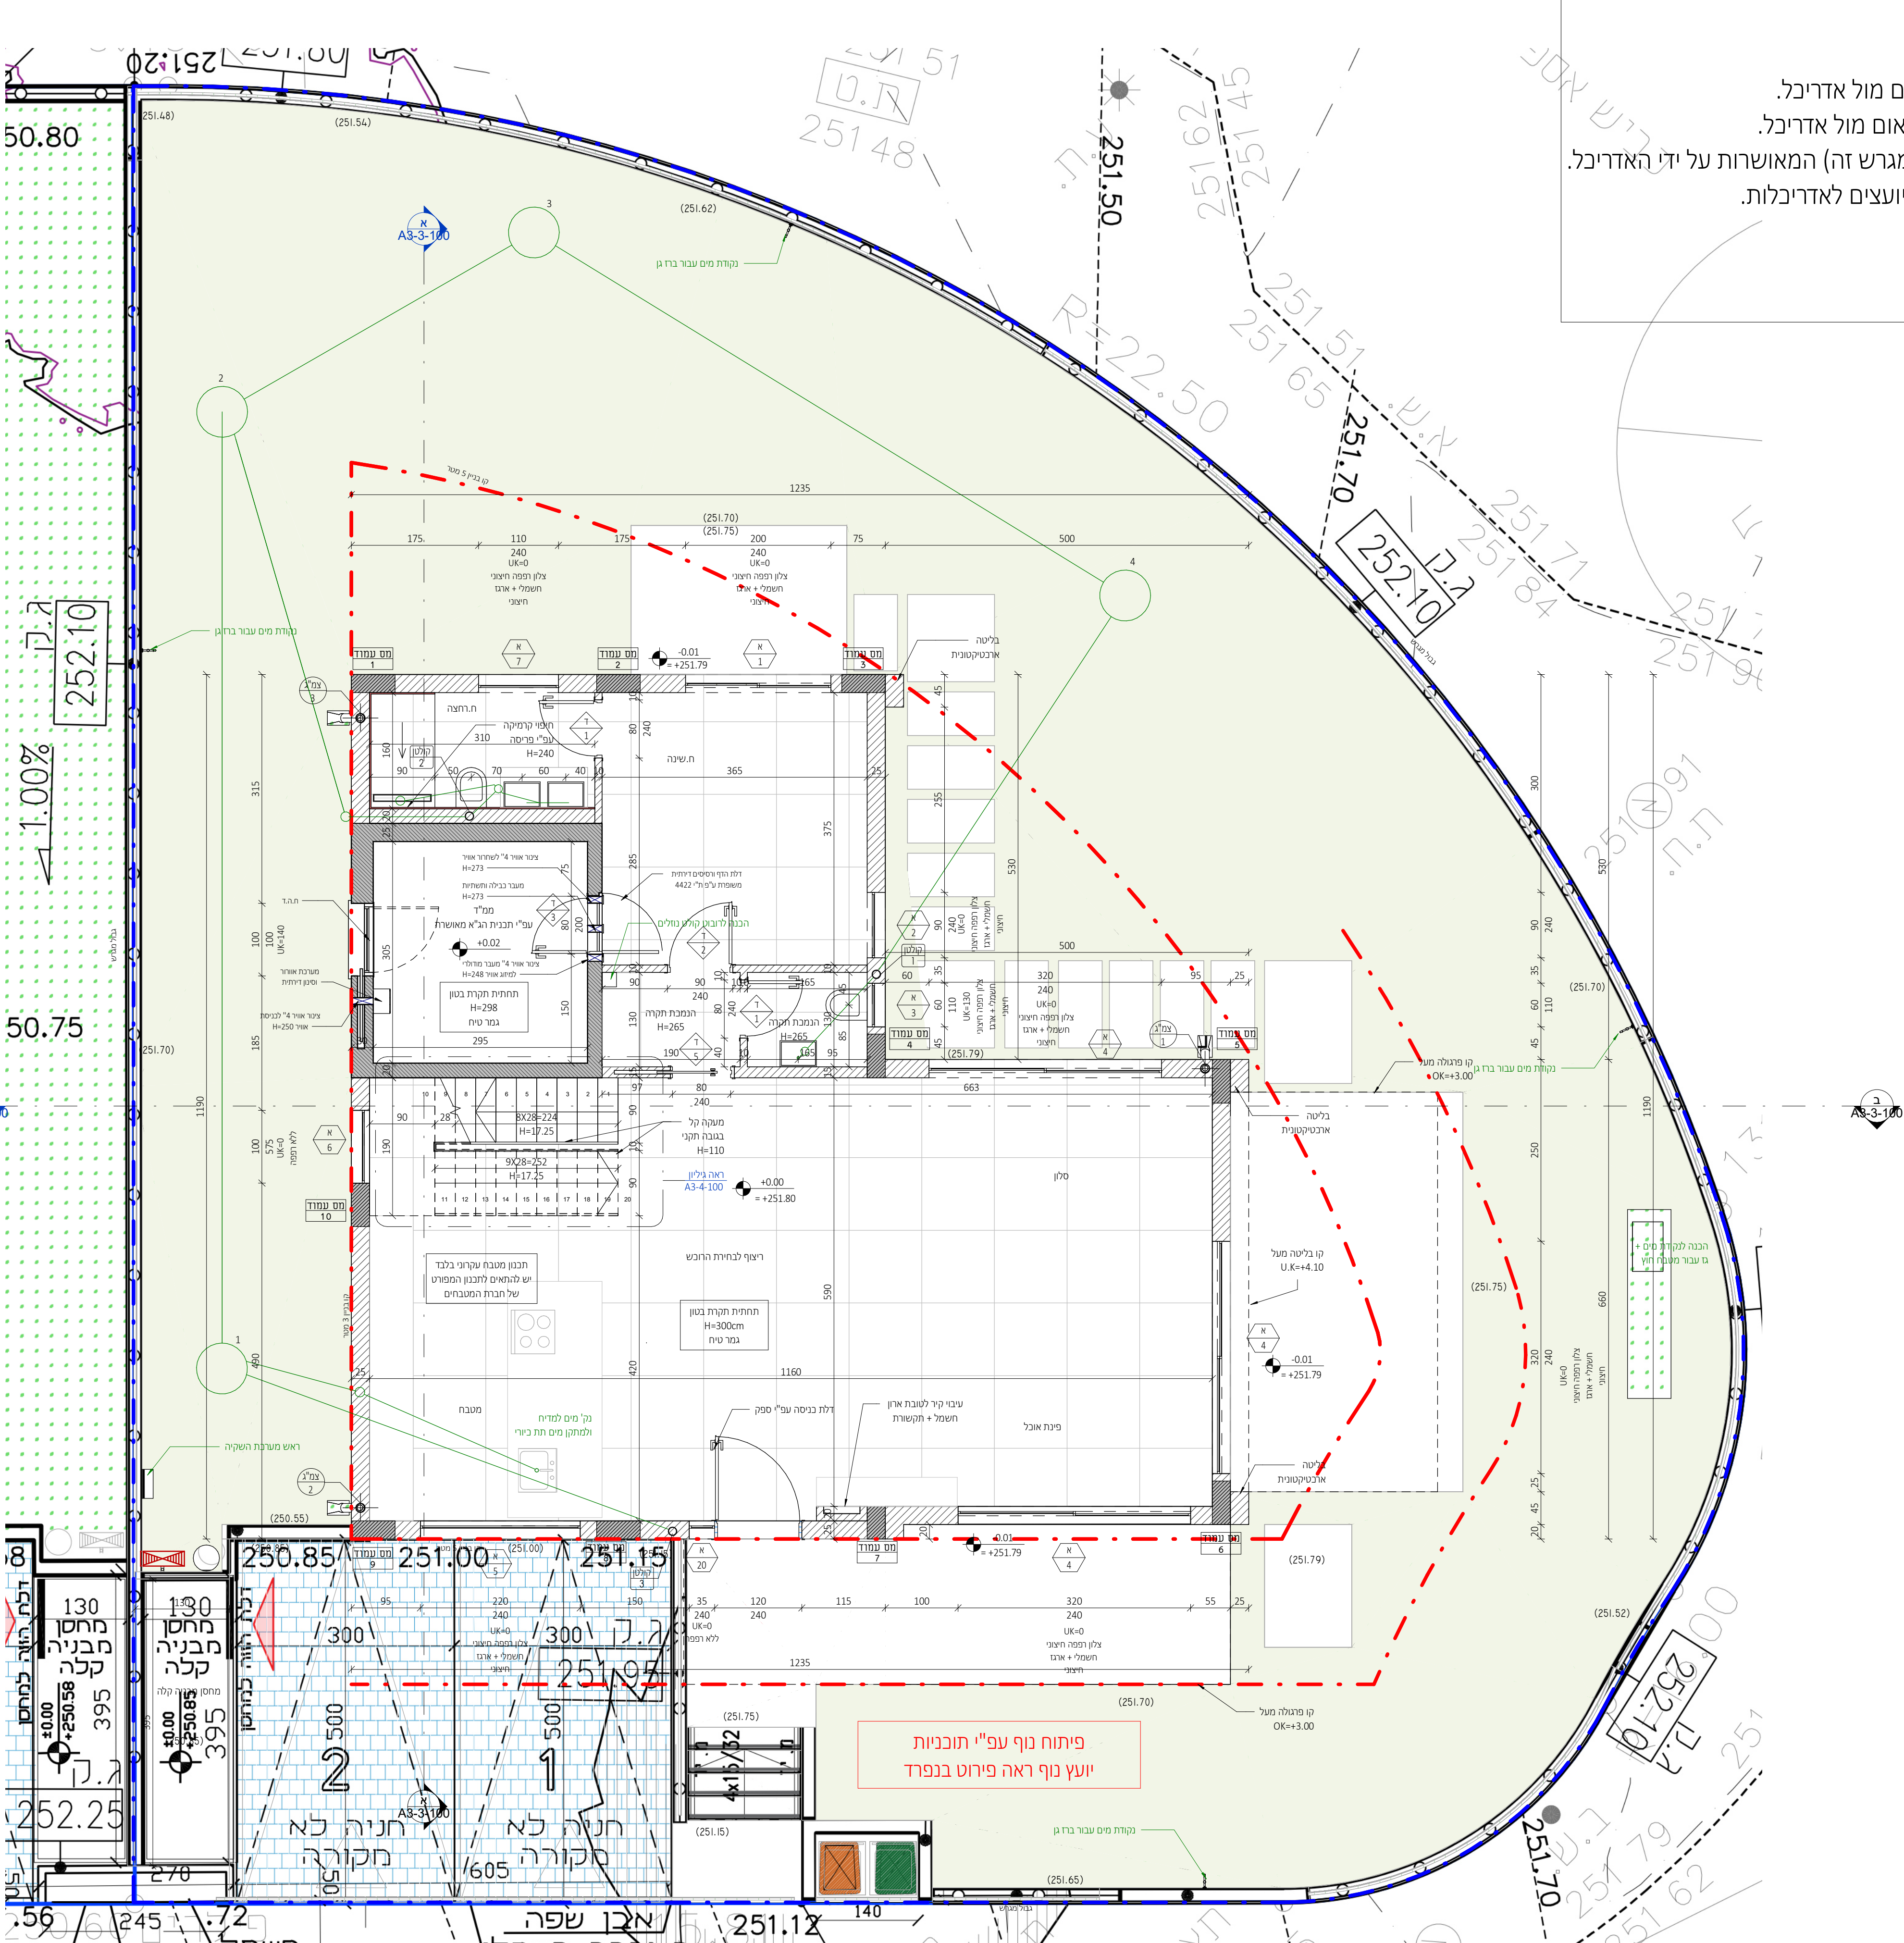

תכנית קומת קרקע

1 : 50

הערות:

1. יש לעבוד במקביל לתכניות יועצים המאושרות על ידי האדריכל.
2. פרטי ספי חלון - עפ"י חוברת אלומיניום של הספק הנבחר ובתיאום מול אדריכל.
3. חימום תת רצפתי (במידה ויש במגרש זה) עפ"י פרטי הספק ובתיאום מול אדריכל.
4. יש לעבוד במקביל לתכניות עיצוב פנים (במידה ויש מעצב פנים במגרש זה) המאושרות על ידי האדריכל.
5. באחריות הקבלן לעדכן את האדריכל על אי התאמה בין התכניות יועצים לאדריכלות.
6. כל הדלתות לפי מפרט מצורף.
7. כל אלמנטי הבטון יקבלו התייחסות תרמית לפי הנחיות יועץ.
8. פרטי איטום, בידוד וניקוז עפ"י תכניות יועצים ובאחריות הקבלן.

ניהול פרויקט
מהיסוד - בן סולומון
פיקוח
מהיסוד - בן סולומון
קונסטרוקציה
ערן שילר
מזוזג אוויר
אייל ארז מהנדסים ויועצים בע"מ
אינסטלציה
איתן אלמסי
חשמל
איתן בסיס
אלומיניום
נוף
נתי בלוקא
חשמל חכם
חימום תת רצפתי
איטום
צבי טל
אקוסטיקה
מעליות
קרקע וביסוס
דיה הנדסת קרקע וביסוס
רישוי

[illegible]

קיר בלוק קיר בטון עמוד בטון

[illegible]


CLIENT NAME:		התחנה	
קבוצת רכישה נופיה			
PROJECT NAME:		סדרת הדיור	
נופיה - מגרש 10			
DRAWING NAME:		סדרת הקניין	
תכנית קומה א			
SHEET NUMBER:		מספר גיליון	
A3-1-102			
SCALE:	קנה מידה:	EDITION:	דפוס:
1 : 50			
STATUS:	סטוס		
למכור			
	[בין ע"י:]	דפוס ע"י:	
DATE:	22.09.2025		
	אדרי:		

NeumanHaynerArchitects

וימן חיינר אדריכלים
מורד ההדריס 2, בית חירות
טל 09-9545842

1 : 50

1. יש לעבוד במקביל לתכניות יועצים המאושרות על ידי האדריכל.
2. פרטי ספי חלון - עפ"י חוברת אלומיניום של הספק הנבחר ובתיאום מול אדריכל.
3. חימום תת רצפתי (במידה ויש במגרש זה) עפ"י פרטי הספק ובתיאום מול אדריכל.
4. יש לעבוד במקביל לתכניות עיצוב פנים (במידה ויש מעצב פנים במגרש זה) המאושרות על ידי האדריכל.
5. באחריות הקבלן לעדכן את האדריכל על אי התאמה בין התכניות יועצים לאדריכלות.
6. כל הדלתות לפי מפרט מצורף.
7. כל אלמנטי הבטון יקבלו התייחסות תרמית לפי הנחיות יועץ.
8. פרטי איטום, בידוד וניקוז עפ"י תכניות יועצים ובאחריות הקבלן.

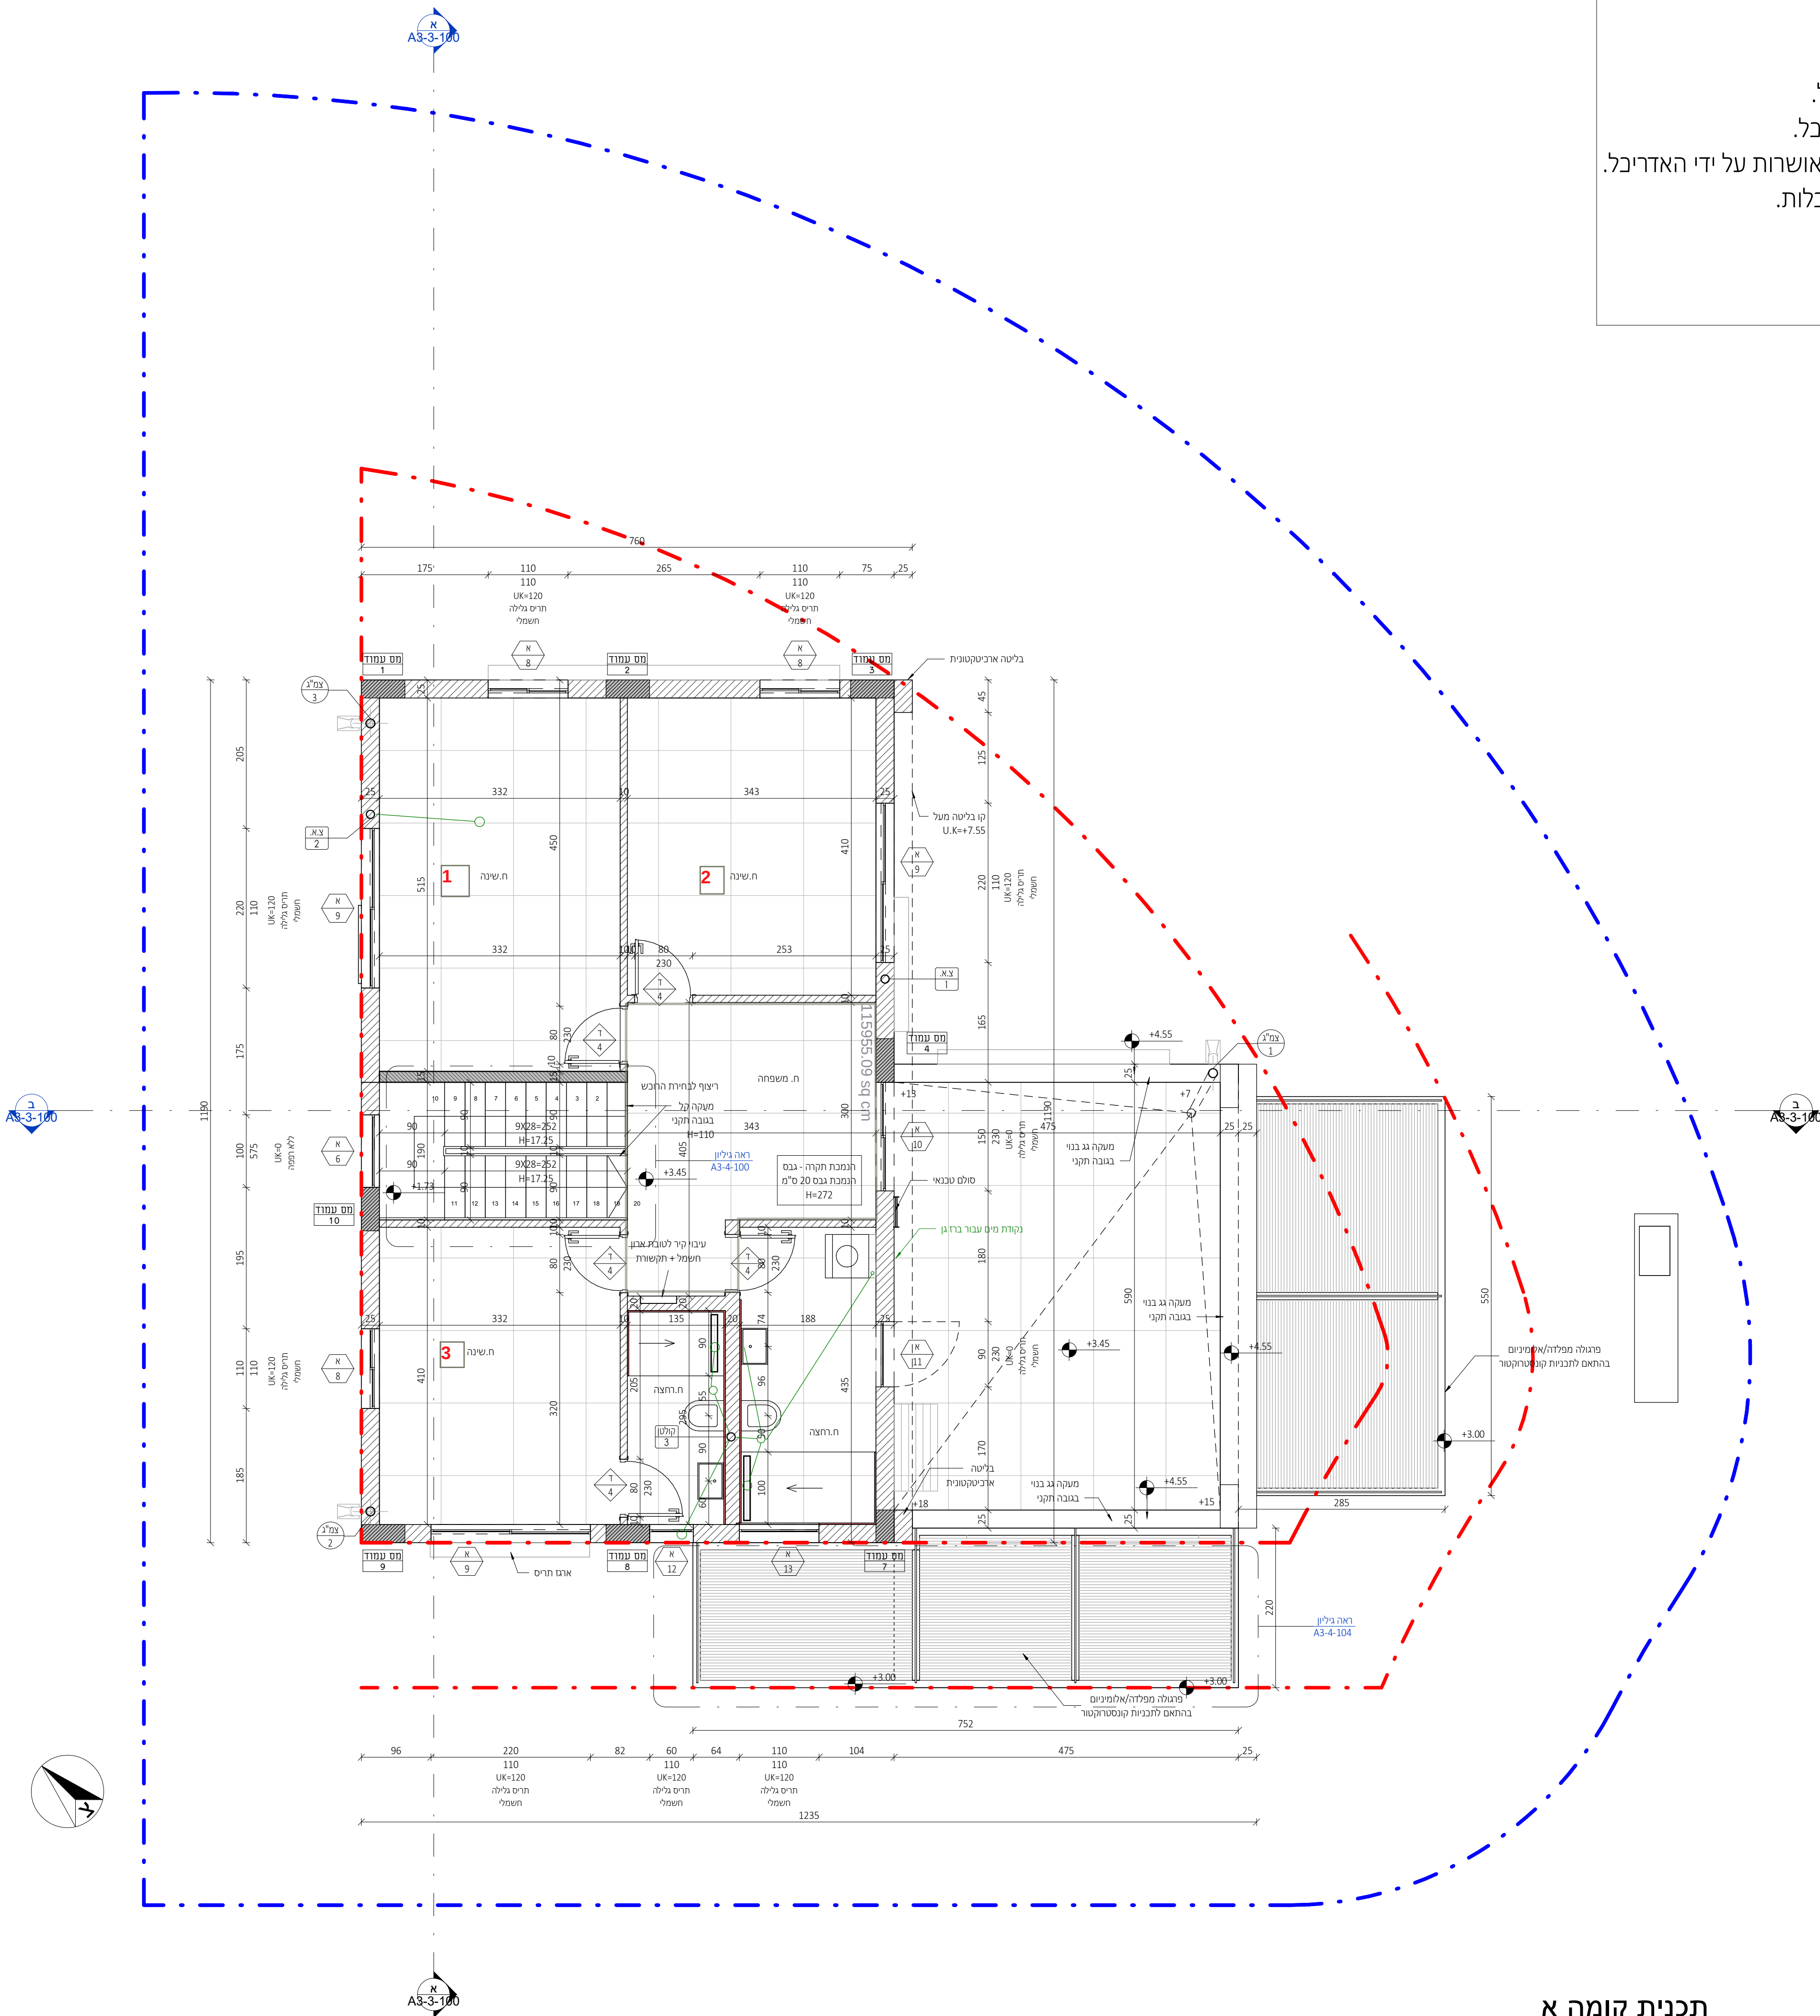

מתכונים:

ניהול פרויקט
מהיסוד - בן סולומון
פיקוח
מהיסוד - בן סולומון
קונסטרוקציה
ערן שילר
מיוזג אוויר
אייל אזר מהנדסים ויועצים בע"מ
אינסטלציה
איתן אלמסי
חשמל
איתן בסיס
אלומיניום
נוף
נתי בלוקא
חשמל חכם
חימום תת רצפתי
איטום
צבי טל
אקוסטיקה
מעליות
קרקע וביסוס
דיה הנדסת קרקע וביסוס
ירשני

$$\pm 0.00 = 251.80$$

ערות:

- כתיבו ו' יש לקרוא אחד עם חכמיו היעוצים.
גובה אבסולוט – ראו תחת פיתוח.
המידות והבין בין הפיתוח הבניה (לא כולל שטח).
החשוב המושג סביב המבנה, כולל חידושים, שכללים, ריצופים.
פיתוחים בגובה, חניה וגניון-ראו חכמיו פיתוח.
אינטוס פיתוח התחנות המבנה במגע עם הקרקע ובידוד תרמי יציב העמידים
והקורות על התחנות – בליות ו' עם פיתוח (גניון) –ראו חכמיו קוטספוסקציה
אין שם יבוצע בעל מישור אפסן הרבול חכמיו.
אין תרמי גומי – כ"פ פיתוח חכמיו, מאושר ע"י פיתוח העורף.

[illegible]

מקרא קירות:

[illegible]

אדריכלות

CLIENT NAME: _____: המזמין:

קבוצת רכישה נופיה

PROJECT NAME: הפרויקט:

בופיה - מגרש 10

DRAWING NAME: תגלית

תכנית מפלס גג

SHEET NUMBER: 99 גליון:

A3-1-103

SCALE: קנה מידה: EDITION: דורה:

1 : 50

STATUS: 1

למכר	
------	---

דסט ע"י: _____ נבדק ע"י: _____

DATE: 22 09 2025 י"ד

Neurological Disorders and Disabilities

office@nh-arch.com משרד ההדריס 2, בית חירות

[illegible]

תכנית גג

1 : 50

מתכננים:

ניהול פרויקט
מהיסוד - בן סולומון
פיקוח
מהיסוד - בן סולומון
קונסטרוקציה
ערן שילר
מיזוג אוויר
אייל ארז מהנדסים ויועצים בע"מ
אינסטלציה
איתן אלמסי
חשמל
איתן בסיס
אלומיניום
נוף
נתי בלוקא
חשמל חכם
חימום תת רצפתי
איטום
צבי טל
אקוסטיקה
מעליות
קרקע וביסוס
דיה הנדסת קרקע וביסוס
רישוי

--

± 0.00 = 251.80
--

הערות:
- תכנית זו יש לקרוא יחד עם תכניות הריטשים. - גובה אבסולוטי: ראו תכנית פיתוח. - הפרדות הן בין קירות הבניה ולא כולל פחים. - פיתוח השטח סביב הבנוה, כולל, מדרגות, נדרות, שבילים, ריצופים, שטחים גברים, חניה וגן עד רוא תכנית פיתוח. - איטום קירות ורצפות הבנוה כחמע עם הקרקע ובנידוד תחרי לאורך העמודים והקורות ומכל התפרות. כלירות או עם סימני גיבוע. ראו תכנית קונסטרוקציה. - אף מים יבוצע בכל מישור אופקי הכולס חתונה. - פוח תחמי בממד"ד ע"פ מפרט תומקיר, מאושר טיי פיקוד העודף.

המבצע אחראי לסידור: עליו לבקר ולבדוק את כל המידוח בתכנית ובקשות הבנייה.
במספר של שטח או אי התאמה בתכנית /או בבנוי, עליו להודיע על כך מיד לאדריכל בסופו המשיך בעבודתו.
המבצע יישמש או ויק בתכנית שאושר לכניסו.
המבצע יחזיק באחר, בכל מה, של מחדכן של תכנית.
אח לקבוע מידוח על ידי חדיה בשו שום.
התכנית הנה רכוש האדריכל ואין לשנות כל שימוש בה או ברעיונות הגלומים בה, אלא באישור בכתב מהאדריכל.
המבצע יחזיק בתכנית זו, ושש לכדו באחריות.
על המפקח והמכין לודא התאמת התכנית האדריכלית "כניסו" לתכנית יחית, המכר והתכנית התאושות פי כל גודלים והרשימים.
התכנית כוללת את כל התפרותיה הדרוג עד ליום תחלפת.

משרד קירות:

		
קיר בלוק	קיר בסון	מחוד בסון

תאריך	תיאור	מהדורה
22.09.2025	מכרז	1

אדריכלות

שם המוסד:

קבוצת רכישה נופיה

שם הפרויקט:

נופיה - מגרש 10

שם הגילוי:

- תכנית תקרה ותאורה קרקע

מספר גילוי:

A3-1-104

תחבורה:

EDITION: קנה מידה:

As indicated

STATUS: למכרז

שורשם ע"י:

תאריך:

22.09.2025



NeumanHaynerArchitects

נוירן חיינר אדריכלים
מודד התודים 2, בית חירות
09-9545842

22/10/2025 15:53:41

זכיות יימור / ע"פ הנחות ע"ד

-תכנית חשמל - תהיה עפ"י גליון של יועץ חשמל.


2. תכנית תאורה, מיקום גופי תאורה - עפ"י גליון זה.

3. יש לעבוד במקביל לתכניות של מתכנן מיזוג אוויר, ובתיאום מול אדריכל.

4. מידות סופיות בין גופי תאורה ינתנו לאחר בחירה סופית של הדגמים.

5. מיזוג אוויר - מיקום התקנת יחידות ומיקום תריסים, פתחי שירות - לתיאום סופי מול אדריכל לפני ביצוע.

6. חימום תת רצפתי עפ"י פרטי הספק ובתיאום מול אדריכל.

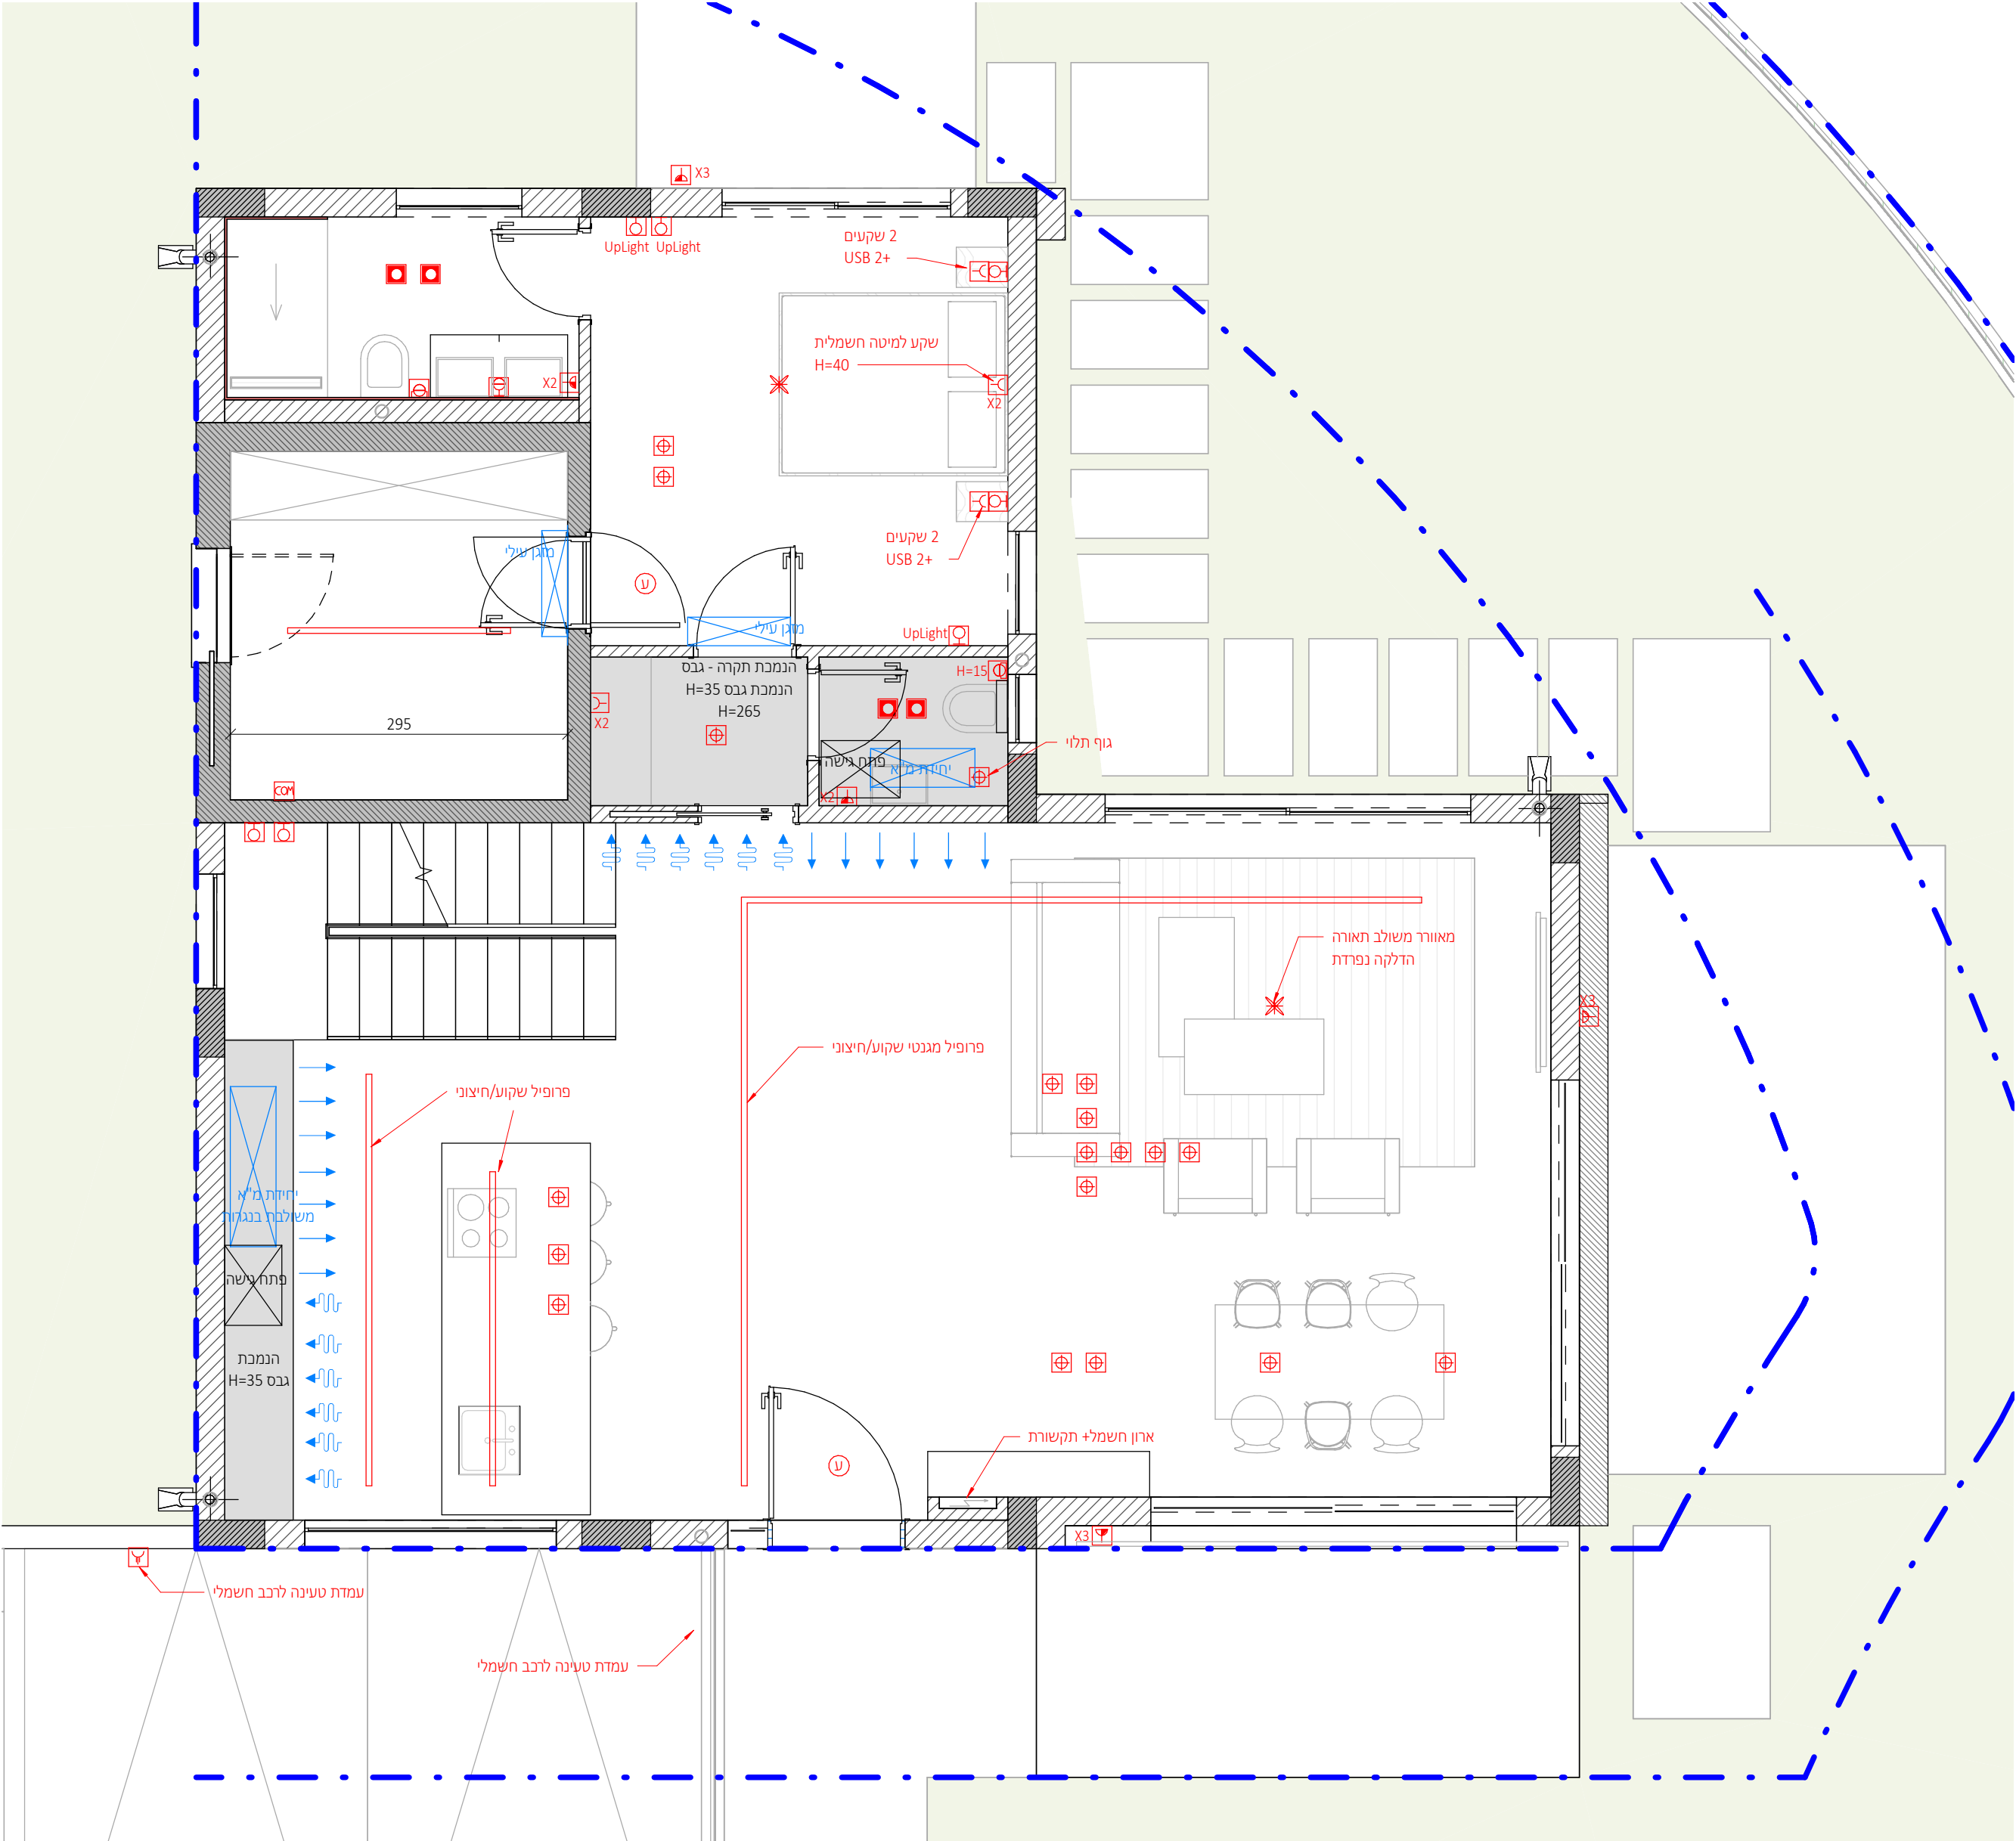

תכנית תאורה - קומת קרקע

1 : 50

מקרא חשמל ותאורה

לחצנים ופקדים	
	מפסק חד קוטבי למאור
	מפסק חד קוטבי למאור עם דימר
	מפסק מחליף למאור
	מפסק מחליף למאור עם דימר
	מפסק לזוונטה
	מפסק לזוויילר / תנור חימום באמבטיה
	לחצן פעמון
	לחצן מדרגות פוספורי
	מפסק בטחון בוילר
	מפסק בטחון ליחידת מ"א
	ארון חשמל תה"ט עם דלת K.O=200
	ארון תקשורת
	קיום עולים
	קיום ירדים
	גלאי עשן

שקעים ואביזרים	
	בית תקע
	בית תקע כוח
	בית תקע מוגן מים
	נקודת טלפון
	נקודת אינטרנט
	נקודת תנור אמבטיה
	נקודת טל"כ / לוויין
	נקודת חזנה למנוע תריס חשמלי
	נקודת הפעלה לתריס חשמלי
	נקודת חזנה למנוע ונטה חשמלי
	צינור שרשרי 15 מ"מ עם חוט משיכה
	נקודת אינטרקום
	נקודת אינטרקום טלויזיוני
	פעמון דירתי תקני 12V
	H=40 סימבוקס אלא אם צוין אחרת

תאורה	
	נקודת מאור חיצונית מהתקרה
	נקודת מאור שקועה בתקרה
	נקודת מאור שקועה בתקרה מוגנת מים
	נקודת מאור שקועה ברצפה מוגנת מים
	נקודת מאור בתקרה עם מאוורר
	מאוורר תקרה
	נקודת מאור על הקיר
	נקודת מאור מוגן מים על הקיר
	נקודת מאור שקועה בקיר
	נקודת מאור מוגן מים שקועה בקיר
	פס צבירה שקוע בתקרה כולל גופי תאורה
	פס צבירה על התקרה כולל גופי תאורה
	דו תכליתי
	תאורת חירום
	נקודת מאור ספוט
	נקודת מאור ספוט - מוגנת מים

הנחיות

- יש לקרוא תוכנית זו בצד תכנית מיזוג
- במקרה של אי התאמה יש לידע את האדריכל
- כל המידות הן למרכז אברזר אלא אם צוין אחרת
- מיקום האביזרים באיזורים משמעותיים מפורט בפרטות יש למקמם בהתאם
- גובה המפסקים הינו H=90 אלא אם צוין אחרת
- בהתקנת מפסקים / מקלדות-אזעקה / פיקוד-מזגן אחד מעל השני יש למרכזם על ציר האמצע
- בין כל רכיב יש להשאיר רווח של 5 ס"מ
- דגם המפסקים יהיו גביס. במידה ודגם שונה, יש לידע את האדריכל
- גמר המפסקים בתיאום מול האדריכל
- חיווט אודי: כל רמקול מגיע בנפרד לאיזור הריכוז (מקום הריס"ב)
- איש הקשר לאודי בבית:
- מפסק תנור חימום אמבטיה ומפסק דוד מים חשמלי H=150 עפ"י התקן
- גובה השקעים הינו H=40 אלא אם צוין אחרת
- גובה מנורות קיר הינו H=210 אלא אם צוין אחרת
- מנורות מעל מדרגות בגובה H=15 אלא אם צוין אחרת

ניהול פרויקט
מהיסוד - בן סולומון
פיקוח
מהיסוד - בן סולומון
קונסטרוקציה
ערן שילר
מיזוג אוויר
אייל ארז מהנדסים ויועצים בע"מ
אינסטלציה
איתן אלמסי
חשמל
איתן בסיס
אלומיניום
בופ
נתי בלוקא
חשמל חכם
חימום תת רצפתי
איטום
צבי טל
אקוסטיקה
מעליות
קרקע וביסוס
דיה הנדסת קרקע וביסוס
רישוי

[illegible]

עמוד בטון קיר בטון רצפת בטון

[illegible]

CLIENT NAME:	ה'תשס"ח
קבוצת רכישה נופיה	
PROJECT NAME:	הפרויקט:
נופיה - מגרש 10	
DRAWING NAME:	שם התוכנית:
תכנית תקרה ותאורה קומה א	
SHEET NUMBER:	מספר גיליון:
A3-1-105	

EDITION:	קנה מידה:	מחזור:
	1 : 50	
	סטוס	מחזור:
	למכר	דסט עיי:
	נבדק עיי:	
22.09.2025		מחזור:



זכויות ייצור / ע"פ הנחיות עו"ד

The diagram is a detailed architectural floor plan of a three-story building. It includes the following elements:

- Furniture and Fixtures:** Three bedrooms are labeled "ח. שינה 1", "ח. שינה 2", and "ח. שינה 3". A central living area is labeled "הגמכת חקירה - בגים" (Investigation Room - Bags). There is also a kitchen area labeled "ארוז חשמל" (Electrical Kitchen) and a bathroom labeled "פרופיל חינני" (Educational Profile).
- Lighting:** Numerous light fixtures are indicated by red symbols and labels such as "Up Light", "X3", "X2", and "X1".
- Dimensions:** Various dimensions are provided for rooms and furniture, including "H=40", "H=120", "H=272", "H=290", "160", and "112".
- Structural Elements:** The plan shows walls, doors, windows, and stairs.
- Annotations:** Hebrew text labels identify specific areas and features, such as "שקט למסדה חשמלית" (Electric Bed Quiet), "שקט למסדה קריאה" (Reading Bed Quiet), and "שקט למסדה קריאה שידות" (Reading Bed Quiet Seats).

1 : 50

מתכנים:


ניהול פרויקט
מהיסוד - בן סולמון
פיקוח
מהיסוד - בן סולמון
קונסטרוקציה
ערן שילר
מיזוג אוויר
אייל ארז מהנדסים ויועצים בע"מ
אינסטלציה
איתן אלמסי
חשמל
איתן בסיס
אלומיניום
נוף
נתי בלוקא
חשמל חכם
חימום תת רצפתי
איטום
צבי טל
אקוסטיקה
מעליות
קרקע וביסוס
דיה הנדסת קרקע וביסוס
רישוי

± 0.00 = 251.80
הערות: 1. תכנית זו הי לקרא יחד עם תכנית הריטשים. 2. גובה אבסטרקט: ראו תכנית פיתוח. 3. המידות הן בין קירות הבניה ולא כולל פחים. 4. פיתוח השטח סביב המבנה, כולל, מדרגות, גדרות, שבילים, ריצופים, שיטות גינה, חניה וכו' ראו תכנית פיתוח. 5. איטום קירות ורצפות המבנה כחמם עם הקרקע ובידוד תרמי לאורך העמודים והקורות למר המקורה. כליות או עם סימני גיבס. ראו תכנית קונסטרוקציה. 6. אף חים יבוצע בכל מישור אופקי הכולל חתוכין. 7. פוח תרמי במסד- ע"פ מפרט תומקיר, מאושר ע"י פיקוד העורף. המבצע אחראי לסידור: עליו לבקר ולבדוק את כל המידות בתכנית ובקשות המבנה. במסד של שטח או אי התאמה בתכנית /או בבנין, עליו להודיע על כך מיד לאדריכל בסדם המשיך בעבודתו. המבצע ישתמש או וקל בתכנית שאושר לכניס. המבצע חותם באחר, בכל מה, של מחדש של תכנית. אח לקבוע מידות על ידי חדיה בשו מוס. התכנית הנה רכוש האדריכל ואין לשנות כל שימוש בה או ברעיונות הגלומים בה, אלא באישור בכתב מהאדריכל. מחמם /או יושם אשר שמו רשום בתכנית זו, נושא לכך באחריות המפתחים והמקורות לתכנית. על המפתח והמבצע לודא התאמת התכנית האדריכלית "לכניס" לתכנית זו. המכר והתכנית הואושות ע"י כל גורמים ורשמיים. התכנית כוללת את כל האחריות והידוע על ליום תחמם.
משרד קירות:
קיר בלוק קיר בסון מחוד בסון

תאריך	תיאור	מהדורה
22.09.2025	מכר	1


אדריכלות			
המחיר:	CLIENT NAME:		
קבוצת רכישה נופיה			
הפרויקט:	PROJECT NAME:		
נופיה - מגרש 10			
הגליון:	DRAWING NAME:		
חזיתות 1			
מספר גליון:	SHEET NUMBER:		
A3-2-200			
חזרה:	EDITION:	קנה מידה:	SCALE:
		1 : 50	
שורס עיי:	נבוק עיי:	למכר	מסוס
תאריך:	DATE:	22.09.2025	

פיתוח נוף עפ"י תוכניות
יועץ נוף ראה פירוט בנפרד

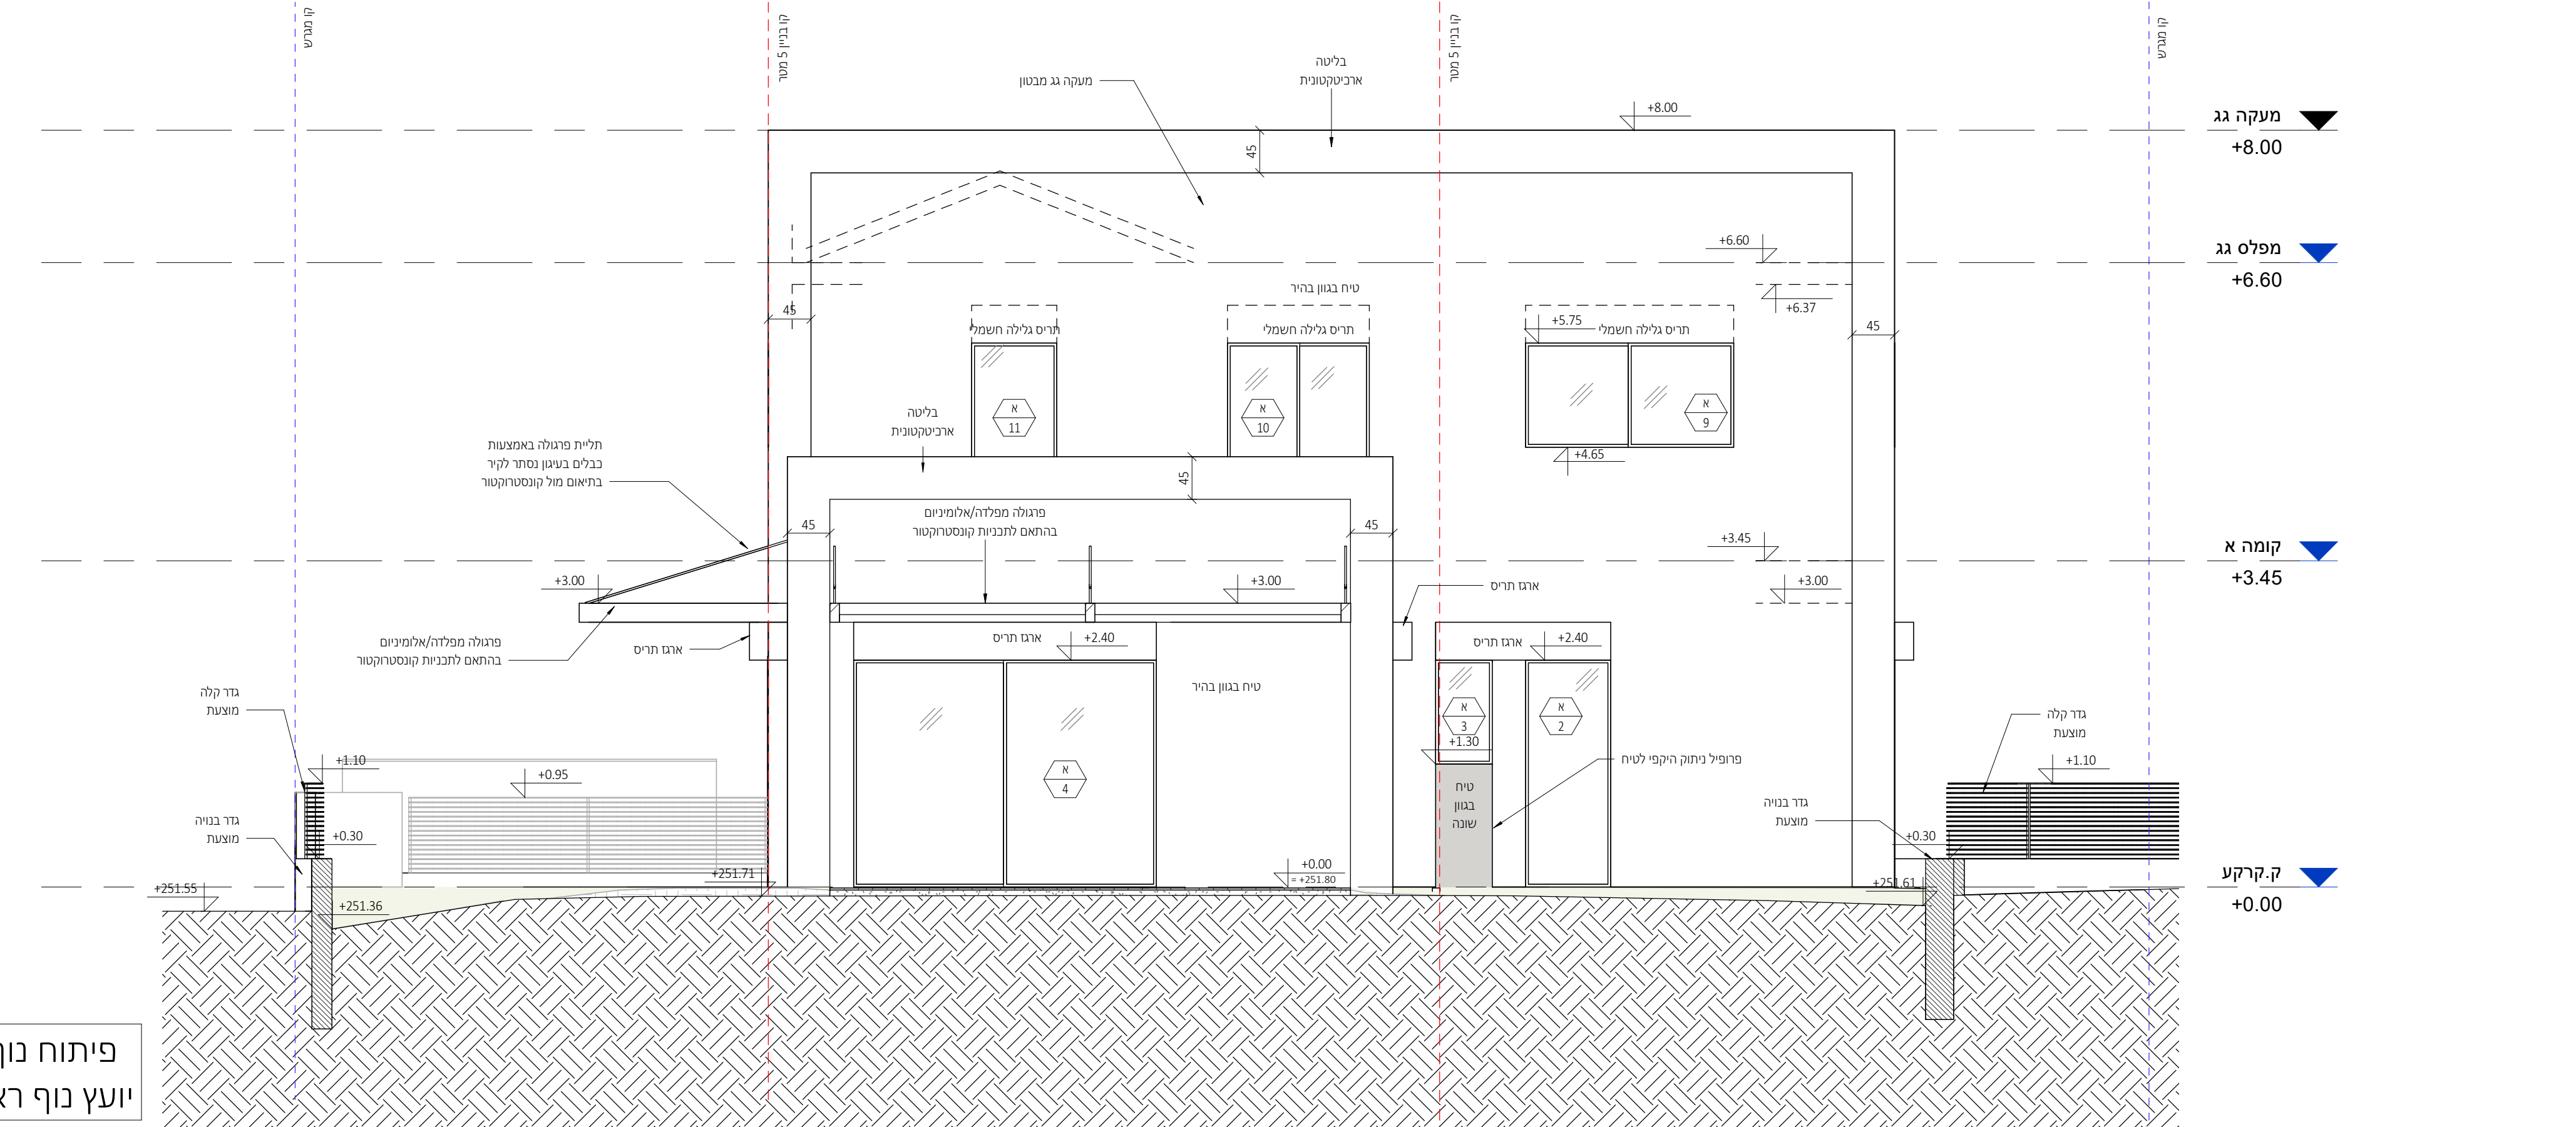

חזית דרום מזרחית

1 : 50

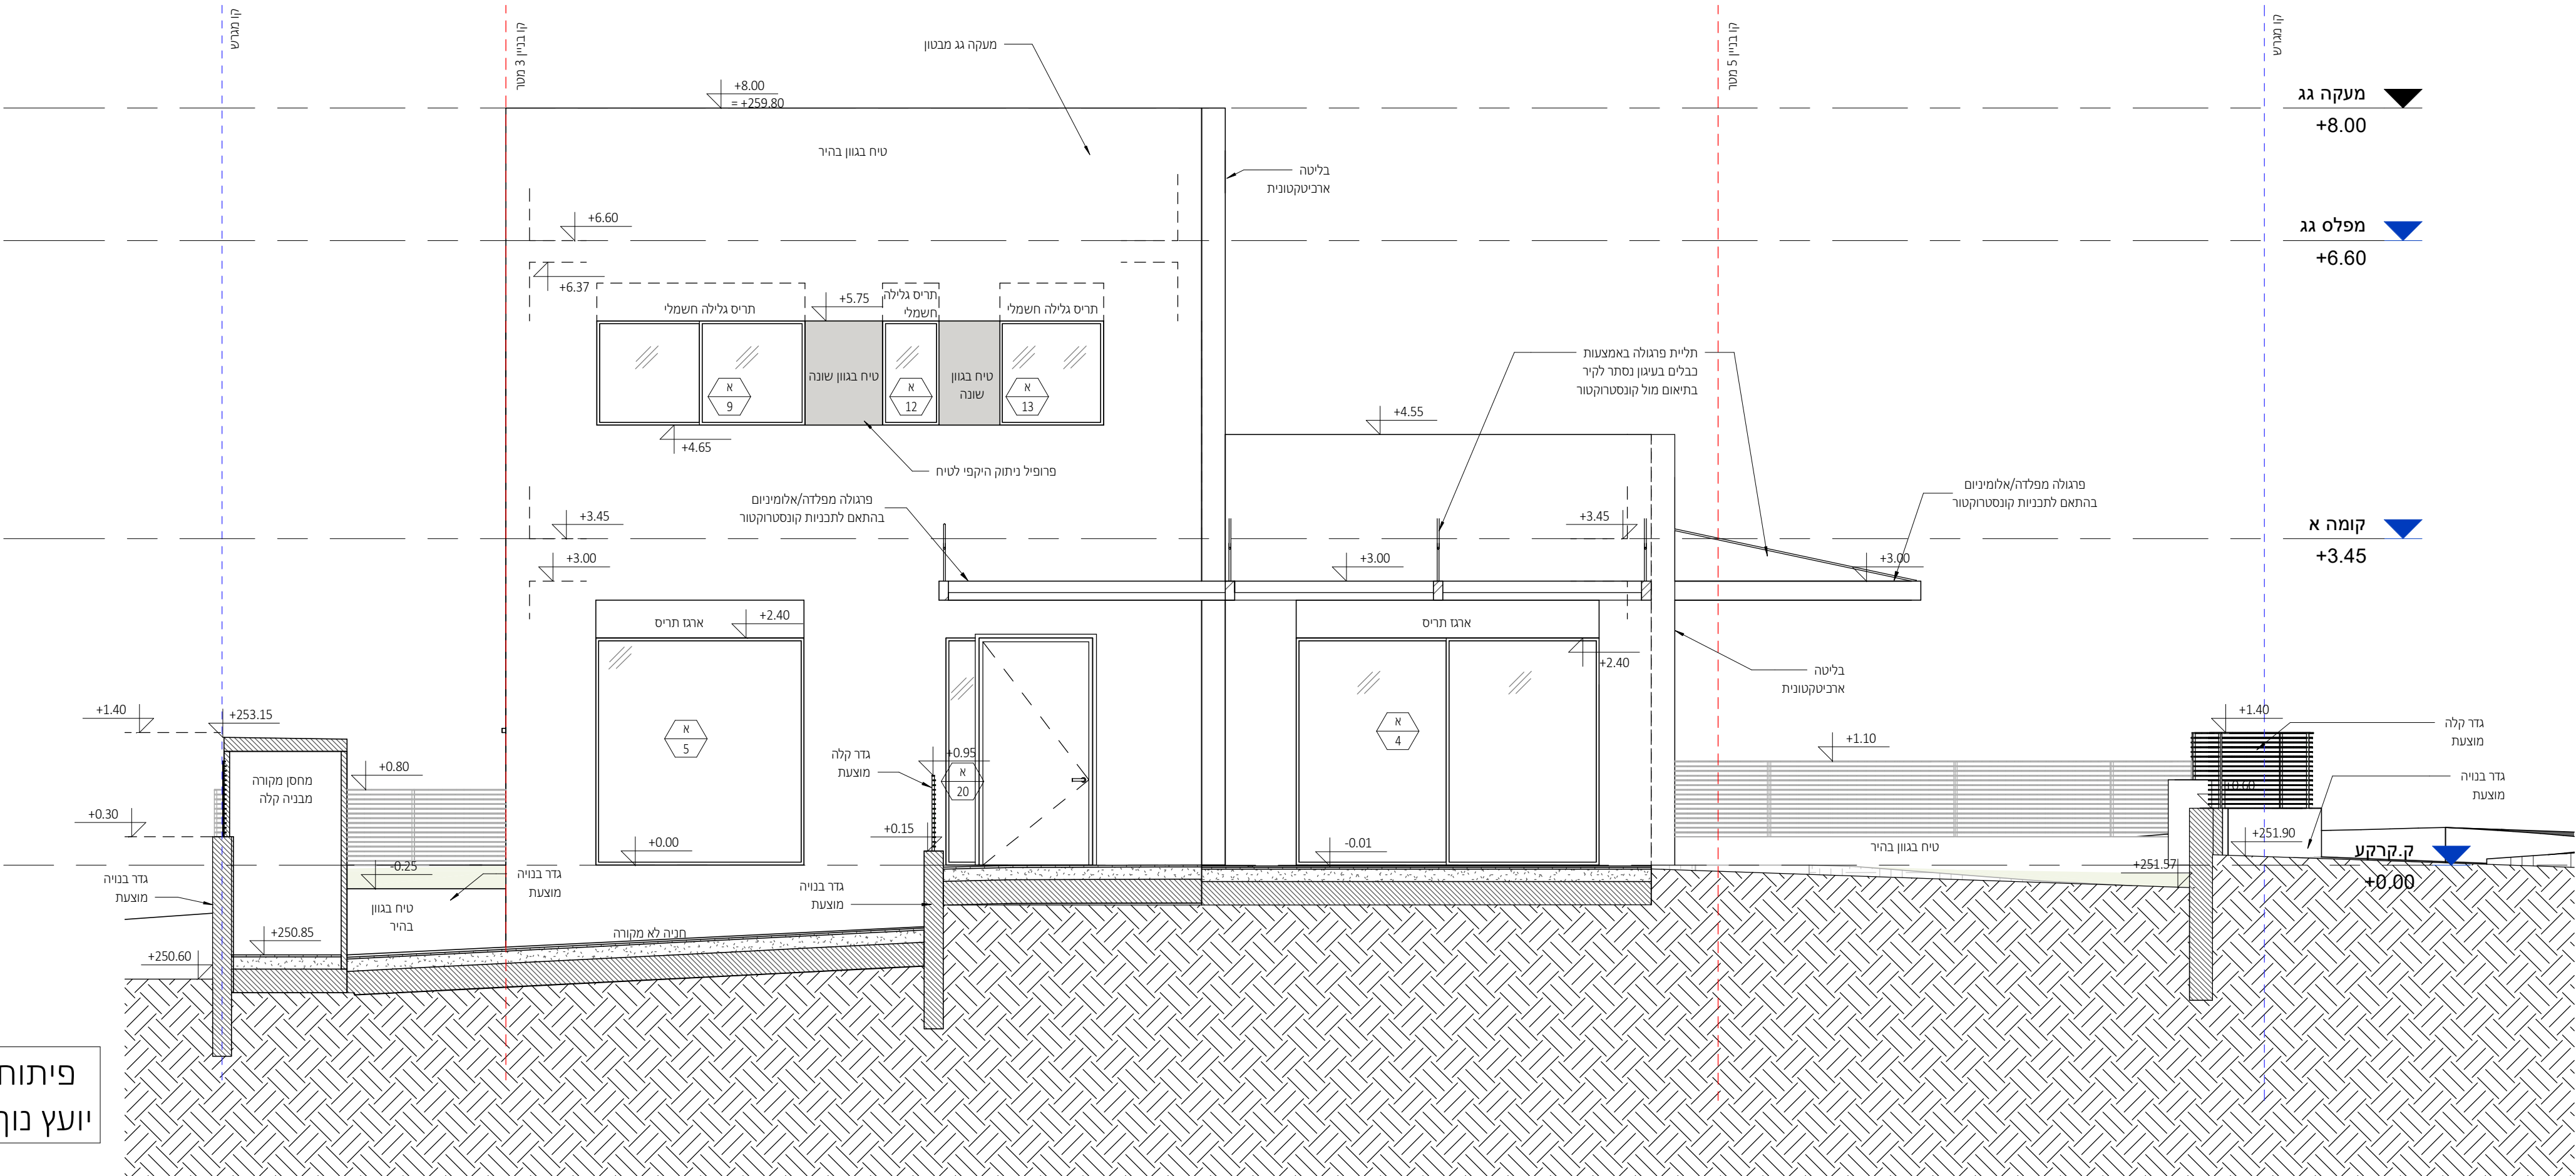

חזית דרום מערבית

1 : 50

מתכננים:


ניהול פרויקט
מהיסוד - בן סולומון
פיקוח
מהיסוד - בן סולומון
קונסטרוקציה
ערן שילר
מיזוג אוויר
אייל ארז מהנדסים ויועצים בע"מ
אינסטלציה
איתן אלמסי
חשמל
איתן בסיס
אלמזיום
נוף
נתי בלוקא
חשמל חכם
חימום תת רצפתי
איטום
צבי טל
אקוסטיקה
מעליות
קרקע וביסוס
דיה הנדסת קרקע וביסוס
רישוי

± 0.00 = 251.80

- הערות:
1. תכנית זו הי לקרא יחד עם תכנית הריטשים.
 2. גובה אבטמנטים: ראו תכנית פיתוח.
 3. הפירות הן בין קירות הבניה ולא כולל פחים.
 4. פיתוח השטח סביב המבנה, כולל, מדרגות, גדרות, שבילים, ריצופים, שטחים גזרים, חניה וגן ראו תכנית פיתוח.
 5. איטום קירות ורצפות המבנה כמעט עם הקרקע ובידוד חרסי לאורך העמודים והקירות ובר המרתה. כליות או עם סימני גיבס. ראו תכנית קונסטרוקציה.
 6. אף חיס יבוצע בכל מישור אופקי הכולל מחבנין.
 7. סיוח חרסי במסגד- ע"פ מפרט חומרים, מאושר ע"י פיקוח העורך.

המבצע אחראי לסידור: עליו לבקר ולבדוק את כל המידוח בתכנית ובקשות העבודה. במסגרת של שטח או אי התאמה בתכנית /או בבנין, עליו להודיע על כך מיד לאדריכל בסופ המשיך שבבנין. המבצע יתחשב או ויק בתכנית שאושר לכניס. המבצע יחזיק אתה, בכל שטח, של מחדש של תכנית. את לקבוע מידוח על ידי חדיה בשו מוס. התכנית הנה רכוש האדריכל ואין לשנות כל שימוש בה או ברעיונות הגלומים בה, אלא באישור בכתב מהאדריכל. מתחם /או יושע אשר שמו רשום בתכנית זו, נושא לכיד באחריות המקצועית והסדית לתכנית. על התפקד והשכלן לודא התאמת התכנית האדריכלית "לכניס" לתכנית ויתר, המכר והתכנית האושרות ע"י כל גורמים הרשמיים. התכנית כוללת את כל האמצעים הדרוג עד ליום תחלית.

משרד קירות:

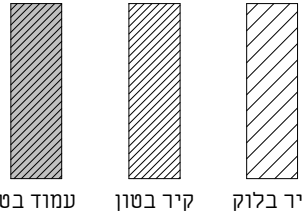

תאריך	תיאור	מהדורה
22.09.2025	מכר	1

אדריכלות


שם המסין:	CLIENT NAME:
קבוצת רכישה נופיה	
שם הפרויקט:	PROJECT NAME:
נופיה - מגרש 10	
שם הגליון:	DRAWING NAME:
חזיתות 2	
מספר גליון:	SHEET NUMBER:
A3-2-201	
תאריך:	DATE:
22.09.2025	



נירן חיינר אדריכלים
מודד תהודים 2, בית חירות
09-954642 78
office@nh-arch.com
www.nh-arch.com


זכיות ייפוי / ע"פ הנחיות ע"ד

פיתוח נוף עפ"י תוכניות
יועץ נוף ראה פירוט בנפרד

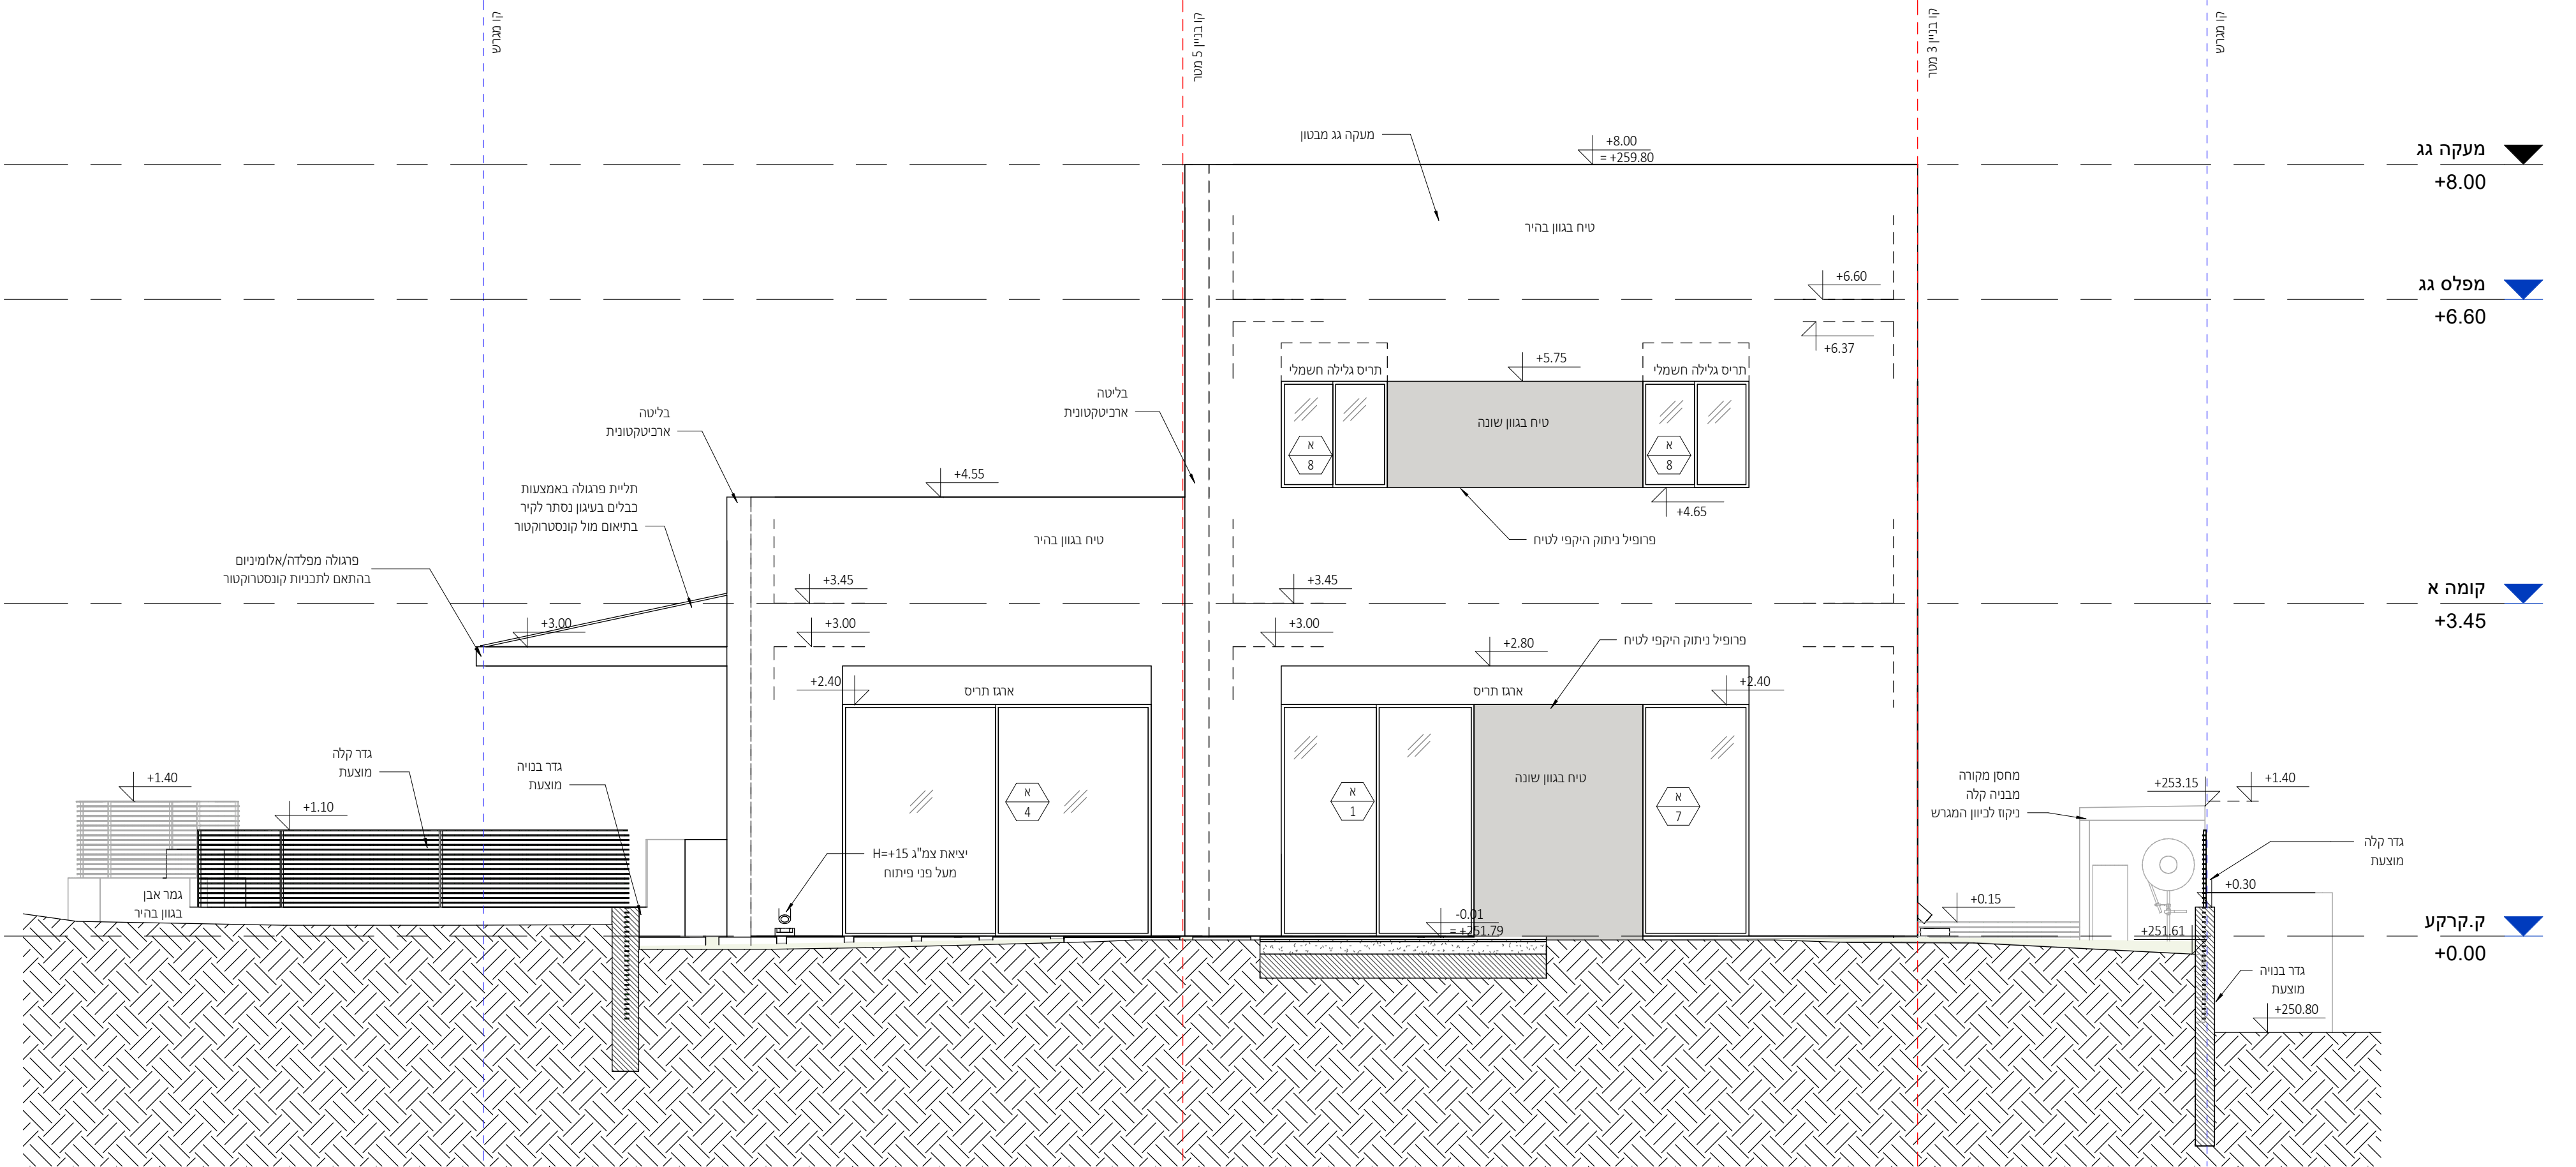

חזית צפון מזרחית

1 : 50

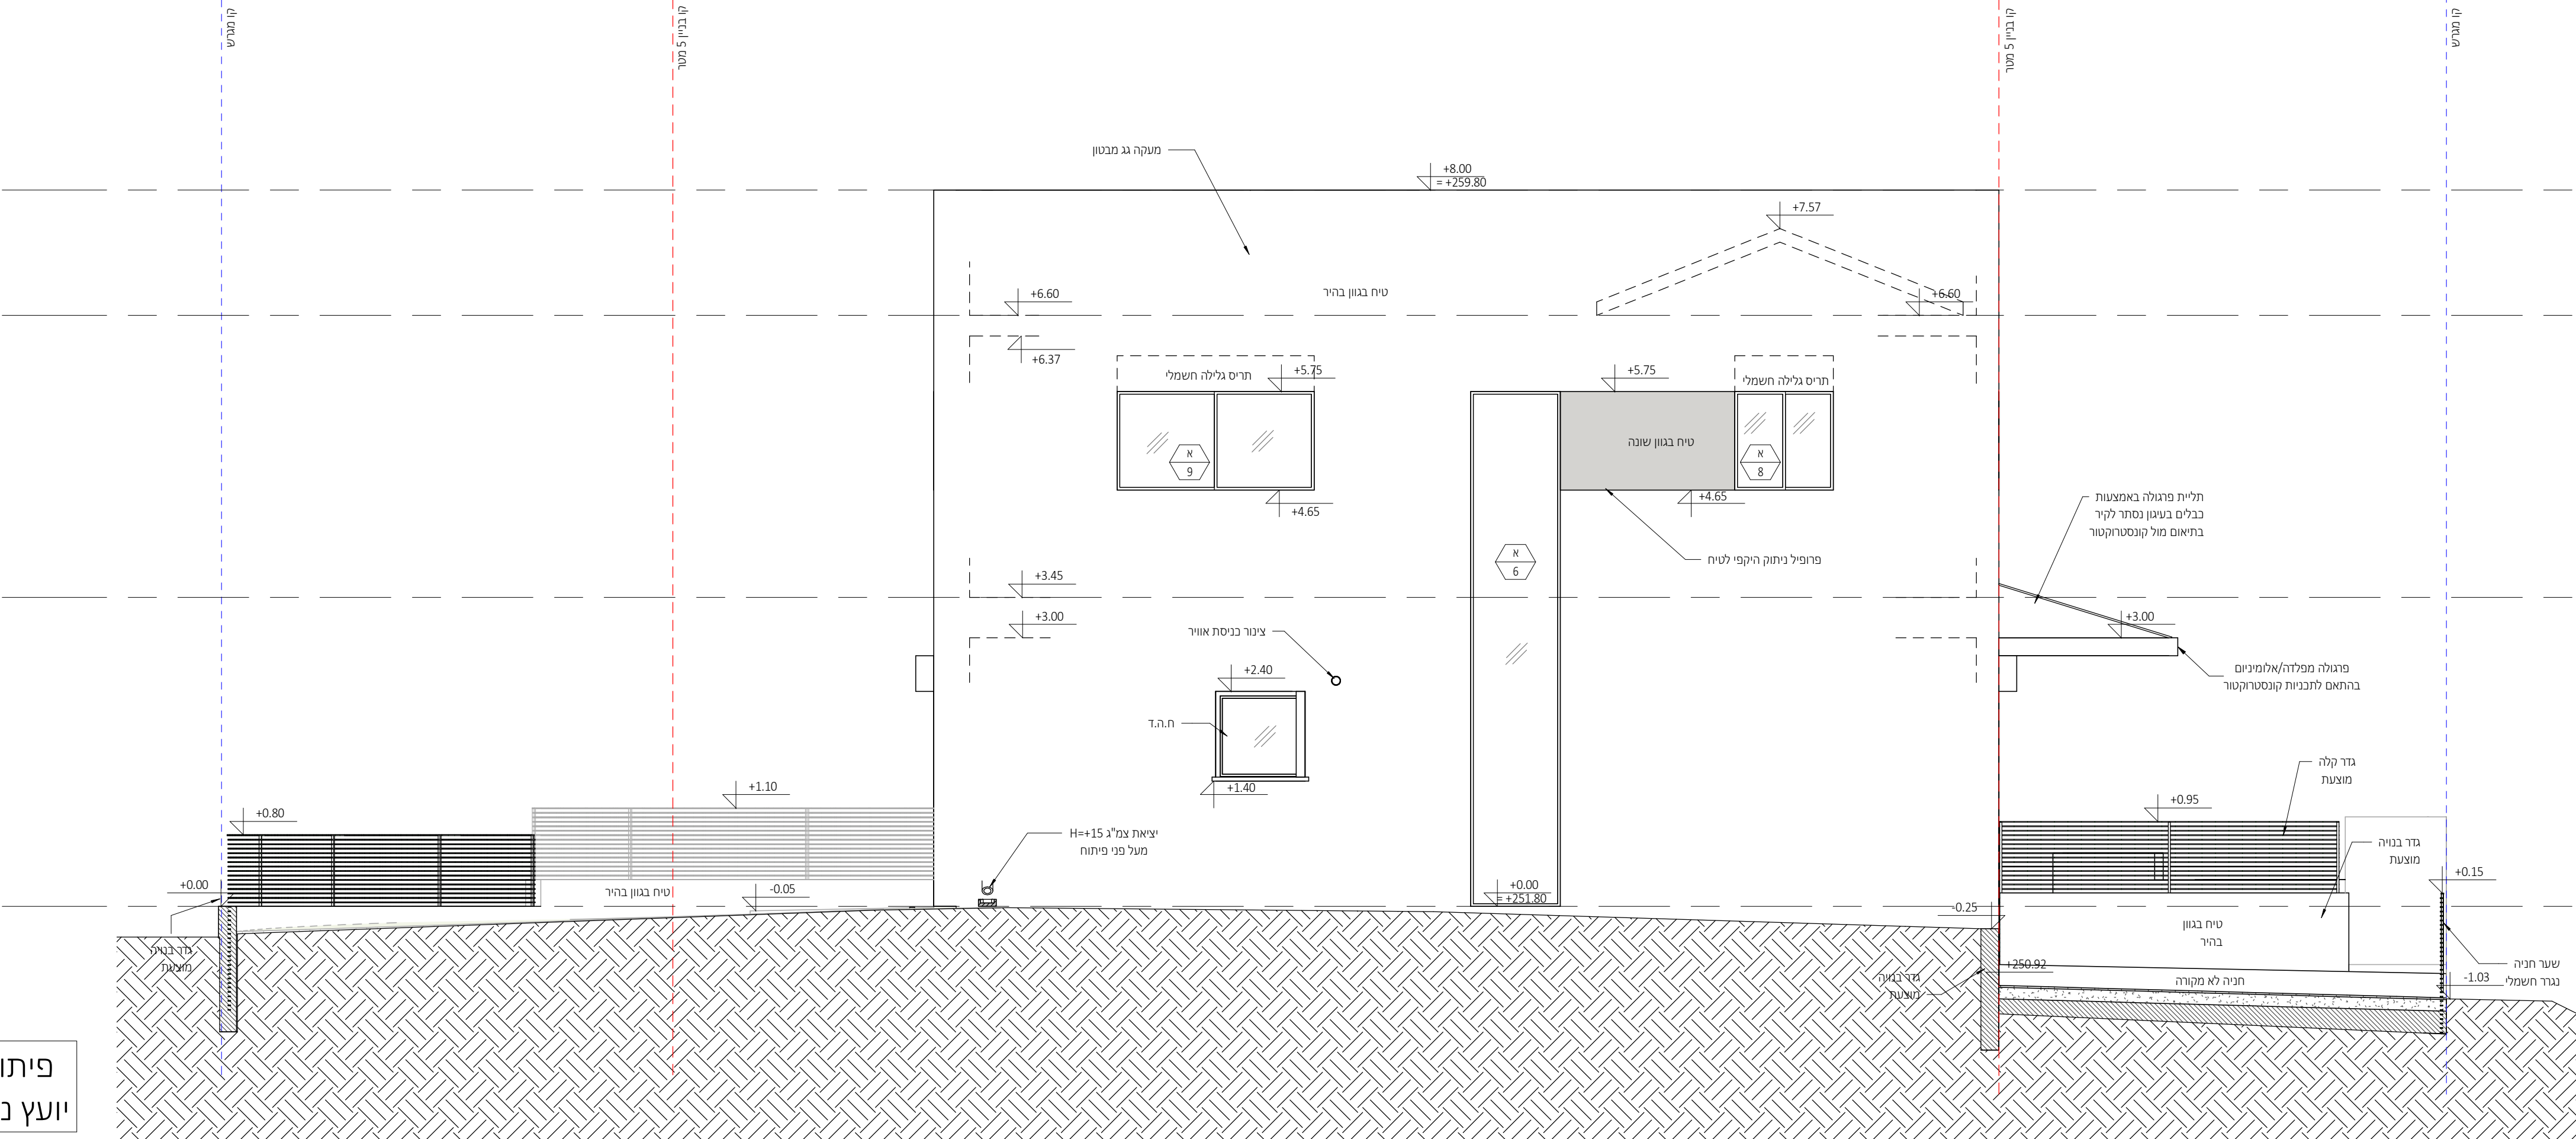

פיתוח נוף עפ"י תוכניות
יועץ נוף ראה פירוט בנפרד

חזית צפון מערבית

1 : 50

מתכננים:

ניהול פרויקט
מהיסוד - בן סולומון
פיקוח
מהיסוד - בן סולומון
קונסטרוקציה
ערן שילר
מיזוג אוויר
איוול ארז מהנדסים ויועצים בע"מ
אינסטלציה
איתן אלמסי
חשמל
איתן בסיס
אלומיניום
נוף
נתי בלוקא
חשמל חכם
חימום תת רצפתי
איטום
צבי טל
אקוסטיקה
מעליות
קרקע וביסוס
דיה הנדסת קרקע וביסוס
רישוי

± 0.00 = 251.80
הערות: 1. תכנית זו יש לקרוא יחד עם תכנית הוויסטים. 2. גובה המסלול: ראש תכנית פיתוח. 3. הפירות הן בין קירות הבניה ולא כולל פיתוח. 4. פיתוח השטח סביב המבנה, כולל, מדרגות, גדרות, שבילים, ריצופים, שטחים גזרים, חניה גג וכו' ראש תכנית פיתוח. 5. איטום קירות ורצפות המבנה כמעט עם הקרקע ובידוד תרמי לאורך העמודים והקירות למל התחתית. כלירות או עם סימני (גומי) - רא תכנית קונסטרוקציה. 6. אף דים יבוצע בכל מישור אופקי הכולל חתוכין. 7. סיוח תרמי במסד"ד - ע"פ מפרט תומקיר, מאושר ע"י פיקוח הנדסי.
המבצע אחראי למידות: עליו לבקר ולבדוק את כל המידות בתכנית ובקטע המבנה. במסגרת של מידות או אי התאמה בתכנית /או בבנין, עליו להודיע על כך מיד לאדריכל בסופו המשיך בעבודתו. המבצע יתחשב או ויק בתכנית שאושר לכיצד. המבצע יחזיק אחרא, בכל מות, של מחדש של תכנית. אין לקבוע מידות על ידי חזירה בשטח. התכנית היתה רכוש האדריכל ואין לשווק כל שימוש בה או ברעיונות הגלומים בה, אלא באישור בכתב מהאדריכל. מומנם /או יושם אשר שמו מופיע בתכנית זו, נושא לכיד באחריות המקצועית והמקצועית לתכנית. על המפקח והמבצע לודא התאמת התכנית האדריכלית "לכיצד" לתכנית. ויתר, המוכר והתכנית המאושרות ע"י כל גורמים רשמיים. התכנית כוללת את כל האחריות והידוע על ליום תחלפת.

משרד קירות:
קיר בלוק
קיר בסון
גומד בסון


תאריך	תיאור	מהדורה
22.09.2025	מכרז	1

אדריכלות
שם המסמך:
קבוצת רכישה נופיה
שם הפרויקט:
נופיה - מגרש 10
שם הגליון:
חתכים
מספר גליון:
A3-3-100
SCALE: קנה מידה: EDITION: 1 : 50
STATUS: 1
שורש ע"י: נבדק ע"י: למכרז
תאריך: 22.09.2025

NeumanHaynerArchitects
נירסן חיינר אדריכלים מודל התודות 2, בית חירות 09-954642 78
office@nh-arch.com www.nh-arch.com
זכויות יוצר / ע"פ הנחיות ע"ד


פיתוח נוף עפ"י תוכניות
יועץ נוף ראה פירוט בנפרד

פיתוח נוף עפ"י תוכניות
יועץ נוף ראה פירוט בנפרד

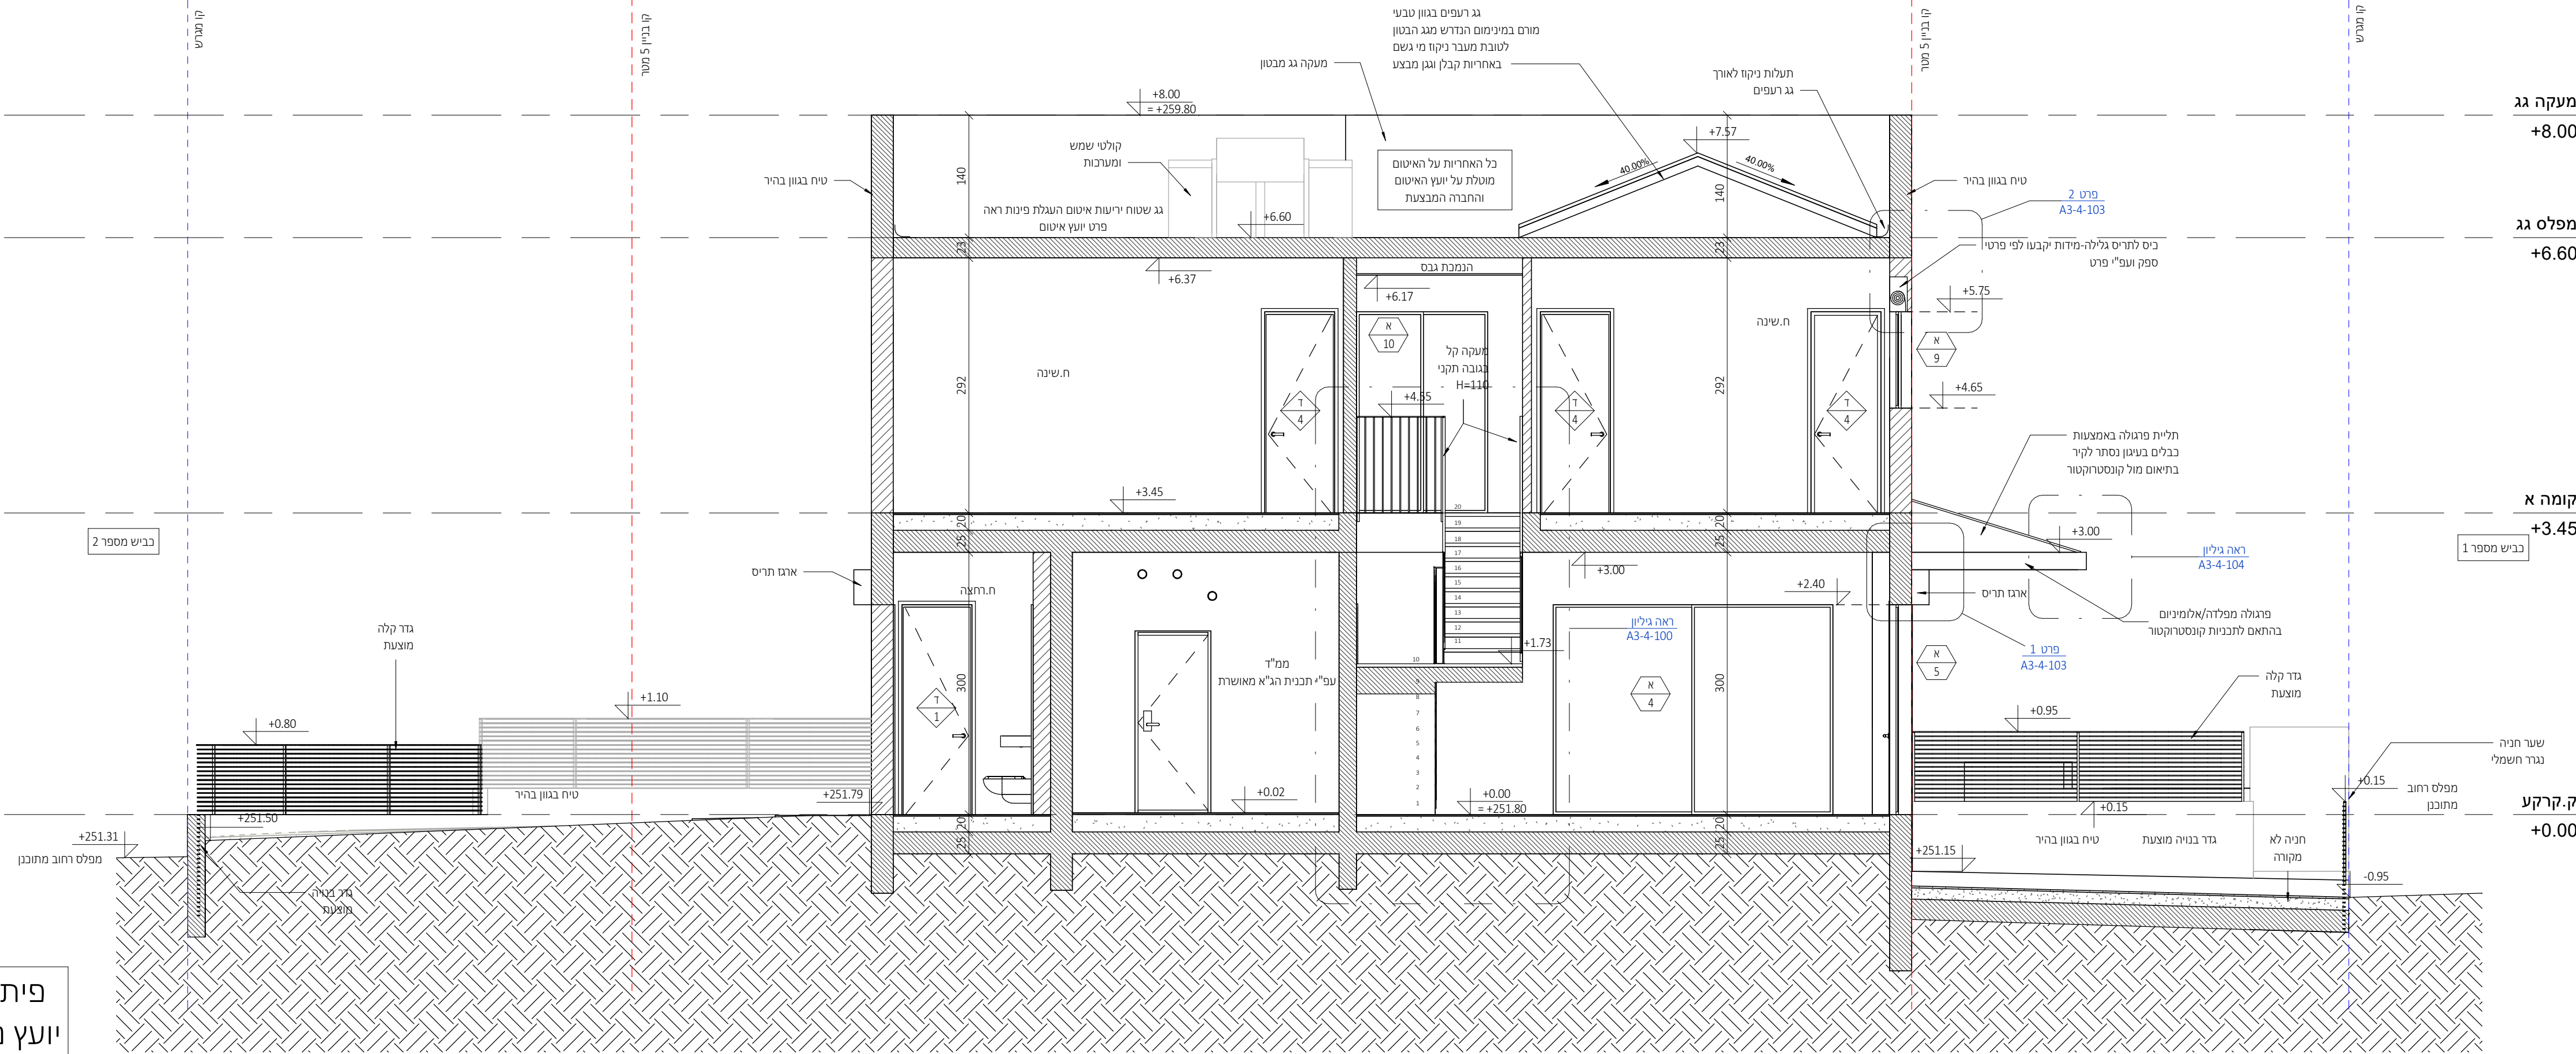

חתך א-א

1 : 50

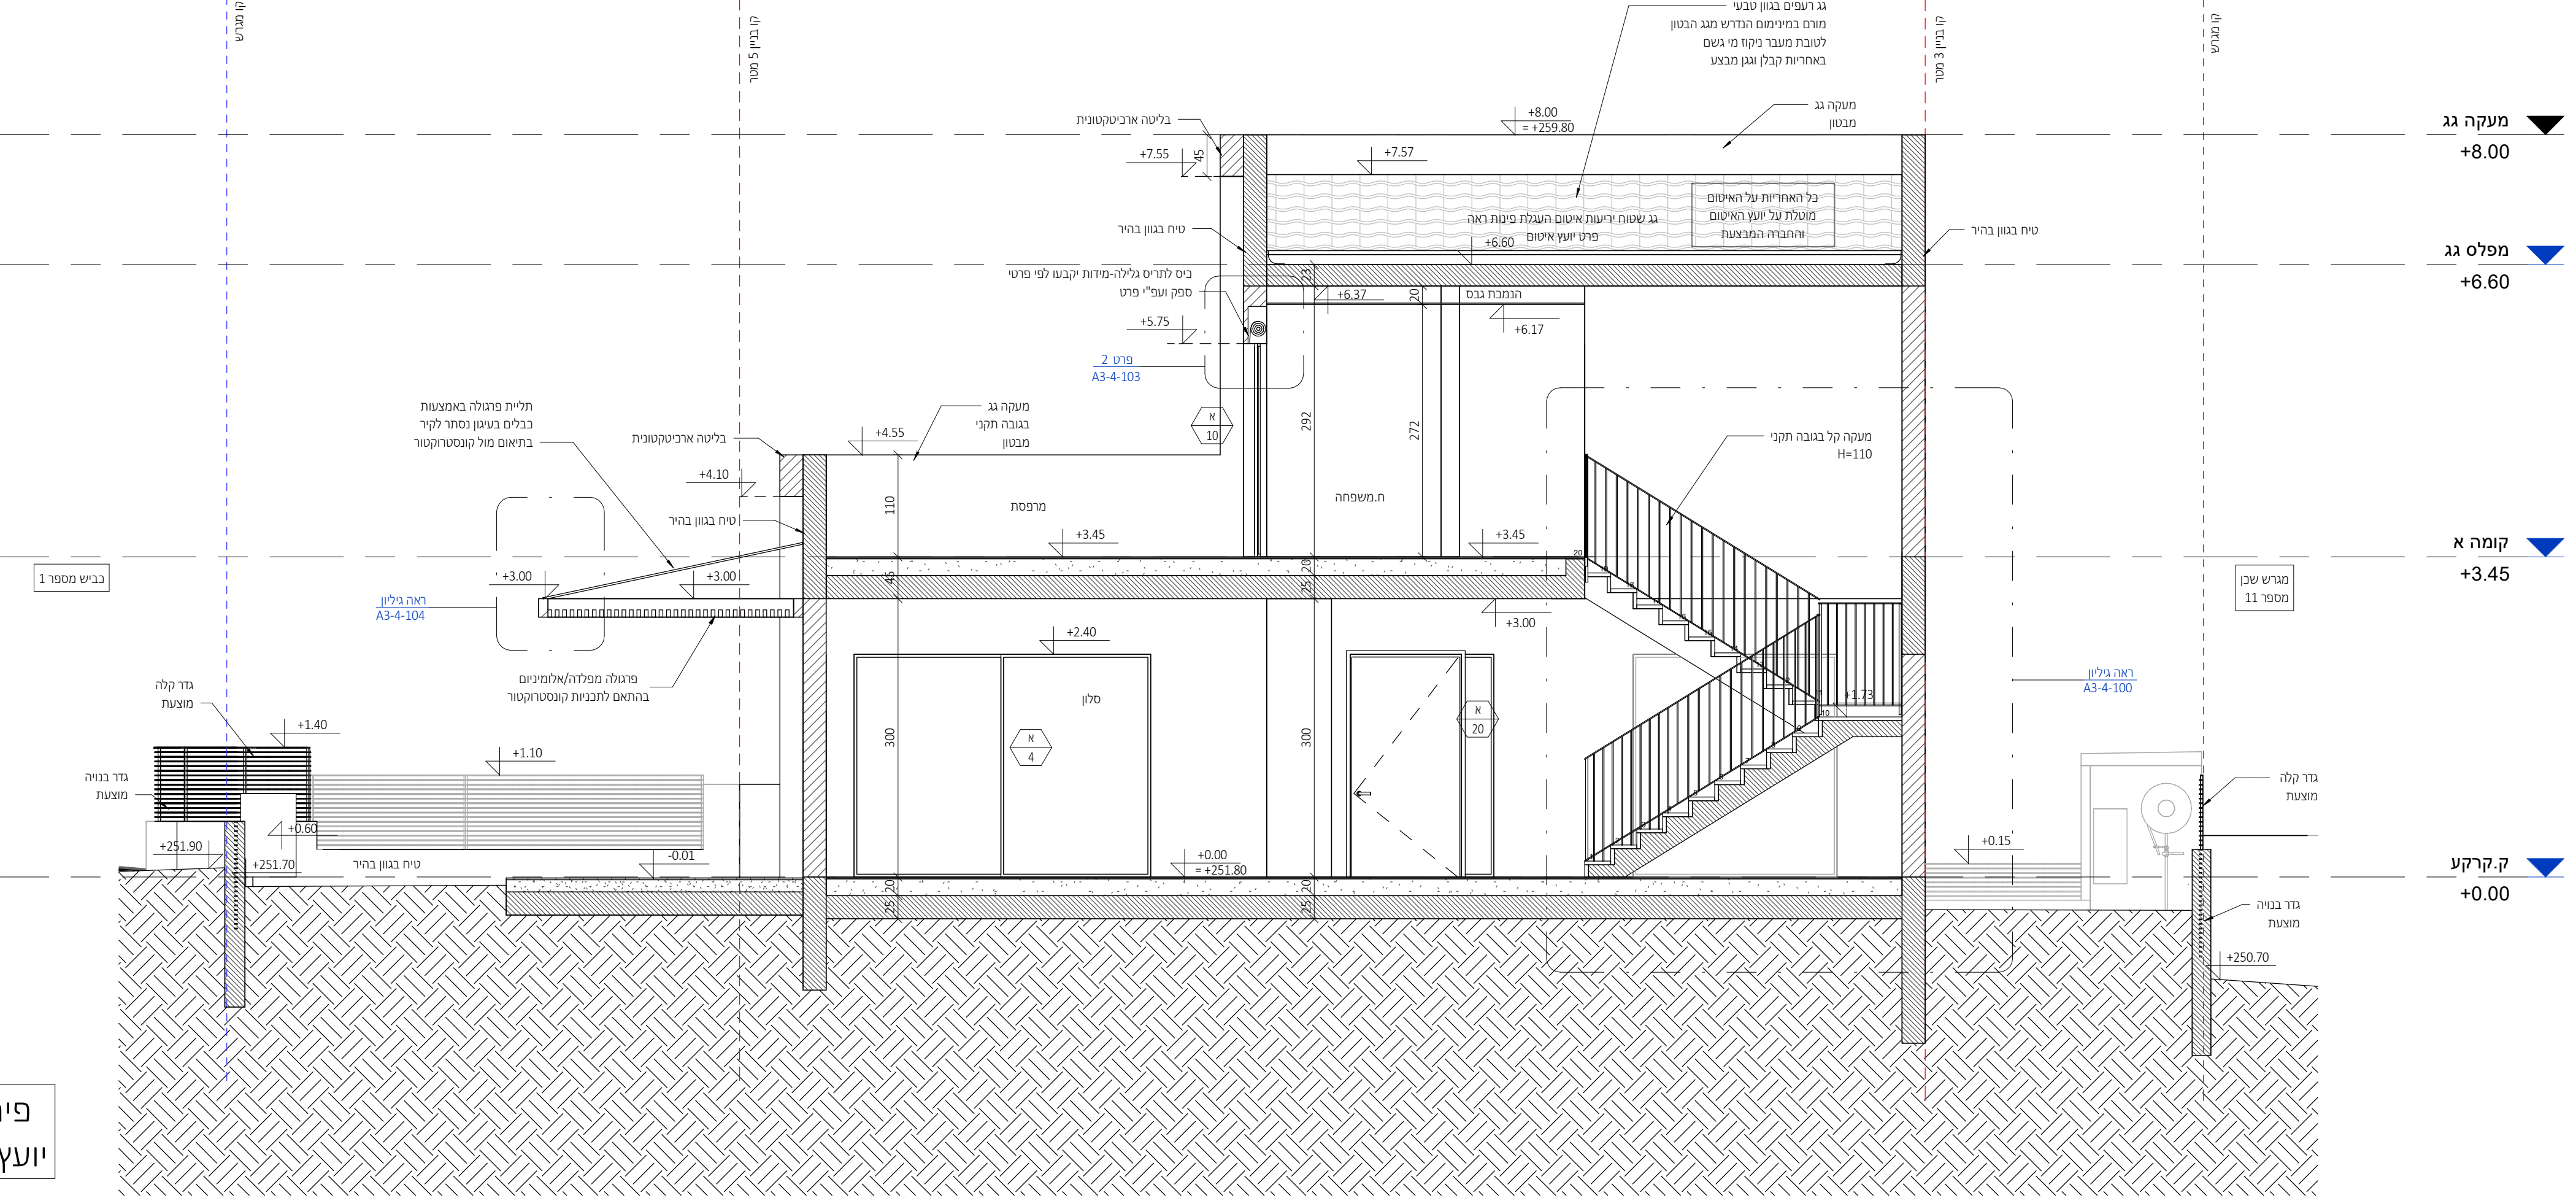

חתך ב-ב

1 : 50

מתכננים:

ניהול פרויקט
מהיסוד - בן סולומון
פיקוח
מהיסוד - בן סולומון
קונסטרוקציה
ערן שילר
מיזוג אוויר
אייל ארז מהנדסים ויועצים בע"מ
אינסטליציה
איתן אלמסי
חשמל
איתן בסיס
אלומיניום
בופ
נתי בלוקא
חשמל חכם
חימום תת רצפתי
איטום
צבי טל
אקוסטיקה
מעליות
קרקע וביסוס
דיה הנדסת קרקע וביסוס
רישוי


± 0.00 = 251.80
הערות: 1. תכנית זו יש לקרוא יחד עם תכנית הוויסטים. 2. גובה אבסולוטי - ראו תכנית פיתוח. 3. הפרדות הן בין קירות הבניה ולא כולל פיתוח. 4. פיתוח השטח סביב הבניה, כולל, מדרגות, גגות, שנילים, ריצופים, שטחים בגובה, חללי גג וראו תכנית פיתוח. 5. איסוס קירות ורצפות הבניה כמנוע עם הקרקע ובנידוד תחסי לאזור העומדים בהקשרות של מדרגות - לפרטים ראו תכנית קונסטרוקציה. 6. איף מים יבוצע בכל מישור אופקי הכולל מהבנין. 7. פיתוח תחסי במסגרת - ע"פ מפרט ותומקור, מאפשר ע"י פיקוד העורף. הבנייה והבניה אחראי לסידור: עליו לבקר ולבדוק את כל המידות בתכנית ובקטע המבנה. במסגרת של שטח או אי התאמה בתכנית /או בבנין, עליו להודיע על כך מיד לאדריכל בסופו המשיך בעבודתו. המבנה יושמש או ויק בתכנית שאפשר לציין. המבנה יחזיק במהלך כלל של, של מדרגות של תכנית. אין לקבוע מידות על ידי חזירה בשטח. התכנית הנה רכוש האדריכל ואין לשנות כל שימוש בה או ברעיונות הגלומים בה, אלא באישור בכתב מהאדריכל. מחנכים והתקנים לתכנית. על המפתח והמכלול לזרז את התאמת התכנית האדריכלית "לביצוע" תכנית כוללת את כל התאמותיה והודיע על ליום תחלפת.

משרד קירות:
קיר בלוק קיר בסון מנדוב בסון

תאריך	תיאור	מהדורה
22.09.2025	מכרז	1


אדריכלות		
CLIENT NAME:	המחזיק:	
קבוצת רכישה נופיה		
PROJECT NAME:	הפרויקט:	
נופיה - מגרש 10		
DRAWING NAME:	התוכנית:	
גליון מדרגות		
SHEET NUMBER:	מספר גליון:	
A3-4-100		
SCALE:	קנה מידה:	
As indicated	EDITION: דור: 1	
STATUS:		000000
למכר		
	מבוק ע"י:	מסמך ע"י:
DATE:	22.09.2025	יור:

NeumanHaynerArchitects
נירסון חיינר אדריכלים מנכ"ל והנדס 2, בית חירות 09-954642 70
office@nh-arch.com www.nh-arch.com
זכויות יוצר / ע"פ הגנת ע"ד

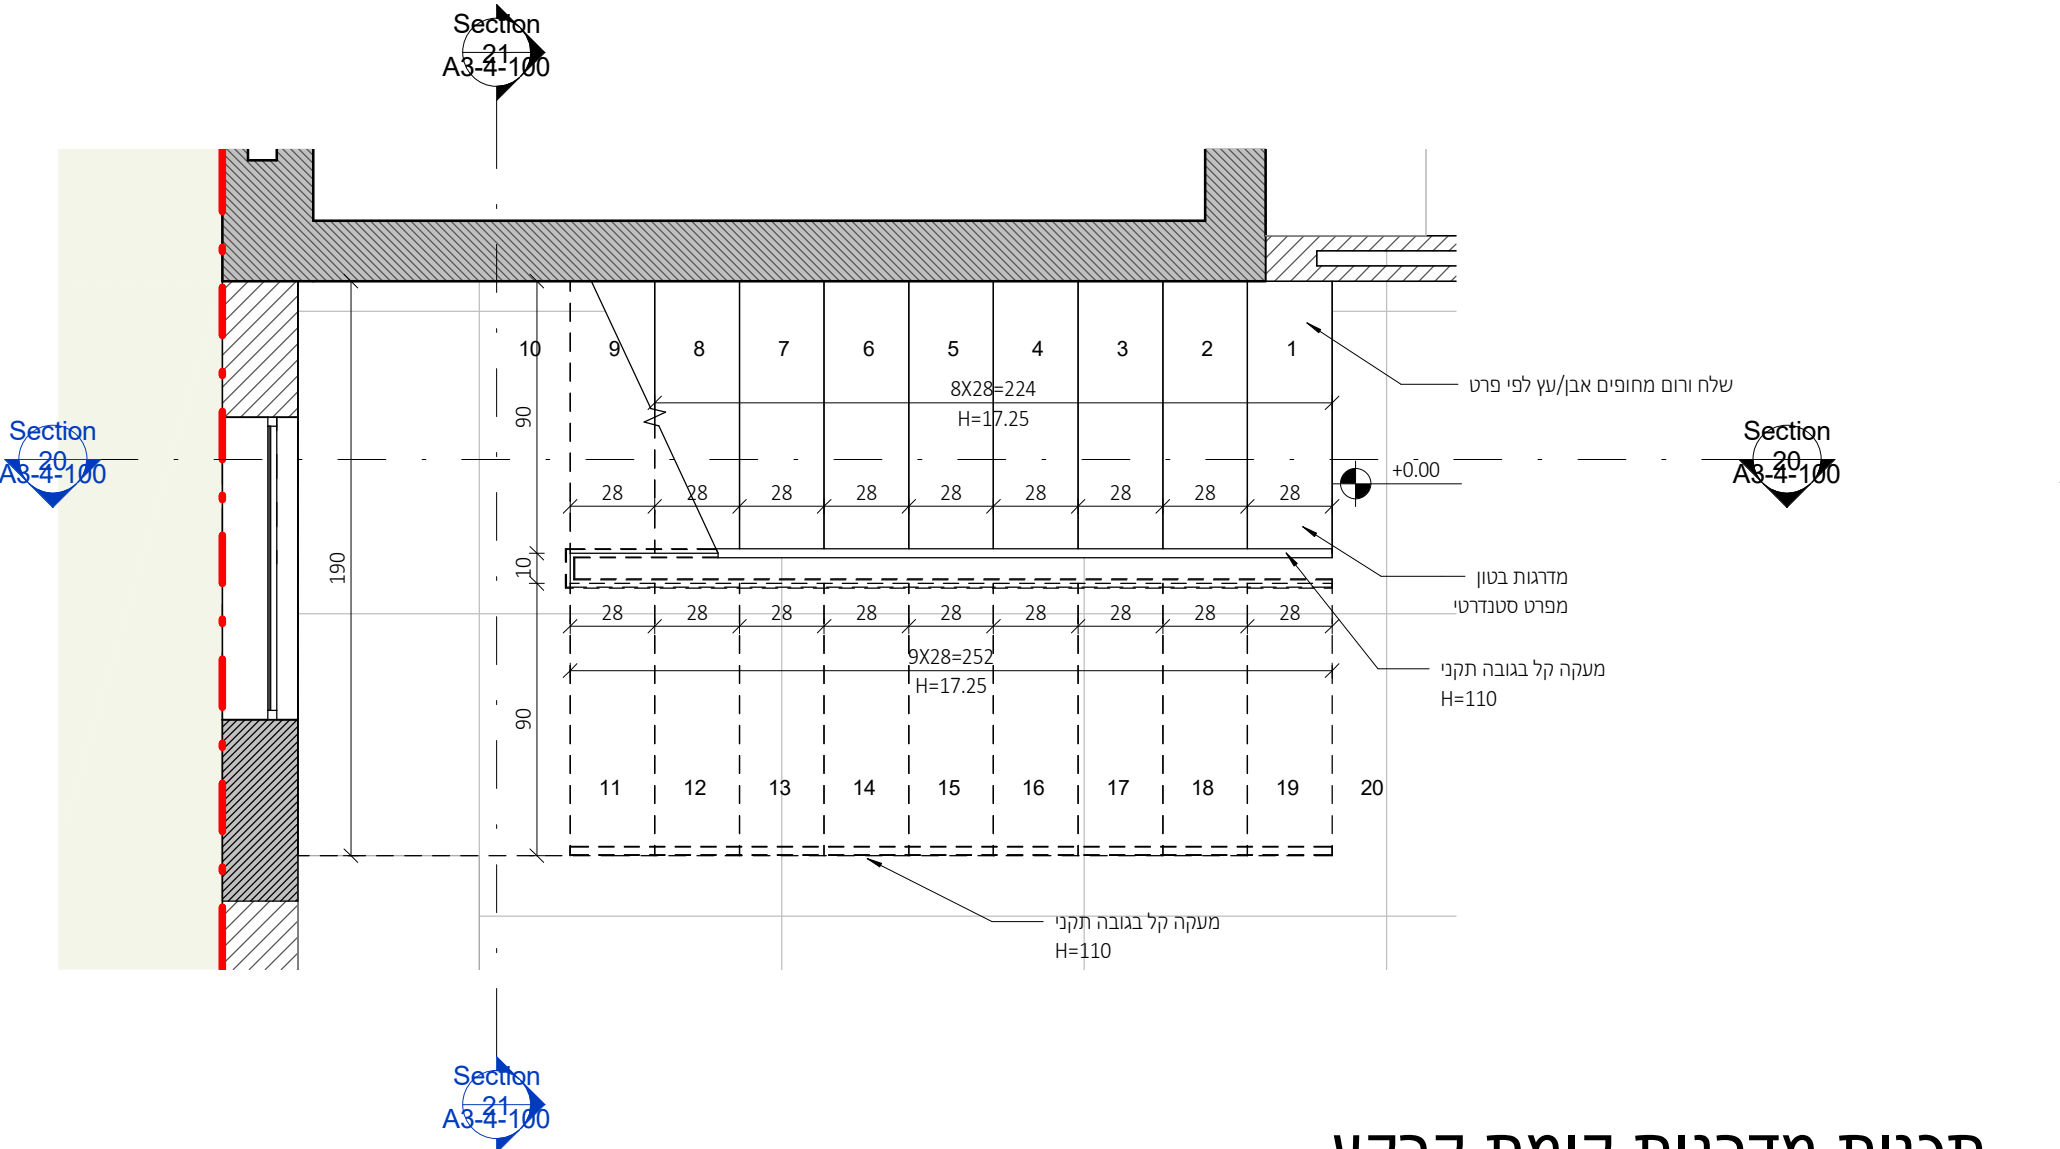


תכנית מדרגות קומת קרקע

1 : 25

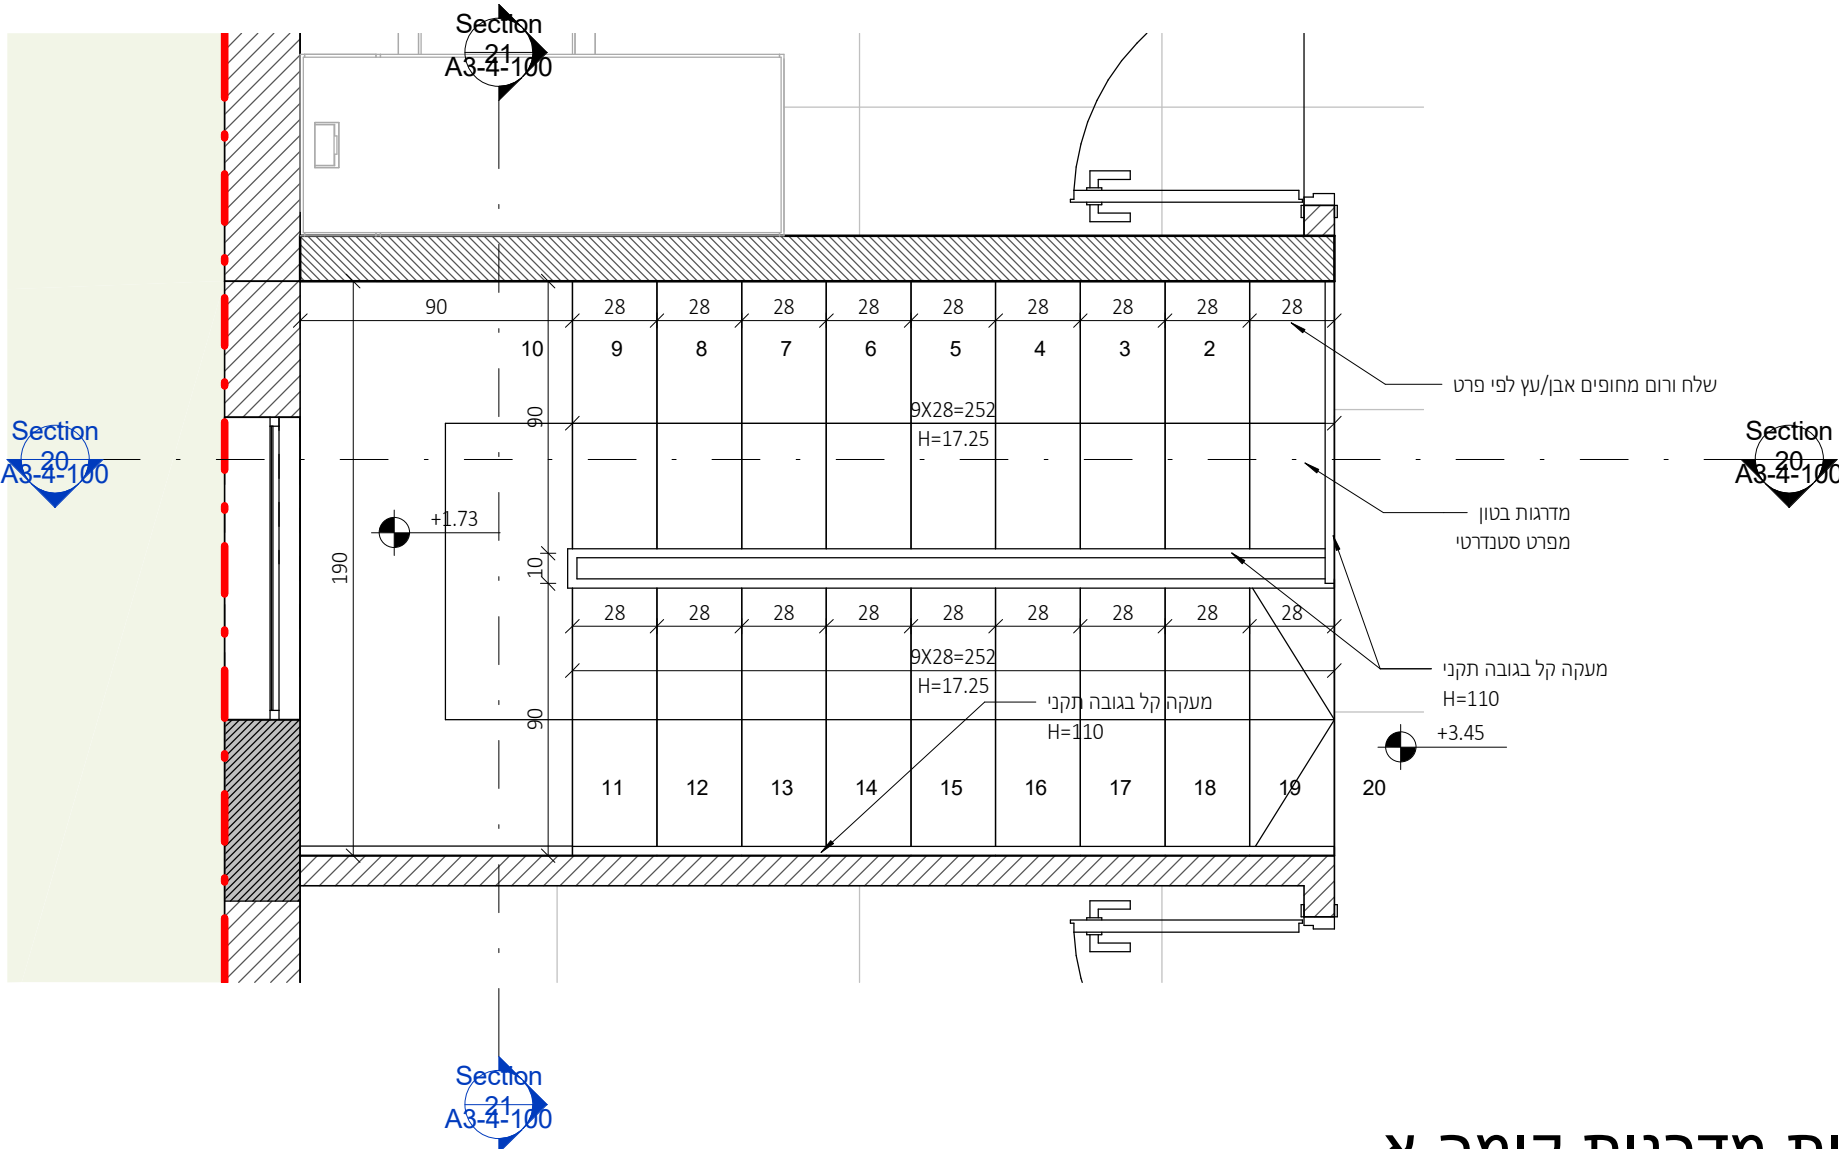

תכנית מדרגות קומה א

1 : 25

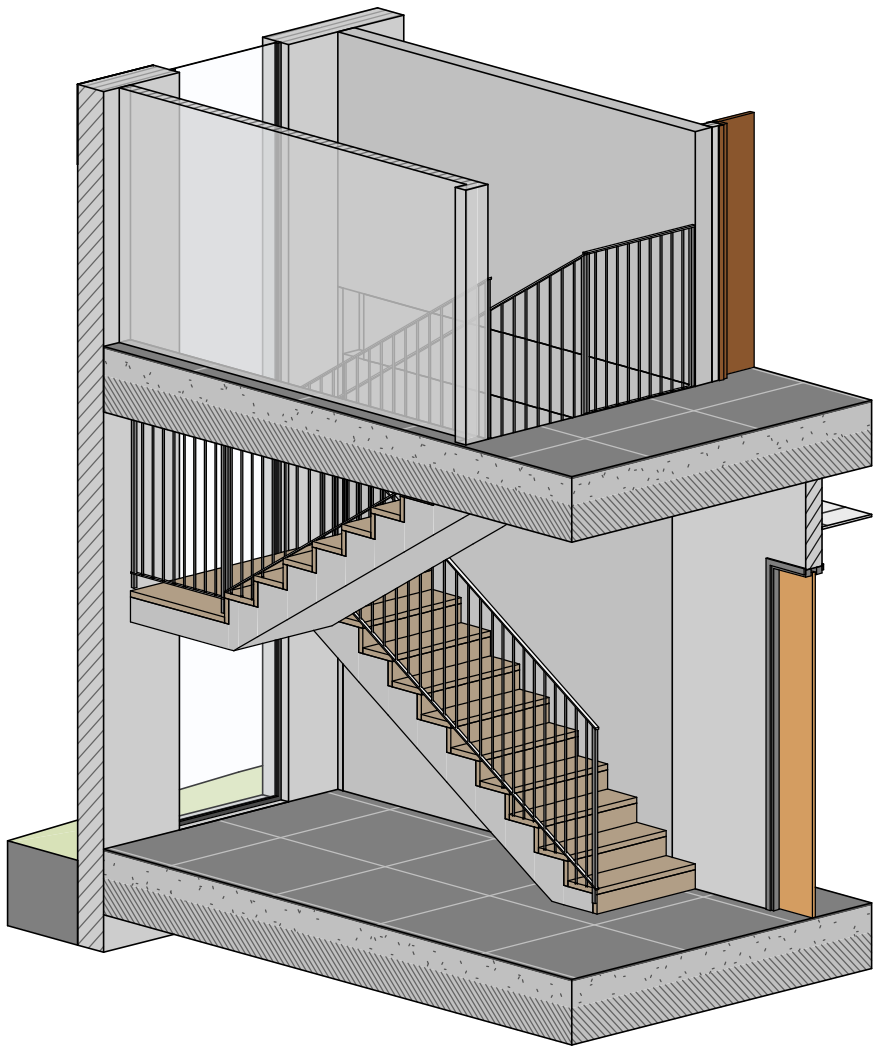

להמשך תיאום

דגם נבחר


מדרגות סטנדרטיות - מפרט סטנדרטי

על הקבלן לשלוח S.D לאישור אדריכל

יש לבצע התאמה לפרט לאחר בחירת חיפוי המדרגות*




תמונה להמחשה בלבד

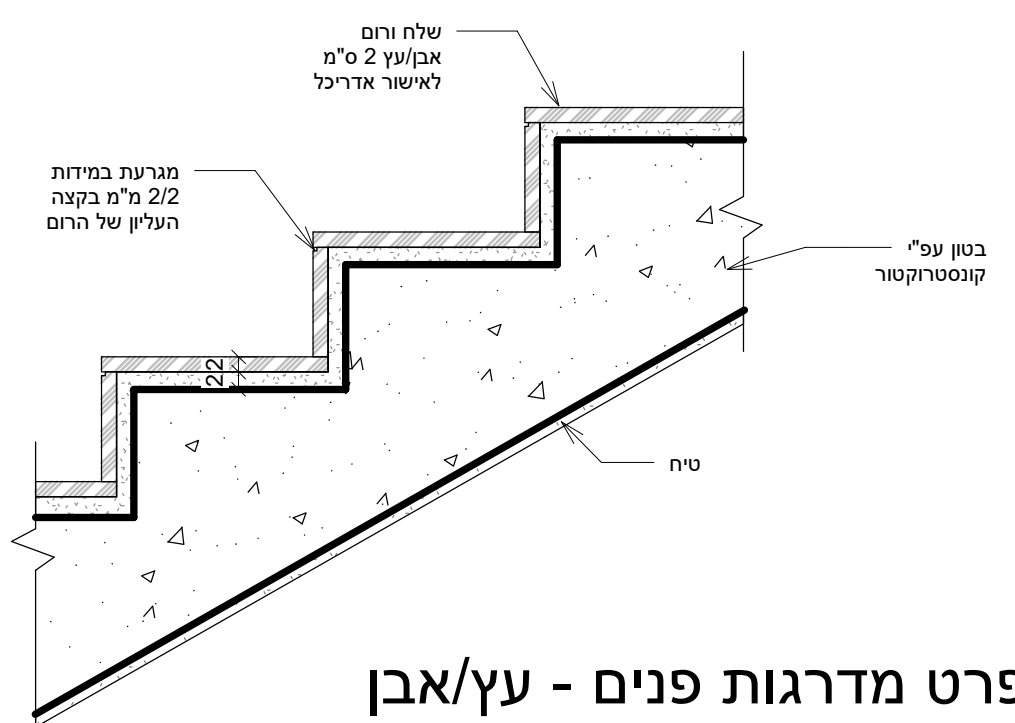


פרט מדרגות פנים - עץ/אבן

1 : 10

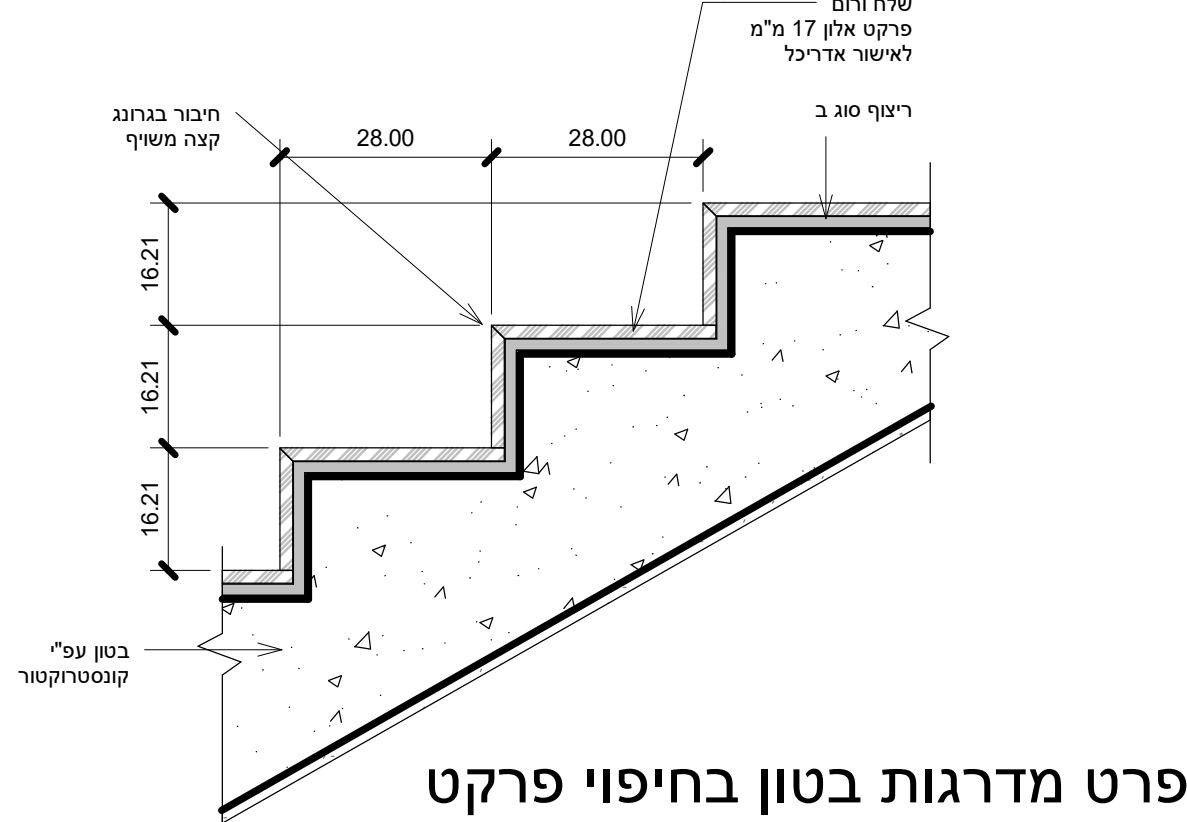



פרט מדרגות בטון בחיפוי פרקט

1 : 10

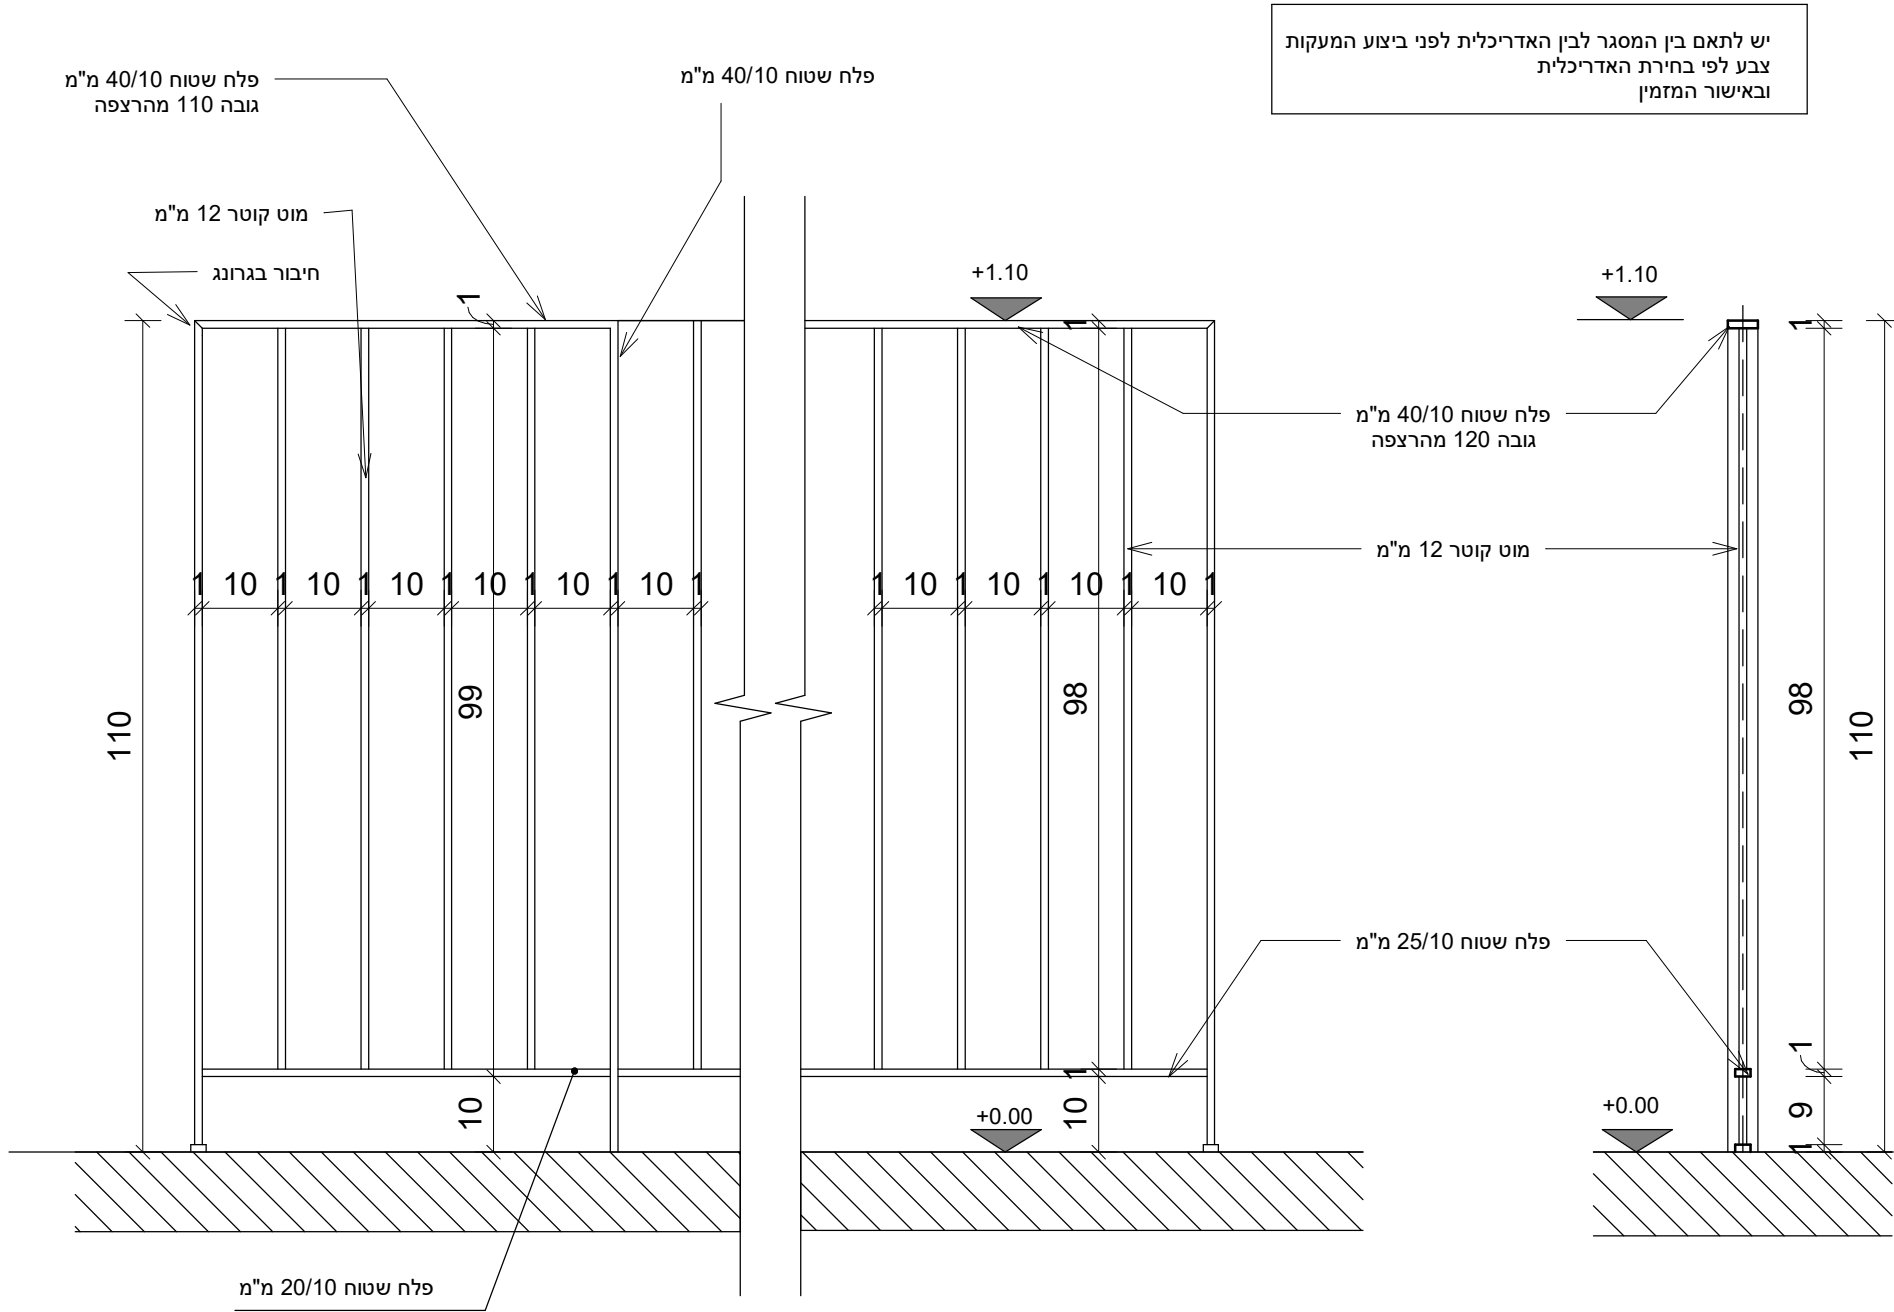

מעקה אנכי

1 : 10

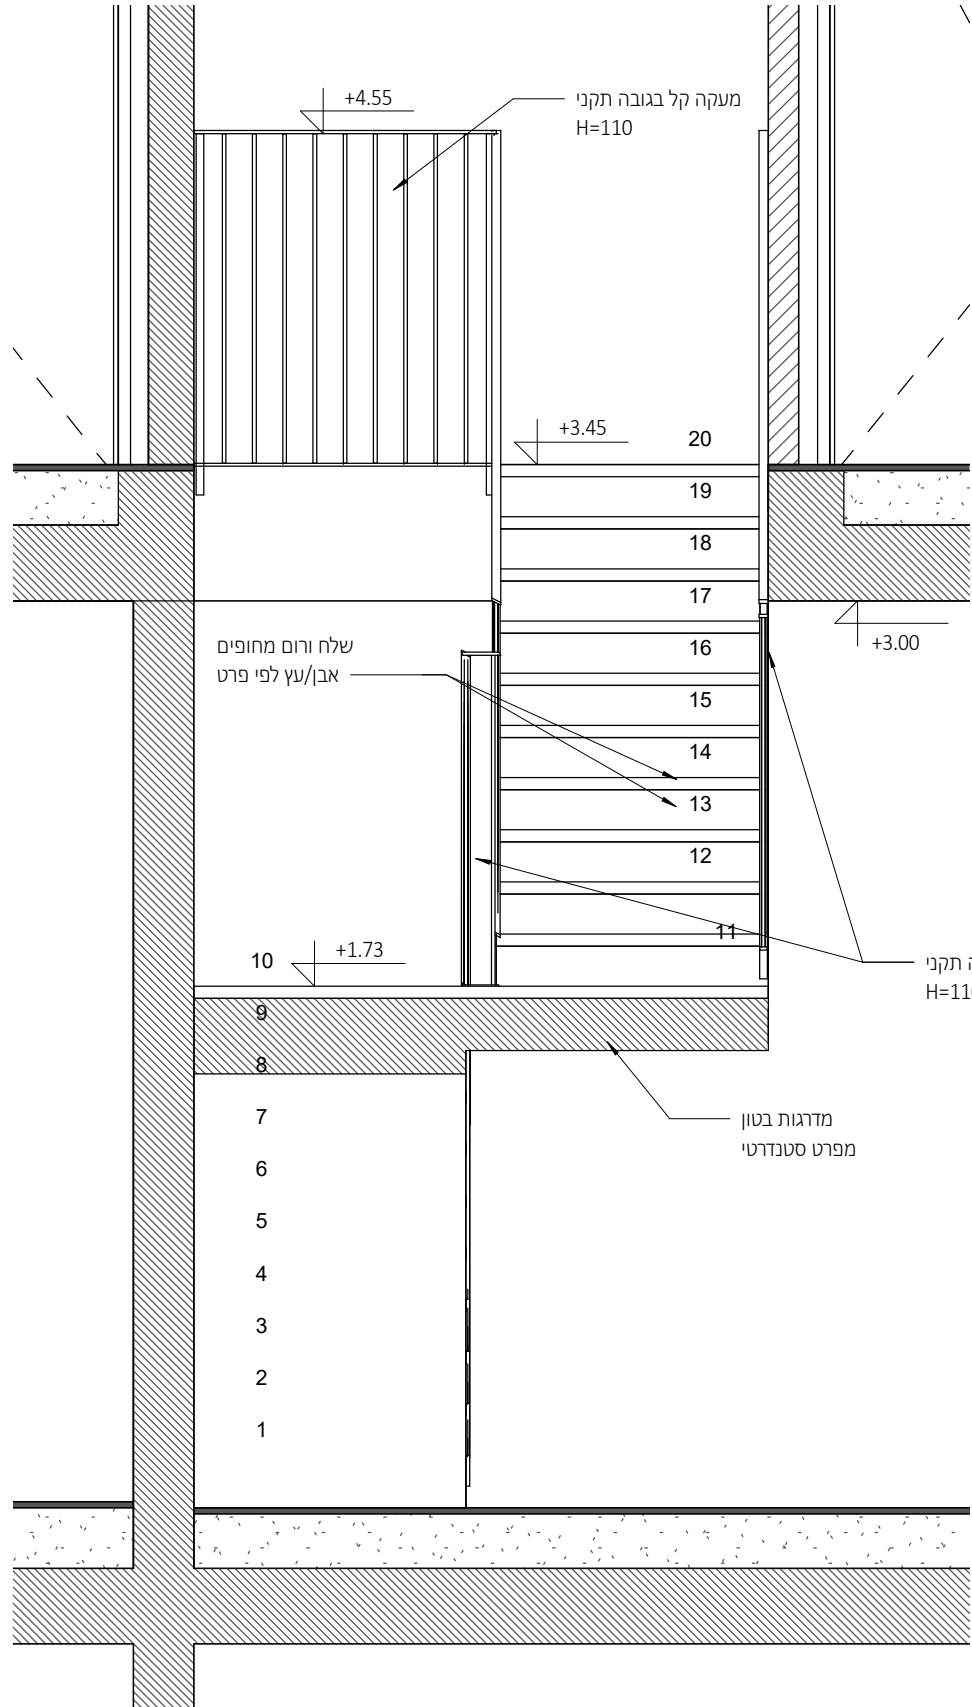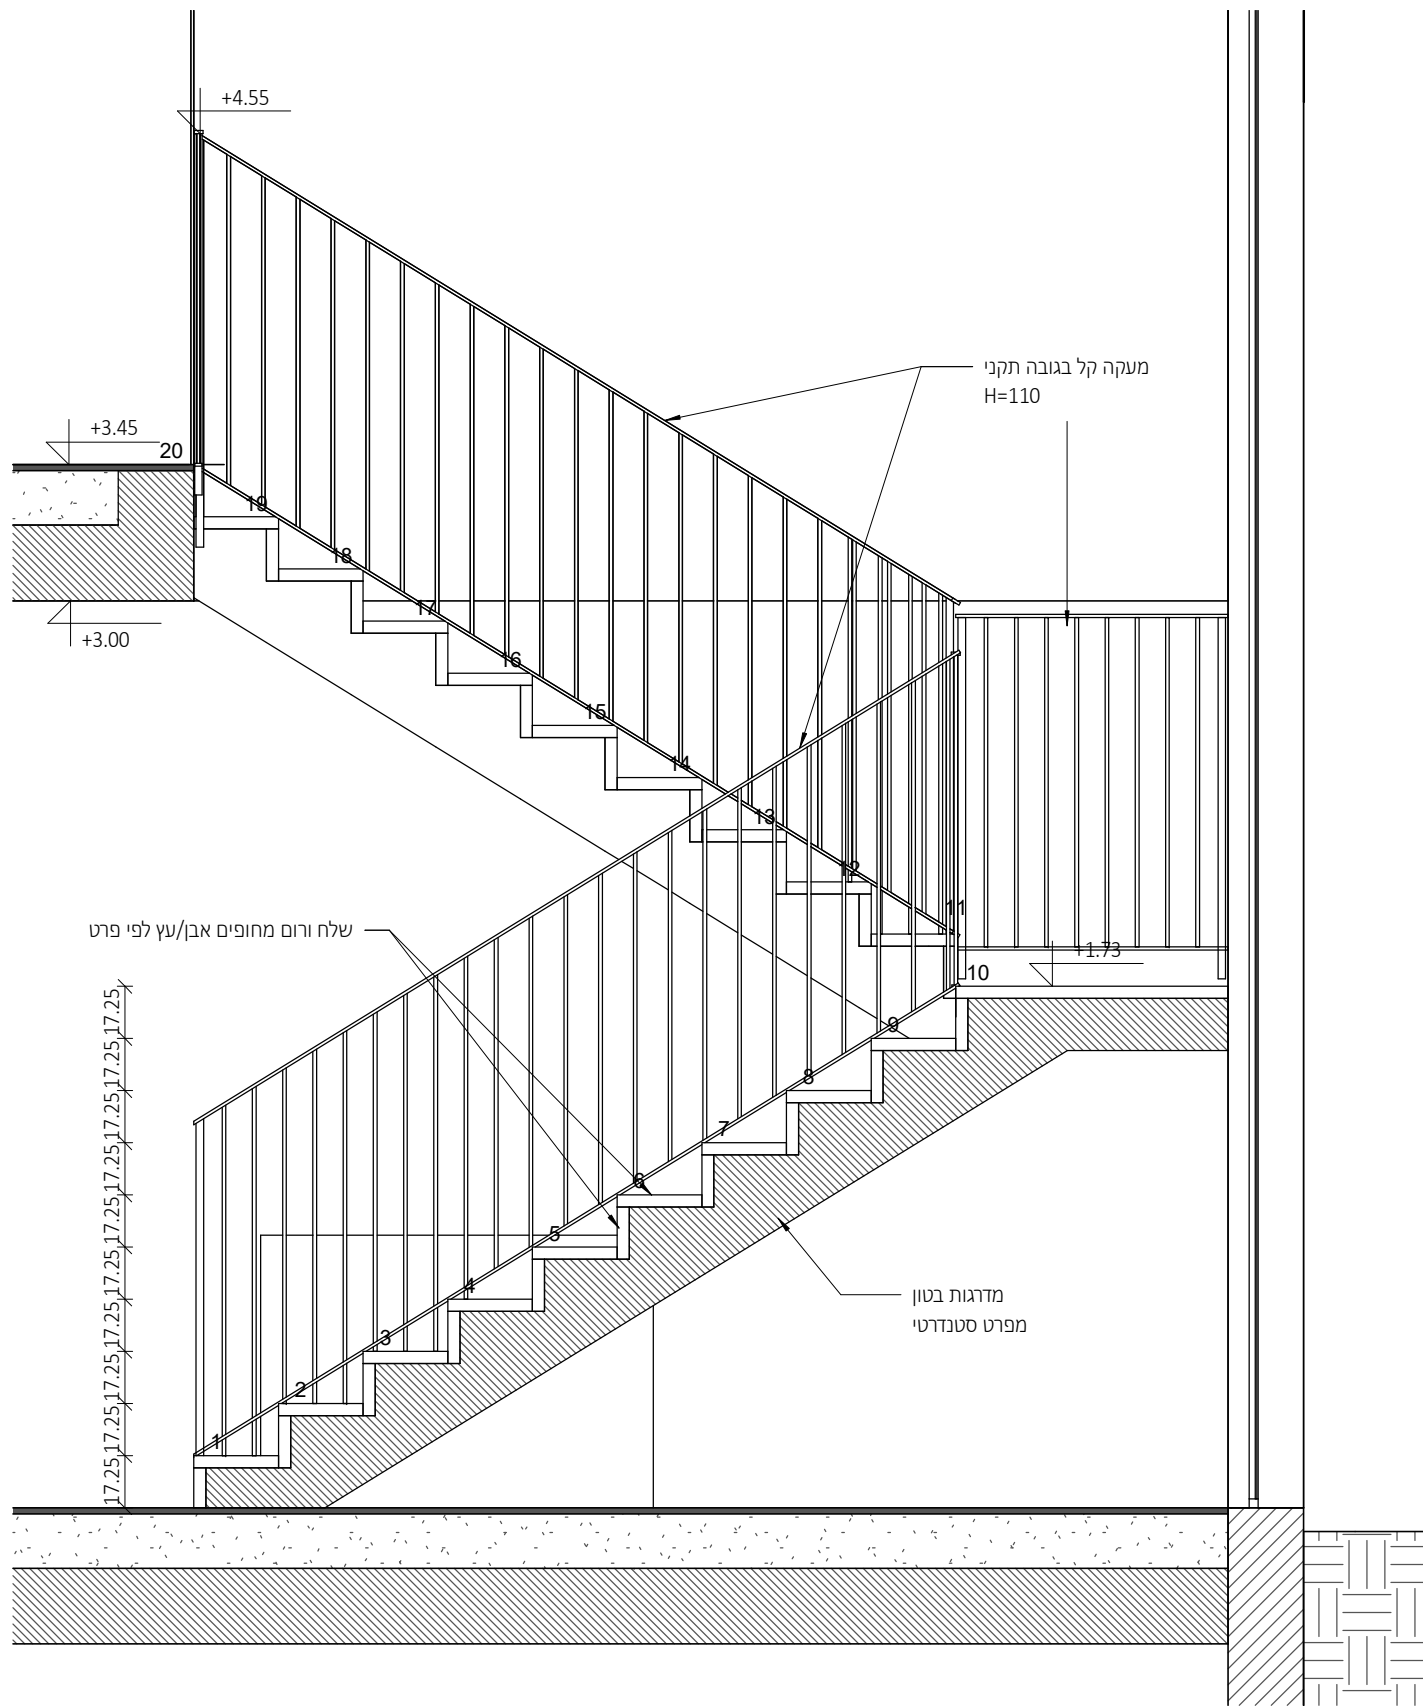

Section 20

1 : 25

Section 21

1 : 25

מתכננים:

ניהול פרויקט
מהיסוד - בן סולומון
פיקוח
מהיסוד - בן סולומון
קונסטרוקציה
ערן שילר
מיזוג אוויר
אייל ארז מהנדסים ויועצים בע"מ
אינסטליציה
איתן אלמסי
חשמל
איתן בסיס
אלומיניום
בופ
נתי בלוקא
חשמל חכם
חימום תת רצפתי
איטום
צבי טל
אקוסטיקה
מעליות
קרקע וביסוס
דיה הנדסת קרקע וביסוס
רישוי

± 0.00 = 251.80
הערות: 1. תכנית זו הי' לקרא יחד עם תכנית הרושפים. 2. גובה אבסולוטי: ראו תכנית פיתוח. 3. הפירות הן בין קירות הבניה ולא כולל פחים. 4. פיתוח השטח סביב הבנוה, כולל, מדרגות, גדרות, שבילים, ריצופים, שטחים גרושים, חניה וגן וראו תכנית פיתוח. 5. איטום קירות ורצפות הבנוה כמנוע עם הקרקע ובידוד תרמי לאורך העמודים והקירות ופול פתחות: כליות או עם סימני גימון- ראו תכנית קונסטרוקציה. 6. אף דום יבוצע בכל מישור אופקי הבולם סתגון. 7. פוח תרמי במגיד- ע"פ מפרט תומקיר, מאפשר ט"י פיקוד העודף.
המבצע אחראי לסידות : עליו לבקר ולבדוק את כל המידות בתכנית ובמקום המבנוה. במסגרת של מידות או אי התאמה בתכנית /או בבנוי, עליו להודיע על כך מיד לאדריכל בסופם המשיך בעבודותיו. המבצע יתחשב אך ורק בתכנית שאושרו לכניסו. המבצע יחזיק באחר, בכל מה, של משרדו של תכנית. את לקבוע מידות על ידי חדיה בשושים התכנית הנה רכוש האדריכל ואין לשנות כל שימוש בה או ברעיונות הגלומים בה, אלא באישור בכתב מהאדריכל. מחדם /או יושב אשר שמו רשום בתכנית זו, נושא לכיד באחריות המקצועית והתקנית לתכנית. על המפקח והמבצע לודא התאמת התכנית האדריכלית "כניסו" לתכנית יחידה, המכר והתכנית המאושרות ע"י כל גורמים הרשמיים. התכנית כוללת את כל האמצעים והדגם עד ליום תחליתה.

משרד קירות:
ממזג בספן קיר בלוק קיר בספן

תאריך	תיאור	מהדורה
22.09.2025	מכרז	1

אדריכלות	
המסמך:	CLIENT NAME:
קבוצת רכישה נופיה	
הפרויקט:	PROJECT NAME:
נופיה - מגרש 10	
הגליון:	DRAWING NAME:
פריסות חדרי רחצה - קרקע	
מספר גליון:	SHEET NUMBER:
A3-4-300	
מחזוריה:	EDITION:
קנה מידה:	SCALE:
1 : 25	
שטחים	STATUS:
למכרז	
שטח ע"י:	בגד ע"י:
תאריך:	DATE:
22.09.2025	


NeumanHaynerArchitects

נירסן חיינר אדריכלים
מודל החדרים 2, בית חירות
09-954642 70

office@nh-arch.com
www.nh-arch.com


22/09/2025 15:53:58

זכויות יימור / ע"פ הנחיות ע"ד

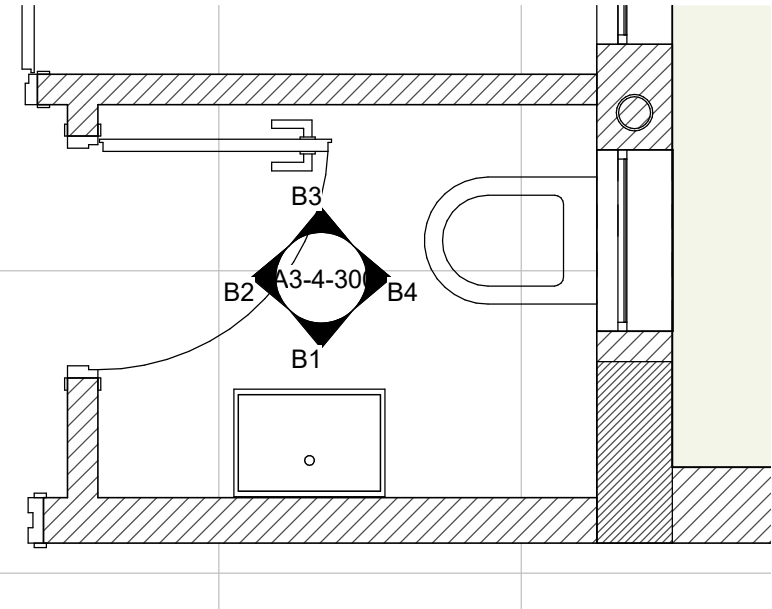

שירותי אורחים

1 : 25

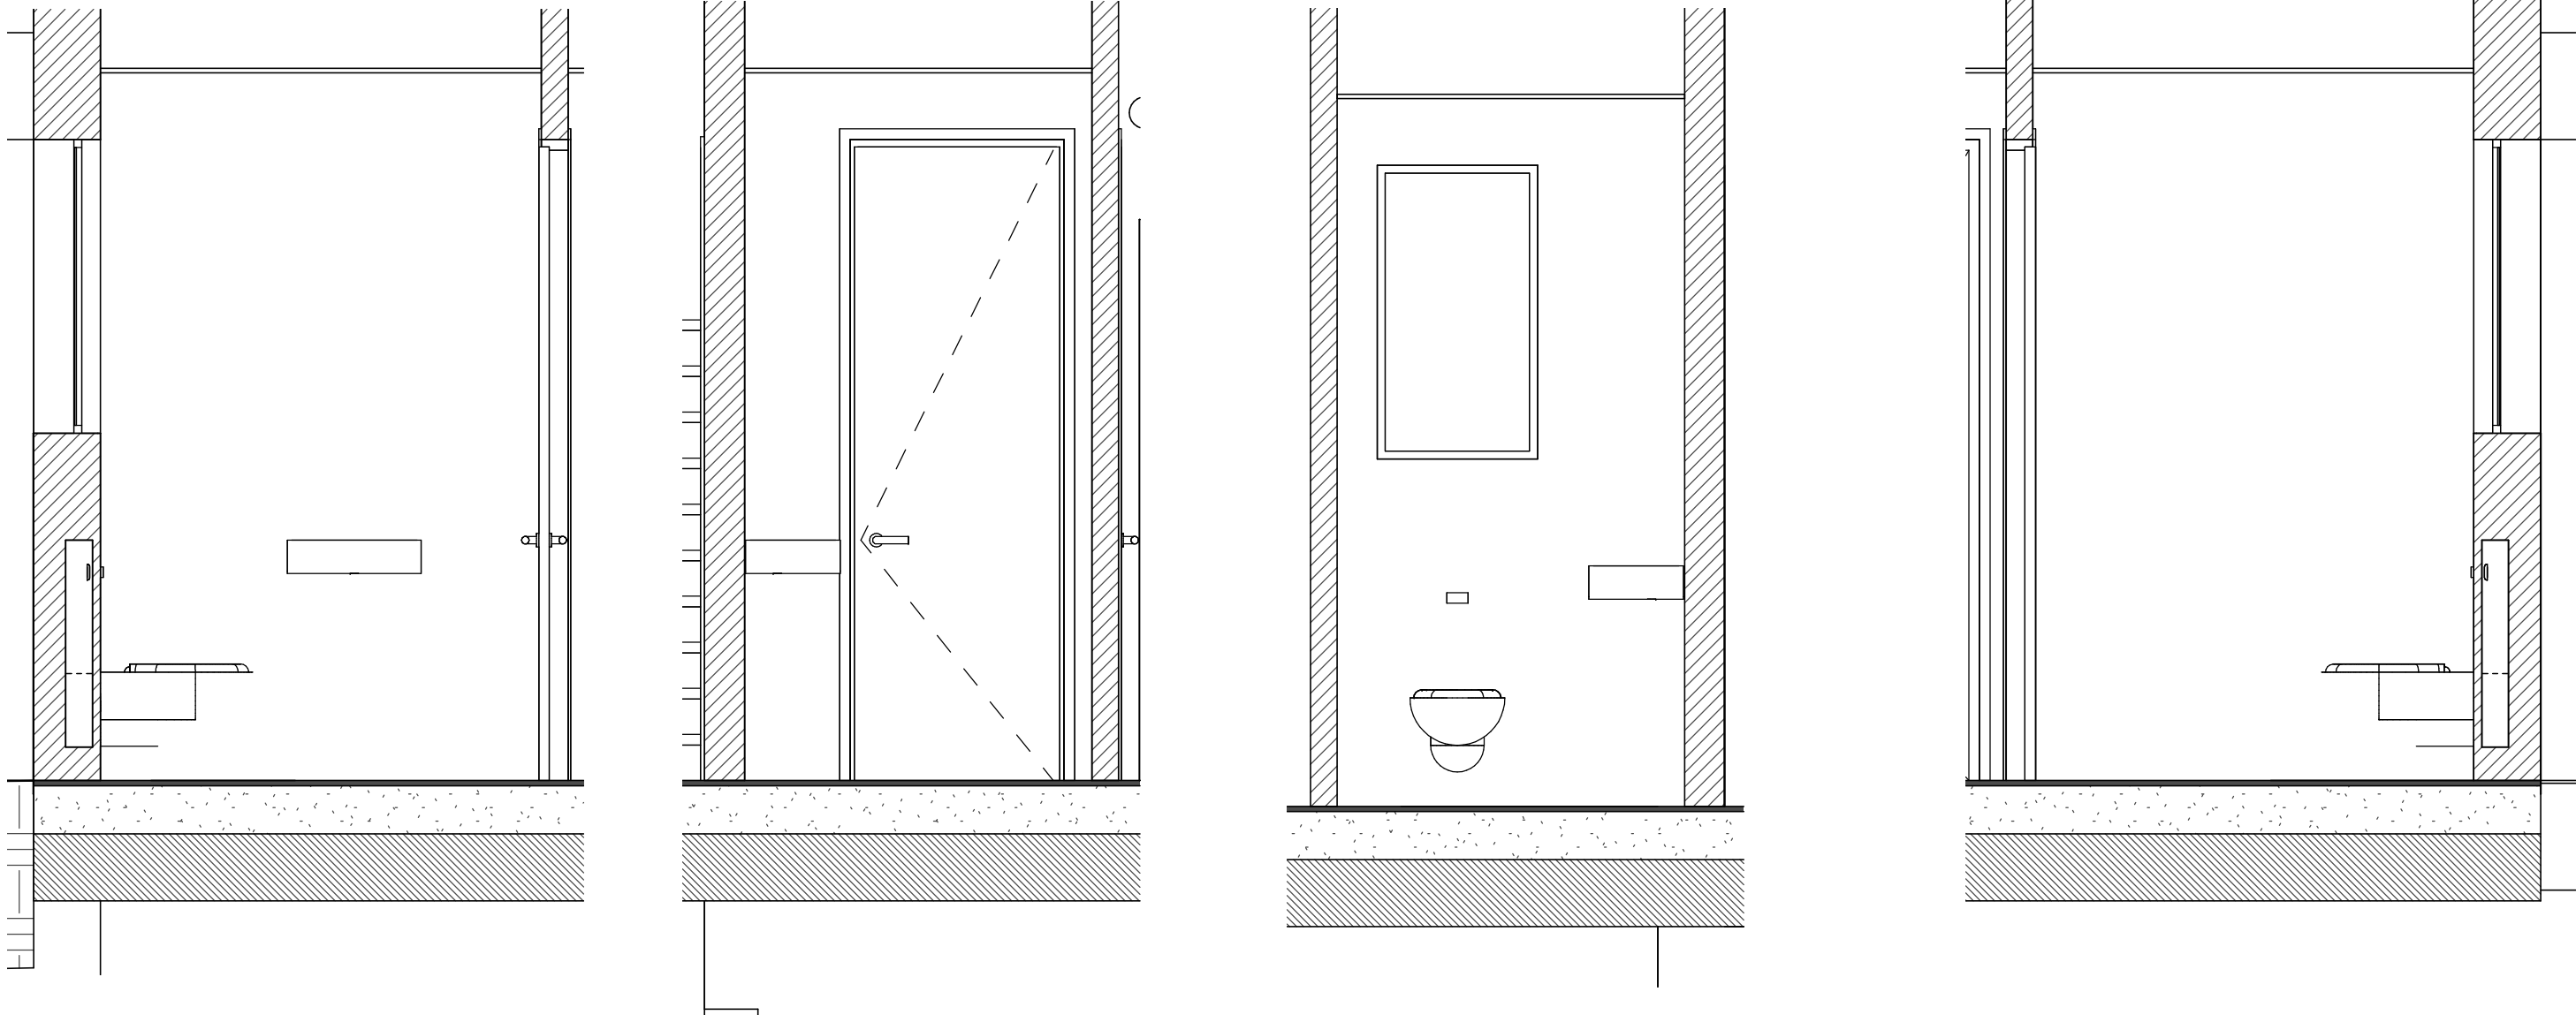

B1

1 : 25

B2

1 : 25


B4

1 : 25

B3


1 : 25

להמשך תכנון

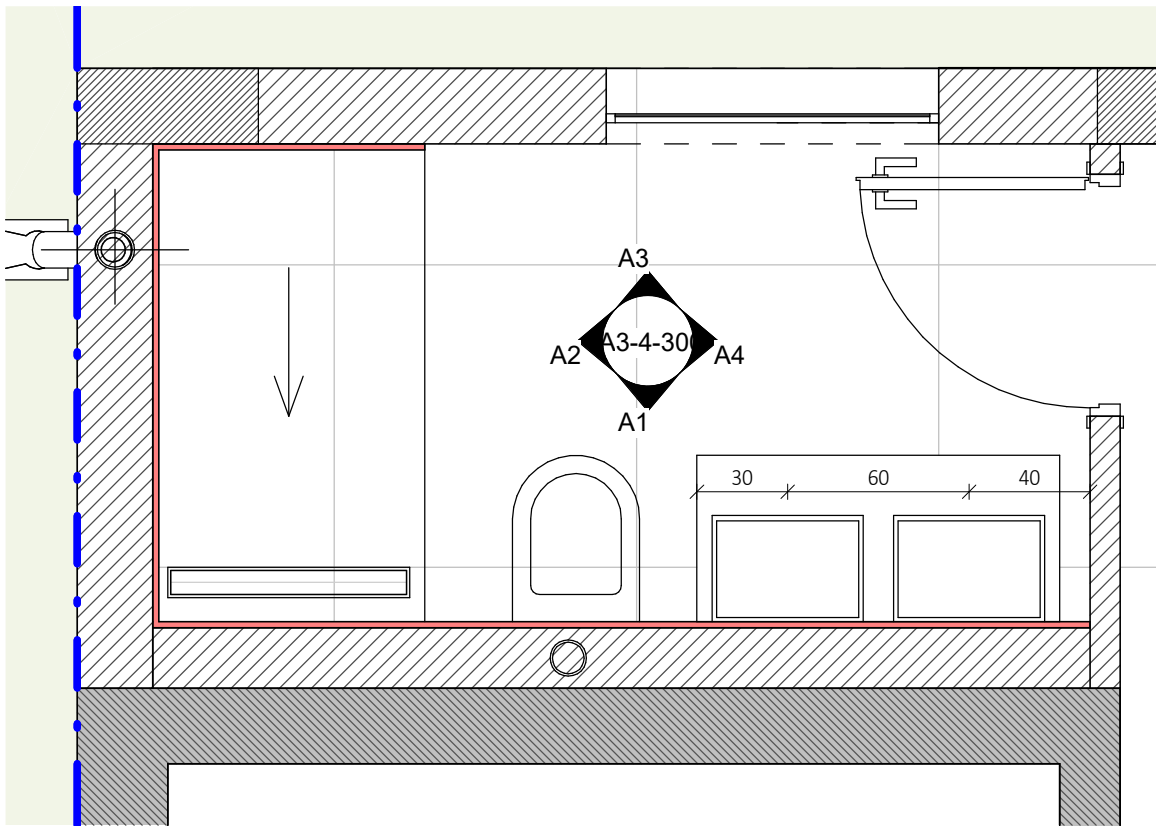


ח. רחצה 1

1 : 25

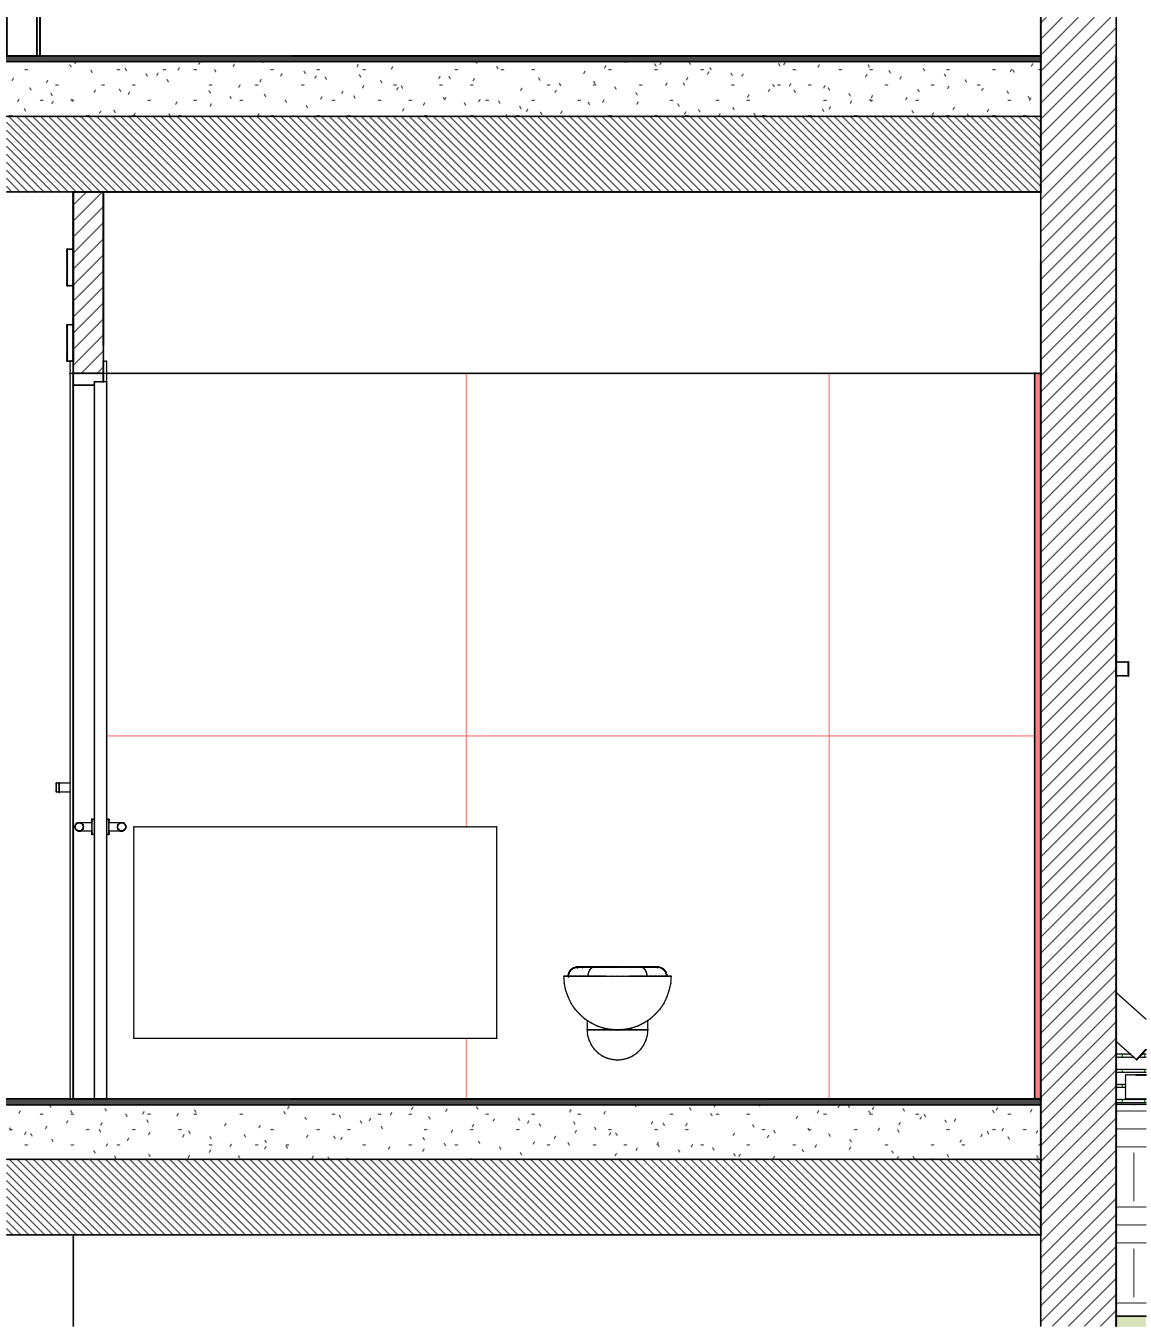


A1

1 : 25

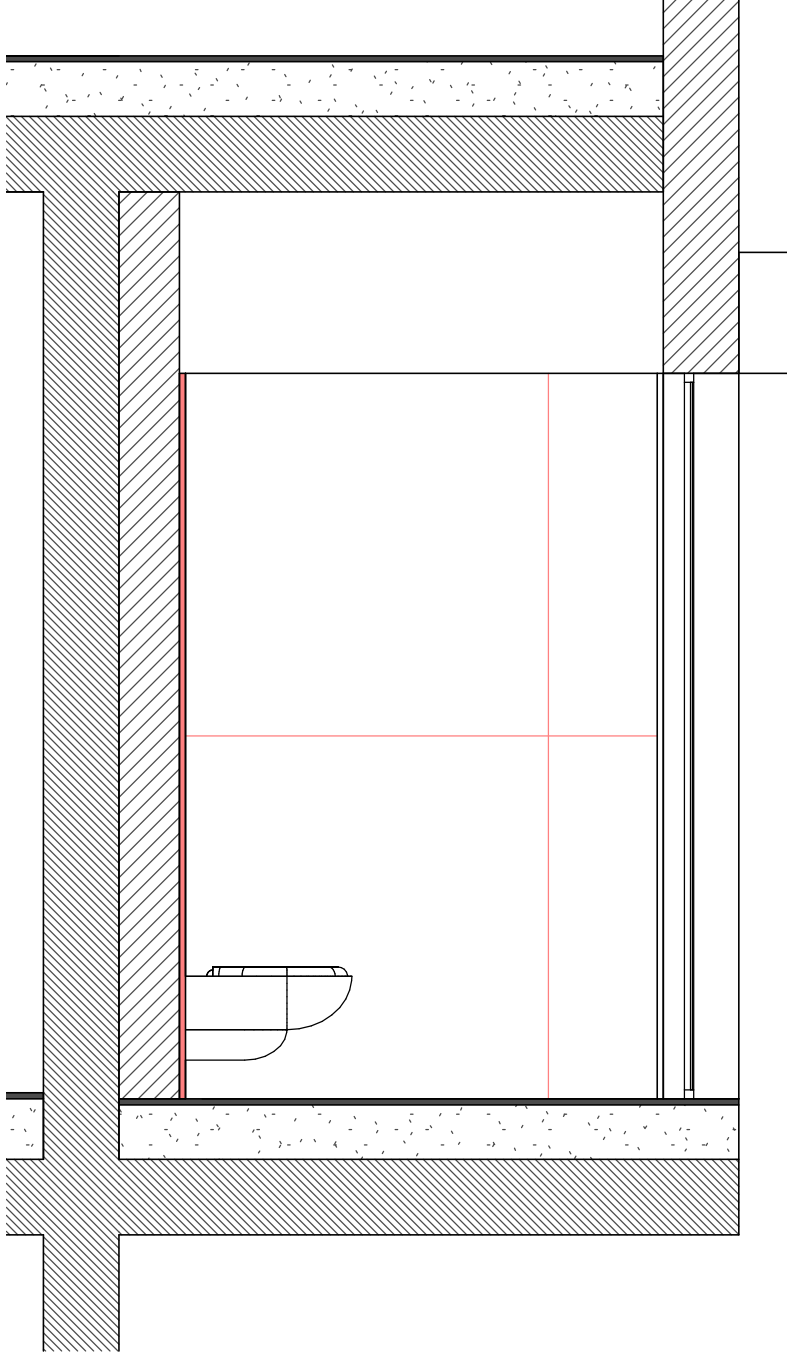


A2

1 : 25

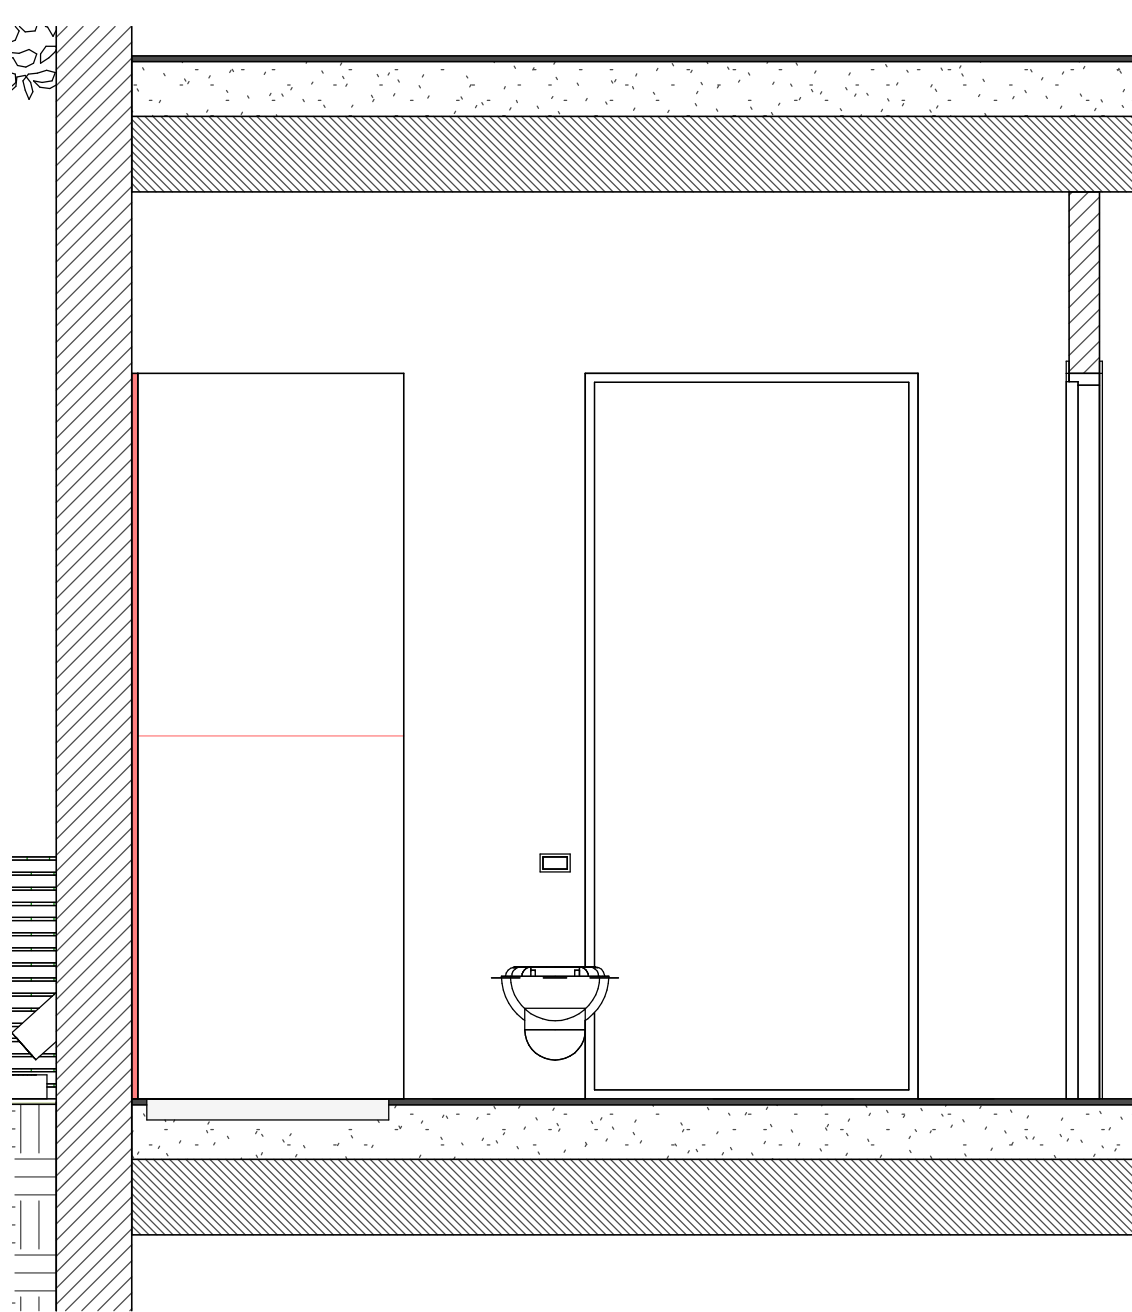

A3

1 : 25

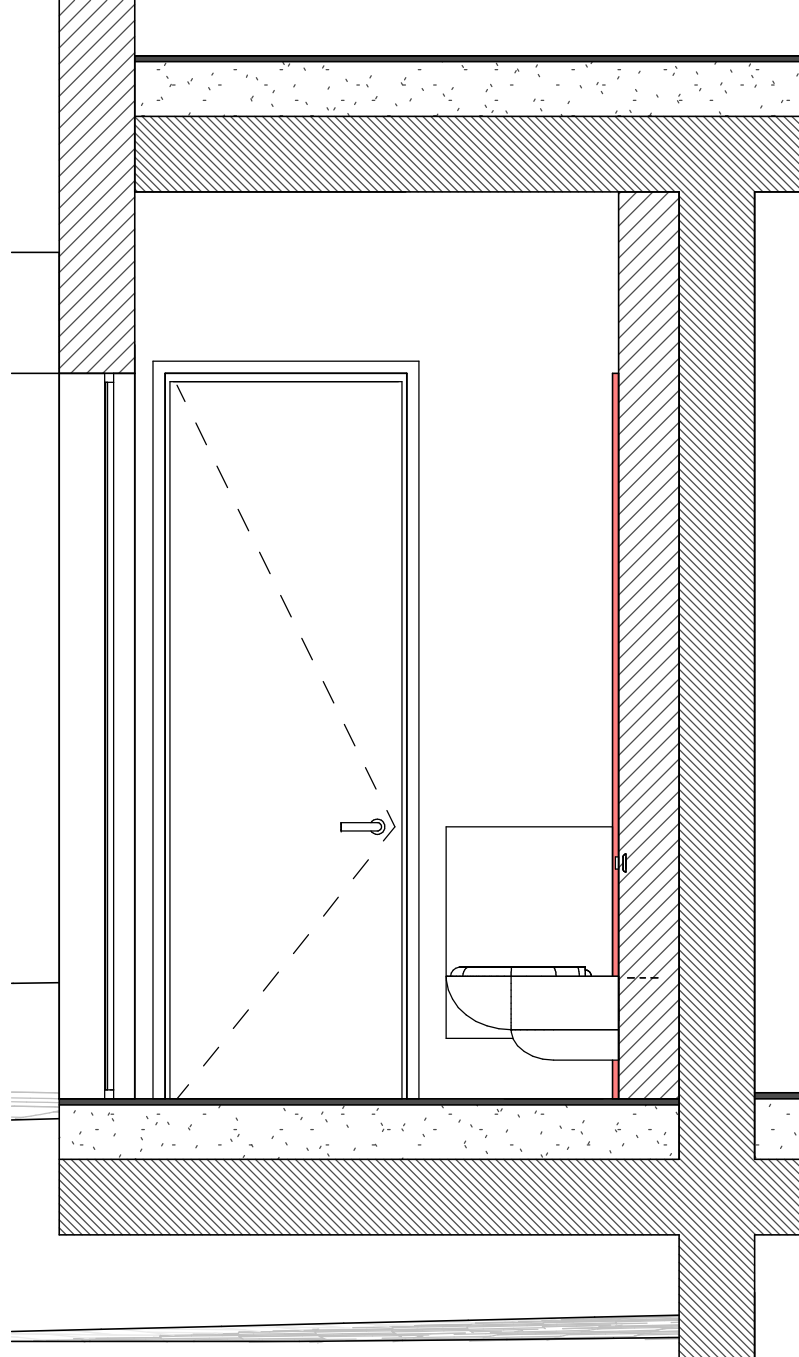

A4

1 : 25

Wall Schedule			
Comments	Area	Family and Type	Type Comments
חיפוי ח. רטוב-NH: Basic Wall			
	7.44 m²	חיפוי ח. רטוב-NH: Basic Wall	חיפוי
	3.79 m²	חיפוי ח. רטוב-NH: Basic Wall	חיפוי
	2.11 m²	חיפוי ח. רטוב-NH: Basic Wall	חיפוי
	3.88 m²	חיפוי ח. רטוב-NH: Basic Wall	חיפוי
	8.61 m²	חיפוי ח. רטוב-NH: Basic Wall	חיפוי
	2.57 m²	חיפוי ח. רטוב-NH: Basic Wall	חיפוי
	4.43 m²	חיפוי ח. רטוב-NH: Basic Wall	חיפוי
	8.99 m²	חיפוי ח. רטוב-NH: Basic Wall	חיפוי
	2.86 m²	חיפוי ח. רטוב-NH: Basic Wall	חיפוי
9	44.69 m²		


ניהול פרויקט
מהיסוד - בן סולומון
פיקוח
מהיסוד - בן סולומון
קונסטרוקציה
ערן שילר
מיזוג אוויר
אייל ארז מהנדסים ויועצים בע"מ
אינסטלציה
איתן אלמסי
חשמל
איתן בסיס
אלומיניום
נוף
נתי בלוקא
חשמל חכם
חימום תת רצפתי
איטום
צבי טל
אקוסטיקה
מעליות
קרקע וביסוס
דיה הנדסת קרקע וביסוס
רישוי

[illegible]

עמוד בטון קיר בטון יור בלוק

[illegible]




CLIENT NAME:	המחירון
קבוצת רכישה נופיה	
PROJECT NAME:	הפרויקט
נופיה - מגרש 10	
DRAWING NAME:	סגנון הציור
פריסות חדרי רחצה - קומה א	
SHEET NUMBER:	פרט גלילון
A3-4-301	

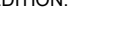SCALE:	קנה מידה:	EDITION:	חזרה:
1 : 25			
STATUS:	סטטוס		
למכר			
	בדוק עיי:		דפוס עיי:
DATE:	22.09.2025		תאריך:


NeumanHaynerArchitects

וימן חיינר אדריכלים
 חורד ההדסים 2, בית חירות
 09-9545842 טל


office@nh-arch.com
 www.nh-arch.com

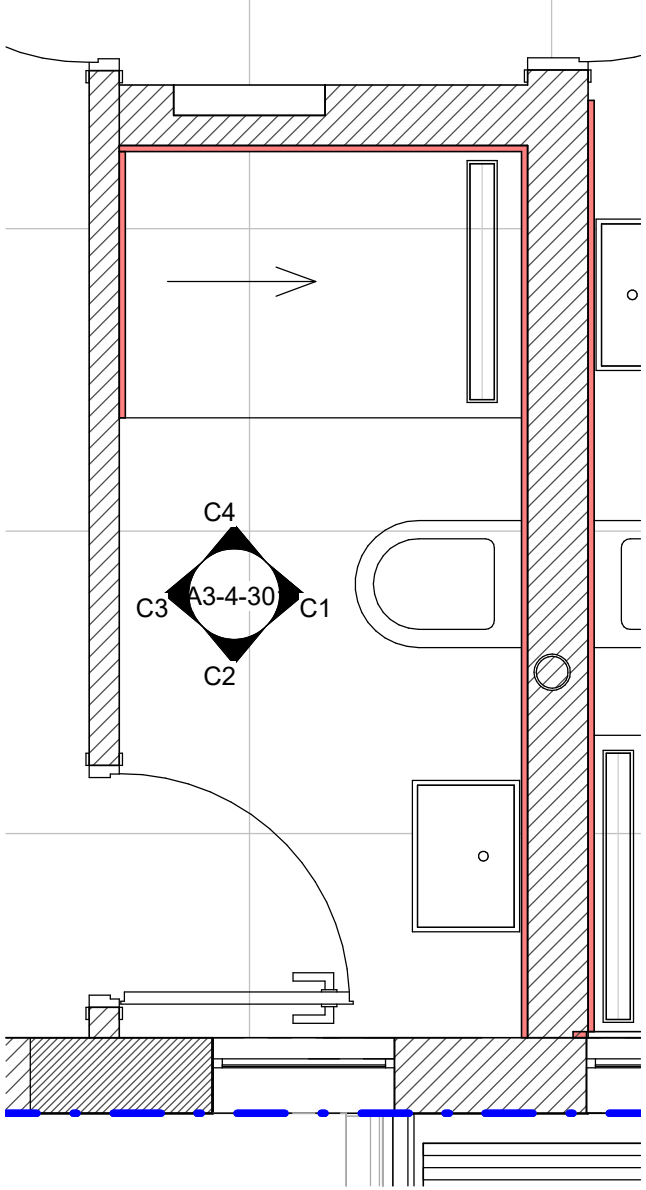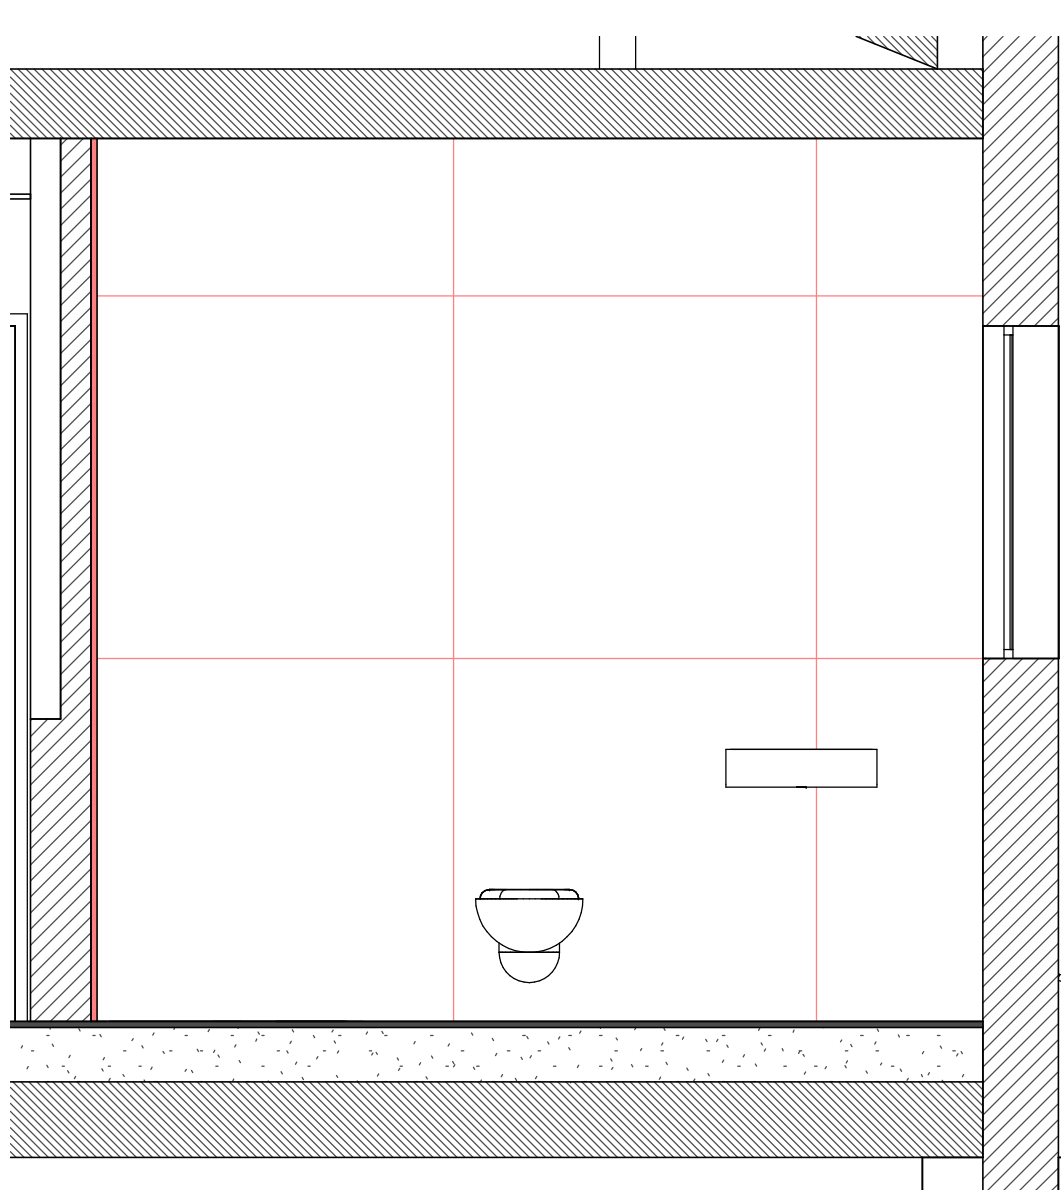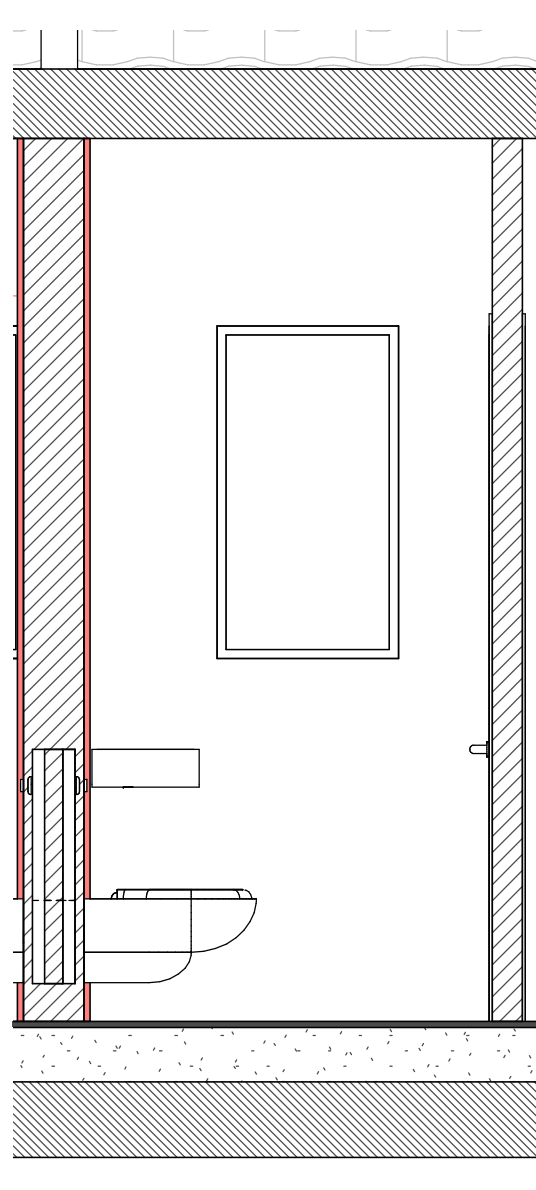[illegible][illegible]

Architectural floor plan of a bathroom (D1). The plan shows a toilet, a sink, and a door. Dimensions are indicated: 52, 120, and 120. The door is shown with a dashed line indicating its swing. The plan is labeled D1 and has a scale of 1:25.

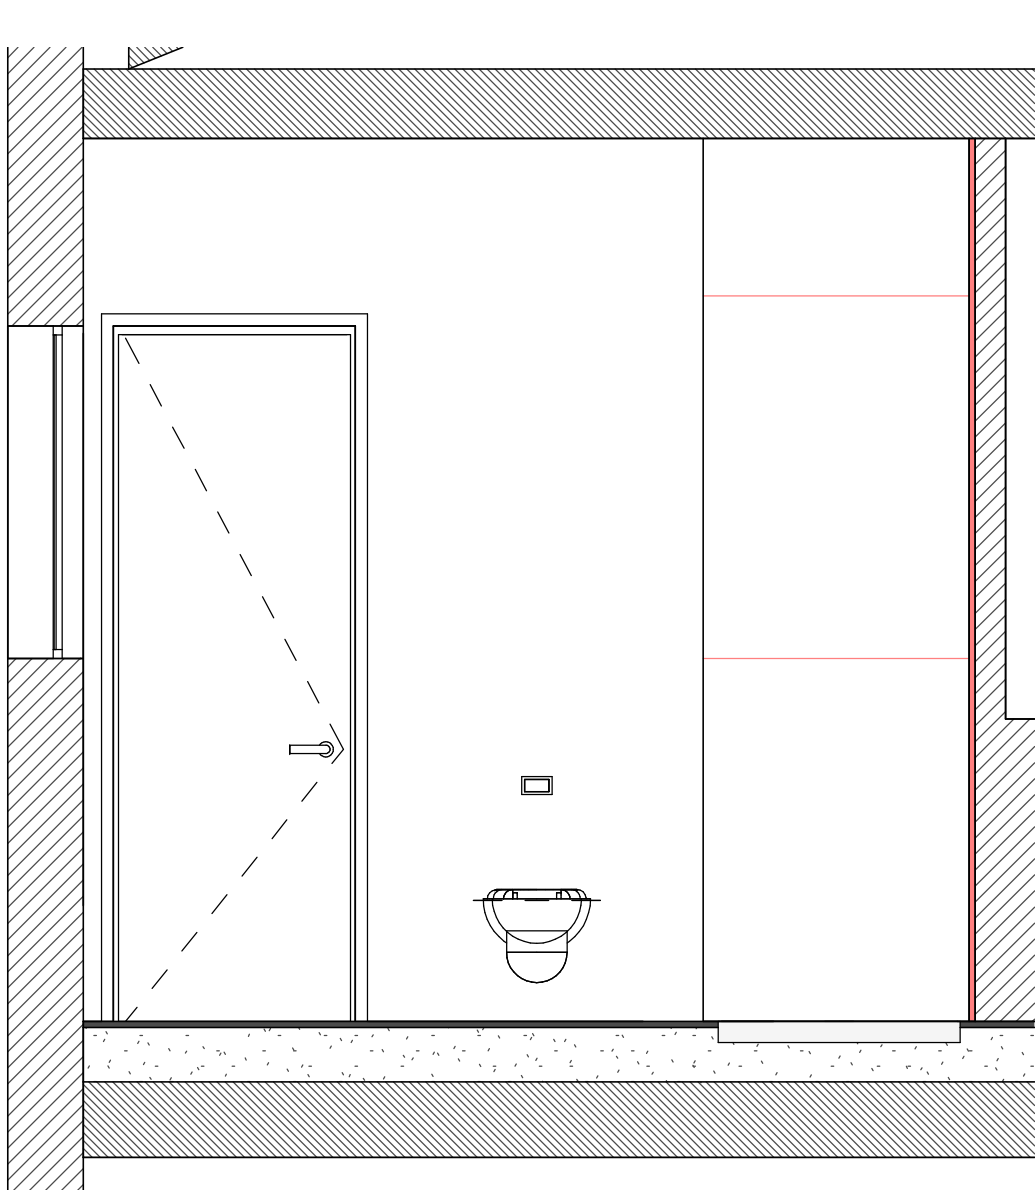

This technical cross-section drawing illustrates a building facade assembly. The roof is shown with a wavy pattern representing insulation. The wall structure includes a thick horizontal layer of insulation (hatched) and a vertical structural element (hatched). A window unit is depicted with a frame and a pane. A door is shown with a handle and a lock mechanism. The floor is represented by a thick horizontal layer of insulation (hatched) and a structural base. The drawing uses various hatching patterns to distinguish between different materials and components.

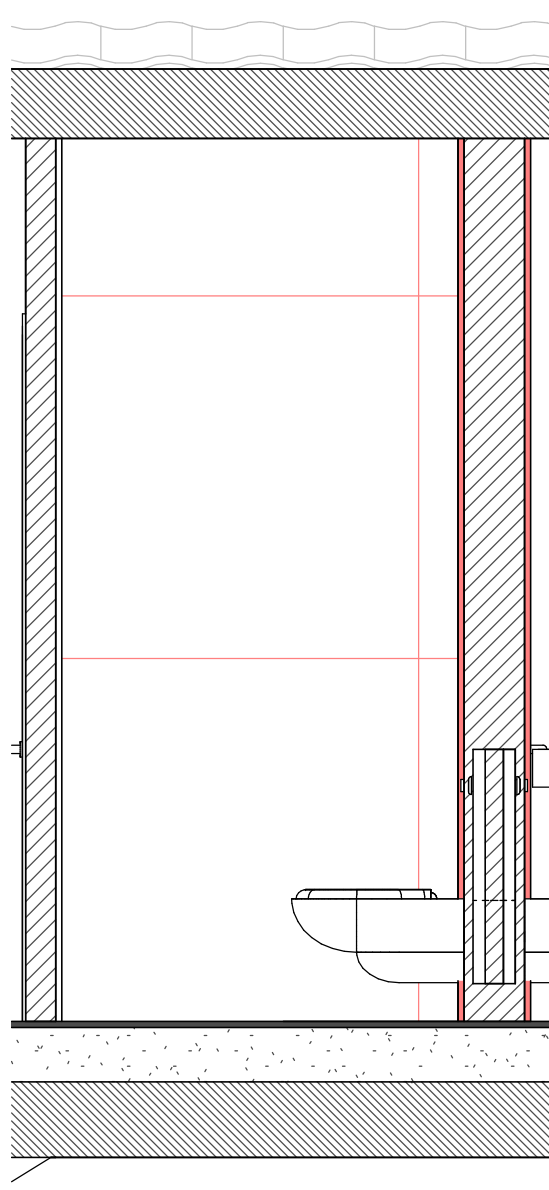

This architectural cross-section drawing shows a bathroom stall. On the left, there is a door with a handle. In the center, there is a tall, narrow rectangular opening, likely for a shower or a large mirror. To the right of this opening is a toilet. Further right is a storage cabinet with two doors, indicated by red horizontal lines. The drawing includes hatching for structural elements like the floor, walls, and ceiling. Below the drawing, the label 'D4' is present, and the scale '1 : 25' is indicated at the bottom right.

להמשך תכנון

רשימת חלונות					
סוג	תיאור	כמות	גובה	רוחב	מס פריט

ק.קרקע

1	200	240	1	צלון רפפה חיצוני חשמלי + ארגז חיצוני	ויטרינה פרופיל 7500 קליל
2	90	240	1	צלון רפפה חיצוני חשמלי + ארגז חיצוני	קבוע עד 130 + חלון קיפ פרופיל 4350 קליל
3	60	110	1	צלון רפפה חיצוני חשמלי + ארגז חיצוני	חלון קיפ פרופיל 4500 קליל
4	320	240	3	צלון רפפה חיצוני חשמלי + ארגז חיצוני	ויטרינה פרופיל 7500 קליל
5	220	240	1	צלון רפפה חיצוני חשמלי + ארגז חיצוני	קבוע עד 130 + חלון הזזה פרופיל 4350 קליל
6	100	575	1	ללא רפפה	חלון קבוע פרופיל 7000 קליל
7	110	240	1	צלון רפפה חיצוני חשמלי + ארגז חיצוני	קבוע עד 130 + חלון קיפ פרופיל 4350 קליל
20	35	240	1	ללא רפפה	חלון קבוע פרופיל 7000 קליל

קומה א

8	110	110	3	תריס גלילה חשמלי	חלון הזזה פרופיל 7000 קליל
9	220	110	3	תריס גלילה חשמלי	חלון הזזה פרופיל 7000 קליל
10	150	230	1	תריס גלילה חשמלי	ויטרינה פרופיל 7500 קליל
11	90	230	1	תריס גלילה חשמלי	דלת כנף פרופיל 4350 קליל
12	60	110	1	תריס גלילה חשמלי	חלון קיפ פרופיל 4500 קליל
13	110	110	1	תריס גלילה חשמלי	חלון קיפ פרופיל 4500 קליל

סוג זכוכית – בהתאם למפורט בדו"ח התרמי (תנאי המינימום בעמוד 9 מתוך המפרט התרמי). כמו כן, הזכוכית תקבע בתיאום עם הקבלן לאחר אישור יועץ התרמי וחברת הניהול

כל פריט יחולק למינימום הכנפיים האפשרי (לתיאום מול ספק האלומיניום ובמסגרת שרטוטי הshop drawing)

רשימת דלתות					
סוג	הערות	כמות	גובה	רוחב	מספר פריט

0	120	240	1	דלת כניסה	דלת חוץ דגם גארדה
1	80	240	2	דלת פנים	דלת פנים "אקוודור" תוצרת חמדיה
2	90	240	1	דלת פנים	דלת פנים "אקוודור" תוצרת חמדיה
3	80	200	1	דלת נגרות ממ"ד	דלת פנים "אקוודור" תוצרת חמדיה
4	80	230	5	דלת פנים	דלת פנים "אקוודור" תוצרת חמדיה
5	80	240	1	דלת הזזה	דלת הזזה "אקוודור" פורמייקה תוצרת חמדיה

נוימן חיינר אדריכלים בע"מ

כל הזכויות שמורות
ט.ל.ח.

NeumanHaynerArchitects

רשימת פתחים

גליון מספר:	A3-6-1000	מהדורה:	22.09.2025	01
שם הפרויקט:	נופיה - מגרש 10	סטטוס:	למכרז	
שם המממן:	קבוצת רכישה נופיה	קנה מידה:		
23/10/2025 15:54:02				