


פתחי גישה אופן ארט בתיאום סופי מול אדריכל
כלל יחידות המיזוג אשר נמצאות בתוך נגרות יש לתאם סופית מול אדריכל ונגרות

Court 10
1st Floor

Option No2
inverter duct unit in living
room and wall mounted in
rooms

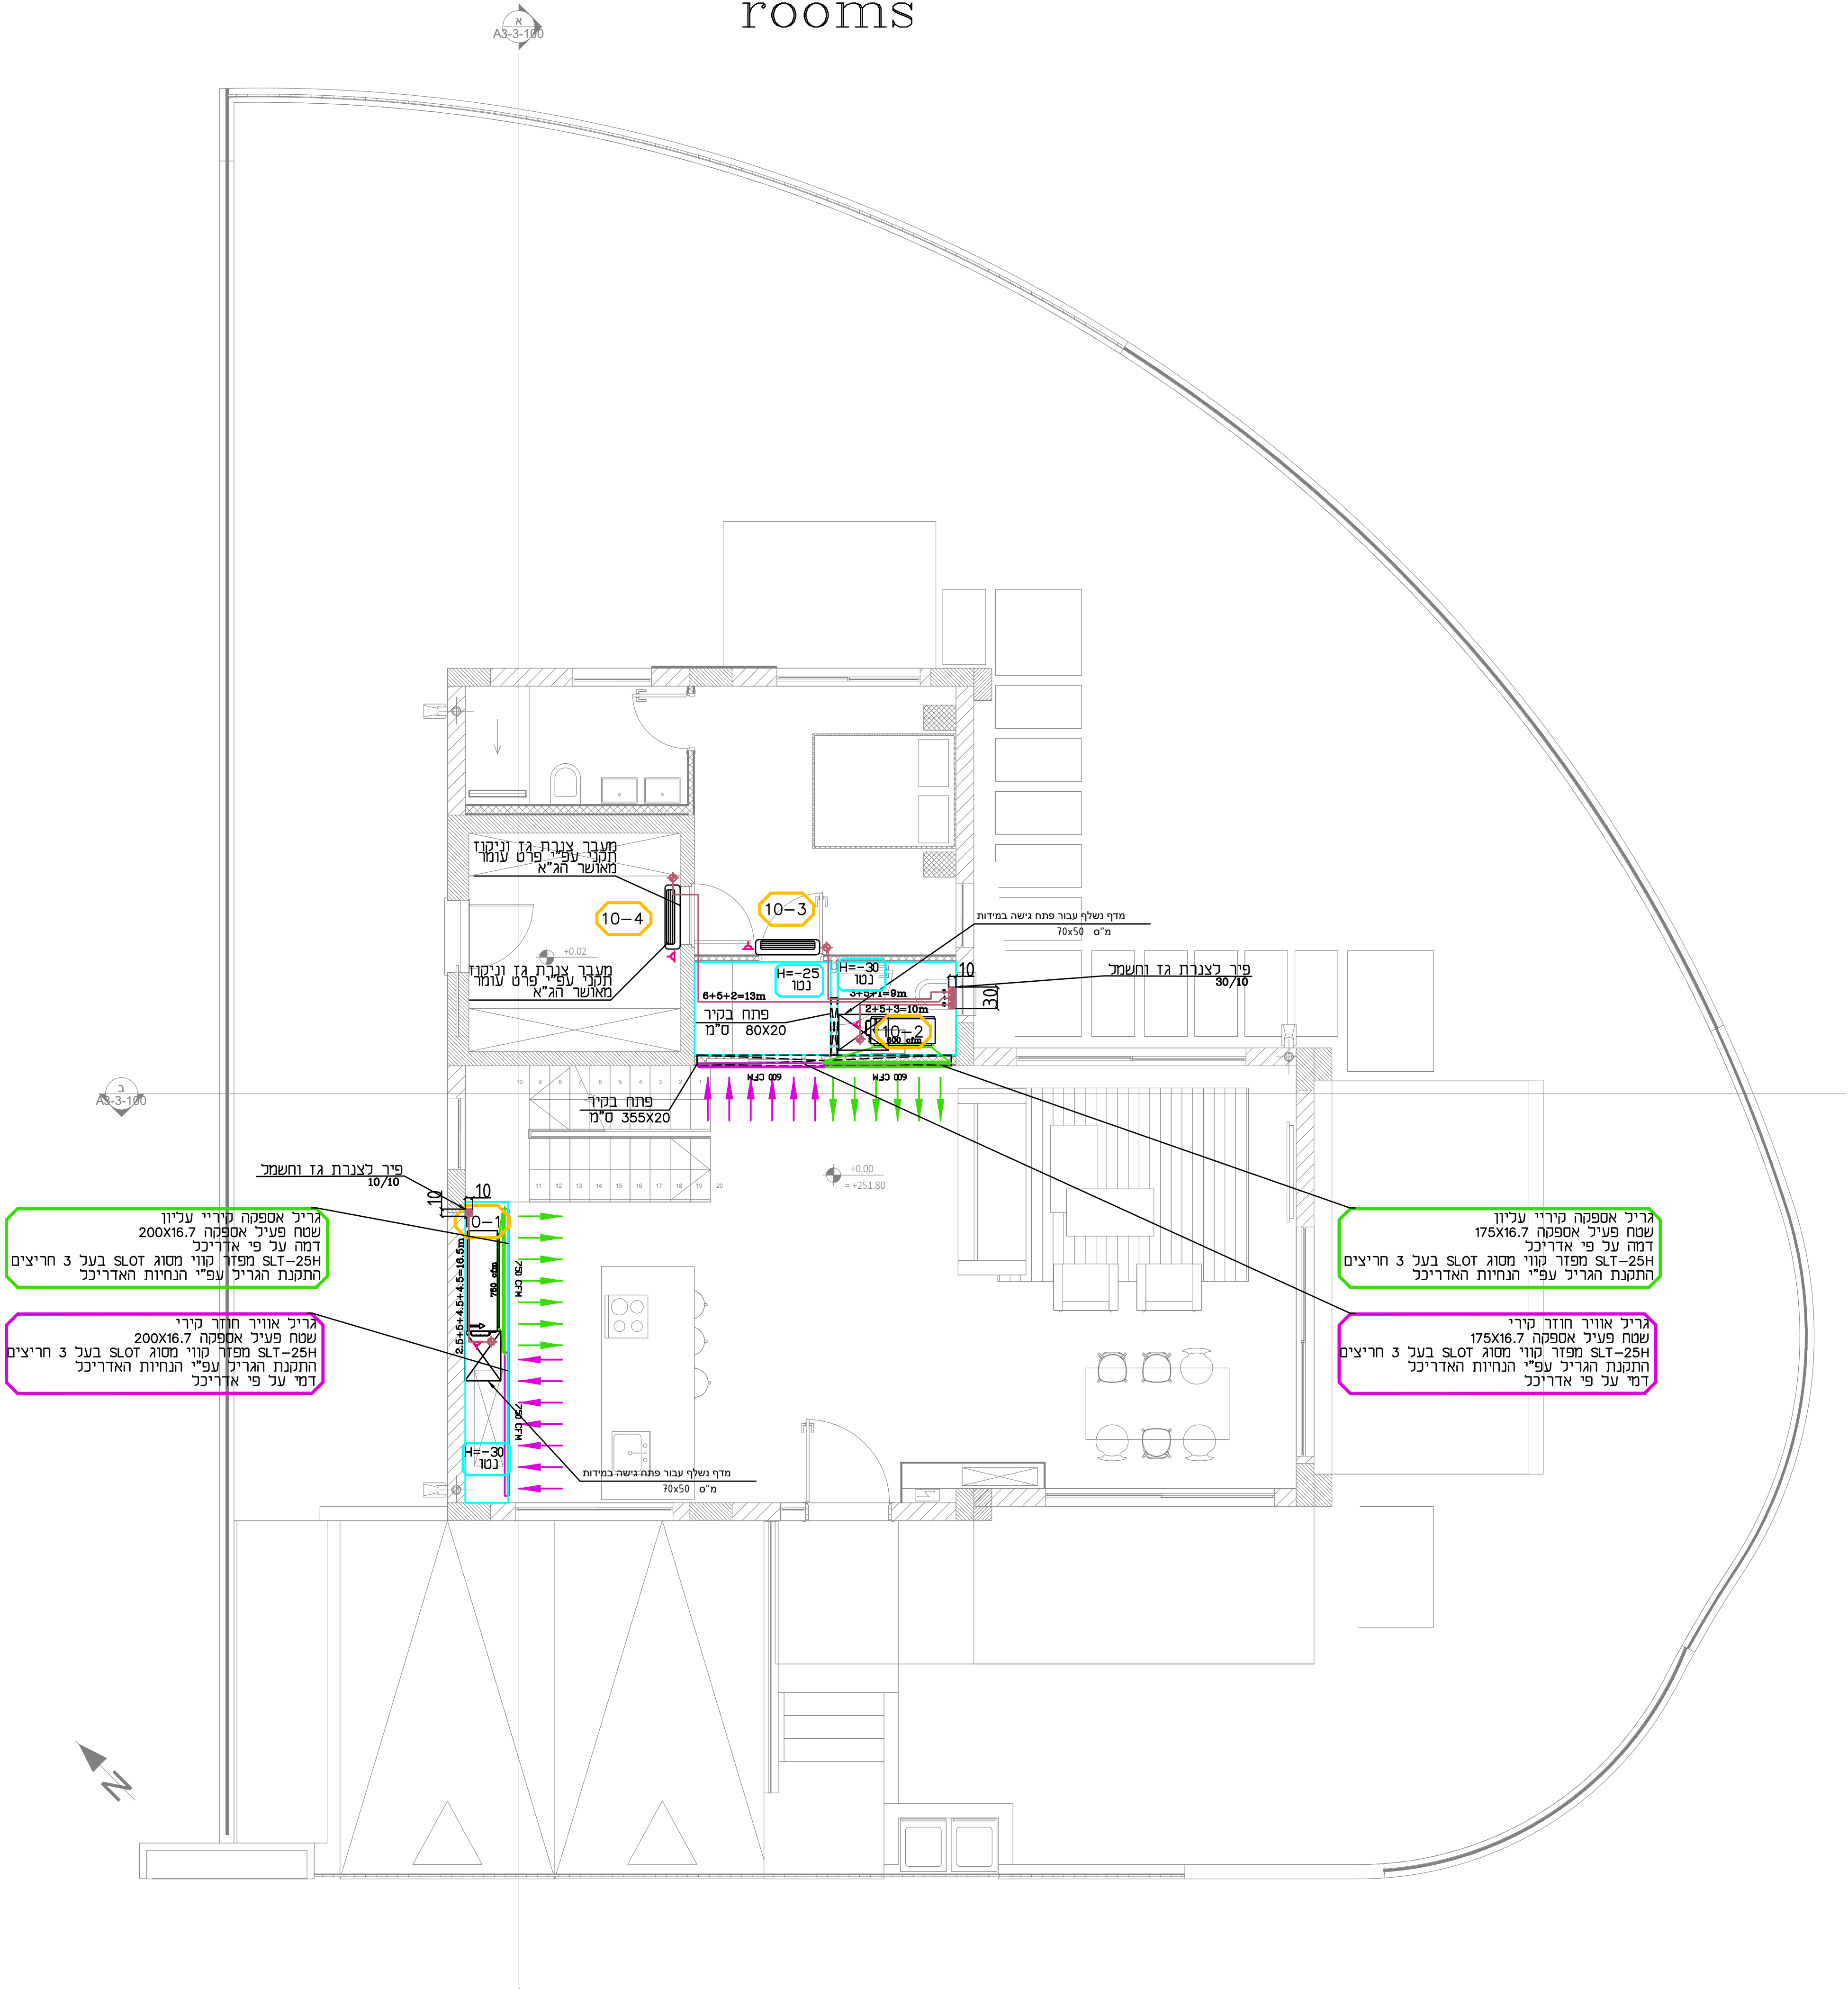

Court 10
2nd Floor

Option No2
inverter duct unit in living
room and wall mounted in
rooms



תפוצה

אדריכל	לוח	תוכן פרויקט	תוכן ראשי	תוכן תאורה	תוכן חשמל	אקוסטיקה	בטיחות אש	אינסטלציה	אדריכל פנים

מהדורה

חבנית לאישור	11.04.2025	⚠️
חבנית לאישור	11.03.2025	⚠️
חבנית לאישור	04.12.2024	⚠️
חבנית לעיון	13.11.2024	⚠️
שנתיים:	חאריד:	טל:

המבצע אחראי למידות ובהתאמתן למציאות
בכל מקרה של אי התאמה, סתירה או טעות
עליו להודיע למתכנן לפני התקדמותו בביצוע
אין לטעות מידות על סמך מדידה בשרטוט.
אין לעשות כל שימוש בחוכנית זו
או ברעיונות והגומים בה ללא אישור בכתב
מאת המתכנן.

הערות

- כל התעלות מחוץ למבנה יבודדו
בידוד אקוסטי בעובי 2" מידות התעלות הן מידות פח
- תעלות מזוג בתוך המבנה יבודדו
בידוד אקוסטי פנימי 1" מידות התעלות הן מידות פח
- תעלות אוויר צח יבודדו
בידוד טרמי 1" מידות התעלות הן מידות פח
- יש לאסום בסיקור את פינות החיבור
של תעלות מזוג אוויר צח כפי כיפוף
הפורום המתחברים

מקרא

- מפ- מפוח
- מ.א.ג. - מפזר אוויר קירי
- מ.א.ת. - מפזר אוויר תקרת
- ת.א.ת. - תריס אוויר חודר
- ת.א.צ. - תריס אוויר צח
- ב.א. - בידוד אקוסטי
- ב.ס. - בידוד טרמי
- כ.ב. - כלא בידוד
- ד.א. - דמפר אש
- טרמסטט לוח הפעלה
- שקע חשמל לספוף יועץ חשמל
- שקע תלת פאזי לספוף יועץ חשמל
- מפסק בסנרון חד פאזי לספוף יועץ חשמל
- מפסק בסנרון תלת פאזי לספוף יועץ חשמל
- ניקוז מאייד לספוף יועץ אינסטלציה בגובה 25 ס"מ מתחתית גובה המאייד
- שלט הפעלה אלקטרוני

מקרא צבעים בתכנית

- תעלות ותריסי אוויר חודר
- תעלות ותריסי אספקת אוויר
- תעלות ותריסי אוויר צח
- תעלות ותריסי יניקת אוויר
- תעלות ותריסי שחרור עשן
- צנרת גז וחשמל
- סימון מעגלי מיזוג אוויר

191	מבני מגורים צמודי קרקע נופיה אפרי מנשה מדרש 10
1:50	מיזוג אוויר ואיוורור
11.04.2025	קומה ראשונה ושנייה
11.04.2025	תאריך פתירה
11.04.2025	תאריך פתירה
תפוצה

אורני

לוח

כותר פרויקט

סמל ראשי

תוספת תמונה

אקסטריק

אסטרטגיה

אורני פנים

מסמך

11.04.2025

11.03.2025

04.12.2024

13.11.2024

שם הפרויקט

שם המעצב

המבצע אחראי למידות ובהתאמתן למציאות בכל מקרה של אי התאמה, סתירה או טעות. עליו להודיע למתכנן לפני התקדמותו בביצוע. אין לנכות מידות על סמך מדידה בשרטוט. אין לעשות כל שימוש בחוכנית זו או ברעיונות והנחיות בה ללא אישור בכתב מאת המתכנן.

הערות

- כל התעלות מחוץ למבנה יבודדו בבידוד אקוסטי בעובי 2" מידות התעלות הן מידות פח
- תעלות מזוג בתוך המבנה יבודדו בבידוד אקוסטי פנים 1" מידות התעלות הן מידות פח
- תעלות אוויר צח יבודדו בבידוד 1" מידות התעלות הן מידות פח
- יש לאסוף בסיקון את פינות החיבור של תעלות מזוג אוויר לפני כיפוף הפחים המתחברים

מקרא

- מפ- מפוח
- מ.א.ג. - מפוח אוויר קורי
- מ.א.ת. - מפוח אוויר תתקרי
- ת.א.ת. - תריס אוויר חוזר
- ת.א.צ. - תריס אוויר צח
- ב.א. - בידוד אקוסטי
- ב.ס. - בידוד טרמי
- כ.ב. - כלא בידוד
- ד.א. - דמפר אש
- סממנט לוח הפעלה
- שקע חשמל לספול יועץ חשמל
- שקע חתך פאזי לספול יועץ חשמל
- מפסק בסנרון חד פאזי לספול יועץ חשמל
- מפסק בסנרון חתך פאזי לספול יועץ חשמל
- ניקוז מאיד לספול יועץ אינסטלציה בגובה 25 ס"מ מתחתית גובה המאיד
- שלט הפעלה אלחוטי

מקרא צבעים בתכנית


- תעלות ותריסי אוויר חוזר
- תעלות ותריסי אספקת אוויר
- תעלות ותריסי אוויר צח
- תעלות ותריסי יניקת אוויר
- תעלות ותריסי שחרור עשן
- צנרת גז וחשמל
- סימון מעגלי מזוג אוויר

מבני מגורים צמודי קרקע	נופיה ארפי מנשה	מגרש 10
191	מספר	מספר
1:50	מספר	מספר
11.04.2025	תאריך	תאריך
קומת גג וטבלאות	שם הפרויקט	שם הפרויקט
4	מספר	מספר
לעיון	למסדר	למסדר
לביצוע	למסדר	למסדר
13.11.2024	תאריך	תאריך
13.11.2024	תאריך	תאריך



Court 10 Roof

Option №2 inverter duct unit in living room and wall mounted in rooms

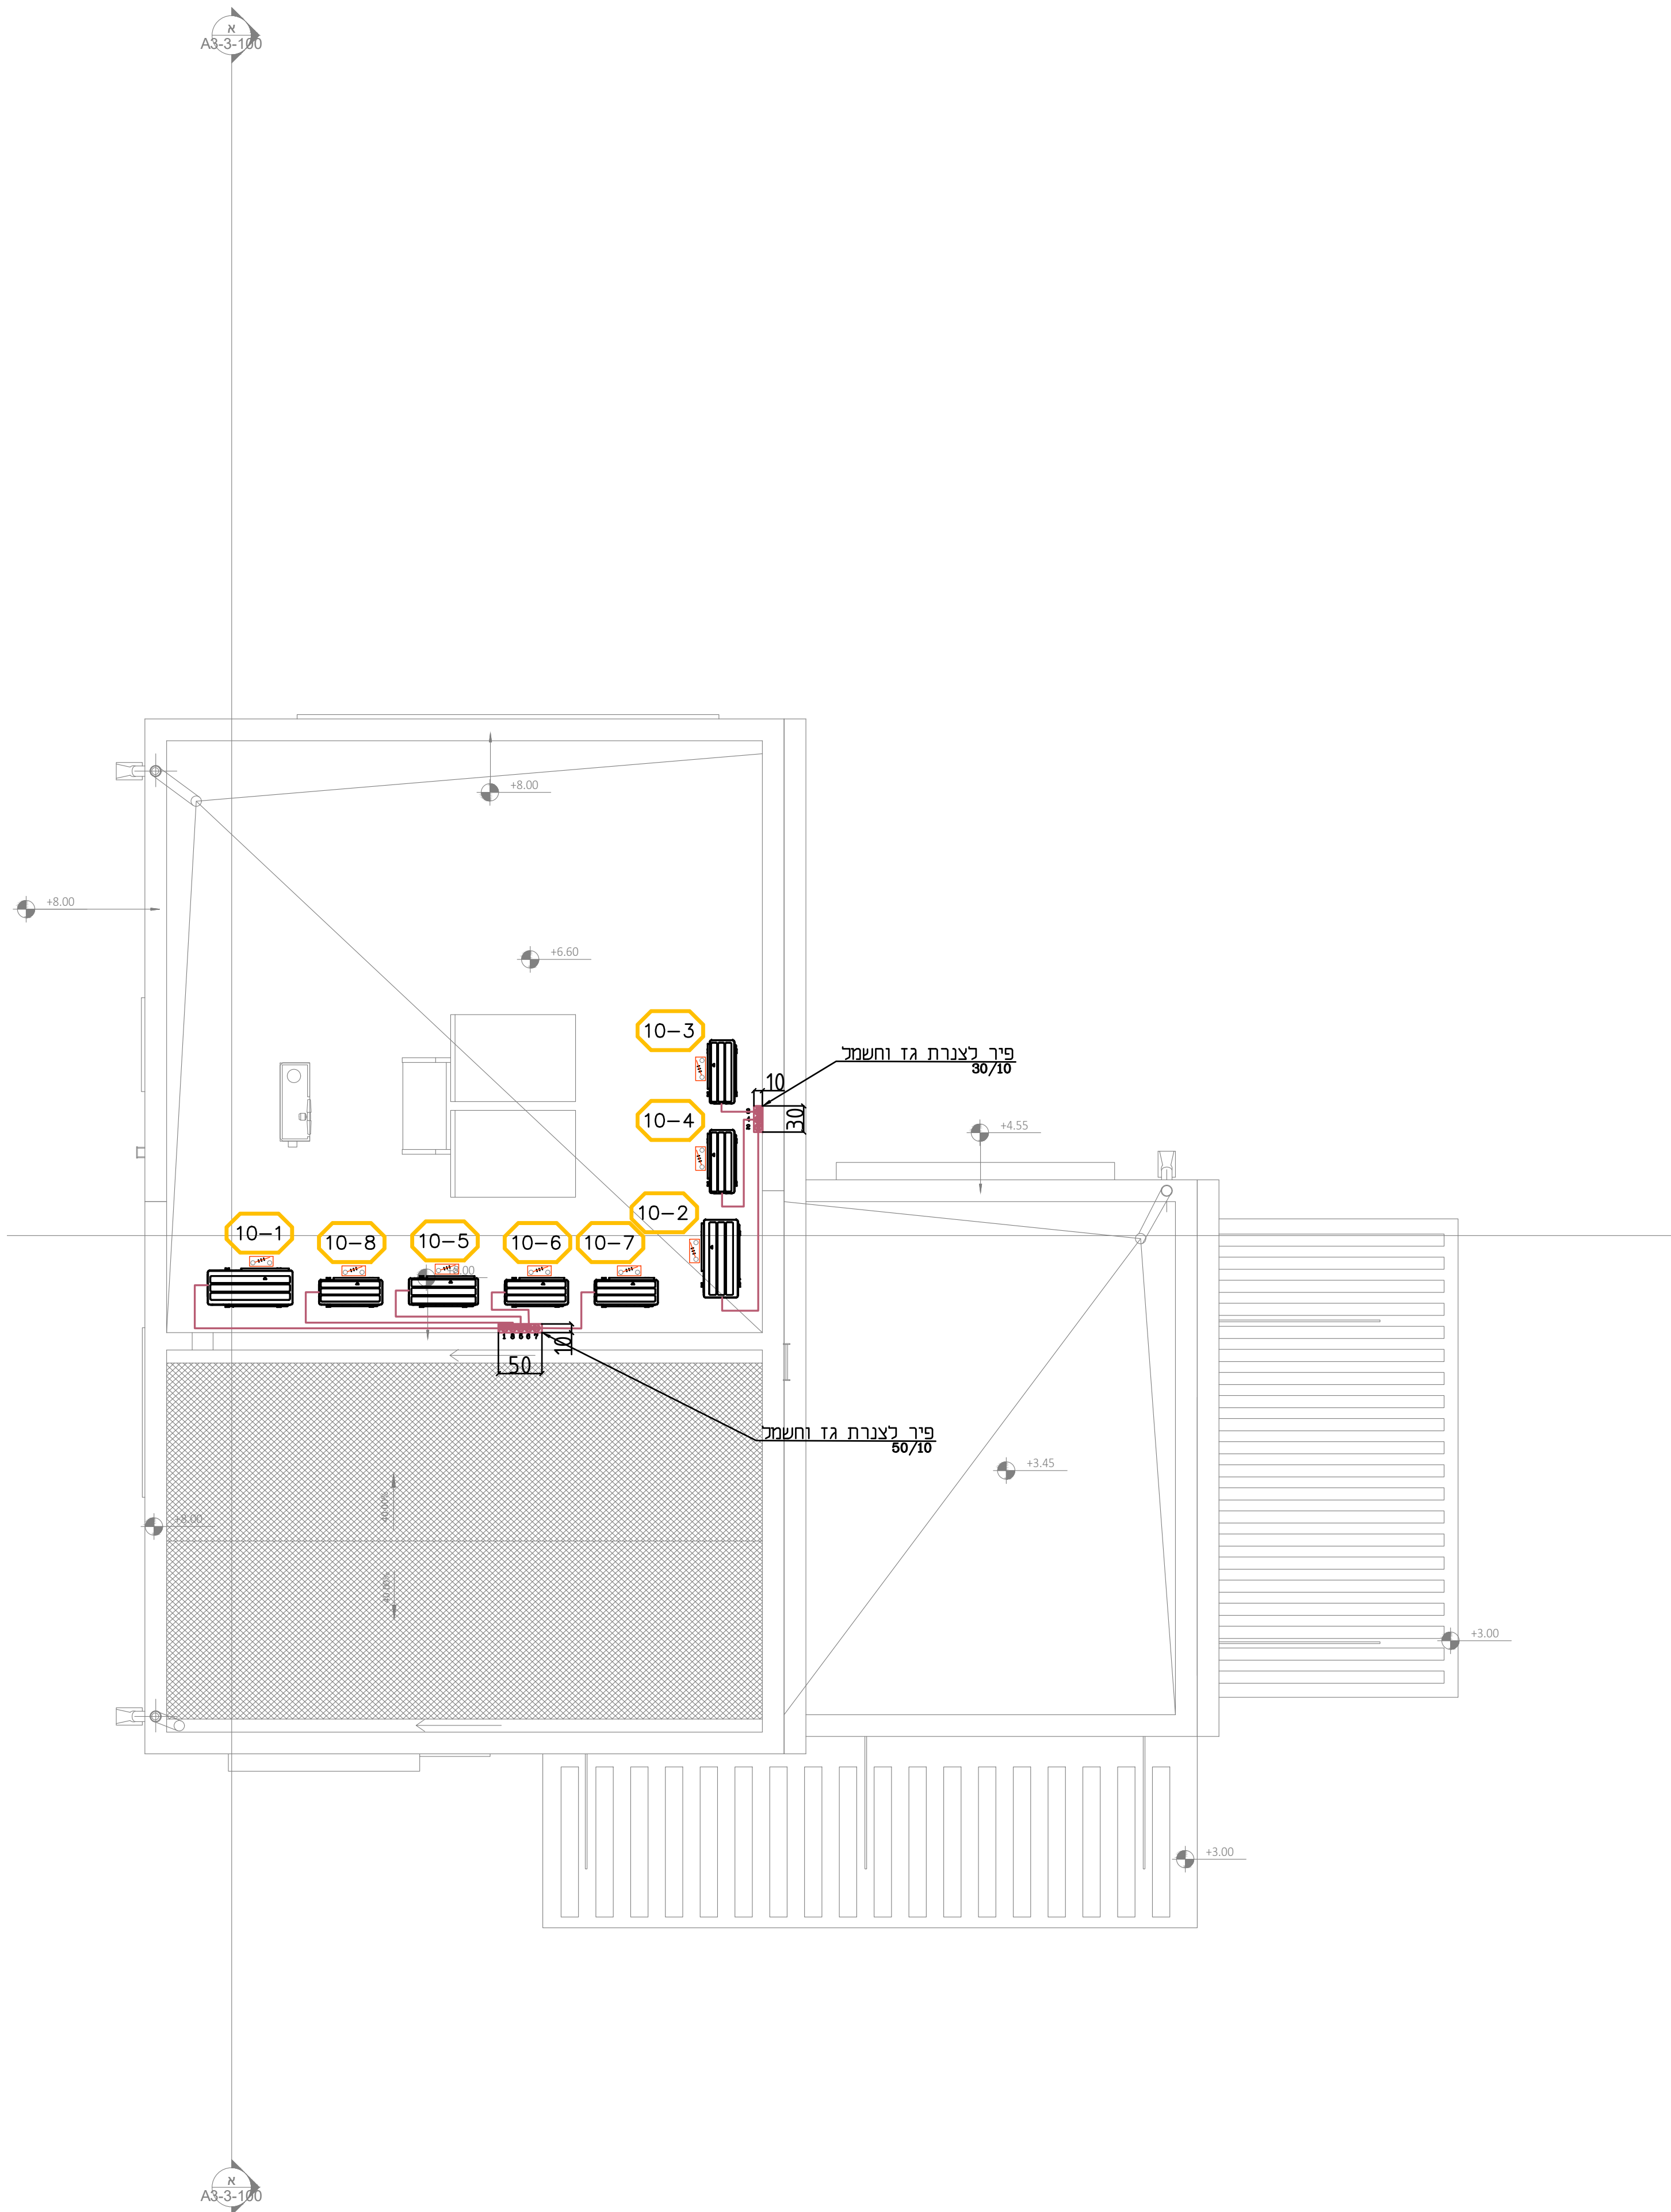

מיקום סופי של המעבים
ייקבע בשטח
בתאום עם האדריכל
תוך פרויקט
מכלול מזוג אוויר

מיקום סופי של הניקוזים
ייקבע בשטח בתאום עם האדריכל
תוך פרויקט
מכלול מזוג אוויר

בסיס במסגרת מינימלי 10 ס"מ
יחידת עיבוי עומדת על ג' בולס רעידות
לטיפול בקבוצת מזוג אוויר

מיקום סופי של המעבים
ייקבע בשטח
בתאום עם האדריכל
תוך פרויקט
מכלול מזוג אוויר

מיקום סופי של הניקוזים
ייקבע בשטח בתאום עם האדריכל
תוך פרויקט
מכלול מזוג אוויר

בסיס במסגרת מינימלי 10 ס"מ
יחידת עיבוי עומדת על ג' בולס רעידות
לטיפול בקבוצת מזוג אוויר

מיקום סופי של המעבים
ייקבע בשטח
בתאום עם האדריכל
תוך פרויקט
מכלול מזוג אוויר

מיקום סופי של הניקוזים
ייקבע בשטח בתאום עם האדריכל
תוך פרויקט
מכלול מזוג אוויר

בסיס במסגרת מינימלי 10 ס"מ
יחידת עיבוי עומדת על ג' בולס רעידות
לטיפול בקבוצת מזוג אוויר

מיקום סופי של המעבים
ייקבע בשטח
בתאום עם האדריכל
תוך פרויקט
מכלול מזוג אוויר

מיקום סופי של הניקוזים
ייקבע בשטח בתאום עם האדריכל
תוך פרויקט
מכלול מזוג אוויר

בסיס במסגרת מינימלי 10 ס"מ
יחידת עיבוי עומדת על ג' בולס רעידות
לטיפול בקבוצת מזוג אוויר

מיקום סופי של המעבים
ייקבע בשטח
בתאום עם האדריכל
תוך פרויקט
מכלול מזוג אוויר

מיקום סופי של הניקוזים
ייקבע בשטח בתאום עם האדריכל
תוך פרויקט
מכלול מזוג אוויר

בסיס במסגרת מינימלי 10 ס"מ
יחידת עיבוי עומדת על ג' בולס רעידות
לטיפול בקבוצת מזוג אוויר

יחידות מזוג סינגל-מאיד+מעבה									
מס' יחידה בתכנית	חוצרת	דגם	תפוקת קרור Btu/h	ספיקת אוויר CFM	הספק עבודה למנוע W	מידות מאיד	מידות מעבה	נתיב דגם c	הערות
10-4	Tadiran	ALPHA PRO INV 140 NG	9,210	320	0,800	21.11/29.12/89.4	33.11/55.52/73.21	1x10C	חזנה במאיד

יחידות מזוג סינגל-מאיד+מעבה									
מס' יחידה בתכנית	חוצרת	דגם	תפוקת קרור Btu/h	ספיקת אוויר CFM	הספק עבודה למנוע W	מידות מאיד	מידות מעבה	נתיב דגם c	הערות
10-3, 10-6, 10-7, 10-8	Tadiran	ALPHA PRO INV 180 NG	11,940	380	1,100	21.11/29.12/89.4	33.11/55.52/73.21	1x10C	חזנה במאיד

יחידות מזוג סינגל-מאיד+מעבה									
מס' יחידה בתכנית	חוצרת	דגם	תפוקת קרור Btu/h	ספיקת אוויר CFM	הספק עבודה למנוע W	מידות מאיד	מידות מעבה	נתיב דגם c	הערות
10-5	Tadiran	ALPHA PRO INV 240 NG	17,740	500	1,800	22.11/30.42/101.4	35.11/55.52/80.21	1x16C	חזנה במאיד

יחידות מזוג סינגל-מאיד+מעבה									
מס' יחידה בתכנית	חוצרת	דגם	תפוקת קרור Btu/h	ספיקת אוויר CFM	הספק עבודה למנוע W	מידות מאיד	מידות מעבה	נתיב דגם c	הערות
10-2	Tadiran	SUPER SLIM INV 26	22,000	600	1,700	22.11/30.42/101.4	44.11/64.2/90.1	1x16C	חזנה במעבה

יחידות מזוג סינגל-מאיד+מעבה									
מס' יחידה בתכנית	חוצרת	דגם	תפוקת קרור Btu/h	ספיקת אוויר CFM	הספק עבודה למנוע W	מידות מאיד	מידות מעבה	נתיב דגם c	הערות
10-1	Tadiran	SUPER SLIM INV 35	30,000	750	2,620	22.11/30.42/101.4	44.11/64.2/90.1	1x20C	חזנה במעבה

##	Model name	length in project	factory length
10-4	ALFA PRO INV 140 NG	13.0	15
10-3	ALFA PRO INV 180 NG	9.0	15
10-6		6.0	15
10-7		7.0	15
10-8		7.5	15
10-5	ALFA PRO INV 240 NG	9.0	15
10-2	SUPER SLIM INV 26	10.0	30
10-1	SUPER SLIM INV 35	16.5	30