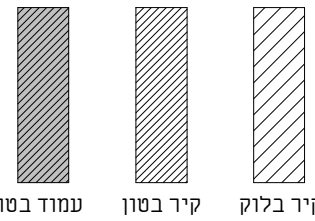


מתכונים:

ניהול פרויקט
מהיסוד - בן סולומון
פיקוח
מהיסוד - בן סולומון
קונסטרוקציה
ערן שילר
מיזוג אוויר
אייל ארז מהנדסים ויועצים בע"מ
אינסטלציה
איתן אלמסי
חשמל
איתן בסיס
אלומיניום
נוף
נתי בלוקא
חשמל חכם
חימום תת רצפתי
איטום
צבי טל
אקוסטיקה
מעליות
קרקע וביסוס
דיה הנדסת קרקע וביסוס
רישוי

[illegible]

מקרא קירות:

[illegible]

אדריכלות

CLIENT NAME: _____ שם המזמין:

קבוצת רכישה נופיה

PROJECT NAME: שם הפרויקט:

נופיה - מגרש 11

RAWING NAME: ס הגליון:

גליון שער

HEET NUMBER: 190 גליון:

A3-1-100

SCALE: קנה מידה: EDITION: הדורה:

STATUS: סטטוס
למכרז

דסט ע"י:	הילה כהנא	נבדק ע"י:
אריך:	22.09.25	א"ת:



NeumanHaynerArchitects


office@nh-arch.com
www.nh-arch.com

וימן חיינר אדריכלים
מורד ההדריס 2, בית חירות
טל 09-9545842

זכויות ייצור / ע"פ הנחיות עו"ד

נופיה - מגרש 11			
מס' גיליון	שם גיליון	מהדורה	תאריך הפצת מהדורה

22.09.2025	1	גליון שער	A3-1-100
22.09.2025	1	תכנית קומת קרקע	A3-1-101
22.09.2025	1	תכנית קומה א	A3-1-102
22.09.2025	1	מפלס גג	A3-1-103
22.09.2025	1	חזיתות 1	A3-2-200
22.09.2025	1	חזיתות 2	A3-2-201
22.09.2025	1	חתיכים	A3-3-100
22.09.2025	1	גליון מדגות	A3-4-100
22.09.2025	1	פרטים	A3-4-103
22.09.2025	1	פרטי פרגולה	A3-4-104
22.09.2025	1	רשימת פתחים	A3-6-1000

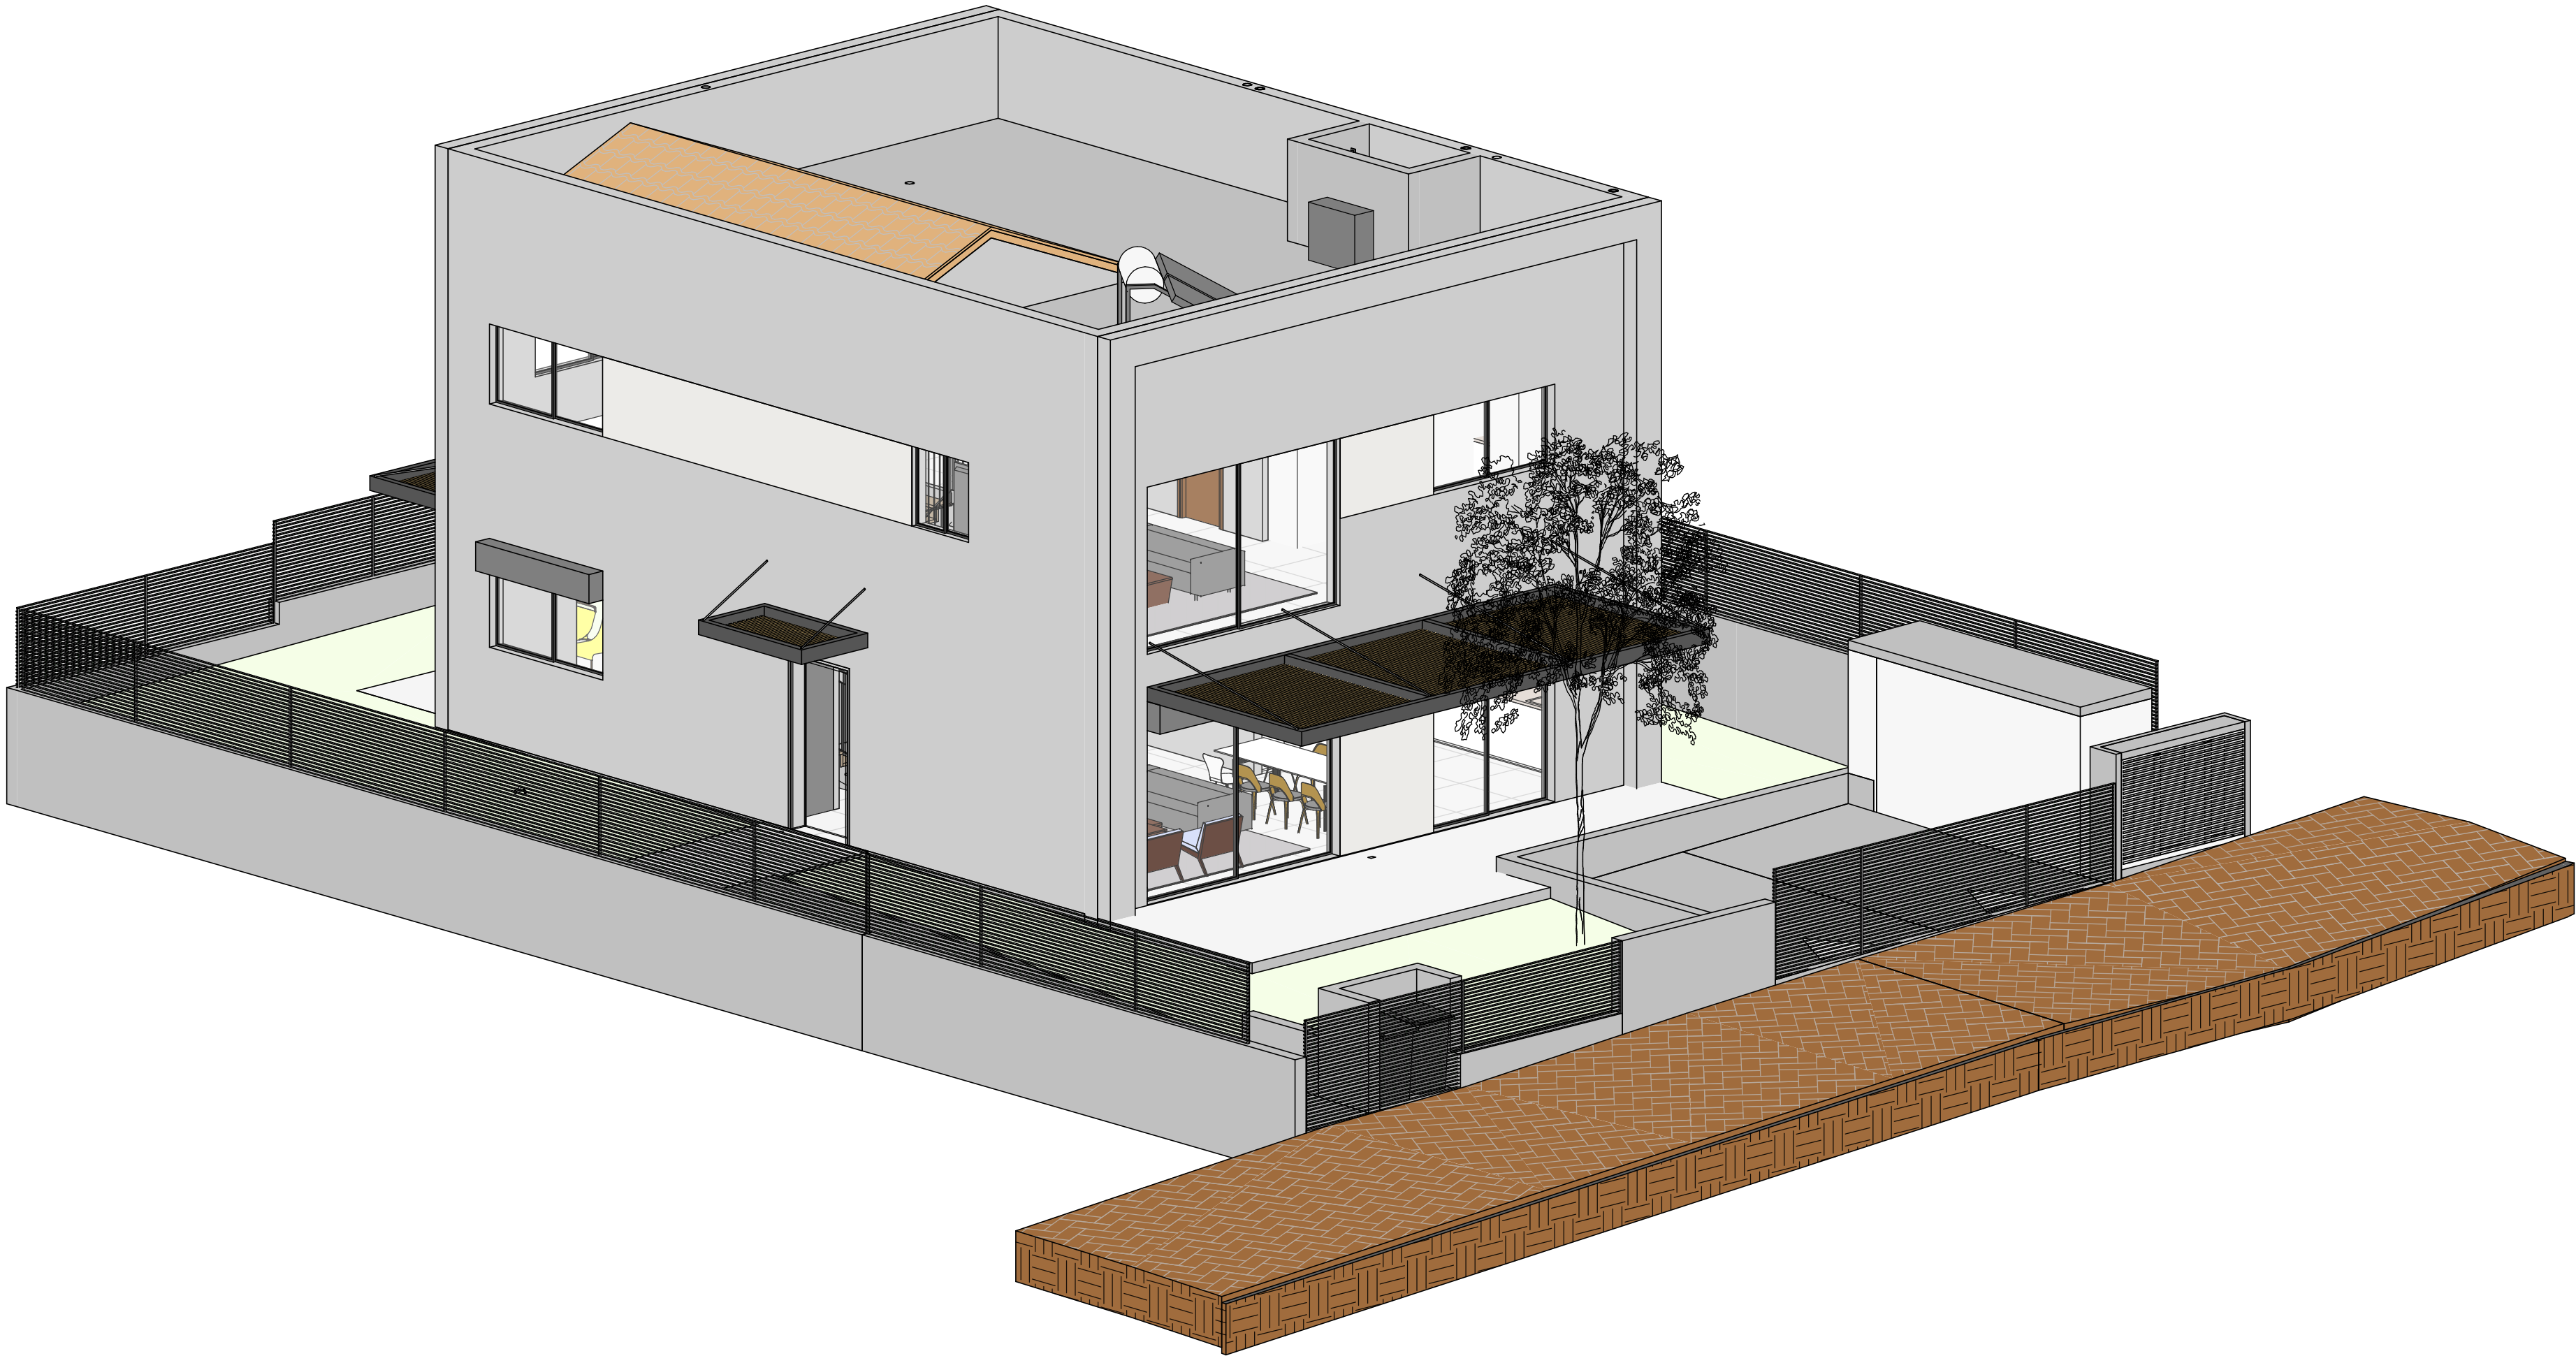

מהיסוד - בן סולומון	ניהל פדריקט
מהיסוד - בן סולומון	פיקוח
קונסטרוקציה	ערן שילר
מזוז אוויר	אייל אזר מהנדסים ויועצים בע"מ
אינסטלציה	איתן אלמסי
חשמל	איתן בסיס
אלומיניום	איתן בסיס
נוף	נתי בלוקא
חשמל חכם	חימום תת רצפתי
איטום	צבי טל
אקוסטיקה	מעליות
קרקע וביסוס	דיה הנדסת קרקע וביסוס
רישוי	

[illegible]

עמוד בטון קיר בטון זיג

[illegible]

CLIENT NAME:	המחלקה
קבוצת רכישה נופיה	
PROJECT NAME:	הפרויקט
נופיה - מגרש 11	
DRAWING NAME:	התכנון
תכנית קומת הרקע	
SHEET NUMBER:	פרט גליון
A3-1-101	


SCALE:	קנה מידה:	EDITION:	דורות:
1 : 50			
STATUS:	סטטוס		
למבר			
	נבדק ע"י:	הילה כהנא	דגסט ע"י:
DATE:	22.09.25		מ"ד:



וימן חיינר אדריכלים
 חורר ההדרים 2, בית חירות
 09-9545842 טל

office@nh-arch.com
 www.nh-arch.com

1. יש לעבוד במקביל לתכניות יועצים המאושרות על ידי האדריכל.
2. פרטי ספי חלון - עפ"י חוברת אלומיניום של הספק הנבחר ובתיאום מול אדריכל.
3. חימום תת רצפתי (במידה ויש במגרש זה) עפ"י פרטי הספק ובתיאום מול אדריכל.
4. יש לעבוד במקביל לתכניות עיצוב פנים (במידה ויש מעצב פנים במגרש זה) המאושרות על ידי האדריכל.
5. באחריות הקבלן לעדכן את האדריכל על אי התאמה בין התכניות יועצים לאדריכלות.
6. כל הדלתות לפי מפרט מצורף.
7. כל אלמנטי הבטון יקבלו התייחסות תרמית לפי הנחיות יועץ.
8. פרטי איטום, בידוד וניקוז עפ"י תכניות יועצים ובאחריות הקבלן.

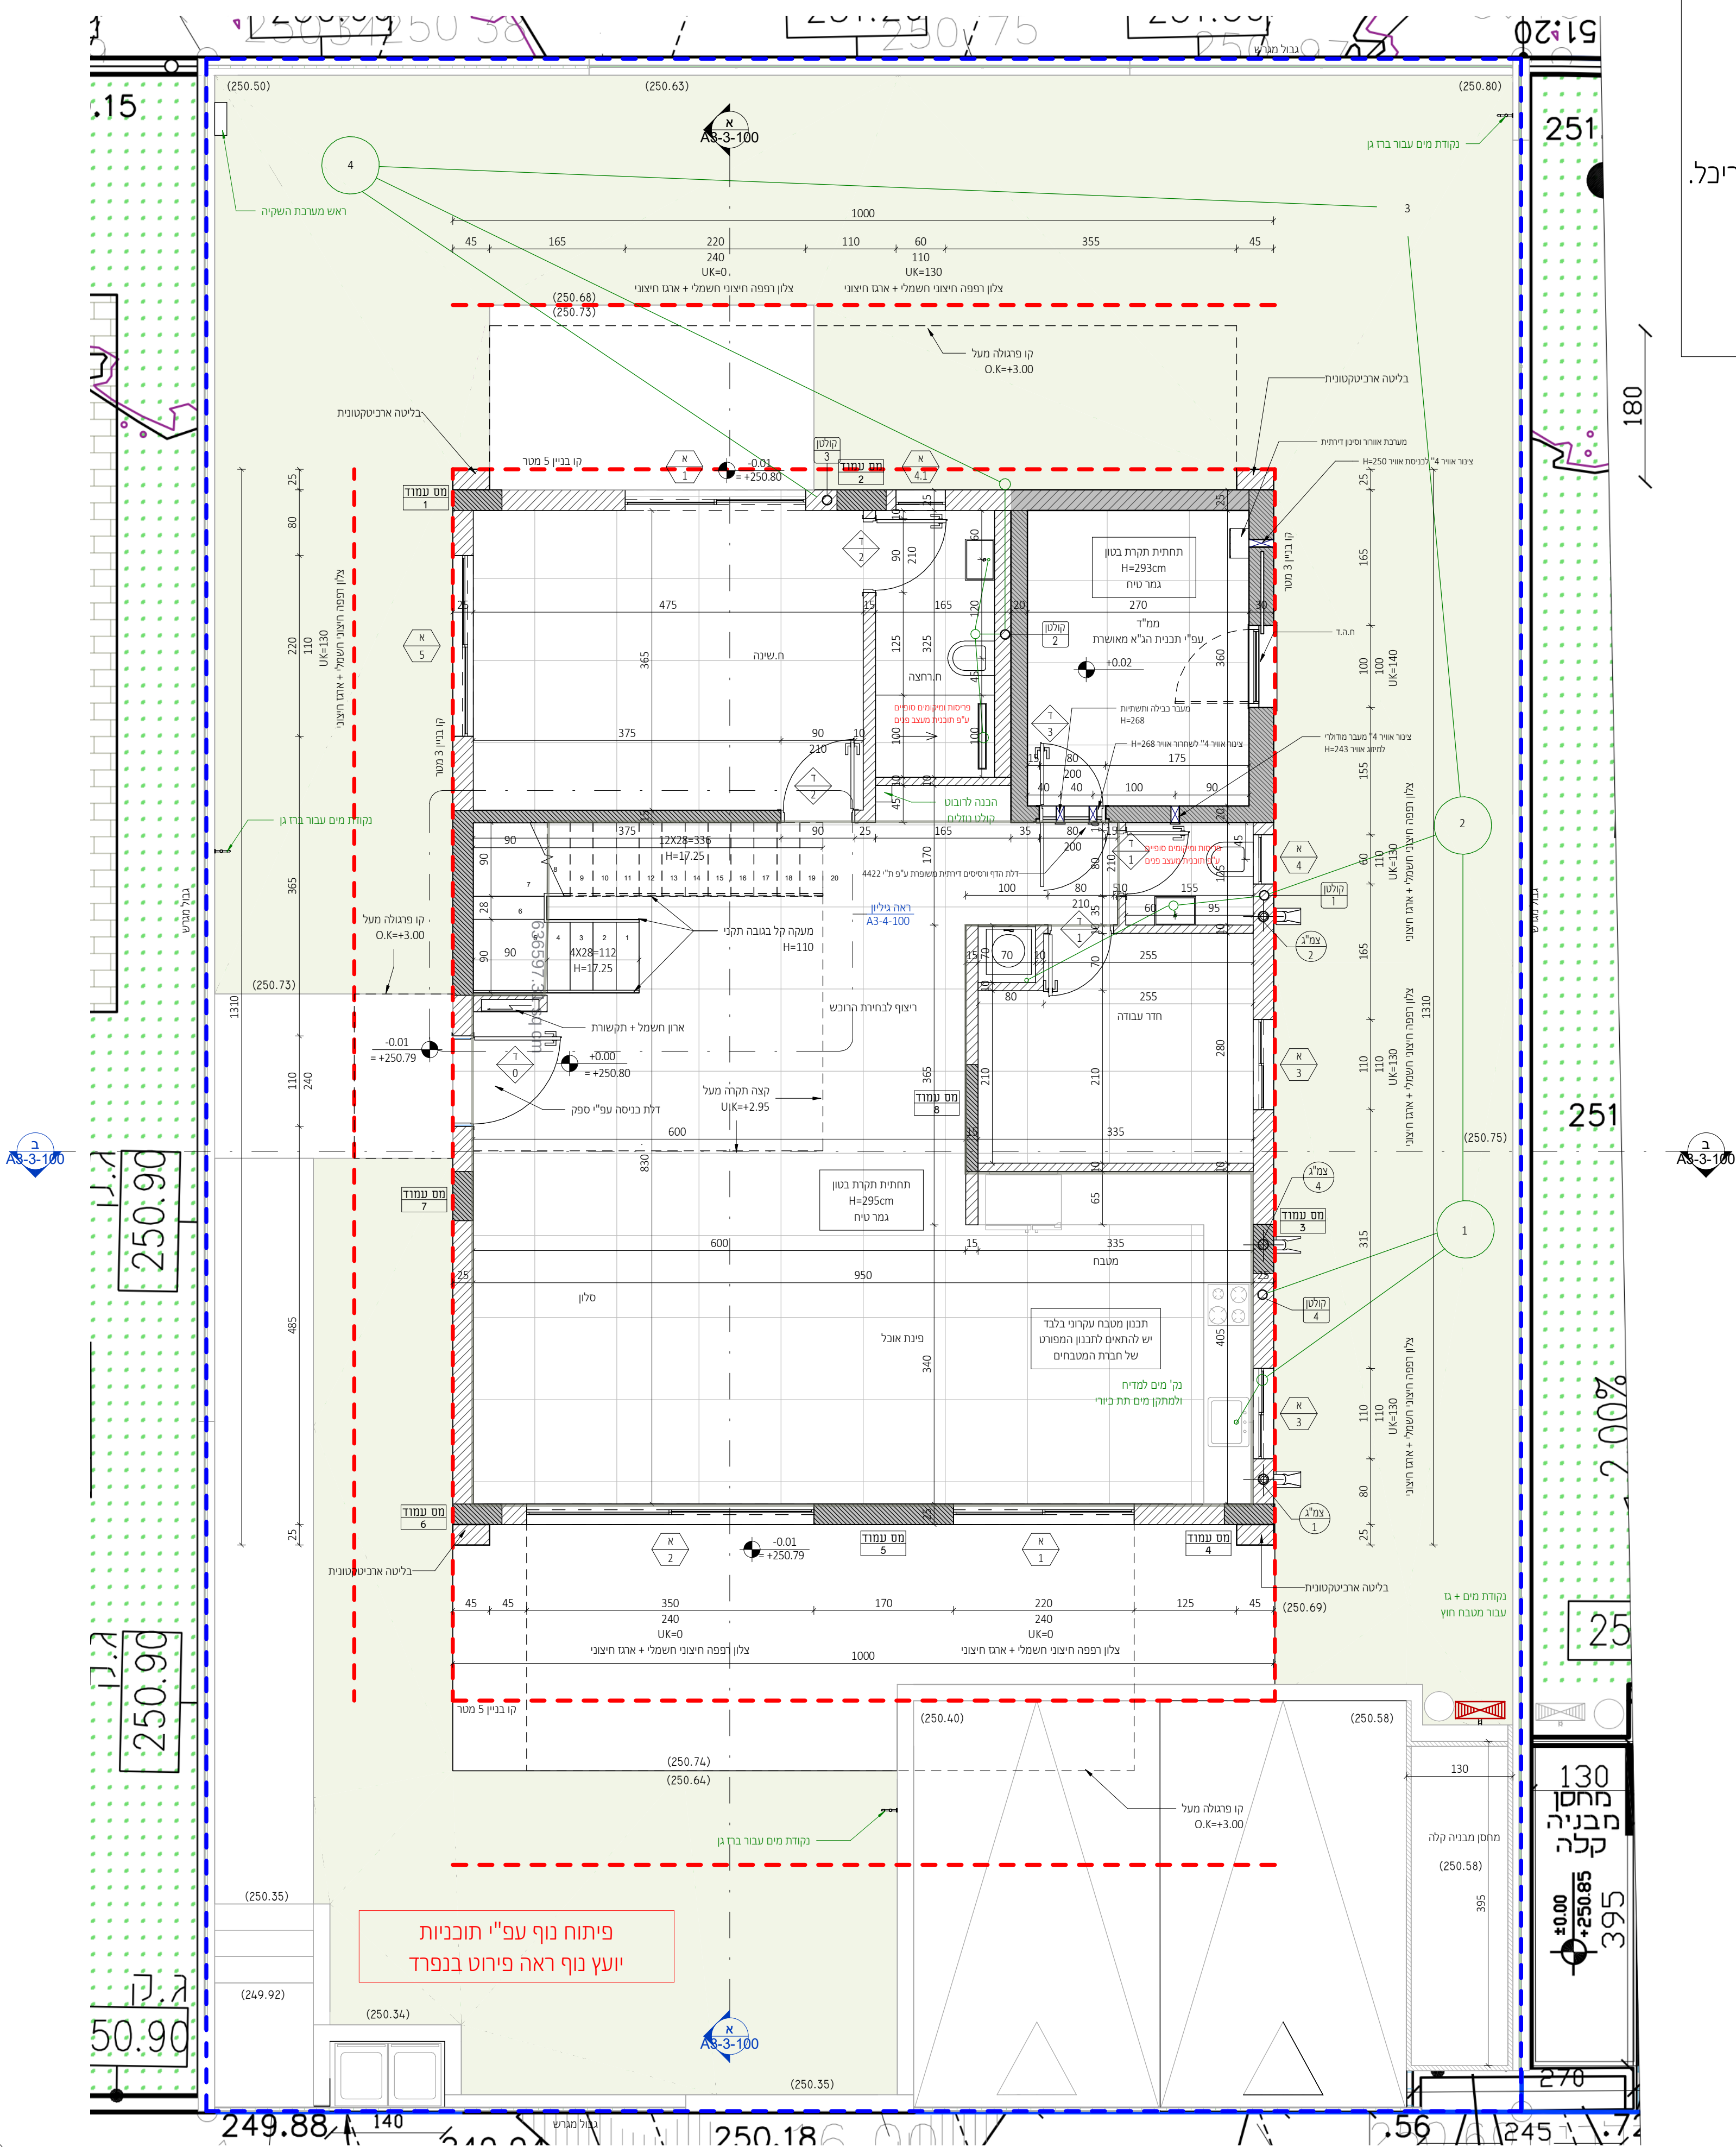


1 : 50

מתכונים:


ניהול פרויקט
מהיסוד - בן סולומון
פיקוח
מהיסוד - בן סולומון
קונסטרוקציה
ערן שילר
מיוזג אוויר
אייל ארז מהנדסים ויועצים בע"מ
אינסטלציה
איתן אלמסי
חשמל
איתן בסיס
אלומיניום
נוף
נתי בלוקא
חשמל חכם
חימום תת רצפתי
איטום
צבי טל
אקוסטיקה
מעליות
קרקע וביסוס
דיה הנדסת קרקע וביסוס
ירשני

[illegible]

מקרא קירות:

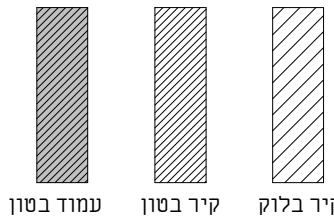[illegible]


אדריכלות

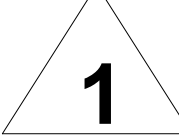PROJECT NAME:		הפרויקט:	
קבוצת רכישה נופיה			
DRAWING NAME:		הציור:	
נופיה - מגרש 11			
SHEET NUMBER:		פר הציור:	
תכנית קומה א			
SCALE:		קנה מידה:	
1 : 50		EDITION:	
STATUS:		מסמך	
למכר			
DATE:		22.09.25	
ירי		הילה בהנא	

NeumanHaynerArchitects

office@nh-arch.com
www.nh-arch.com

זכריות ייצור / ע"פ הנחיות עו"ד

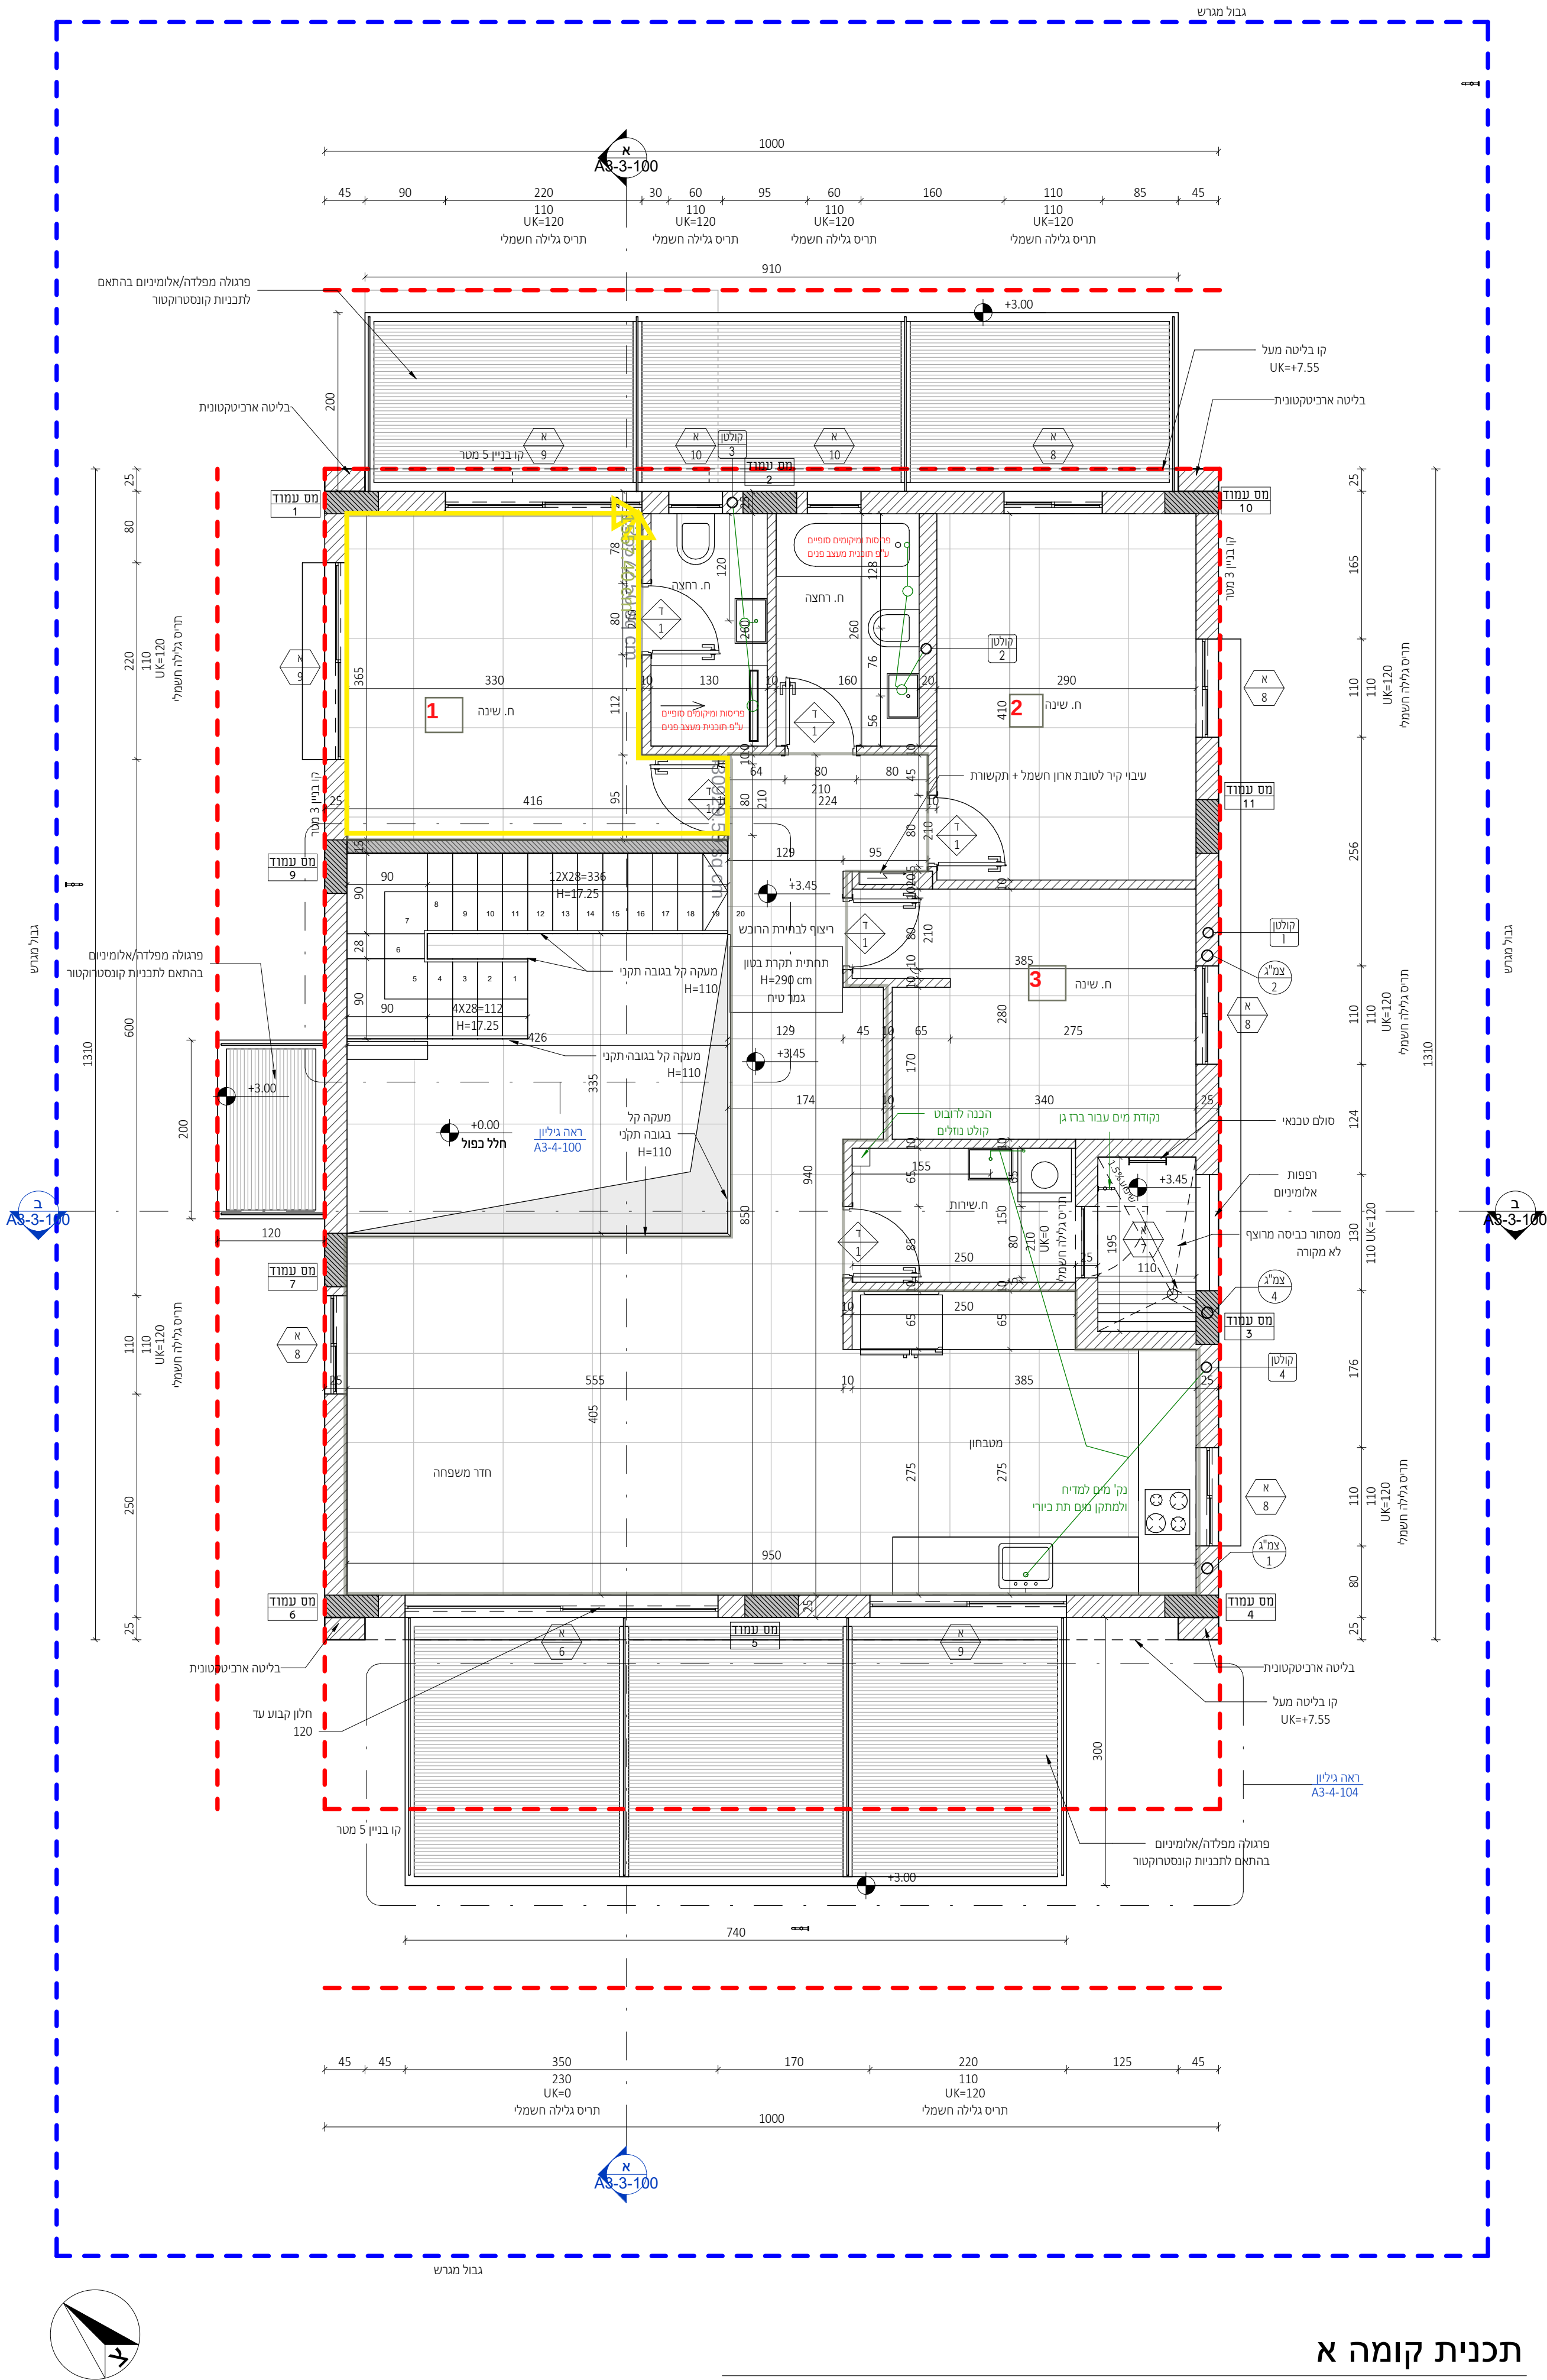


תכנית קומה א


הערות:

1. יש לעבוד במקביל לתכניות יועצים המאושרות על ידי האדריכל.
2. פרטי ספי חלון - עפ"י חוברת אלומיניום של הספק הנבחר ובתיאום מול אדריכל.
3. חימום תת רצפתי (במידה ויש במגרש זה) עפ"י פרטי הספק ובתיאום מול אדריכל.
4. יש לעבוד במקביל לתכניות עיצוב פנים (במידה ויש מעצב פנים במגרש זה) המאושרות על ידי האדריכל.
5. באחריות הקבלן לעדכן את האדריכל על אי התאמה בין התכניות יועצים לאדריכלות.
6. כל הדלתות לפי מפרט מצורף.
7. כל אלמנטי הבטון יקבלו התייחסות תרמית לפי הנחיות יועץ.
8. פרטי איטום, בידוד וניקוז עפ"י תכניות יועצים ובאחריות הקבלן.

פרטי איטום, בידוד וניקוז עפ"י תכניות יועצים ובאחריות הקבלן

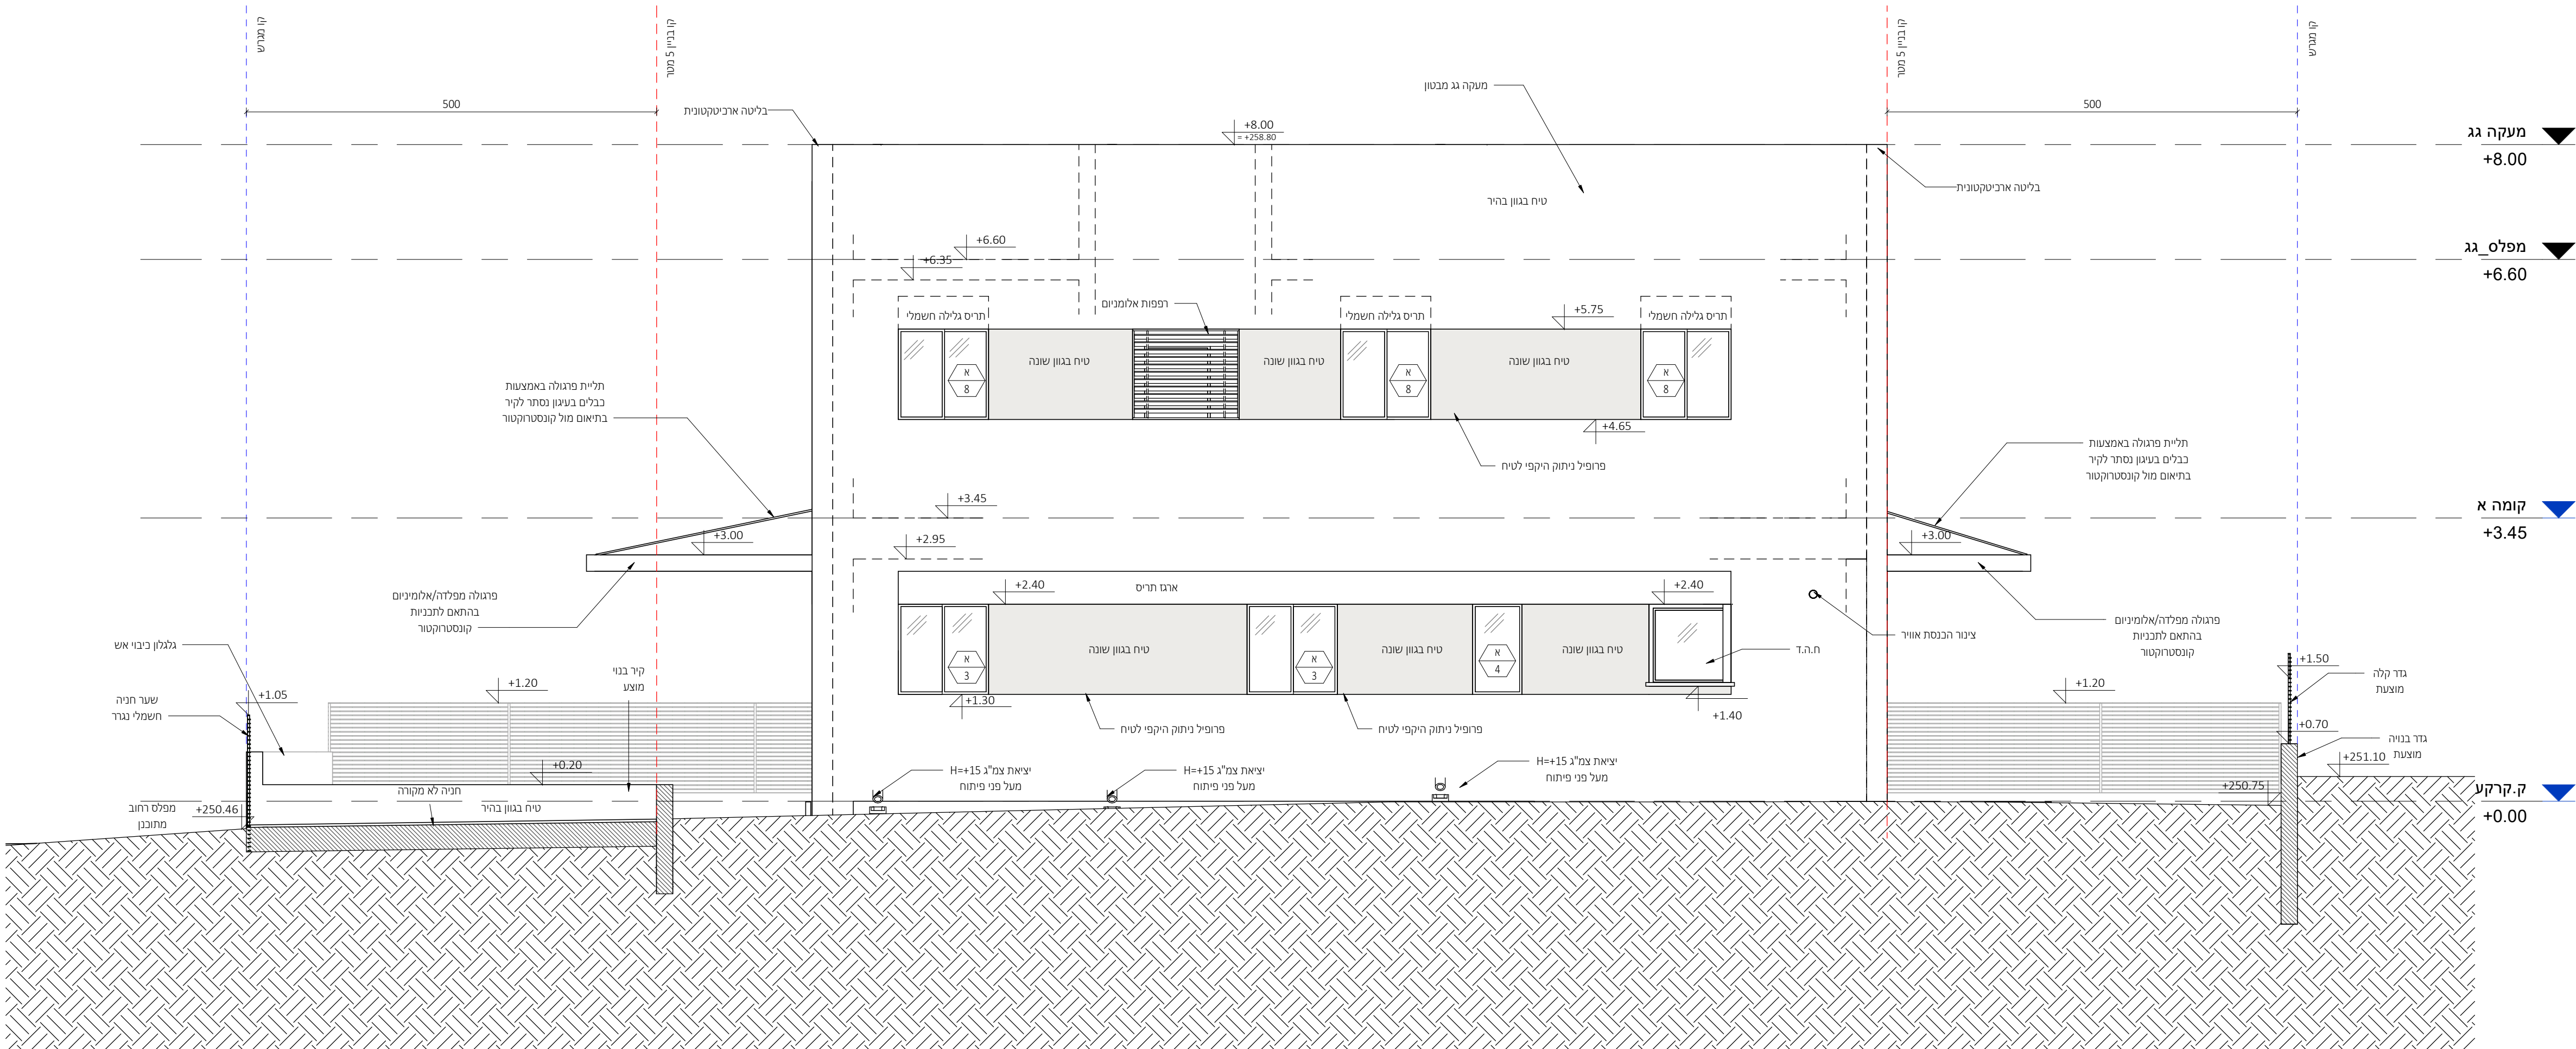

פיתוח נוף עפ"י תוכניות
יועץ נוף ראה פירוט בנפרד

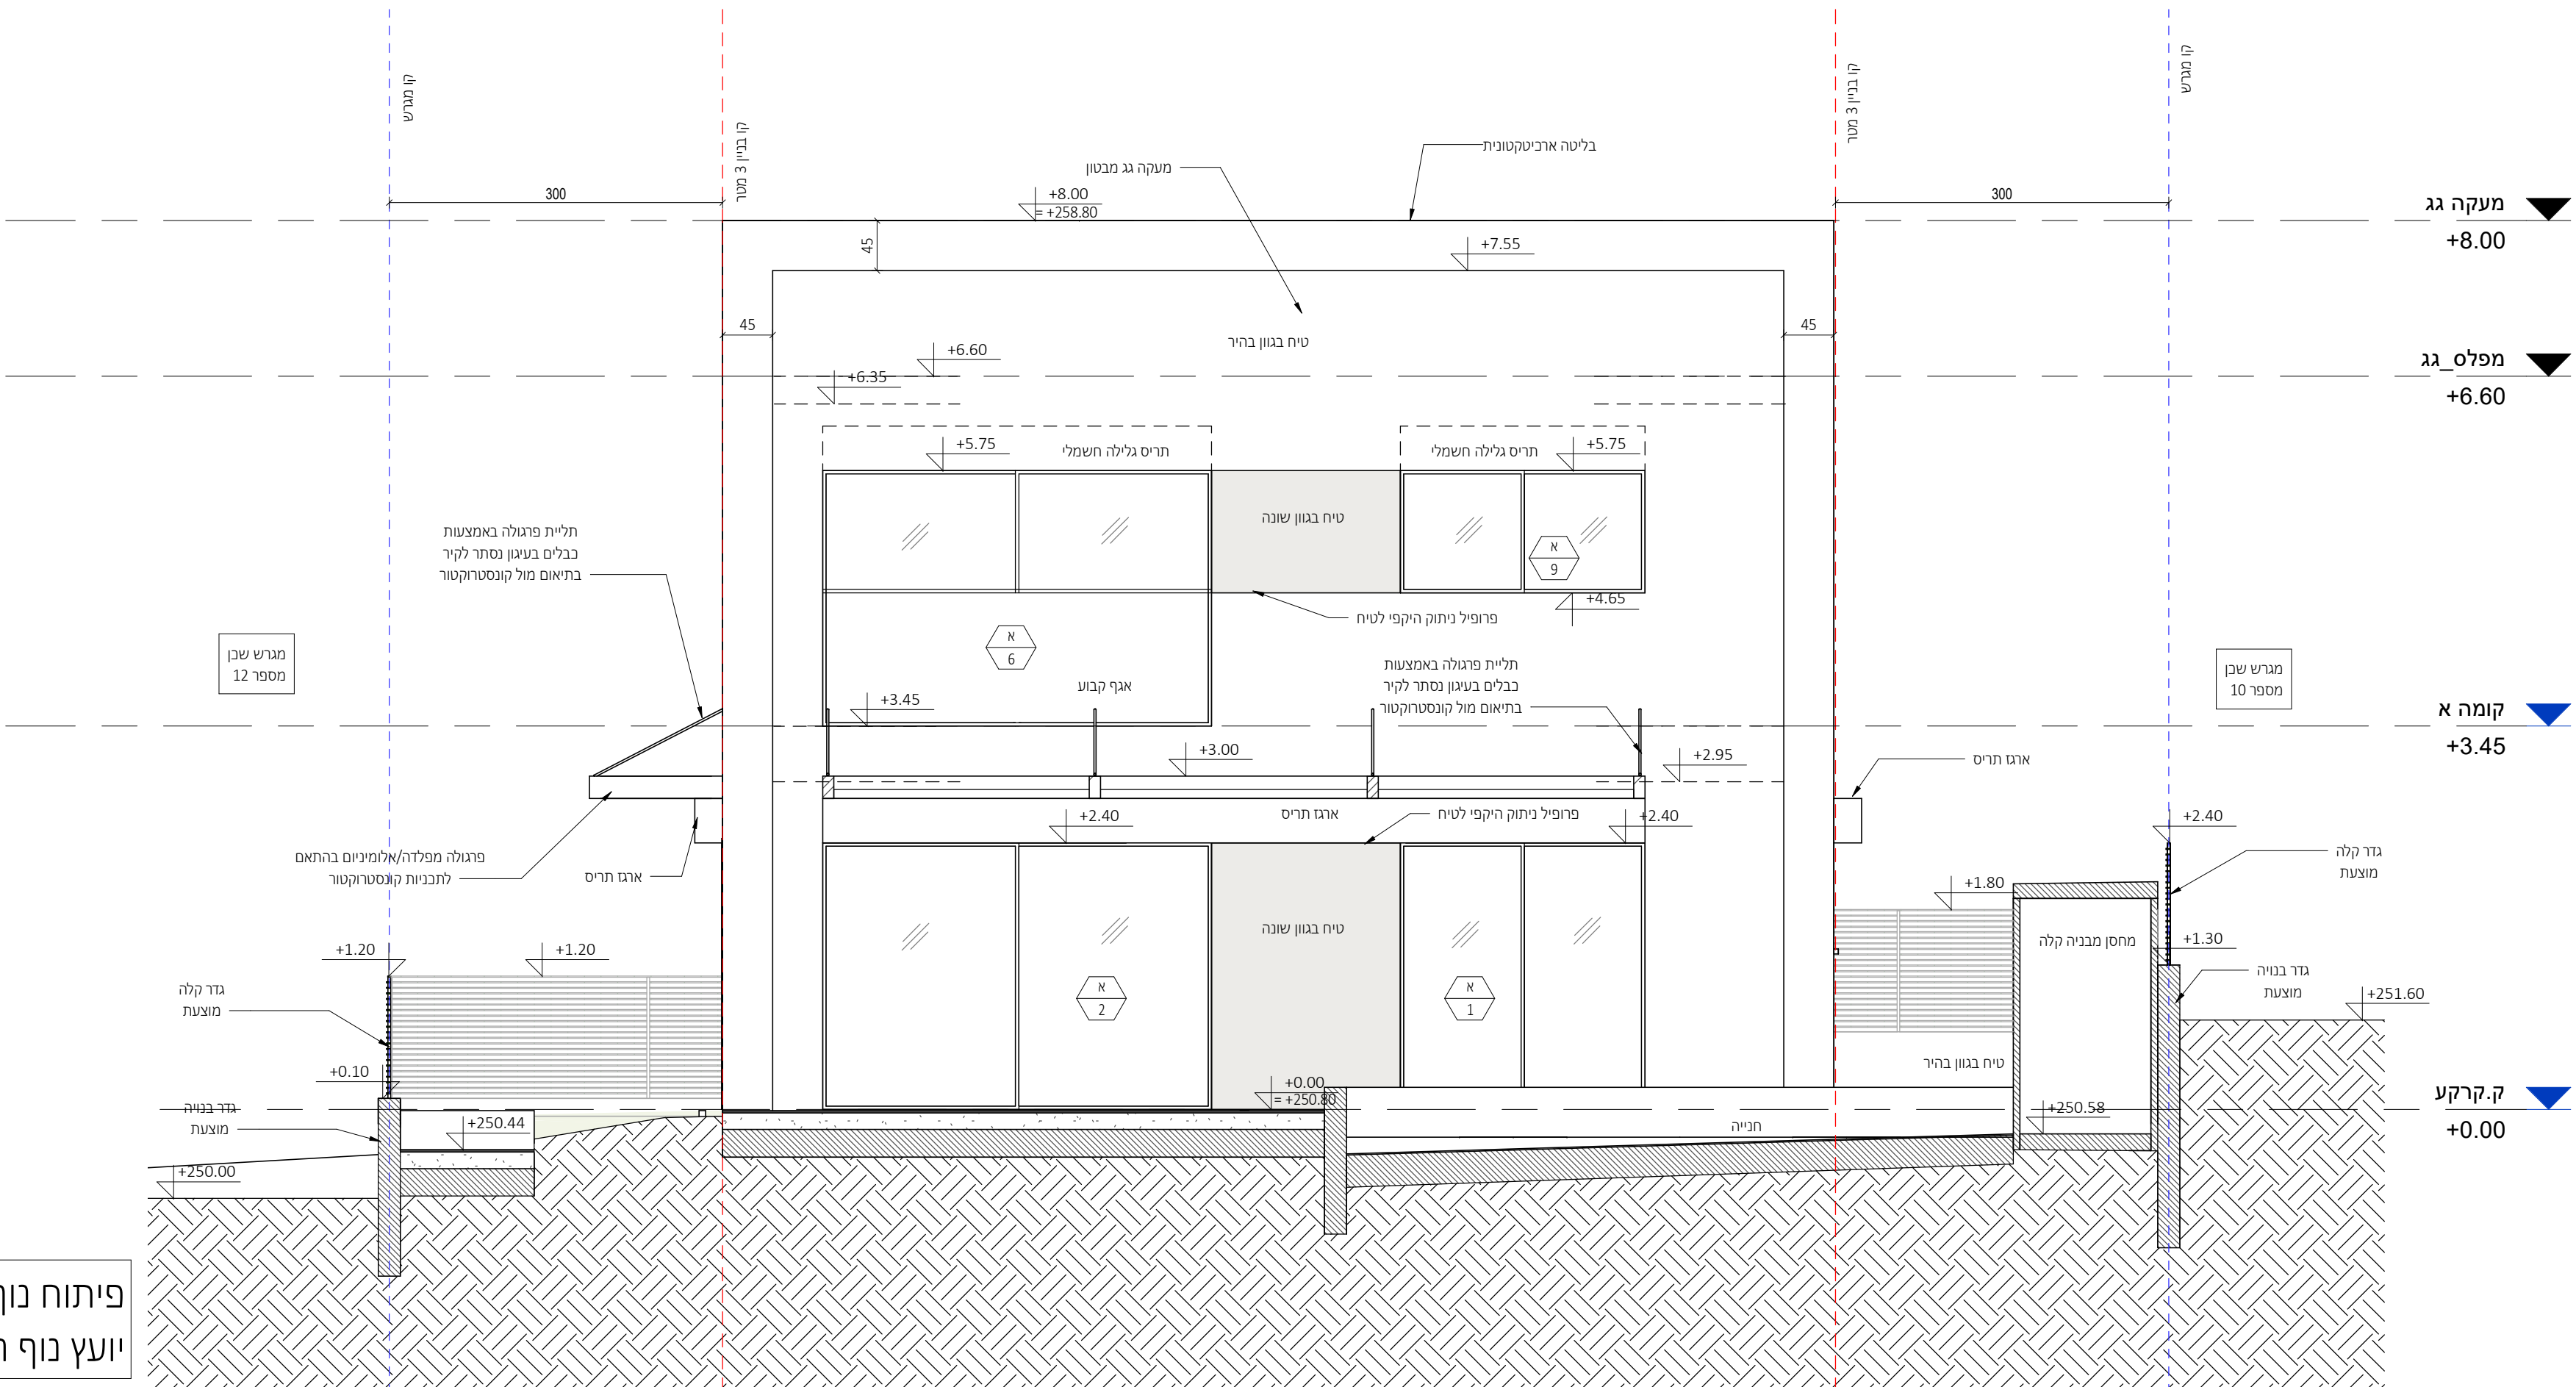

פיתוח נוף עפ"י תוכניות
יועץ נוף ראה פירוט בנפרד


חזית דרום מערבית

1 : 50

מיתכננים:	
ביהל פרויקט	
מהיסוד - בן סולומון	
פיקוח	
מהיסוד - בן סולומון	
קונסטרוקציה	
ערן שילר	
מיוז אוויר	
איל ארז מהנדסים ויועצים בע"מ	
אינסטלציה	
איתן אלמסי	
חשמל	
איתן בסיס	
אלומיניום	
נוף	
נתי בלוקא	
חשמל חכם	
חימום רצפת חפתי	
איטום	
צבי טל	
אקוסטיקה	
מעליות	
קרקע וביסוס	
דיה הנדסת קרקע וביסוס	
רשיו	

תשובה	אחוז
כן	50%
לא	50%

[illegible]

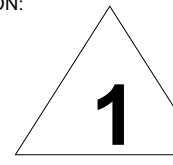CLIENT NAME:		המספר:	
קבוצת רכישה נופיה			
PROJECT NAME:		הפרויקט:	
נופיה - מגרש 11			
DRAWING NAME:		התאריך:	
חזיתות 1			
SHEET NUMBER:		פרג'נט:	
A3-2-200			
CALL:	קנה מידה:	EDITION:	דור:
1 : 50			
TATUS:	סטוס		
למכר			
	(בדף ע"י):	הילה כהנא	סטוס ע"י:
DATE:	22.09.25		ירד:

מעקה גג
+8.00

מפלס גג
+6.60

קומה א
+3.45

ק.קרקע
+0.00

חזית צפון מזרחית

1 : 50

מעקה גג
+8.00

מפלס גג
+6.00

קומה א
+3.45

ק.קרקע
+0.00

מפלס רחוב
+249.92

חזית צפון מערבית

1 : 50

מתכננים:


ניהול פרויקט
מהיסוד - בן סולומון
פיקוח
מהיסוד - בן סולומון
קונסטרוקציה
ערן שילר
מיזוג אוויר
אייל ארז מהנדסים ויועצים בע"מ
אינסטלציה
איתן אלמסי
חשמל
איתן בסיס
אלומיניום
נוף
נתי בלוקא
חשמל חכם
חימום תת רצפתי
איטום
צבי טל
אקוסטיקה
מעליות
קרקע וביסוס
דיה הנדסת קרקע וביסוס
רישוי

± 0.00 = +250.80

- הערות:
1. תכנית זו יש לקרוא יחד עם תכנית הריטשים.
 2. גובה אבטמטיסי: ראה תכנית פיתוח.
 3. הפרדות הן בין קירות הבניה ולא כולל פיתח.
 4. פיתוח השטח סביב הבנינה, כולל, מדרגות, גדרות, שבילים, ריצופים, שטחים גזרים, חניה וכו' ראה תכנית פיתוח.
 5. איטום קירות ורצפות הבניה כמעט עם הקרקע ובידוד תרמי לאורך העמודים והקירות וכל התפרים. כליות יא עם סימני גימון. ראה תכנית קונסטרוקציה.
 6. אף דום יבוצע בכל מישור אופקי הכולל חתוכי.
 7. פיתוח תרמי במסגרת ע"פ מפרט תרמוקיר, מאושר ע"י פיקוח העיר.

המבצע אחראי לסידור: עליו לבקר ולבדוק את כל הפרדות בתכנית ובקשות הבניה. במקרה של שינוי או אי התאמה בתכנית /או בבנין, עליו להודיע על כך מיד לאדריכל בסופו המשיך בעבודתו. המבצע יחזיק את רוב התכנית שאושר לביצוע. המבצע יחזיק את כל המבצע, כולל המבצע, של המבצע. את לקבוע מידות של יד חתיה בשטח. התכנית הנה תכנית האדריכל ואין לשנות כל שינוש בה או ברעיונות הגלומים בה, אלא באישור בכתב מהאדריכל. מתנדס /או יועץ אשר שמו רשום בתכנית זו, נושא לכך באחריות המקצועית והתקנית לתכנית. על התפתח והשקלן ליוזא התאמת התכנית האדריכלית "לביצוע" לתכנית כוללת את כל האחריות והודע על ליום תוצאת.

משרד קירות:

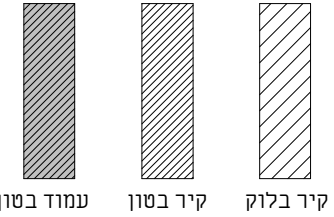

תאריך	תיאור	מהדורה
22.09.2025	מכרז	1

אדריכלות

שם המשיין:	CLIENT NAME:
קבוצת רכישה נופיה	
שם הפרויקט:	PROJECT NAME:
נופיה - מגרש 11	
שם הגיליון:	DRAWING NAME:
חזיתות 2	
מספר גיליון:	SHEET NUMBER:
A3-2-201	
תאריך:	DATE:
22.09.25	

NeumanHaynerArchitects


נירן חיינו אדריכלים
מודל התדוים 2, בית חירות
09-9546842

office@nh-arch.com
www.nh-arch.com


20102025 16:01:02

זכיות ייצור / ע"פ הנחיות ע"ד

פיתוח נוף עפ"י תוכניות
יועץ נוף ראה פירוט בנפרד

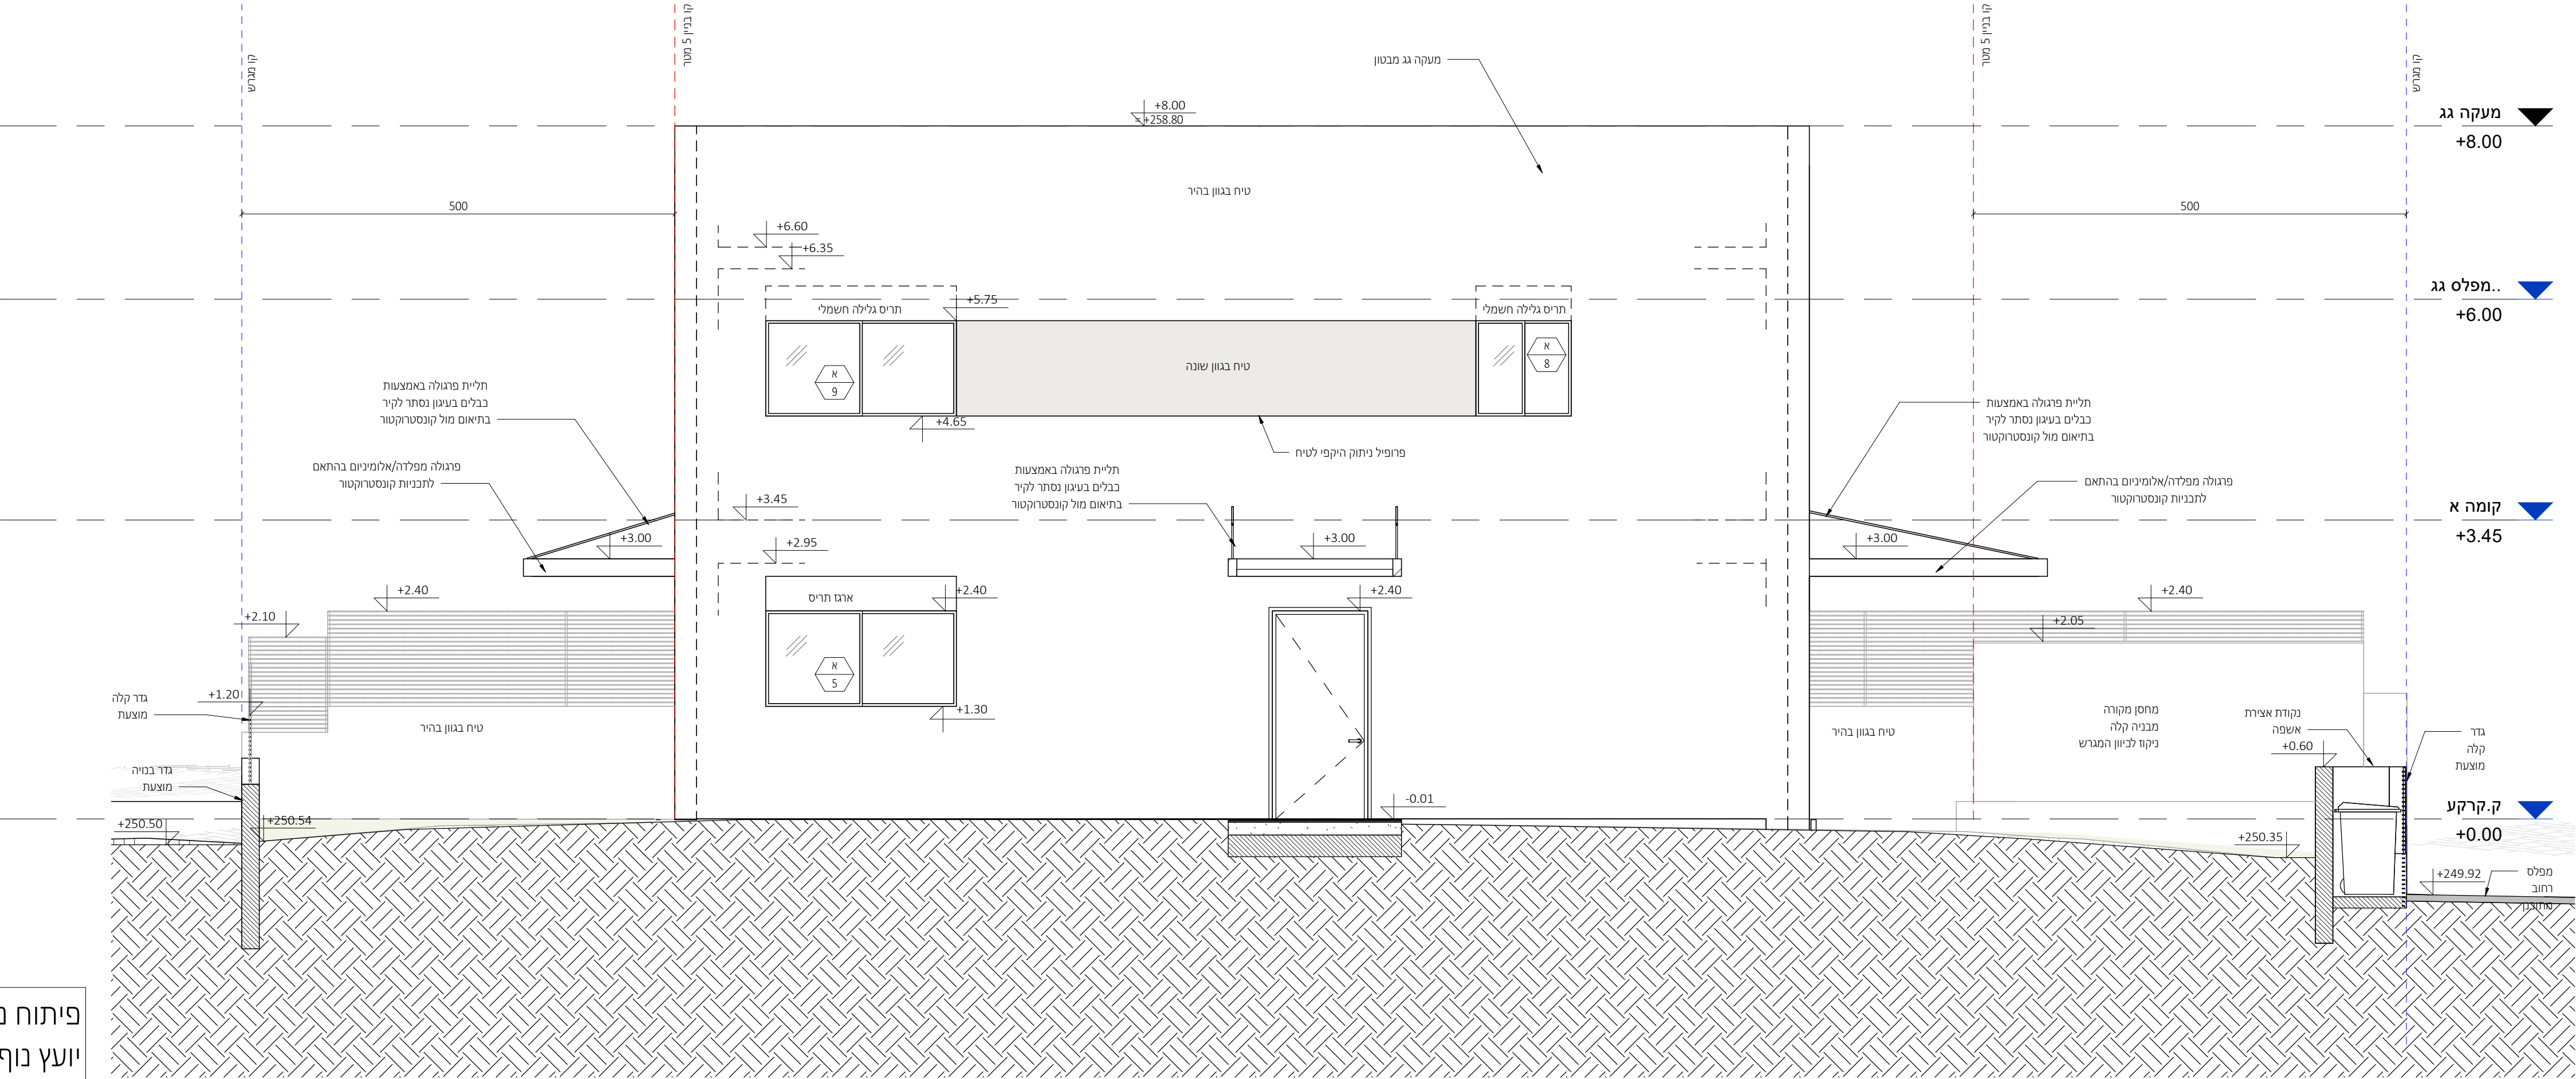

פיתוח נוף עפ"י תוכניות
יועץ נוף ראה פירוט בנפרד

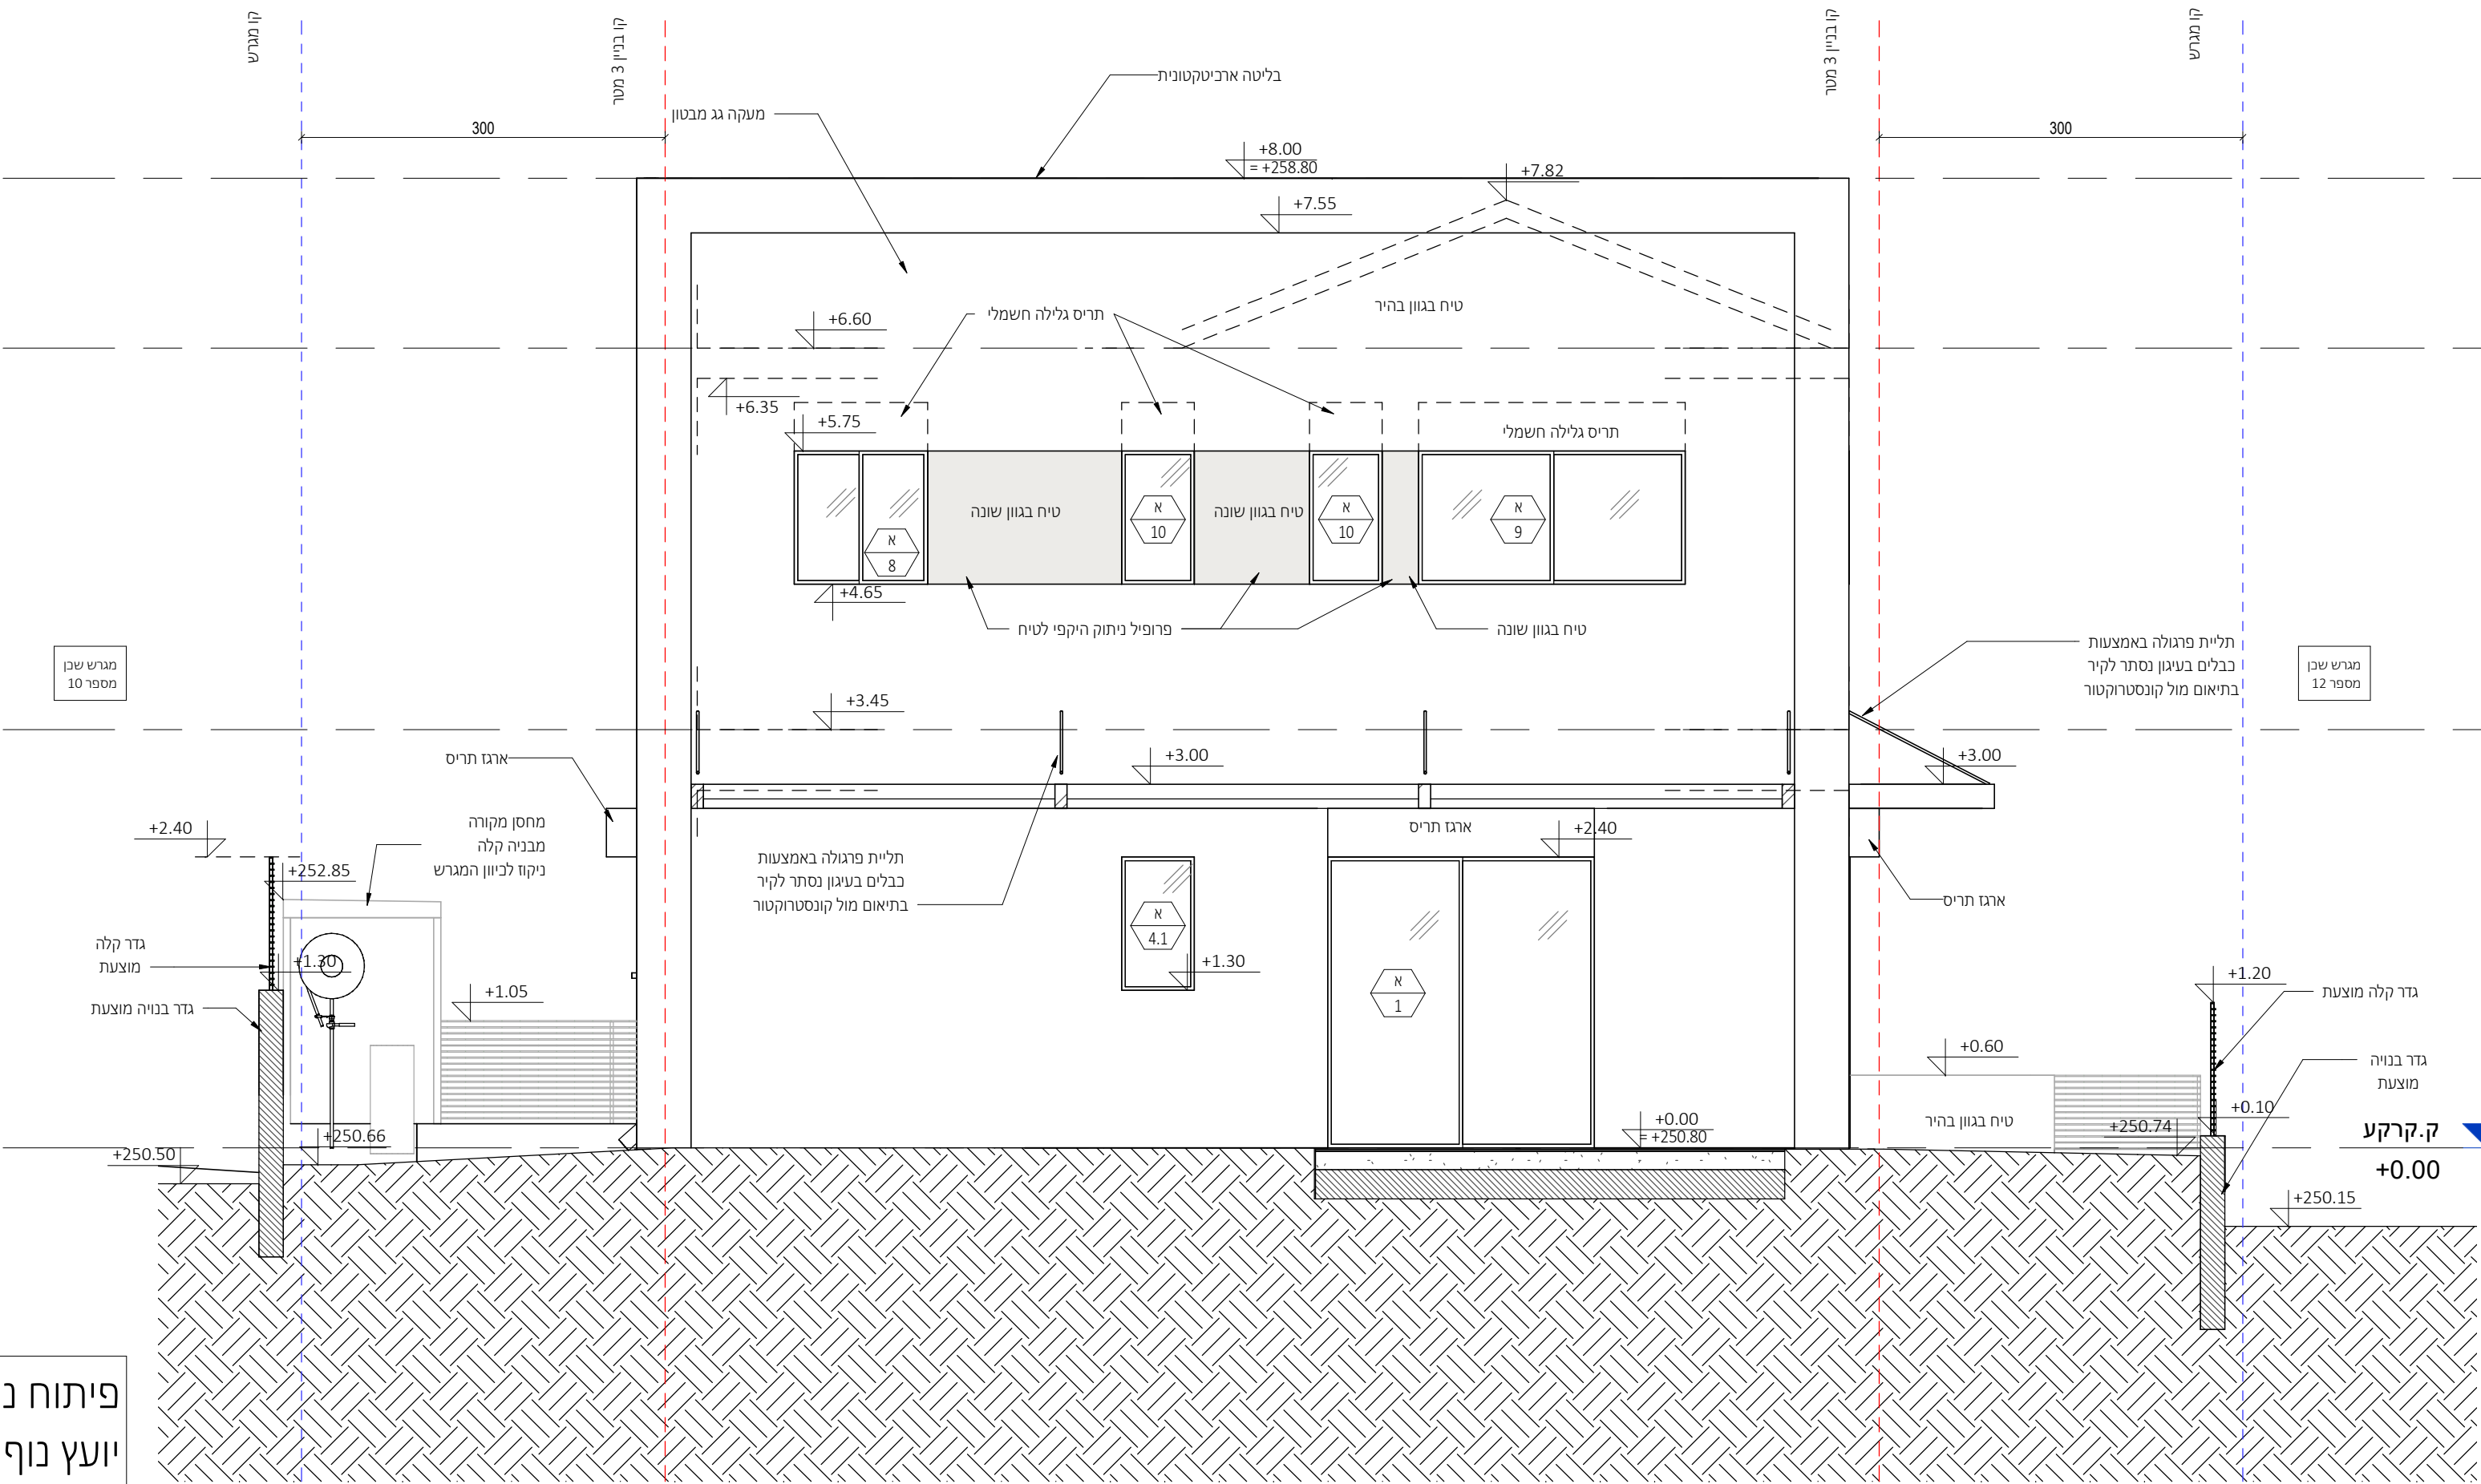

מתכונים:



ניהול פרויקט
מהיסוד - בן סולמון
פיקוח
מהיסוד - בן סולמון
קונסטרוקציה
ערן שילר
מיוזג אוויר
איל ארז מהנדסים ויועצים בע"מ
אינסטלציה
איתן אלמסי
חשמל
איתן בסיס
אלומיניום
נוף
נתי בלוקא
חשמל חכם
חימום תת רצפתי
איטום
צבי טל
אקוסטיקה
מעליות
קרקע וביסוס
דיה הנדסת קרקע וביסוס
רישוי

שנה	כן	לא	אין לי מושג
2006	25%	65%	10%
2007	55%	35%	10%
2008	45%	45%	10%

[illegible]

אדריכלות

הפריטים:	
קבוצת רכישה נופיה	
הפרויקט:	PROJECT NAME:
נופיה - מגרש 11	
הנגזירן:	DRAWING NAME:
חתיכים	
פר גניין:	SHEET NUMBER:
A3-3-100	
דורה:	EDITION:
ענה מידה:	SCALE:
מסוס	1 : 50
מסוס עיי'	TATUS:
למכור	
הילה הנבא	נבדק עיי':
יורי:	DATE:
	22.09.25

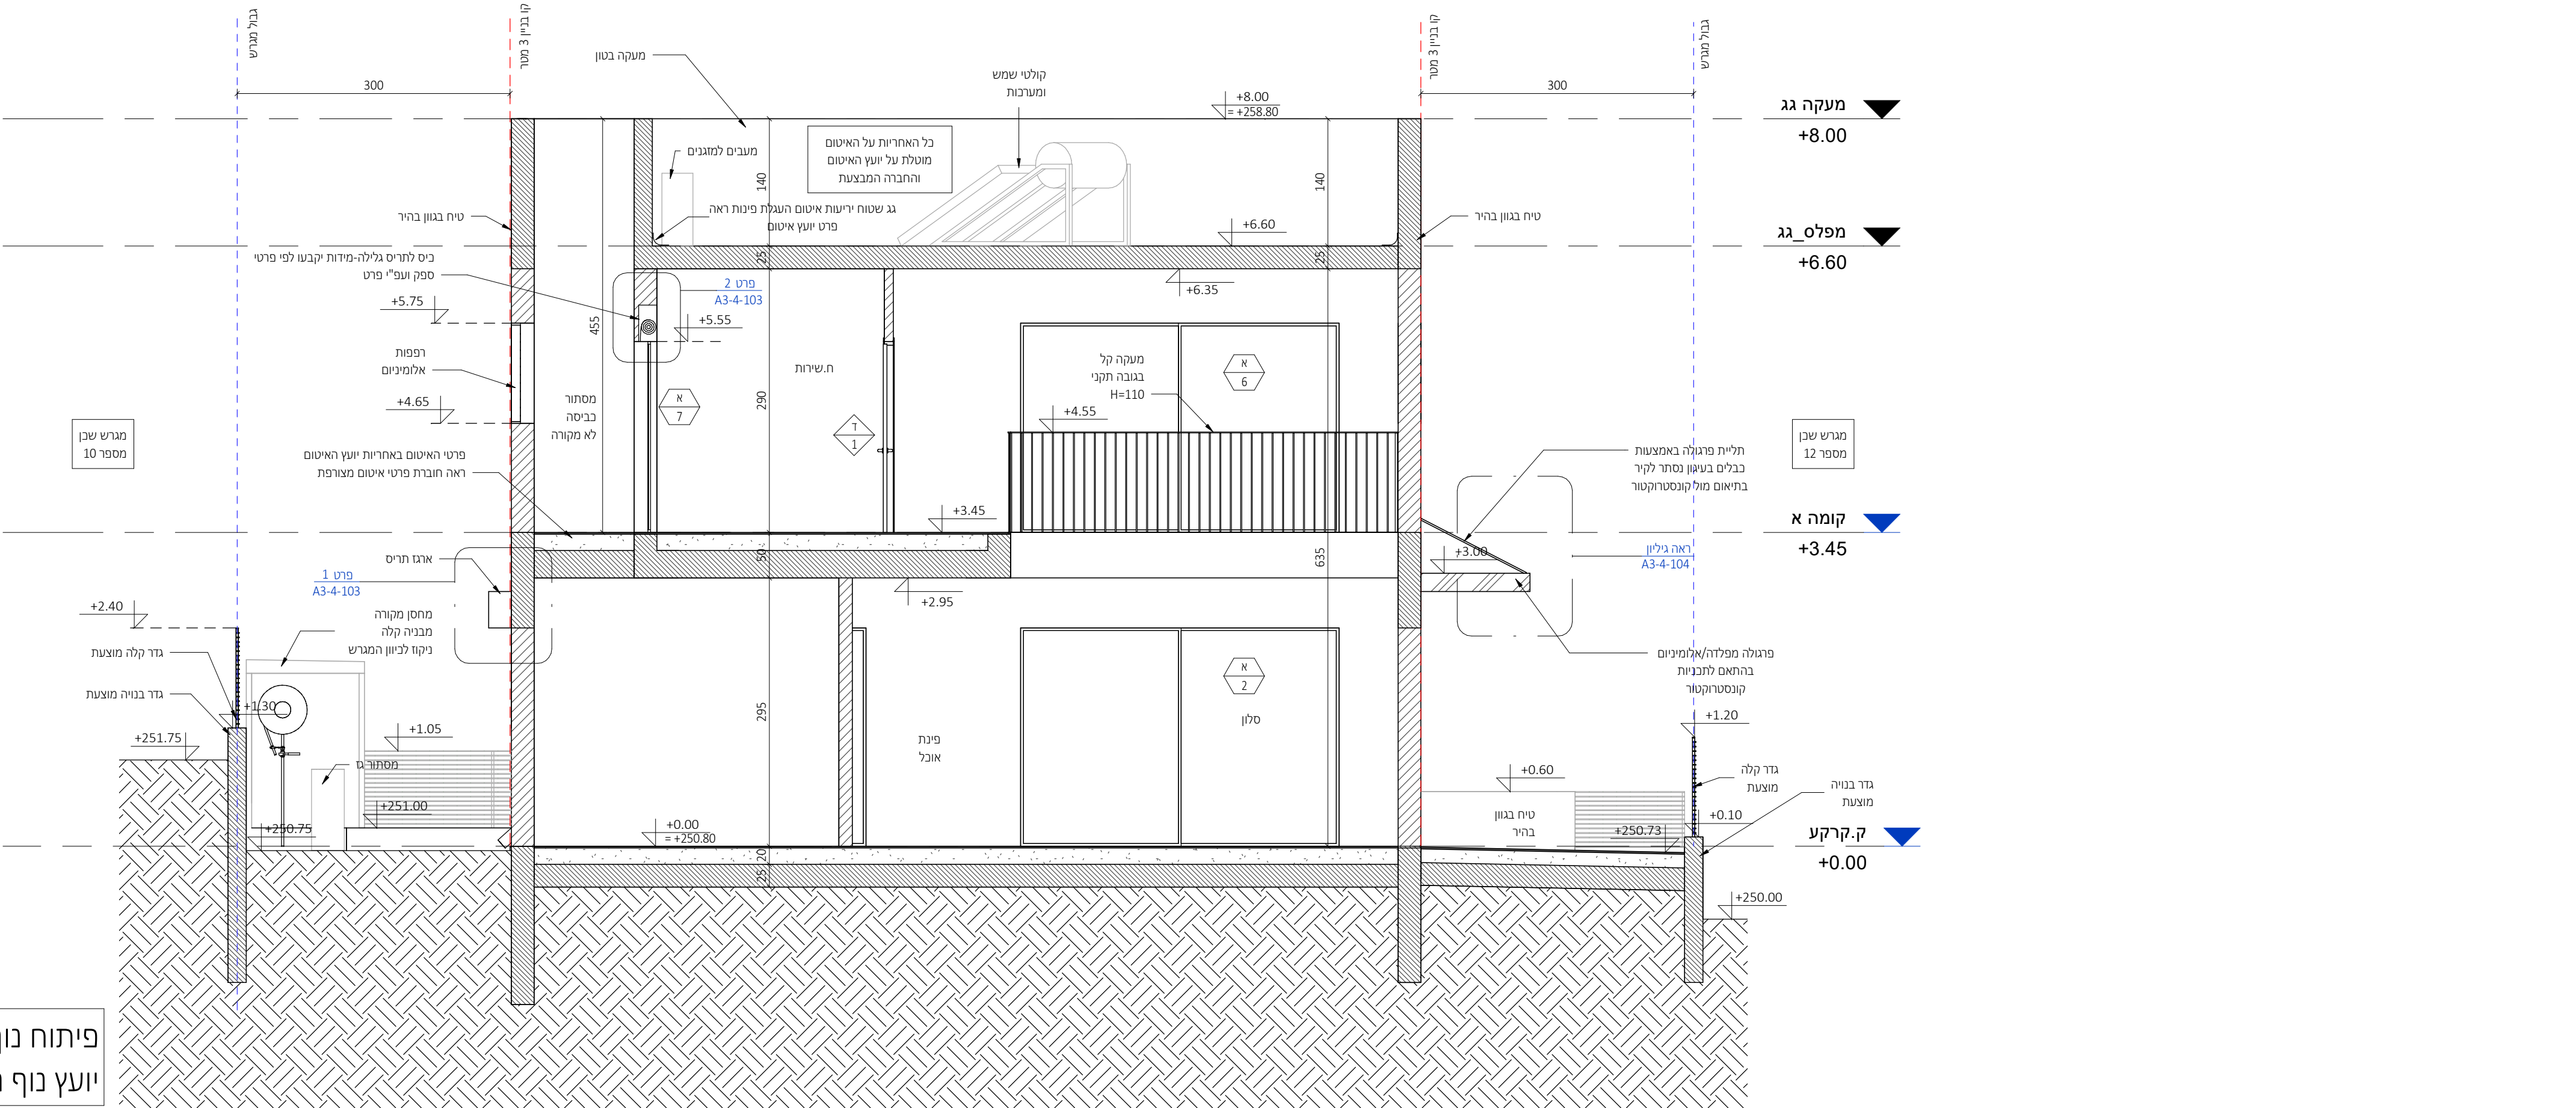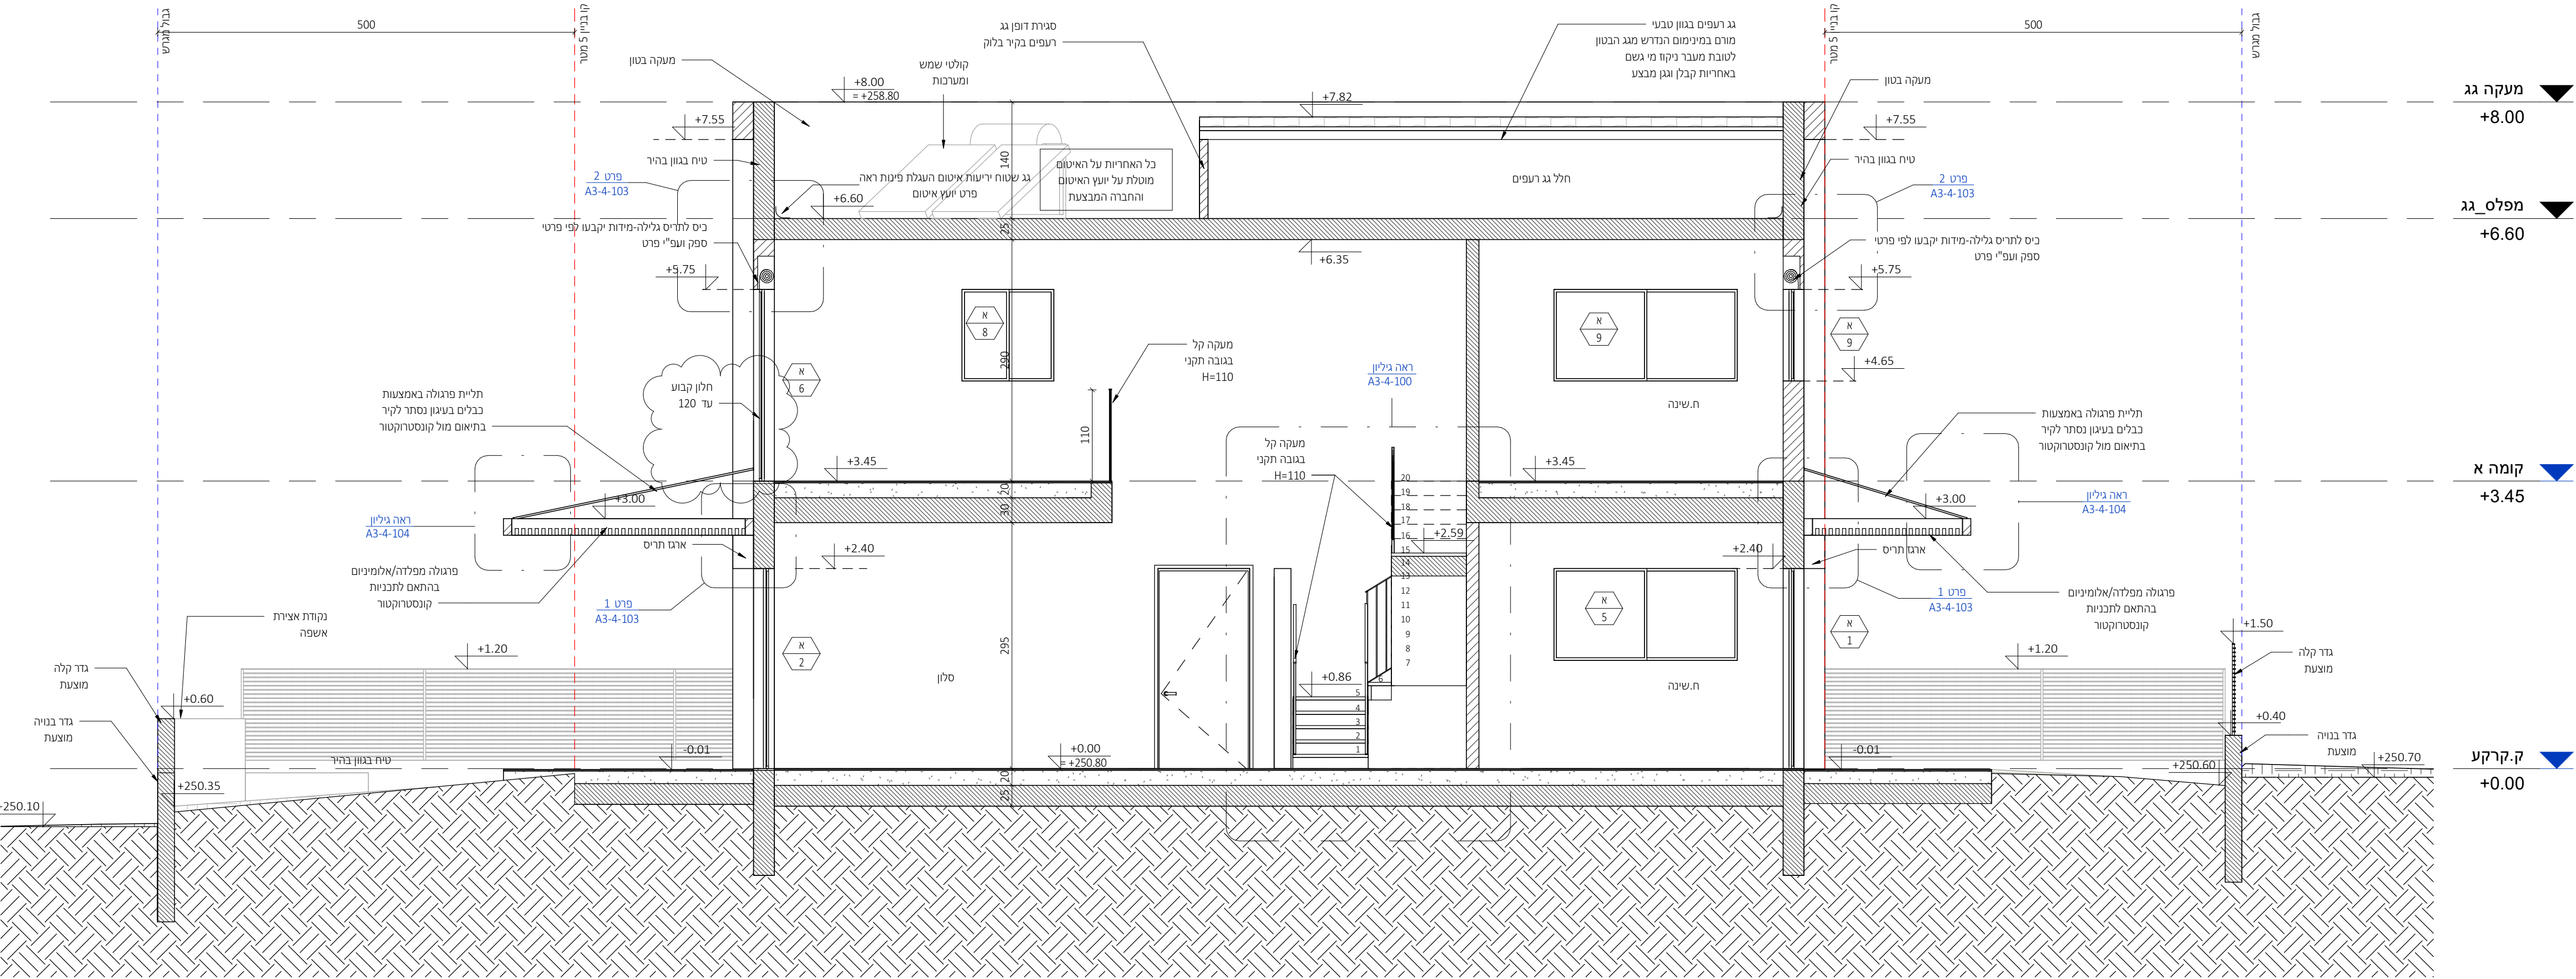

ניהול פרויקט
מהיסוד - בן סולומון
פיקוח
מהיסוד - בן סולומון
קונסטרוקציה
ערן שילר
מיזוג אוויר
אייל ארז מהנדסים ויועצים בע"מ
אינסטלציה
איתן אלמסי
חשמל
איתן בסיס
אלומיניום
נוף
נתי בלוקא
חשמל חכם
חימום תת רצפתי
איטום
צבי טל
אקוסטיקה
מעליות
קרקע וביסוס
דיה הנדסת קרקע וביסוס
רישוי

[illegible]


עמוד בטן קיר בטון בלוק

[illegible]

CLIENT NAME:		המחיר: 0	
PROJECT NAME:		שם הפרויקט:	
קבוצת רכישה נופיה			
נופיה - מגרש 11			
DRAWING NAME:		שם הגליון:	
גליון מדרגות			
SHEET NUMBER:		מספר הגליון:	
A3-4-100			
SCALE:	קנה מידה:	EDITION:	דפוס:
As indicated			
STATUS:	סטוס:	דפוס ע"י:	
למכר		הילה כהנא	
נבדק ע"י:		דפוס ע"י:	
DATE:		תאריך:	
22.09.25			



1 : 25

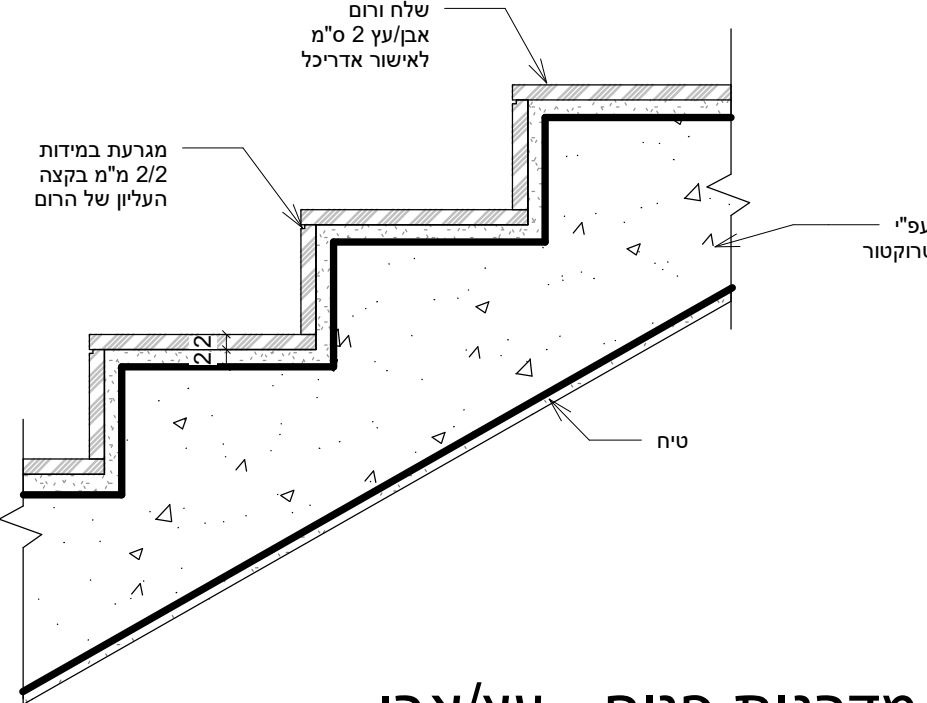


1 : 10

תמונה להמחשה בלבד



1 : 25

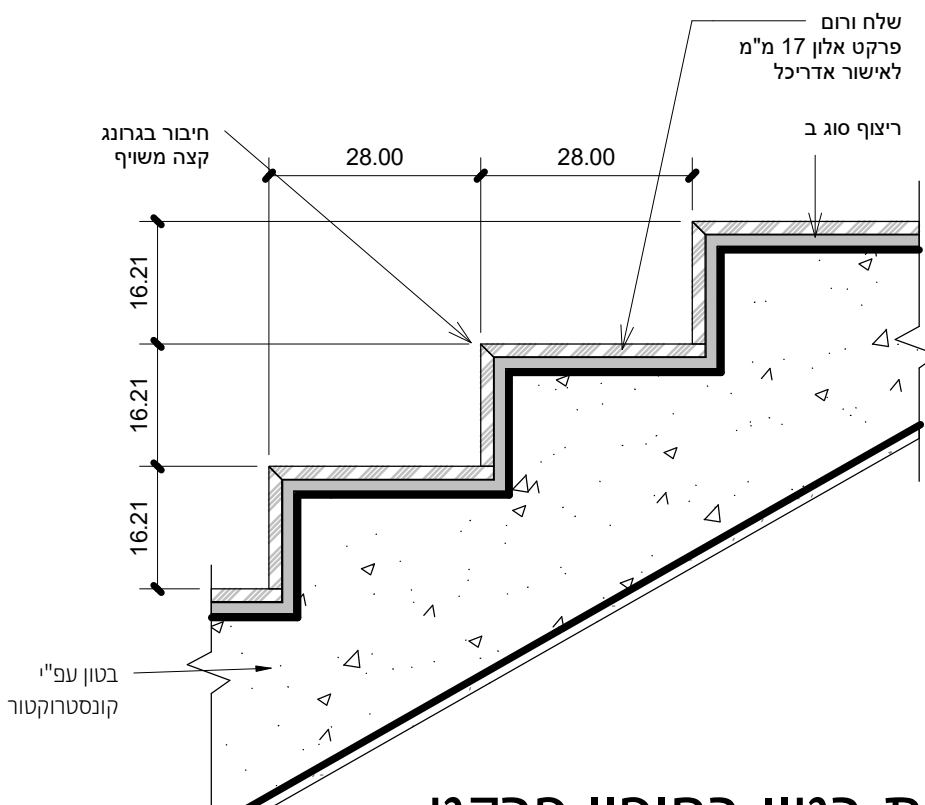

1 : 10


להמשך תיאום

דגם נבחר


מדרגות סטנדרטיות - מפרט סטנדרטי

על הקבלן לשלוח S.D לאישור אדריכל



יש לבצע התאמה לפרט לאחר בחירת חיפוי המדרגות*

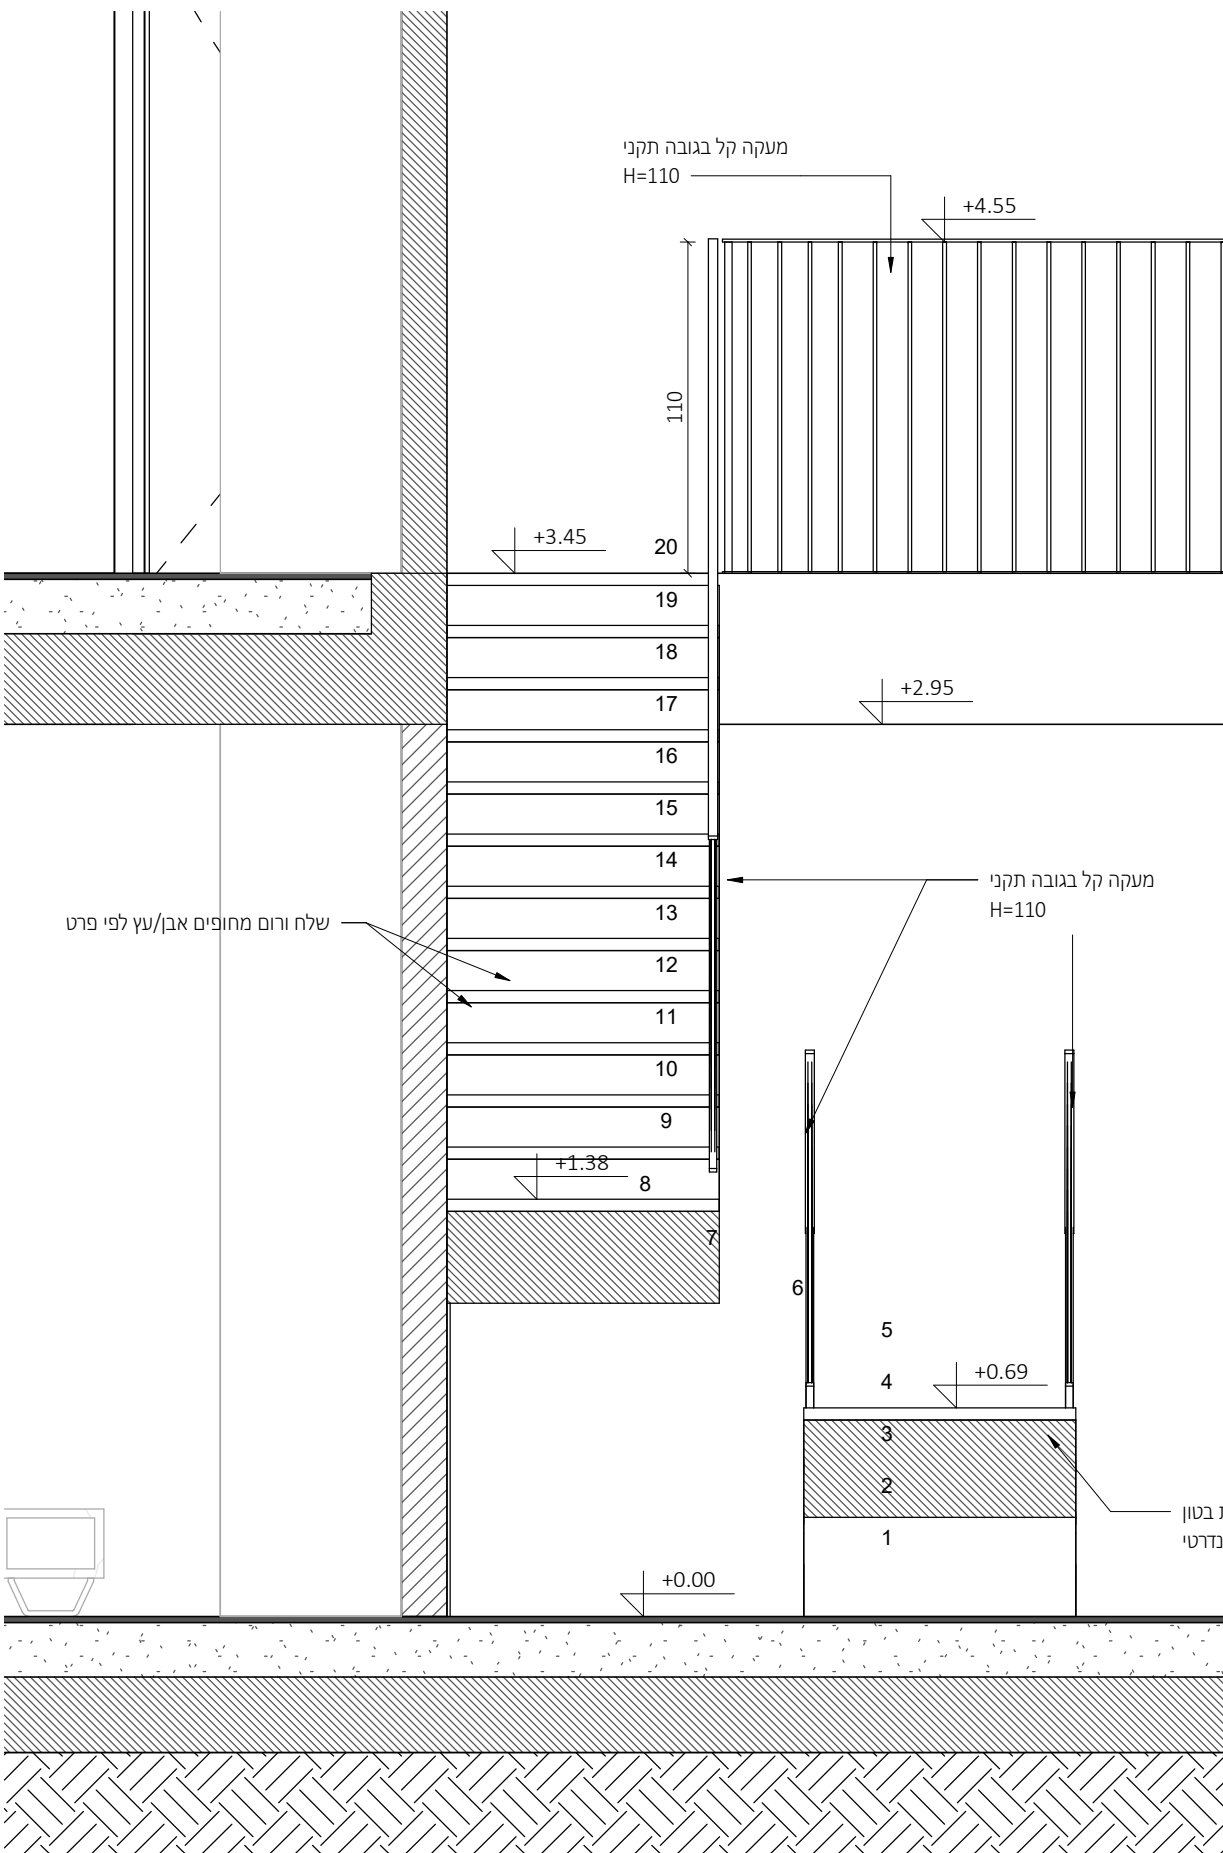

1 : 25

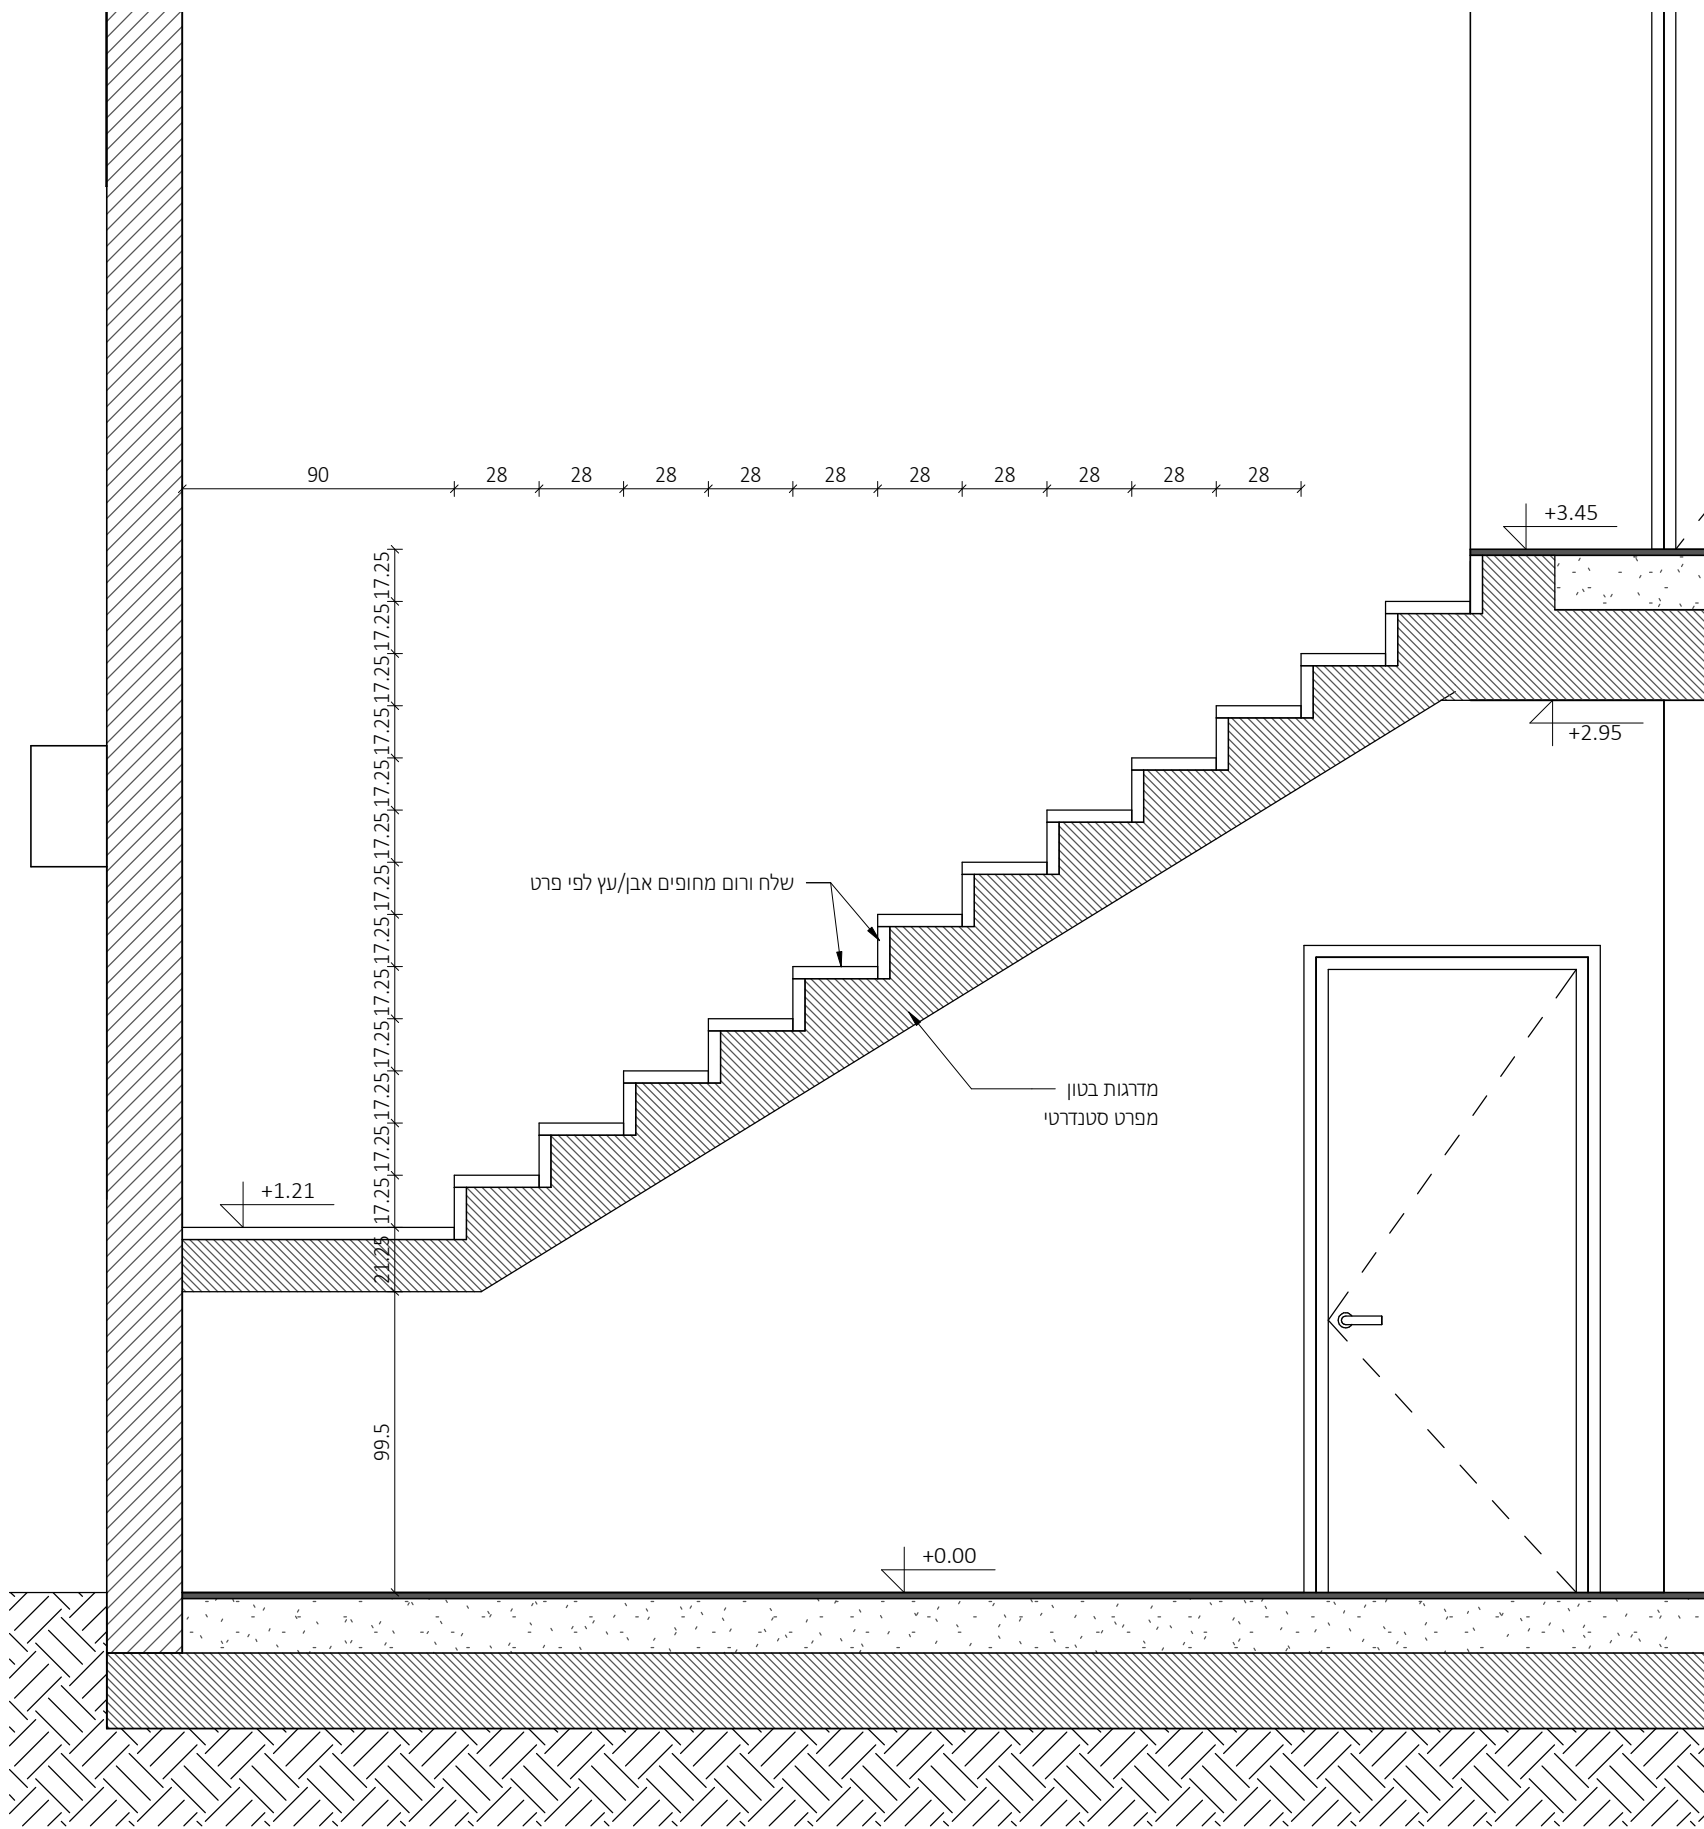

1 : 25

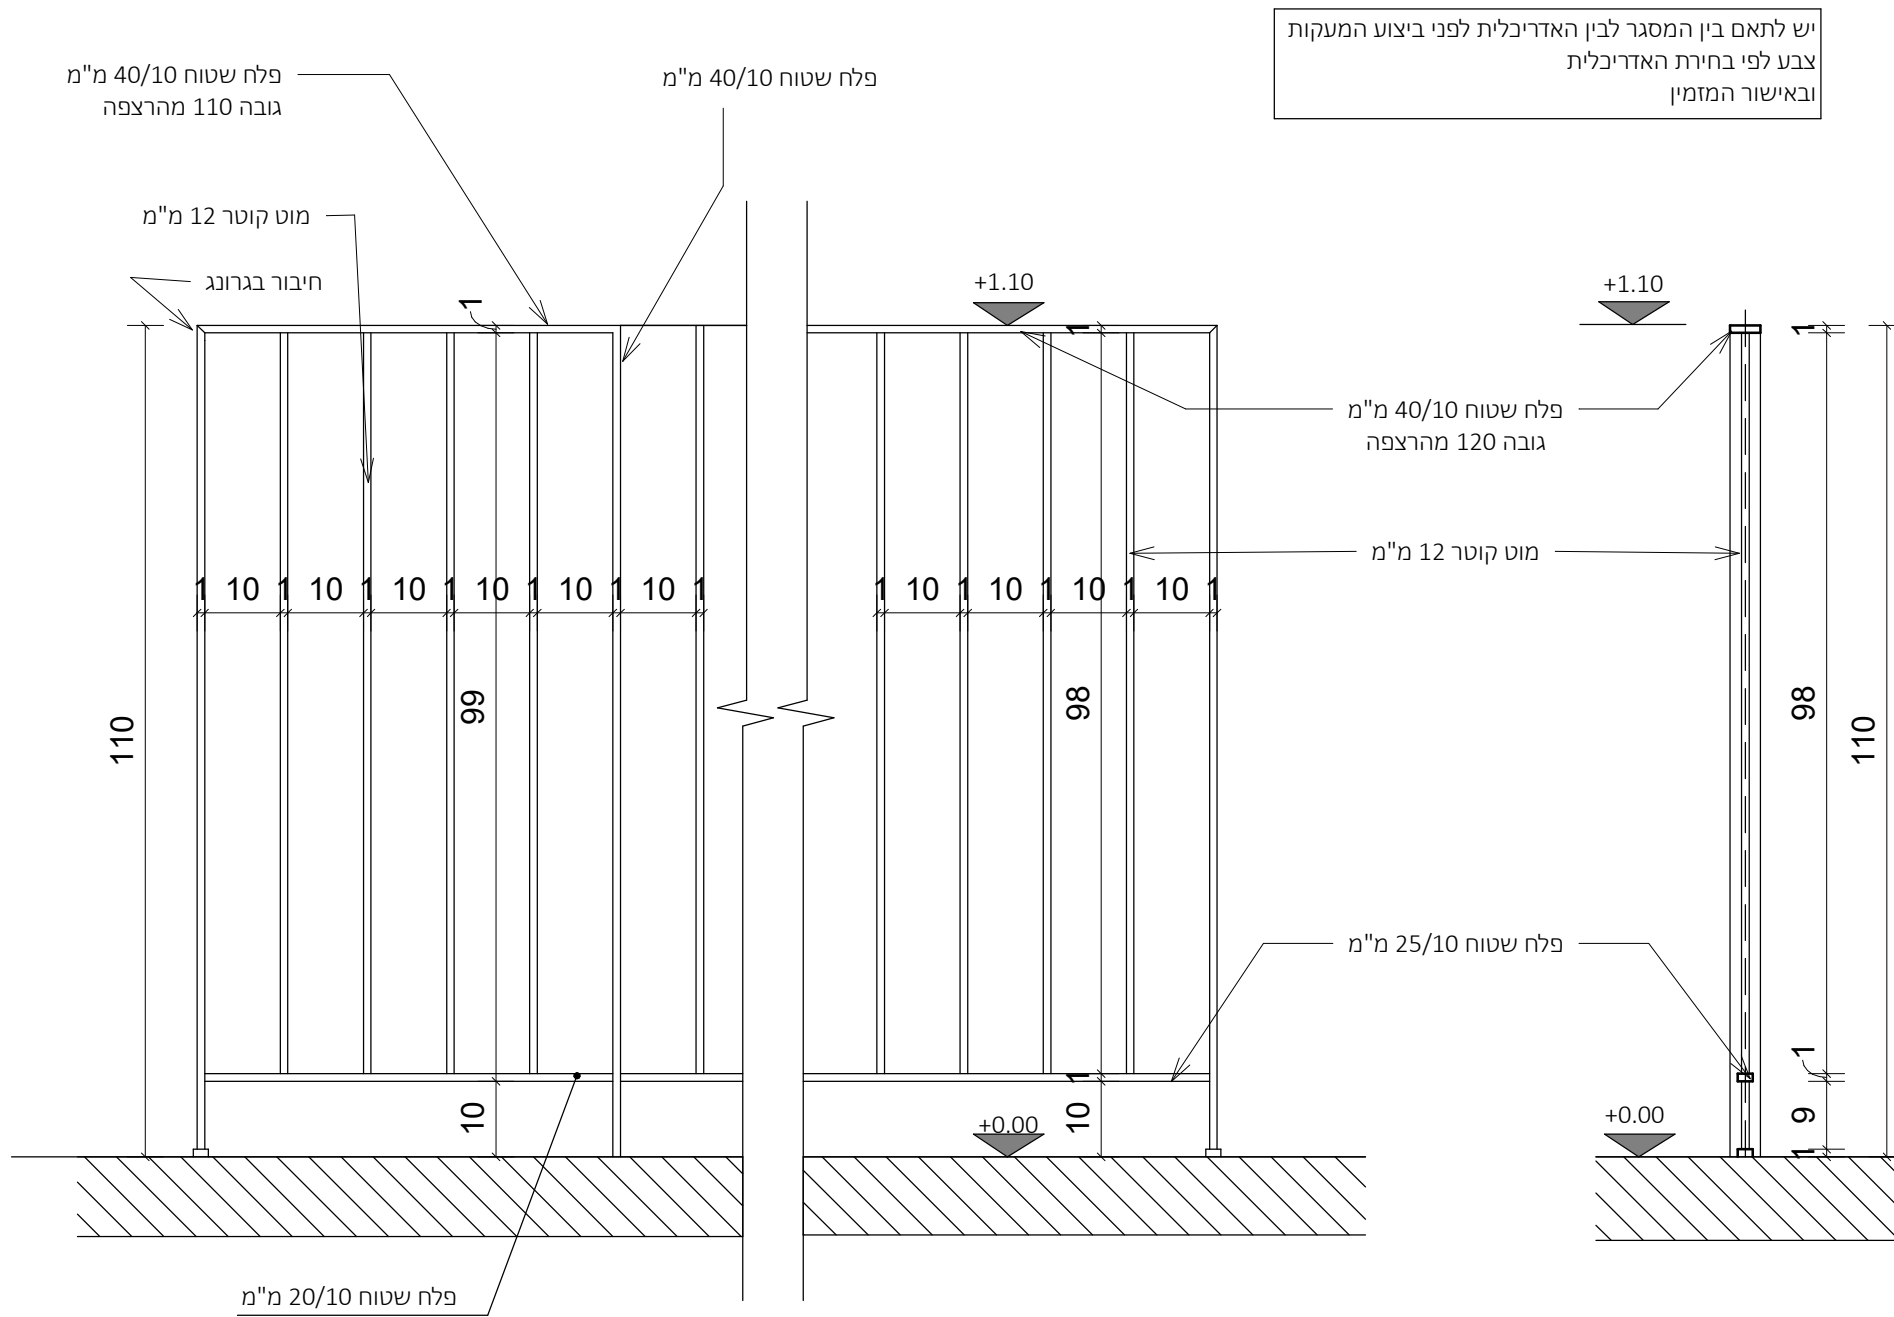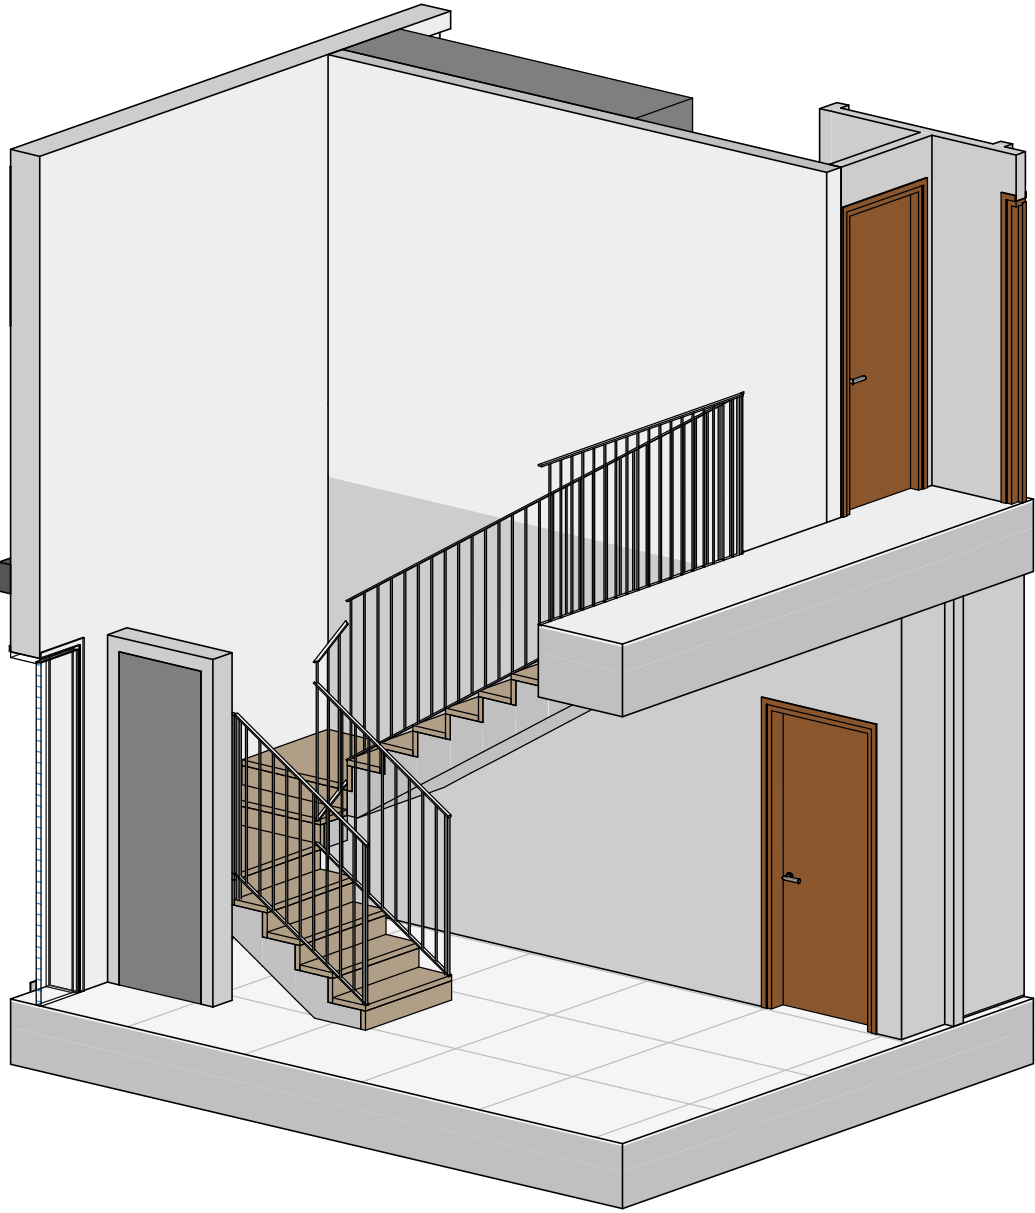

1 : 10

ניהול פרויקט
מהיסוד - בן סולומון
פיקוח
מהיסוד - בן סולומון
קונסטרוקציה
ערן שילר
מיזוג אוויר
אייל ארז מהנדסים ויועצים בע"מ
אינסטלציה
איתן אלמסי
חשמל
איתן בסיס
אלומיניום
נוף
נתי בלוקא
חשמל חכם
חימום תת רצפתי
איטום
צבי טל
אקוסטיקה
מעליות
קרקע וביסוס
דיה הנדסת קרקע וביסוס
רישוי

[illegible]

עמוד במ קיר בטון יור בלוק

[illegible]


CLIENT NAME:		החמיס	
קבוצת רכישה נופיה			
PROJECT NAME:		הפרויקט:	
נופיה - מגרש 11			
DRAWING NAME:		שם הגליון:	
פרטים			
SHEET NUMBER:		מספר גליון:	
A3-4-103			
CALCULATE:	עוד הוכנה:	EDITION:	הדורה:
As indicated	סטוסים		
TATUS:			
למכר	נבדק עדי:	הילה כהנא	רשם עדי:
DATE:	22.09.25		חיד:




NeumanHaynerArchitects

יומן חיינר אדריכלים
מחזור ההדפס 2, בית חירות
7690509-09-9545842


office@nh-arch.com
www.nh-arch.com

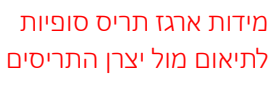

1 : 10

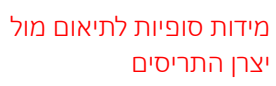


1 : 10

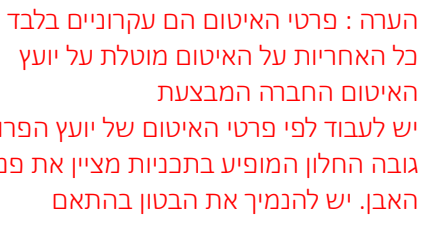

פרט עקרוני בלבד - פרט סופי מספק החלונות

1 : 10

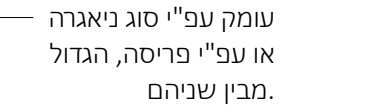


יפוי לוח גבס
יזק

ערכת סמויה

1 : 10

פרטי האיטום באחריות יועץ האיטום
ראה חוברת פרטי איטום מצורפת

להמשך תיאום

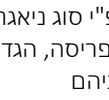

מר עפ"י פריס

צרכת סמויה

1 : 10




בולט החוצה
2 ס"מ

1 : 5

פרגולת אלומיניום




תמונה להמחשה בלבד

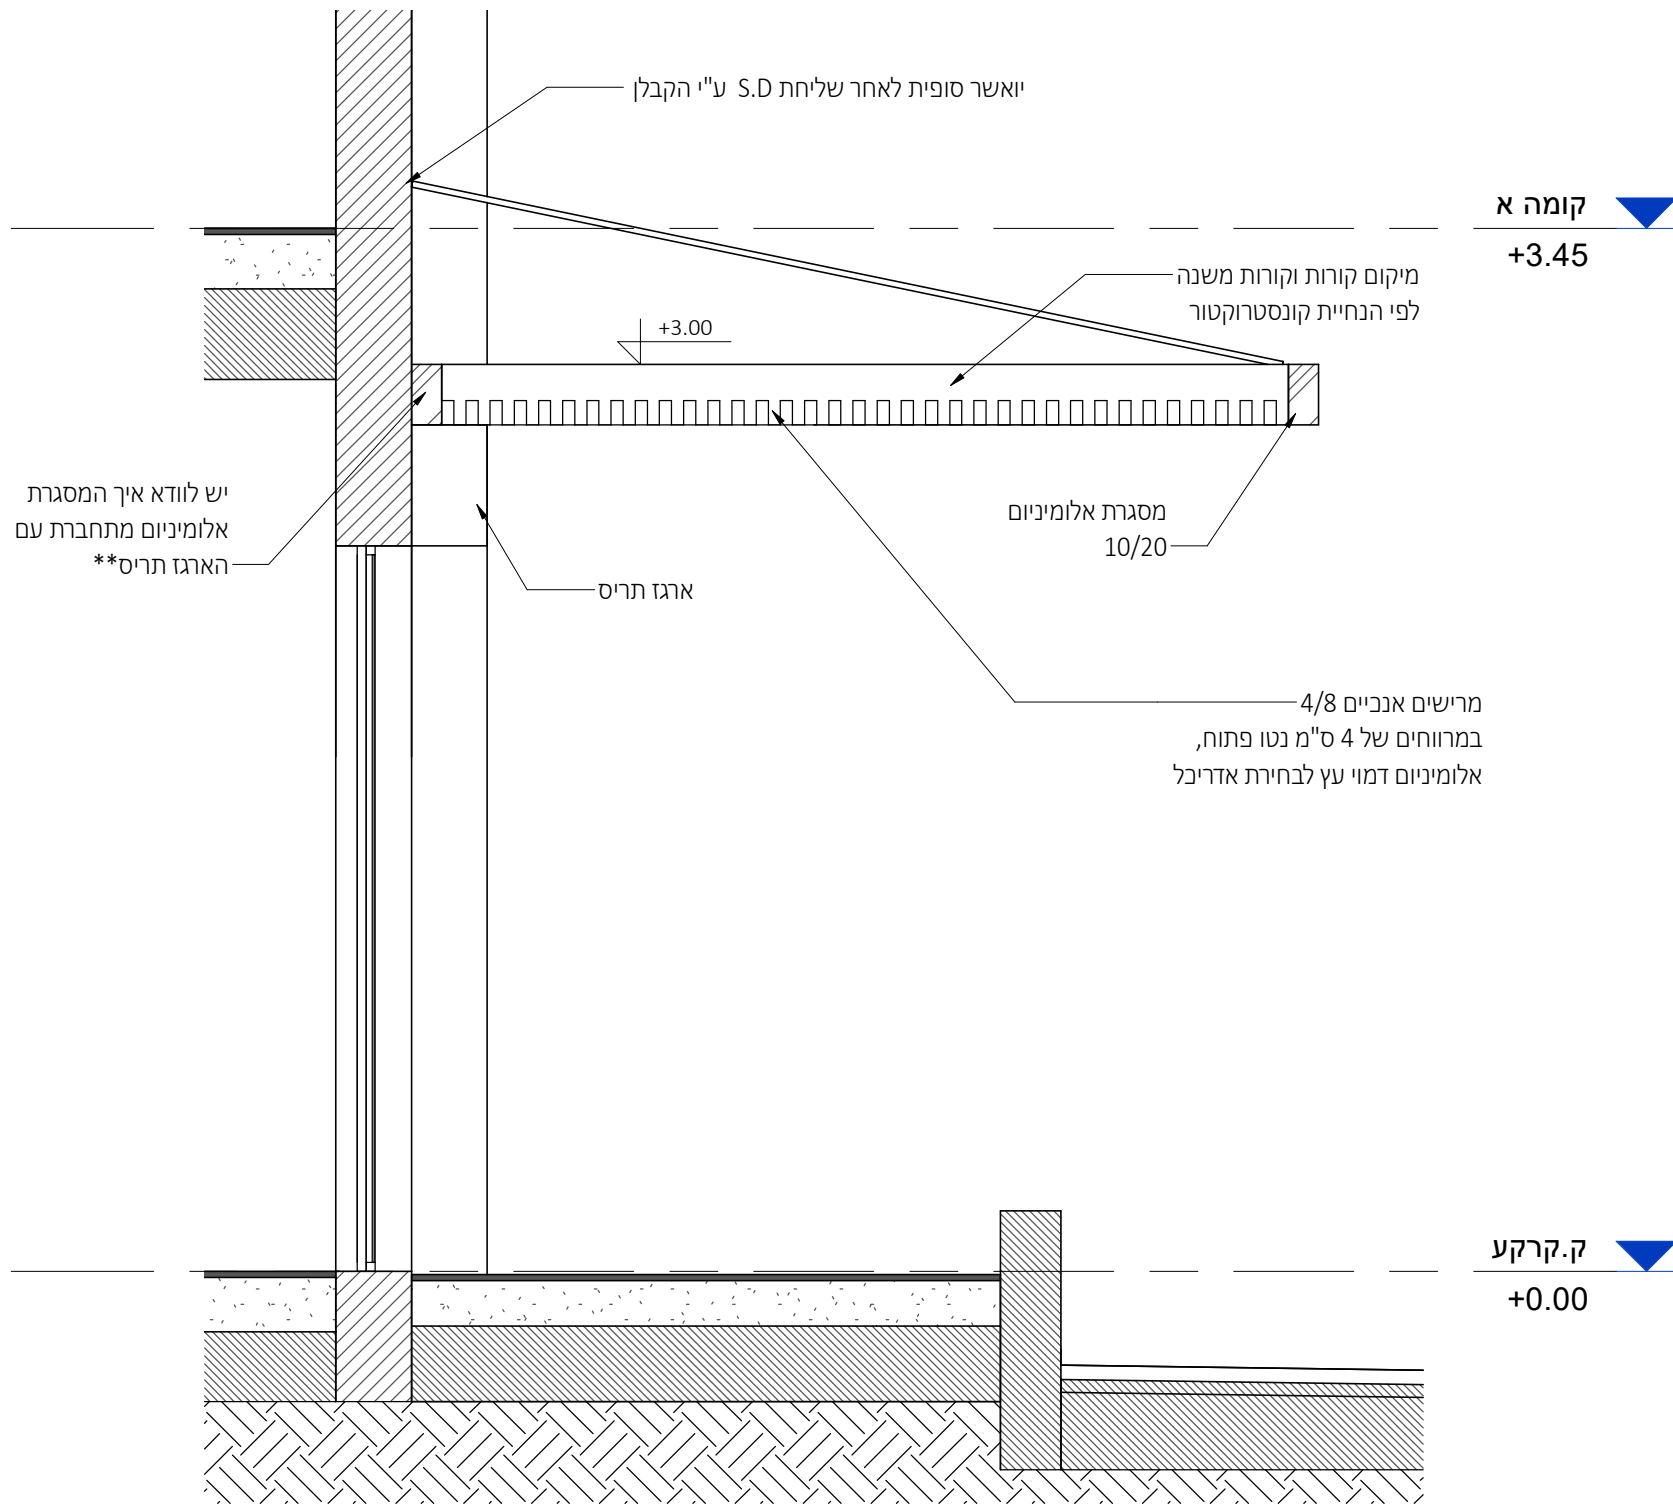

Section 19


1 : 25

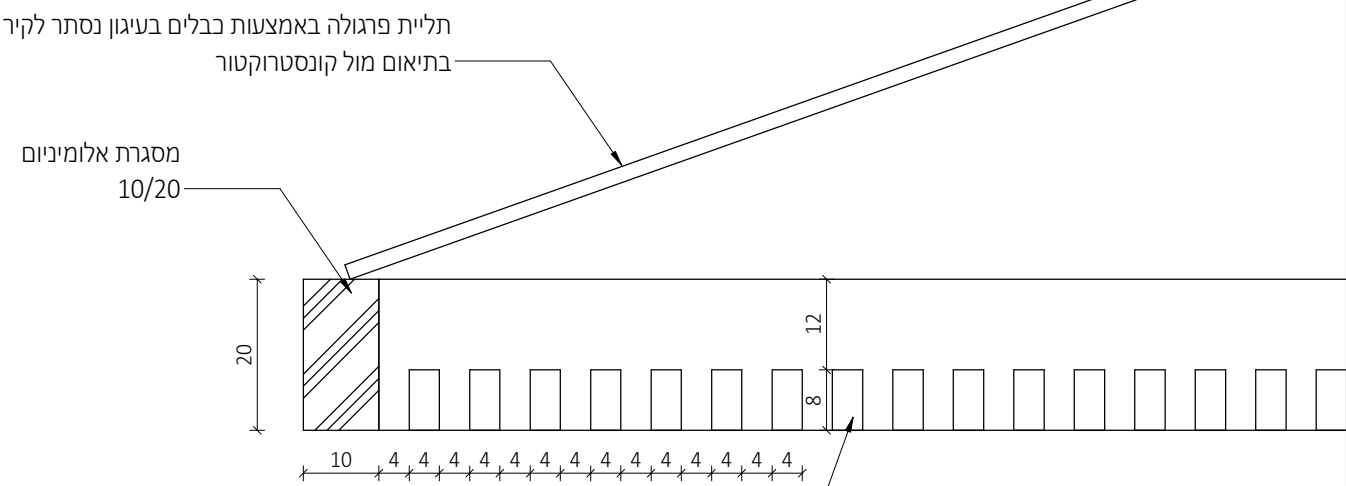

פרגולה - חתך רוחב


1 : 10

להמשך תיאום

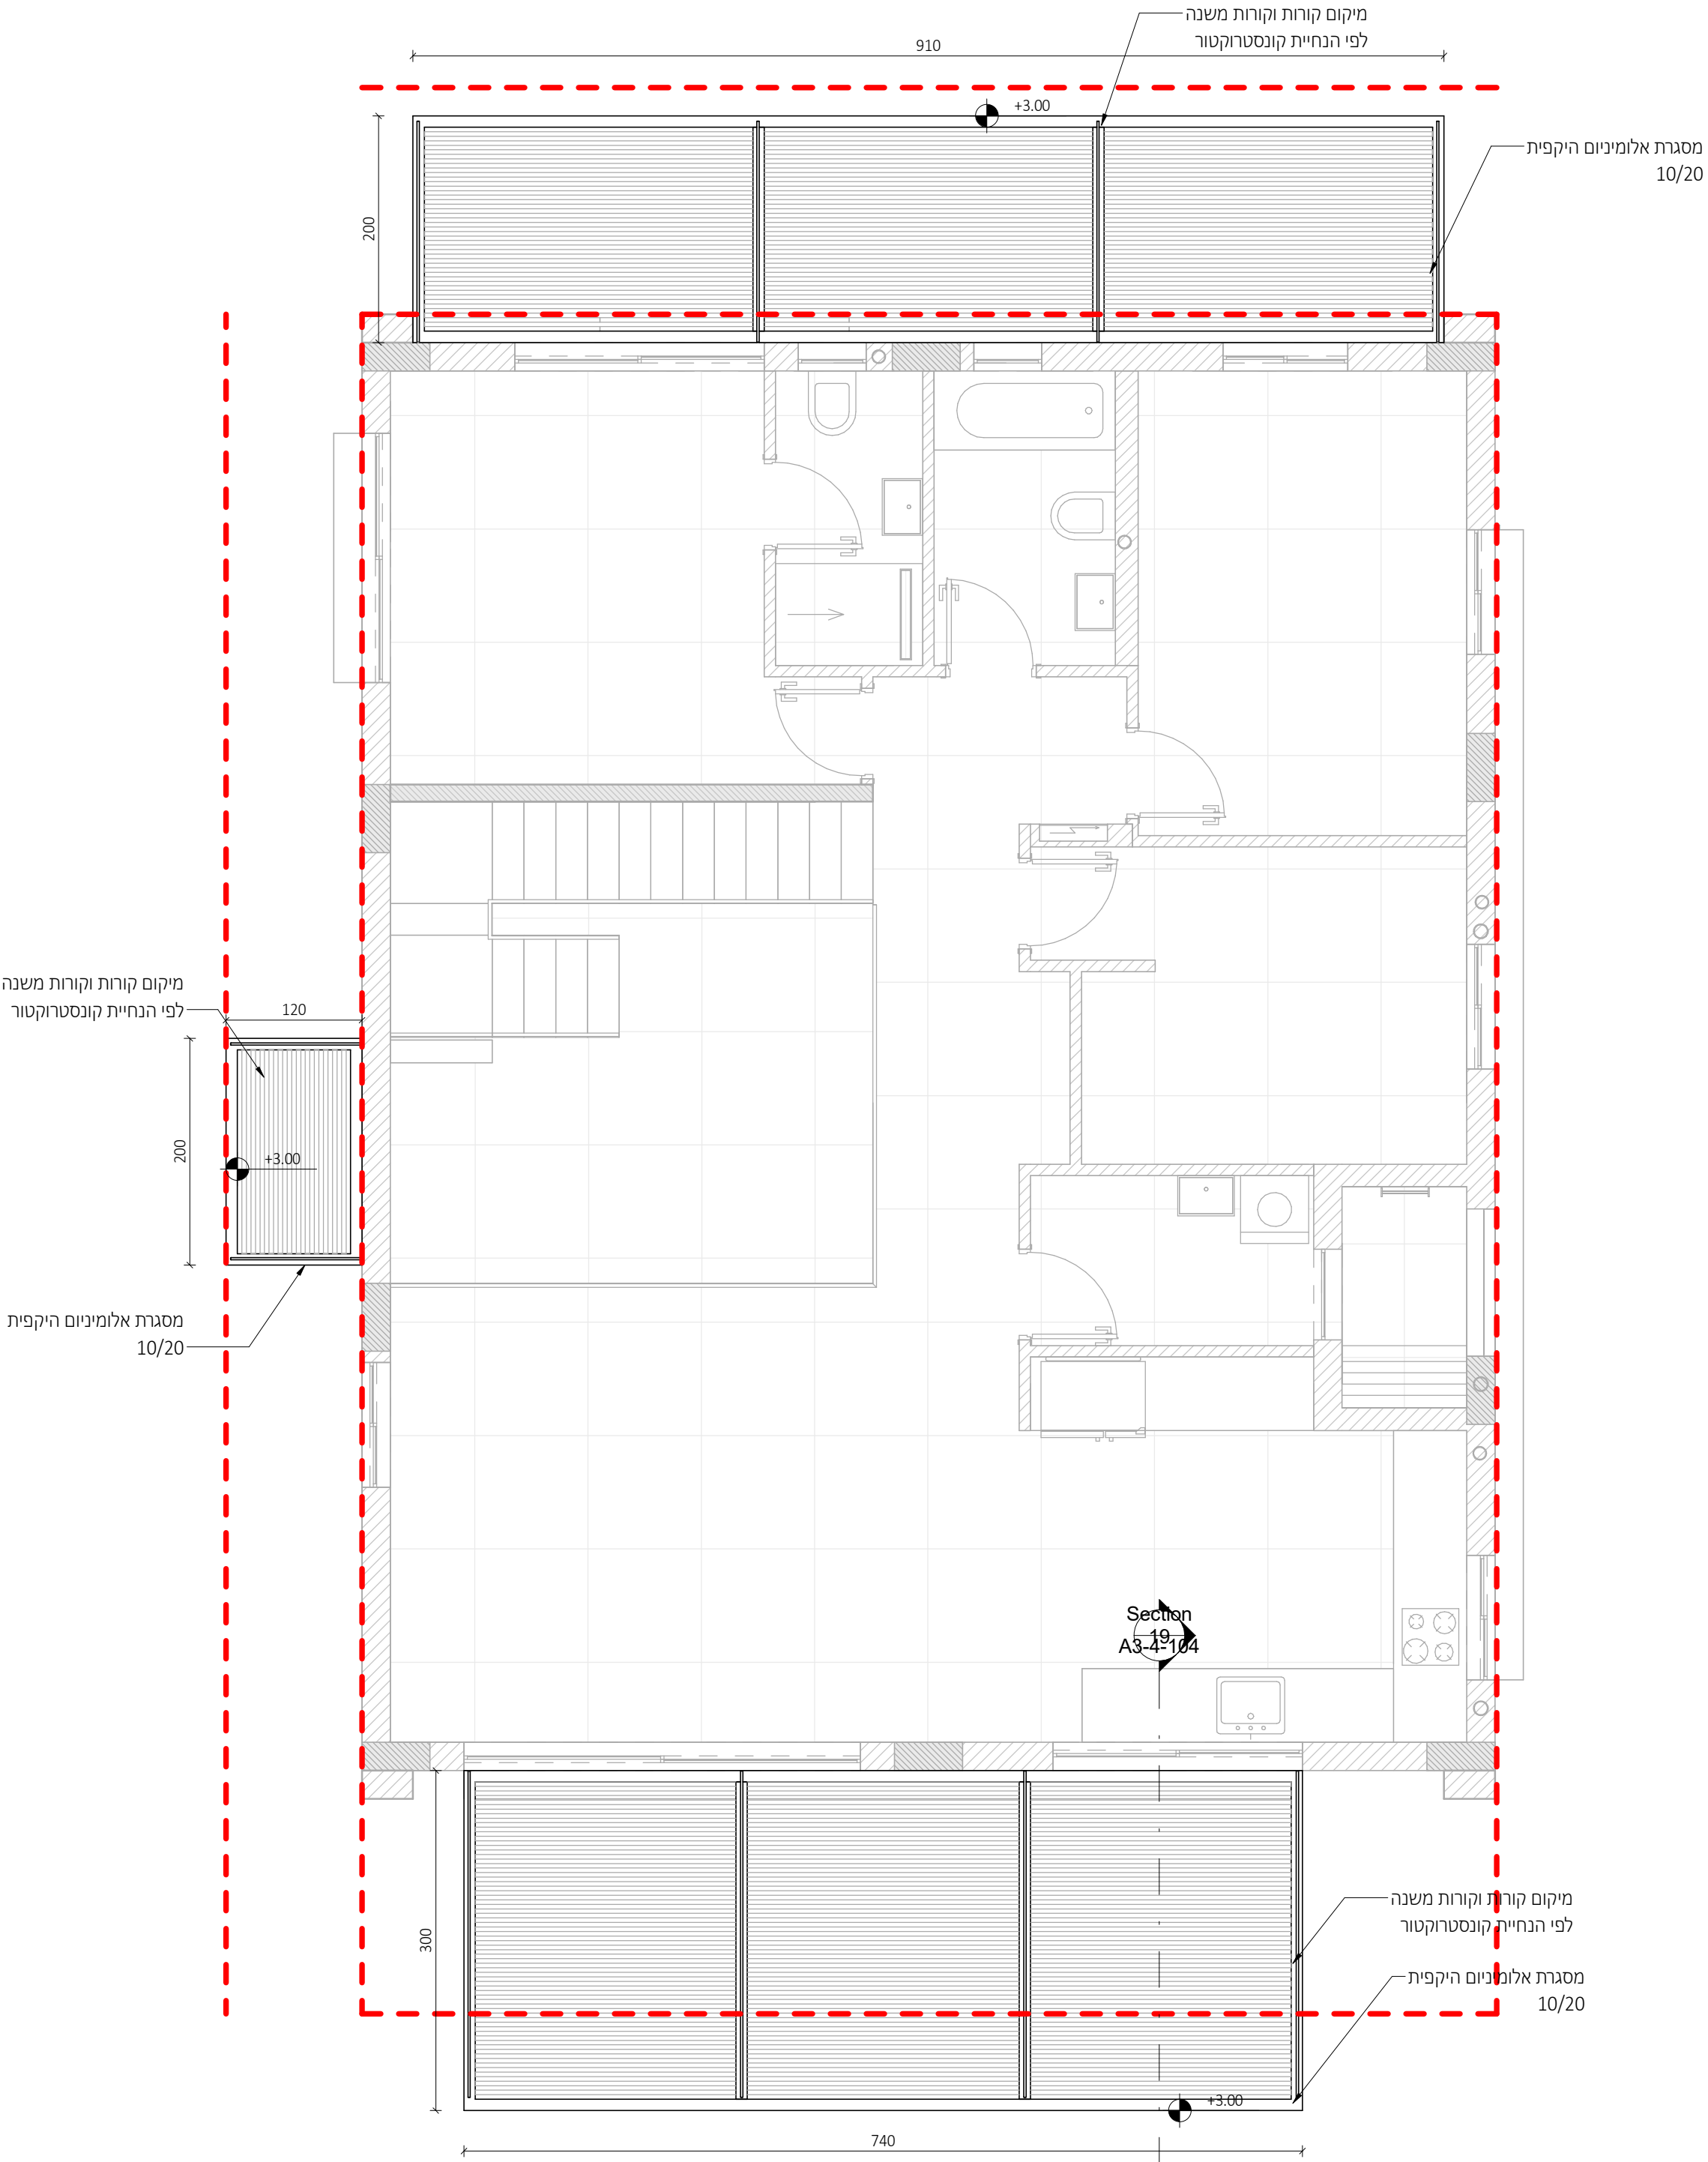

תכנית קומה א

1 : 50

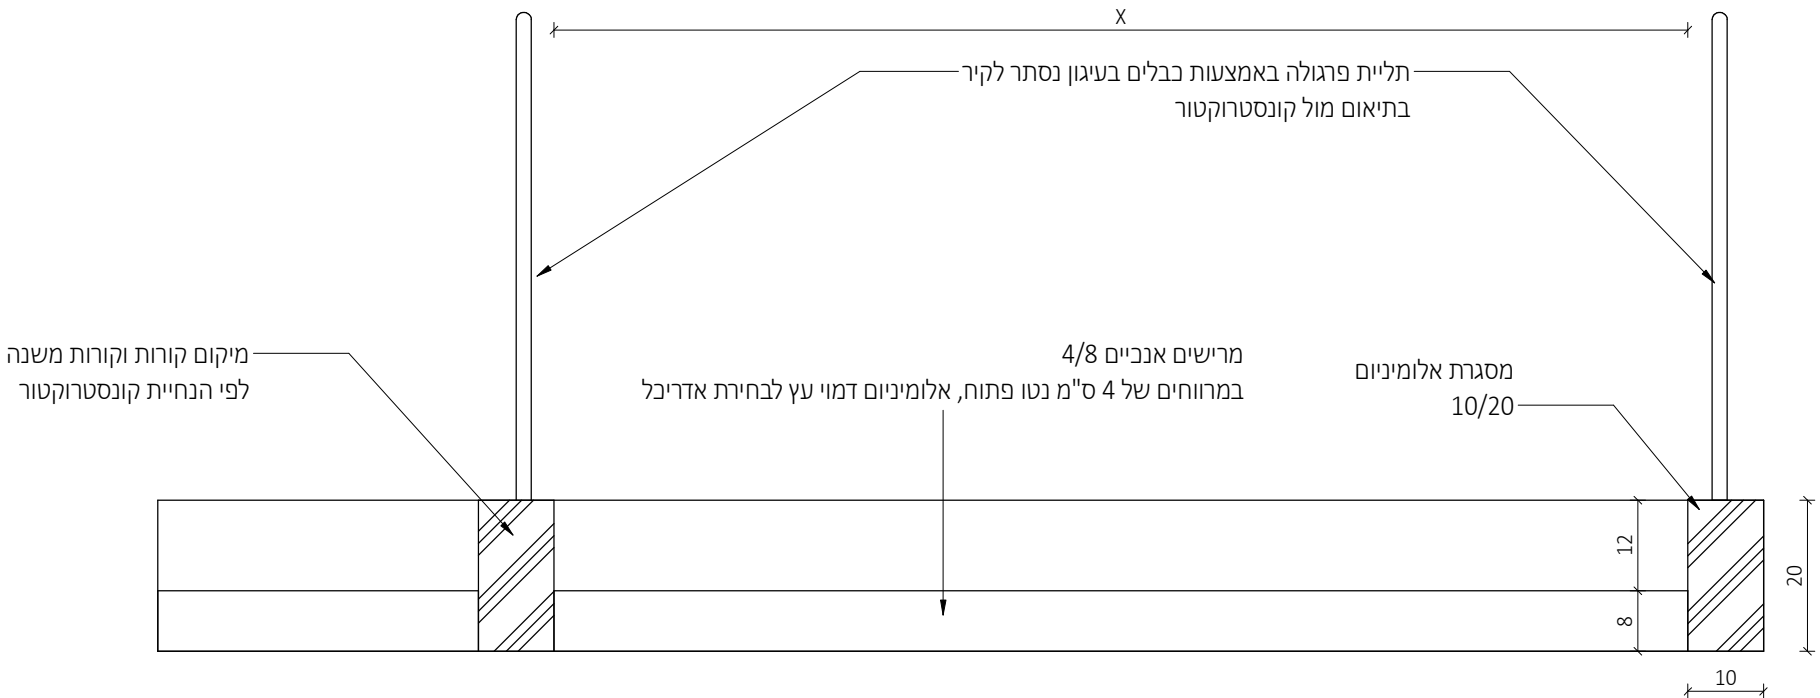

פרגולה - חתך אורך

1 : 10


מתכננים:

ניהול פרויקט
מהיסוד - בן סולומון
פיקוח
מהיסוד - בן סולומון
קונסטרוקציה
ערן שילר
מיזוג אוויר
אייל ארז מהנדסים ויועצים בע"מ
אינסטלציה
איתן אלמסי
חשמל
איתן בסיס
אלומיניום
נוף
נתי בלוקא
חשמל חכם
חימום תת רצפתי
איטום
צבי טל
אקוסטיקה
מעליות
קרקע וביסוס
דיה הנדסת קרקע וביסוס
רישוי

± 0.00 = +250.80

הערות:
1. תכנית זו יש לקרוא יחד עם תכנית הרישויים.
2. גובה אבטלס: ראו תכנית פיתוח.
3. המידות הן בין קירות הבניה ולא כולל פיתוח.
4. פיתוח השטח סביב הבניה, כולל, מדרגות, גדרות, שבילים, ריצופים, שפופים, גדרים, חניה וגן ראו תכנית פיתוח.
5. איסוס קירות הצפת הבניה כמעט עם הקרקע ובנידוד תרמי לאורך העמודים והקורות מול קונסטרוקטור. כלירות או עם סימני גיבוי. ראו תכנית קונסטרוקציה.
6. איף דים יבוצע בכל מישור אופקי הבולם חתונן.
7. סיוח תרמי במפיד- ע"פ מפרט חומקיר. מאושר ע"י פיקוח העודף.
המבצע אחראי לסידור: עליו לבקר ולבדוק את כל המידות בתכנית ובמקום הבניה. ראו תכנית פיתוח.
במקום של סתירה או אי התאמה בתכנית /או בבנין, עליו להודיע על כך מיד לאדריכל בסדר המשיך בעבודתו.
המבצע ישתמש אך ורק בתכנית שאושר לכניסו.
המבצע יחזיק באחריות, בכל שלב, על משרדו של תכנית.
אין לקבוע מידות על ידי חזירה בשר שום.
התכנית היתה רכוש האדריכל ואין לנשות כל שימוש בה או ברעיונות הגלומים בה, אלא באישור בכתב מהאדריכל.
מהנדס /או יועץ אשר שמו רשום בתכנית זו, נושא לכיד באחריות המקצועית והתקנית לתכנית.
על המפקח והמבצע לוודא התאמת התכנית האדריכלית "כניסו" לתכנית זו. המכר והתכנית המאושרות ע"י כל הגורמים הרשמיים.
התכנית כוללת את כל האמצעים והידוע על ליום תוצאתה.

משרד קירות:

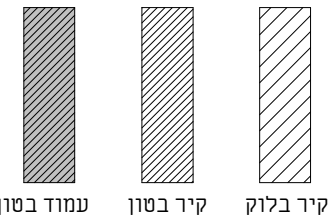

תאריך	תיאור	מהדורה
22.09.2025	מכרז	1

אדריכלות

שם המסמך:	CLIENT NAME:
קבוצת רכישה נופיה	
שם הפרויקט:	PROJECT NAME:
נופיה - מגרש 11	
שם הגיליון:	DRAWING NAME:
פרטי פרגולה	
מספר גיליון:	SHEET NUMBER:
A3-4-104	
מהדורה:	EDITION:
קנה מידה:	SCALE:
As indicated	
סטוס:	STATUS:
למכרז	
שורסס ע"י:	הילה בהנא
נבדק ע"י:	
תאריך:	DATE:
22.09.25	



נירסן חיינר אדריכלים
מורד החדרס 2, בית חירות
09-9545642 72
www.nh-arch.com
office@nh-arch.com

זכיות ייצור / ע"פ הנחיות ע"ד

רשימת חלונות					
סוג	הערות	כמות	גובה	רוחב	מס פריט

1	220	240	2	צלון רפפה חיצוני חשמלי + ארגז חיצוני	ויטרינה פרופיל 7500 קליל
2	350	240	1	צלון רפפה חיצוני חשמלי + ארגז חיצוני	ויטרינה פרופיל 7500 קליל
3	110	110	2	צלון רפפה חיצוני חשמלי + ארגז חיצוני	חלון הזזה פרופיל 7000 קליל
4	60	110	1	צלון רפפה חיצוני חשמלי + ארגז חיצוני	חלון קיפ פרופיל 4500 קליל
4.1	60	110	1	צלון רפפה חיצוני חשמלי + ארגז חיצוני	חלון קיפ פרופיל 4500 קליל
5	220	110	1	צלון רפפה חיצוני חשמלי + ארגז חיצוני	חלון הזזה פרופיל 7000 קליל

6	350	230	1	תריס גלילה חשמלי	קבוע עד לגובה 120+חלון הזזה פרופיל 7000 קליל
7	80	210	1	תריס גלילה חשמלי	דלת כנף פרופיל 4350 קליל
8	110	110	5	תריס גלילה חשמלי	חלון הזזה פרופיל 7000 קליל
9	220	110	3	תריס גלילה חשמלי	חלון הזזה פרופיל 7000 קליל
10	60	110	2	תריס גלילה חשמלי	חלון קיפ פרופיל 4500 קליל

כל פריט יחולק למינימום הכנפיים האפשרי (לתיאום מול ספק האלומיניום ובמסגרת שרטוטי ה shop drawing)

רשימת דלתות					
סוג	הערות	גובה	רוחב	כמות	מספר פריט

נוימן חיינר אדריכלים בע"מ

26/10/2025 16:01:11