



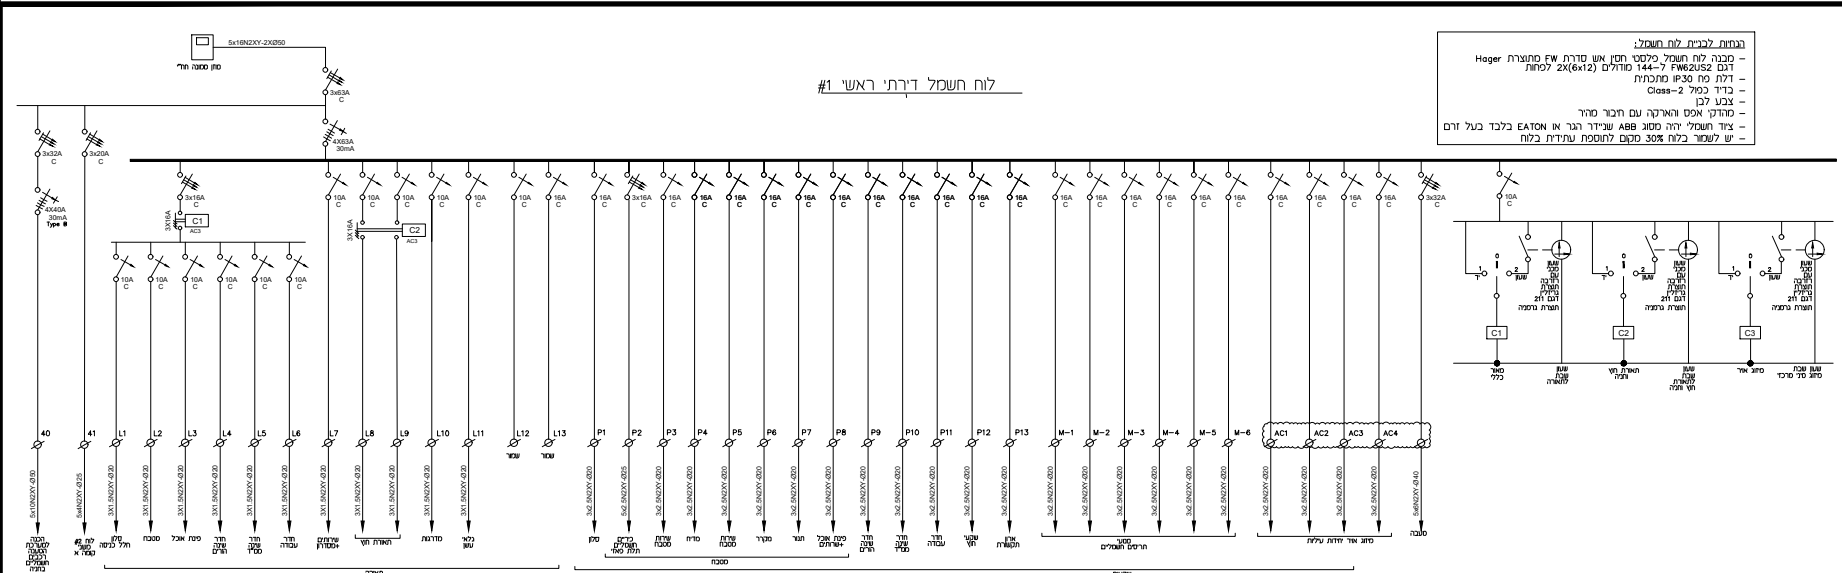

הנחת לביכת לחלחול:
 - מבנה לוח חשמל סלסטי חסן אש סדרת FW סחצרת Hager
 - דגם FWA2052 144-7 מודלים 2x(6x12) למחית
 - דלת לוח סלסטי סחצרת
 - Class-2
 - צבנו לן
 - סחצרת אסס וארירה עם חכיר סחצרת
 - ציד חשכל זה ססס ABB עניידר רגר או EATON בלכד בעל זור
 - ע- ש- לשחור בלוח 30% סקס לחספת עתירת בלוח

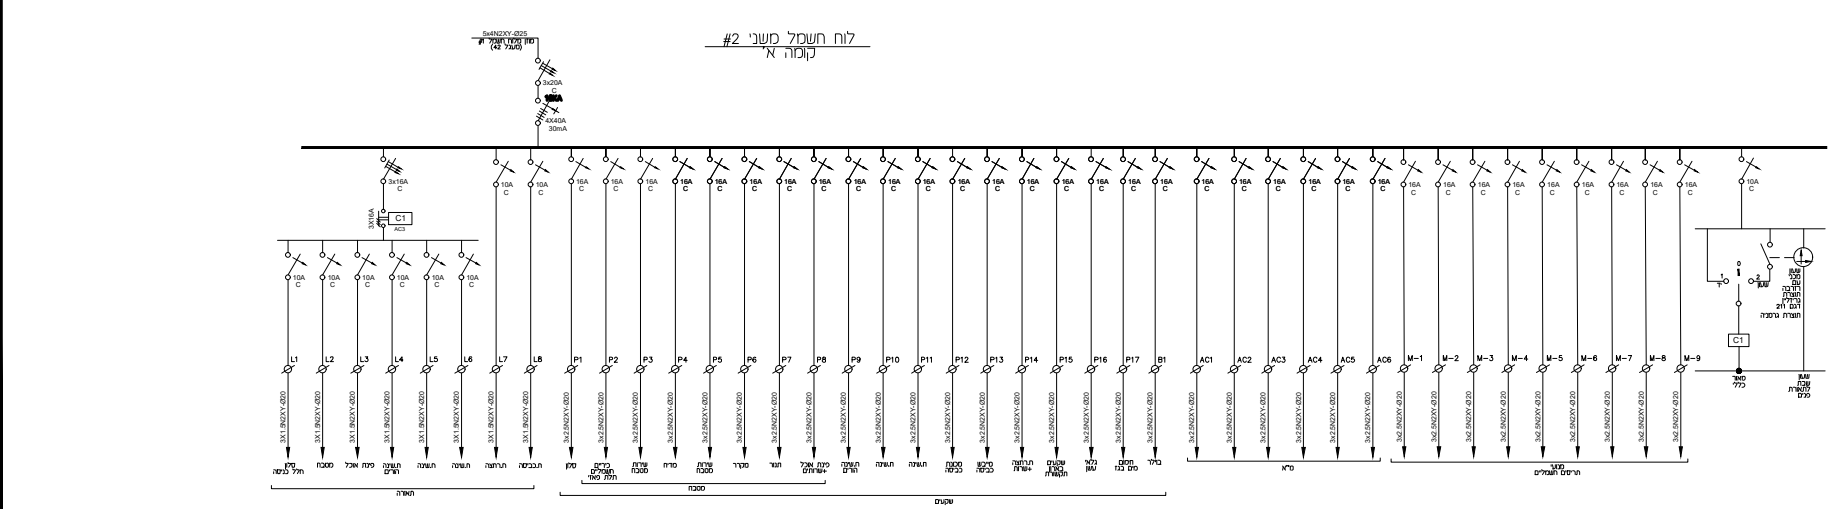

שם המיקום:	נופיה-אלפי מנשה		
שם התכנית:	לוחות חשמל מגרש 11, נופיה		
מיקום:	נעין	מסלול	מסלול
תאריך:	8.4.2025	מסלול:	675W.dwg
תכנון:	שרס:	אשר:	איתן
יפעת	כיאל	איתן	
מסלול:	מסלול:	מסלול:	
0	11	675	