

אוריכל פנים
אינסטלציה
בסירות אש
אקוסטיקה
חשמל והדמרה
קונסטרוקציה
קבלו ראשי
ניווט פריונקט
לקוח
אדיינג

תחילת ראשון	16.06.2025	📅
תחילת ראשון	26.05.2025	📅
תחילת ראשון	02.05.2025	📅
תחילת ראשון	31.03.2025	📅
תחילת ראשון	11.03.2025	📅
שני	תאריך:	סל

הערות

- λ

- ## מקרא צבעים בתכנית


- | | |
|--------------------------|---|
| תעלות ותריסי אוויר חוזר |  |
| תעלות ותריסי אספקת אוויר |  |
| תעלות ותריסי צח |  |
| תעלות ותריסי ניקת אוויר |  |
| תעלות ותריסי שיחרור עשן |  |
| צנרת גז וחשמל |  |
| סימון מעגלי מידוג אוויר |  |

[illegible]


Court 11
1st Floor

Court 11
2nd Floor

Option ~~No~~1
VRF duct unit in living room
and wall mounted in rooms

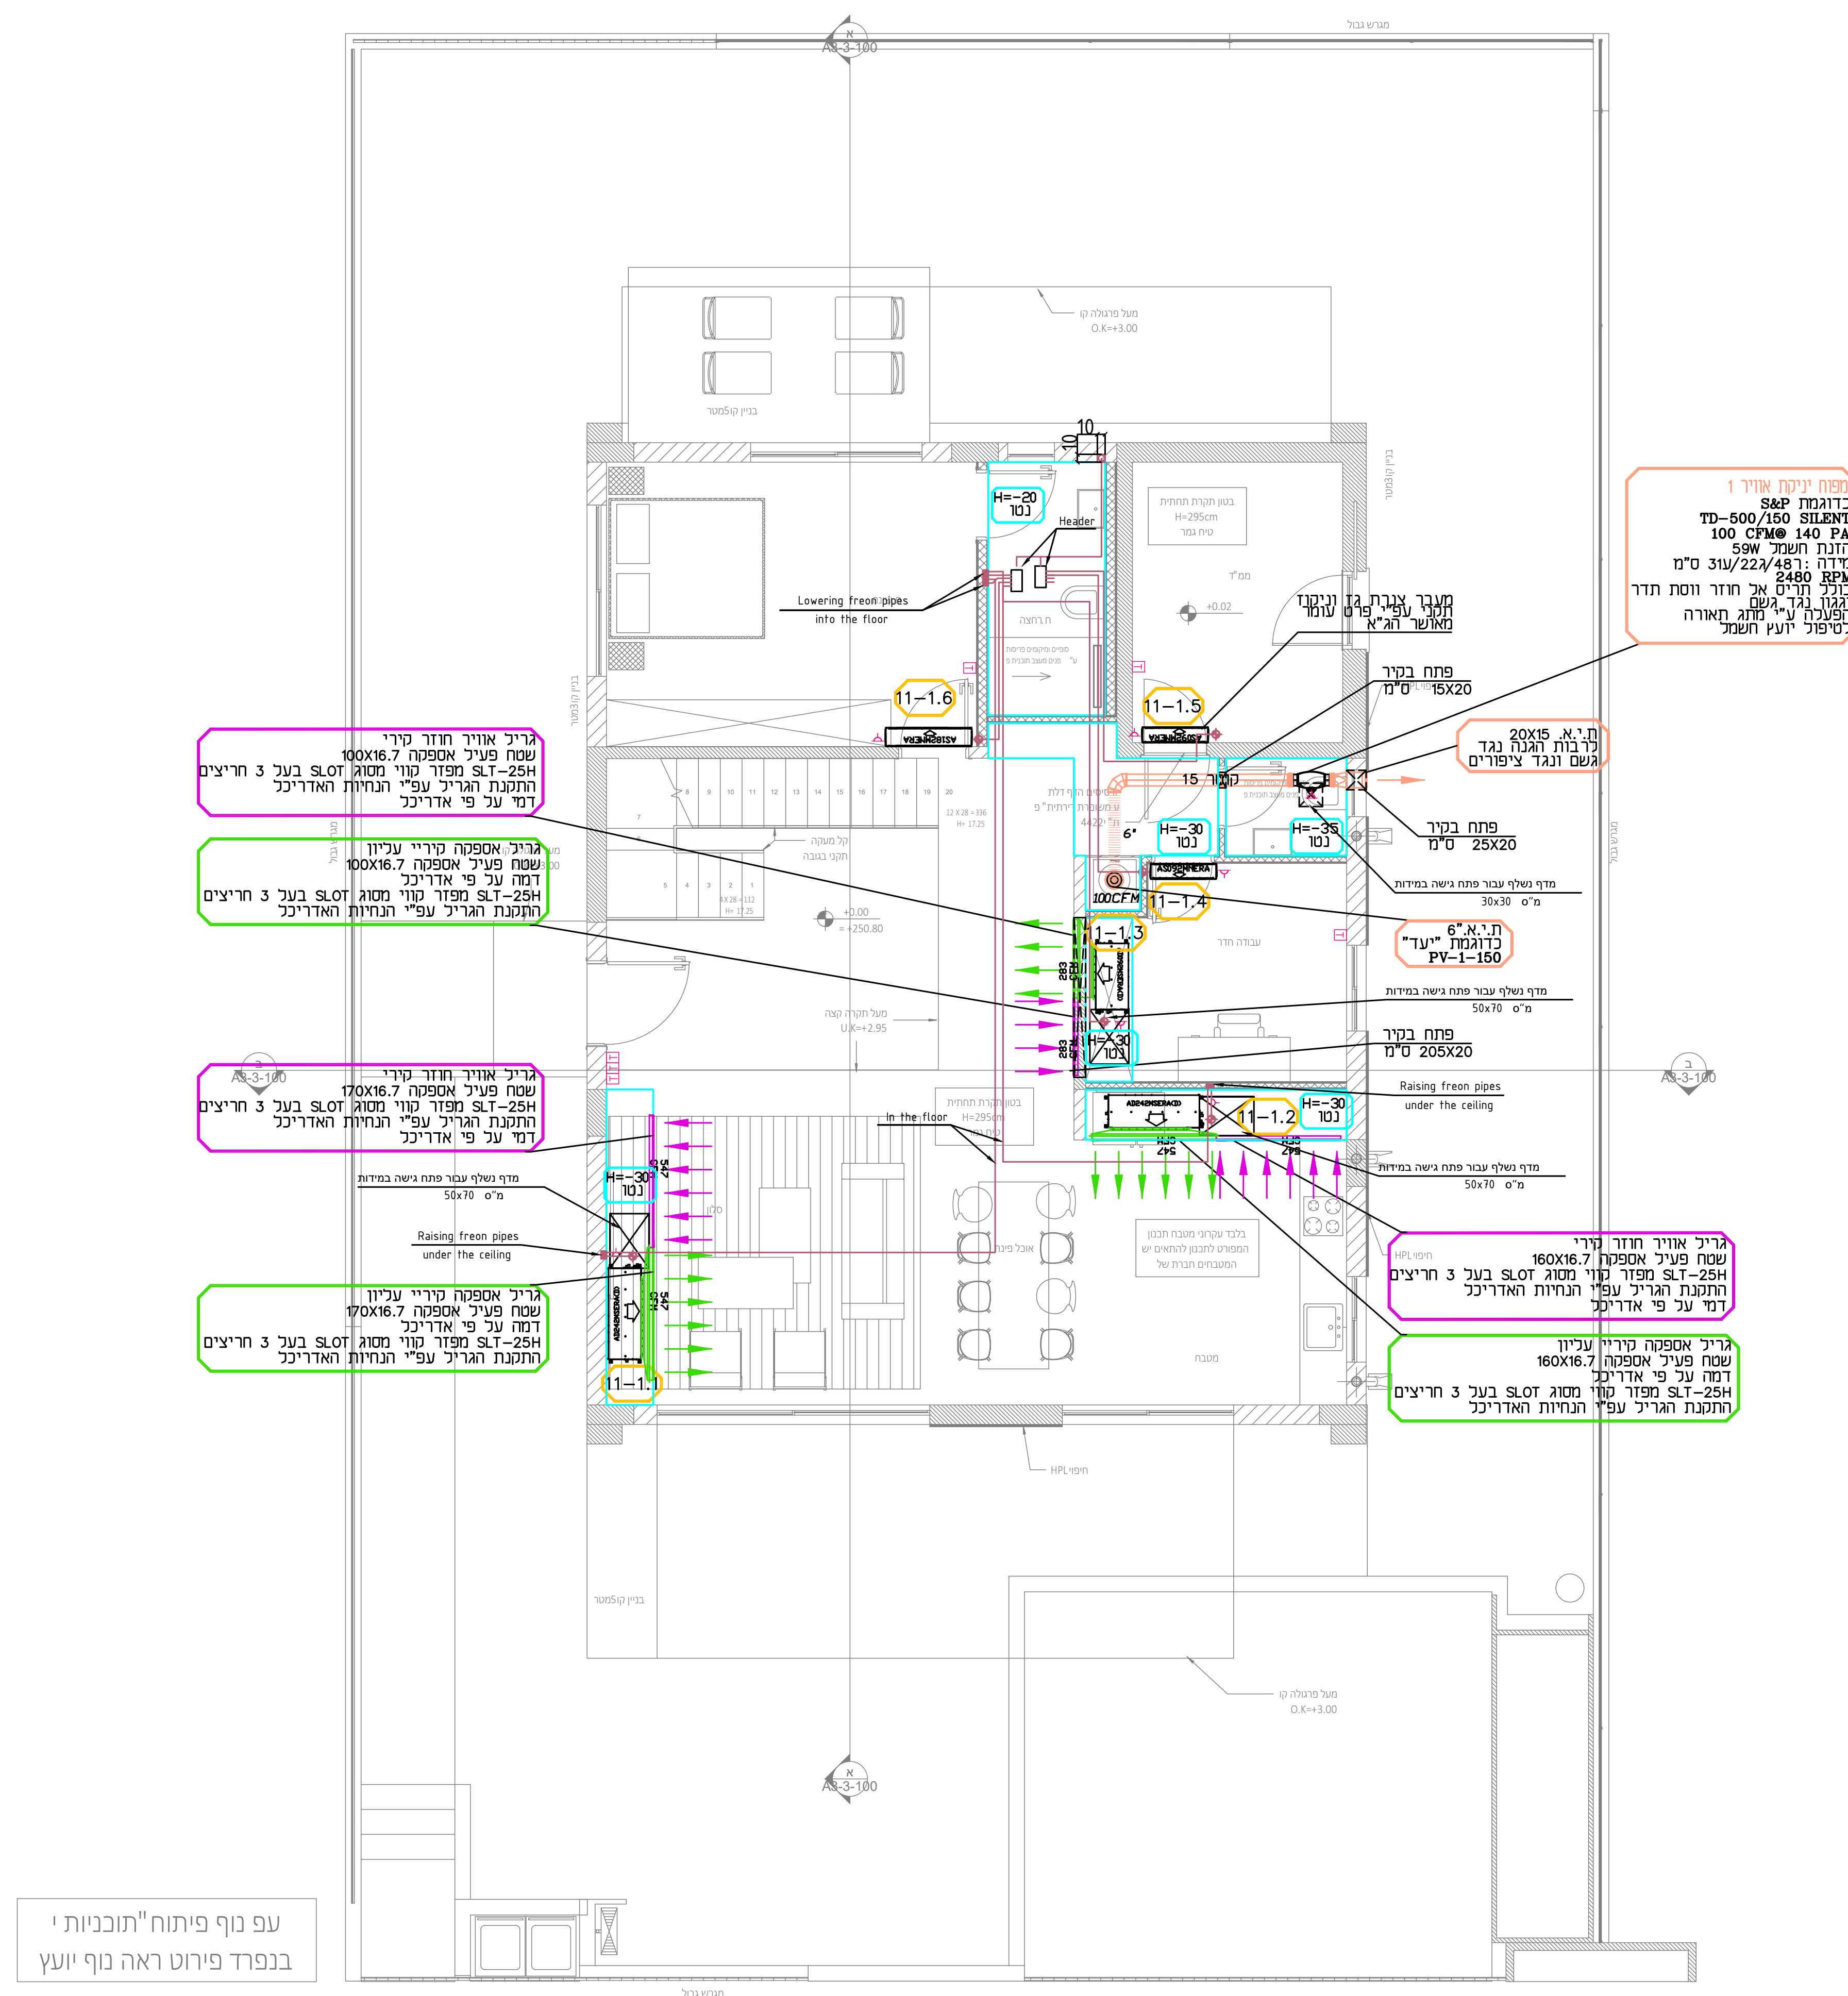


עפּ נאָך פּיטאָח "תּוּכּנּיּוּת
בּנּפּרד פּירוט ראה נאָך יונ

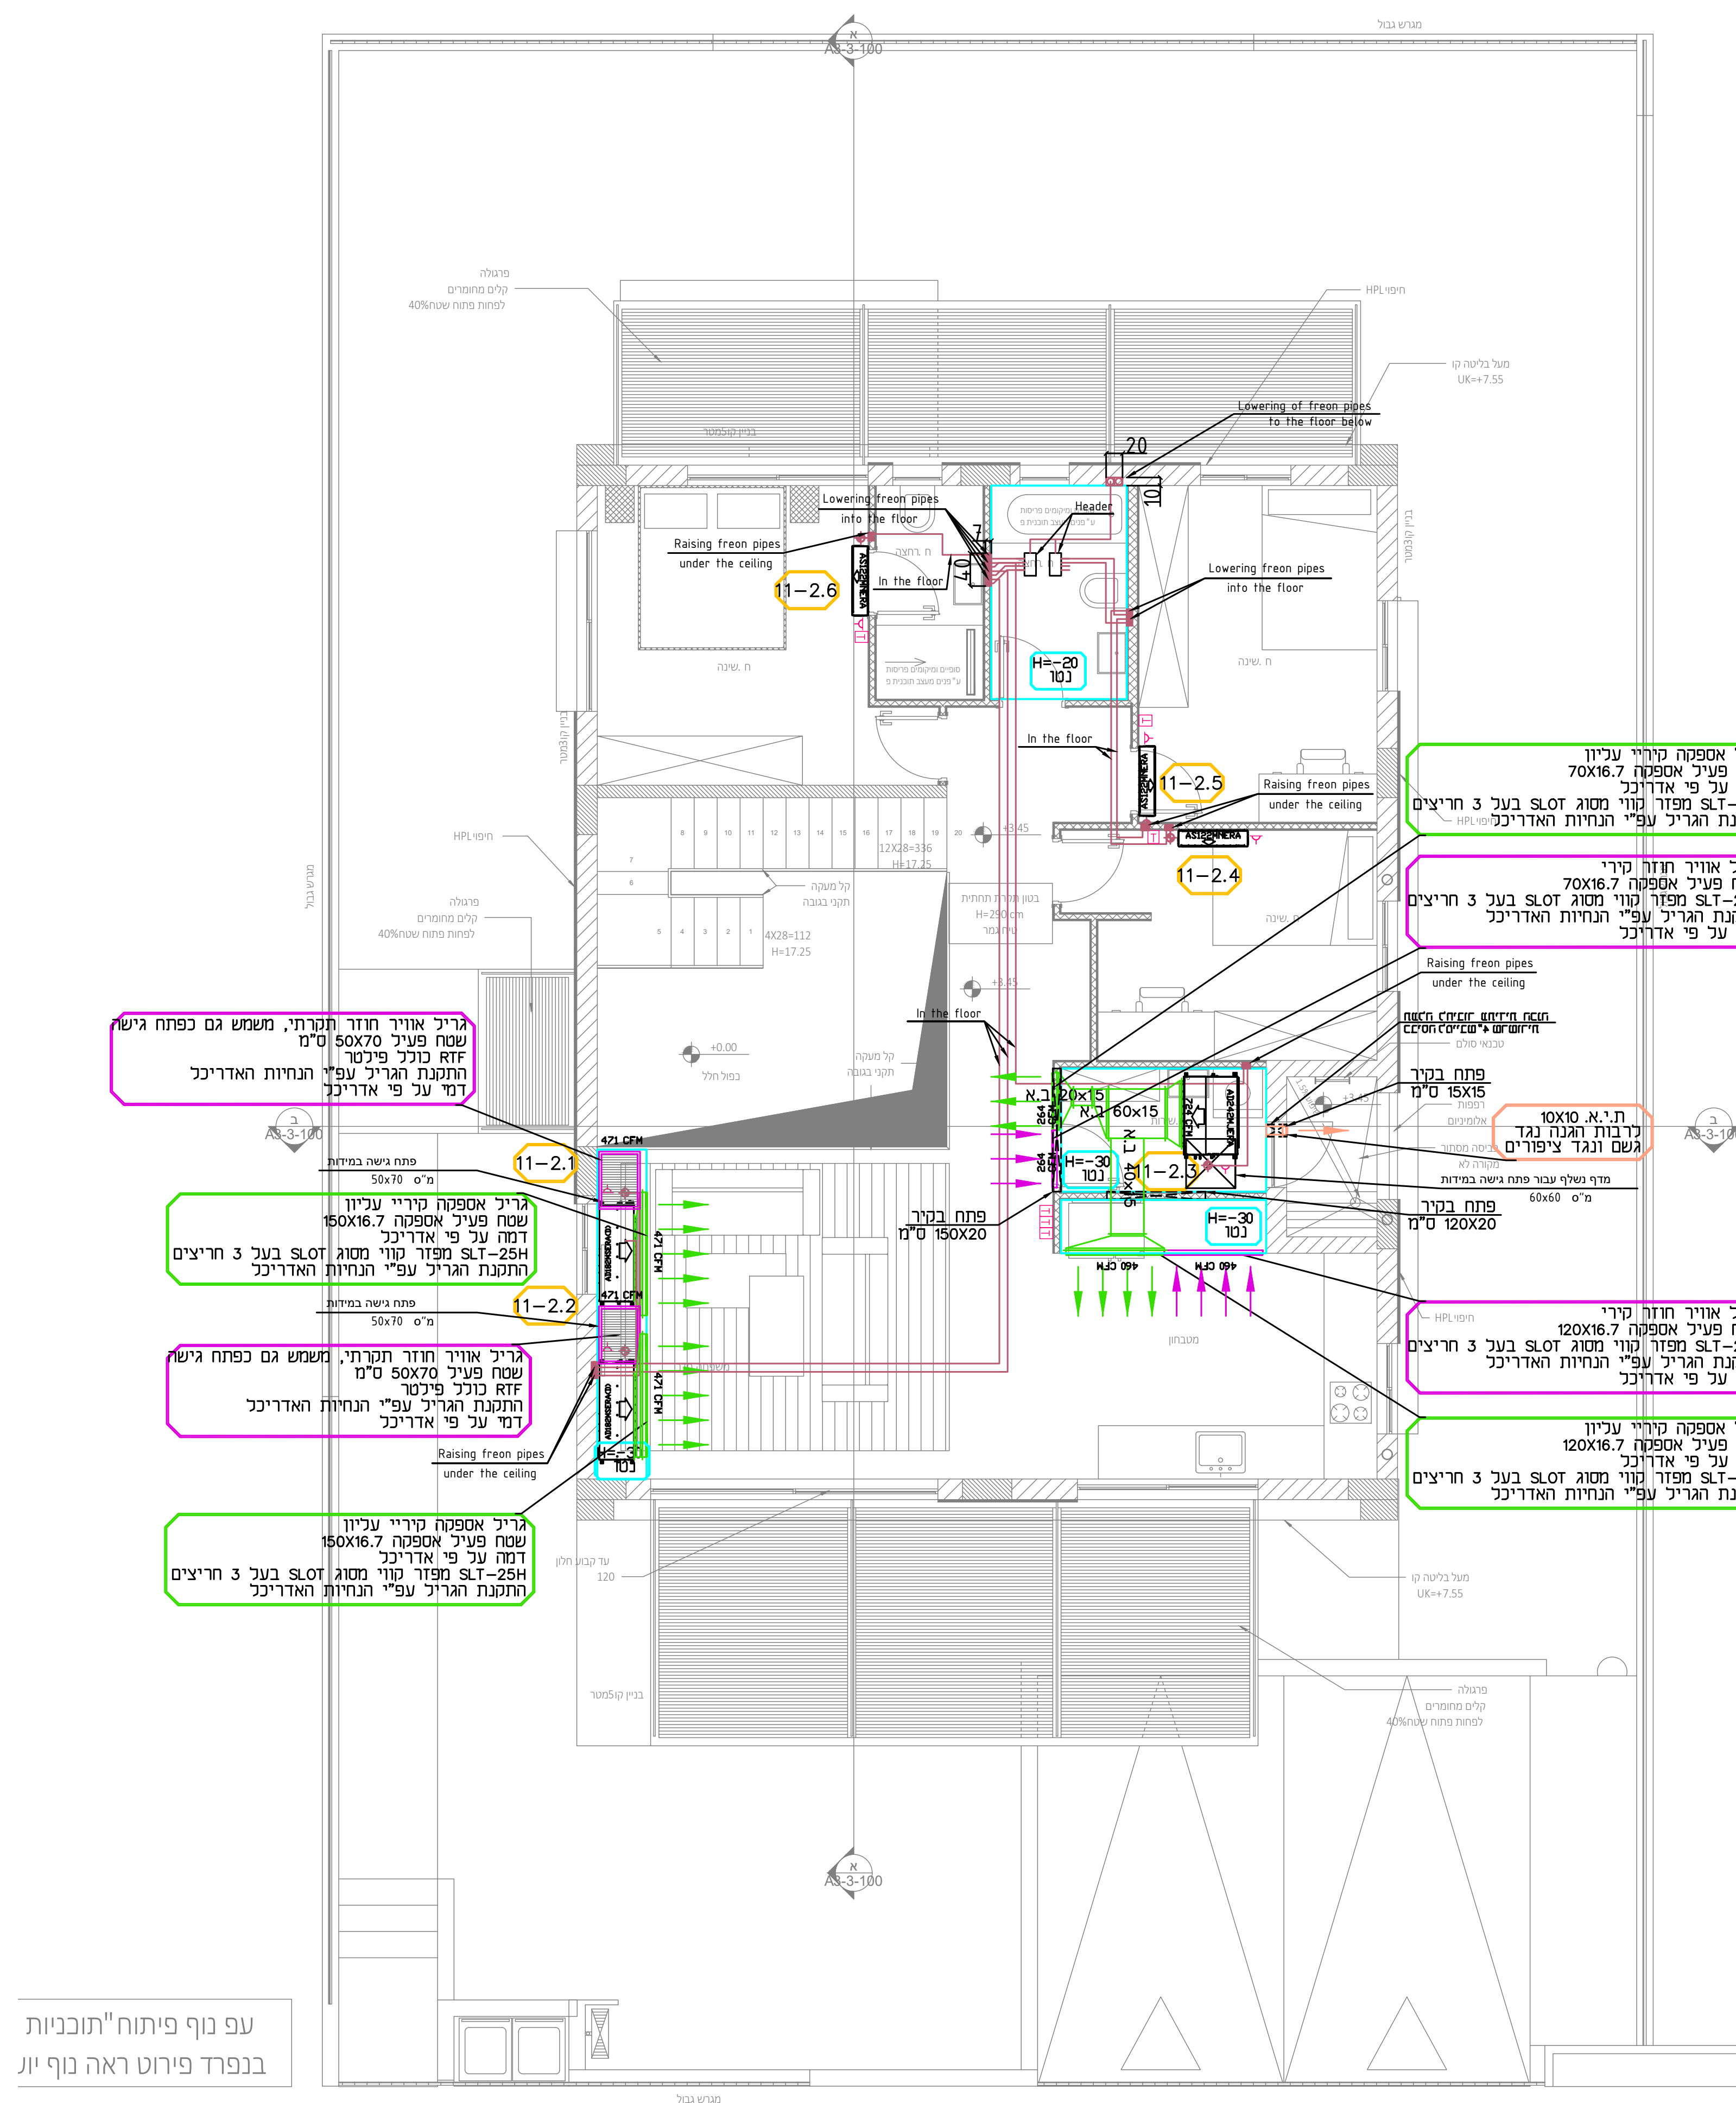

Court 11
Roof

Option **No1**

VRF duct unit in living room
and wall mounted in rooms

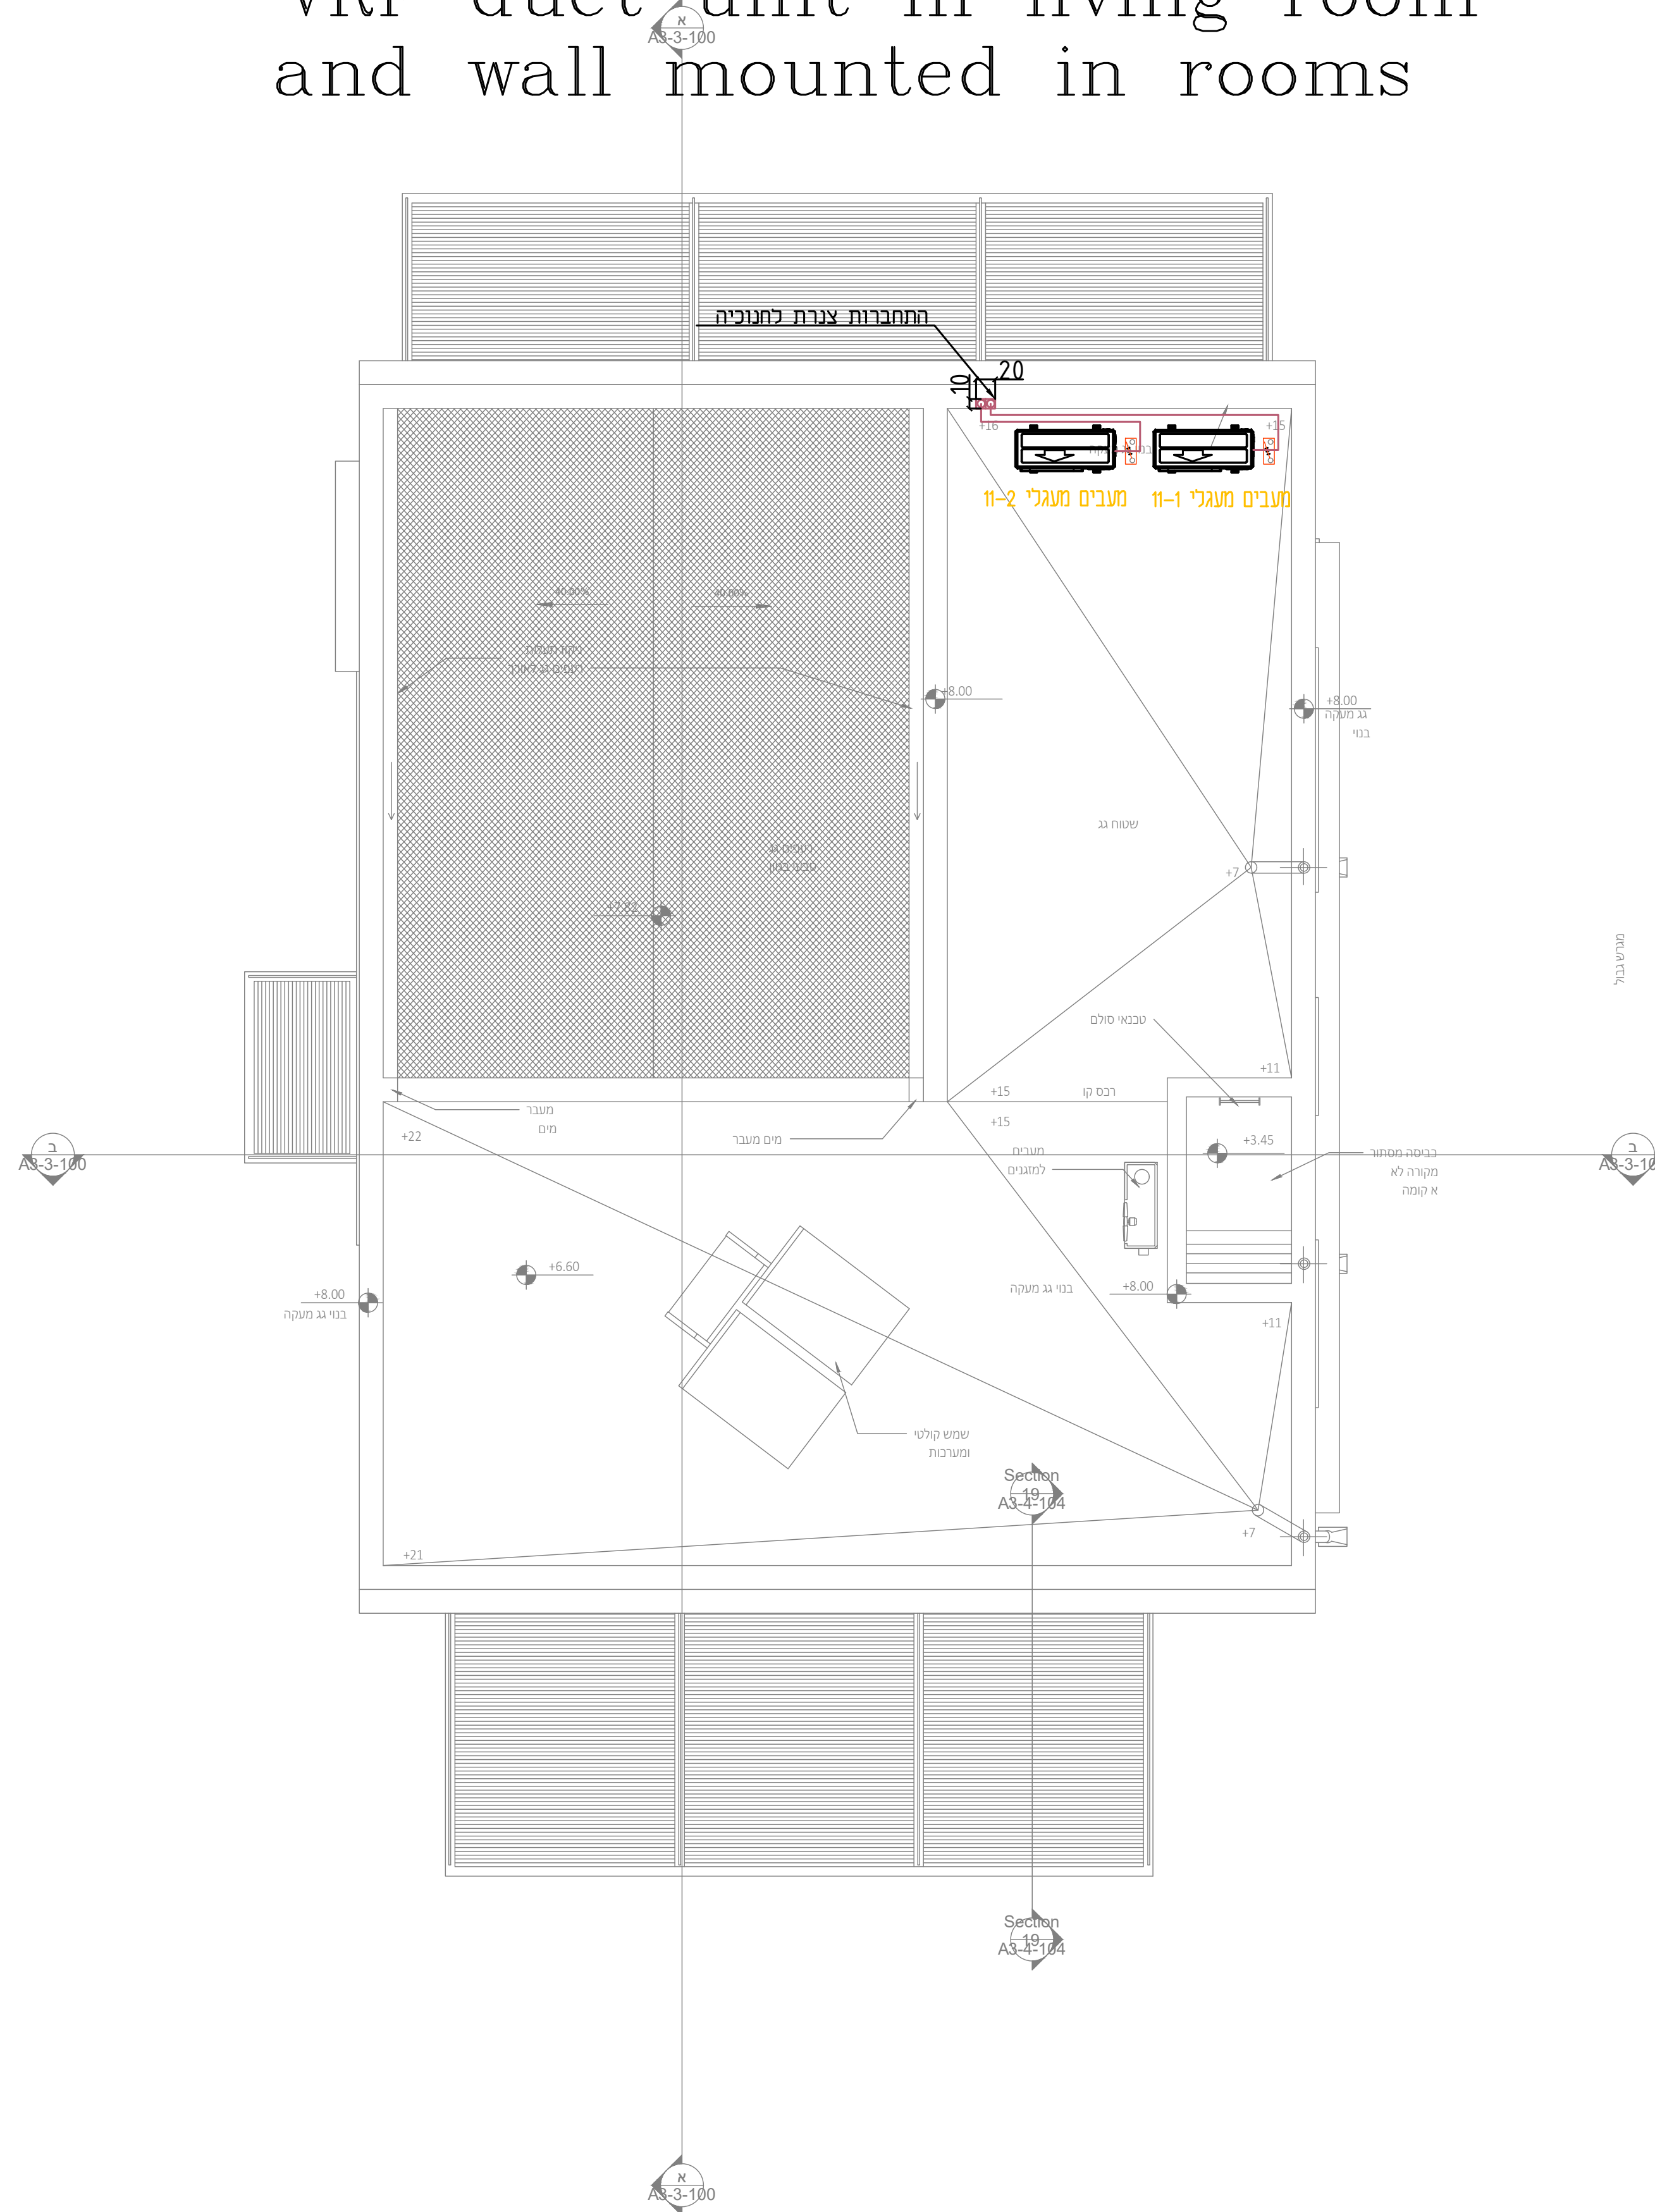

בסיס בטון בגובה מינימלי 10 ס"מ
יחידת עיבוי עומדת ע"ג בולמי רעידות
למיפול הרלו מזוג אוויר

מיקום סופי של המעבים
ייקבע בשטח
בתיאום עם האדריכל
וקבלן מיזוג אוויר

מיקום סופי של הניקוזים
ייתבע בשטח בתאום עם האדריכל
יועץ אינסטלציה וקבלן מיזוג אוויר

בסיס בטון בגובה מינימלי 10 ס"מ
יחידת עיבוי עומדת ע"ג בולמי רעידות
לטיפול קבלן מזוג אוויר

מיקום סופי של המעבים
ייקבע בשטח
בתיאום עם האדריכל
וקבלו מיזוג אוויר

מיקום סופי של הניקוזים
ייתבצע בשטח בתאום עם האדריכל
יועץ אינסטלציה וקבלן מיזוג אוויר

מעבים מעגלי-ז-11
 AVIONMSETA : דגם
 95,500 BTU/Hr : תפוקה
 40מ"ס 163.6/1057 : מידה
 3x25 [A] : נתיך חשמלי
 168 ק"ג : משקל
 8 [KW] : הספק נצרך
 58 dB(A) : /

מכשירי מעגלי II-2
AVIONMSETA : דגם
95,500 BTU/Hr : תפוקה
מ"מ 40x163.6x105.7 : מידה
3x25 (A) : נתיב השמיר
168 ק"ג : משקל
8 (KW) : צריכת
58 dB(A) : רעש

יחידות ספה תעמל 1-10											
הספק קוורט W	מחם תזנה V/Hz/Ph	פניות פני	יחידות גז	מאכלי KG	רמת רעש dB(A)	ספיקת אוויר CFM	תפוקת סירור Btu/h	מאייד	דגם	חוצרת	שם יחידה בחבנית
---	230/50/1	---	42W/85.5/85.1 ס"מ	17.5	27	283	9,500	Slim Duct Low ESP	AD092MSERA(D)	Haier	11-1,3
---	230/50/1	---	42.5W/85.5/107.1 ס"מ	24	38	547	24,200	Slim Duct Low ESP	AD242MSERA(D)	Haier	11-1,1 11-1,2
---	230/50/1	---	20W/28.8/85.5 ס"מ	10	36	352	9,500	מאייד עיני	AS092MNERA	Haier	11-1,4 11-1,5
---	230/50/1	---	25W/33.6/111.5 ס"מ	16	40	541	10,100	מאייד עיני	AS102MNERA	Haier	11-1,6

יחידות ספה מעל 2-2									
מס' יחידה בתכנית	חוצרת	דגם	מאי"ד	חפזת: קוטר Rear/h	ספוט אוויר CFM	מאכל kg	מירות פרג דלת	מחוז וזנה V/h/oz	הספק קוטר ש
11-2.3	Haier	AD242MJERA		24,800	724	42	33	230/50/1	---
11-2.1 11-2.2	Haier	AD182MSERA(D)		19,100	471	33	22.2	230/50/1	---
11-2.4 11-2.5 11-2.6	Haier	AS122MNRA	מאי"ד ע"י	12,300	371	37	10	230/50/1	---

תפוצה

[illegible]

מהדורה

חבנית ראשון	16.06.2025	
חבנית ראשון	26.05.2025	
חבנית ראשון	02.05.2025	
חבנית ראשון	31.03.2025	
חבנית מעון	11.03.2025	
שניים	חארי:	סל

המבצע אחראי למידות ולהתאמתן למציאות בכל מקרה של אי התאמה, סתירה או סעוּת עֵלִי להודיע למתכנן לפני התקדמותו בביצוע! אין לקבוע מידות על סמך מדידה בשרטוט. אין לעשות כל שימוש בתוכנית זו או ברעיונות הגלומים בה ללא אישור בכתב מאת המתכנן.

הערות

1. כל התעלות מחוץ למבנה יבודוד
ביבדוד אקוסטי בבו"ב 2"
מידות התעלות וזן מידות פח
2. תעלות מחוץ בתוך המבנה יבודוד
ביבדוד אקוסטי אקו"פ 1"
מידות התעלות וזן מידות פח
3. תעלות אוויר צה יבודוד
ביבדוד טרע"ז 1"
מידות התעלות וזן מידות פח
4. יש האסות בסימיקות ואי פינות החיבור
של תעלות מזוג אוויר לפני כיפוף
הפחים המתחברים

מקרא

- מ- מפוח
- מ-מא. - מפוח אוויר קריר
- מ-מא. - מפוח אוויר תתקרי
- מ-מא. - חריט אוויר חודר
- מ-מא. - חריט אוויר צח
- ב-א - בידוד לאוסטי
- ב-א - בידוד טרמי
- ב-ב - לכל בידוד
- ד-א - דמפר אש
- טורסטנט - לוח הפעלה
- שקע חשמל - לסיפון יועץ חשמל
- שקע תחת פאזי - לסיפון יועץ חשמל
- מסכה בחסון חדר פאזי - לסיפון יועץ חשמל
- מסכה בחסון חדר פאזי - לסיפון יועץ חשמל
- ניקוח תמידי - לסיפון פאזי אינסטלציה
- גובה 25 ס"מ מחתית גובה תמידי
- שקע חשמל אחרוני

מקרא צבעים בתכנית

- | | |
|--------------------------|---|
| תעלות ותריסי אוויר חוזר |  |
| תעלות ותריסי אספקת אוויר |  |
| תעלות ותריסי אוויר צח |  |
| תעלות ותריסי ניקת אוויר |  |
| תעלות ותריסי שחרור עשן |  |
| צנרת גז וחשמל |  |
| סימון מעגלי מיוזג אוויר |  |

[illegible]