

מתכונים:


ניהול פרויקט
מהיסוד - בן סולומון
פיקוח
מהיסוד - בן סולומון
קונסטרוקציה
ערן שילר
מיזוג אוויר
אייל ארז מהנדסים ויועצים בע"מ
אינסטלציה
איתן אלמסי
חשמל
איתן בסיס
אלומיניום
נוף
נתי בלוקא
חשמל חכם
חימום תת רצפתי
איטום
צבי טל
אקוסטיקה
מעליות
קרקע וביסוס
דיה הנדסת קרקע וביסוס
רישוי

$$\pm 0.00 = +250.20$$

הערות:
 1. תבנית זו י"ש לקרוא יחד עם תבניות הוועצים.
 2. גובה אסכולים: ארבע תבניות פחות.
 3. המידות הן ב"ב קירות ואלו כולל מ"מ.
 4. פחות השטח שמימי התובה, כלכל, מדורות, שבילים, רציפות,
 5. פשיטות בסיס, ארבע ילד-גורן: ארבע תבניות פחות.
 6. אסכולים: קירות ורצפות תחומים במגע עם הקרקע ובידוד תרמי לאורך המעטרים
 7. והקורות על-התקרות: גליות או עם מימיו (גורן) - ארבע תבניות קונסטרוקציה
 8. א"פ א"פ כיבוע כל-מידור אופייני מאבן חבושה.
 9. א"פ תרמי במסגרת עם מפרס מרמור, מאבן, ע"י פידוק מרמור.

[illegible]

זקרא קירות:

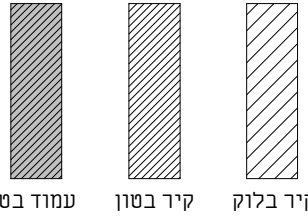[illegible]

אדריכלות

CLIENT NAME: _____ שם המזמין:

קבוצת רכישה נופיה

PROJECT NAME: שם הפרויקט:

בופיה - מגרש 12

RAWING NAME: ס הגליון:

HEET NUMBER: 197 גליון:

A3-1-100

EDITION: קנה מידה: SCALE: הדורה:

STATUS: סמטוט 1

רשט ע"י: עלמוט גור
נבדק ע"י:

DATE: 22.09.2025 עמוד: 1



NeumanHaynerArchitects


office@nh-arch.com
www.nh-arch.com

וימן חיינר אדריכלים
אורד ההדרים 2, בית חירות
טל 09-9545842

זכויות ייצור / ע"פ הנחיות עו"ד

נופיה - מגרש 12			
מס' גיליון	שם גיליון	מהדורה	תאריך הפצת מהדורה

22.09.2025	1	גליון שער	A3-1-100
22.09.2025	1	תכנית קומת קרקע	A3-1-101
22.09.2025	1	תכנית קומה א	A3-1-102
22.09.2025	1	גג	A3-1-103
22.09.2025	1	חזיתות 1	A3-2-200
22.09.2025	1	חזיתות 2	A3-2-201
22.09.2025	1	חתכים	A3-3-100
22.09.2025	1	גליון מדרגות	A3-4-100
22.09.2025	1	פרטים	A3-4-103
22.09.2025	1	פרטי פרגולה	A3-4-104
22.09.2025	1	רשימת פתחים	A3-6-1000

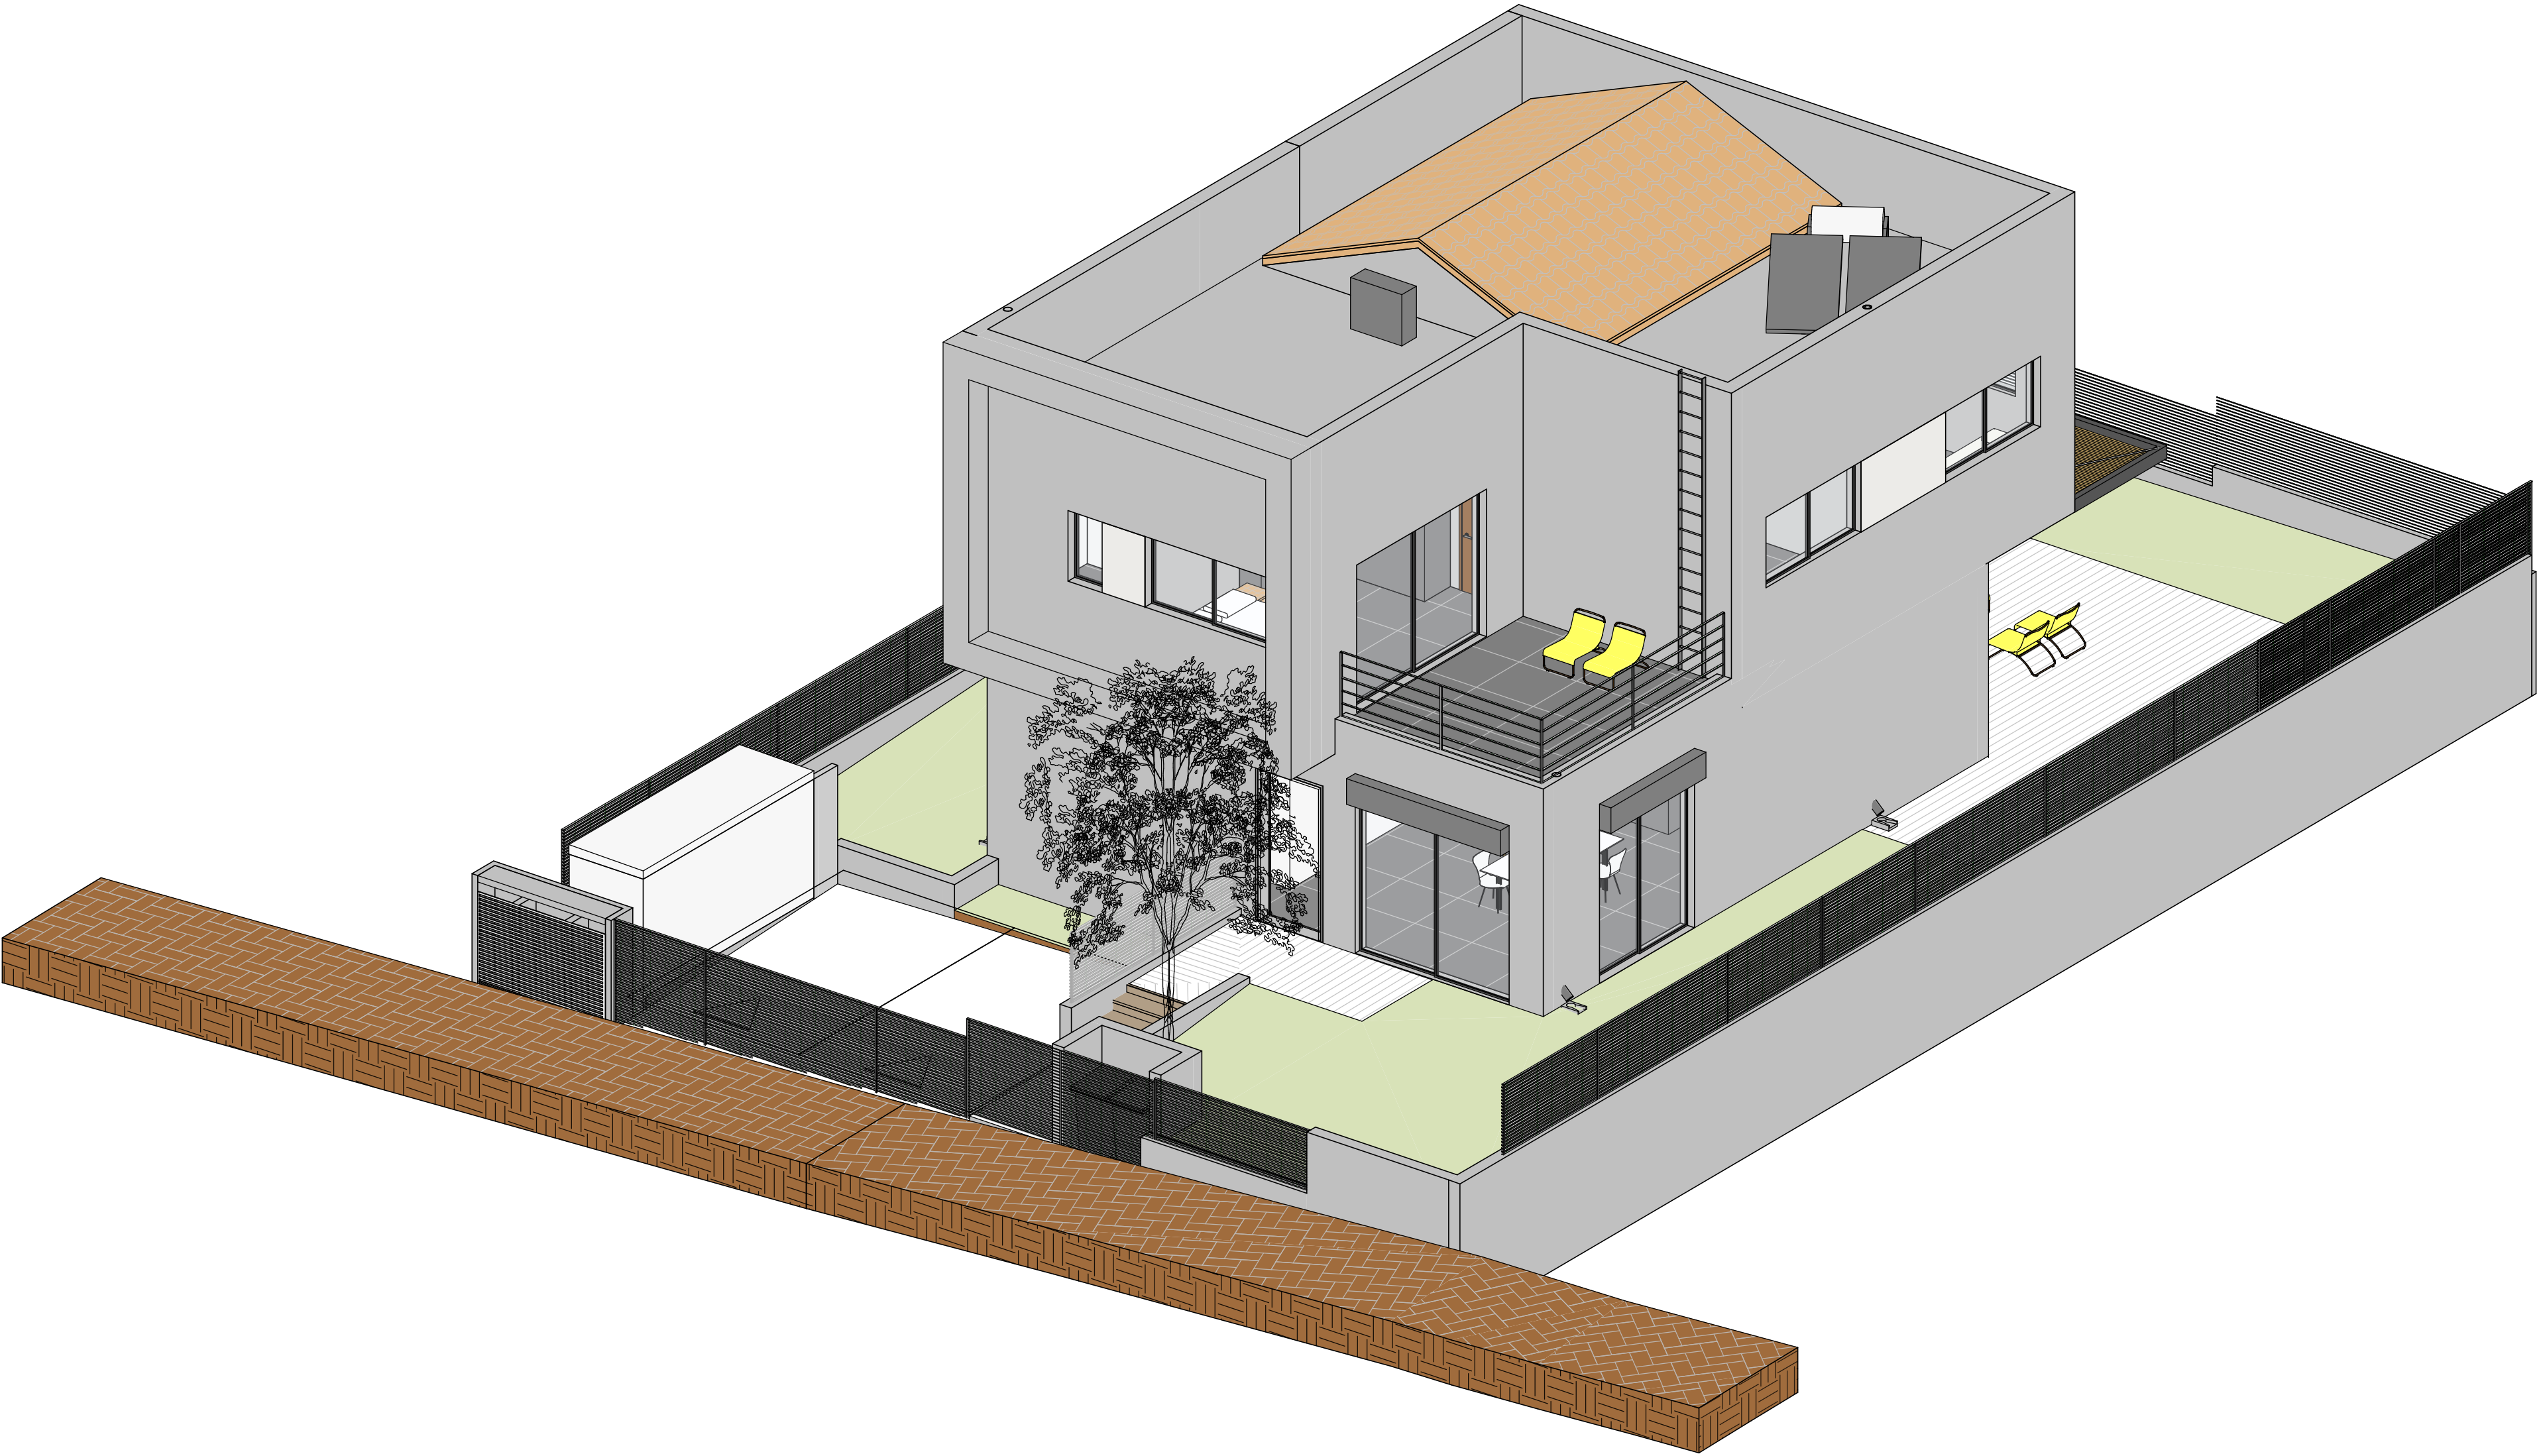

ניהול פרויקט
מהיסוד - בן סולומון
פיקוח
מהיסוד - בן סולומון
קונסטרוקציה
ערן שילר
מזוג אוויר
אייל ארז מהנדסים ויועצים בע"מ
אינסטלציה
איתן אלמסי
חשמל
איתן בסיס
אלומיניום
בנף
נתי בלוקא
חשמל חכם
חימום תת רצפתי
איטום
צבי טל
אקוסטיקה
מעליות
קרקע וביסוס
דיה הנדסת קרקע וביסוס
רישוי

[illegible]

עמוד בטון קיר בטון רצפת בטון


[illegible]

CLIENT NAME:	הפרויקט:	
קבוצת רכישה נופיה		
PROJECT NAME:	הפרויקט:	
נופיה - מגרש 12		
DRAWING NAME:	הפרויקט:	
תכנית קומת קרקע		
SHEET NUMBER:	פרוטוקול:	
A3-1-101		
SCALE:	קנה מידה:	EDITION:
1 : 50		
STATUS:	סטוס:	
למכר		
	נבדק ע"י:	
		אלמוג אור
DATE:	22.09.2025	יר:

NeumanHaynerArchitects

ימן חיינר אדריכלים
רוד ההדרים 2, בית חירות
09-9545842

זכויות יצור / ע"פ הו"ח עו"ד

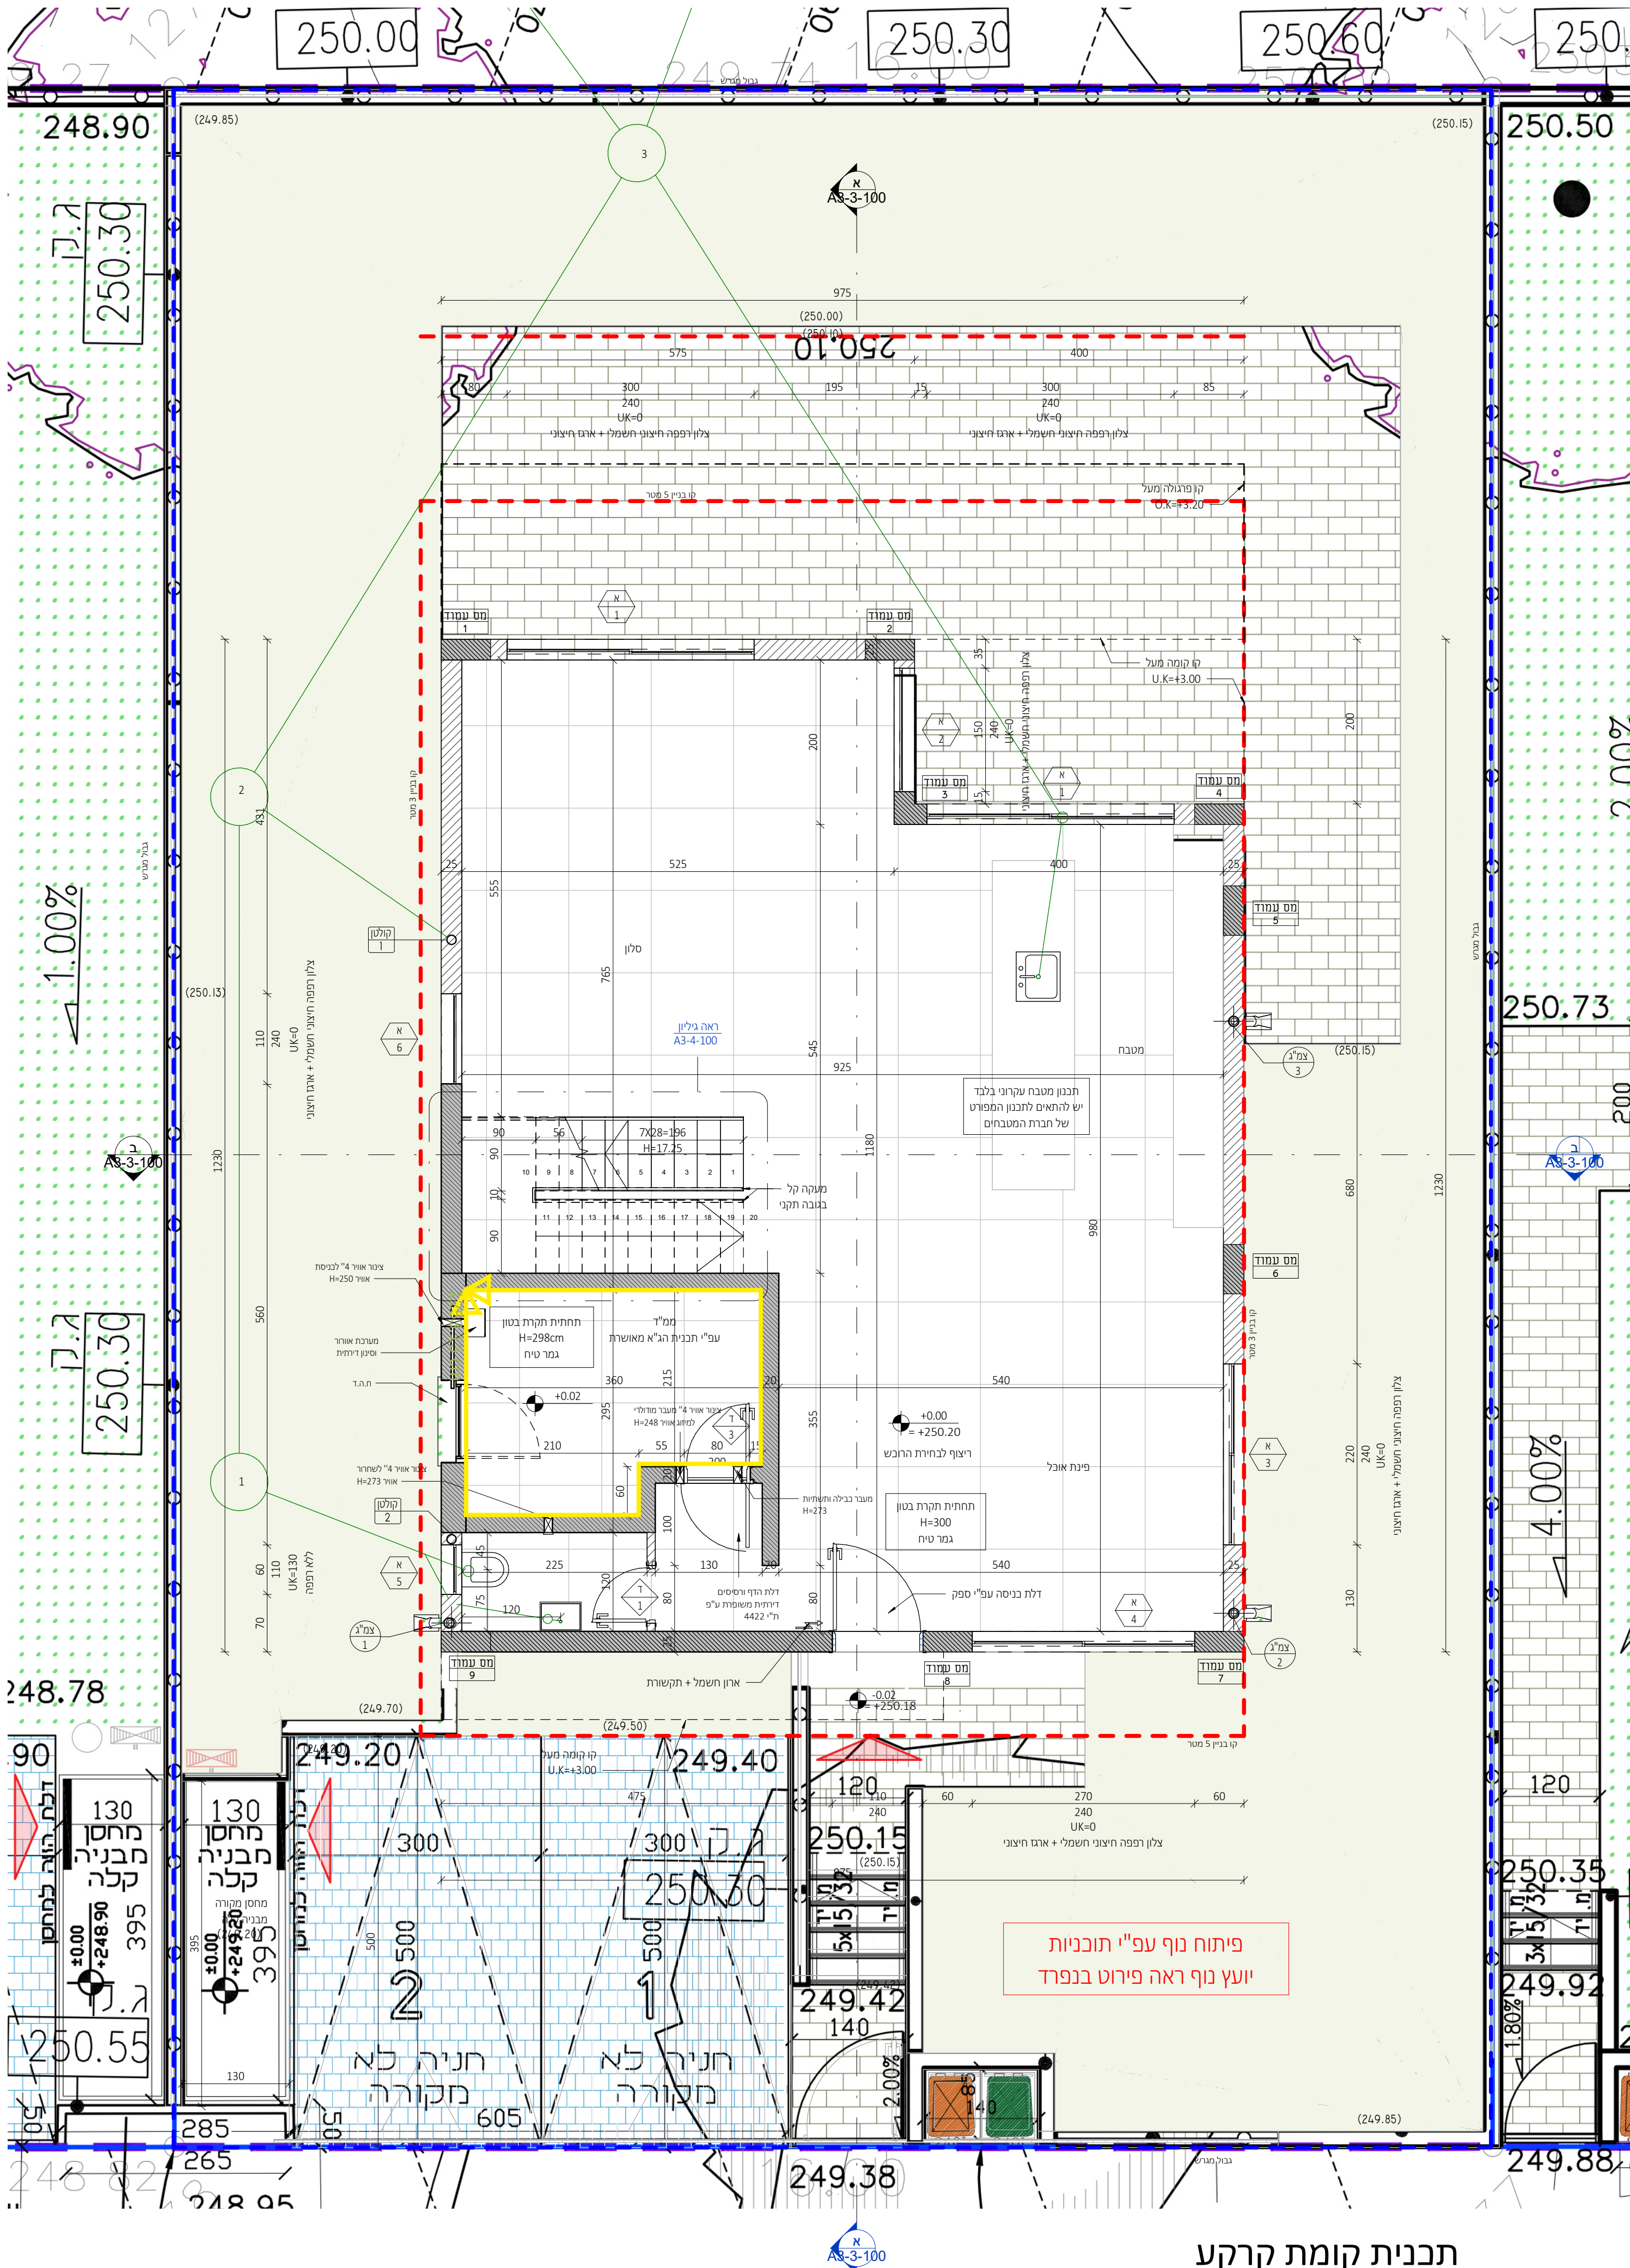

1 : 50

1. יש לעבוד במקביל לתכניות יועצים המאושרות על ידי האדריכל.
2. פרטי ספי חלון - עפ"י חוברת אלומיניום של הספק הנבחר ובתיאום מול אדריכל.
3. חימום תת רצפתי (במידה ויש במגרש זה) עפ"י פרטי הספק ובתיאום מול אדריכל.
4. יש לעבוד במקביל לתכניות עיצוב פנים (במידה ויש מעצב פנים במגרש זה) המאושרות על ידי האדריכל.
5. באחריות הקבלן לעדכן את האדריכל על אי התאמה בין התכניות יועצים לאדריכלות.
6. כל הדלתות לפי מפרט מצורף.
7. כל אלמנטי הבטון יקבלו התייחסות תרמית לפי הנחיות יועץ.
8. פרטי איטום, בידוד וניקוז עפ"י תכניות יועצים ובאחריות הקבלן.

מתכונים:


ניהול פרויקט
מהיסוד - בן סולומון
פיקוח
מהיסוד - בן סולומון
קונסטרוקציה
ערן שילר
מיוזג אוויר
אייל ארז מהנדסים ויועצים בע"מ
אינסטלציה
איתן אלמסי
חשמל
איתן בסיס
אלומיניום
נוף
נתי בלוקא
חשמל חכם
חימום תת רצפתי
איטום
צבי טל
אקוסטיקה
מעליות
קרקע וביסוס
דיה הנדסת קרקע וביסוס
ירשני

+ 0.00 = +250.20

הערת:
 תכנית זו איש לקראת ידע תכנית הוועיצים.
 נגבה אבסולוט. ראו תכנית פיתוח.
 הפיתוח הוא בלא קורות הבית, כולל, מדרגות, בחדר, ריצופים, שטיפים, שטיחים ויגון-רא תכנית פיתוח.
 איסוס ותקופות התקופות במבנה עם הקרקע בידוד תמי לאורך המעודים
 התקופות וכל התקופות, גלירות ואם פילי (יגון). ראו תכנית פיתוח/סנסקורק
 אדם קיצוץ כלל תמי אופקי הכולל תכנית.
 שים תיחם תכנית, טיפ פסוס תכנית, תאוסו טי פיקוד העורף.

[illegible]

קרא קירות:

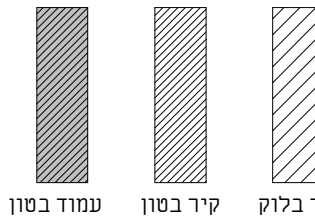[illegible]

אדריכלות

CLIENT NAME: _____: המזמין:

קבוצת רכישה נופיה

PROJECT NAME: הפרויקט:

בופיה - מגרש 12

DRAWING NAME: תגליון:

תכנית קומה א

SHEET NUMBER: 99 גליון:

A3-1-102


SCALE: קנה מידה: EDITION: דורה: ^

1 : 50

למחרת

רמטט ע"י:	אלמוג יצור	ובדק ע"י:
-----------	------------	-----------


DATE: 22.09.2025 י"ד

 

NeumanHaynerArchitects

ימן חיינר אדריכלים
בנין חדרים 4 בתי מדרשות

www.nh-arch.com 09-9545842 7

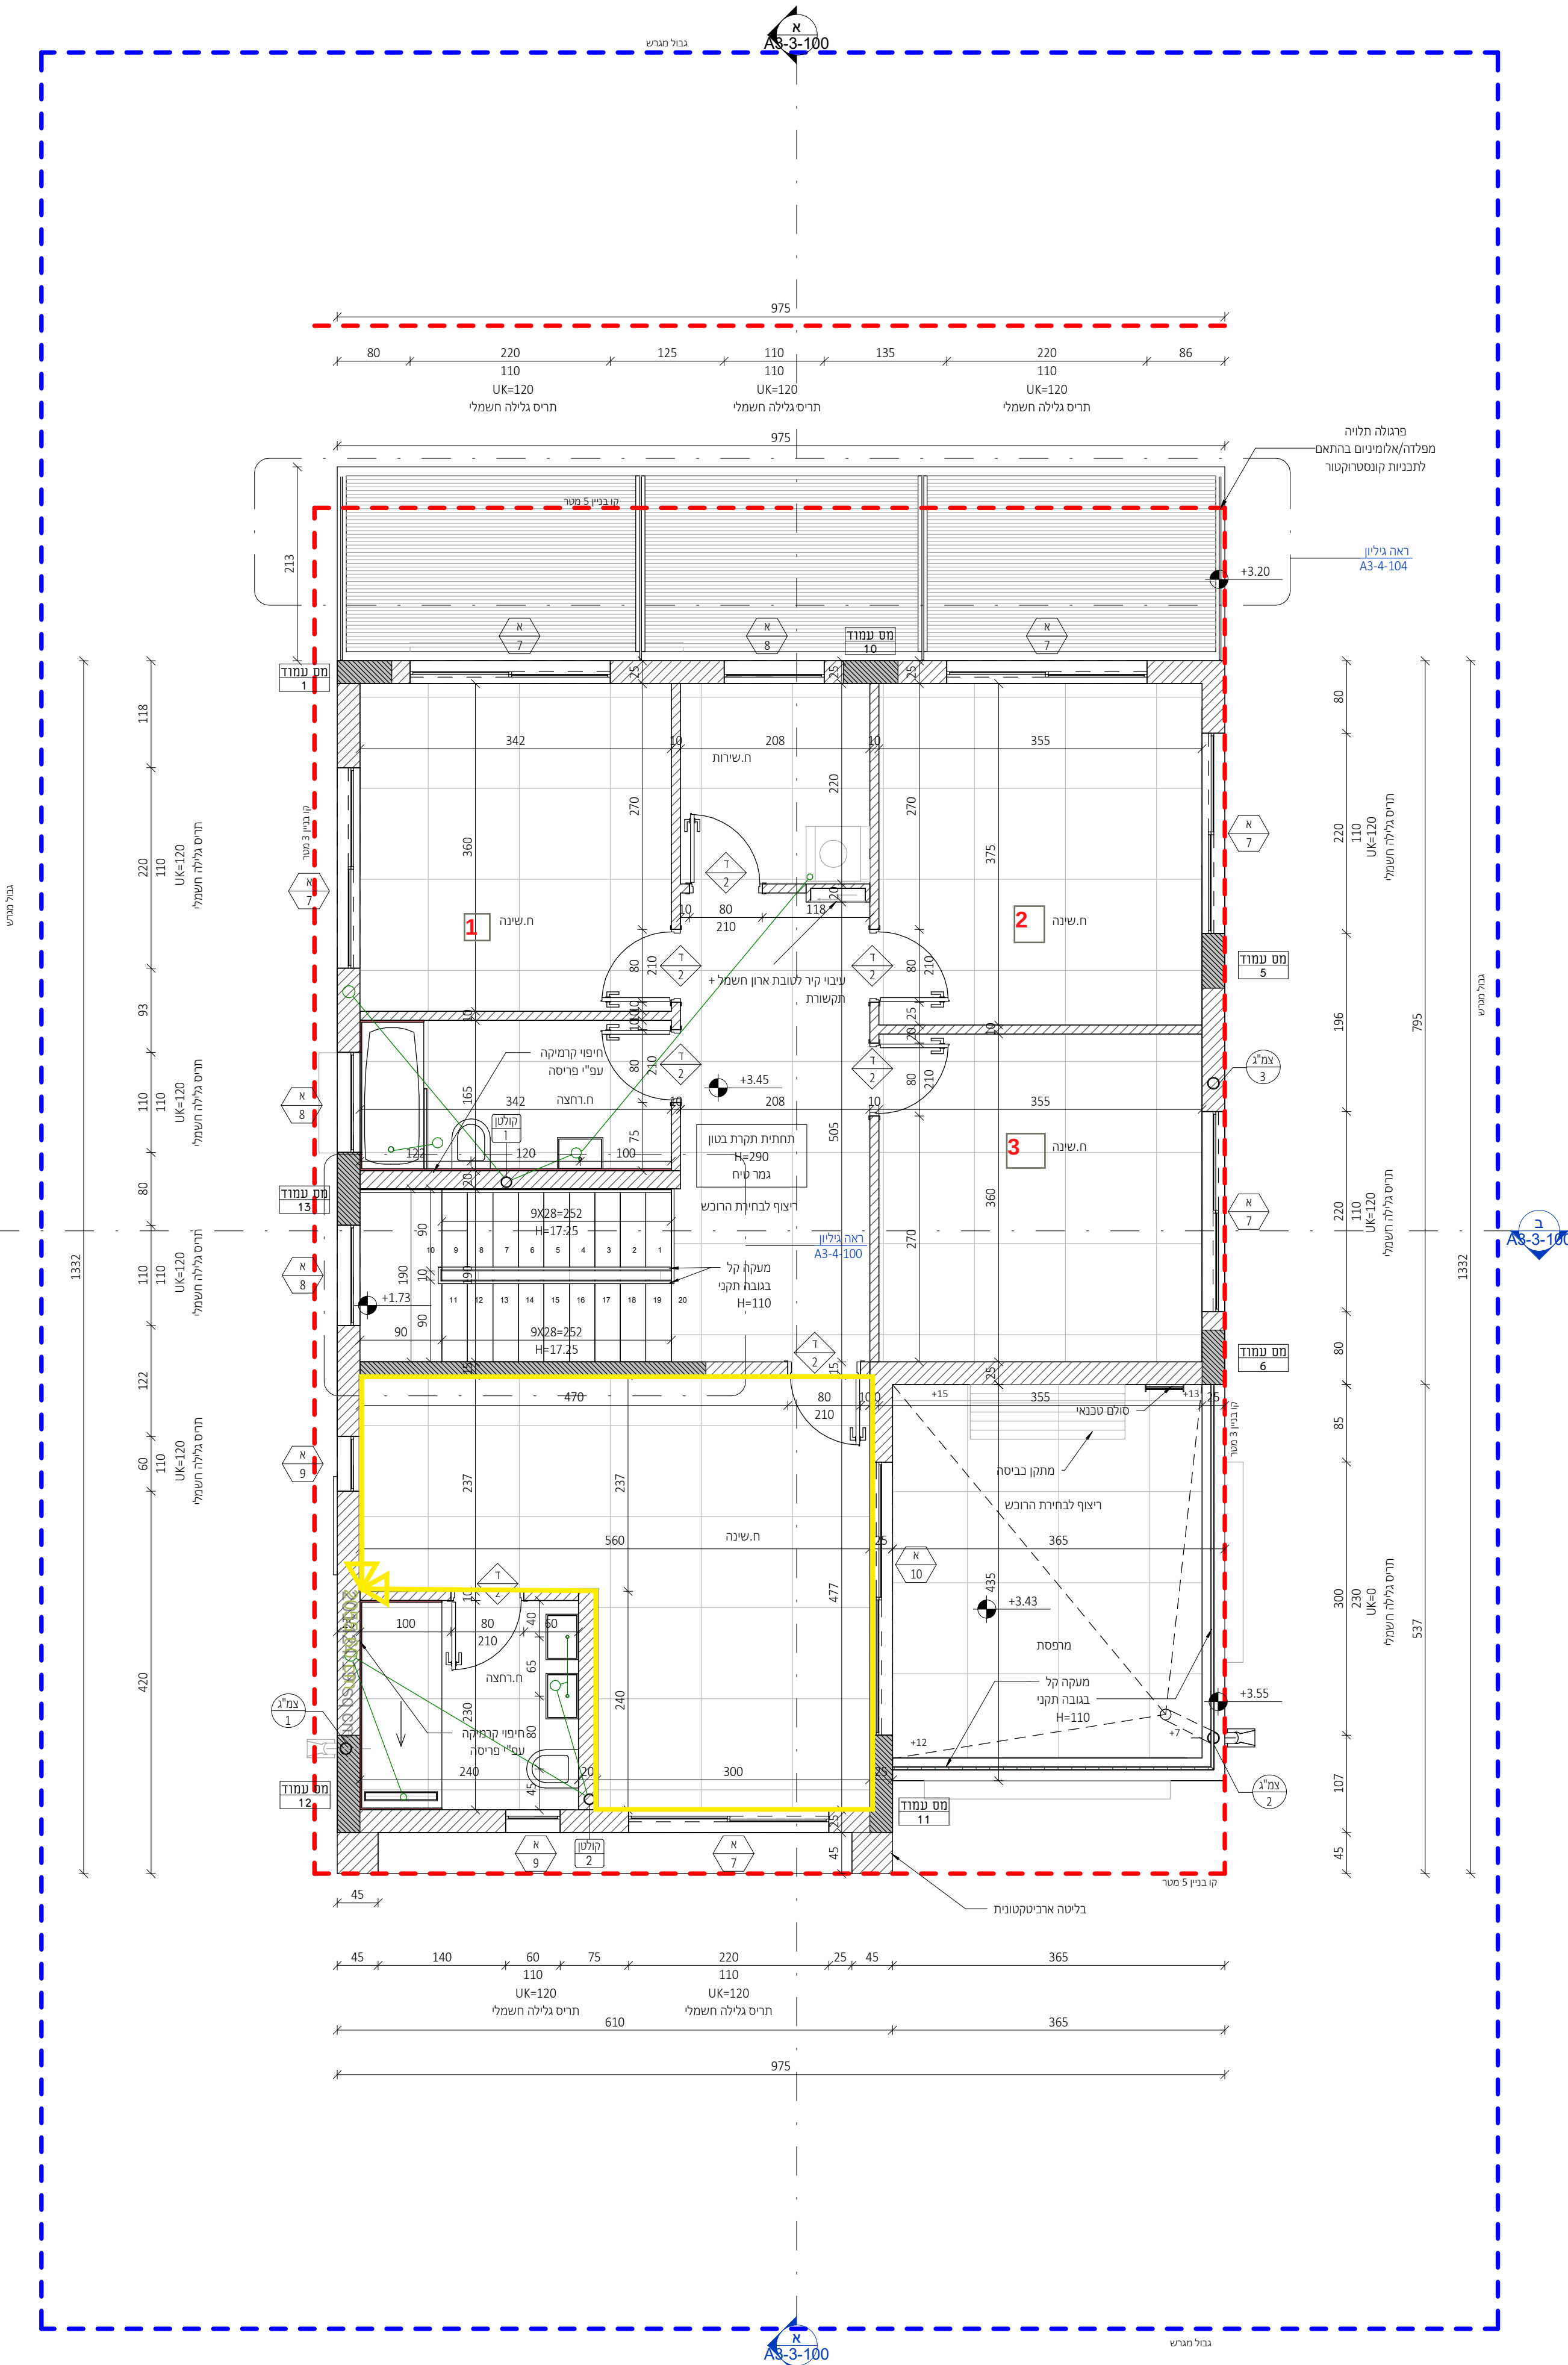

תכנית קומה א

1 : 50

הערות:

1. יש לעבוד במקביל לתכניות יועצים המאושרות על ידי האדריכל.
2. פרטי ספי חלון - עפ"י חוברת אלומיניום של הספק הנבחר ובתיאום מול אדריכל.
3. חימום תת רצפתי (במידה ויש במגרש זה) עפ"י פרטי הספק ובתיאום מול אדריכל.
4. יש לעבוד במקביל לתכניות עיצוב פנים (במידה ויש מעצב פנים במגרש זה) המאושרות על ידי האדריכל.
5. באחריות הקבלן לעדכן את האדריכל על אי התאמה בין התכניות יועצים לאדריכלות.
6. כל הדלתות לפי מפרט מצורף.
7. כל אלמנטי הבטון יקבלו התייחסות תרמית לפי הנחיות יועץ.
8. פרטי איטום, בידוד וניקוז עפ"י תכניות יועצים ובאחריות הקבלן.

מתכונים:

ניהול פרויקט
מהיסוד - בן סולומון
פיקוח
מהיסוד - בן סולומון
קונסטרוקציה
ערן שילר
מיוזג אוויר
אייל אזר מהנדסים ויועצים בע"מ
אינסטלציה
איתן אלמסי
חשמל
איתן בסיס
אלומיניום
נוף
נתי בלוקא
חשמל חכם
חימום תת רצפתי
איטום
צבי טל
אקוסטיקה
מעליות
קרקע וביסוס
דיה הנדסת קרקע וביסוס
רישוי

$$\pm 0.00 = +250.20$$

רות:

- תכנית זו יש לקרוא יחד עם תכנית היועצים.
גובה הסבסובל – ראו תכנית פיתוח.
המיתות הן בין קירות הבניה (כלל כולל סיח).
פיתוח השטח הבניה – חדרות, כולל, חדרות, שבילים, רציפים,
פועינים וכו'.
אישום פיתוח תוכנית ההבנה ממעט עם הקרקע וכיבוד תכנית לאורך העמודים
הקורות ועל התקרות – לרבות לא עם פיתוח – ראו תכנית תוססורציה
אף שם יבוצע בעל משרד אופעי תבועס חבנין.
אם תרתי ממתי – ע"פ משרד תבועס חבנין, מאמר ע"י פוקד העורף.

המבצע אחראי למידות: עליו לבקר ויבדוק את כל המידות הבחיניות ובמסגרת המבדור.
מקדים של שעות או ימי התאמה בחיניות ו/או בבנין, עליו להודיע על
מידות לאורכיים בסוף המשך נעבודתו.
המבצע ישתמש ארוך בחיניות שאסור לביצוע.
המבצע יבדוק אחת, בכל שנה, שעות שחזר על ביצוע.
המבצע יבדוק שעות שחזר על ביצוע שעות שחזר על ביצוע.
החינוכית הורה שהאדריכל יעלה על שימוש בה או ברעיונות
הגלויים, ב, אלס באישור כתבת האדריכל
המנהל ו/או יועץ אשר מוסר שעות בחיניות, ו, נטא לבדו באחיות
המפעילות החוקיות לחיניות.
על הפסקה והקצול, וזאת התאמת החיניות האדריכלית "לביצוע"
לחיניות: תורן, המכר החיניות והאשכולות ע"י כל הגורמים שהם
המבצע יבדוק שעות שחזר על ביצוע שעות שחזר על ביצוע.

מקרא קירות:

[illegible]

אדריכלות

CLIENT NAME: _____: המזמין:

קבוצת רכישה נופיה

PROJECT NAME: הפרויקט:

נופיה - מגרש 12

DRAWING NAME: תגלית

גג

SHEET NUMBER: 99 גליון:

A3-1-103

SCALE: קנה מידה: EDITION: דורה:

1 : 50

STATUS:

0.10

DATE: 22.09.2025




NeumanHaynerArchitects

ימן חיינר אדריכלים

09-9545842 ל' **ורד ההדרים 2, בית חירות**

09-9545842 7

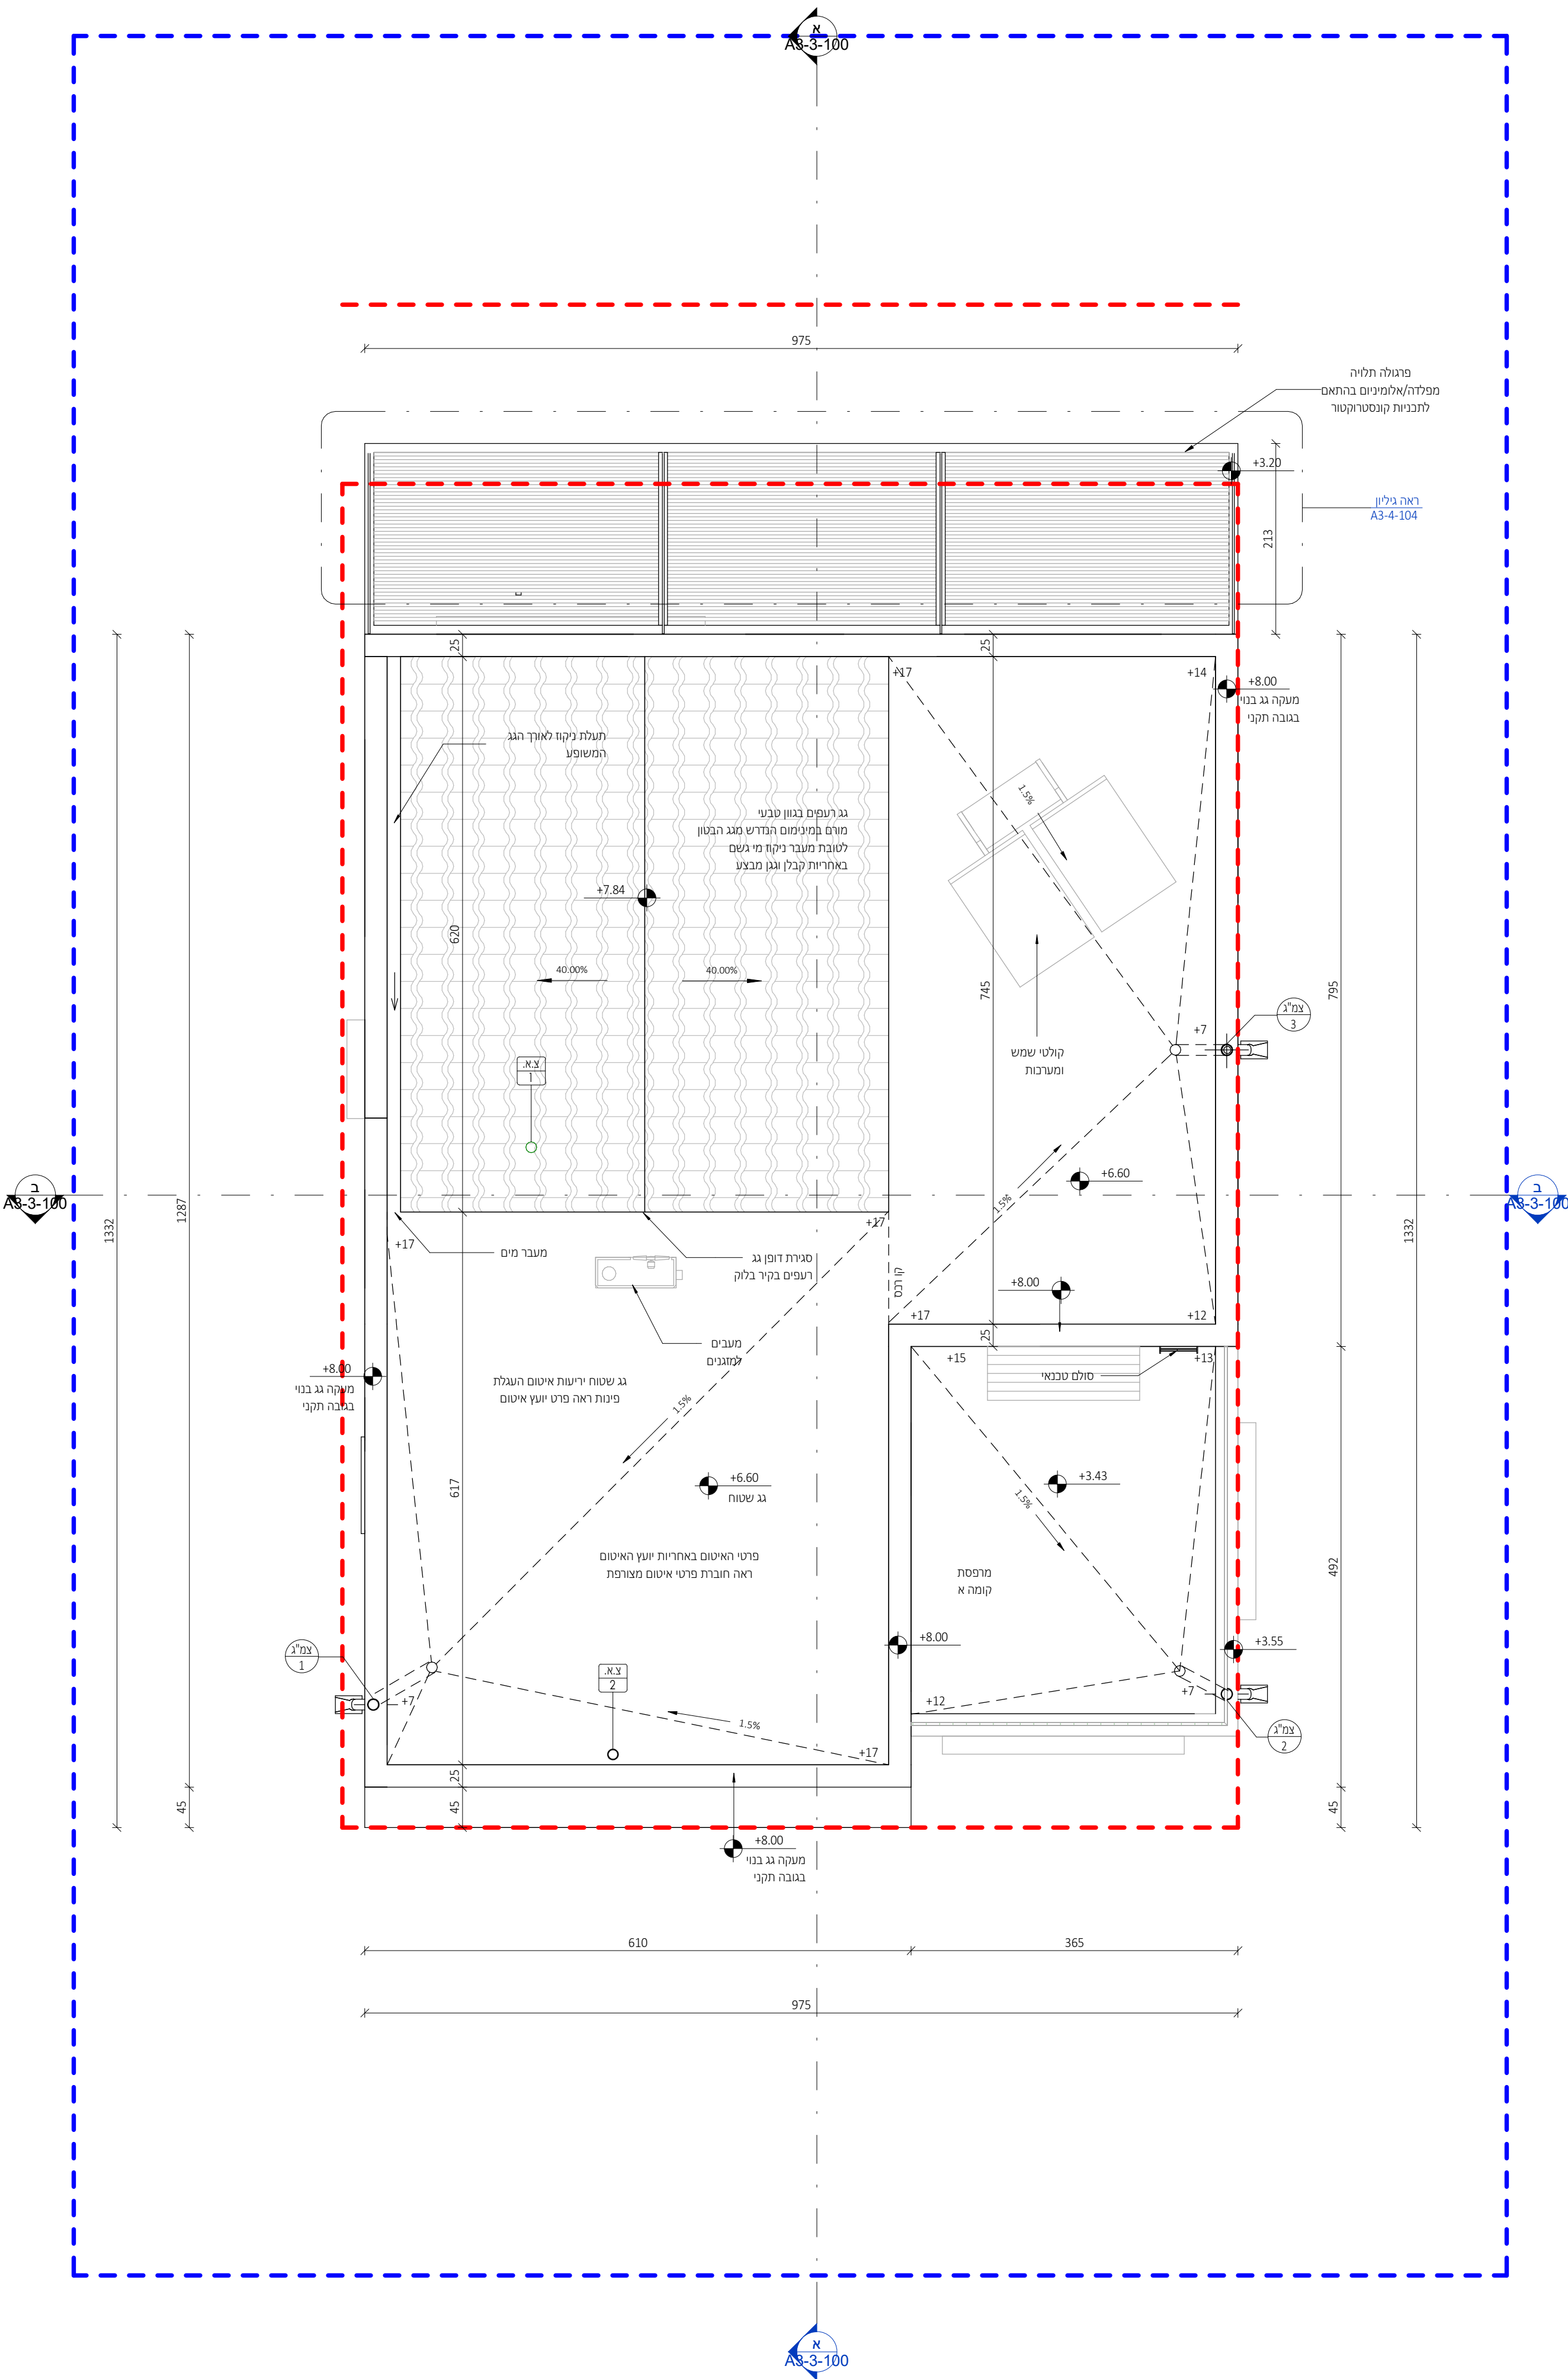

תכנית גג

1 : 50

מתכננים:

ניהול פרויקט
מהיסוד - בן סולומון
פיקוח
מהיסוד - בן סולומון
קונסטרוקציה
ערן שילר
מיזוג אוויר
אייל ארז מהנדסים ויועצים בע"מ
אינסטלציה
איתן אלמסי
חשמל
איתן בסיס
אלומיניום
נוף
נתי בלוקא
חשמל חכם
חימום תת רצפתי
איטום
צבי טל
אקוסטיקה
מעליות
קרקע וביסוס
דיה הנדסת קרקע וביסוס
רישוי

± 0.00 = +250.20
הערות: 1. תכנית זו יש לקרוא יחד עם תכנית הרושפים. 2. גובה אבסולוטי - ראו תכנית פיתוח. 3. הפרדות הן בין קירות הבניה ולא כולל פיתוח. 4. פיתוח השטח סביב הבנויה, כולל, מדרגות, גדרות, שבילים, ריצופים, שטחים גרושים, חניה וגן ואף תכנית פיתוח. 5. איטום קירות ורצפות הבנויה כמנוע עם הקרקע ובידוד תורני לאורך העמודים והקורות ופיר סימני (גומן) - ראו תכנית קונסטרוקציה. 6. אף דום יבוצע בכל מישור אופקי הכולל מהבנויה. 7. סיוח תורני במסגרת - ע"פ מפרט תרומקור, מאושר ע"י פיקוח העונדף. הנבעת אחראי למידות : עליו לבקר ולבדוק את כל המידות בתכנית ובמקום הבנויה. במסגרת של מידות או אי התאמה בתכנית /או בבנוי, עליו להודיע על כך מיד לאדריכל בסיום המשיך בעבודותיו. המבצע יתחשב או ויק, בתכנית שאושר לכניסו. המבצע יחזיק באחר, בכל של, של מידות של תכנית. אין לקבוע מידות על ידי חדייה בשום מום. התכנית הנה רכוש האדריכל ואין לשנות כל שימוש בה או ברעיונות הגלומים בה, אלא באישור בכתב מהאדריכל. מוחזק /או יושב אשר שמו רשום בתכנית זו, נושא לכיד באחריות המקצועית והטכנית לתכנית. על המפעל והמבצע לזרוא התאמת התכנית האדריכלית "לכניסו" לתכנית זוהי, המכר והתכנית האושרות ע"י כל הגורמים הרשמיים. התכנית כוללת את כל האחריות והידוע עד ליום חתימתה.

משרד קירות:



תאריך	תיאור	מהדורה
22.09.2025	מכרז	1

אדריכלות


שם המסמך:	CLIENT NAME:
קבוצת רכישה נופיה	
שם הפרויקט:	PROJECT NAME:
נופיה - מגרש 12	
שם הגיליון:	DRAWING NAME:
חזיתות 1	
מספר גיליון:	SHEET NUMBER:
A3-2-200	
תאריך:	DATE:
22.09.2025	




נירסן חיינר אדריכלים
מנכ"ל ומנהל
09-5545642
www.nh-arch.com
office@nh-arch.com

חזית דרומית

1 : 50

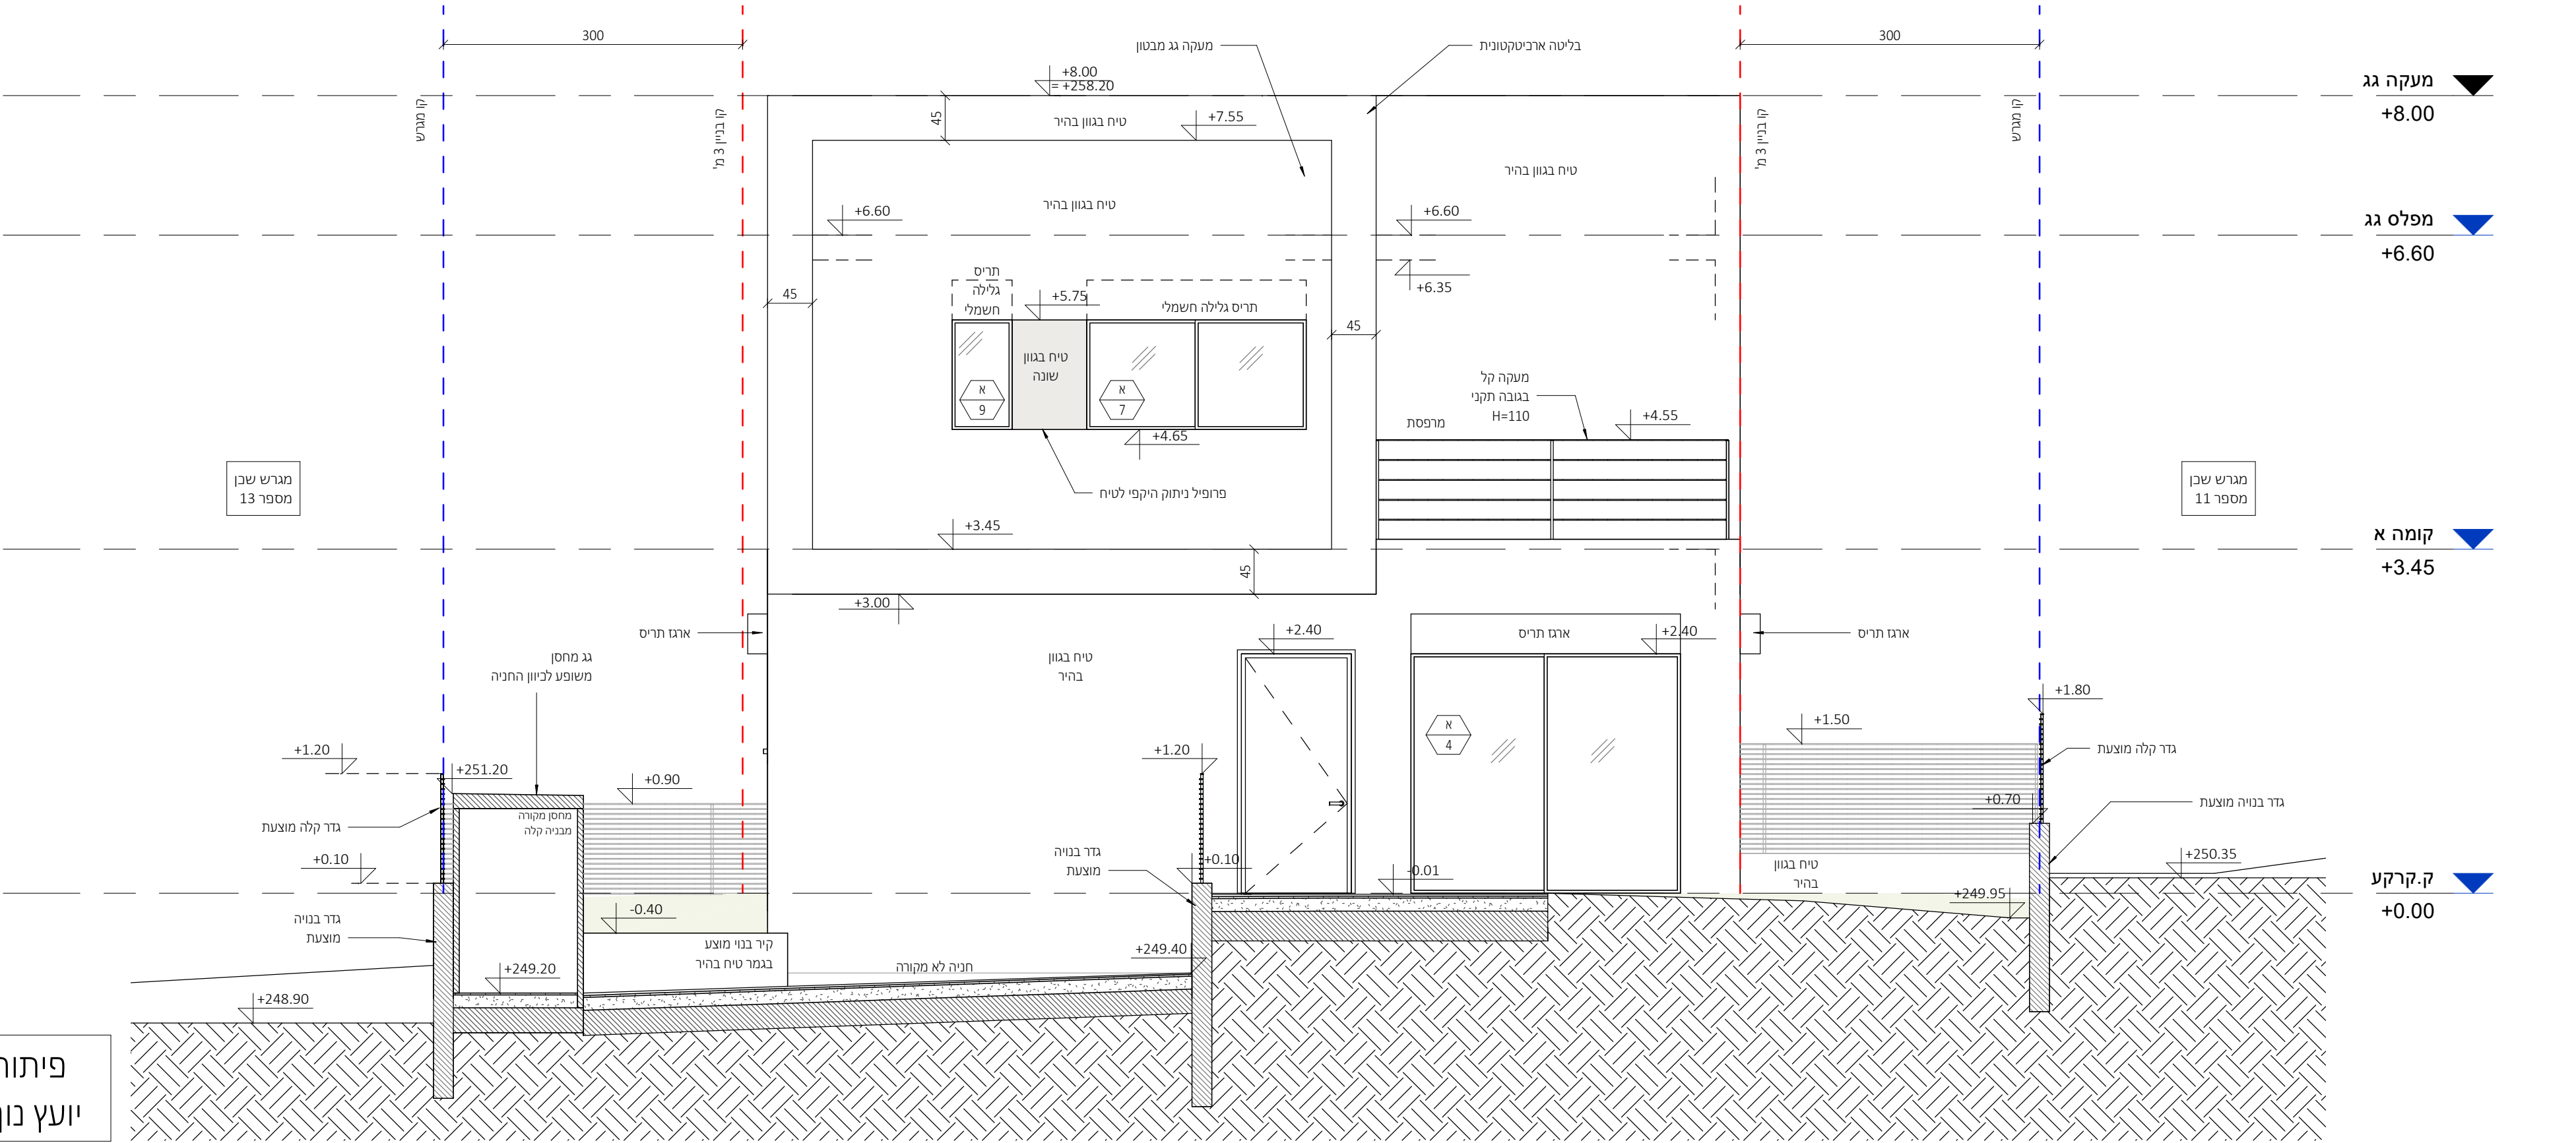

פיתוח נוף עפ"י תוכניות
יועץ נוף ראה פירוט בנפרד

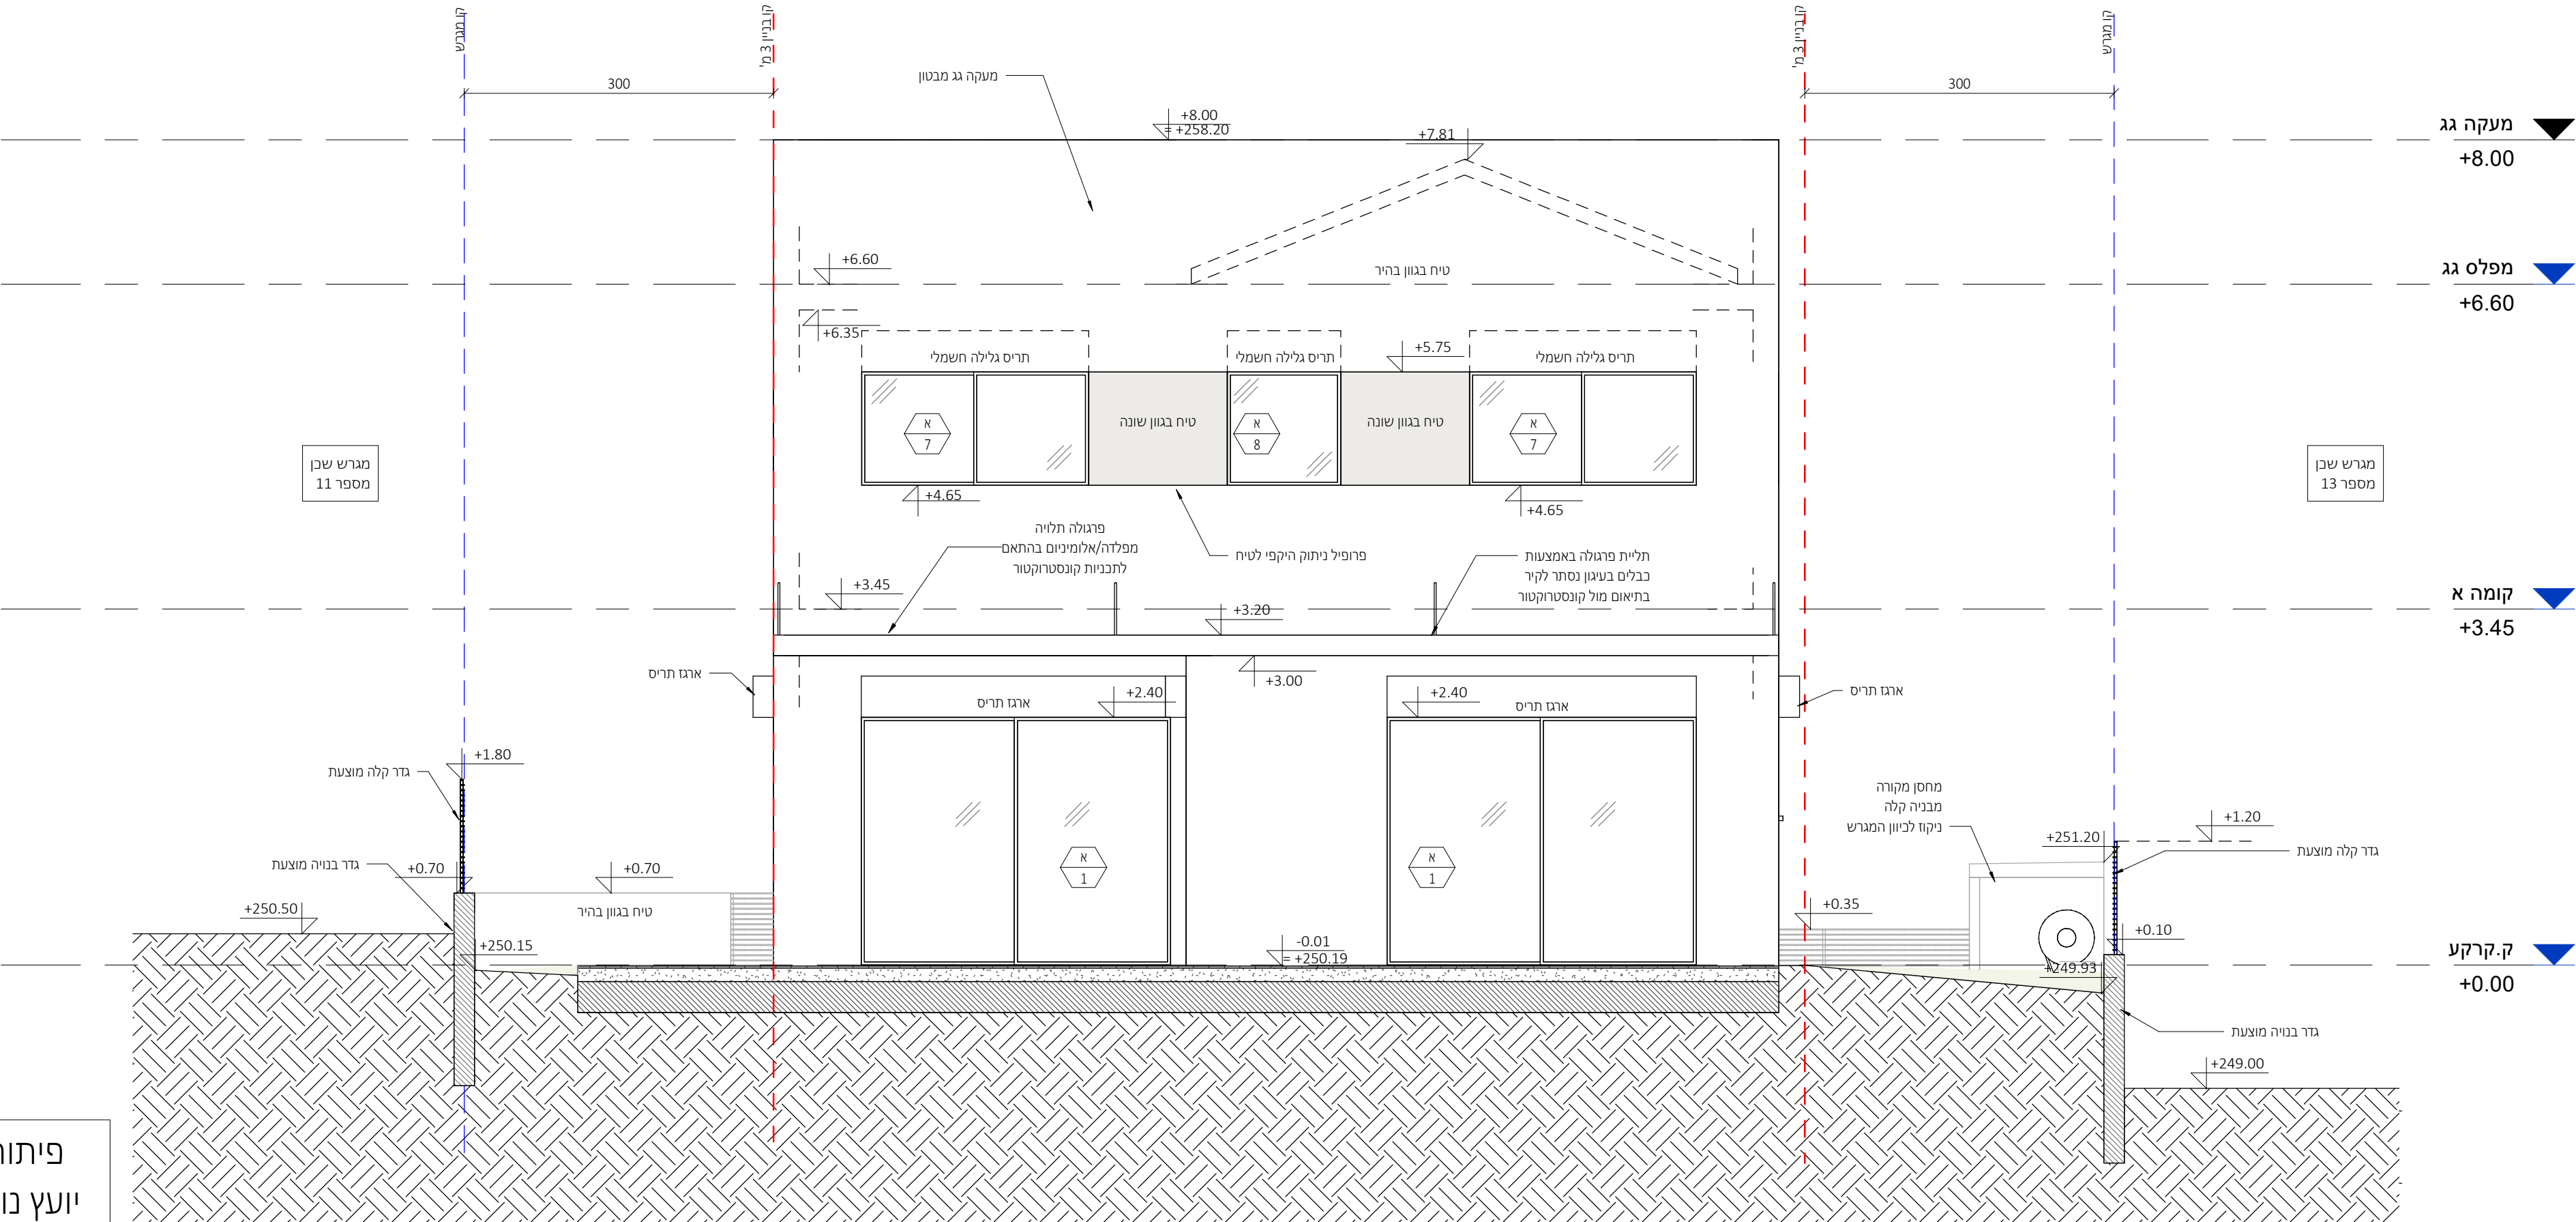

פיתוח נוף עפ"י תוכניות
יועץ נוף ראה פירוט בנפרד

חזית צפונית

1 : 50

פרטי איטום, בידוד וניקוז עפ"י תכניות יועצים ובאחריות הקבלן

מתכונים:


ניהול פרויקט
מהיסוד - בן סולומון
פיקוח
מהיסוד - בן סולומון
קונסטרוקציה
ערן שילר
מיזוג אוויר
אייל ארז מהנדסים ויועצים בע"מ
אינסטלציה
איתן אלמסי
חשמל
איתן בסיס
אלומיניום
נוף
נתי בלוקא
חשמל חכם
חימום תת רצפתי
איטום
צבי טל
אקוסטיקה
מעליות
קרקע וביסוס
דיה הנדסת קרקע וביסוס
רישוי

[illegible]

קוּרָא וְקוּדוּשָׁה

[illegible]


אדריכלות

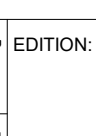PROJECT NAME:		קבוצת רכישה נופיה	
DRAWING NAME:		נופיה - מגרש 15	
SHEET NUMBER:		חזיתות 2	
SCALE:		1 : 50	
TATUS:		למכר	
DATE:		22.09.2025	
EDITION:			
DRAWER:		אלמוג אור	
CHECKER:		דסס עיי	

NeumanHaynerArchitects

office@nh-arch.com
www.nh-arch.com


זכויות ייצור / ע"פ הנחיות עו"ד

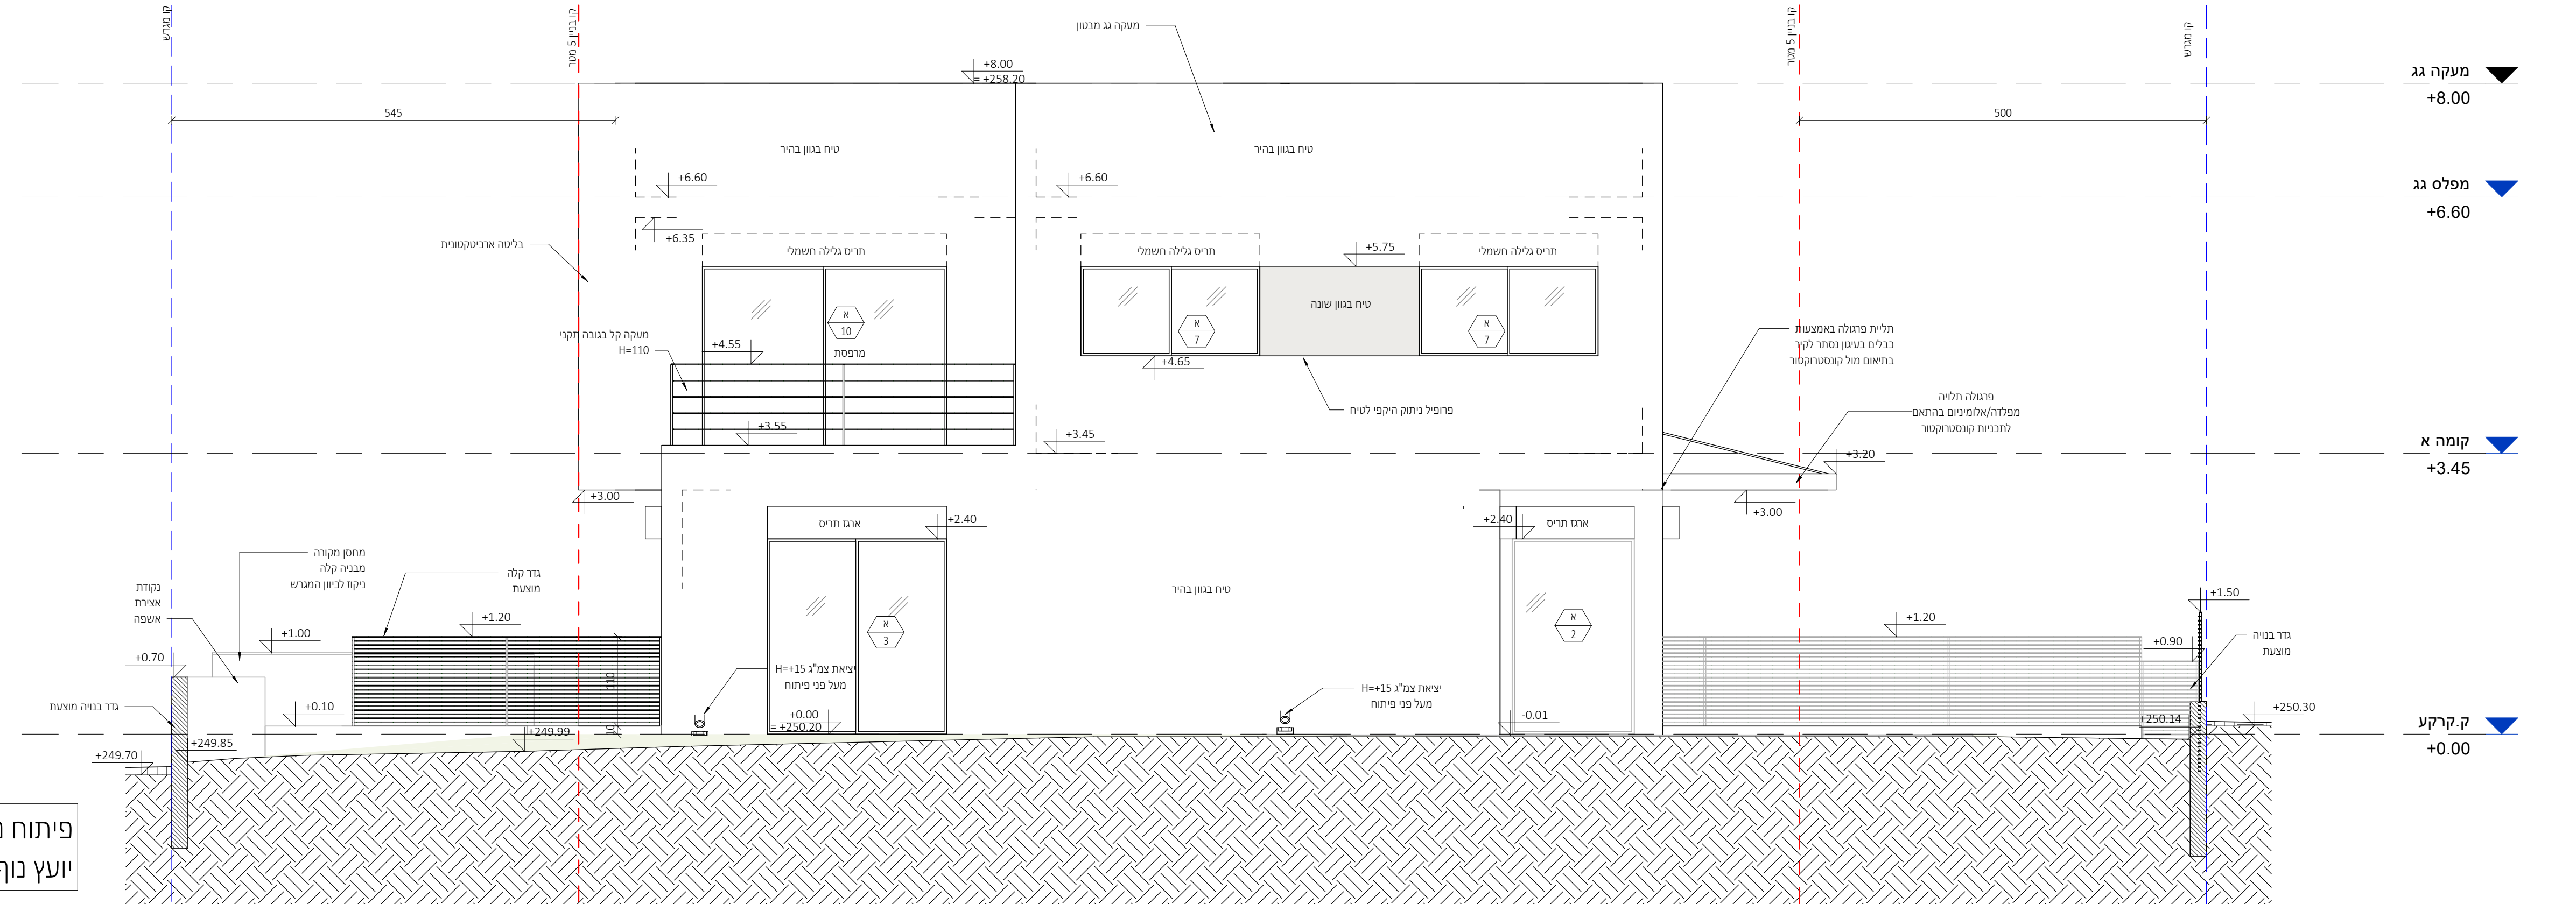

פיתוח נוף עפ"י תוכניות
יועץ נוף ראה פירוט בנפרד

חזית מזרחית

1 : 50

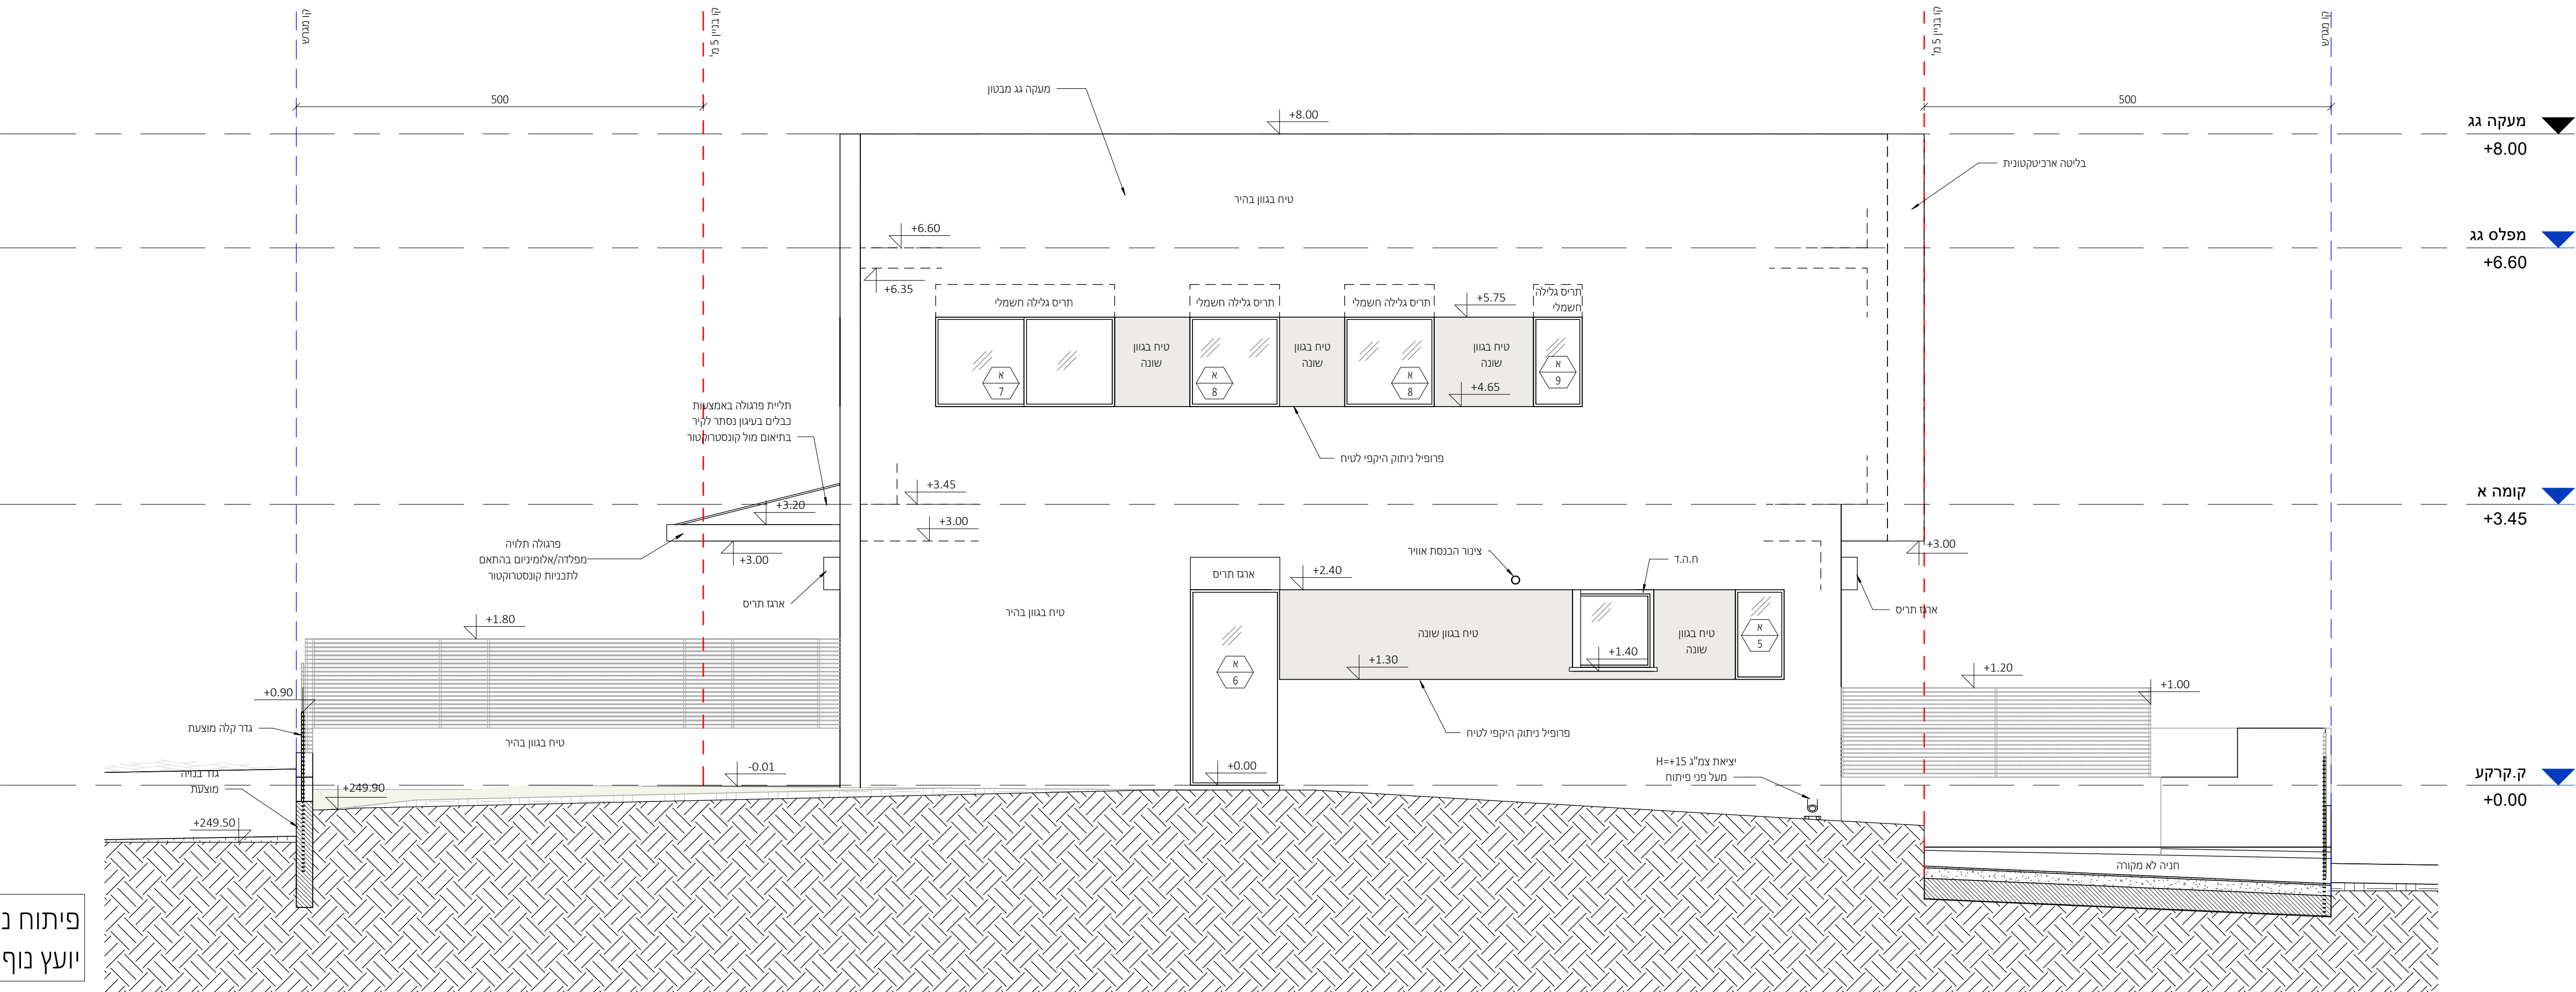

פיתוח נוף עפ"י תוכניות
ועץ נוף ראה פירוט בנפרד

חזית מערבית

1 : 50

פרטי איטום, בידוד וניקוז עפ"י תכניות יועצים ובאחריות הקבלן

מתכונים:

ניהול פרויקט
מהיסוד - בן סולומון
פיקוח
מהיסוד - בן סולומון
קונסטרוקציה
ערן שילר
מיזוג אוויר
אייל ארז מהנדסים ויועצים בע"מ
אינסטלציה
איתן אלמסי
חשמל
איתן בסיס
אלומיניום
נוף
נתי בלוקא
חשמל חכם
חימום תת רצפתי
איטום
צבי טל
אקוסטיקה
מעליות
קרקע וביסוס
דיה הנדסת קרקע וביסוס
רישוי

[illegible]

מקרא קירות:

		
עמוד בסון	קיר בסון	קיר בלוק

[illegible]


אדריכלות

CLIENT NAME:		הפרויקט:	
PROJECT NAME:		הפרויקט:	
קבוצת רכישה נופיה			
נופיה - מגרש 12			
DRAWING NAME:		שם הגליון:	
חתיכים			
SHEET NUMBER:		מספר הגליון:	
A3-3-100			
SCALE:	קנה מידה:	EDITION:	הדורה:
1 : 50			
STATUS:	סטוס:		
למכור			
	נבדק ע"י:	אומדן ע"י:	
DATE:	22.09.2025		אריך:


NeumanHaynerArchitects

וימן חיינר אדריכלים
מורד ההדרים 2, בית חירות
טל 09-9545842

זכויות ייצור / ע"פ הנחיות עו"ד

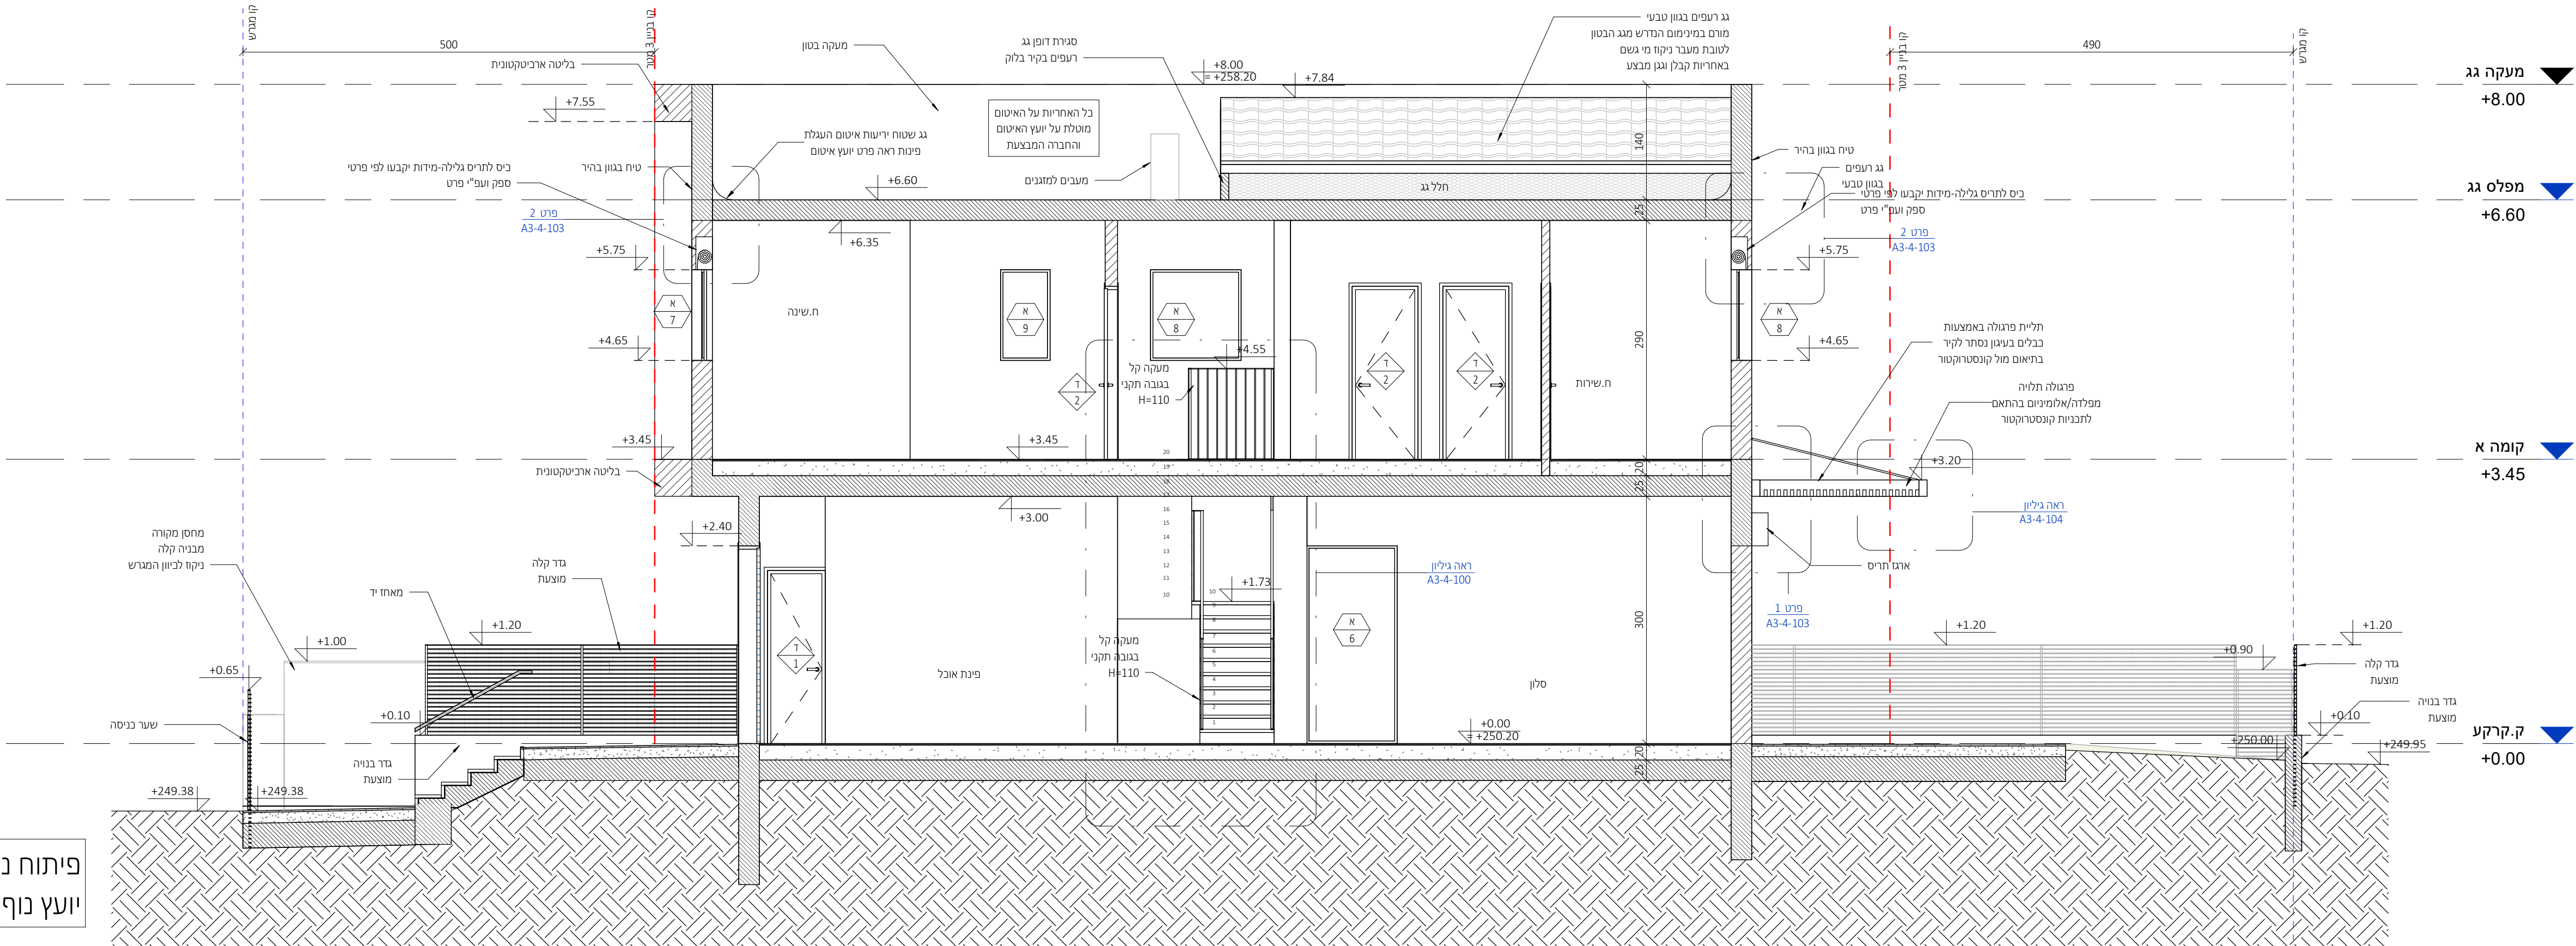

פיתוח נוף עפ"י תוכניות
יועץ נוף ראה פירוט בנפרד

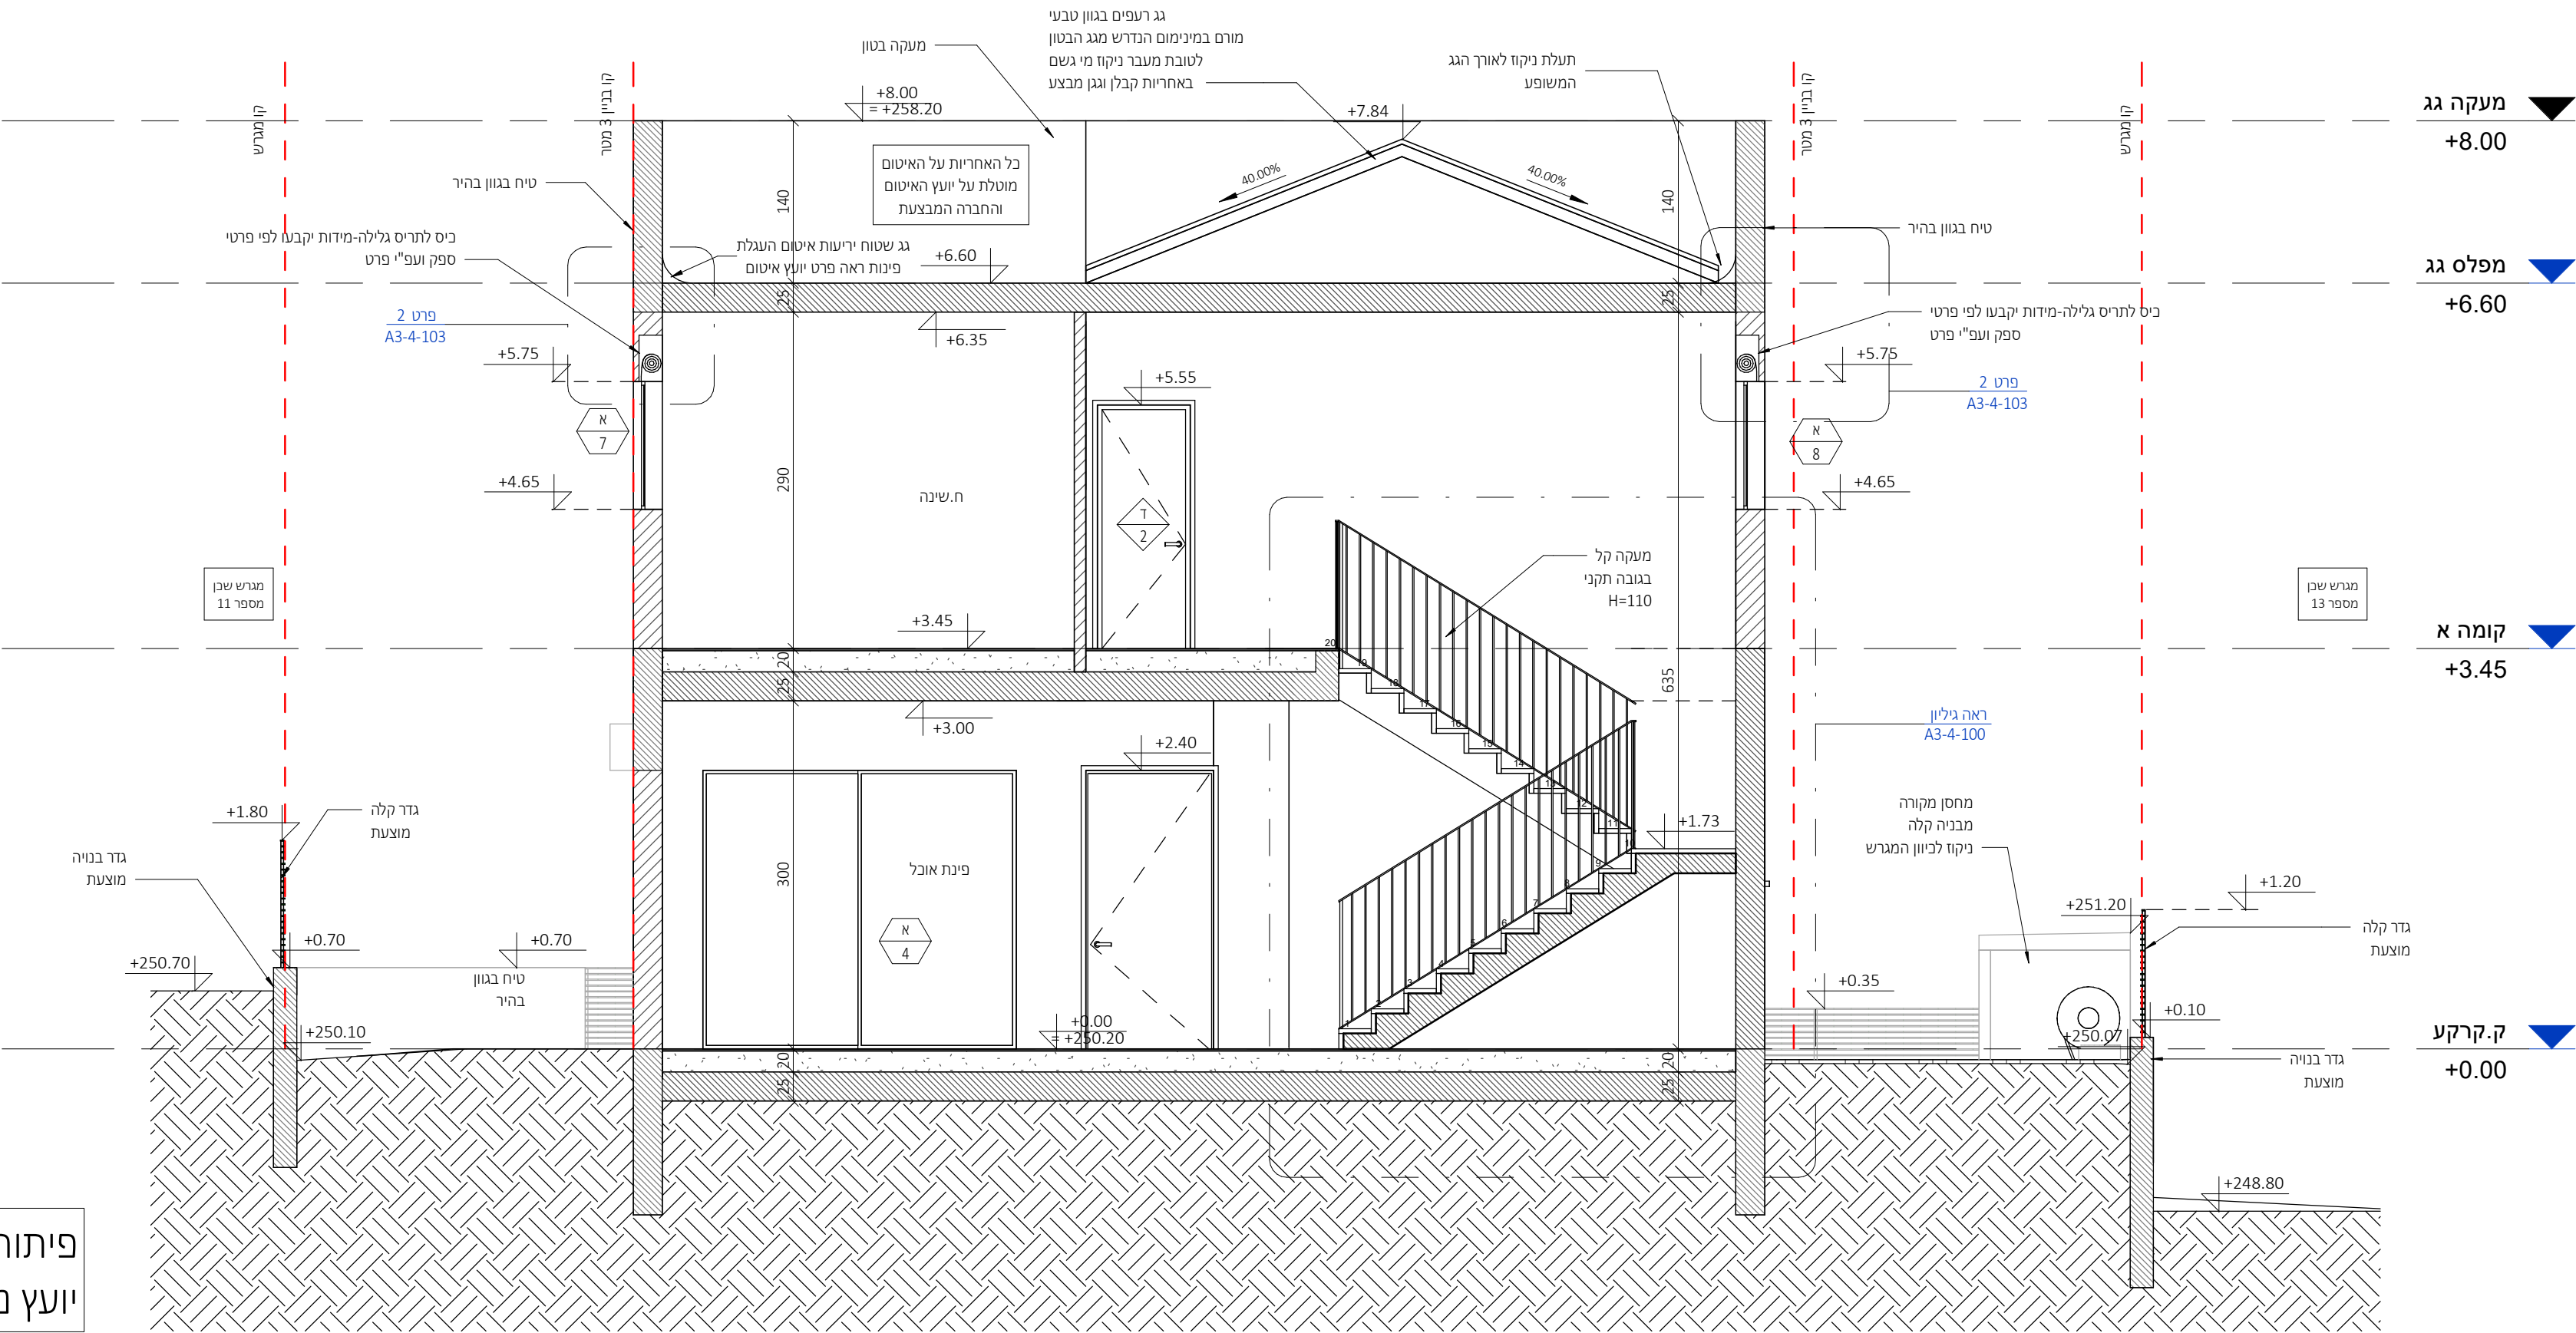


פיתוח נוף עפ"י תוכניות
יועץ נוף ראה פירוט בנפרד


חתך ב-ב

1 : 50


ניהול פרויקט
מהיסוד - בן סולומון
פיקוח
מהיסוד - בן סולומון
קונסטרוקציה
ערן שילר
מיזוג אוויר
אייל ארז מהנדסים ויועצים בע"מ
אינסטלציה
איתן אלמסי
חשמל
איתן בסיס
אלומיניום
בופ
נתי בלוקא
חשמל חכם
חימום תת רצפתי
איטום
צבי טל
אקוסטיקה
מעלות
קרקע וביסוס
דיה הנדסת קרקע וביסוס
רישוי

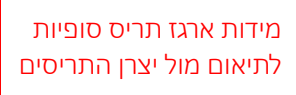

1 : 10


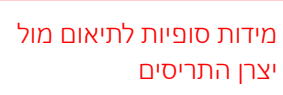


1 : 10

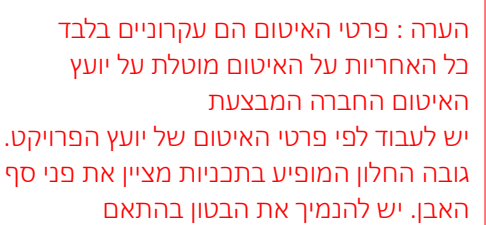

פרט עקרוני בלבד - פרט סופי מספק החלונות

1 : 10

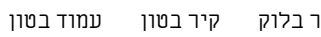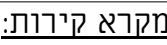

אדריכלות

CLIENT NAME: _____; שם המזמין:

קבוצת רכישה נופיה

PROJECT NAME: _____: שם הפרויקט:

נוסח - מורחב 12

DRAWING NAME: ס הגליון:

פרקים

SHEET NUMBER: 297 גליון:

Λ3-1-103

7/5 / 105

SCALE: קנה מידה: EDITION: הדורה: 

As indicated	

למבחן

דטסט ע"י:	אלמוג אור
נבדק ע"י:	


DATE: 22 09 2025 אר"י:




יומן חיינר אדריכלים
 וורד ההדרים 2, בית חירות
 09-9545842 גל

office@nh-arch.com
 www.nh-arch.com


זכויות ייצור / ע"פ הנחיות עו"ד

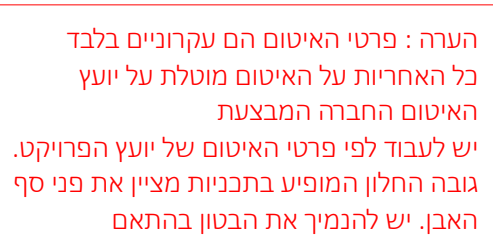

1 : 5

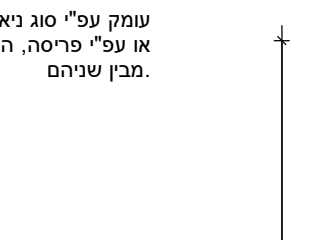

1 : 10

 

1 : 10

פרטי האיטום באחריות יועץ האיטום
ראה חוברת פרטי איטום מצורפת





להמשך תיאום

פרגולת אלומיניום



תמונה להמחשה בלבד

להמשך תיאום

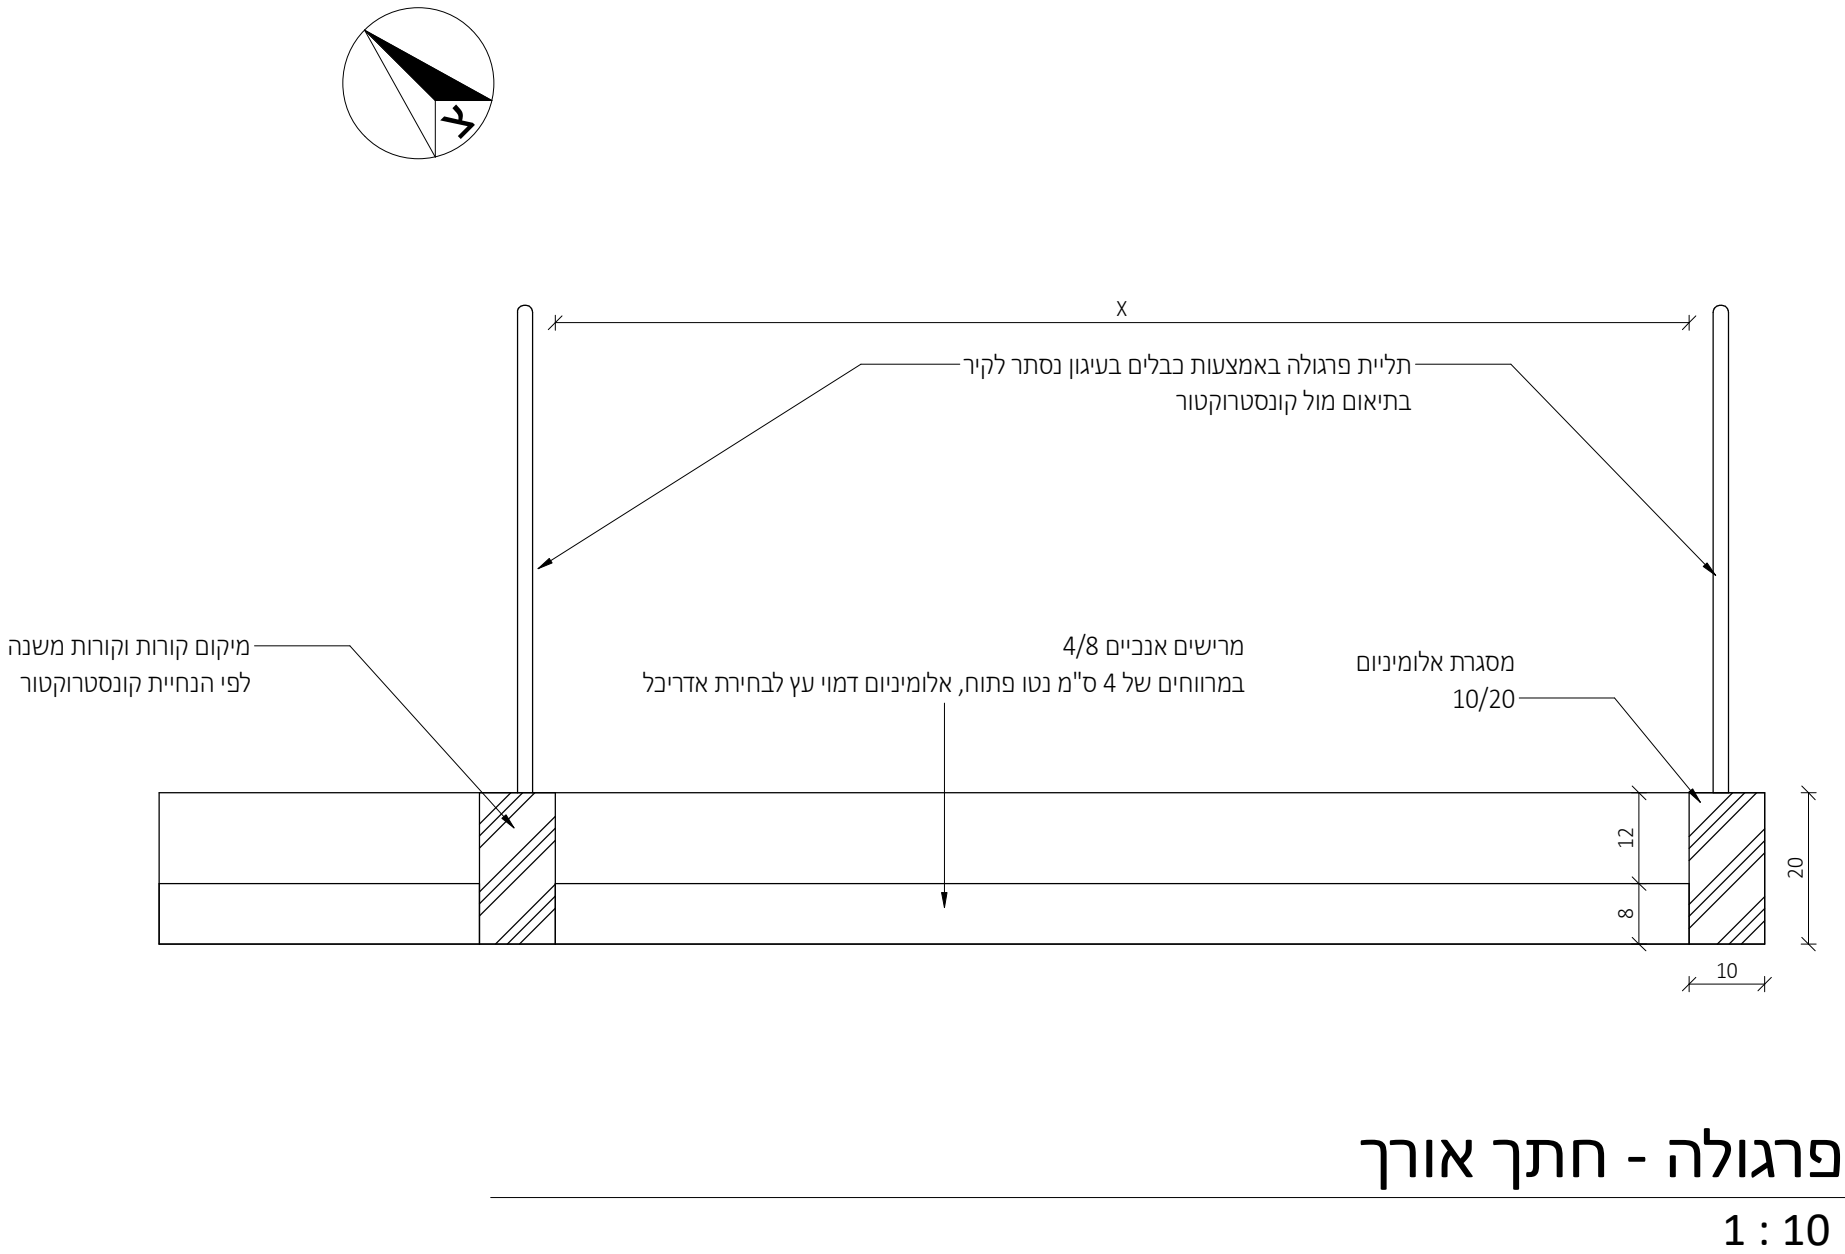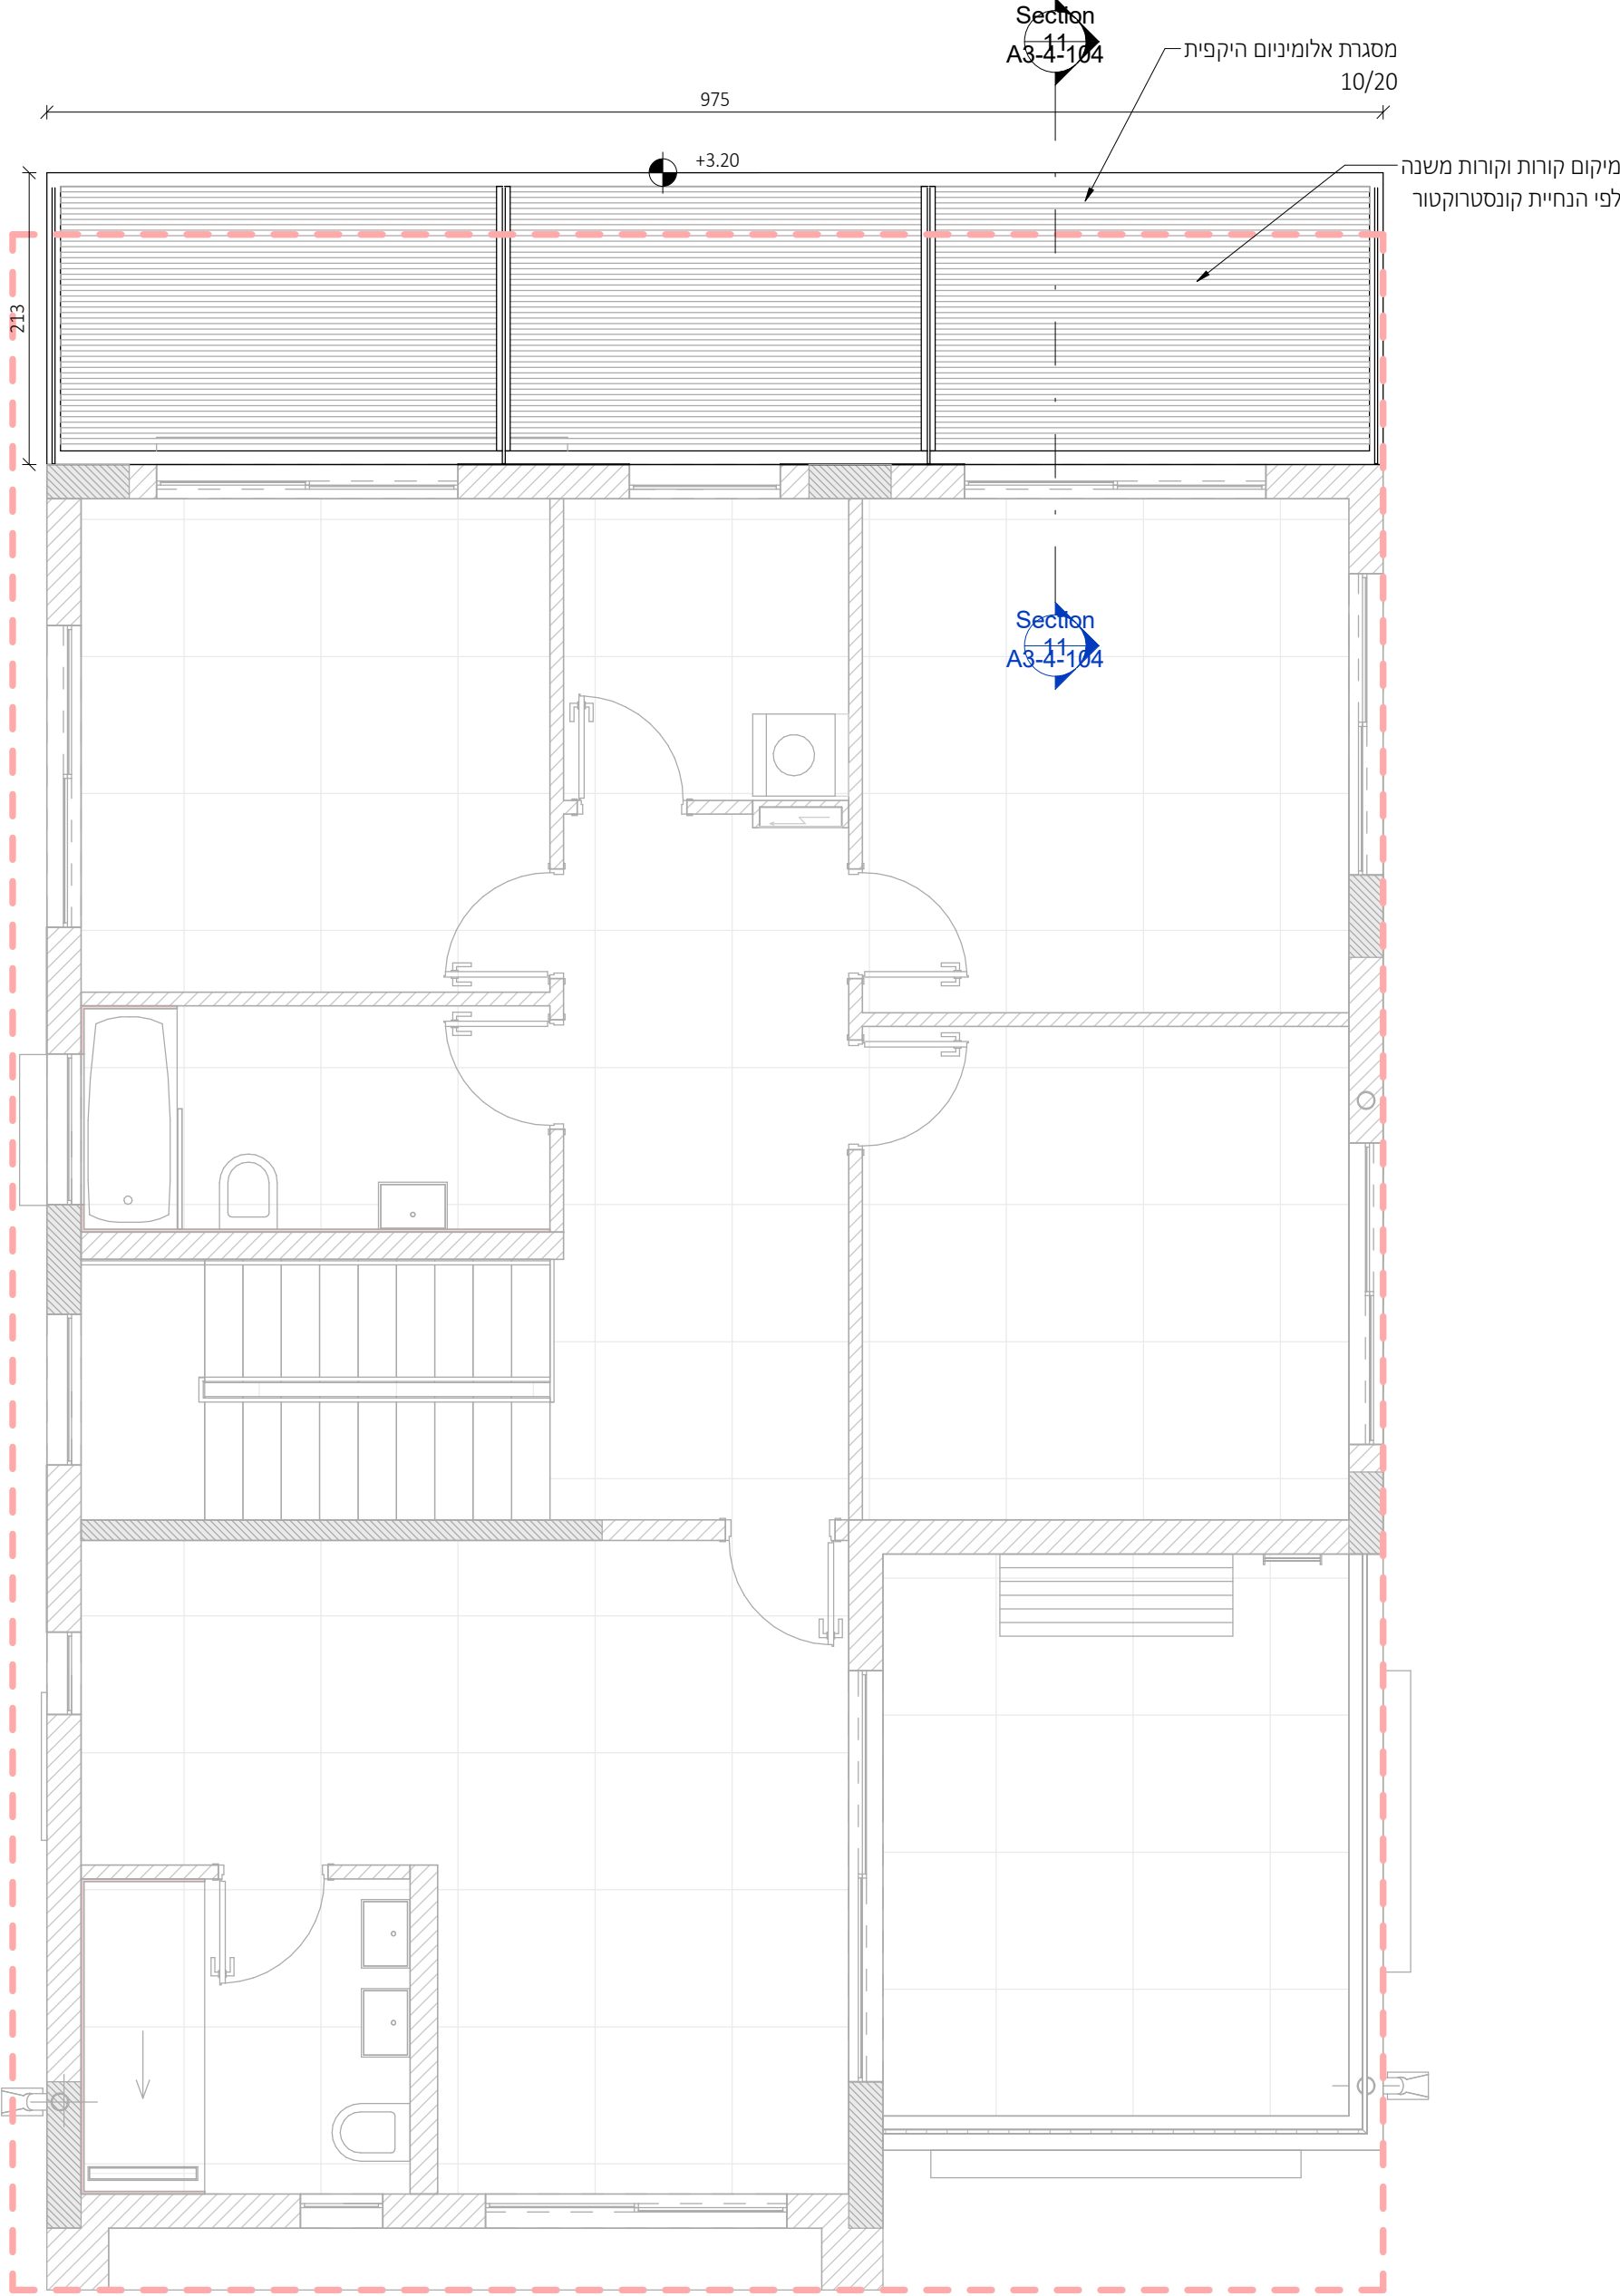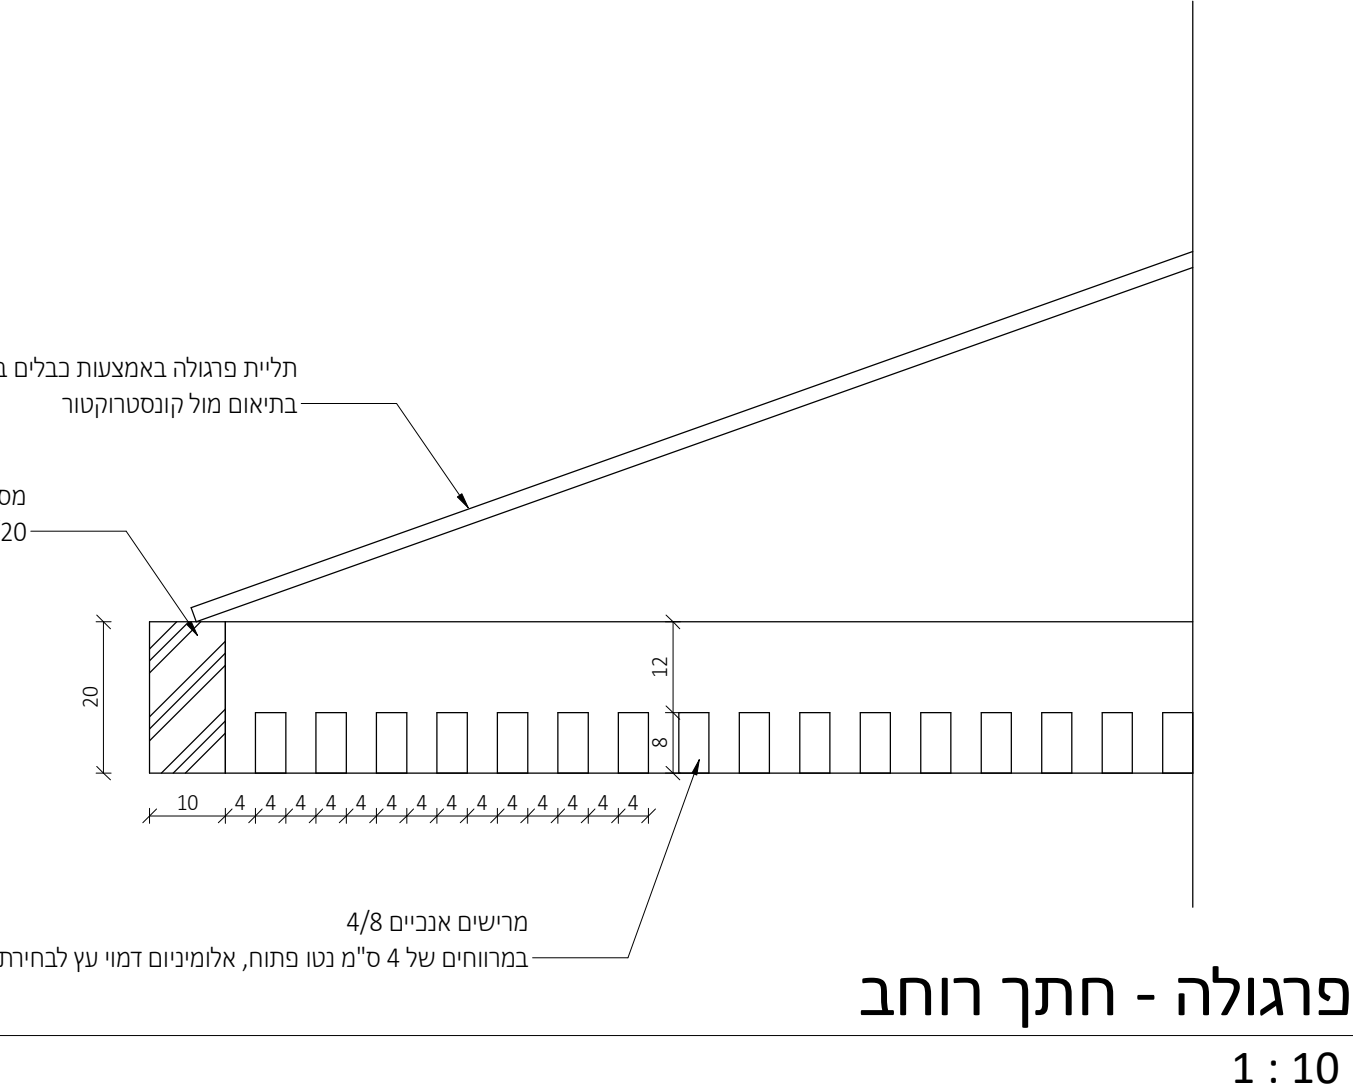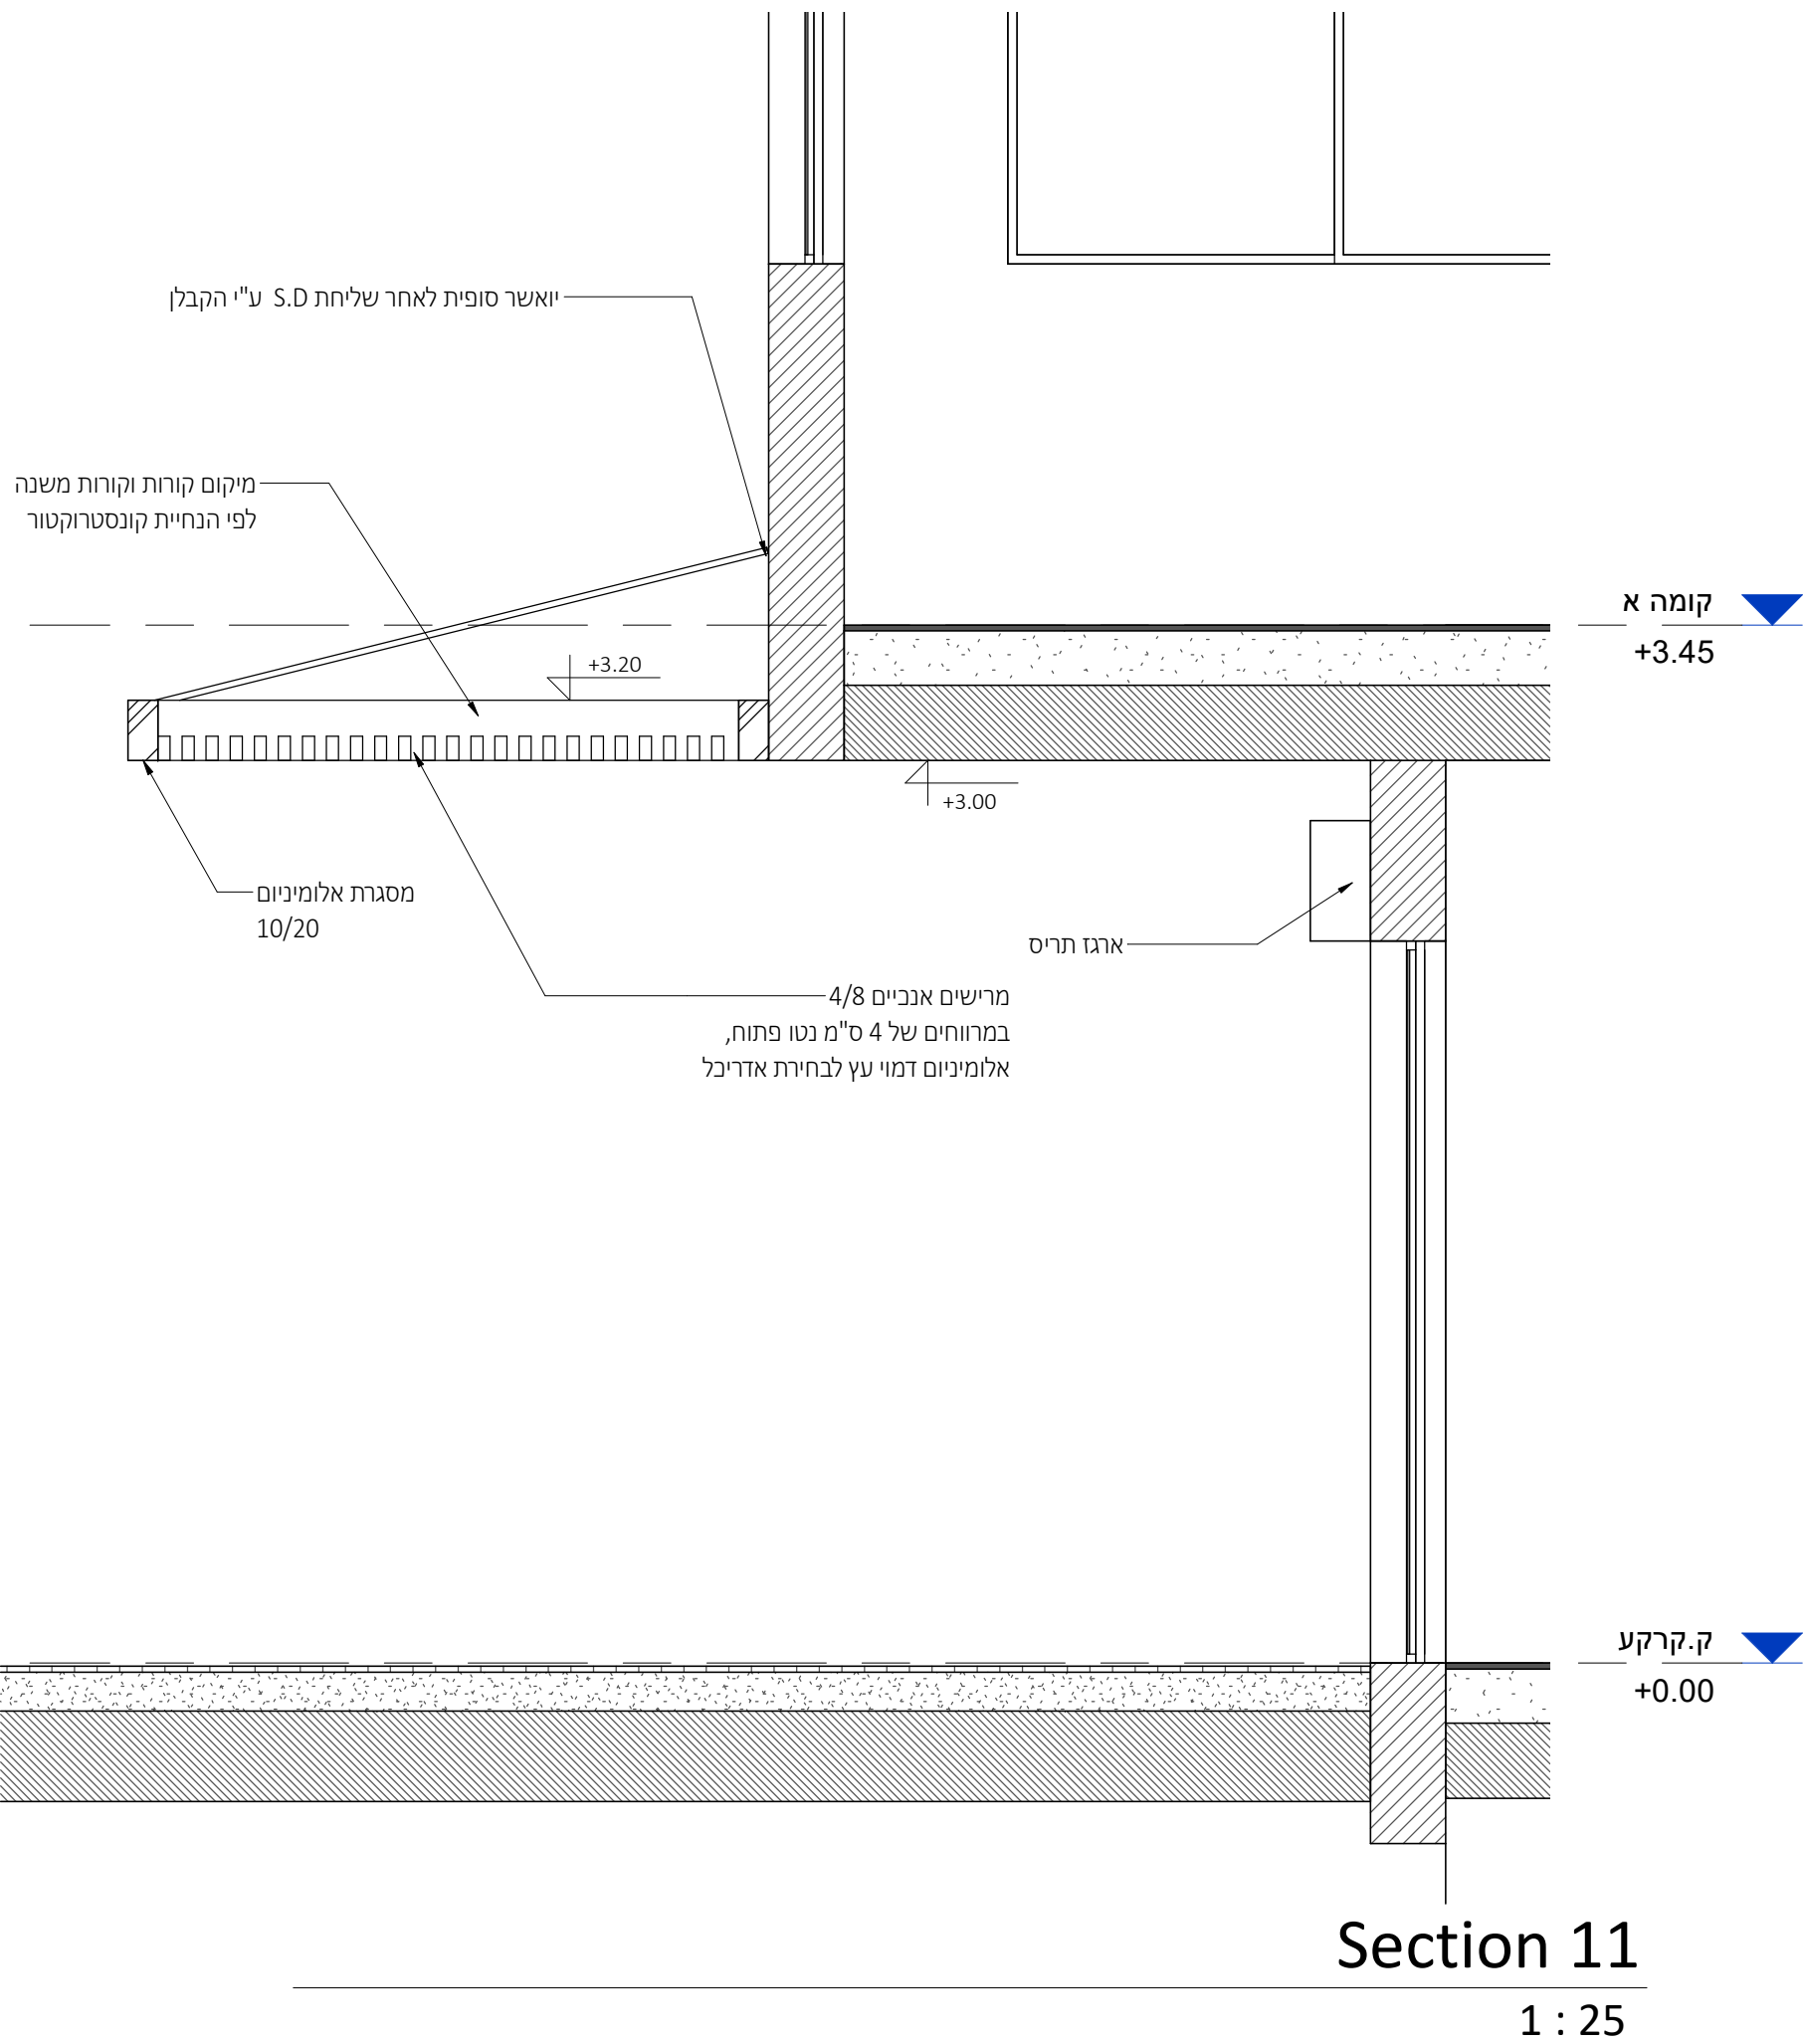

מתכננים:

ניהול פרויקט
מהיסוד - בן סולומון
פיקוח
מהיסוד - בן סולומון
קונסטרוקציה
ערן שילר
מיזוג אוויר
אייל ארז מהנדסים ויועצים בע"מ
אינסטלציה
איתן אלמסי
חשמל
איתן בסיס
אלומיניום
נוף
נתי בלוקא
חשמל חכם
חימום תת רצפתי
איטום
צבי טל
אקוסטיקה
מעליות
קרקע וביסוס
דיה הנדסת קרקע וביסוס
רישוי

± 0.00 = +250.20
הערות: 1. תכנית זו יש לקרוא יחד עם תכנית הרישום. 2. גובה אבטומיניום: ראו תכנית פיתוח. 3. המידות הן בין קירות הבניה ולא כולל פיתוח. 4. פיתוח השטח סביב הבנוה, כולל, מדרגות, נדרות, שנילים, ריצופים, שפופים, גדרים, חניה וכו' ראו תכנית פיתוח. 5. איסוס קירות והצפת הבנוה כמתנ עם הקרקע ובנידוד תחסי לאורר העמודים והקורות וכל המפרט. כלירות או עם סימני (גטון)- ראו תכנית קונסטרוקציה. 6. אף דים יבוצע בכל מישור אופקי הכולס מתגבר. 7. פיתוח תחסי בממיד- ע"פ מפרט התומקיר, מאשרר ט"י פיקוד העורף. המבצע אחראי למידות : עליו לבקר ולבדוק את כל המידות בתכנית ובמקום המבנוה. במקרה של שטות או אי התאמה בתכנית /או בבנוי, עליו להודיע על כך מיד לאדריכל בסדס המשך המבנוה. המבצע יישמש או ויק בתכנית שמשורר לכניסוע. המבצע יחזיק באחר, כלל שט, של מנדכו של תכנית. את לקבוע מידות על ידי מדידה בשטח. התכנית הנה רכוש האדריכל ואין לשנות כל שימוש בה או ברעיונות הגלומים בה, אלא באישור בכתב מהאדריכל. מחדס /או יושע אשר שמו רשום בתכנית זו, נושא לכיד באחריות המקצועית והתקנית לתכנית. על המפסח והשכלן לודא התאמת התכנית האדריכלית "לכניסוע" לתכנית ויתר, המכר והתכנית המאושרות ע"י כל גורמים הרשמיים. התכנית כוללת את כל האמצעים והדוג עד ליום חתימת.

משרד קירות:
קיר בלוק
קיר בסון
מנדכו בסון

תאריך	22.09.2025
תאור	מכר
מהדורה	1

אדריכלות	
CLIENT NAME:	שם המסמך:
קבוצת רכישה נופיה	
PROJECT NAME:	שם הפרויקט:
נופיה - מגרש 12	
DRAWING NAME:	שם הגליון:
פרטי פרגולה	
SHEET NUMBER:	מספר גליון:
A3-4-104	
SCALE:	קנה מידה:
As indicated	
TATUS:	סטוס
למכר	
נבדק ע"י:	
EDITION:	מהדורה:
	1
אלמוג אור	סטוס ע"י:
22.09.2025	תאריך:

FILE NAME: -----כלל הפרויקטים להיתר\12\00 תכנית\nofia