

מס'	שנויים	תאריך
1	עדכון חכנית	8.8.24
2	עדכון חכנית	5.11.24
3	עדכון חכנית	10.12.24
4	עדכון חכנית	23.12.24
5	עדכון חכנית לפי שנויי דירים	15.5.25

- הערות:
 - מיקום סופי לנקודות תאורה
 - יקבעו ע"פ תכנית עיצוב פנים
 - תאורת חץ- ע"פ ענף פיתוח
 - במידה והוחלט בעל הבעה לבית חכם:
 - בהכנה לבית חכם ולדעת חכמה יש להאדיר
 - חוט 0 כחול נוסף בכל מסגרת הדריכה
 - להכנתו בענף עשהש"כ מסק פנ"ב חכם
 - הבעה למיזוג אדיר, קירוםם חת צרפתי,
 - מערכת אבטחה, וחיטום מיס בחשמל
 - יזיר עז הנחיות יועץ לכל תחזוקה
- יש לקרוא תכנית זו יחד עם תכנית אדריכלות
- נמסרים בקופסא אדריכלות

א. בסיס
הנדסת חשמל בע"מ

משרד: יד חרוזים 16, ירושלים 93420
טל': 074-7021015 נייד: 050-6550484
פקס: 077-5131015 דוא"ל: office@ebasis.co.il



שם העיון: תוכנית חשמל טיפוסית לאישור

לגבהים של הדלקות,
ה ותריסים:


[illegible]

- * כל הגברים בתכנית הינם למרכז אביר
אלא אם ציין במפורש אחרת
- * מיקום סופי לנקודות תאורה
ייקבע ע"פ תכנית עיצוב פנים
תאורת חוץ – ע"פ יועץ פיתוח
- * מיקום סופי לשקעי מיזוג
ע"פ תוכנית יועץ מיזוג

גבול מוגרש

קומה א'

מעקה גג בנוי
בגובה תקני

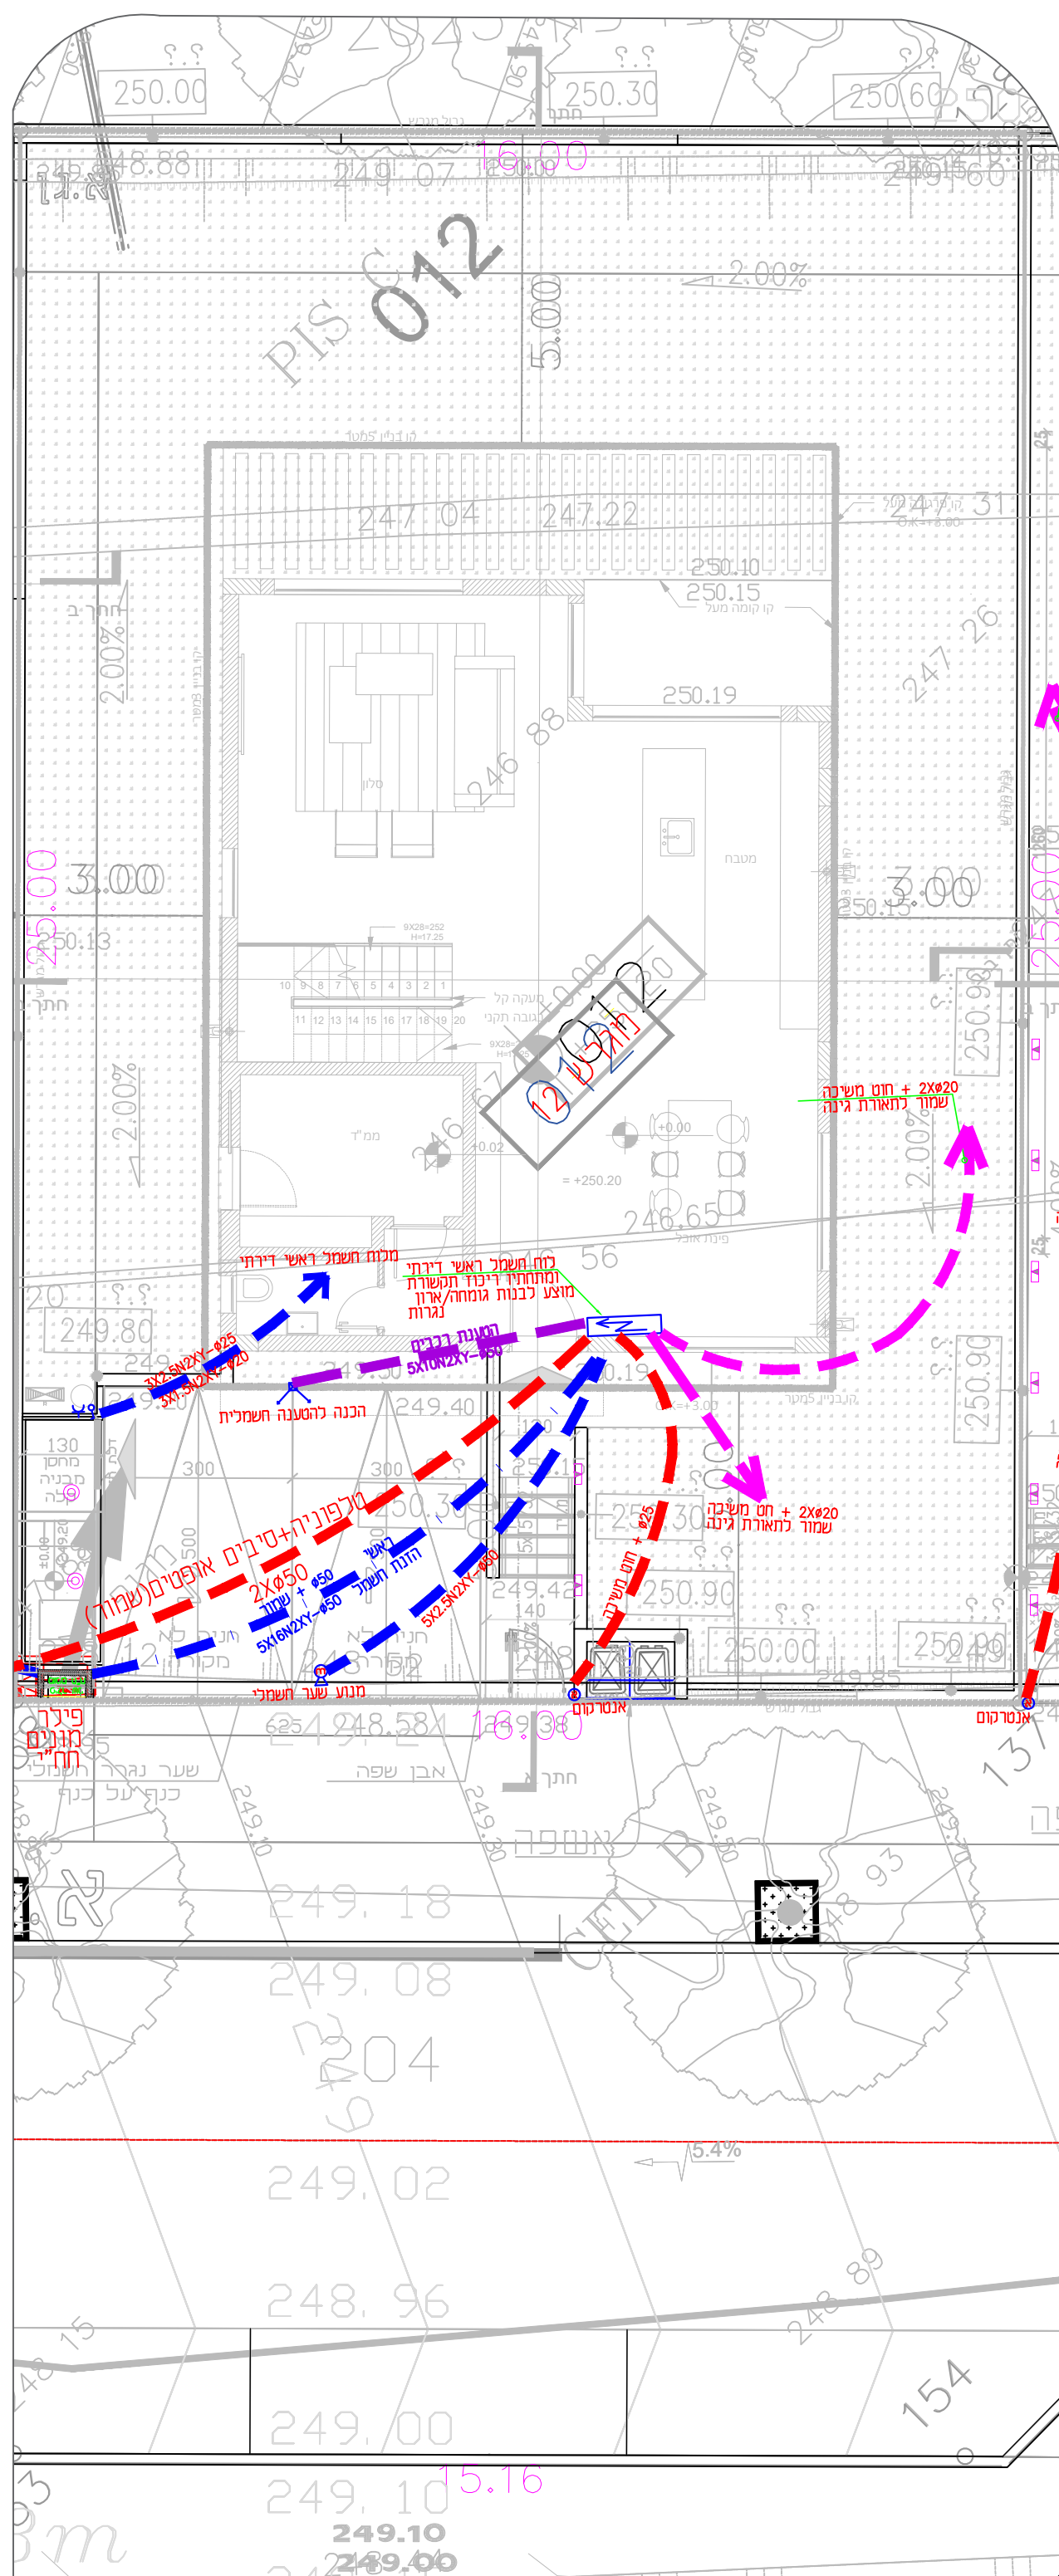

תכנית פיתוח-מגרש 12
קנ"ח 1:100

[illegible][illegible]

עודכן ע"י: _____ רחל

א. בסיס
הנדסת חשמל בע"מ
משרד: יד חוזקים 16, ירושלים 93420
טל': 074-7021015 נייד: 050-6550484
פקס: 077-5131015 ר"ת: office@ebasis.co.il

שם הפרויקט:

נופיה-אלפי מנשה

שם הגיליון:

תוכנית פיתוח מגרש 12

○ ● ○ ○ כביצוץ למכרז לאישור לעיון				קנה מידה: 1:100	
File: מס' קובץ: 675P.dwg		Date: תאריך: 17.06.2024			
אישור: איתן		שרטט: אילה		תכנן: איתן	
מס' הפרויקט: 675		מס' הגליון: P12		מס' עדכון: 0	