


פתחי גישה אופן ארט בתיאום סופי מול אדריכל
כלל יחידות המיזוג אשר נמצאות בתוך נגרות יש לתאם סופית מול אדריכל ונגרות

Court 12
1st Floor


Option **No1**
VRF duct unit in living room
and wall mounted in rooms

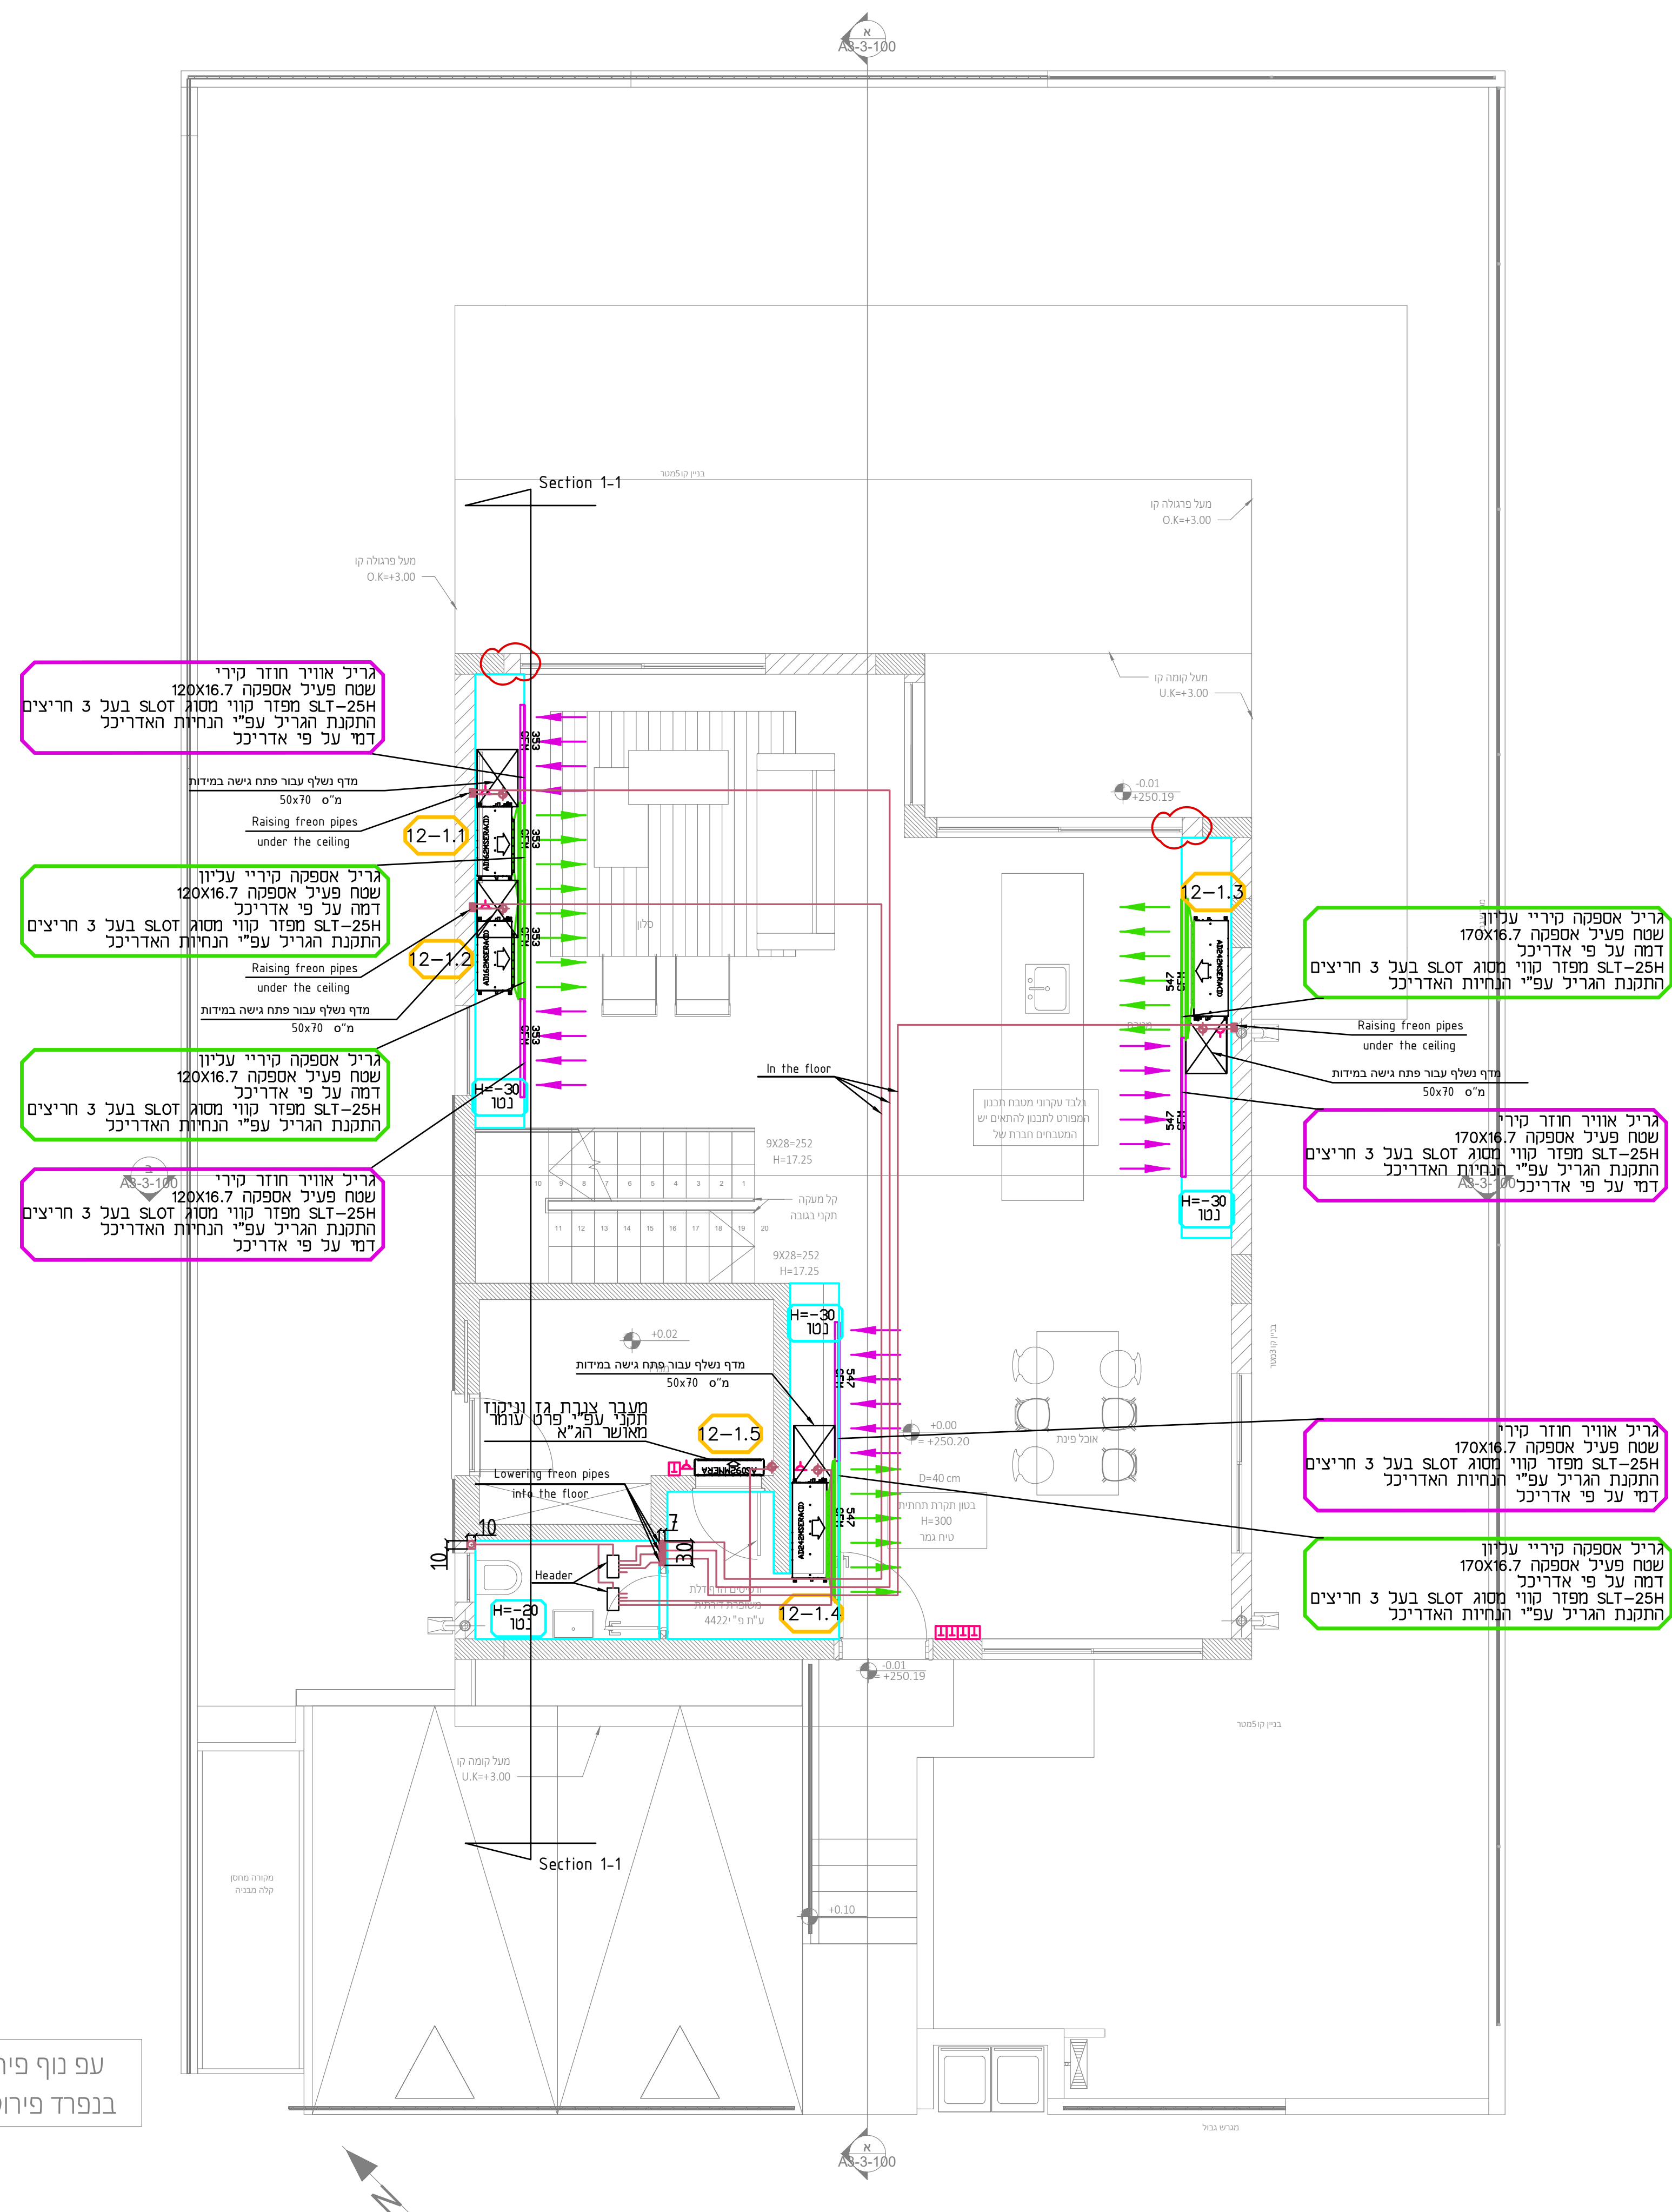

עפּ נאָך פֿיטאָח"תּוּכניוֹת י
בנפֿרד פֿירוט ראה נאָך יועץ

Court 12
2nd Floor

Option **No1**
VRF duct unit in living room
and wall mounted in rooms

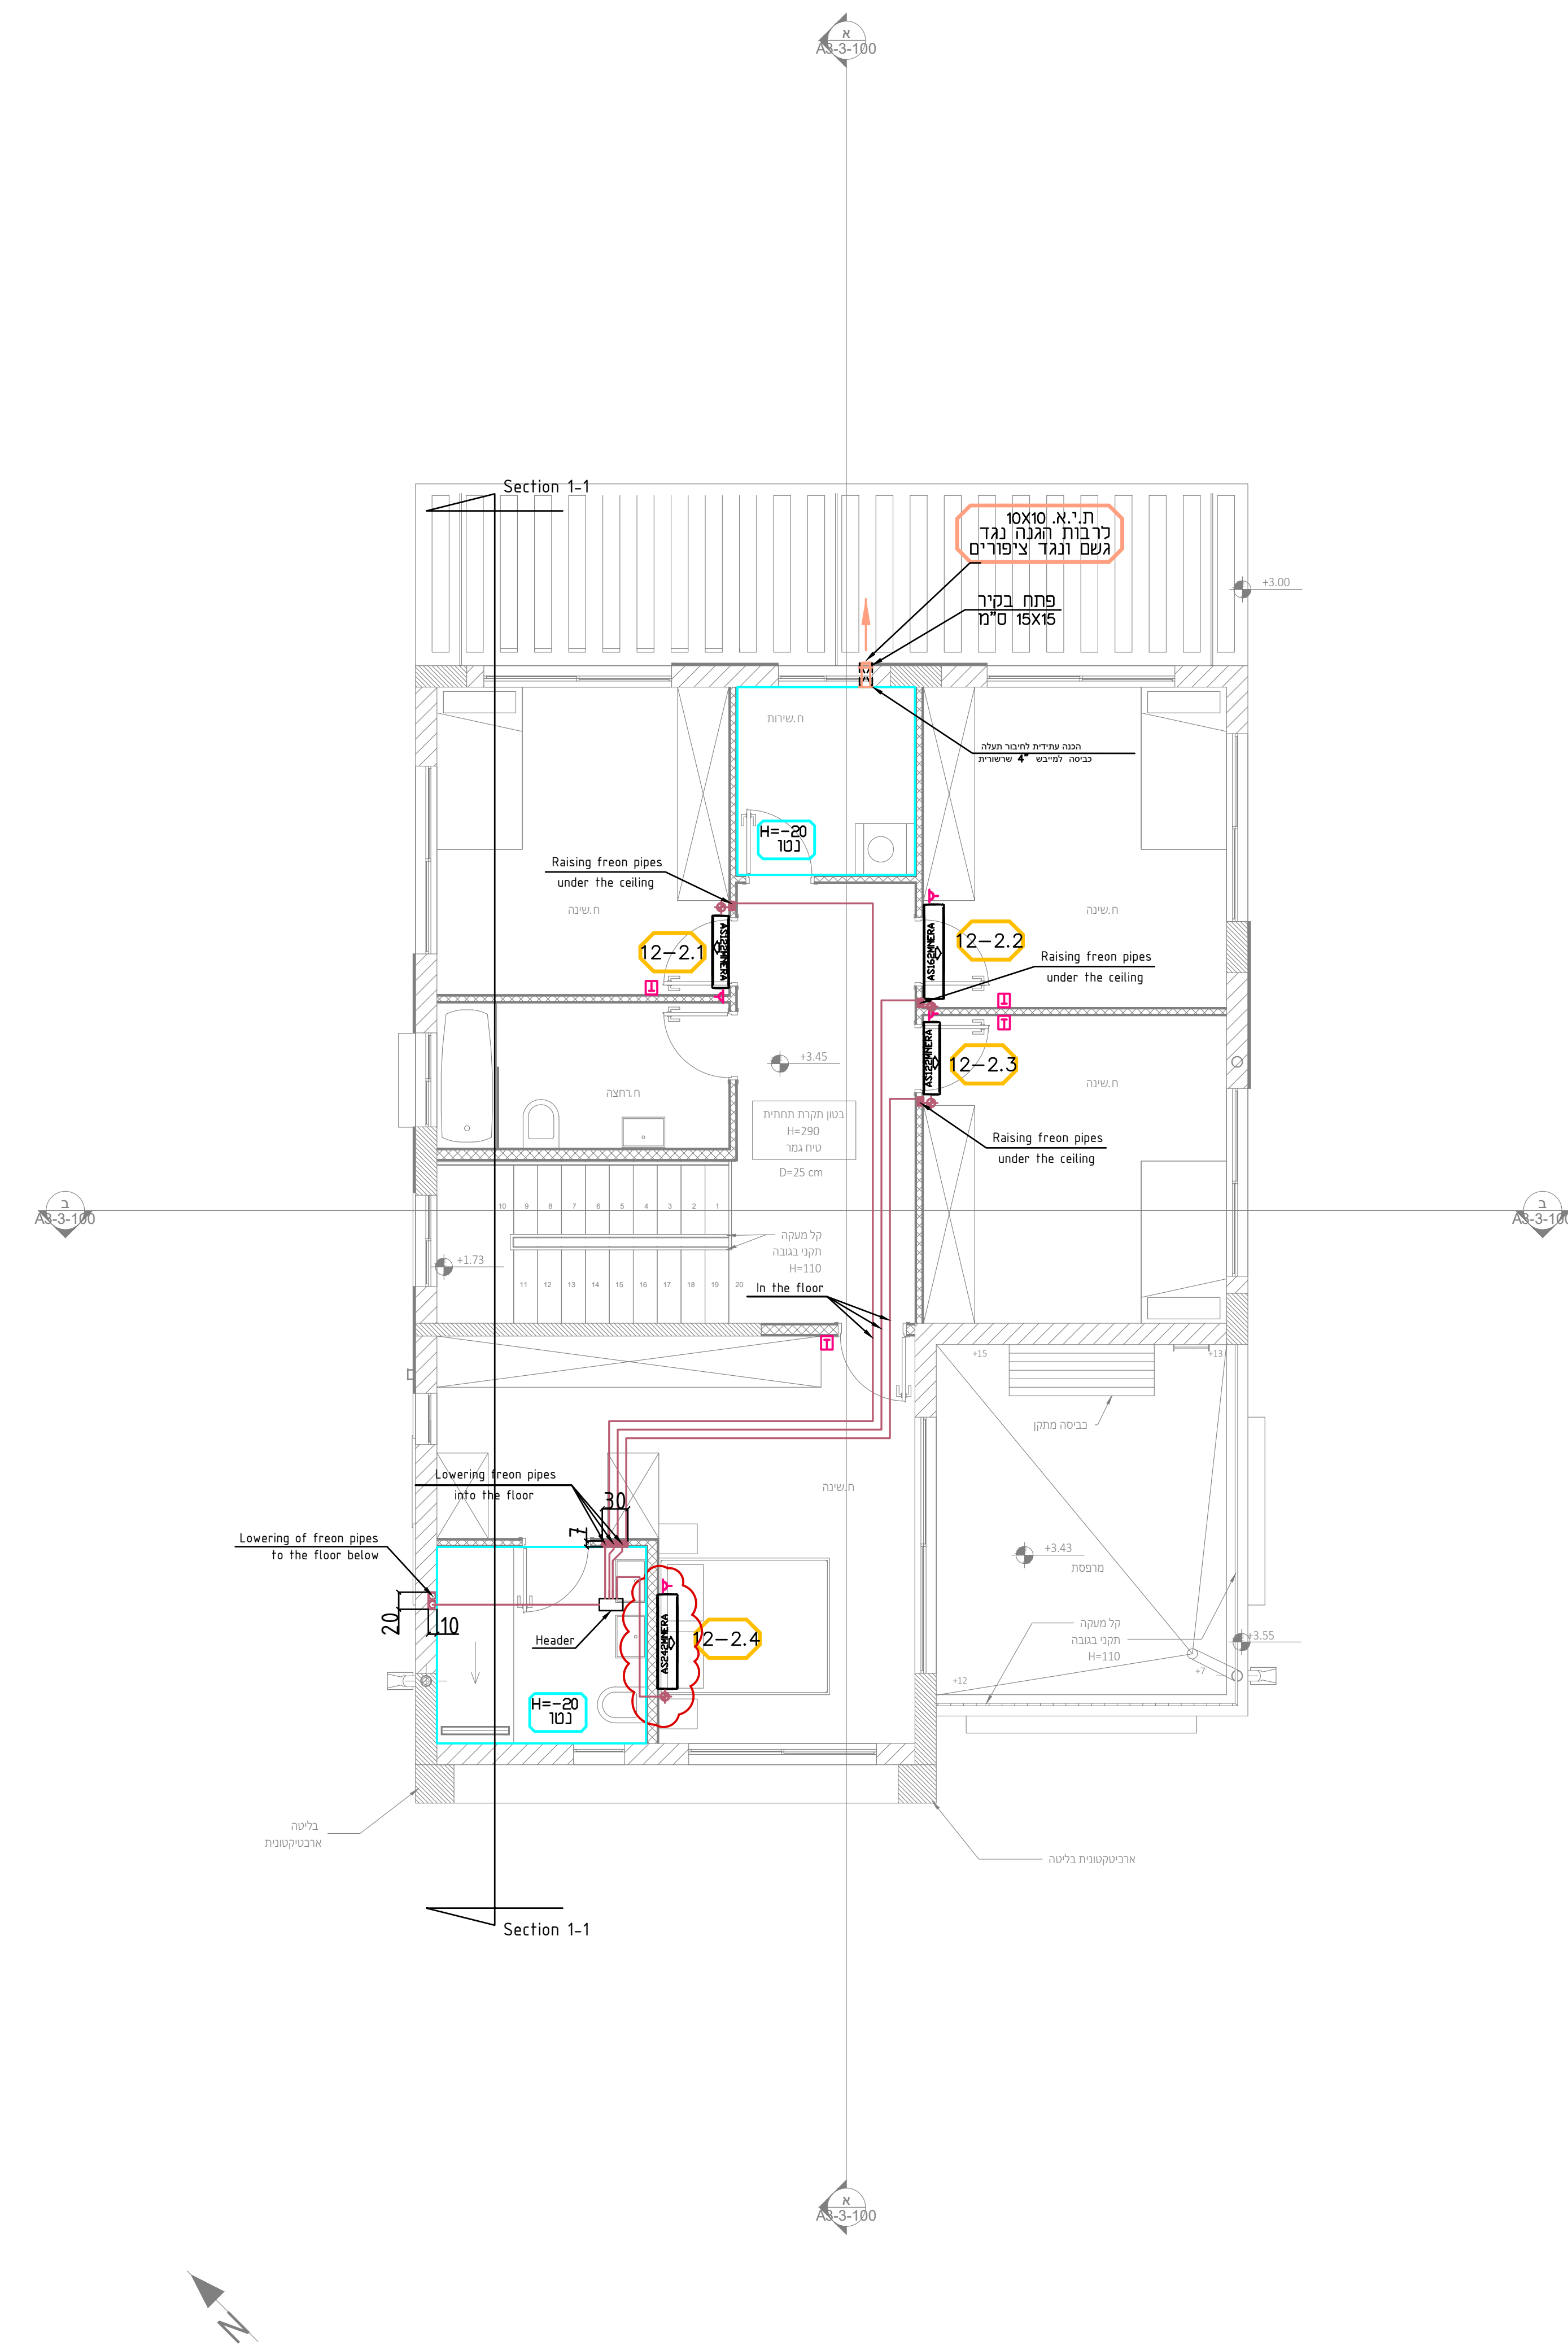

תפוצה

אדריכל	פנים
אונטסציה	
בסחות אש	
אונטסציה	
חשד ותאורה	
קונסטרוקציה	
קבץ ראש	
ניהול פרויקט	
קמח	
אדריכל	

מהדורה

			⚠
			⚠
חנניות לאישור	31.03.2025		⚠
חנניות לעיון	11.03.2025		⚠
שניים:	חאריד:	סל:	

המבצע אחראי למידות ולהתאמתן למציאות בכל מקרה של אי התאמה, סתירה או טעות עליו להודיע למתכנן לפני התקדמותו בביצועו. אין לקבוע מידות על סמך מדידה בשרטוט. אין לרעוּש כל שימוש בתוכנית זו או ברעיונות הגלומים בה ללא אישור בכתב מאת המתכנן.

הערות

1. כל התעלות מחוץ למבנה יבודרו
בירודו אוקסוס פמ"ב 2"
מידות התעלות הן מידות פח
2. תעלות מזוג בחור המבנה יבודרו
בבירודו אוקסוס פמ"ב 1"
מידות התעלות הן מידות פח
3. תעלות אוויר צה יבודרו
בבירודו פמ"ב 1"
מידות התעלות הן מידות פח
4. יש לאסוס במסילקון את פינות החיבור
של תעלות מידות אוויר לפני כיפוף
הפחים המתחברים

מקרא

- פנ- מנחם**
 מ.א.ה. – מפדו אוויר קריר
 מ.א.ה. – מפדו אוויר חמרי
 מ.א.ה. – מפדו אוויר חרד
 מ.א.ה. – תריס אוויר חרד
 ב.א. – בידוד אוקוסט
 ב.ט. – בידוד טרמי
 ב.ט. – נלא בידוד
 ד.א. – דמפר אש
 סרמטסט דוח הפעלה


 שבע חמשל כספול יוענ חשמשל
 שבע תרת פאיז כספול יוענ חשמשל
 פסקס בחור ד פאיז כספול יוענ חשמשל
 חמשל כספול תרת פאיז כספול יוענ חשמשל
 יקונד יאמיר כספול יוענ חשמשל
 גובא 28 ס"מ תחתינית גובה המאיר
 שכל הפעלה ארכיטסי

מקרא צבעים בתכנית

- | | |
|--------------------------|---|
| תעלות ותריסי אוויר חוזר |  |
| תעלות ותריסי אספקת אוויר |  |
| תעלות ותריסי אוויר צח |  |
| תעלות ותריסי יניקת אוויר |  |
| תעלות ותריסי שיחרור עשן |  |
| צנרת גז וחשמל |  |
| סימון מעגלי מזוג אוויר |  |

191	מבני מקדשים צמודי קרקע נזיפה אפיקי מנשה נמרש 12
מז פרינס	ספ פרינס
1:50	מיזוג אוויר ואיוורור
מז	קומה ראשונה ושנייה
31.03.2025	ספ העריכה
תאריך סגירת	
2	
תאריך	ספ העריכה
☐ ברעוץ ☐ מכרז ☒ מאשר ☐ תעון	
	תאריך: 11.03.2025
	הנכח הרשום: אילן אידן

Option **No1**

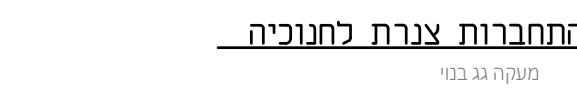

מיקום סופי של הניקוזים
ייקבע בשטח בתאום עם האדריכל
יועץ אינסטלציה וקבלן מיזוג אוויר

- מהדורה

המבצע אחראי למידות ולהתאמתן למציאות

הערות

מחוצ למבנה
מי רעורני?"

- מקרא

אוויר קירי

תעלות ותריסי אוויר חוזר

