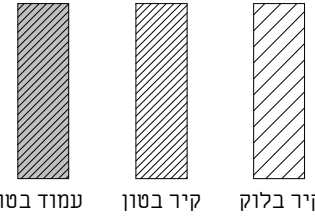


מתכונים:

ניהול פרויקט
מהיסוד בן שלומון
פיקוח
מהיסוד - בן שלומון
קונסטרוקציה
ערן שילר
מיזוג אוויר
אייל ארז מהנדסים ויועצים בע"מ
אינסטלציה
איתן אלמסי
חשמל
איתן בסיס
אלומיניום
נוף
נתי בלוקא
חשמל חכם
חימום תת רצפתי
איטום
צבי טל
אקוסטיקה
מעליות
קרקע וביסוס
דיה הנדסת קרקע וביסוס
רישוי

[illegible]

מקרא קירות:

[illegible]

אדריכלות

קבוצת רכישה נופיה		שם הפרויקט:	
PROJECT NAME:		שם הפרויקט:	
נופיה - מגרש 13		שם הגליון:	
DRAWING NAME:		שם הגליון:	
גליון שער		שם הפרויקט:	
SHEET NUMBER:		שם הפרויקט:	
A3-1-099		שם הפרויקט:	
SCALE:		EDITION:	
סטוס:		הצורה:	
למכור			
נבדק ע"י:		הצורה:	
DATE:		22.09.2025	




NeumanHaynerArchitects

וימן חיינר אדריכלים
מורד ההדרים 2, בית חירות
טל' 09-9545842

זכויות ייצור / ע"פ הנחיות עו"ד

נופיה - מגרש 13			
מס' גיליון	שם גיליון	מהדורה	תאריך הפצת מהדורה
A3-1-099	גיליון שער	1	22.09.2025
A3-1-100	תכנית קומת מרתף	2	17.12.2025
A3-1-101	תכנית קומת קרקע	1	22.09.2025
A3-1-102	תכנית קומה א	1	22.09.2025
A3-1-103	תכנית גג	1	22.09.2025
A3-2-200	חזיתות 1	1	22.09.2025
A3-2-201	חזיתות 2	1	22.09.2025
A3-3-100	חתכים	1	22.09.2025
A3-4-100	גליון מדרגות	1	22.09.2025
A3-4-103	פרטים	1	22.09.2025
A3-4-104	פרטי פרגולה	1	22.09.2025
A3-6-1000	רשימת פתחים	1	22.09.2025

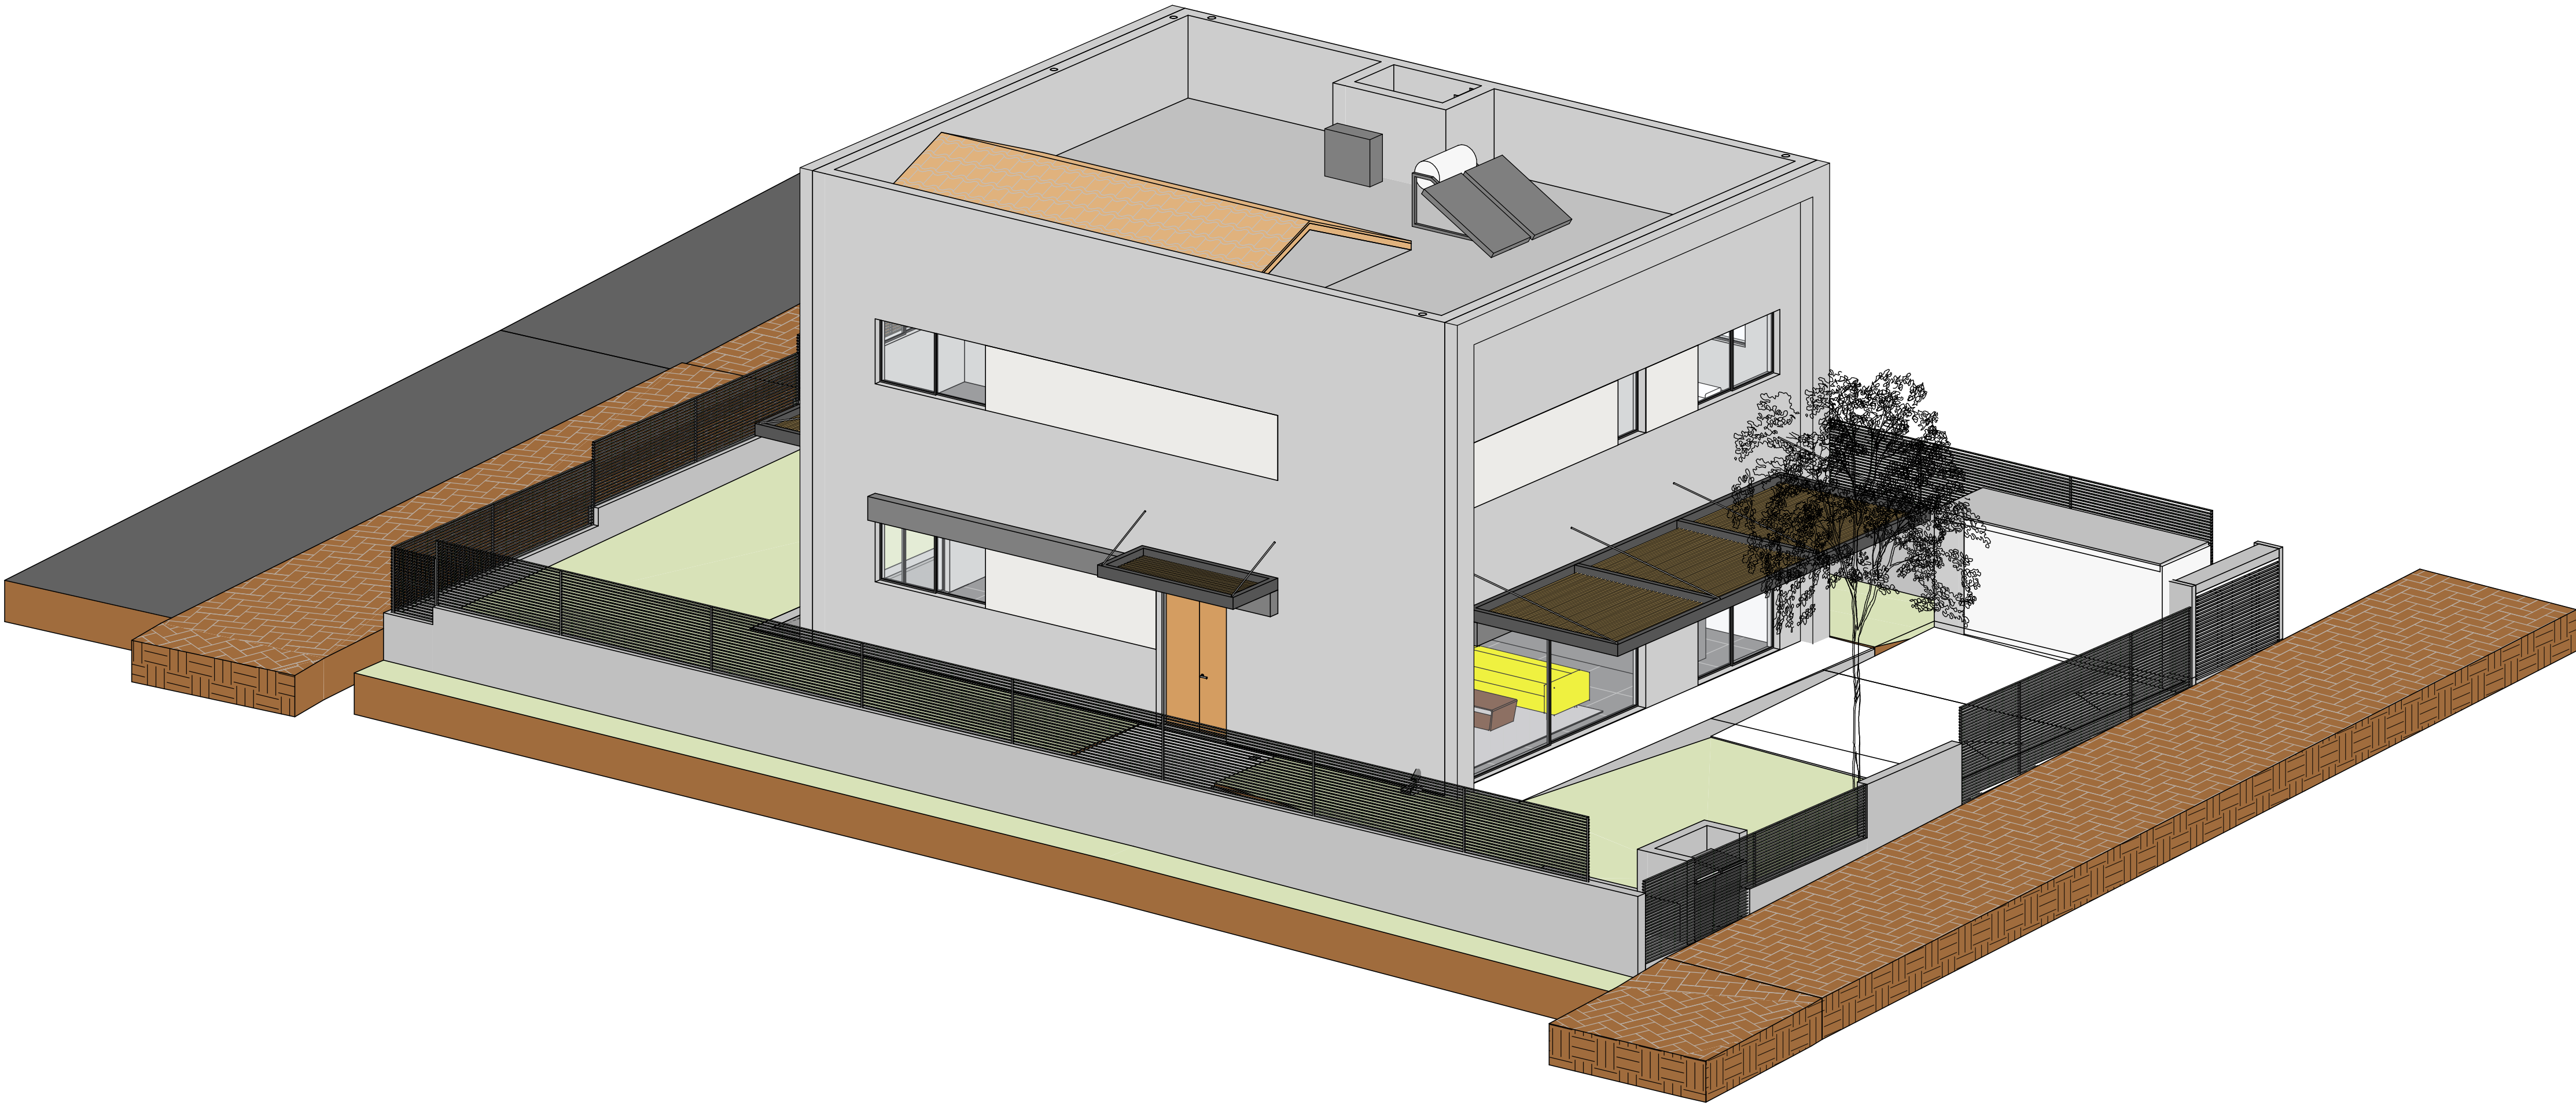

ניהול פרויקט
מהיסוד בן סלומון
פיקוח
מהיסוד - בן סולומון
קונסטרוקציה
ערן שילר
מיזוג אוויר
אייל ארז מהנדסים ויועצים בע"מ
אינסטלציה
איתן אלמסי
חשמל
איתן בסיס
אלומיניום
בופ
נתי בלוקא
חשמל חכם
חימום תת רצפתי
איטום
צבי טל
אקוסטיקה
מעליות
קרקע וביסוס
ד"ה הנדסת קרקע וביסוס
רישוי

± 0.00 = +249.00
הערות: 1. תכנית זו יש לקרוא יחד עם תכנית הריטשים. 2. גובה אבסולוטי - ראו תכנית סימום. 3. המידות הן בין קירות הבניה ולא כולל פחים. 4. פיתוח השטח סביב המבנה, כולל, מדרגות, גדרות, שבילים, ריצופים, שטחים גזרים, חניה וכו' ראו תכנית פיתוח. 5. איטום קירות ורצפות המבנה כמעט עם הקרקע ובידוד תרמי לאורך העמודים והקורות ורצפות. כליות או עם סימני גיבס - ראו תכנית קונסטרוקציה. 6. אין מים יבוצע בכל מישור אופקי הכולל מתבנית. 7. מים תרמי במס"ד - ע"פ מפרט חומרים, מאפשר ט"י פיבוד העורף. המבצע אחראי לסידור : עליו לבקר ולבדוק את כל המידות בתכנית ובקטע העבודה. במסגרת של סימון או אי התאמה בתכנית /או בבנוי, עליו להודיע על כך מיד לאדריכל במסד המשרד בעברותיו. המבצע יישמש או ויקי בתכנית שאמור לכיפוף. המבצע יחזיק באחריות, לכל מה, של מתבנית של תכנית. אין לקבוע מידות על ידי מדידה בשטח. התכנית היתה רחבה האדריכל ואין לשנות כל שימוש בה או ברעיונות הגלומים בה, אלא באישור בכתב מהאדריכל. מחדש /או יועץ אשר שמו רשום בתכנית זו, נושא לכיד באחריות המקצועית והטכנית לתכנית. על המפקח והמבצע לזרז את האמת התכנית האדריכלית "כיפוף" לתכנית יחידה, המכר והתכנית המאושרת שי" כל גורמים רשמיים. תכנית כוללת את כל האחריות והידוע על ליום תוצאות.

משרד קירות:

	קיר בלוק
	קיר בסון
	מחוד בסון

תאריך	תיאור	מהדורה
22.09.2025	מכר	1
17.12.2025	הוספת ת. רחצה במרתף	2


אדריכלות	
המסמך:	CLIENT NAME:
קבוצת רכישה נופיה	
הפרויקט:	PROJECT NAME:
נופיה - מגרש 13	
הגיליון:	DRAWING NAME:
תכנית קומת מרתף	
מספר גיליון:	SHEET NUMBER:
A3-1-100	
הדורה:	EDITION:
קנה מידה:	SCALE:
2	1 : 50
שורשם ע"י:	STATUS:
הילה בהנא	למכר
נבדק ע"י:	
תאריך:	DATE:
22.09.2025	

17/12/2025 10:25:25

נירן חיינר אדריכלים
מנכ"ל התחנה 2, בית חירות
09-9545642 70

office@nh-arch.com
www.nh-arch.com

זכיות ייצור / ע"פ הנחיות ע"ד

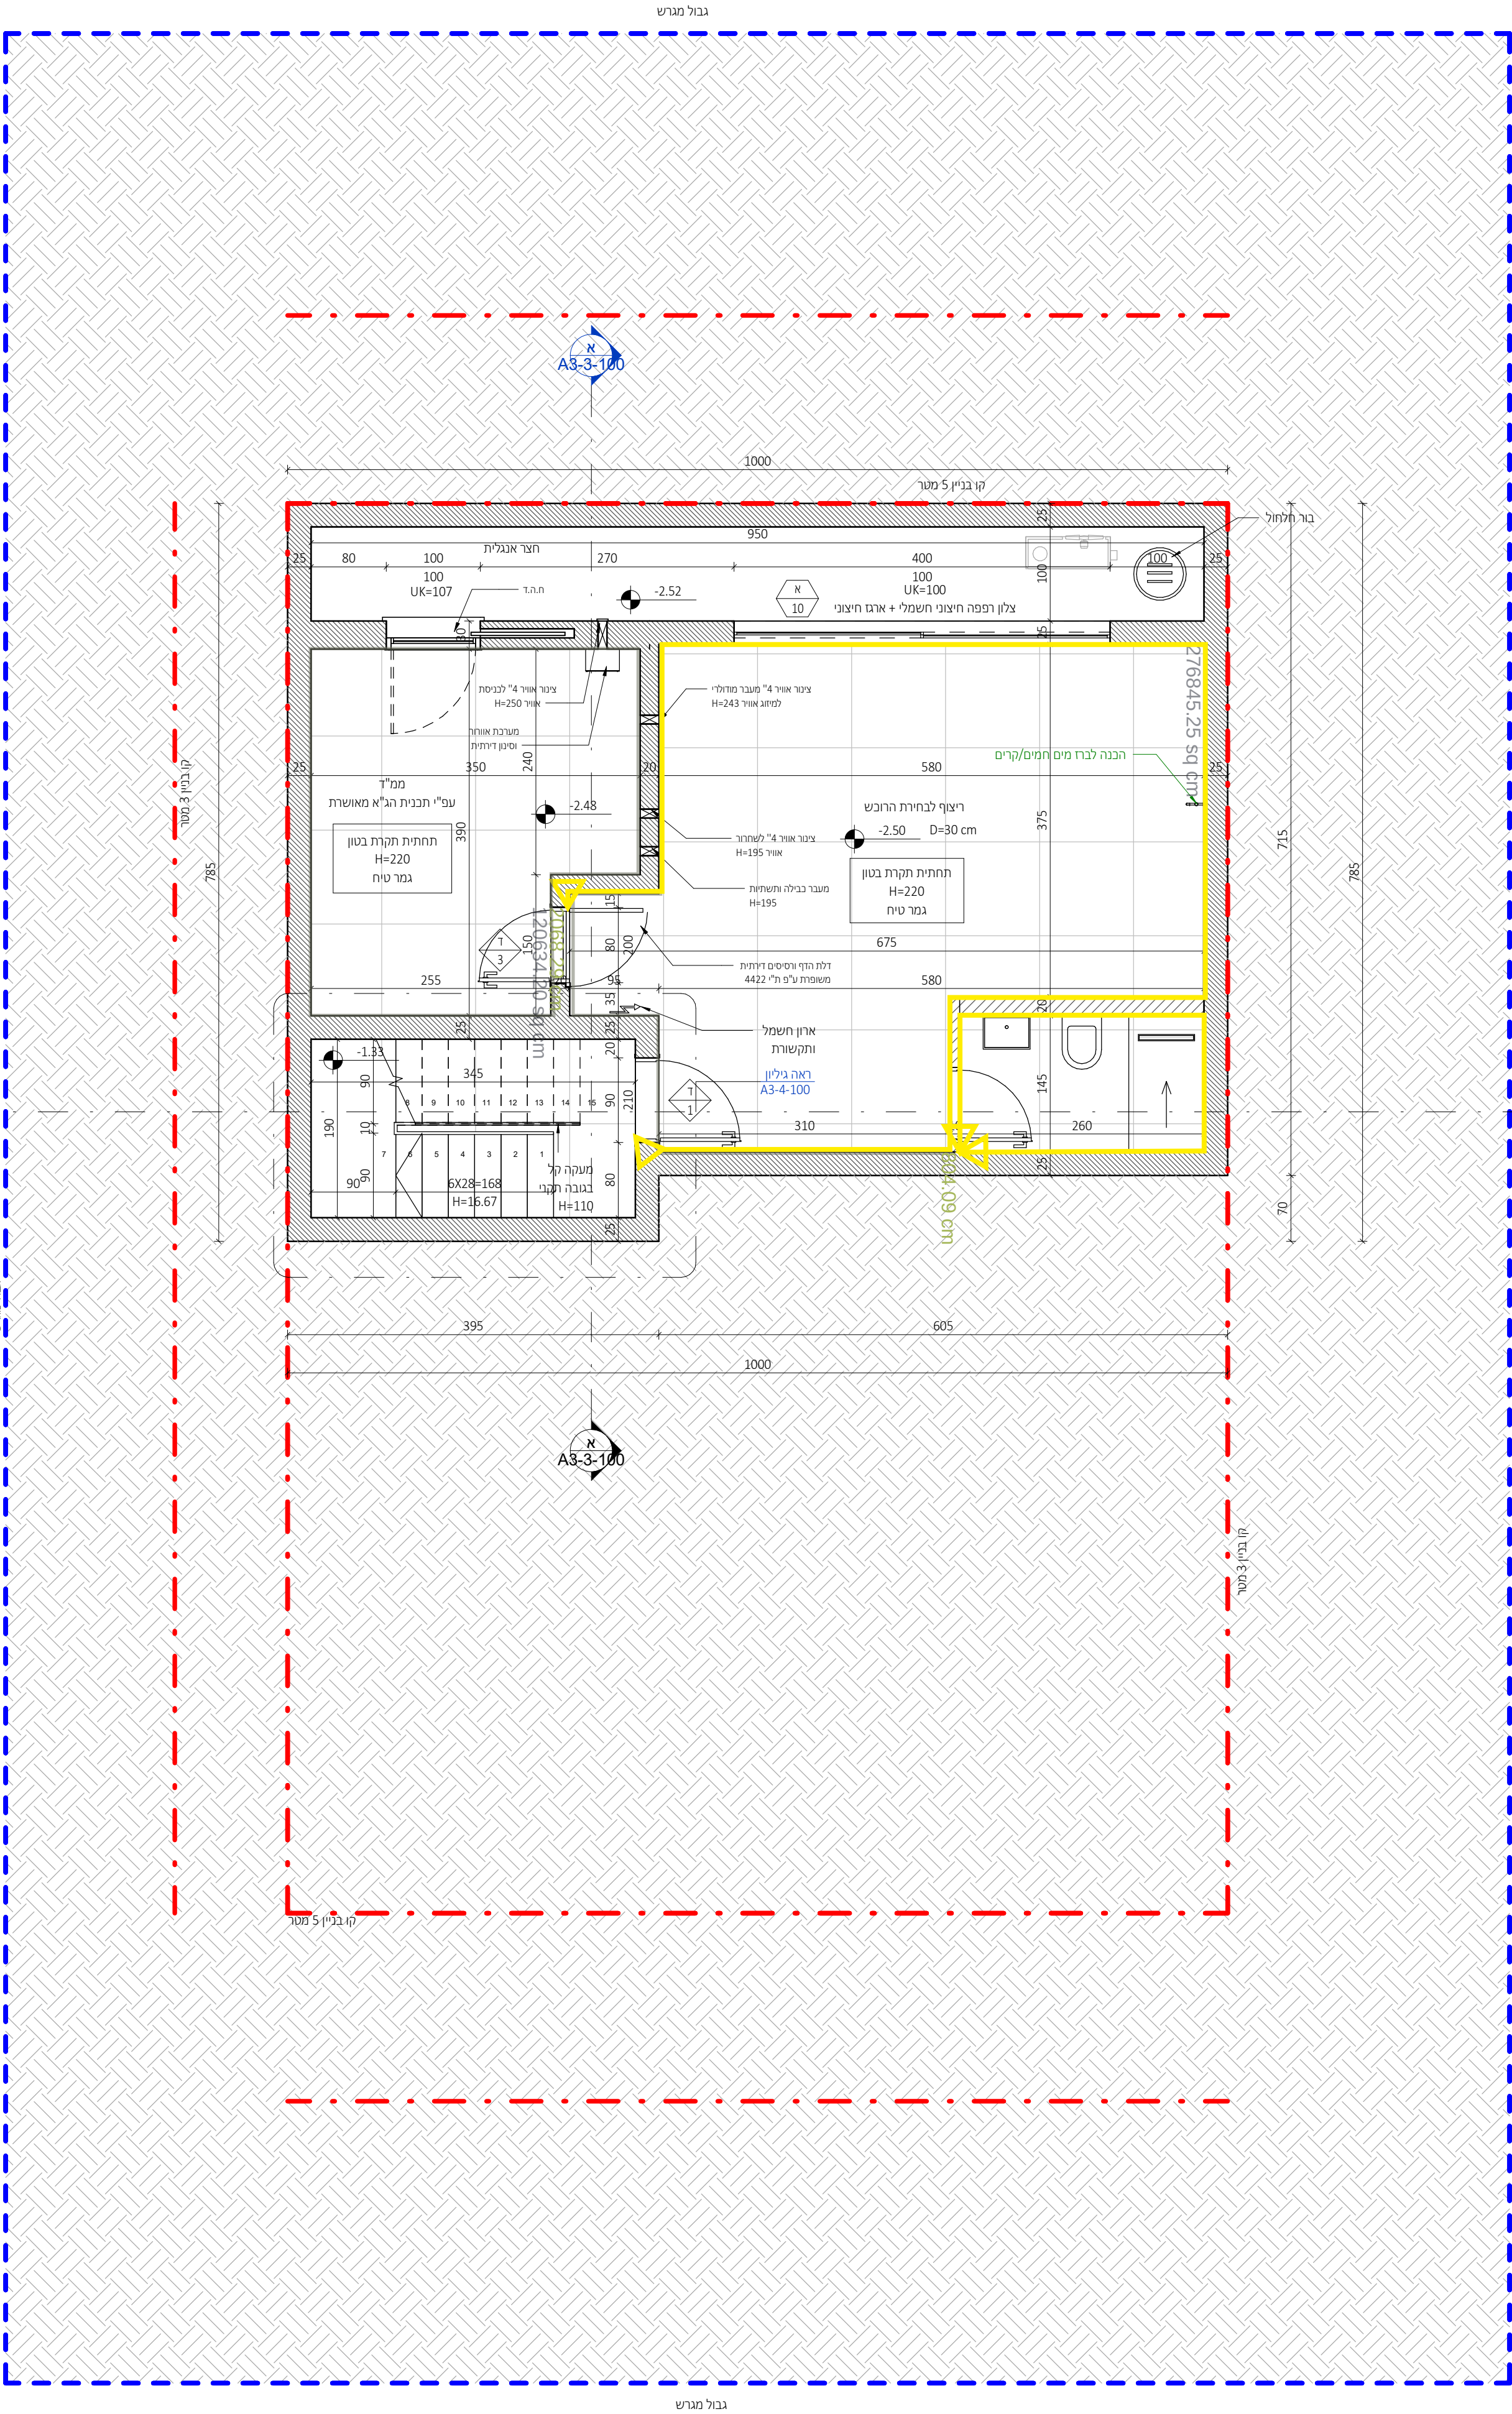

- הערות:
- יש לעבוד במקביל לתכניות יועצים המאושרות על ידי האדריכל.
 - פרטי ספי חלון - עפ"י חוברת אלומיניום של הספק הנבחר ובתיאום מול אדריכל.
 - חימום תת רצפתי (במידה ויש במגרש זה) עפ"י פרטי הספק ובתיאום מול אדריכל.
 - יש לעבוד במקביל לתכניות עיצוב פנים (במידה ויש מעצב פנים במגרש זה) המאושרות על ידי האדריכל.
 - באחריות הקבלן לעדכן את האדריכל על אי התאמה בין התכניות יועצים לאדריכלות.
 - כל הדלתות לפי מפרט מצורף.
 - כל אלמנטי הבטון יקבלו התייחסות תרמית לפי הנחיות יועץ.
 - פרטי איטום, בידוד וניקוז עפ"י תכניות יועצים ובאחריות הקבלן.

ניהול פרויקט
מהיסוד בן סולומון
פיקוח
מהיסוד - בן סולומון
קונסטרוקציה
ערן שילר
מיזוג אוויר
אייל ארז מהנדסים ויועצים בע"מ
אינסטלציה
איתן אלמסי
חשמל
איתן בסיס
אלומיניום
נוף
נתי בלוקא
חשמל חכם
חימום תת רצפתי
איטום
צבי טל
אקוסטיקה
מעליות
קרקע וביסוס
דיה הנדסת קרקע וביסוס
רישוי

[illegible]

עמוד בטון קיר בטון בלוק

אדריכלות

קבוצת רכישה נופיה


נופיה - מגרש 13

תכנית קומת קרקע

A3-1-101

:0119J

לה כהנא

 

NeumanHaynerArchitects

וימן חיינר אדריכלים
אורד הקדריים 2 בית חירות

office@nh-arch.com
www.nh-arch.com



הערות:

- 17/12/2025 10:25:27

ניהול פרויקט
מהיסוד בן ס
פיקוח
מהיסוד - בן ס
קונסטרקציה
ערן שילר
מיזוג אוויר
אייל ארז מהר
אינסטלציה
איתן אלמסי
חשמל
איתן בסיס
אלומיניום
נוף
נתי בלוקא
חשמל חכם
חימום תת רצפתי
איטום
צבי טל
אקוסטיקה
מעליות
קרקע וביסוס
דיה הנדסת
רשוי

[illegible][illegible]

אדריכלות

CLIENT NAME: _____: המזמין:

PROJECT NAME: הפרויקט:

DRAWING NAME: _____: תגליון:

SHEET NUMBER: 99 גליון:


A3-1-102



NeumanHaynerArchitects

ימון חיינר אדריכלים
 רוד ההדרים 2, בית חירות
 09-9545842 ל'
 office@nh-arch.com
 www.nh-arch.com

זכויות ייצור / ע"פ הנחיות עו"ד

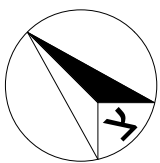

1 : 50

- הערות:
1. יש לעבוד במקביל לתכניות יועצים המאפשרות על ידי האדריכל.
 2. פרטי ספי חלון - עפ"י חוברת אלומיניום של הספק הנבחר ובתיאום מול אדריכל.
 3. חימום תת רצפתי (במידה ויש במגרש זה) עפ"י פרטי הספק ובתיאום מול אדריכל.
 4. יש לעבוד במקביל לתכניות עיצוב פנים (במידה ויש מעצב פנים במגרש זה) המאפשרות על ידי האדריכל.
 5. באחריות הקבלן לעדכן את האדריכל על אי התאמה בין התכניות יועצים לאדריכלות.
 6. כל הדלתות לפי מפרט מצורף.
 7. כל אלמנטי הבטון יקבלו התייחסות תרמית לפי הנחיות יועץ.
 8. פרטי איטום, בידוד וניקוז עפ"י תכניות יועצים ובאחריות הקבלן.

הערות:

פרטי איטום, בידוד וניקוז עפ"י תכניות יועצים ובאחריות הקבלן

מתכונים:

ניהול פרויקט
מהיסוד בן שלומון
פיקוח
מהיסוד - בן שלומון
קונסטרוקציה
ערן שילר
מיזוג אוויר
אייל ארז מהנדסים ויועצים בע"מ
אינסטלציה
איתן אלמסי
חשמל
איתן בסיס
אלומיניום
נוף
נתי בלוקא
חשמל חכם
חימום תת רצפתי
איטום
צבי טל
אקוסטיקה
מעליות
קרקע וביסוס
דיה הנדסת קרקע וביסוס
רישוי

[illegible]

מקרא קירות:


		
עמוד בסון	קיר בסון	קיר בלוק

[illegible]

אדריכלות


CLIENT NAME:		הפרויקט:	
PROJECT NAME:		הפרויקט:	
13 מגרש -		סוג המגרש:	
DRAWING NAME:		סוג המגרש:	
1 חזיתות		מספר המגרש:	
SHEET NUMBER:		מספר המגרש:	
A3-2-200		מספר המגרש:	
SCALE:	קנה מידה:	EDITION:	חזרה:
1 : 50			
STATUS:	סטטוס:		
למכר			
	נבדק ע"י:		הילה כהנא
DATE:	22.09.2025		חידוש:

פיתוח נוף עפ"י תוכניות
יועץ נוף ראה פירוט בנפרד

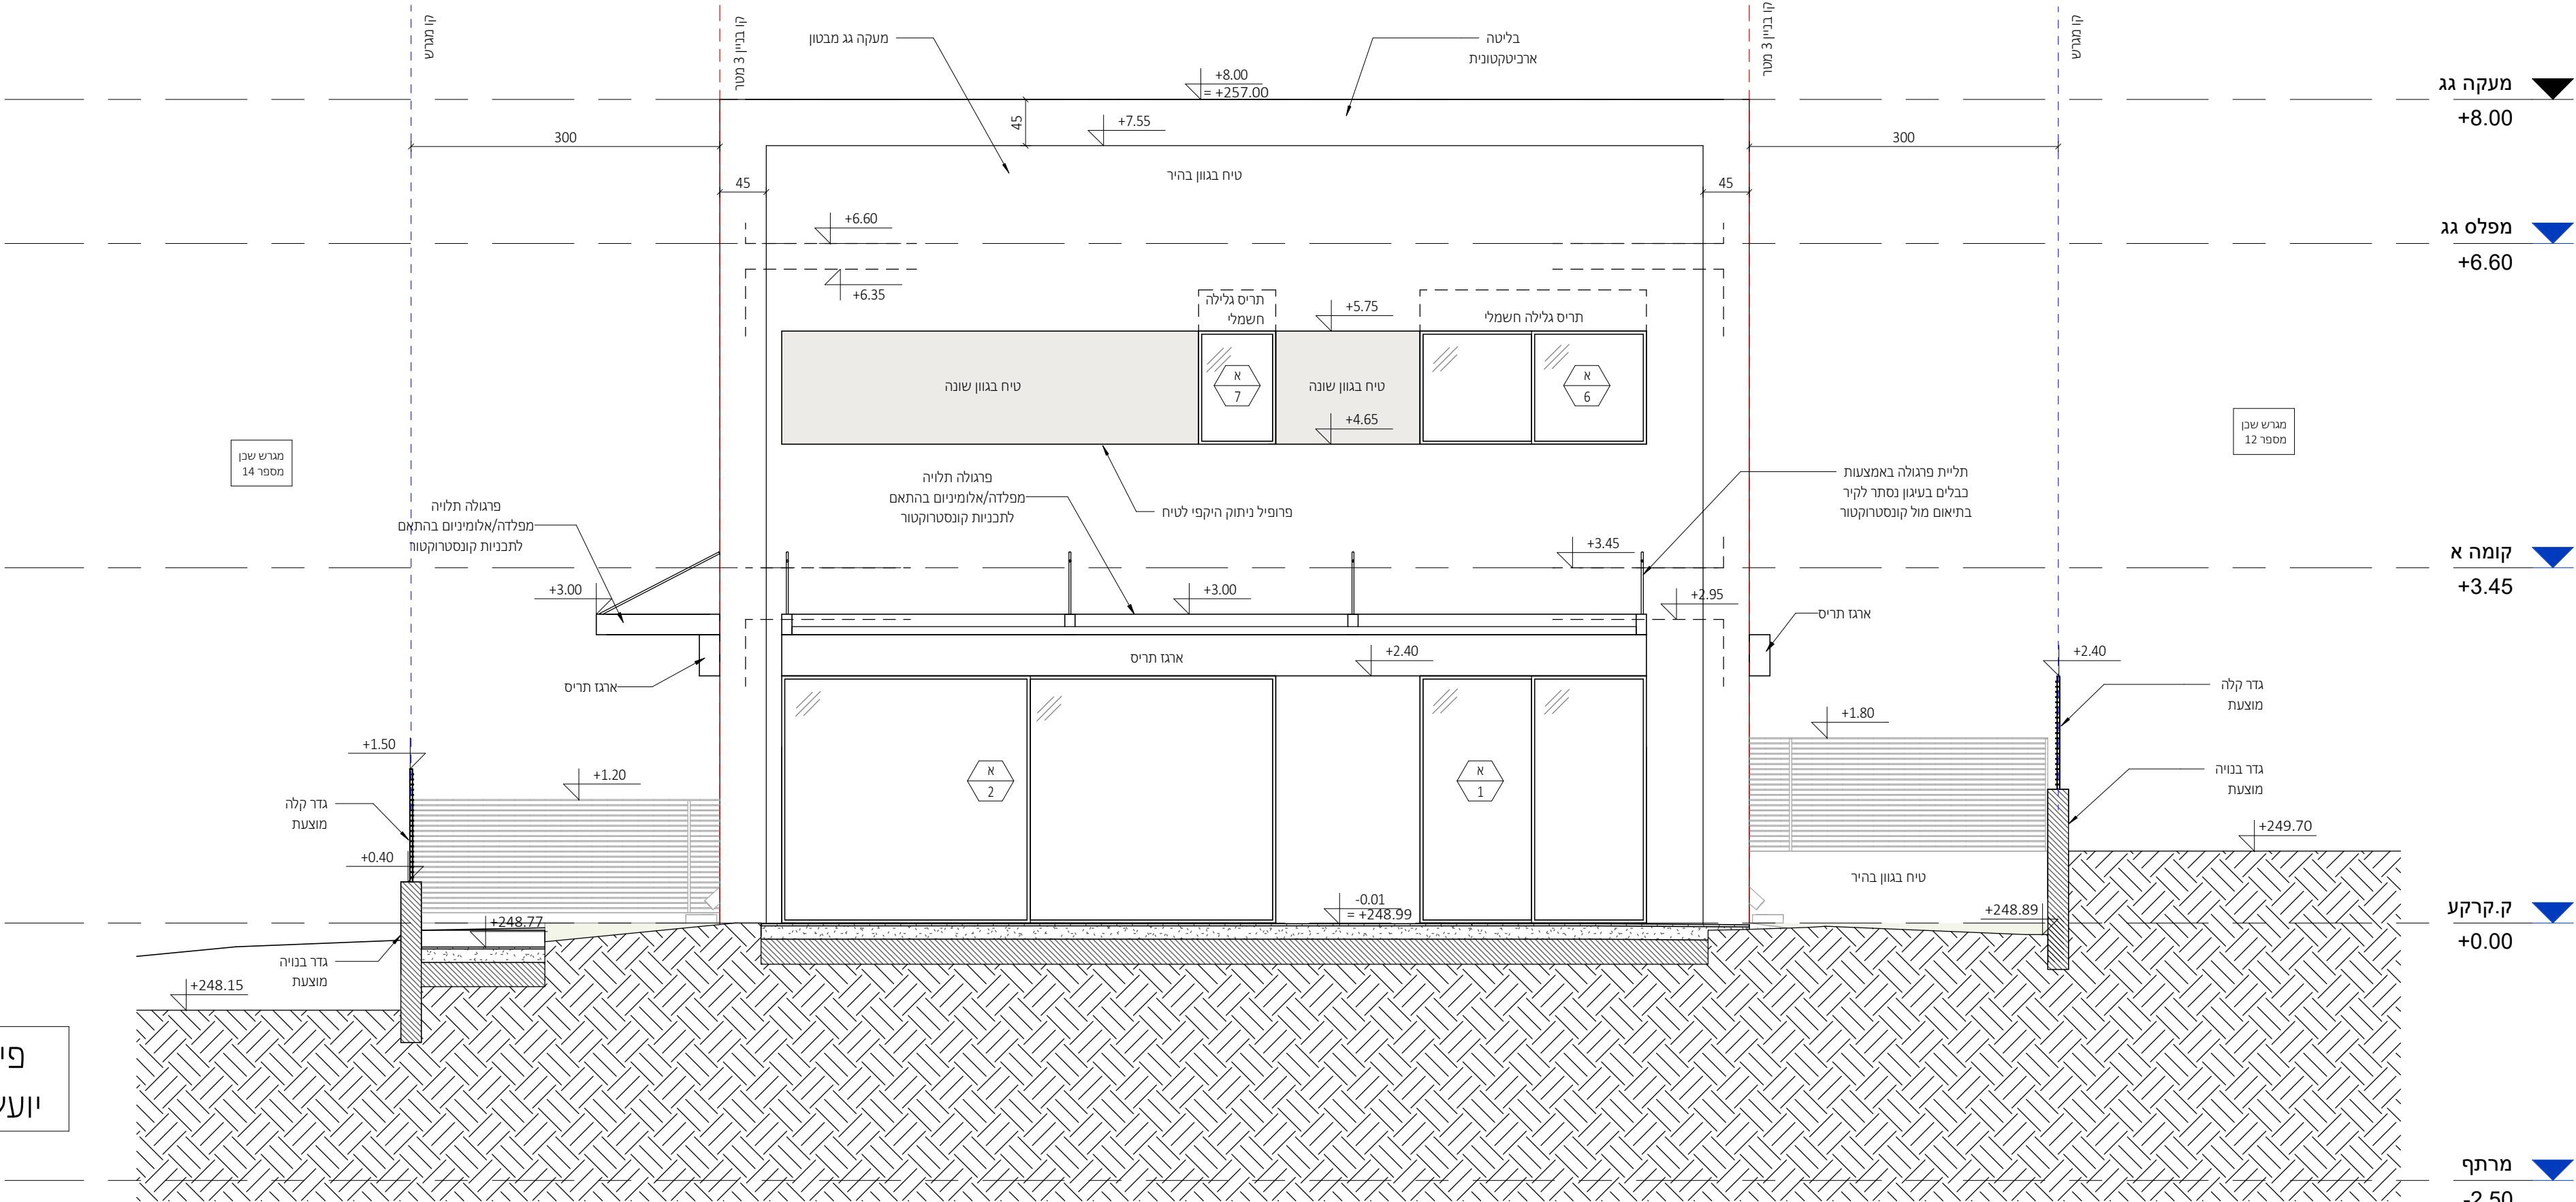

חזית דרומית

1 : 50

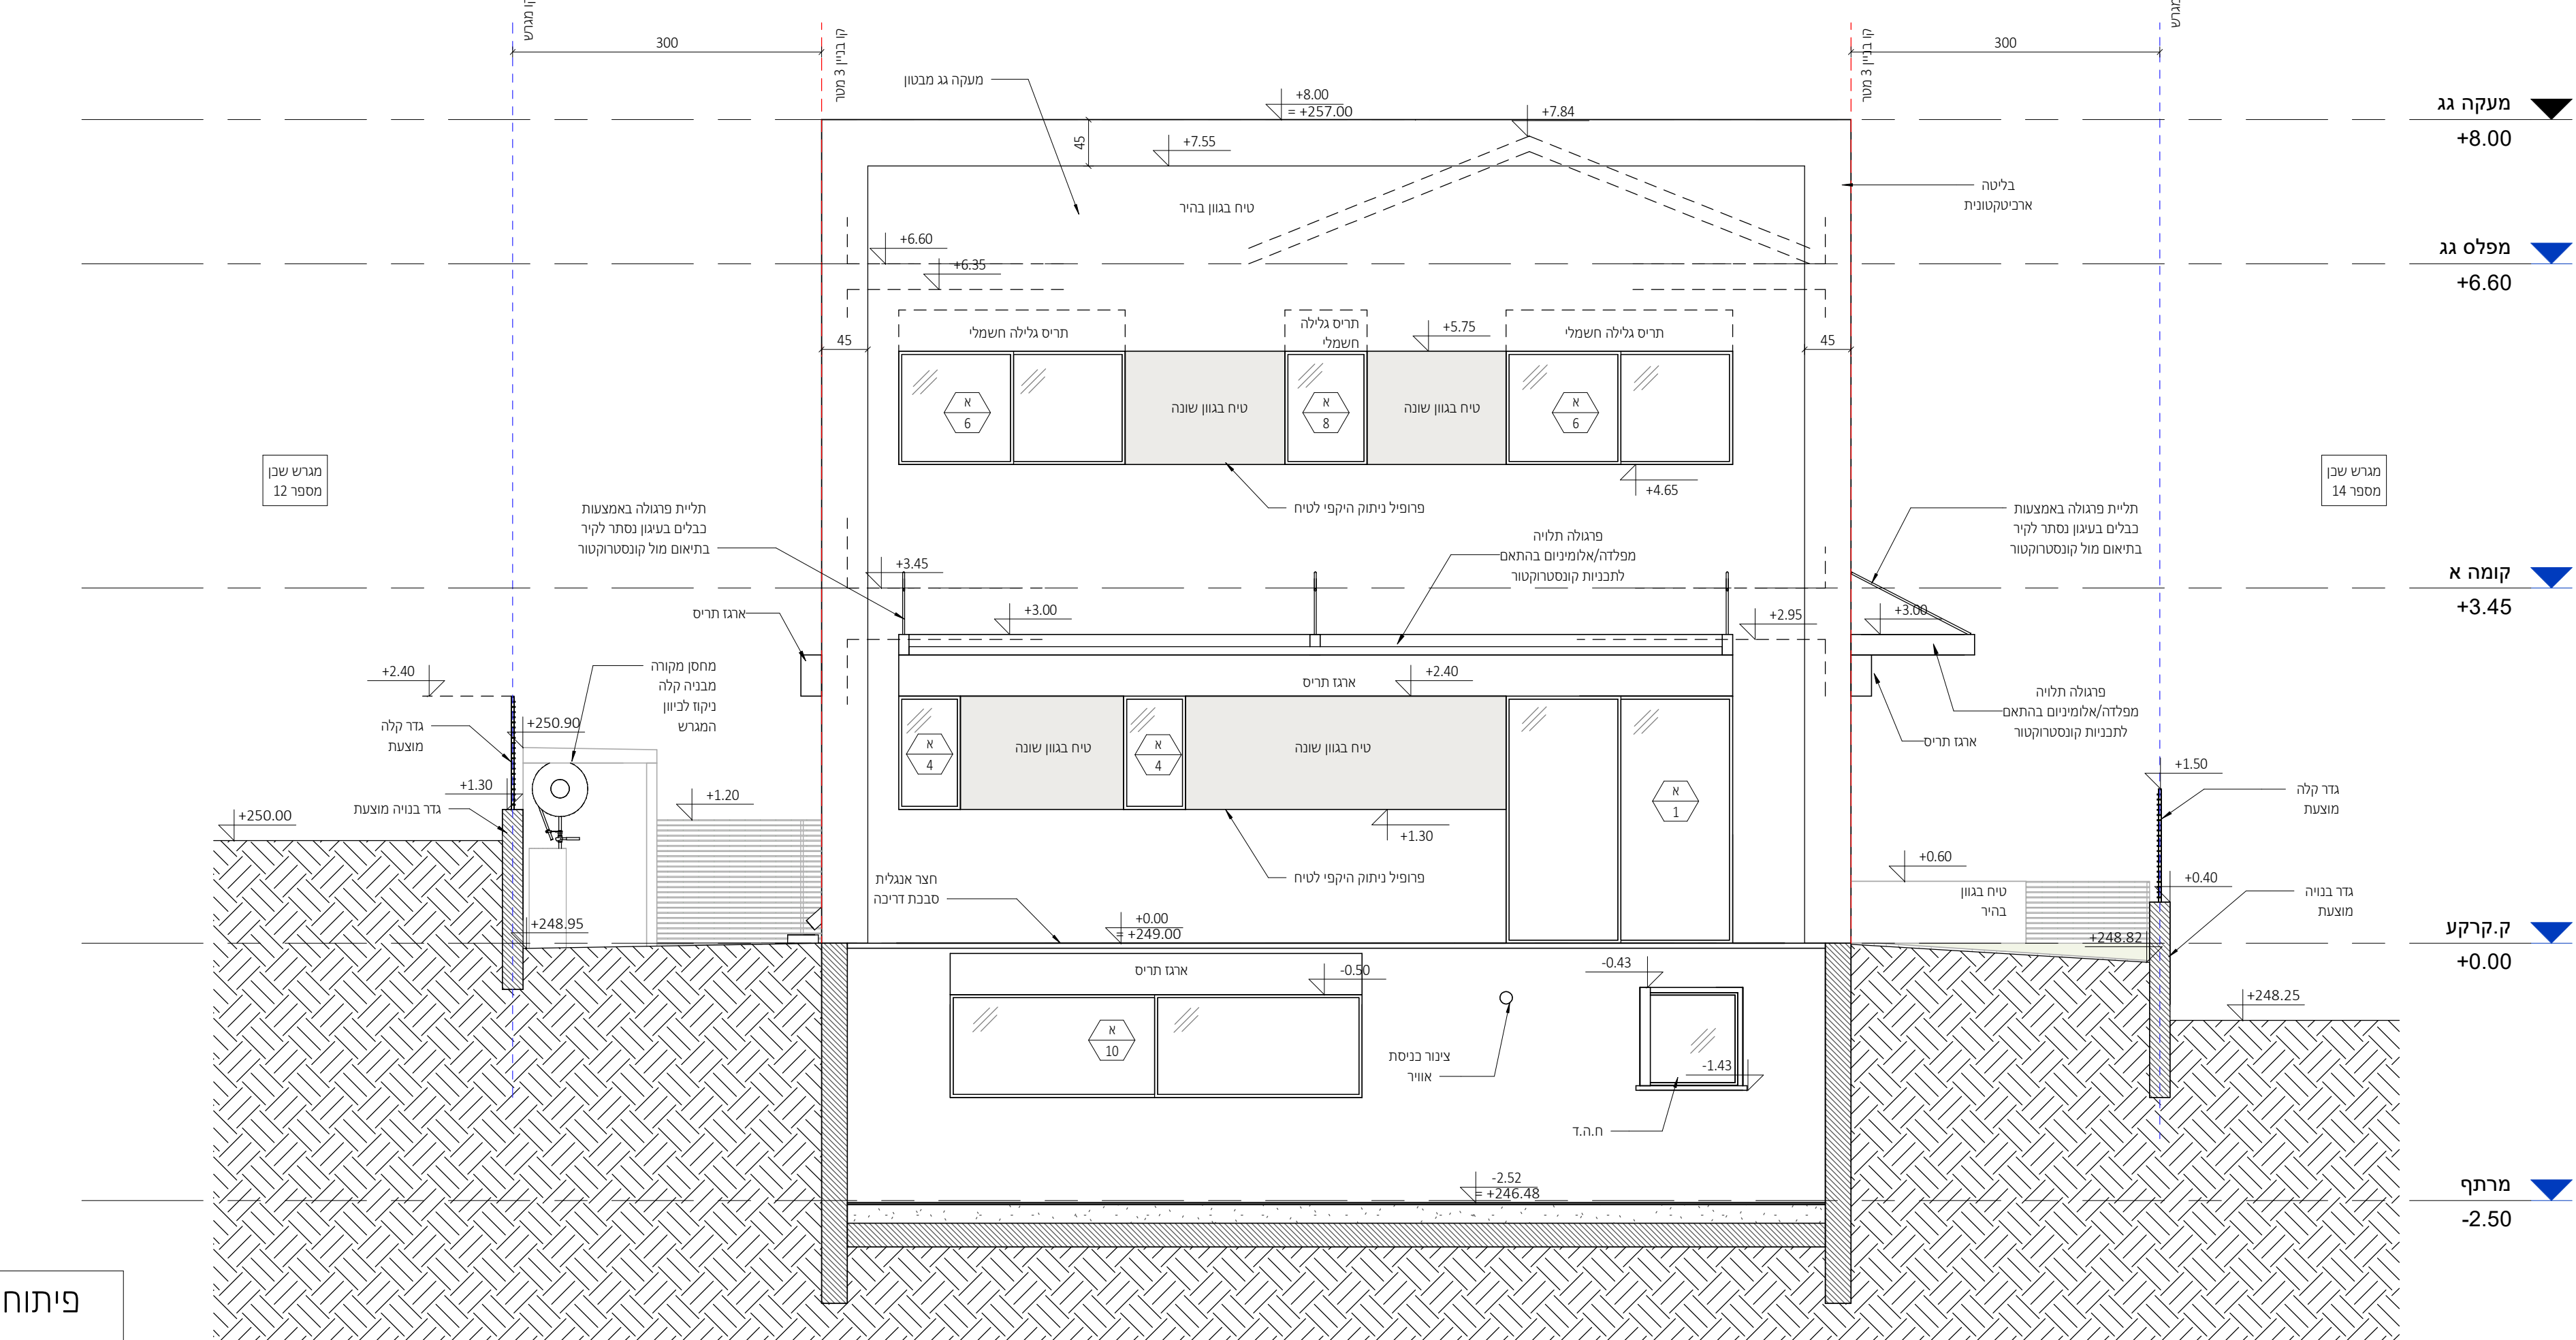



חזית צפונית

1 : 50

ניהול פרויקט
מהיסוד בן סולומון
פיקוח
מהיסוד - בן סולומון
קונסטרוקציה
ערן שילר
מיזוג אוויר
אייל ארז מהנדסים ויועצים בע"מ
אינסטלציה
איתן אלמסי
חשמל
איתן בסיס
אלומיניום
נוף
נתי בלוקא
חשמל חכם
חימום תת רצפתי
איטום
צבי טל
אקוסטיקה
מעליות
קרקע וביסוס
דיה הנדסת קרקע וביסוס
רישוי

[illegible]

CLIENT NAME:		הורחם	
קבוצת רכישה נופיה			
PROJECT NAME:		הפרויקט:	
נופיה - מגרש 13			
DRAWING NAME:		שם הציור:	
חזיתות 2			
SHEET NUMBER:		מספר הציור:	
A3-2-201			
SCALE:	קנה מידה:	EDITION:	דפוס:
1 : 50			
STATUS:	סטוס		
לנכר			
	(בדק ע"י)	חילה כהנא דפוס ע"י:	
DATE:	22.09.2025	ימיו:	

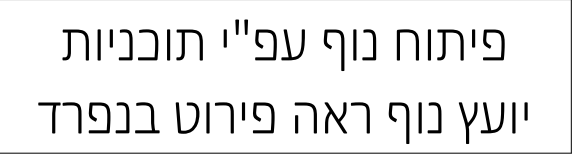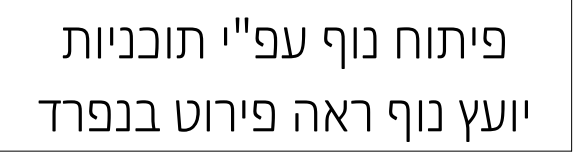

1 : 50

1 : 50

ניהול פרויקט
מהיסוד בן שלומון
פיקוח
מהיסוד - בן סולומון
קונסטרוקציה
ערן שילר
מיזוג אוויר
אייל ארז מהנדסים ויועצים בע"מ
אינסטלציה
איתן אלמסי
חשמל
איתן בסיס
אלומיניום
נוף
נתי בלוקא
חשמל חכם
חימום תת רצפתי
איטום
צבי טל
אקוסטיקה
מעליות
קרקע וביסוס
דיה הנדסת קרקע וביסוס
רישוי







הערות:
 תכנית זו יש לקרוא יחד עם תכנית הווע"פ.
 גובה אסכולות: ראו תכנית פיתוח
 המידות הן בין קירות הבניה ולא כולל מ"מ.
 פיתוח השטח סביב המבנה, כולל, מדרכות, גדרות, שבילים, ריצופים,
 פסיפגים בברים... חו"ה ניתן-ראו תכנית פיתוח
 אסוס: פיתוח תרופות הנבנות במגנט עם הקרקע ביכודו תחמי לאורך העמודים
 והקורות לכל המבנה וקירותיו או מ"מ (ניתן) ראו תכנית קונסטרוקציה
 אף מ"מ ביצוע בכל מפרט אופטי הכולל מחבין.
 מ"מ תחמי בממ"ד ע"פ משרד המדריך, מאושר ע"י פיקוד העורף.

[illegible]




אדריכלות	
CLIENT NAME:	ס הסינים
קבוצת רכישה נופיה	
PROJECT NAME:	פרויקט הסינים
נופיה - מגרש 13	
DRAWING NAME:	ס הגיליון
גליון מדרגות	
SHEET NUMBER:	מפר גליון
A3-4-100	
SCALE:	קנה מידה:
As indicated	מדרגות
STATUS:	סטטוס
למכר	בבדק ע"י
DATE:	הילה כהנא
22.09.2025	אריה

יומן חיינו אדריכלים
 חורף ההדורים 2, בית חירות
 09-9545842

זכויות ייצור / ע"פ הנחיות עו"ד
 office@nh-arch.com
 www.nh-arch.com

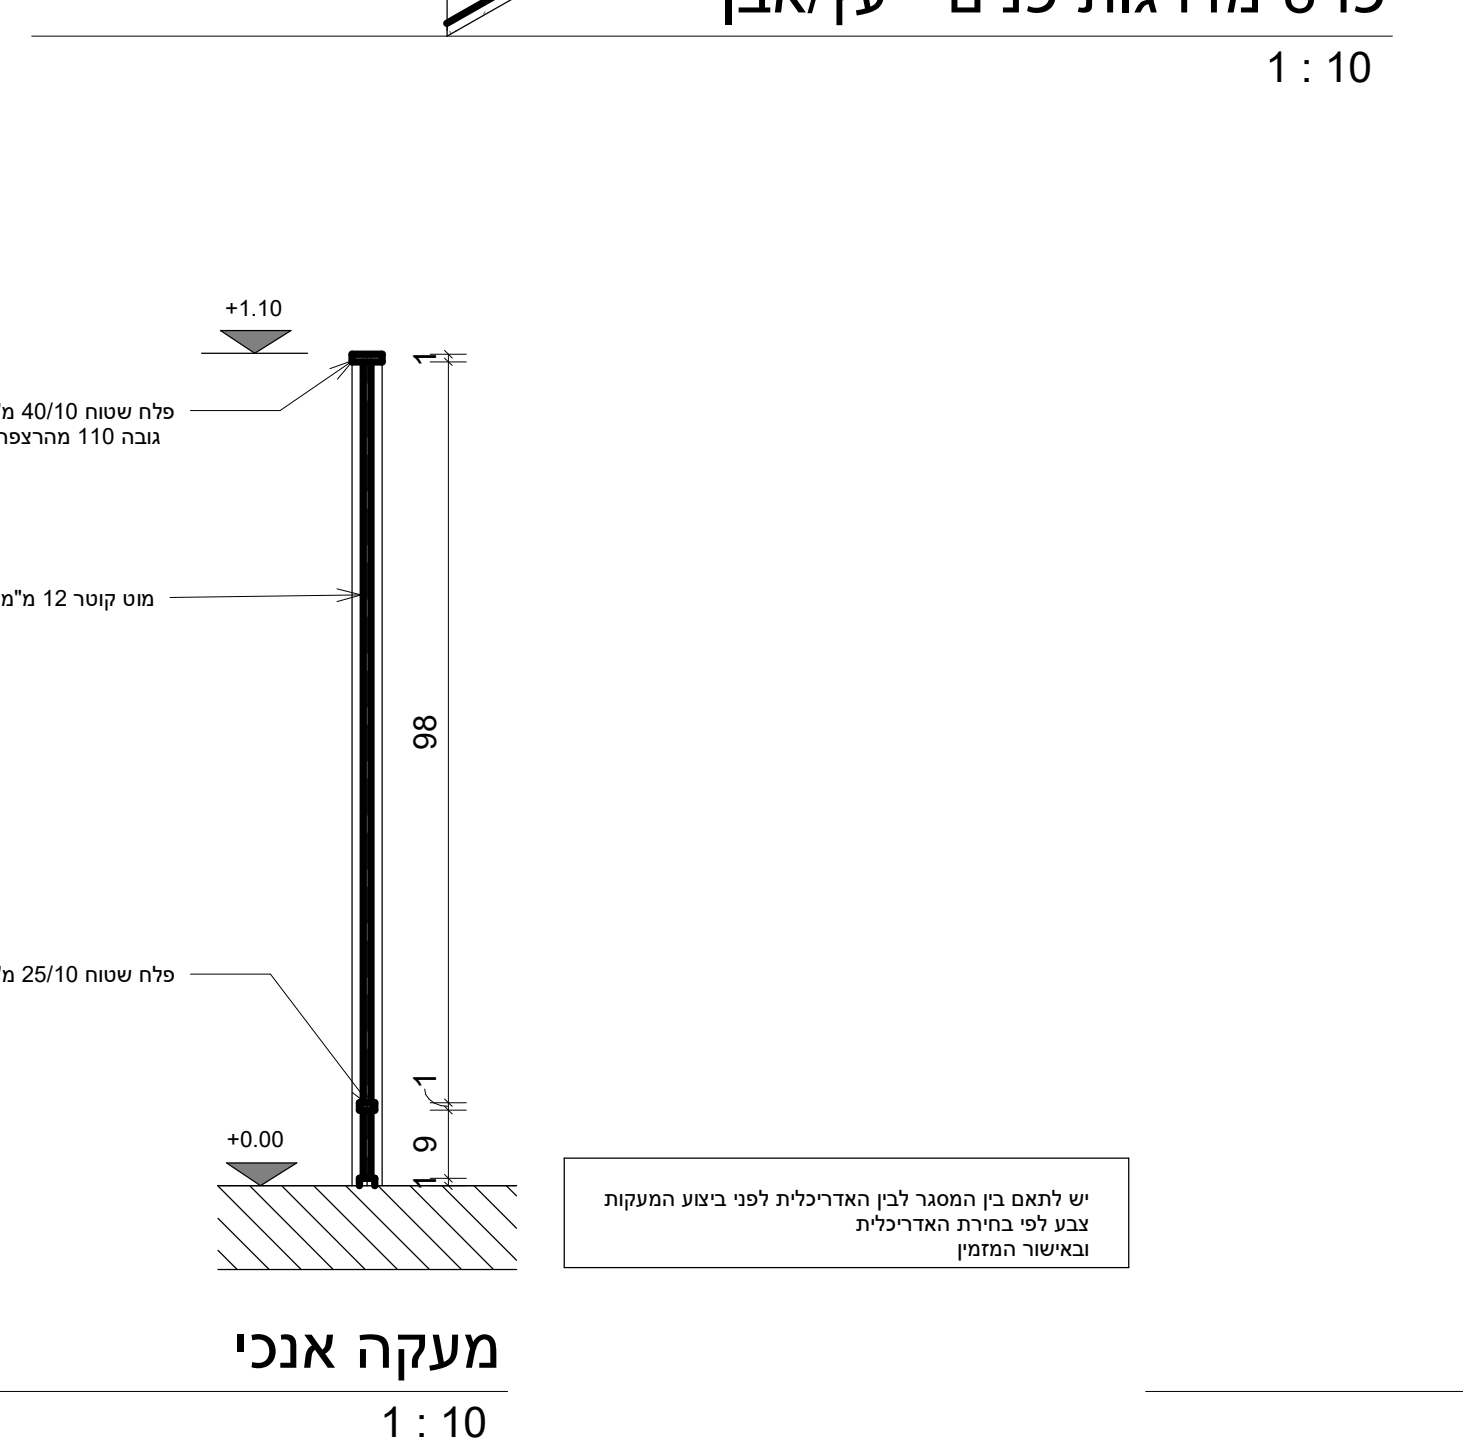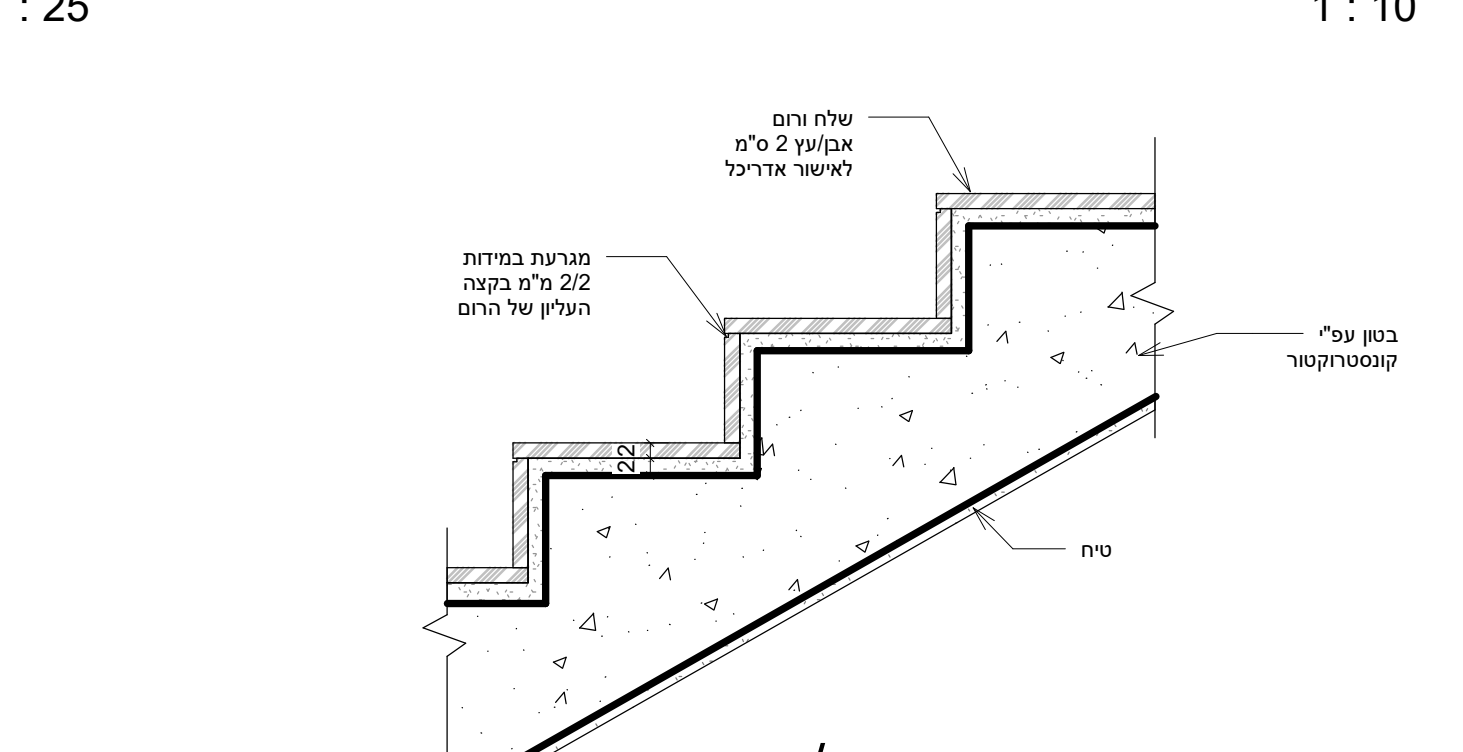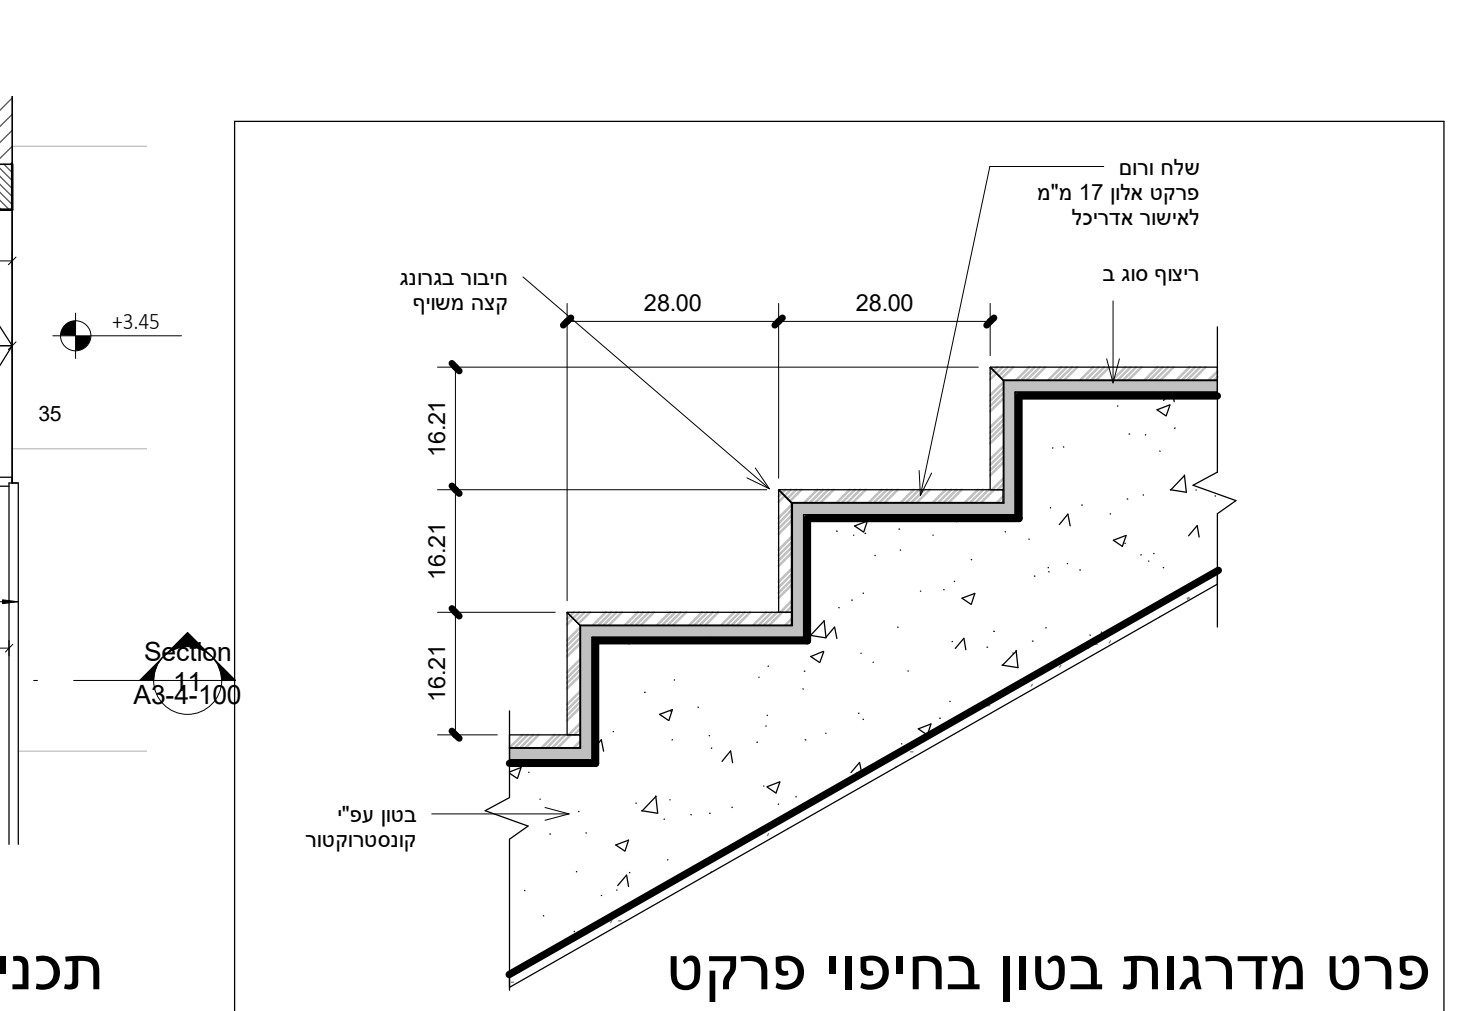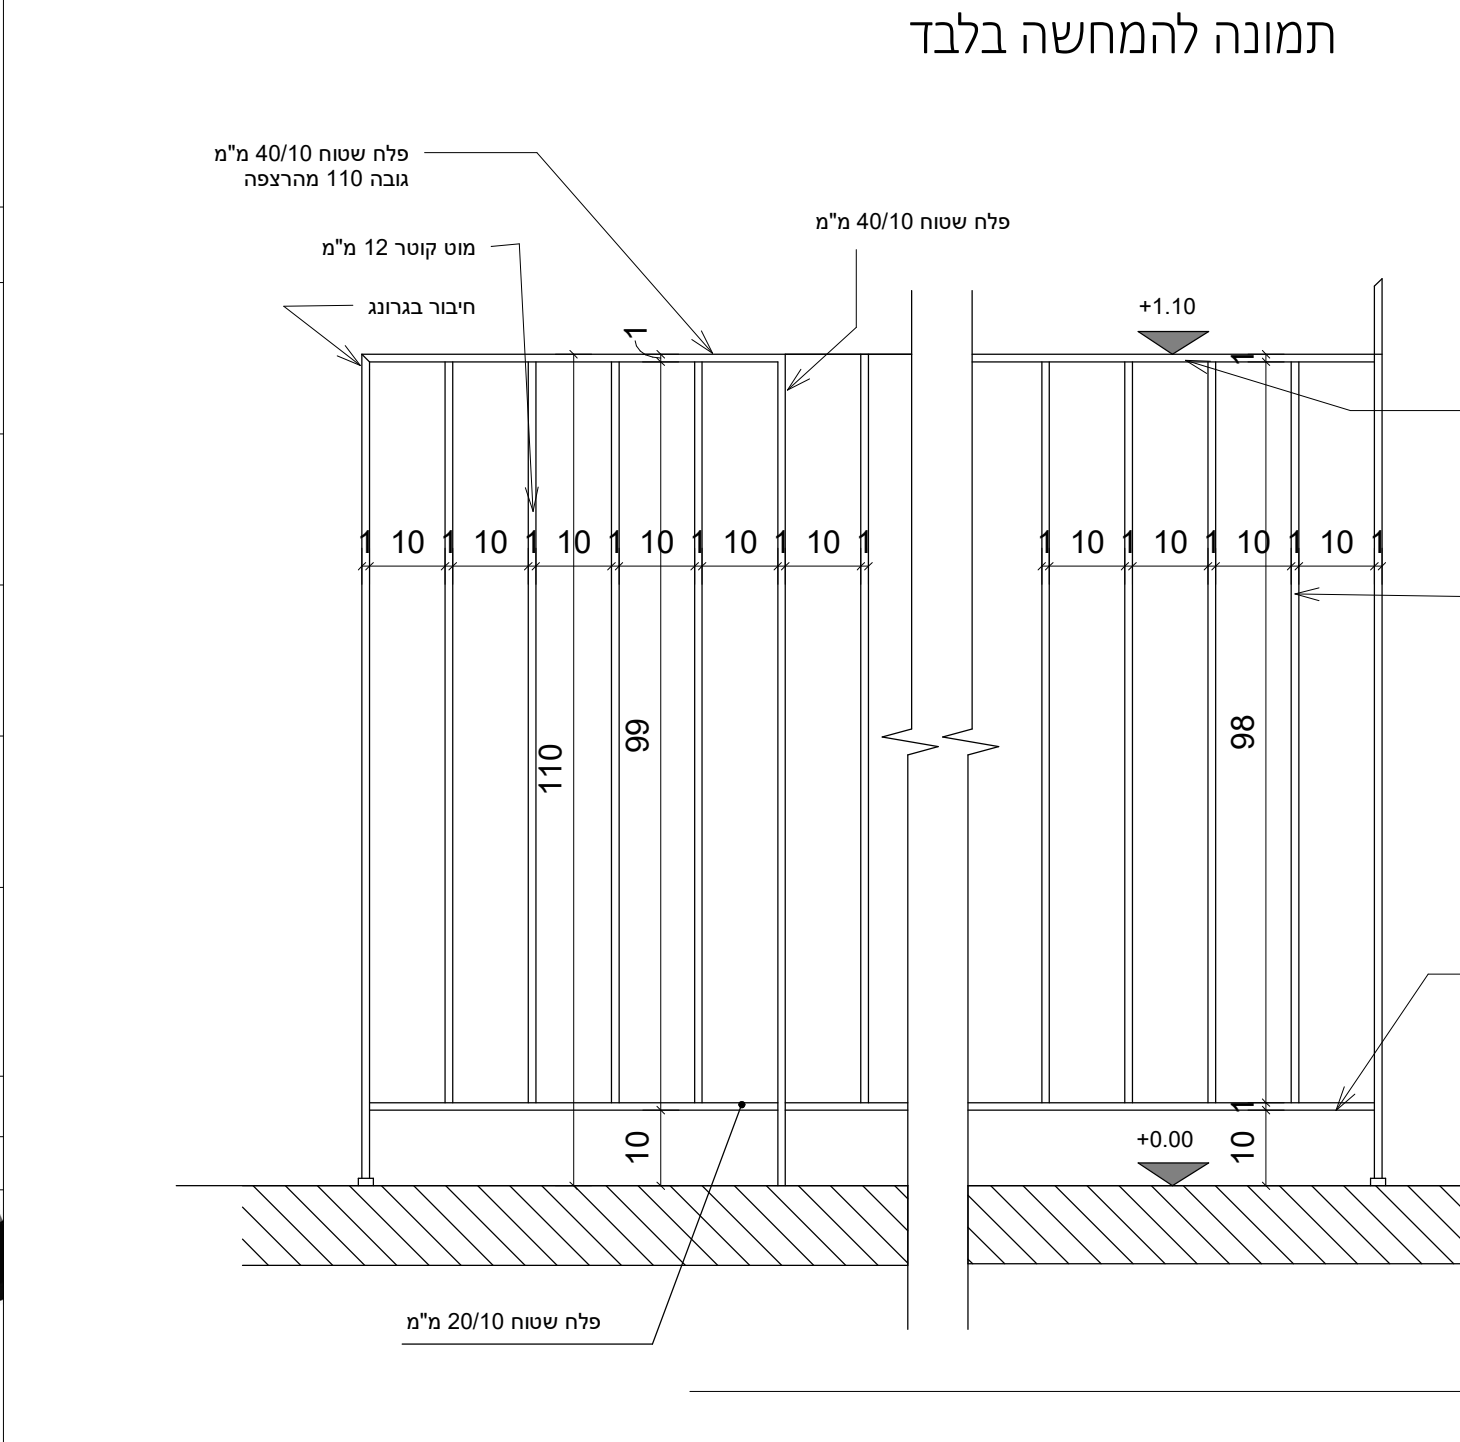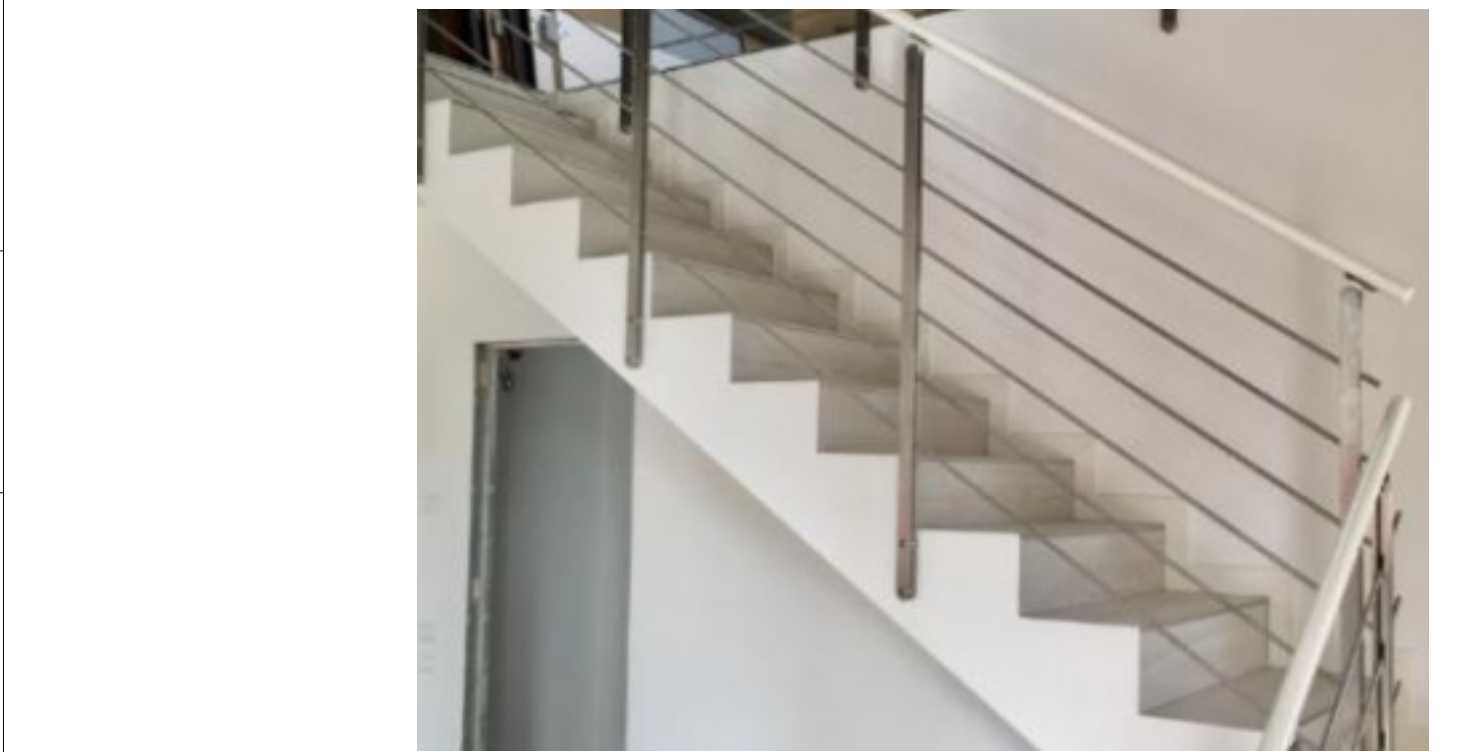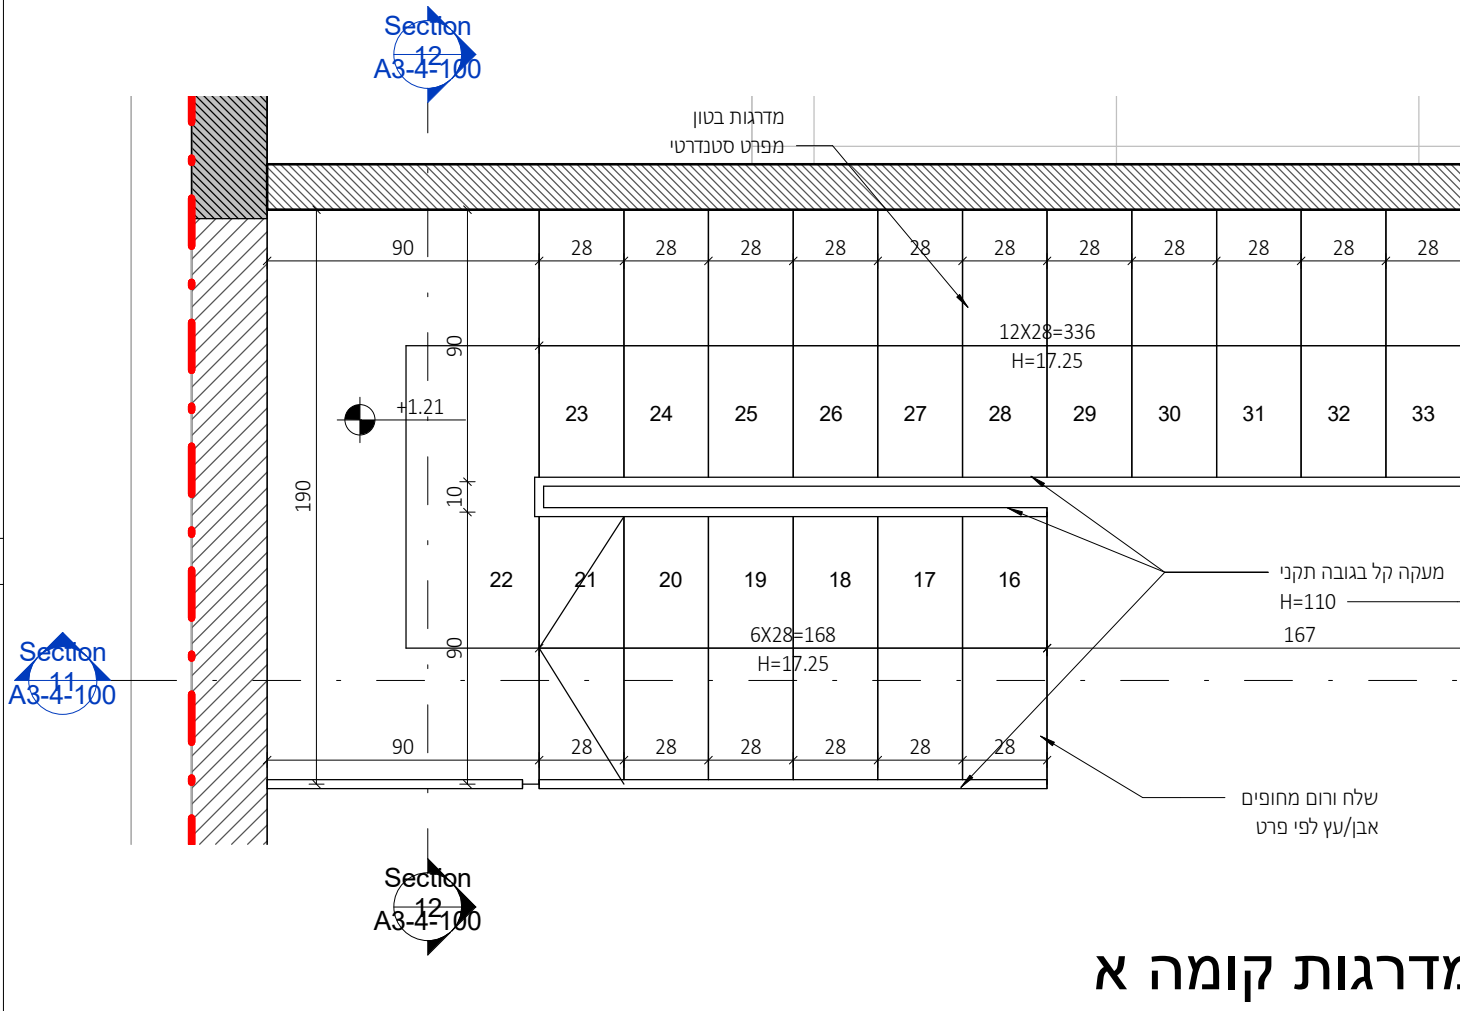

דגם נבחר
מדרגות סטנדרטיות - מפרט סטנדרטי
על הקבלן לשלוח S.D לאישור אדריכל
יש לבצע התאמה לפרט לאחר בחירת
חיפוי המדרגות*

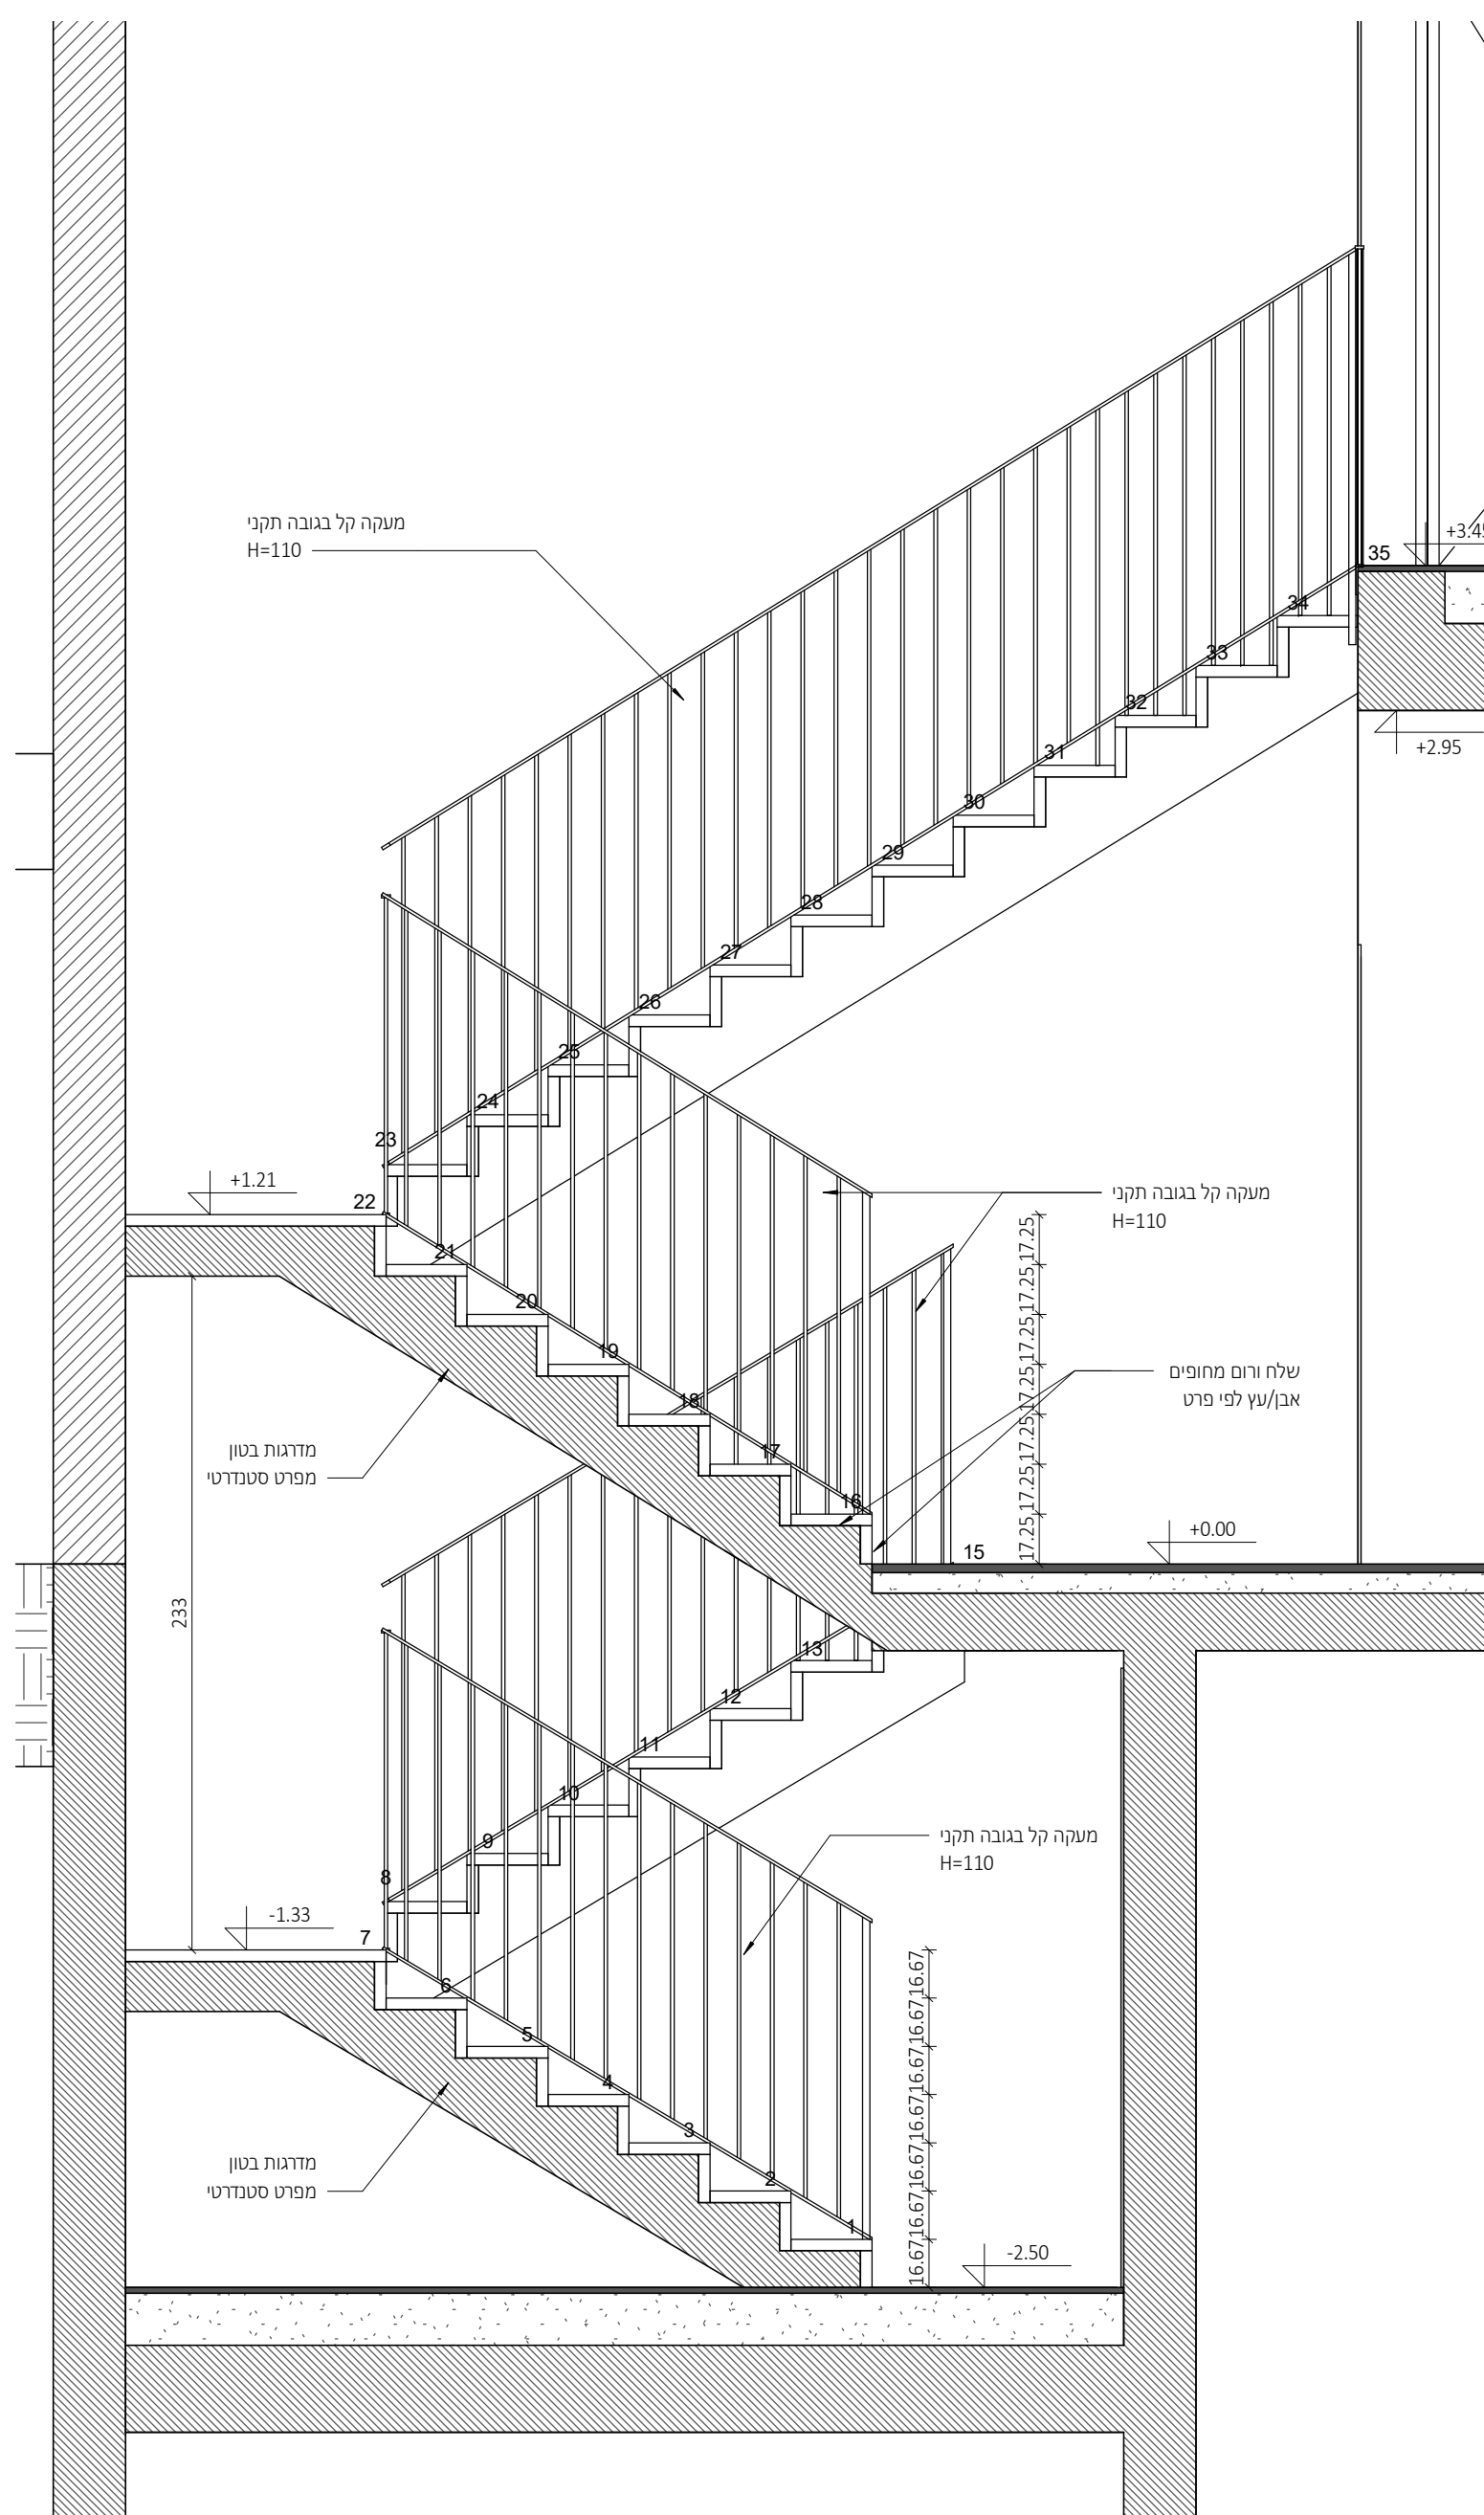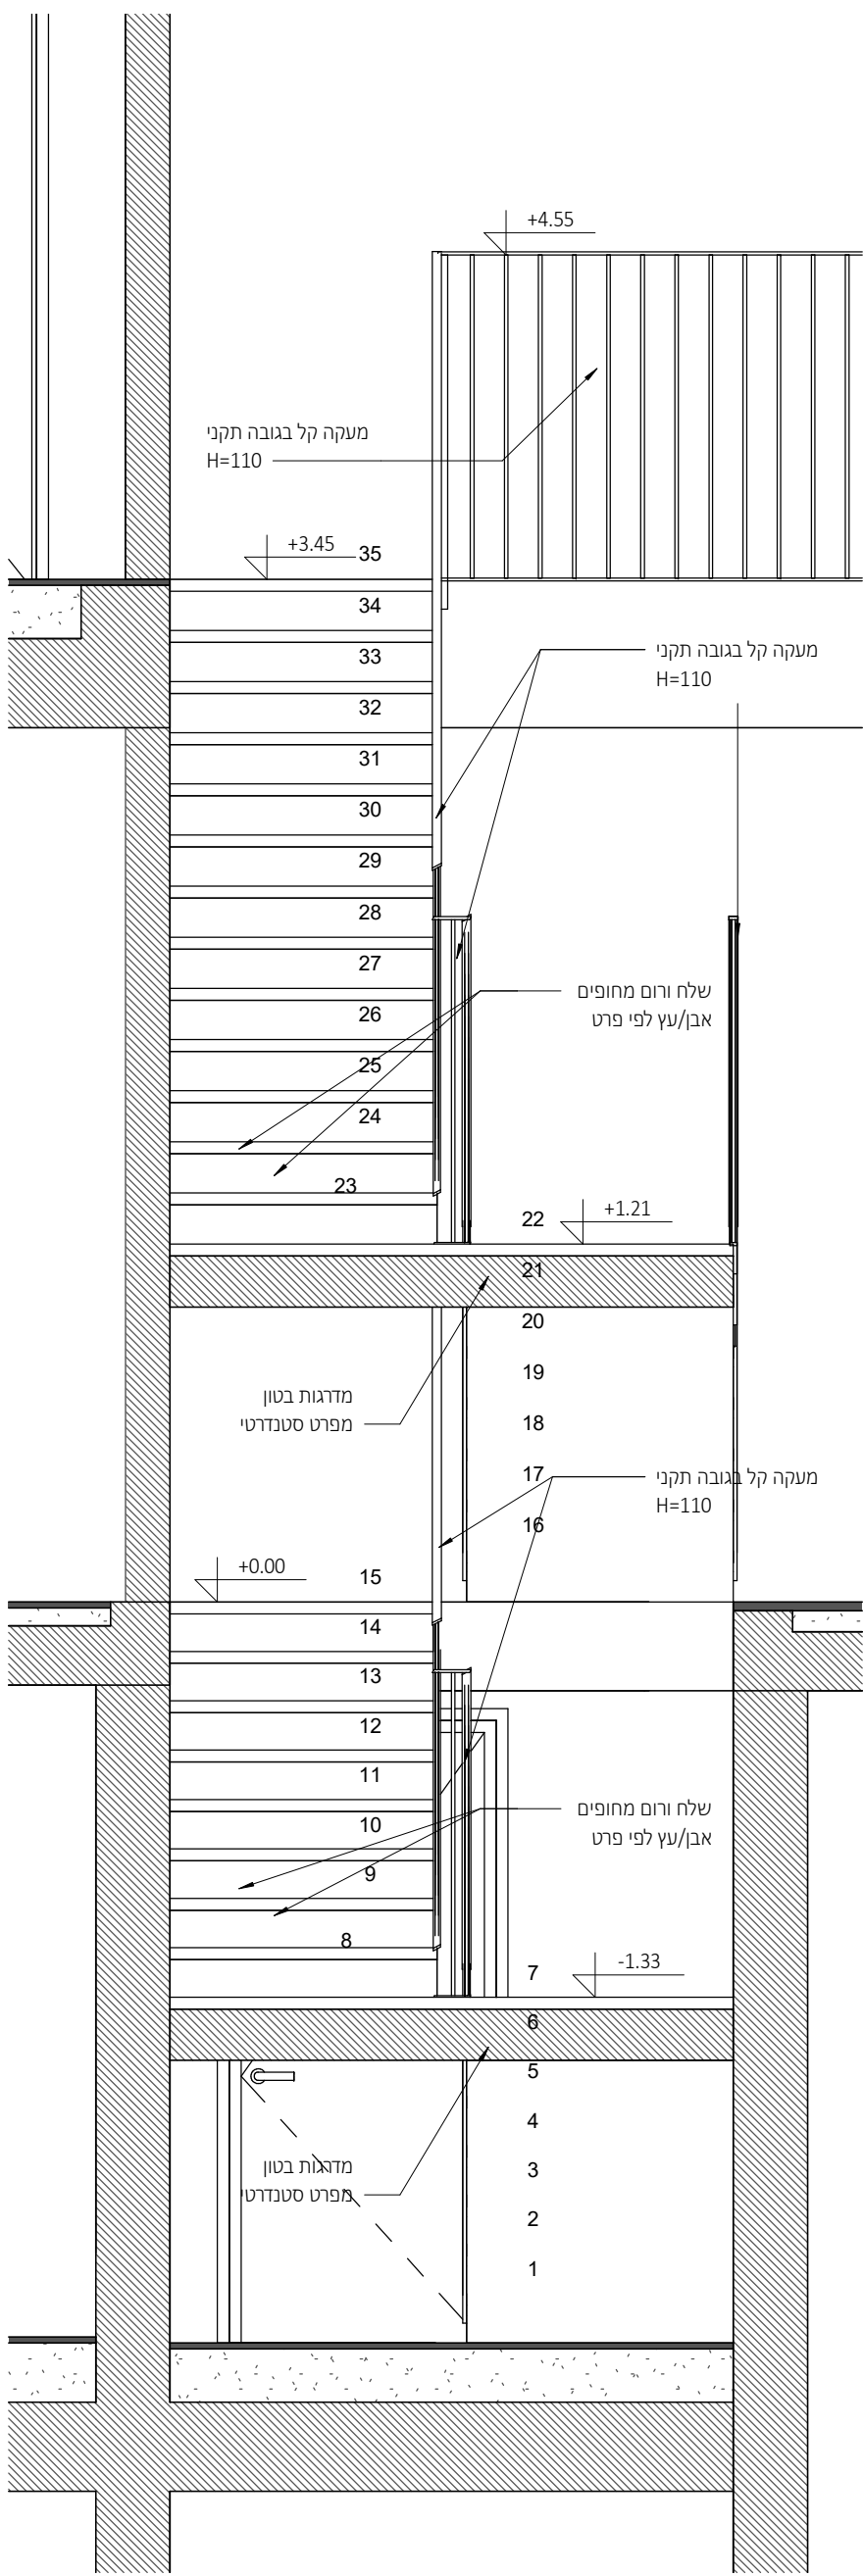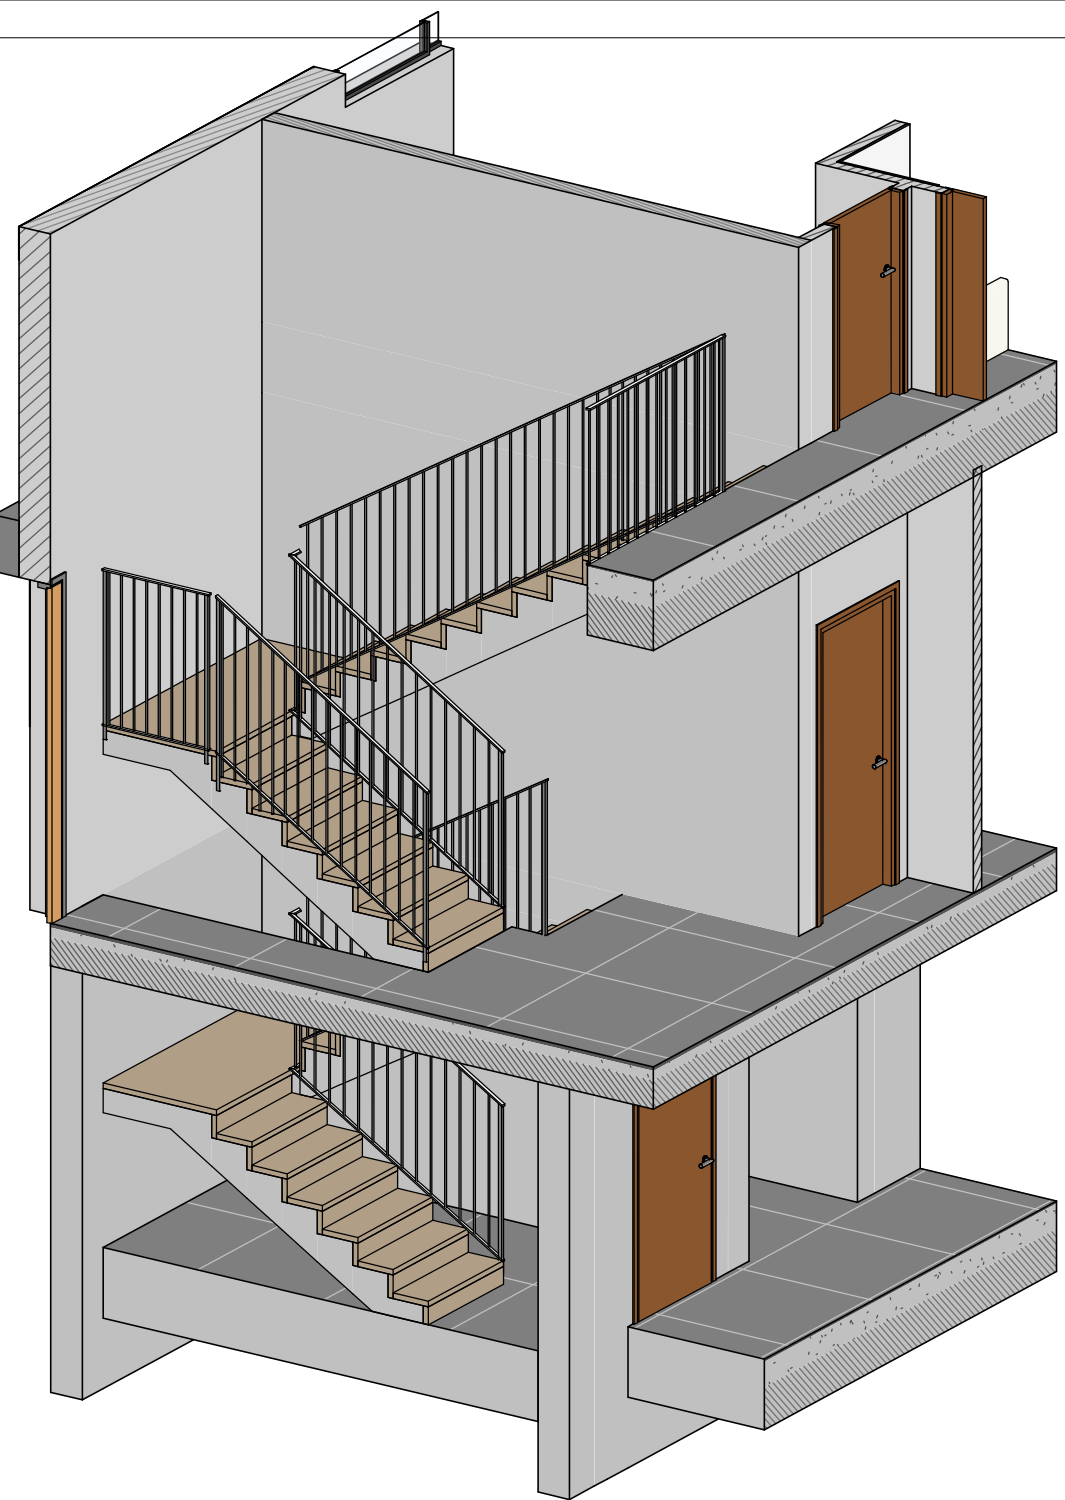

ניהול פרויקט
מהיסוד בן שלומון
פיקוח
מהיסוד - בן שלומון
קונסטרוקציה
ערן שילר
מיזוג אוויר
אייל ארז מהנדסים ויועצים בע"מ
אינסטלציה
איתן אלמסי
חשמל
איתן בסיס
אלומיניום
נוף
נתי בלוקא
חשמל חכם
חימום תת רצפתי
איטום
צבי טל
אקוסטיקה
מעליות
קרקע וביסוס
דיה הנדסת קרקע וביסוס
רישוי

[illegible][illegible]

CLIENT NAME: _____ שם המזמין:

PROJECT NAME: _____ ת. הפרויקט: _____

DRAWING NAME: ס הגליון:

HEET NUMBER: 190 גליון:

SCALE:	קנה מידה:	EDITION:	דפוס:
--------	-----------	----------	-------

למכר

DATE: 22.09.2025




NeumanHaynerArchitects

office@nh-arch.com
www.nh-arch.com


זכויות ייצור / ע"פ הנחיות עו"ד



1 : 10

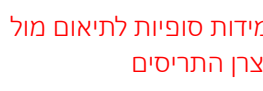


1 : 10

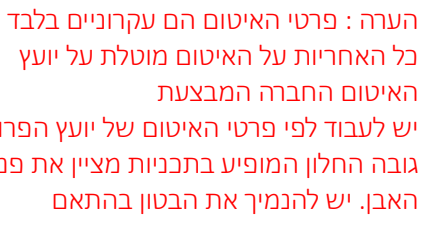


פרט עקרוני בלבד - פרט סופי מספק החלונות

1 : 10

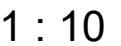


פרטי האיטום באחריות יועץ האיטום
ראה חוברת פרטי איטום מצורפת

להמשך תיאום

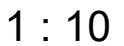

1 : 5

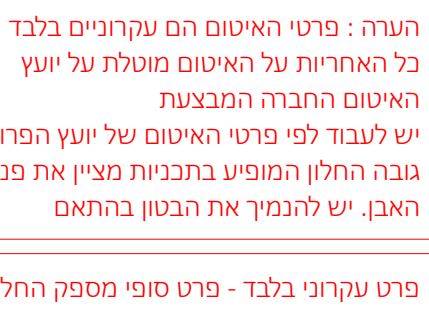

10	400	100	1	צלון רפפה חיצוני חשמלי + ארגז חיצוני	חלון הזזה פרופיל 7000 קליל
----	-----	-----	---	--------------------------------------	----------------------------

1	220	240	3	צלון רפפה חיצוני חשמלי + ארגז חיצוני	ויטרינה פרופיל 7500 קליל
2	480	240	1	צלון רפפה חיצוני חשמלי + ארגז חיצוני	ויטרינה פרופיל 7500 קליל
3	220	110	1	צלון רפפה חיצוני חשמלי + ארגז חיצוני	חלון הזהה פרופיל 7000 קליל
4	60	110	2	צלון רפפה חיצוני חשמלי + ארגז חיצוני	חלון קיפ פרופיל 4500 קליל

5	80	210	1	תריס גלילה חשמלי	דלת כנף פרופיל 4350 קליל
6	220	110	5	תריס גלילה חשמלי	חלון הזזה פרופיל 7000 קליל
7	75	110	1	תריס גלילה חשמלי	חלון קיפ פרופיל 4500 קליל
8	80	110	1	תריס גלילה חשמלי	חלון קיפ פרופיל 4500 קליל
9	60	110	1	תריס גלילה חשמלי	חלון קיפ פרופיל 4500 קליל

כל פריט יחולק למינימום הכנפיים האפשרי (לתיאום מול ספק האלומיניום ובמסגרת שרטוטי shop drawing)

0	140	240	1	דלת כניסה	דלת חוץ דגם גארדה
1	90	210	2	דלת פנים	דלת פנים "אקוודור" תוצרת חמדיה
2	80	210	8	דלת פנים	דלת פנים "אקוודור" תוצרת חמדיה
3	80	200	2		דלת פנים "אקוודור" תוצרת חמדיה

17/12/2025 10:25:50