
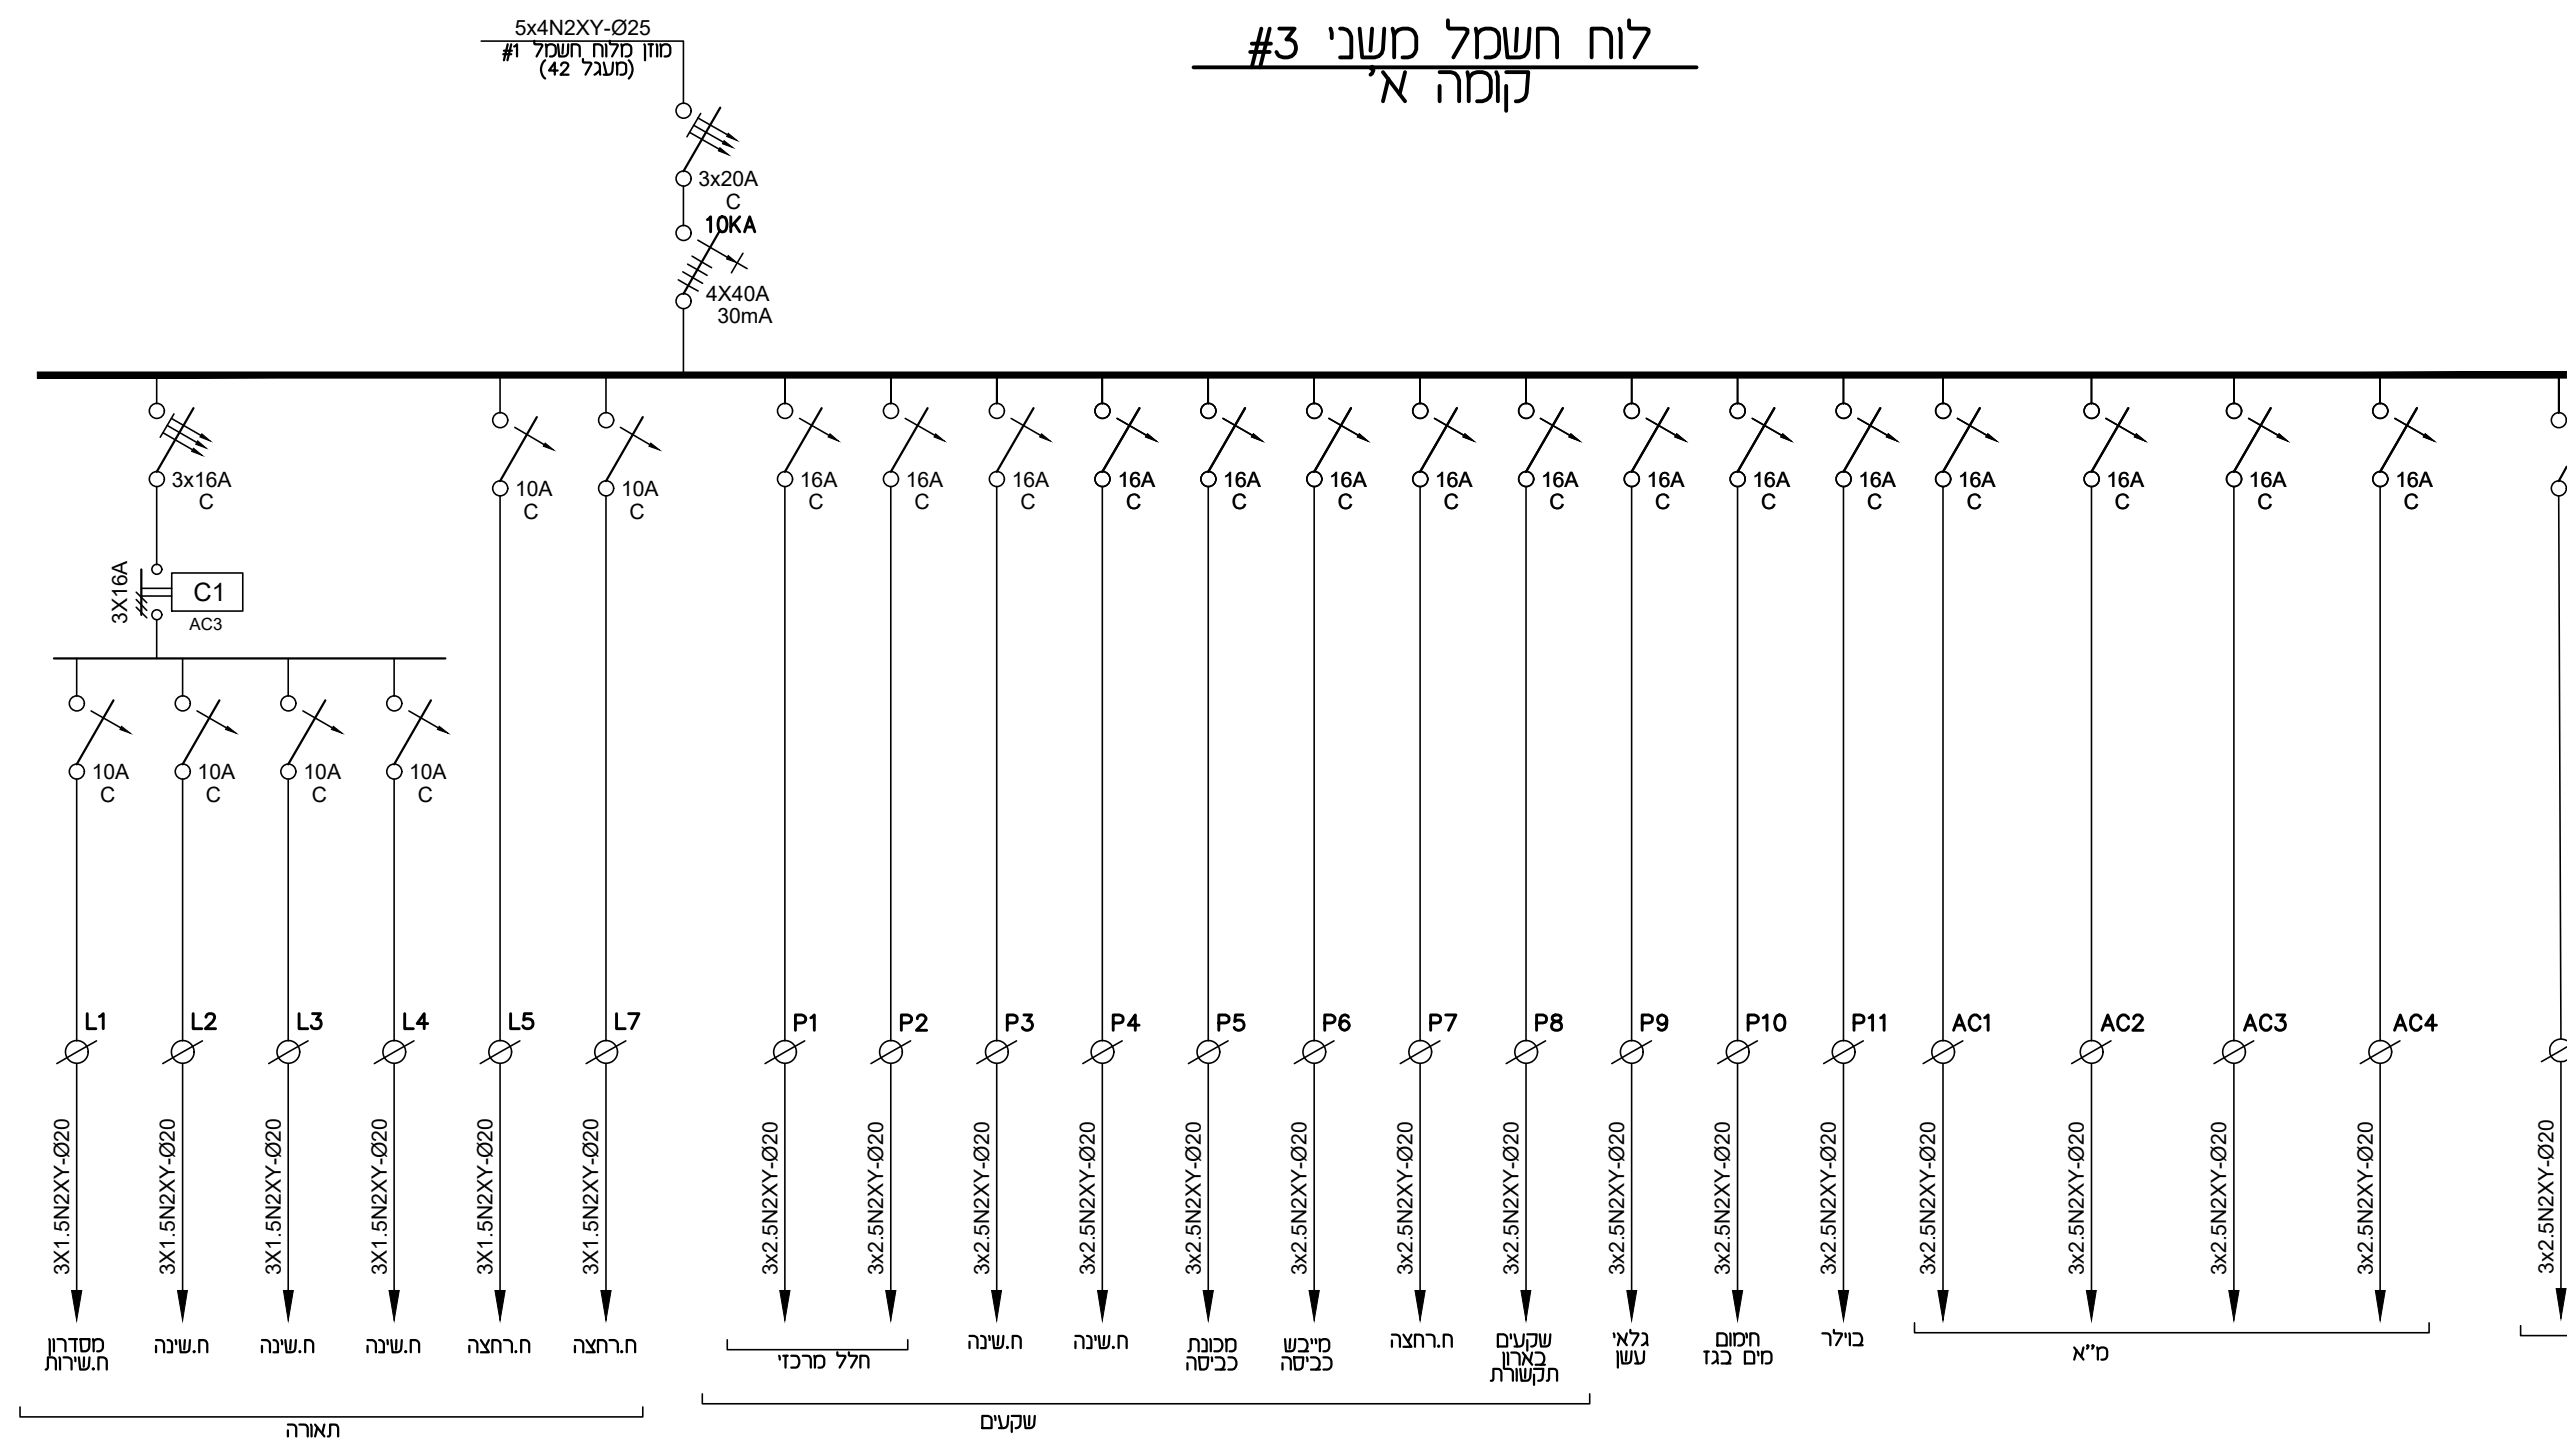
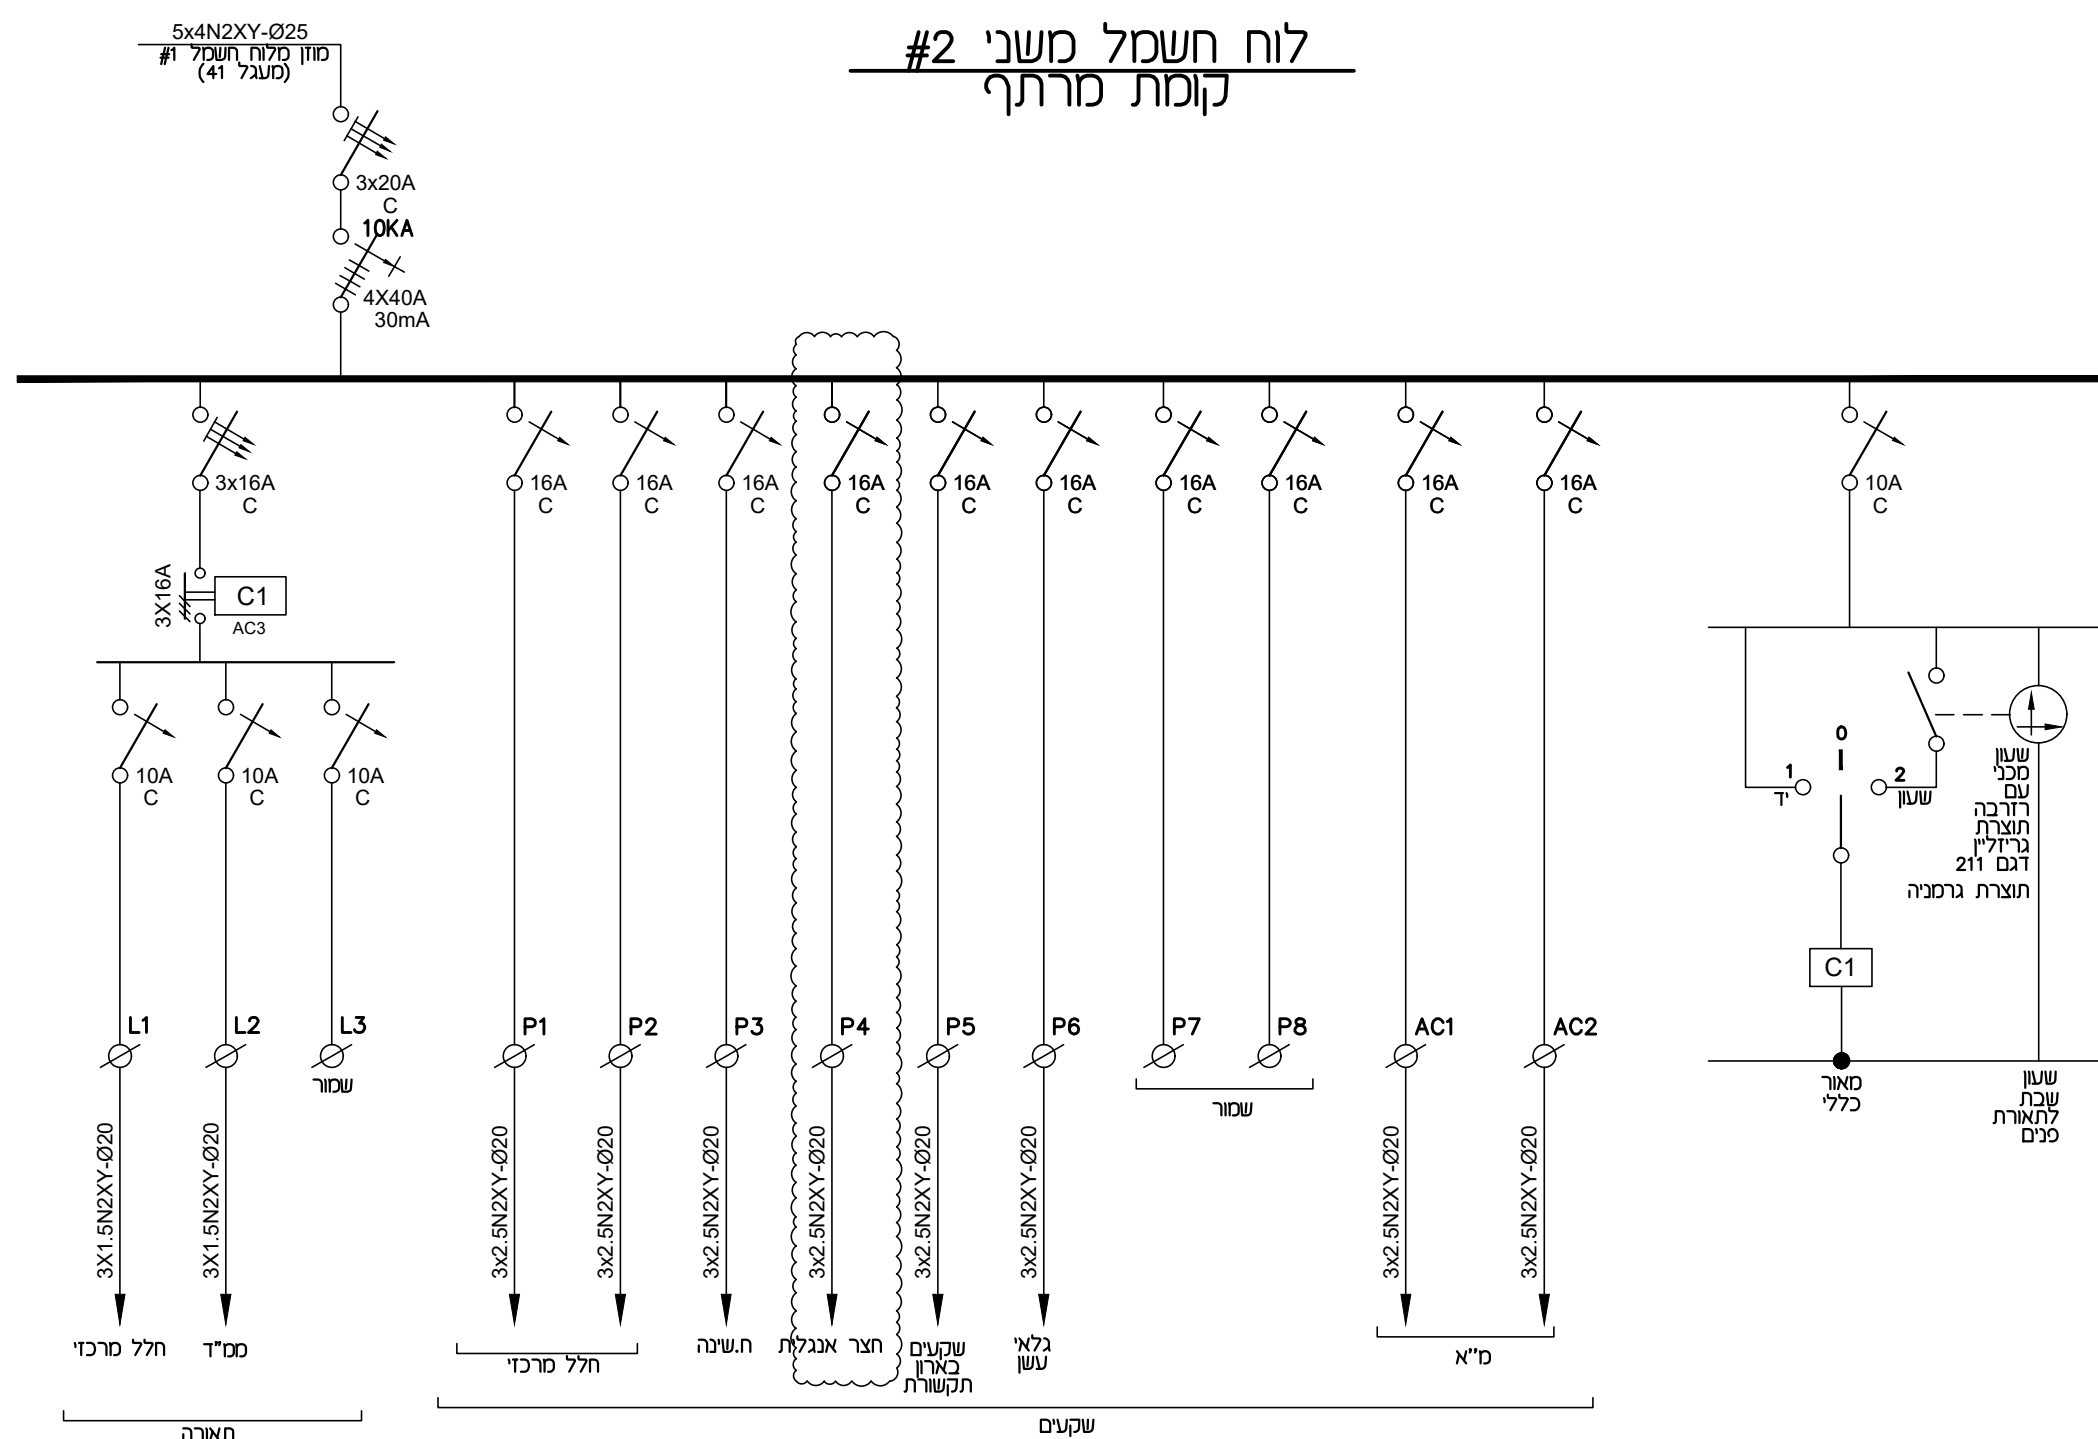


עודכן ע"י: _____ יפעת

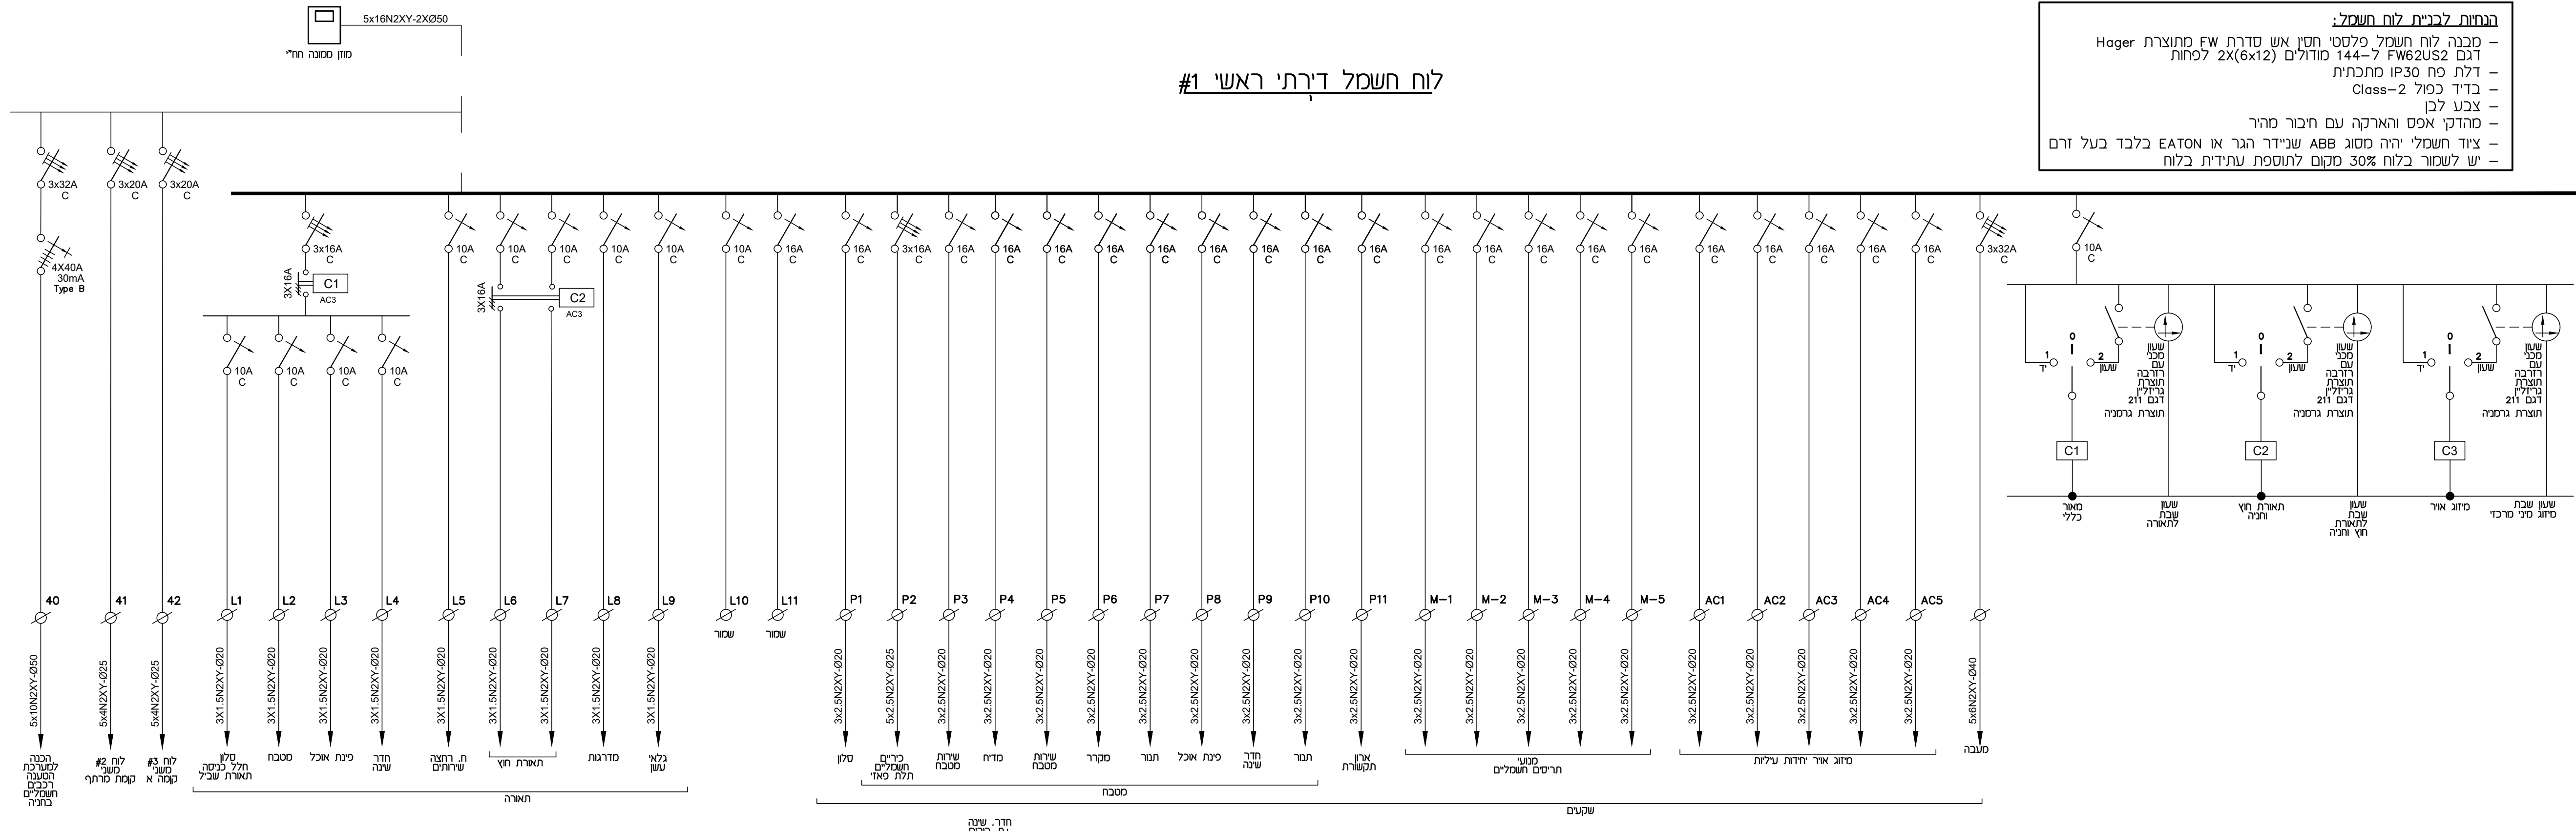

שם הפרויקט:

נופיה-אלפי מנשה

שם התכנית:

לוחות חשמל 3#,2#,#1
מגרש 13, נופיה

מס' עדכון:	מס' הגליון:	מס' הפרויקט:
0	13	675