

Court 13
Roof
Option No4

אדיינ פנים	
אינסטיציע	
בסירות אש	
אוטסטירע	
חשת ותאורה	
קונסטראקציע	
מבני ראשי	
ניווי פריונט	
לעוו	
אדיינ	

			4
חברות לא-שור	04.12.2024		4
חברות לעיון	13.11.2024		4
שנתיים:	חאיר:	סך:	



הערות

- ## מקרא

- מקרא צבעים בתכנית

- | | |
|--------------------------|---|
| תעלות ותריסי אוויר חוזר |  |
| תעלות ותריסי אספקת אוויר |  |
| תעלות ותריסי אוויר צח |  |
| תעלות ותריסי ניקת אוויר |  |
| תעלות ותריסי שיחרור עשן |  |
| צנרת גז וחשמל |  |
| סימון מעגלי מזוג אוויר |  |

191	מבני מגורים צמודי קרקע נופיה אפרי' מנשה מבנה 13
שם הפרויקט תאריך	שם הפרויקט תאריך
1:50 גרס'	מיזוג אוויר ואווירורר
04.12.2024 תאריך התכנון	גג קומה שנייה וקומת המרתף
2 מסלול	
☐ נכרוע ☐ למסד ☒ למישר	שם המבנה תאריך 13.11.2024 חנוכה 5785 אייל אדל

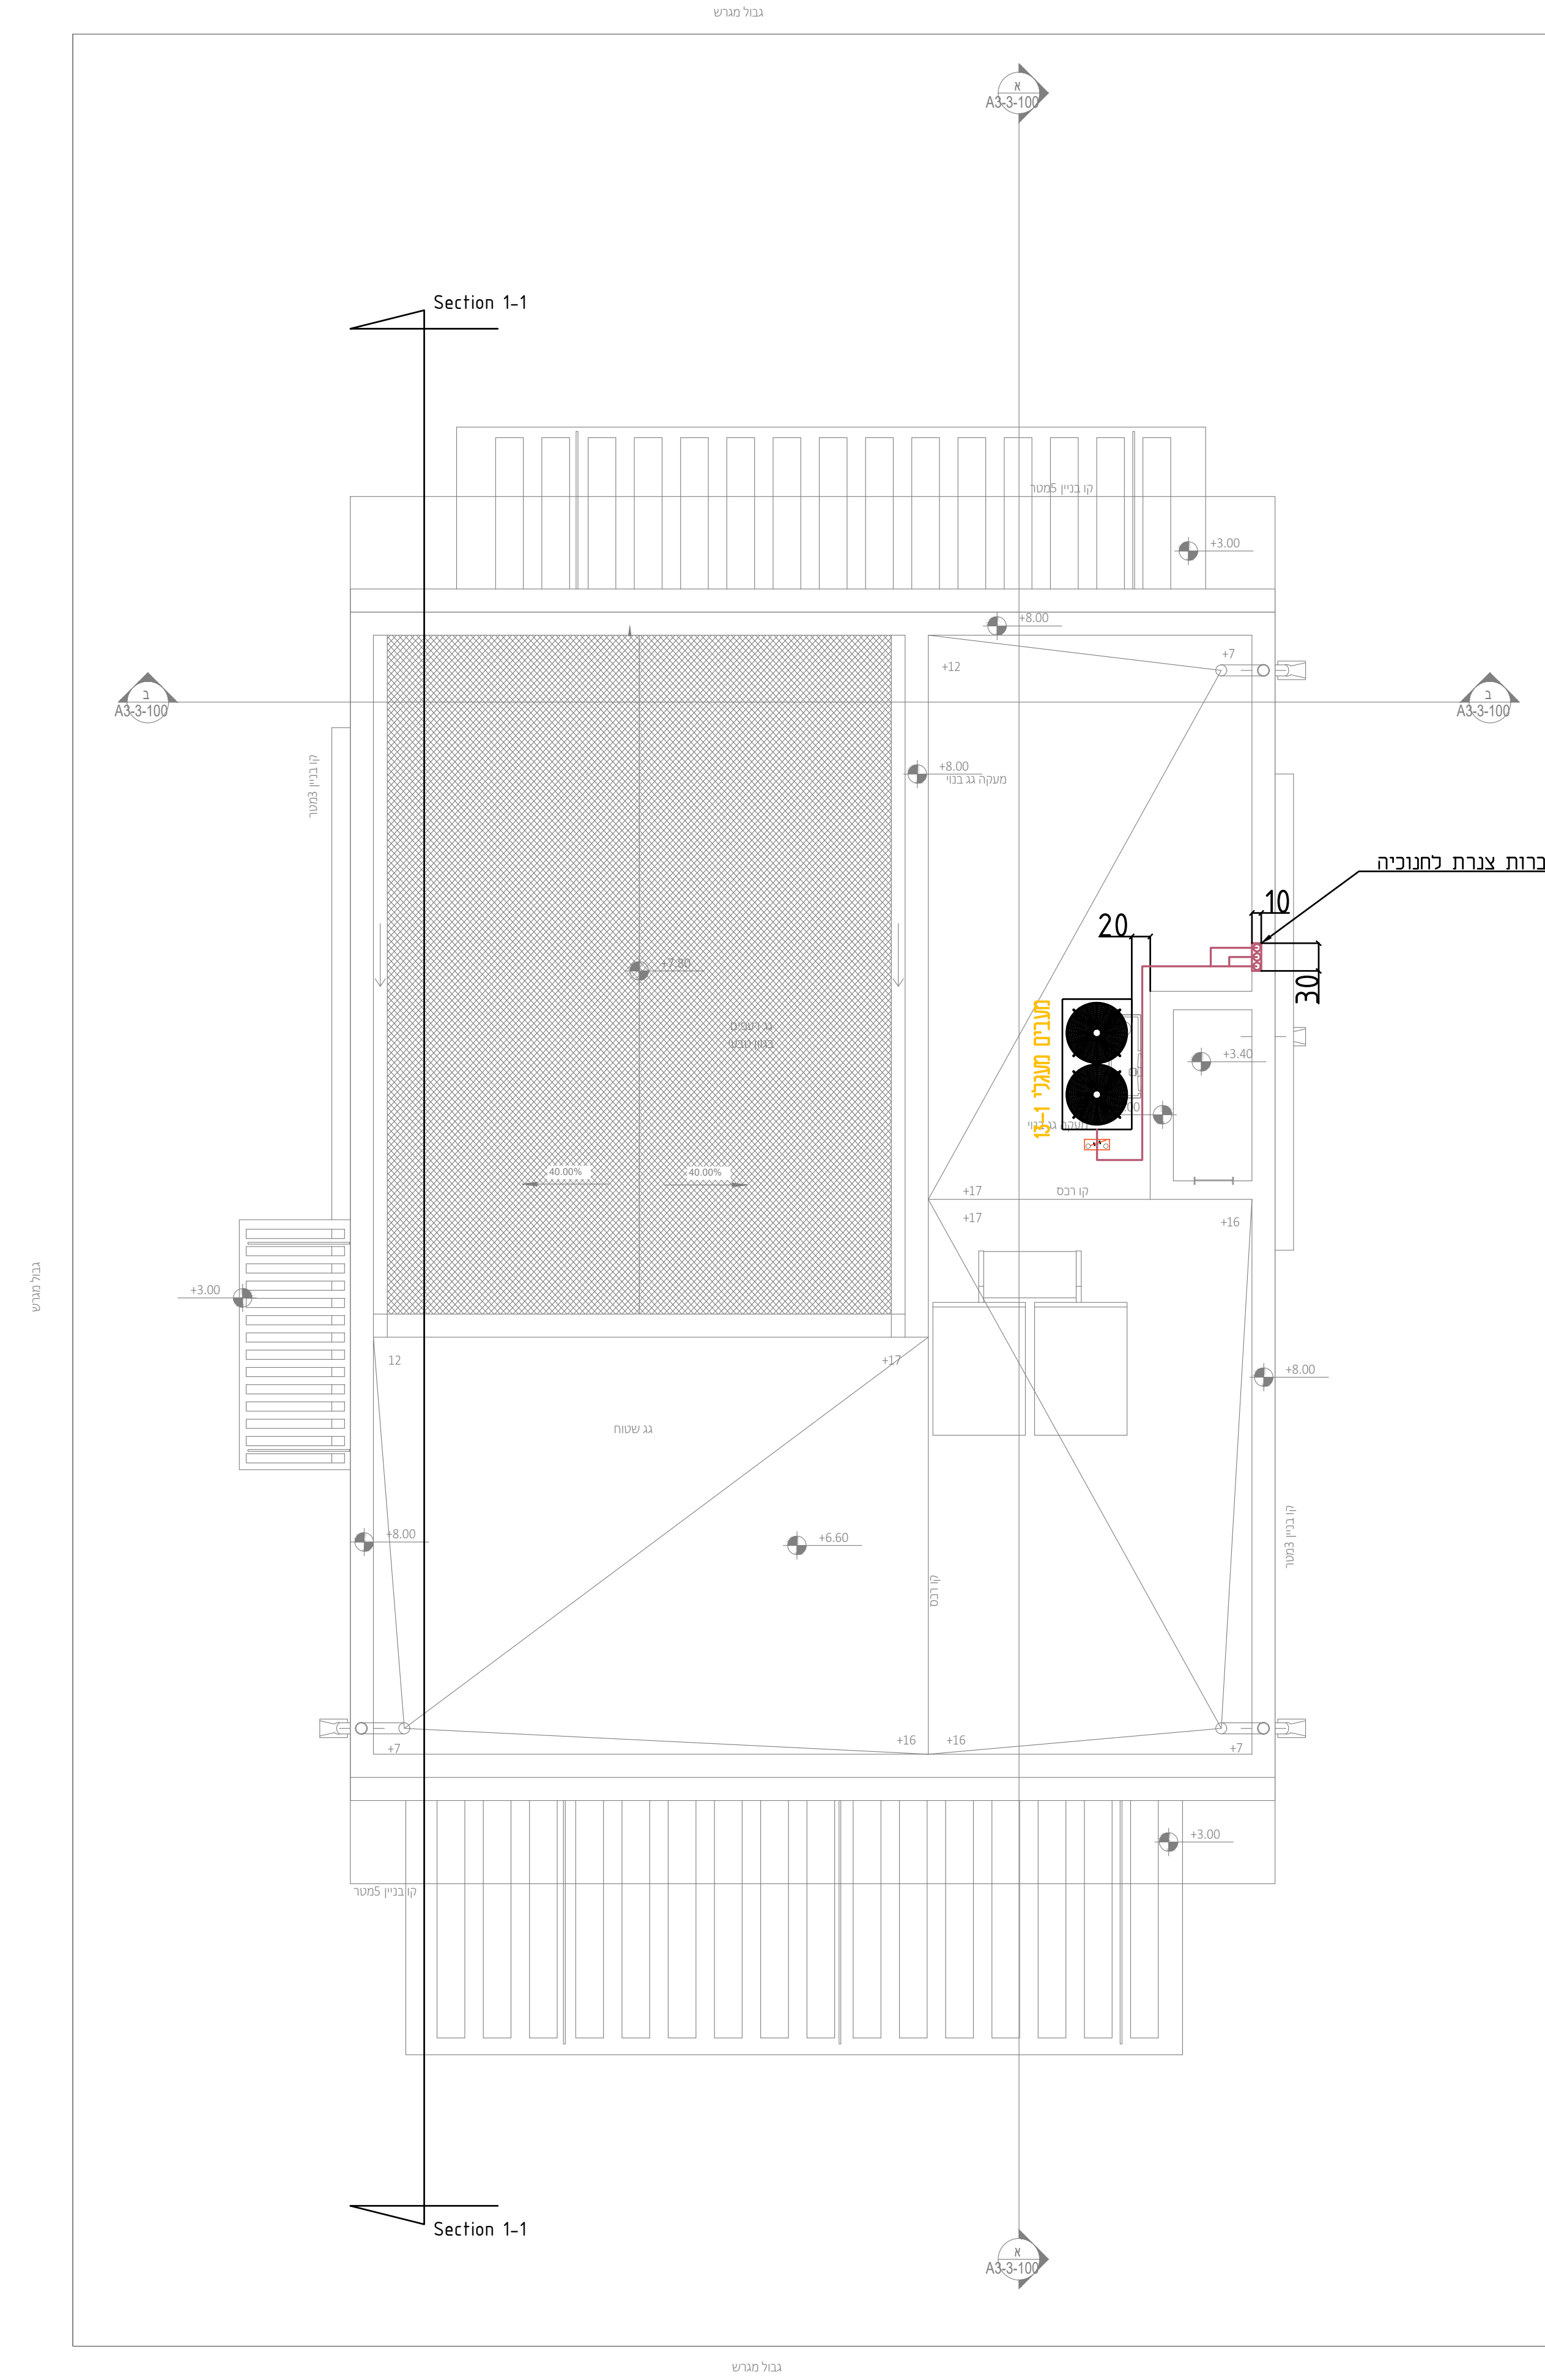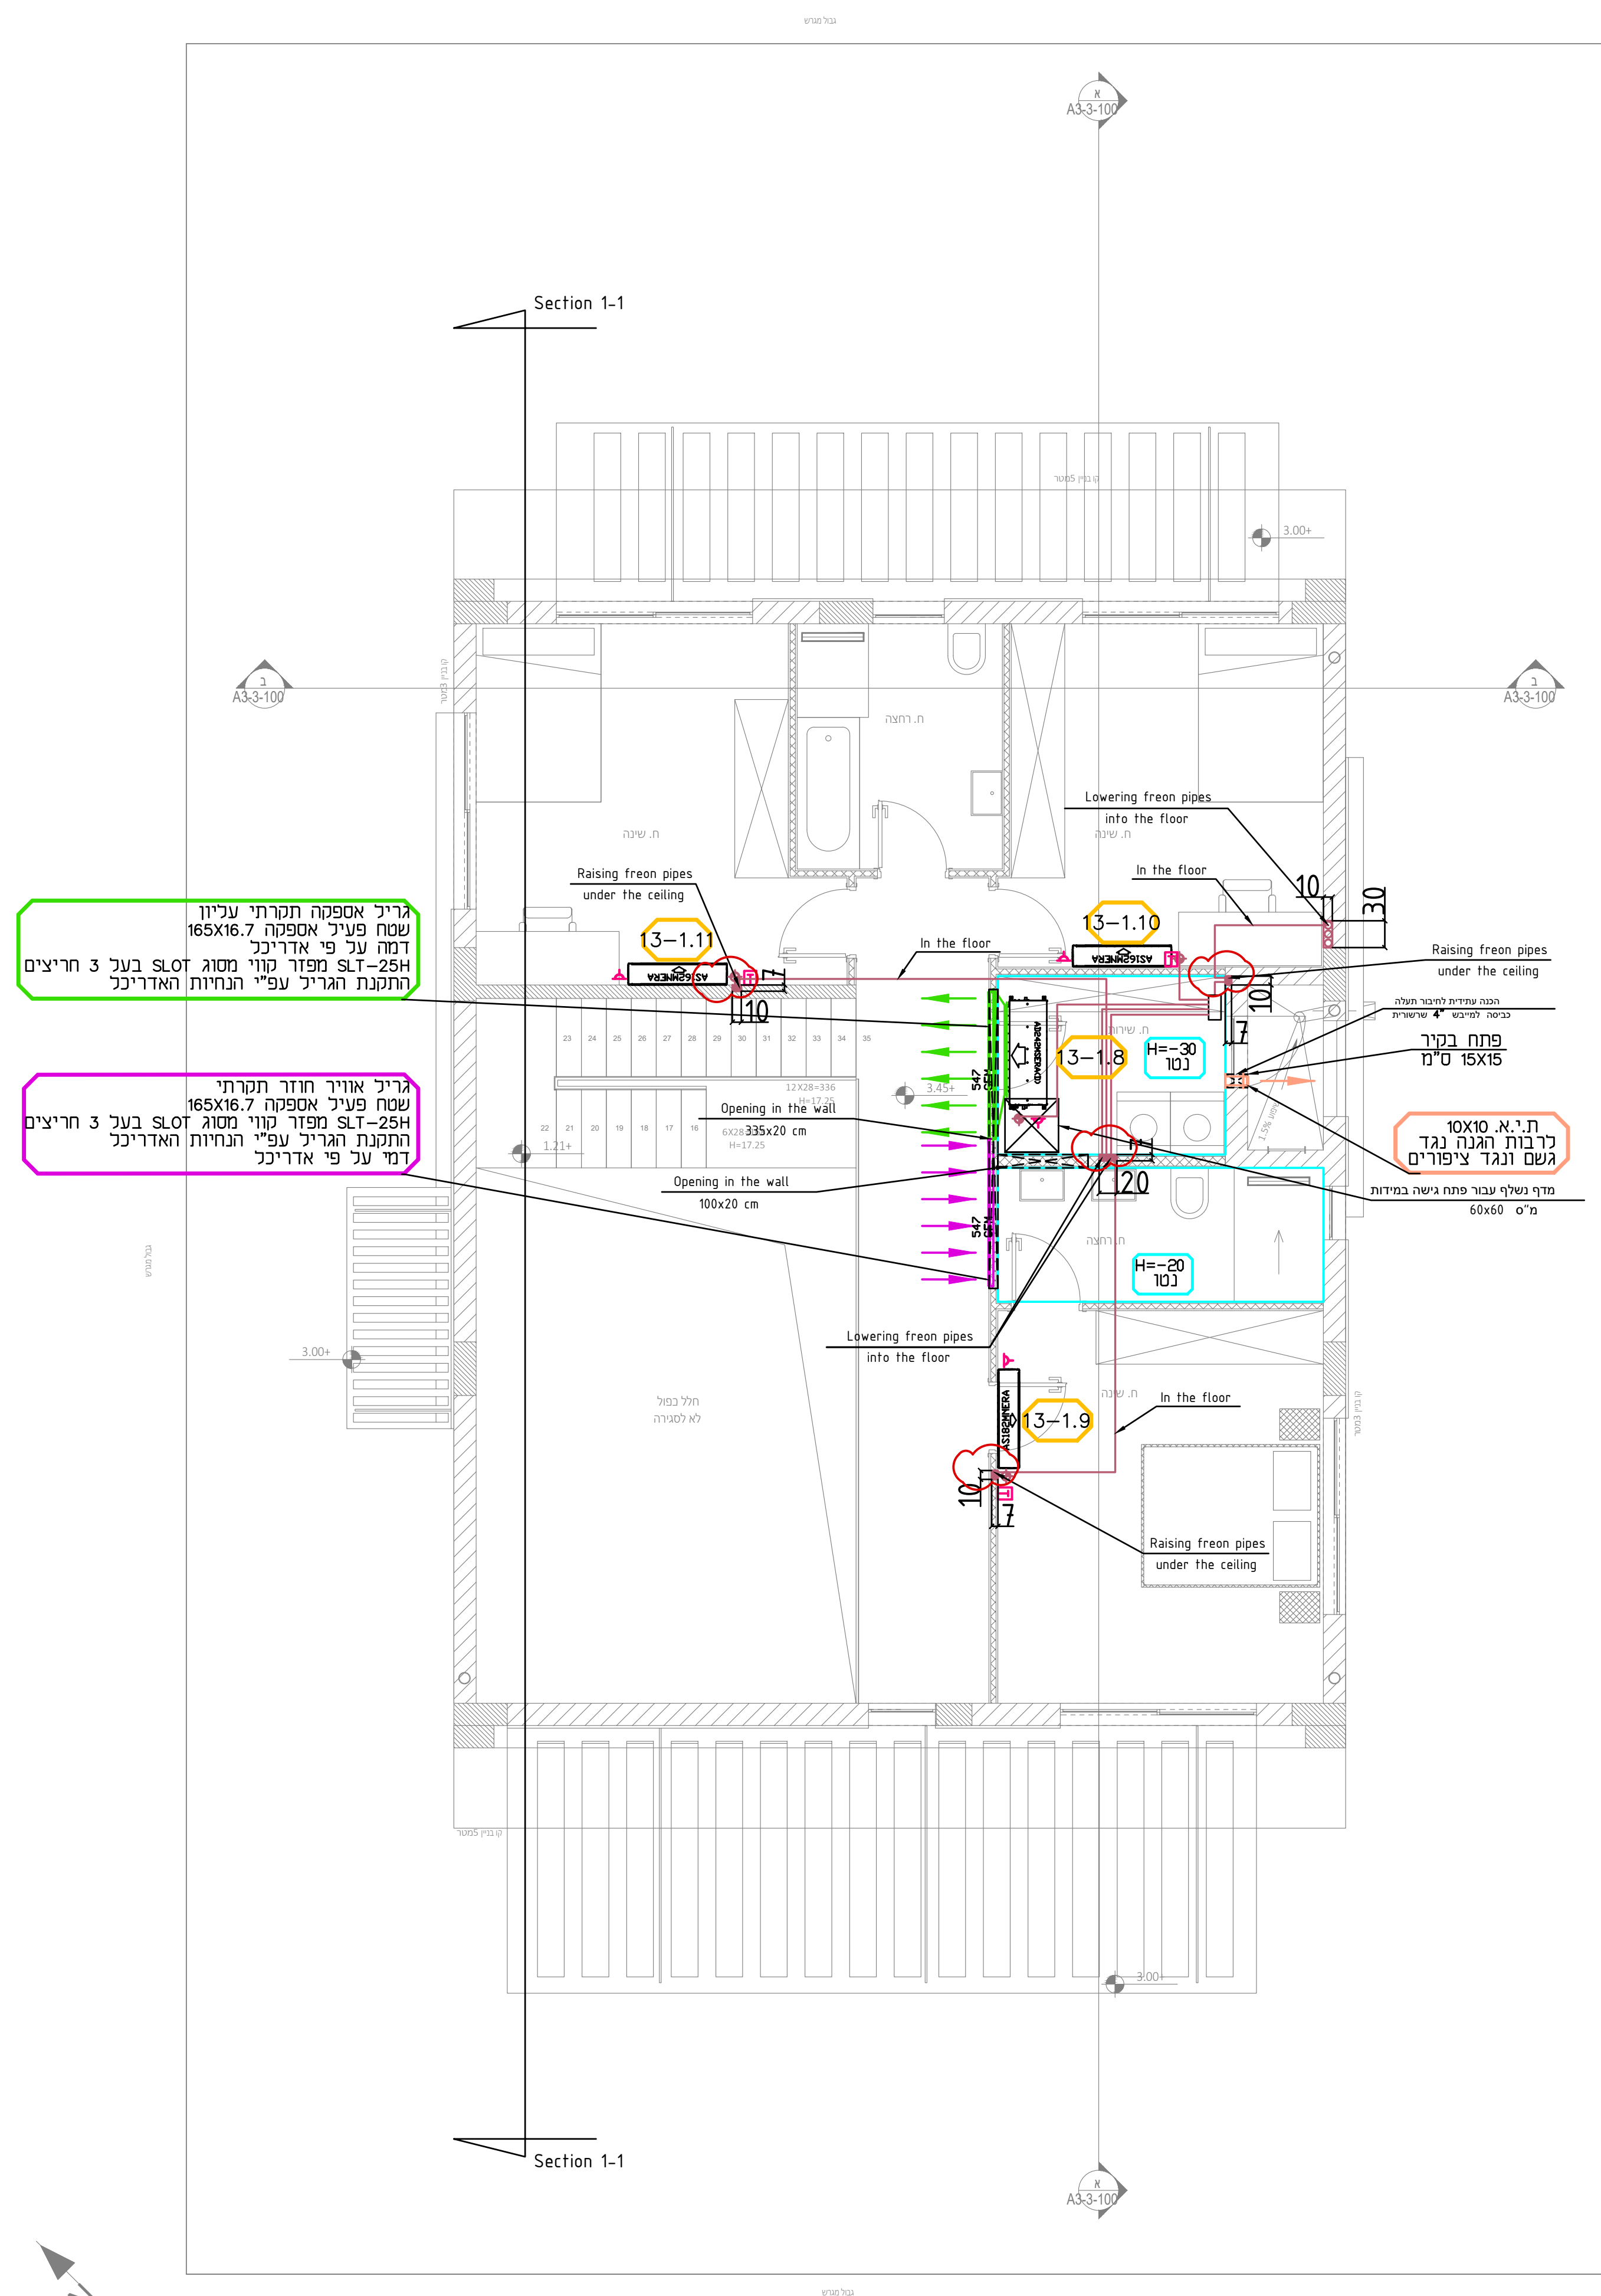

תפוצה

אוריכל פנים	
אינסטיציה	
בסיחת אש	
אקוסטיקה	
חשתי והזרה	
קונסטרוקציה	
קבלו ראש	
ניחול פרויקט	
נמח	
אוריכל	

מהדורה

		⚠
		⚠
חבנית כאשר	04.12.2024	⚠
חבנית רעיון	13.11.2024	⚠
שנתיים:	חאריץ:	סוף

המבצע אחראי למידות ולהתאמתן למציאות בכל מקרה של אי התאמה, סתירה או טעות עליו להודיע למתכנן לפני התקדמותו בביצועו אין לקבוע מידות על סמך מדיניות בשרטוט. אין לעשות כל שימוש בתוכנית זו ברעיונות הגלומים בה ללא אישור בכתב מאת המתכנן.

הערות

1. כל הבנייה מחוץ למבנה יבודרו
ברידור אקוטס' בעובי "2"
מידות העלעות ה מידות פח
2. תעלות מידות בתוך המבנה יבודרו
ברידור אקוטס' פנים "1"
מידות העלעות ה מידות פח
3. תעלות אוויר צה יבודרו
ברידור טומ "1"
מידות העלעות ה מידות פח
4. יש לאסוס בסיליקון פנית התיבור
ש תעלות מידות אוויר לפני כיפוף
הפנים המתחרים

מקרא


[illegible]

מקרא צבעים בתכנית

תעלות ותריסי אוויר חוזר	
תעלות ותריסי אספקת אוויר	
תעלות ותריסי אוויר צח	
תעלות ותריסי יניקת אוויר	
תעלות ותריסי שיחרור עשן	
צנרת גז וחשמל	
סימון מעגלי מיוזג אוויר	


191	מבני מקורים צמודי קרקע נופיה אפי' מנשה במנה 13
1:50	סליל
04.12.2024	מבטאים
2	מבטאים
☐ לבנים ☐ כסדר ☒ לאשר ☐ עיון	13.11.2024 חג המנוחות י"ז אדר

Court 13
Basement
Option ~~No~~4

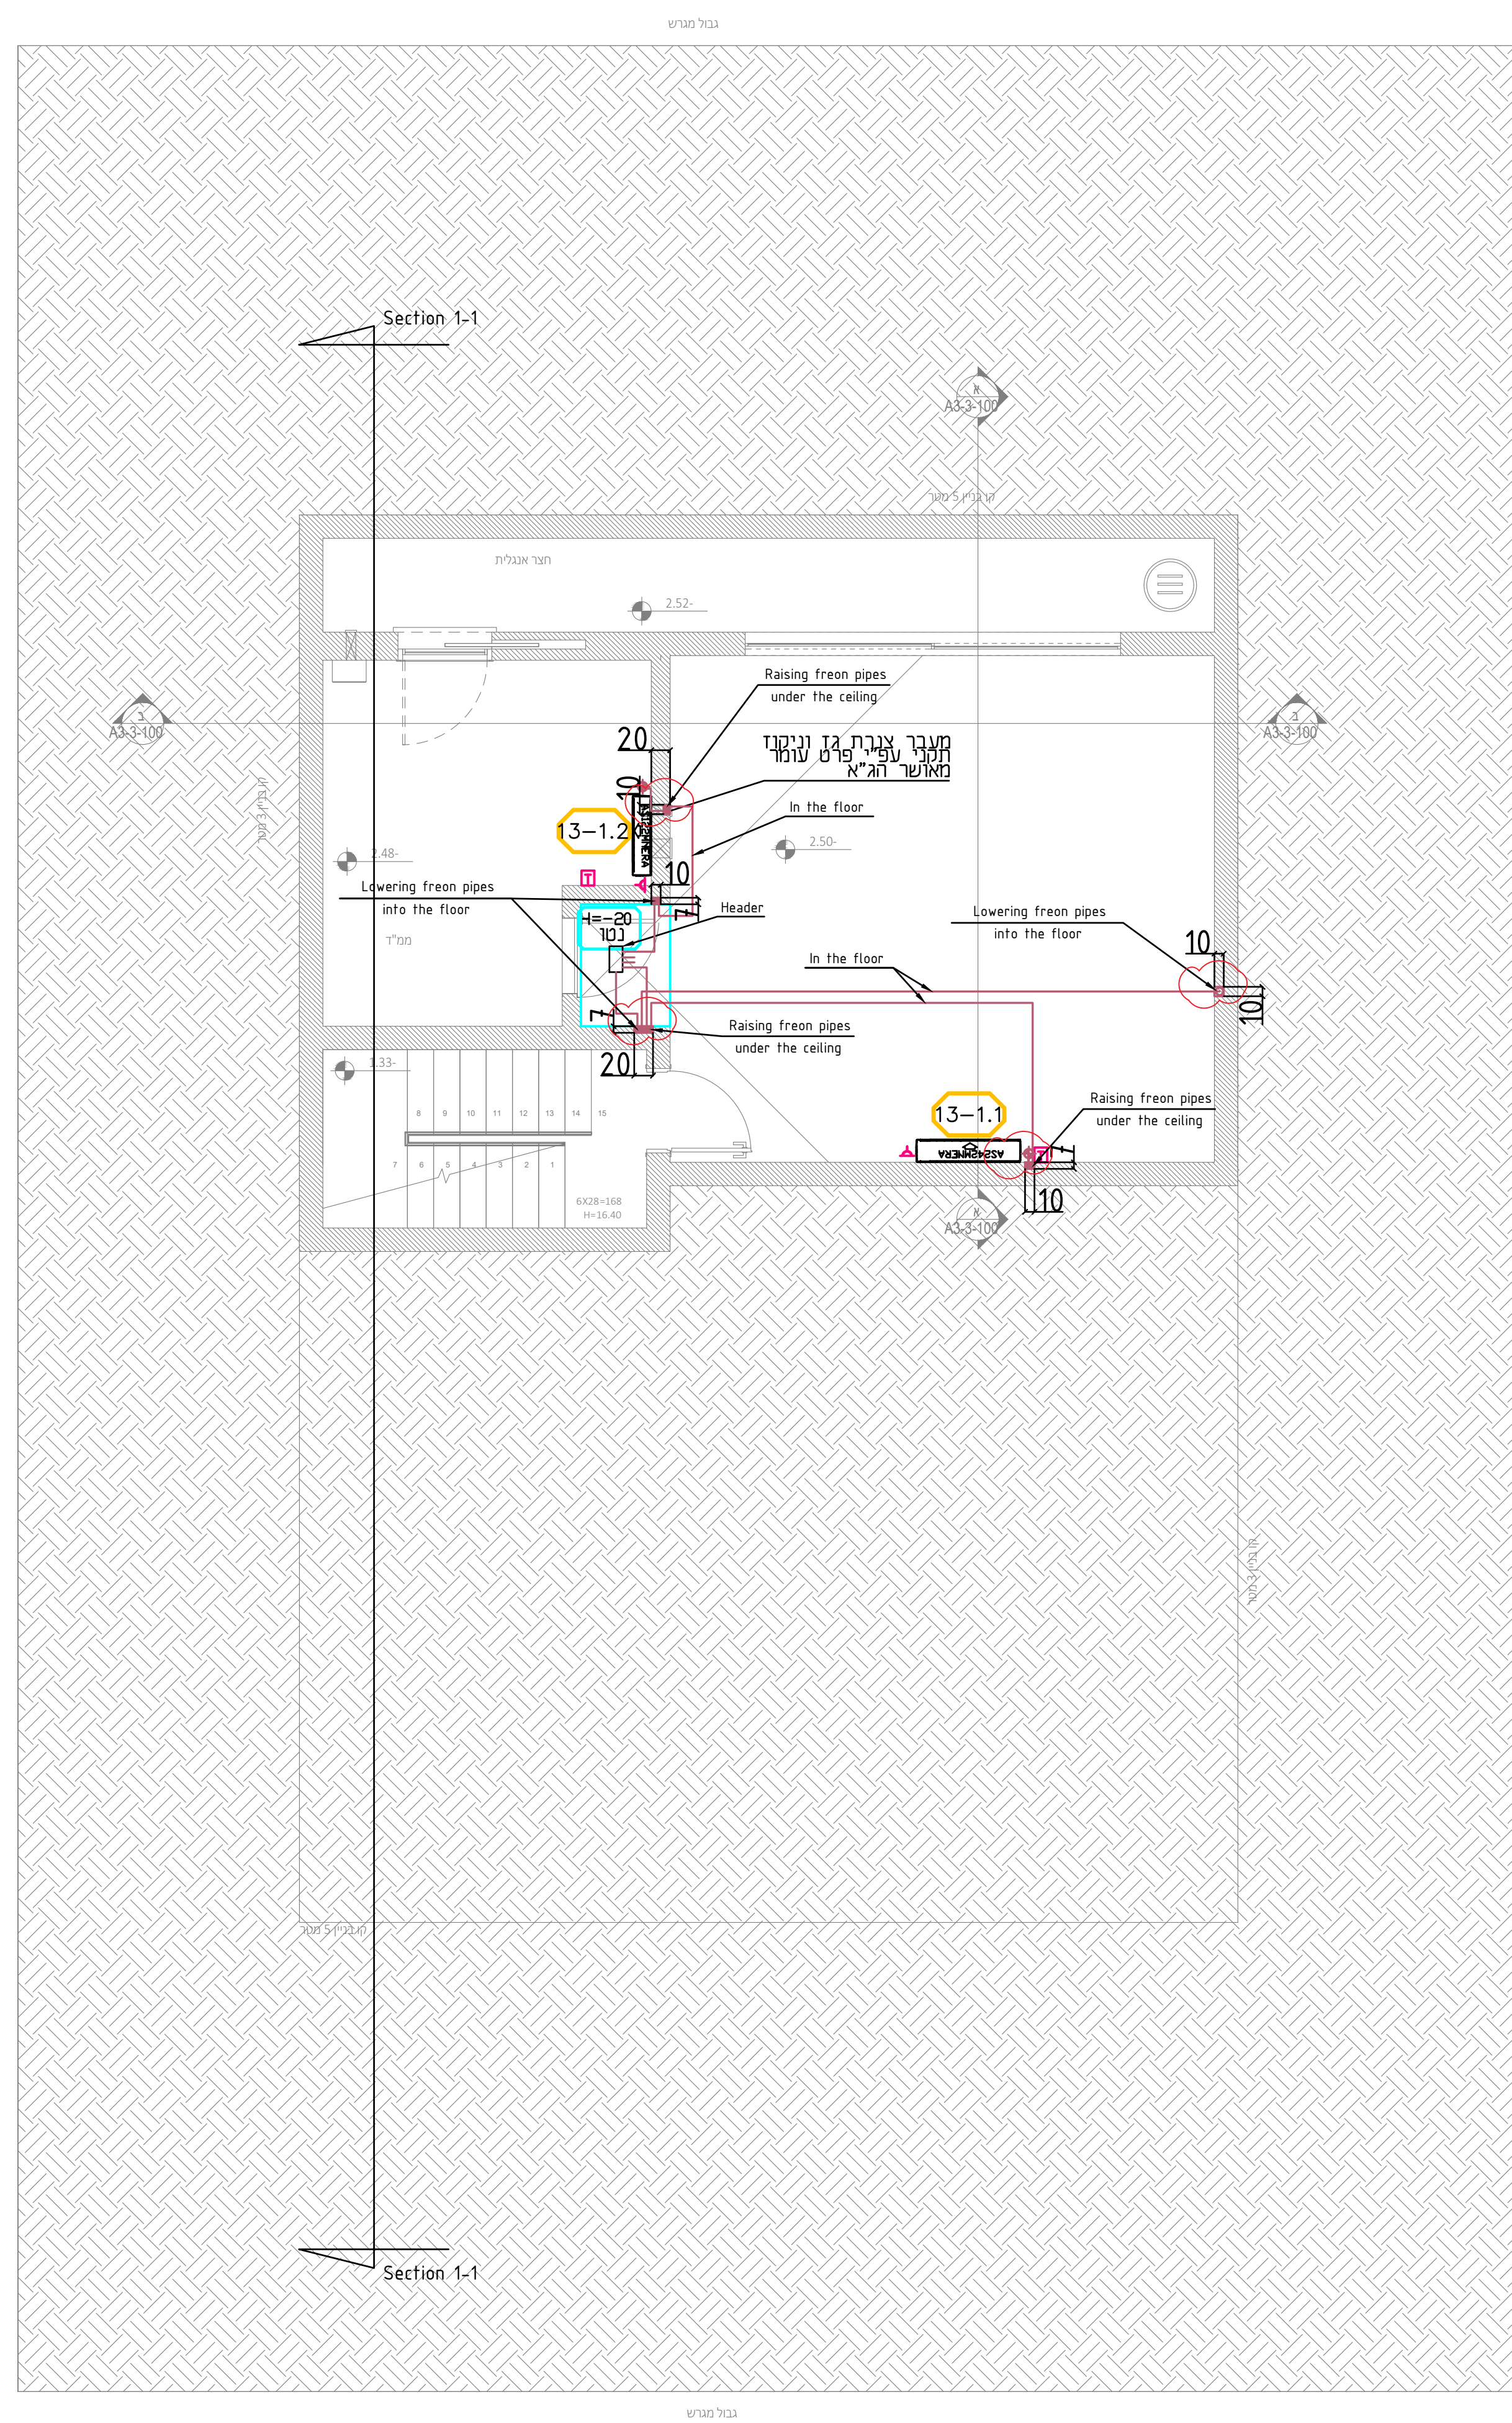

פתחי גישה אופן ארט בתיאום סופי מול אדריכל
כלל יחידות המיזוג אשר נמצאות בתוך נגרות יש לתאם סופית מול אדריכל ונגרות

Court 13
1st Floor
Option **No**4

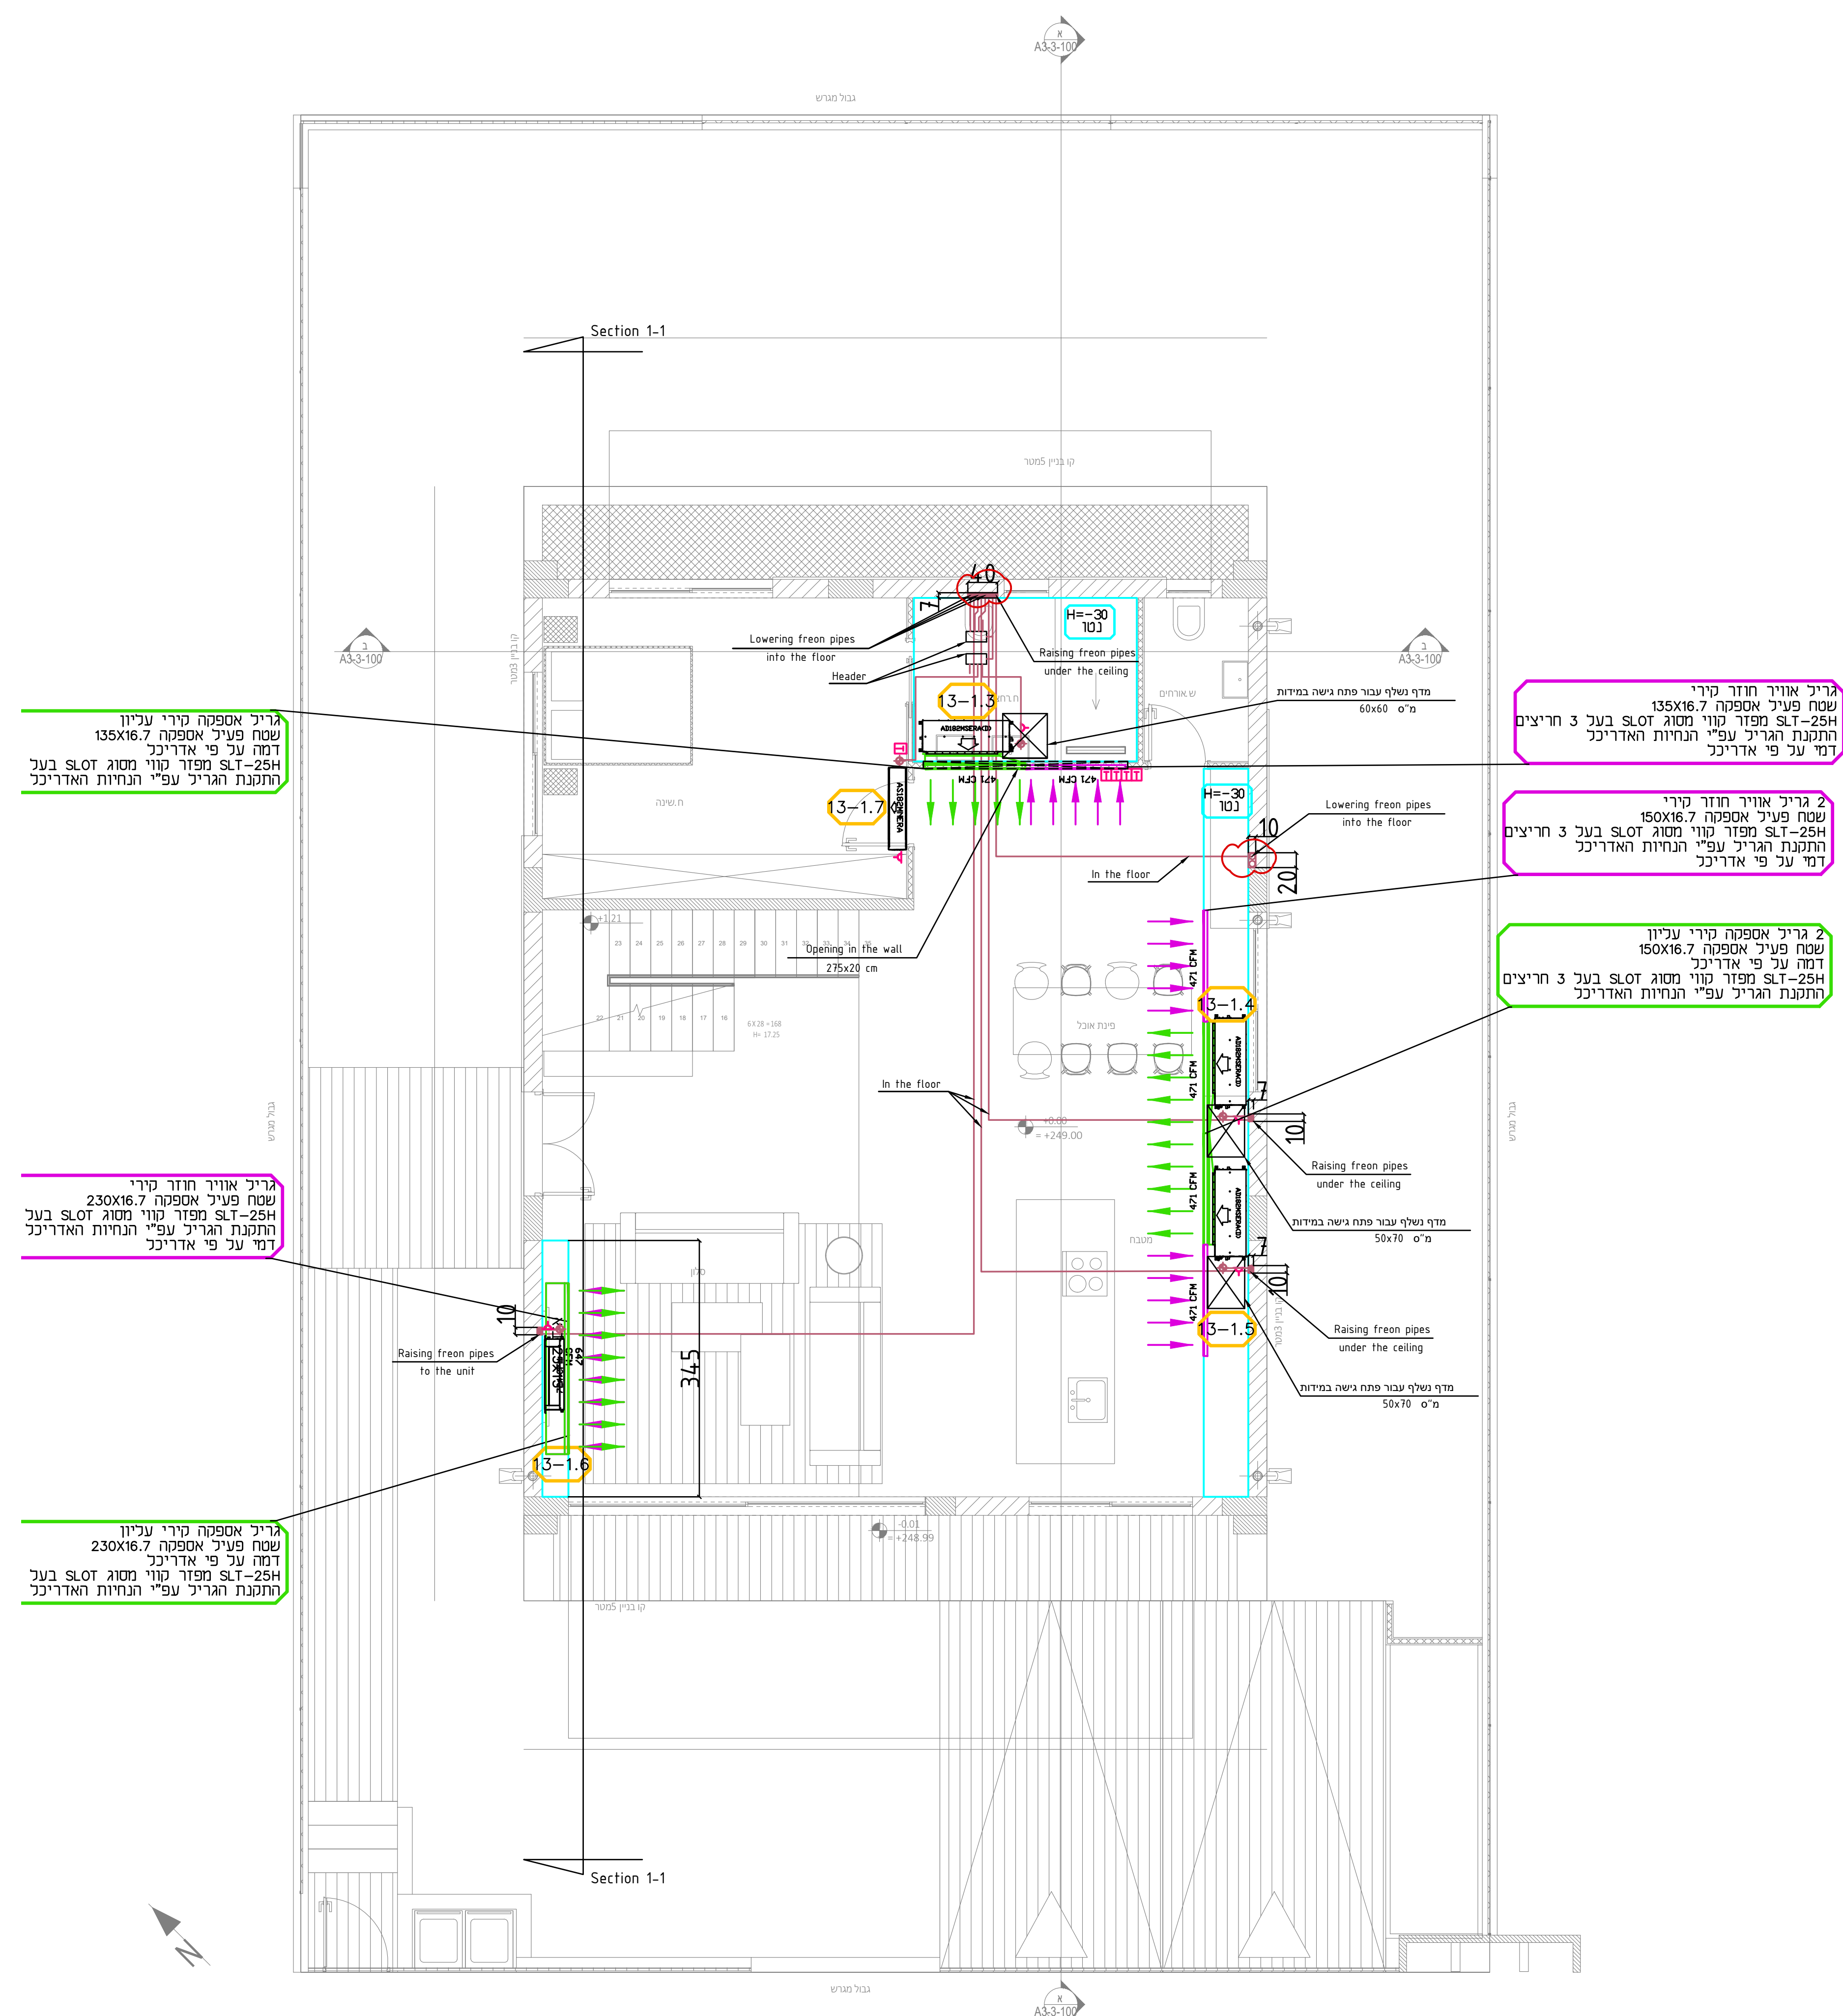

תפוצה

אורינג	
קעז	
נירויט פרינקט	
קבינ ראש	
קונסטראקציע	
חשמל ווארע	
אווסטיקע	
בסירות אש	
אינסטליציע	
אדוויי פנים	

מהדורה

			⚠
			⚠
תכנית ראשון	04.12.2024		⚠
תכנית רעיון	13.11.2024		⚠
שנתיים:	חמ"ד:	סל:	

המבצע אחראי למידות ולהתאמתו למציאות בכל מקרה של אי התאמה, סתירה או טעות. עליו להודיע למתכנן לפני התקדמותו בביצועו. אין לקבוע מידות על סמך מדידה בשרטוט. אין לעשות כל שימוש בתוכנית זו או ברעיונות הגלומים בה ללא אישור בכתב מאת המתכנן.

הערות

1. כל התעלות מחזי למננה יבדורו
בבידור אקוסט² מידות
מידות התעלות הן מידות פח
2. תעלות מזוג בתור המבנה יבדורו
בבידור אקוסט³ פנים⁴
מידות התעלות הן מידות פח
3. תעלות אוויר צח יבדורו
בבידור טרמי⁵
מידות התעלות הן מידות פח
4. יש לאסוס בסיליקון את פינות החיבור
של תעלות מיד אוויר לפני כיפוף
החפים המתחברים

מקרא

- | | |
|--------------------------|---|
| פנ-פנח | פנח |
| מ.א.ג. - מפדז אוויר כירי | |
| מ.א.ג. - מפדז אוויר תחזק | |
| ת.א.ג. - תריס אוויר תחזק | |
| ת.א.ג. - תריס אוויר צח | |
| ב.א. - בידוד אקסט | |
| ב.ט. - בידוד טרז | |
| ג.ב. - גלבי בידוד | |
| ד.א. - דתפרז אש | |
| |  סרומטס נדח הפעלה |
| | שקע עשמה תרפוז יועג חשמה |
| |  שקע תרת פאזי תרפוז יועג חשמה |
| | פסקס בחסוך חד פאזי תרפוז יועג חשמה |
| |  פסקס בחסוך תרת פאזי תרפוז יועג חשמה |
| | ניקוז חאמיר תרפוז יועג אקסטנציע |
| |  גובה 20 ס"מ מחתחית גובה המאפיד |
| | שלס הפעילה אלוחס |
| |  |


מקרא צבעים בתכנית

- | | |
|---------------------------|---|
| תעלות ותרסיסי אוויר תוזר |  |
| תעלות ותרסיסי אספקת אוויר |  |
| תעלות ותרסיסי אוויר צח |  |
| תעלות ותרסיסי ניקת אוויר |  |
| תעלות ותרסיסי שיחרור עשן |  |
| צנרת גז וחשמל |  |
| סימון מעגלי מזווג אוויר |  |


191	מבני מגורים צמודי קרקע נופיה אפרי' מנשה מבנה 13
1:50	מיוזג אוויר ואווירור
04.12.2024	קומת מרתף וקומה ראשונה
החיר מחלוקה	מס' תעודת
2	
מחלוקה	מס' תעודת
☐ כניסה ☐ למסדר ☒ למשור	☐ תענין 13.11.2024 זמן אדון

כלל יחידות המיזוג אשר נמצאות בתוך נגרות יש לתאם סופית מול אדריכל ונגרות

Option No4

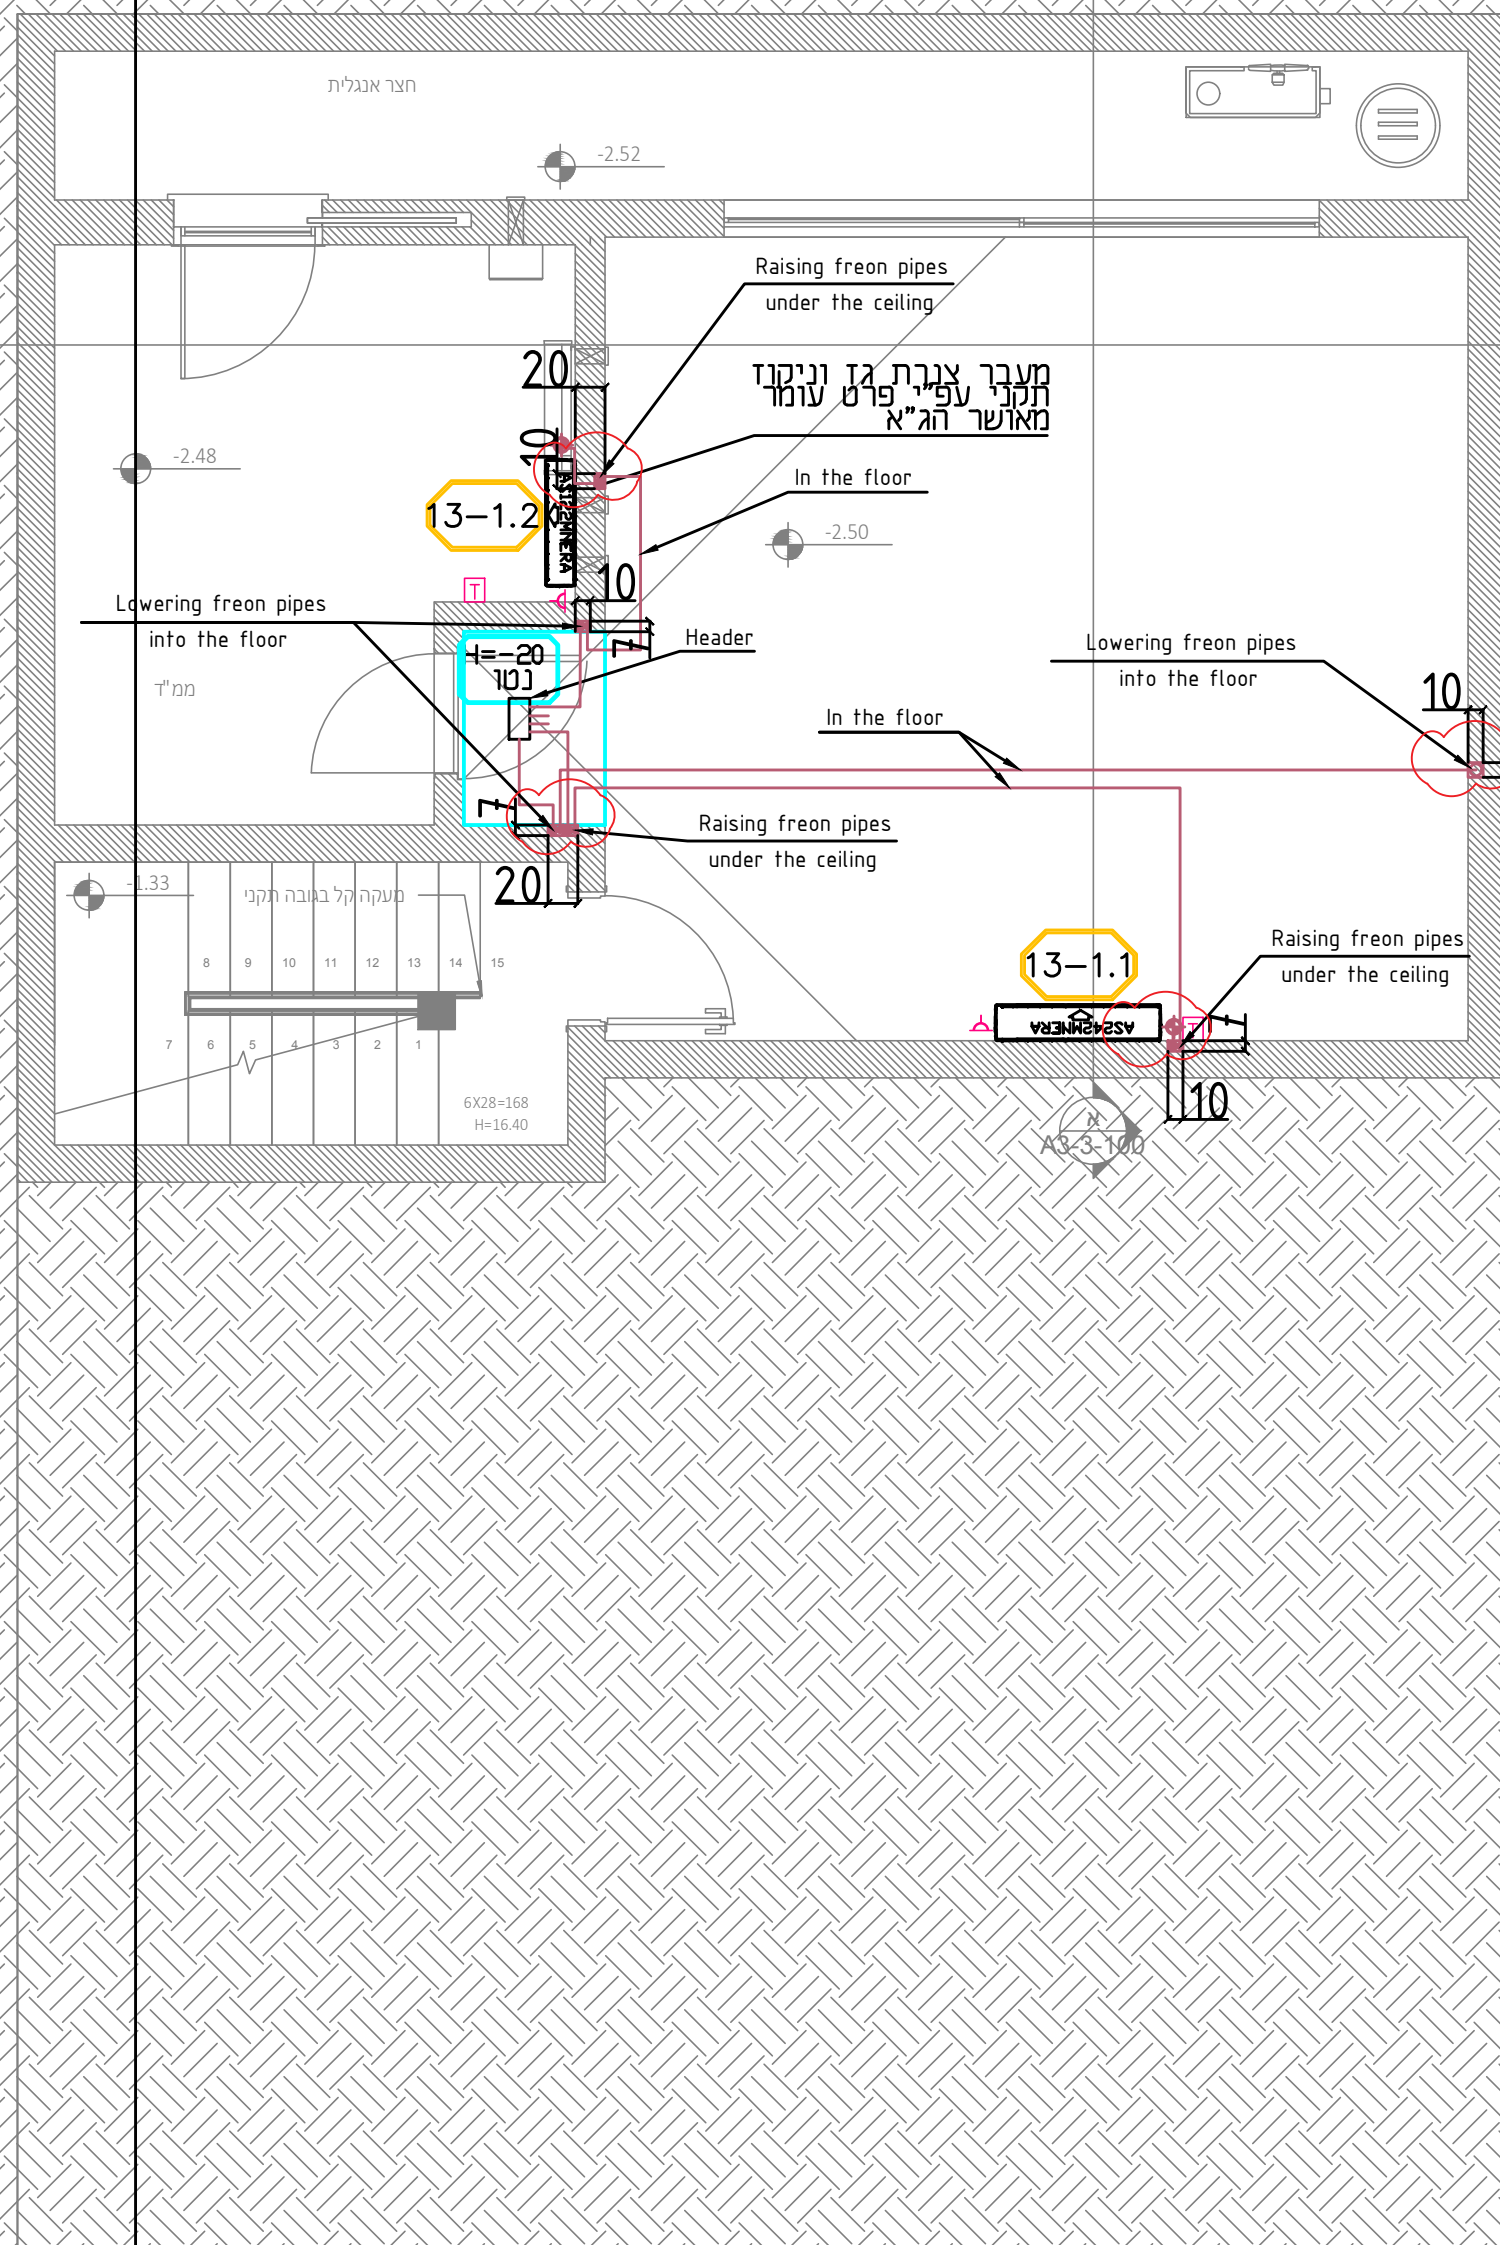

Option No4

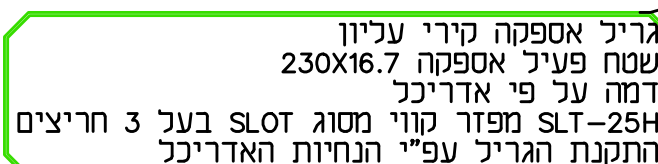[illegible]

מהדורה

חברות נאסד	04.06.2025	⬆
חברות נאסד	04.12.2024	⬆
חברות נעז	13.11.2024	⬆
שנייה	הרד:	ס:

המבצע אחראי למידות ולהתאמתן למציאות בכל מקרה של אי התאמה, סתירה או טעות עליו להודיע למתכנן לפני התקדמותו בביצוע! אין לקבוע מידות על סמך מדידה בשרטוט. אין לעשות כל שימוש בתוכנית זו ברעיונות, הגורמים בה ללא אישור בכתב מאת המתכנן.

מערות

1. כל התעלות מחוץ למבנה יבודוד
בידוד אקוסטי בעיבי 2"²
מידות התעלות הן מידות פה
2. תעלות מזוד בחור מבנה יבודוד
בידוד אקוסטי פנימי 1"²
מידות התעלות הן מידות פה
3. תעלות אוויר צה יבודוד
בידוד סריף 1"²
מידות התעלות הן מידות פה
4. יש לאסום סבייקווא את פינות החיבור
של תעלות מזוד אוויר לפני כיפוף
הפחים המתחברים

יִקְרָא

- [illegible]

קרא צבעים בתכנית

- | | |
|--------------------------|---|
| תעלות ותריסי אוויר חוזר |  |
| תעלות ותריסי אספקת אוויר |  |
| תעלות ותריסי אוויר צח |  |
| תעלות ותריסי יניקת אוויר |  |
| תעלות ותריסי שיחור עשן |  |
| צנרת גז וחשמל |  |
| סימון מעגלי מדוז אוויר |  |

191	מבני מאורים צמודי קרקע נופיה אפרי מנשה מבנה 13
מד כריסט	סמ הדרום
1:50	מידוג אוויר ואווורור
04.06.2025	קומת מרתף וקומה אשונה
מאיר מחרוזת	
3	
מחרוזת	סמ הדרום
לביצוע	העיון
	13.11.2024
	טען מפת
	איי אר

[illegible]

מהדורה		
תחילת הכשר	04.06.2025	▲
תחילת הכשר	04.12.2024	▲
תחילת הכשר	13.11.2024	▲
סיום	תאריך:	

הערות

- מקרא

- מקרא צבעים בתכנית

- | | |
|------------|---|
| 91 | מבני מגורים צמודי קרקע
נופיה אפרי' מנשה
מבנה 13 |
| 50:01 | מזיגז אוויר ואווירורור |
| 26.06.2025 | גג קומה שנייה וקומת |
| 3 | העיר (העיר) |
| מחזור | העיר |
| כביש | מיון |
| | 13.11.2024 |
| | החג |
| | איל איל |

אוריכל פנים	
אינטסטיציה	
בסיחת אש	
אקוטסיקה	
חשמל וחמורה	
קונסטרוקציה	
קבלת ראשי	
ניחול פריוטט	
נעוה	
אוריכל	

שנתיים:	תאריך:	00:
תכנית לעיון	13.11.2024	1
תכנית לאישור	04.12.2024	2
		3
		4

תעלות ותריסי אוויר חוזר	
תעלות ותריסי אספקת אוויר	
תעלות ותריסי אוויר צח	
תעלות ותריסי יניקת אוויר	
תעלות ותריסי שיחורז עשן	
צנרת גז וחשמל	
סימון מעגלי מידוג אוויר	

אייל ארז | מהנדסים יועצים
ייעוץ ותכנון מפעלות מיזוג ואקלים, פיקוח עליון

דגם :
תצורה :
מחיר :
דור :
מחיר נצטר :
מחיר

הערכת Y-5
Audi IPEERA
43000 BTU/H
מ"מ 370/950/134
16x23 H
400
3-6 (kW)
57 dB(A)

היסט כטון בגובה מינימלי 10 ע"מ
יחידת יבוי עומדת ע"ג בולנד ירדו
סיפסר בלבן מדוג אוור

מיטות סופי של התמכר
ייקבע בשטח
העומדים
האדריכל
מבלין מדוג אוור

מיטות סופי של תריקונים
ייקבע בשטחם במתחם
האדריכל
אייקסניסטימ"ר מבלין מדוג אוור

[illegible]

(תוכנית חלוקה 15-3)
 AV08NMSEITA : דגם :
 209.880 A/C : מספר :
 75U/144/169 : מ"מ :
 1950 : שנת הייצור :
 370 : שנת המכירה :
 16-5 : מספר (צבע) :
 61 dBA : רעש

בסים בטון בגובה מימית' 10 ס"מ
 ירידות יבוי שומדת ע"ג בונדס ריעודת
 לכיסוף כבול מוזה אוריר

מיסוס סופי של תועב'ס
 ייבוק בטסח
 בריאוס עם האורירי
 ועבול מוזה אוריר

מיסוס סופי של גימק'ס
 ייבוק בטסח
 בריאוס עם האורירי
 ועובי אטמסורה ועבול מוזה אוריר

