

מתכונים:


ניהול פרויקט
מהיסוד - בן סולומון
פיקוח
מהיסוד - בן סולומון
קונסטרוקציה
ערן שילר
מיזוג אוויר
אייל ארז מהנדסים ויועצים בע"מ
אינסטלציה
איתן אלמסי
חשמל
איתן בסיס
אלומיניום
נוף
נתי בלוקא
חשמל חכם
חימום תת רצפתי
איטום
צבי טל
אקוסטיקה
מעליות
קרקע וביסוס
דיה הנדסת קרקע וביסוס
רישוי

+ 0.00 = +248.30

הערות:
 1. תביתו ויש לקרוא יחד עם הכביות הוועים.
 2. גבה אסכולים: ארה תבית פחות.
 3. המדתו הן בין קירות ולבן כולל שיה.
 4. פחות השטח שיה התבית, לכול, מדורת, שבילים, ריצופים,
 5. פושטים שיה יתנו: ארה תבית פחות.
 6. אסכולים קירות רופצות התבית במגע עם הקרקע ובידוד תרמי לאורך המעמדים
 7. והקורות על הקירות: גליות ויש מיני (גילון) ארה תביות קוטסומקסיה
 8. ארה תבית ביצוע גלית תימוד אופיי תבית: חמור.
 9. ארה תרמי במסגרת שיה מפרס תומוקר, חמור: עיי פידוק תורוק.

[illegible]

זקרא קירות:

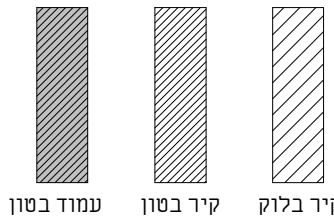[illegible]

אדריכלות

CLIENT NAME: _____ שם המזמין:

קבוצת רכישה נופיה

PROJECT NAME: _____ שם הפרויקט:

בופיה - מגרש 14

DRAWING NAME: ס הגליון:

SHEET NUMBER: 190 גליון:

A3-1-100

SCALE: קנה מידה: EDITION: הדורה:

STATUS: סמסוט
1
 למכר

DATE: 22.09.25 אר"י:



NeumanHaynerArchitects

office@nh-arch.com
www.nh-arch.com


וימן חיינר אדריכלים
מורד ההדריס 2, בית חירות
טל 09-9545842

09-9545842 טל

זכויות ייצור / ע"פ הנחיות עו"ד

נופיה - מגרש 14			
מס' גיליון	שם גיליון	מהדורה	תאריך הפצת מהדורה

22.09.2025	1	גליון שער	A3-1-100
22.09.2025	1	קומת קרקע	A3-1-101
22.09.2025	1	קומה א	A3-1-102
22.09.2025	1	גג	A3-1-103
22.09.2025	1	חזיתות 1	A3-2-200
22.09.2025	1	חזיתות 2	A3-2-201
22.09.2025	1	חתכים	A3-3-100
22.09.2025	1	גליון מדרגות	A3-4-100
22.09.2025	1	פרטים	A3-4-103
22.09.2025	1	פרטי פרגולה	A3-4-104
22.09.2025	1	רשימת פתחים	A3-6-1000

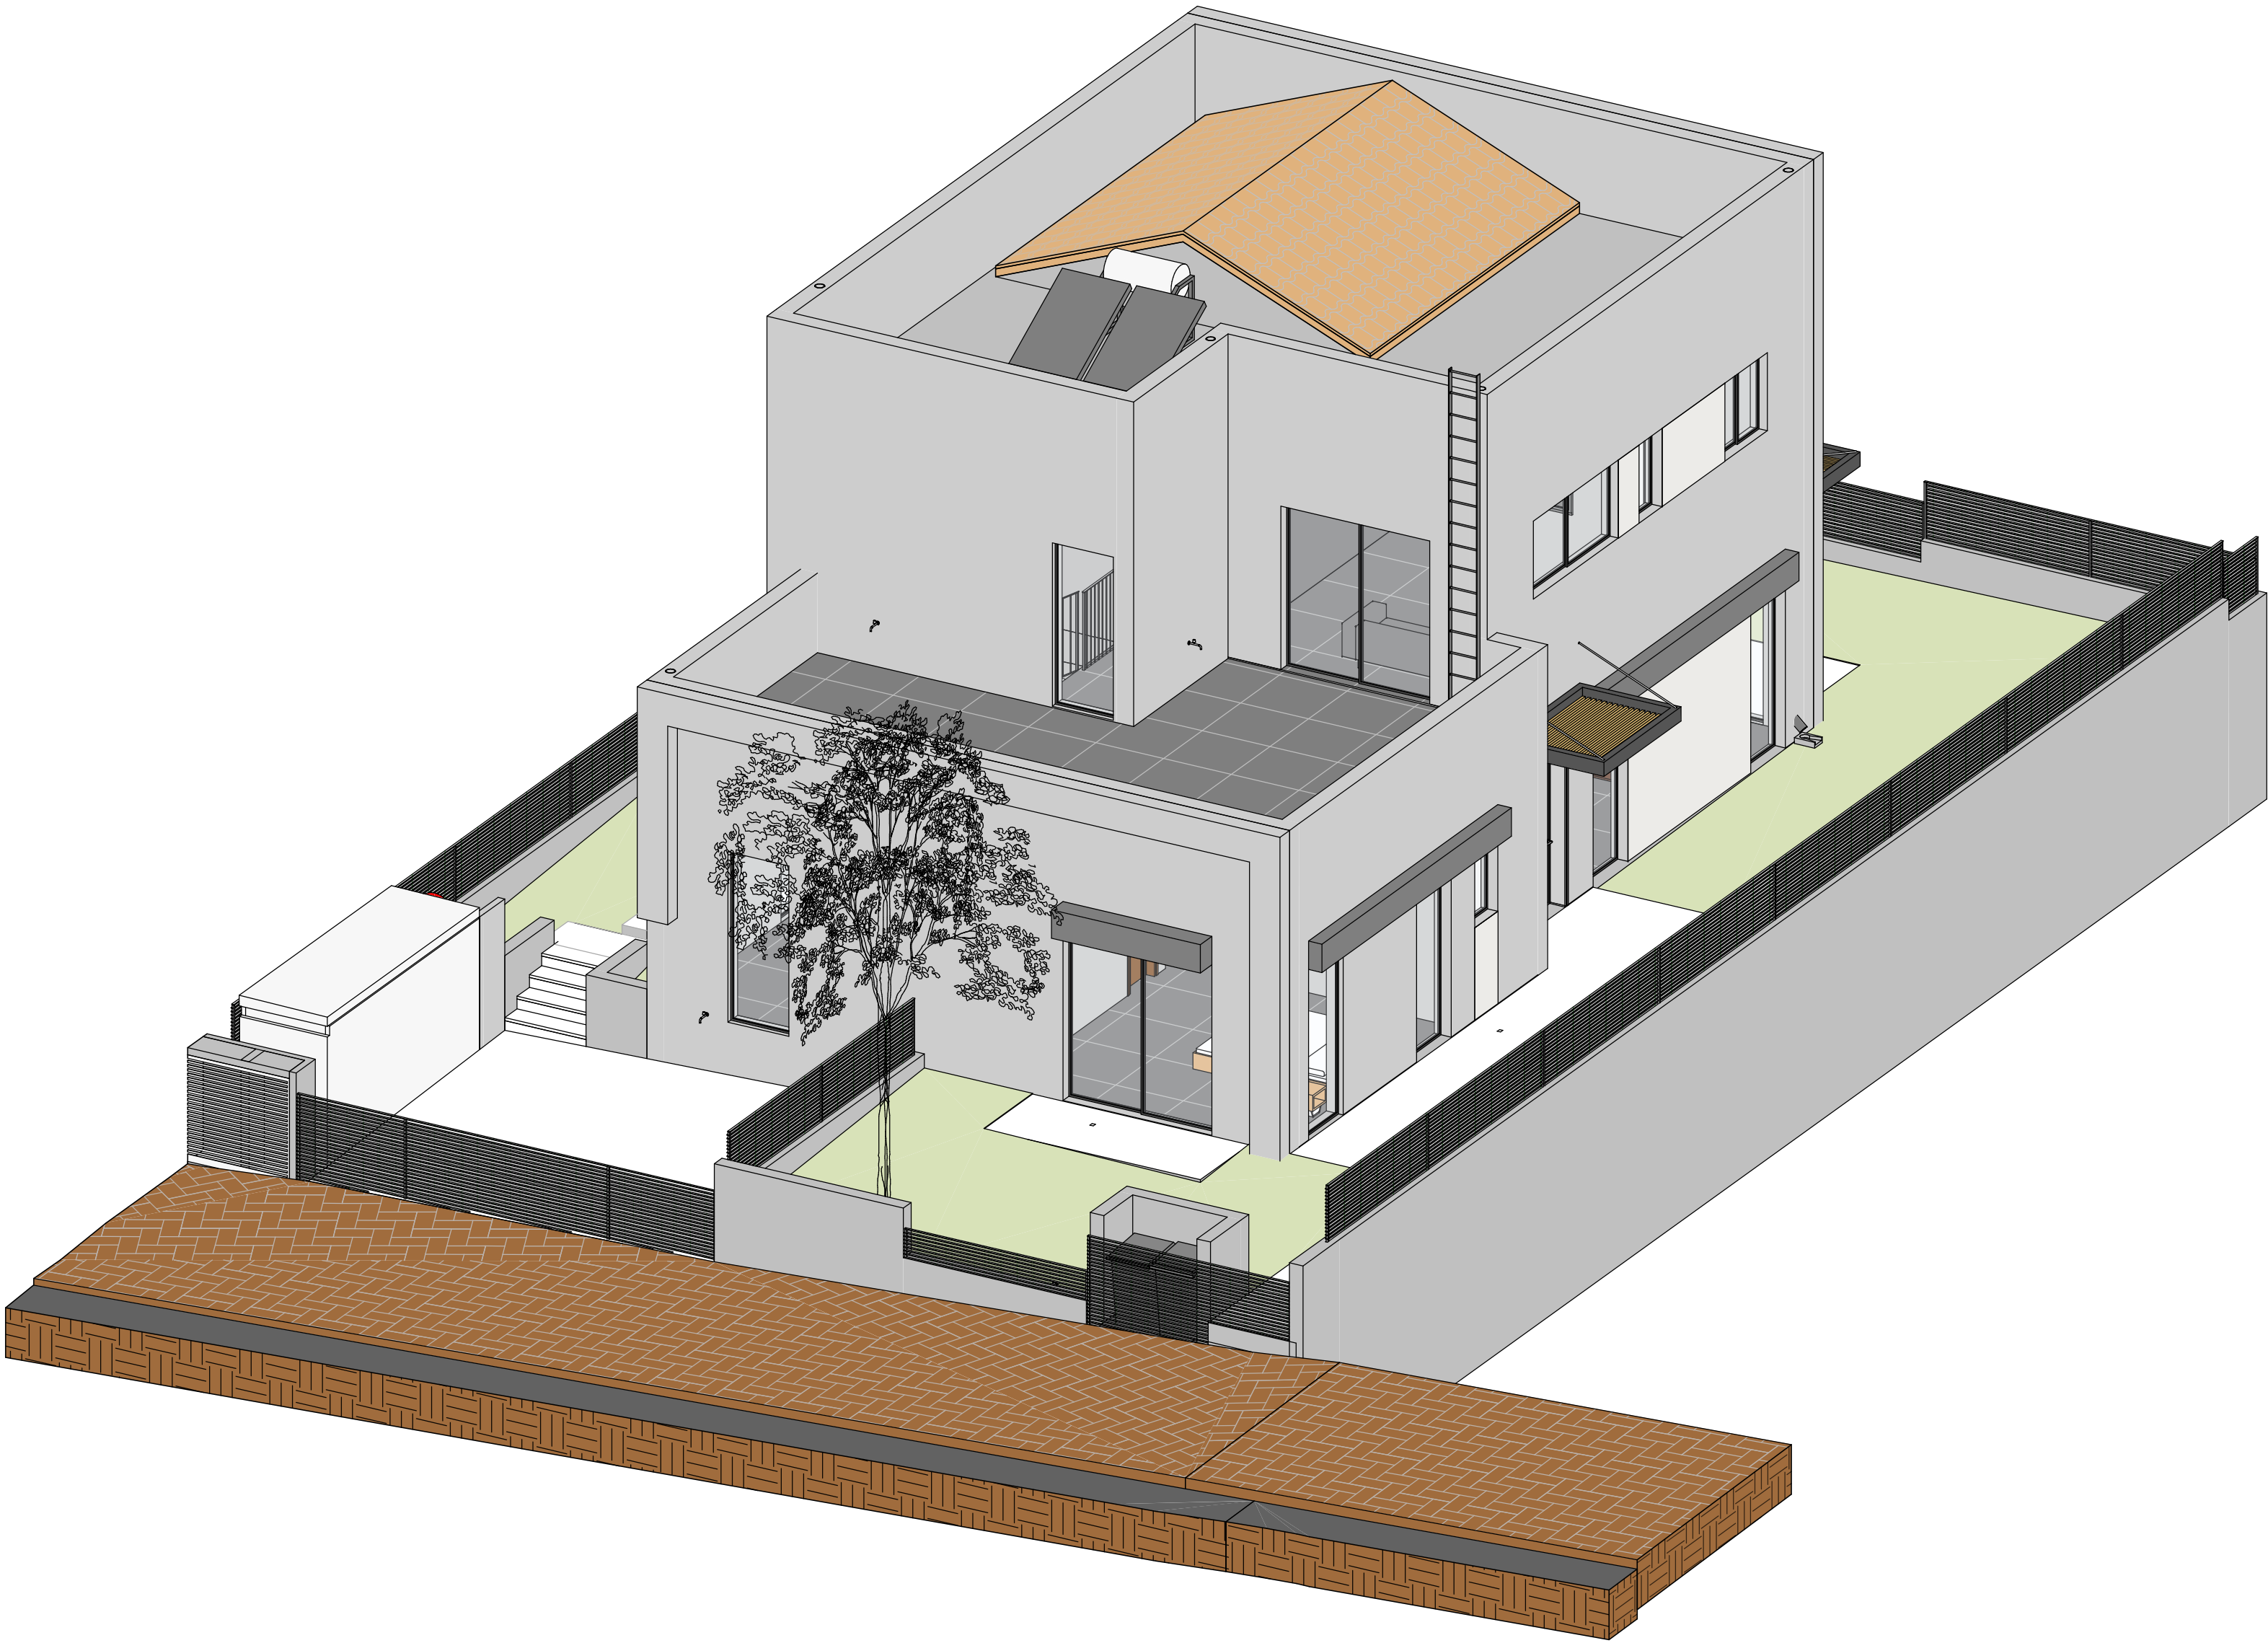

ניהל פרויקט
מהיסוד - בן סולומון
פיקוח
מהיסוד - בן סולומון
קונסטרוקציה
ערן שילר
מיזוג אוויר
אייל ארז מהנדסים ויועצים בע"מ
אינסטלציה
איתן אלמסי
חשמל
איתן בסיס
אלומיניום
נוף
נתי בלוקא
חשמל חכם
חימום תת רצפתי
איטום
צבי טל
אקוסטיקה
מעליות
קרקע וביסוס
דיה הנדסת קרקע וביסוס
רישוי

[illegible]

מקו & קירות

עמוד בסון קיר בסון קיר בלוק

[illegible]

CLIENT NAME:	המחזיק
קבוצת רכישה נופיה	
PROJECT NAME:	הפרויקט
נופיה - מגרש 14	
DRAWING NAME:	התכנון
קומת קרקע	
SHEET NUMBER:	מספר גליון
A3-1-101	


SCALE:	קנה מידה:	EDITION:	חזרות:
1 : 50	סטוסוס		
STATUS:	למבר		
	בדק עיי:		דסט עיי:
DATE:	22.09.25		איר:



וימן חיינר אדריכלים
מורד ההדרים 2, בית חירות
טל 09-9545842

מזל 09-9545842

זכויות ייצור / ע"פ הנחיות עו"ד

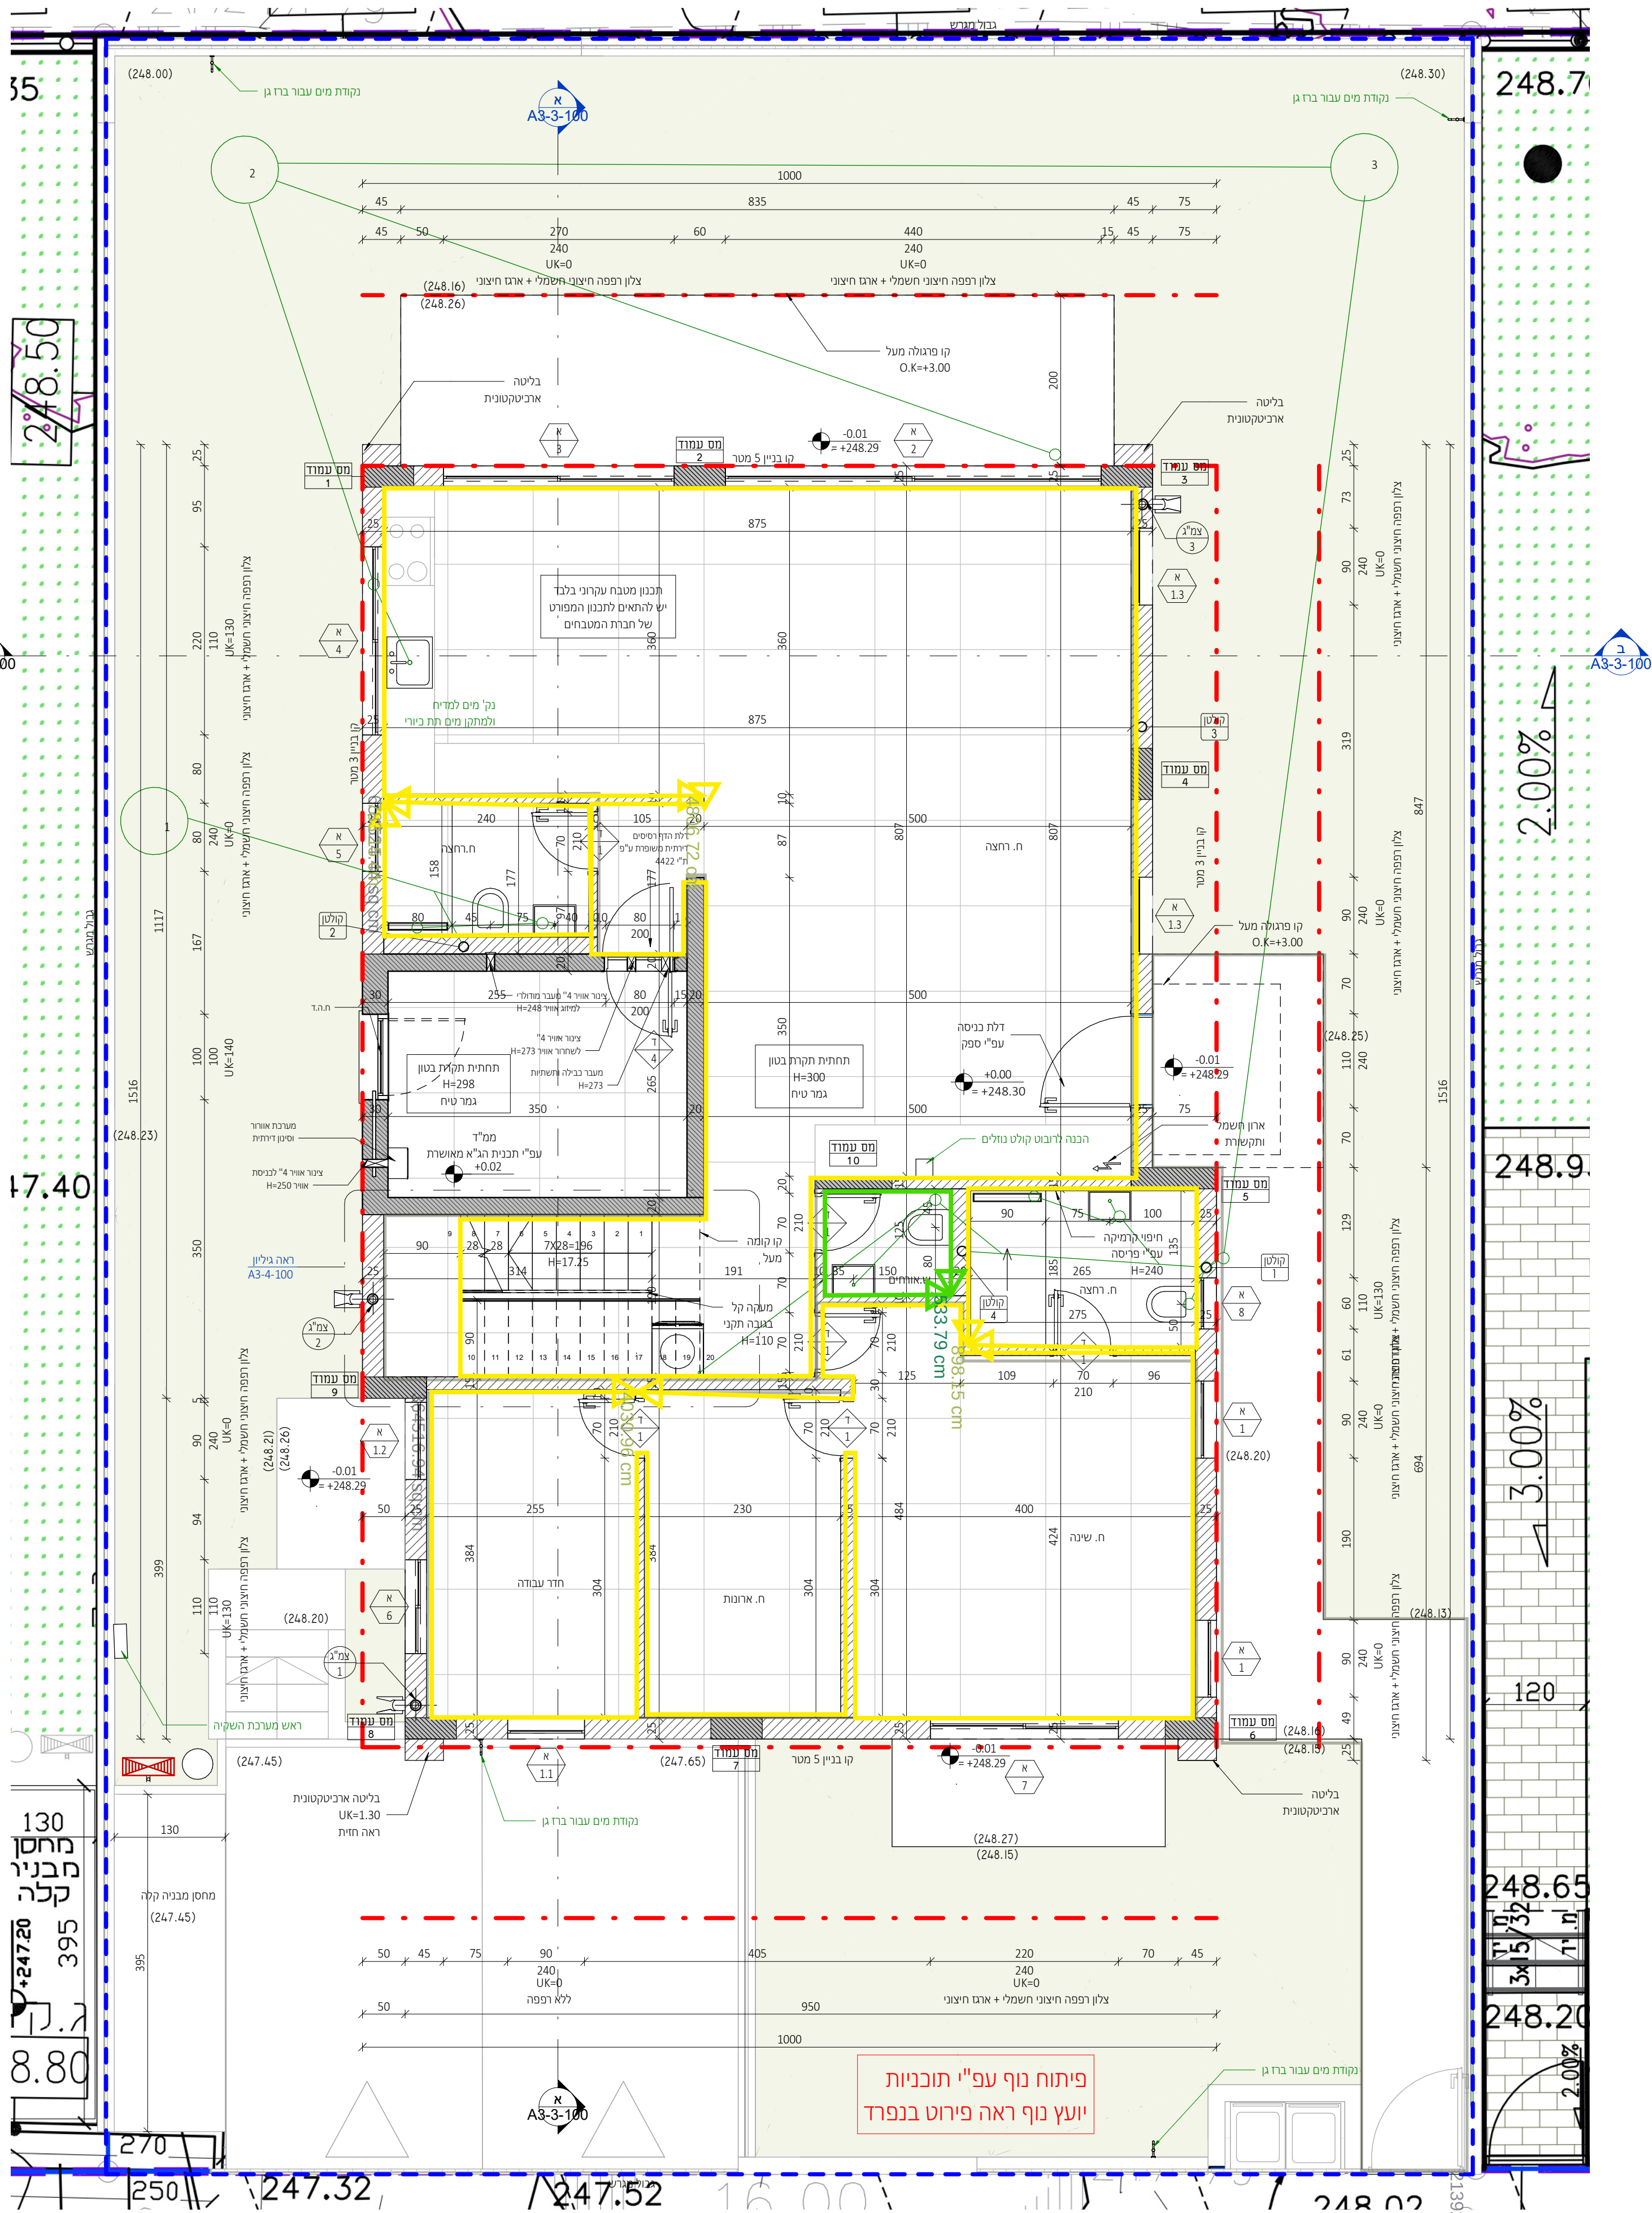

1 : 50


1. יש לעבוד במקביל לתכניות יועצים המאושרות על ידי האדריכל.
2. פרטי ספי חלון - עפ"י חוברת אלומיניום של הספק הנבחר ובתיאום מול אדריכל.
3. חימום תת רצפתי (במידה ויש במגרש זה) עפ"י פרטי הספק ובתיאום מול אדריכל.
4. יש לעבוד במקביל לתכניות עיצוב פנים (במידה ויש מעצב פנים במגרש זה) המאושרות על ידי האדריכל.
5. באחריות הקבלן לעדכן את האדריכל על אי התאמה בין התכניות יועצים לאדריכלות.
6. כל הדלתות לפי מפרט מצורף.
7. כל אלמנטי הבטון יקבלו התייחסות תרמית לפי הנחיות יועץ.
8. פרטי איטום, בידוד וניקוז עפ"י תכניות יועצים ובאחריות הקבלן.

מתכונים:


ניהול פרויקט
מהיסוד - בן סולומון
פיקוח
מהיסוד - בן סולומון
קונסטרוקציה
ערן שילר
מיוזג אוויר
אייל ארז מהנדסים ויועצים בע"מ
אינסטלציה
איתן אלמסי
חשמל
איתן בסיס
אלומיניום
נוף
נתי בלוקא
חשמל חכם
חימום תת רצפתי
איטום
צבי טל
אקוסטיקה
מעליות
קרקע וביסוס
דיה הנדסת קרקע וביסוס
ירשני

[illegible][illegible]

קרא קירות:

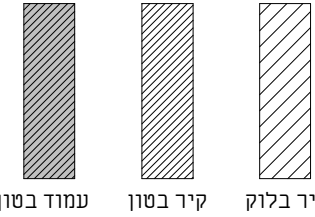[illegible]

אדריכלות

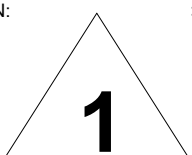
CLIENT NAME:	הפרויקט:	
קבוצת רכישה נופיה		
PROJECT NAME:	הפרויקט:	
נופיה - מגרש 14		
DRAWING NAME:	הפרויקט:	
קומה א		
SHEET NUMBER:	פרוטוקול:	
A3-1-102		
SCALE:	קנה מידה:	EDITION:
1 : 50	000000	
STATUS:	למכר	000000 ע"י:
	נבדק ע"י:	
DATE:	22.09.25	ירי:



NeumanHaynerArchitects

ימון חיינר אדריכלים
ורד ההדרים 2, בית חירות
ל 09-9545842

זכויות ייצור / ע"פ הנחיות עו"ד

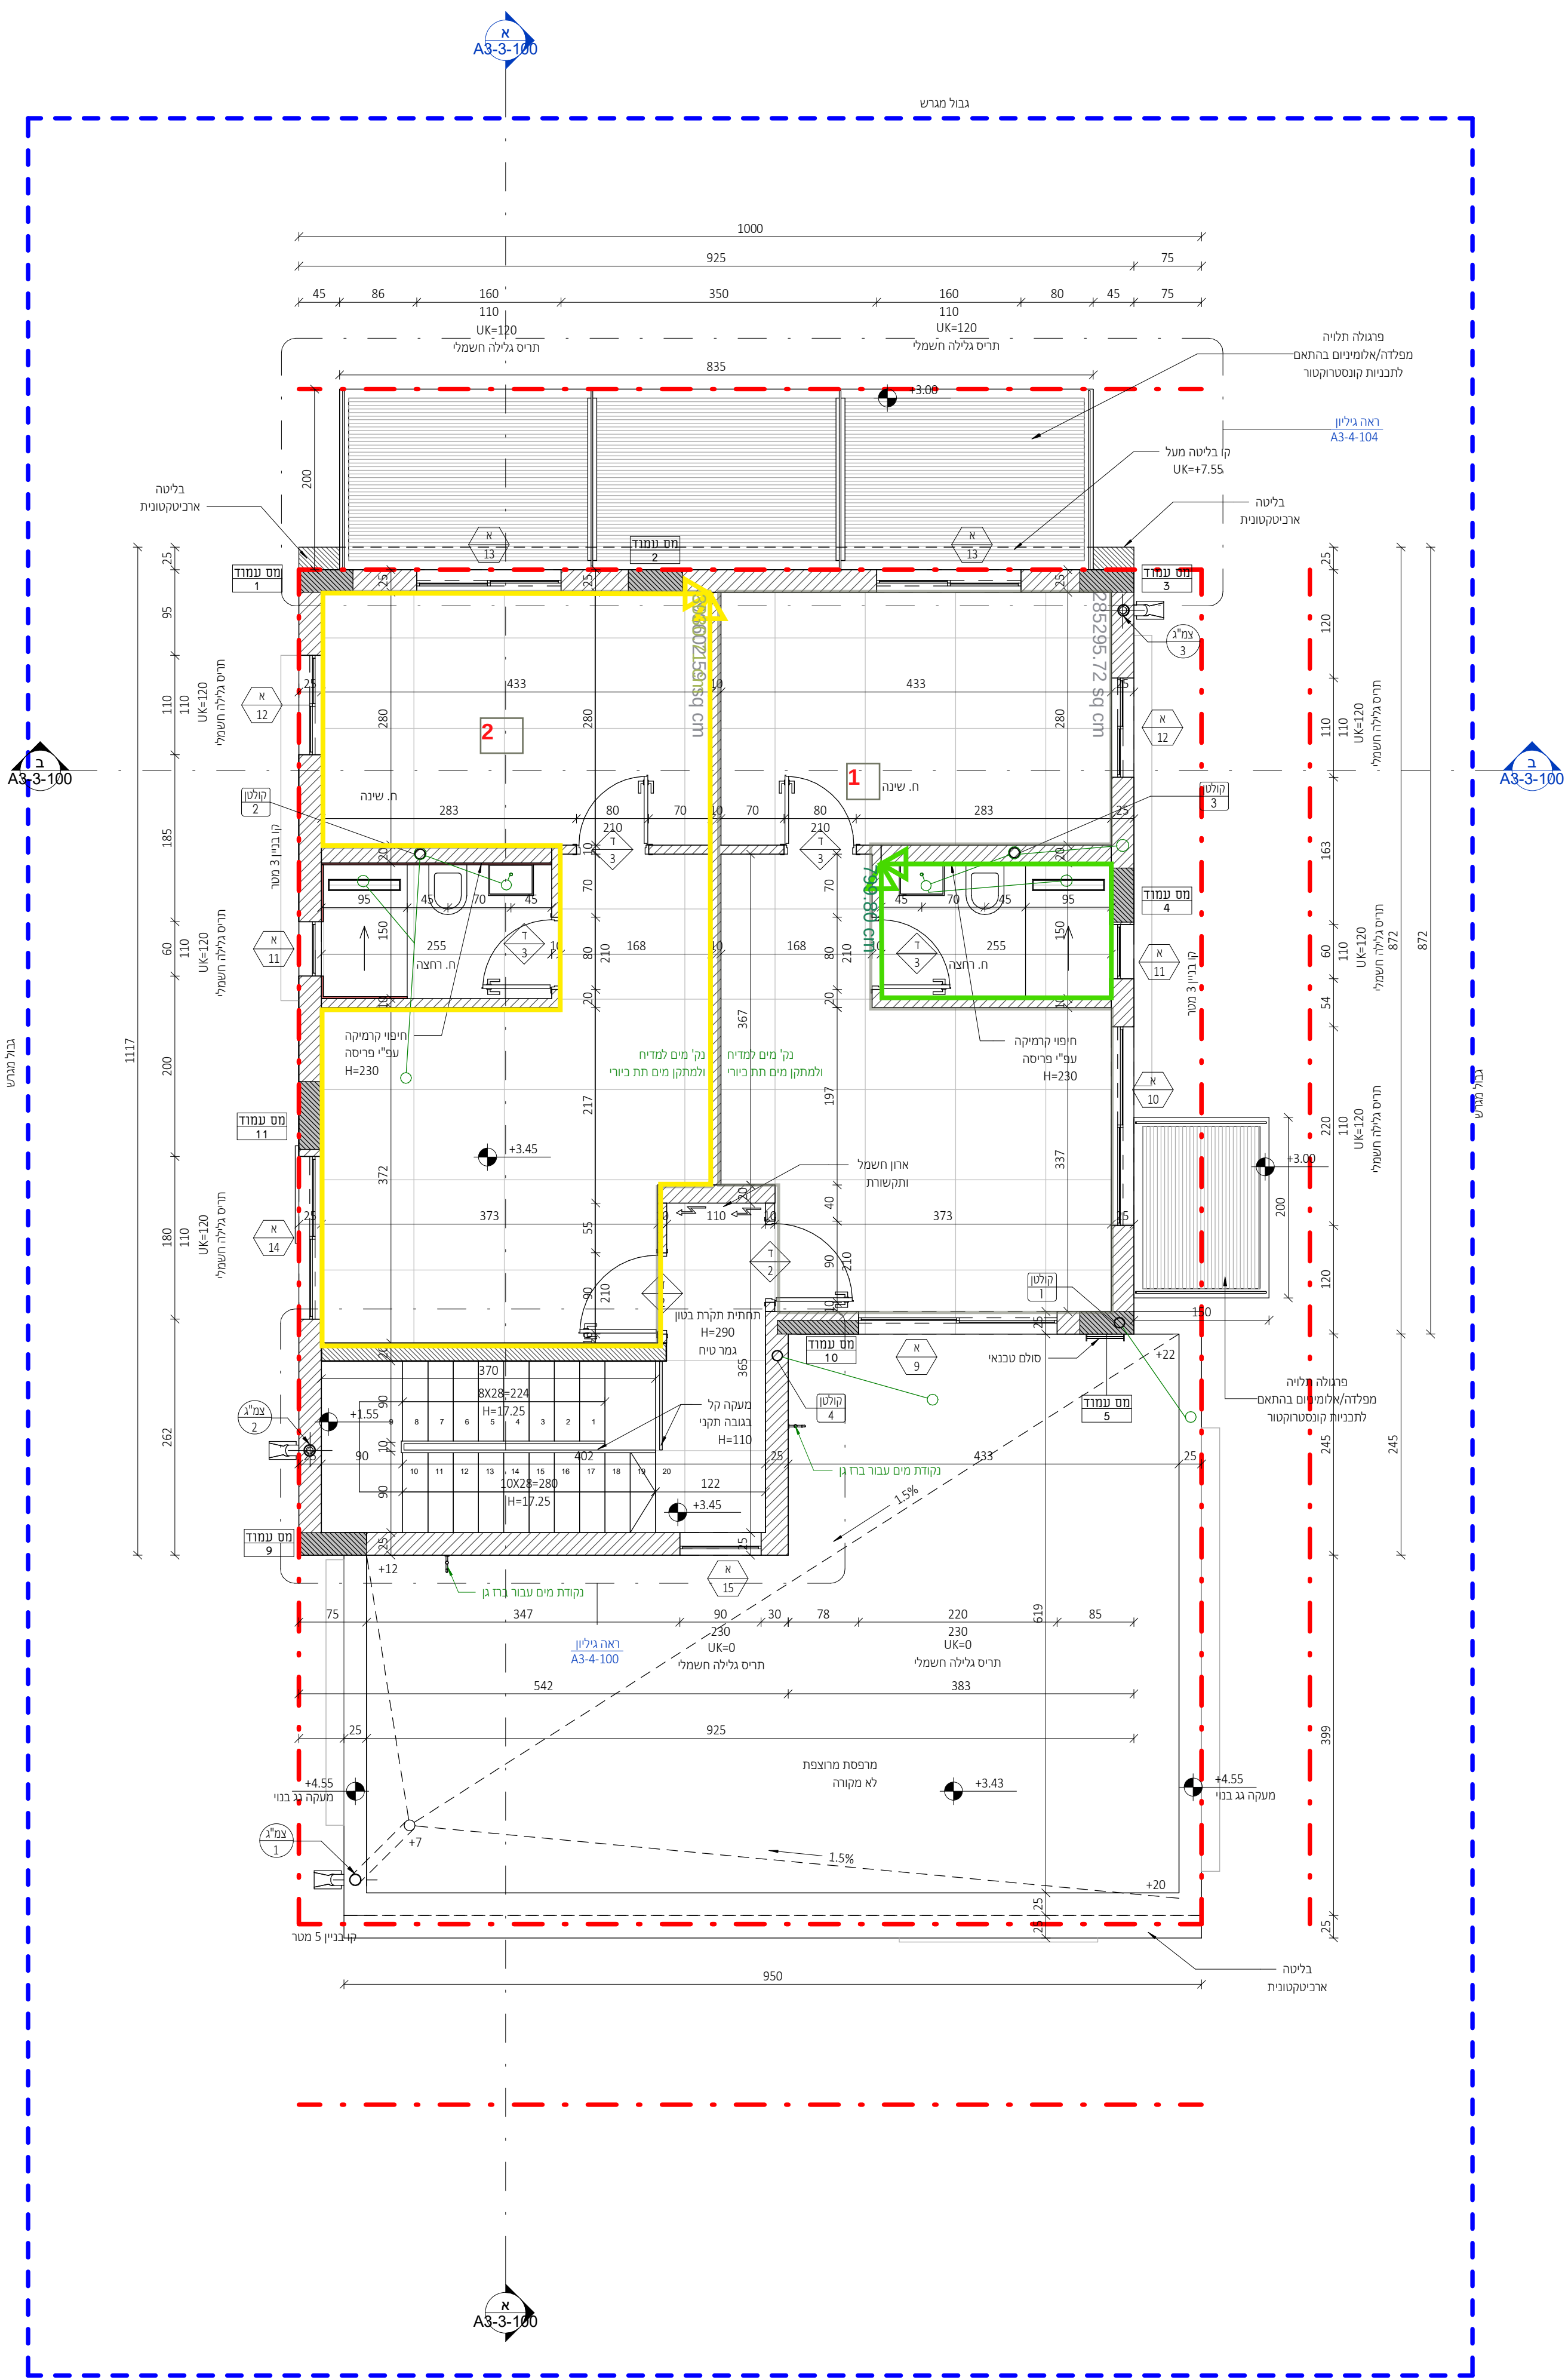

תכנית קומה א

1 : 50

הערות:


1. יש לעבוד במקביל לתכניות יועצים המאושרות על ידי האדריכל.
2. פרטי ספי חלון - עפ"י חוברת אלומיניום של הספק הנבחר ובתיאום מול אדריכל.
3. חימום תת רצפתי (במידה ויש במגרש זה) עפ"י פרטי הספק ובתיאום מול אדריכל.
4. יש לעבוד במקביל לתכניות עיצוב פנים (במידה ויש מעצב פנים במגרש זה) המאושרות על ידי האדריכל.
5. באחריות הקבלן לעדכן את האדריכל על אי התאמה בין התכניות יועצים לאדריכלות.
6. כל הדלתות לפי מפרט מצורף.
7. כל אלמנטי הבטון יקבלו התייחסות תרמית לפי הנחיות יועץ.
8. פרטי איטום, בידוד וניקוז עפ"י תכניות יועצים ובאחריות הקבלן.

מתכננים:

ניהול פרויקט
מהיסוד - בן סולומון
פיקוח
מהיסוד - בן סולומון
קונסטרוקציה
ערן שילר
מיזוג אוויר
אייל ארז מהנדסים ויועצים בע"מ
אינסטלציה
איתן אלמסי
חשמל
איתן בסיס
אלומיניום
נוף
נתי בלוקא
חשמל חכם
חימום תת רצפתי
איטום
צבי טל
אקוסטיקה
מעליות
קרקע וביסוס
דיה הנדסת קרקע וביסוס
רישוי

± 0.00 = +248.30
הערות: 1. תכנית זו יש לקרוא יחד עם תכנית הרישום. 2. גובה אבסולוטי - ראו תכנית פיתוח. 3. הפירות הן בין קירות הבניה ולא כולל פחים. 4. פיתוח השטח סביב הבנוה, כולל, מדרגות, גדרות, שבילים, ריצופים, שפכים, גדרים, חניה וגנין וראו תכנית פיתוח. 5. איטום קירות והצפות הבנוה כמנוע עם הקרקע ובזווית תחסי לאורך העמודים והקירות וכל תכנית-כלית או עם סימני גיבס- ראו תכנית קונסטרוקציה. 6. אף חם יבוצע בכל מישור אופקי הבולם חתכו. 7. פוח תחמי במס"ד- ע"פ מפרט תומקיר, מאושר ע"י פיקוד העורף.
המבצע אחראי לסידור : עליו לבקר ולבדוק את כל המידות בתכנית ובקטע הטבוחה. במסגרת של מידות או אי התאמה בתכנית /או בבנוי, עליו להודיע על כך מיד לאדריכל במסג המשרד בעברותיו. המבצע יאשרשם או ויק תכניתו שאושר לכניסו. המבצע יחזיק אתה, בכל עת, של משרדו של תכנית. אח לקבוע מידות על ידי חדיה בשו מוס. התכנית היתה רכוש האדריכל ואין לשווח כל שימוש בה או ברעיונות הגלומים בה, אלא באישור בכתב מהאדריכל. מומנם /או יושם אשר שמו רשום בתכנית זו, נושא לכד באחריות המקצועית והטכנית לתכנית. על המפקח והמכיל לודא התאמת התכנית האדריכלית "לביצוע" תכניתו כוללת את כל האחריות והידוע עד ליום תחלתה.

משרד קירות:

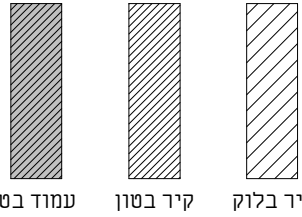


תאריך	תיאור	מהדורה
22.09.2025	מכרז	1

אדריכלות

שם המסין:	CLIENT NAME:
קבוצת רכישה נופיה	
שם הפרויקט:	PROJECT NAME:
נופיה - מגרש 14	
שם הגליון:	DRAWING NAME:
גג	
מספר גליון:	SHEET NUMBER:
A3-1-103	
תחבורה:	EDITION:
קנה מידה:	SCALE:
1 : 50	
סטוס:	STATUS:
למכרז	
שורסס עיי:	נבדק עיי:
תאריך:	DATE:
22.09.25	

נויטן חיינר אדריכלים
מודד התדרים 2, בית חירות
09-9545842 78
office@nh-arch.com
www.nh-arch.com

זכיות ייצור / ע"פ הנחיות ע"ד

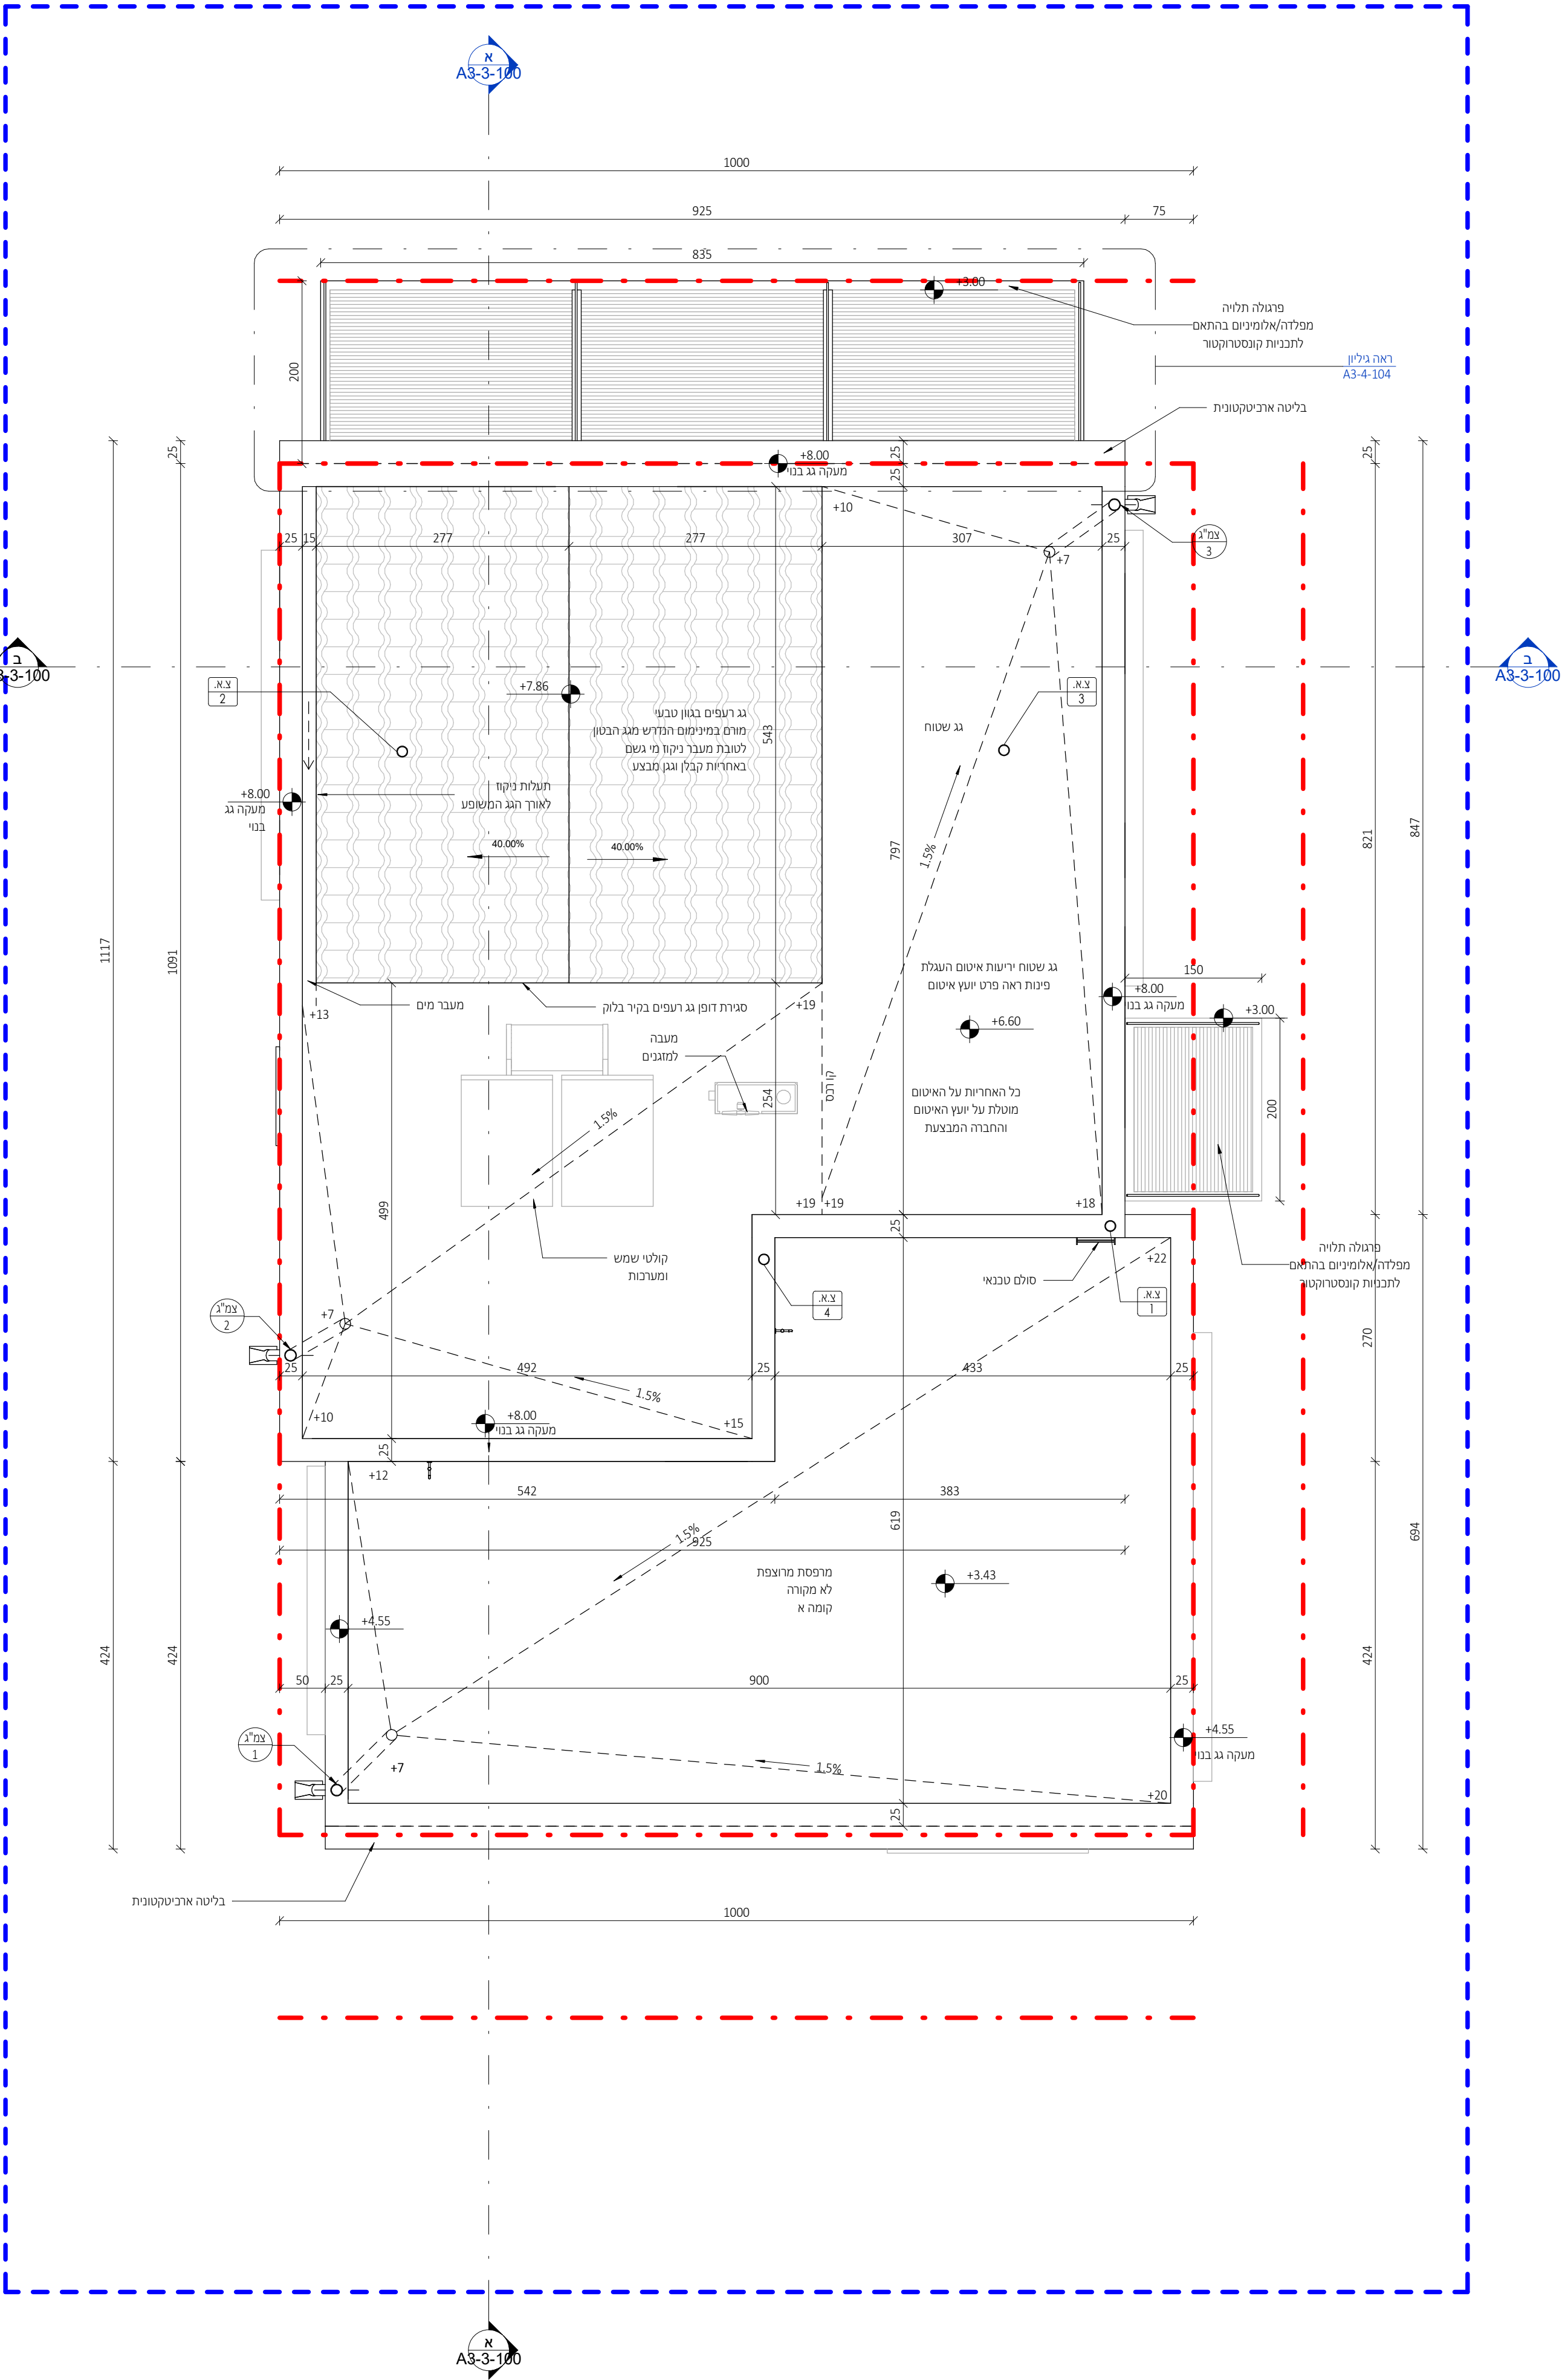

תכנית גג

1 : 50

מתכונים:

ניהול פרויקט
מהיסוד - בן סולומון
פיקוח
מהיסוד - בן סולומון
קונסטרוקציה
ערן שילר
מיזוג אוויר
אייל ארז מהנדסים ויועצים בע"מ
אינסטלציה
איתן אלמסי
חשמל
איתן בסיס
אלומיניום
נוף
נתי בלוקא
חשמל חכם
חימום תת רצפתי
איטום
צבי טל
אקוסטיקה
מעליות
קרקע וביסוס
דיה הנדסת קרקע וביסוס
רישוי

[illegible][illegible]

אדריכלות





CLIENT NAME:		המחלקה	
קבוצת רכישה נופיה			
PROJECT NAME:		הפרויקט	
נופיה - מגרש 14			
DRAWING NAME:		התוכנית	
חזיתות 1			
SHEET NUMBER:		מספר הגיליון	
A3-2-200			
SCALE:	קנה מידה:	EDITION:	הדורה:
1 : 50			
STATUS:	סטוס		
למכר			
	נבדק ע"י:		דוסס ע"י:
DATE:	22.09.25		תאריך:



וימן חיינר אדריכלים
מורד ההדרים 2, בית חירות
טל 09-9545842

וימן חיינר אדריכלים
מורד ההדרים 2, בית חירות
טל 09-9545842

זכויות ייצור / ע"פ הנחיות עו"ד

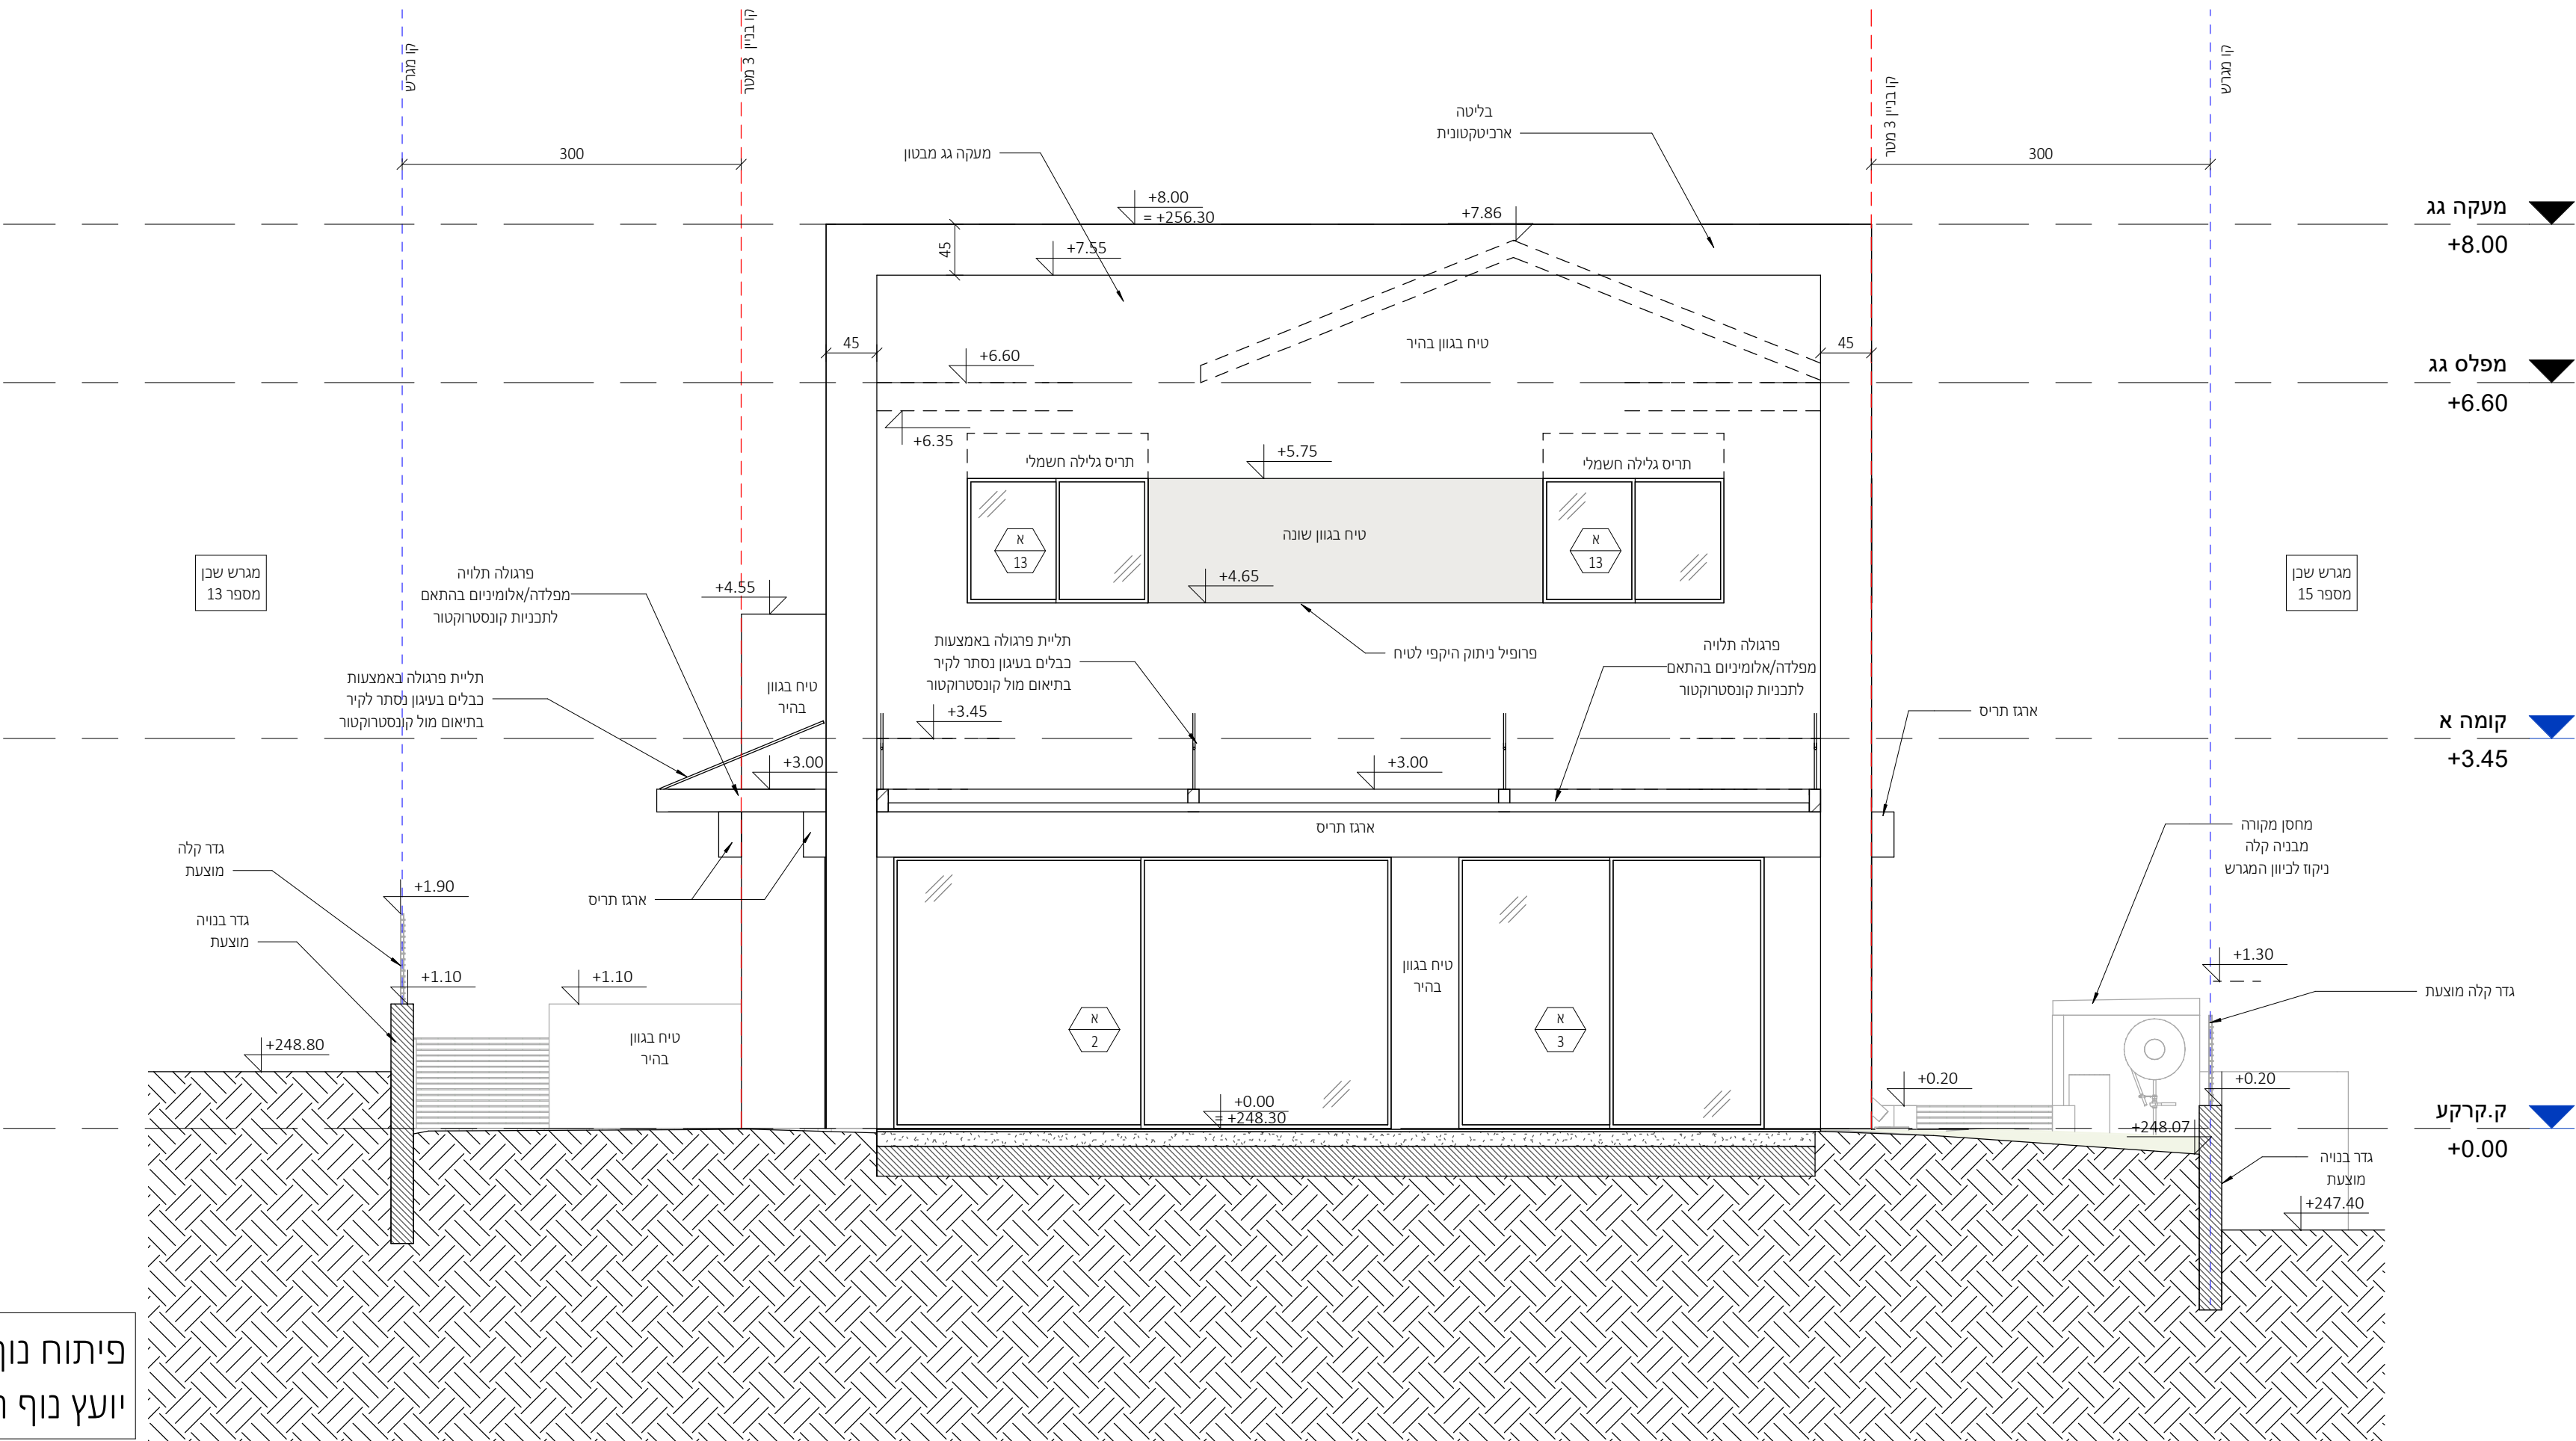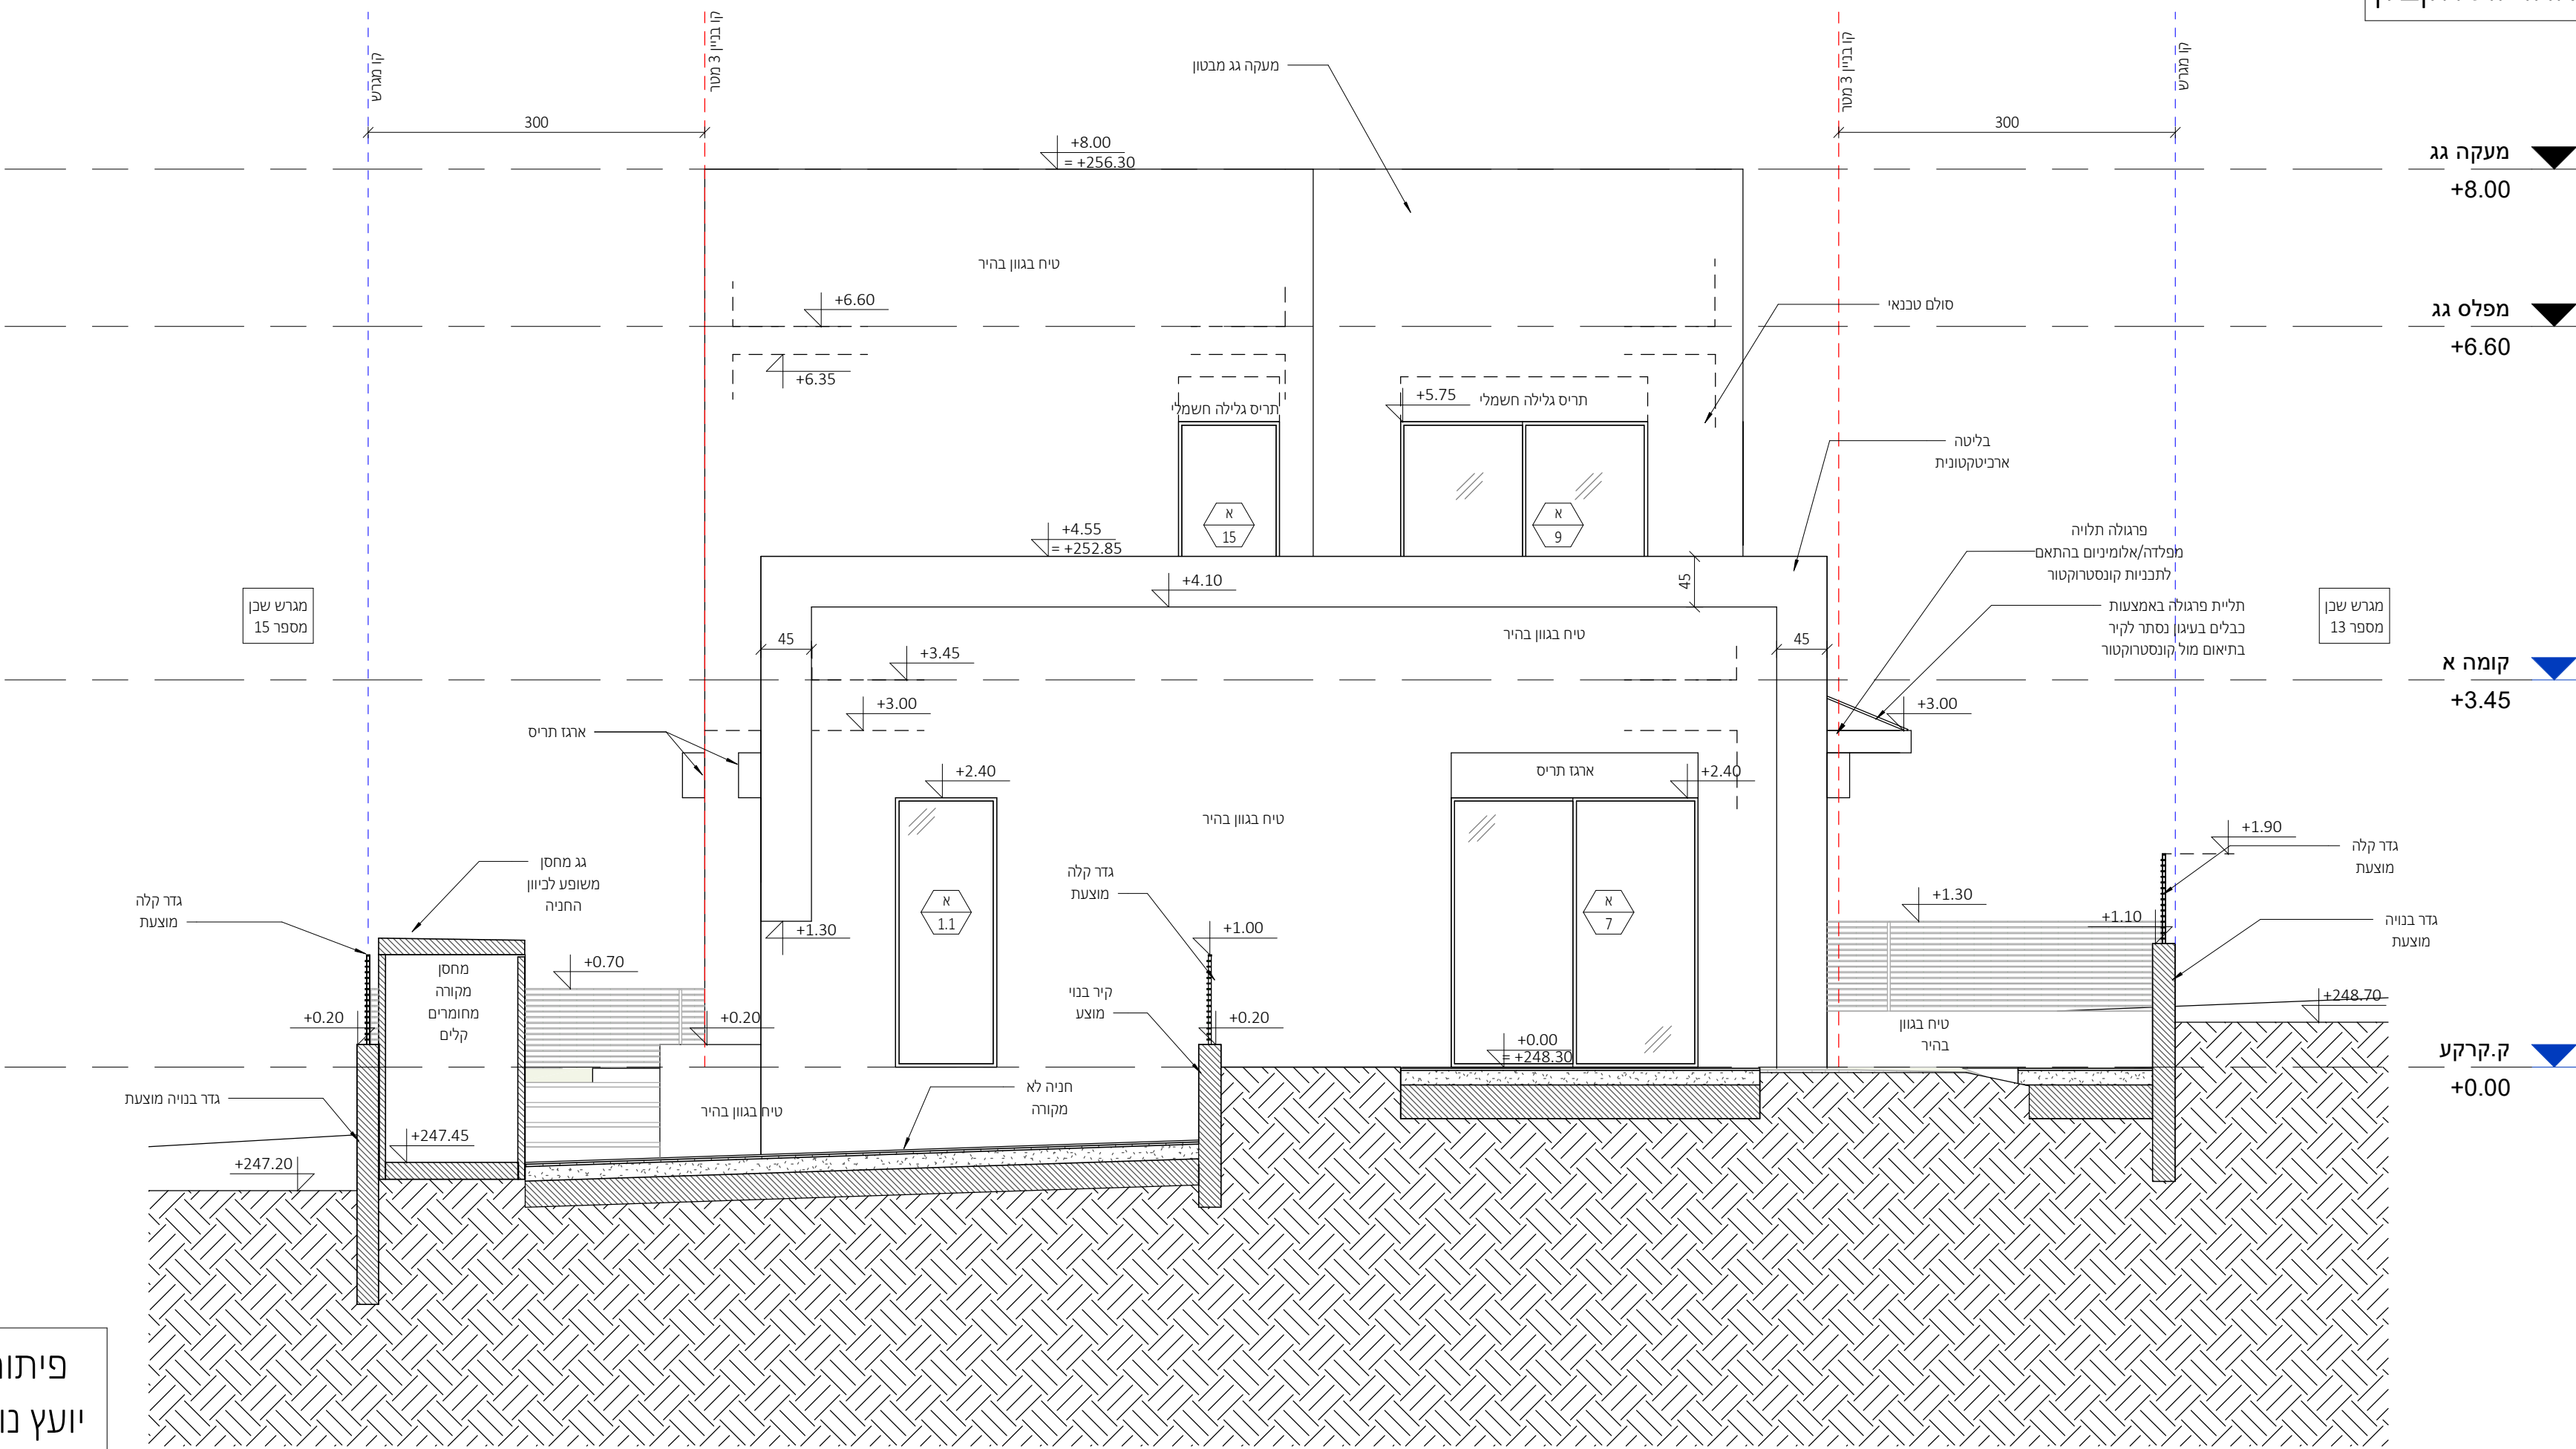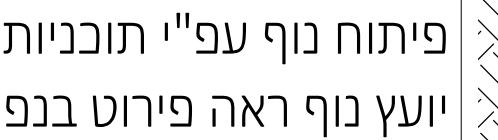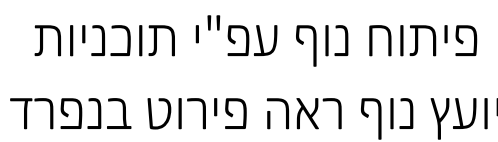

חזית דרומית

1 : 50

חזית צפונית

1 : 50

מתכונים:

ניהול פרויקט
מהיסוד - בן סולמון
פיקוח
מהיסוד - בן סולמון
קונסטרוקציה
ערן שילר
מיזוג אוויר
אייל ארז מהנדסים ויועצים בע"מ
אינסטלציה
איתן אלמסי
חשמל
איתן בסיס
אלומיניום
נוף
נתי בלוקא
חשמל חכם
חימום תת רצפתי
איטום
צבי טל
אקוסטיקה
מעליות
קרקע וביסוס
דיה הנדסת קרקע וביסוס
רישוי

[illegible][illegible]


אדריכלות

CLIENT NAME:		המחלקה	
קבוצת רכישה נופיה			
PROJECT NAME:		הפרויקט	
נופיה - מגרש 14			
DRAWING NAME:		התוכנית	
חזיתות 2			
SHEET NUMBER:		מספר הגיליון	
A3-2-201			
SCALE:	קנה מידה:	EDITION:	הדורה:
1 : 50			
STATUS:	סטוס		
למכר			
	נבדק ע"י:		דוסס ע"י:
DATE:	22.09.25		תאריך:


NeumanHaynerArchitects

office@nh-arch.com

זכויות ייצור / ע"פ הנחיות עו"ד

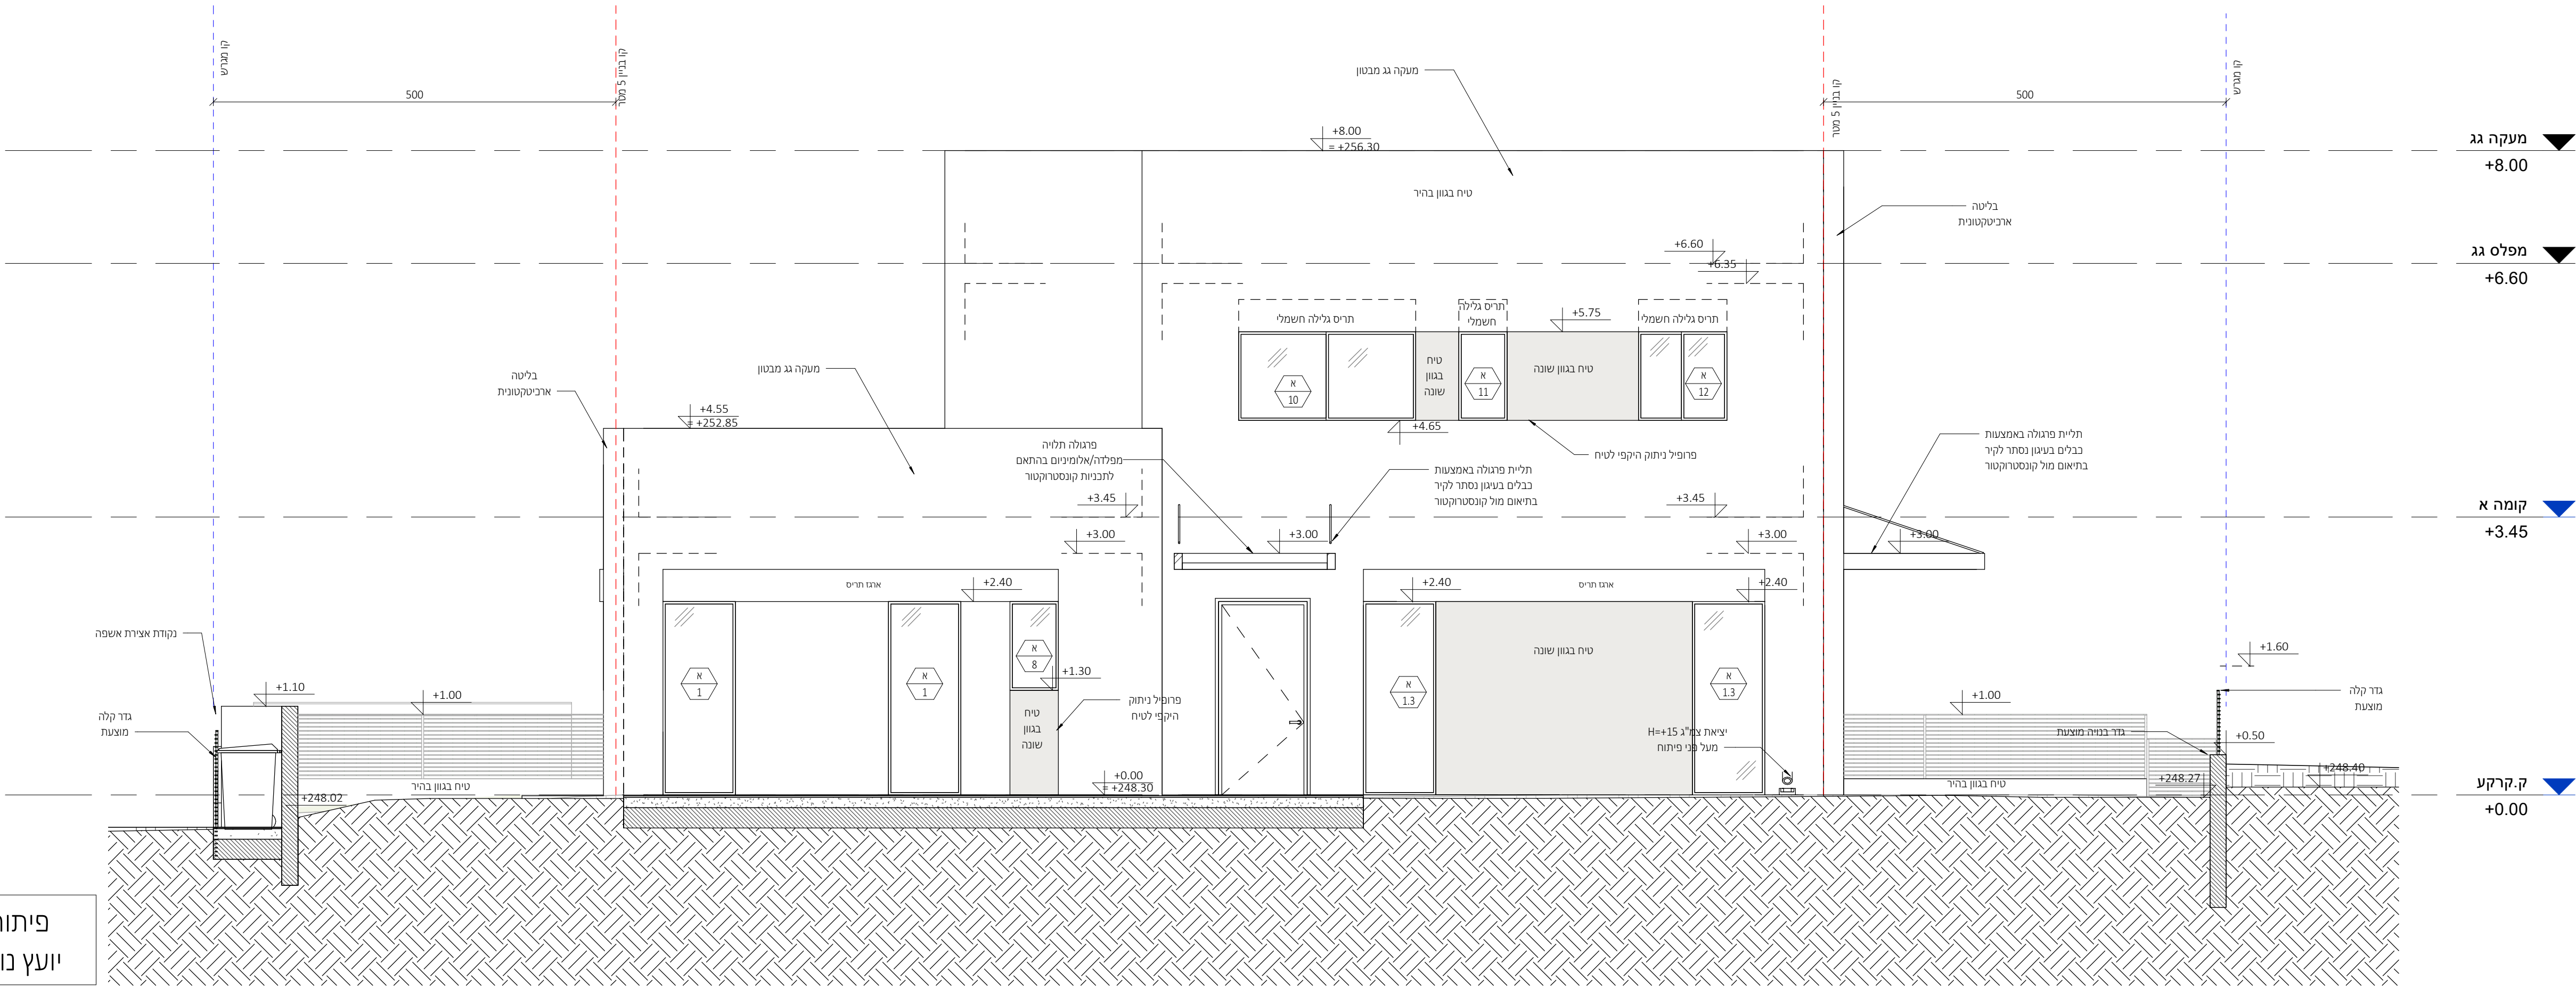

פיתוח נוף עפ"י תוכניות
יועץ נוף ראה פירוט בנפרד

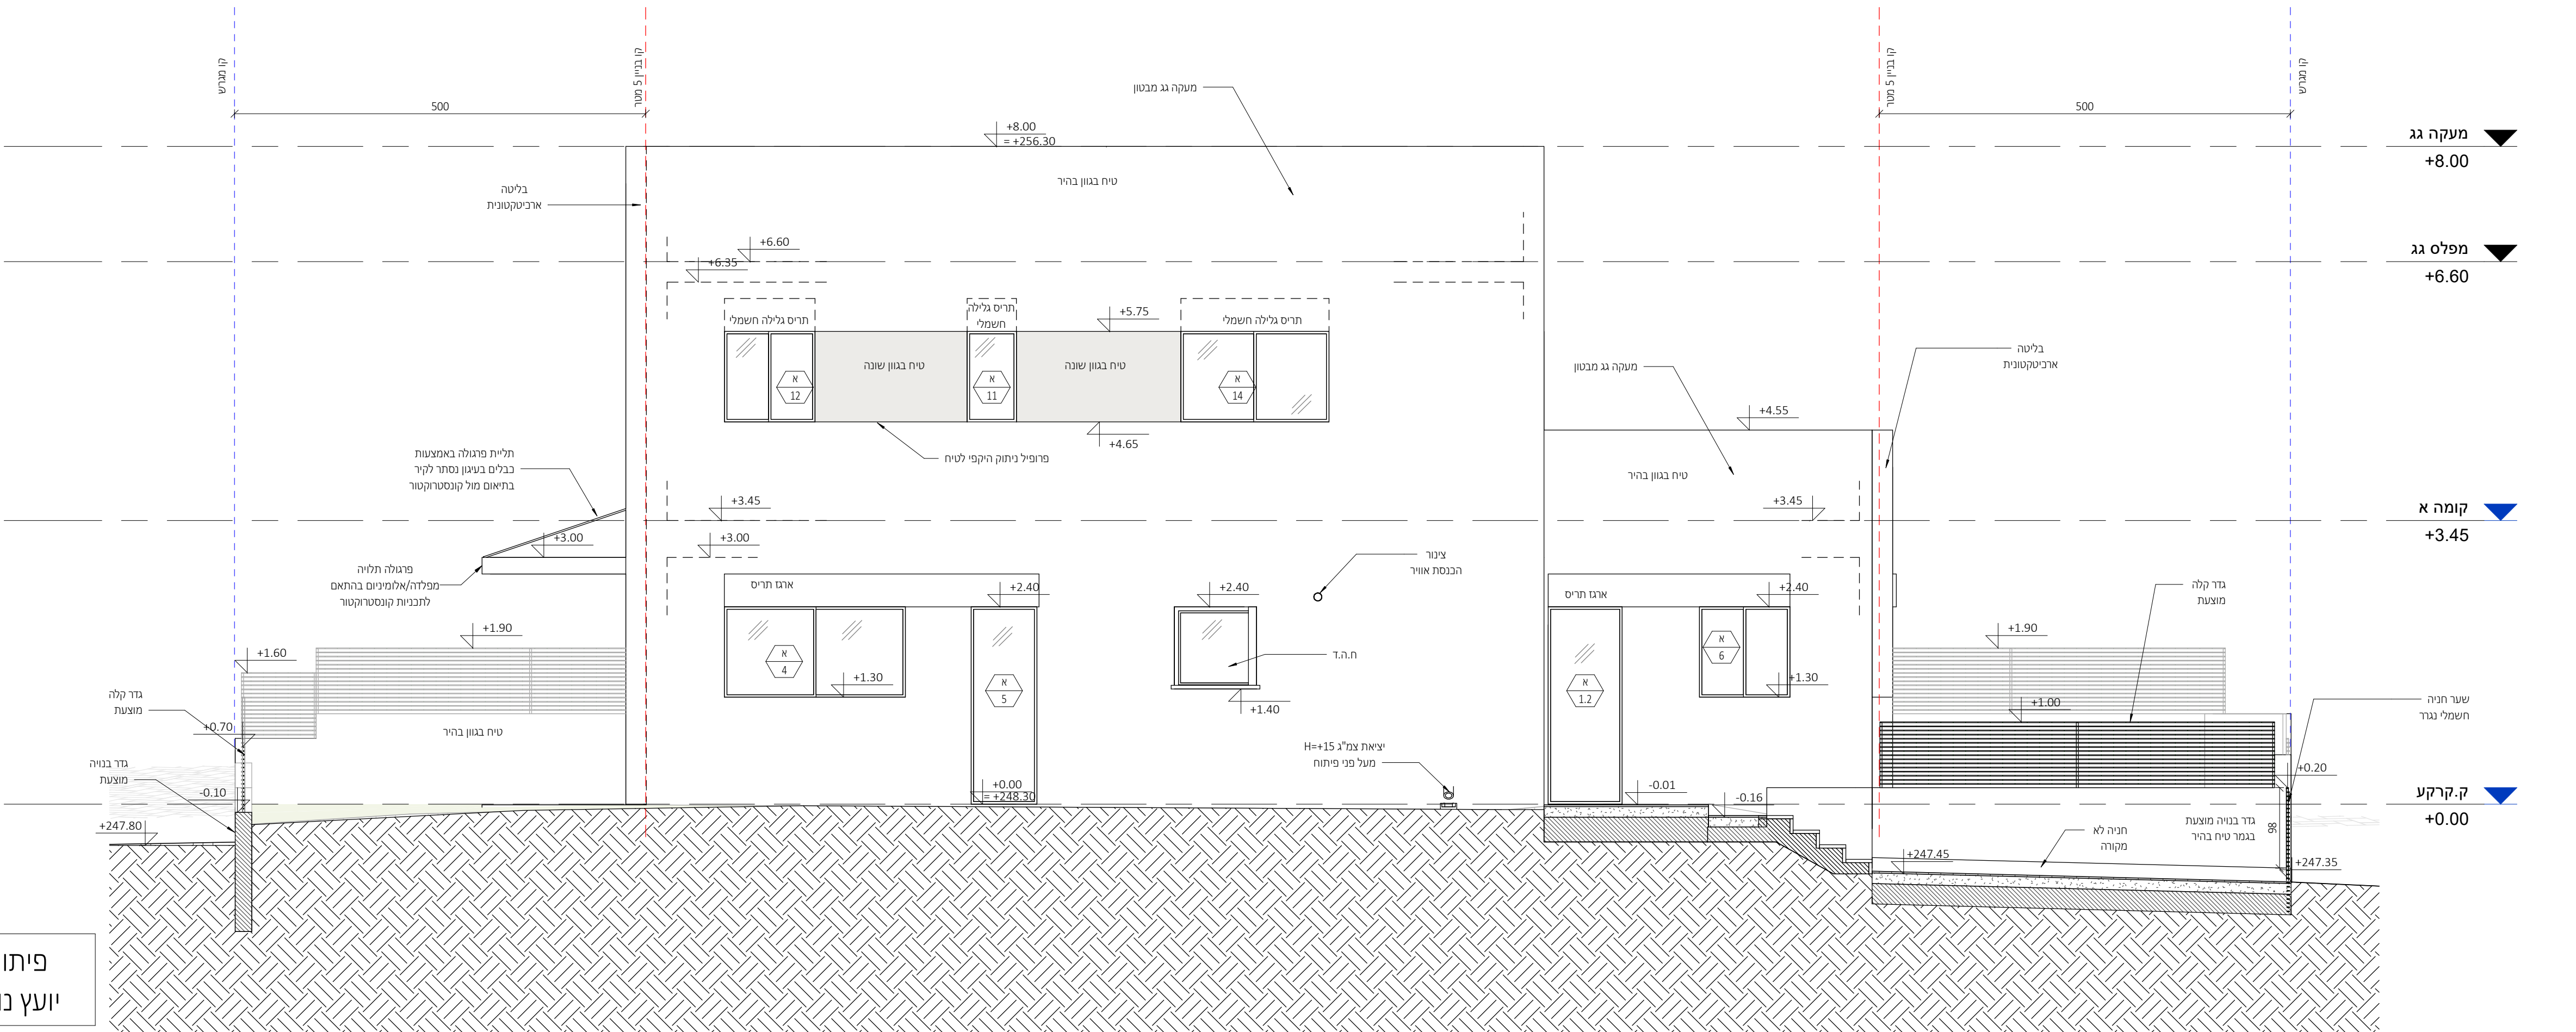

פיתוח נוף עפ"י תוכניות
יועץ נוף ראה פירוט בנפרד

חזית מערבית

1 : 50


פרטי איטום, בידוד וניקוז עפ"י תכניות יועצים ובאחריות הקבלן

מתכונים:


ניהול פרויקט	מהיסוד - בן סולומון
פיקוח	מהיסוד - בן סולומון
קונסטרוקציה	ערן שילר
מיוזג אוויר	אייל ארז מהנדסים ויועצים בע"מ
אינסטלציה	איתן אלמסי
חשמל	איתן בסיס
אלומיניום	
נוף	נתי בלוקא
חשמל חכם	
חימום תת רצפתי	
איטום	צבי טל
אקוסטיקה	
מעליות	
קרקע וביסוס	דיה הנדסת קרקע וביסוס
ירשוי	

[illegible][illegible]


אדריכלות

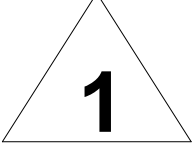CLIENT NAME:	המספר	
קבוצת רכישה נופיה		
PROJECT NAME:	הפרויקט	
נופיה - מגרש 14		
DRAWING NAME:	התוכנית	
חתכים		
SHEET NUMBER:	פרגמנט	
A3-3-100		
SCALE:	קנה מידה:	EDITION:
1 : 50	000000	
STATUS:	למכר	000000 ע"י
	נבדק ע"י	
DATE:	22.09.25	ירד

office@nh-arch.com
www.nh-arch.com

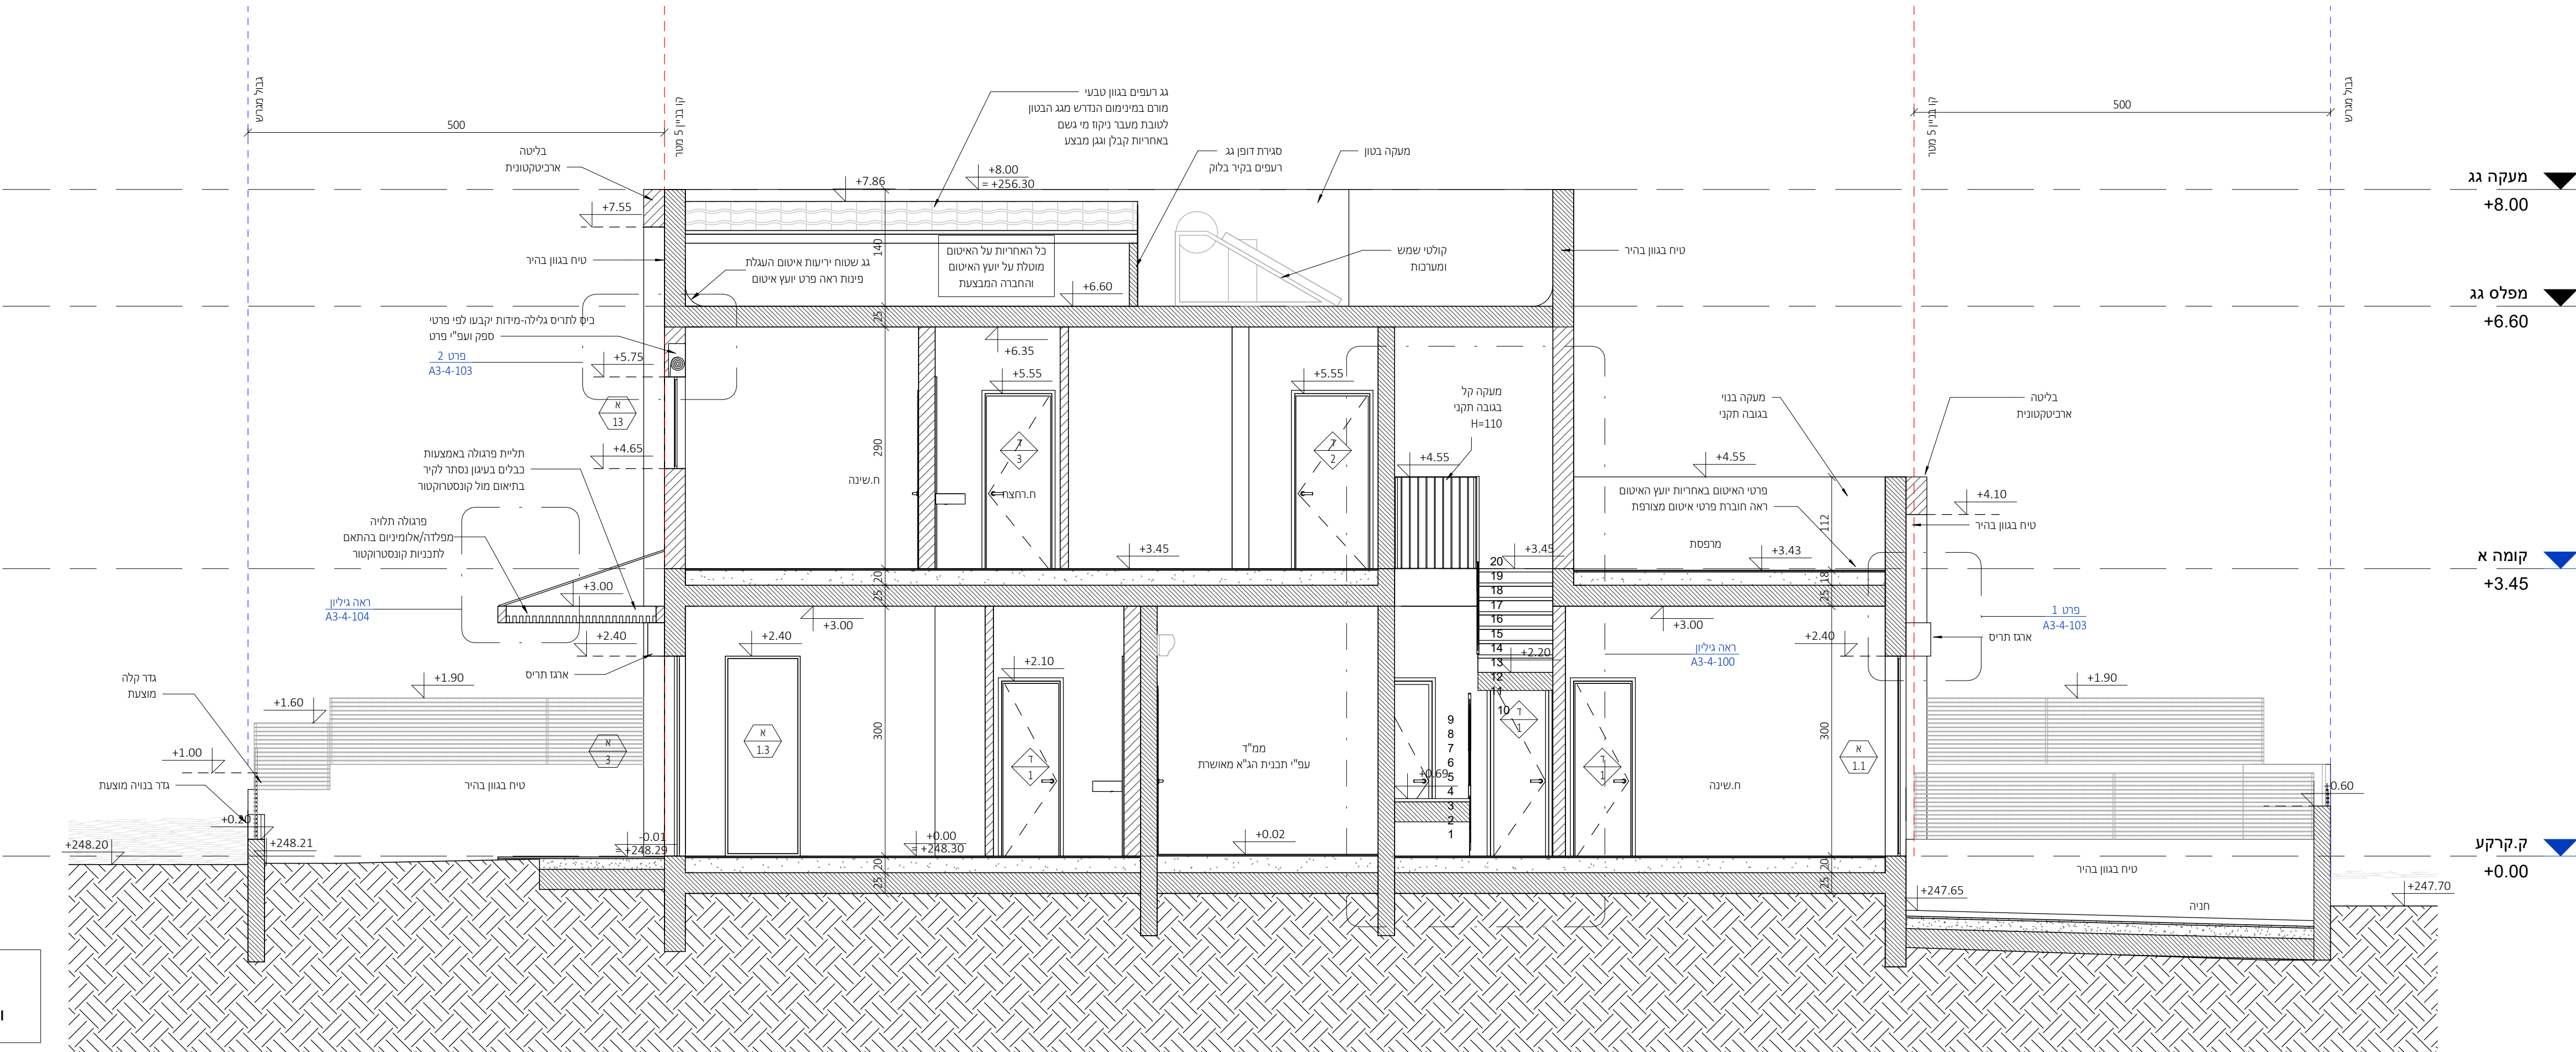

פיתוח נוף עפ"י תוכניות
ועץ נוף ראה פירוט בנפרד

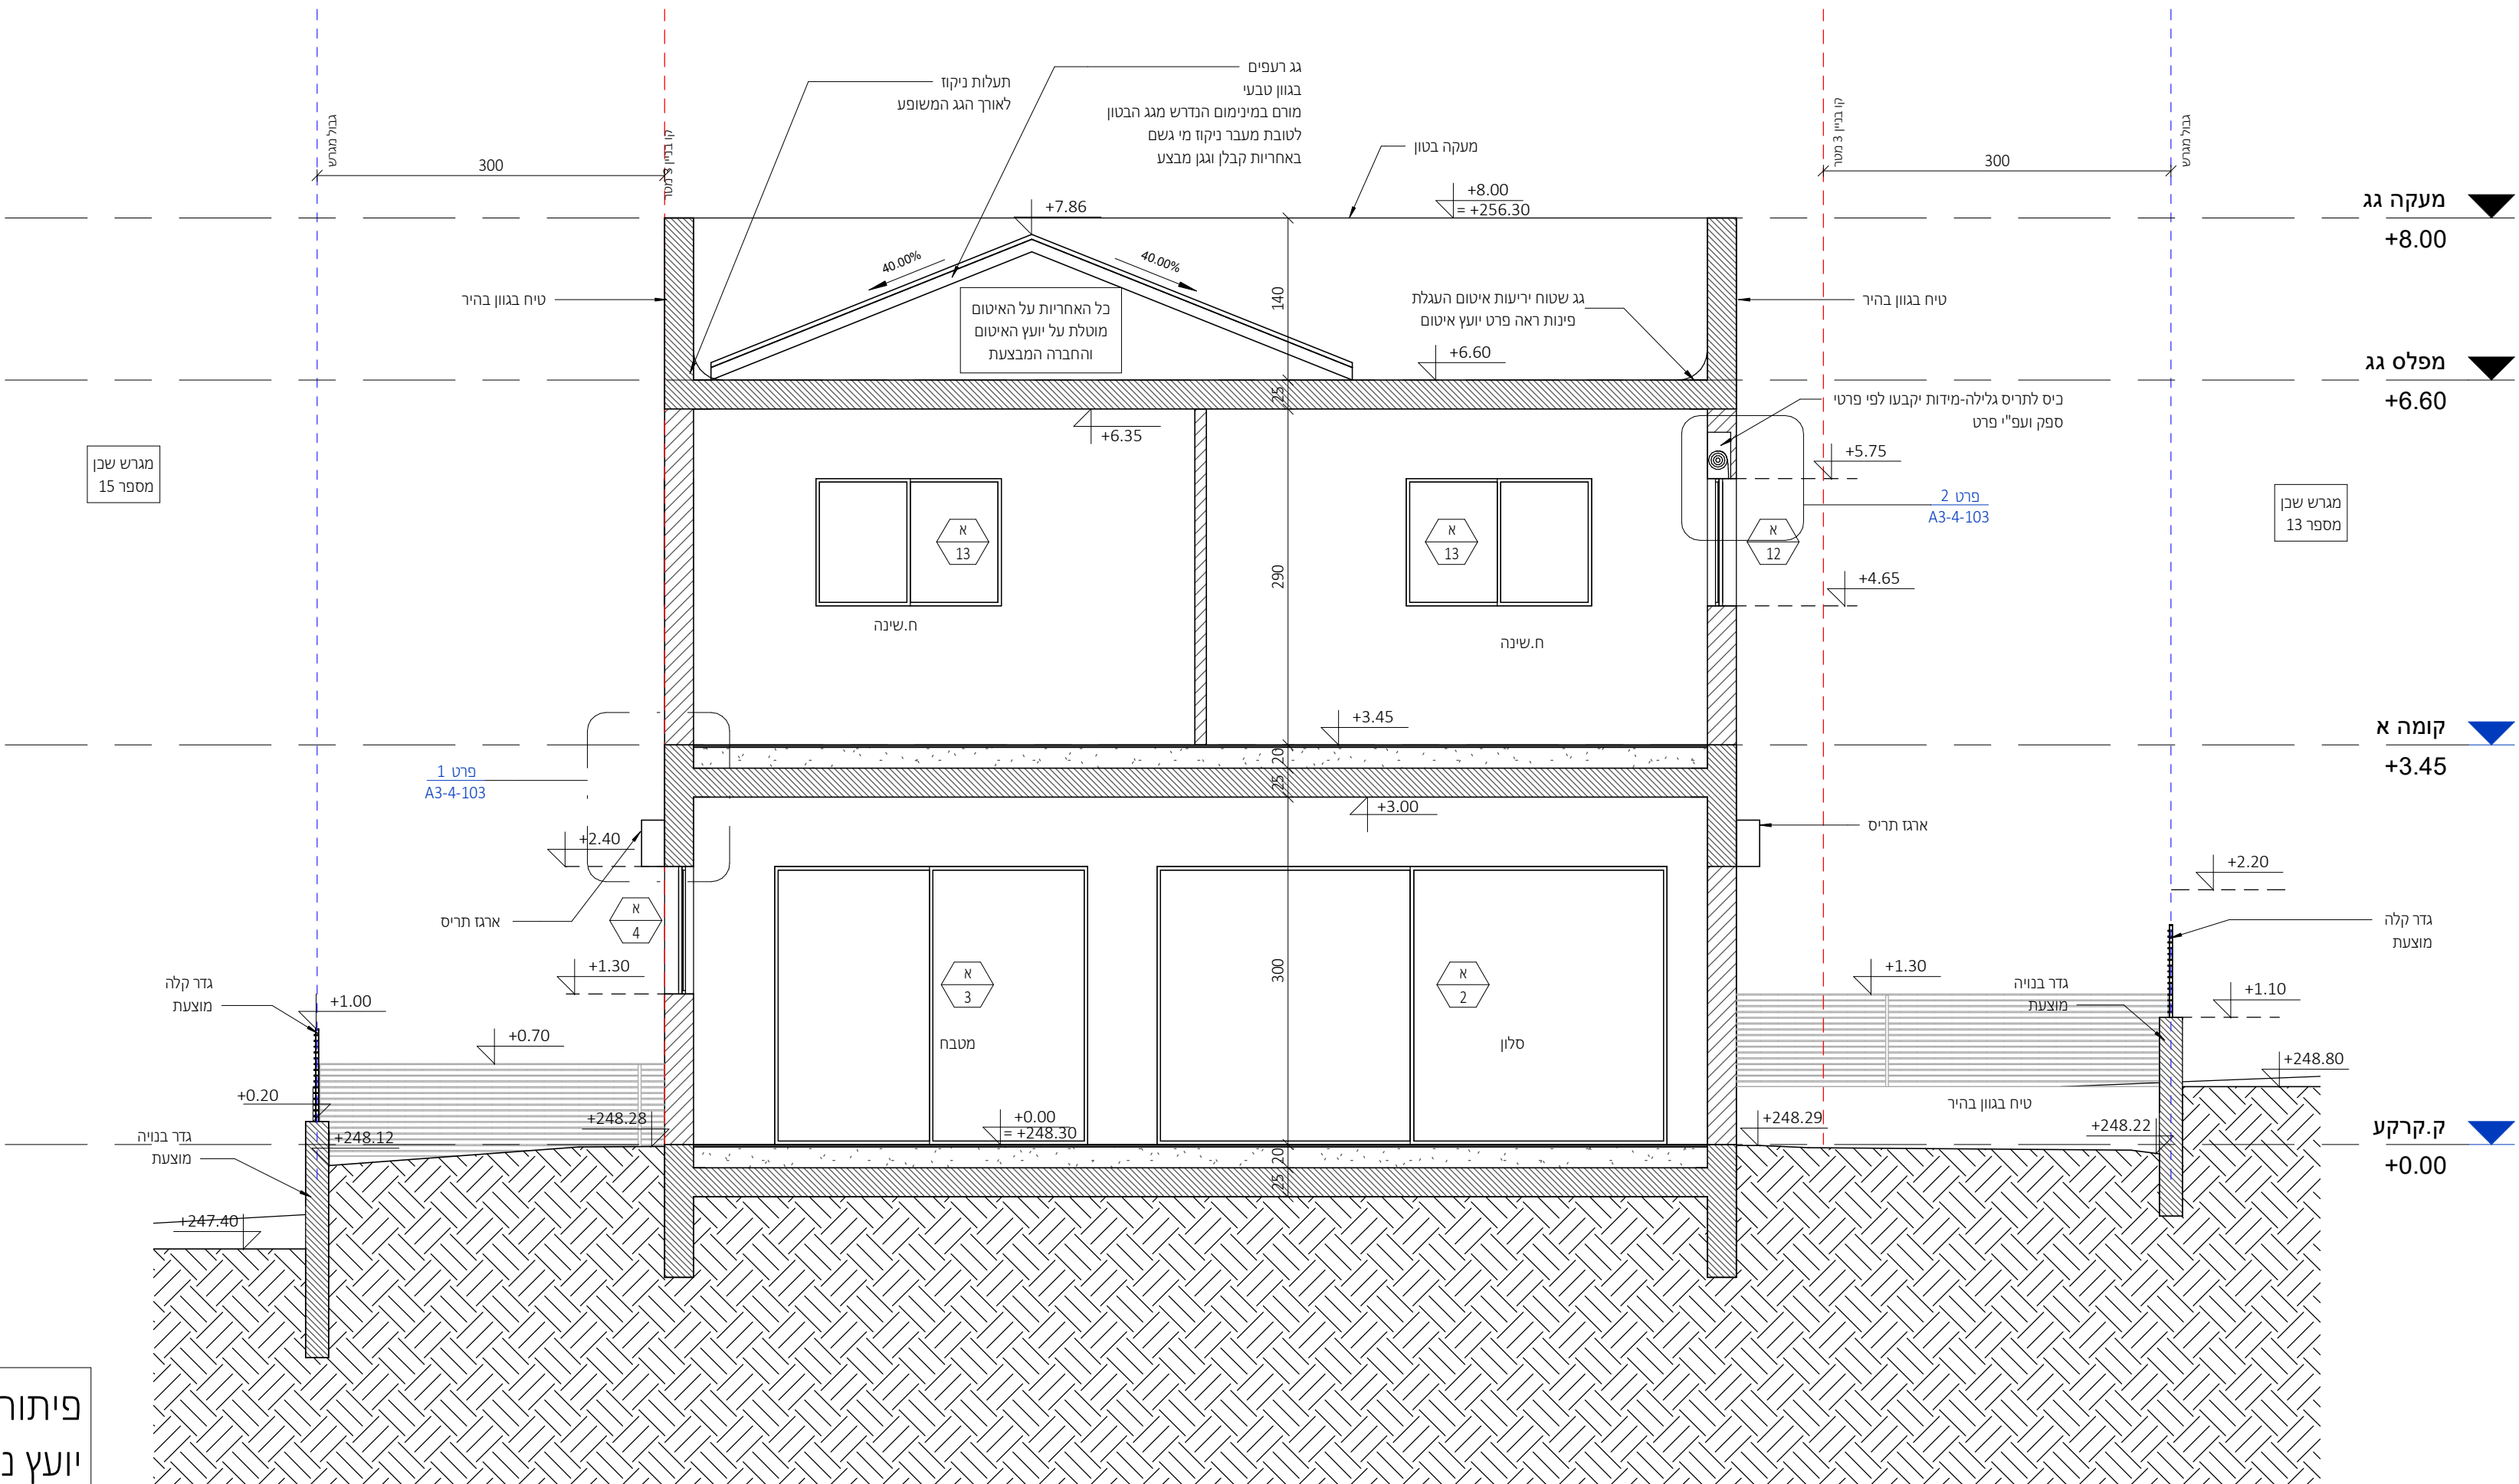

פיתוח נוף עפ"י תוכניות
יועץ נוף ראה פירוט בנפרד

חֶתֶךְ א-א

1 : 50

חתך ב-ב

1 : 50

מתכננים:

ניהול פרויקט
מהיסוד - בן סולומון
פיקוח
מהיסוד - בן סולומון
קונסטרוקציה
ערן שילר
מיזוג אוויר
אייל ארז מהנדסים ויועצים בע"מ
אינסטלציה
איתן אלמסי
חשמל
איתן בסיס
אלומיניום
בופ
נתי בלוקא
חשמל חכם
חימום תת רצפתי
איטום
צבי טל
אקוסטיקה
מעליות
קרקע וביסוס
דיה הנדסת קרקע וביסוס
ירשני

± 0.00 = +248.30
הערות: 1. תכנית זו הי לקראת יריד עם תכנית הריטשים. 2. גובה אומדני - ראו תכנית פיתוח. 3. המידות הן בין קירות הבניה ולא כולל פיטום. 4. פיטום השטח סביב המבנה, כולל, מדרגות, גדרות, שנילים, ריצופים, שפיטים, גדרים, חניה וגגות לא תכנית פיתוח. 5. איטום קירות ורצפות המבנה כמעט עם הקרקע ובנידוד תרסי לאורך העמודים והקירות של קומות - כלירות זה עם סימני גיטון - ראו תכנית קונסטרוקציה. 6. אי דים יבוצע בכל מישור אופקי הכולל חתוכיו. 7. סוף תרסי במסיד - ע"פ מפרט תרומקור, מאופשר טיי פיקוד המוקד.
המבצע אחראי לסידות : עליו לבקר ולבדוק את כל המידות הבחנית והקטעות הנבדורות. במסגרת של שטח זה אי התאמה הבחנית /או בבנין, עליו להודיע על כך מיד לאדריכל במסגרת המשרד המבצע ובמבדורות. המבצע יישמש את ויק הבחנית שאומדן לכניסיו. המבצע יחזיק באחר, בכל מה, של מחדש של תכנית. אח לקבוע מידות על ידי חזירה בשטח. התכנית תהיה תרסה האדריכל ואין לשנות כל שימוש בה או ברעיונות הגלומים בה, אלא באישור בכתב מהאדריכל. מחדש /או יושא אשר שמו רשום בתכנית זו, נושא לכיד באחריות המקצועית והתקנית לתכנית. על המפקח והמבצע לודא התאמת התכנית האדריכלית "כניסיו" לתכנית יחידה, המכר והתכנית האומדות על כל גורמים ורשימים. התכנית כוללת את כל האומדות והידוע על ליום תחפציה.

משרד קירות:

קיר בלוק
קיר בסון
מחוד בסון

תאריך	תיאור	מהדורה
22.09.2025	מכרז	1


אדריכלות

שם המסמך:	CLIENT NAME:
קבוצת רכישה נופיה	
שם הפרויקט:	PROJECT NAME:
נופיה - מגרש 14	
שם הגיליון:	DRAWING NAME:
גליון מדרגות	
מספר גליון:	SHEET NUMBER:
A3-4-100	
החידורה:	EDITION:
קנה מידה:	SCALE:
As indicated	
סטוס:	STATUS:
למכרז	
שורסר עיי:	נבוק עיי:
תאריך:	DATE:
22.09.25	




נירסן חיינר אדריכלים
מודד התודיס 2, בית חירות
09-954642 78
www.nh-arch.com
office@nh-arch.com

זכיות יימר / ע"פ הנחיות ע"ד

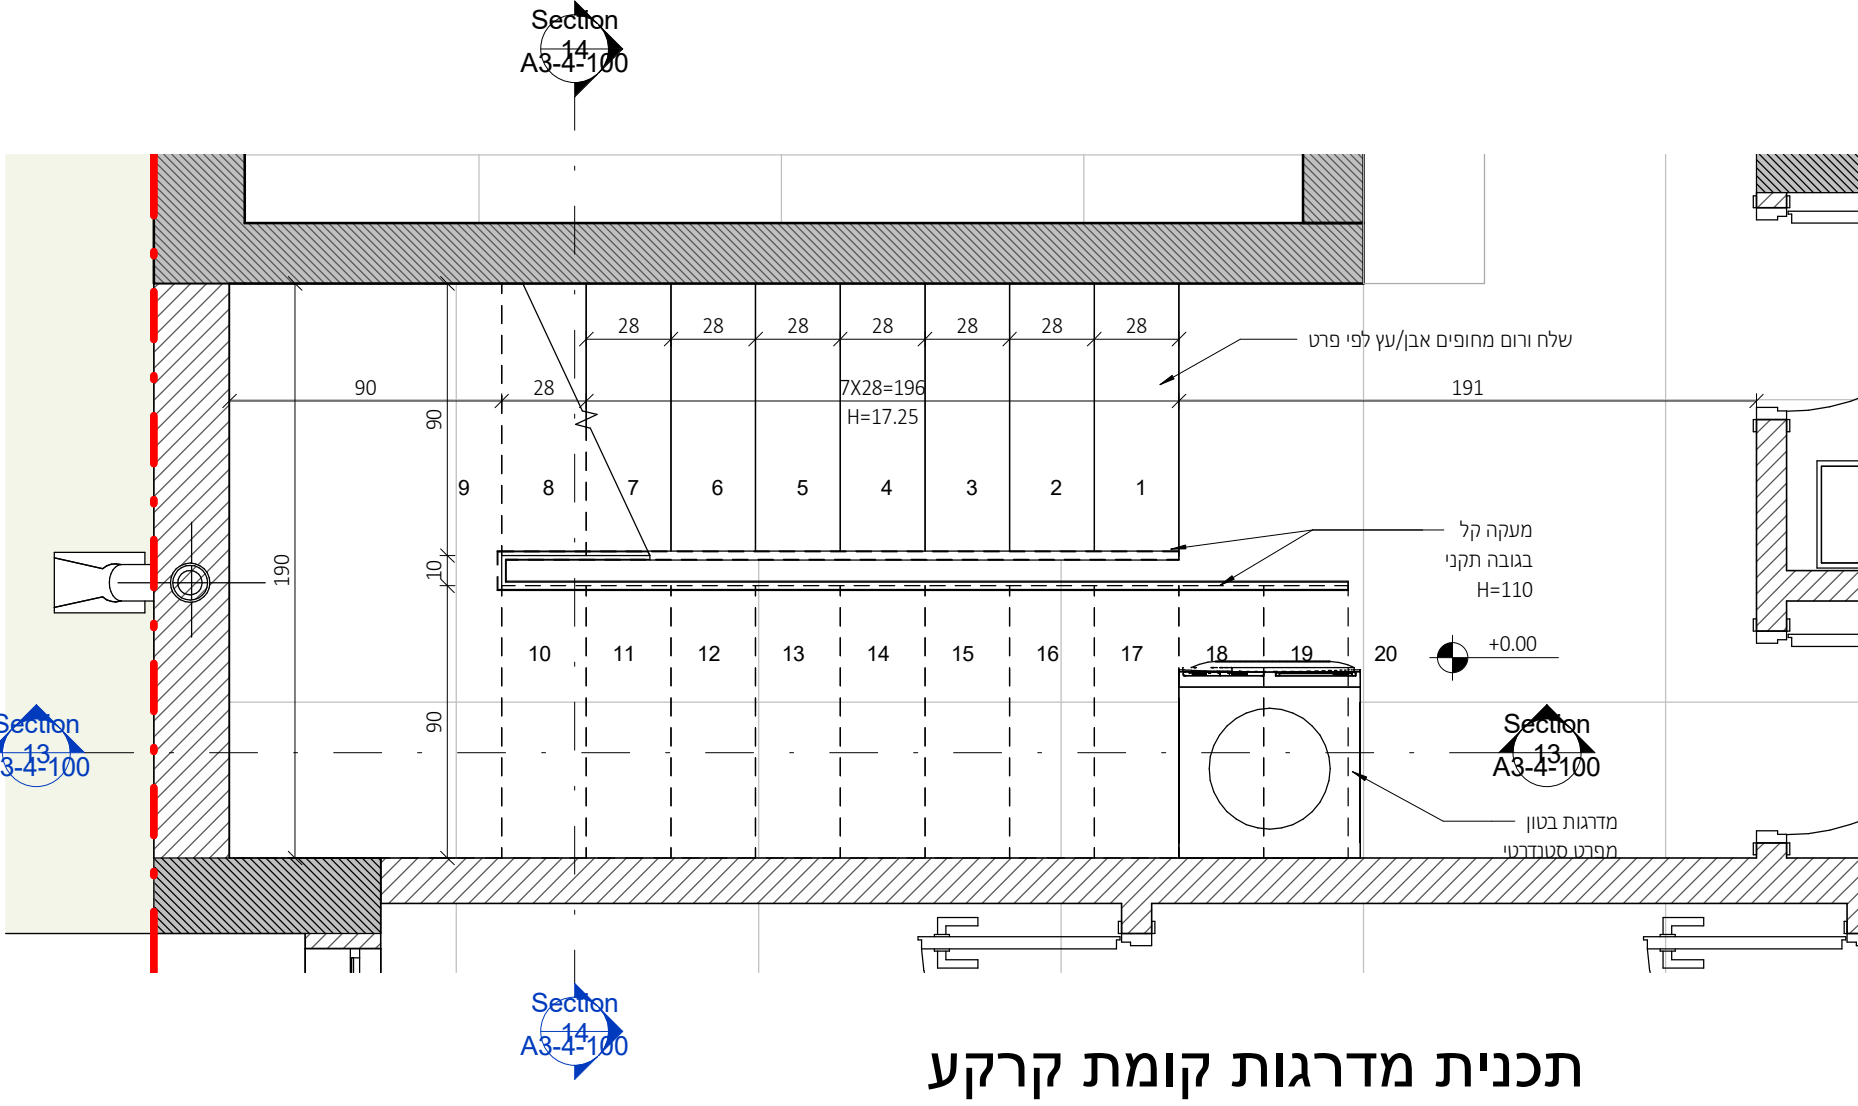


תכנית מדרגות קומת קרקע

1 : 25

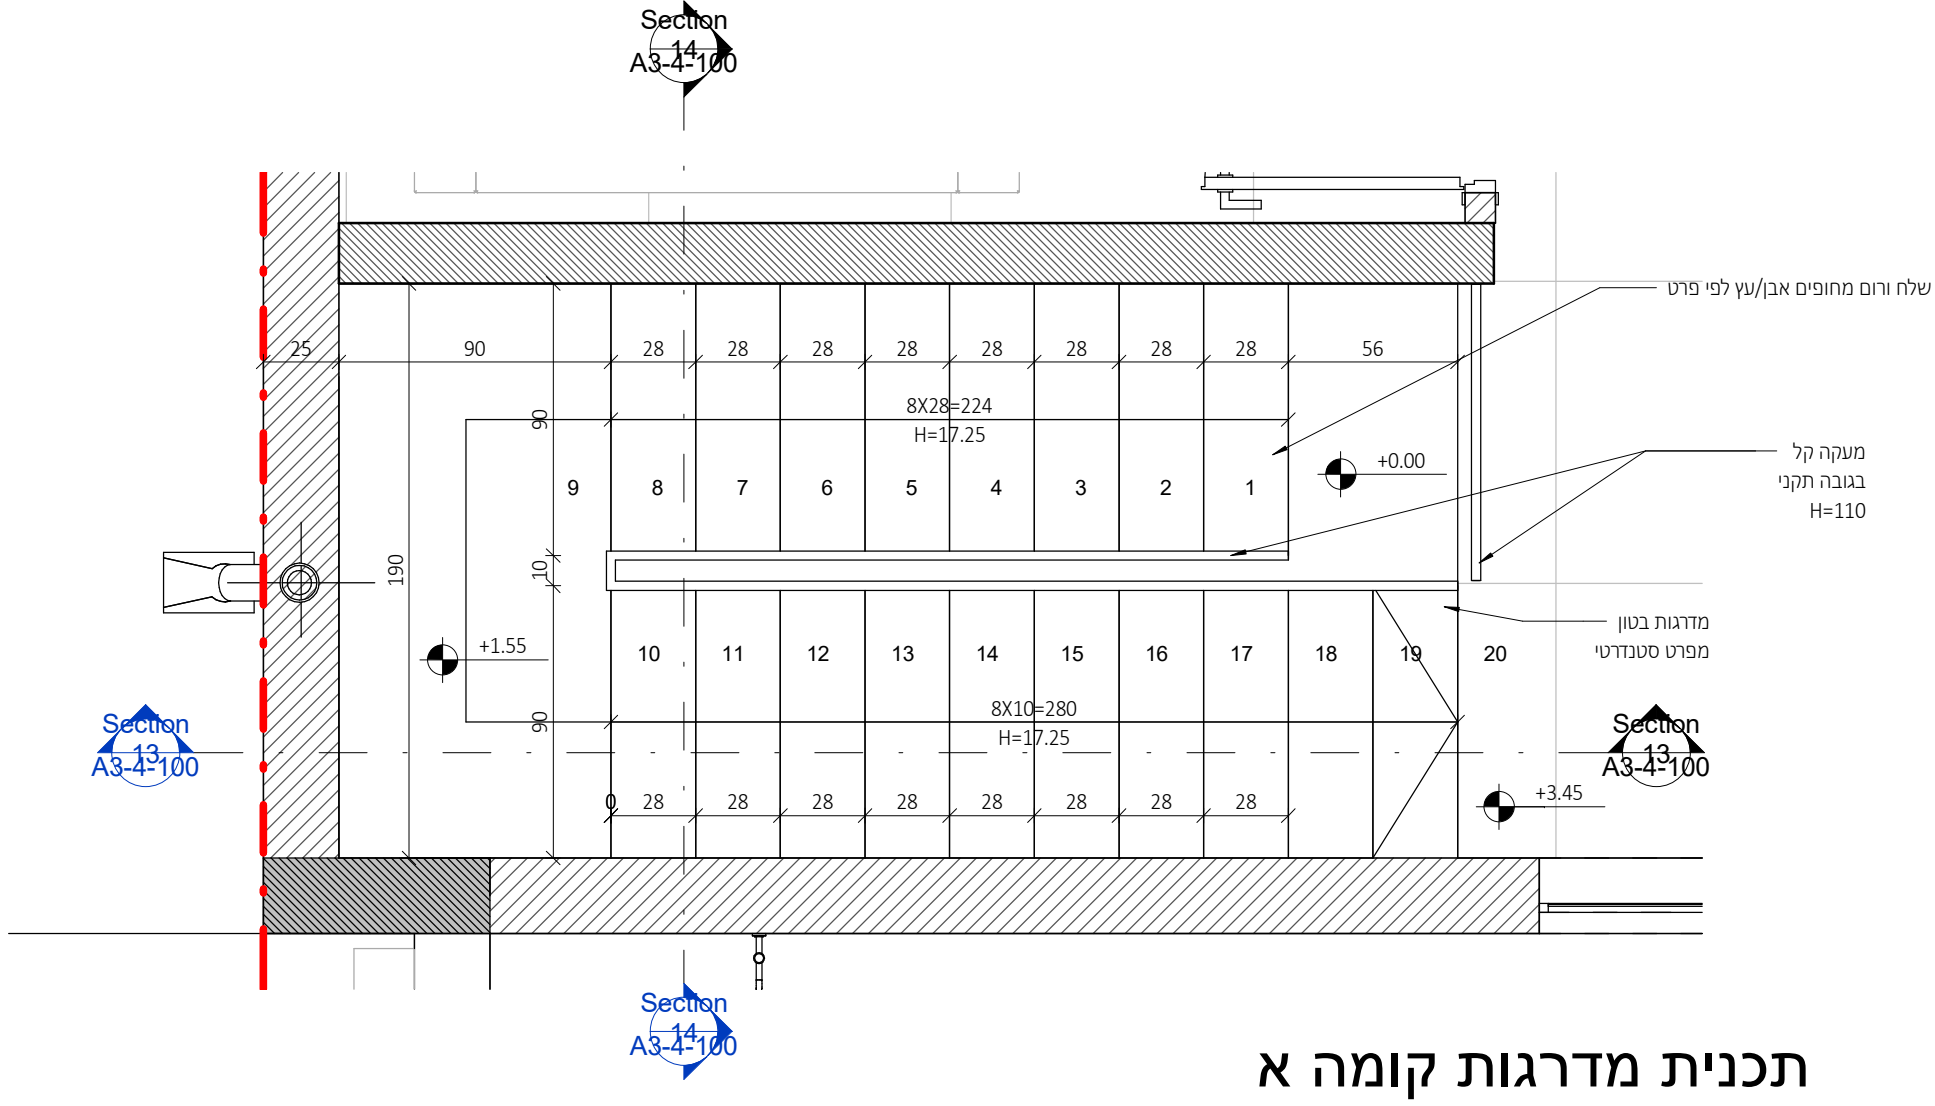

תכנית מדרגות קומה א

1 : 25

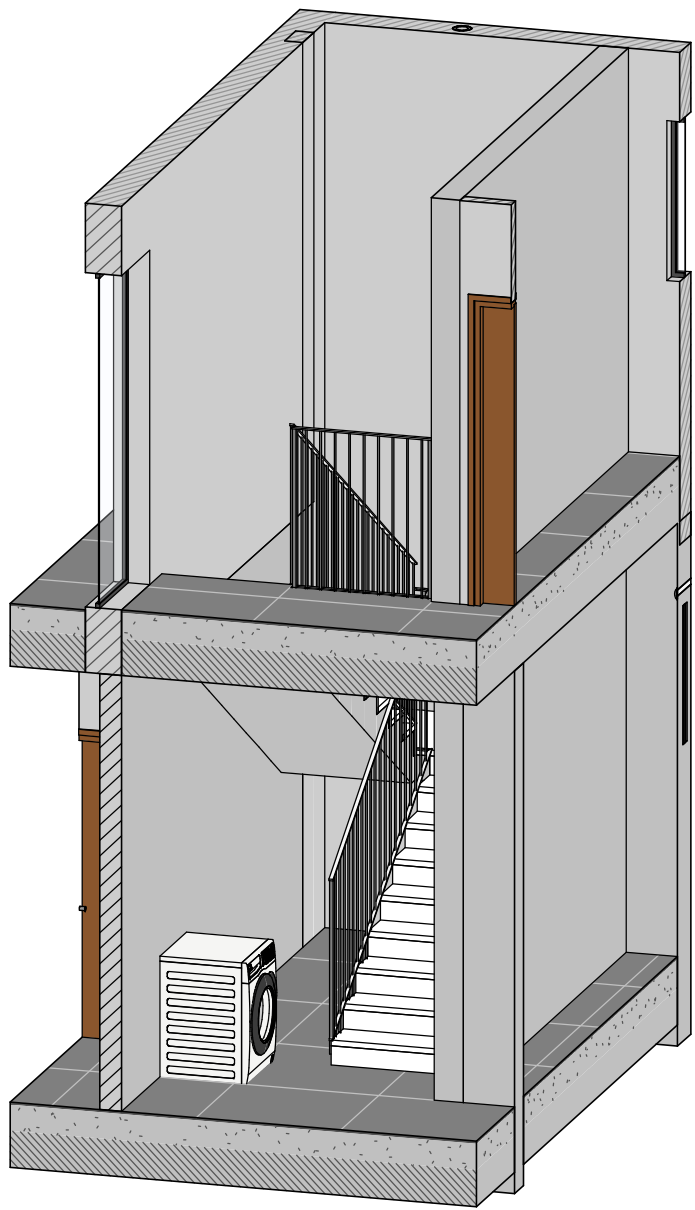


להמשך תיאום

דגם נבחר

מדרגות סטנדרטיות - מפרט סטנדרטי


על הקבלן לשלוח S.D לאישור אדריכל

יש לבצע התאמה לפרט לאחר בחירת חיפוי המדרגות*

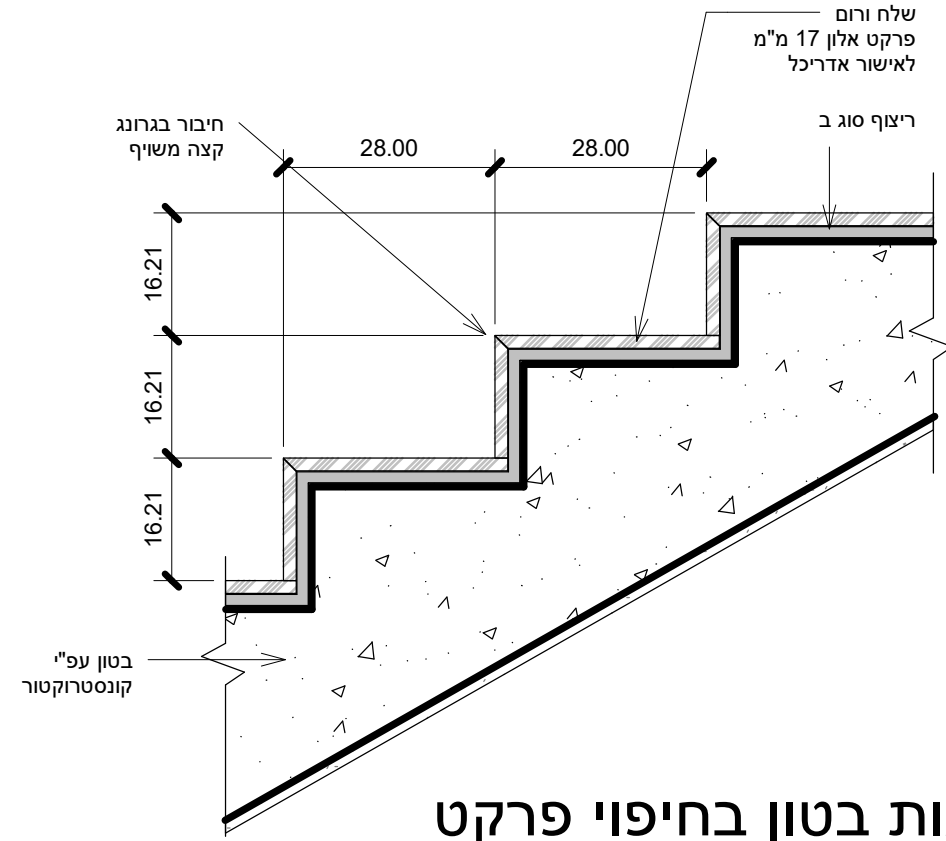

פרט מדרגות בטון בחיפוי פרקט

1 : 10

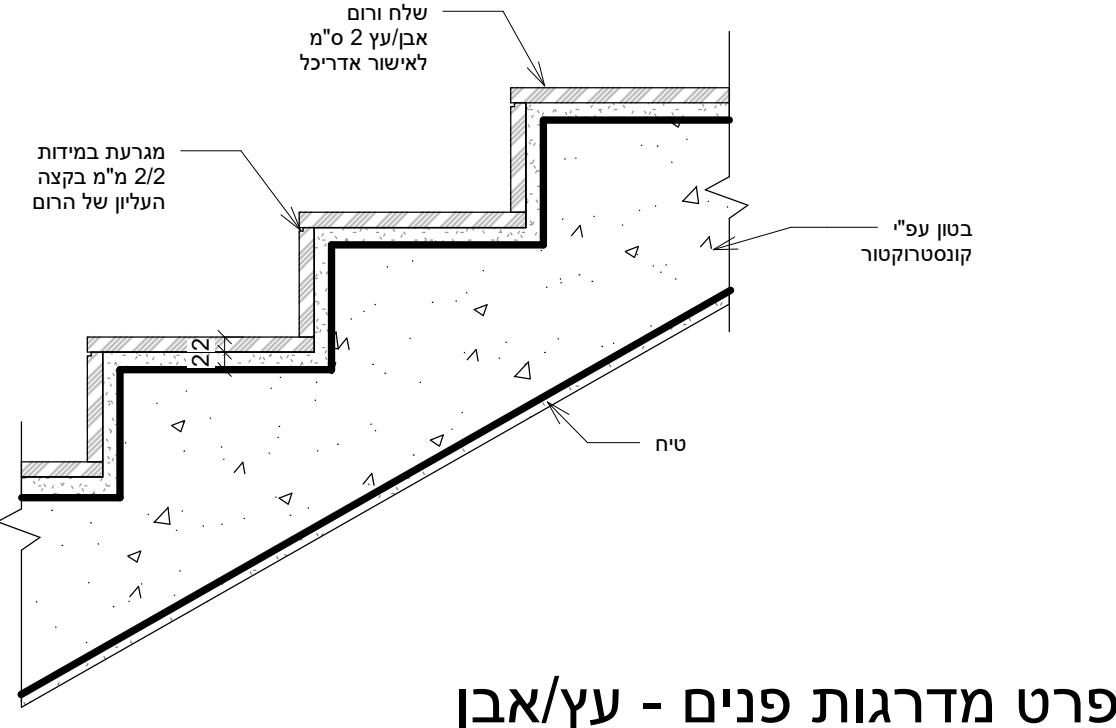


פרט מדרגות פנים - עץ/אבן

1 : 10




תמונה להמחשה בלבד

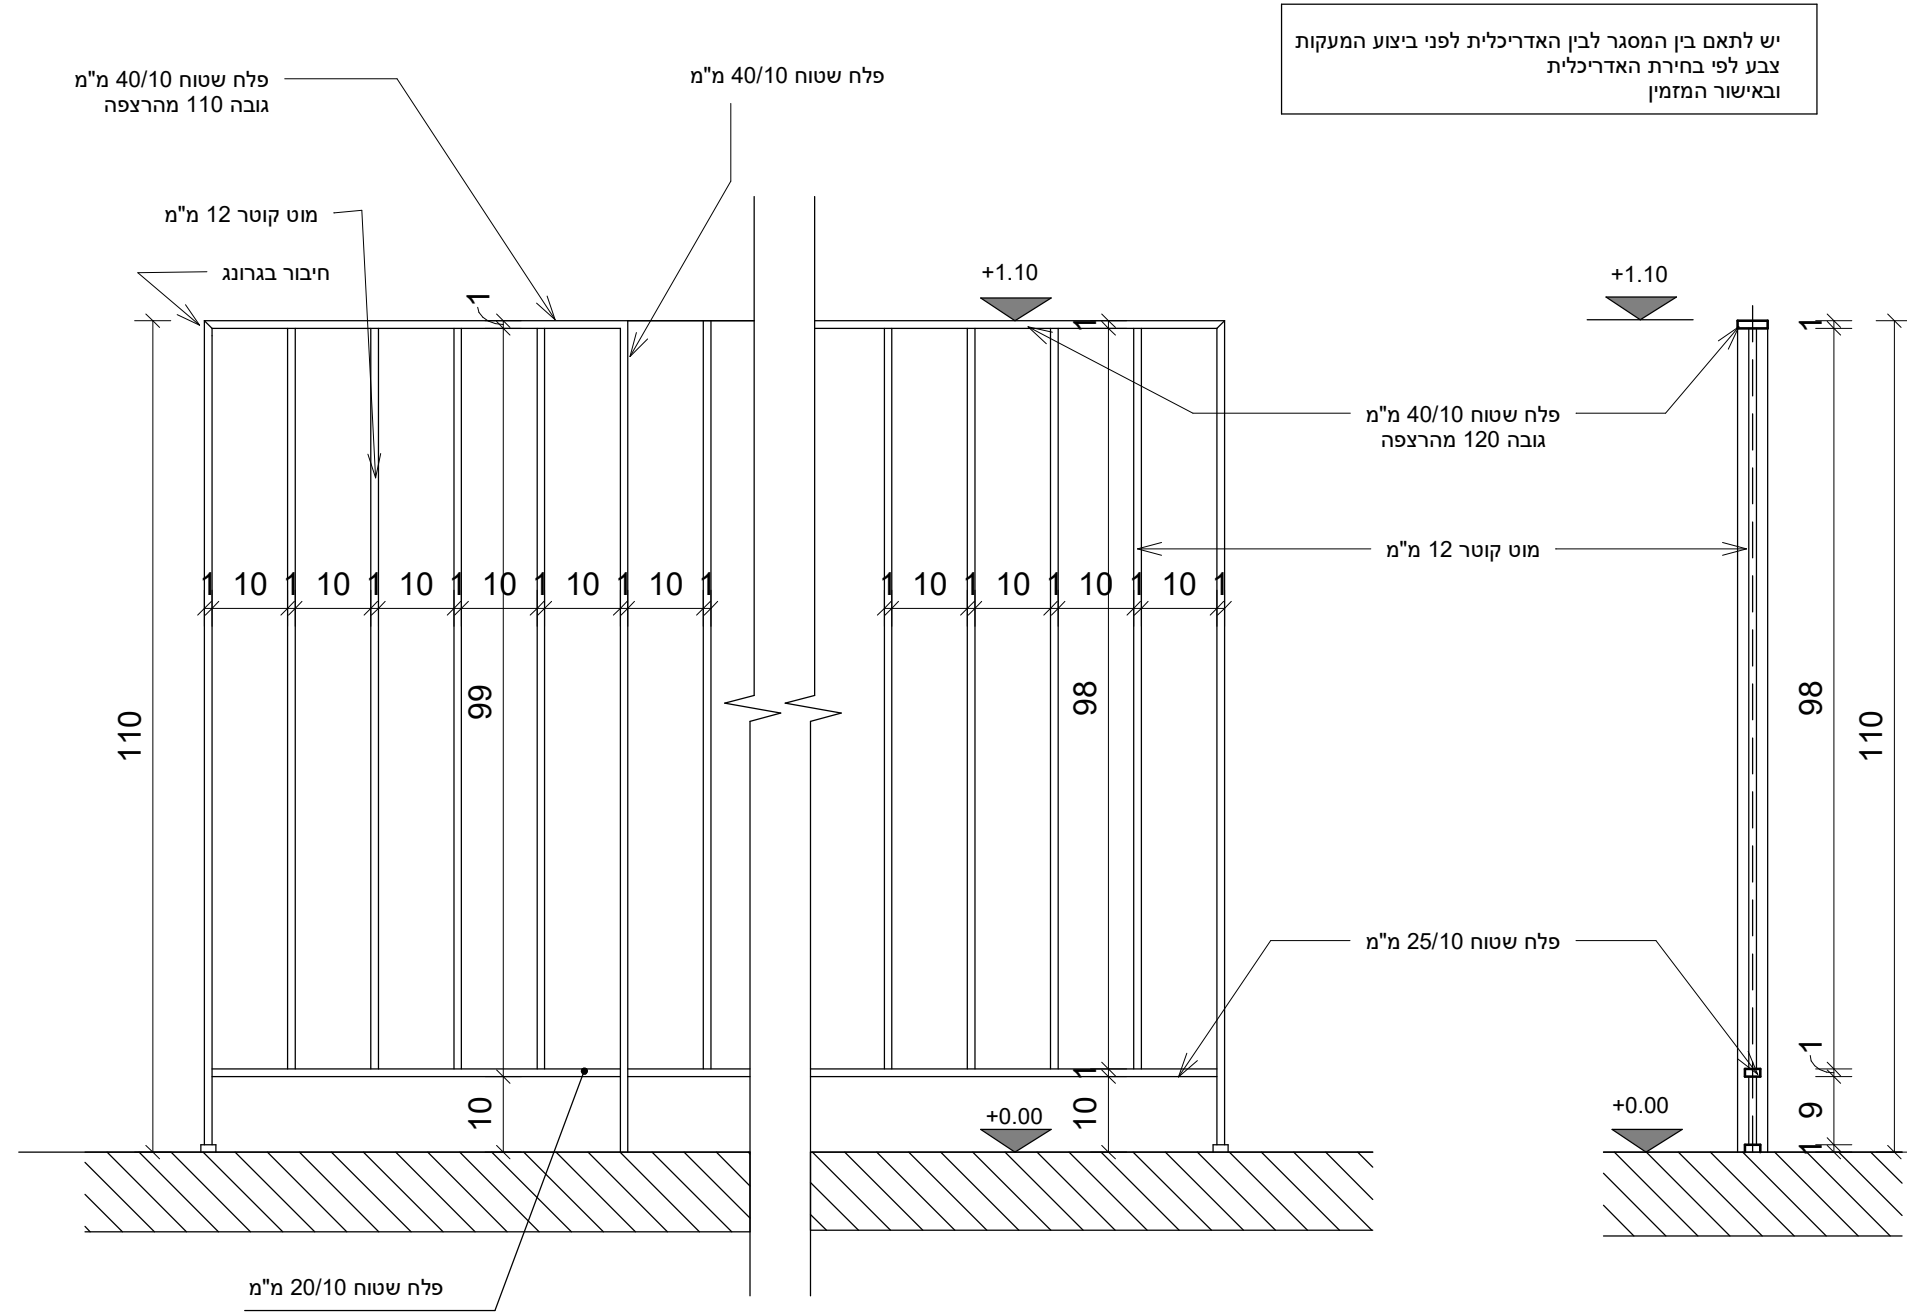


מעקה אנכי

1 : 10

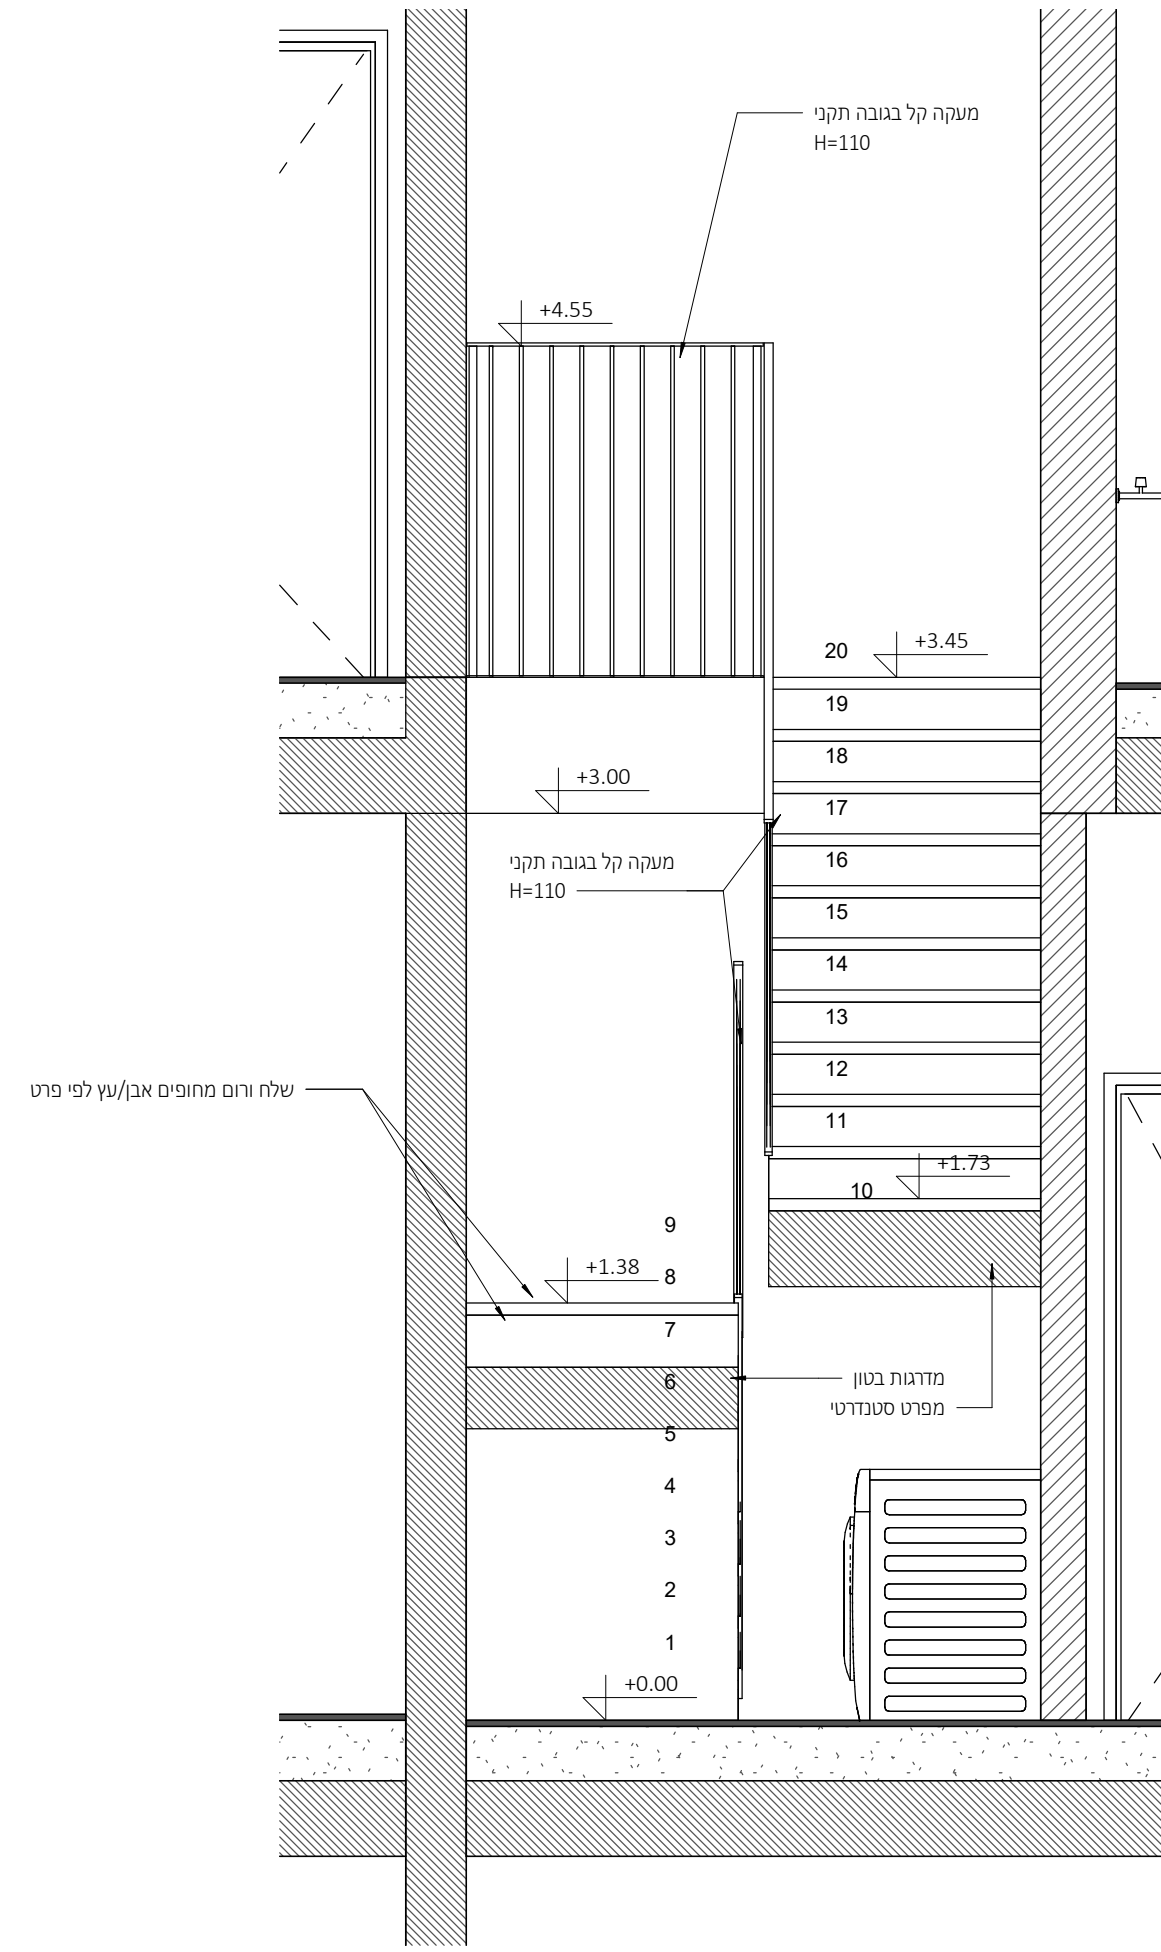

Section 14

1 : 25

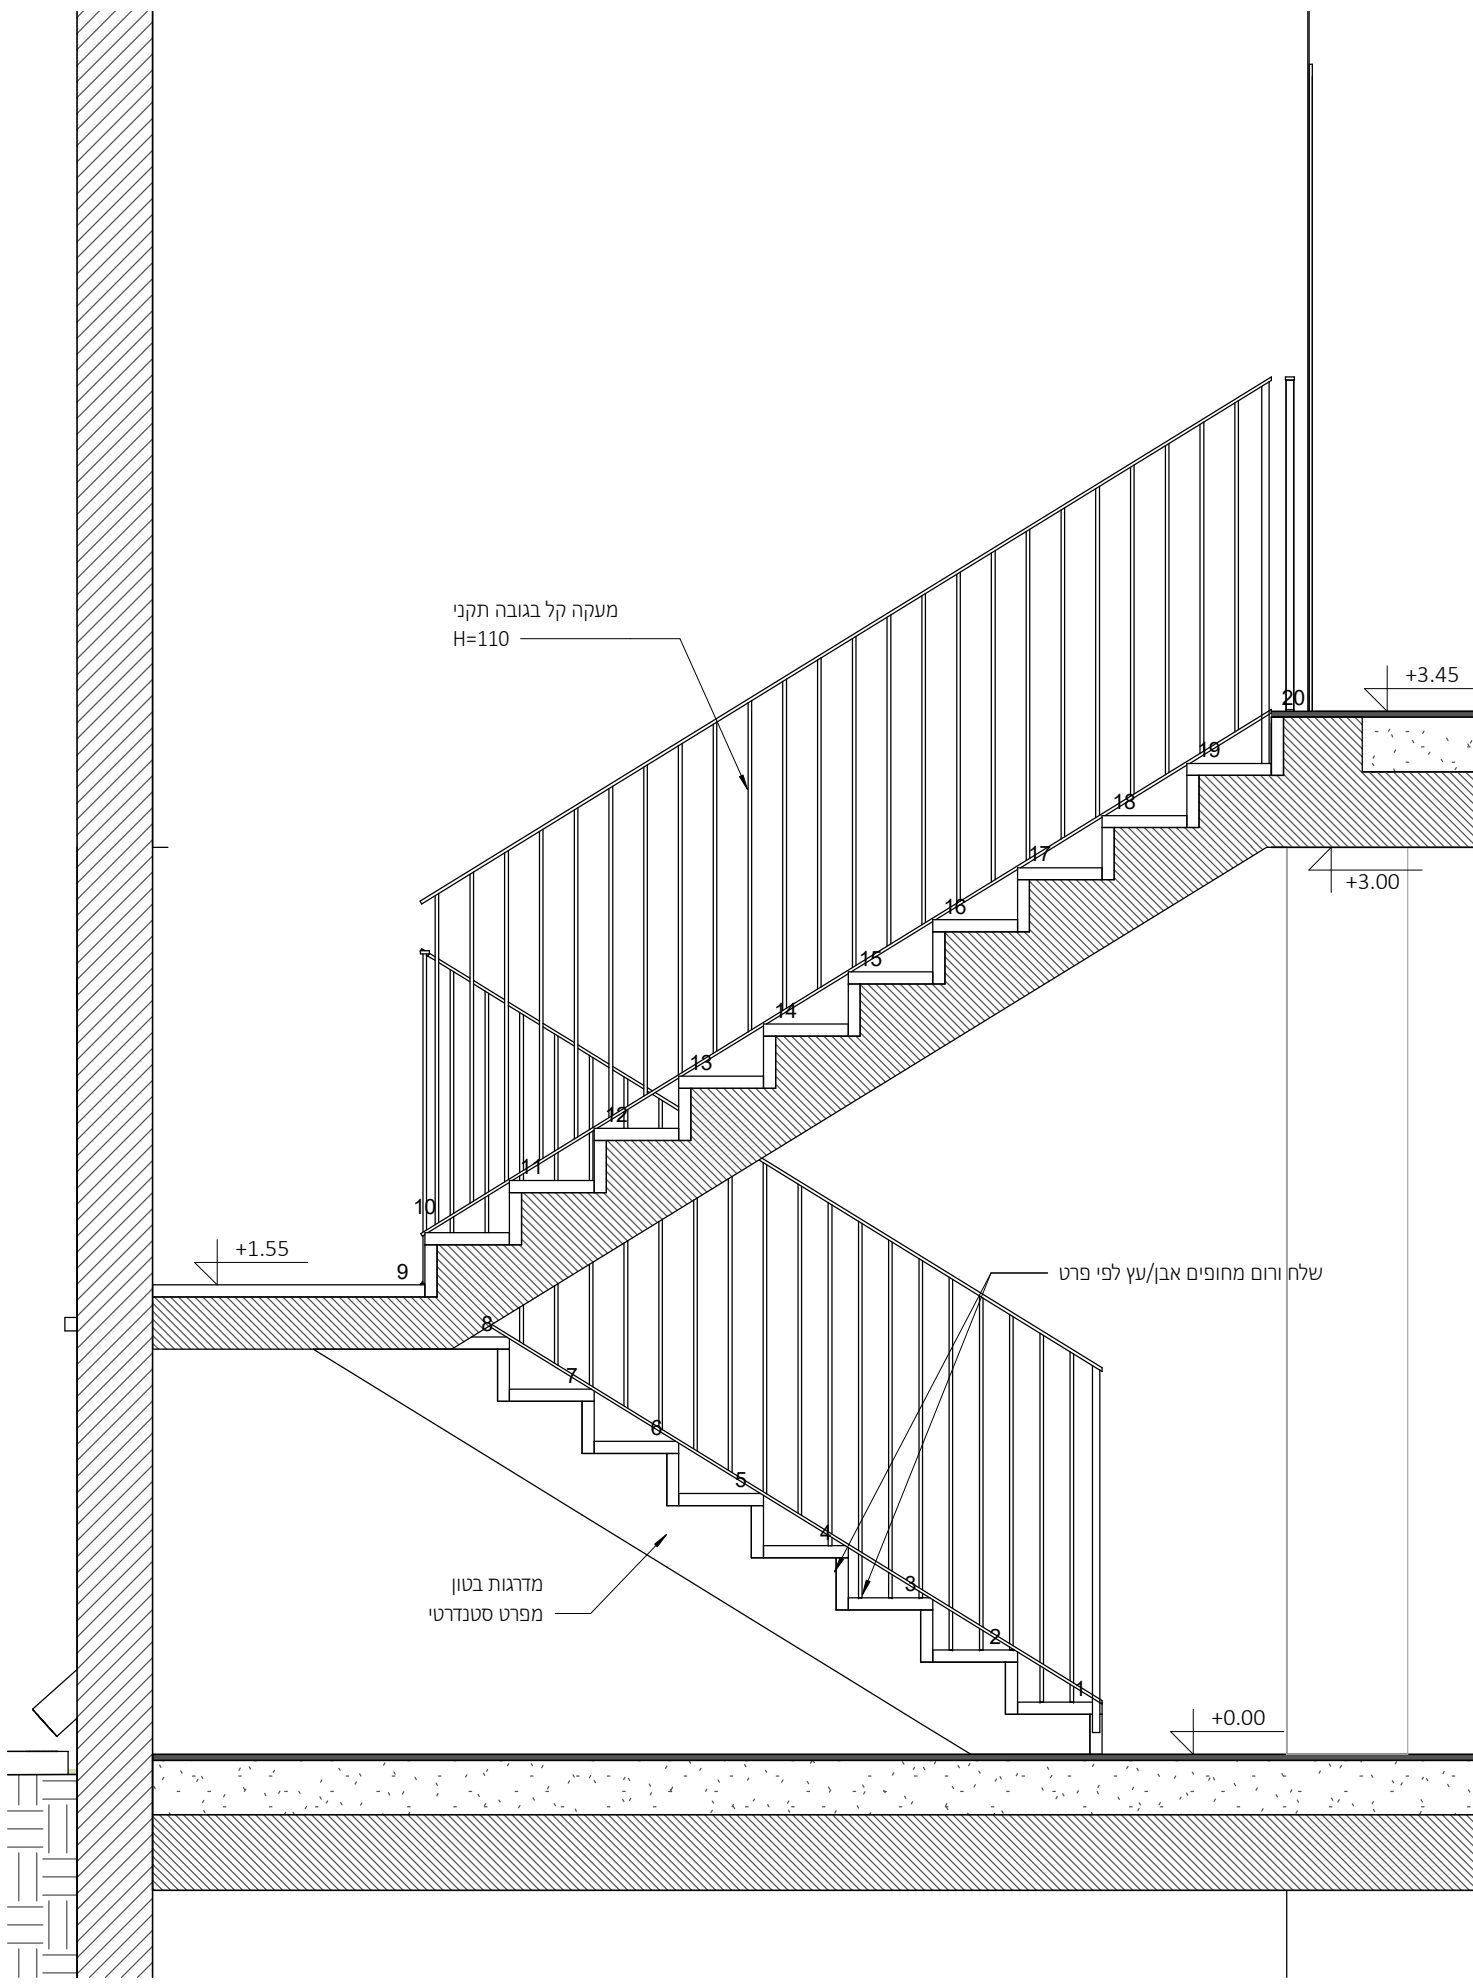

Section 13

1 : 25

ניהל פרויקט
מהיסוד - בן סולומון
פיקוח
מהיסוד - בן סולומון
קונסטרוקציה
ערן שילר
מיזוג אוויר
אייל ארז מהנדסים ויועצים בע"מ
אינסטלציה
איתן אלמסי
חשמל
איתן בסיס
אלומיניום
נוף
נתי בלוקא
חשמל חכם
חימום תת רצפתי
איטום
צבי טל
אקוסטיקה
מעליות
קרקע וביסוס
דיה הנדסת קרקע וביסוס
רישוי

[illegible]


PROJECT NAME:		הפרויקט:	
קבוצת רכישה נופיה			
DRAWING NAME:		שם הנגזר:	
נופיה - מגרש 14			
SHEET NUMBER:		מספר העמוד:	
A3-4-103			
SCALE:	קנה מידה:	EDITION:	הדורה:
As indicated			
STATUS:	סטוס:		
למכר			
DATE:		דפוס ע"י:	
22.09.25		א"ר:	




Neuman-HaynerArchitects

יוסוף חיינר אדריכלים
 חורד המדרס 2, בית חירות
 09-9545842

office@nh-arch.com
 www.nh-arch.com

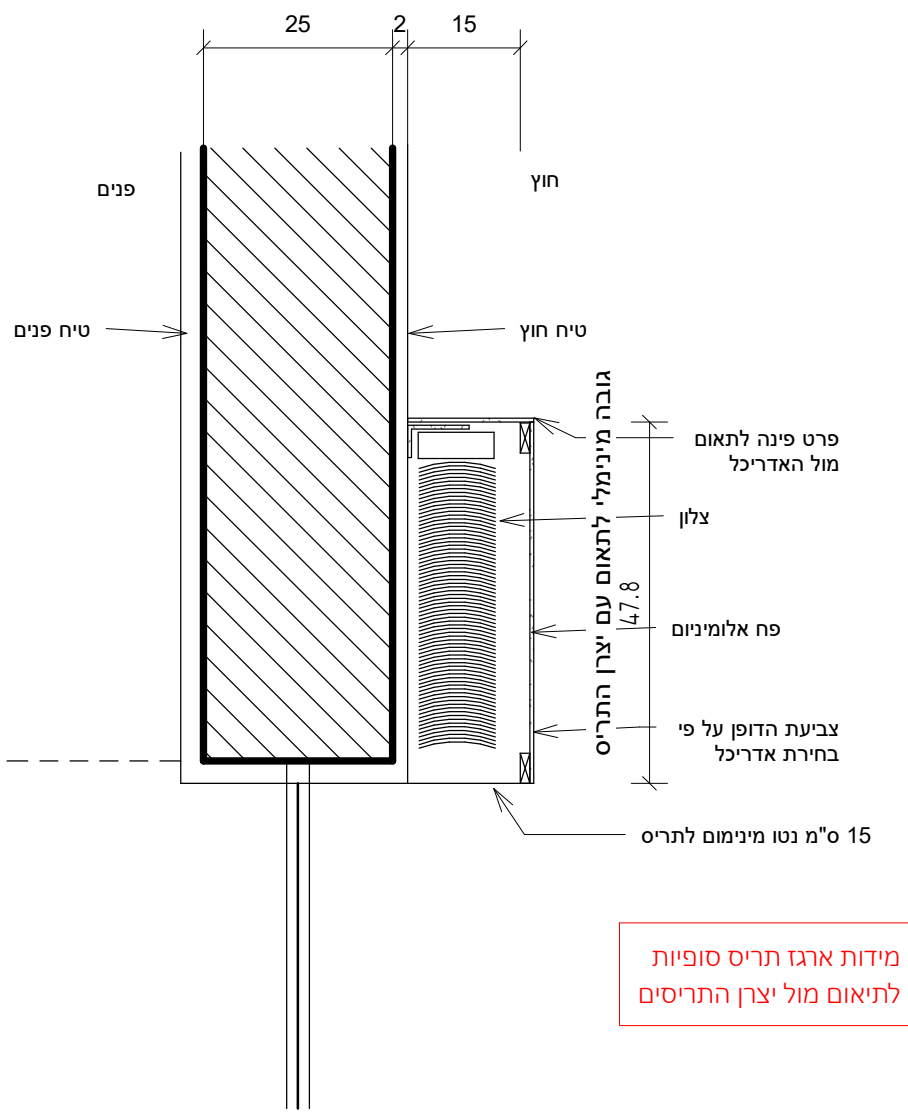


פרט 1 - כיס צלון חיצוני

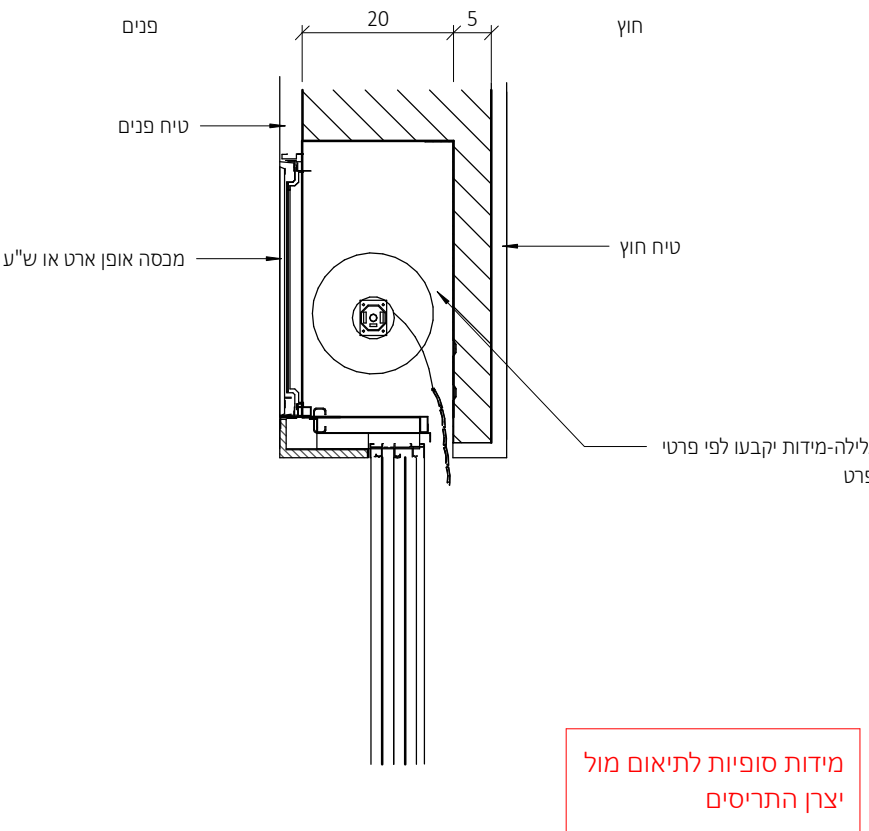


פרט 2 - תריס גלילה

1 : 10

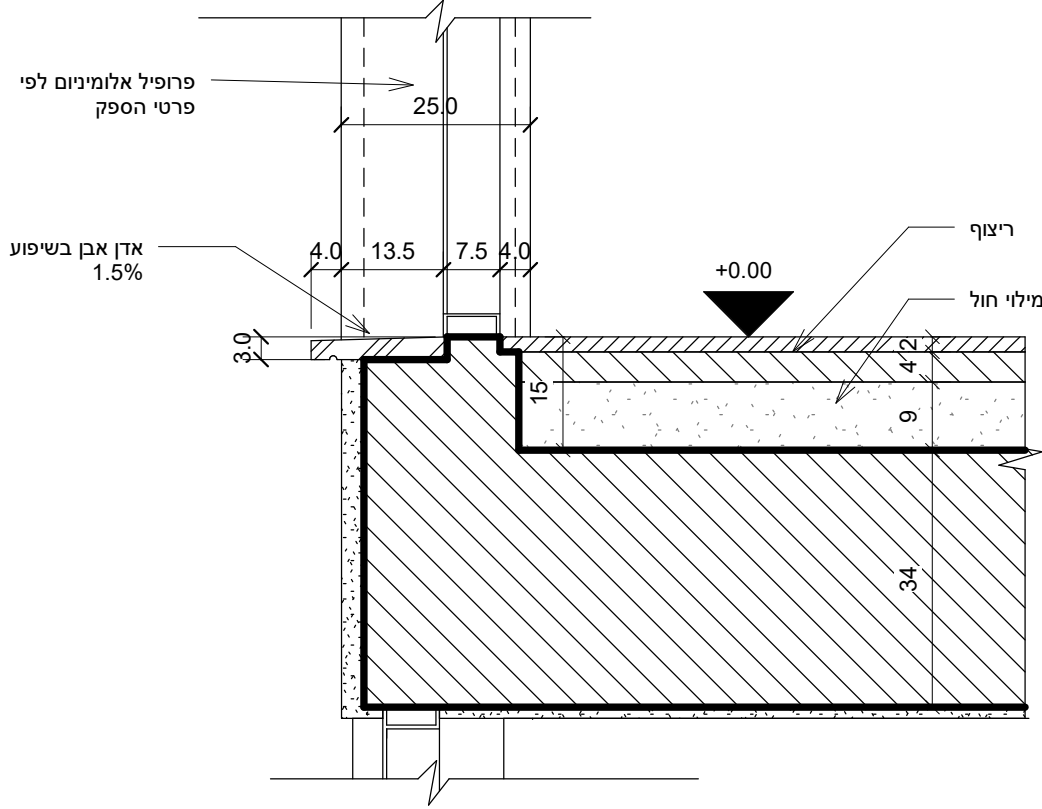


פרט 3 - מפגש חלון ורצפה

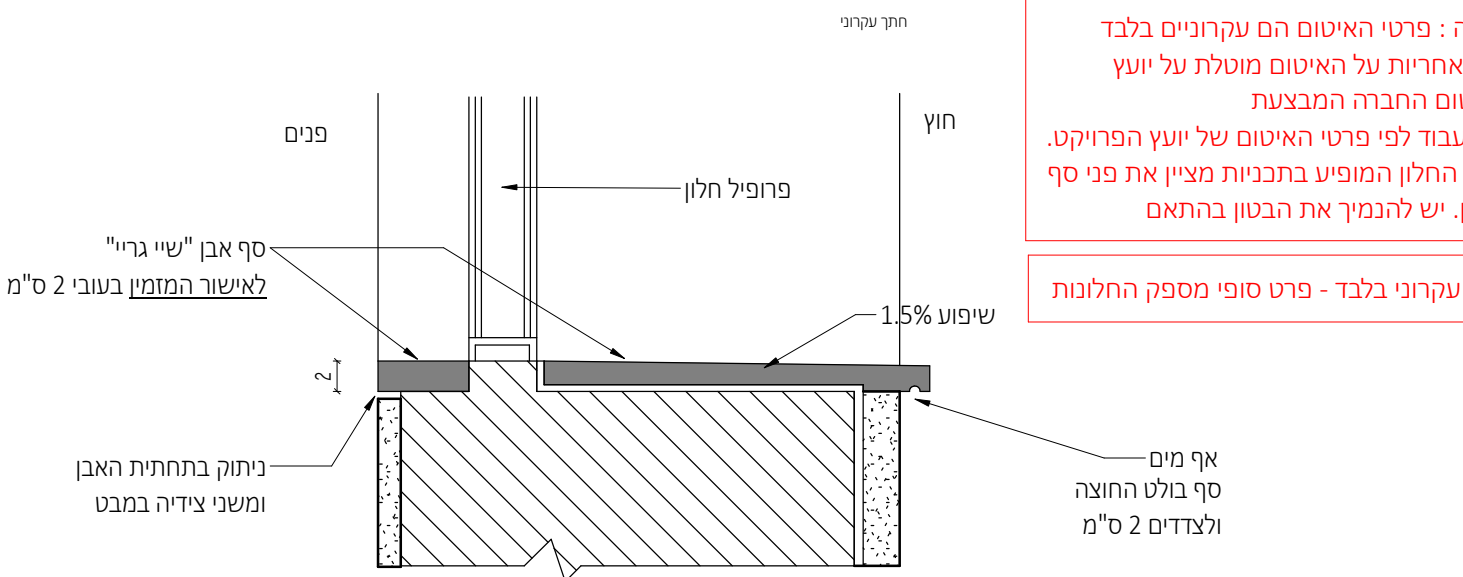


פרט 4 - חלון - פרט טיפוס י - סף חלון

1:5

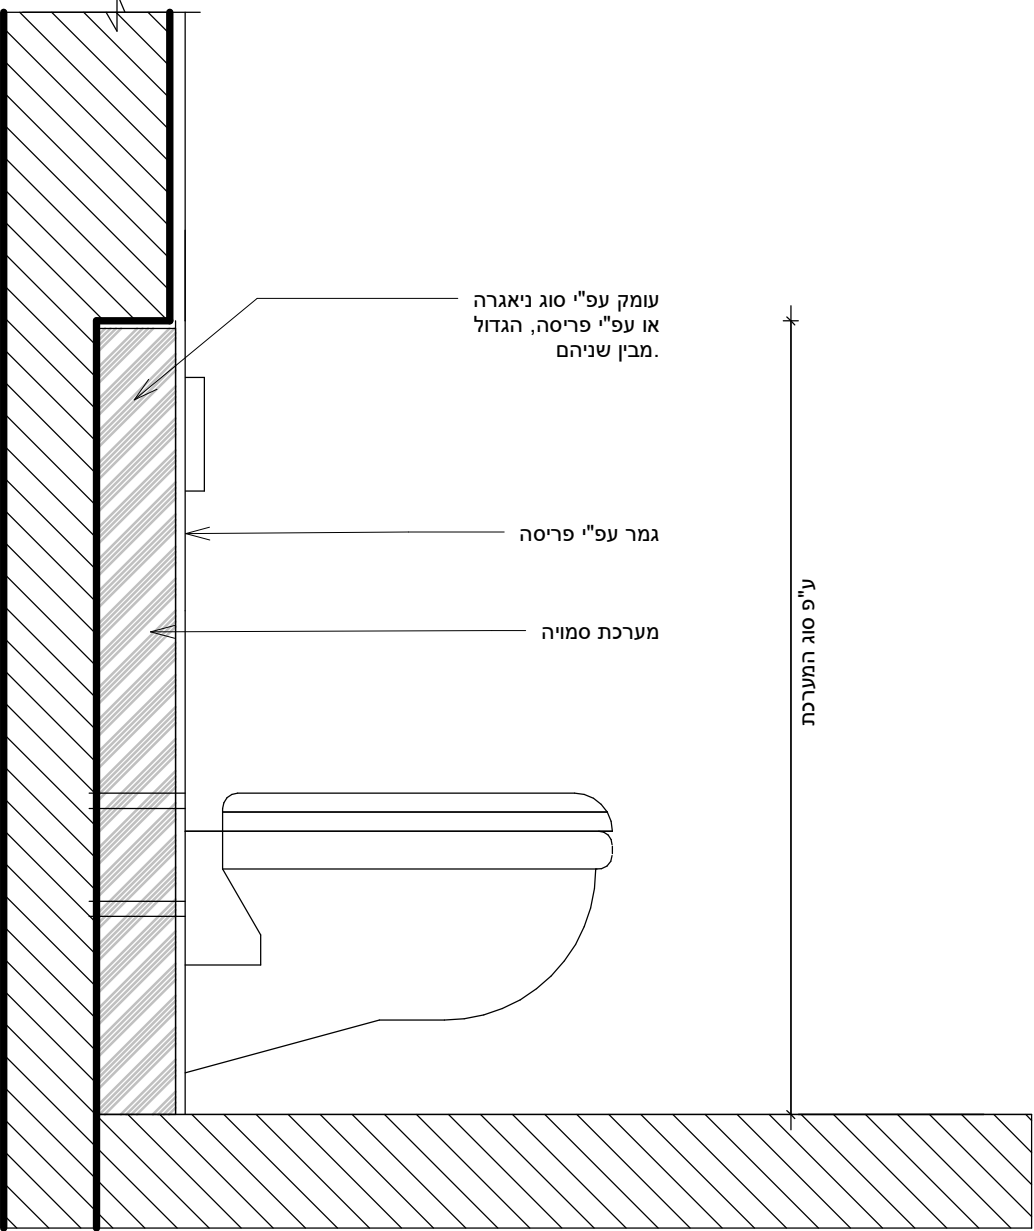

פרט 5 - אסלה תלויה בקיר 20

1 : 10

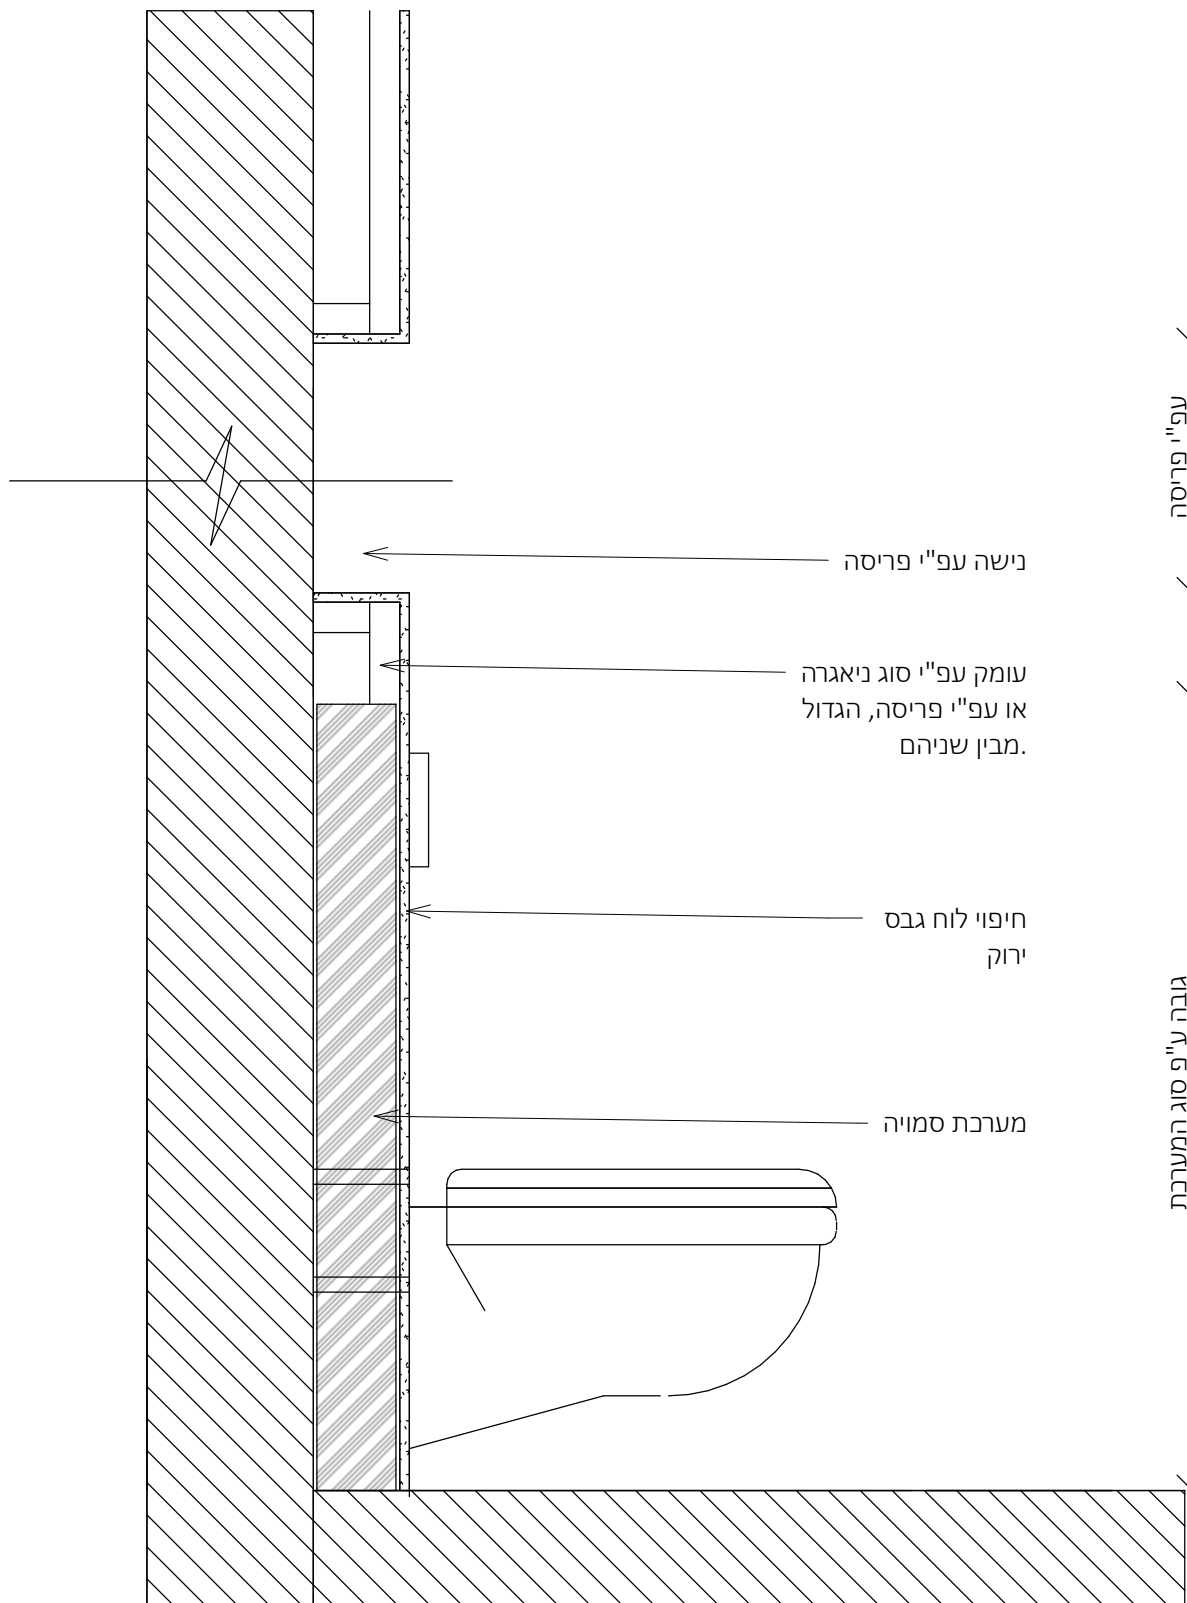

פרט 6 -אסלה תלויה מנגנון סמוי בעיבוי גבס

יש לעבוד במקביל לפרטים שיספק מעצב הפנים (במידה וקייים במגרש זה) המאושרות על ידי האדריכל.

פרטי האיטום באחריות יועץ האיטום
ראה חוברת פרטי איטום מצורפת

להמשך תיאום

רשימת חלונות					
סוג	תיאור	כמות	גובה	רוחב	מס פריט

ק.קרקע

חלון קבוע פרופיל 7000 קליל	צלון רפפה חיצוני חשמלי + ארגז חיצוני	2	240	90	1
דלת כנף פרופיל 4350 קליל	ללא רפפה	1	240	90	1.1
דלת כנף פרופיל 4350 קליל	צלון רפפה חיצוני חשמלי + ארגז חיצוני	1	240	90	1.2
דלת כנף פרופיל 4350 קליל	צלון רפפה חיצוני חשמלי + ארגז חיצוני	2	240	90	1.3
ויטרינה פרופיל 7500 קליל	צלון רפפה חיצוני חשמלי + ארגז חיצוני	1	240	440	2
ויטרינה פרופיל 7500 קליל	צלון רפפה חיצוני חשמלי + ארגז חיצוני	1	240	270	3
חלון הזזה פרופיל 7000 קליל	צלון רפפה חיצוני חשמלי + ארגז חיצוני	1	110	220	4
דלת כנף + קיפ בחלק העליון פרופיל 4350 קליל	צלון רפפה חיצוני חשמלי + ארגז חיצוני	1	240	80	5
חלון הזזה פרופיל 7000 קליל	צלון רפפה חיצוני חשמלי + ארגז חיצוני	1	110	110	6
ויטרינה פרופיל 7500 קליל	צלון רפפה חיצוני חשמלי + ארגז חיצוני	1	240	220	7
חלון קיפ פרופיל 4500 קליל	צלון רפפה חיצוני חשמלי + ארגז חיצוני	1	110	60	8

קומה א

ויטרינה פרופיל 7500 קליל	תריס גלילה חשמלי	1	230	220	9
חלון הזזה פרופיל 7000 קליל	תריס גלילה חשמלי	1	110	220	10
חלון קיפ פרופיל 4500 קליל	תריס גלילה חשמלי	2	110	60	11
חלון הזזה פרופיל 7000 קליל	תריס גלילה חשמלי	2	110	110	12
חלון הזזה פרופיל 7000 קליל	תריס גלילה חשמלי	2	110	160	13
חלון הזזה פרופיל 7000 קליל	תריס גלילה חשמלי	1	110	180	14
דלת כנף פרופיל 4350 קליל	תריס גלילה חשמלי	1	230	90	15

סוג זכוכית – בהתאם למפורט בדו"ח התרמי (תנאי המינימום בעמוד 9 מתוך המפרט התרמי). כמו כן, הזכוכית תקבע בתיאום עם הקבלן לאחר אישור יועץ התרמי וחברת הניהול

כל פריט יחולק למינימום הכנפיים האפשרי (לתיאום מול ספק האלומיניום ובמסגרת שרטוטי shop drawing)

רשימת דלתות					
סוג	הערות	כמות	גובה	רוחב	מספר פריט
דלת חוץ דגם גארדה	דלת כניסה	1	240	110	0
דלת פנים "אקוודור" תוצרת חמדיה	דלת פנים	6	210	70	1
דלת פנים "אקוודור" תוצרת חמדיה	דלת פנים	2	210	90	2
דלת פנים "אקוודור" תוצרת חמדיה	דלת פנים	4	210	80	3
דלת פנים "אקוודור" תוצרת חמדיה	דלת נגרות ממ"ד	1	200	80	4

נוימן חיינר אדריכלים בע"מ

כל הזכויות שמורות
ט.ל.ח.

NeumanHaynerArchitects



רשימת פתחים		שם התכנית:
גליון מספר: A3-6-1000	מהדורה: 22.09.2025	01 סטטוס:
שם הפרויקט: נופיה - מגרש 14	שם המממן: קבוצת רכישה נופיה	
26/10/2025 16:16:36		קנה מידה:

