

[illegible]

| תאריך    | חש' / שניונים            |
|----------|--------------------------|
| 29.10.24 | עברו רקע אדריכלות        |
| 29.10.24 | עברו תניית               |
| 10.12.24 | עברו תניית               |
| 15.12.24 | עברו תניית               |
| 23.12.24 | עברו תניית               |
| 11.5.25  | עברו תניית               |
| 22.5.25  | עברו תניית               |
| 3.6.25   | המסעת מ"א                |
| 19.6.25  | תכנון מעקרים והתאמה כלוח |
| 17.11.25 | עברו תניית               |
| 30.11.25 | עברו תניית               |
| 14.12.25 | עברו תניית               |

עודכן ע"י: \_\_\_\_\_ יפעת

**א. בסיס**  
**הנדסת שמל בע"מ**

משרד: יד חרוצים 16, ירושלים 93420  
טל: 074-7021015 (י"ד) 050-6550484  
077-5131015 \*2" office@ebasis.co.il



שם הפרויקט:

נופיה-אלפי מנשה  
מגרש 14

שם הגיליון:

## תוכנית חשמל

|                             |                             |                                       |                             |            |  |
|-----------------------------|-----------------------------|---------------------------------------|-----------------------------|------------|--|
| קנה מידה:                   |                             |                                       |                             |            |  |
| 1:50                        |                             |                                       |                             |            |  |
| <input type="radio"/> כינוי | <input type="radio"/> ישיבו | <input checked="" type="radio"/> שמרן | <input type="radio"/> ריצוע |            |  |
| Date:                       | מס' קובץ:                   |                                       | File:                       |            |  |
| 29.10.2024                  | 675-14.dwg                  |                                       |                             |            |  |
| תנן:                        |                             | שרטט:                                 |                             | איש:       |  |
| איתו                        |                             | אירל                                  |                             | איתו       |  |
| מס' עדכון:                  |                             | מס' הגיון:                            |                             | מס' הריוט: |  |
| 12                          |                             | E                                     |                             | 675        |  |

מקרא חשמל ותאורה:

[illegible]

הערות:  
- מיקום סופי לנקודות תאורה  
ייקבע ע"פ תכנית עיצוב פנים  
תאורת חוץ- ע"פ יועץ פיתוח


– במידה והוחלט על הכנות לבית חכם: כהכנה לבית חכם ולדלת חכמה יש ל חוט 0 כחול נוסף בכל מפסק הדלקה התכנון עצמו יעשה ע"י ספק בית חכם

- הכנות למיזוג אור, חימום תת רצפתי, מערכות אבטחה, וחימום מים בחשמל יהיו עפ הנחיות יועץ לכל תחום 1411


יש לקרוא תכנית זו יחד עם תכנית אדריכלות  
למבנה בלוחות אדריכלות

הערות:


- \* כל הגבהים בתכנית הינם למרכז אביזר  
אלא אם ציין במפורש אחרת
- \* מיקום סופי לנקודות תאורה  
ייקבע ע"פ תכנית עיצוב פנים  
תאורת חוץ – ע"פ יועץ פיתוח
- \* מיקום סופי לשקעי מידוג  
ע"פ תוכנית יועץ מידוג

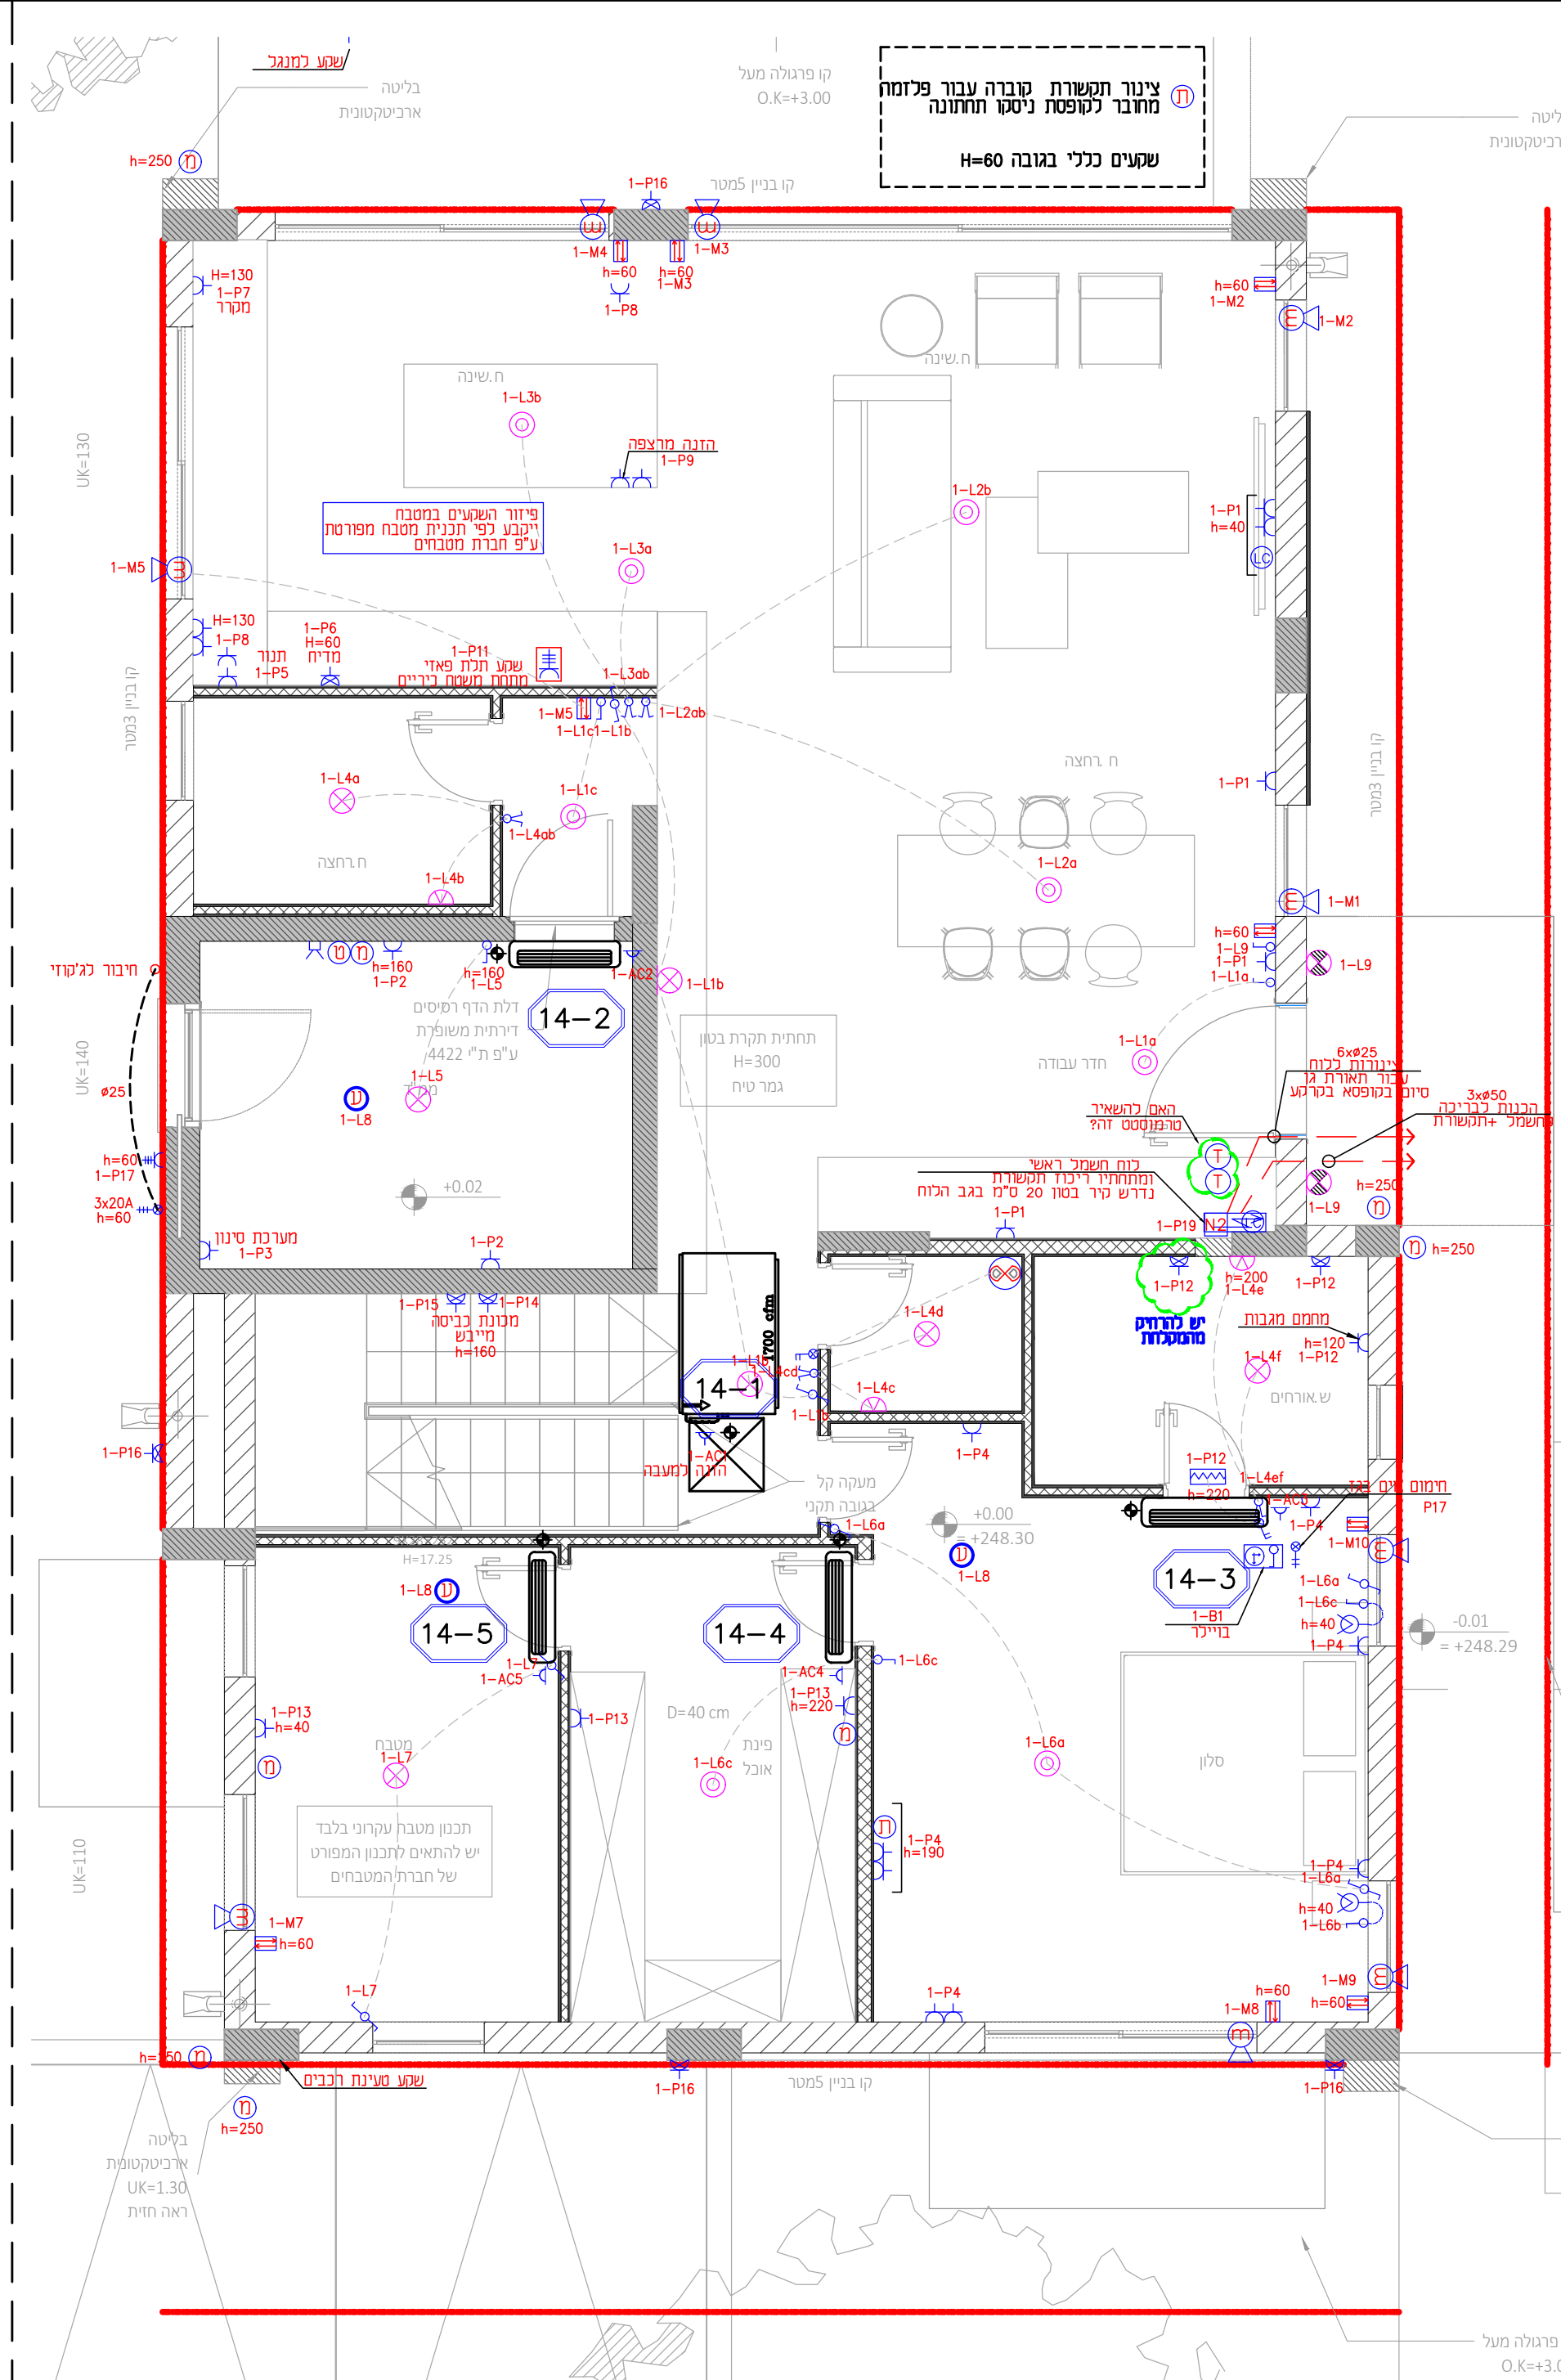

## קומת קרקע

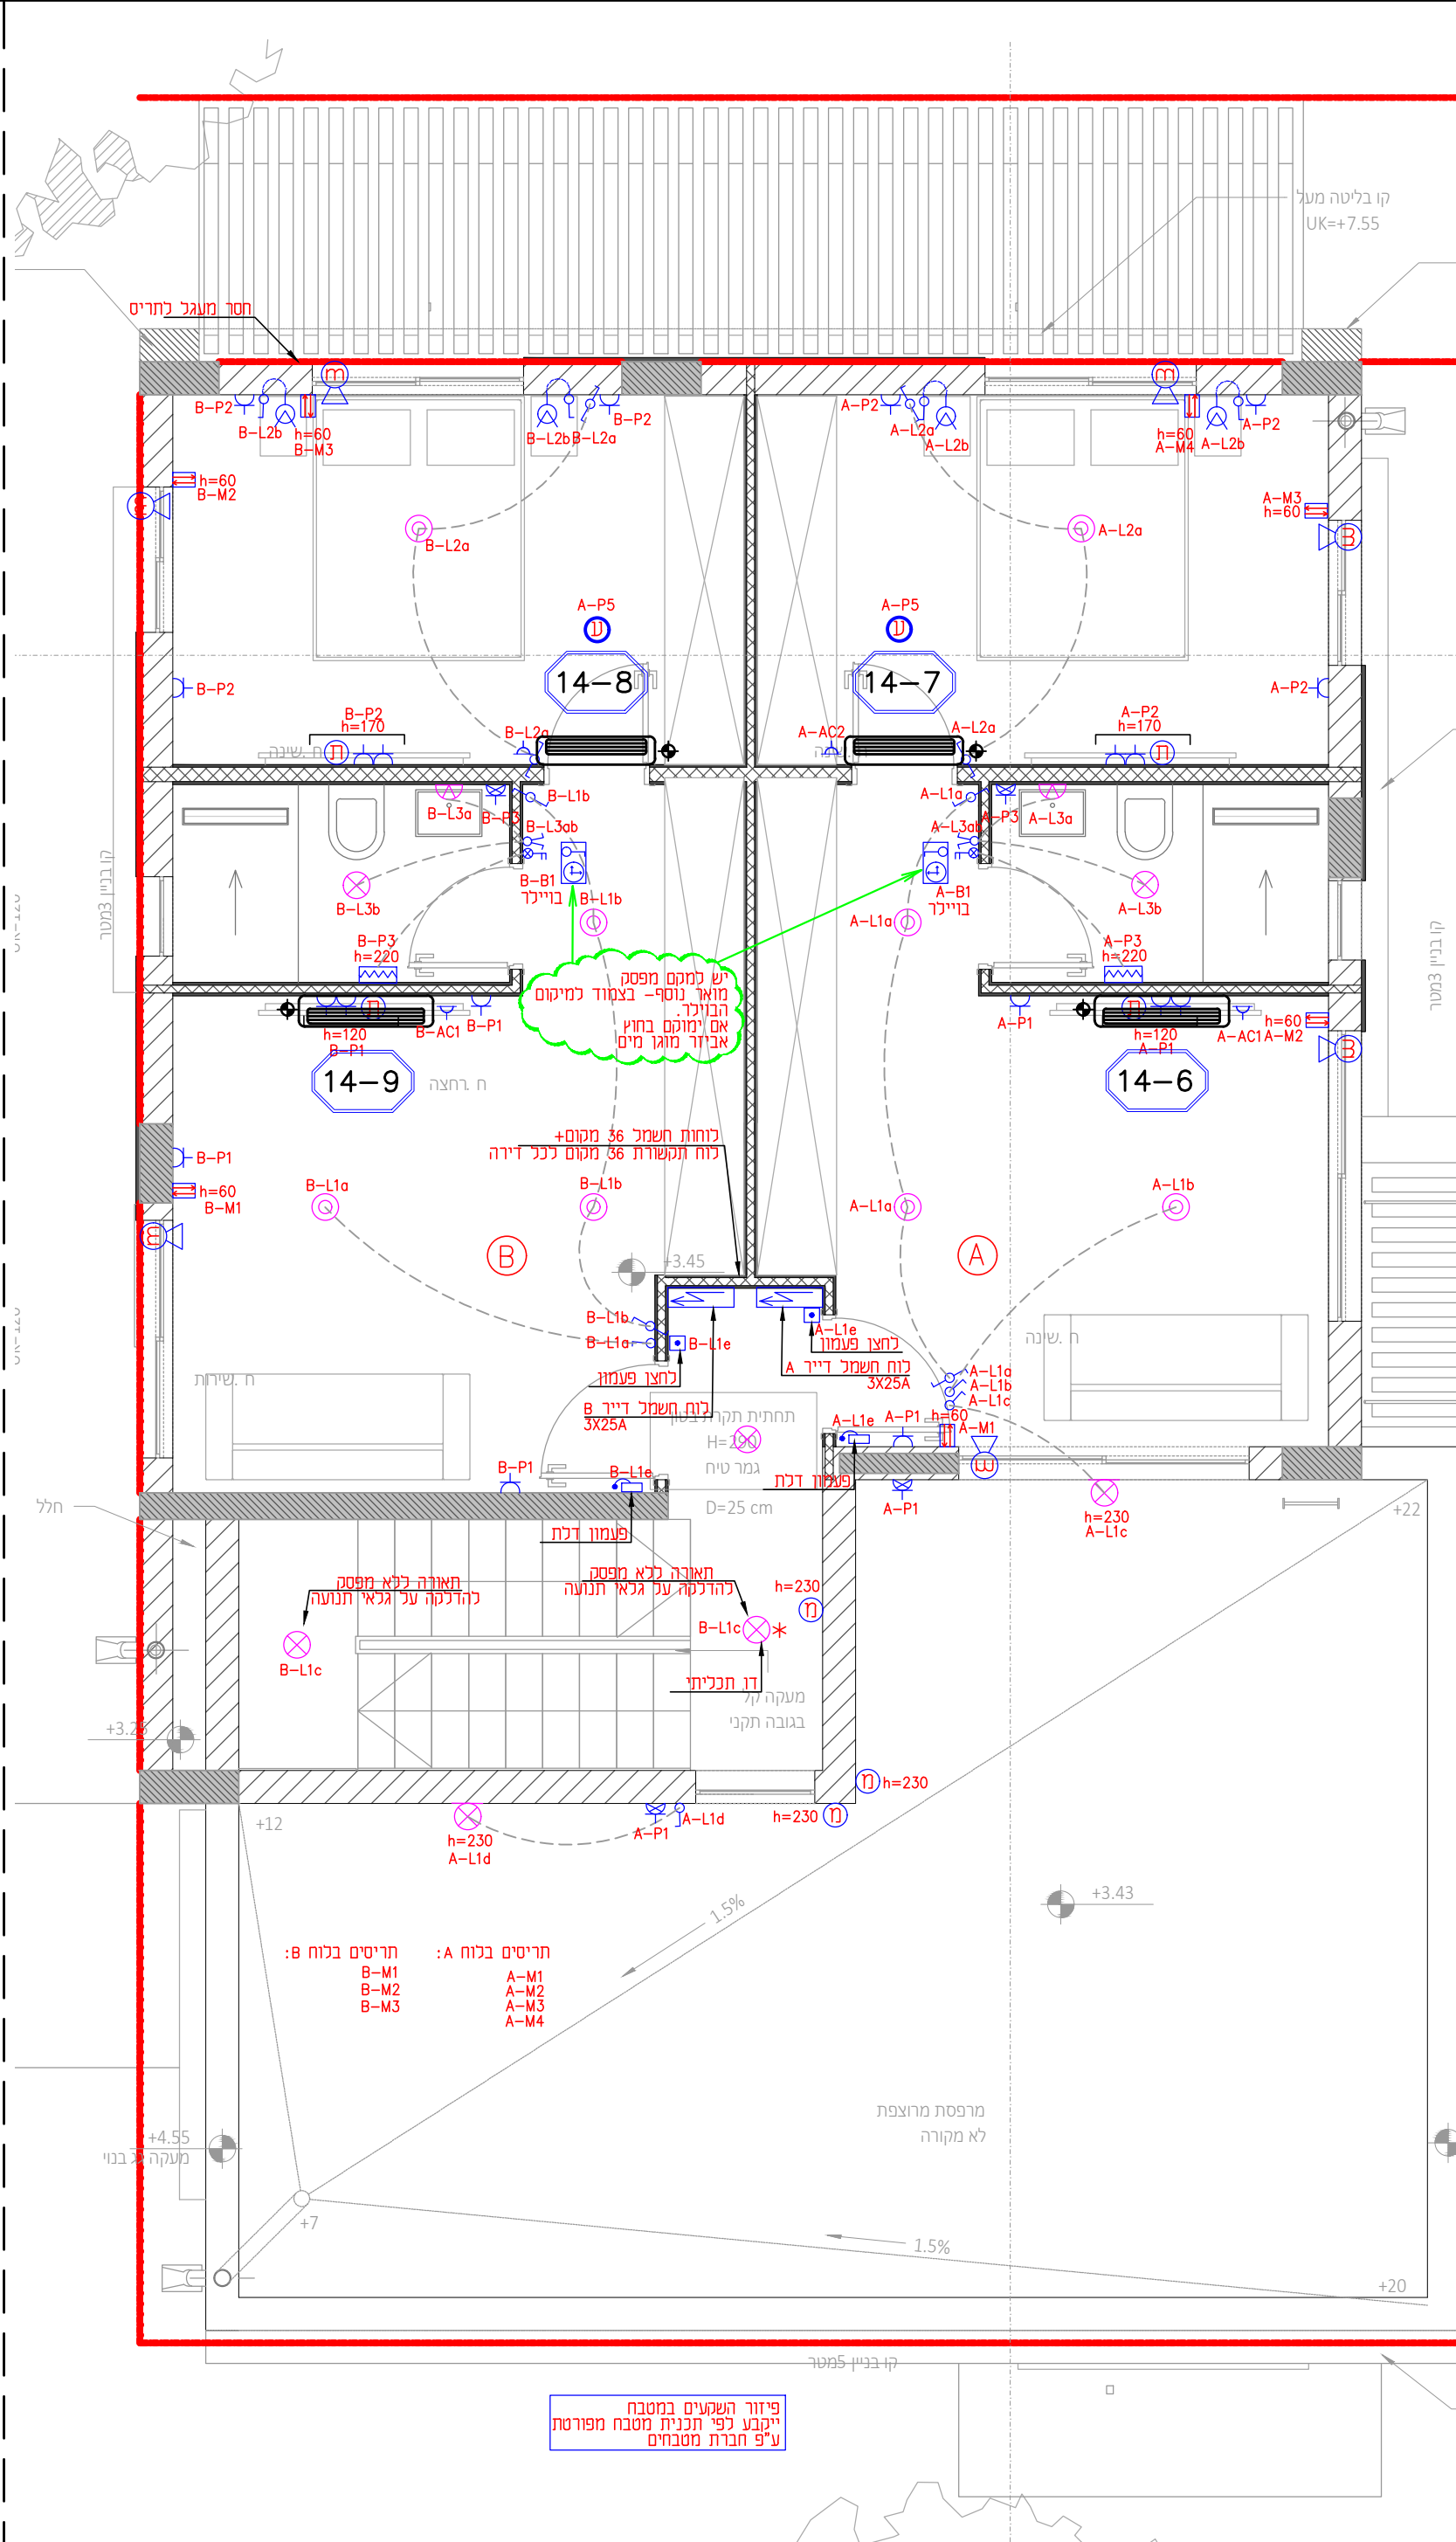

קומה א'

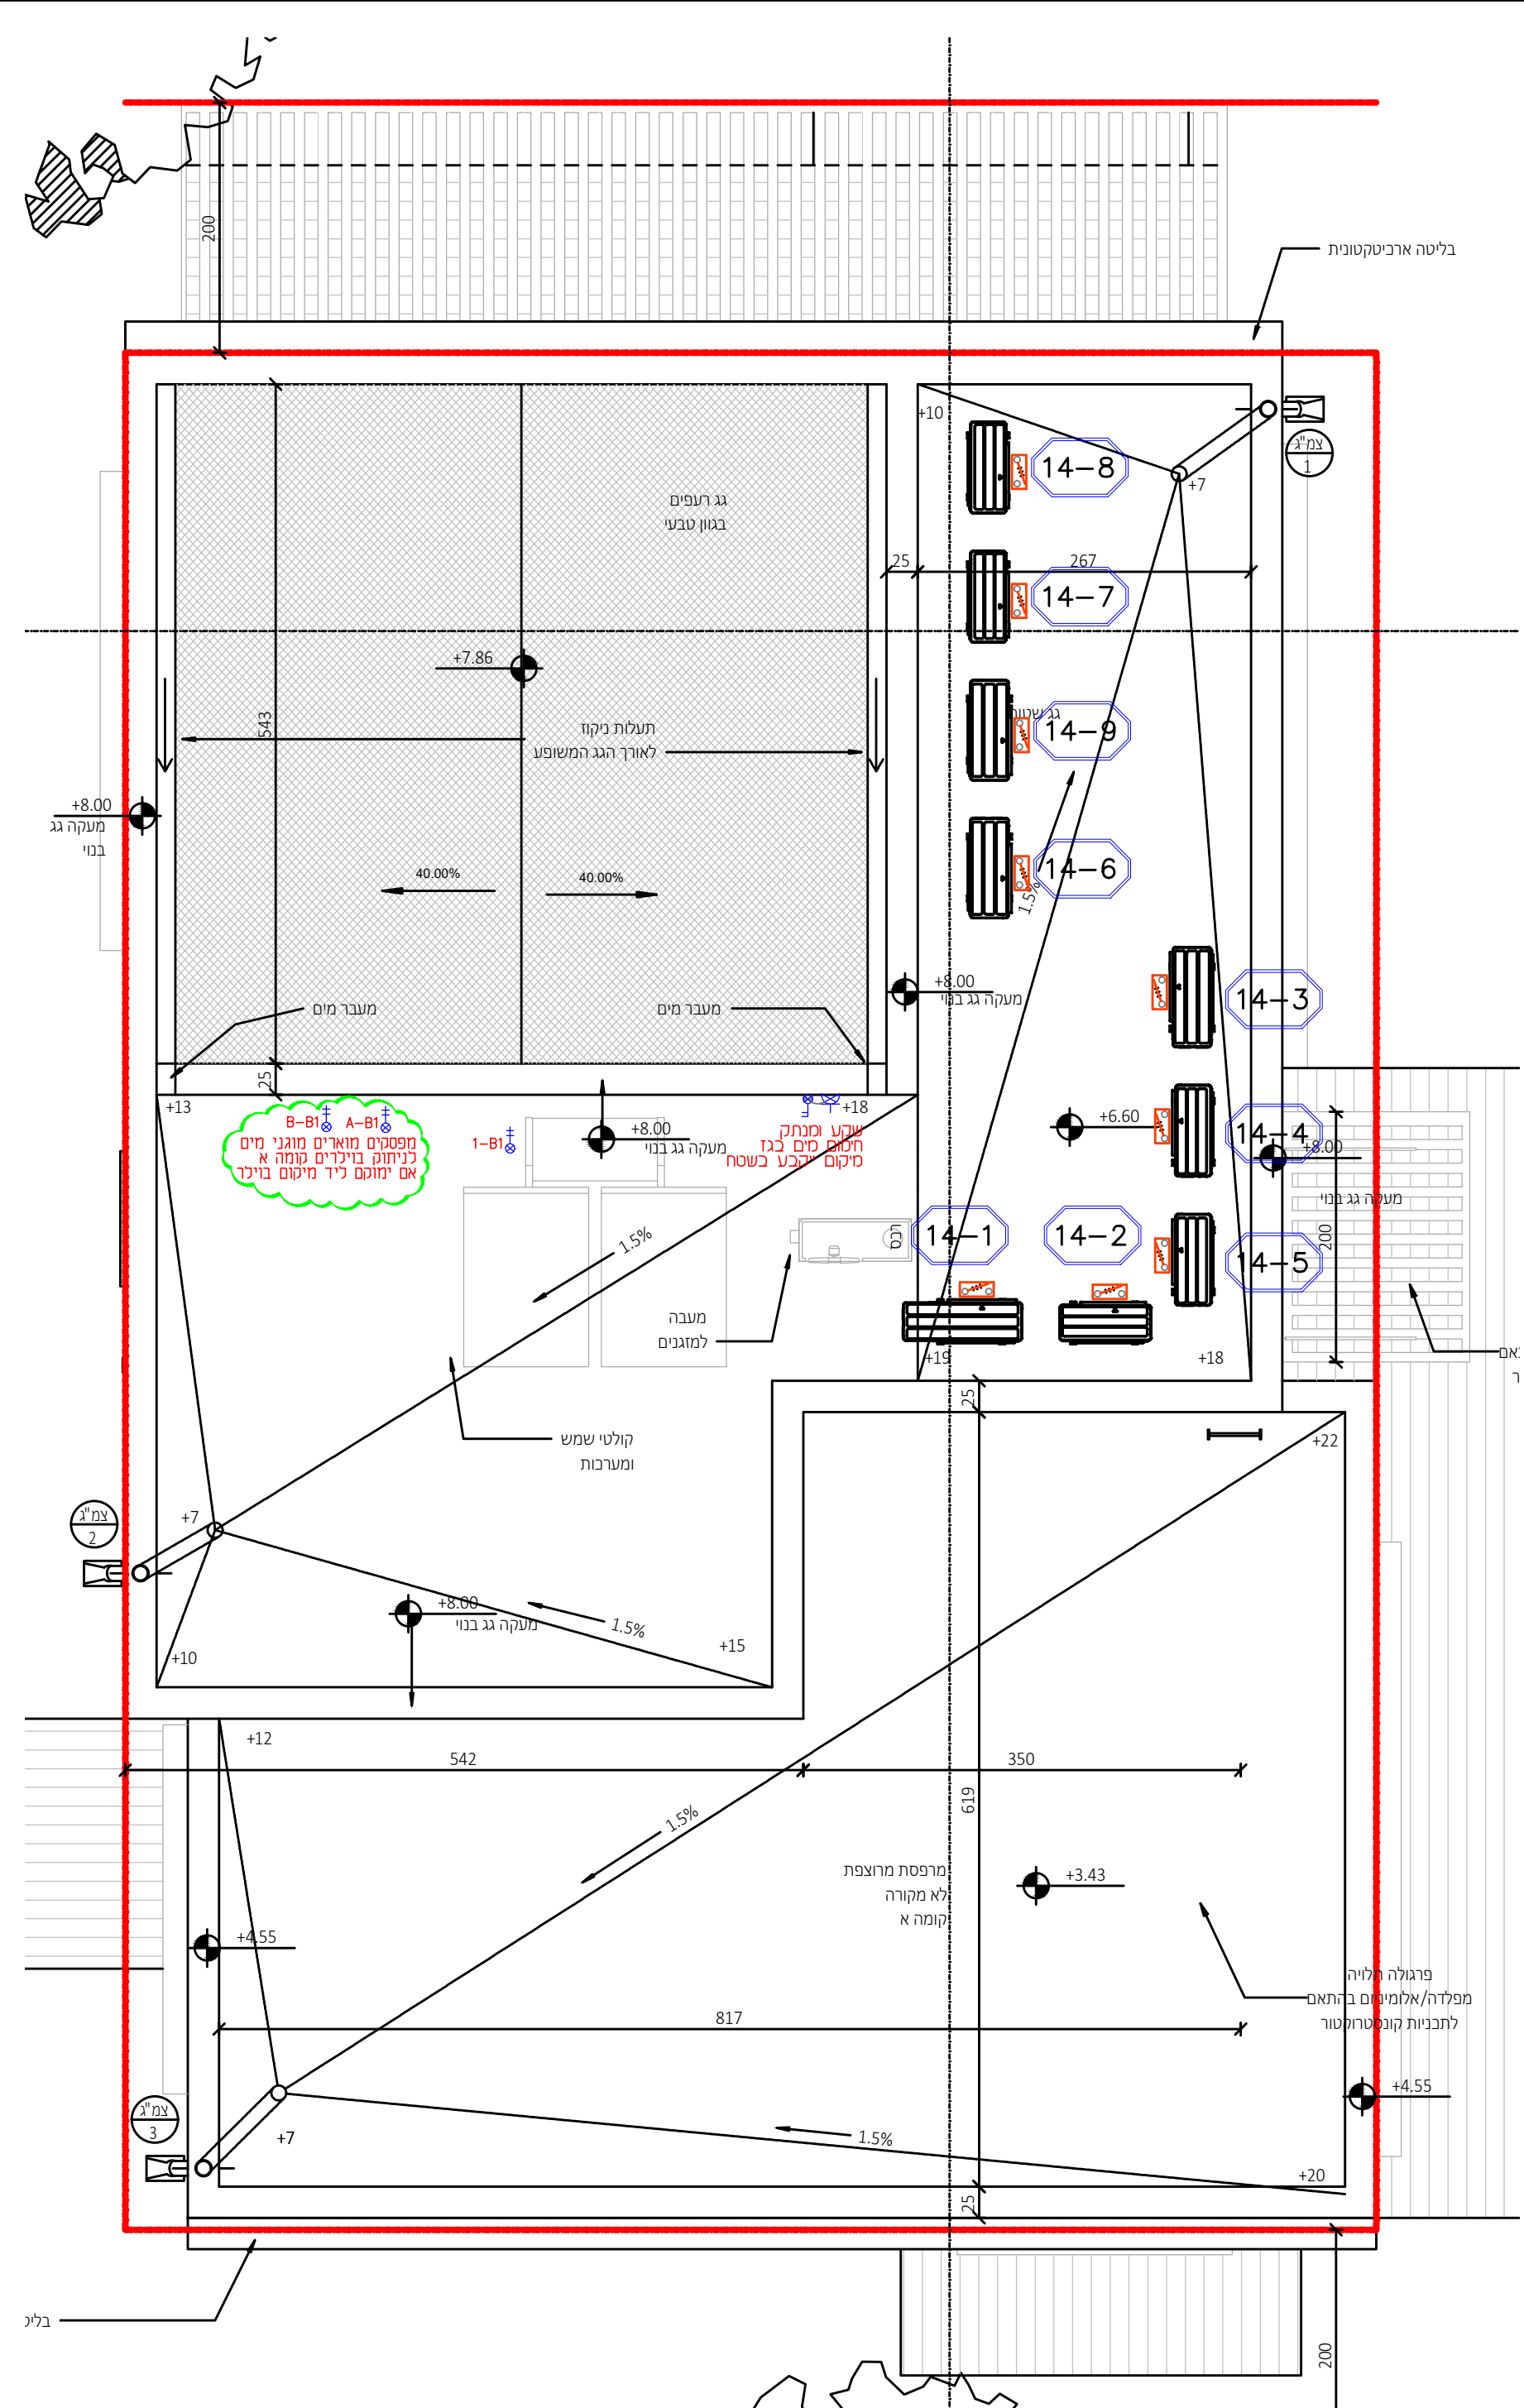

קומה גג


| יחידות מיוג סינגל-מאיד+מעבה |       |      |                            |                       |            |            |            |                |                 |       |             |
|-----------------------------|-------|------|----------------------------|-----------------------|------------|------------|------------|----------------|-----------------|-------|-------------|
| מס' יחידה במגזין            | חוצות | דגם  | תפוצה ברוך<br>CPM<br>Blu/H | הספק עבודה למנוע<br>W | מידות מאיד | מידות מעבה | נתיך דגם C | חצרות          |                 |       |             |
| 14-5                        | 14-4  | 14-2 | Tediran                    | ALPHA PRO INY 140 NG  | 9,210      | 320        | 0,800      | 21.6/29.0/98.4 | 33.9/55.3/73.21 | 1x10C | חזנה באיידר |

| יחידות מיוזג סינגל-מאיד+מעבה |       |                |               |       |                  |                 |                      |         |                  |
|------------------------------|-------|----------------|---------------|-------|------------------|-----------------|----------------------|---------|------------------|
| הערות                        | דגם C | נחיר מעבה      | מידות מאיד    | דגם W | תפוסת מים<br>CFM | חשמל כוח<br>W/h | דגם                  | חיצית   | מט' יחידה במתנית |
| חזנה במאיד                   | 1x100 | 330/55.5/73.21 | 21x/29.0/89.4 | 1,100 | 380              | 11,840          | ALPHA PRO INV 180 NG | Tedraen | 14-7 14-8        |

| יחידות מיוג טינג-מאייד+מעבה |       |      |                     |                      |                       |             |            |                                  |                      |
|-----------------------------|-------|------|---------------------|----------------------|-----------------------|-------------|------------|----------------------------------|----------------------|
| מס' יחידה במכונה            | חוצית | דגם  | תפוסת חרוך<br>Blu/h | ספיט<br>CFM          | הספק עבודה למנוע<br>W | מידות מאייד | מידות מעבה | נחץ דגם C                        | הערות                |
| 14-3                        | 14-6  | 14-9 | Tedran              | ALPHA PRO INY 240 NG | 17,740                | 500         | 1,800      | 359/55.5/80.21<br>222/30.4/40.14 | 1x10C<br>חונה במאייד |

| יחידות מיוזג סינגל-מא"ד+מעבה |       |             |             |                  |       |        |                             |
|------------------------------|-------|-------------|-------------|------------------|-------|--------|-----------------------------|
| הערות                        | דגם   | נחיר        | דגם         | מס' יחידה במונתי | חיצית | דגם    | תופסת מים<br>CM/h           |
| דחנה במעבה                   | 3x16C | 344/353/361 | 800/353/330 | 7,000            | 1700  | 47,770 | AMCOR SLIM INV<br>SQ-600/3P |
|                              |       |             |             |                  |       |        | Tadiren                     |

חזית לוח חשמל ראשי וארונות תקשורת

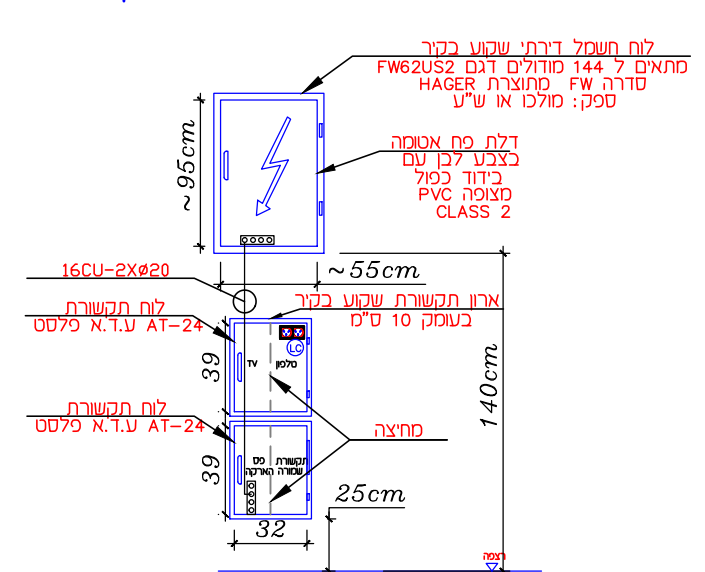

פּרָט לַגְבוּרִים שֶׁל הַדְּלֵקוֹת.  
חֲשׂוֹרָה וְחֲרִיזִים:

מיקום סופי של המעבים  
ייתכן בשטח  
בתיאום עם האדריכל  
מנהל פרויקט  
וקבלן מזוג אוויר

מיקום סופי של המעבים  
ייתכן בשטח  
בתיאום עם האדריכל  
מנהל פרויקט  
וקבלן מיזוג אוויר

מיקום סופי של המעבים  
ייתכן בשטח  
בתיאום עם האדריכל  
מנהל פרויקט  
וקבלן מזוג אוויר

מיקום סופי של המעבים  
ייתכנו בשטח  
בתיאום עם האדריכל  
מנהל פרויקט  
וקבלת מידע אוויר

בסיס בטון בגובה מינימלי 10 ס"מ  
מידת עירוי מומדת 2"3 רורמ רעידות

| ח'ס' ש'ינויים  | תאריך    |
|----------------|----------|
| 1 עדכון תוכנית | 23.11.25 |
| 2 עדכון תוכנית | 30.11.25 |
|                |          |
|                |          |
|                |          |
|                |          |

עודכן ע"י: \_\_\_\_\_ יפעת

|   |                                    |                            |  |
|---|------------------------------------|----------------------------|--|
| שם הפרויקט:   |                                    | שם התחבית:                 |  |
| נופיה-אלפי מנשה   |                                    |                            |  |
| שם הפרויקט:   |                                    | שם התחבית:                 |  |
| לוח #-1 מגרש 14, נופיה   |                                    |                            |  |
| גודל מרחב:   |                                    | 1:50                       |  |
| <input checked="" type="radio"/> שטח<br><input type="radio"/> יער<br><input type="radio"/> אבן<br><input type="radio"/> מים | File: 675W.dwg<br>Date: 05.03.2025 | תאריך: 05.03.2025<br>חתום: |  |
| אדריכל:<br>יאיר   | מהנדס:<br>יאיר                     | יפעת                       |  |
| שם הפרויקט:<br>675   | שם התחבית:<br>14                   | שם עובד:<br>2              |  |

