


פתחי גישה אופן ארט בתיאום סופי מול אדריכל
כלל יחידות המיזוג אשר נמצאות בתוך נגרות יש לתאם סופית מול אדריכל ונגרות

Court 14 1st Floor

Option №2
inverter duct unit in living
room and wall mounted in
rooms


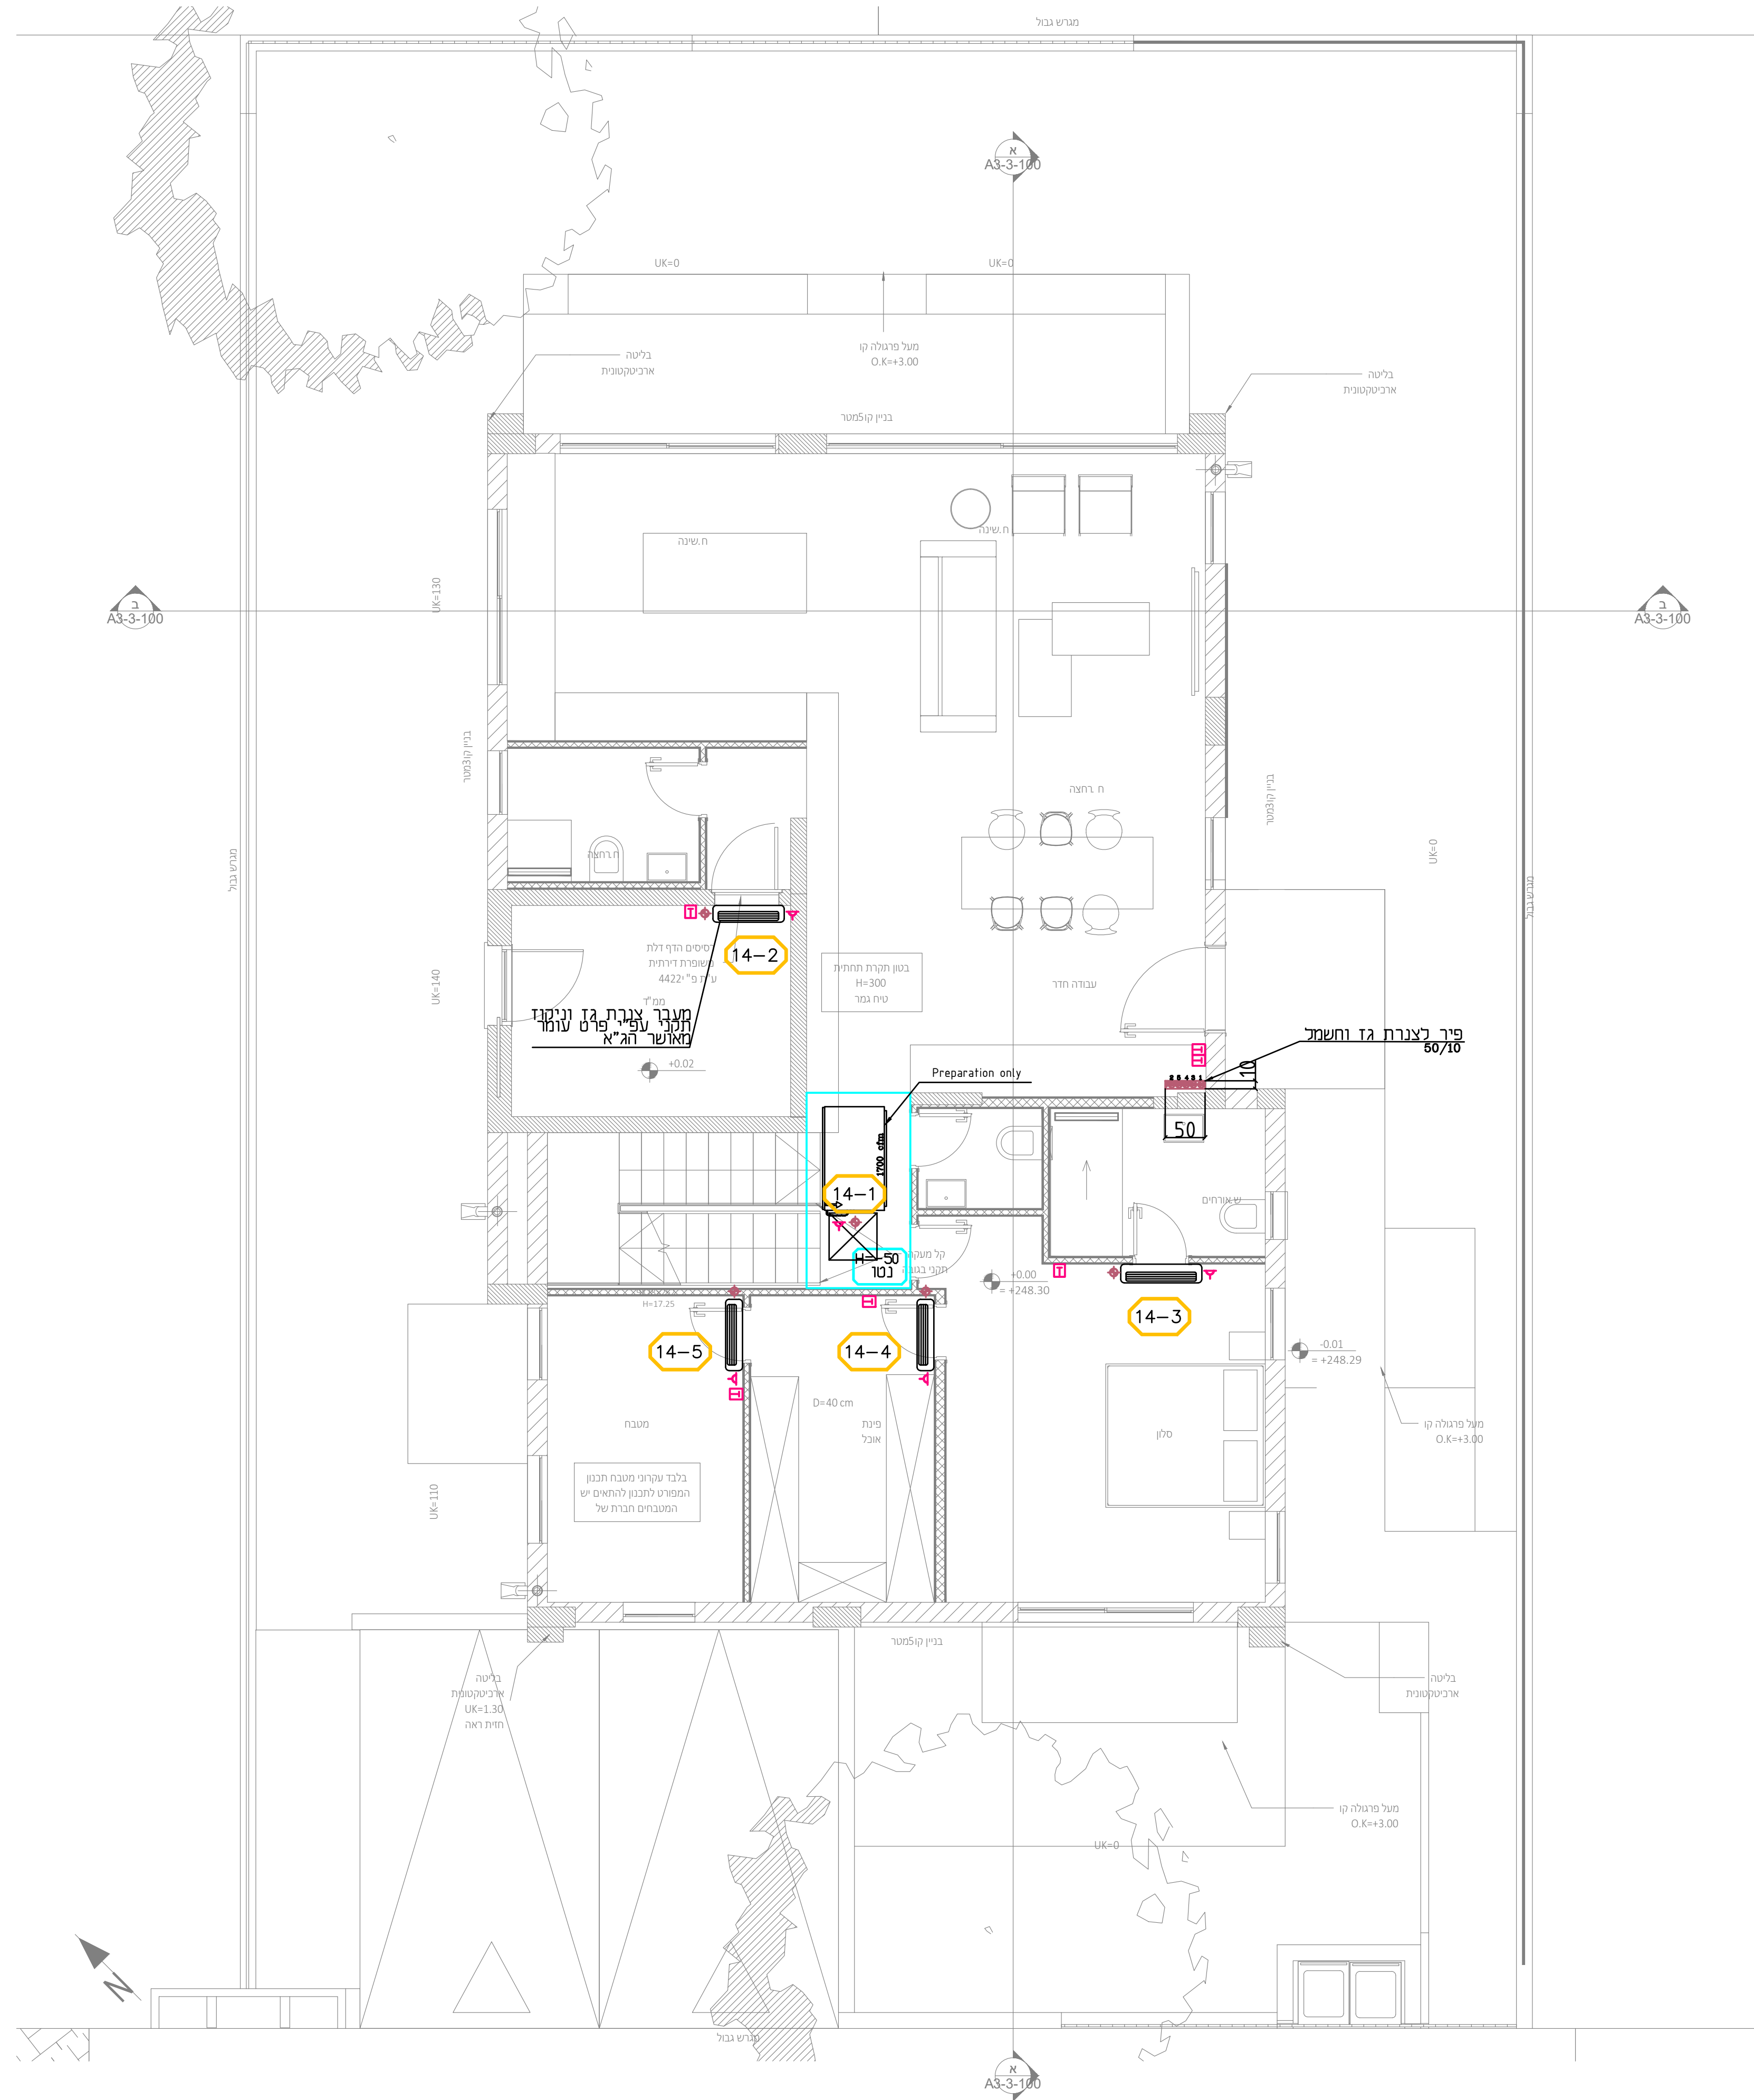


עפ"י פיתוח "תוכניות" י
בנפרד פירוט ראה נוף יועץ

עפ"י פיתוח "תוכניות" י
בנפרד פירוט ראה נוף יועץ

Court 14 2nd Floor

Option №2
inverter duct unit in living
room and wall mounted in
rooms

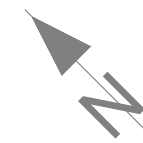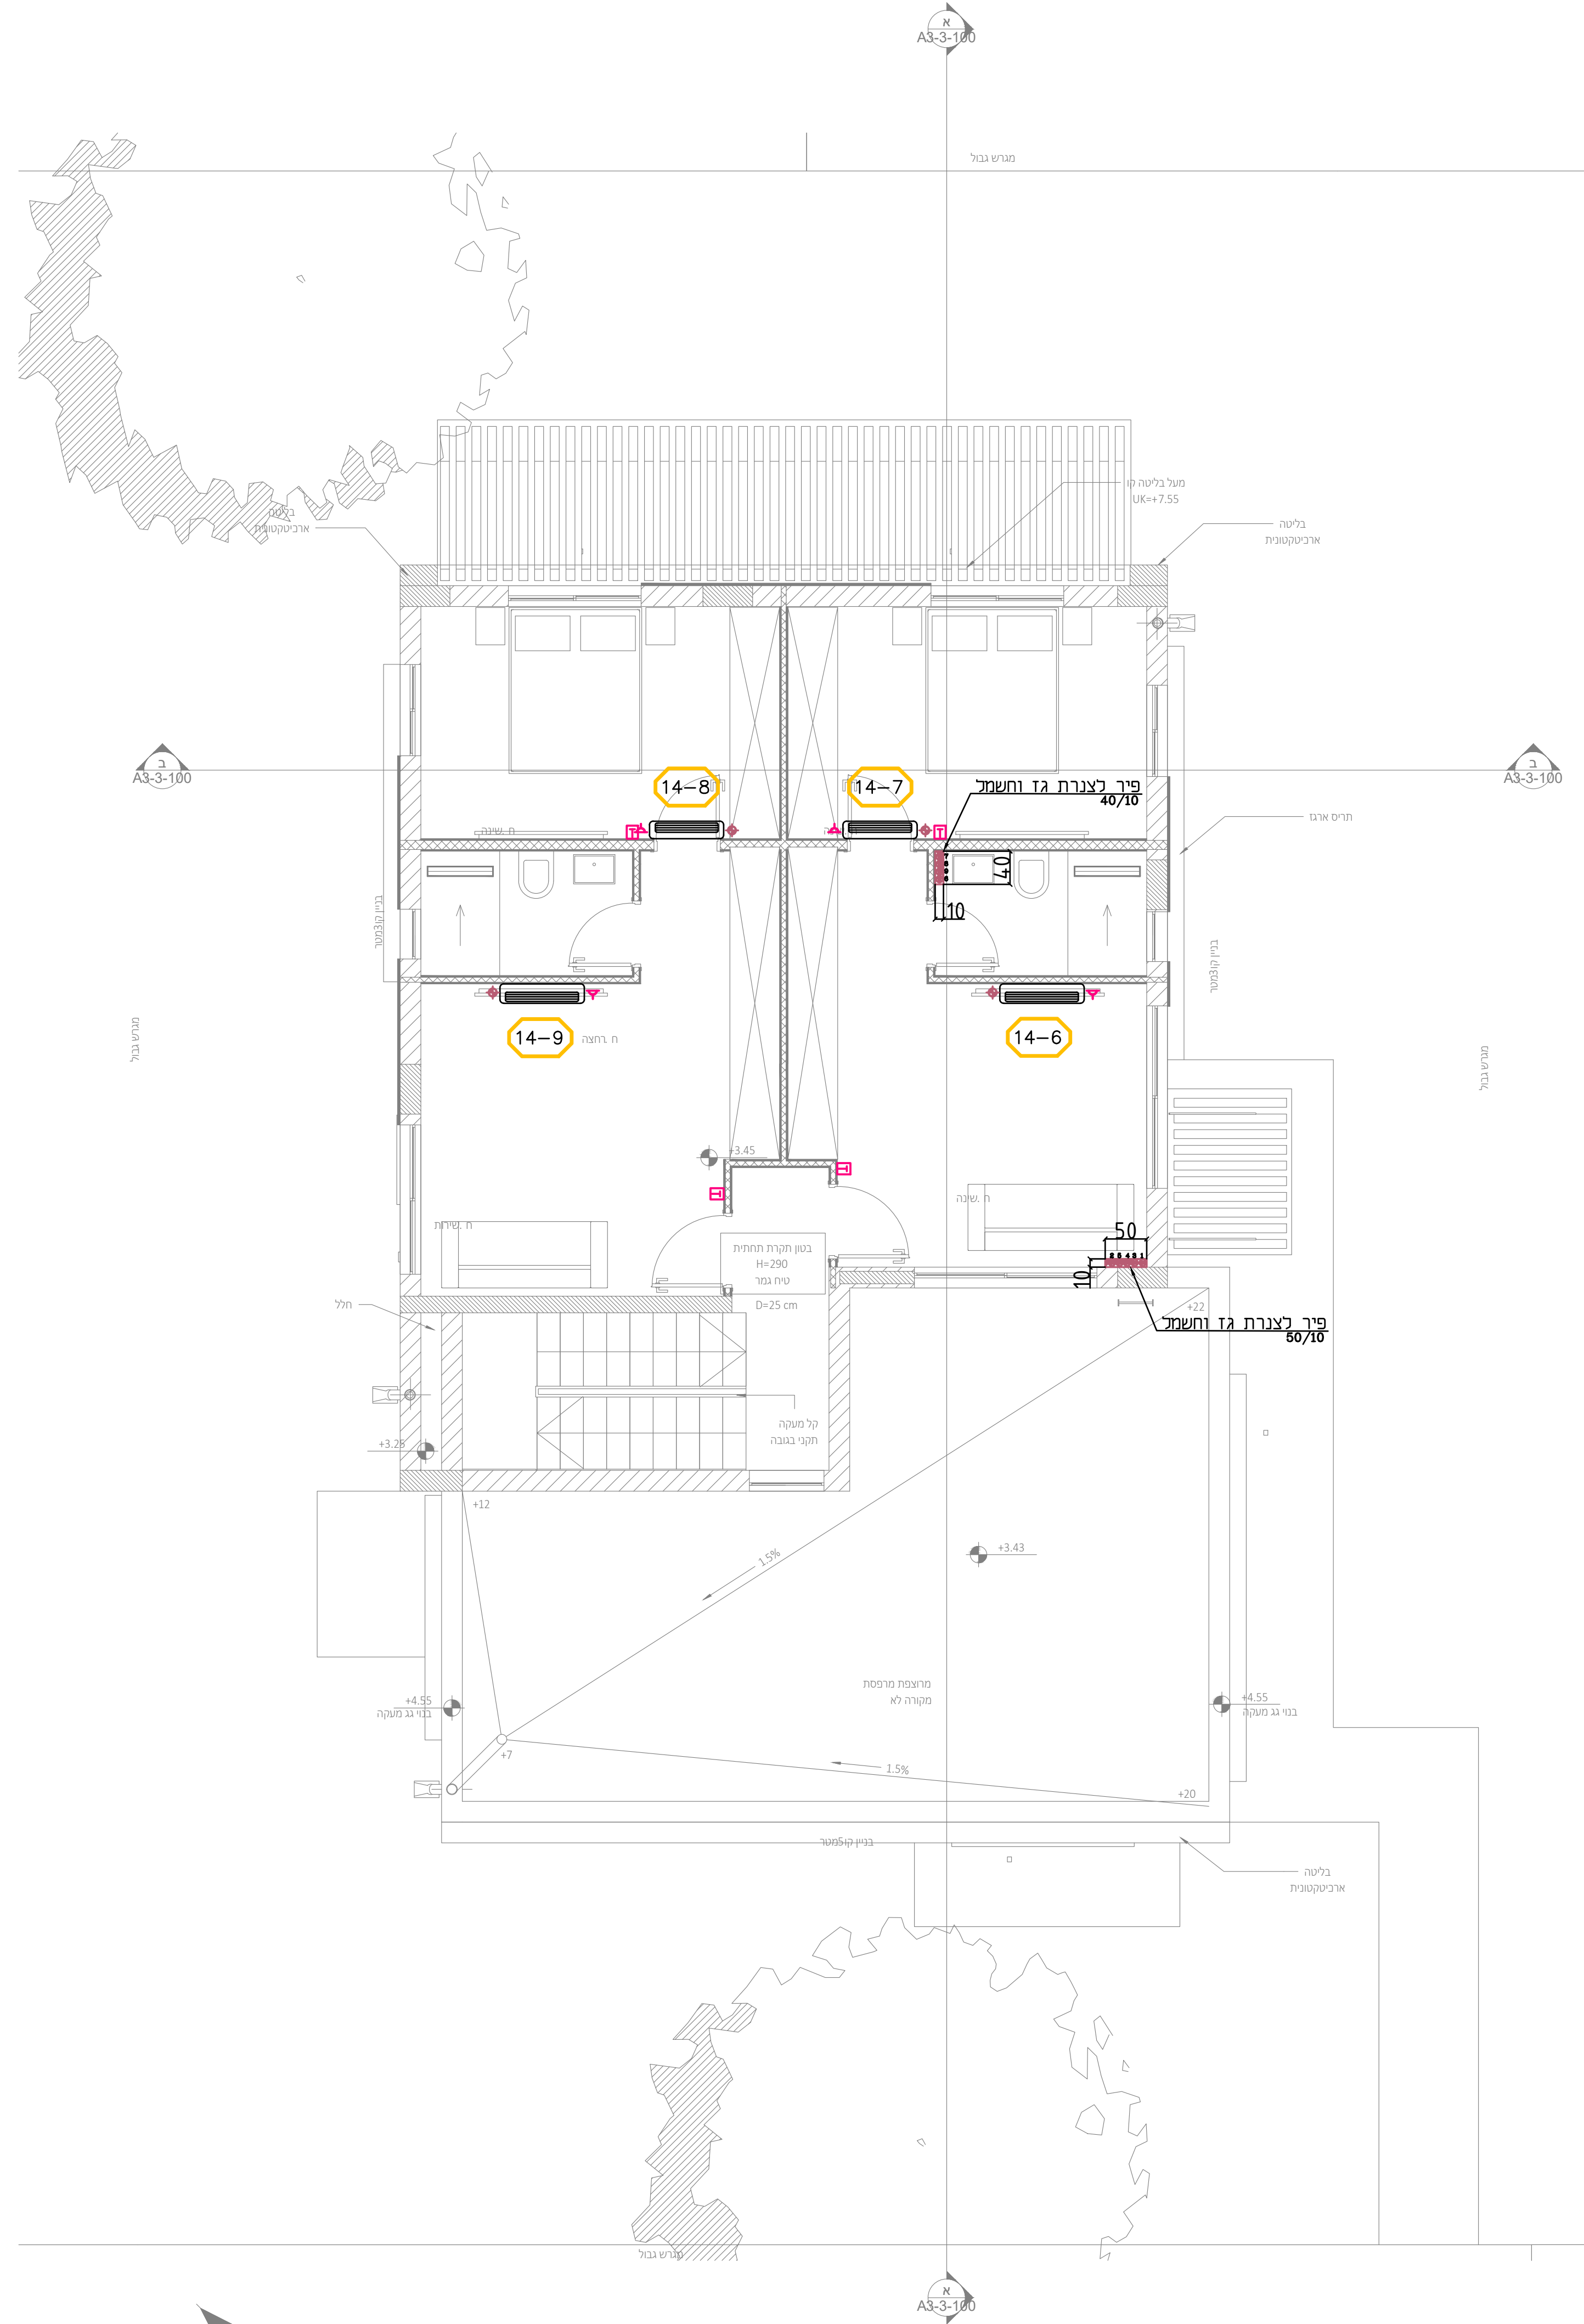

תפוצה									
אורנית	לחץ	כוח פורקט	מבלי ראש	מבלי ראש	מבלי ראש	מבלי ראש	מבלי ראש	מבלי ראש	מבלי ראש

מהדורה									

המבצע אחראי למידות ובהתאמתן למציאות
בכל מקרה של אי התאמה, מתיחה או טעות
עליו להודיע למתכנן לפני התקנתו בביצוע
אין להעביר מידות על סמך מדידה בשטח.
אין ברשות כל שימוש בתוכנית זו
או ברעיונות והגומים בה ללא אישור בכתב
מאת המתכנן.

הערות

- כל התעלות מחוץ למבנה יבודדו
בבידוד אקוסטי בעובי 2"
- תעלות מזוג בתוך המבנה יבודדו
בבידוד אקוסטי פנימי 1"
- תעלות אוויר צח יבודדו
בבידוד טרמי 1"
- יש לאסוף בסיקור את פינות החיבור
של תעלות מזוג אוויר לפני כיפוף
הפורום המתחברים

מקרא

- מפ- מפוח
- מ.א.ג. - מפוח אוויר קורי
- מ.א.ת. - מפוח אוויר תת-קורי
- ת.א.ת. - תריס אוויר חוזר
- ת.א.צ. - תריס אוויר צח
- ב.א. - בידוד אקוסטי
- ב.ס. - בידוד טרמי
- כ.ב. - כלא בידוד
- ד.א. - דמפר אש
- טרמסטט לוח הפעלה
- שקע חשמל לספוף יועץ חשמל
- שקע תלת פאזי לספוף יועץ חשמל
- מפסק בסחון חד פאזי לספוף יועץ חשמל
- מפסק בסחון תלת פאזי לספוף יועץ חשמל
- ניקוד מאיד לסיפוף יועץ אינסטלציה
בגובה 25 ס"מ מתחתית גובה המאיד
- שלט הפעלה אלחוטי


מקרא צבעים בתכנית

- תעלות ותריסי אוויר חוזר
- תעלות ותריסי אספקת אוויר
- תעלות ותריסי אוויר צח
- תעלות ותריסי יניקת אוויר
- תעלות ותריסי שחרור עשן
- צנרת גז וחשמל
- סימון מעגלי מיזוג אוויר

191	מבני מגורים צמודי קרקע נופיה אכ"פ מנשה מגרש 14
דני פרידמן	שם הפרויקט
1:50	מיזוג אוויר ואזווור- הגנות בלבד
02.05.2025	קומה ראשונה ושנייה
דני פרידמן	שם הפרויקט
2	מדידת
לעיון	למשל
לביצוע	לביצוע
02.04.2025	תאריך
דני פרידמן	דני פרידמן



Option No4
inverter duct unit in living
room and wall mounted in
rooms

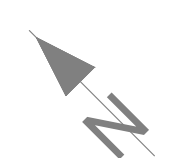[illegible]

חבנית לאשור	02.05.2025	
חבנית נעיון	02.04.2025	
שנתיים:	חאריי:	סל:

הערות

- מקרא

- מקרא צבעים בתכנית

- | | |
|--------------------------|---|
| תעלות ותריסי אוויר חוזר |  |
| תעלות ותריסי אספקת אוויר |  |
| תעלות ותריסי אוויר צח |  |
| תעלות ותריסי ניקת אוויר |  |
| תעלות ותריסי שיחזור עשן |  |
| צנרת גז וחשמל |  |
| סימון מעגלי מידוג אוויר |  |

אייל ארז | מהנדסים ויעצים
עיצוב תוכנית מעבדות מיוחדת, פיקוח עליון

מקום סופי של המעבים
ייתבע בשטח
בתיאום עם האדריכל
מתוך פרויקט
וקבלו מזוג אוויר

מקום סופי של הניקוזים
ייתבע בשטח בתאום עם האדריכל
יועץ אינסטלציה וקבלו מזוג אוויר

בסיס בטון בגובה מינימלי 10 ס"מ
יחדת עיבוי עומדת על"ג בולמי רעידות
לטיפול בקבלו מזוג אוויר