


מתכננים:

ניהול פרויקט
מהיסוד - בן סולומון
פיקוח
מהיסוד - בן סולומון
קונסטרוקציה
ערן שילר
מיזוג אוויר
אייל ארז מהנדסים ויועצים בע"מ
אינסטלציה
איתן אלמסי
חשמל
איתן בסיס
אלומיניום
נוף
נתי בלוקא
חשמל חכם
חימום תת רצפתי
איטום
צבי טל
אקוסטיקה
מעליות
קרקע וביסוס
דיה הנדסת קרקע וביסוס
רישוי

± 0.00 = +247.40
הערות: 1. תכנית זו יש לקרוא יחד עם תכנית הריטשים. 2. גובה אבטמנטים: ראו תכנית פיתוח. 3. המידות הן בין קירות הבניה ולא כולל פיתח. 4. פיתוח השטח סביב הבנוה, כולל, מדרגות, גדרות, שבילים, ריצופים, שיפועים וכו'. 5. איטום קירות והצפות הבנוה כמנוע עם הקרקע ובנידוד תחסי לאורר העמודים והקורות וכל המעטות. כלירות או עם סימני גיטון- ראו תכנית קונסטרוקציה. 6. אף ימים יבוצע ככל מישור אופקי הכולס מהבנין. 7. פיתח תחמי בממד"ד ע"פ מפרס ותמוסיר, מאושר ט"י פיקוד העורף.
המבצע אחראי לסידות : עליו לבקר ולבדוק את כל המידות בתכנית ובנקטת הבנייה. במסגרת של מנות או אי התאמה בתכנית /או בבנין, עליו להודיע על כך מיד לאדריכל כנסם המשיך בעבודתו. המבצע יתחשב או ורק בתכנית שאושרו לכניסוע. המבצע יחזיק באחר, כלכל, נט, של מנדובו של תכנית. אין לקבוע מידות על ידי מדידה בשטח. התכנית הנה רכוש האדריכל ואין לשנות כל שימוש בה או ברעיונות הגלומים בה, אלא באישור בכתב מהאדריכל. מחננס /או יושע אשר שמו רשום בתכנית זו, נושא לכיד באחריות המקצועית והתקנית לתכנית. על המפעל והמכלן לודא התאמת התכנית האדריכלית "לכניסוע" לתכנית ויתר, המכלן והתכנית המאושרות ע"י כל הגורמים הרשמיים. התכנית כוללת את כל האמצעים והידוע עד ליום תוצאתה.

משרד קירות:

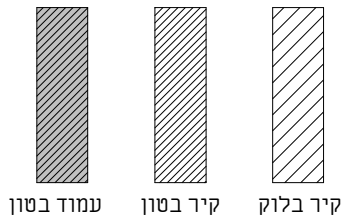

תאריך	תיאור	מהדורה
22.09.2025	מכרז	1

אדריכלות

שם המסמך:	CLIENT NAME:
קבוצת רכישה נופיה	
שם הפרויקט:	PROJECT NAME:
נופיה - מגרש 15	
שם הגליון:	DRAWING NAME:
גליון שער	
מספר גליון:	SHEET NUMBER:
A3-1-100	
מהדורה:	EDITION:
SCALE:	קנה מידה:
STATUS:	סטוס
למכרז	
שורטס ע"י:	נבדק ע"י:
תאריך:	DATE:
22.09.25	


נויטן חיינר אדריכלים
מודד והנדס 2, בית חירות
09-9545642

office@nh-arch.com
www.nh-arch.com

09/11/2025 8:55:22


זכיות ייצור / ע"פ הנחיות ע"ד

נופיה - מגרש 15			
מס' גליון	שם גליון	מהדורה	תאריך הפצת מהדורה
A3-1-100	גליון שער	1	22.09.2025
A3-1-101	תכנית קומת קרקע		
A3-1-102	תכנית קומה א	1	22.09.2025
A3-1-103	תכנית גג	1	22.09.2025
A3-2-200	חזיתות 1	1	22.09.2025
A3-2-201	חזיתות 2	1	22.09.2025
A3-3-100	חתכים	1	22.09.2025
A3-4-100	גליון מדרגות	1	22.09.2025
A3-4-103	פרטים	1	22.09.2025
A3-4-104	פרטי פרגולה	1	22.09.2025
A3-6-1000	רשימת פתחים	1	22.09.2025

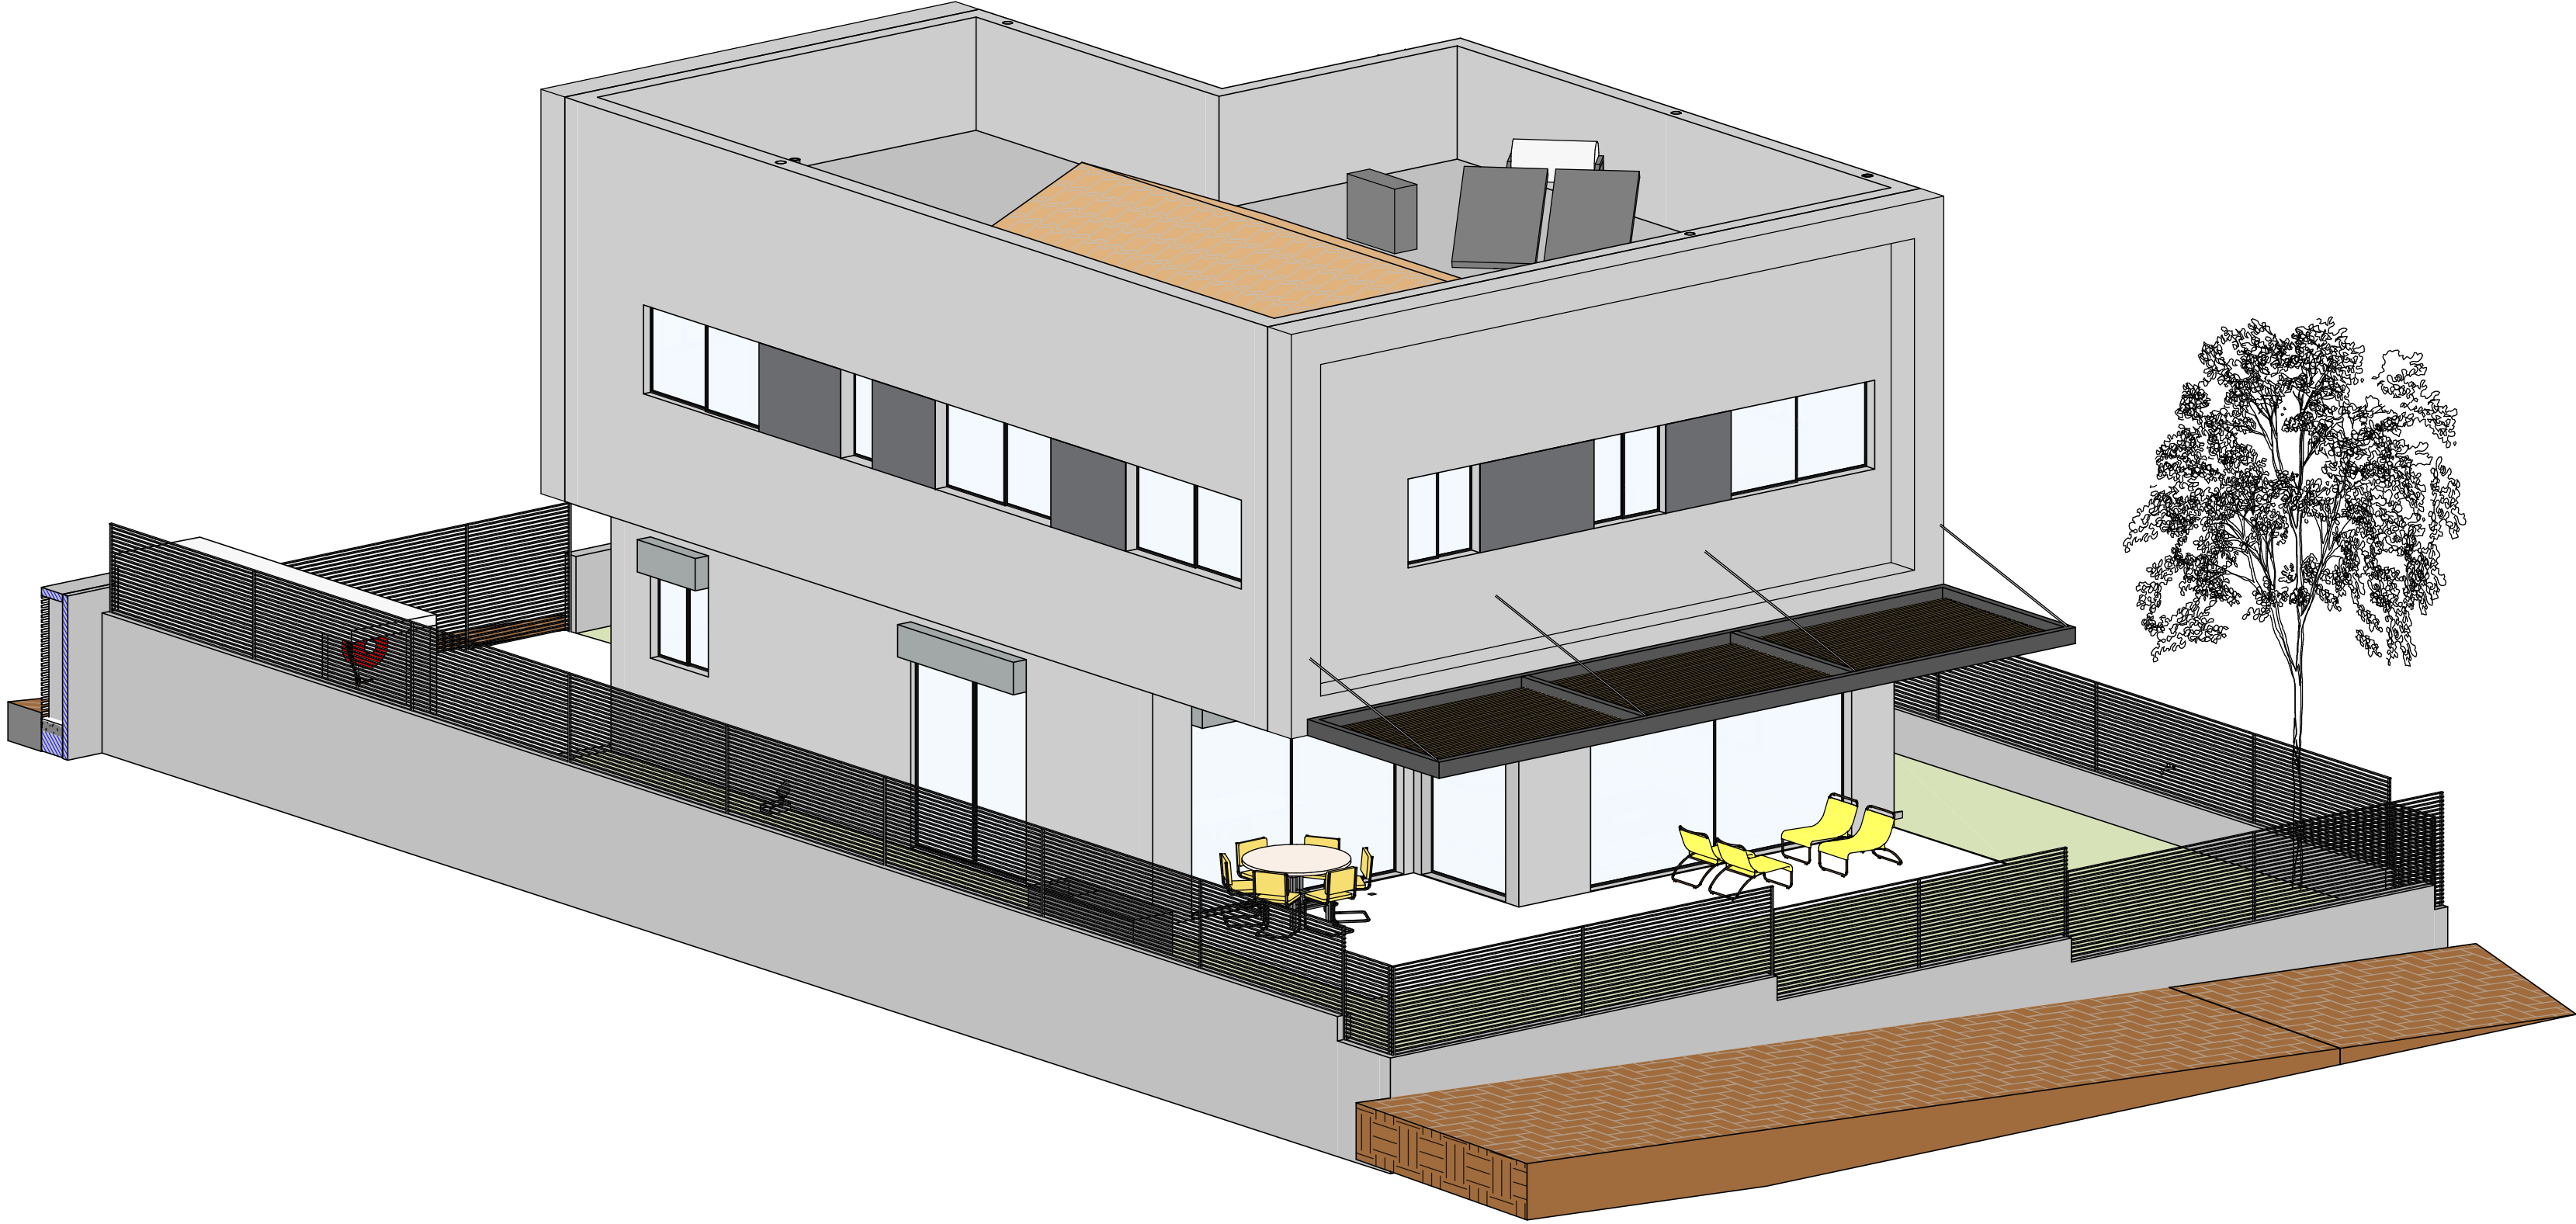

הערות:

- יש לעבוד במקביל לתכניות יועצים המאושרות על ידי האדריכל.
- פרטי ספי חלון - עפ"י חוברת אלומיניום של הספק הנבחר ובתיאום מול אדריכל.
- חימום תת רצפתי (במידה ויש במגרש זה) עפ"י פרטי הספק ובתיאום מול אדריכל.
- יש לעבוד במקביל לתכניות עיצוב פנים (במידה ויש מעצב פנים במגרש זה) המאושרות על ידי האדריכל.
- באחריות הקבלן לעדכן את האדריכל על אי התאמה בין התכניות יועצים לאדריכלות.
- כל הדלתות לפי מפרט מצורף.
- כל אלמנטי הבטון יקבלו התייחסות תרמית לפי הנחיות יועץ.
- פרטי איטום, בידוד וניקוז עפ"י תכניות יועצים ובאחריות הקבלן.

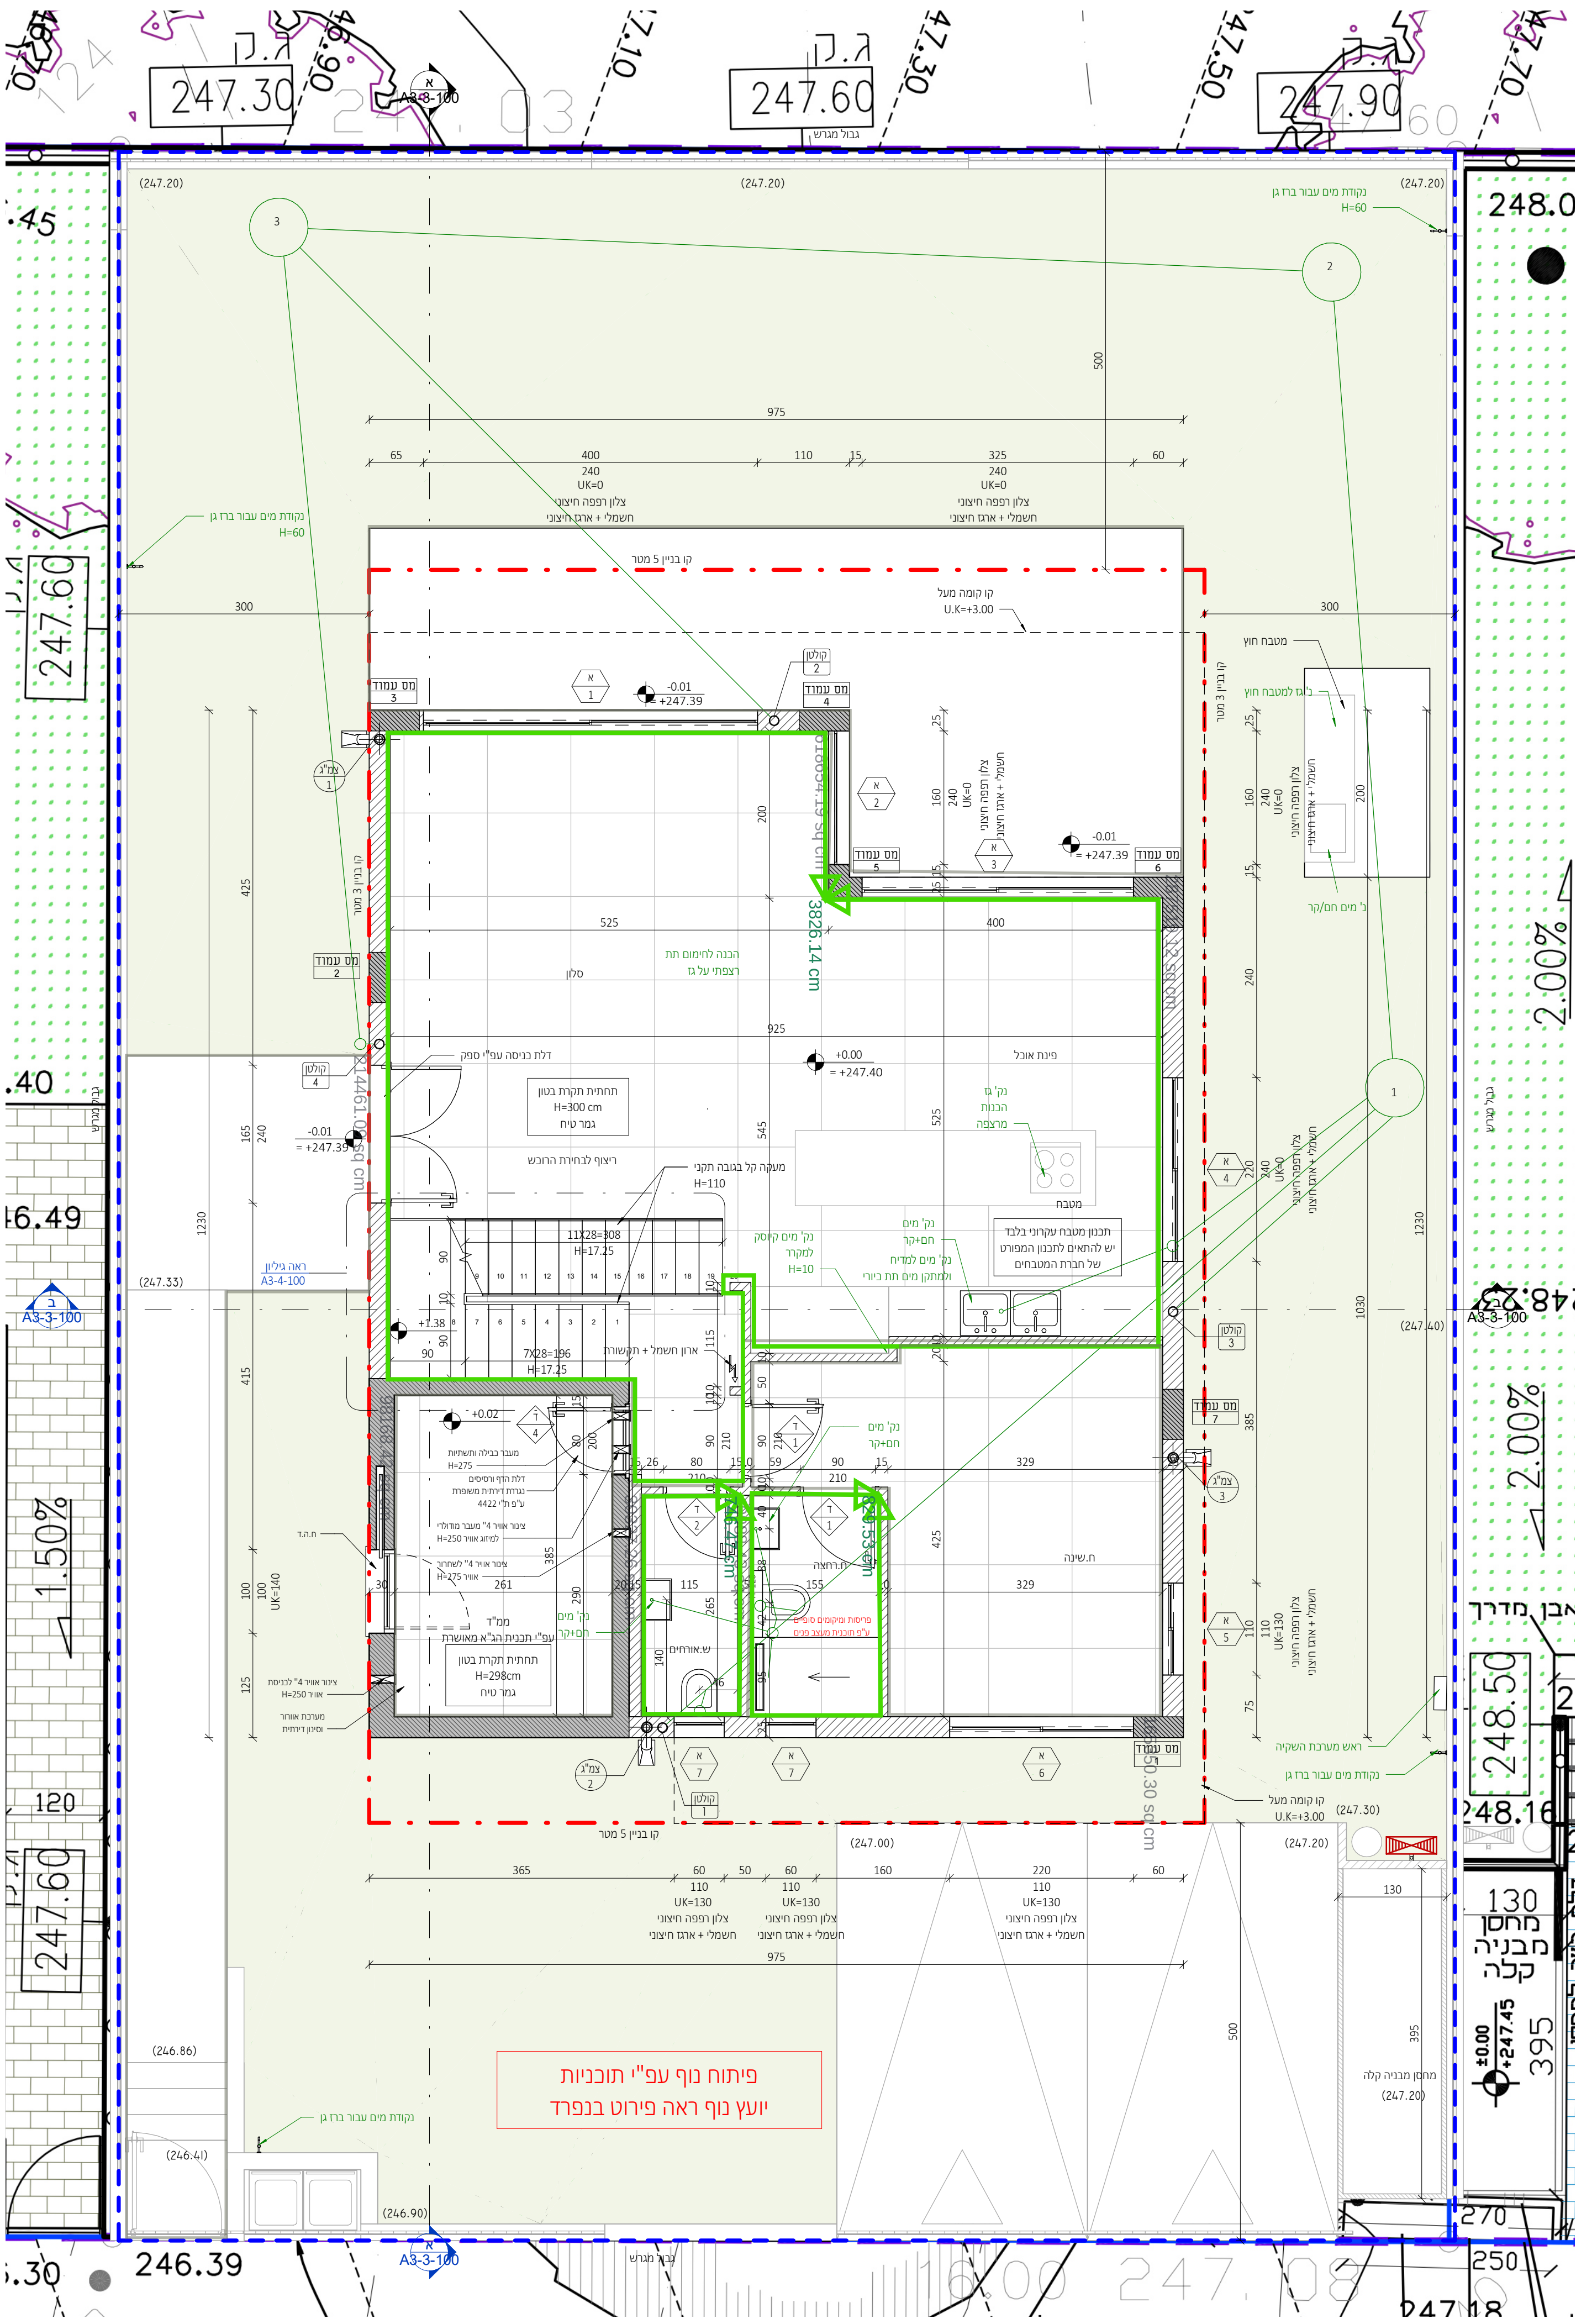

תכנית קומת קרקע

מתכנים:

ניהול פרויקט
מהיסוד - בן סולומון
פיקוח
מהיסוד - בן סולומון
קונסטרוקציה
ערן שילר
מיזוג אוויר
אייל ארז מהנדסים ויועצים בע"מ
אינסטלציה
איתן אלמסי
חשמל
איתן בסיס
אלומיניום
נוף
נתי בלוקא
חשמל חכם
חימום תת רצפתי
איטום
צבי טל
אקוסטיקה
מעליות
קרקע וביסוס
דיה הנדסת קרקע וביסוס
רישוי

± 0.00 = +247.40
הערות: 1. תכנית זו יש לקרוא יחד עם תכניות הרושפים. 2. גובה אבסולוטי - ראה תכנית פיתוח. 3. הפרדות הן בין קירות הבניה ולא כולל פחים. 4. פיתוח השטח סביב הבנוי, כולל, סדרות, גדרות, שבילים, ריצופים, שטחים גזרים, חניה וגן ראו תכנית פיתוח. 5. איטום קירות ורצפות הבנוי כמנוע עם הקרקע ובזווית חתכי לאורך העמודים והקירות ולכל המפרקים. כליות או עם סימני גיבס - ראו תכנית קונסטרוקציה. 6. איזורים בוצעו בכל מישור אופקי הבולם בחתוכי. 7. סוף חתכי במסלול - ע"פ מפרט חומרים, מאושר ע"י פיקוח העורך.
הבנוע אחראי לסידור: עליו לבקר ולבדוק את כל המידות בתכנית ובקטע המבנה. במסלול של מידות או אי התאמה בתכנית /או בבנוי, עליו להודיע על כך מיד לאדריכל בסיום המשיך בעבודתו. הבנוע יישמש או ויק בתכנית שאושרו לכניס. המבנה יחזיק במהלך כלל של, של מידות של תכנית. אין לקבוע מידות על ידי חדיה בשום. התכנית הבנוי רכוש האדריכל ואין לשנות כל שימוש בה או ברעיונות הולמים בה, אלא באישור בכתב מהאדריכל. מונחים /או יושם אשר שמו רשום בתכנית זו, נושא לכד באחריות המקצועית והתקנית לתכנית. על המפקח והמבנה לודא התאמה התכנית האדריכלית - לכניס. לתכנית זו, המפרט והתכנית המאושרות ע"י כל העורכים והרשמים. התכנית כוללת את כל האפשרויות הדרוש על ליום תחלפת.

משרד קירות:

קיר בלוק
קיר בסון
עמוד בסון

תאריך	תיאור	מהדורה

אדריכלות

שם המשיין:	CLIENT NAME:
קבוצת רכישה נופיה	
שם הפרויקט:	PROJECT NAME:
נופיה - מגרש 15	
שם הנליין:	DRAWING NAME:
תכנית קומת קרקע	
מספר גיליון:	SHEET NUMBER:
A3-1-101	
תאריך:	DATE:
22.09.25	


ניהול פרויקט
מהיסוד - בן סולומון
פיקוח
מהיסוד - בן סולומון
קונסטרוקציה
ערן שילר
מזוזג אוויר
אייל ארז מהנדסים ויועצים בע"מ
אינסטלציה
איתן אלמסי
חשמל
איתן בסיס
אלומיניום
נוף
נתי בלוקא
חשמל חכם
חימום תת רצפתי
איטום
צבי טל
אקוסטיקה
מעליות
קרקע וביסוס
דיה הנדסת קרקע וביסוס
רישוי

הערות:
 1. הכנית י"ש לקראת יחד עם הכניות היועצים.
 2. גבש אבסולוטס – ראו הכנית פיתוח.
 3. המידות הן בין קירות הכנית (לא כולל סף).
 4. פיתוח השטח סביב המבנה, כולל, מדרכות, שבילים, רציפים, שיטות גינה, חניה גיטון-ראו הכנית פיתוח.
 5. איסוס תכנית ריצפת הכנית במגע עם קרקע ובידוד תרמי לאורך הנעמדים.
 6. הקורות על הקירות- תלבוזת זה עם מיני (גיטון-ראו הכנית) קונסטרוקציה.
 7. אף מי יבוצע בכל מישור אופקי הכולס מחביר.
 8. שטח תחם במסגרת ע"פ מפרט תרומיקר, אאוור ע"י פיקוד הנורף.

[illegible]

עמוד בטון קיר בטון יד בלוק

www.nh-arch.com 09-9545842 70

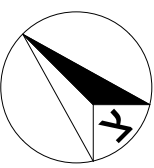

1 : 50

1. יש לעבוד במקביל לתכניות יועצים המאושרות על ידי האדריכל.
2. פרטי ספי חלון - עפ"י חוברת אלומיניום של הספק הנבחר ובתיאום מול אדריכל.
3. חימום תת רצפתי (במידה ויש במגרש זה) עפ"י פרטי הספק ובתיאום מול אדריכל.
4. יש לעבוד במקביל לתכניות עיצוב פנים (במידה ויש מעצב פנים במגרש זה) המאושרות על ידי האדריכל.
5. באחריות הקבלן לעדכן את האדריכל על אי התאמה בין התכניות יועצים לאדריכלות.
6. כל הדלתות לפי מפרט מצורף.
7. כל אלמנטי הבטון יקבלו התייחסות תרמית לפי הנחיות יועץ.
8. פרטי איטום, בידוד וניקוז עפ"י תכניות יועצים ובאחריות הקבלן.

מתכונים:


ניהול פרויקט
מהיסוד - בן סולומון
פיקוח
מהיסוד - בן סולומון
קונסטרוקציה
ערן שילר
מיוזג אוויר
אייל אזר מהנדסים ויועצים בע"מ
אינסטלציה
איתן אלמסי
חשמל
איתן בסיס
אלומיניום
נוף
נתי בלוקא
חשמל חכם
חימום תת רצפתי
איטום
צבי טל
אקוסטיקה
מעליות
קרקע וביסוס
דיה הנדסת קרקע וביסוס
ירשני

$$\pm 0.00 = +247.40$$

הערת:
 תכנית זו איש לקראת ידע תכנית הוועיצים.
 נגבה אבסולוט. ראו תכנית פחות.
 הפיתוח הוא בראי קורות הבית, כולל, מדרגות, בדרות, שילובים, ריצופים,
 שיפוטים מבטיחים ויגורן-ראו תכנית פחות.
 איסוס ותכנית הרפואת הבית מבטגם על הקרקע בידוד תמימ לאורך המעודים
 תחנות וועל התחרות. בקליות וועל פילוי (ניגון). ראו תכנית פחות וסנסרוסקופיה
 אדם קיצוב כלכלי ופחות אופייני הבולט תחבין.
 פחות תמימ. כפי פסוס תחבין, תאמנני ועל פיקוד העורפ.

[illegible]

מקרא קירות:

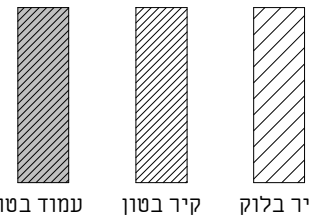[illegible]

אדריכלות

CLIENT NAME: _____: המזכיר

קבוצת רכישה נופיה

PROJECT NAME: הפרויקט:

נופיה - מגרש 15

DRAWING NAME: תגלית

תכנית גג

SHEET NUMBER: 99 גליון:

A3-1-103

SCALE: קנה מידה: EDITION: דורה:

1 : 50

STATUS: 1

למכר	
------	---


דסט ע"י: _____ נבדק ע"י: _____

DATE: 22 09 25 ר"ר:

Neurological Disorders and Disabilities

office@nh-arch.com מרכז ההדורים 2, בית חירות

$\mu_{\text{H}_2} = \mu_{\text{H}} + \mu_{\text{H}} = 2\mu_{\text{H}}$

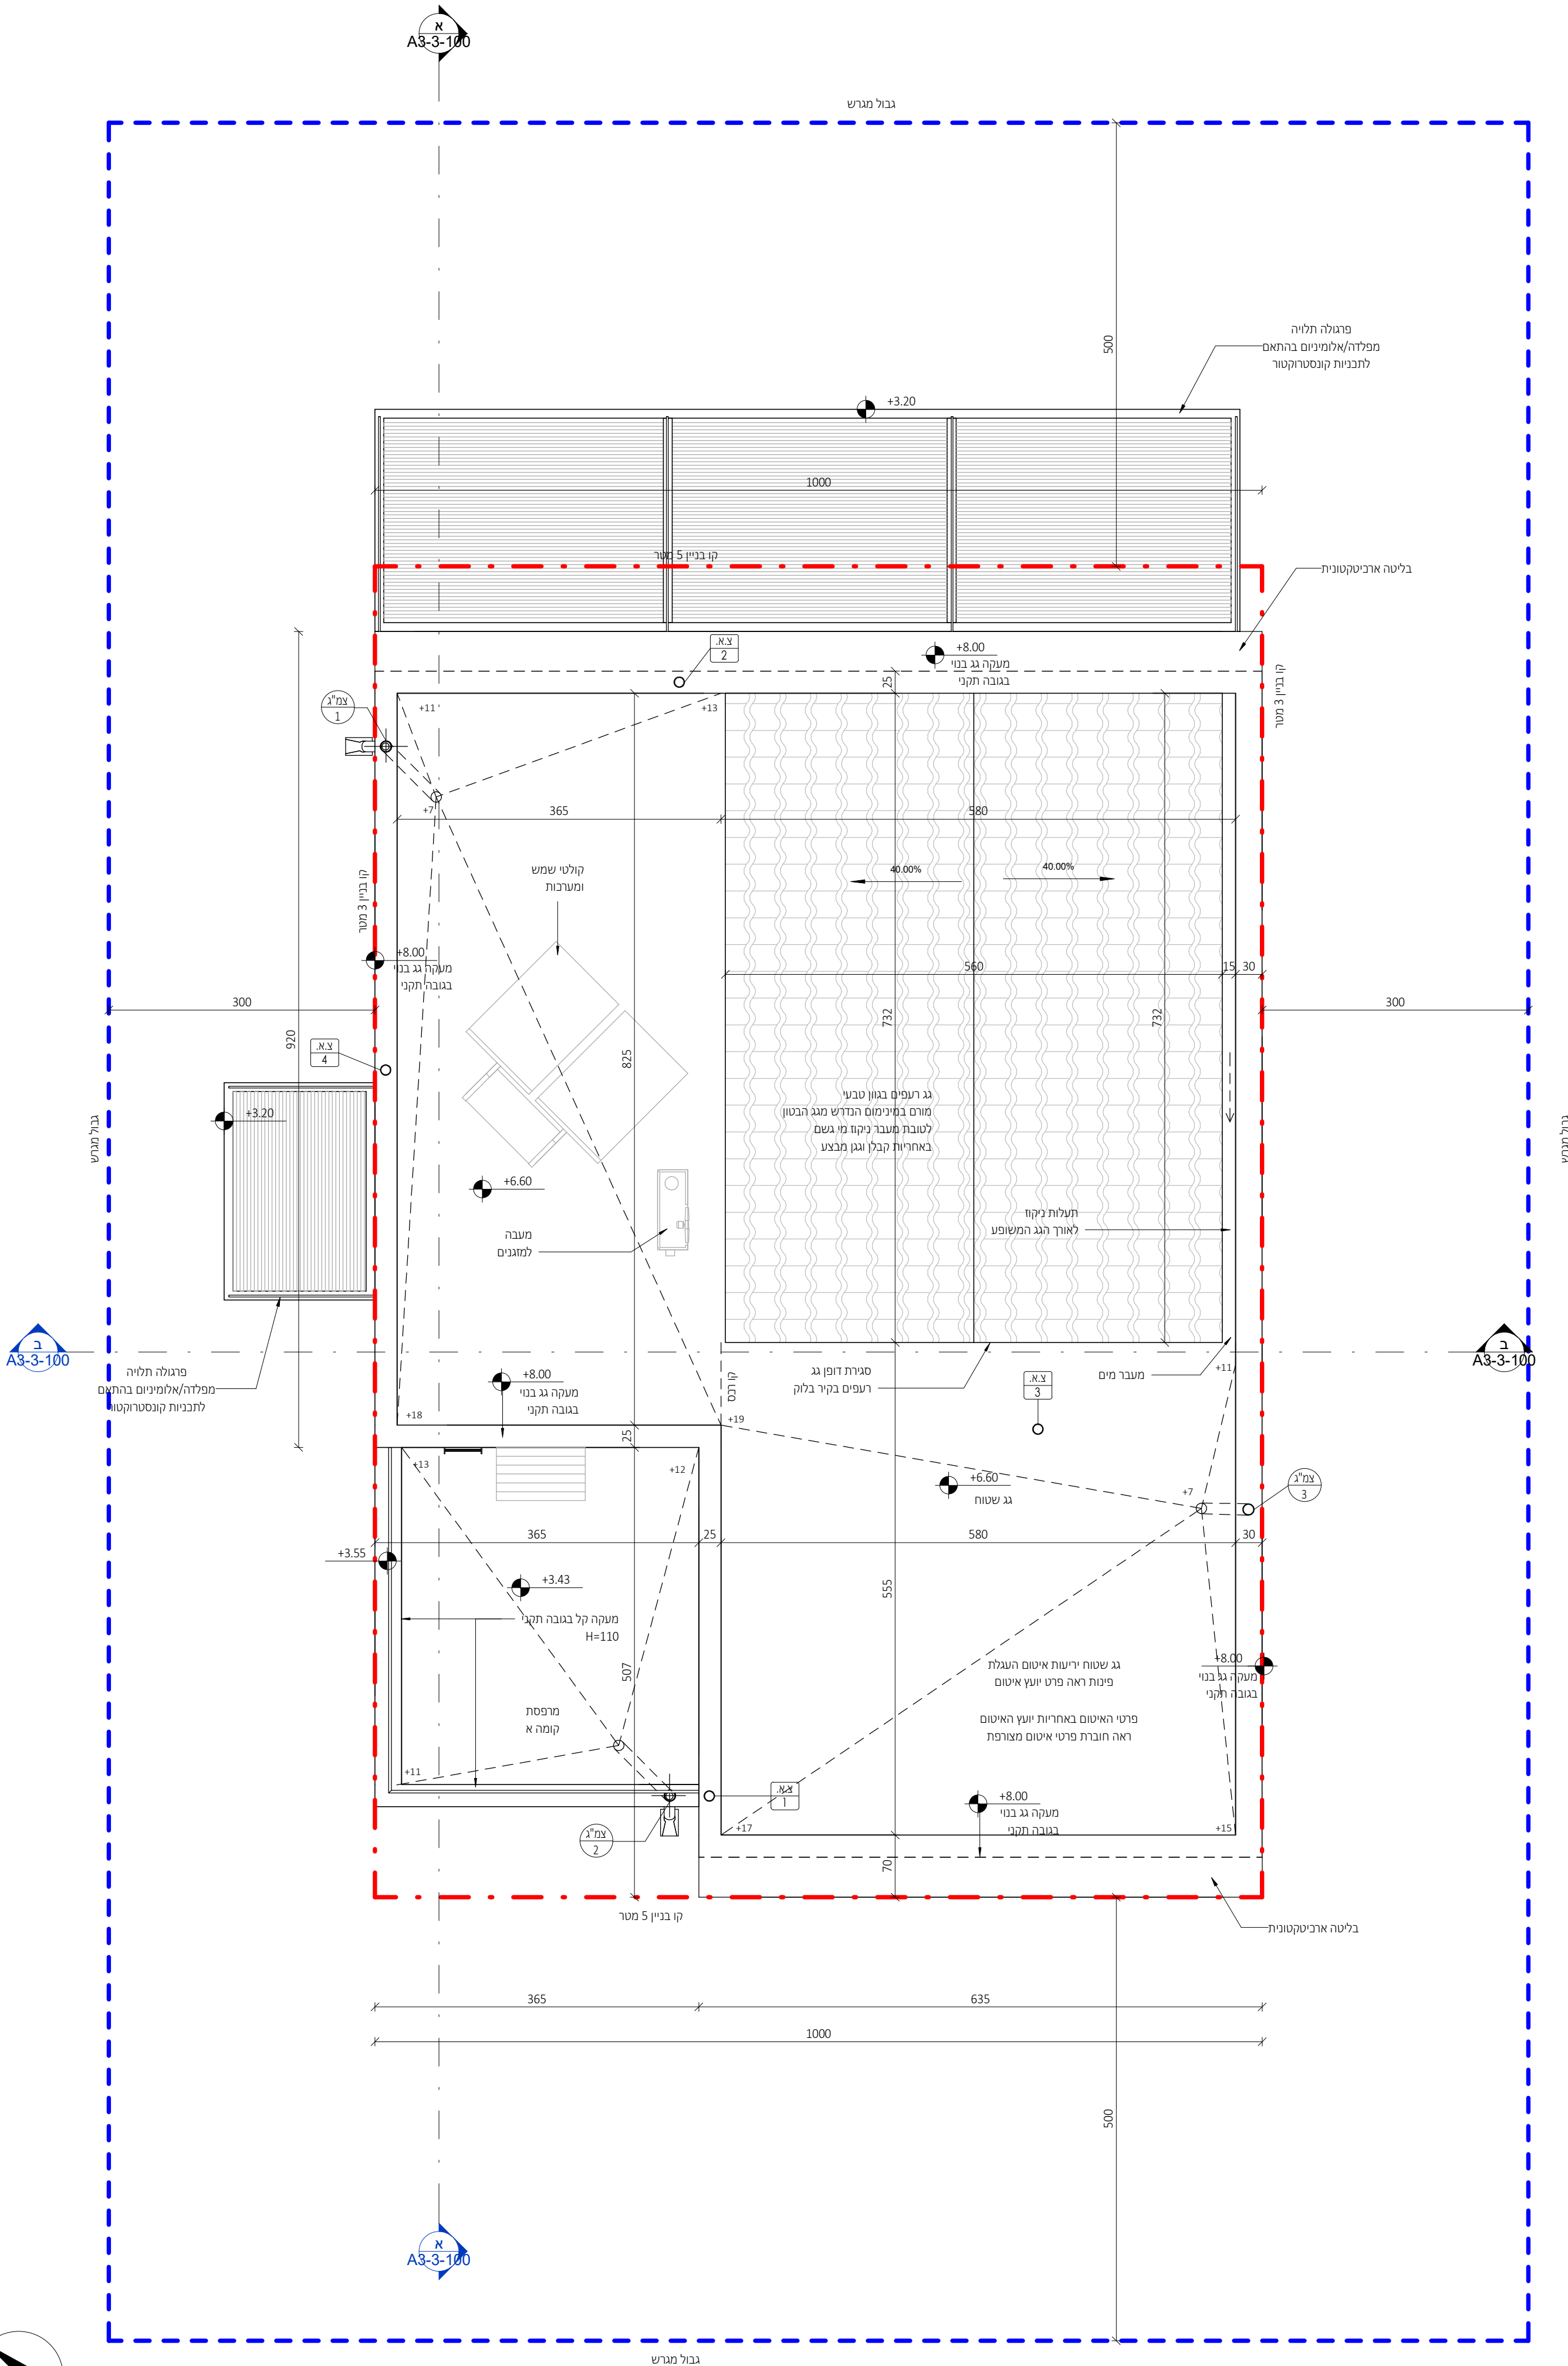

תכנית גג


1 : 50

מתכננים:

ניהול פרויקט
מהיסוד - בן סולומון
פיקוח
מהיסוד - בן סולומון
קונסטרוקציה
ערן שילר
מיזוג אוויר
אייל ארז מהנדסים ויועצים בע"מ
אינסטלציה
איתן אלמסי
חשמל
איתן בסיס
אלומיניום
נוף
נתי בלוקא
חשמל חכם
חימום תת רצפתי
איטום
צבי טל
אקוסטיקה
מעליות
קרקע וביסוס
דיה הנדסת קרקע וביסוס
רישוי

± 0.00 = +247.40
הערות: 1. תכנית זו הי לקרא יחד עם תכנית הריטשים. 2. גובה המסלול: ראו תכנית פיתוח. 3. המידות הן בין קירות הבניה ולא כולל פחים. 4. פיתוח השטח סביב המבנה, כולל, מדרגות, גדרות, שבילים, ריצופים, שטחים גזרים, חניה גג ורא תכנית פיתוח. 5. איטום קירות ורצפות המבנה כמתנ עם הקרקע ובידוד תרמי לאורך העמודים והקירות למעט הקירות. כליות או עם סימני גיבוי. ראו תכנית קונסטרוקציה. 6. אף חים יבוצע בכל מישור אופקי הכולל מהגבון. 7. סיוח תרמי במסיד- ע"פ מפרט דומקור, מאושר ט"י פיקוד העורף. המבצע אחראי למידות : עליו לבקר ולבדוק את כל המידות בתכנית ובקשות העבודה. במסלול של מידות או אי התאמה בתכנית /או בגבון, עליו להודיע על כך מיד לאדריכל בסיום המשיך המעבר במבנה. המבצע ישתמש או ויק בתכנית המשיך המעבר למינימום. המבצע יחזיק במהלך כלל המ, של משרדו של תכנית. אין לקבוע מידות על ידי חזירה בשר מוס. התכנית היתה רכוש האדריכל ואין לשנות כל שימוש בה או ברעיונות הגלומים בה, אלא באישור בכתב מהאדריכל. מחדש /או יועץ אשר שמו רשום בתכנית זו, נושא לכיד באחריות המקצועית והתקנית לתכנית. על המבצע והמקבל לזרז את המבצע התכנית האדריכלית "לביצוע" לתכנית זו. המבצע והתכנית המאושרות על ידי הגורמים הרשמיים. התכנית כוללת את כל האמצעים והדגם עד ליום תחילתה.

משרד קירות:

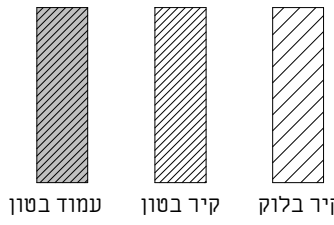

תאריך	תיאור	מהדורה
22.09.2025	מכרז	1

אדריכלות

שם המסמך:	CLIENT NAME:
קבוצת רכישה נופיה	
שם הפרויקט:	PROJECT NAME:
נופיה - מגרש 15	
שם הגיליון:	DRAWING NAME:
חזיתות 1	
מספר גיליון:	SHEET NUMBER:
A3-2-200	
תאריך:	DATE:
22.09.25	

NeumanHaynerArchitects

נוירן חיינר אדריכלים
מודרן והדריס 2, בית חירות
09-9546842


office@nh-arch.com
www.nh-arch.com

09/11/2025 8:55:30

זכיות יימור / ע"פ הנחיות ע"ד


פיתוח נוף עפ"י תוכניות
יועץ נוף ראה פירוט בנפרד

פיתוח נוף עפ"י תוכניות
יועץ נוף ראה פירוט בנפרד

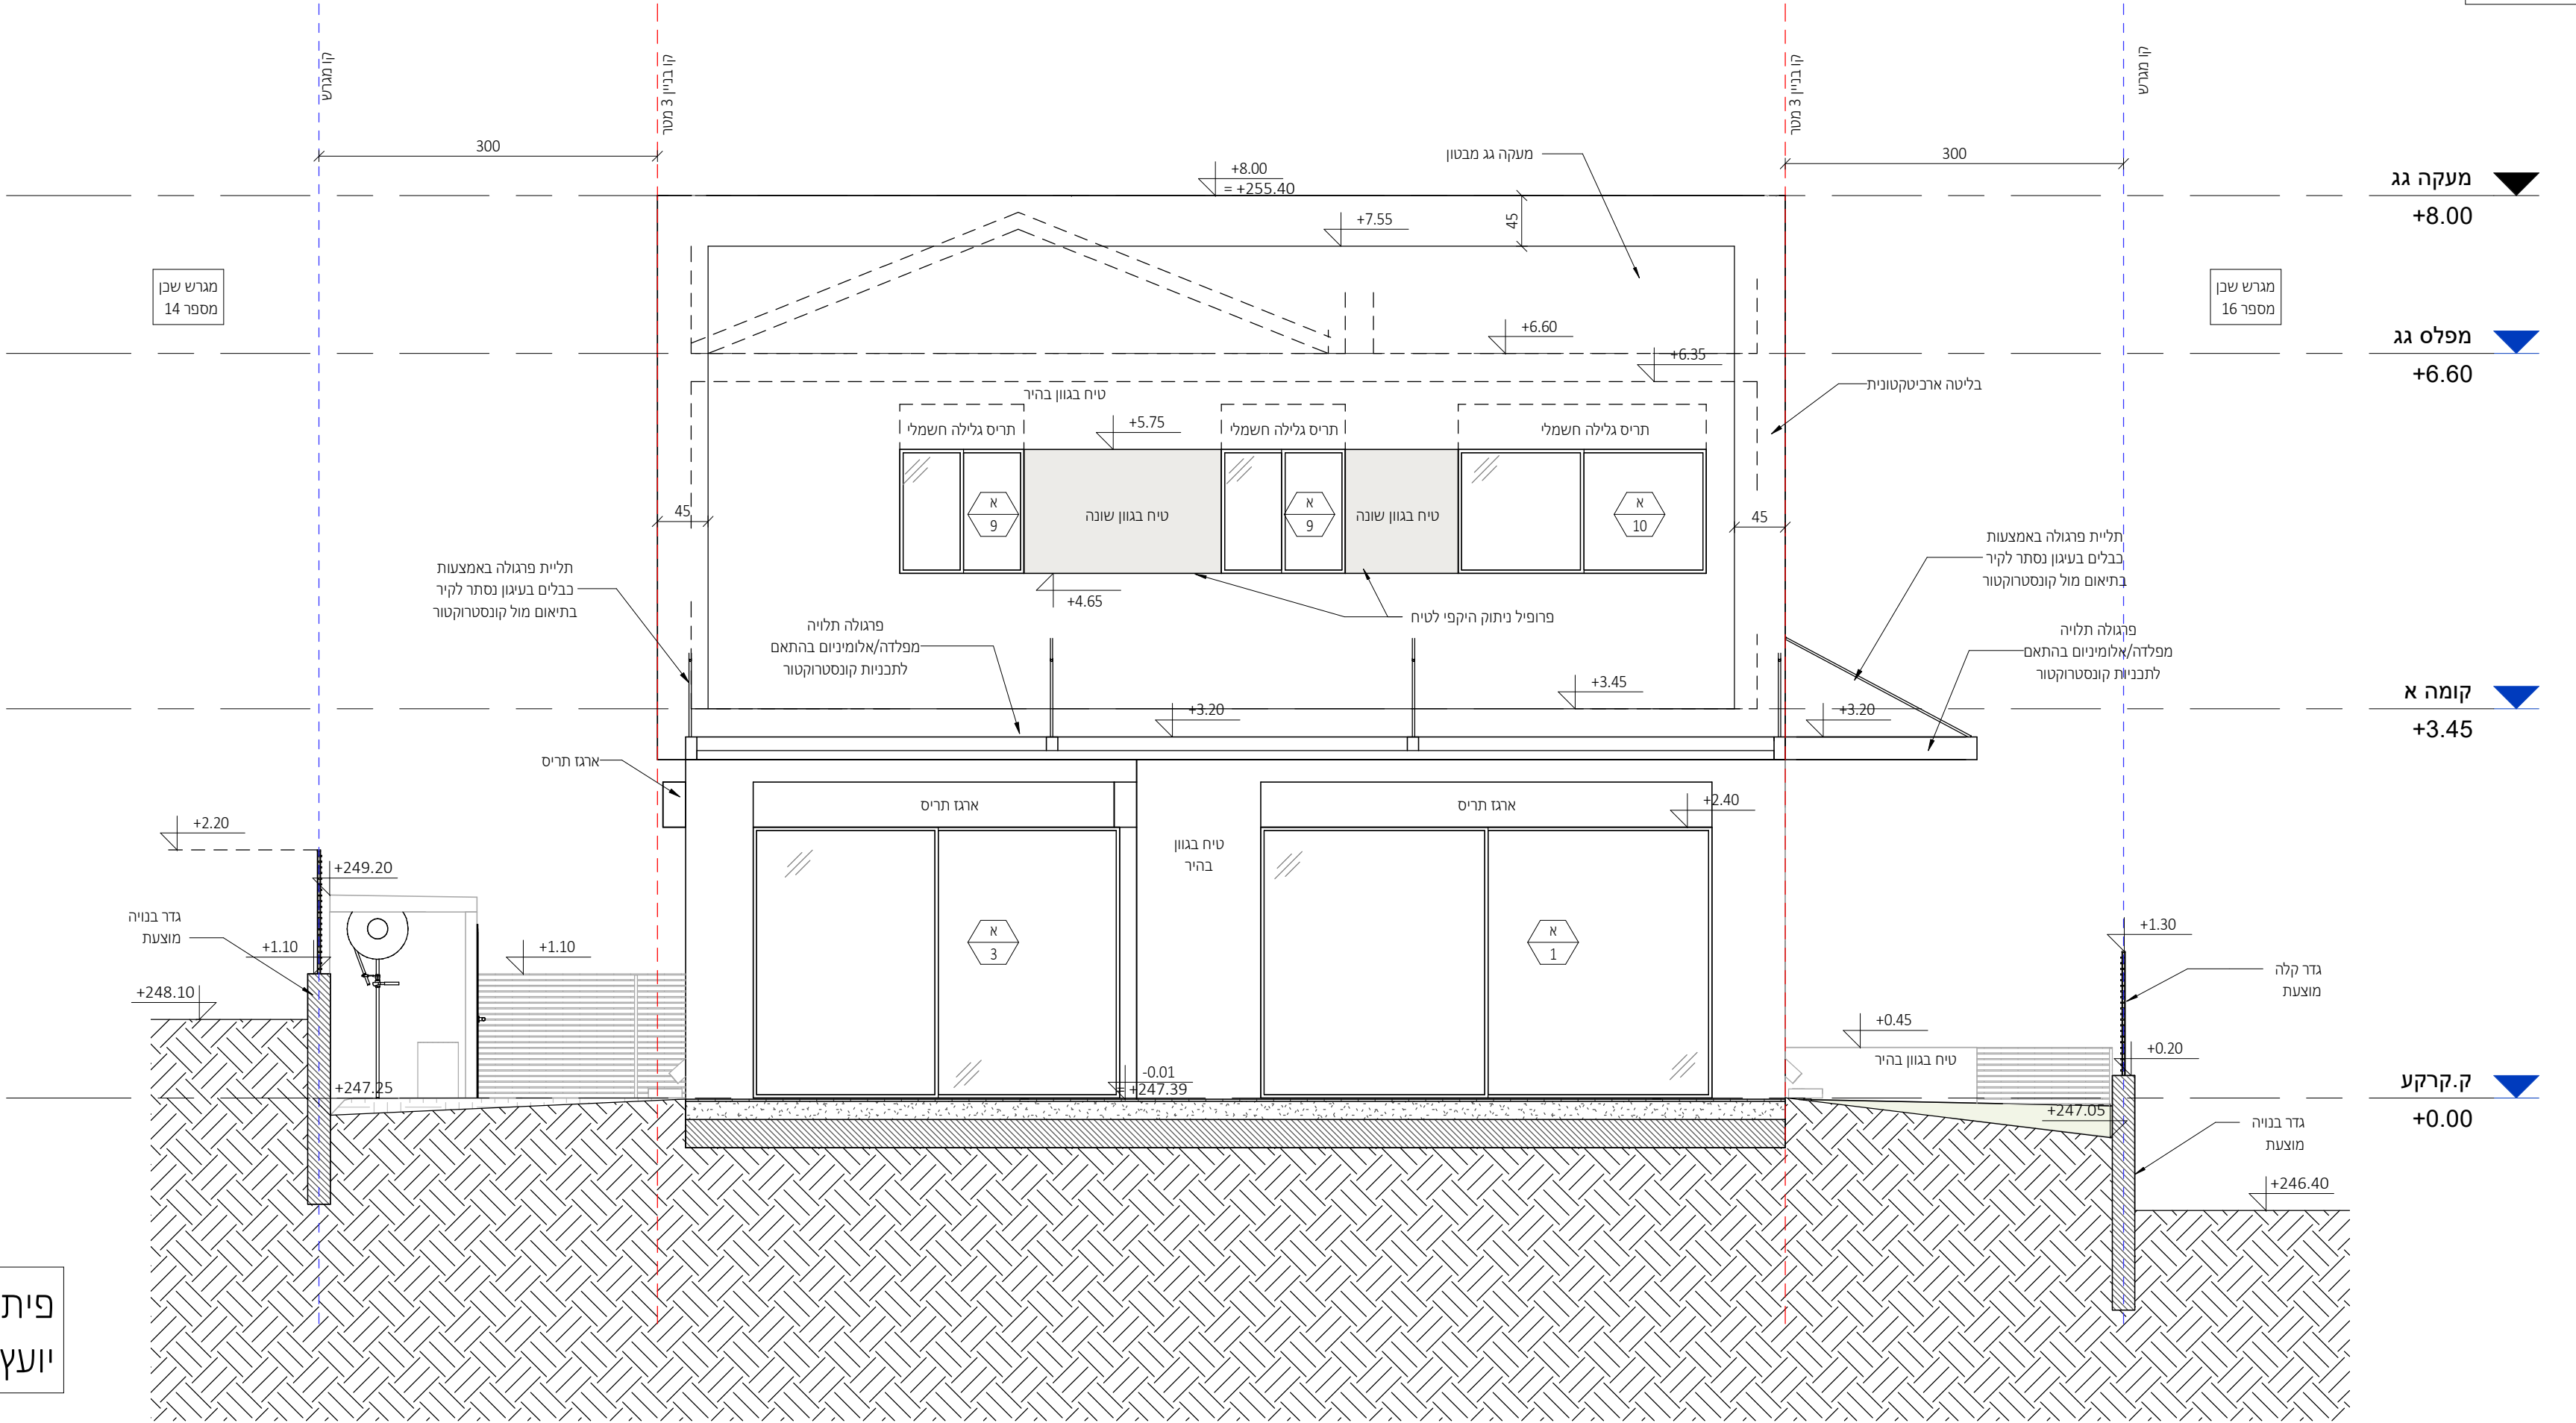

חזית דרומית


1 : 50

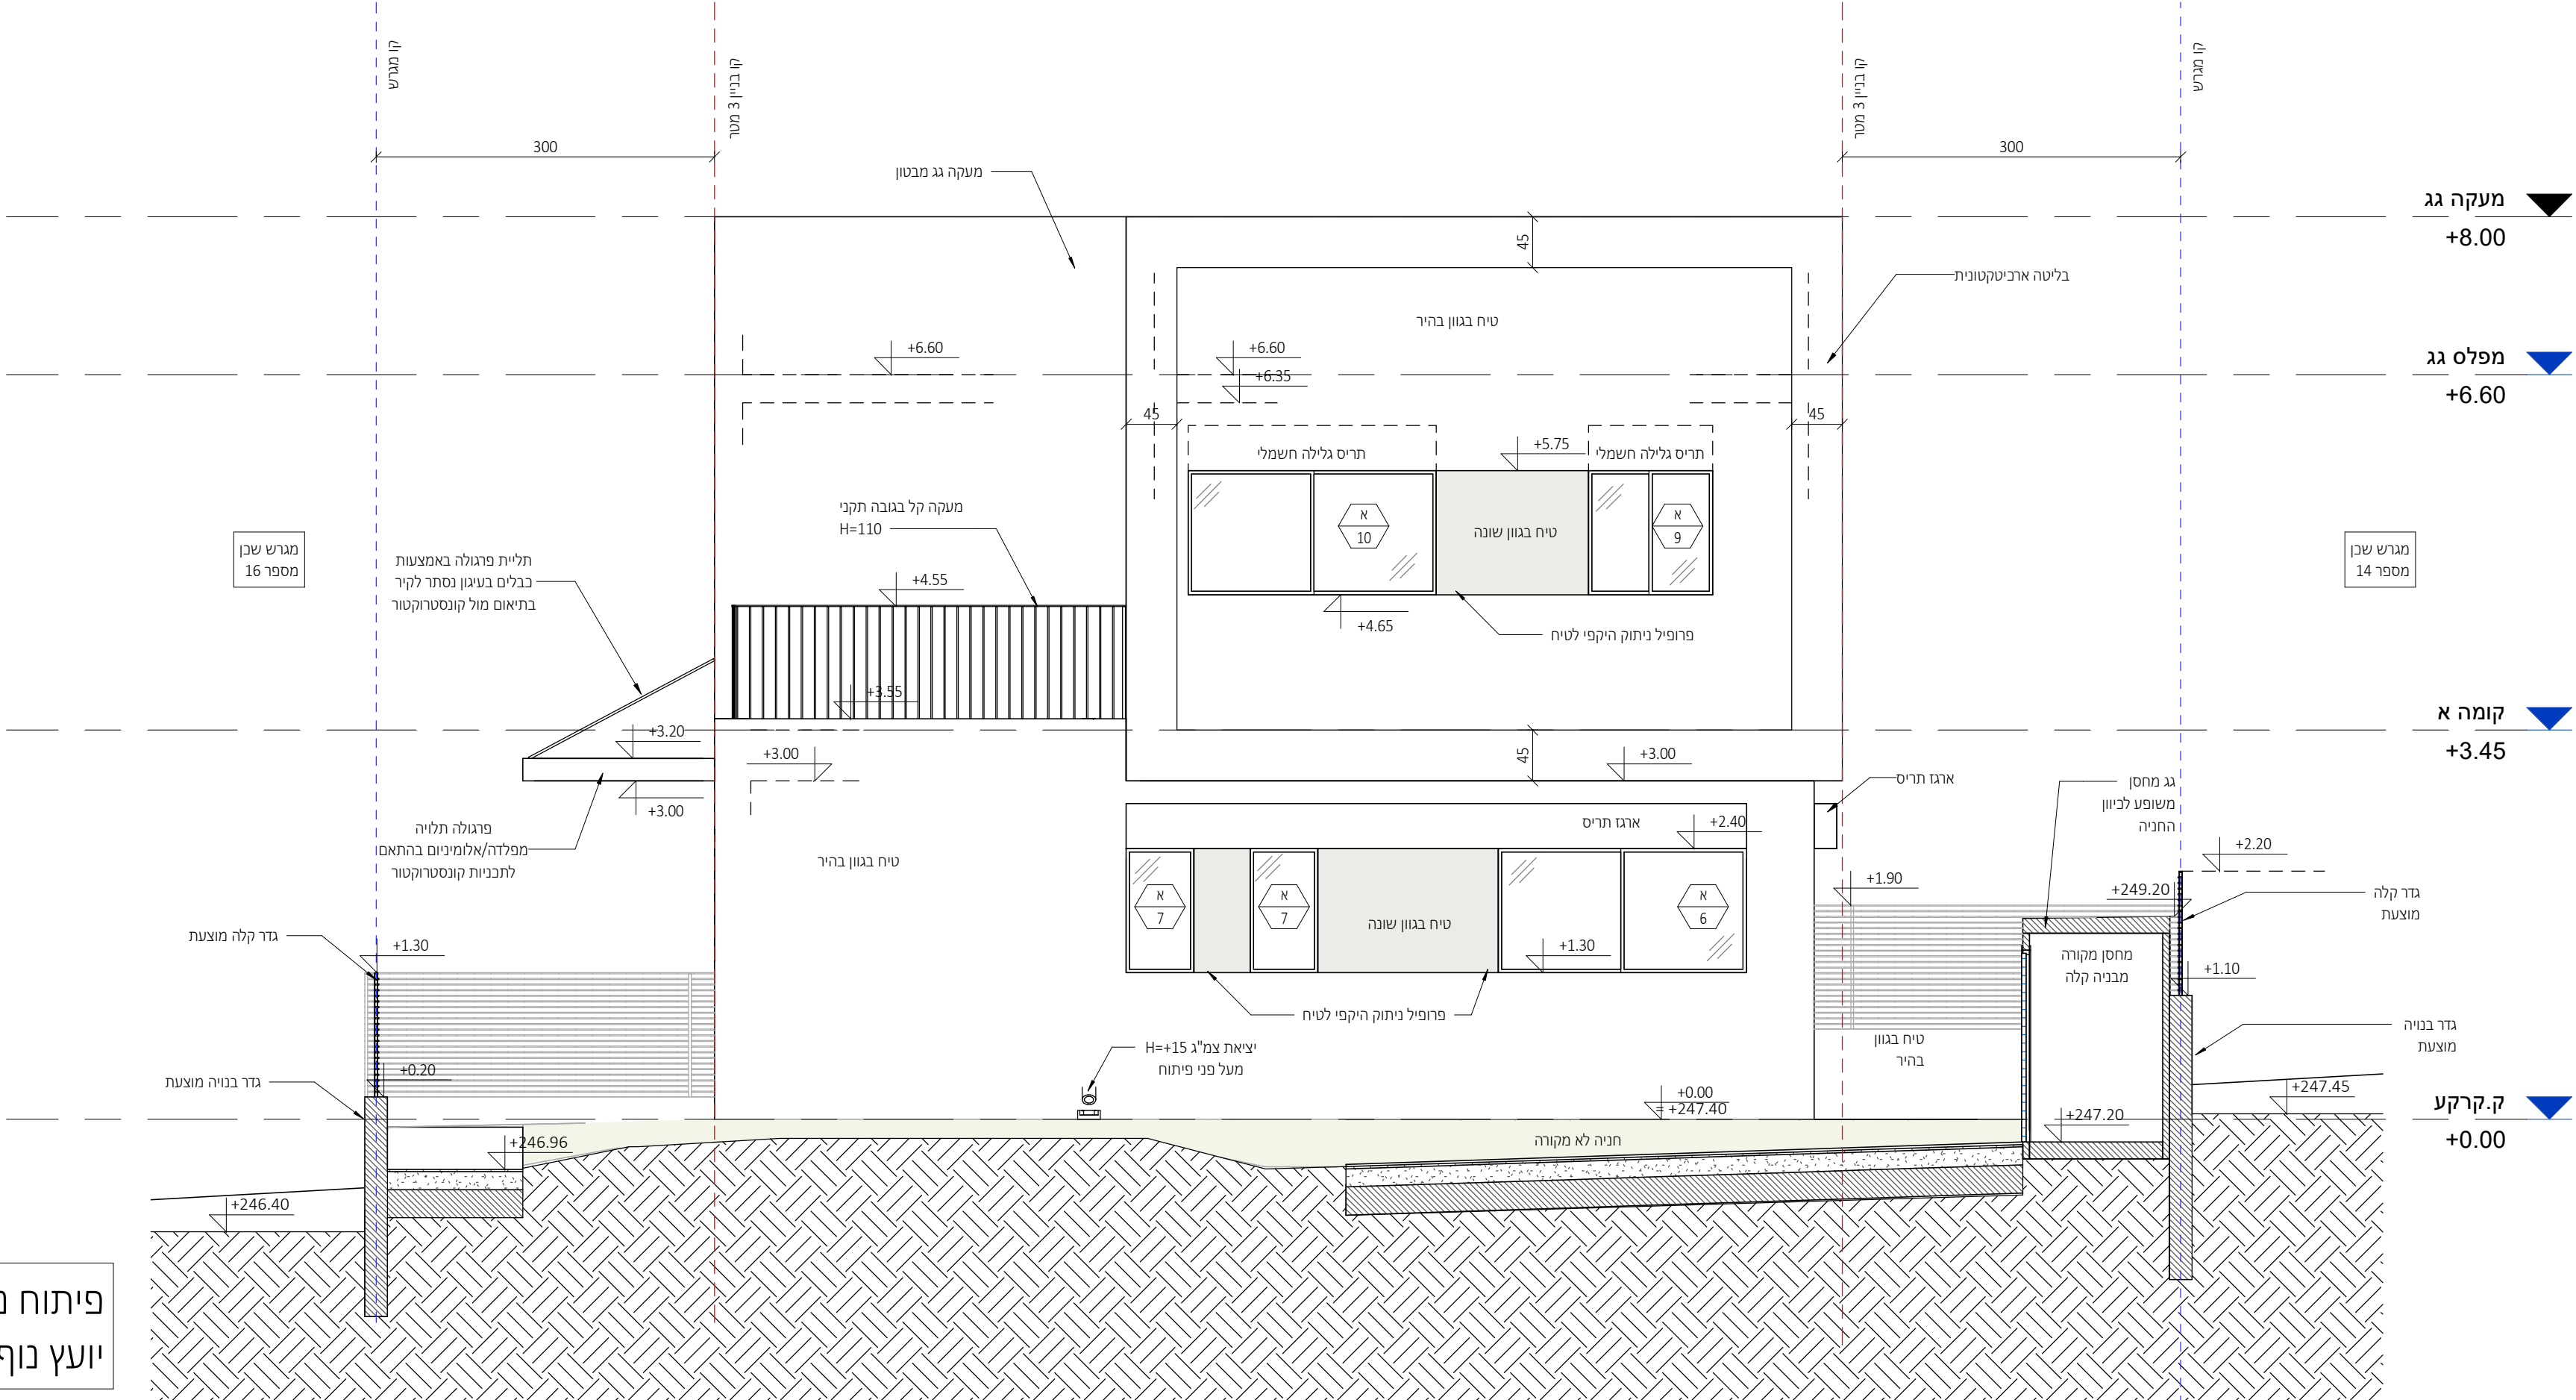

חזית צפונית


1 : 50

פרטי איטום, בידוד וניקוז עפ"י תכניות יועצים ובאחריות הקבלן

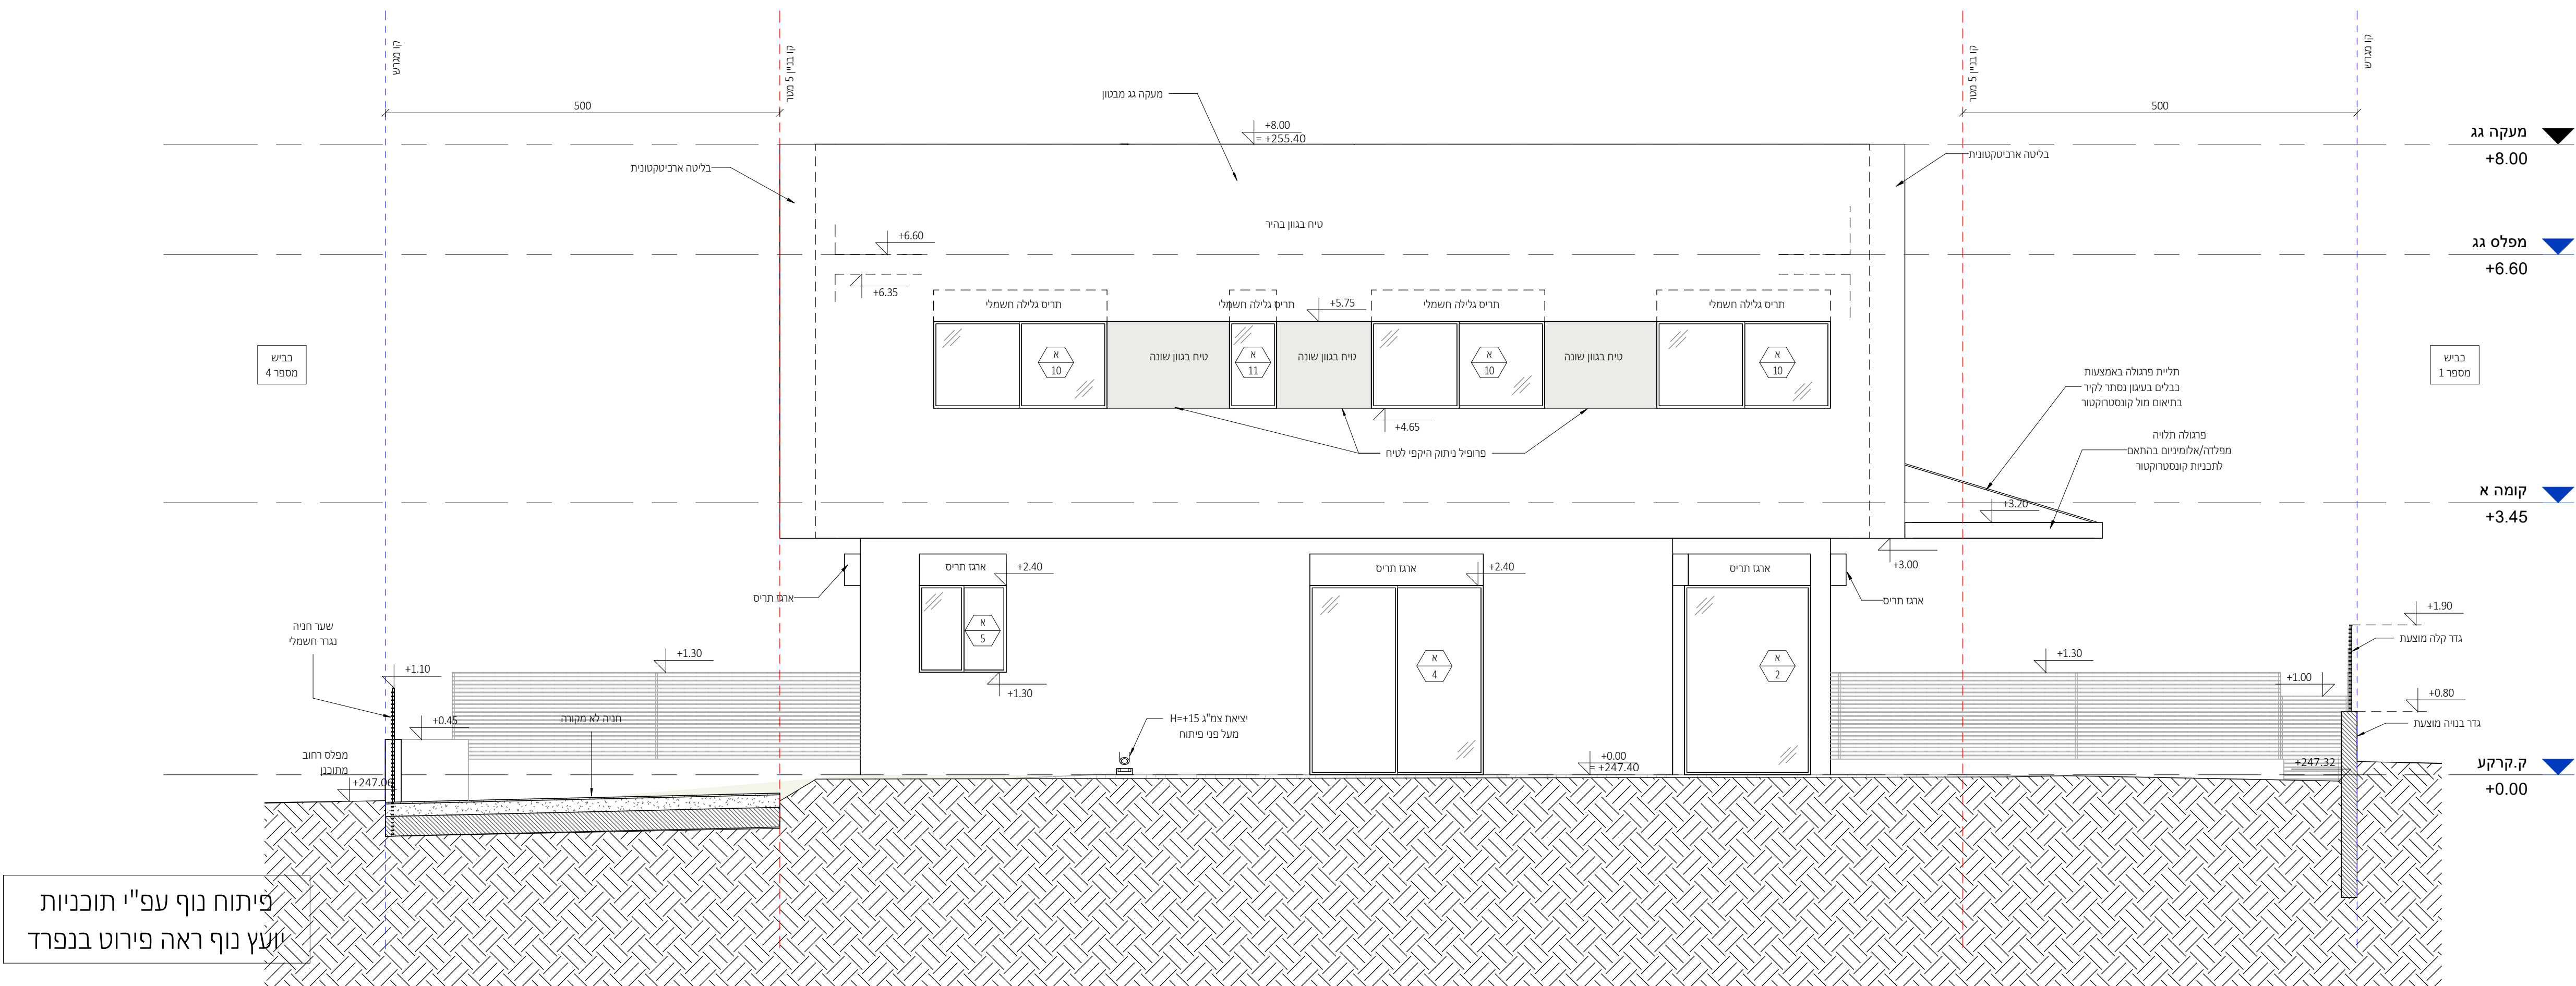

חזית מערבית

1 : 50

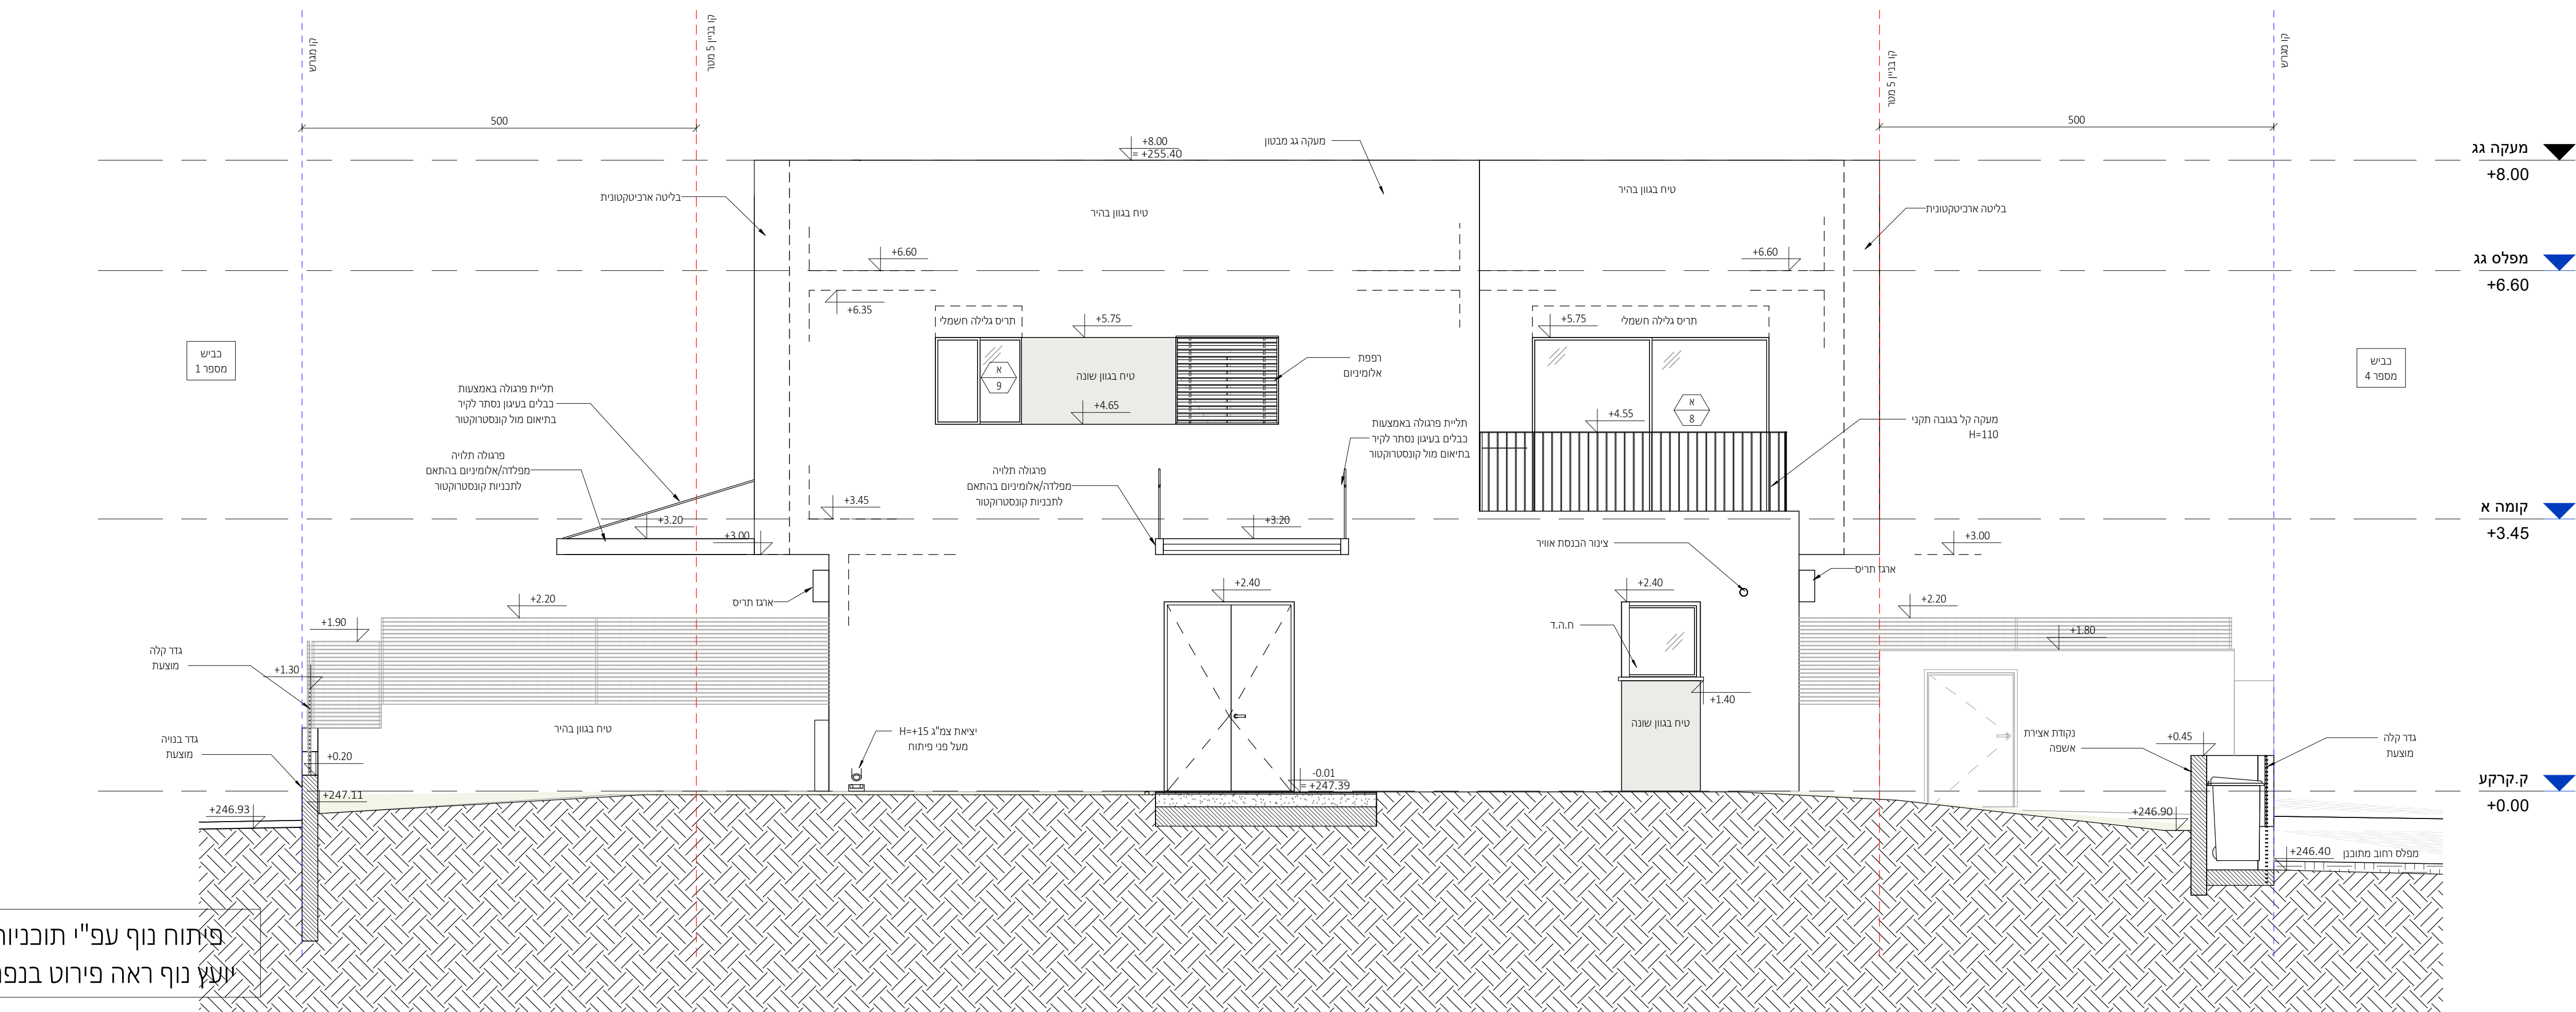

חזית מזרחית


1 : 50

מתכונים:

ניהול פרויקט
מהיסוד - בן סולומון
פיקוח
מהיסוד - בן סולומון
קונסטרוקציה
ערן שילר
מיזוג אוויר
אייל ארז מהנדסים ויועצים בע"מ
אינסטלציה
איתן אלמסי
חשמל
איתן בסיס
אלומיניום
נוף
נתי בלוקא
חשמל חכם
חימום תת רצפתי
איטום
צבי טל
אקוסטיקה
מעליות
קרקע וביסוס
דיה הנדסת קרקע וביסוס
רישוי

[illegible]

זקרא קירות:

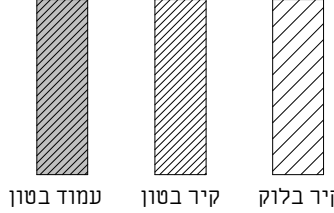[illegible]

אדריכלות

ש המזמין:

CLIENT NAME: _____ שם המזמין:

קבוצת רכישה נופיה

1970s, 1980s, 1990s, 2000s, 2010s, 2020s

PROJECT NAME:	התכנית החדשה
---------------	--------------

נופיה - מגרש 15

ס הגליון:

DRAWING NAME: ס הגליון:

חזיתות 2

ספר גליון:

SHEET NUMBER: 190

A3-2-201

SCALE: קנה מידה: EDITION: הדורה: ^

1 : 50

STATUS:	תחזוקה
---------	--------

STATUS: **1**

(13/17)	
---------	---

רשט ע"י: _____ נבדק ע"י: _____

DATE: 22 09 25 :8717

NeumanHaynerArchitects

וימן חיינר אדריכלים
אנציקלופדיה של חיינו

www.nh-arch.com 09-9545842 70

זכויות ייצור / ע"פ הנחיות עו"ד

פרטי איטום, בידוד וניקוז עפ"י תכניות יועצים ובאחריות הקבלן

מתכונים:

ניהול פרויקט
מהיסוד - בן סולומון
פיקוח
מהיסוד - בן סולומון
קונסטרוקציה
ערן שילר
מיוזג אוויר
אייל ארז מהנדסים ויועצים בע"מ
אינסטלציה
איתן אלמסי
חשמל
איתן בסיס
אלומיניום
נוף
נתי בלוקא
חשמל חכם
חימום תת רצפתי
איטום
צבי טל
אקוסטיקה
מעליות
קרקע וביסוס
דיה הנדסת קרקע וביסוס
ירשני

[illegible]

קרא קירות:

עמוד בסון קיר בסון קיר בלוק

אדריכלות

המזמין: _____

CLIENT NAME: _____

קבוצת רכישה נופיה

PROJECT NAME: הפרויקט:

נופיה - מגרש 15

חתיכים


SHEET NUMBER: A3-3-100

SCALE:	קנה מידה:	EDITION:	דפוס
1 : 50	סטטוס		
STATUS:	למבחן		
	בדק עיני:		דפוס עיני:
DATE:	22.09.25		יור

NeumanHaynerArchitects


ימן חיינר אדריכלים
רוד ההדרים 2, בית חירות
09-9545842

office@nh-arch.com
www.nh-arch.com

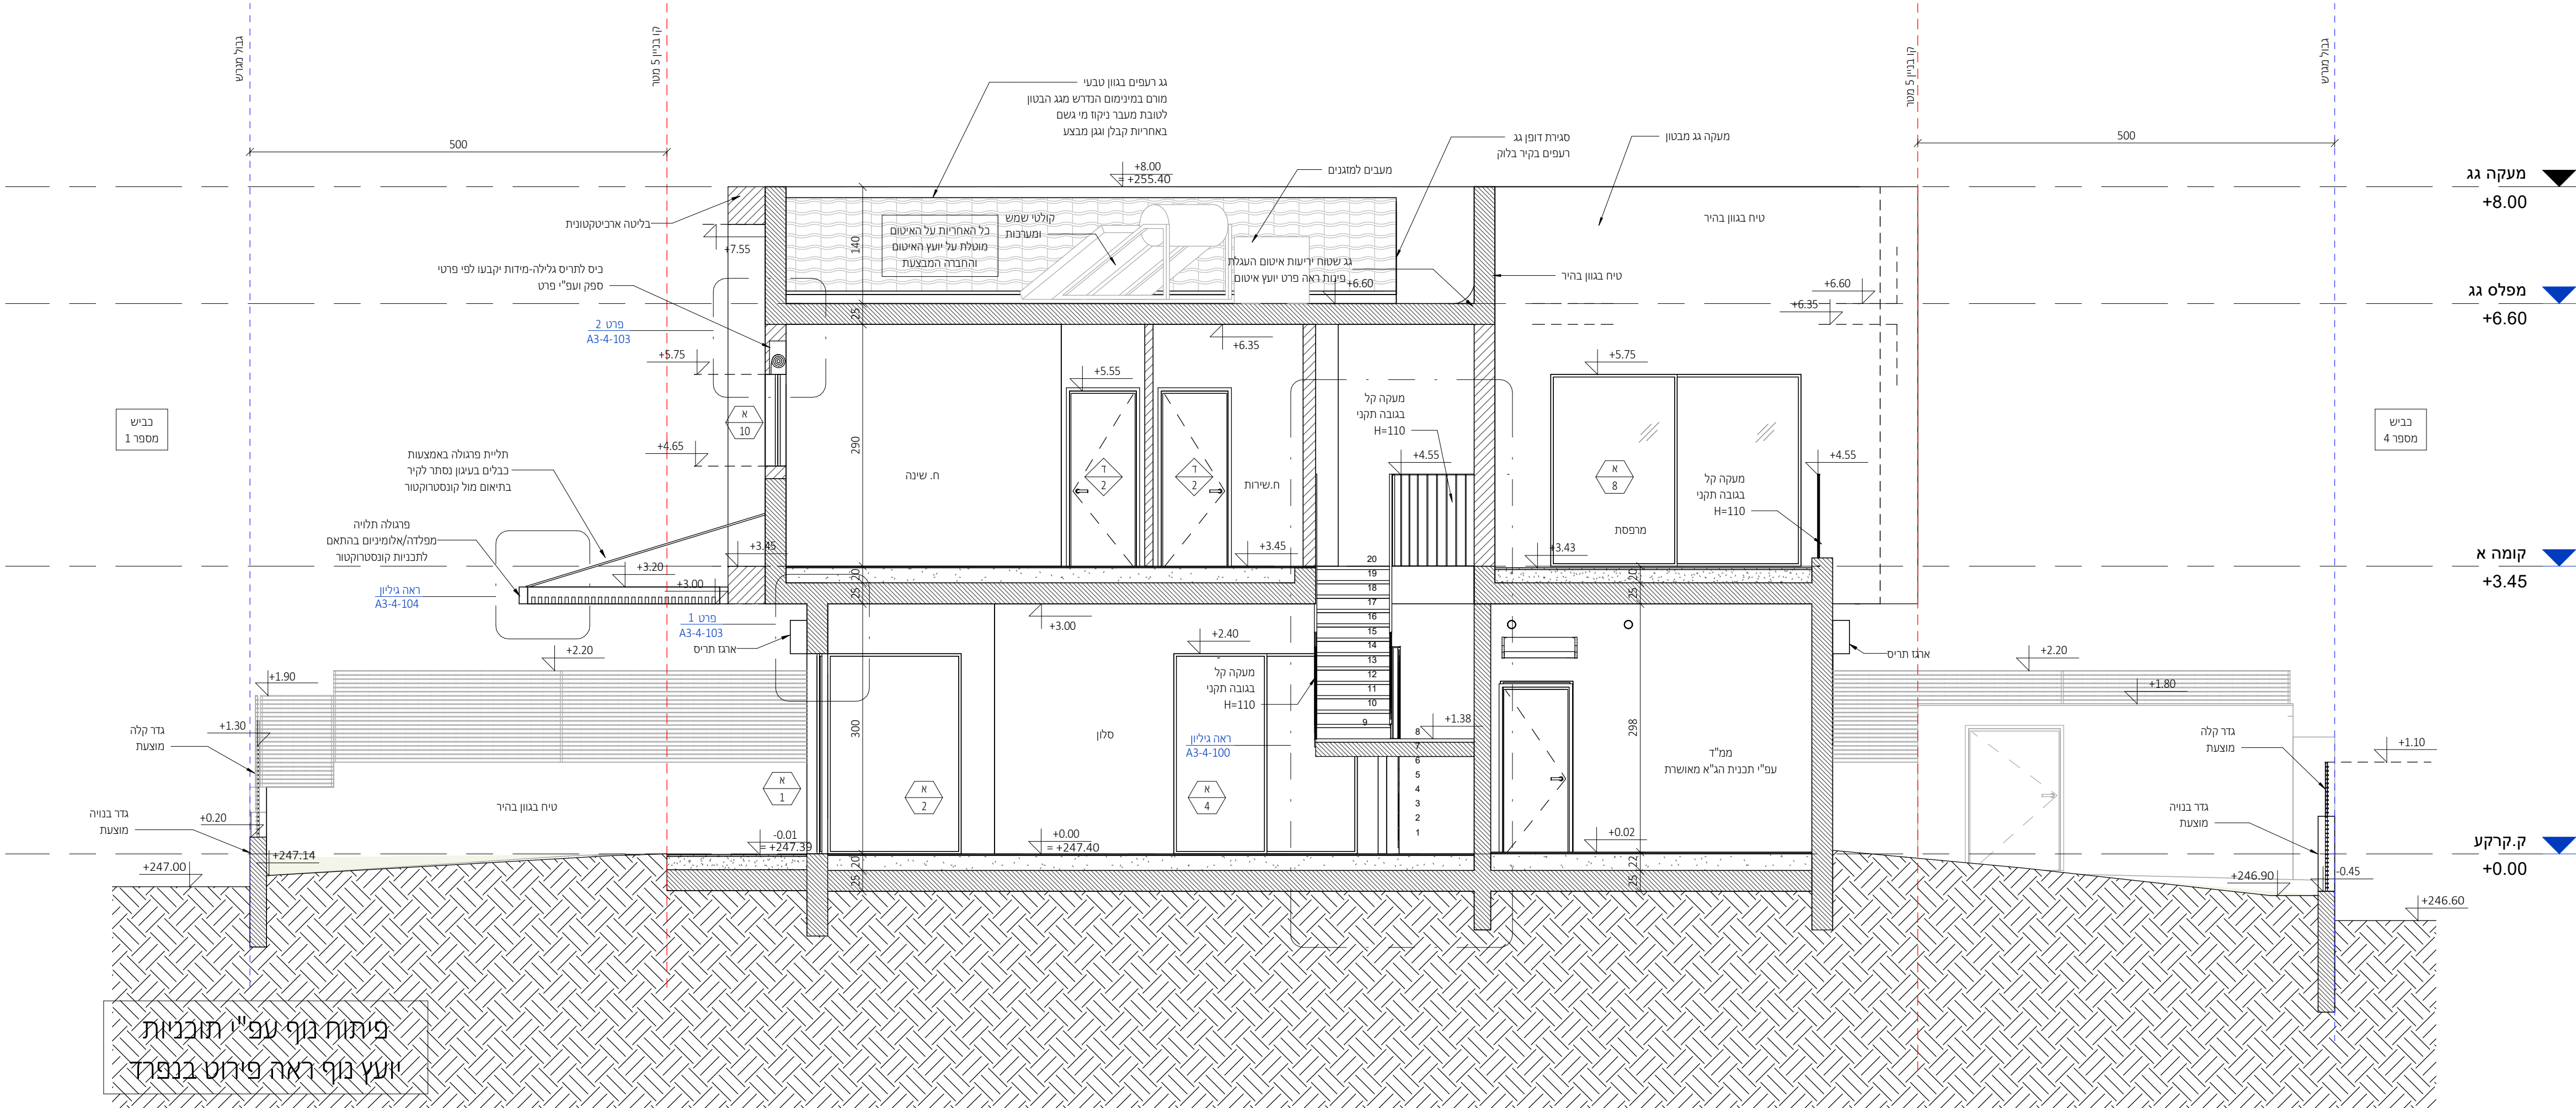

חתך א-א

1 : 50

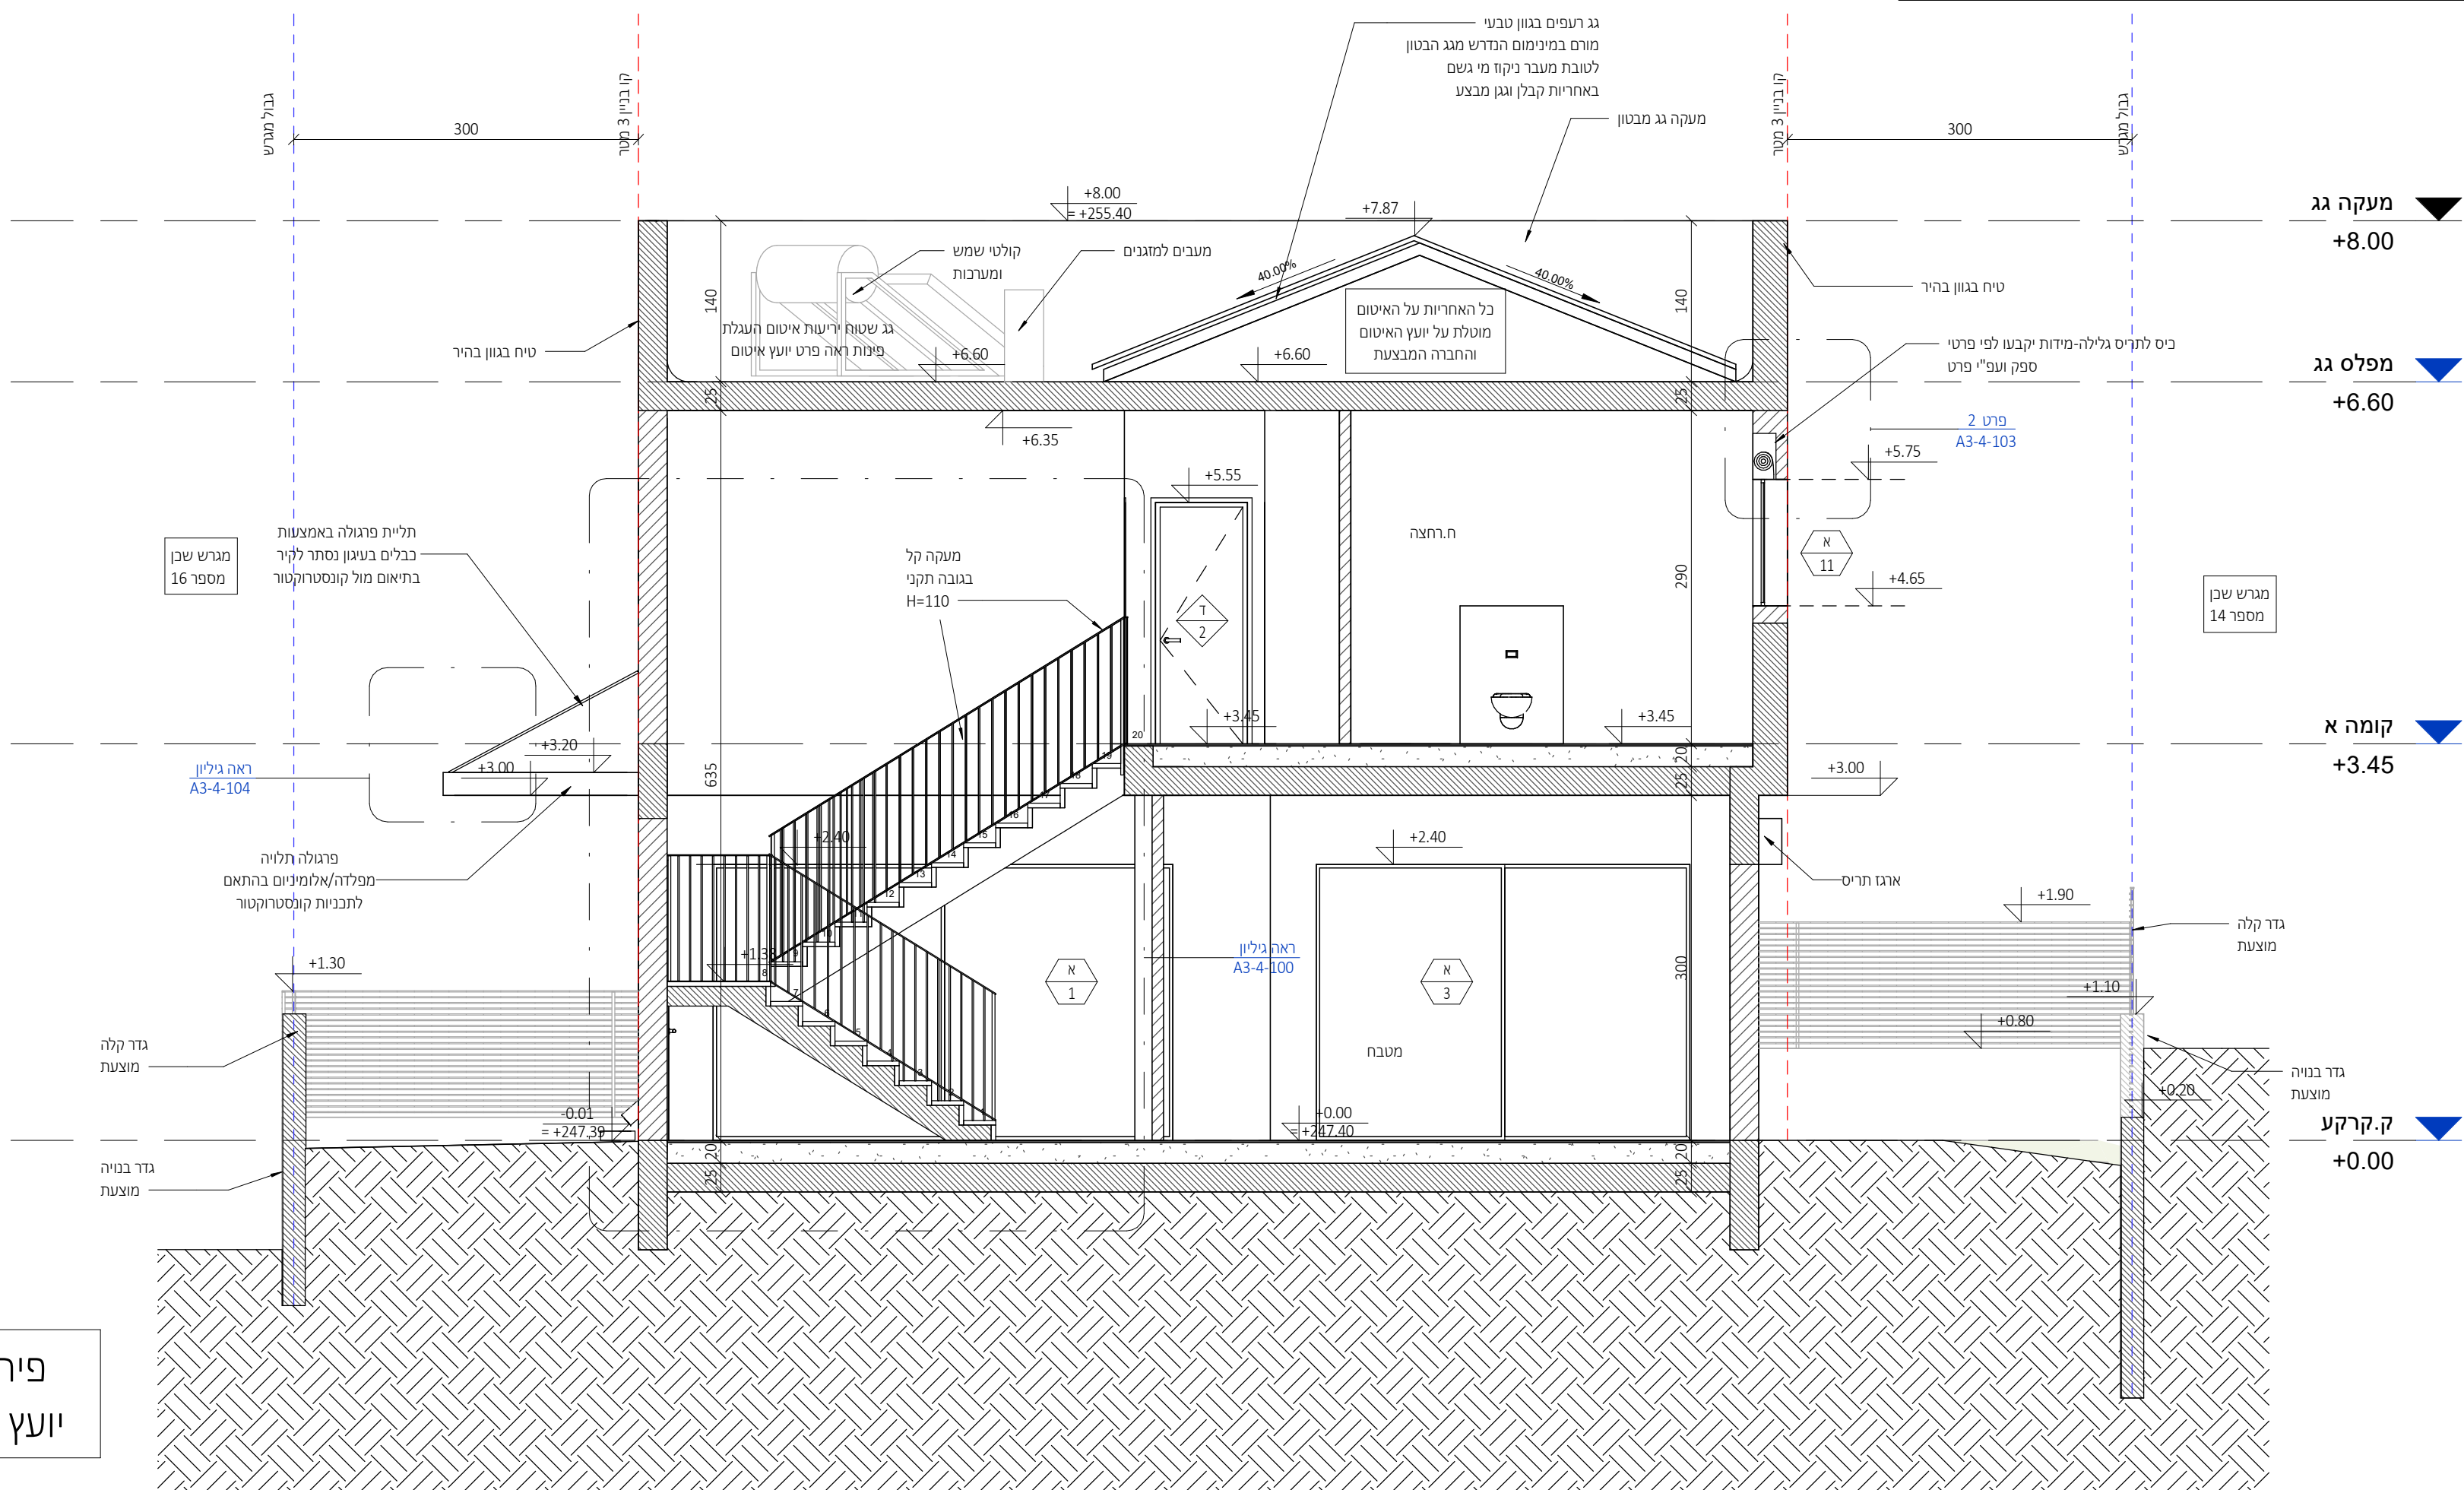

חתך ב-ב

1 : 50

פיתוח נוקף עפ"י תוכניות

ועץ נוף ראה פירוט בנפרד

ניהול פרויקט
מהיסוד - בן סולומון
פיקוח
מהיסוד - בן סולומון
קונסטרוקציה
ערן שילר
מיזוג אוויר
אייל ארז מהנדסים ויועצים בע"מ
אינסטלציה
איתן אלמסי
חשמל
איתן בסיס
אלומיניום
בופ
נתי בלוקא
חשמל חכם
חימום תת רצפתי
איטום
צבי טל
אקוסטיקה
מעלות
קרקע וביסוס
דיה הנדסת קרקע וביסוס
רישוי

$\pm 0.00 = +247.40$

מקרא קירות:

		
עמוד בסון	קיר בסון	קיר בלוק


[illegible]

CLIENT NAME:		ה' תשפ"ב	
PROJECT NAME:		ה' תשפ"ב	
קבוצת רכישה נופיה			
נופיה - מגרש 15			
DRAWING NAME:		ה' תשפ"ב	
גליון מדרגות			
SHEET NUMBER:		ה' תשפ"ב	
A3-4-100			
CALC:	עוד מידע:	EDITION:	ה' תשפ"ב
As indicated	סטוס		
TATUS:			
למכר	נבדק ע"י:	רשם ע"י:	
DATE:	22.09.25		ה' תשפ"ב


NeumanHaynerArchitects

וימן חיינר אדריכלים
 חורד ההדסים 2, בית חירות
 09-9545842 זל

office@nh-arch.com
 www.nh-arch.com

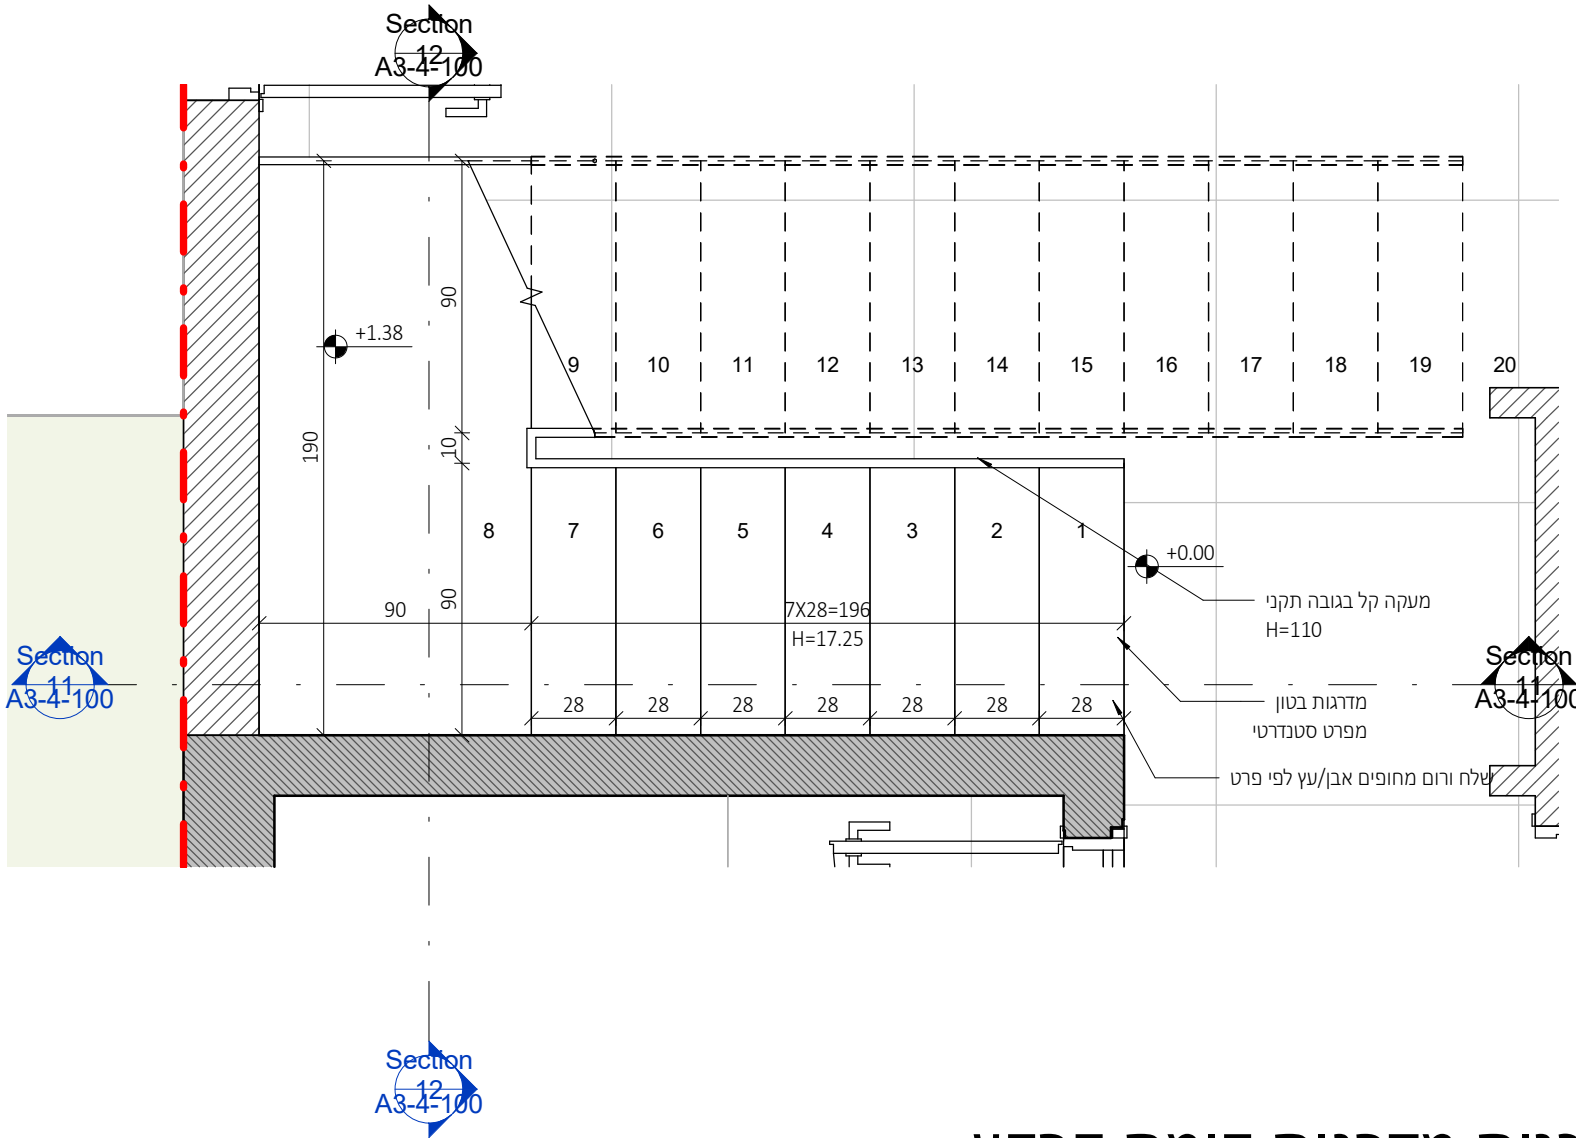


1 : 25

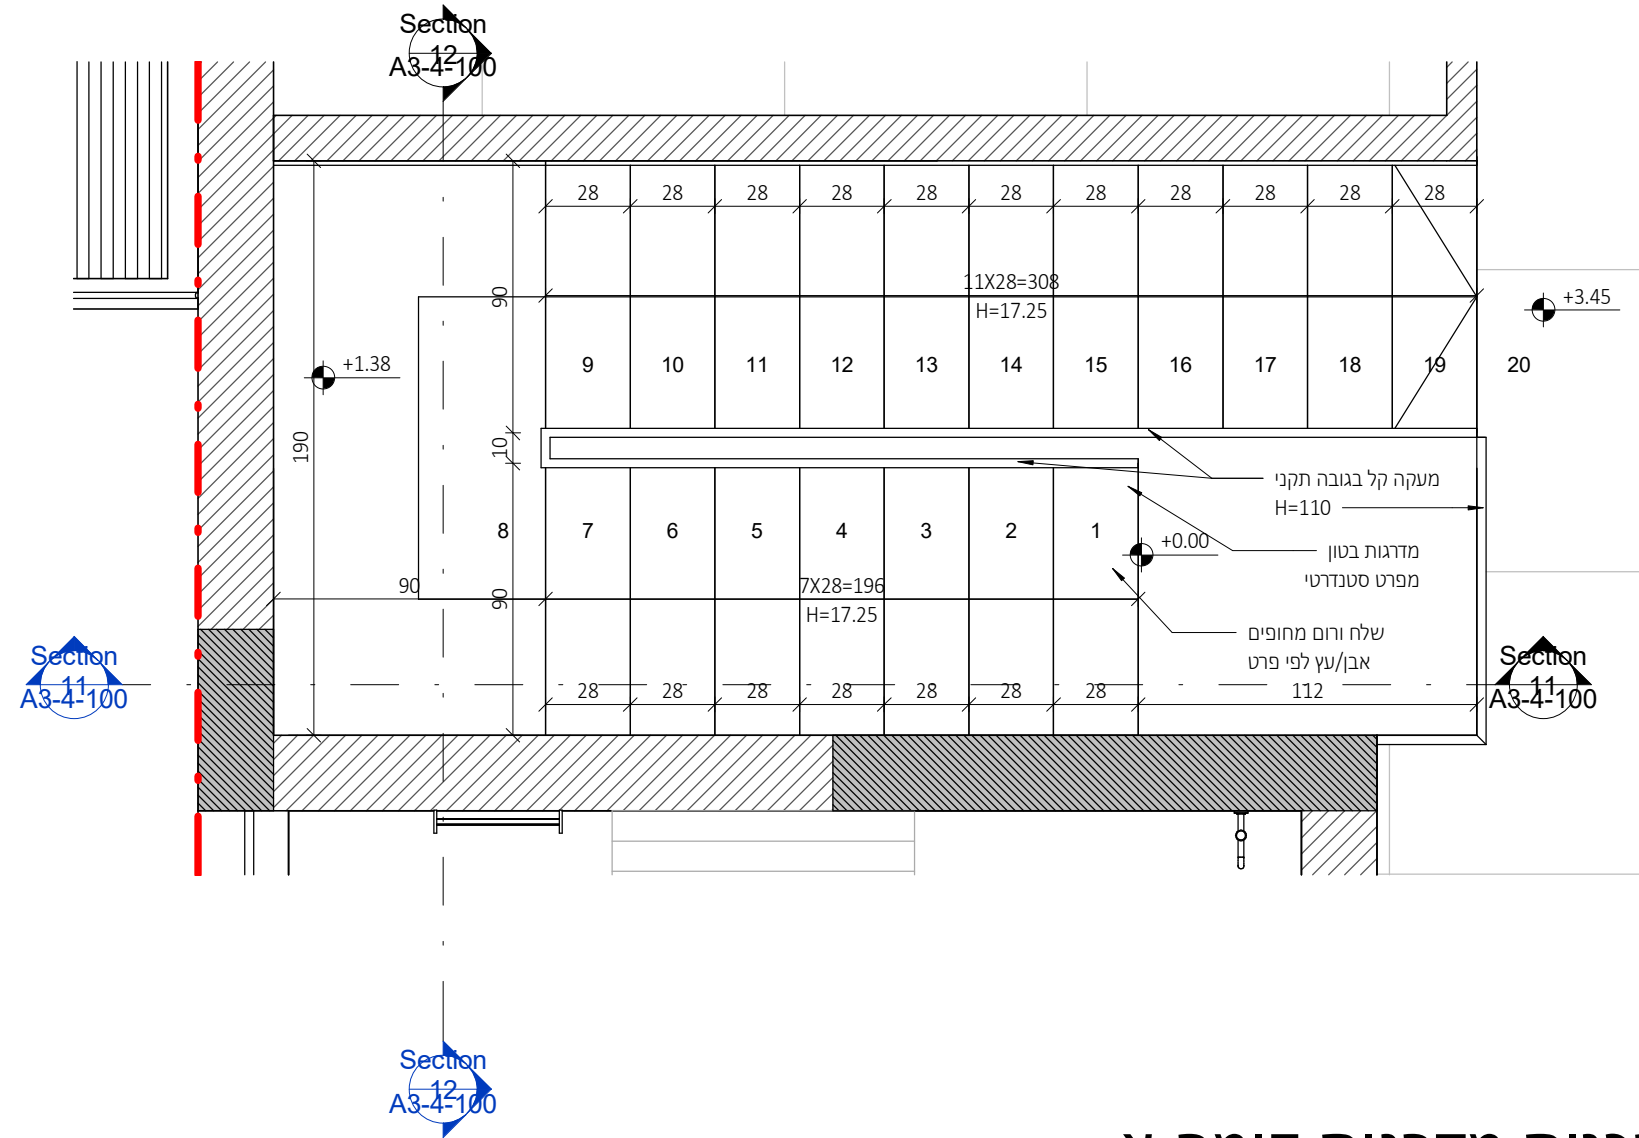


1 : 25




1 : 10

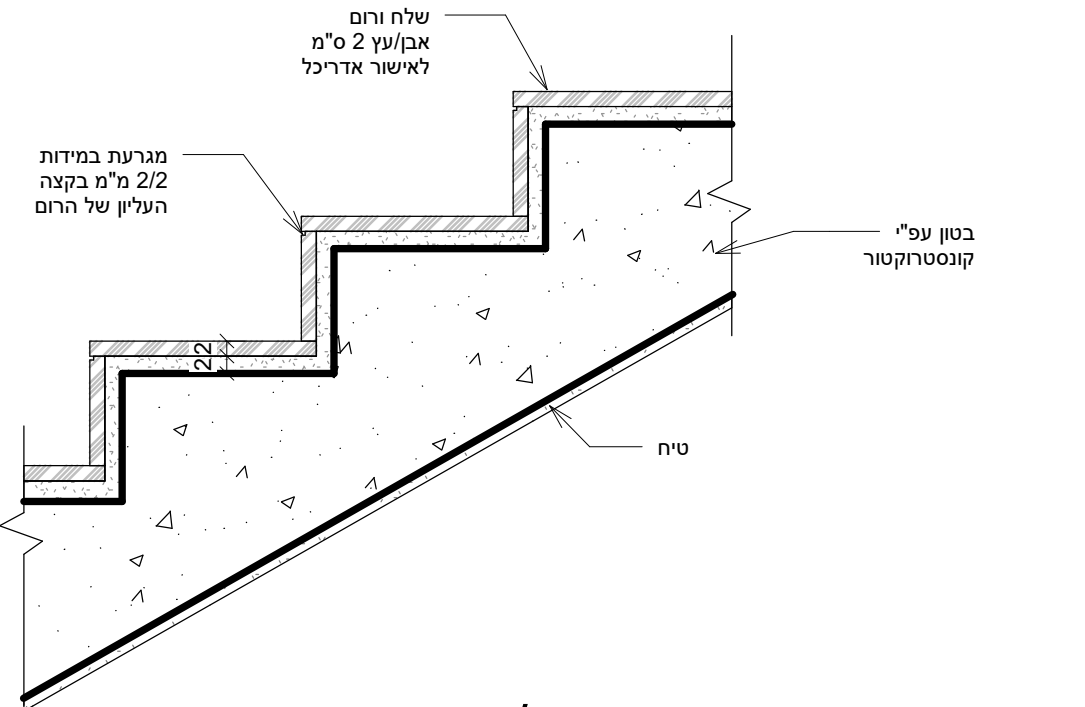


1 : 10

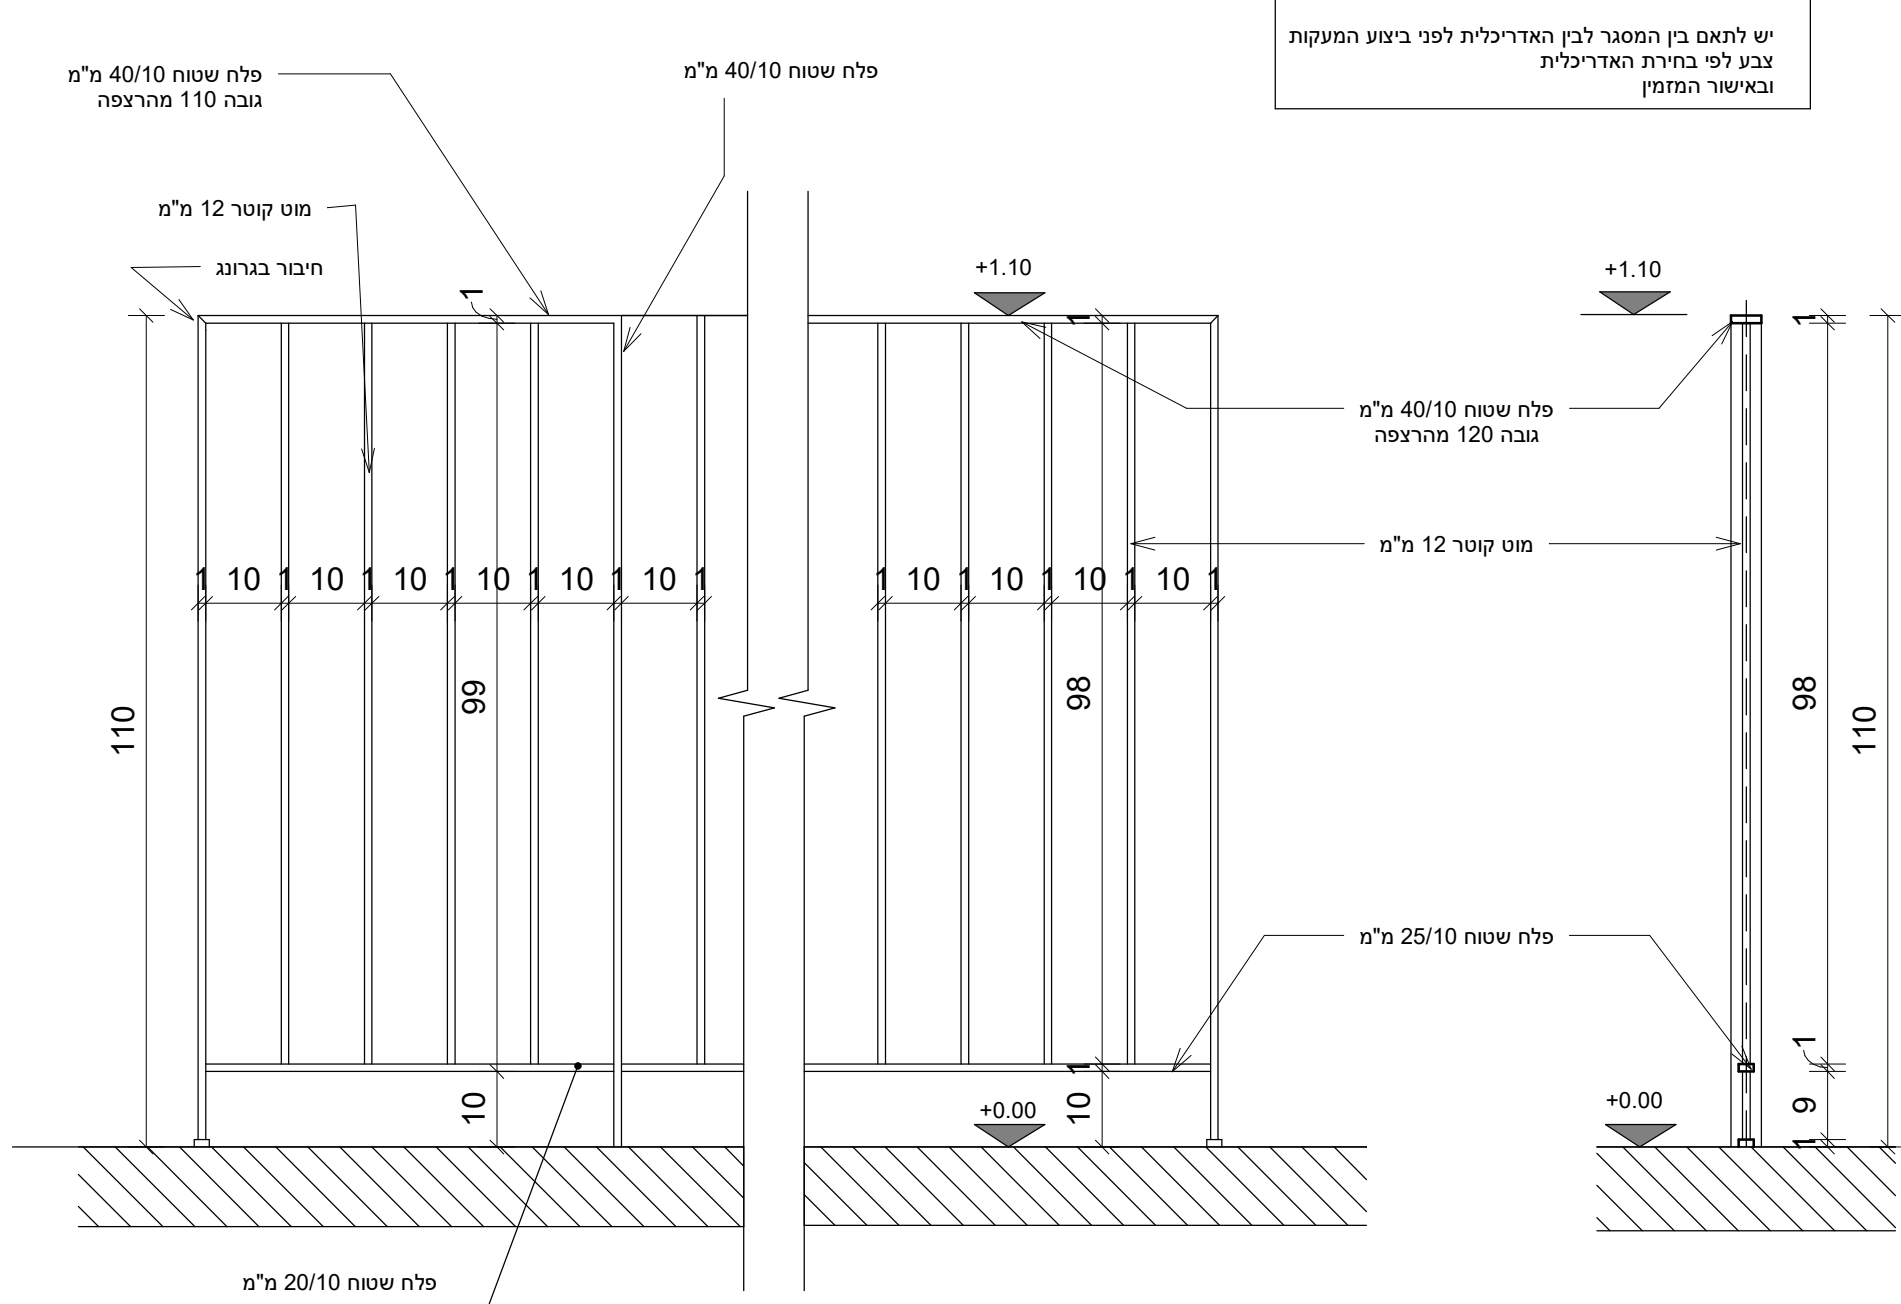


1 : 10

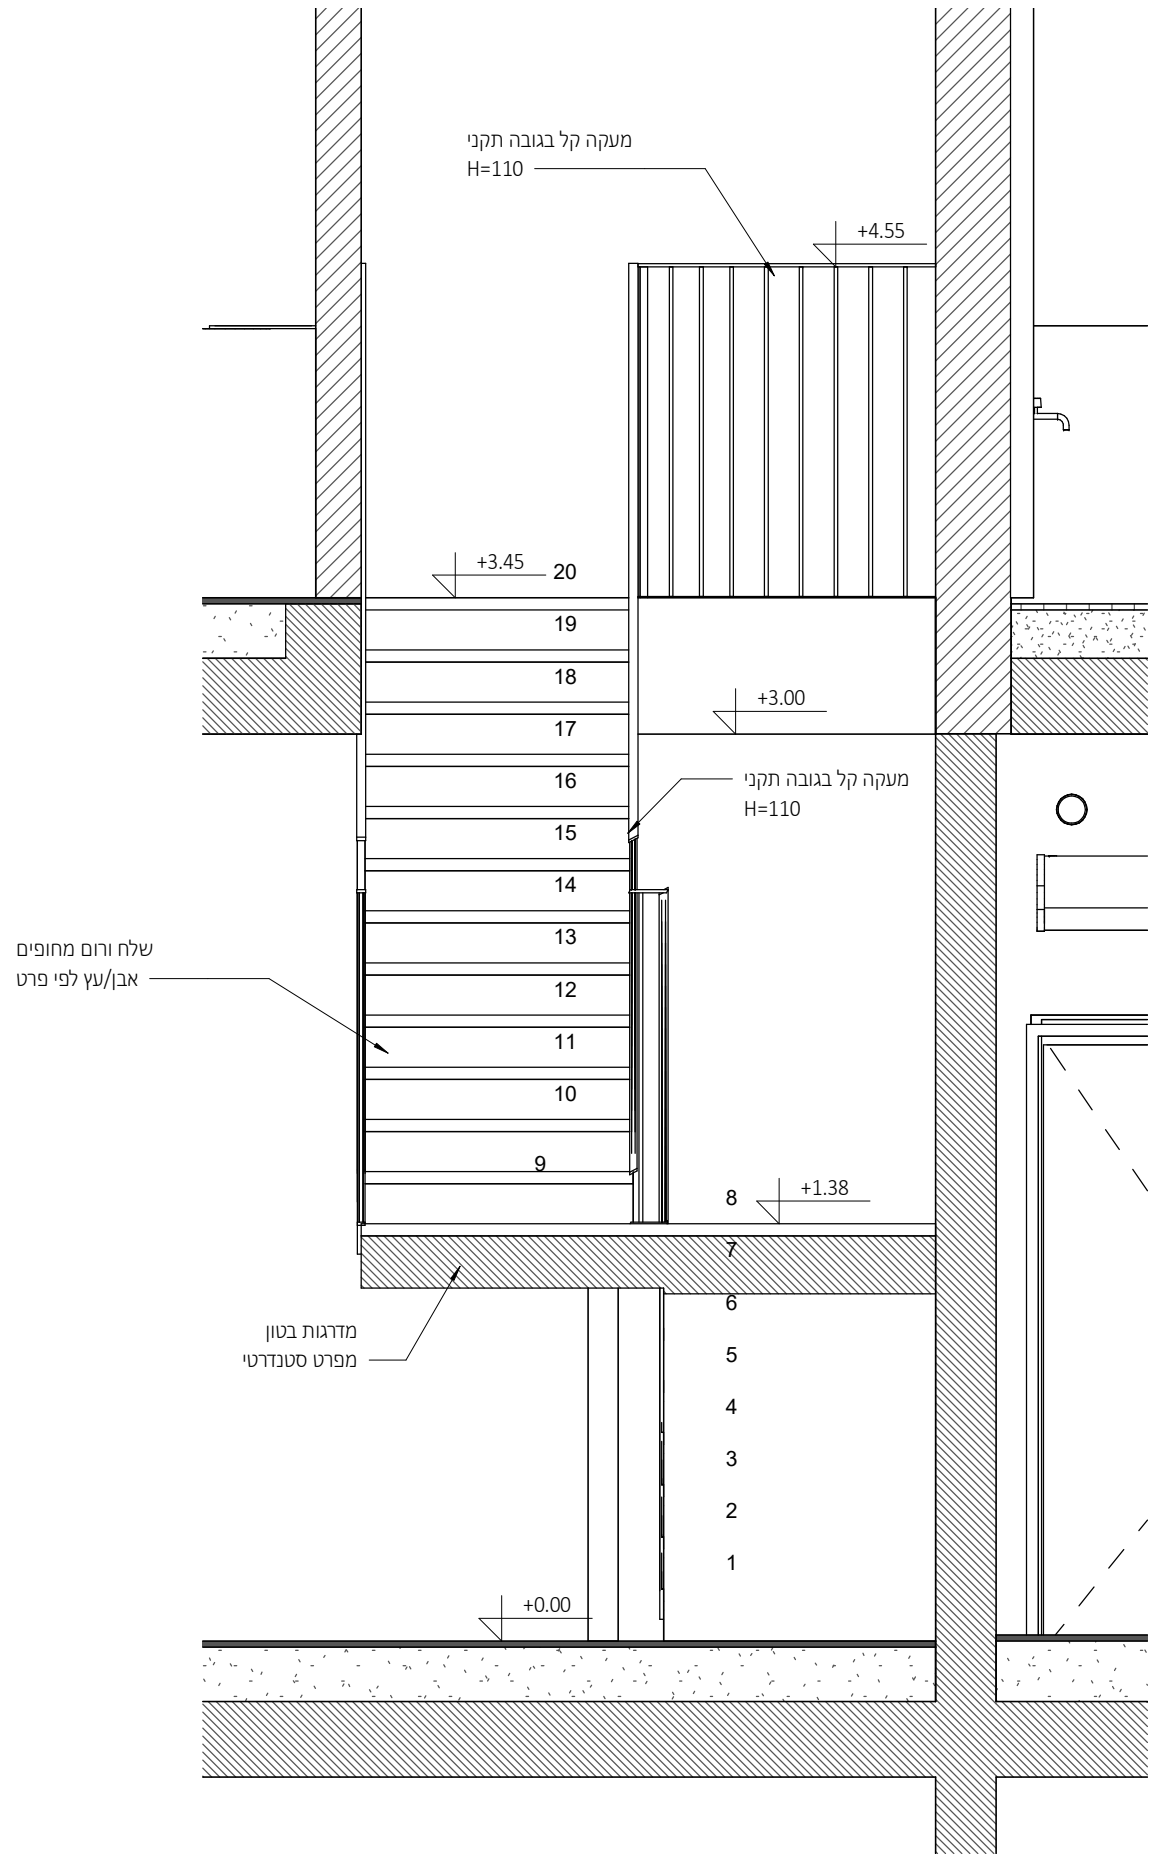

1 : 25

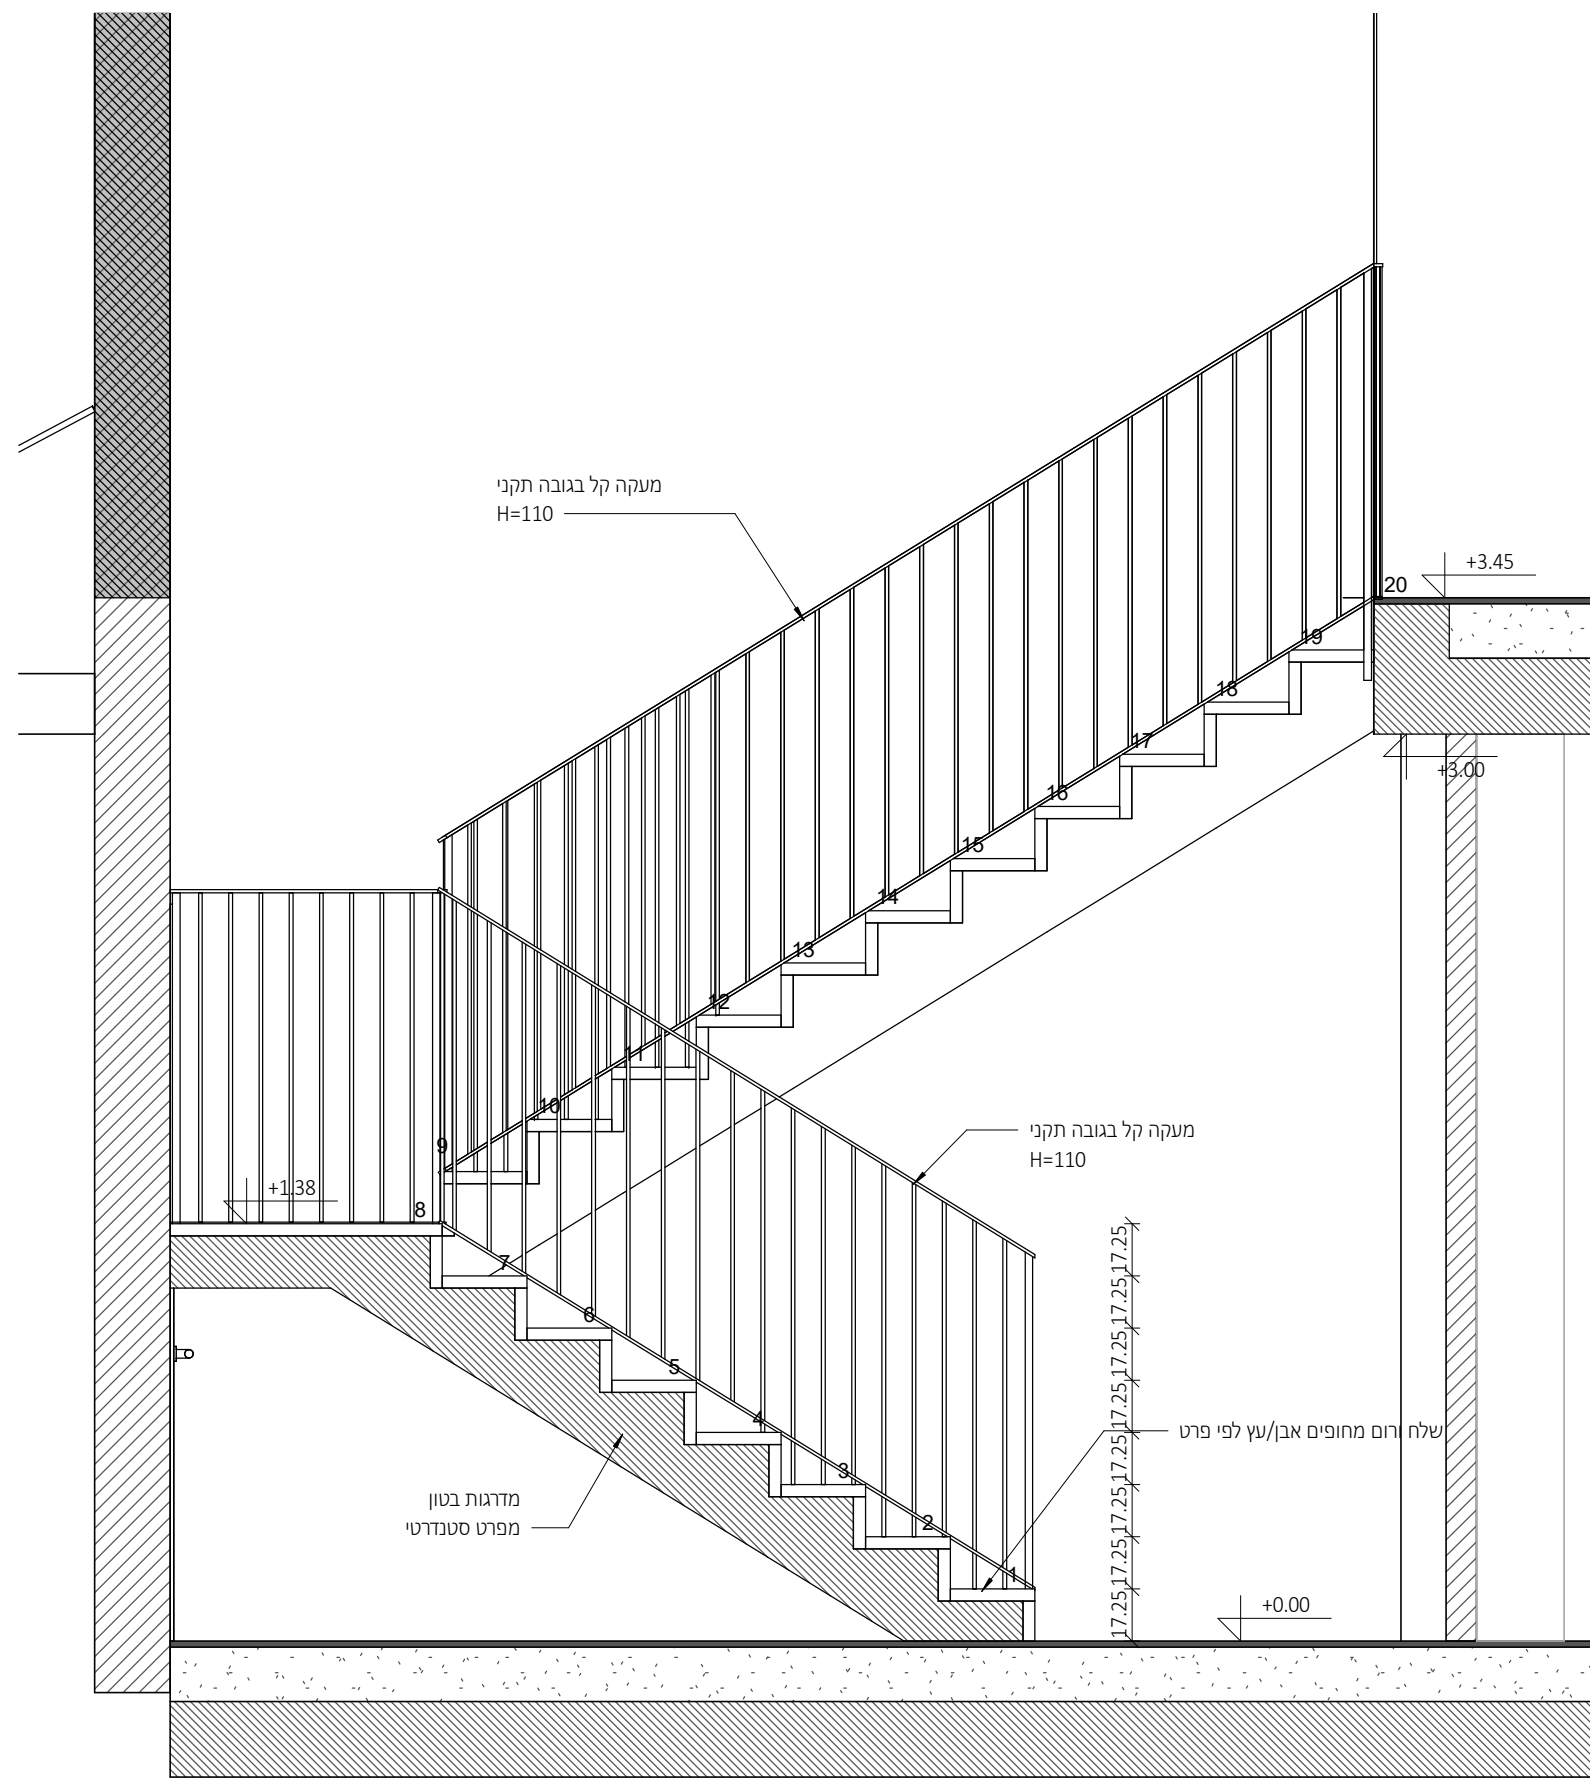

1 : 25

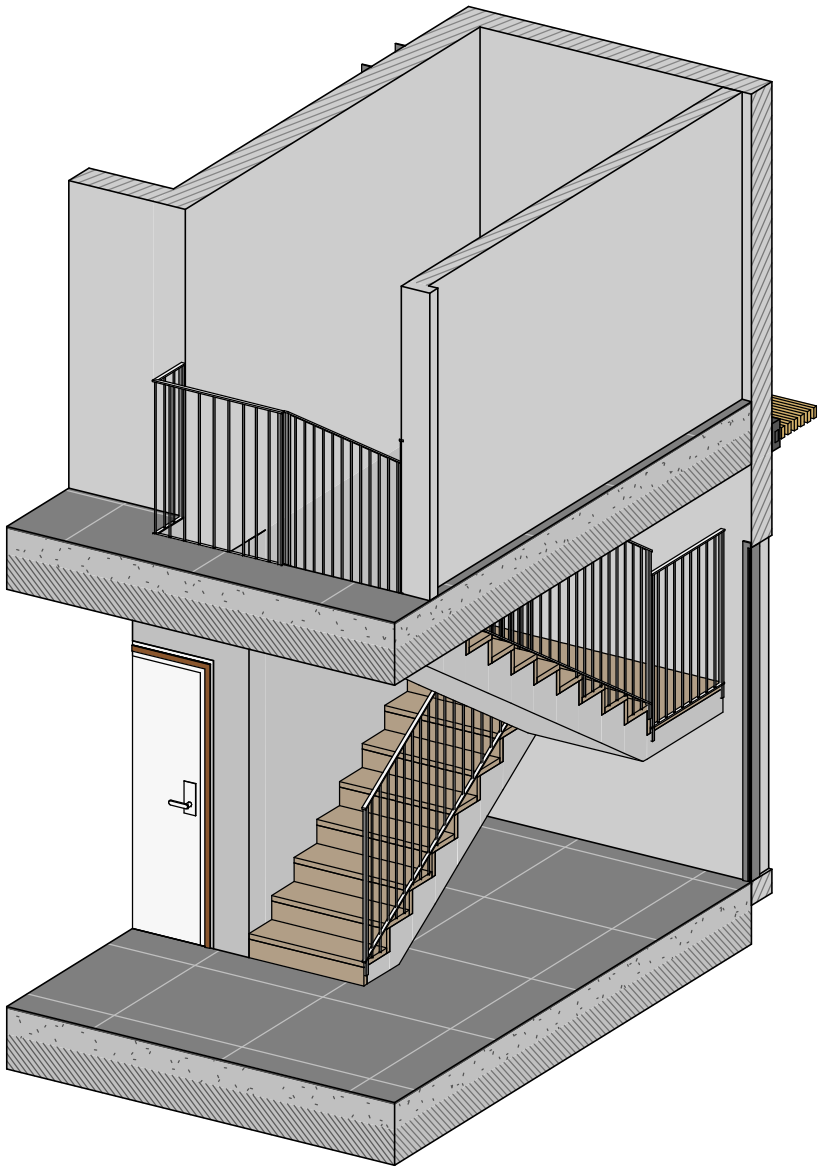

ניהול פרויקט
מהיסוד - בן סולומון
פיקוח
מהיסוד - בן סולומון
קונסטרוקציה
ערן שילר
מיזוג אוויר
אייל ארז מהנדסים ויועצים בע"מ
אינסטלציה
איתן אלמסי
חשמל
איתן בסיס
אלומיניום
בופ
נתי בלוקא
חשמל חכם
חימום תת רצפתי
איטום
צבי טל
אקוסטיקה
מעלות
קרקע וביסוס
דיה הנדסת קרקע וביסוס
רישוי

[illegible]

קיר בלוק קיר בטון עמוד בטון

[illegible]

CLIENT NAME: _____ שם המזמין:

PROJECT NAME: _____: שם הפרויקט:

RAWING NAME: ס הגליון:

HEET NUMBER: 197 גליון:

SCALE:	קנה מידה:	EDITION:	הדורה:
--------	-----------	----------	--------


As indicated	
STATUS: מסמס למכר נבדק ע"י:	
DATE: 22.09.25	דוסט ע"י: מ"ד:



NeumanHaynerArchitects


office@nh-arch.com
 www.nh-arch.com

זכויות ייצור / ע"פ הנחיות עו"ד

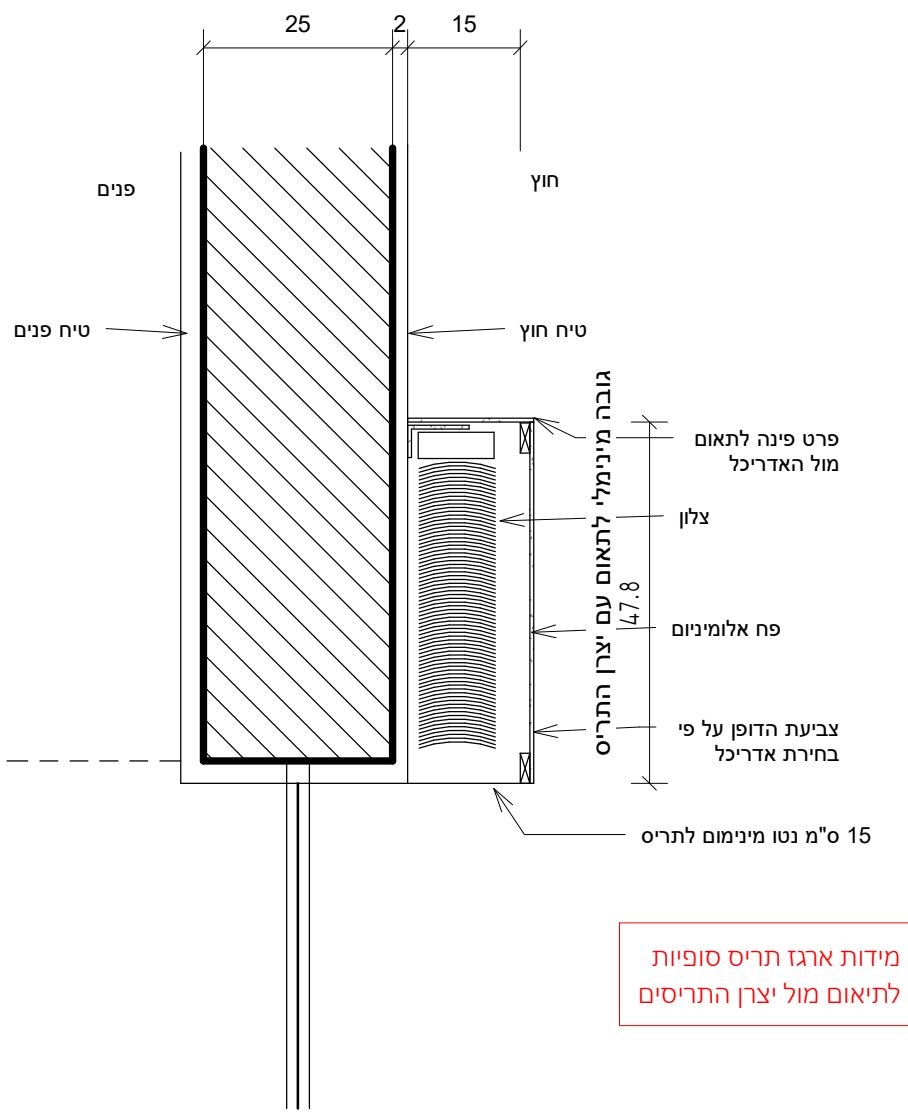

מידות ארגז תריס סופיות
לתיאום מול יצרן התריסים


1 : 10

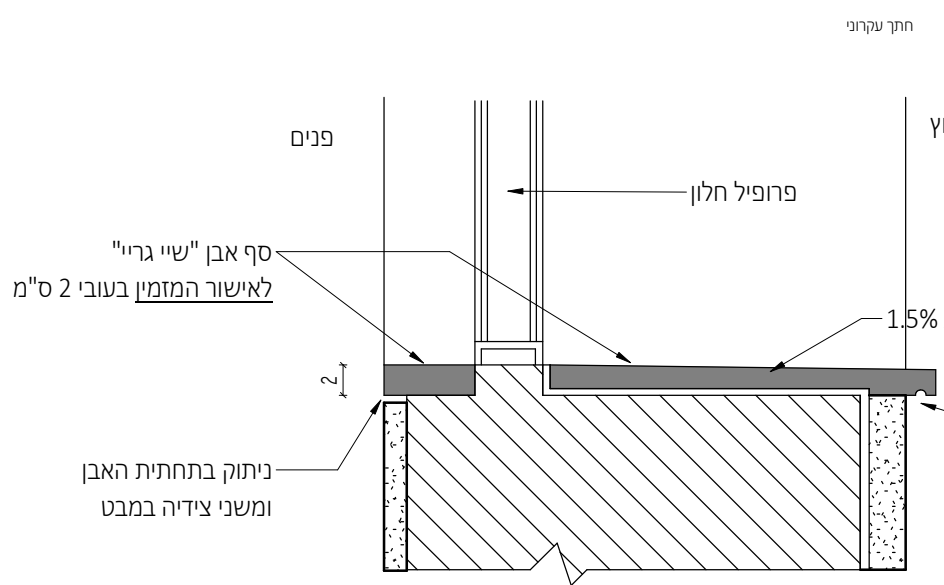

הערה : פרטי האיטום הם עקרוניים בלבד
כל האחריות על האיטום מוטלת על יועץ
האיטום החברה המבצעת
יש לעבוד לפי פרטי האיטום של יועץ הפרויקט.
גובה החלון המופיע בתכניות מציין את פני סף
האבן. יש להנמיך את הבטון בהתאם


פרט עקרוני בלבד - פרט סופי מספק החלונות

1 : 5

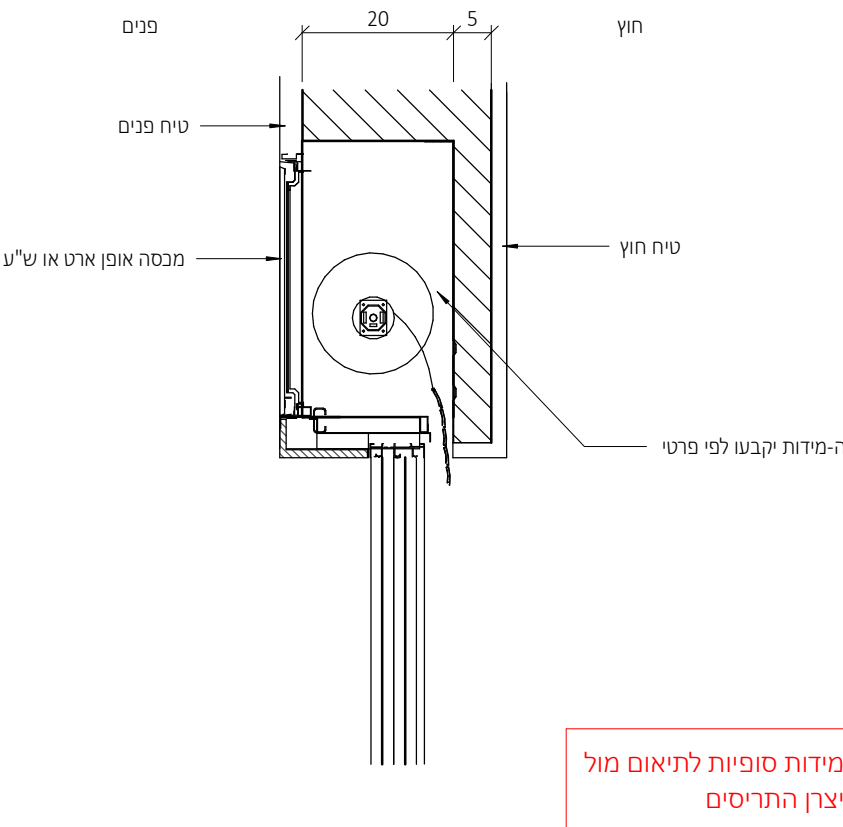


מדידות סופיות לתיאום מול
יצרן התריסים

1 : 10

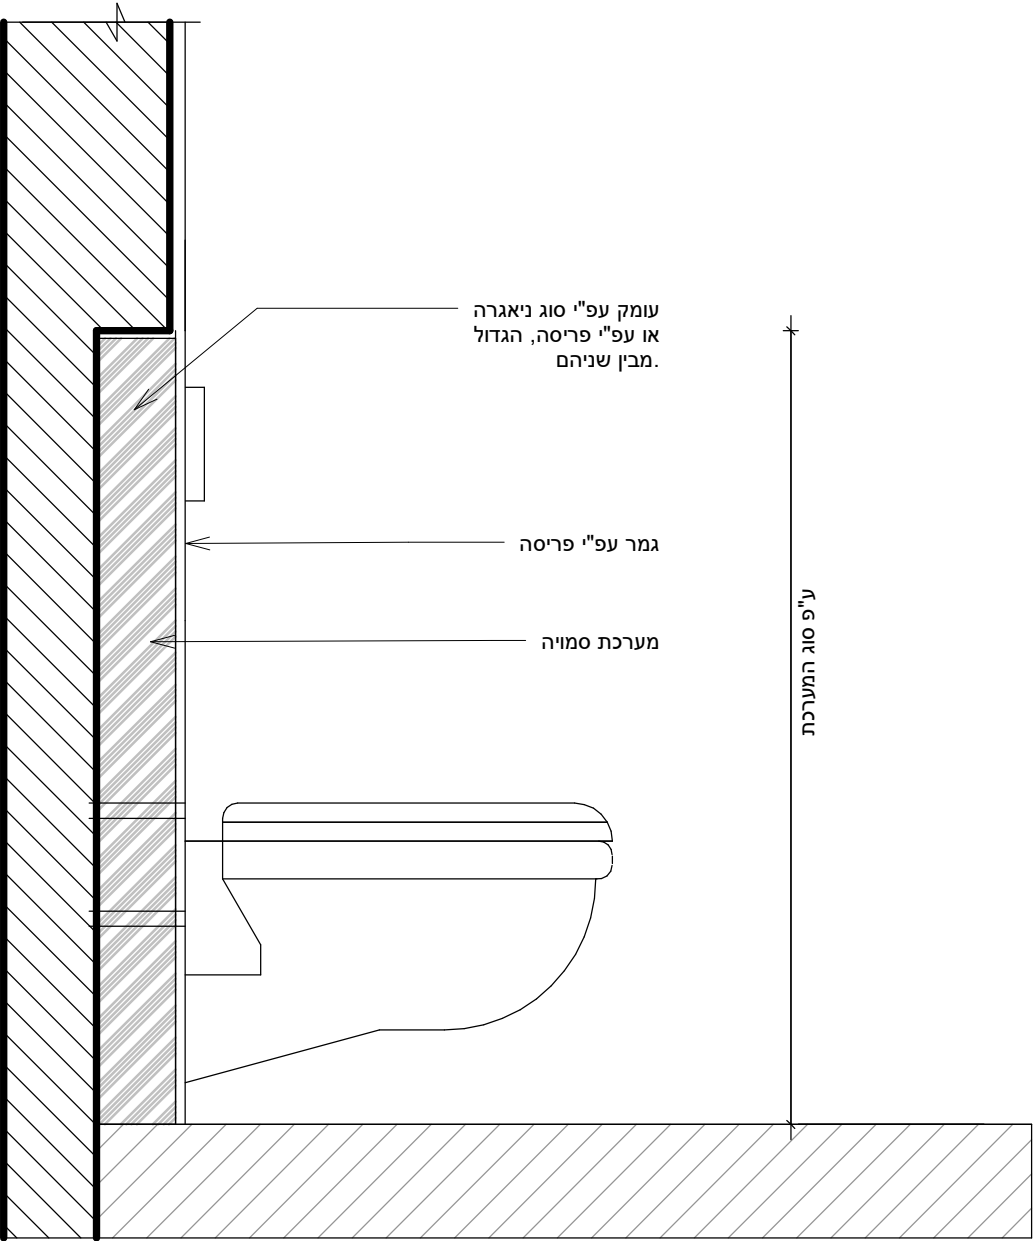


1 : 10

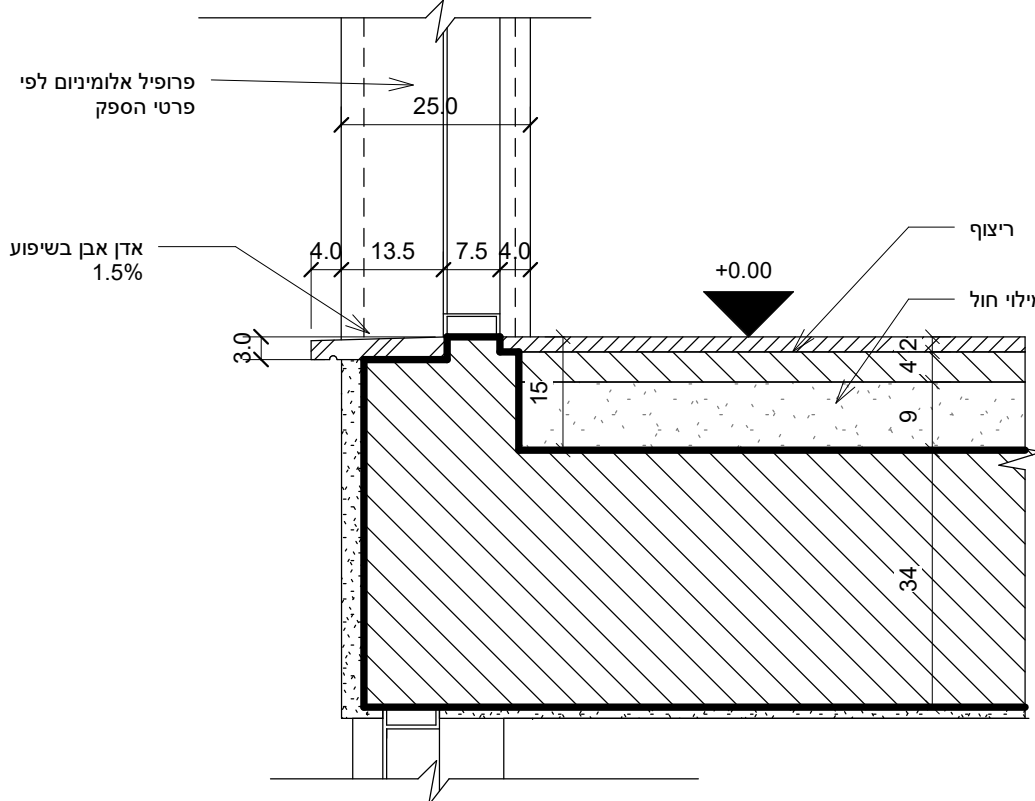

הערה : פרטי האיטום הם עקרוניים בלבד
כל האחריות על האיטום מוטלת על יועץ
האיטום החברה המבצעת
יש לעבוד לפי פרטי האיטום של יועץ הפרויקט.
גובה החלון המופיע בתכניות מציין את פני סף
האבן. יש להנמיך את הבטון בהתאם

פרט עקרוני בלבד - פרט סופי מספק החלונות

1 : 10

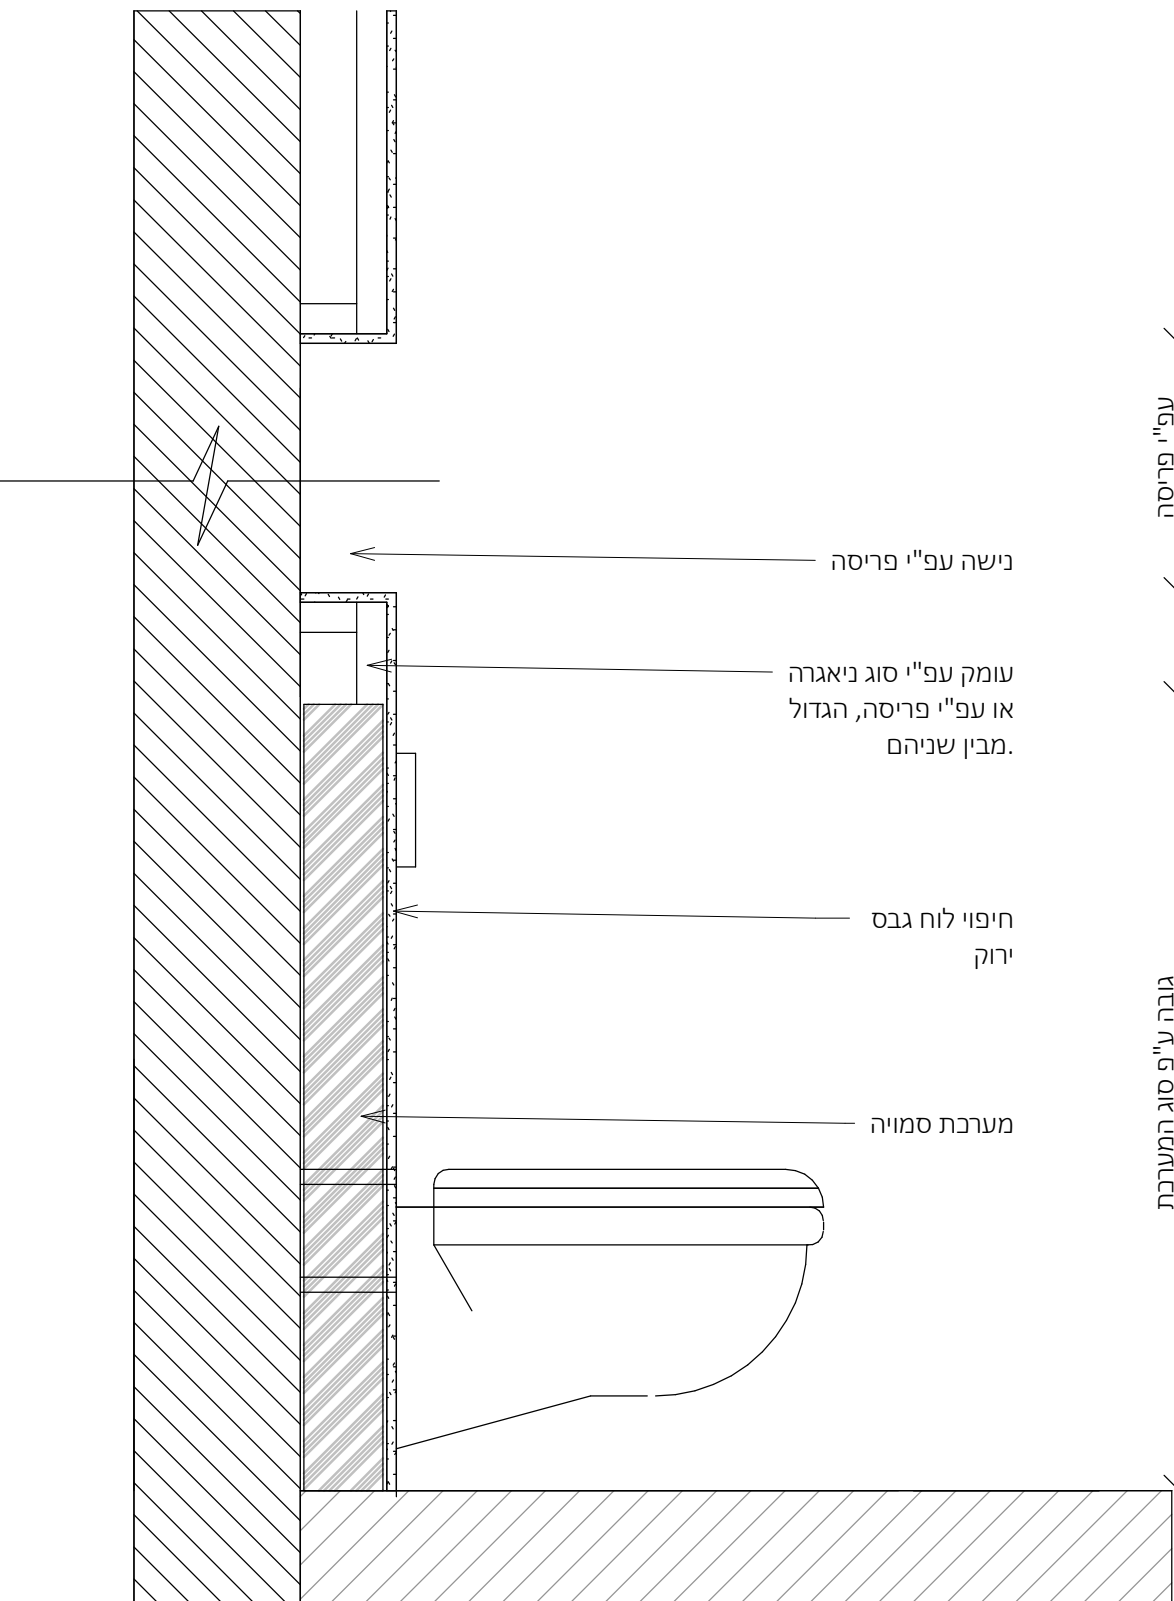

1 : 10

יש לעבוד במקביל לפרטים שיספק
מעצב הפנים (במידה וקיים במגרש זה)
המאושרות על ידי האדריכל.

פרטי האיטום באחריות יועץ האיטום
ראה חוברת פרטי איטום מצורפת


להמשך תיאום

פרגולת אלומיניום




תמונה להמחשה בלבד

להמשך תיאום

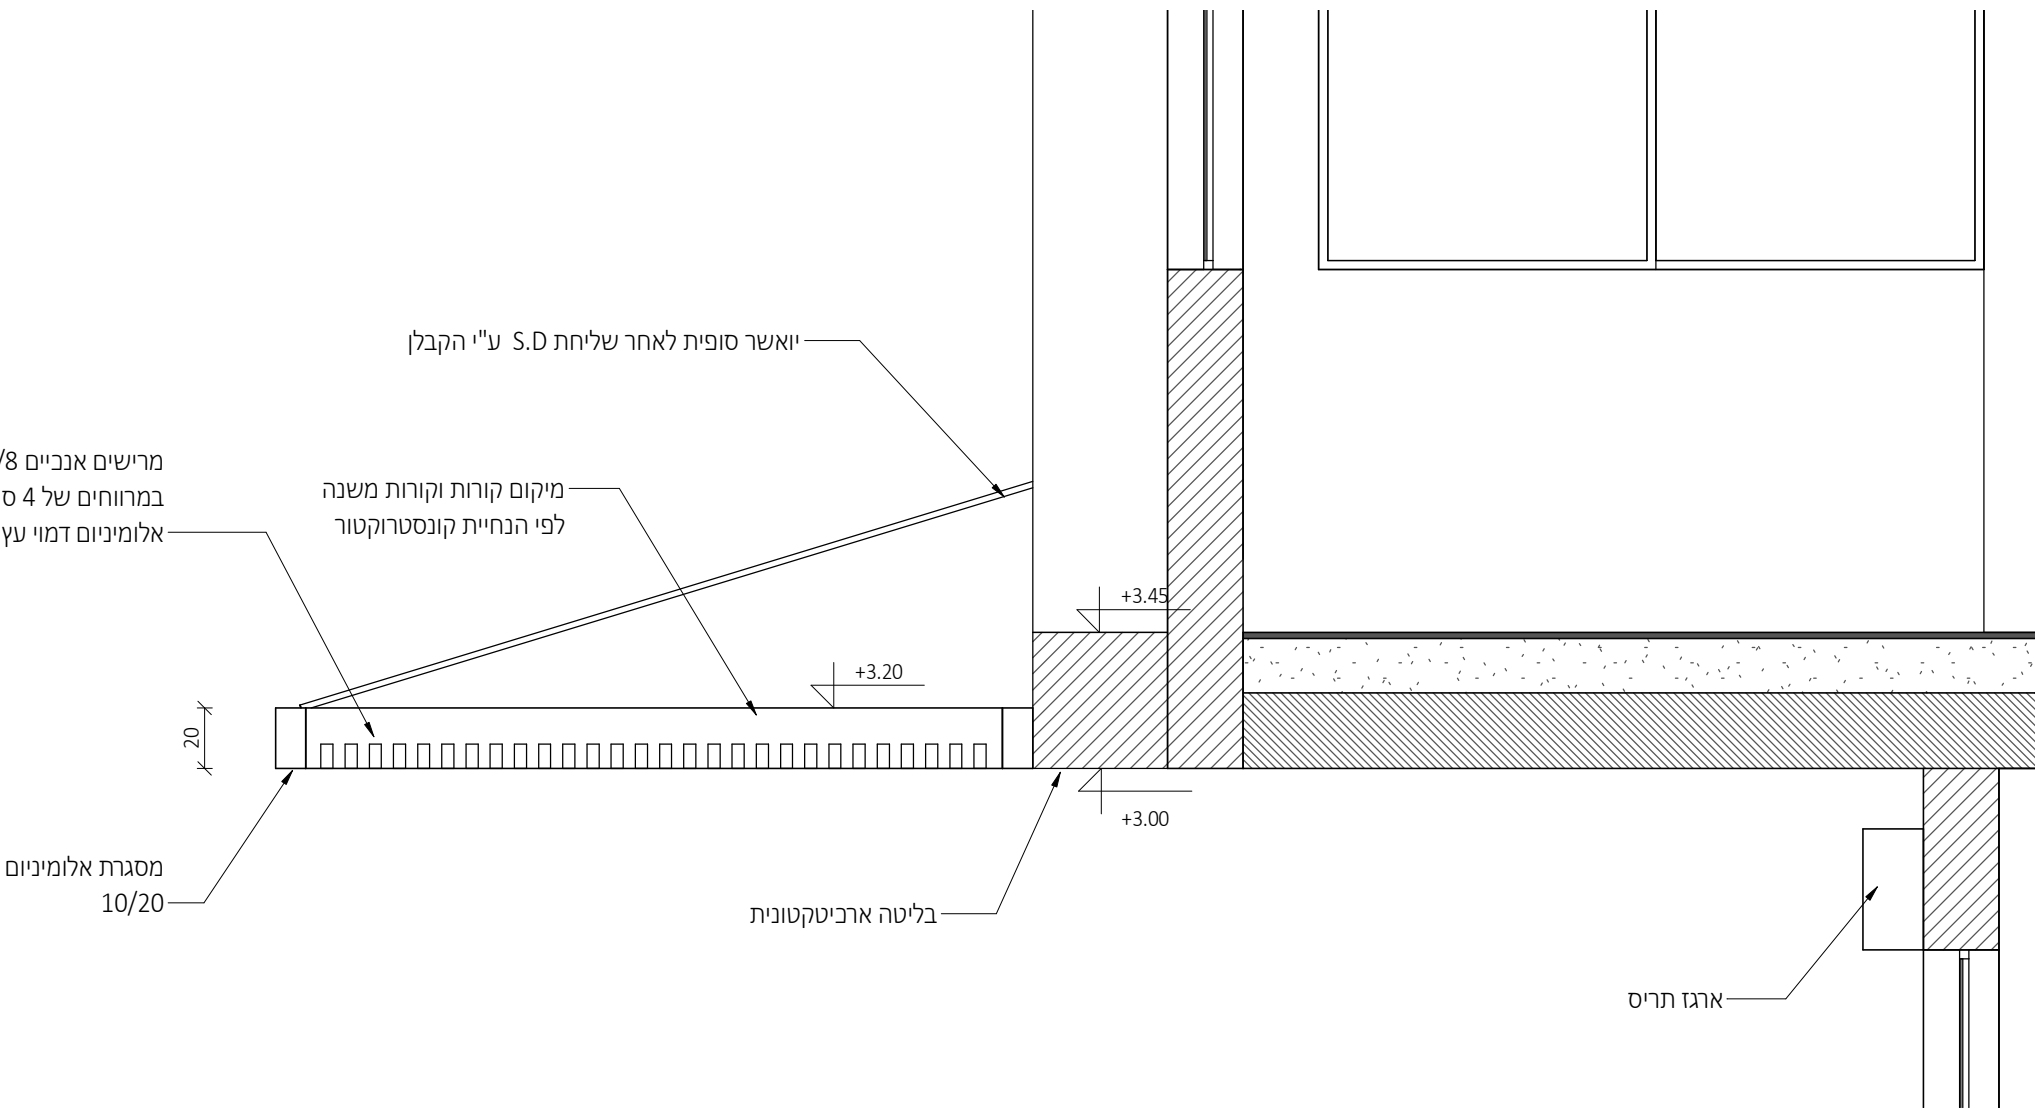


Section 13

1 : 25

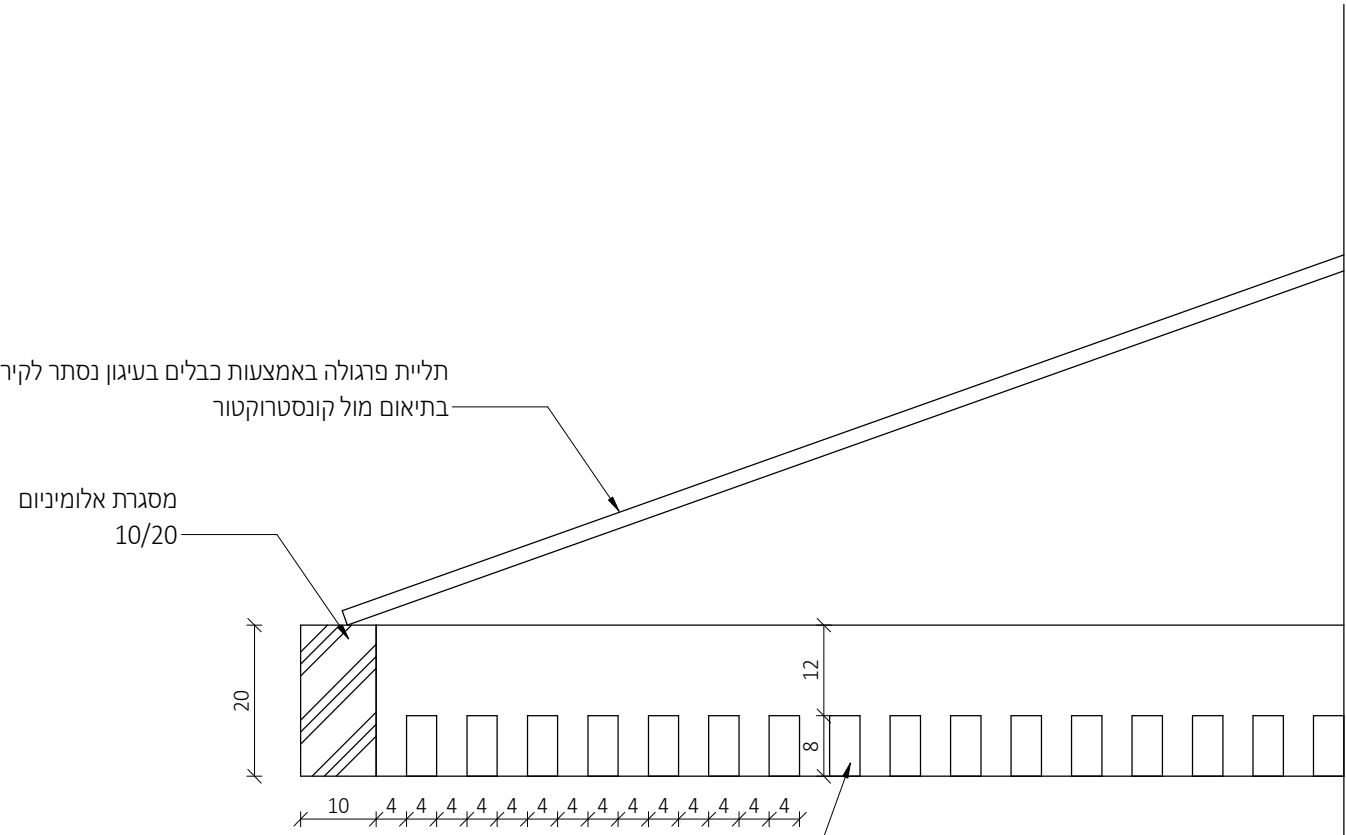

פרגולה - חתך רוחב

1 : 10

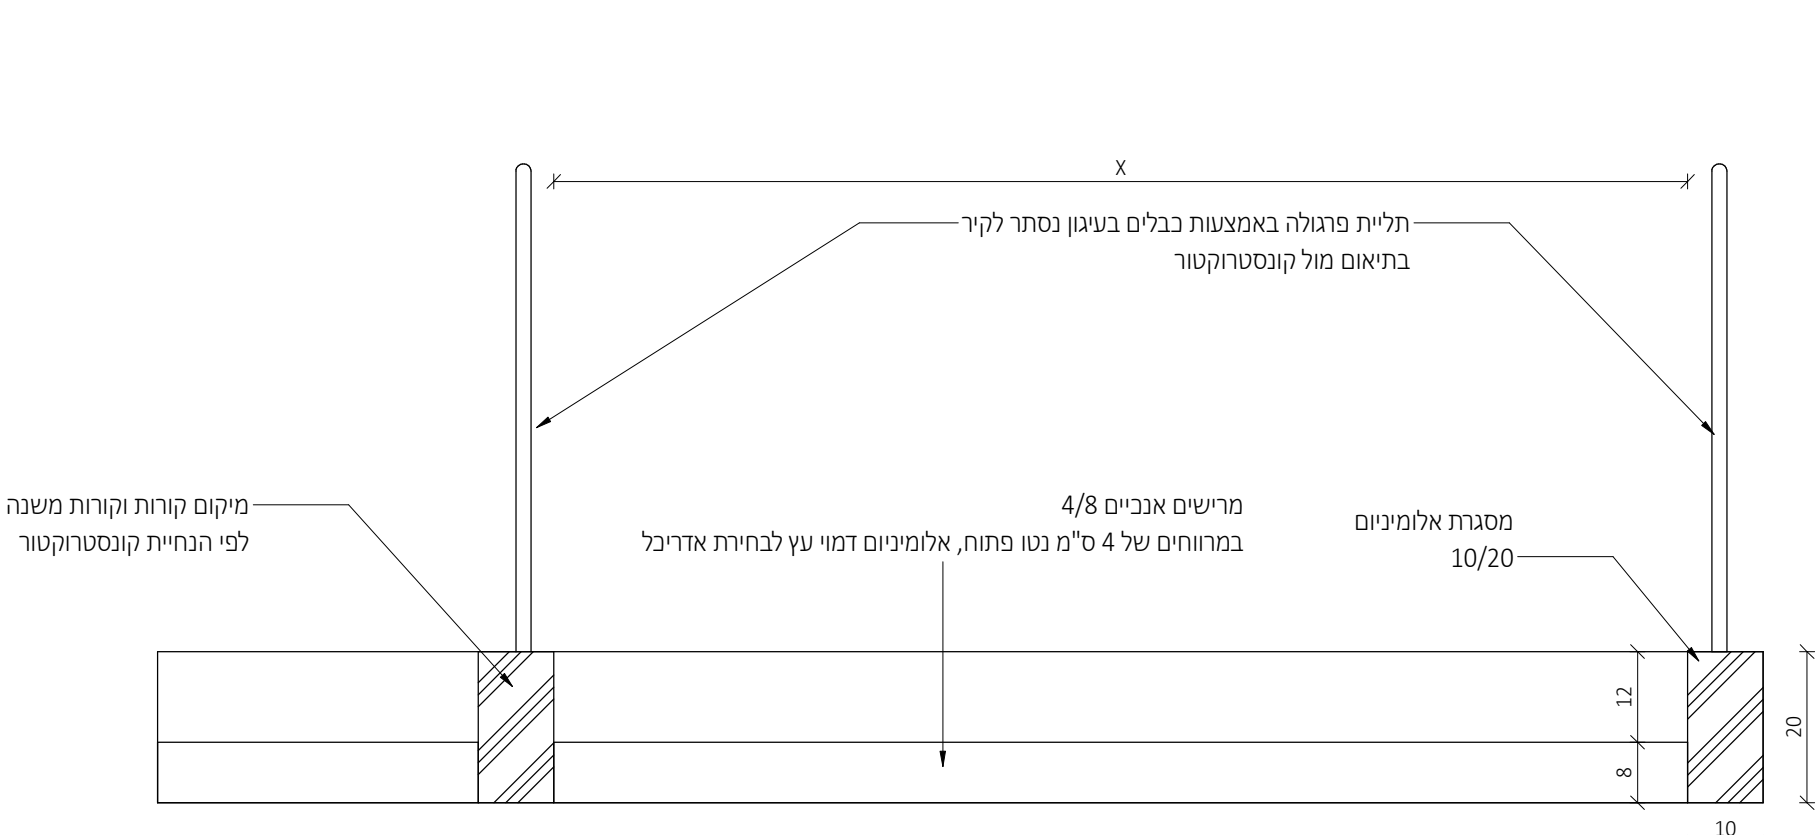


פרגולה - חתך אורך

1 : 10

ניהול פרויקט
מהיסוד - בן סולומון
פיקוח
מהיסוד - בן סולומון
קונסטרוקציה
ערן שילר
מיזוג אוויר
אייל ארז מהנדסים ויועצים בע"מ
אינסטלציה
איתן אלמסי
חשמל
איתן בסיס
אלומיניום
נוף
נתי בלוקא
חשמל חכם
חימום תת רצפתי
איטום
צבי טל
אקוסטיקה
מעליות
קרקע וביסוס
דיה הנדסת קרקע וביסוס
רישוי

± 0.00 = +247.40
הערות: 1. תכנית זו אינה לקרא יחד עם תכנית הרישוי. 2. גובה אבטומיניום: ראו תכנית פיתוח. 3. המידות הן בין קירות הבניה ולא כולל פיתוח. 4. פיתוח השטח סביב הבניה, כולל, מדרגות, גדרות, שבילים, ריצופים, שטחים בגנים, חניה גינה ואף תכנית פיתוח. 5. איסוס קירות והצפת הבניה כמעט עם הקרקע ובנידוד תחסי לאורך העמודים והקורות וכל התקנות. כלירות או עם סימני (גטון). ראו תכנית קונסטרוקציה. 6. אף דים יבוצע בכל מישור אופקי הבולם מהגבון. 7. סוף תחסי במס"ד- ע"פ מפרס תומקור. מאושר ט"י פיקוד העורף. המבצע אחראי לסידור: : עליו לבקר ולבדוק את כל המידות בתכנית ובמקום המבניה. במס"ד של מידות או אי התאמה בתכנית /או בבנין, עליו להודיע על כך מיד לאדריכל בסופו המשיך בעבודתו. המבצע ישתמש או ויקי בתכנית שאושר לכניסו. המבצע יחזיק באחר, בכל מה, של מידות של תכנית. את לקבוע מידות על ידי מדידה בשטח. התכנית היתה רכוש האדריכל ואין לשנות כל שימוש בה או ברעיונות הגלומים בה, אלא באישור בכתב מהאדריכל. מחדס /או יושע אשר שמו רשום בתכנית זו, נושא לכיד באחריות המקצועית והתקנית לתכנית. על המפקח והמבצע לודא התאמת התכנית האדריכלית "לכניסו" לתכנית הינה, המכר והתכנית המאושרות ע"י כל גורמים הרשמיים. התכנית כוללת את כל האמצעים והידוע עד ליום תחלתה.

משרד קירות:

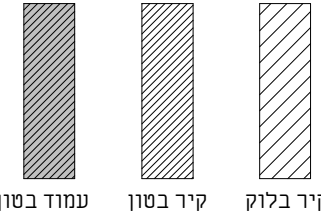

תאריך	תיאור	מהדורה
22.09.2025	מכרז	1

אדריכלות

שם המסמך:	CLIENT NAME:
קבוצת רכישה נופיה	
שם הפרויקט:	PROJECT NAME:
נופיה - מגרש 15	
שם הגיליון:	DRAWING NAME:
פרטי פרגולה	
מספר גיליון:	SHEET NUMBER:
A3-4-104	
תאריך:	EDITION:
תאריך:	SCALE:
תאריך:	STATUS:
תאריך:	DATE:
תאריך:	DATE:

NeumanHaynerArchitects

נוימן חיינר אדריכלים
מחלל התדורים 2, בית חירות
99-9545642 78
www.nh-arch.com
office@nh-arch.com

09/11/2025 8:55:39

זכויות יימור / ע"פ הנחיות ע"ד

רשימת חלונות					
סוג	תיאור	כמות	גובה	רוחב	מס פריט

קרקע

1	400	240	1	צלון רפפה חיצוני חשמלי + ארגז חיצוני	ויטרינה פרופיל 7500 קליל
2	160	240	1	צלון רפפה חיצוני חשמלי + ארגז חיצוני	חלון קבוע פרופיל 7000 קליל
3	325	240	1	צלון רפפה חיצוני חשמלי + ארגז חיצוני	
4	220	240	1	צלון רפפה חיצוני חשמלי + ארגז חיצוני	ויטרינה פרופיל 7500 קליל
5	110	110	1	צלון רפפה חיצוני חשמלי + ארגז חיצוני	חלון הזזה פרופיל 7000 קליל
6	220	110	1	צלון רפפה חיצוני חשמלי + ארגז חיצוני	חלון הזזה פרופיל 7000 קליל
7	60	110	2	צלון רפפה חיצוני חשמלי + ארגז חיצוני	חלון קיפ פרופיל 4500 קליל

קומה א

8	300	230	1	תריס גלילה חשמלי	ויטרינה פרופיל 7500 קליל
9	110	110	4	תריס גלילה חשמלי	חלון הזזה פרופיל 7000 קליל
10	220	110	5	תריס גלילה חשמלי	חלון הזזה פרופיל 7000 קליל
11	60	110	1	תריס גלילה חשמלי	חלון קיפ פרופיל 4500 קליל

סוג זכוכית – בהתאם למפורט בדו"ח התרמי (תנאי המינימום בעמוד 9 מתוך המפרט התרמי). כמו כן, הזכוכית תקבע בתיאום עם הקבלן לאחר אישור יועץ התרמי וחברת הניהול

כל פריט יחולק למינימום הכנפיים האפשרי (לתיאום מול ספק האלומיניום ובמסגרת שרטוטי shop drawing)

רשימת דלתות					
סוג	הערות	כמות	גובה	רוחב	מספר פריט

0	165	240	1	דלת כניסה	דלת חוץ דגם גארדה
1	90	210	2	דלת פנים	דלת פנים "אקוודור" תוצרת חמדיה
2	80	210	7	דלת פנים	דלת פנים "אקוודור" תוצרת חמדיה
3	80	210	1	דלת הזזה	דלת הזזה "אקוודור" פורמייקה תוצרת חמדיה
4	80	200	1	דלת נגרות ממ"ד	דלת פנים "אקוודור" תוצרת חמדיה

נוימן חיינר אדריכלים בע"מ

כל הזכויות שמורות
ט.ל.ח.

NeumanHaynerArchitects



רשימת פתחים			שם התכנית:
גליון מספר:	A3-6-1000	מהדורה:	01
שם הפרויקט:	נופיה - מגרש 15	תאריך:	22.09.2025
שם המממן:	קבוצת רכישה נופיה	סטטוס:	למכרז
09/11/2025 8:55:40			קנה מידה: