

עודכן ע"י: _____ יפעת

א. בסיס
הנדסת חשמל בע"מ
משרד: יד חרוצים 16, ירושלים 93420
טל: 074-7021015 נייד: 050-6550484
077-5131015 פקס: office@ebasis.co.il א"ל

שום הפרויקט:

נופיה-אלפי מנשה

שם התכנית:


וח #1 - מגרש 15, נופיה

○ ● ○ ○ כריכות מכרז כאשר ענין		קנה מידה: 1:50	
File: מס' קובץ: 6755.dwg		Date: תאריך: 05.03.2025	
אישו: איתן		שרטט: ניאיר	
מס' הפרויקט: 675		מס' הגליון: 15	
		מס' עדכון: 1	

הנחיות לבניית לוח חשמל:

- מבנה לוח השמך פלסטי חסין אש סדרת FW מחוברת Hager
- דגם W62u2000 ל-144 מודולים (2x6x12) לפחות
- דלת פח 30x30 מתכתית
- בדיד כפול 2-Class
- צבע לבן
- מהדקי אספ והאקרי עם חיבור מהיר
- ציוד חשמלי יריה סגור ABB שנייה הגר או Eaton ככלד בעל דגם
- יש לשמור רכוש 30% מקטן ספייקד עמידות רכוש

לוח חשמל דירתי ראשי #1
מגרש 15

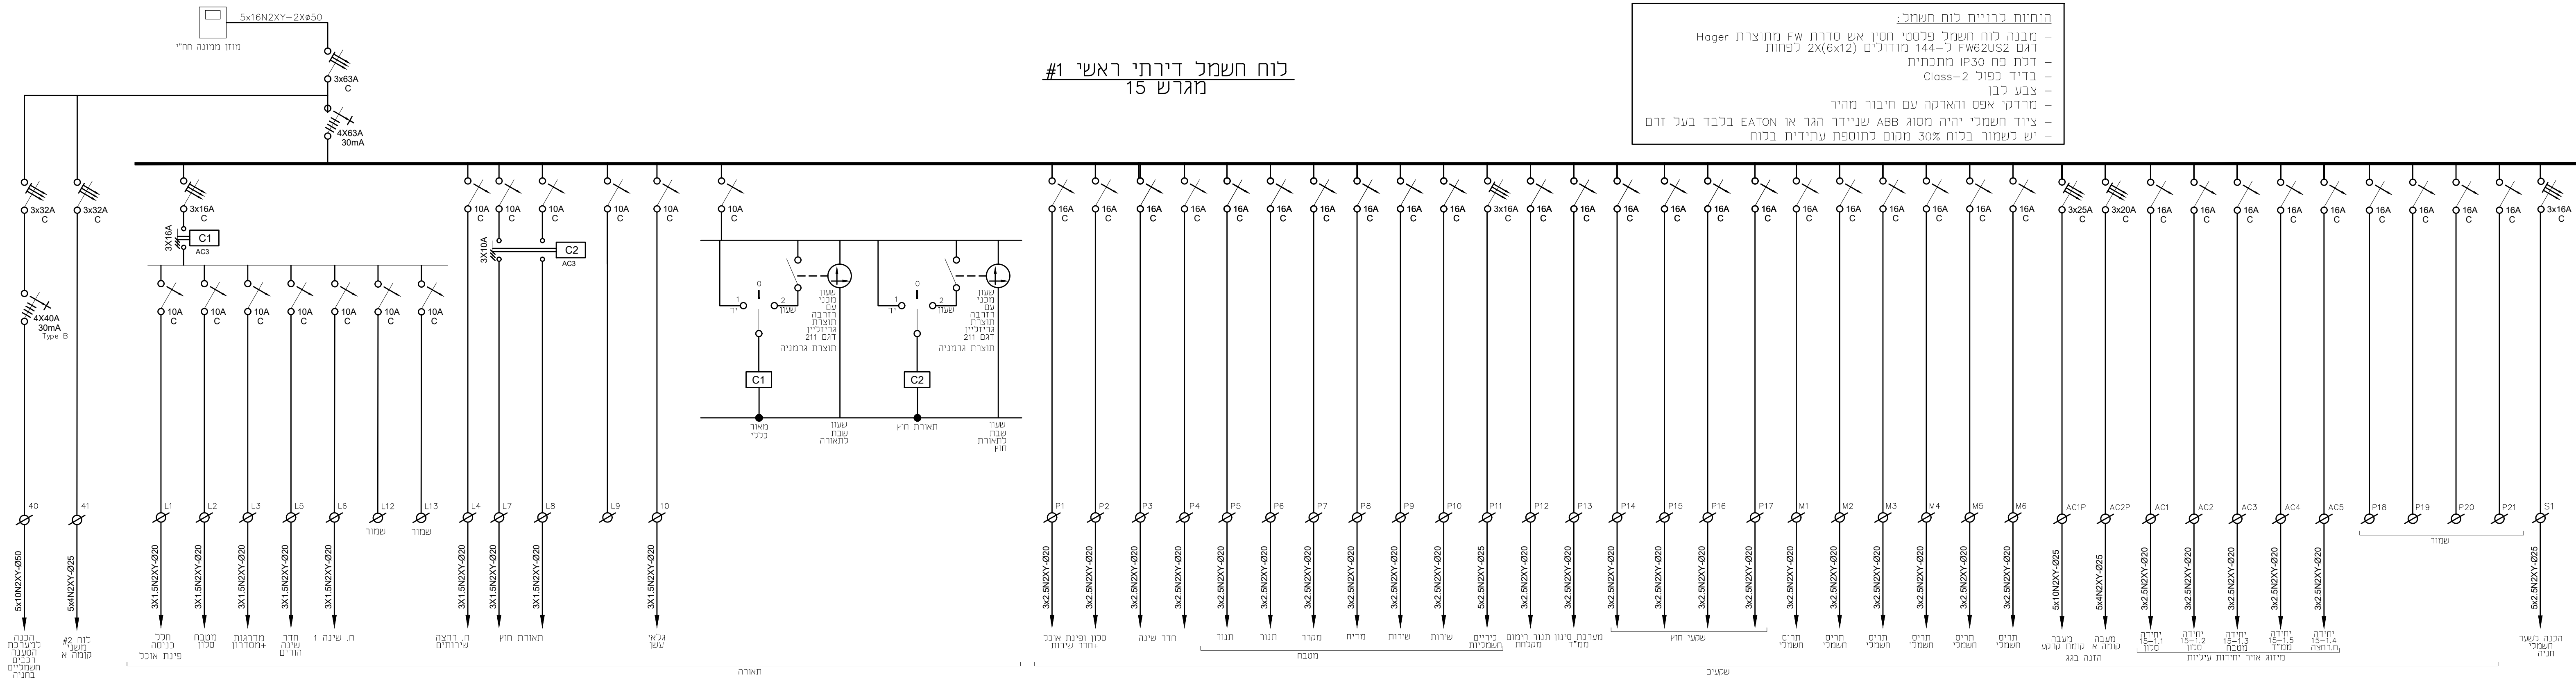

#2 לוח חשמל משני
מגרש 15

