
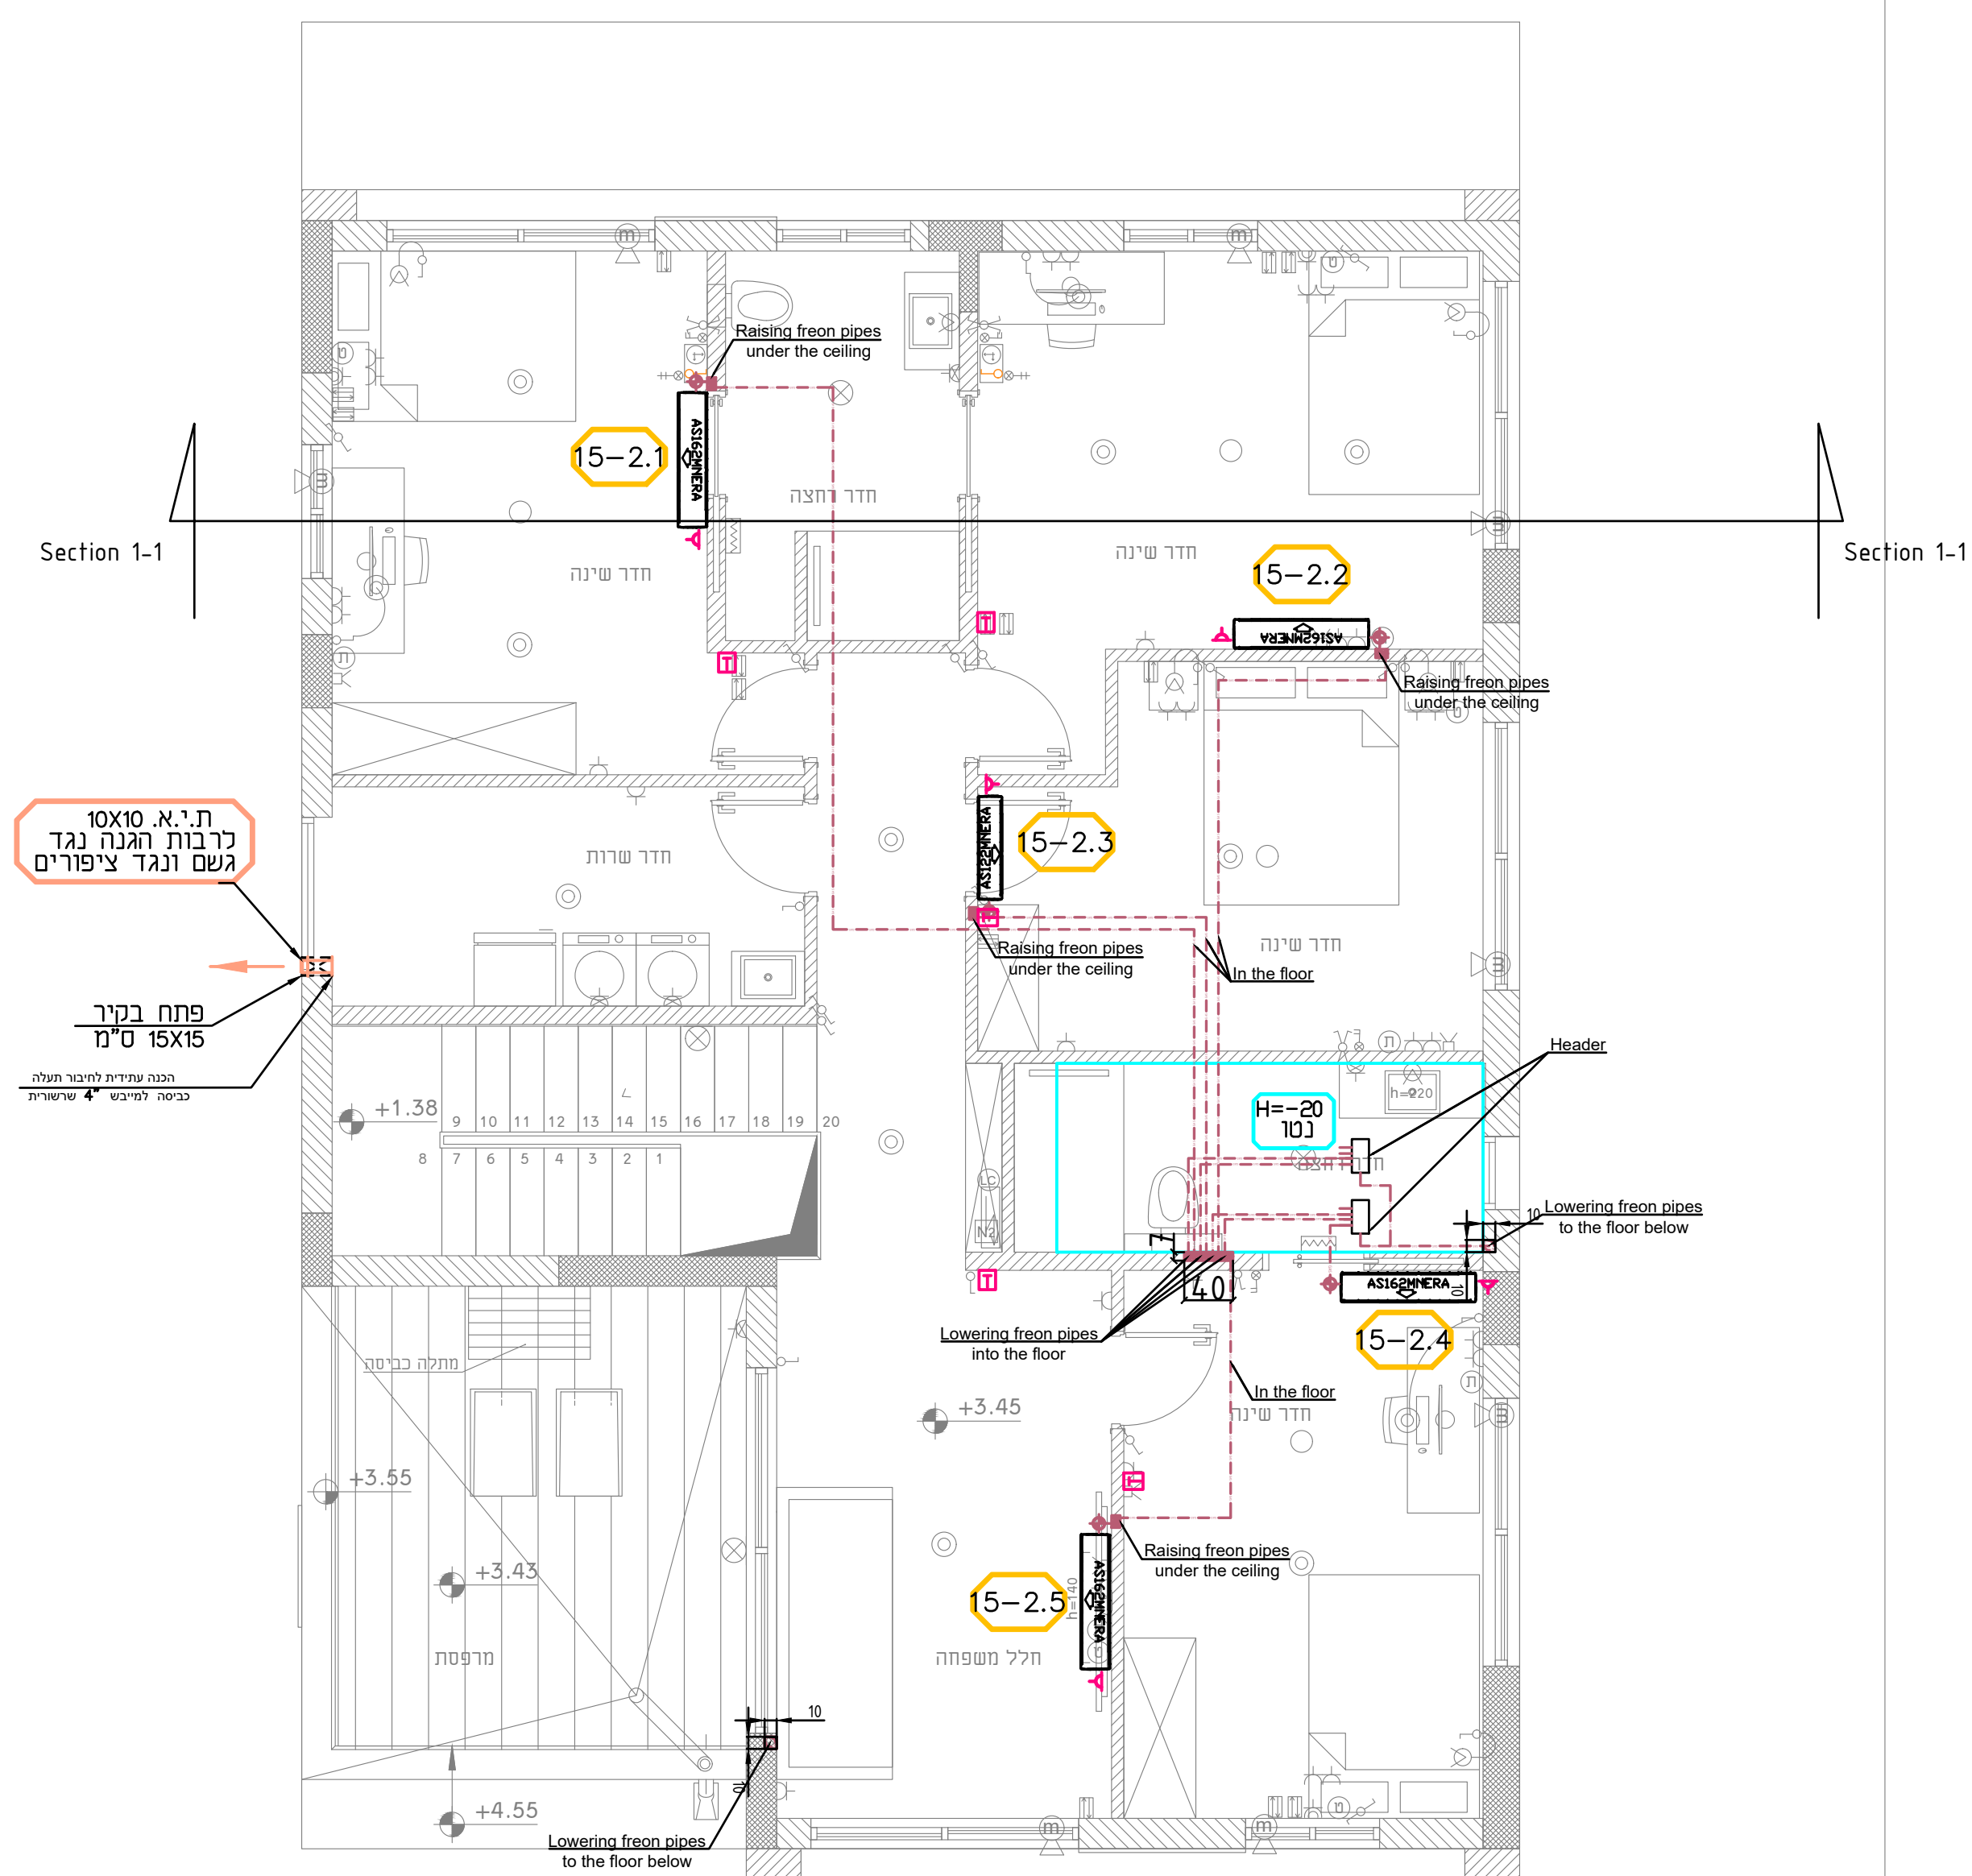


אוריכל פנים	
אינסטיציה	
בסיחת אש	
אקוסטיקה	
חשתי והזרה	
קונסטרוקציה	
קבלו ראש	
ניחול פרויקט	
נמח	
אוריכל	



חברות לאשור	22.12.2025	⚠️
חברות לאשור	26.05.2025	⚠️
חברות כעיון	01.05.2025	⚠️
שנתיים:	חאריץ:	100

תעלות ותריסי אוויר חוזר	
תעלות ותריסי אספקת אוויר	
תעלות ותריסי אוויר צח	
תעלות ותריסי יניקת אוויר	
תעלות ותריסי שיחרור עשן	
צנרת גז וחשמל	
סימון מעגלי מזווג אוויר	

אייל ארז | מהנדסים יעוצים
ייעוץ ותכנון מערכות מיזוג ואוויר, פיקוח עליון
0545919748

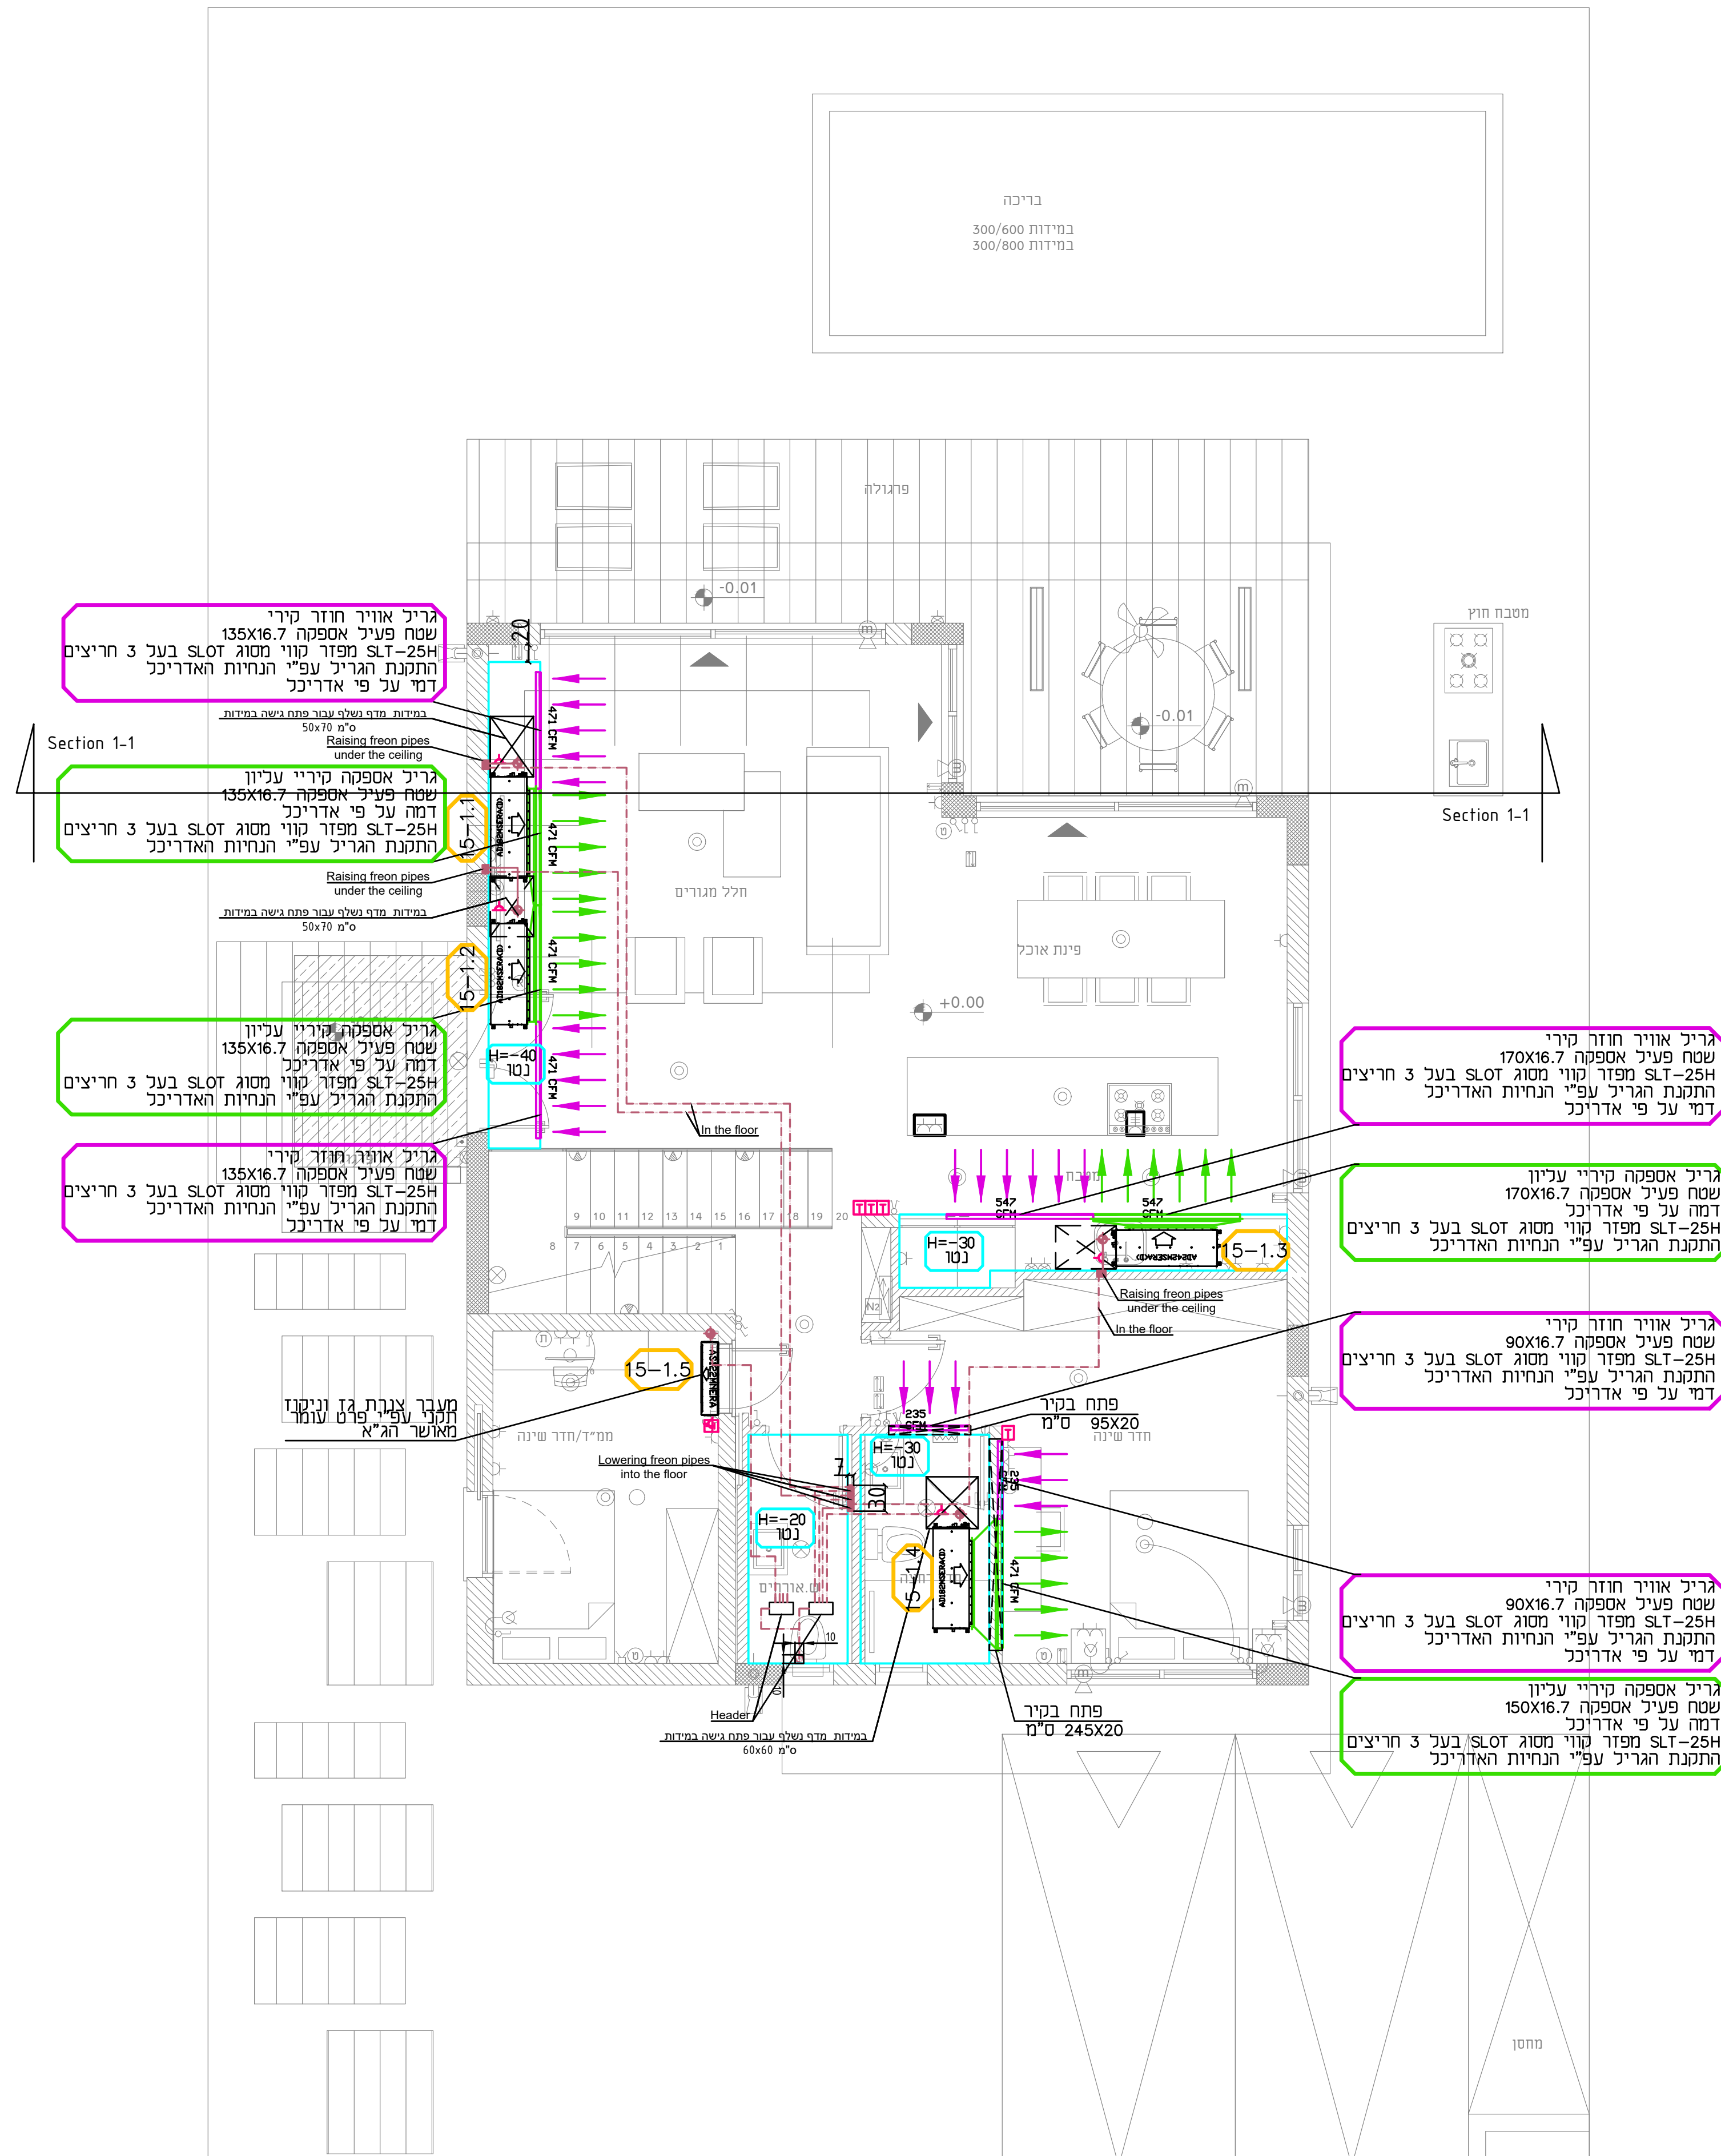

Option ~~No~~1
VRF duct unit in living room
and wall mounted in rooms

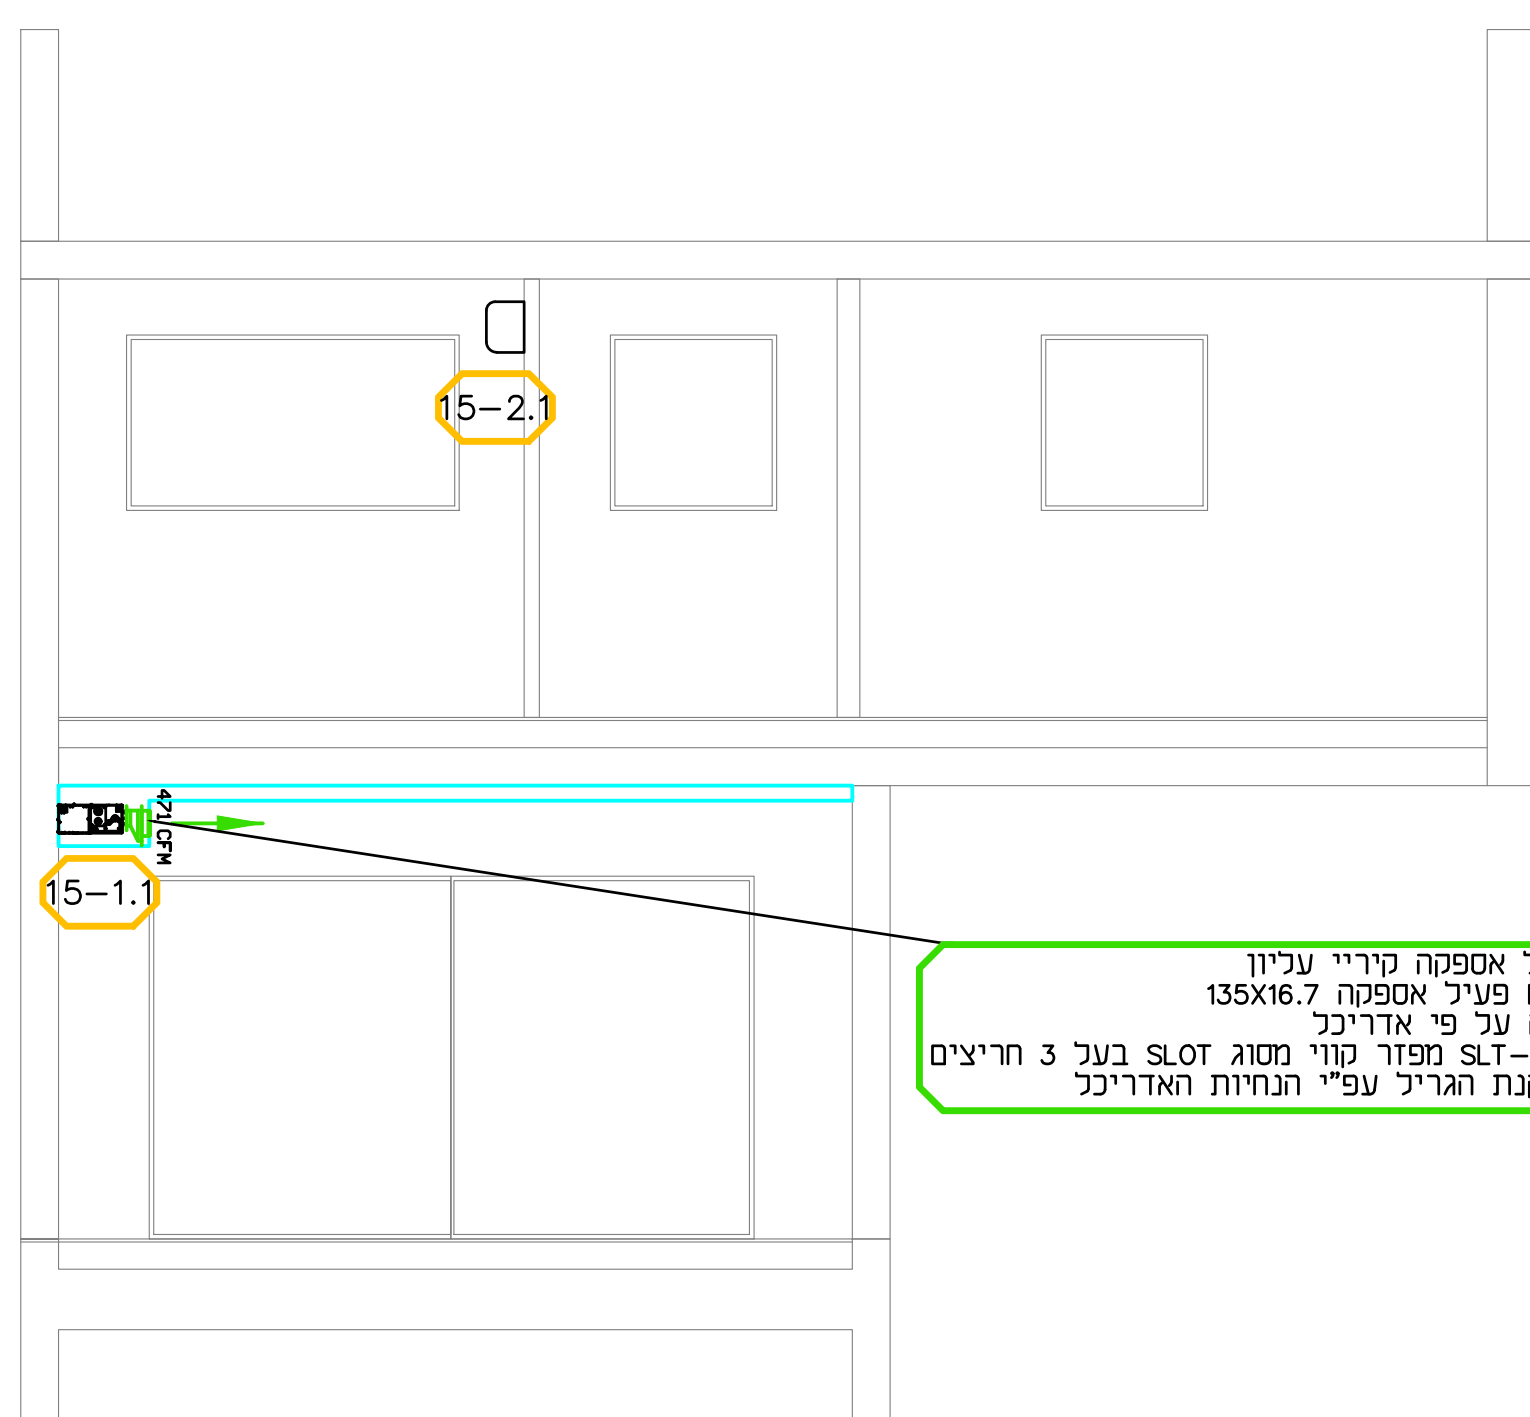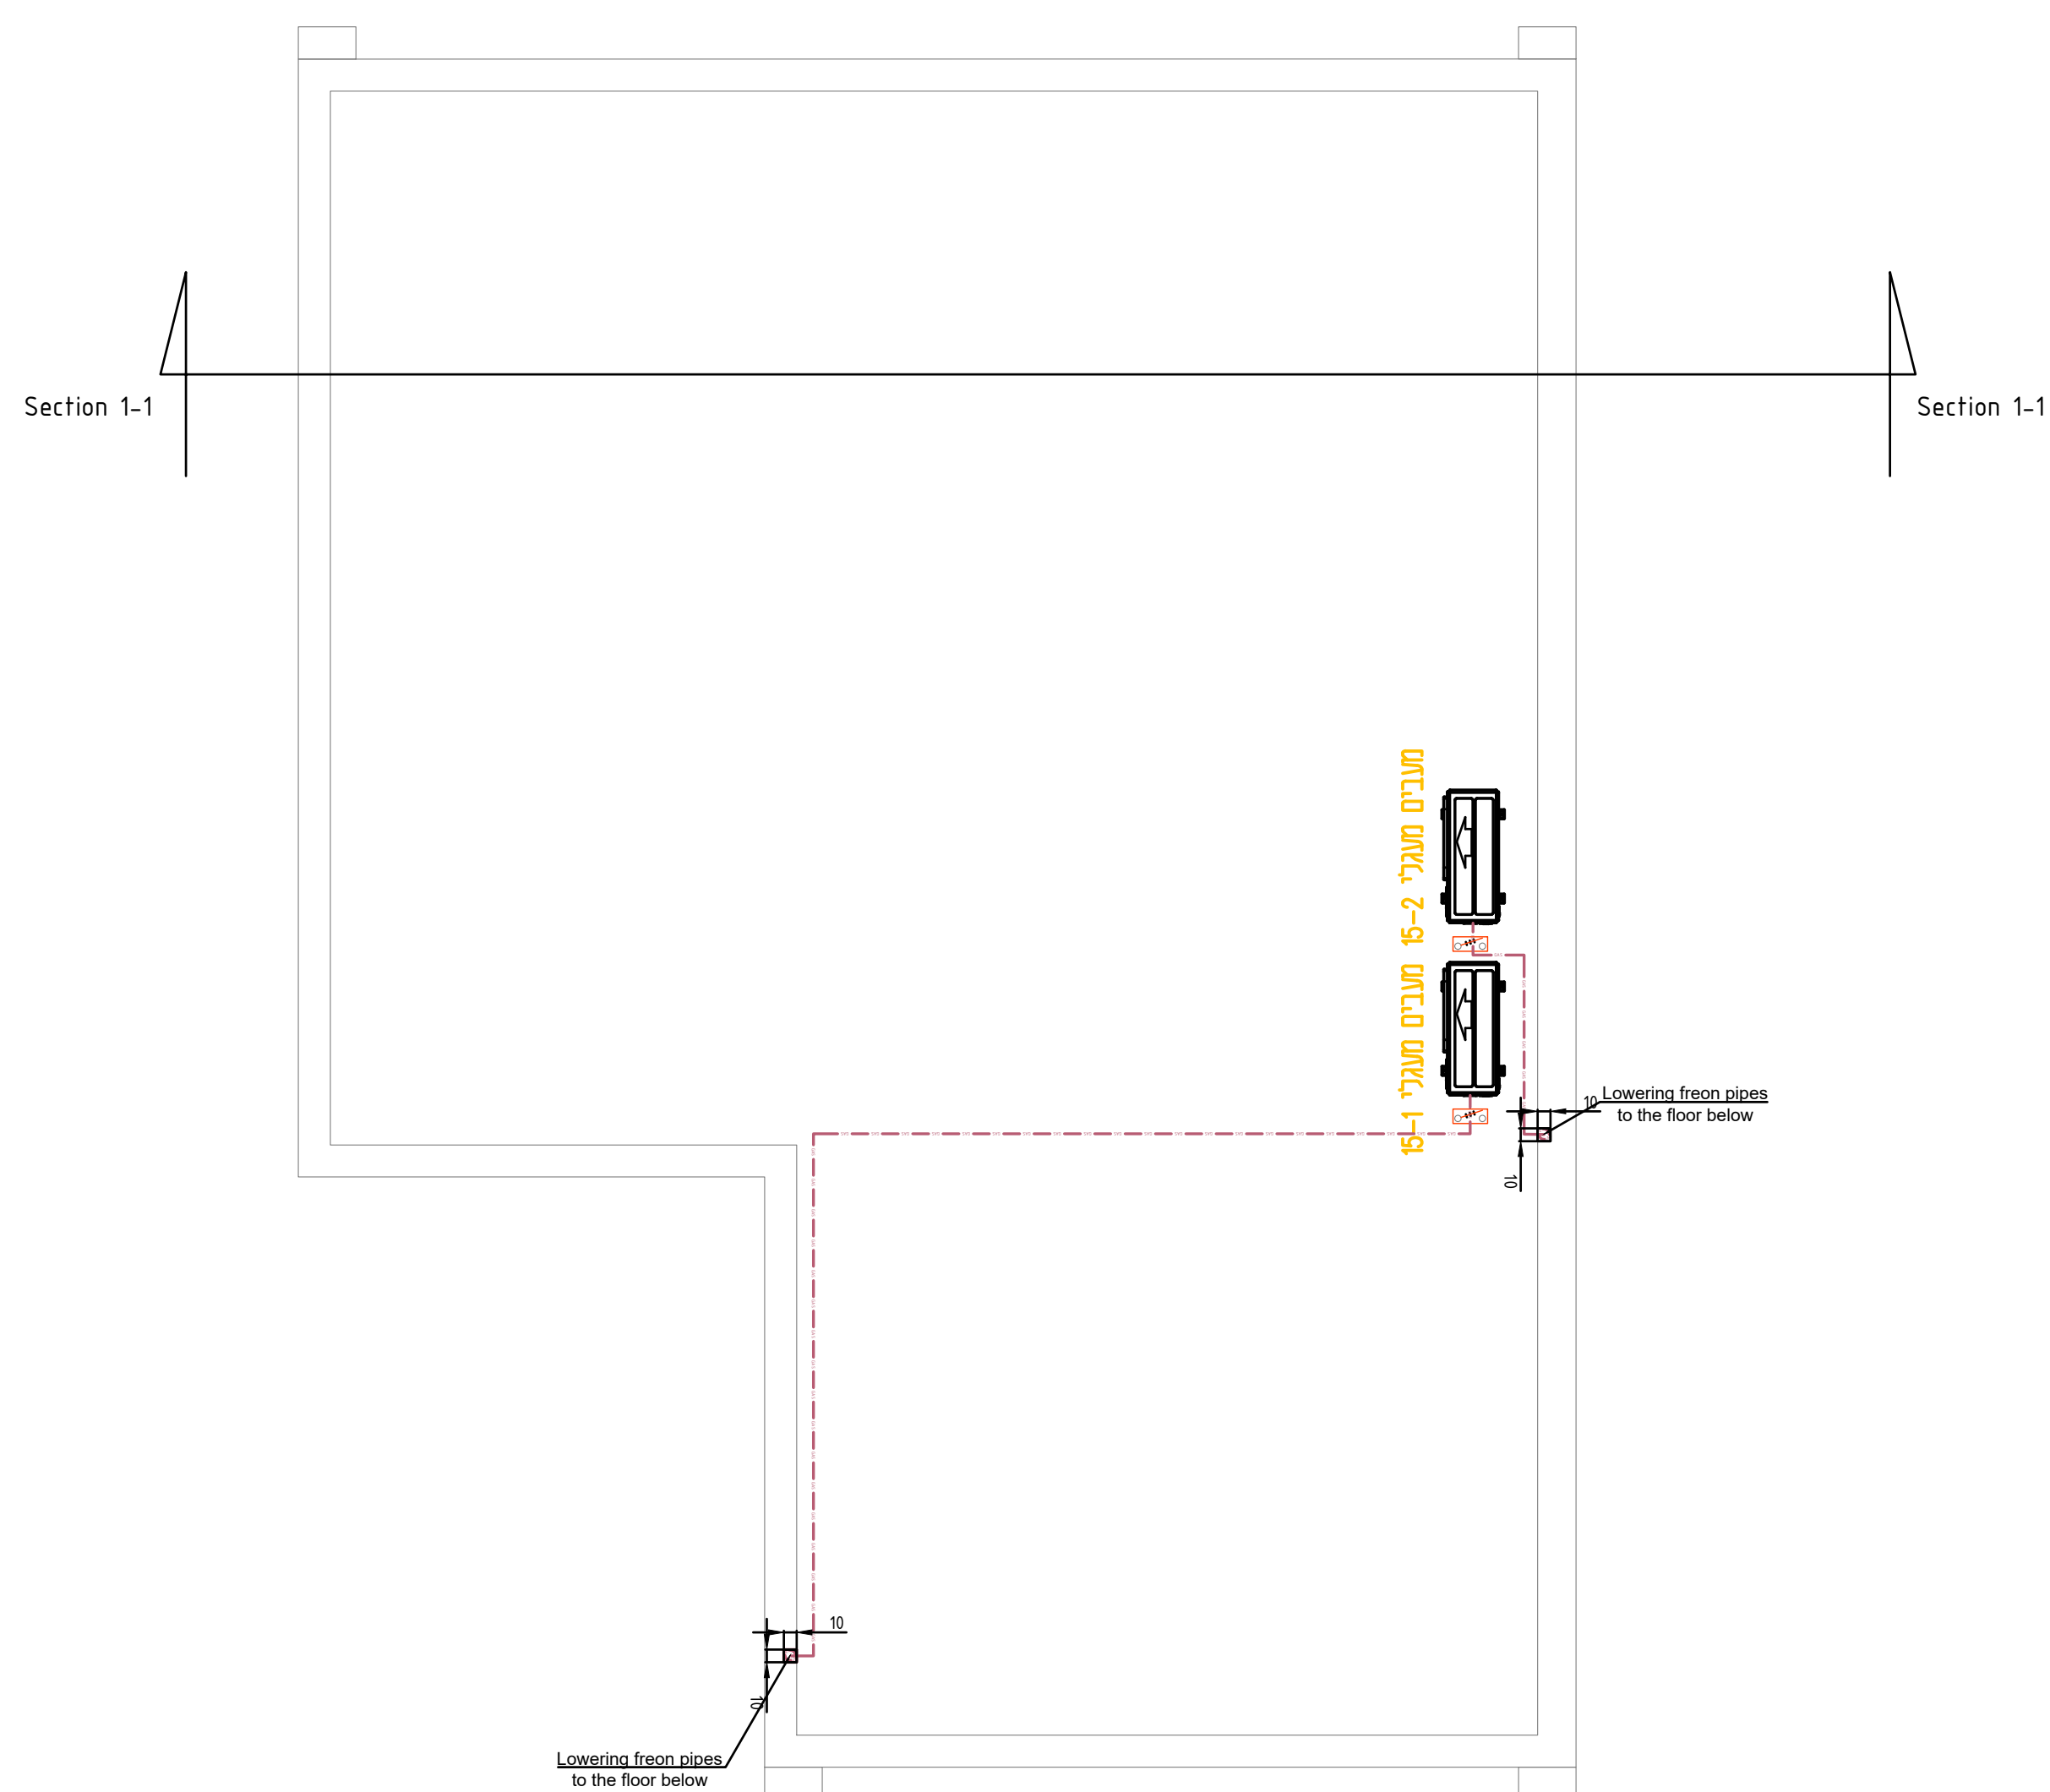

יחידות קצה מעגל 1-5											
מס' יחידה בתכנית	חוצרת	דגם	מאייד	תפוקת קורר Btu/h	ספירת חז"ר CFM	רומר רשש kg/d(A)	משקל kg	מידות ק"מ	מידות פנול	מחזק חזון V/hz/Ph	הספק נצרך
5-1, 5-2, 5-4	Haier	AD182MSERA(D)	Slim Duct Low ESP	19,100	471	33	22.2	421/18.5/177	---	230/50/1	---
5-1, 5	Haier	AD242MSERA(D)	Slim Duct Low ESP	24,200	547	36	24	421/18.5/177	---	230/50/1	---
5-1, 5	Haier	AS122MNERA	מאייד עילי	12,300	371	37	10	201/28.3/85.5	---	230/50/1	---

יחידות ספד מעגל 15-2										
ספד צנר ω	ספד חזנה V/mHz/Ph	סדו 35	סדו גד	ספד KG	סד רש dB(A)	ספד סר CPM	ספד סר Btu/h	ספד	ספד	ספד ספד
---	230/50/1	---	101 204/85.5	10	37	371	12,300	ספד ספד	AS182MNERA	ספד
---	230/50/1	---	101 254/33.6/111.5	16	39	471	15,300	ספד ספד	AS162MNERA	ספד

מיקום סופי של הניקוזים
ייתבע בשטח בתאום עם האדריכל
יועץ אינסטלציה וקבלן מיזוג אוויר

מיקום סופי של הניקוזים
ייקבע בשטח בתאום עם האדריכל
יועץ אינסטלציה וקבלן מזוג אוויר



- | מהדורה | | |
|-------------|------------|----|
| | | ⚠ |
| חברות לאשר | 28.05.2025 | ⚠ |
| חברות כעיון | 01.05.2025 | ⚠ |
| שניים: | חאיר: | סג |

המבצע אחראי למידות ולהתאמותו למציאות בכל מקרה של אי התאמה, סתירה או טעות עליו להודיע למתכנן לפני התקדמותו בביצוע! אין לקבוע מידות על סמך מדידה בשרטוט. אין לעשות כל שימוש בתוכנית זו ארבעינות הגלומים בה ללא אישור בכתב מאת המתכנן.

1. כל התעלות מחוץ למבנה יבורדו
בבידוד אקוסטי צבוי "2"
מידות התעלות הן מידות פח
2. תעלות מזוג בחור המבנה יבורדו
בבידוד אקוסטי פנימי "1"
מידות התעלות הן מידות פח
3. תעלות אוויר צה יבורדו
בבידוד טורי "1"
מידות התעלות הן מידות פח
4. יש לאסוס בסיסיות און פינות החיבור
של תעבות מזוג אוויר רכני כיפוף
הפחים המתחברים

מפ- פסוק	
מאג- מפזר אוויר קרי	
מגת- מפזר אוויר תחת	
מחז- תריס אוויר חזר	
מחצ- תריס אוויר צח	
מב- בירוד קוטבי	
בס- בירוד סרט	
בכ- לכא בירוד	
דא- דמפר אש	
סרמטסט- סרור הפעלה	
שקע השביל- תפוח יועץ חשמל	
שקע תלת פאזי- תפוח יועץ חשמל	
מסמס במחור חד פאזי- תפוח יועץ חשמל	
מסמס במחור תלת פאזי- תפוח יועץ חשמל	
ניקוז המים- תפוח יועץ חשמל	
גובה 20 מ"מ- תחתית גובה המאייד	
שלם הפעלה אחרות	

תעלות ותריסי אוויר חוזר	
תעלות ותריסי אספקת אוויר	
תעלות ותריסי אוויר צח	
תעלות ותריסי ניקת אוויר	
תעלות ותריסי שיחרור עשן	
צנרת גז וחשמל	
סימון מעגלי מזוג אוויר	

191	מבני מגורים צמודי קרקע נופיה אפרי' מנשה מגרש 15	שם הפרויקט
1:50	מיזוג אוויר ואווירור	שם
26.05.2025	קומת גג וטבלאות	תאריך
2		שם הפרויקט
מחזורית	מחזור	שם הפרויקט
נכנס	מחזור	שם הפרויקט
01.05.2025	מחזור	שם הפרויקט
מחזור	מחזור	שם הפרויקט