


מתכננים:

ניהול פרויקט
בן סולומון - מהיסוד
פיקוח
בן סולומון - מהיסוד
קונסטרוקציה
ערן שילר
מיזוג אוויר
אייל ארז מהנדסים ויועצים בע"מ
אינסטלציה
איתן אלמסי
חשמל
איתן בסיס
אלומיניום
נוף
נתי בלוקא
חשמל חכם
חימום תת רצפתי
איטום
צבי טל
אקוסטיקה
מעליות
קרקע וביסוס
דיה הנדסת קרקע וביסוס
רישוי

± 0.00 = +246.50
הערות: 1. תכנית זו יש לקרוא יחד עם תכנית הריטשים. 2. גובה אבסולוטי: ראו תכנית פיתוח. 3. המידות הן בין קירות הבניה (לא כולל פית). 4. פיתוח השטח סביב הבנוה, כולל, מדרגות, גדרות, שבילים, ריצופים, שטחים צדדים, חניה גינה וראו תכנית פיתוח. 5. איסוס קירות ורצפות הבנוה כמתנ עם הקרקע ובידוד תרמי לאורך העמודים והקורות ורצפות כליות או עם סימני (גינה)- ראו תכנית קונסטרוקציה. 6. אף חים יבוצע בכל מישור אופקי הבולם מהגבן. 7. פית תרמי בממד" ע"פ מפרט חומרים, מאושר ע"י פיקוח העודף. המבצע אחראי לסידות : עליו לבקר ולבדוק את כל המידות בתכנית ובנקטת הבקרה. במסגרת של מנות או אי התאמה בתכנית /או בבנוי, עליו להודיע על כך מיד לאדריכל במסד המשרד בענבודות. המבצע ישתמש או וקע בתכנית שאושרו לכניצוע. המבצע יחזיק באחר, בכל מה, של משרדנו של תכנית. את לקבוע מידות על ידי חדייה בשר מוס. התכנית היתה רכוש האדריכל ואין לשנותה כל שימוש בה או ברעיונות הגלומים בה, אלא באישור בכתב מהאדריכל. מהנדס /או' יושע אשר שמו רשום בתכנית זו, נושא לכיד באחריות המקצועית והטקטית לתכנית. על המפקח והמבצע לזוודא התאמת התכנית האדריכלית "לכניצוע" לתכנית זוהי, המכר והתכנית המאושרות ע"י כל הגורמים הרשמיים. תכנית כוללת את כל האמצעים והידוע עד ליום תחצתה.

משרד קירות:

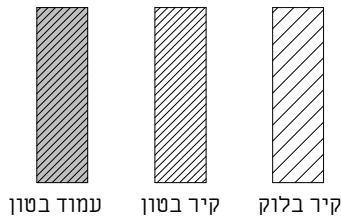

תאריך	תיאור	מהדורה
22.09.2025	מכרז	1


אדריכלות

שם המסין:	CLIENT NAME:
קבוצת רכישה נופיה	
שם הפרויקט:	PROJECT NAME:
נופיה - מגרש 16	
שם הגליון:	DRAWING NAME:
גליון שער	
מספר גליון:	SHEET NUMBER:
A3-1-100	
מהדורה:	EDITION:
קנה מידה:	SCALE:
סטוס:	STATUS:
למכרז	
שורטס ע"י:	אולמוג אור
תאריך:	DATE:
29.12.25	

נויטן חיינו אדריכלים
מודד והנדס 2, בית חירות
99-9545842 09

office@nh-arch.com
www.nh-arch.com

נופיה - מגרש 16			
מס' גליון	שם גליון	מהדורה	תאריך הפצת מהדורה
A3-1-100	גליון שער	1	22.09.2025
A3-1-101	תכנית קומת קרקע	2	29.12.2025
A3-1-102	תכנית קומה א	1	22.09.2025
A3-1-103	תכנית מפלס גג	1	22.09.2025
A3-1-400	תכנית תקרה ותאורה	1	22.09.2025
A3-2-200	חזיתות 1	1	22.09.2025
A3-2-201	חזיתות 2	1	22.09.2025
A3-3-100	חתכים	1	22.09.2025
A3-4-100	גליון מדרגות	1	22.09.2025
A3-4-103	פרטים	1	22.09.2025
A3-4-104	פרטי פרגולה	1	22.09.2025
A3-6-1000	רשימת פתחים	1	22.09.2025

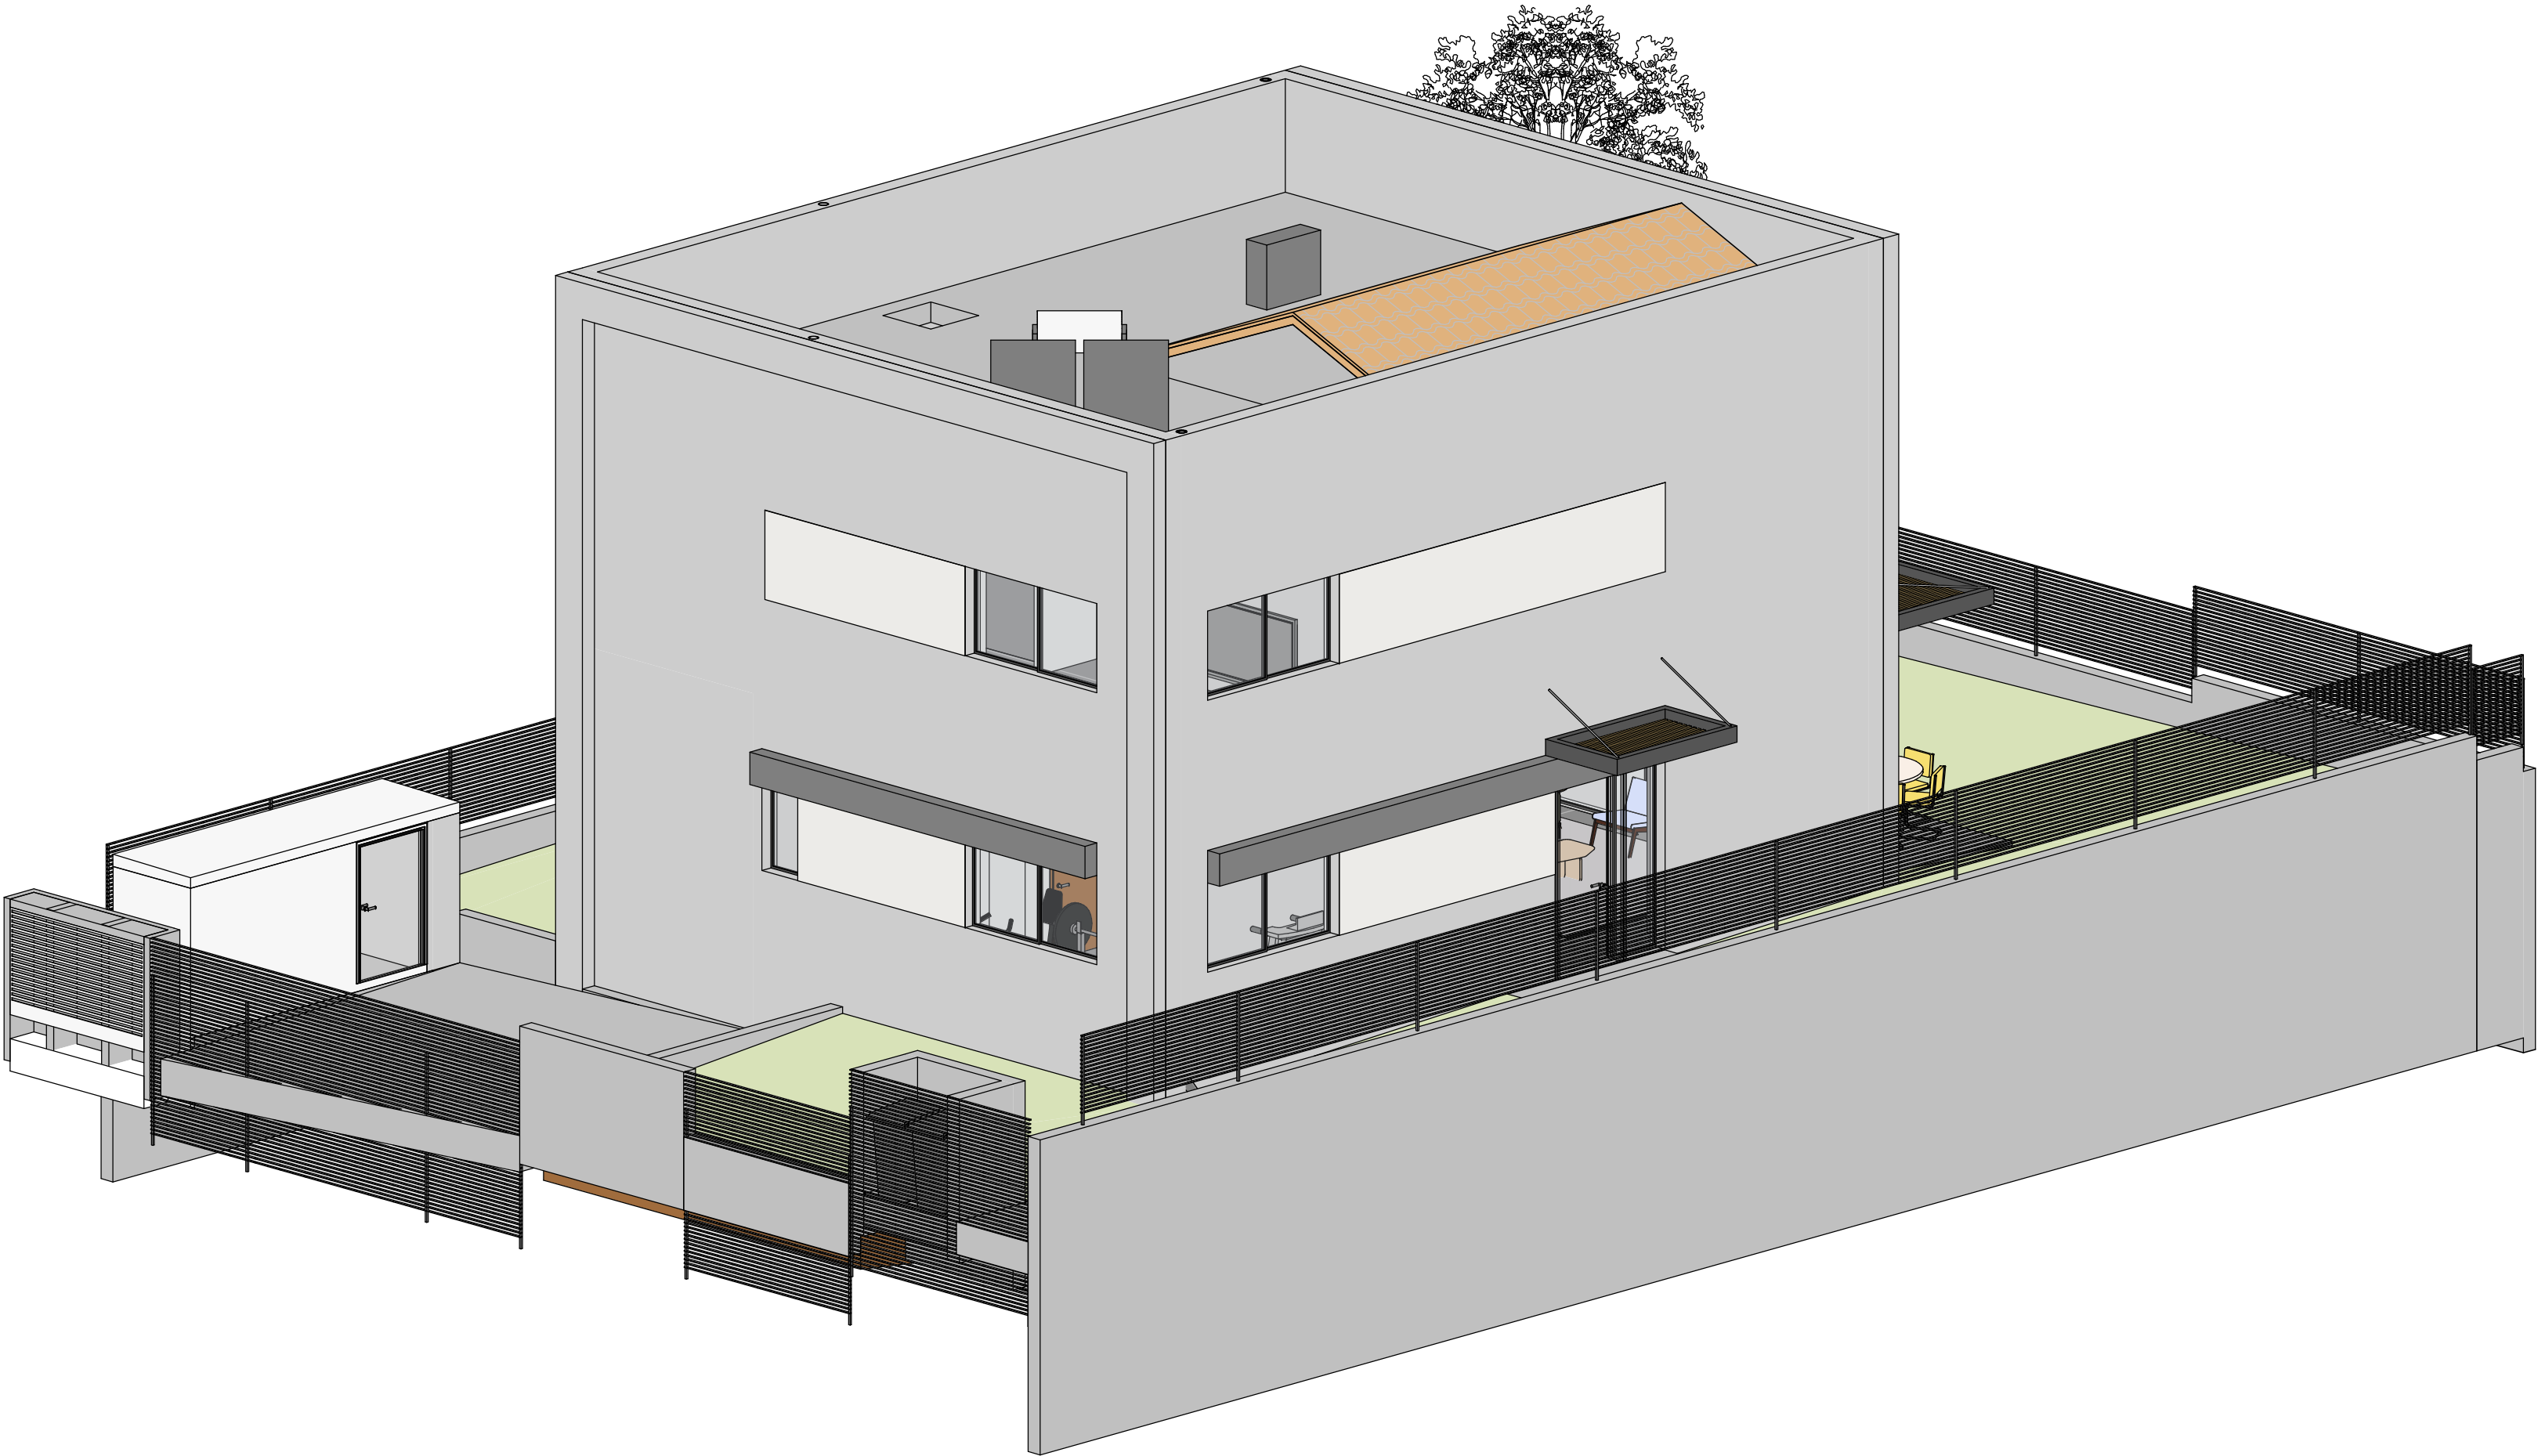

מתכונים:

ניהול פרויקט
בן סולומון - מהיסוד
פיקוח
בן סולומון - מהיסוד
קונסטרוקציה
ערן שילר
מזיג אוזיר
אייל ארז מהנדסים ויועצים בע"מ
אינסטלציה
איתן אלמסי
חשמל
איתן בסיס
אלומיניום
נוף
נתי בלוקא
חשמל חכם
חימום תת רצפתי
איטום
צבי טל
אקוסטיקה
מעליות
קרקע וביסוס
דיה הנדסת קרקע וביסוס
רישוי

$$\pm 0.00 = +246.50$$

הערות:
 1. תביתו ויש לקרוא יחד עם הכביות הוועצים.
 2. גובה אסכולים: ארבע תביות פחות.
 3. המידות הן בין קירות חלון לבין כלול (ס"ח).
 4. פיתוח השטח שביני חתובה, לכולל, מדורות, שבילים, רציפות, פשיטות בסיס וכו'.
 5. אסכולים: קירות ורצפות חתובה במגע עם הקרקע ובידוד תרמי לאורך המעטדים והקורות על-התקרות. גליות ויש מיזל (ניגון) – ארבע תביות קונסטרוקציה.
 6. אף כי יבוצע במידה אופיינית חתובה.
 7. יש תרמי במסגרת של מפרס ומחזיק, מאגרי עיי פידוק מורקף.

[illegible]

זקרא קירות:

[illegible]

אדריכלות

CLIENT NAME: _____ שם המזמין:

קבוצת רכישה נופיה

PROJECT NAME: שם הפרויקט:

בופיה - מגרש 16

DRAWING NAME: ס הגליון:

תכנית קומת קרקע

מספר גיליון


A3-1-101

EDITION:	סוף חידה:	CALE:	תאריך:
----------	-----------	-------	--------

1 : 50

STATUS: 01000

רמת מים	מדידת מים
---------	-----------

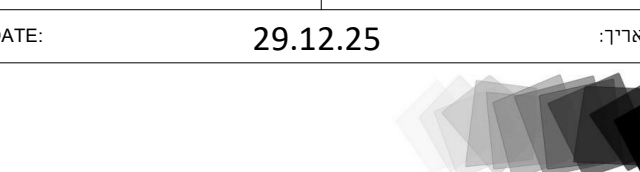


NeumanHaynerArchitects

office@nh-arch.com
www.nh-arch.com

זכויות ייצור / ע"פ הנחיות עו"ד

הערות:

1. יש לעבוד במקביל לתכניות יועצים המאושרות על ידי האדריכל.
2. פרטי ספי חלון - עפ"י חוברת אלומיניום של הספק הנבחר ובתיאום מול אדריכל.
3. חימום תת רצפתי (במידה ויש במגרש זה) עפ"י פרטי הספק ובתיאום מול אדריכל.
4. יש לעבוד במקביל לתכניות עיצוב פנים (במידה ויש מעצב פנים במגרש זה) המאושרות על ידי האדריכל.
5. באחריות הקבלן לעדכן את האדריכל על אי התאמה בין התכניות יועצים לאדריכלות.
6. כל הדלתות לפי מפרט מצורף.
7. כל אלמנטי הבטון יקבלו התייחסות תרמית לפי הנחיות יועץ.
8. פרטי איטום, בידוד וניקוז עפ"י תכניות יועצים ובאחריות הקבלן.

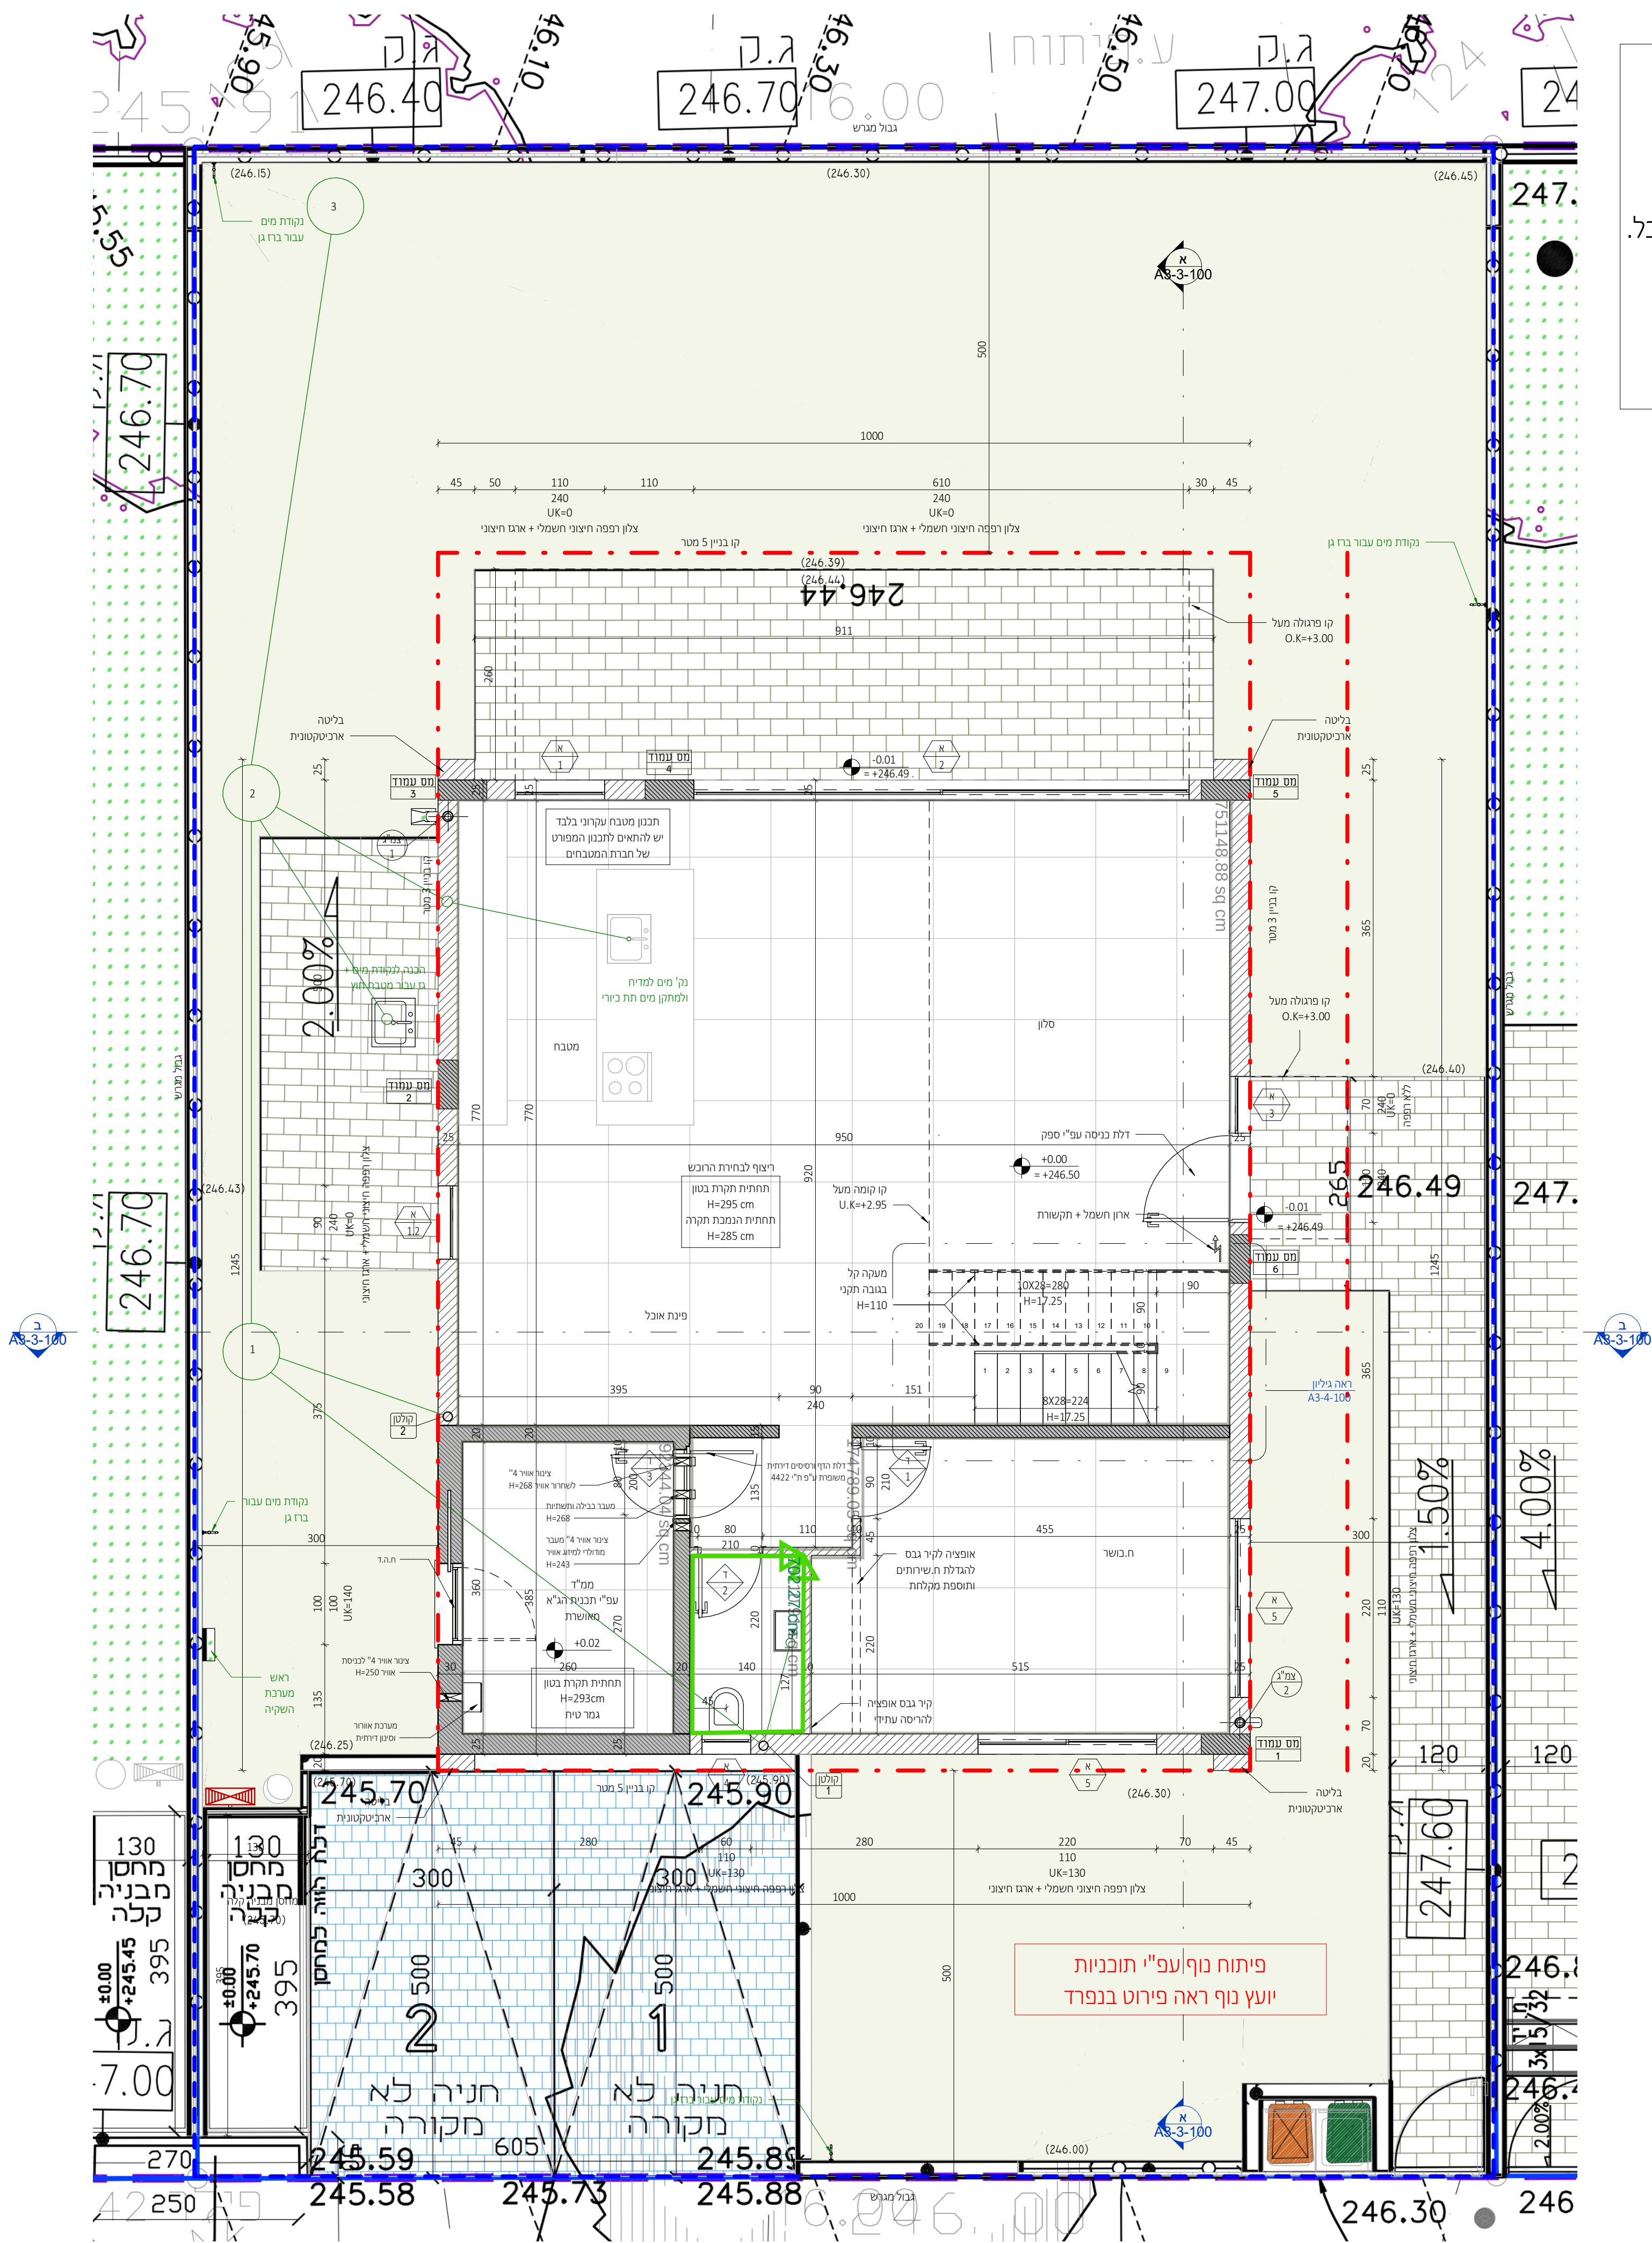

תכנית קומת קרקע

1 : 50

מתכונים:

ניהול פרויקט	בן סולומון - מהיסוד
פיקוח	בן סולומון - מהיסוד
קונסטרוקציה	ערן שילר
מיוזג אוויר	אייל ארז מהנדסים ויועצים בע"מ
אינסטלציה	איתן אלמסי
חשמל	איתן בסיס
אלומיניום	
נוף	נתי בלוקא
חשמל חכם	
חימום תת רצפתי	
איטום	צבי טל
אקוסטיקה	
מעליות	
קרקע וביסוס	דיה הנדסת קרקע וביסוס
ירשוי	

[illegible]


קרא קירות:



עמוד בטון קיר בטון קיר בלוק

[illegible]

אדריכלות

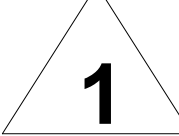CLIENT NAME:	הפרויקט:	
קבוצת רכישה נופיה		
PROJECT NAME:	הפרויקט:	
נופיה - מגרש 16		
DRAWING NAME:	התכנית:	
תכנית קומה א		
SHEET NUMBER:	פרוטוקול:	
A3-1-102		
SCALE:	קנה מידה:	EDITION:
1 : 50	000000	
STATUS:	מסמך	1 אלמנט אור
DATE:	29.12.25	1000000000 יום


NeumanHaynerArchitects

ימון חיינר אדריכלים
ורד ההדרים 2, בית חירות
ל 09-9545842

office@nh-arch.com
www.nh-arch.com

ימון חיינר אדריכלים
ורד ההדרים 2, בית חירות
ל 09-9545842

זכויות ייצור / ע"פ הנחיות עו"ד

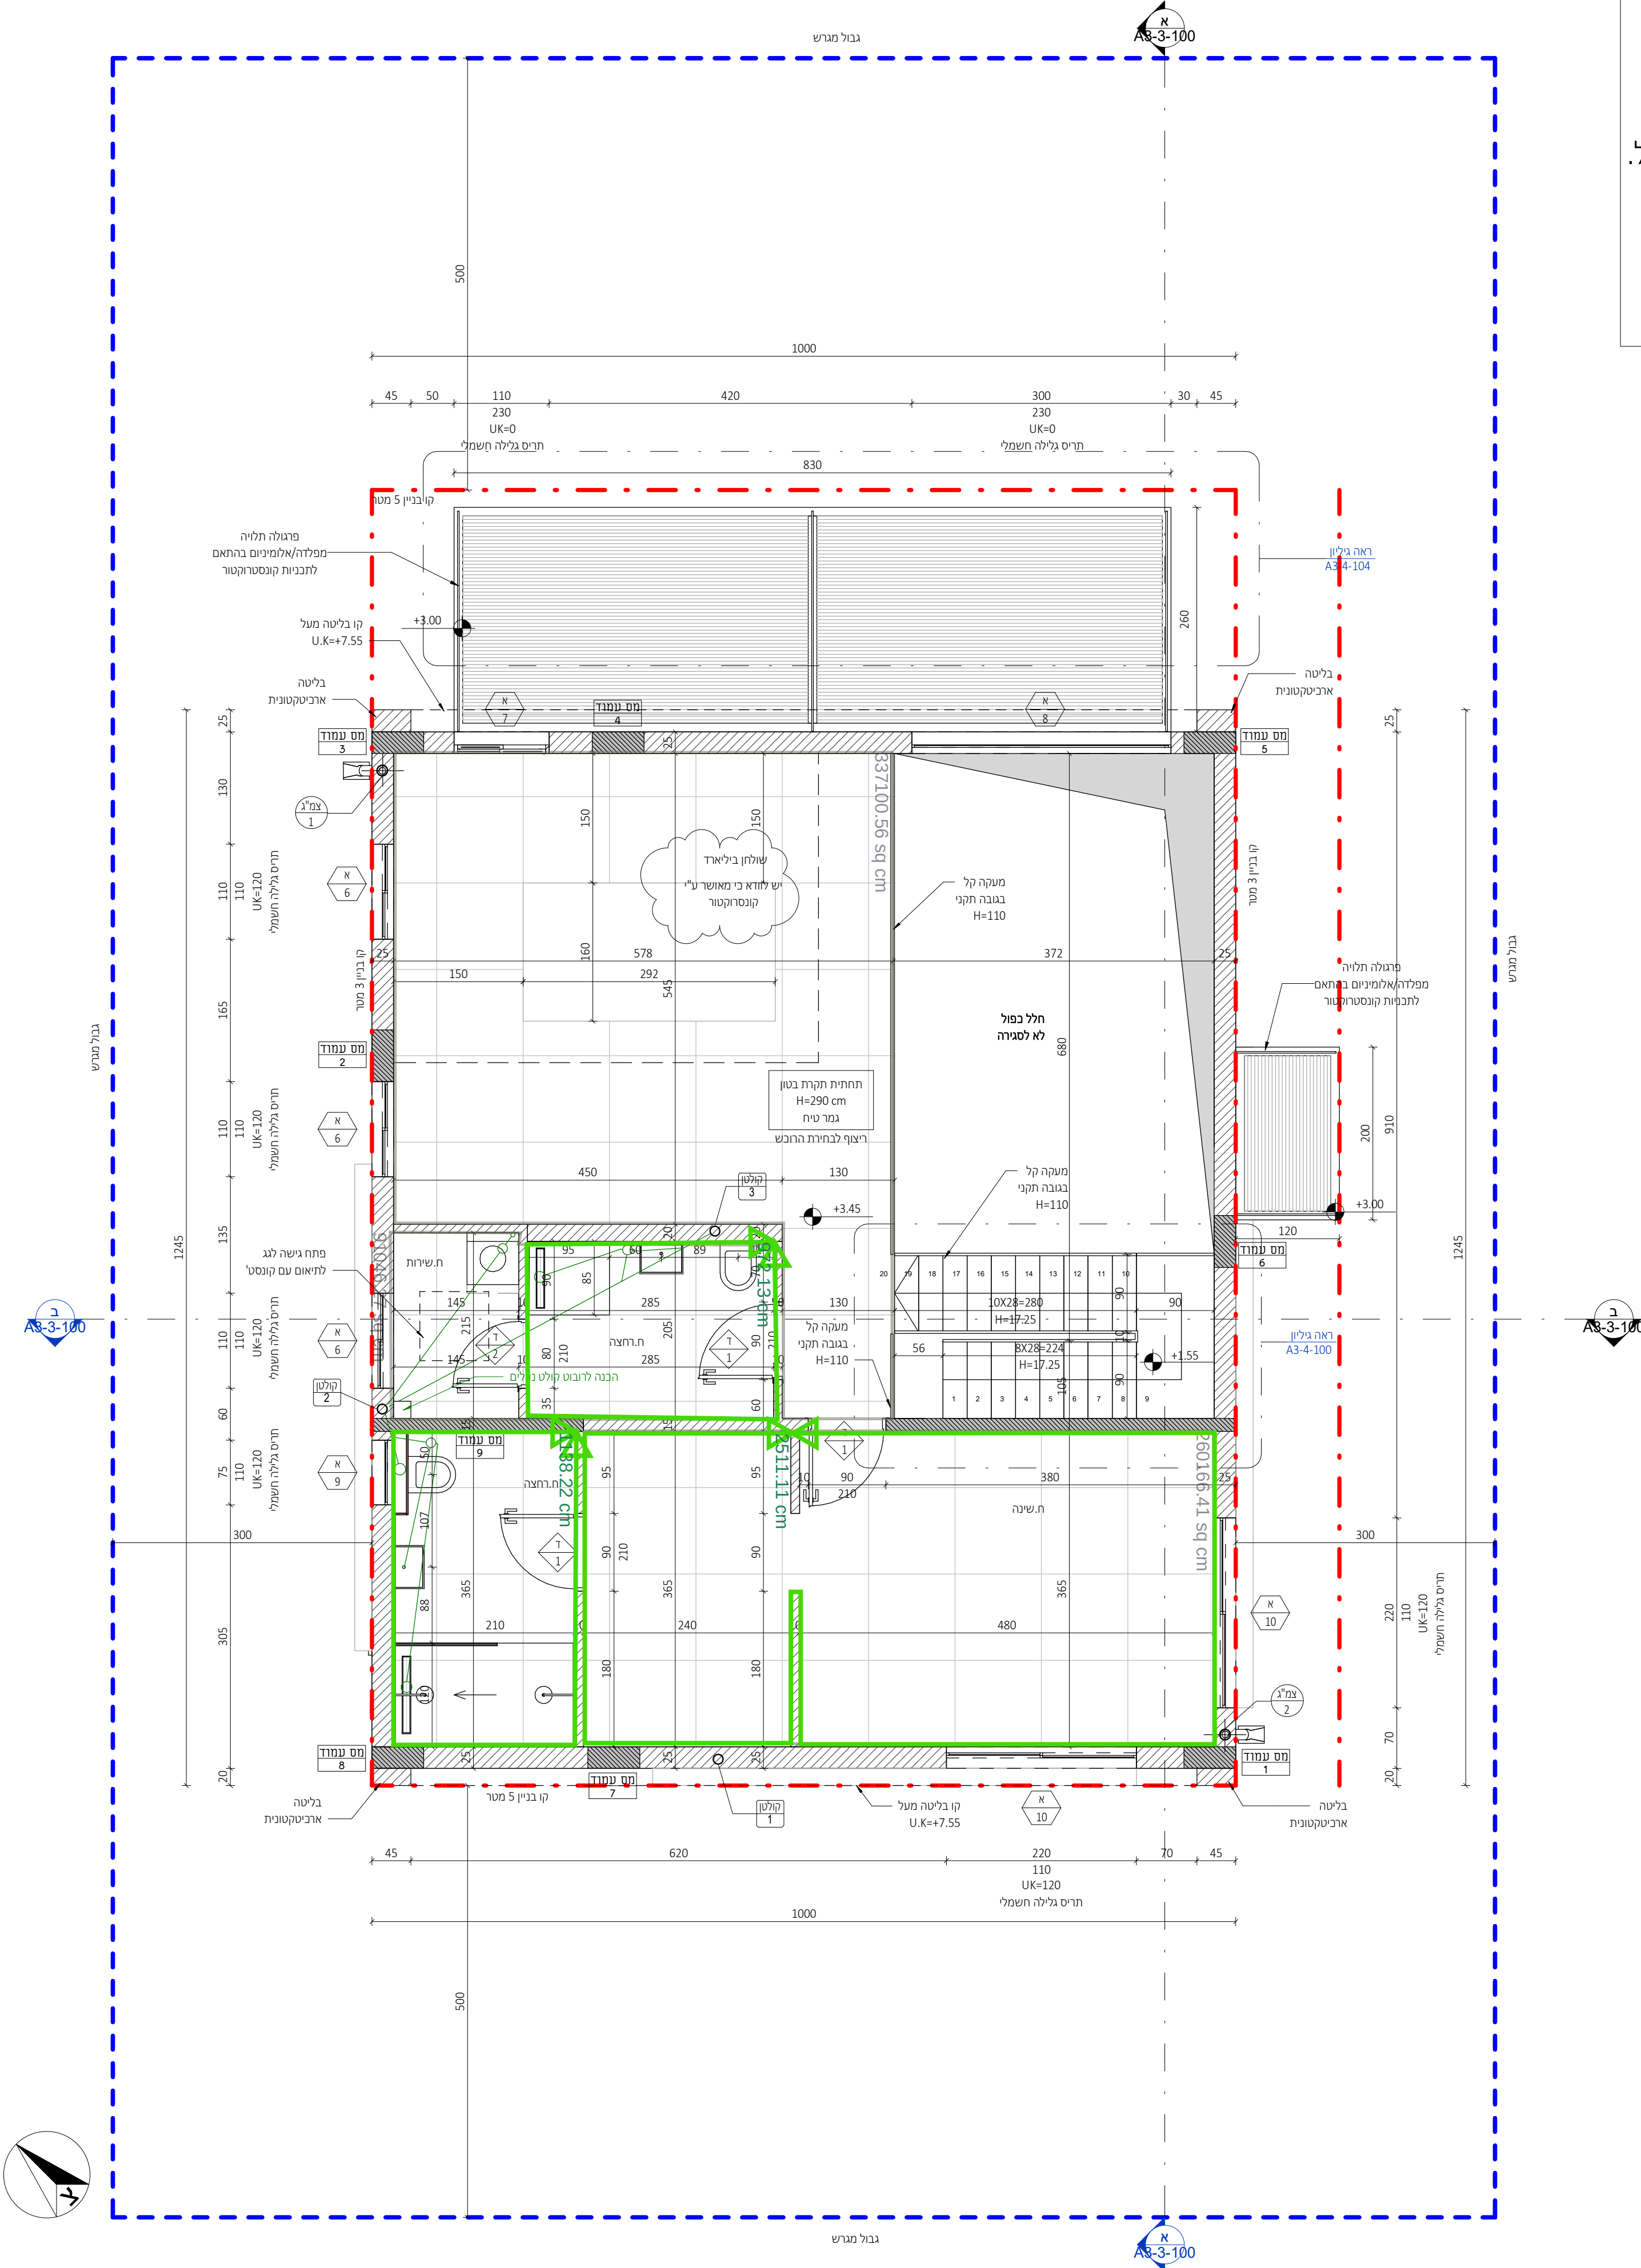

תכנית קומה א

1 : 50

- הערות:
1. יש לעבוד במקביל לתכניות יועצים המאושרות על ידי האדריכל.
 2. פרטי ספי חלון - עפ"י חוברת אלומיניום של הספק הנבחר ובתיאום מול אדריכל.
 3. חימום תת רצפתי (במידה ויש במגרש זה) עפ"י פרטי הספק ובתיאום מול אדריכל.
 4. יש לעבוד במקביל לתכניות עיצוב פנים (במידה ויש מעצב פנים במגרש זה) המאושרות על ידי האדריכל.
 5. באחריות הקבלן לעדכן את האדריכל על אי התאמה בין התכניות יועצים לאדריכלות.
 6. כל הדלתות לפי מפרט מצורף.
 7. כל אלמנטי הבטון יקבלו התייחסות תרמית לפי הנחיות יועץ.
 8. פרטי איטום, בידוד וניקוז עפ"י תכניות יועצים ובאחריות הקבלן.

מתכננים:

ניהול פרויקט
בן סולומון - מהיסוד
פיקוח
בן סולומון - מהיסוד
קונסטרוקציה
ערן שילר
מיזוג אוויר
אייל ארז מהנדסים ויועצים בע"מ
אינסטלציה
איתן אלמסי
חשמל
איתן בסיס
אלומיניום
נוף
נתי בלוקא
חשמל חכם
חימום תת רצפתי
איטום
צבי טל
אקוסטיקה
מעליות
קרקע וביסוס
דיה הנדסת קרקע וביסוס
רישוי

± 0.00 = +246.50
הערות: 1. תכנית זו אינה קריאה יחד עם תכנית הרישום. 2. גובה אבטומט - ראו תכנית פיקוח. 3. המידות הן בין קירות הבניה ולא כולל פחים. 4. פחות השטח מכיון המבנה, כולל, פורטות, נדרות, שנילים, ריצופים, שיפופים, גדרים, חניה וגן ראו תכנית פיקוח. 5. איטום קירות ורצפות המבנה כמעט עם הקרקע ובנידון תחיל לאורך העמודים והקירות של המבנה. כליות או עם סימני גיבוי - ראו תכנית קונסטרוקציה. 6. אף ימים יבוצע כל מישור אופקי הבולם חתונן. 7. סיוח תחיל במסלול - ע"פ מפרט חומרים, מאושר ע"י פיקוח העורך.
המבצע אחראי לסיווח: עליו לבקר ולבדוק את כל המידות בתכנית הקונסטרוקציה. במסלול של מידות או אי התאמה בתכנית /או בבנין, עליו להודיע על כך מיד לאדריכל בספר המשרד בעברותיו. המבצע יחשש או ויק בתכנית שאיננה לביצוע. המבצע יחזיק באחריות, בכל מה, על מידות של תכנית. אין לקבוע מידות על ידי מדידה בשטח. התכנית הנה תכנית האדריכל ואין לשנות כל שימוש בה או ברעיונות הגלומים בה, אלא באישור כותב תכנית האדריכל. המבצע יחזיק באחריות על המידות והתכנית. על המבצע והפיקוח לודא התאמה בתכנית האדריכלית - לביצוע תכנית זו. המבצע והתכנית האדריכלית על כל גורמים והחלטות. התכנית כוללת את כל האחריות והידוע על כל המידות.

משרד קירות:
קיר בלוק קיר בסון עמוד בסון

תאריך	תיאור	מהדורה
22.09.2025	מכרז	1

אדריכלות

שם המוסד: CLIENT NAME:

קבוצת רכישה נופיה

שם הפרויקט: PROJECT NAME:

נופיה - מגרש 16

שם הגליון: DRAWING NAME:

תכנית תקרה ותאורה

מספר גליון: SHEET NUMBER:

A3-1-400

תאריך: EDITION: קנה מידה: SCALE:

As indicated

סטטוס: STATUS: מוסמך


שורש ע"י: שורש ע"י: אלמוג אור

תאריך: DATE: 29.12.25



נתיס חיינו אדריכלים
מודל התהליך: 2. בית חירות
09-9545642

זכיות ייצור / ע"פ הנחיות ע"י

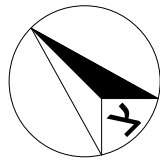

אודיו וידאו
רמקול באמצעות צינור פ.נ 16 מ"מ
רמקול שקוע בקיר. קופסה לפי תוכנית
רמקול שקוע בתקרה. קופסה לפי תוכנית

בטחון
מקלדת הפעלה
צופר אזעקה
גלאי נפח
גלאי יולון חיצוני

הנחיות


- יש לקרוא תוכנית זו בצד תוכנית מיזוג
- במקרה של אי התאמה יש לידע את האדריכל
- כל המידות הן למרכז אבזור אלא אם צוין אחרת
- מיקום האבזורים באיזורים משמעותיים מפורט בפרטים
- יש לתקדם בהתאם
- גובה התפוסקים הינו H=90 מ"מ אלא אם צוין אחרת
- בהתקנת מפתקים / מקלדת-אזעקה / פיקוד-מזג אחד מעל השני יש למרכז על ציר האמצע
- רווח של 5 ס"מ
- גובה התפוסקים הינו הביס.
- יש לידע את האדריכל
- גובה התפוסקים ביטאום מול האדריכל
- חוט אודיו: כל רמקול מעד בנפרד לאיזור הריכוז (מקום הריכוז)
- איש הקשר לאודיו בבית
- מפתק תנור חימום אמבטיה ומפתק דוד מים חשמלי H=150 ע"פ התקן
- גובה השקעים הינו H=40 אלא אם צוין אחרת
- גובה מנורות קיר הינו H=210 אלא אם צוין אחרת
- מנורות מעל מדרגות בגובה H=15 אלא אם צוין אחרת

תאורה
נקודת מאור חיצונית מהתקרה
נקודת מאור שקועה בתקרה
נקודת מאור שקועה בתקרה מוגנת מים
נקודת מאור שקועה ברצפה מוגנת מים
נקודת מאור בתקרה עם מאוורר
מאוורר תקרה
נקודת מאור על הקיר
נקודת מאור מוגן מים על הקיר
נקודת מאור שקועה בקיר
נקודת מאור מוגן מים שקועה בקיר
פס צבירה שקוע בתקרה כולל גופי תאורה
פס צבירה על התקרה כולל גופי תאורה
דוד תכליתי
תאורת חירום
נקודת מאור ספוט
נקודת מאור ספוט - מוגנת מים

שקעים ואבזורים
בית תקע
בית תקע כוח
בית תקע מוגן מים
נקודת טלפון
נקודת אינטרנט
נקודת תנור אמבטיה
נקודת טל"כ / לוויין
נקודת הזנה למנוע תריס חשמלי
נקודת הפעלה לתריס חשמלי
נקודת הזנה למנוע ונטה חשמלי
צינור שרשרתי 15 מ"מ עם חוט משיכה
נקודת אינטרקום
נקודת אינטרקום טלוויזיוני
פעמון דירתי תקני 12V
H=40 סימבוסק אלא אם צוין אחרת

מקרא חשמל ותאורה

לחצנים ופקידים
מפתק חד קוטבי למאור
מפתק חד קוטבי למאור עם דימר
מפתק מחליף למאור
מפתק מחליף למאור עם דימר
מפתק לזונטה
מפתק לזיילר / תנור חימום באמבטיה
לחצן פעמון
לחצן מדרגות פוספורי
מפתק בטחון ביולר
מפתק בטחון ליחידת מ"א
ארון חשמל תה"ט עם דלת K.O=200
ארון תקשורת
קיום עולים
קיום יורדים

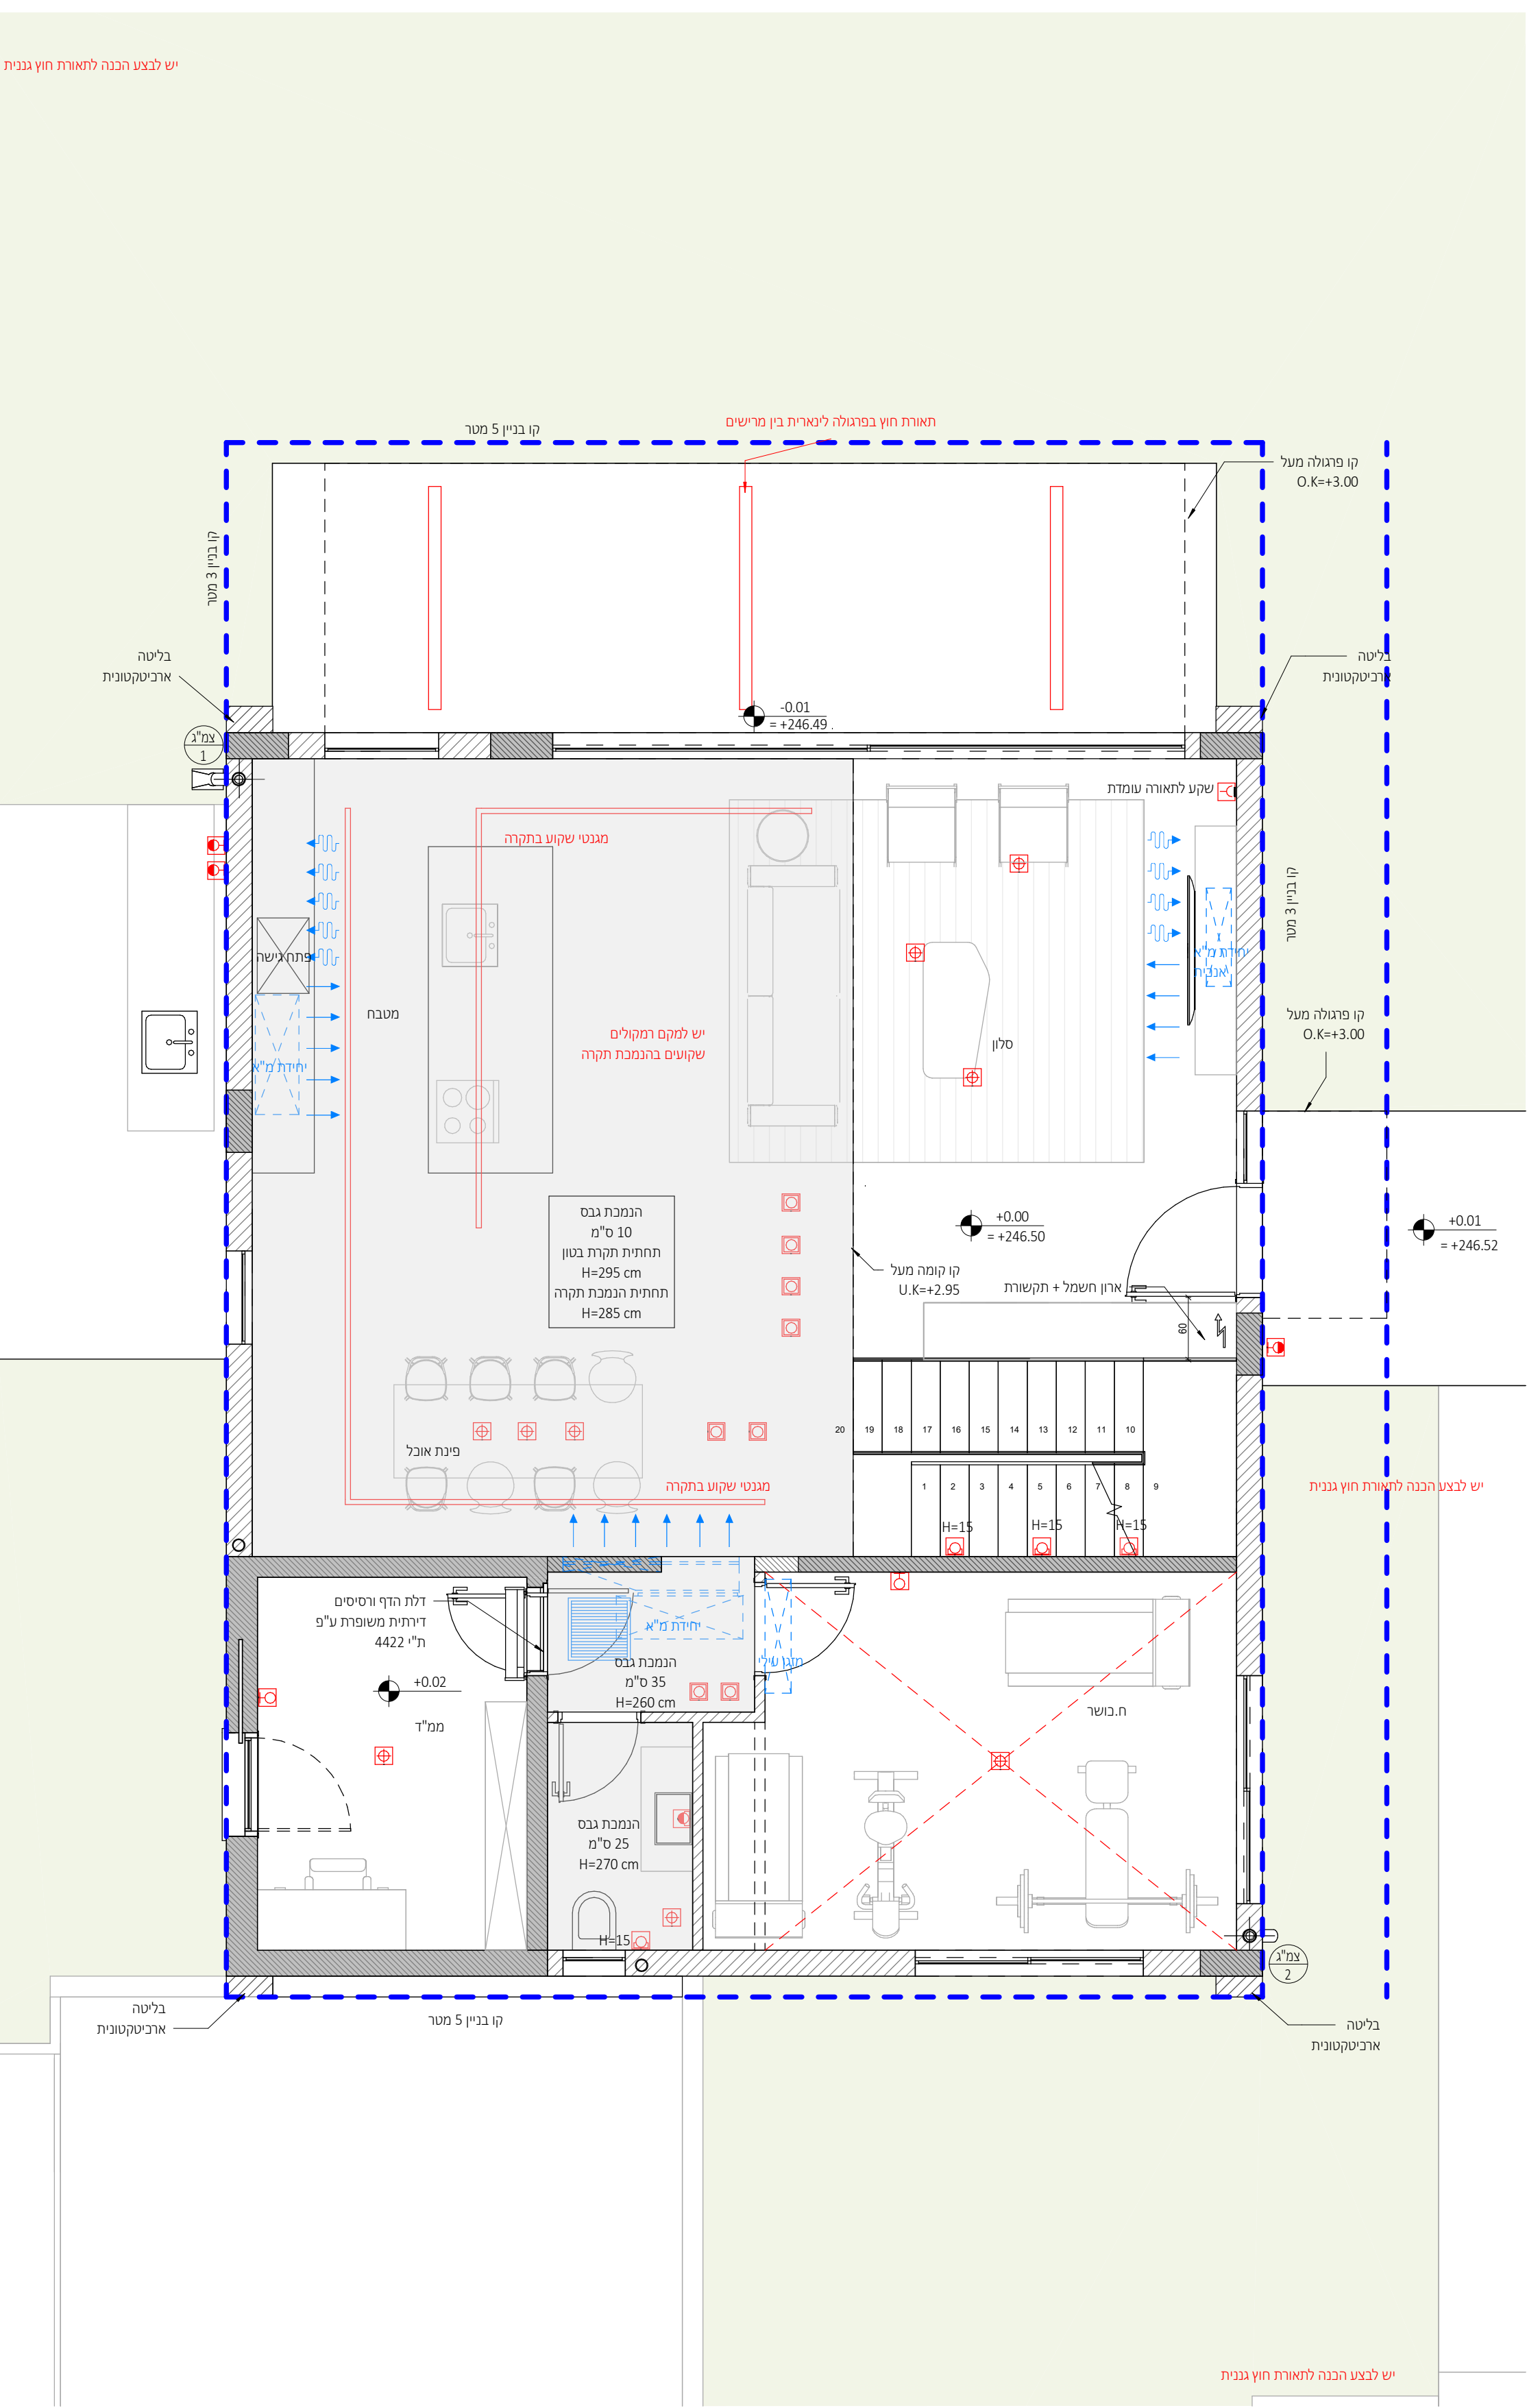

תכנית תקרה ותאורה - קרקע

1 : 50


- תכנית חשמל - תהיה עפ"י גליון של יועץ חשמל.
- תכנית תאורה, מיקום גופי תאורה - עפ"י גליון זה.
- יש לעבוד במקביל לתכנית של מתכנן מיזוג אוויר, ובתיאום מול אדריכל.
- מידות סופיות בין גופי תאורה יתנתן לאחר בחירה סופית של הדגמים.
- מיזוג אוויר - מיקום התקנת יחידות ומיקום תריסים, פתחי שירות - לתיאום סופי מול אדריכל לפני ביצוע.
- חימום תת רצפתי עפ"י פרטי הספק ובתיאום מול אדריכל.

מתכננים:

ניהול פרויקט
בן סולומון - מהיסוד
פיקוח
בן סולומון - מהיסוד
קונסטרוקציה
ערן שילר
מיזוג אוויר
אייל ארז מהנדסים ויועצים בע"מ
אינסטלציה
איתן אלמסי
חשמל
איתן בסיס
אלומיניום
נוף
נתי בלוקא
חשמל חכם
חימום תת רצפתי
איטום
צבי טל
אקוסטיקה
מעליות
קרקע וביסוס
דיה הנדסת קרקע וביסוס
רישוי

± 0.00 = +246.50
הערות: 1. תכנית זו יש לקרוא יחד עם תכנית הרושפים. 2. גובה אבטמנטיים: ראו תכנית פיתוח. 3. הפירות הן בין קירות הבניה ולא כולל פיתח. 4. פיתוח השטח סביב המבנה, כולל, מדרגות, גדרות, שבילים, ריצופים, שטחים גזרים, חניה וגן ראו תכנית פיתוח. 5. איטום קירות ורצפות המבנה כמעט עם הקרקע ובידוד תרמי לאורך העמודים והקירות נגד התקרות. כליות או עם סימני גימון- ראו תכנית קונסטרוקציה. 6. אף דום יבוצע בכל מישור אופקי הכולל חתוכי. 7. סיוח תרמי במסגרת ע"פ מפרט תרמוקור, מאושר ע"י פיקוד העורף. המבצע אחראי לסידור: עליו לבקר ולבדוק את כל המידות בתכנית ובקטע העבודה. במסגרת של מידות או את התאמה בתכנית /או בבנוי, עליו להודיע על כך מיד לאדריכל בסיום המשיך בעבודתו. המבצע יחזיק את ריק בתכנית שאושר לכניס. המבצע יחזיק אתה, בכל מה, של מידות של תכנית. אין לקבוע מידות על ידי חזירה בשו"מ. התכנית היתה רחבה האדריכל ואין לשנות כל שימוש בה או ברעיונות הגולמים בה, אלא באישור בכתב מהאדריכל. מומנים /או יועץ אשר שמו רשום בתכנית זו, נושא לכך באחריות המקצועית והתקנית לתכנית. על המפקח והמבצע לזרז את התאמת התכנית האדריכלית "לכניס" לתכנית הינה, המכר והתכנית המאושרות ע"י כל הגורמים הרשמיים. התכנית כוללת את כל האמצעים והידוע עד ליום תחלתה.

משרד קירות:

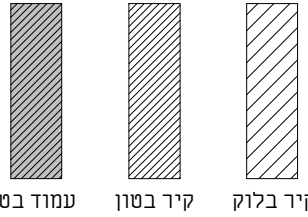

תאריך	תיאור	מהדורה
22.09.2025	מכרז	1

אדריכלות

שם המסמך:	CLIENT NAME:
קבוצת רכישה נופיה	
שם הפרויקט:	PROJECT NAME:
נופיה - מגרש 16	
שם הגיליון:	DRAWING NAME:
חזיתות 2	
מספר גיליון:	SHEET NUMBER:
A3-2-201	
תחבורה:	EDITION:
קנה מידה:	SCALE:
1 : 50	
סטוס:	STATUS:
למכרז	
שורשים ע"י:	אולמו אור
תאריך:	DATE:
29.12.25	

NeumanHaynerArchitects


נוימן חיינר אדריכלים
מחזור החדשים 2, בית חירות
09-9545842 78

office@nh-arch.com
www.nh-arch.com

זכיות ייצור / ע"פ הנחיות ע"ד


פיתוח נוף עפ"י תוכניות
יועץ נוף ראה פירוט בנפרד

פיתוח נוף עפ"י תוכניות
יועץ נוף ראה פירוט בנפרד

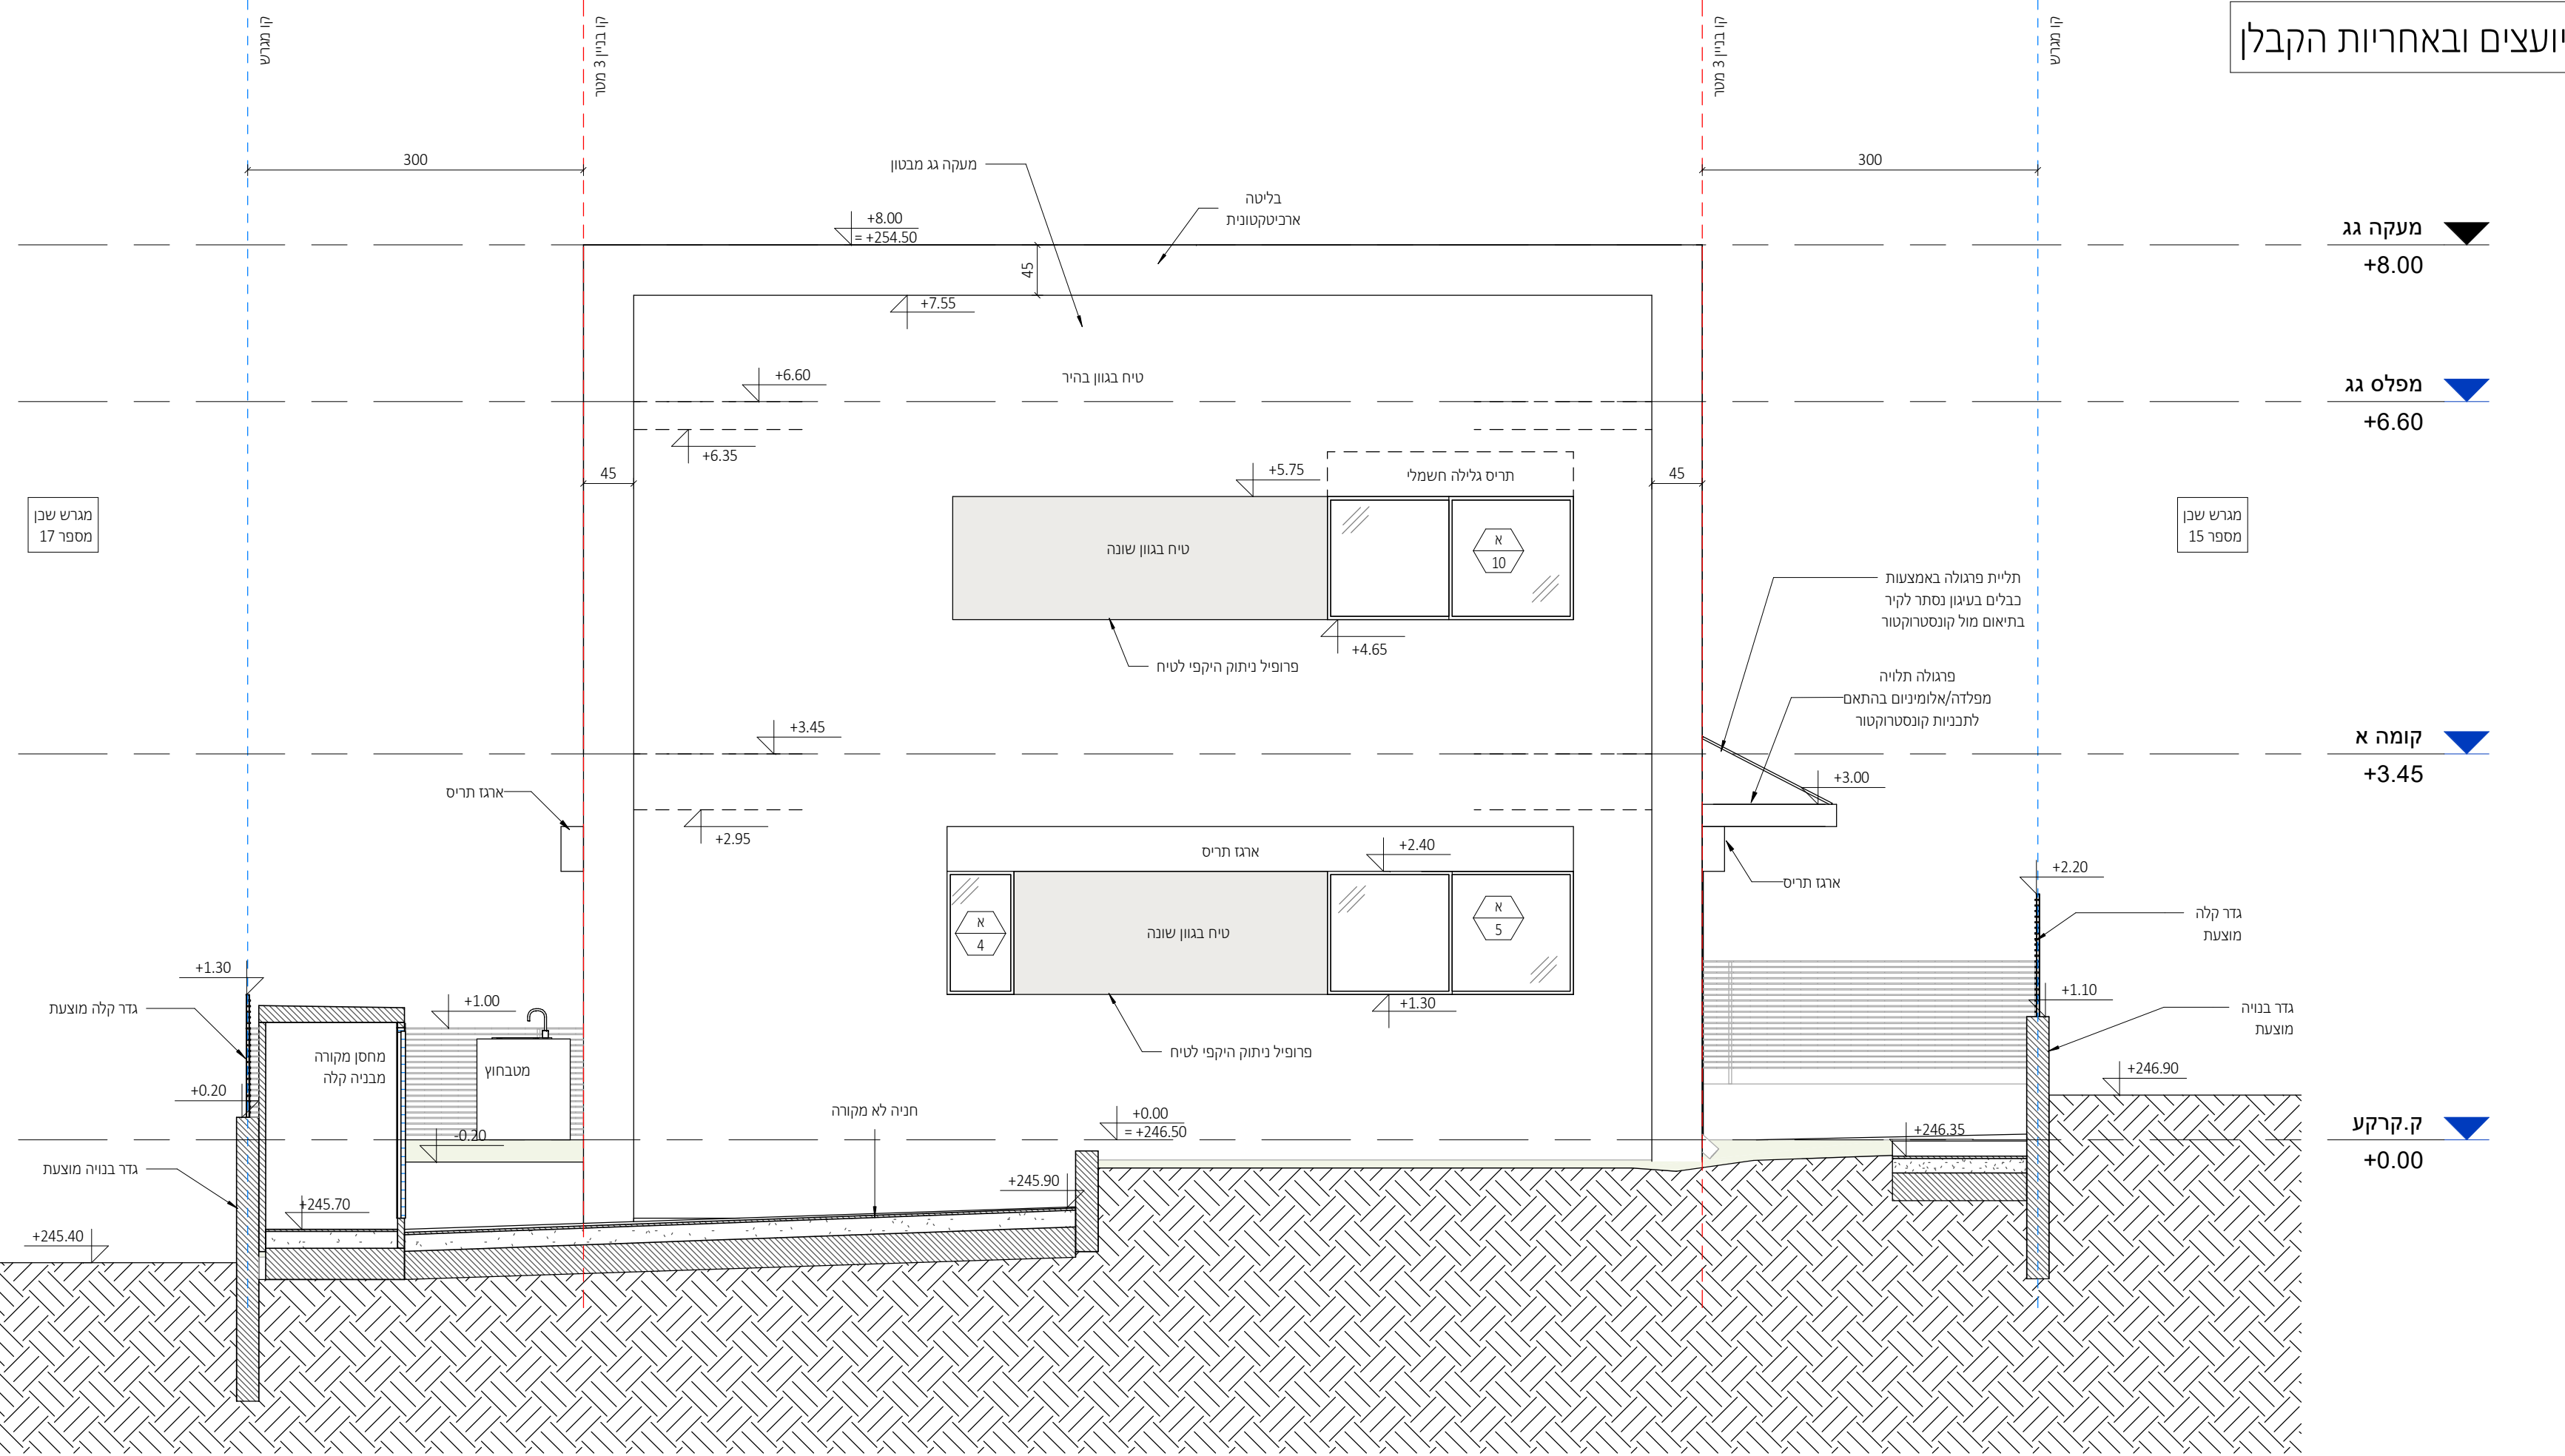

חזית צפונית

1 : 50

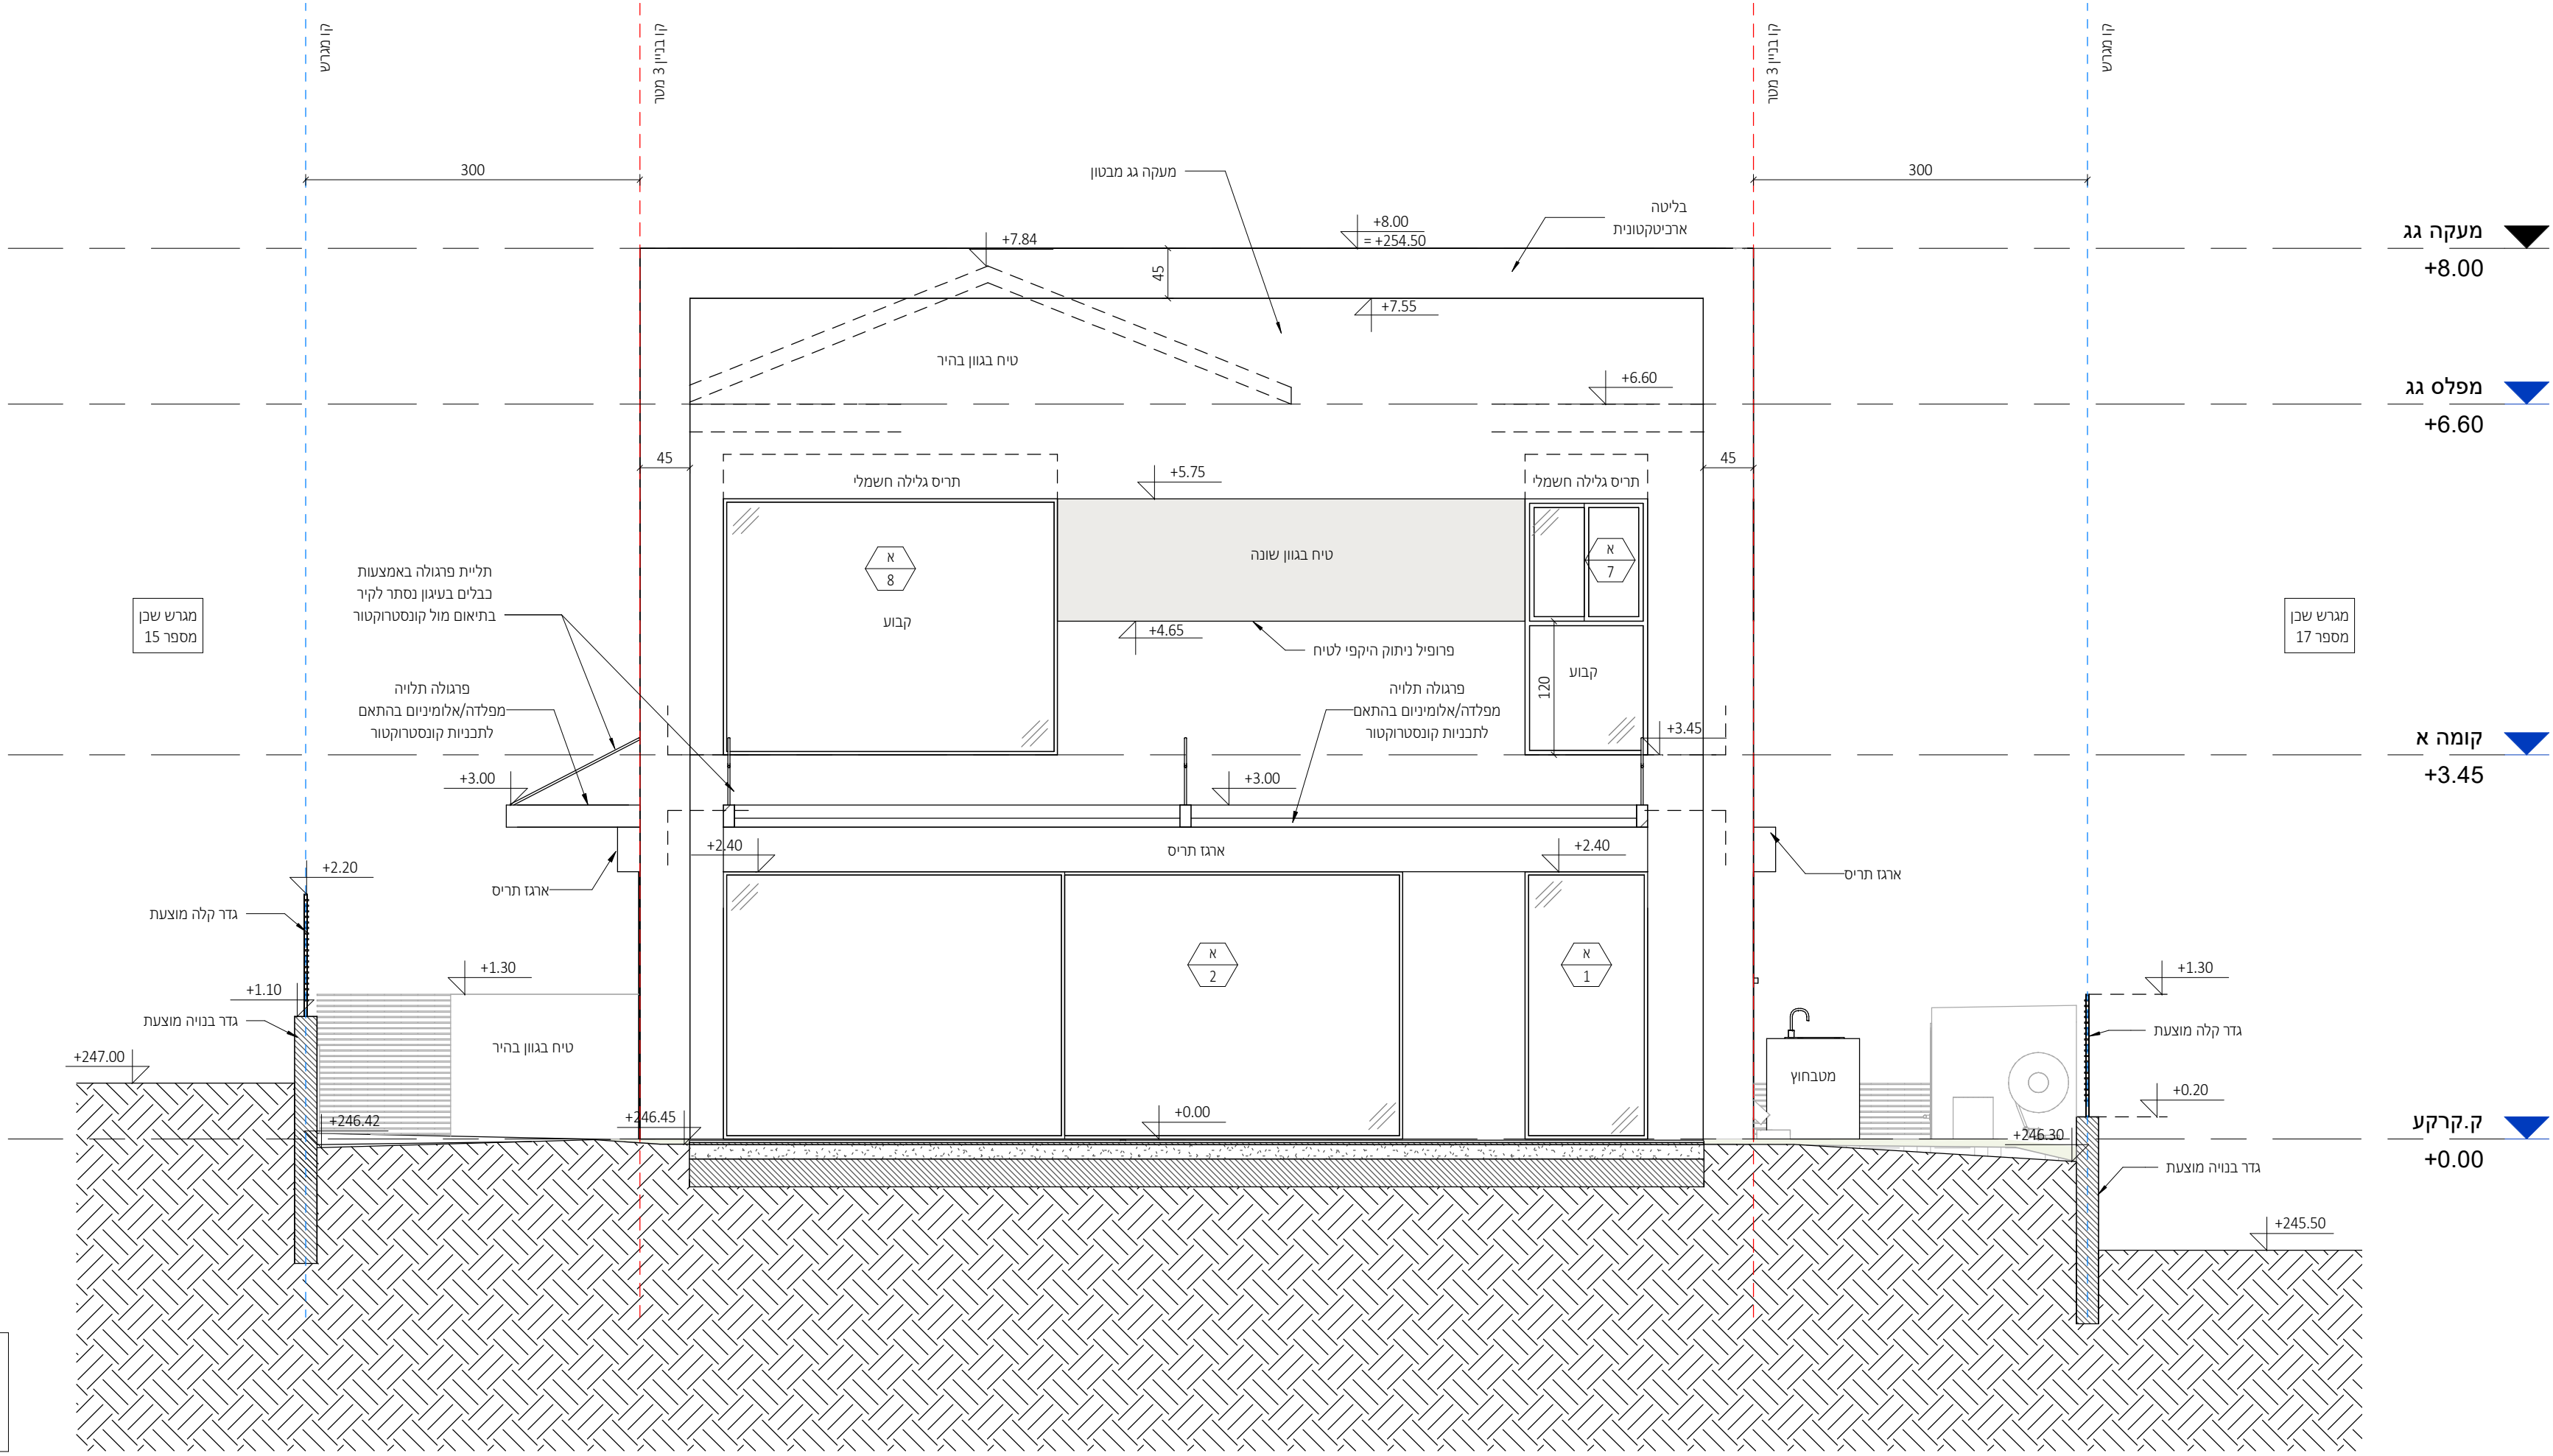

חזית דרומית

1 : 50

מתכננים:

ניהול פרויקט
בן סולומון - מהיסוד
פיקוח
בן סולומון - מהיסוד
קונסטרוקציה
ערן שילר
מיזוג אוויר
אייל ארז מהנדסים ויועצים בע"מ
אינסטלציה
איתן אלמסי
חשמל
איתן בסיס
אלומיניום
נוף
נתי בלוקא
חשמל חכם
חימום תת רצפתי
איטום
צבי טל
אקוסטיקה
מעליות
קרקע וביסוס
דיה הנדסת קרקע וביסוס
רישוי

± 0.00 = +246.50

- הערות:
- תכנית זו יש לקרוא יחד עם תכניות הרושפים.
 - גובה אבטומיטי - ראה תוכנית פירוט.
 - הפירות הן בין קירות הבניה ולא כולל פחים.
 - פיתוח השטח סביב המבנה, כולל, מדרגות, גדרות, שבילים, ריצופים, שטחים גרושים, חניה וגן ראו תכנית פירוט.
 - איטום קירות ורצפות המבנה כמעט עם הקרקע ובדיווח תחילי לאור העומדים והקורות של התכנית. כליות או עם סימני גיבוי - ראו תכנית קונסטרוקציה.
 - אף דים יבוצע בכל מישור אופקי הכולל מחבנין.
 - פוח דומי במסגרת - ע"פ מפרט חומרים, מאושר ע"י פיקוח הנדסה.

המבצע אחראי למידות: עליו לבקר ולבדוק את כל המידות בתכנית ובמקום המבנה.
במסגרת של מידות או אי התאמה בתכנית /או בבנין, עליו להודיע על כך מיד לאדריכל בסיום המשיך בעבודתו.
המבצע יתחשב או ויק במוכנות שאושרו לכניסיו.
המבצע יחזיק באחריות, בכל מה, של מחדש של תכנית.
אין לקבוע מידות על ידי מדידה בשטח.
התכנית היתה רכוש האדריכל ואין לשמש כל שימוש בה או ברעיונות הגלומים בה, אלא באישור בכתב מהאדריכל.
מחנדים וא/י רשע אשר שמו רשות בתכנית זו, ונשא לכך באחריות המבצעים והתקנים לתכנית.
על המפקח והמכיל לודא התאמת התכנית האדריכלית "לכניסיו" לתכנית. יתרה, המכר והתכנית והאישות ע"י כל גורמים ורשמיים.
התכנית כוללת את כל האחריות והידוע על ליום תחלפת.


משרד קירות:

קיר בלוק
קיר בסון
מחוז בסון

תאריך	תיאור	מהדורה
22.09.2025	מכר	1


אדריכלות

שם המסין:	CLIENT NAME:
קבוצת רכישה נופיה	
שם הפרויקט:	PROJECT NAME:
נופיה - מגרש 16	
שם הגיליון:	DRAWING NAME:
חתכים	
מספר גיליון:	SHEET NUMBER:
A3-3-100	
מחזור:	EDITION:
קנה מידה:	SCALE:
1 : 50	
סטוס:	STATUS:
למכר	
שורשים ע"י:	אולמו אור
נבדק ע"י:	
תאריך:	DATE:
29.12.25	

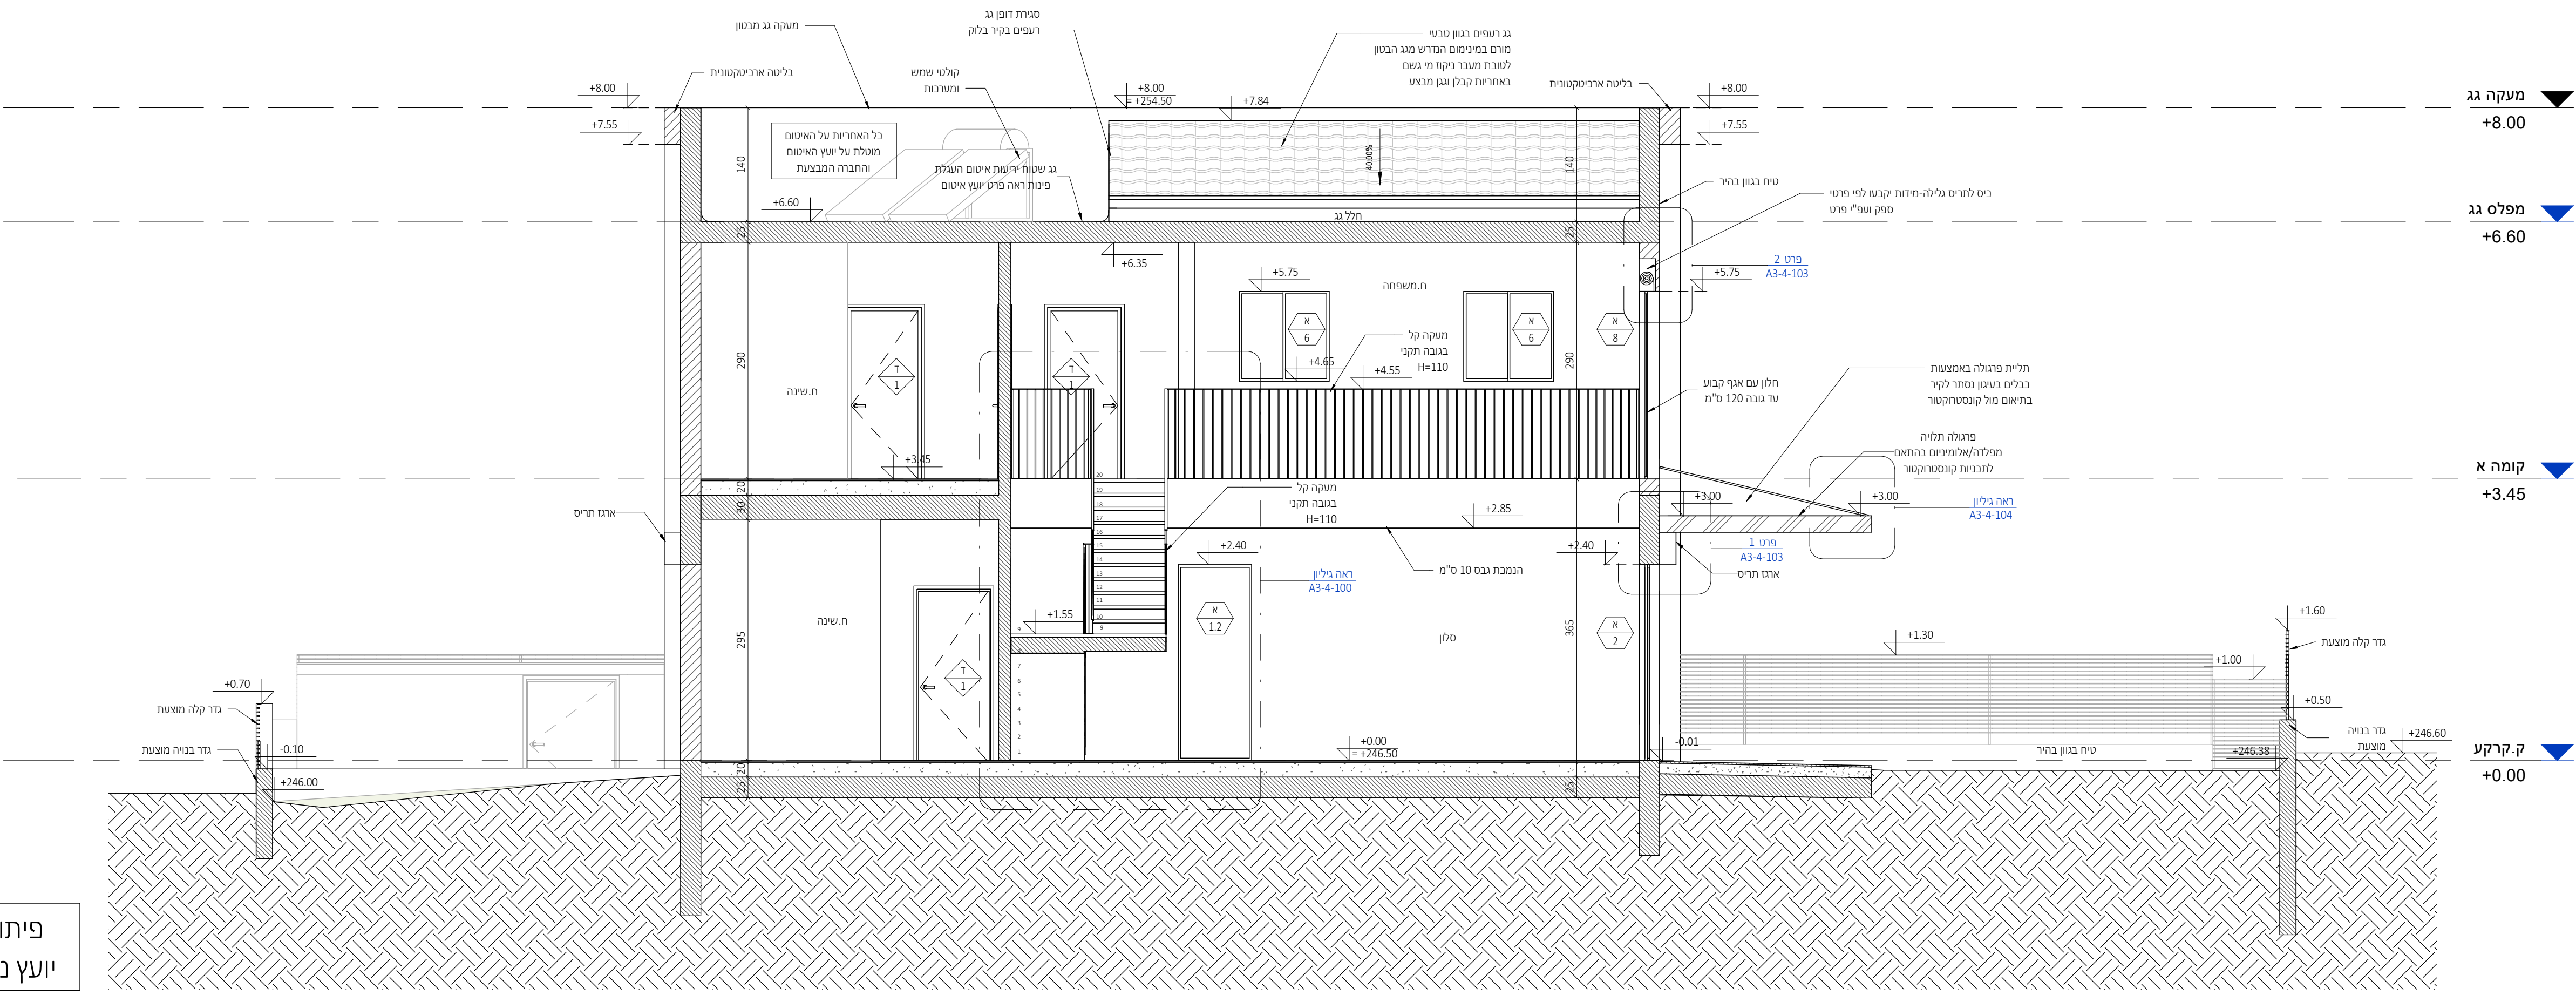

חתך א-א

1 : 50

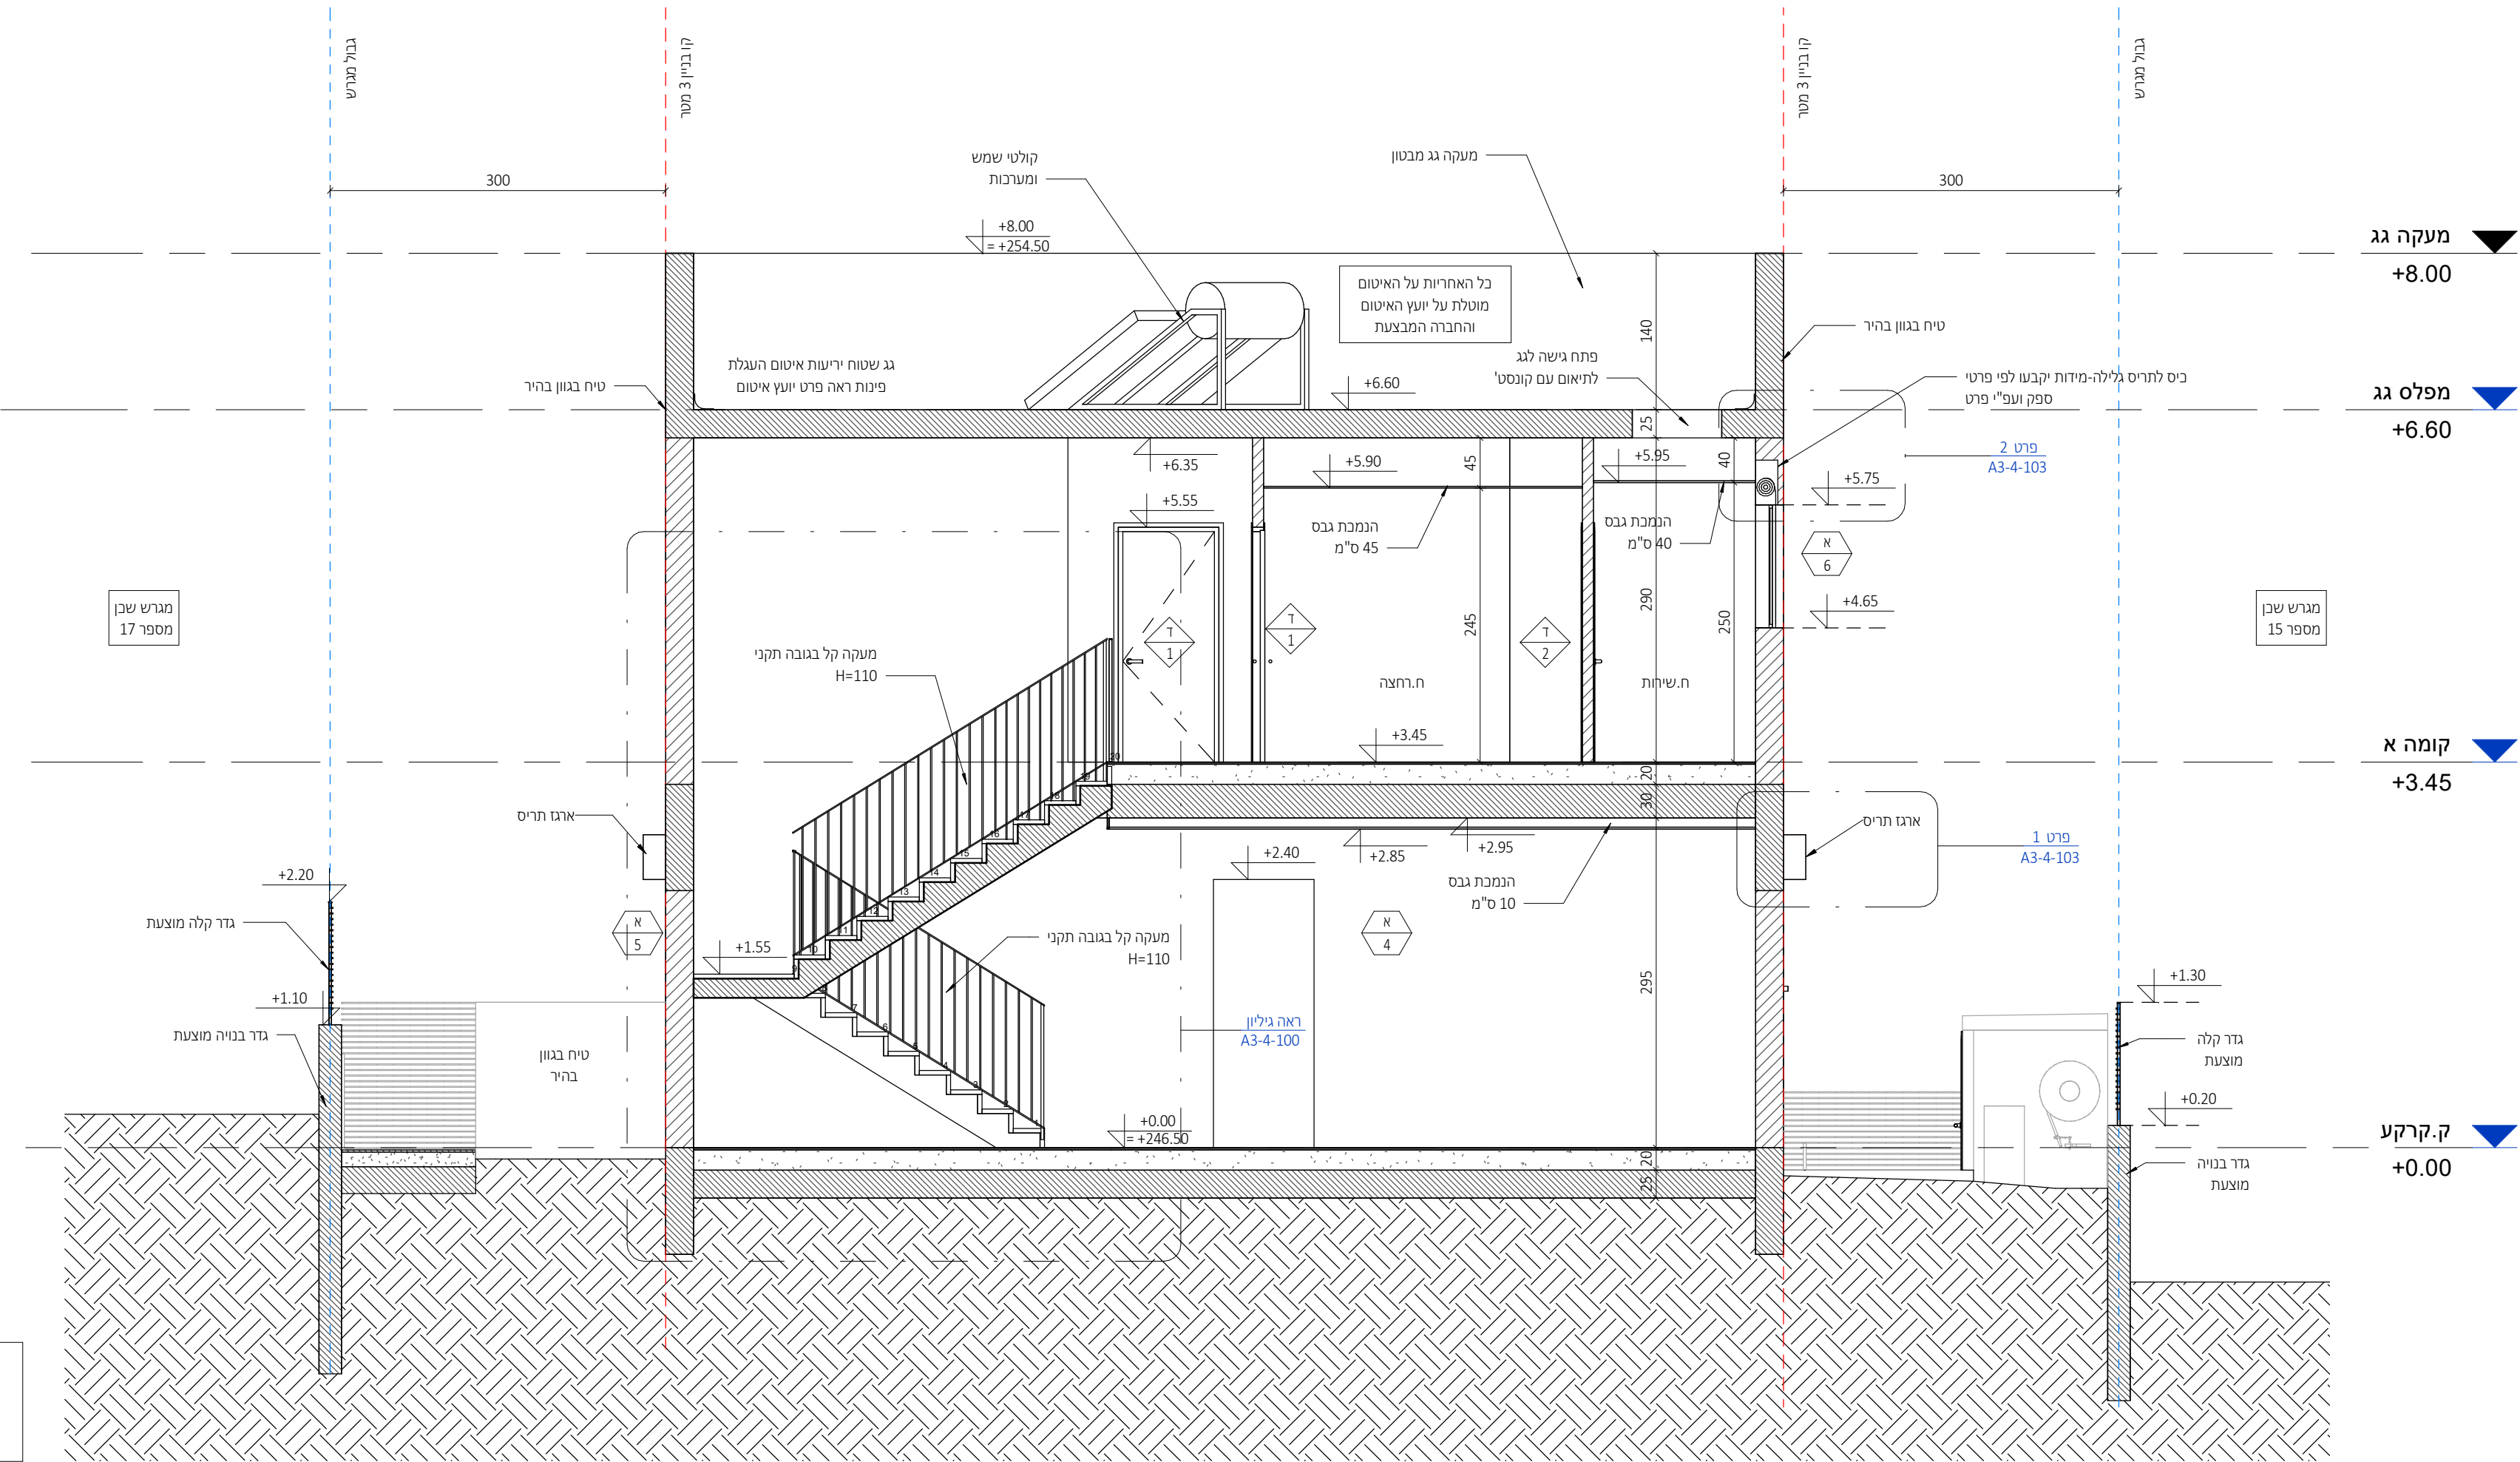

חתך ב-ב

1 : 50



	ניהול פרויקט
בן סולומון - מהיסוד	פיקוח
בן סולומון - מהיסוד	קונסטרוקציה
	ערן שילר
	מיזוג אוויר
אייל אורז מהנדסים ויועצים בע"מ	אינסטלציה
	איתן אלמסי
	חשמל
	איתן בסיס
	אלומיניום
	נוף
	נתי בלוקא
	חשמל חכם
	חימום תת רצפת
	איטום
	צבי טל
	אקוסטיקה
	מעלות
	קרקע וביסוס
דיה הנדסת קרקע וביסוס	רישוי

מקרא קירות:



עמוד בטון קיר בטון קיר בלוק

אדריכלות החומר: קבוצת רכישה נופיה	
הפרויקט: נופיה - מגרש 16	
השכמה: גליון מדרגות	
המספר: A3-4-100	
המקור: As indicated	הגרסה: 1
הסטוס: למכר	הסטוס: אלמנח אור
התאריך: 29.12.25	התאריך:

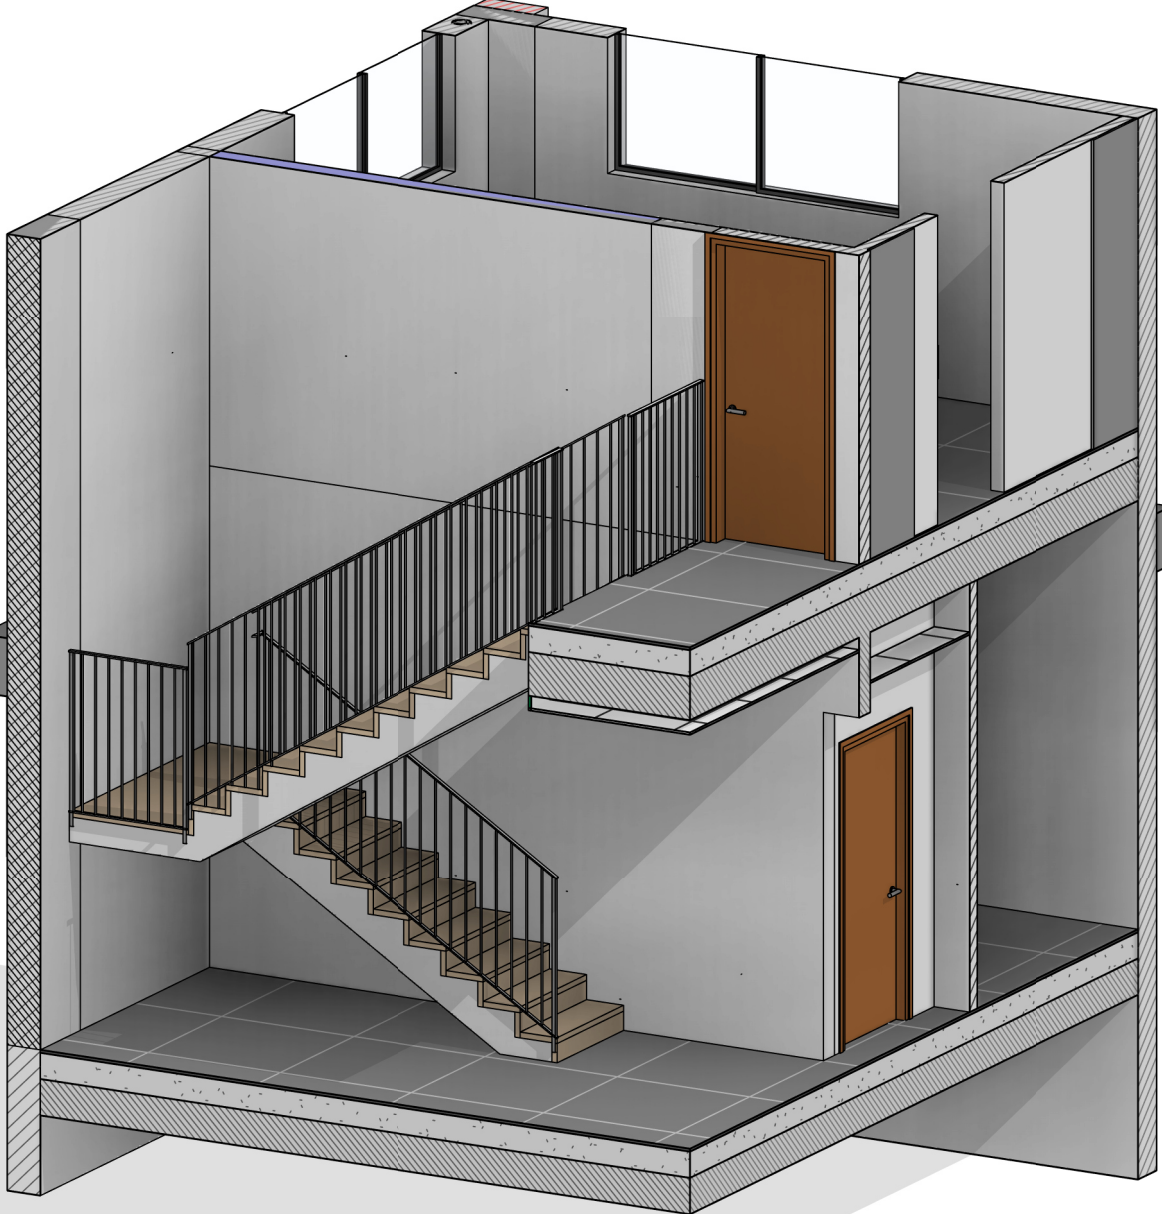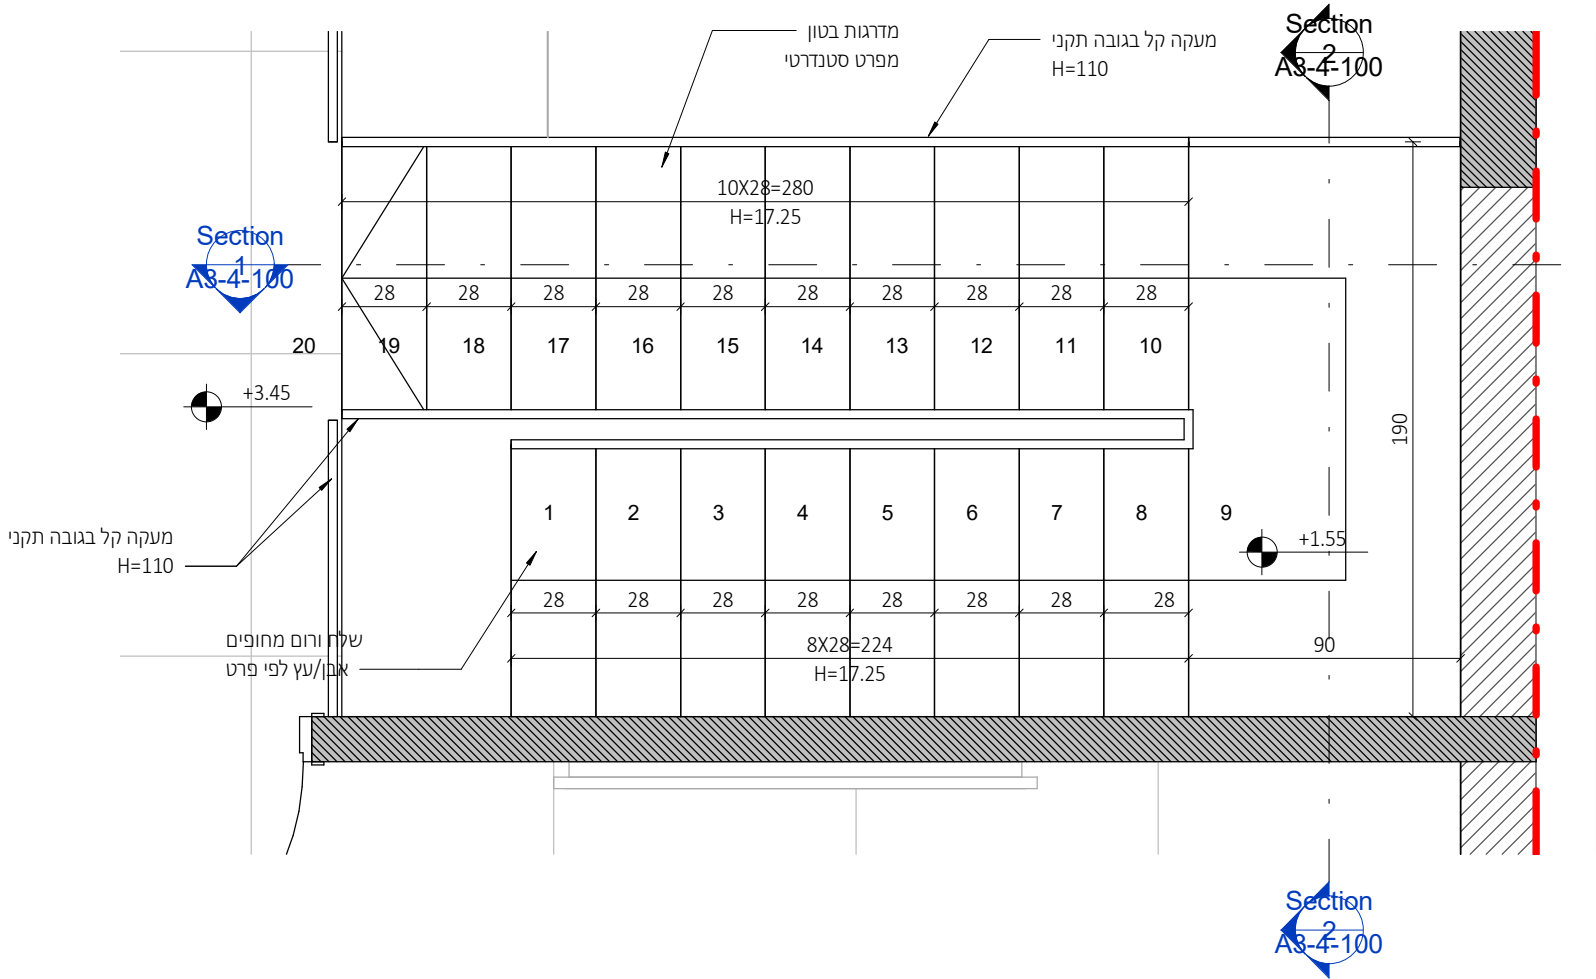12/29/2025 3:39:27 PM

1 : 25


מתכננים: ניהול פרויקט בן סולומון - מהיסוד פיקוח בן סולומון - מהיסוד קונסטרוקציה ערן שילר מיזוג אוויר אייל ארז מהנדסים ויועצים בע"מ אינסטלציה איתן אלמסי חשמל איתן בסיס אלומיניום בופ נתי בלוקא חשמל חכם חימום תת רצפתי איטום צבי טל אקוסטיקה מעליות קרקע וביסוס דיה הנדסת קרקע וביסוס רישוי


± 0.00 = +246.50 הערות: 1. תכנית זו יש לקרוא יחד עם תכנית הריטשים. 2. גובה אבטומיטי: ראו תכנית פיתוח. 3. המידות הן בין קירות הבניה ולא כולל פחים. 4. פיתוח השטח סביב המבנה, כולל, מדרגות, גדרות, שבילים, ריצופים, שיפועים, גדרים, חניה גינה וראו תכנית פיתוח. 5. איטום קירות ורצפות המבנה כמנוע עם הקרקע ובידוד תרמי לאורך העמודים והקורות וכל המפרקים. כלירות או עם סימני גיבסן. ראו תכנית קונסטרוקציה. 6. אף מים יבוצעו בכל מישור אופקי הכולל מהגבון. 7. סחי תרמי בממד"ד - ע"פ מפרט תומקיר, מאושר ע"י פיקוד העורף. המבצע אחראי לסידות : עליו לבקר ולבדוק את כל המידות הבחנית והקטום המבוצה. במסגרת של מנות או אי התאמה בתכנית /או בבנין, עליו להודיע על כך מיד לאדריכל בסופו המשיך בעבודתו. המבצע ישתמש או ורק בתכנית שאושרו לכניסו. המבצע יחזיק באחר, בכל מה, של מחדכן של תכנית. את לקבוע מידות של ידי חזירה בשו"ס. התכנית הנה רכוש האדריכל ואין לשנות כל שימוש בה או ברעיונות הגלומים בה, אלא באישור בכתב מהאדריכל. מחדס /או יועץ אשר שמו רשום בתכנית זו, נושא לכיד באחריות המקצועית והטכנית לתכנית. על המפקח והמכני לודא התאמת התכנית האדריכלית "לביצוע" לתכנית זוהי, המכר והתכנית המאושרות ע"י כל הגורמים הרשמיים. התכנית כוללת את כל האמצעים והידוע עד ליום תחלתה. משרד קירות: קיר בלוק קיר בסון עמוד בסון


אדריכלות שם המסמך: CLIENT NAME: קבוצת רכישה נופיה שם הפרויקט: PROJECT NAME: נופיה - מגרש 16 שם הגליון: DRAWING NAME: פרטים מספר גליון: SHEET NUMBER: A3-4-103 מחזורית: EDITION: SCALE: קנה מידה: As indicated סטוס: סטוס: למכר שורסס ע"י: אלמוג אור תאריך: DATE: 29.12.25  ניומן חיינר אדריכלים מודד והנדס 2, בית חירות 09-9545842 78 ניומן חיינר אדריכלים office@nh-arch.com www.nh-arch.com
--


12/29/2025 3:39:29 PM


זכיות ייצור / ע"פ הנחיות ע"ד

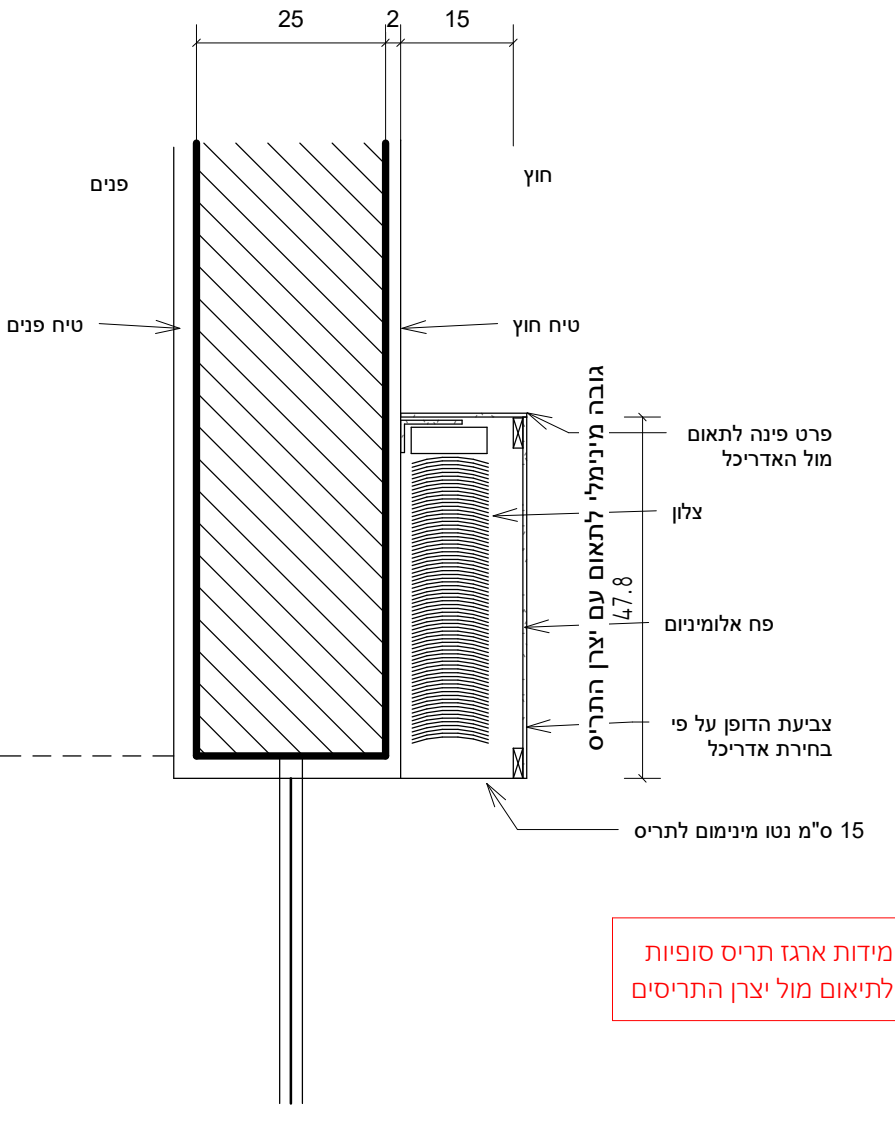
 מידות ארגז תריס סופיות לתיאום מול יצון התריסים פרט 1- כיס צלון חיצוני 1 : 10

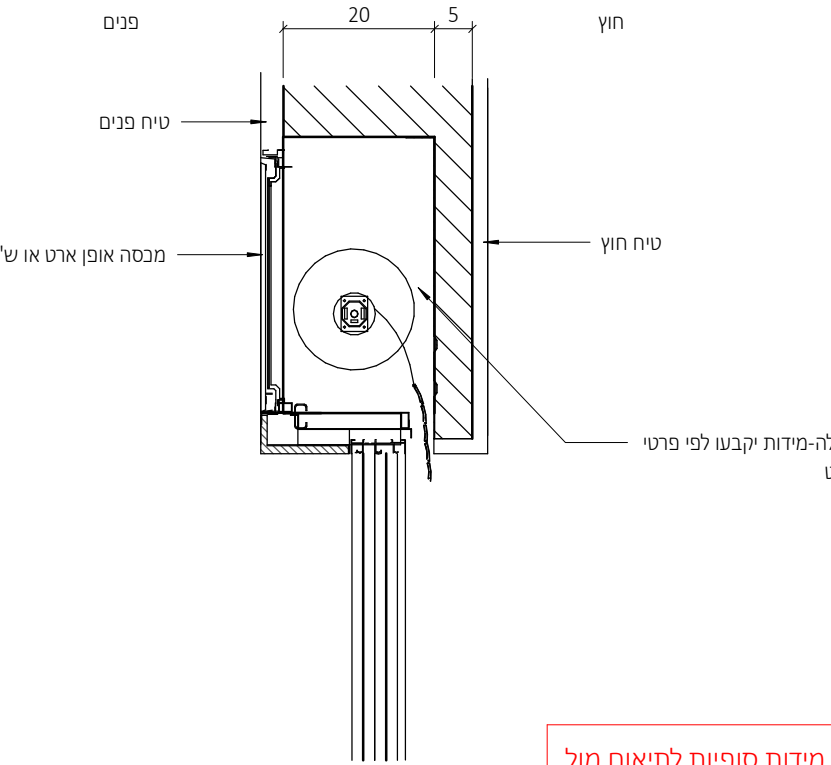 מידות סופיות לתיאום מול יצון התריסים פרט 2- תריס גלילה 1 : 10
--

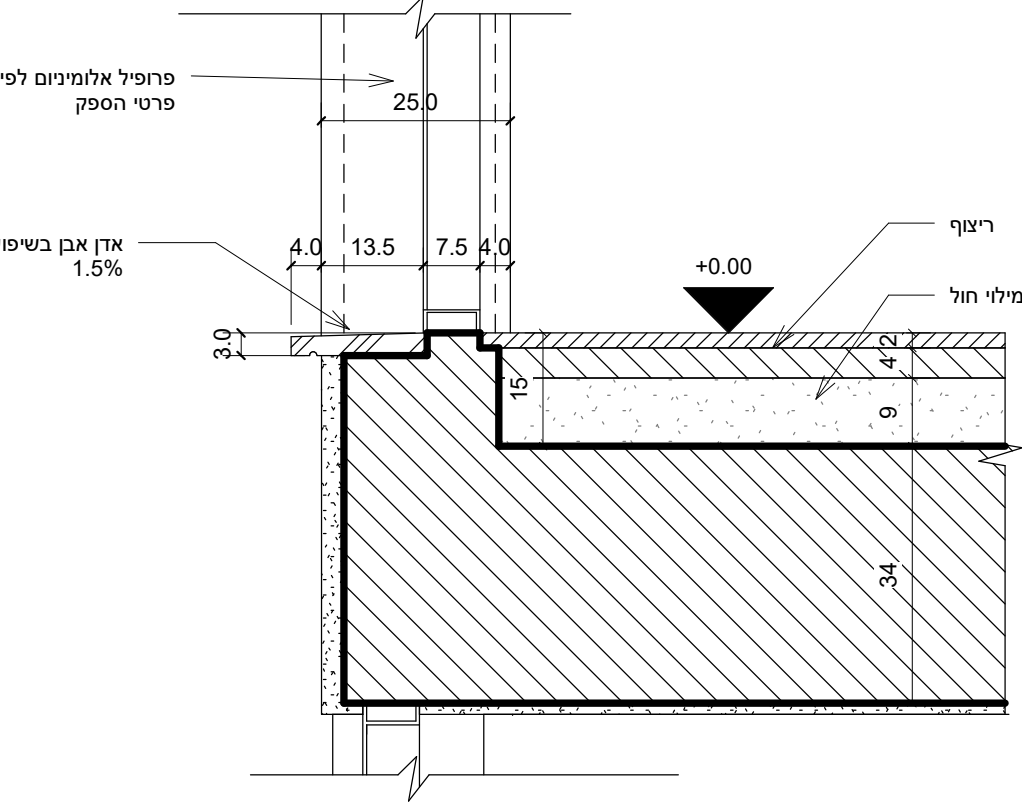 הערה: פרטי האיטום הם עקרוניים בלבד כל האחראיות על האיטום מוטלות על יועץ האיטום החברה המבצעת יש לעבוד לפי פרטי האיטום של יועץ הפרויקט. גובה החלון המופיע בתכנית מצוין את פני סף האבן. יש להנמיך את הבטון בהתאם פרט עקרוני בלבד - פרט סופי מספק החלונות פרט 3- מפגש חלון ורצפה 1 : 10
--

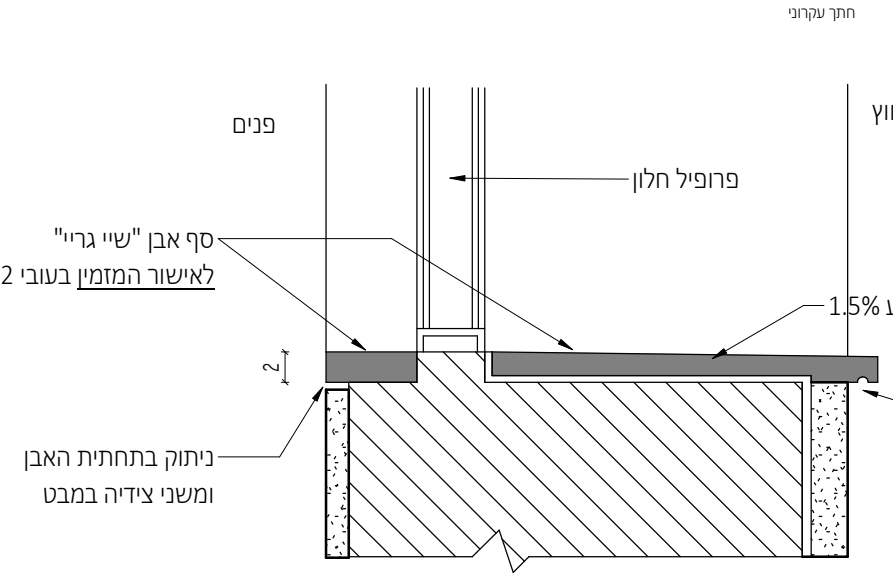 הערה: פרטי האיטום הם עקרוניים בלבד כל האחראיות על האיטום מוטלות על יועץ האיטום החברה המבצעת יש לעבוד לפי פרטי האיטום של יועץ הפרויקט. גובה החלון המופיע בתכנית מצוין את פני סף האבן. יש להנמיך את הבטון בהתאם פרט עקרוני בלבד - פרט סופי מספק החלונות פרט 4- חלון - פרט טיפוסי - סף חלון 1 : 5

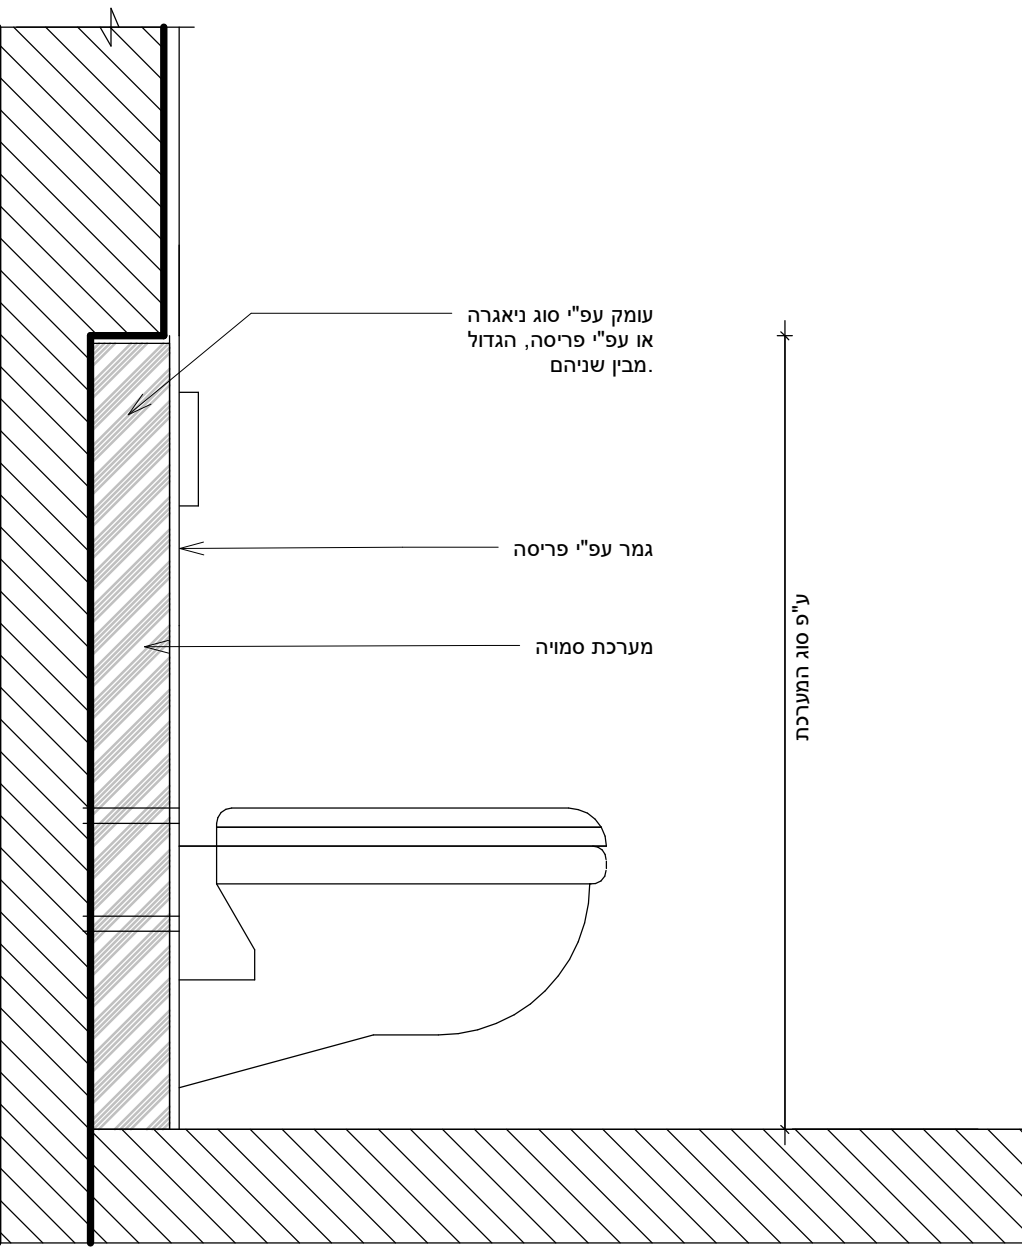 פרט 5- אסלה תלויה בקיר 20 1 : 10
--

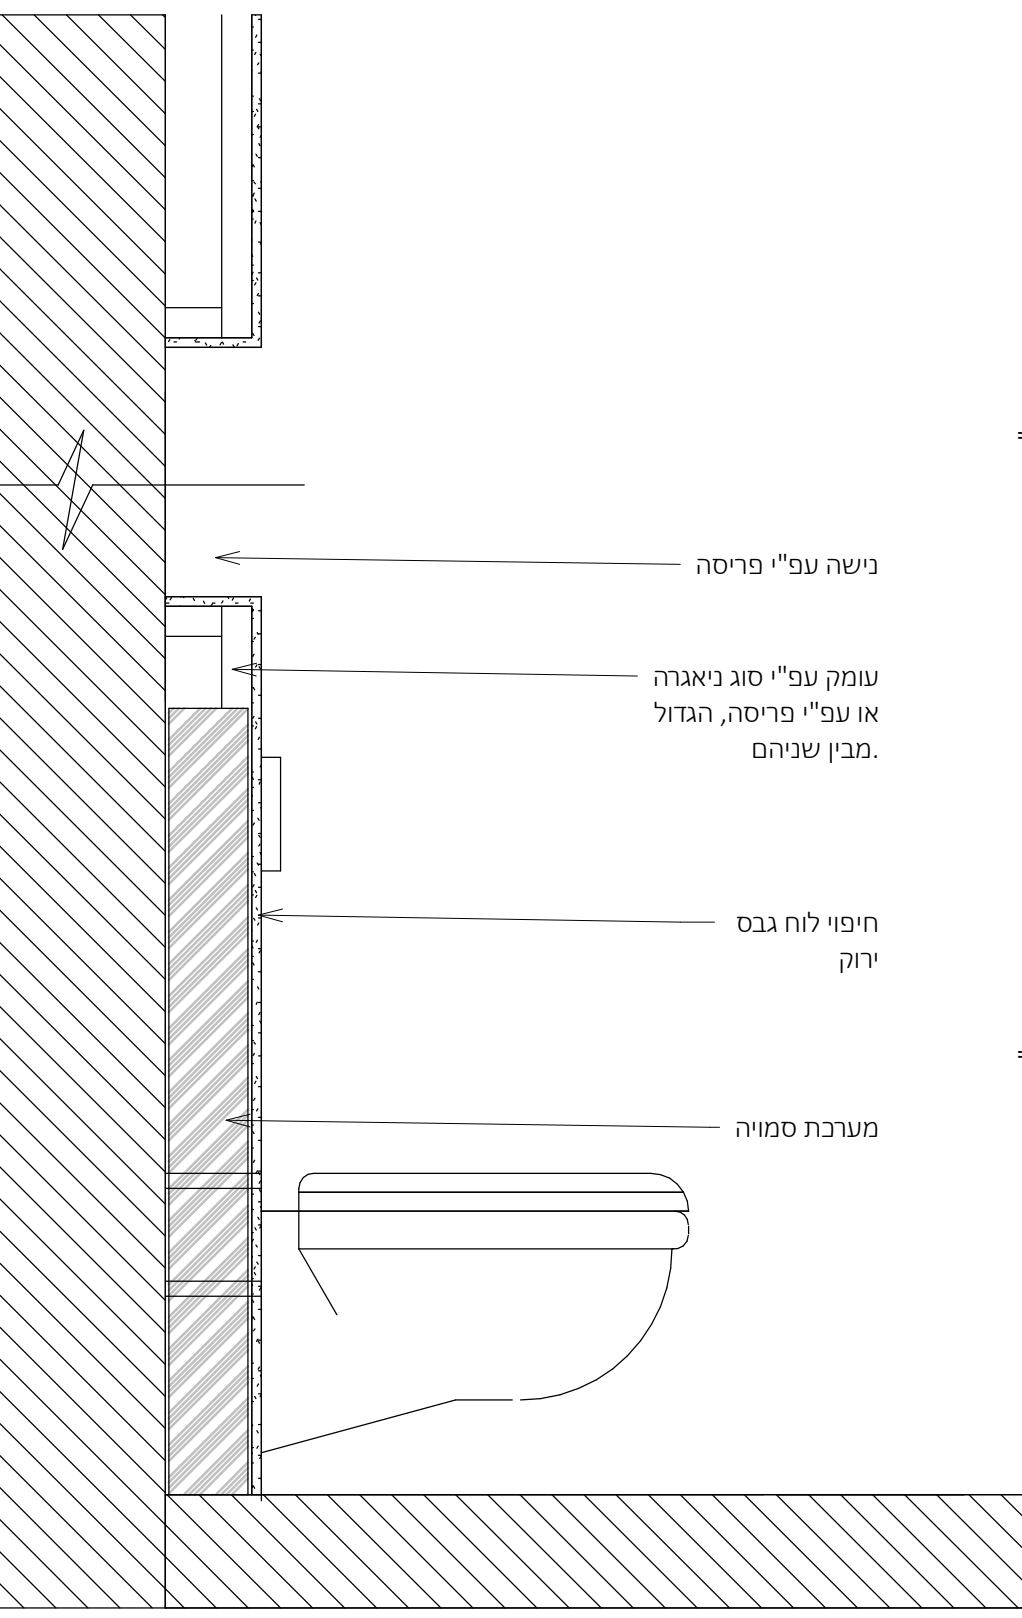 פרט 6-אסלה תלויה מנגנון סמוי בעיבוי גבס 1 : 10
--

יש לעבוד במקביל לפרטים שסיפק מעצב הפנים (במידה וקיים במגרש זה) המאושרות על ידי האדריכל.

פרטי האיטום באחריות יועץ האיטום ראה חוברת פרטי איטום מצורפת


להמשך תיאום

פרגולת אלומיניום




תמונה להמחשה בלבד

להמשך תיאום

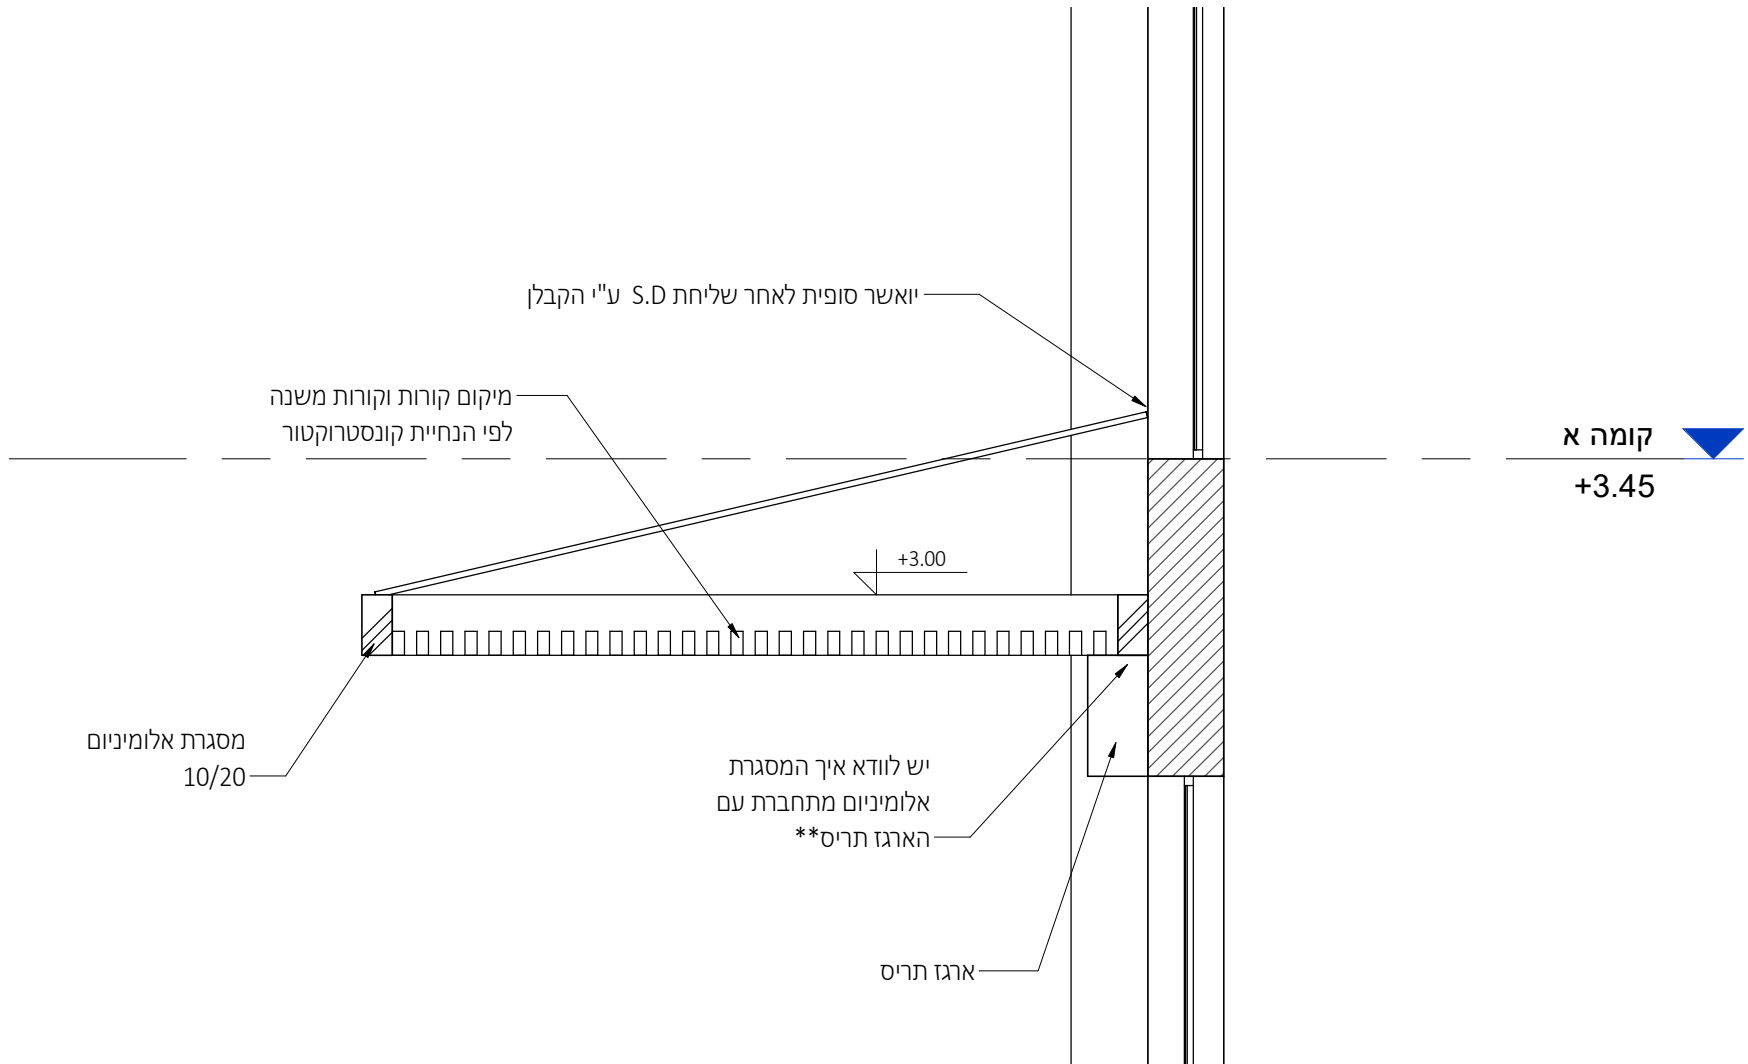


Section 3

1 : 25

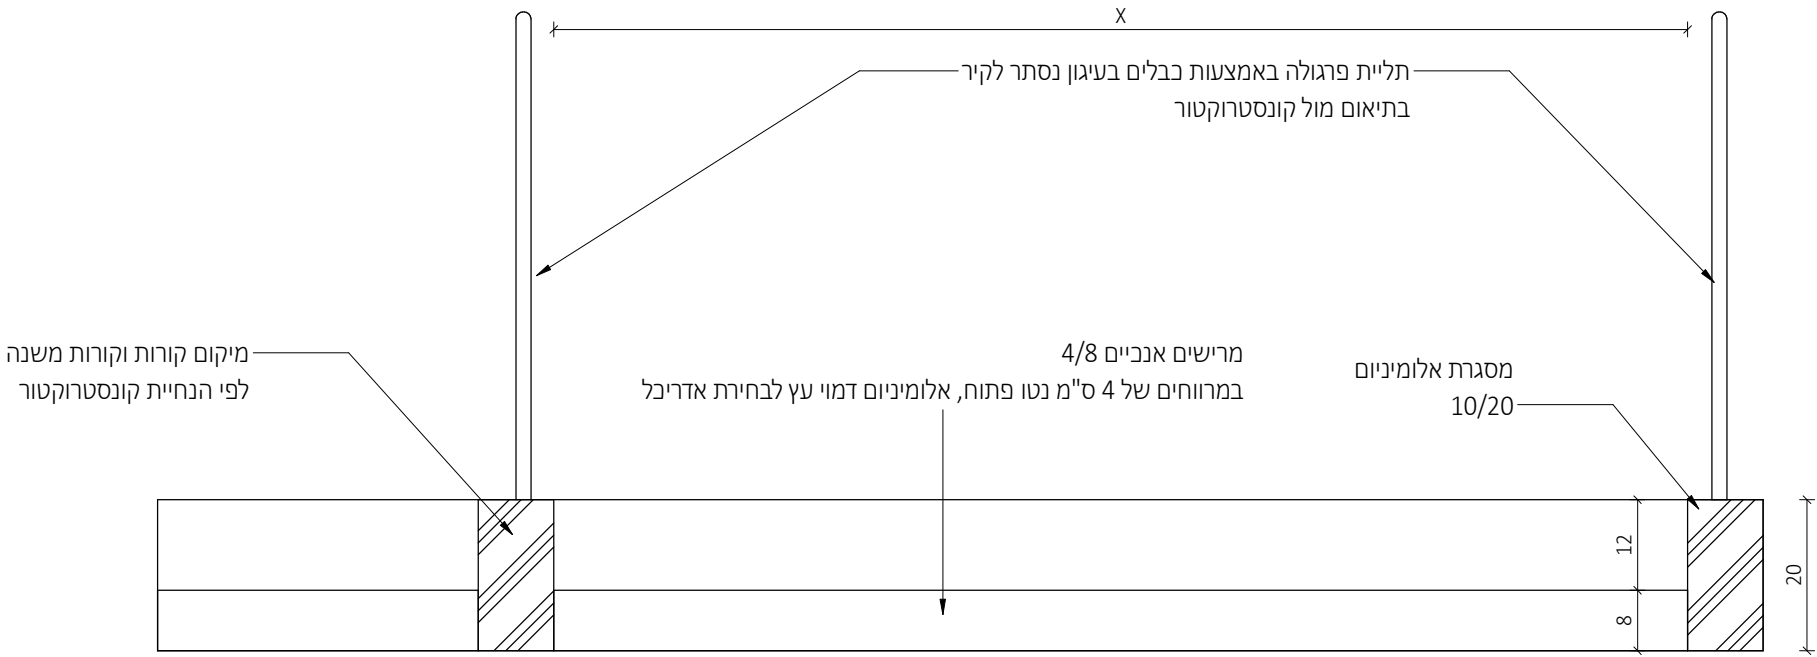

פרגולה - חתך אורך

1 : 10

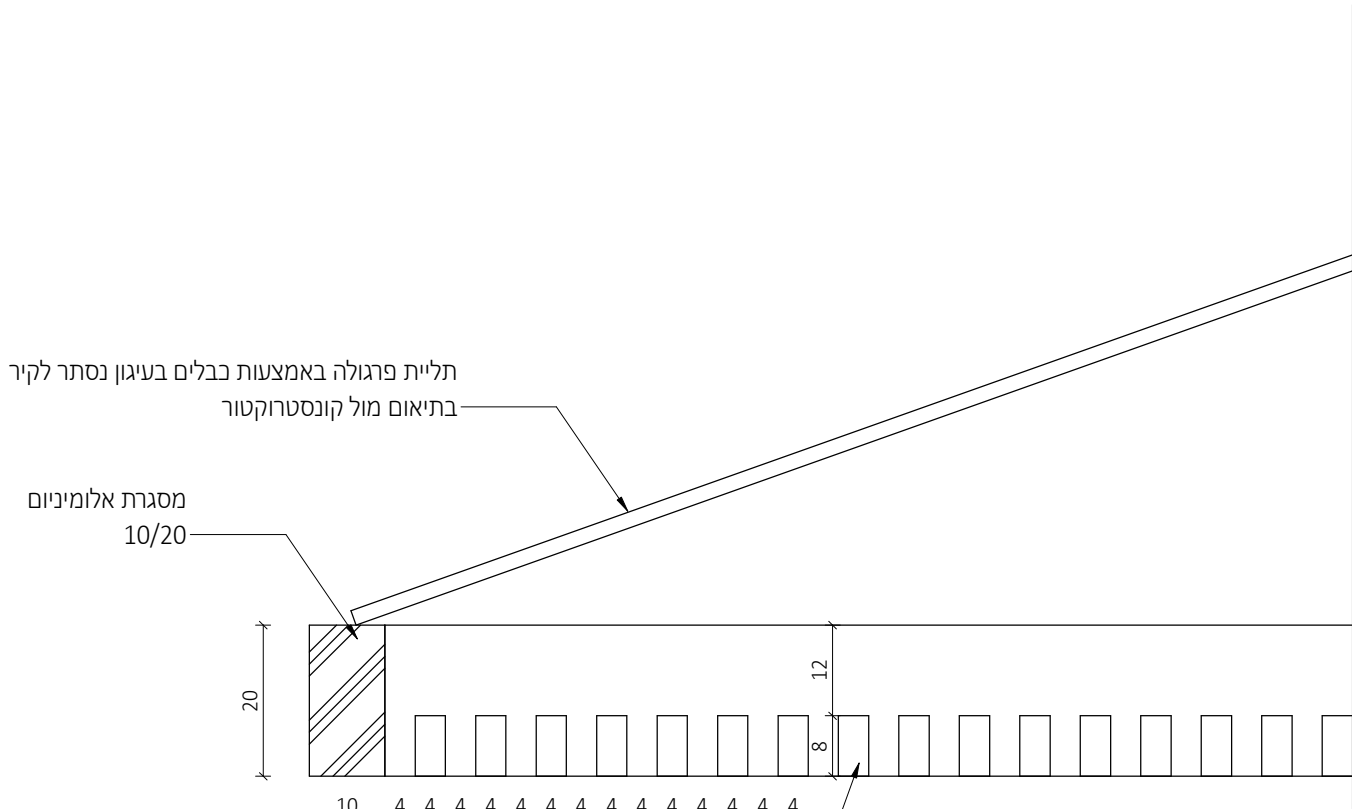

פרגולה - חתך רוחב


1 : 10

מתכננים:

ניהול פרויקט
בן סולומון - מהיסוד
פיקוח
בן סולומון - מהיסוד
קונסטרוקציה
ערן שילר
מיזוג אוויר
אייל ארז מהנדסים ויועצים בע"מ
אינסטלציה
איתן אלמסי
חשמל
איתן בסיס
אלומיניום
נוף
נתי בלוקא
חשמל חכם
חימום תת רצפתי
איטום
צבי טל
אקוסטיקה
מעליות
קרקע וביסוס
דיה הנדסת קרקע וביסוס
רישוי

± 0.00 = +246.50
הערות: 1. תכנית זו אינה לקרא יחד עם תכנית הרישויים. 2. גובה אבסולוטי - ראו תכנית פיתוח. 3. המידות הן בין קירות הבניה ולא כולל פיתוח. 4. פיתוח השטח סביב הבניה, כולל, מדרגות, גדרות, שנילים, ריצופים, שטחים בגובה, חניה וגובה לא תכנית פיתוח. 5. איסוס קירות והצפות הבניה בתנע עם הקרקע ובנידוד תרסי לאורך העמודים והקורות מול התמורה. כלירות יא עם סימני גובה - ראו תכנית קונסטרוקציה. 6. אף מים יבוצע בכל מישור אופקי הכולל מהגבן. 7. סיוח תרסי במסלול - ע"פ מפרט התמקור, מאפשר טיי פיקוד העודף. המבצע אחראי לסידור : עליו לבקר ולבדוק את כל המידות בתכנית ובמקום הבניה. במסלול של מידות או אי התאמה בתכנית /או בבנין, עליו להודיע על כך מיד לאדריכל בסופו המשיך בעבודתו. המבצע יאמנעם או ויק בתכנית שאפשר לביצוע. המבצע יחזיק באחר, כלל, את, של משרדו של תכנית. אין לקבוע מידות על ידי חזירה בשר מוס. התכנית היתה תכנה האדריכל ואין לשנות כל שימוש בה או ברעיונות הגלומים בה, אלא באישור בכתב מהאדריכל. מחנכים /א' יושע אשר שמו רשום בתכנית זו, נושא לכיד באחריות המקצועית והמקצועית בתכנית. על המפתח והמכני לודא התאמת התכנית האדריכלית "לביצוע" לתכנית זו. המכני והתכנית המאשרות ע"י כל גורמים הרשמיים. התכנית כוללת את כל המפרטים והידוע על ליום תחלפת.

משרד קירות:

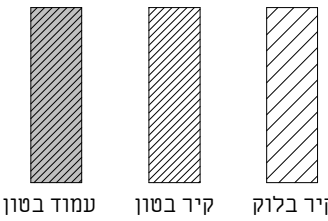

תאריך	תיאור	מהדורה
22.09.2025	מכרז	1

אדריכלות

שם המסמך:	CLIENT NAME:
קבוצת רכישה נופיה	
שם הפרויקט:	PROJECT NAME:
נופיה - מגרש 16	
שם הגיליון:	DRAWING NAME:
פרטי פרגולה	
מספר גיליון:	SHEET NUMBER:
A3-4-104	
מהדורה:	EDITION:
SCALE:	קנה מידה:
As indicated	
STATUS:	סטוס:
למכרז	
שורסע ע"י:	אלמוג אור
DATE:	29.12.25
תאריך:	

NeumanHaynerArchitects

נויטן חיינר אדריכלים
מורד התודים 2, בית חירות
09-9545642 78
office@nh-arch.com
www.nh-arch.com

זכיות ייצור / ע"פ הנחיות ע"ד

רשימת חלונות					
סוג	תיאור	כמות	גובה	רוחב	מס פריט

קרקע

1	110	240	1	צלון רפפה חיצוני חשמלי + ארגז חיצוני	דלת כנף פרופיל 4350 קליל
1.2	90	240	1	צלון רפפה חיצוני חשמלי + ארגז חיצוני	דלת כנף פרופיל 4350 קליל
2	610	240	1	צלון רפפה חיצוני חשמלי + ארגז חיצוני	ויטרינה פרופיל 7500 קליל
3	70	240	1	ללא רפפה	חלון קבוע פרופיל 7000 קליל
4	60	110	1	צלון רפפה חיצוני חשמלי + ארגז חיצוני	חלון קיפ פרופיל 4500 קליל
5	220	110	2	צלון רפפה חיצוני חשמלי + ארגז חיצוני	חלון הזזה פרופיל 7000 קליל

קומה א

6	110	110	3	תריס גלילה חשמלי	חלון הזזה פרופיל 7000 קליל
7	110	230	1	תריס גלילה חשמלי	קבוע עד 120 + חלון הזזה פרופיל 4350 קליל
8	300	230	1	תריס גלילה חשמלי	חלון קבוע פרופיל 7000 קליל
9	75	110	1	תריס גלילה חשמלי	חלון קיפ פרופיל 4500 קליל
10	220	110	2	תריס גלילה חשמלי	חלון הזזה פרופיל 7000 קליל

סוג זכוכית – בהתאם למפורט בדו"ח התרמי (תנאי המינימום בעמוד 9 מתוך המפרט התרמי). כמו כן, הזכוכית תקבע בתיאום עם הקבלן לאחר אישור יועץ התרמי וחברת הניהול

כל פריט יחולק למינימום הכנפיים האפשרי (לתיאום מול ספק האלומיניום ובמסגרת שרטוטי הshop drawing)

רשימת דלתות					
סוג	הערות	כמות	גובה	רוחב	מספר פריט

0	110	240	1	דלת כניסה	דלת חוץ דגם גארדה
1	90	210	6	דלת פנים	דלת פנים "אקוודור" תוצרת חמדיה
2	80	210	2	דלת פנים	דלת פנים "אקוודור" תוצרת חמדיה
3	80	200	1	דלת נגרות ממ"ד	דלת פנים "אקוודור" תוצרת חמדיה

נוימן חיינר אדריכלים בע"מ

כל הזכויות שמורות
ט.ל.ח

NeumanHaynerArchitects

רשימת פתחים

שם התכנית:

A3-6-1000

גליון מספר:

מהדורה:

22.09.2025



נופיה - מגרש 16

שם הפרויקט:

למכרז

סטטוס:

קבוצת רכישה נופיה

שם המממן:

קנה מידה:

12/29/2025 3:39:32 PM