


פתחי גישה אופן ארט בתיאום סופי מול אדריכל
כלל יחידות המידוג אשר נמצאות בתוך נגרות יש לתאם סופית מול אדריכל ונגרות

Court 16 1st Floor


Option No1
VRF duct unit in living room
and wall mounted in rooms

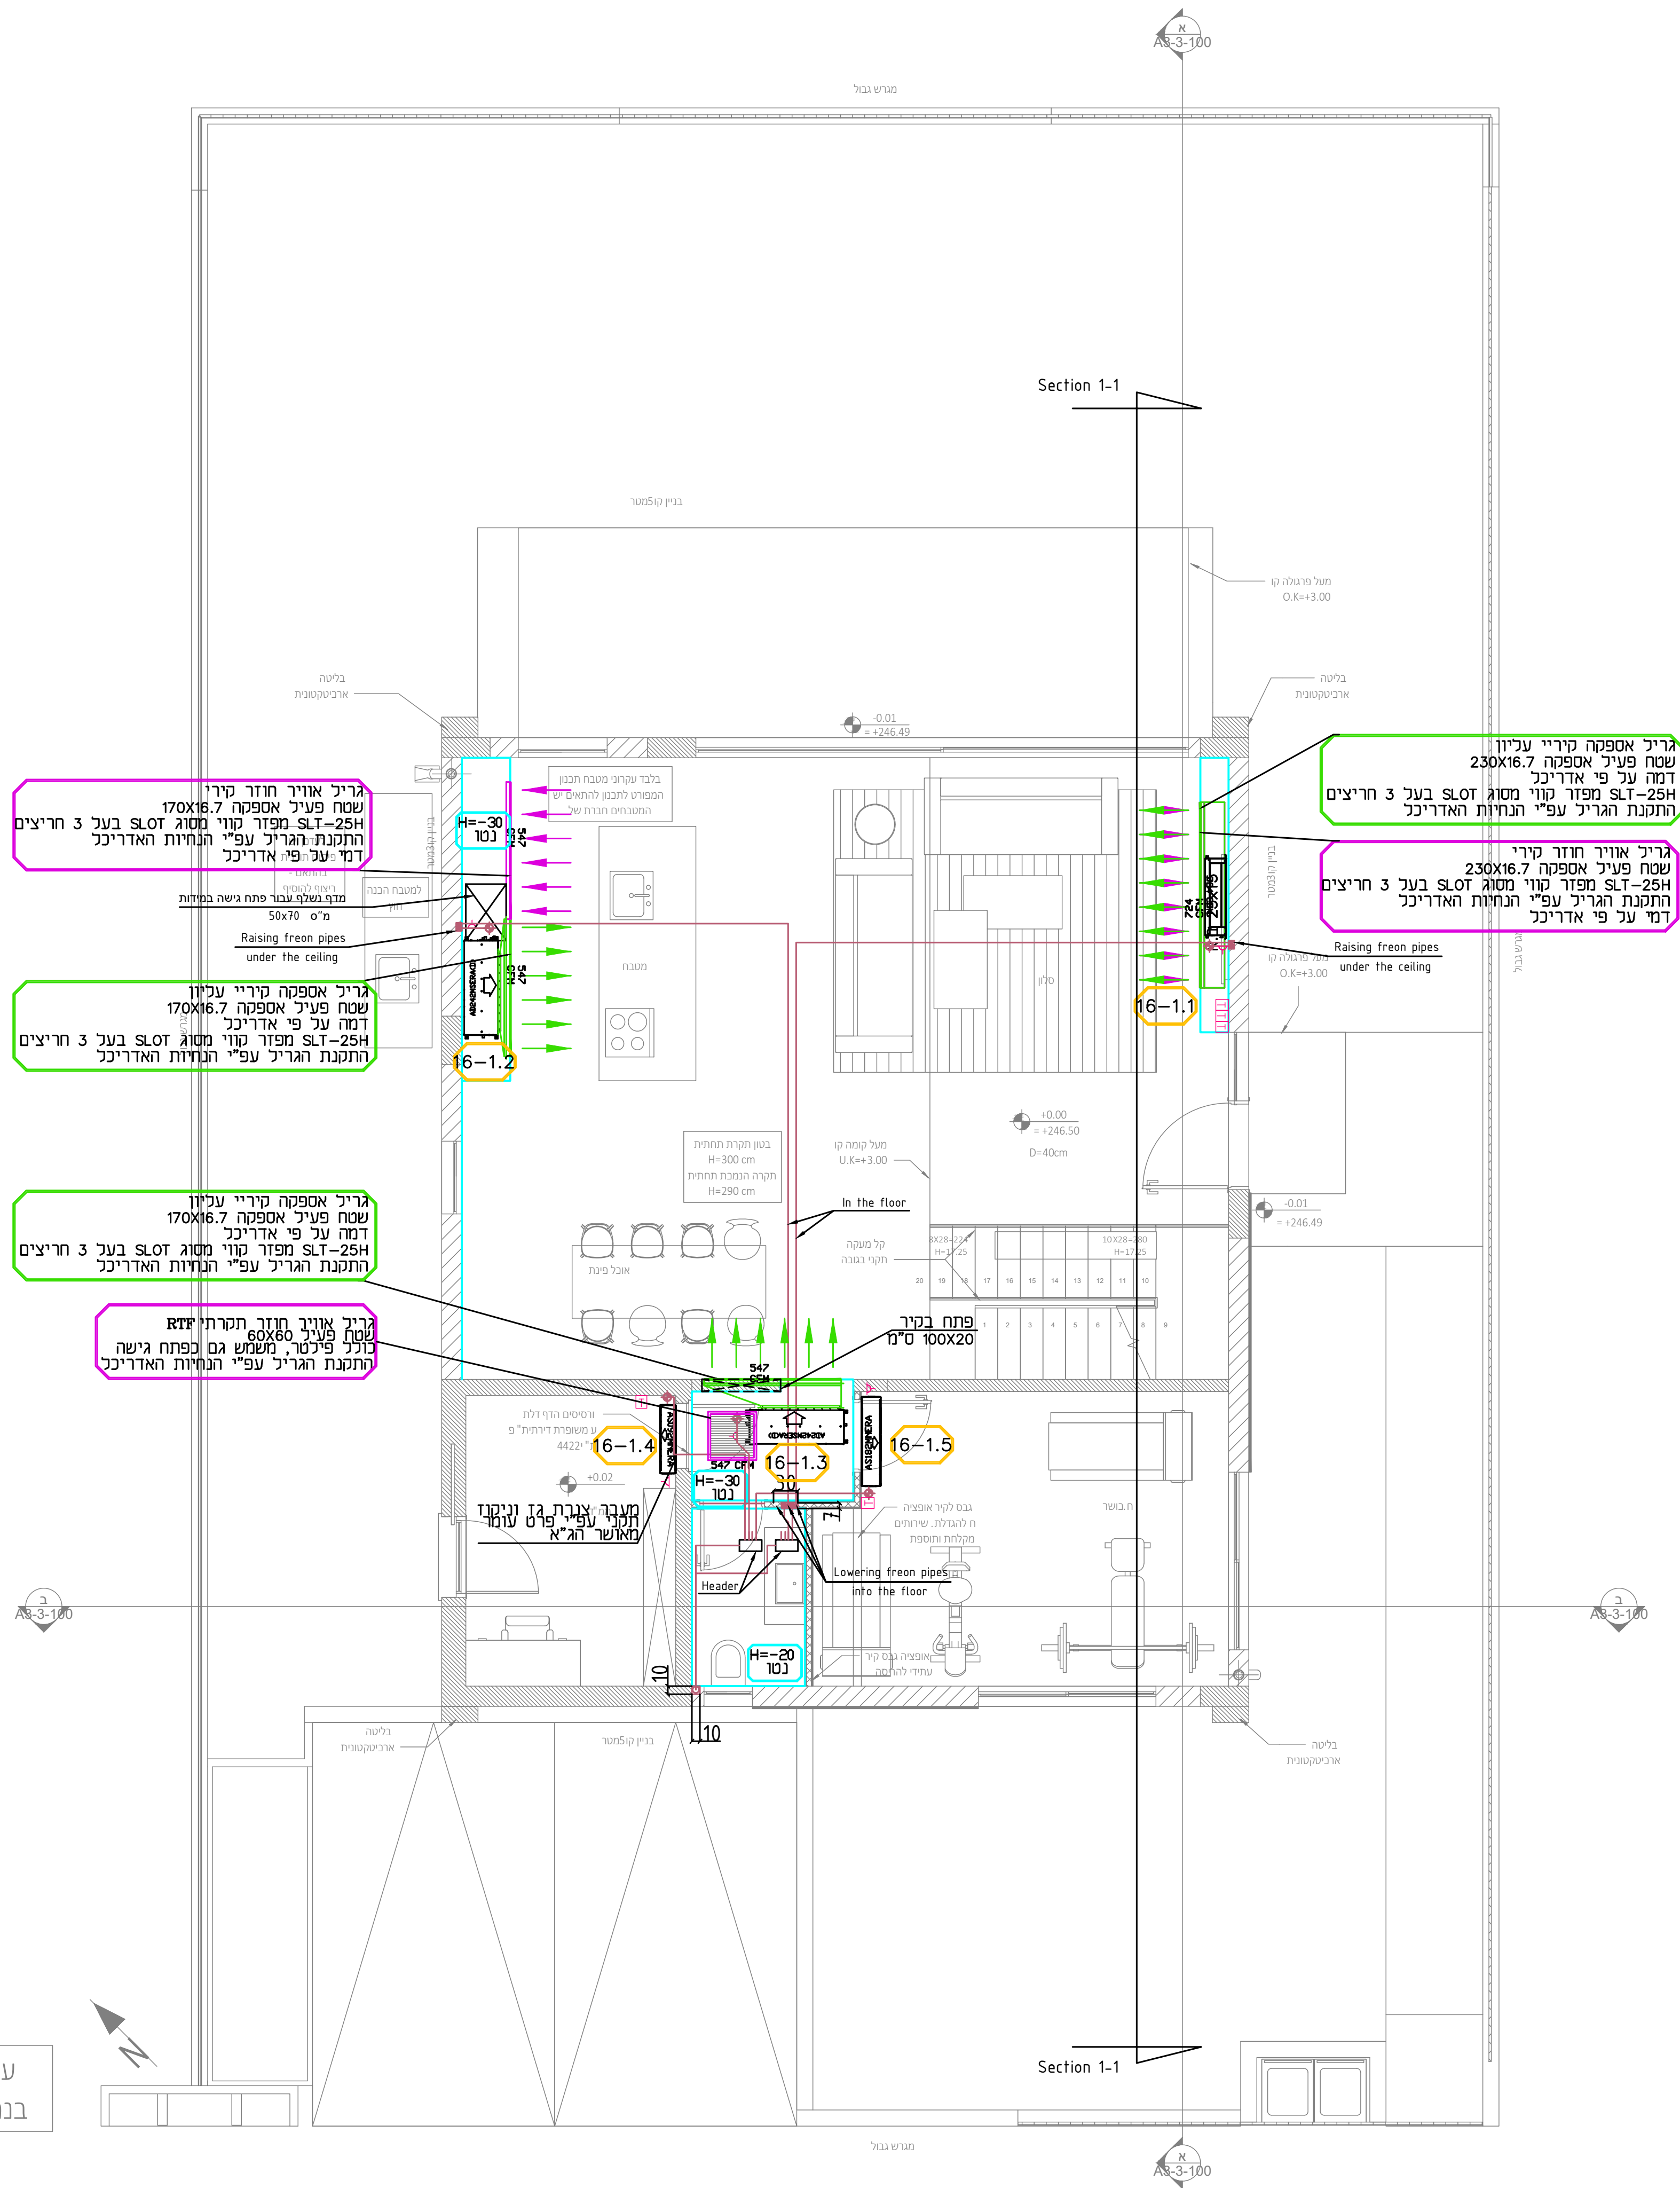

עפ כוף פיתוח"תוכניות י
בנפרד פירוט ראה כוף יועץ

Court 16 2nd Floor

Option No1
VRF duct unit in living room
and wall mounted in rooms

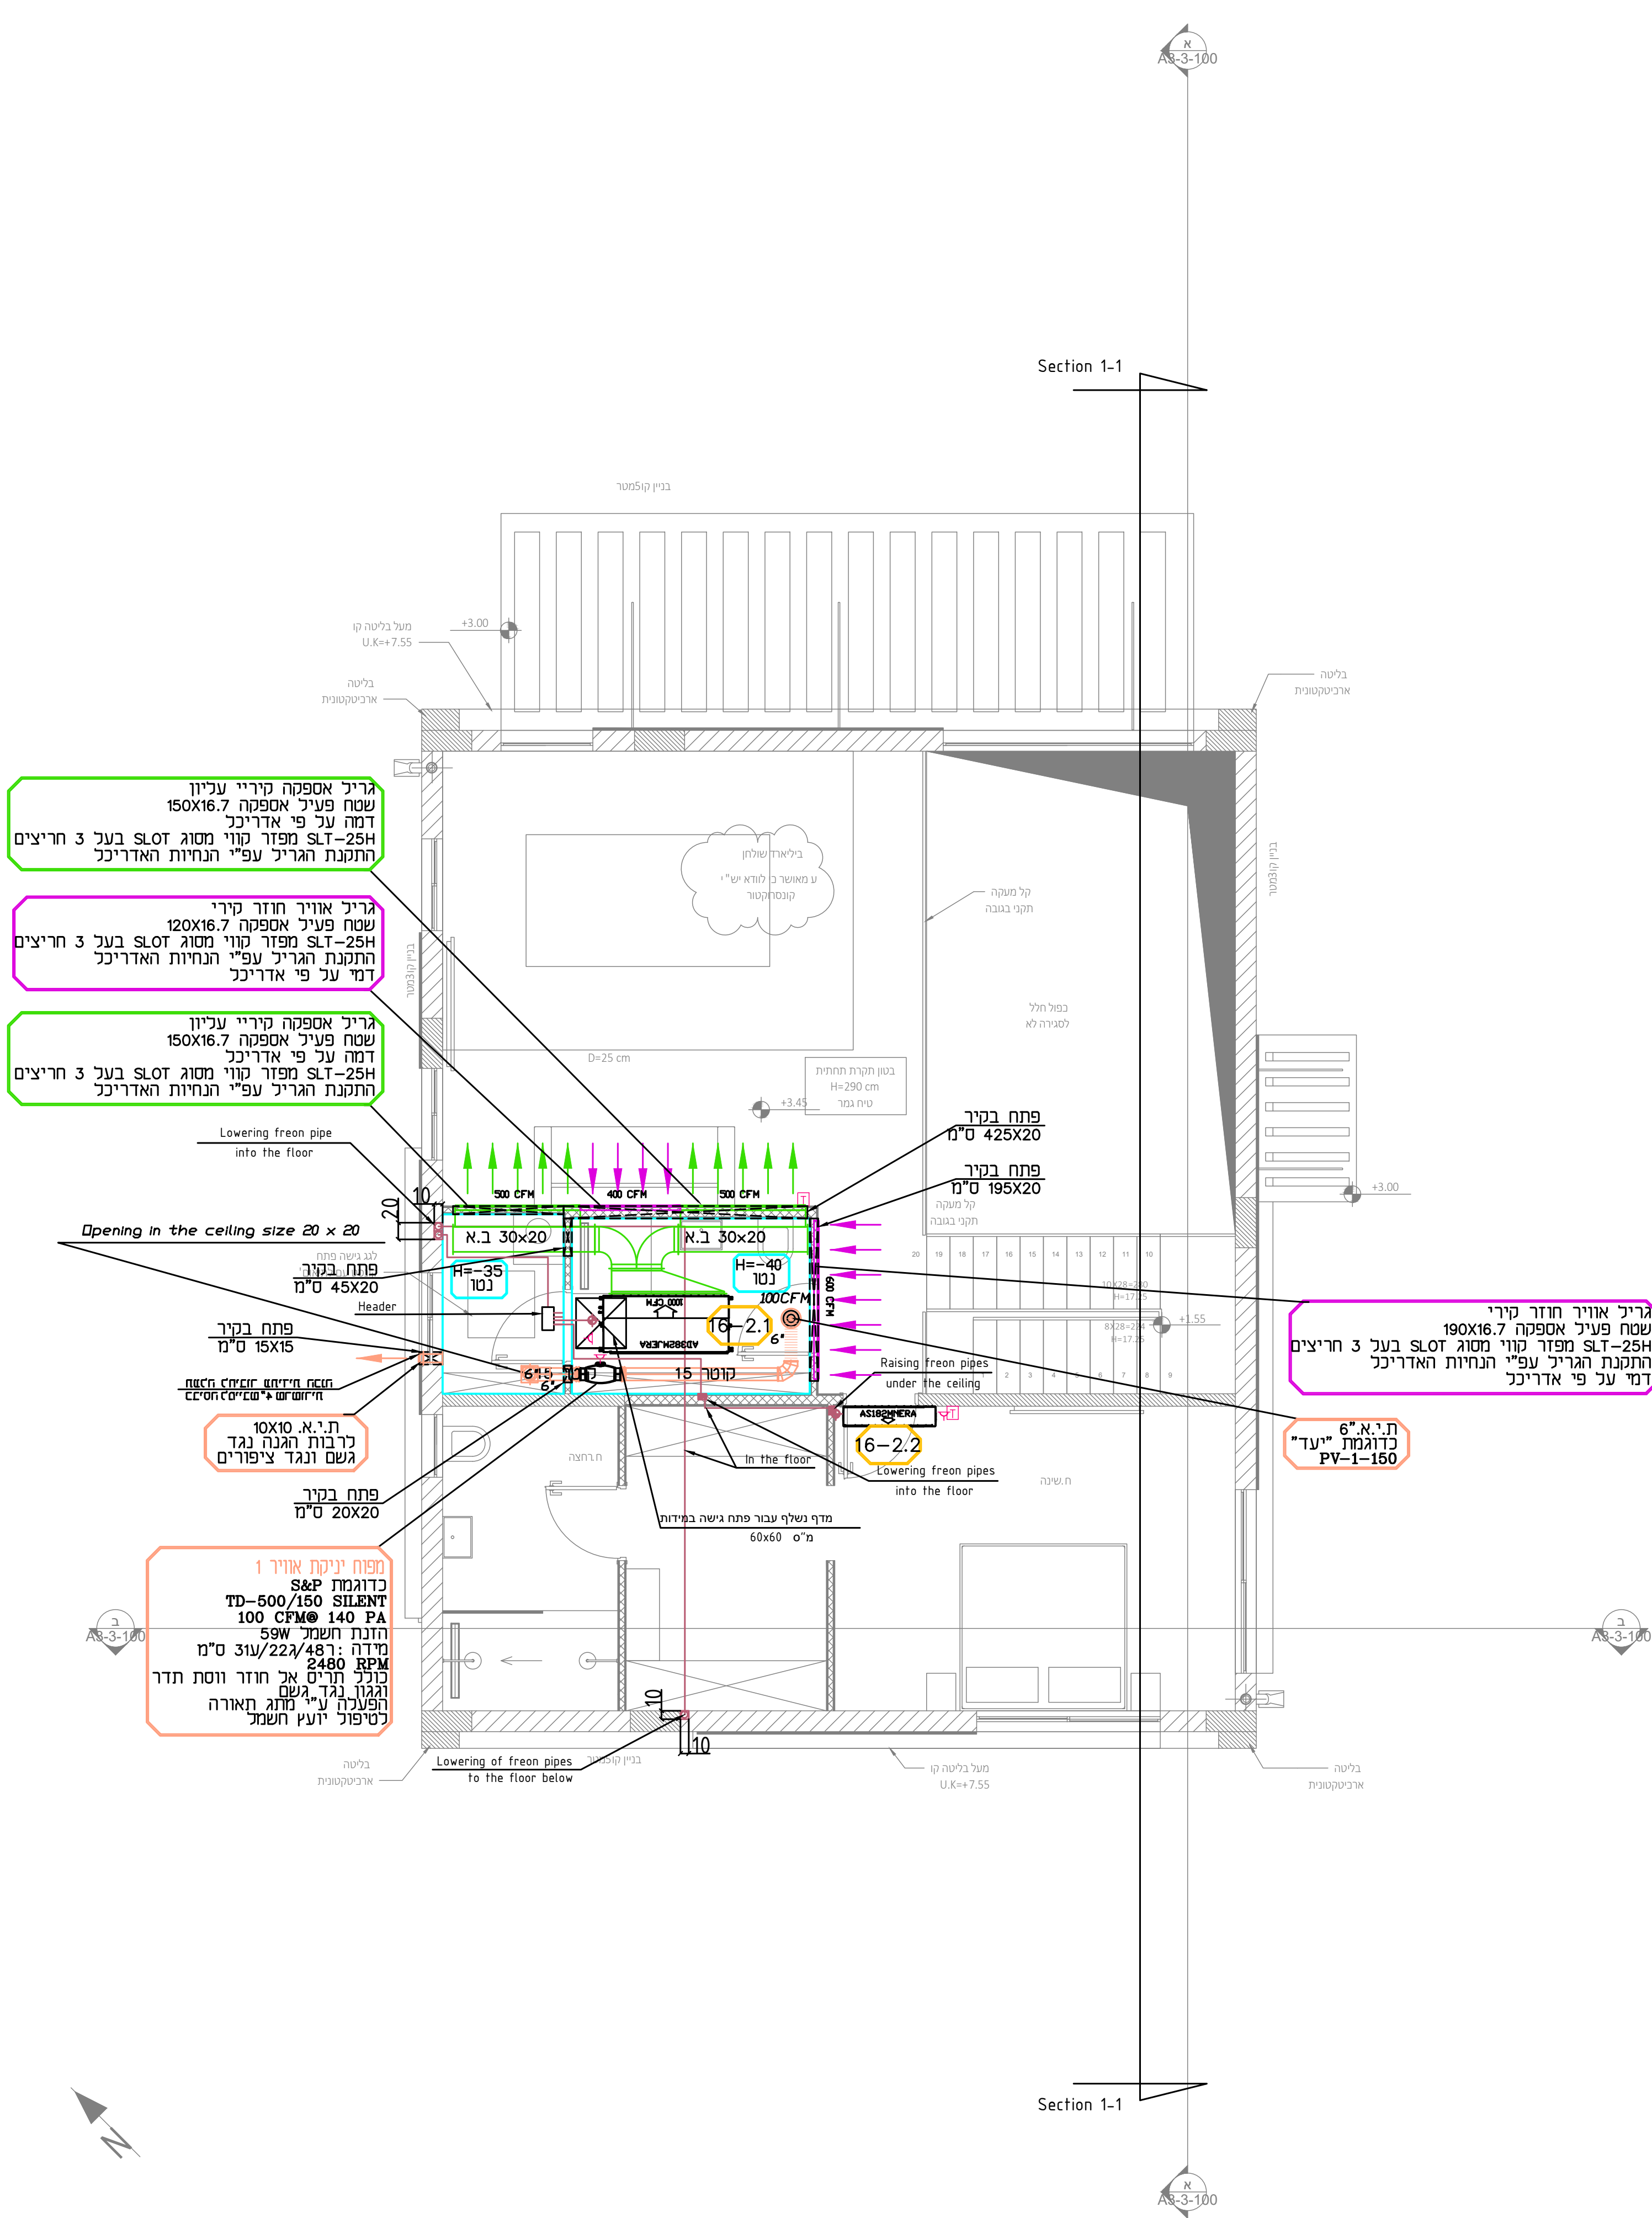

תפוצה

אדריכל	לוח	תוכן פרויקט	תוכן ראשי	תוכן תוכנית	תוכן תוכנית	תוכן תוכנית	תוכן תוכנית	תוכן תוכנית	תוכן תוכנית
אדריכל	לוח	תוכן פרויקט	תוכן ראשי	תוכן תוכנית	תוכן תוכנית	תוכן תוכנית	תוכן תוכנית	תוכן תוכנית	תוכן תוכנית
מהדורה

15.05.2025	תוכן ראשי	1
08.05.2025	תוכן ראשי	2
31.03.2025	תוכן ראשי	3
11.03.2025	תוכן ראשי	4
11.03.2025	תוכן ראשי	5
11.03.2025	תוכן ראשי	6
11.03.2025	תוכן ראשי	7
11.03.2025	תוכן ראשי	8
11.03.2025	תוכן ראשי	9
11.03.2025	תוכן ראשי	10

המבצע אחראי למידות ומהתאמות למציאות
בכל מקרה של אי התאמה, מתירה או טעות
עליו להודיע למתכנן לפני התקדמותו בביצוע
אין לקבוע מידות על סמך מדידה בשרטוט.
אין ברעיונות בחזיתות זו
אין ברעיונות הגומים בה לכל אישור בבחב
מאז המתכנן.

הערות

- כל תעלות מחוץ למבנה יבודדו
בידוד אקוסטי בעובי 2"
- תעלות מזוג בתוך המבנה יבודדו
בידוד אקוסטי פנימי 1"
- תעלות אוויר צח יבודדו
בידוד טרמי 1"
- יש לאסום בסיקור את פינות החיבור
של תעלות מזוג אוויר לפני כיפוף
הפחים המתחברים

מקרא

- מפ- מפוח
- מ.א.ג. - מפוח אוויר קירי
- מ.א.ת. - מפוח אוויר תתקרי
- ת.א.ת. - תריס אוויר חודר
- ת.א.צ. - תריס אוויר צח
- ב.א. - בידוד אקוסטי
- ב.ס. - בידוד טרמי
- ד.א. - דמפר
- סרמסט - לוח הפעלה
- שקע חשמל - לספוף יועץ חשמל
- שקע חתך פאזי - לספוף יועץ חשמל
- מפסק בסחון חד פאזי - לספוף יועץ חשמל
- מפסק בסחון חתך פאזי - לספוף יועץ חשמל
- ניקוז מאיד - לספוף יועץ אינסטלציה
- בגובה 25 ס"מ מתחתית גובה המאיד
- שלט הפעלה אלקטרי

מקרא צבעים בתכנית

- תעלות ותריסי אוויר חודר
- תעלות ותריסי אספקת אוויר
- תעלות ותריסי אוויר צח
- תעלות ותריסי יניקת אוויר
- תעלות ותריסי שחרור עשן
- צנרת גז וחשמל
- סימון מעגלי מידוג אוויר

191	מבני מגורים צמודי קרקע נופיה אכפי מנשה מגרש 16
1:50	מידוג אוויר ואיוורור
15.05.2025	קומה ראשונה ושנייה
15.05.2025	תוכן תוכנית
15.05.2025	תוכן תוכנית
Option **No1**

בסיס בטון בגובה מינימלי 10 ס"מ
יחידת עיבוי עומדת ע"ג בולמי רעידות
לטיפול קבלן מזדג אוויר

מיקום סופי של המעבים
ייקבע בשטח
בתיאום עם האדריכל
וקבלן מיזוג אוויר

מיקום סופי של הניקוזים
ייקבע בשטח בתאום עם האדריכל
יועץ אינסטלציה וקבלן מיזוג אוויר

בסיס בטון בגובה מינימלי 10 ס"מ
יחידת עיבוי עומדת ע"ג בולמי רעידות
לטיפול קבלן מזוג אוויר

מיקום סופי של המעבים
ייקבע בשטח
בתיאום עם האדריכל
וקבלן מיזוג אוויר

מיקום סופי של הניקוזים
ייקבע בשטח בתאום עם האדריכל
יועץ אינסטלציה וקבלן מיזוג אוויר

16-ע"מ מעגרי ו-
 AV12NMSETA : דגם
 114,300 BTU/Hr : תפוקה
 110/163.6/1057 : מידה
 נתיב חשמלי: (A) 3x32
 168 ק"ג : משקל
 9.25 (kW) : חשמל
 60 dB(A) : רעש

מערבס מעגרי 2-6
AV07NFPEUA : דגם
61.400 BTU/Hr : תפוקה
37v/134r/95r : מידה
נתיך חשמלי: 3x16 (A)
801 ק"ג : משק
4.75 [KW] : הפק
59 dB(A) : נצרך


יחידות סדרה משגב 16-1											
מס' יחידה בחנקית	תוצרת	דגם	מאייד	תפוקת כורוד	ספיטת אייר CFM	רמת רעש db(A)	משקל KG	סידרת גוף	סידרת פני	מרחק חוזה V/mz/Ph	הספק גנרר w
16-1,3	Haier	AD242MSERA(D)	Slim Duct Low ESP	24,200	547	36	24	ר717/422/421 ס"מ	---	230/50/1	---
16-1,1	Haier	AD242MJERA	Duct Medium ESP	24,200	724	38	33	ר717/254/722 ס"מ	---	230/50/1	---
16-1,4	Haier	AS092MNERA	מאייד עיני	9,500	352	36	10	ר85,5/287/204 ס"מ	---	230/50/1	---
16-1,5	Haier	AS182MNERA	מאייד עיני	19,100	541	40	16	ר115,7/33,6/251 ס"מ	---	230/50/1	---

יידות קצה מערך 2-16											
מס' יחידה בחבנית	תוצרת	דגם	מאיד	תפוקת כוור Btu/h	ספיקת אויר CFM	רעש דבל dB(A)	משקל KG	גוף דיות	דיות פנר	קוטר חונה v/Hz/Ph	הספק צנור W
6-2	Haier	AD382MJERA	Duct Medium ESP	38,200	1000	42	48	רסו 70w/25x150 ס"מ	---	230/50/1	---
6-2.2	Haier	AS182MNERA	מאיד עקי	19,100	541	40	18	רסו 25w/33.6x111.5 ס"מ	---	230/50/1	---

גריל אספקה קירי עליון
שטח פעיל אספקה 230x16.7
דמה על פי אדריכל
SLT-25H מפור קווי מסוג slot בעל 3 חריצים
התקנת הגריל עפ"י הנחיות האדריכל

גריד אוויר חוזר קירי
שטח פועל אספקה 230x16.7
SLT-25H מפזר קווי מסוג SLOT בעל 3 חריצים
התקנת הגריד עפ"י הנחיות האדריכל
דמי על פי אדריכל

גריד אוויר חוזר קירי
שטח פועל אספקה 230x16.7
SLT-25H מפזר קווי מסוג SLOT בעל 3 חריצים
התקנת הגריד עפ"י הנחיות האדריכל
דמי על פי אדריכל

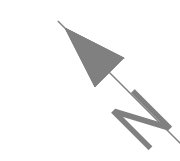

אוריכל פנים	
אינסטיציה	
בסירות אש	
אקוטריקה	
חשמת ותואורה	
קונסטרוקציה	
קבלו ראש	
ניחול פרויקט	
נלכות	
אוריכל	

תחנות לאשור	15.05.2025	15.05.2025	15.05.2025
תחנות לאשור	08.05.2025	08.05.2025	08.05.2025
תחנות לאשור	31.03.2025	31.03.2025	31.03.2025
תחנות נעים	11.03.2025	11.03.2025	11.03.2025
שנתיים	תאריך:	שנתיים	שנתיים

הערות

- מקרא

- מקרא צבעים בתכנית

- | | |
|--------------------------|---|
| תעלות ותריסי אוויר חוזר |  |
| תעלות ותריסי אספקת אוויר |  |
| תעלות ותריסי אוויר צח |  |
| תעלות ותריסי יניקת אוויר |  |
| תעלות ותריסי שחרור עשן |  |
| צנרת גז וחשמל |  |
| סימון מעגלי מדוז אוויר |  |

191	מבני מגורים צמודי קרקע נופיה אלפי מנשה מגרש 16
1:50	מיוזג אוויר ואווורור
15.05.2025	קומת גג וטבלאות
4	
מחירים	
○ לבציע	□ נכסרו
	● לאשרר
	△ עניין
	11.03.2025
	האריך
	מבני מגורים
	איי ארץ