

מתכונים:

ניהול פרויקט
מהיסוד - בו סולומון
פיקוח
מהיסוד - בו סולומון
קונסטרוקציה
ערן שילר
מיזוג אוויר
אייל ארז מהנדסים ויועצים בע"מ
אינסטלציה
איתן אלמסי
חשמל
איתן בסיס
אלומיניום
נוף
נתי בלוקא
חשמל חכם
חימום תת רצפתי
איטום
צבי טל
אקוסטיקה
מעליות
קרקע וביסוס
דיה הנדסת קרקע וביסוס
רישוי

+ 0.00 = +245.60


ערות:

- וכיבית וְיִקְרָא וְיַדְּ תַּחְבִּית הַיּוֹעִצִּים.
גִּבּוֹהַּ אֲבֻסְלוֹם וְרֹא אֲבִיתָהּ יִפְתּוֹ.
הַיְּהוּדִים וְכִן קִרְיַת הַבְּנֵי (לֹא כֹלֵל שָׁמָּה).
יִפְתּוֹ הַשֵּׁשֶׁת מִכֵּיב הַדְּרוֹת, כֹּלֵל, הַדְּרוֹת, שְׂבִילִים, רִצּוּפִים,
שִׁמְשִׁים בְּהֵרֶם, מִתָּה וְיִגְזֹן-וְרֹא אֲבִיתָהּ יִפְתּוֹ.
אִישׁוֹס קִרְיַת הַמִּצְוָה בְּמַגֵּעַ עַל הַקִּרְקַע וְיִבְדֵּד תִּרְמִי לֶאֱרֹר הַמְּעֻדִים
וְהַקּוֹרֵעַ וְהַתְּפֹצֵת לְגִדּוֹת אֹן עַל מִצְלֵי (נִגְזֹן)-וְרֹא אֲבִיתָהּ קִנְסוֹרְקוּיָהּ
4 אִישׁ מִתָּה בְּמַגֵּעַ עַל הַקִּרְקַע וְאִפְכִי הַבֹּחֶס מְחֻבָּר.
4 אִישׁ מִתָּה בְּמַגֵּעַ עַל הַקִּרְקַע וְאִפְכִי הַבֹּחֶס מְחֻבָּר.
4 אִישׁ מִתָּה בְּמַגֵּעַ עַל הַקִּרְקַע וְאִפְכִי הַבֹּחֶס מְחֻבָּר.

המבצע אחראי למידות : עליו לבקר ולבדוק את כל המידות בתכנית
ורמקום הוורודה

[illegible]

מקרא קירות:

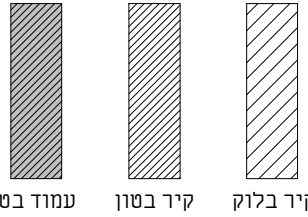[illegible]

אדריכלות

שם המזמין

CLIENT NAME:

קבוצת רכישה נופיה

שם הפרויקט

PROJECT NAME:

נופיה - מגרש 17

שם הגליון

DRAWING NAME:

גליון שער

מספר גליון

SHEET NUMBER:

A3-1-100

מהדורה:

SALE:

STATUS:

מטמור

0.10

בדף

שורט ע"י

DATE: 29.12.25

תאריך:



NeumanHaynerArchitects


office@nh-arch.com
www.nh-arch.com

מועדון הספרים, בית חירות
טל 09-9545842

זכויות ייצור / ע"פ הנחיות עו"ד

נופיה - מגרש 17			
מס' גיליון	שם גיליון	מהדורה	תאריך הפצת מהדורה

22.09.2025	1	גליון שער	A3-1-100
29.12.2025	2	תכנית קומת קרקע	A3-1-101
22.09.2025	1	תכנית קומה א	A3-1-102
22.09.2025	1	תכנית מפלס גג	A3-1-103
22.09.2025	1	חזיתות 1	A3-2-200
22.09.2025	1	חזיתות 2	A3-2-201
22.09.2025	1	חתכים	A3-3-100
22.09.2025	1	גליון מדרגות	A3-4-100
22.09.2025	1	פרטים	A3-4-103
22.09.2025	1	פרטי פרגולה	A3-4-104
22.09.2025	1	רשימת פתחים	A3-6-1000

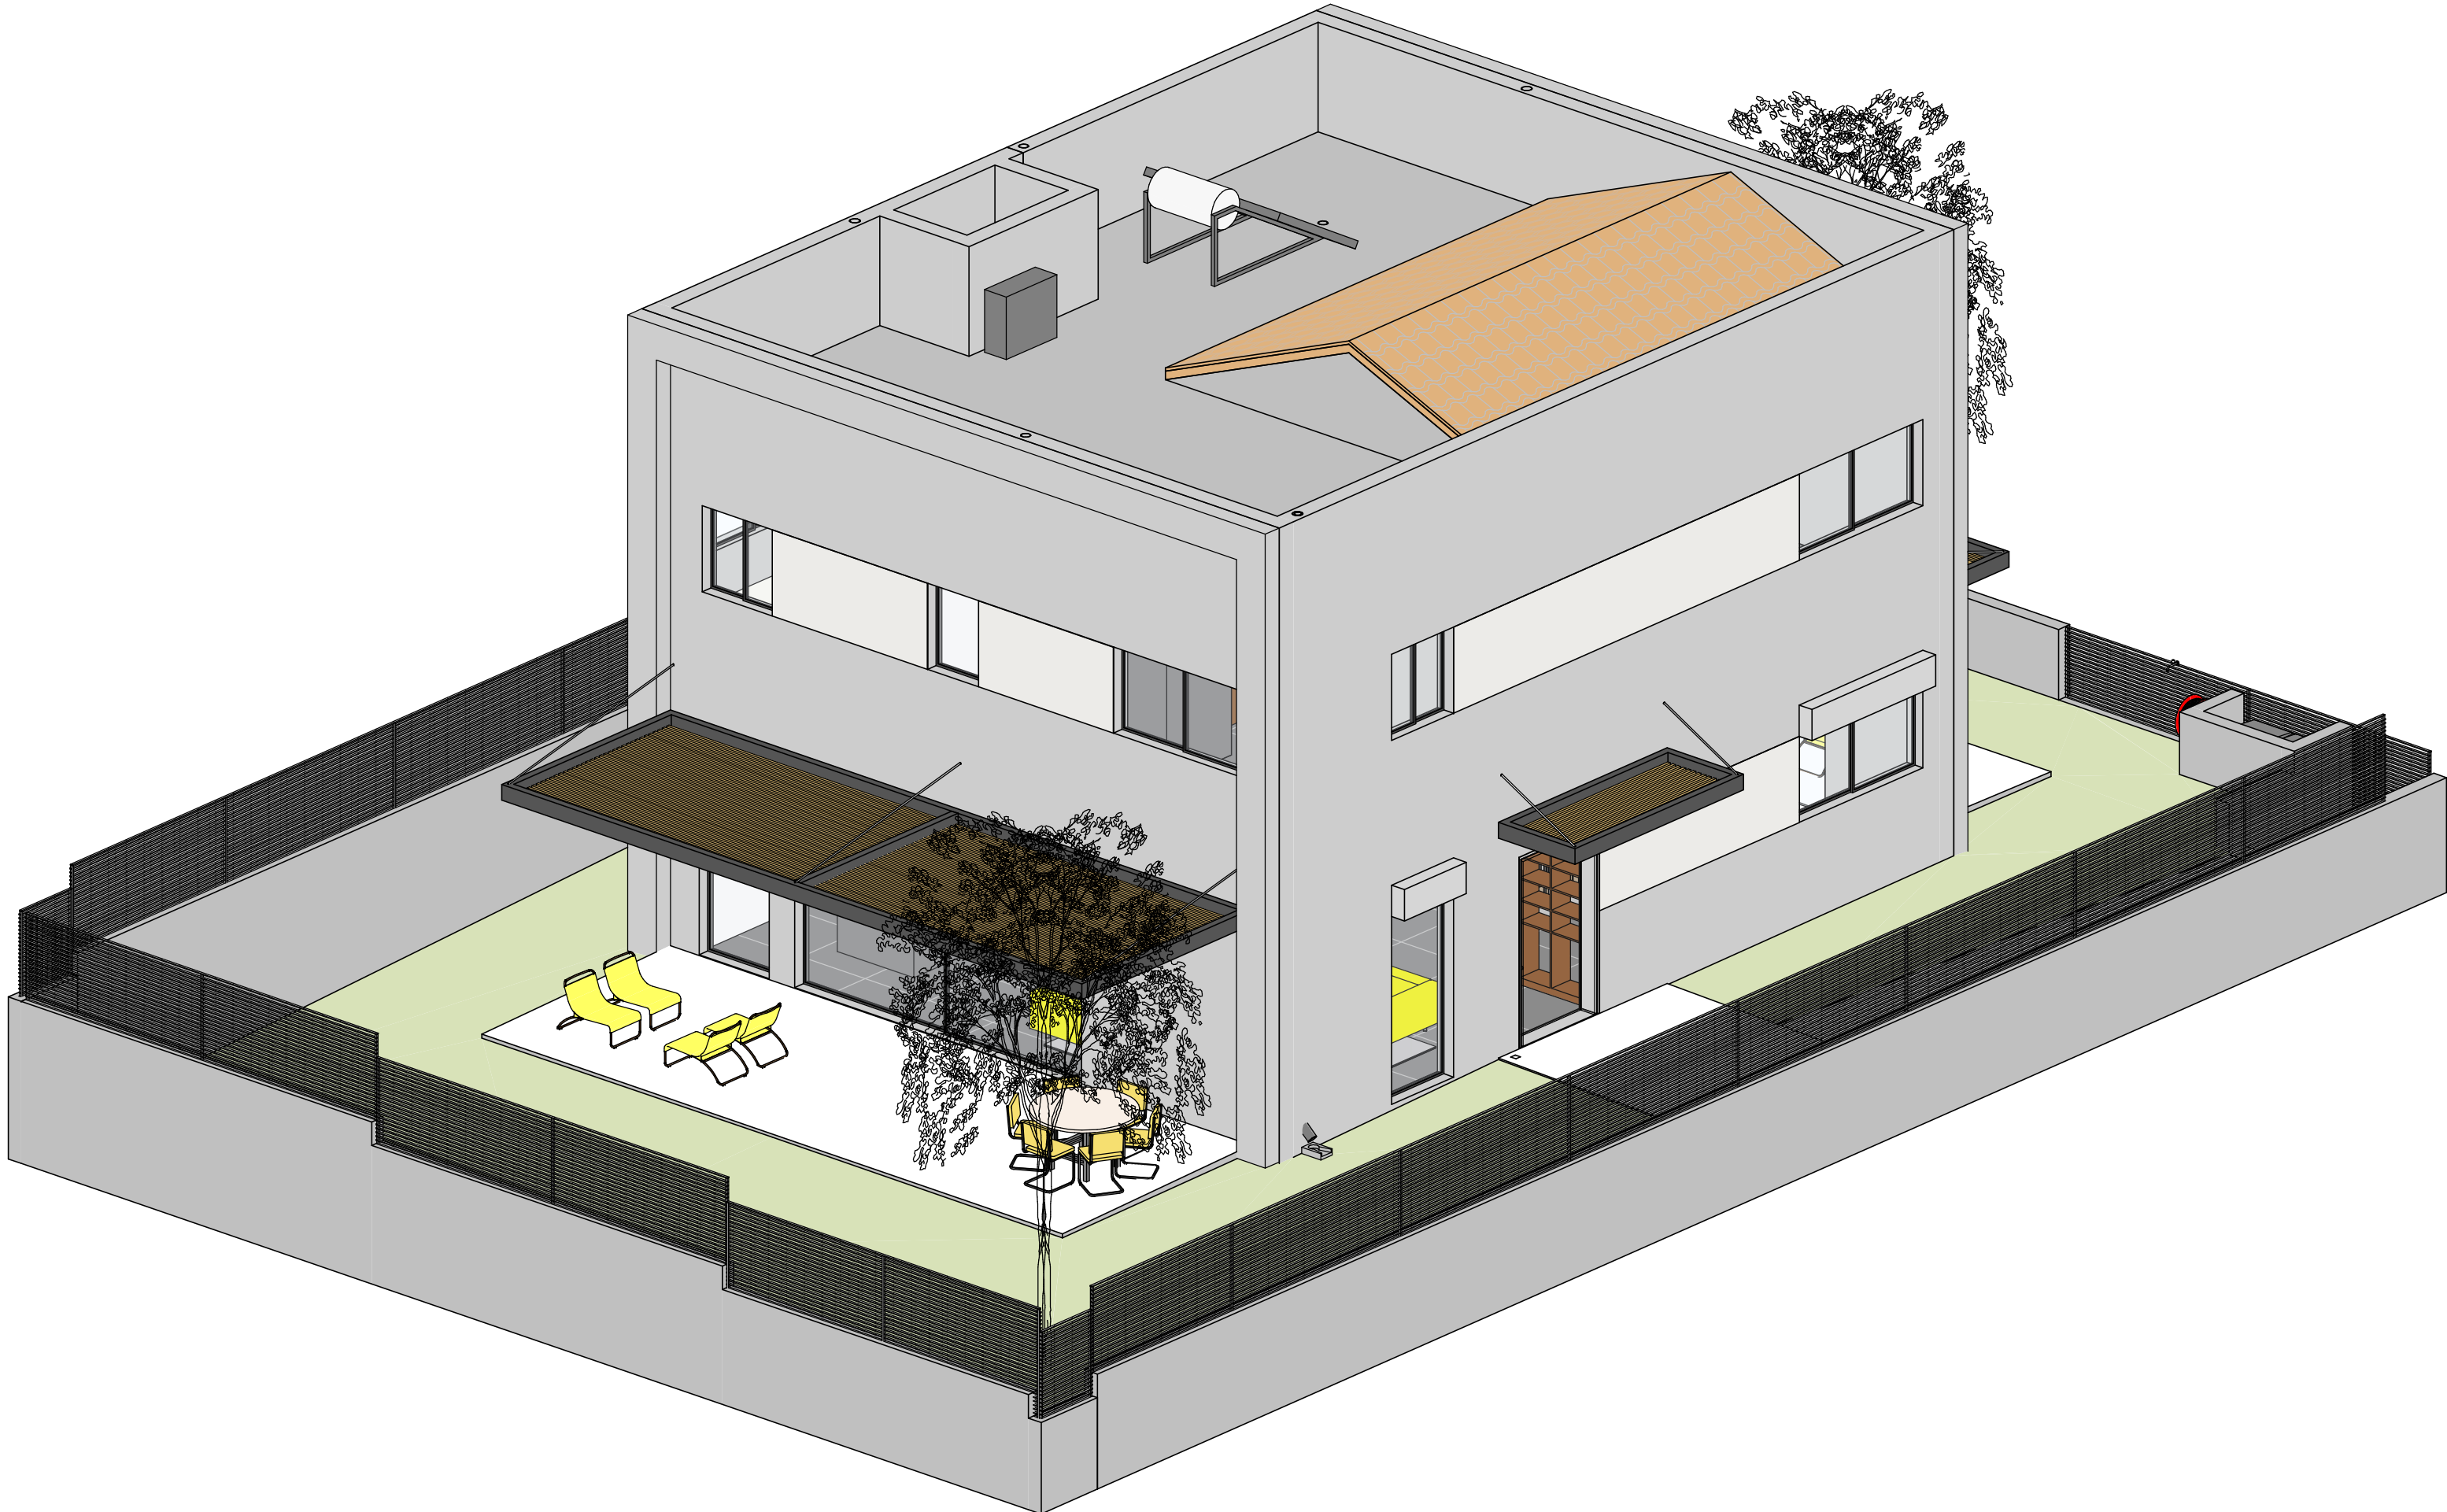


ניהול פרויקט
מהיסוד - בו סולומון
פיקוח
מהיסוד - בו סולומון
קונסטרוקציה
ערן שילר
מיזוג אוויר
אייל ארז מהנדסים ויועצים בע"מ
אינסטליציה
איתן אלמסי
חשמל
איתן בסיס
אלומיניום
נוף
נתי בלוקא
חשמל חכם
חימום תת רצפתי
איטום
צבי טל
אקוסטיקה
מעליות
קרקע וביסוס
דיה הנדסת קרקע וביסוס
רישוי

± 0.00 = +245.60 הערות: 1. תכנית זו יש לקרוא יחד עם תכנית היסודים. 2. גובה אבסולוטי - ראש תוכנית פיתוח. 3. המידות הן בין קירות הבניה ולא כולל סיום. 4. פיתוח השטח כפי הוגש, כולל סדרות, שנילים, ריצופים, שפופים, גדרים, חניה וכו' ראש תוכנית פיתוח. 5. איטום קירות ורצפות הבניה כמגע עם הקרקע ובנידוד תחרי לאורך העמודים והקירות לכל תמורות. כליות או עם סימני גיבס - רא תכנית קונסטרוקציה. 6. אי מים יבוצע בכל מישור אופקי הכולל חתוכין. 7. סוף תחרי במסיד - ע"פ מפרט חומקיר, מאושר ע"י פיקוח העירי. המבצע אחראי לסידות: עליו לבקר ולבדוק את כל המידות בתכנית ובקטעו הטכניקה. במסדו של מסדו או אי התאמה בתכנית /או בבנוי, עליו להודיע על כך מיד לאדריכל בסדם המשך עבודותיו. המבצע יאשמש או ויק, בתוכנית שאושר לכיצד. המבצע יחזיק אחרא, לכל מה, של מחדש של תכנית. אח לקבוע מידות על ידי חדיה בשום. התכנית הכוללת הכוללת האדריכלי ו/או לשושה כל שימוש בה או ברעיונות הגולמים בה, אלא באישור כתוב מהאדריכל. המבצע /או יושם אשר שמו מחדש בתכנית זו, נושא לכד באחריות המבצעת והתוכנית תכנית. על המבצע והמבצע לודא התאמת התכנית האדריכלית "כיצד" לתכנית היסוד, המבנה והתאמת המאשרות ע"י כל גורמים הרשמיים. התכנית כוללת את כל האפשרויות הדרוש עד סיום תחבולת.	
--	--

משרד קירות: קיר בלוק קיר בסון עמוד בסון	
---	--

תאריך	תיאור	מהדורה
22.09.2025	מכרז	1
29.12.2025	עדכן פיתוח	2

אדריכלות שם המסמך: קבוצת רכישה נופיה שם הפרויקט: נופיה - מגרש 17 שם הגליון: תכנית קומת קרקע מספר גליון: A3-1-101 תאריך: 29.12.25 מחזור: 2 מספר: 1:50 סטוס: למכרז שורסע ע"י: נבדק ע"י: תאריך: 29.12.25 NeumanHaynerArchitects ניוסן חיינו אדריכלים מודד התודים 2, בית חירות 09-954642 70 office@nh-arch.com www.nh-arch.com זכויות ייפור / ע"פ הנחיות ע"י	
--	--

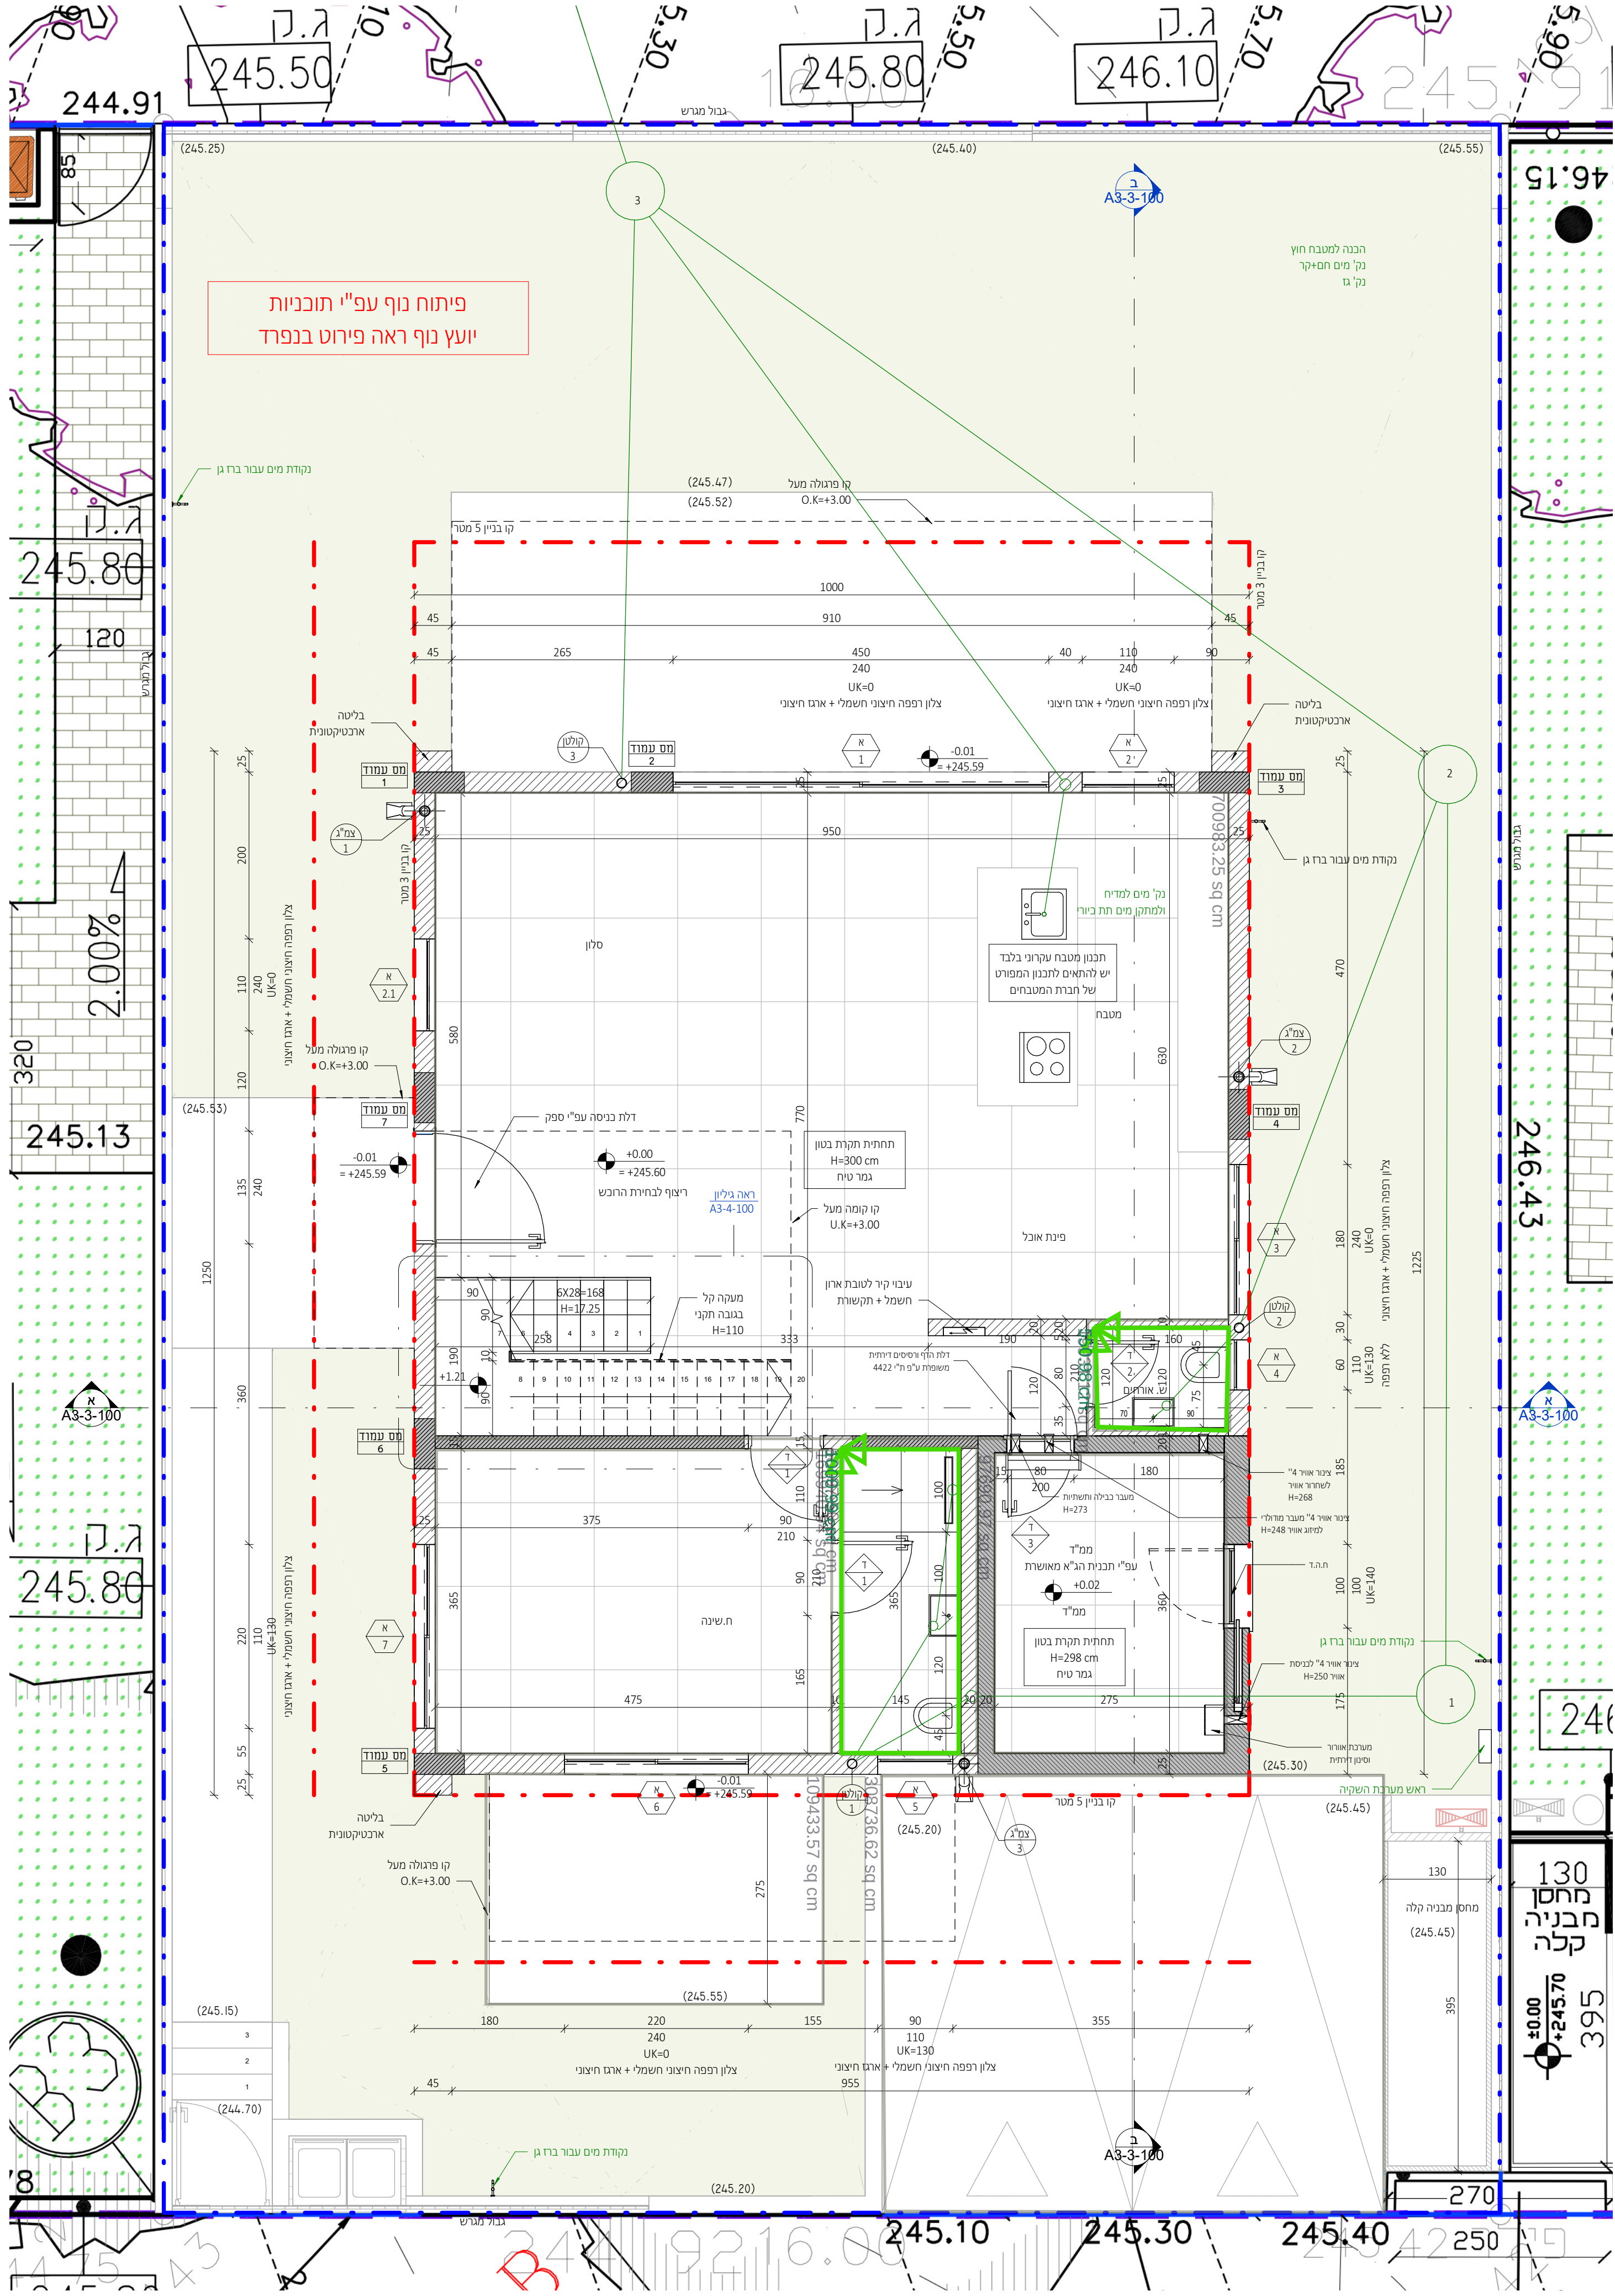

מתכונים:


ניהול פרויקט
מהיסוד - בו סולומון
פיקוח
מהיסוד - בו סולומון
קונסטרוקציה
ערן שילר
מיוזג אוויר
אייל ארז מהנדסים ויועצים בע"מ
אינסטלציה
איתן אלמסי
חשמל
איתן בסיס
אלומיניום
נוף
נתי בלוקא
חשמל חכם
חימום תת רצפתי
איטום
צבי טל
אקוסטיקה
מעליות
קרקע וביסוס
דיה הנדסת קרקע וביסוס
ירשני

+ 0.00 = 1245.60

הערת:
 תכנית זו איש לקראת ידע תכנית הוועיצים.
 נגבה אבסולוט. ראו תכנית פיתוח.
 הפיתוח הוא בראי קורות הבית, כולל, מדרגות, בדרות, שילובים, ריצופים, שטיפים, סביבה ויגון-ראו תכנית פיתוח.
 איסוס ותכנית הרצפת הבית במגנט עם הקרקע ביודות תמימ לאורך המעודים
 תחנת וועל התחרות: בקליות ווא עם פילוי (יגון)- ראו תכנית פיתוח/סנסורסקופ
 אדם קיבוצי ככל שפסס אופיקי הבולס תחבין.
 פסס תחבין תחבין- טפס פססס תחבין, תאסוד טפס פיקוד העורף.

המבצעים אחראים יסודית: עליו לבדוק ולקבוע את כל היחידות הבחינת
ובמסמך המבצעים.
במקרים של שטות או של התאמתה הבחינת/או לבנין, על הורעים על כך
לעבור על האדריכלי בעת המבצעים.
המבצעים יסודית: עליו לבדוק ולקבוע את כל היחידות הבחינת/או לבנין, על הורעים על כך
לעבור על האדריכלי בעת המבצעים.
המבצעים יסודית: עליו לבדוק ולקבוע את כל היחידות הבחינת/או לבנין, על הורעים על כך
לעבור על האדריכלי בעת המבצעים.

קרא קירות:

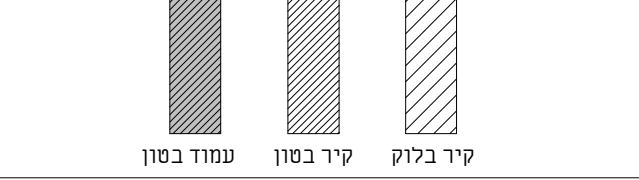[illegible]

אדריכלות

CLIENT NAME: _____; המזמין:

קבוצת רכישה נופיה

PROJECT NAME: הפרויקט:

בופיה - מגרש 17

DRAWING NAME: _____; שם הגליון:

תכנית קומה א

SHEET NUMBER: 99 גליון:

SCALE: קנה מידה: EDITION: דורה:

1 : 50

STATUS: סמטוט 1

למכרז	
-------	---

דמטט ע"י:	נבדק ע"י:
-----------	-----------

DATE: 20.12.25

DATE: 29.12.23




NeumanHaynerArchitects

ימן חיינר אדריכלים

office@nh-arch.com
www.nh-arch.com

זכויות יוצר / ע"פ הורחיות עו"ד

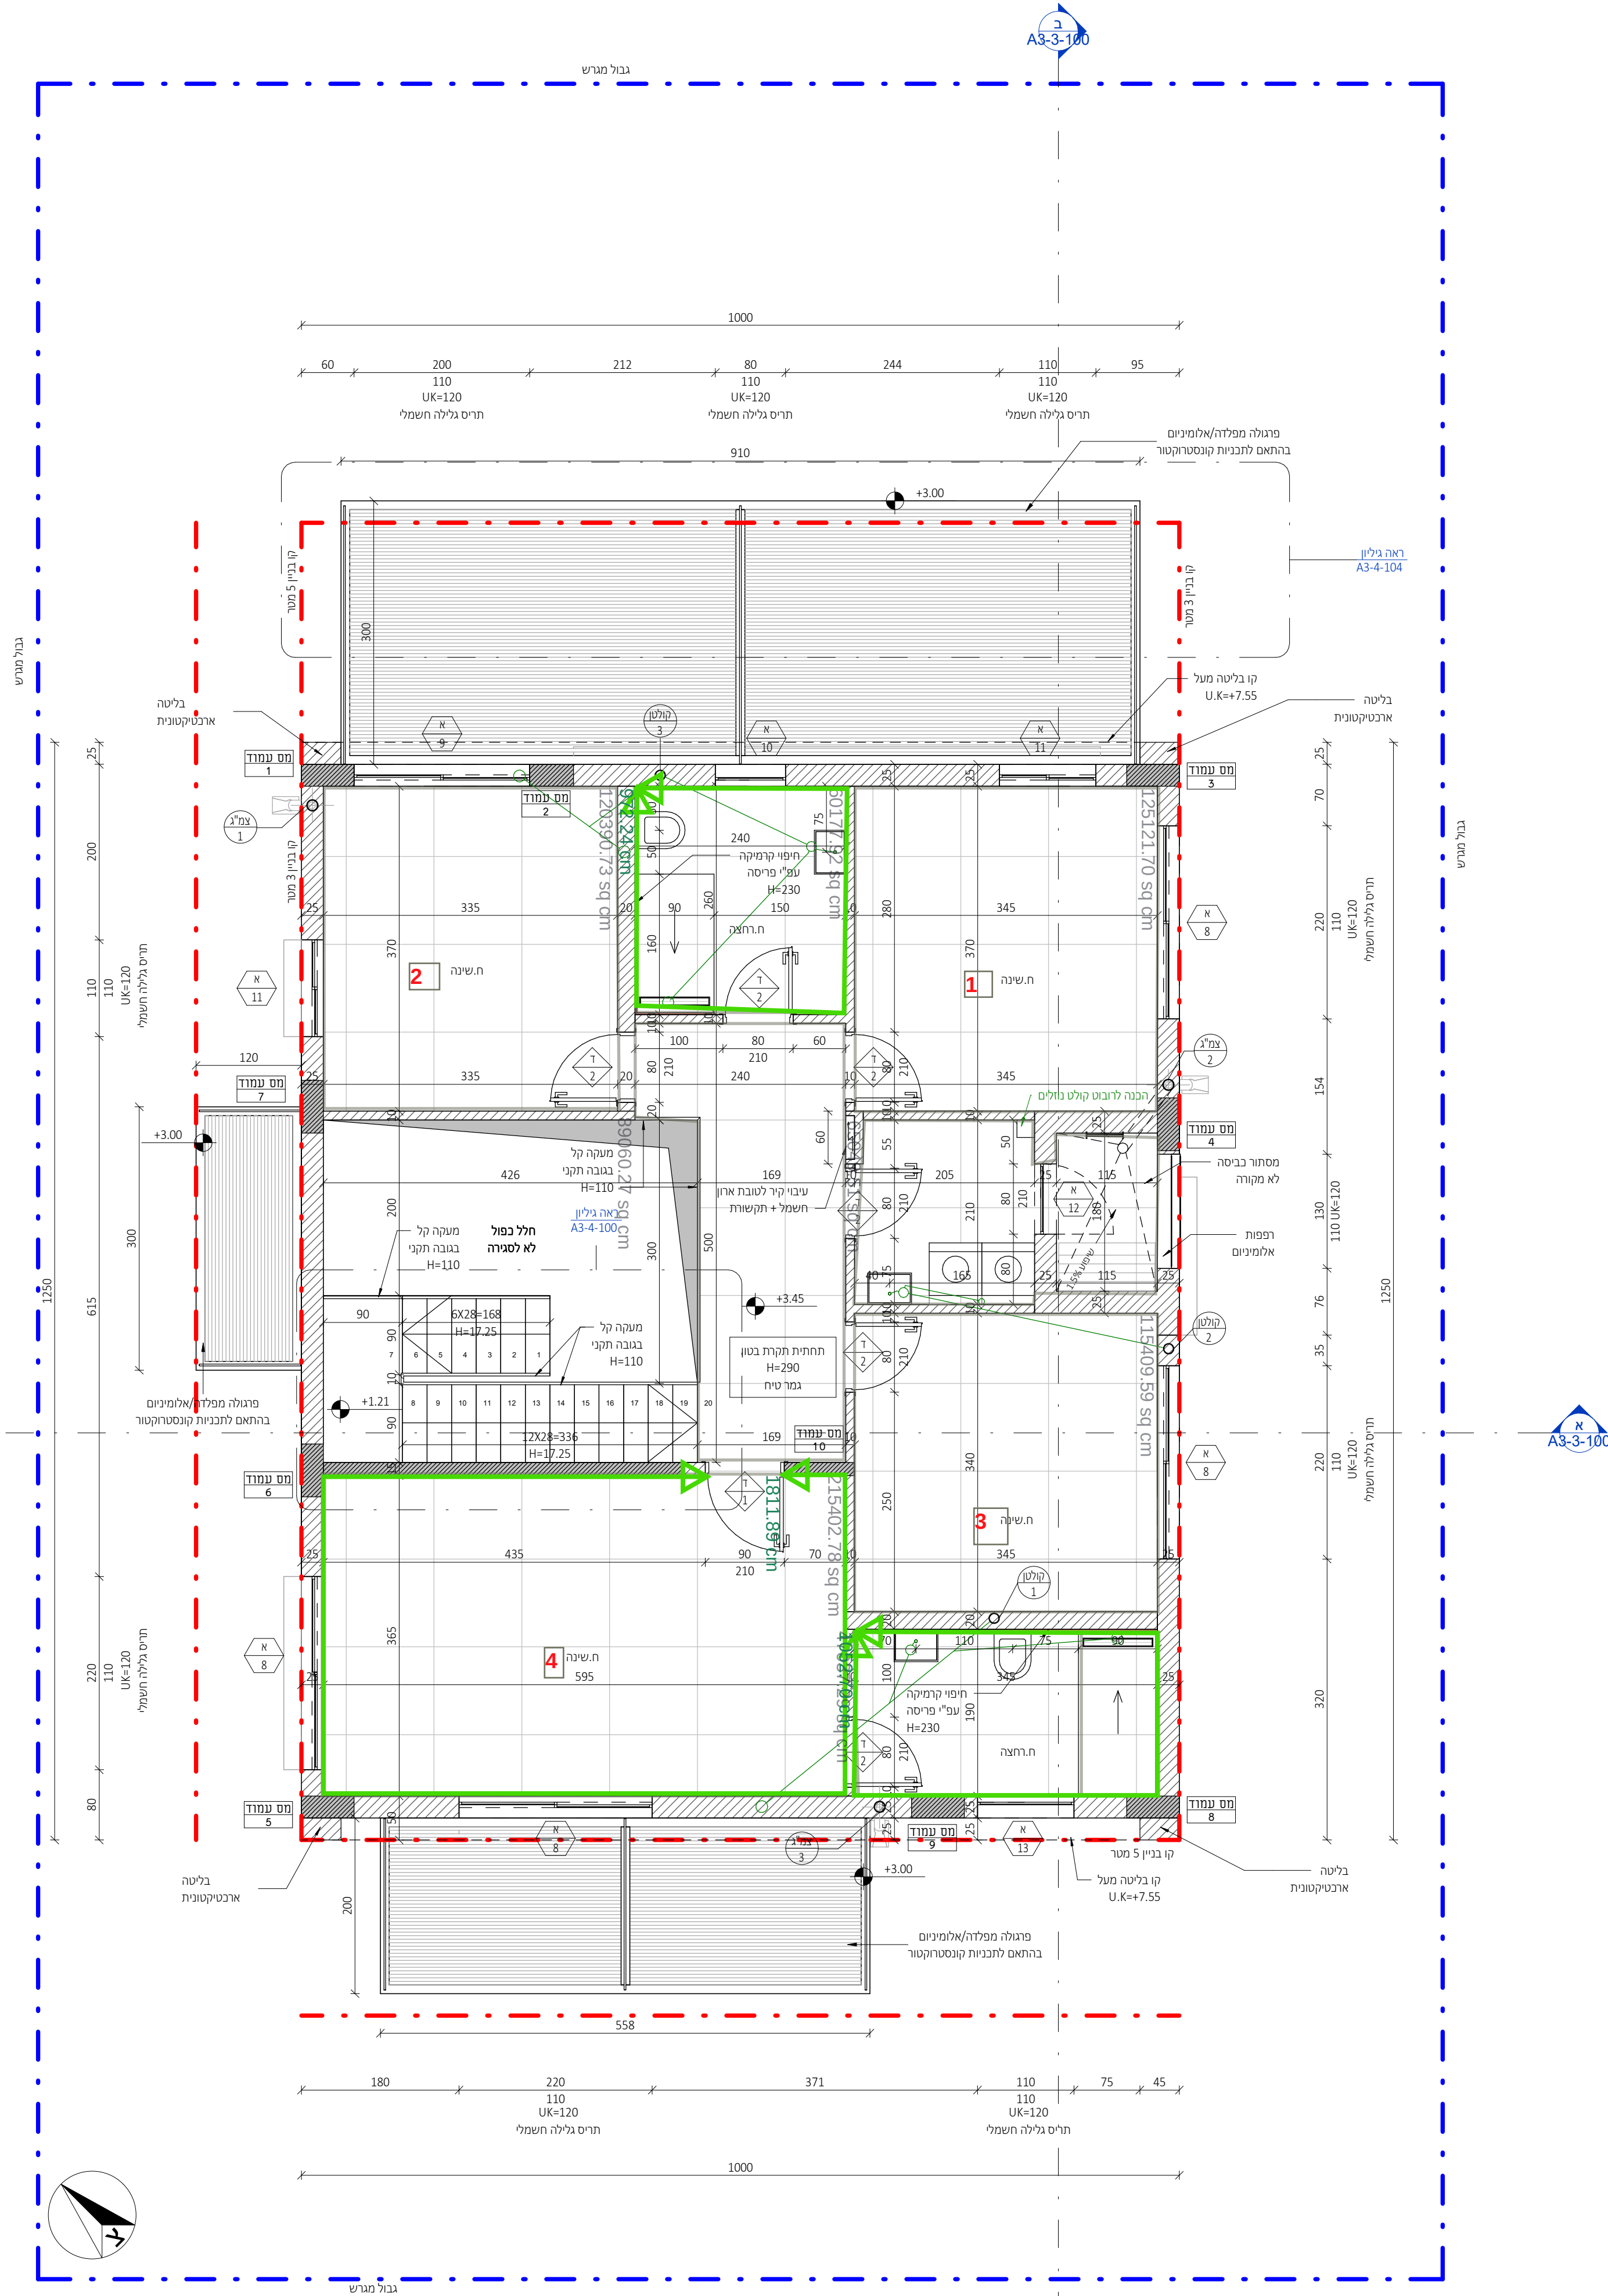


תכנית קומה א

1 : 50

- הערות:
1. יש לעבוד במקביל לתכניות יועצים המאושרות על ידי האדריכל.
 2. פרטי ספי חלון - עפ"י חוברת אלומיניום של הספק הנבחר ובתיאום מול אדריכל.
 3. חימום תת רצפתי (במידה ויש במגרש זה) עפ"י פרטי הספק ובתיאום מול אדריכל.
 4. יש לעבוד במקביל לתכניות עיצוב פנים (במידה ויש מעצב פנים במגרש זה) המאושרות על ידי האדריכל.
 5. באחריות הקבלן לעדכן את האדריכל על אי התאמה בין התכניות יועצים לאדריכלות.
 6. כל הדלתות לפי מפרט מצורף.
 7. כל אלמנטי הבטון יקבלו התייחסות תרמית לפי הנחיות יועץ.
 8. פרטי איטום, בידוד וניקוז עפ"י תכניות יועצים ובאחריות הקבלן.


פרטי איטום, בידוד וניקוז עפ"י תכניות יועצים ובאחריות הקבלן

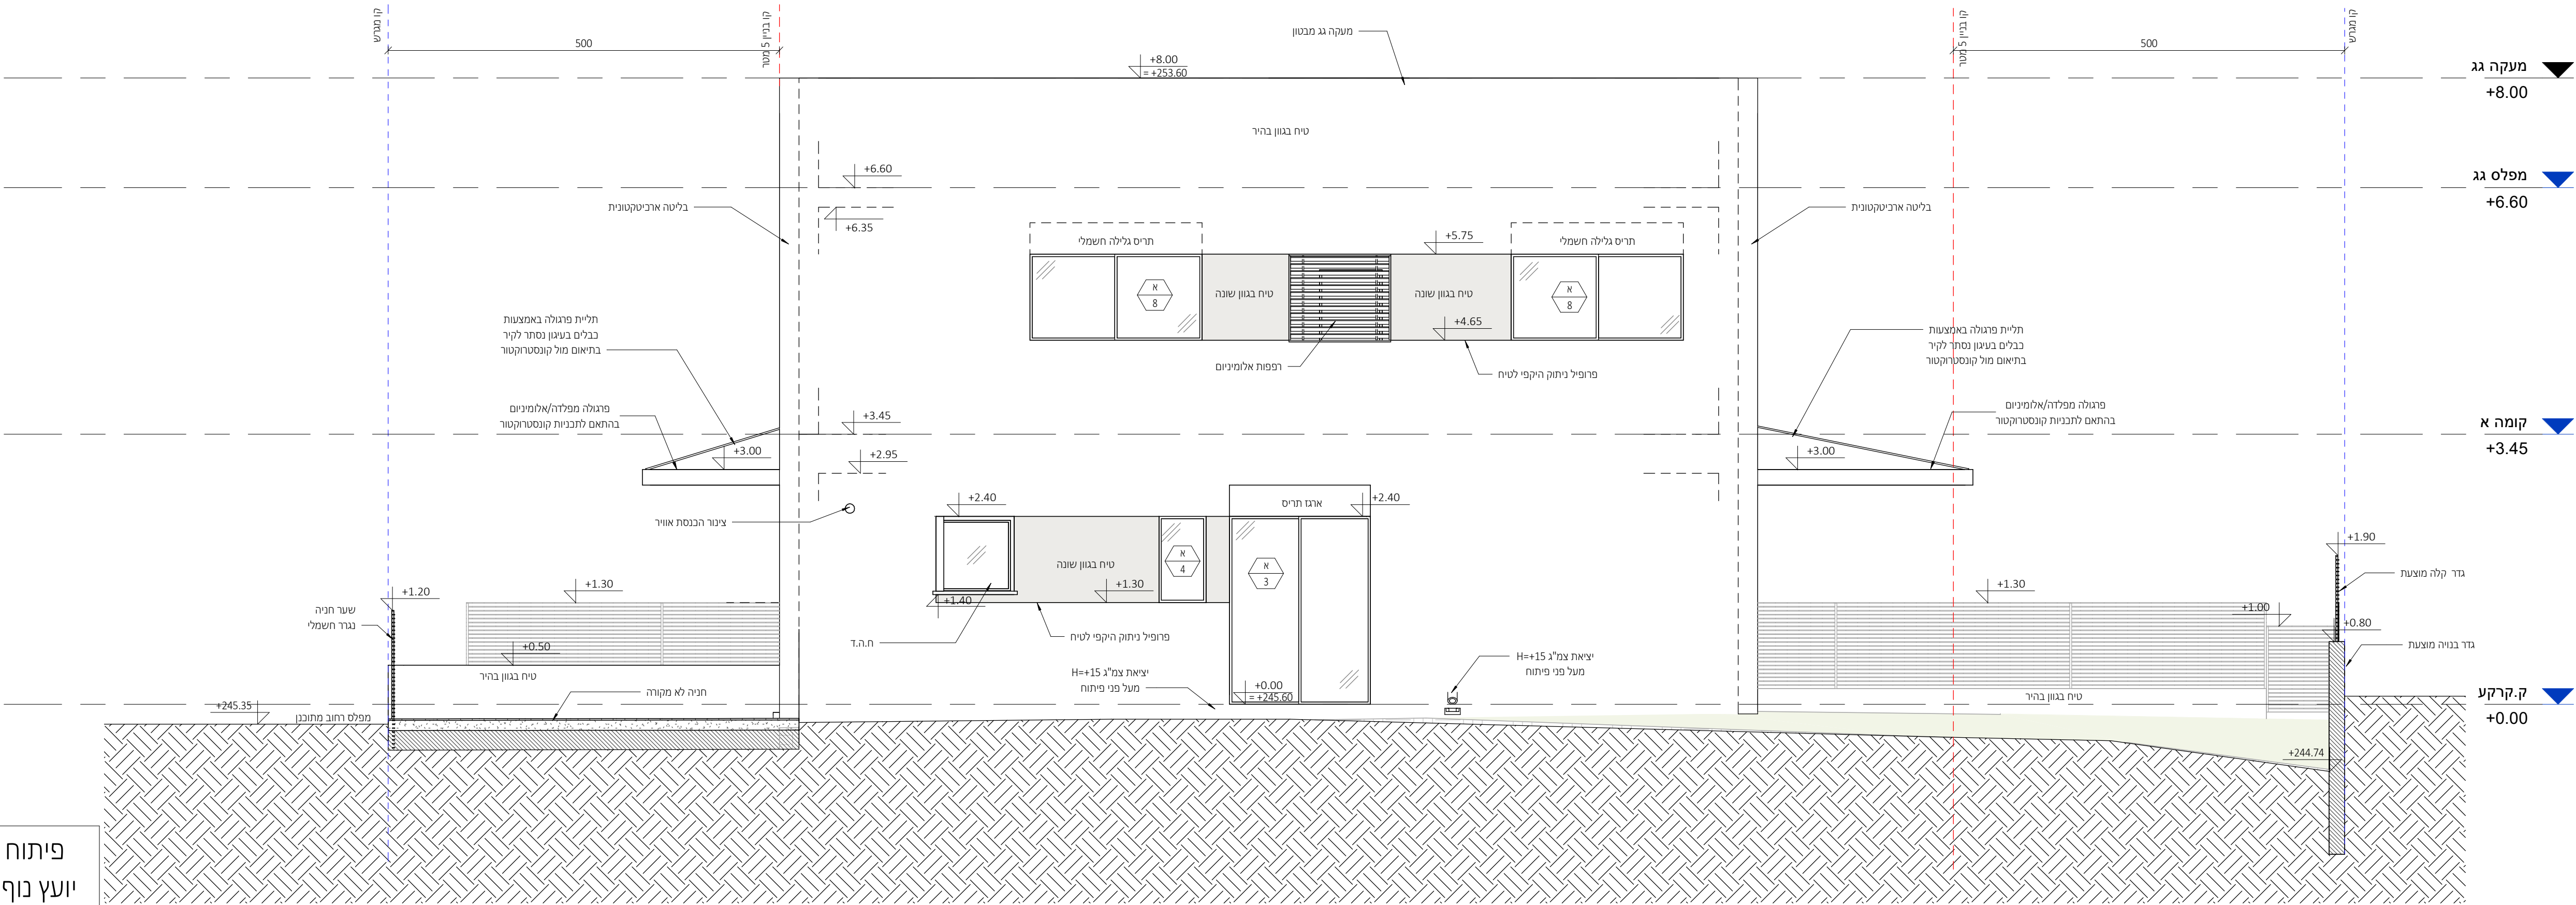

פיתוח נוף עפ"י תוכניות
יועץ נוף ראה פירוט בנפרד

חזית דרום מזרחית

1 : 50

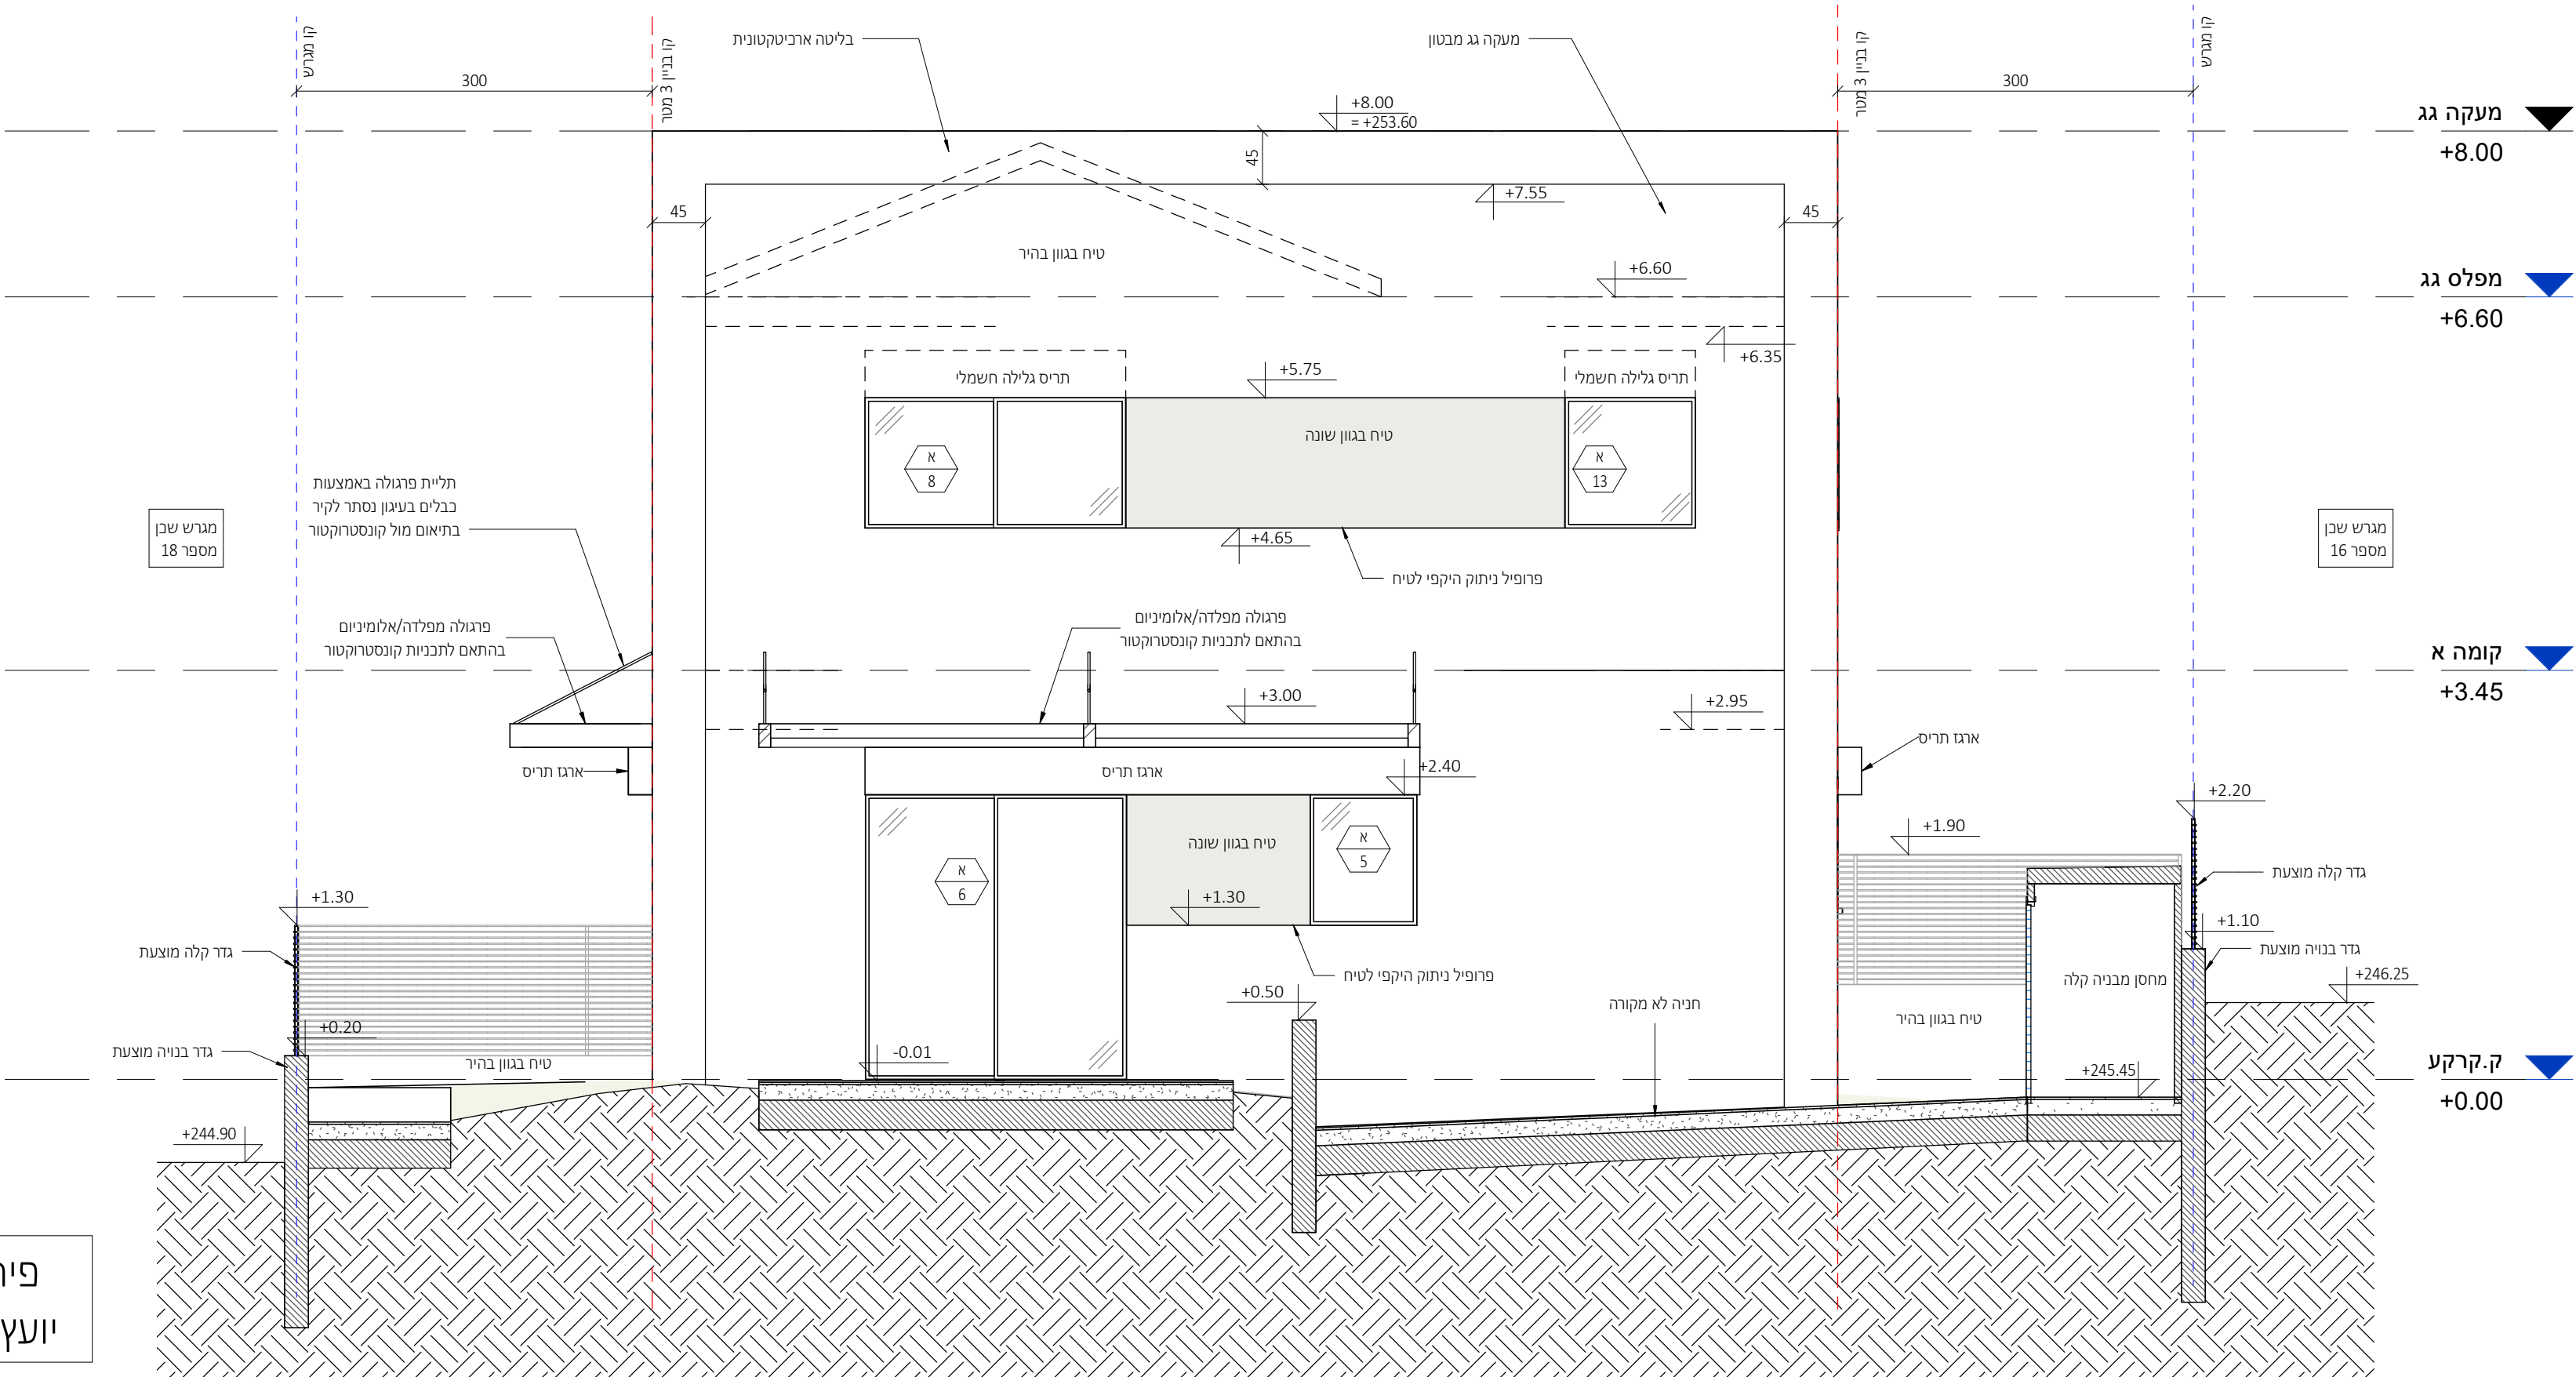

פיתוח נוף עפ"י תוכניות
ועץ נוף ראה פירוט בנפרד

חזית דרום מערבית

1 : 50


מתכונים:

ניהול פרויקט
מהיסוד - בו סולומון
פיקוח
מהיסוד - בו סולומון
קונסטרוקציה
ערן שילר
מיוזג אוויר
אילי ארז מהנדסים ויועצים בע"מ
אינסטלציה
איתן אלמסי
חשמל
איתן בסיס
אלומיניום
נוף
נתי בלוקא
חשמל חכם
חימום תת רצפתי
איטום
צבי טל
אקוסטיקה
מעליות
קרקע וביסוס
דיה הנדסת קרקע וביסוס
רישוי

הערות:
 1. לקראת דוד עם חביתיו העצים
 גבה אבן-מוסר: וא חביתו פחות
 הדיחות וא ב'ין קירות הבית (לא שלל מוסר)
 שפוטם הבית, חסד ויחזקו וא חבית פחות
 אסמם ורשעית הבית: בגמ' על השקט
 וקורות על הקרקע: ליתור וא על מילד
 וא אס' עובד על מילד שפוטם חסד
 וא חסד ויחזקו: אס' חסד ויחזקו, אסמם
 ורשעית חסד ויחזקו, אסמם ורשעית חסד ויחזקו

[illegible]

מקרא קירות:

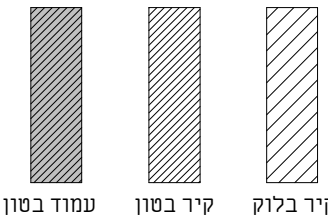[illegible]

אדריכלות

ליקטן שם:		המספר:	
קבוצת רכישה נופיה			
שם הפרויקט:		הפרויקט:	
נופיה - מגרש 17			
שם המשרד:		המחלקה:	
חזיתות 1			
שם היצרן:		היצרן:	
A3-2-200			
שם המודל:		המודל:	
1 : 50		EDITION: 	
סטוס:		סטוס ע"י:	
למכור			
נבדק ע"י:		סטוס ע"י:	
29.12.25			
שם היצרן:		היצרן:	

פרטי איטום, בידוד וניקוז עפ"י תכניות יועצים ובאחריות הקבלן

מתכונים:


ניהול פרויקט
מהיסוד - בו סולומון
פיקוח
מהיסוד - בו סולומון
קונסטרוקציה
ערן שילר
מיוזג אוויר
אילי ארז מהנדסים ויועצים בע"מ
אינסטלציה
איתן אלמסי
חשמל
איתן בסיס
אלומיניום
נוף
נתי בלוקא
חשמל חכם
חימום תת רצפתי
איטום
צבי טל
אקוסטיקה
מעליות
קרקע וביסוס
דיה הנדסת קרקע וביסוס
רישוי

$$\pm 0.00 = +245.60$$

הערות:
 תכנית זו אינה מקרית, ויש לקרוא יחד עם תוכנית הורעיסם.
 נגבה אבסולוטית, דא תכנית פחות
 המידות הן בין קירות הבניה (לא כולל סמ"מ).
 תוכנית השטח סביב חתכי הבניה, כליל, מדגרת, גורות, שביליים, ריצופים,
 שופטים מדרגים, מנהר יתרון-דא תכנית פחות.
 אסוס קירות ורפפת התבנית במגע עם הקרקע וכידוד תרמי לאורך המעודדים
 והקורות וכל תכנית-גליות זו עם מיליון (גורן)-דא תכנית ונוסטרסוס
 אסוס כיצוד ככל מדרש אופיקי חתכי-גליות.
 אסוס תרמי במחיר-דא ספרס תרמיקלי, ואסוס זה פיקוד העורף.

[illegible]

קרא קירות:

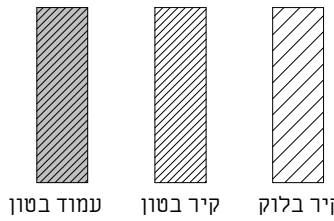[illegible]

אדריכלות

המזמין:

CLIENT NAME: _____: המזמין:

קבוצת רכישה נופיה

הפרויקט

PROJECT NAME: הפרויקט:

בופיה - מגרש 17

ט הגליון:

DRAWING NAME: תגלית

חזיתות 2

פר גליון:

SHEET NUMBER: 99 גליון:

A3-2-201

דורה:

SCALE: קנה מידה: EDITION: דורה:

1 : 50

STATUS: סמסס 1

למכור	
-------	---

דטטע ע"י: _____ נבדק ע"י: _____


DATE: 29.12.25 י"ד

NeumanHaynerArchitects

נמנו חנוכה אדוורכלות


office@nh-arch.com
www.nh-arch.com

צביה / ח' תשס"ח

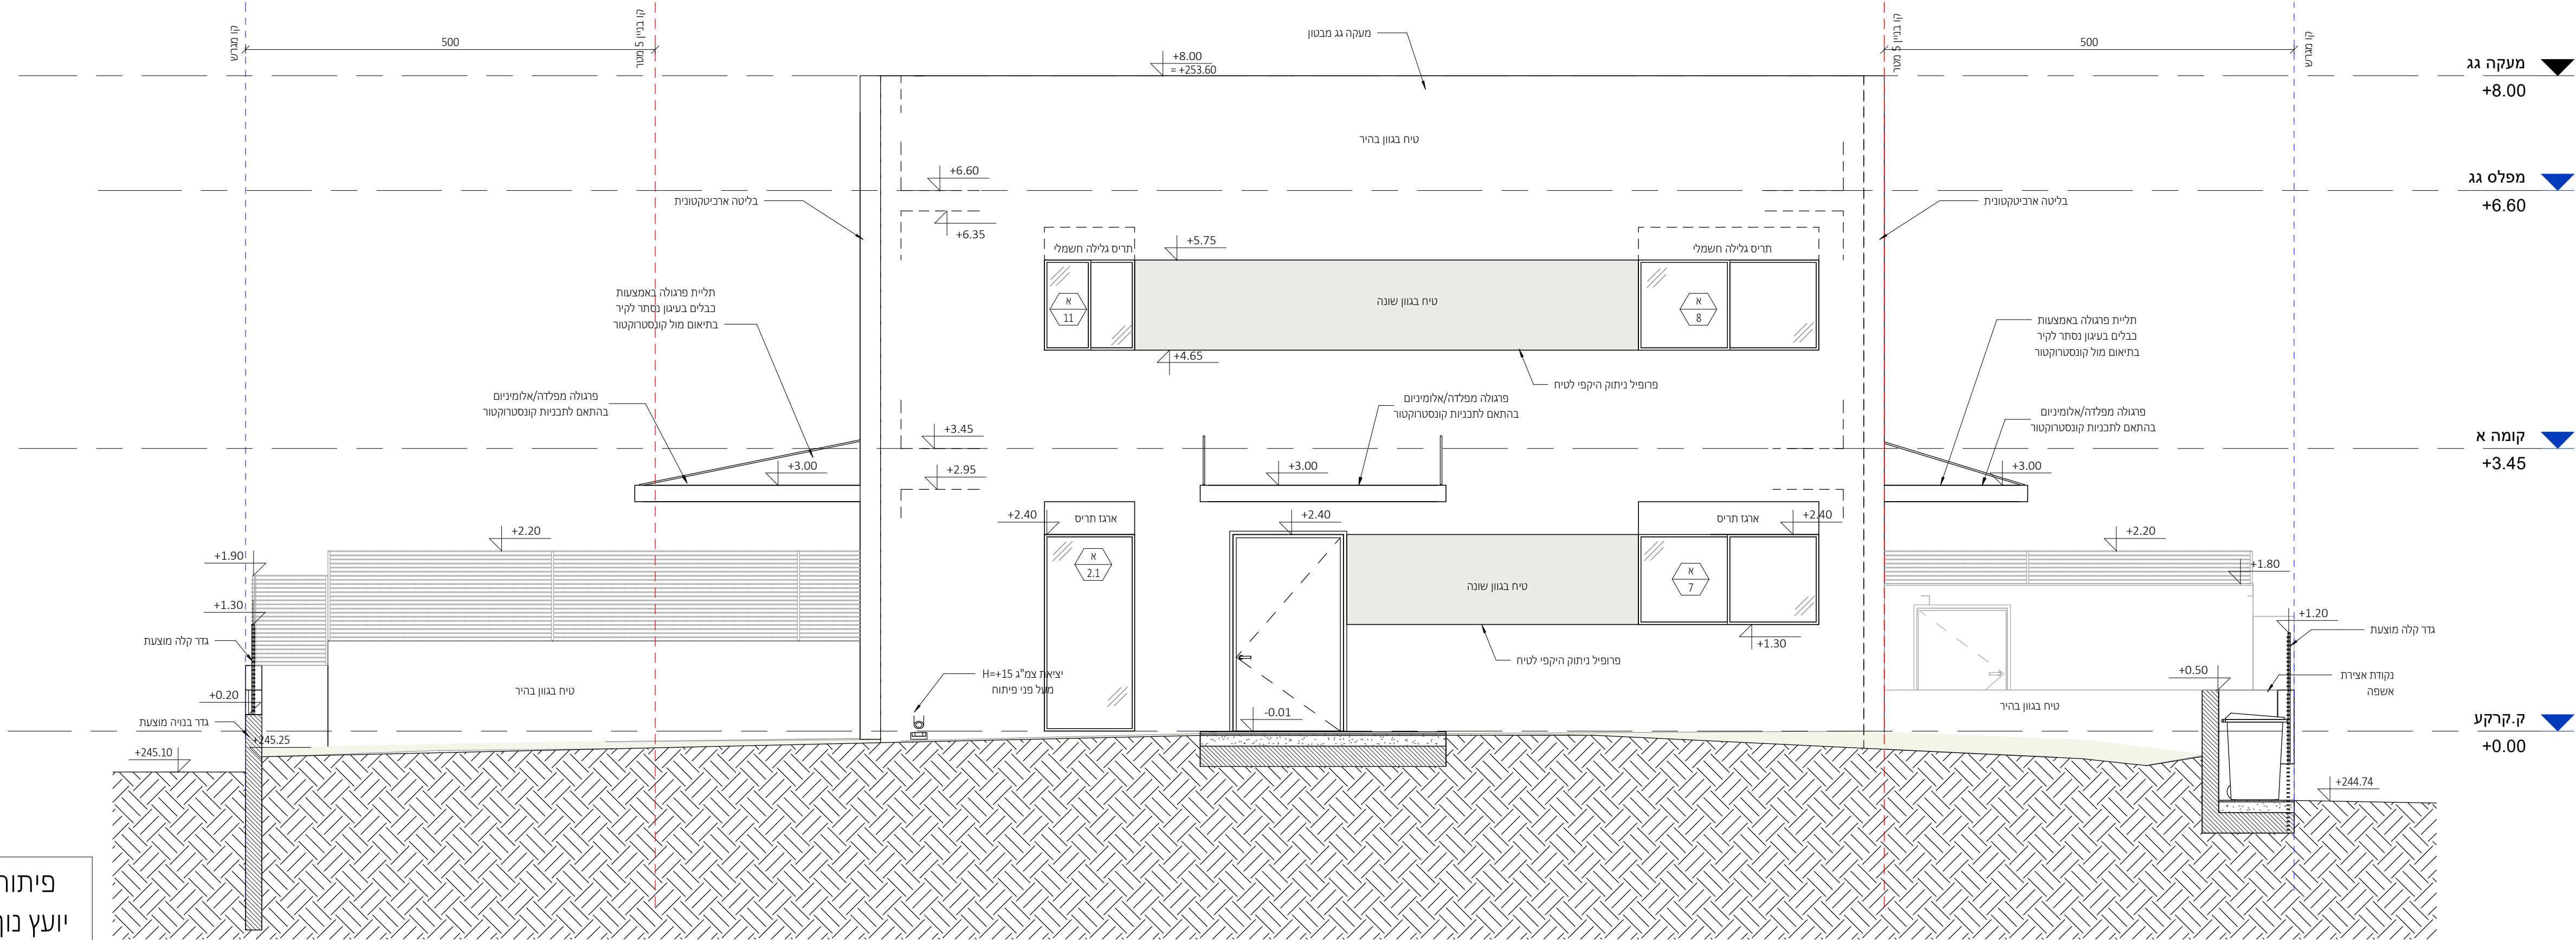

פיתוח נוף עפ"י תוכניות

יועץ נוף ראה פירוט בנפרד

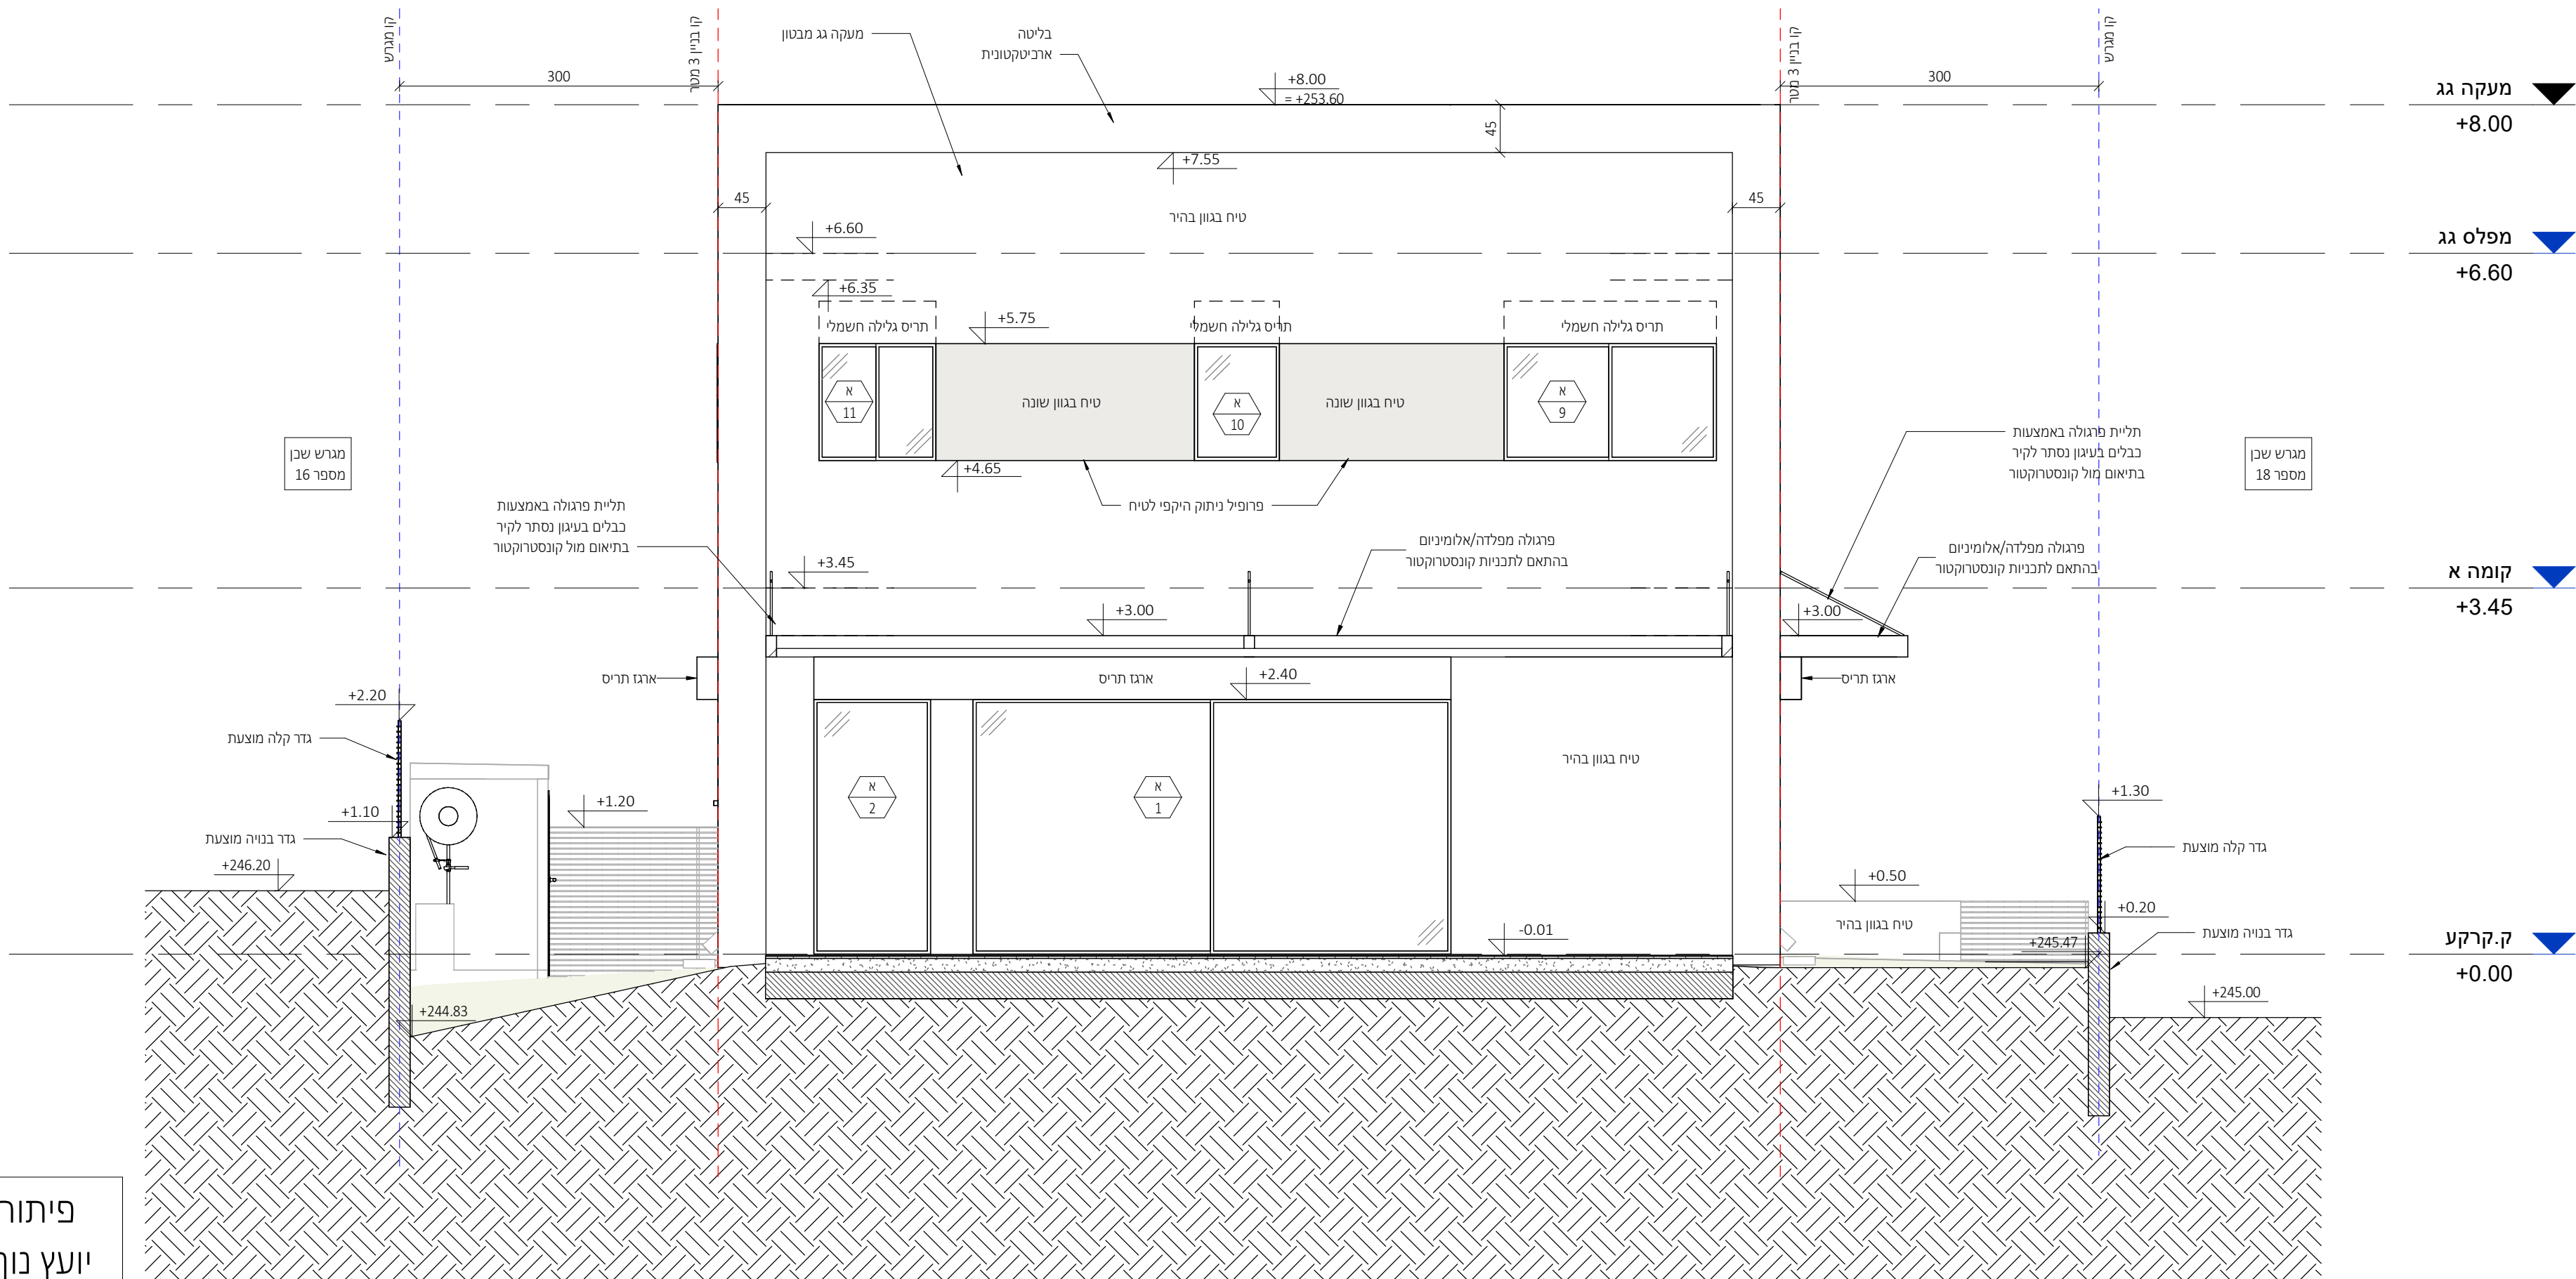

פיתוח נוף עפ"י תוכניות

יועץ נוף ראה פירוט בנפרד

חזית צפון מזרחית

1 : 50

פרטי איטום, בידוד וניקוז עפ"י תכניות יועצים ובאחריות הקבלן

מתכונים:


ניהול פרויקט
מהיסוד - בו סולומון
פיקוח
מהיסוד - בו סולומון
קונסטרוקציה
ערן שילר
מיזוג אוויר
אייל ארז מהנדסים ויועצים בע"מ
אינסטלציה
איתן אלמסי
חשמל
איתן בסיס
אלומיניום
נוף
נתי בלוקא
חשמל חכם
חימום תת רצפתי
איטום
צבי טל
אקוסטיקה
מעליות
קרקע וביסוס
דיה הנדסת קרקע וביסוס
רישוי

הערות:


1. תבנית זו נלקחה יחד עם תוכנית העיונים.
2. כל מילוסלסל – אחד תבנית אחת.
3. המידות הן ברוחב ובהגובה (כלל המידות הן: 100, 150, 200, 30300

[illegible]

אדריכלות

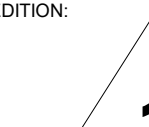
CLIENT NAME:		השם המלא:	
קבוצת רכישה נופיה			
PROJECT NAME:		שם הפרויקט:	
נופיה - מגרש 17			
DRAWING NAME:		שם התוכנית:	
חתכים			
SHEET NUMBER:		מספר גיליון:	
A3-3-100			
SCALE:	קנה מידה:	EDITION:	דפוס:
1 : 50	סטוס		
TATUS:	למכר		
נבדק ע"י:		דפוס ע"י:	
DATE:		תאריך:	
29.12.25			

פיתוח נוף עפ"י תוכניות
יועץ נוף ראה פירוט בנפרד

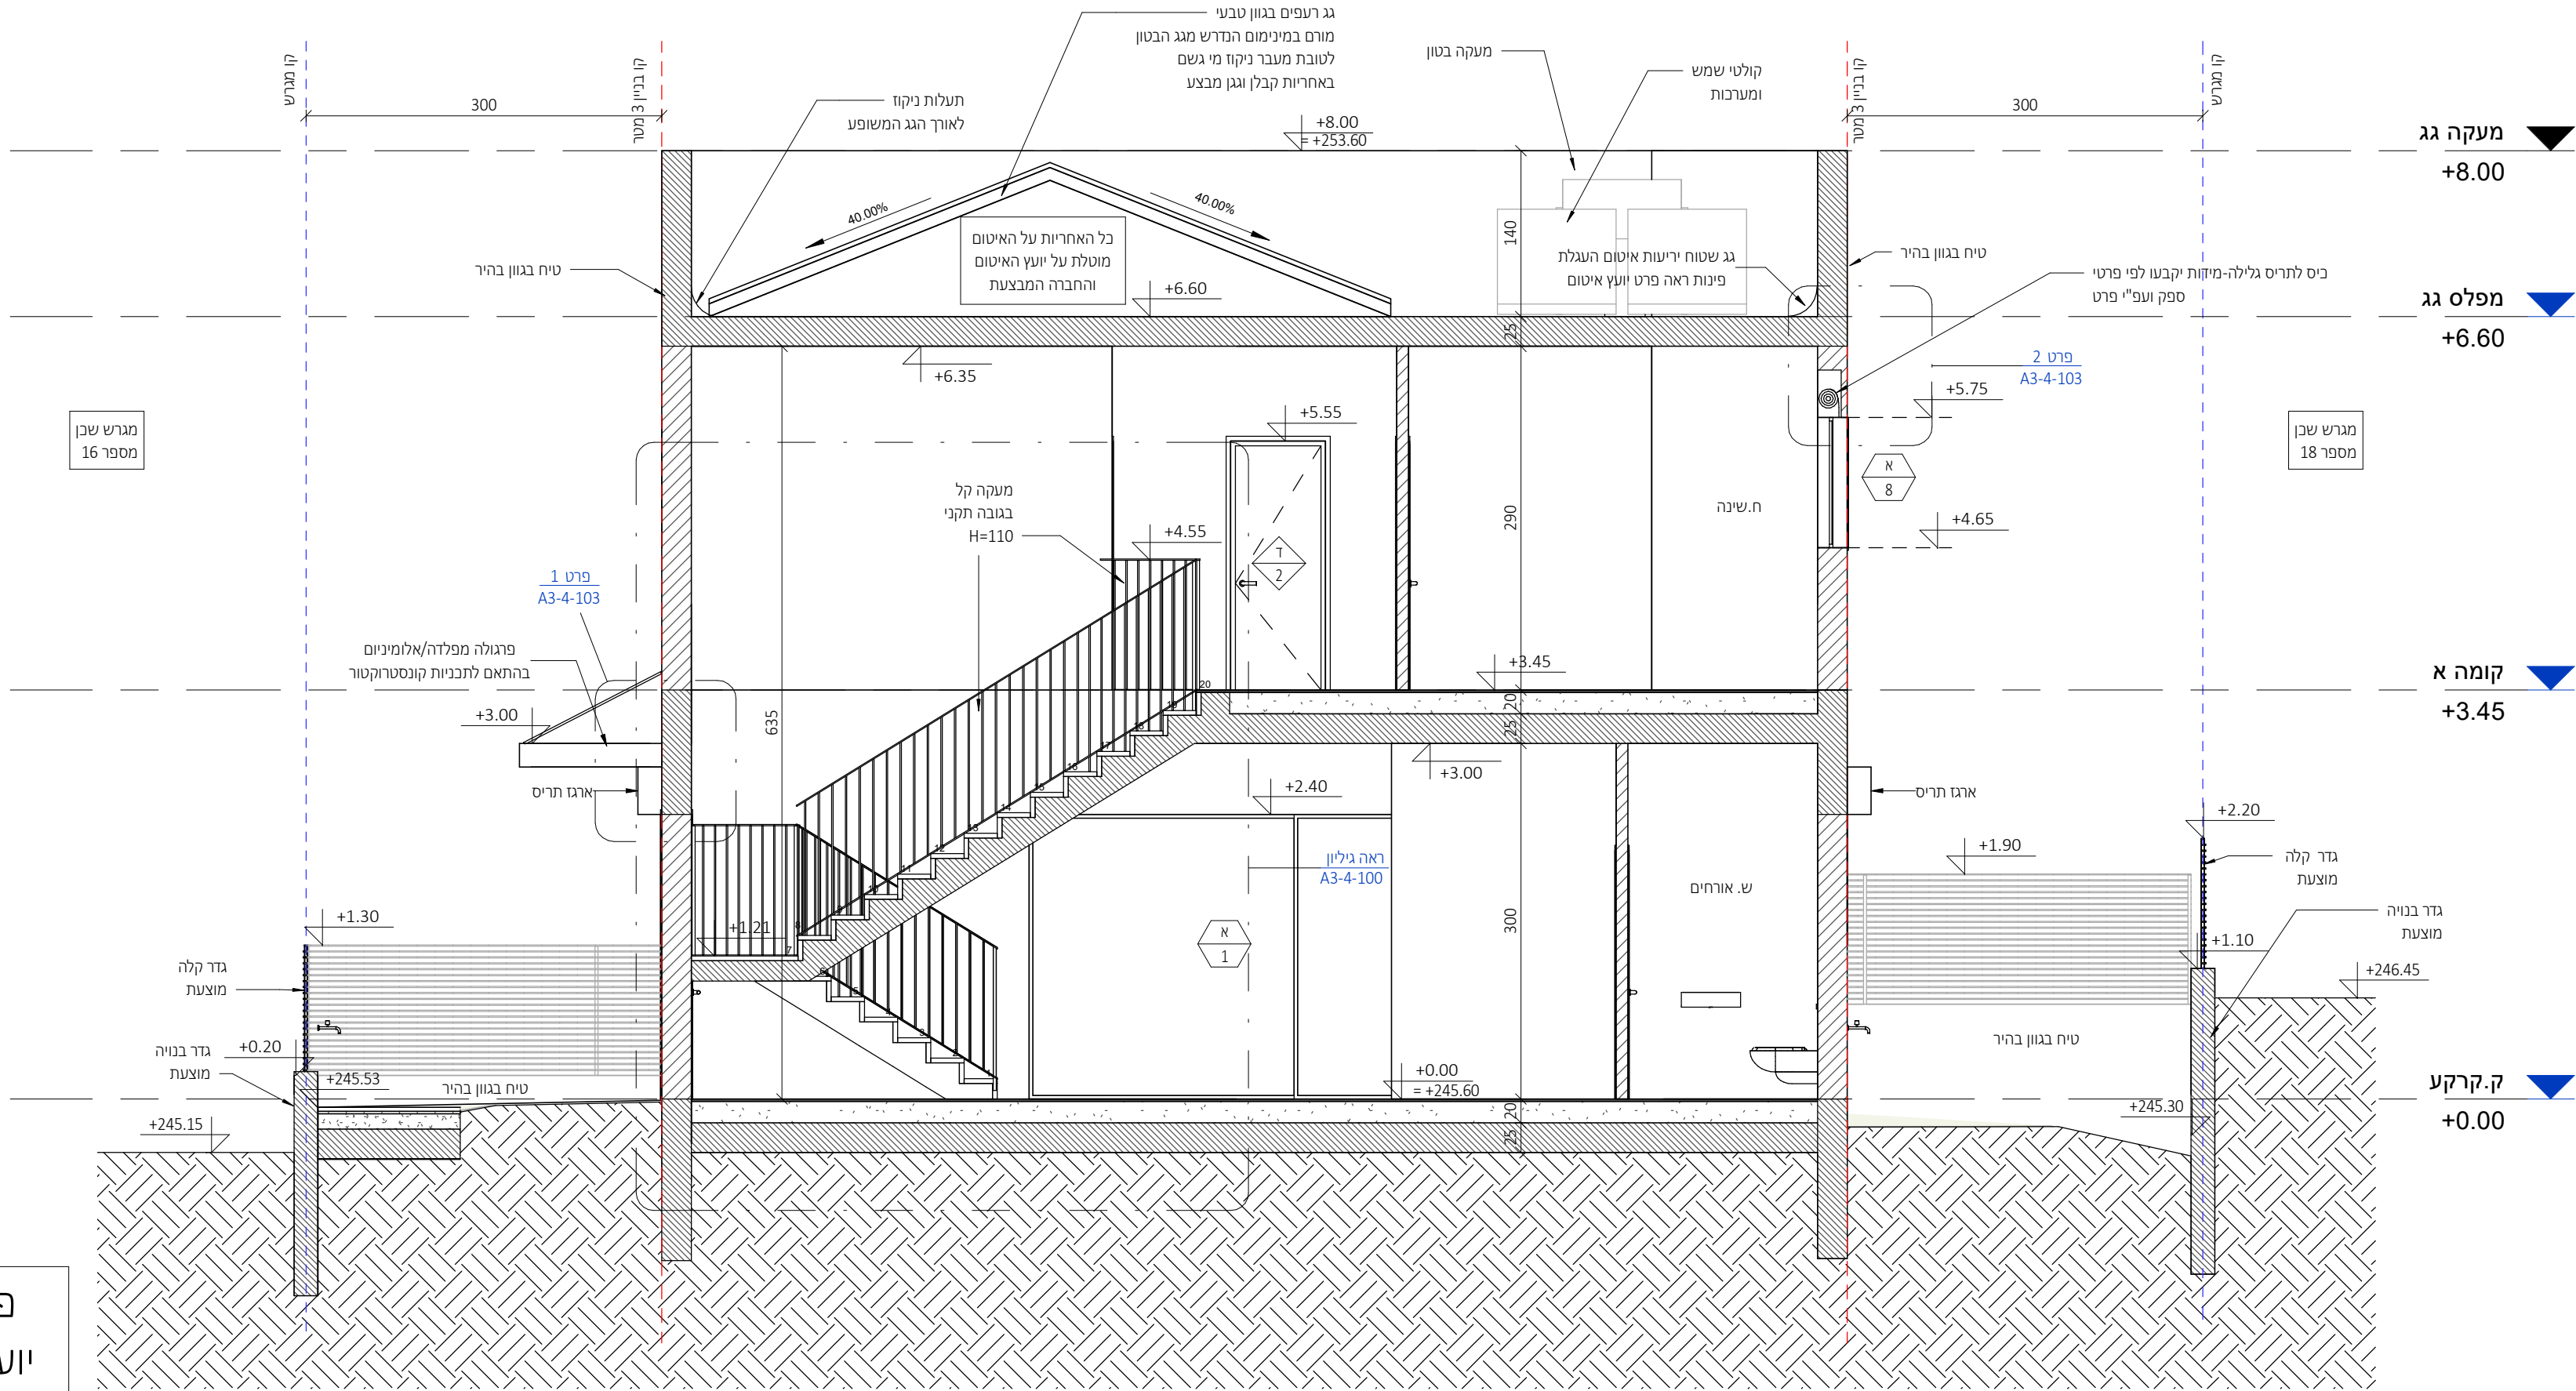

חתך א-א

1 : 50

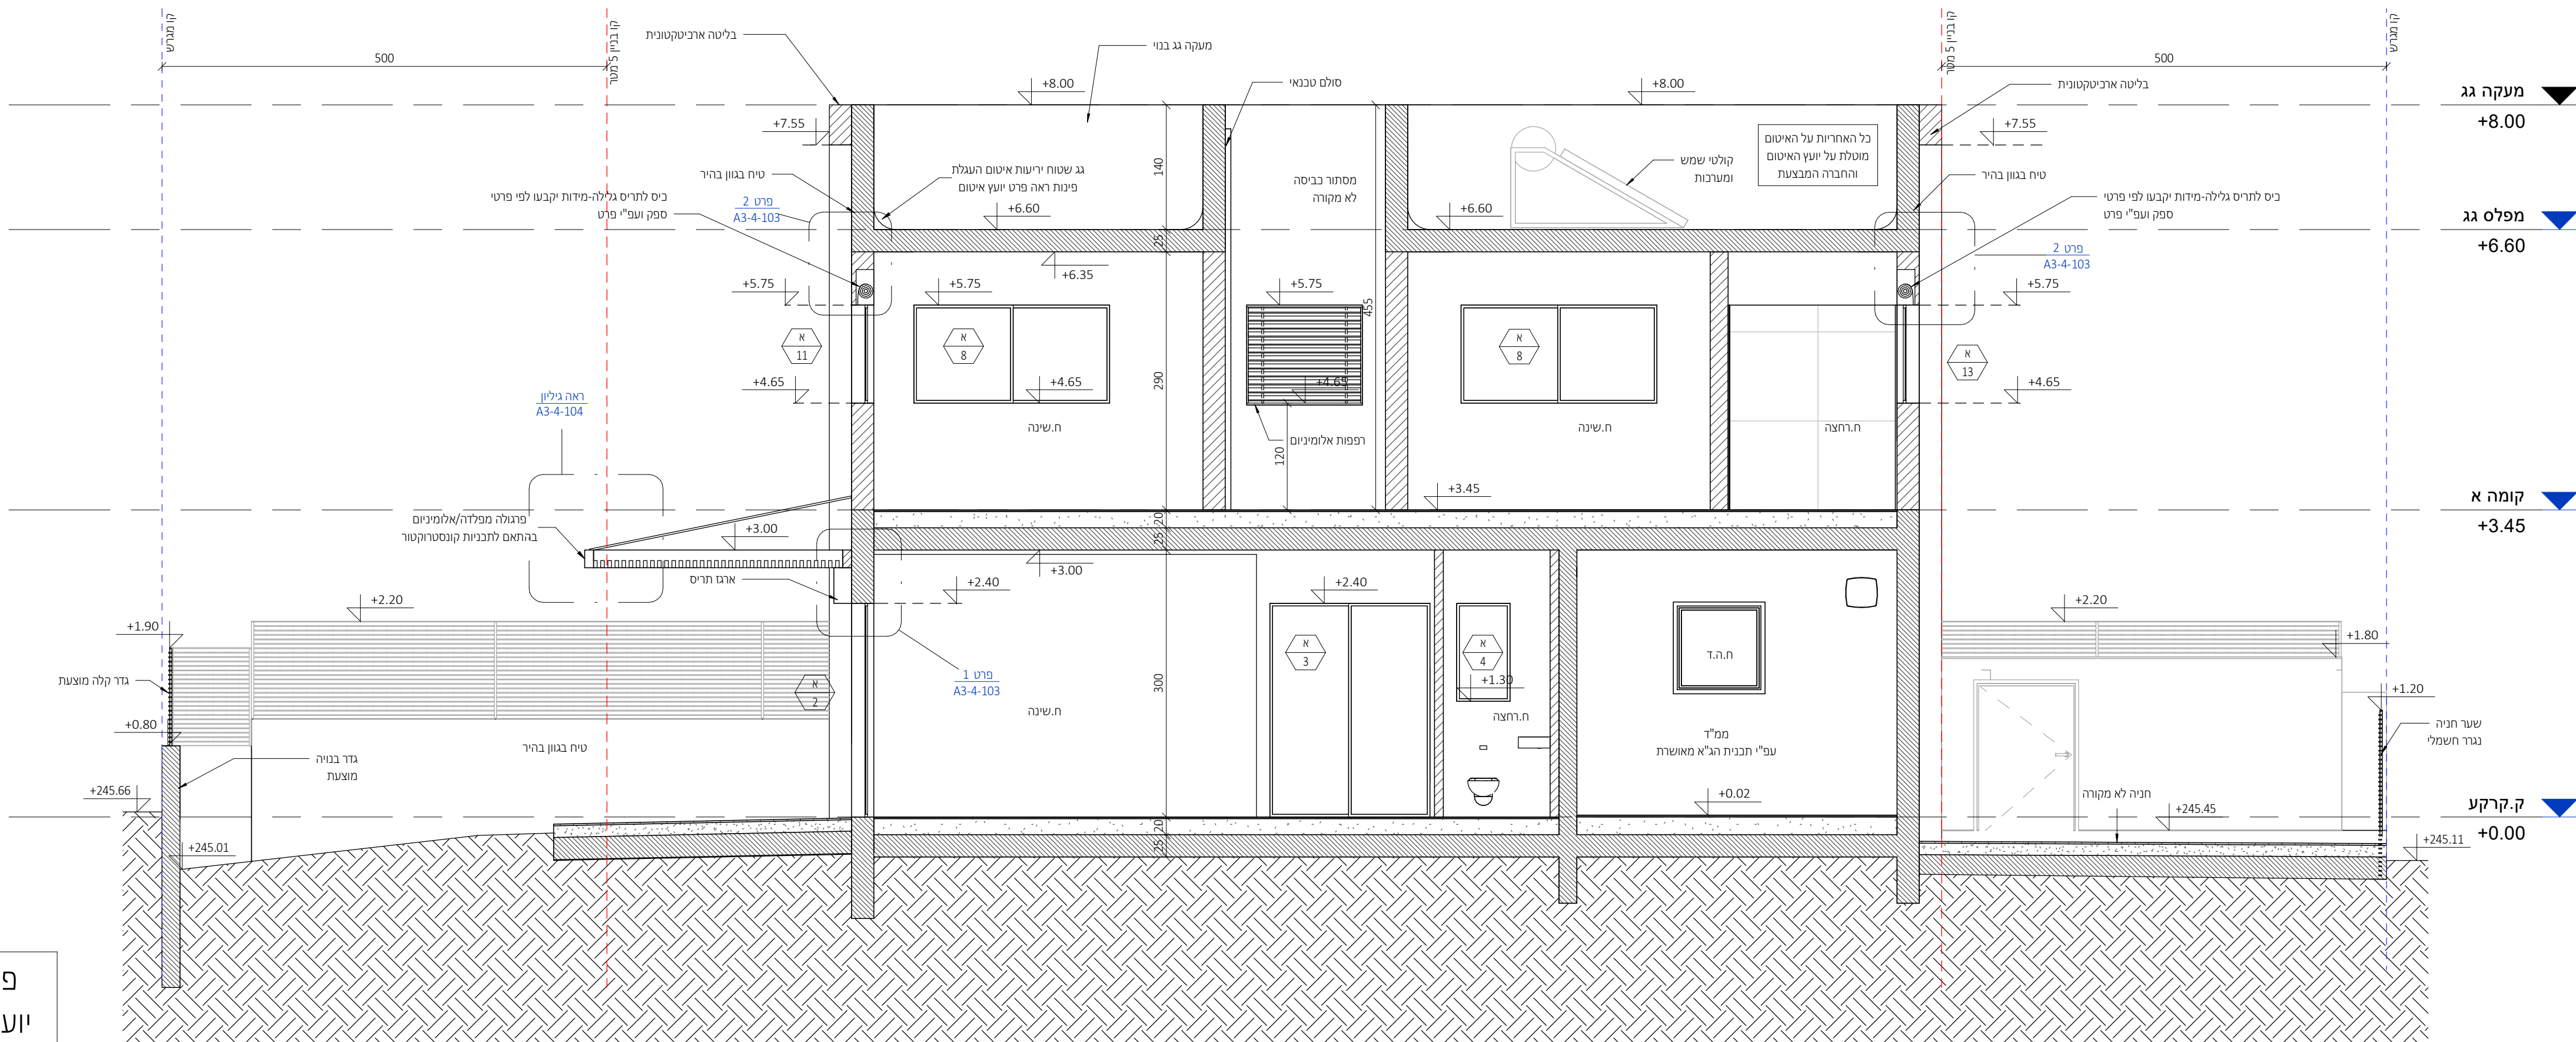

חתך ב-ב

1 : 50

מתכננים:

ניהול פרויקט
מהיסוד - בו סולומון
פיקוח
מהיסוד - בו סולומון
קונסטרוקציה
ערן שילר
מיזוג אוויר
אייל ארז מהנדסים ויועצים בע"מ
אינסטליציה
איתן אלמסי
חשמל
איתן בסיס
אלומיניום
נוף
נתי בלוקא
חשמל חכם
חימום תת רצפתי
איטום
צבי טל
אקוסטיקה
מעליות
קרקע וביסוס
דיה הנדסת קרקע וביסוס
רישוי


± 0.00 = +245.60
הערות: 1. תכנית זו יש לקרוא יחד עם תכנית הוויסטים. 2. גובה אבסורדטי - ראו תכנית פיתוח. 3. המידות הן בין קירות הבניה ולא כולל פחים. 4. פיתוח השטח סביב הבנוי, כולל, מדרגות, נדרות, שבילים, ריצופים, שטחים בגובה, חניה וכו' ראו תכנית פיתוח. 5. איסוס קירות ורצפות הבנוי כמנוע עם הקרקע ובירידות חוצי לאורך המעברים והקירות של המעברות. כלירות או עם סימני גומי - ראו תכנית קונסטרוקציה. 6. אף דים יבוצע בכל מישור אופקי הבולם חתונות. 7. סיוח חומי בממיד" ע"פ מפרט חומקיר, מאושר ט"י פיקוד העורף. הבטע אחראי לסידור: עליו לבקר ולבדוק את כל המידות בתכנית ובקטע המבנה. במסגרת של מידות או אי התאמה בתכנית /או בבנוי, עליו להודיע על כך מיד לאדריכל בסדר המשך עבודותיו. התכנית יושמט או ויק בתכנית שאושר לכיצוע. המבצע יחזיק באחר, בכל מה, של מידות של תכנית. אח לקבוע מידות על ידי חזירה בשטח. התכנית הנה רכוש האדריכל ואין לשנות כל שימוש בה או ברעיונות הגלומים בה, אלא באישור בכתב מאדריכל. חומס /או יושע אשר שמו רשום בתכנית זו, נושא לכיד באחריות המקצועית והמקצועית לתכנית. על המפתח והמכלול לודא התאמת התכנית האדריכלית "כיצוע" לתכנית יחית, המכל התכנית והאשרות ע"י כל גורמים ורשמיים. התכנית כוללת את כל האחריות והידוע על ליום תוצאת.

משרד קירות:
קיר בלוק קיר בסון מעוד בסון

תאריך	תיאור	מהדורה
22.09.2025	מכרז	1

אדריכלות	
המחיר:	CLIENT NAME:
קבוצת רכישה נופיה	
הפרויקט:	PROJECT NAME:
נופיה - מגרש 17	
הגליון:	DRAWING NAME:
גליון מדרגות	
מספר גליון:	SHEET NUMBER:
A3-4-100	
הדורה:	EDITION:
קנה מידה:	SCALE:
1	As indicated
סטוס ע"י:	סטוס
נבדק ע"י:	למכר
תאריך:	DATE:
29.12.25	

NeumanHaynerArchitects
נויון חיינר אדריכלים מודד התודים 2, בית חירות 09-9545842 78 office@nh-arch.com www.nh-arch.com
זכיות יימור / ע"פ הנחיות ע"ד

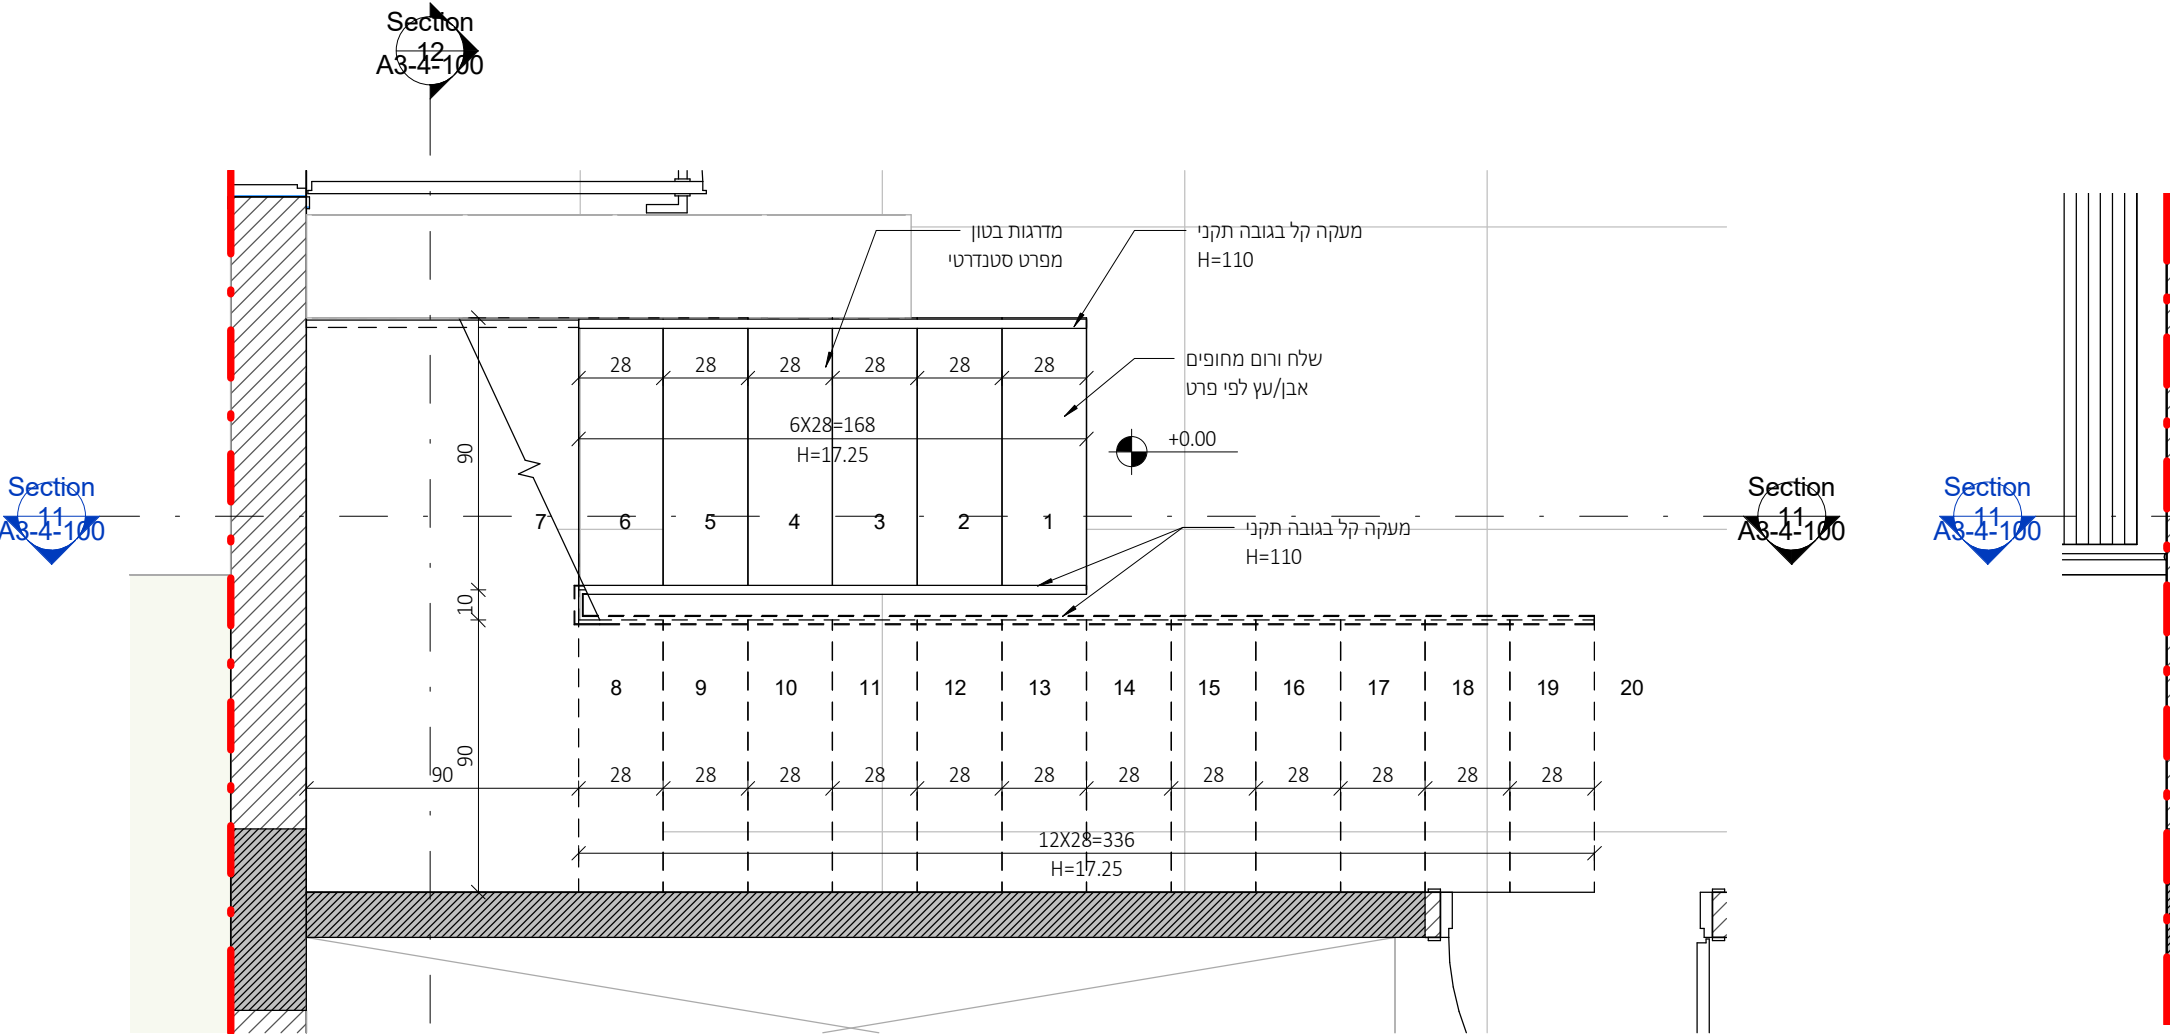


תכנית מדרגות קומת קרקע

1 : 25




תמונה להמחשה בלבד

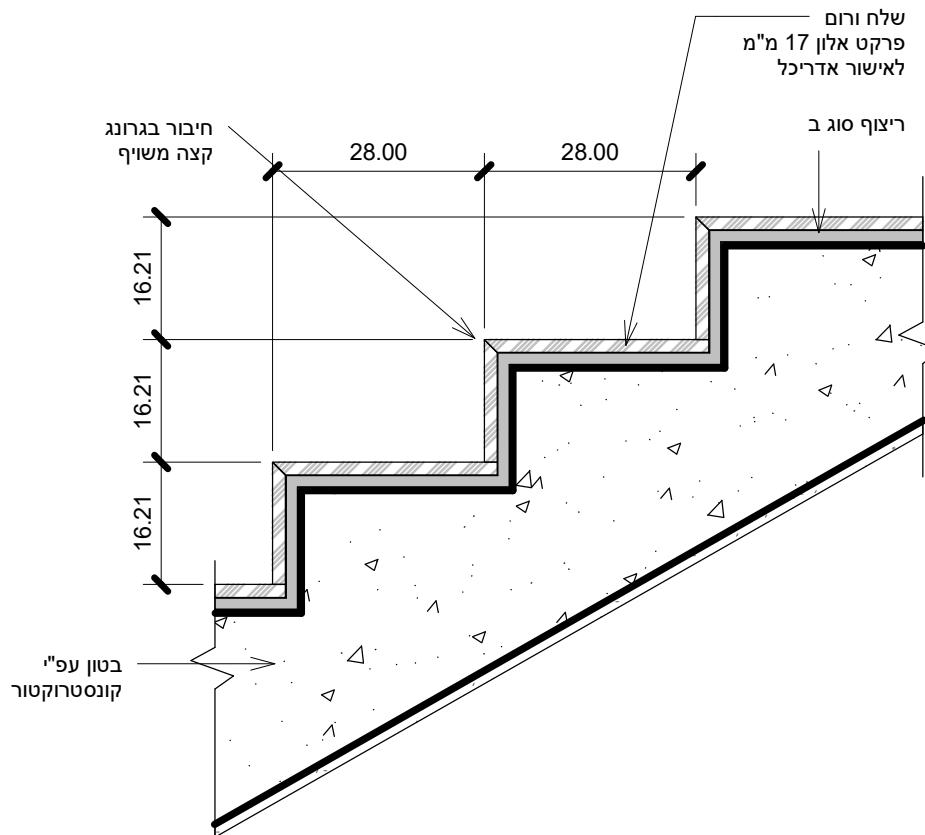


פרט מדרגות בטון בחיפוי פרקט

1 : 10

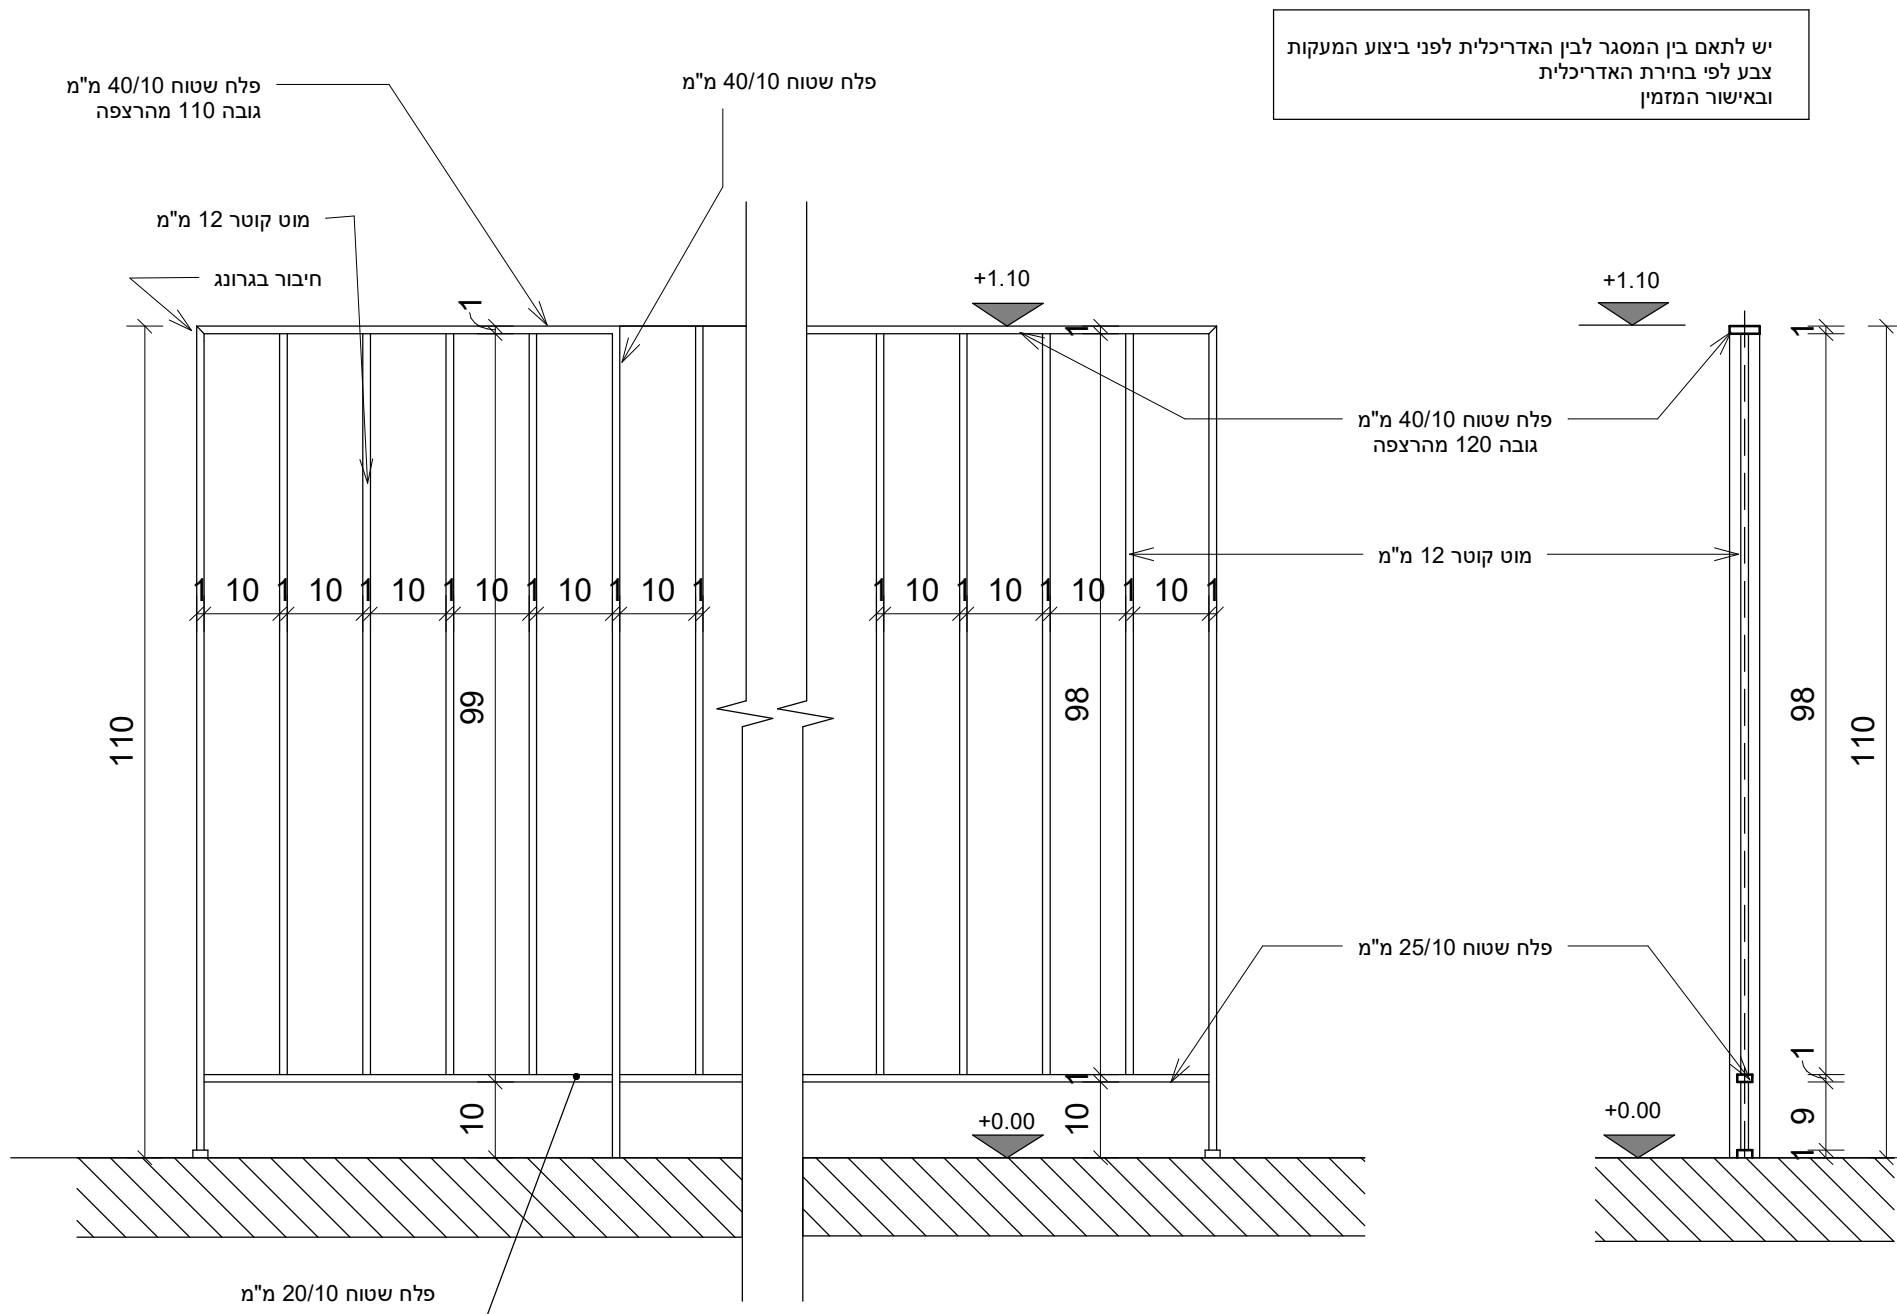


מעקה אנכי

1 : 10

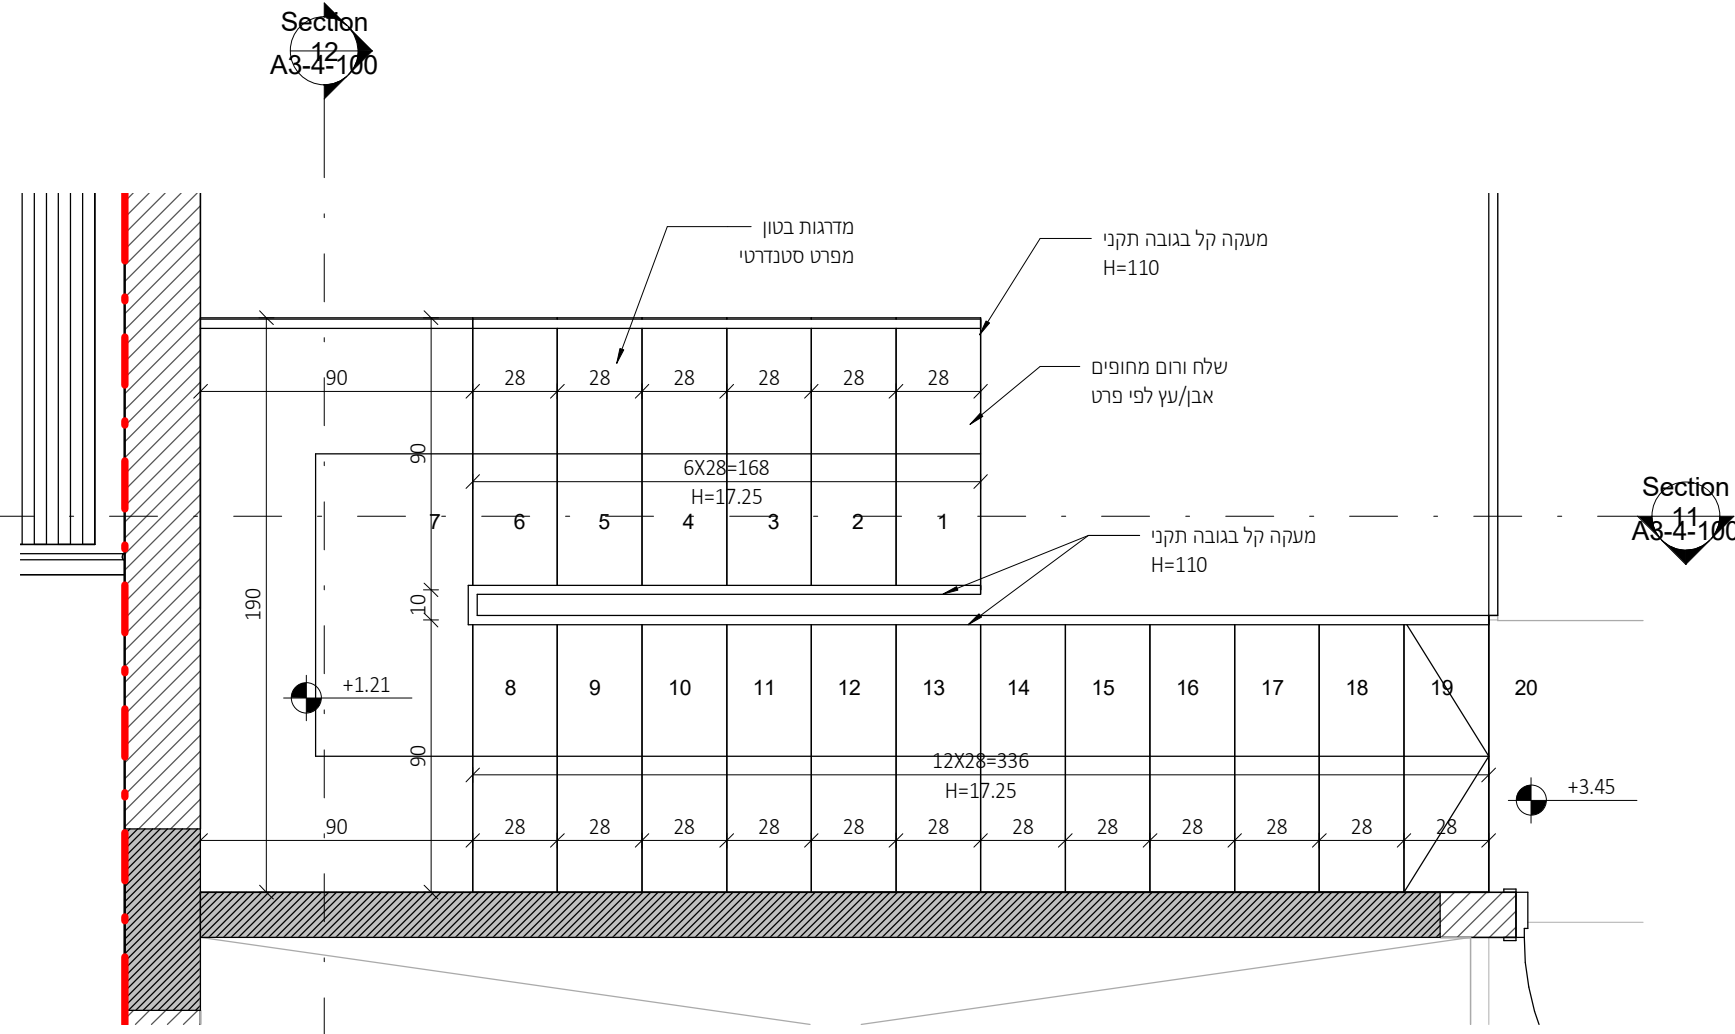


תכנית מדרגות קומה א

1 : 25

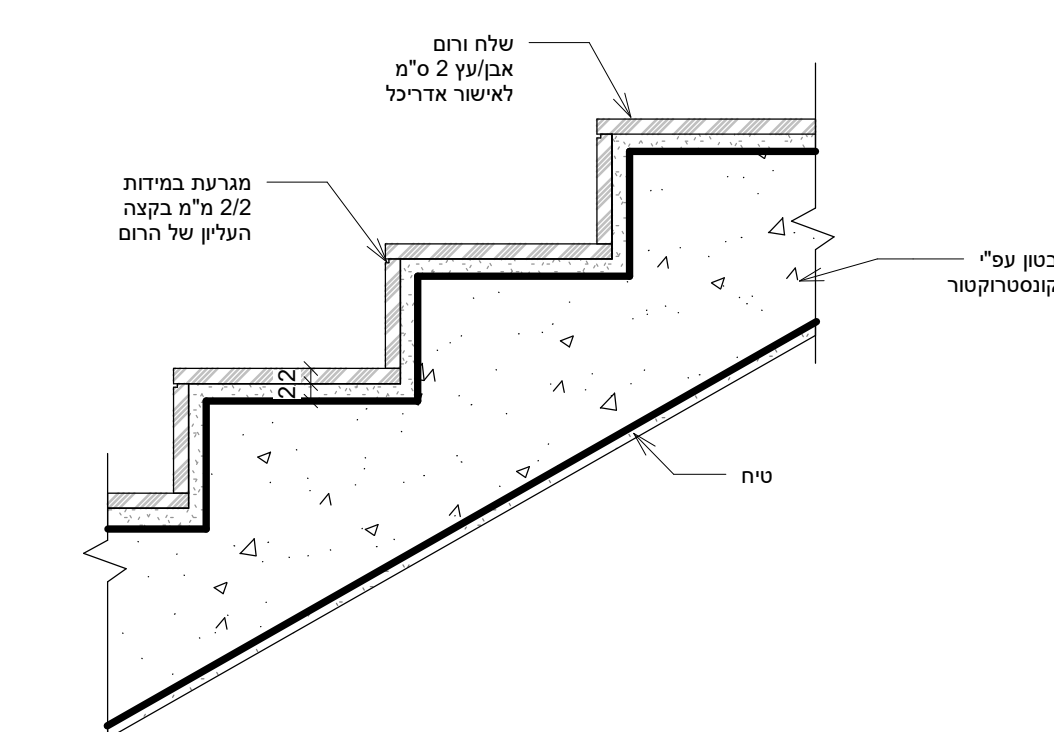


פרט מדרגות פנים - עץ/אבן

1 : 10

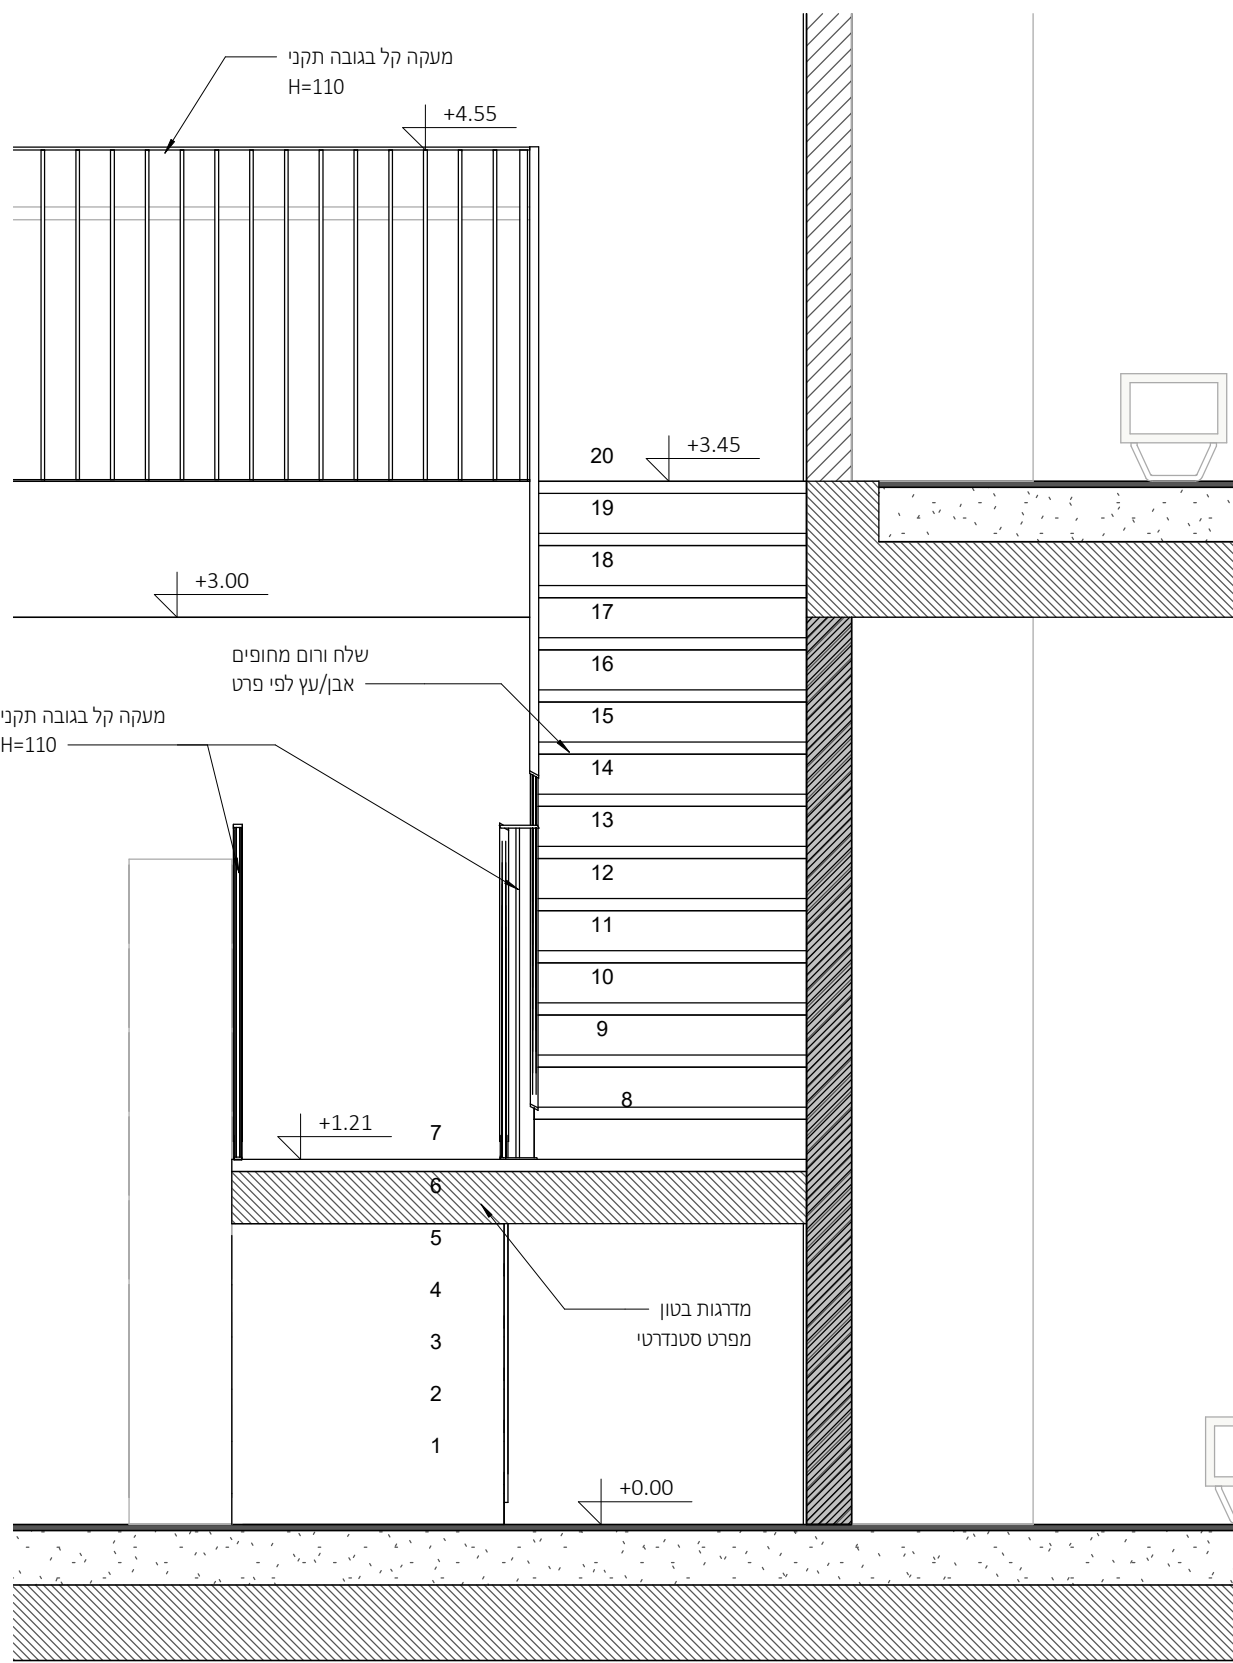


Section 12

1 : 25

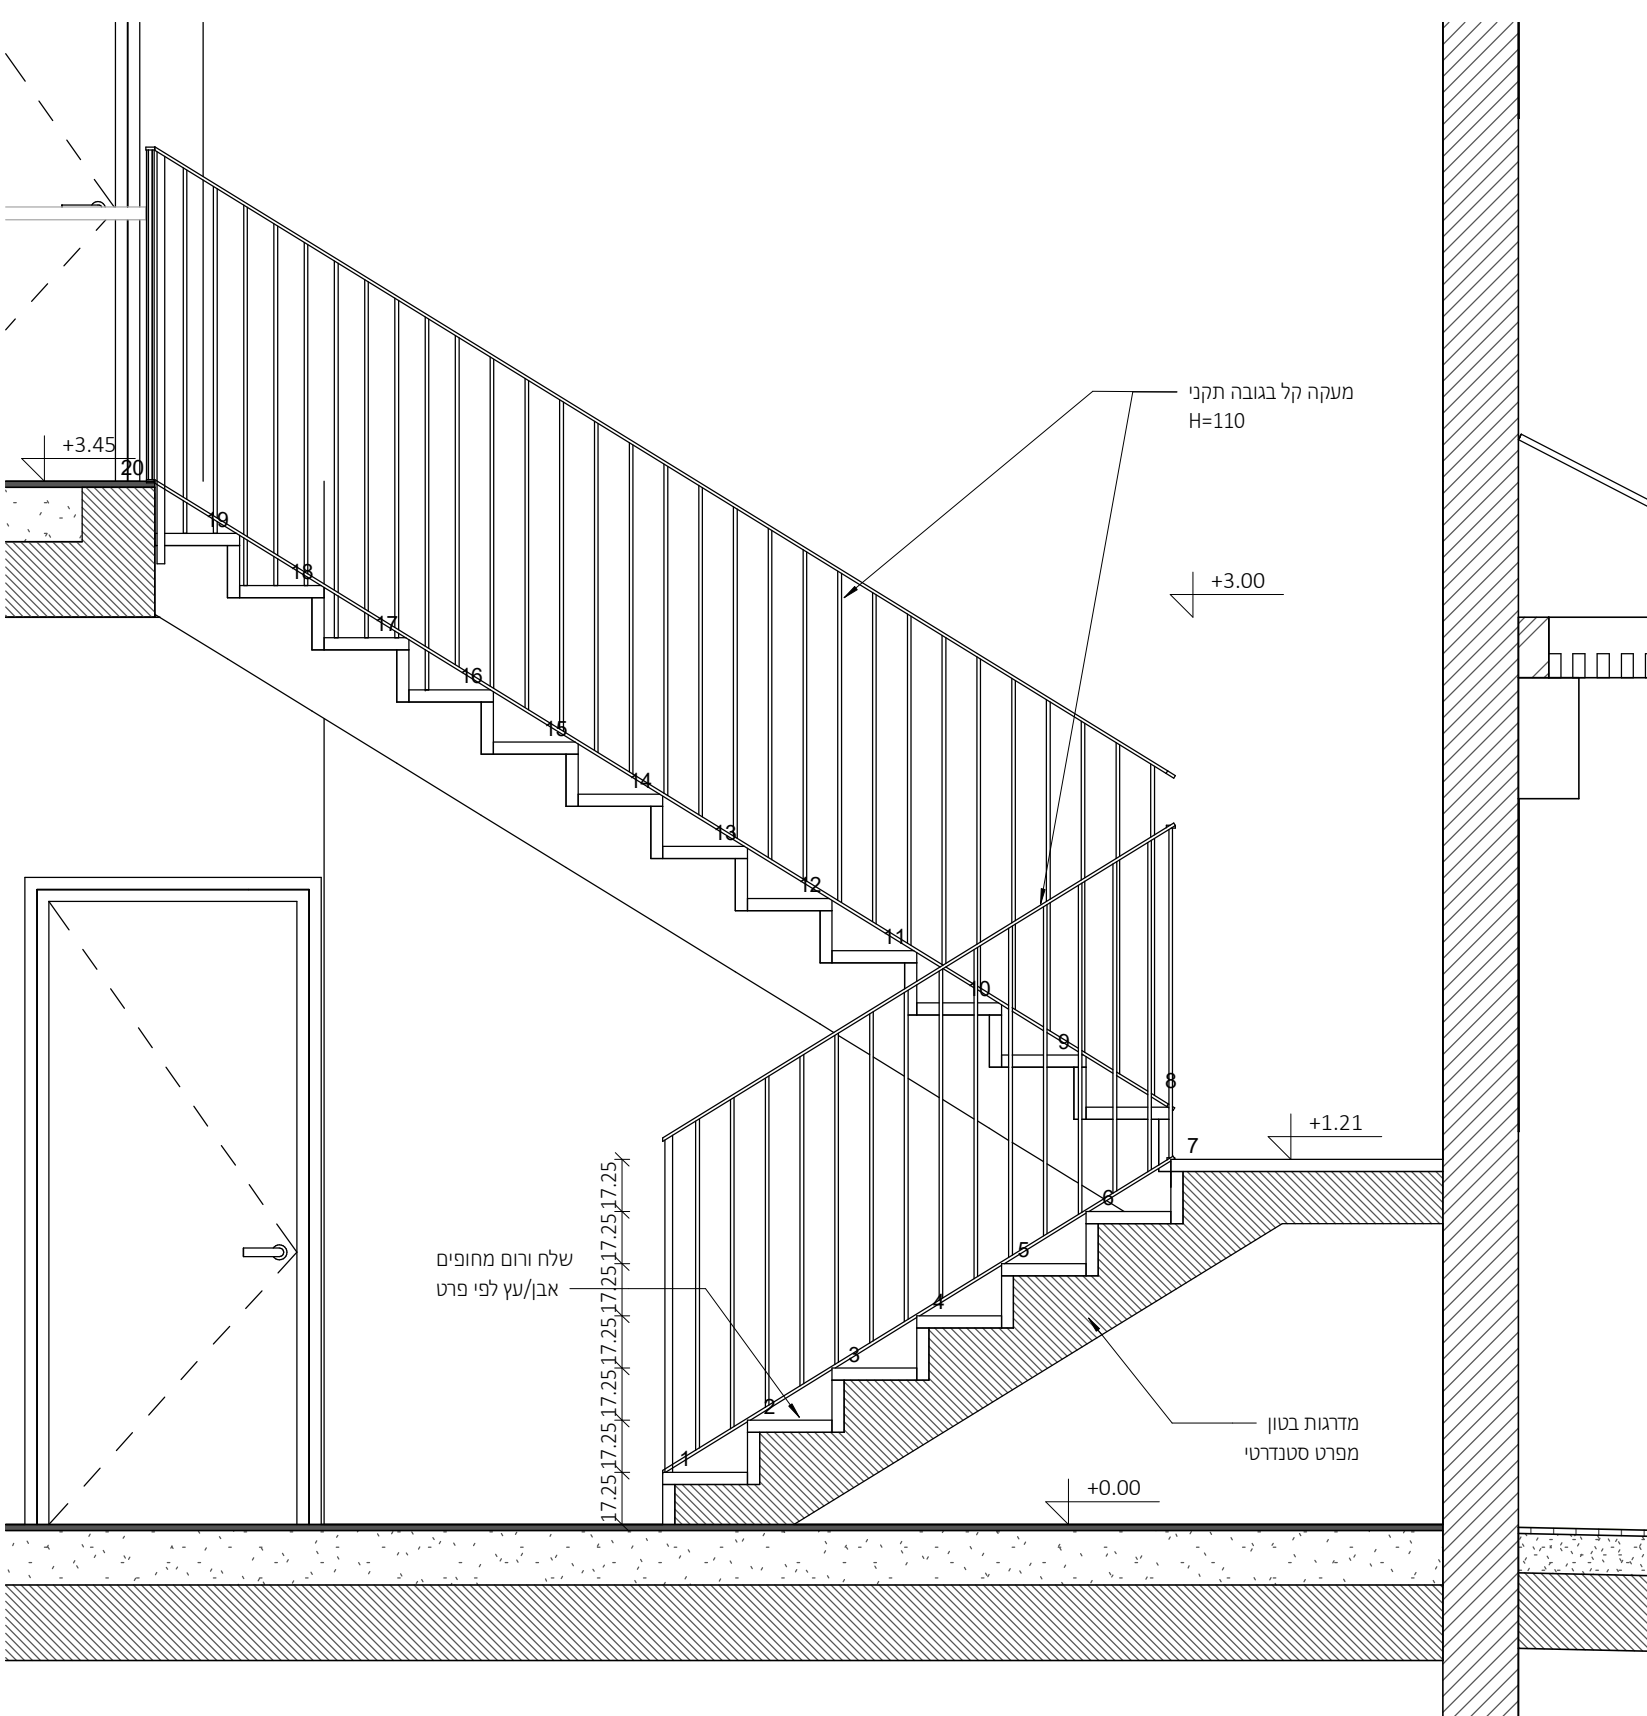

Section 11

1 : 25

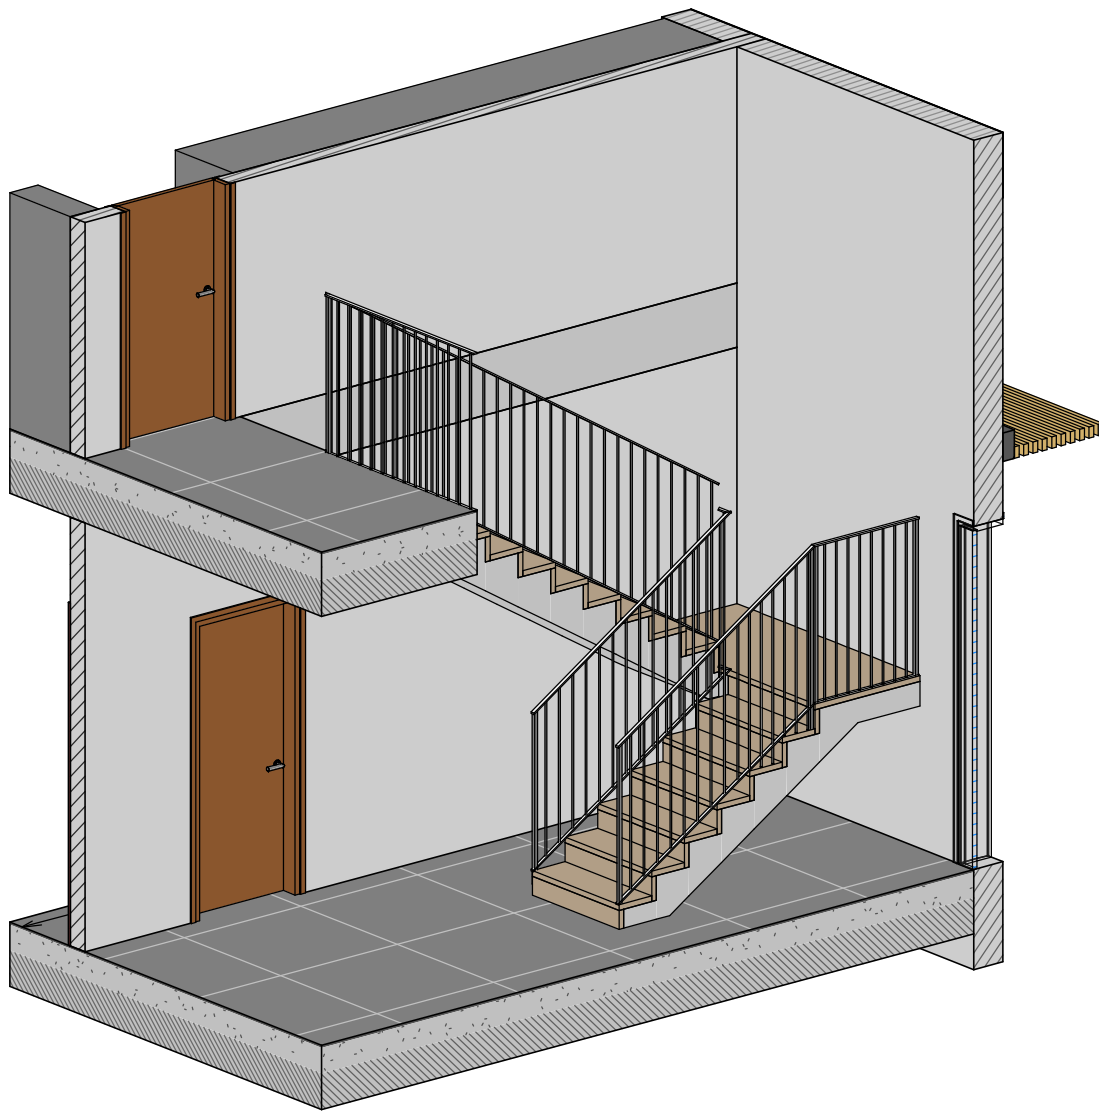

דגם נבחר

מדרגות סטנדרטיות - מפרט סטנדרטי

על הקבלן לשלוח S.D לאישור אדריכל

יש לבצע התאמה לפרט לאחר בחירת חיפוי המדרגות*

להמשך תיאום

ניהל פרויקט
מהיסוד - בו סולומן
פיקוח
מהיסוד - בו סולומן
קונסטרוקציה
ערן שילר
מיזוג אוויר
אייל ארז מהנדסים ויועצים בע"מ
אינסטלציה
איתן אלמסי
חשמל
איתן בסיס
אלומיניום
נוף
נתי בלוקא
חשמל חכם
חימום תת רצפתי
איטום
צבי טל
אקוסטיקה
מעליות
קרקע וביסוס
דיה הנדסת קרקע וביסוס
רישוי

[illegible][illegible]


CLIENT NAME:	קבוצת רכישה נופיה		
PROJECT NAME:	נופיה - מגרש 17		
DRAWING NAME:	פרטים		
SHEET NUMBER:	A3-4-103		
SCALE:	קנה מידה:	EDITION:	דפוס:
As indicated	סמסוס		
STATUS:	למכר		דפוס ע"י:
	נכדע ע"י:		
DATE:	29.12.25		חיר:




NeumanHaynerArchitects

יומן חיינר אדריכלים
חורר ההדרים 2, בית חירות
09-9545842 זל

office@nh-arch.com
www.nh-arch.com

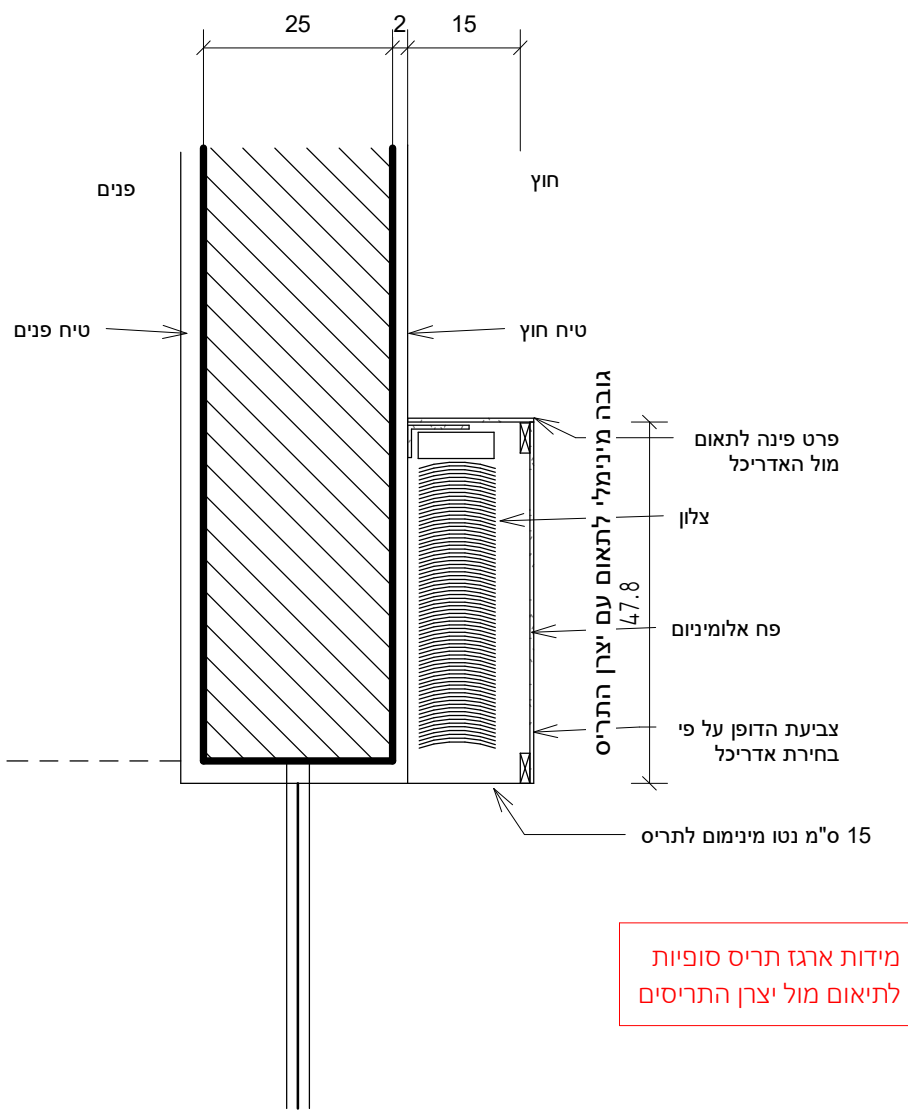


פרט 1 - כיס צלון חיצוני

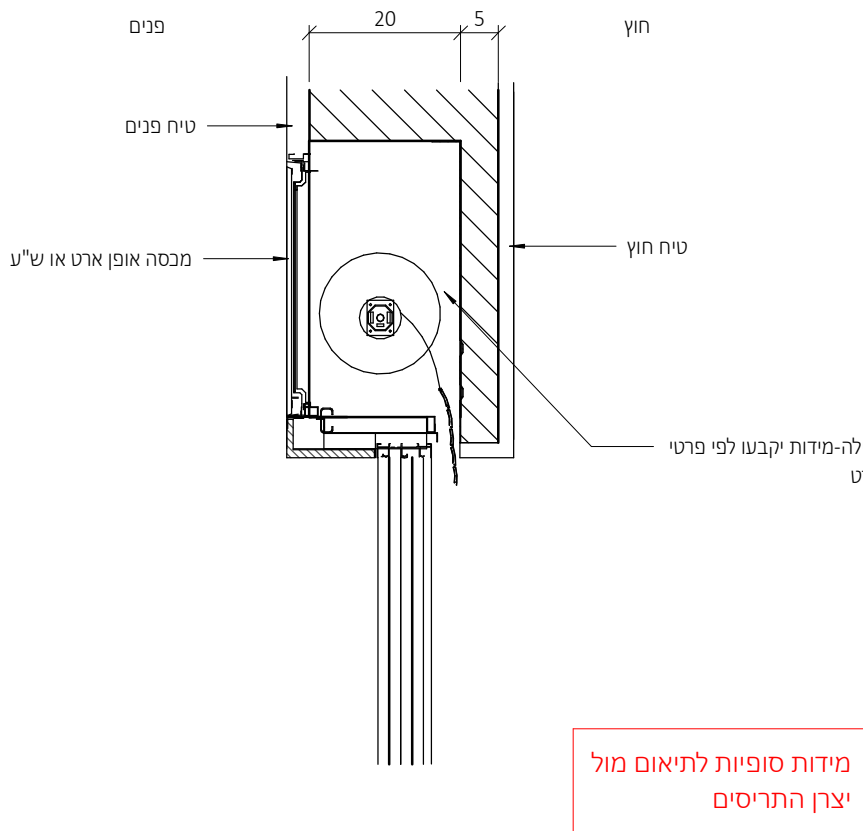


פרט 2 - תריס גלילה

1 : 10


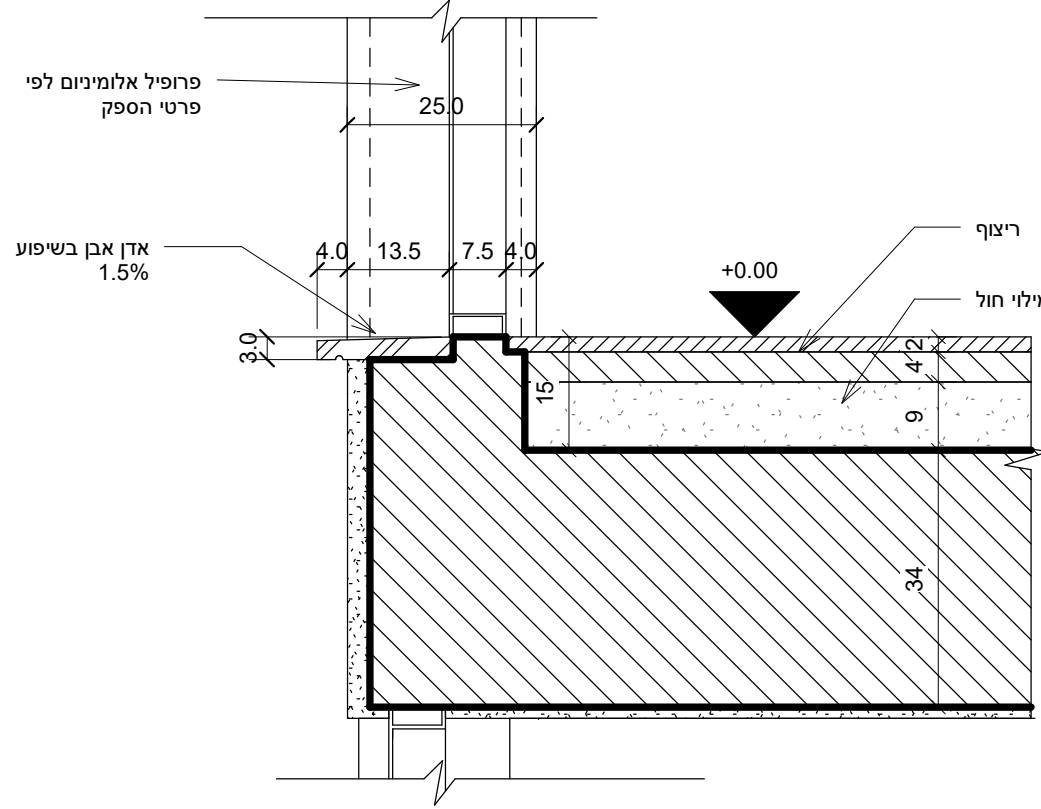


הערה: פרטי האיטום הם עקרוניים בלבד.
כל האחריות על האיטום מוטלת על יועץ
האיטום החברה המבצעת
יש לעבוד לפי פרטי האיטום של יועץ הפרויקט.
גובה החלון המופיע בתכניות מצוין את פני סף
האבן, יש להנמיך את הבטון בהתאם

פרט עקרוני בלבד - פרט סופי מספק החלונות

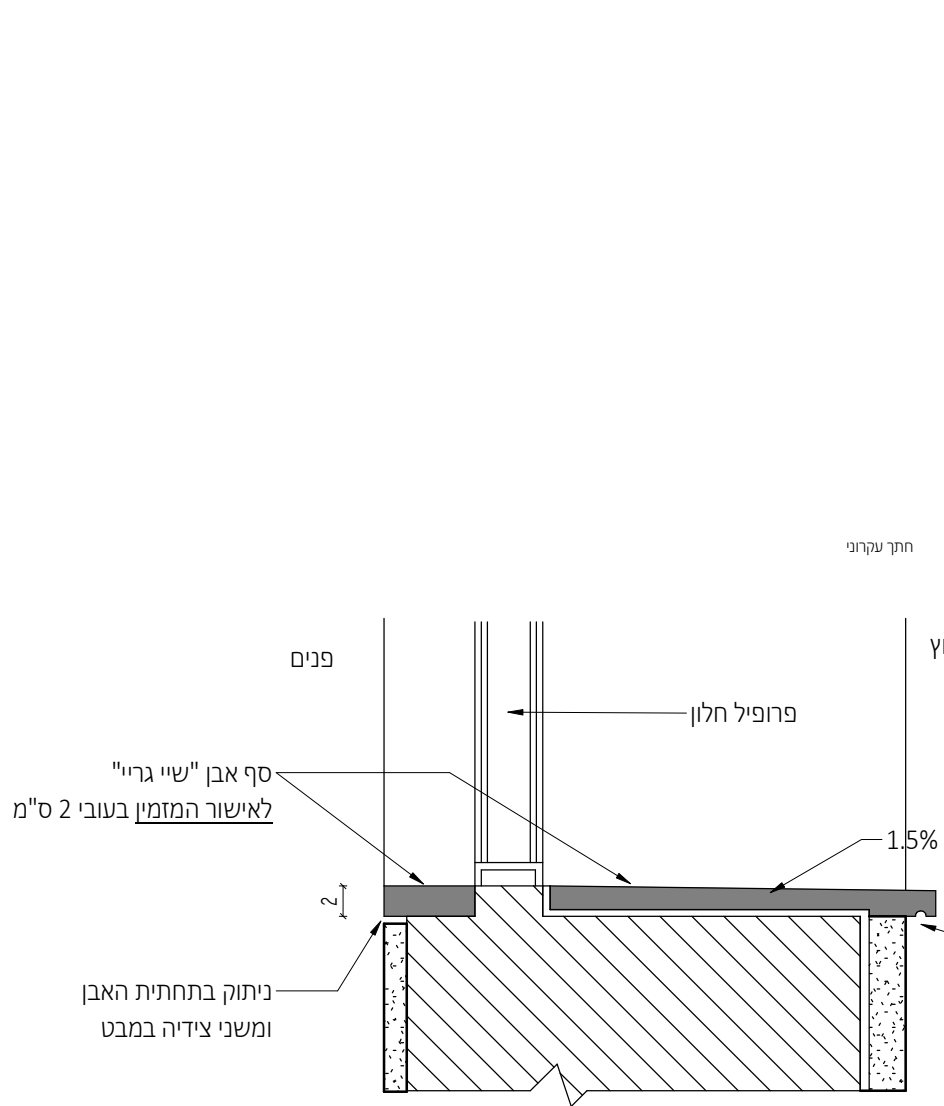פרט 3 - מפגש חלון ורצפה
1 : 10

פרט 4 - חלון - פרט טיפוס י - סף חלון

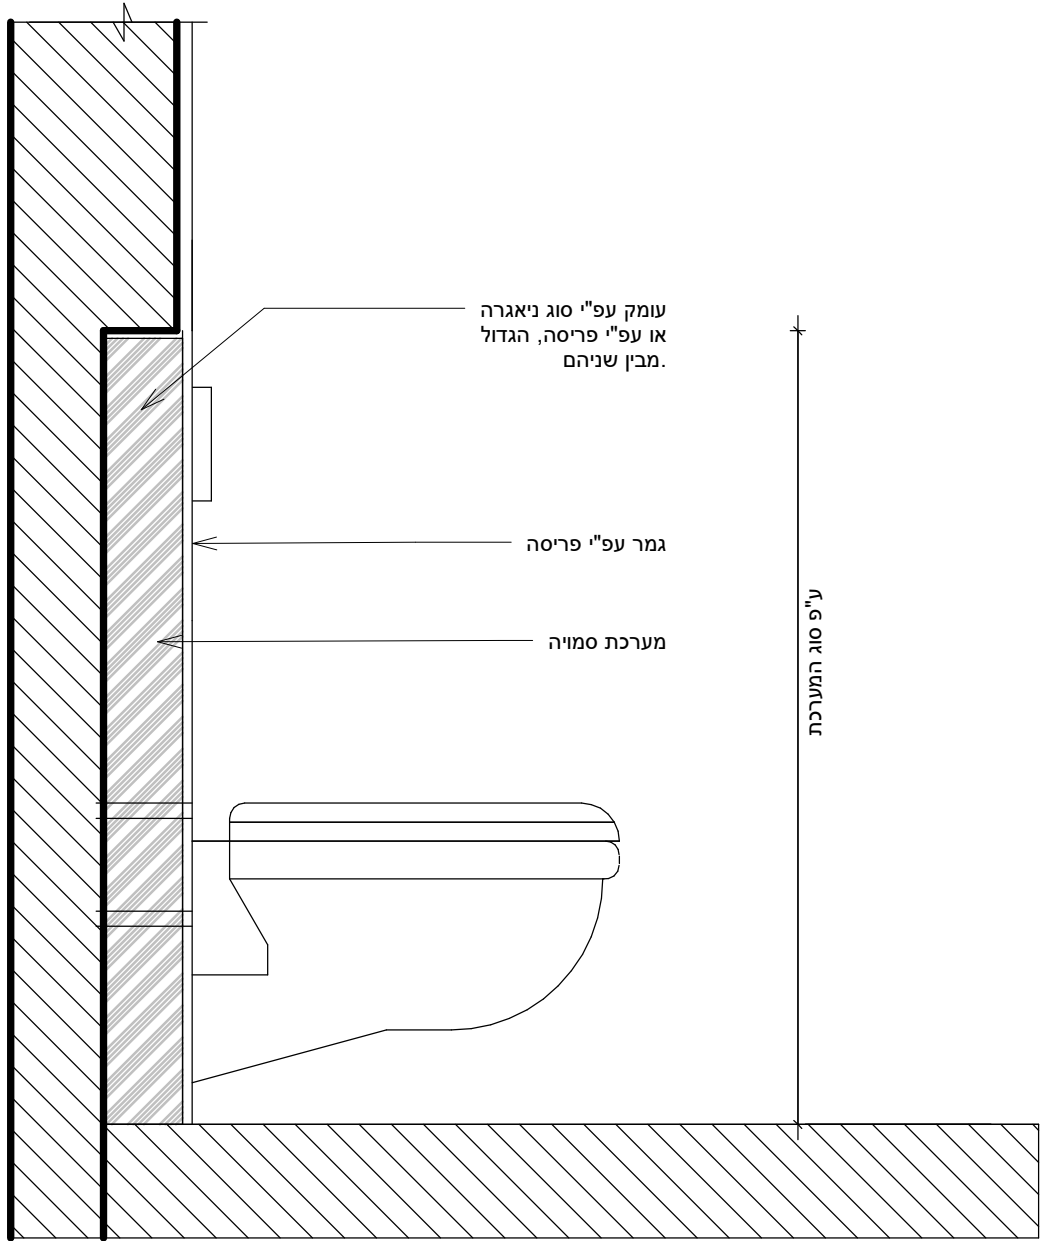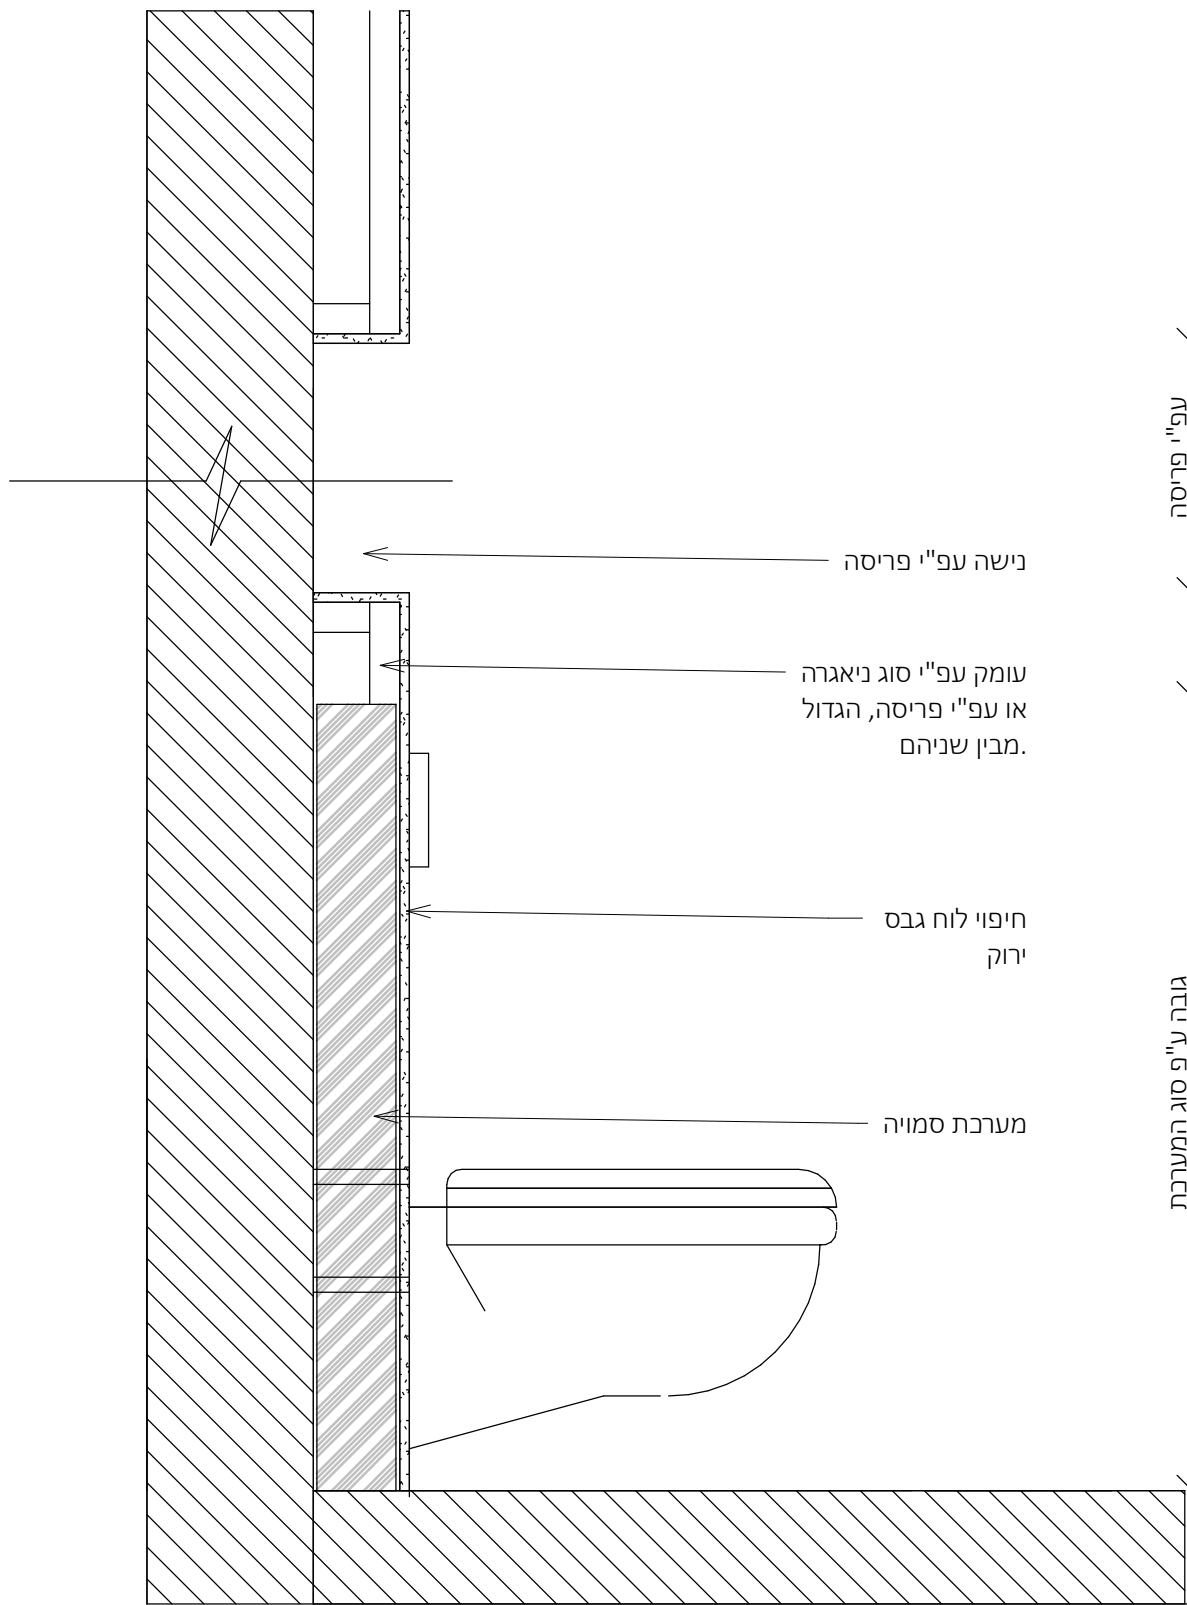פרט 5 - אסלה תלויה בקיר 20
1 : 10

פרט 6 -אסלה תלויה מנגנון סמוי בעיבוי גבס

יש לעבוד במקביל לפרטים שייספק
מעצב הפנים (במידה וקיים במגרש זה)
המאושרות על ידי האדריכל.

פרטי האיטום באחריות יועץ האיטום
ראה חוברת פרטי איטום מצורפת


להמשך תיאום

פרגולת אלומיניום




תמונה להמחשה בלבד

להמשך תיאום

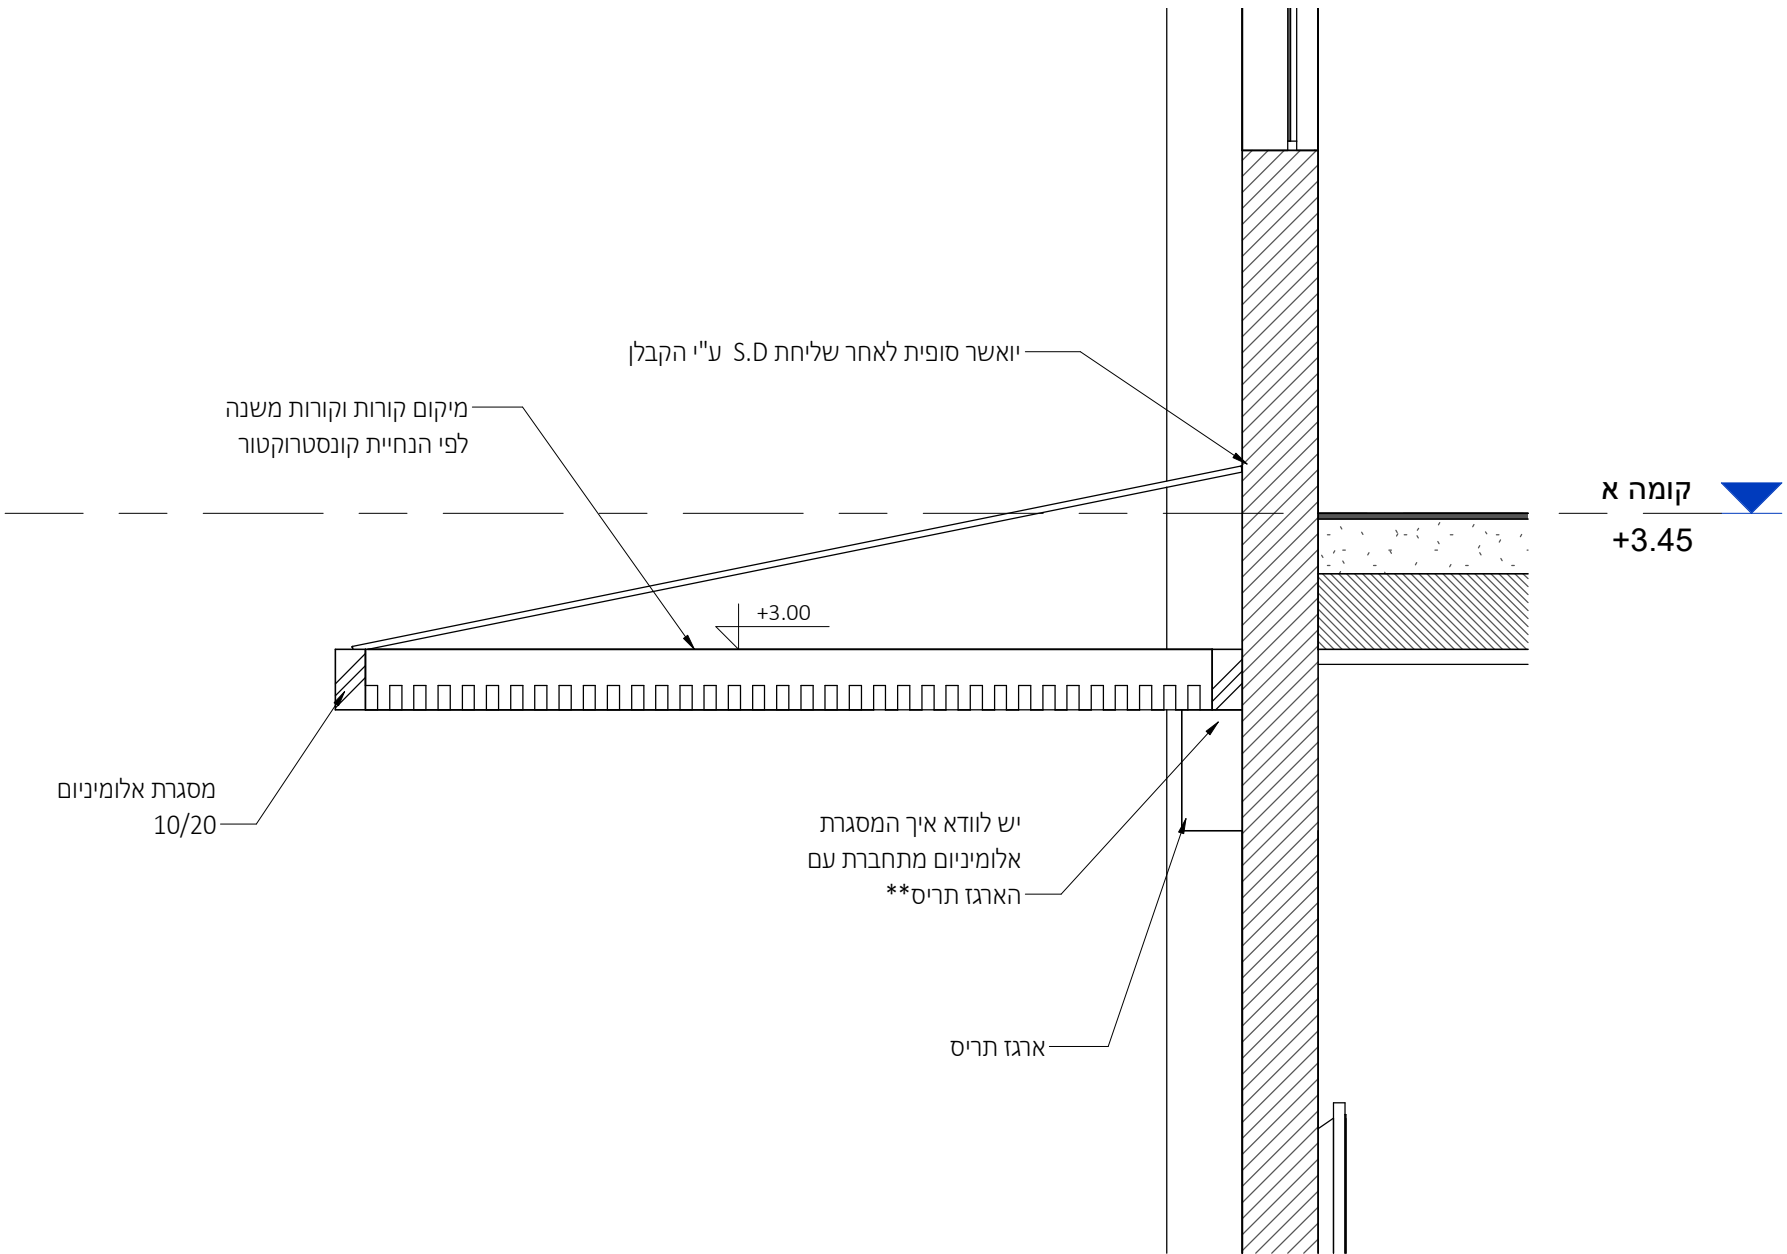


Section 13

1 : 25

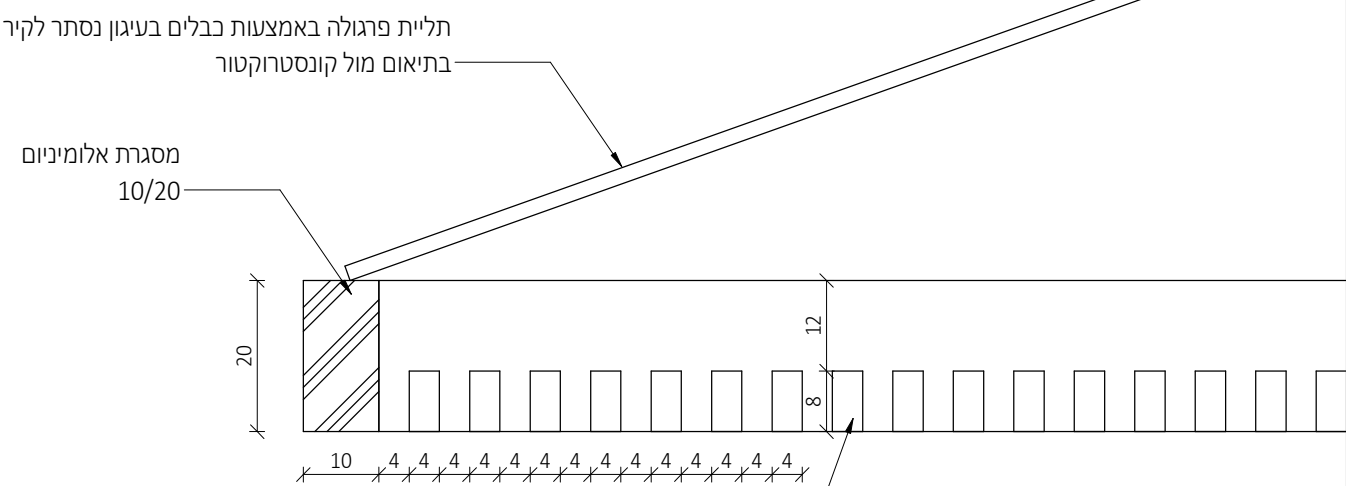



פרגולה - חתך רוחב

1 : 10

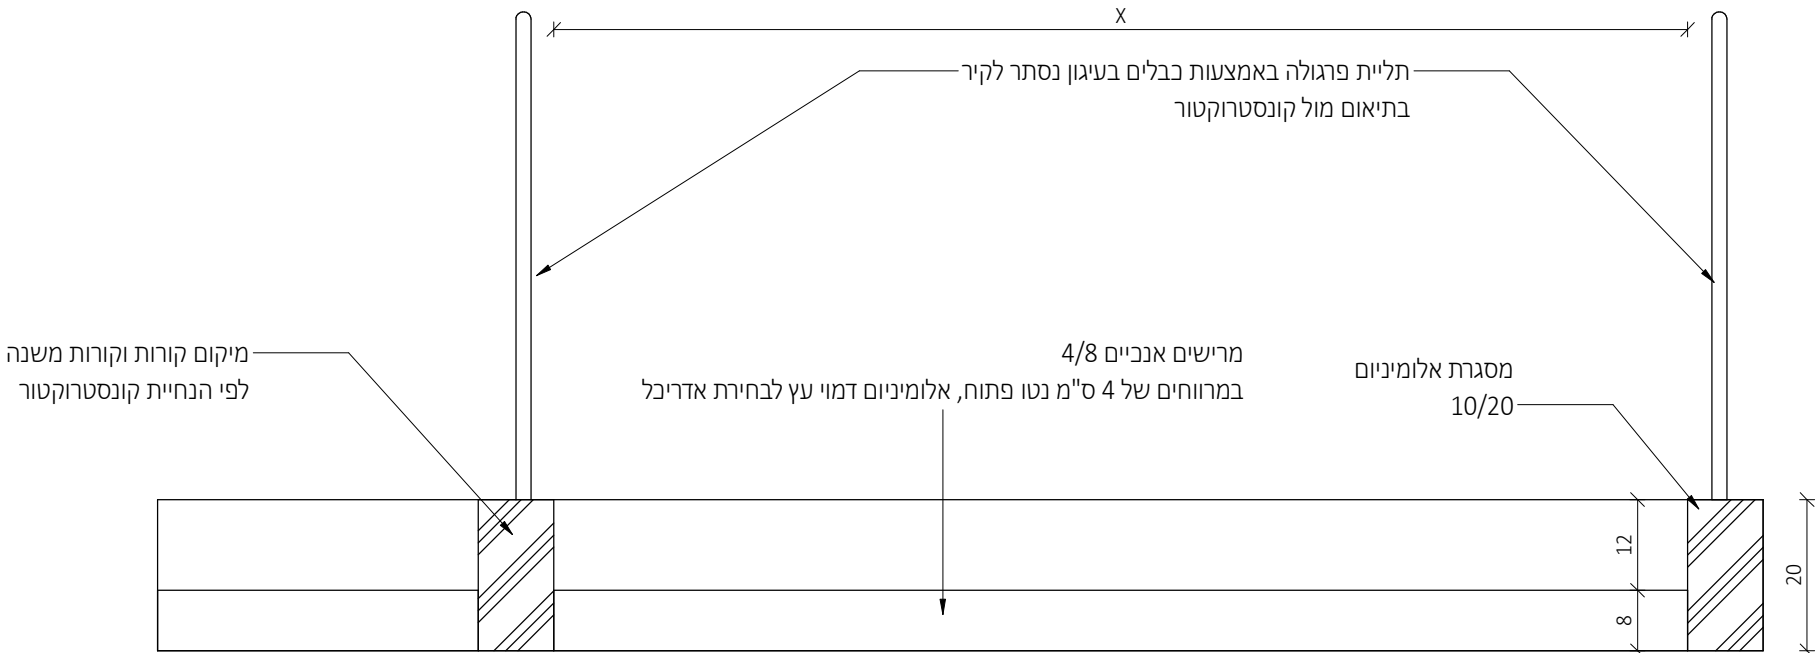

פרגולה - חתך אורך

1 : 10

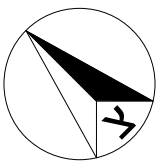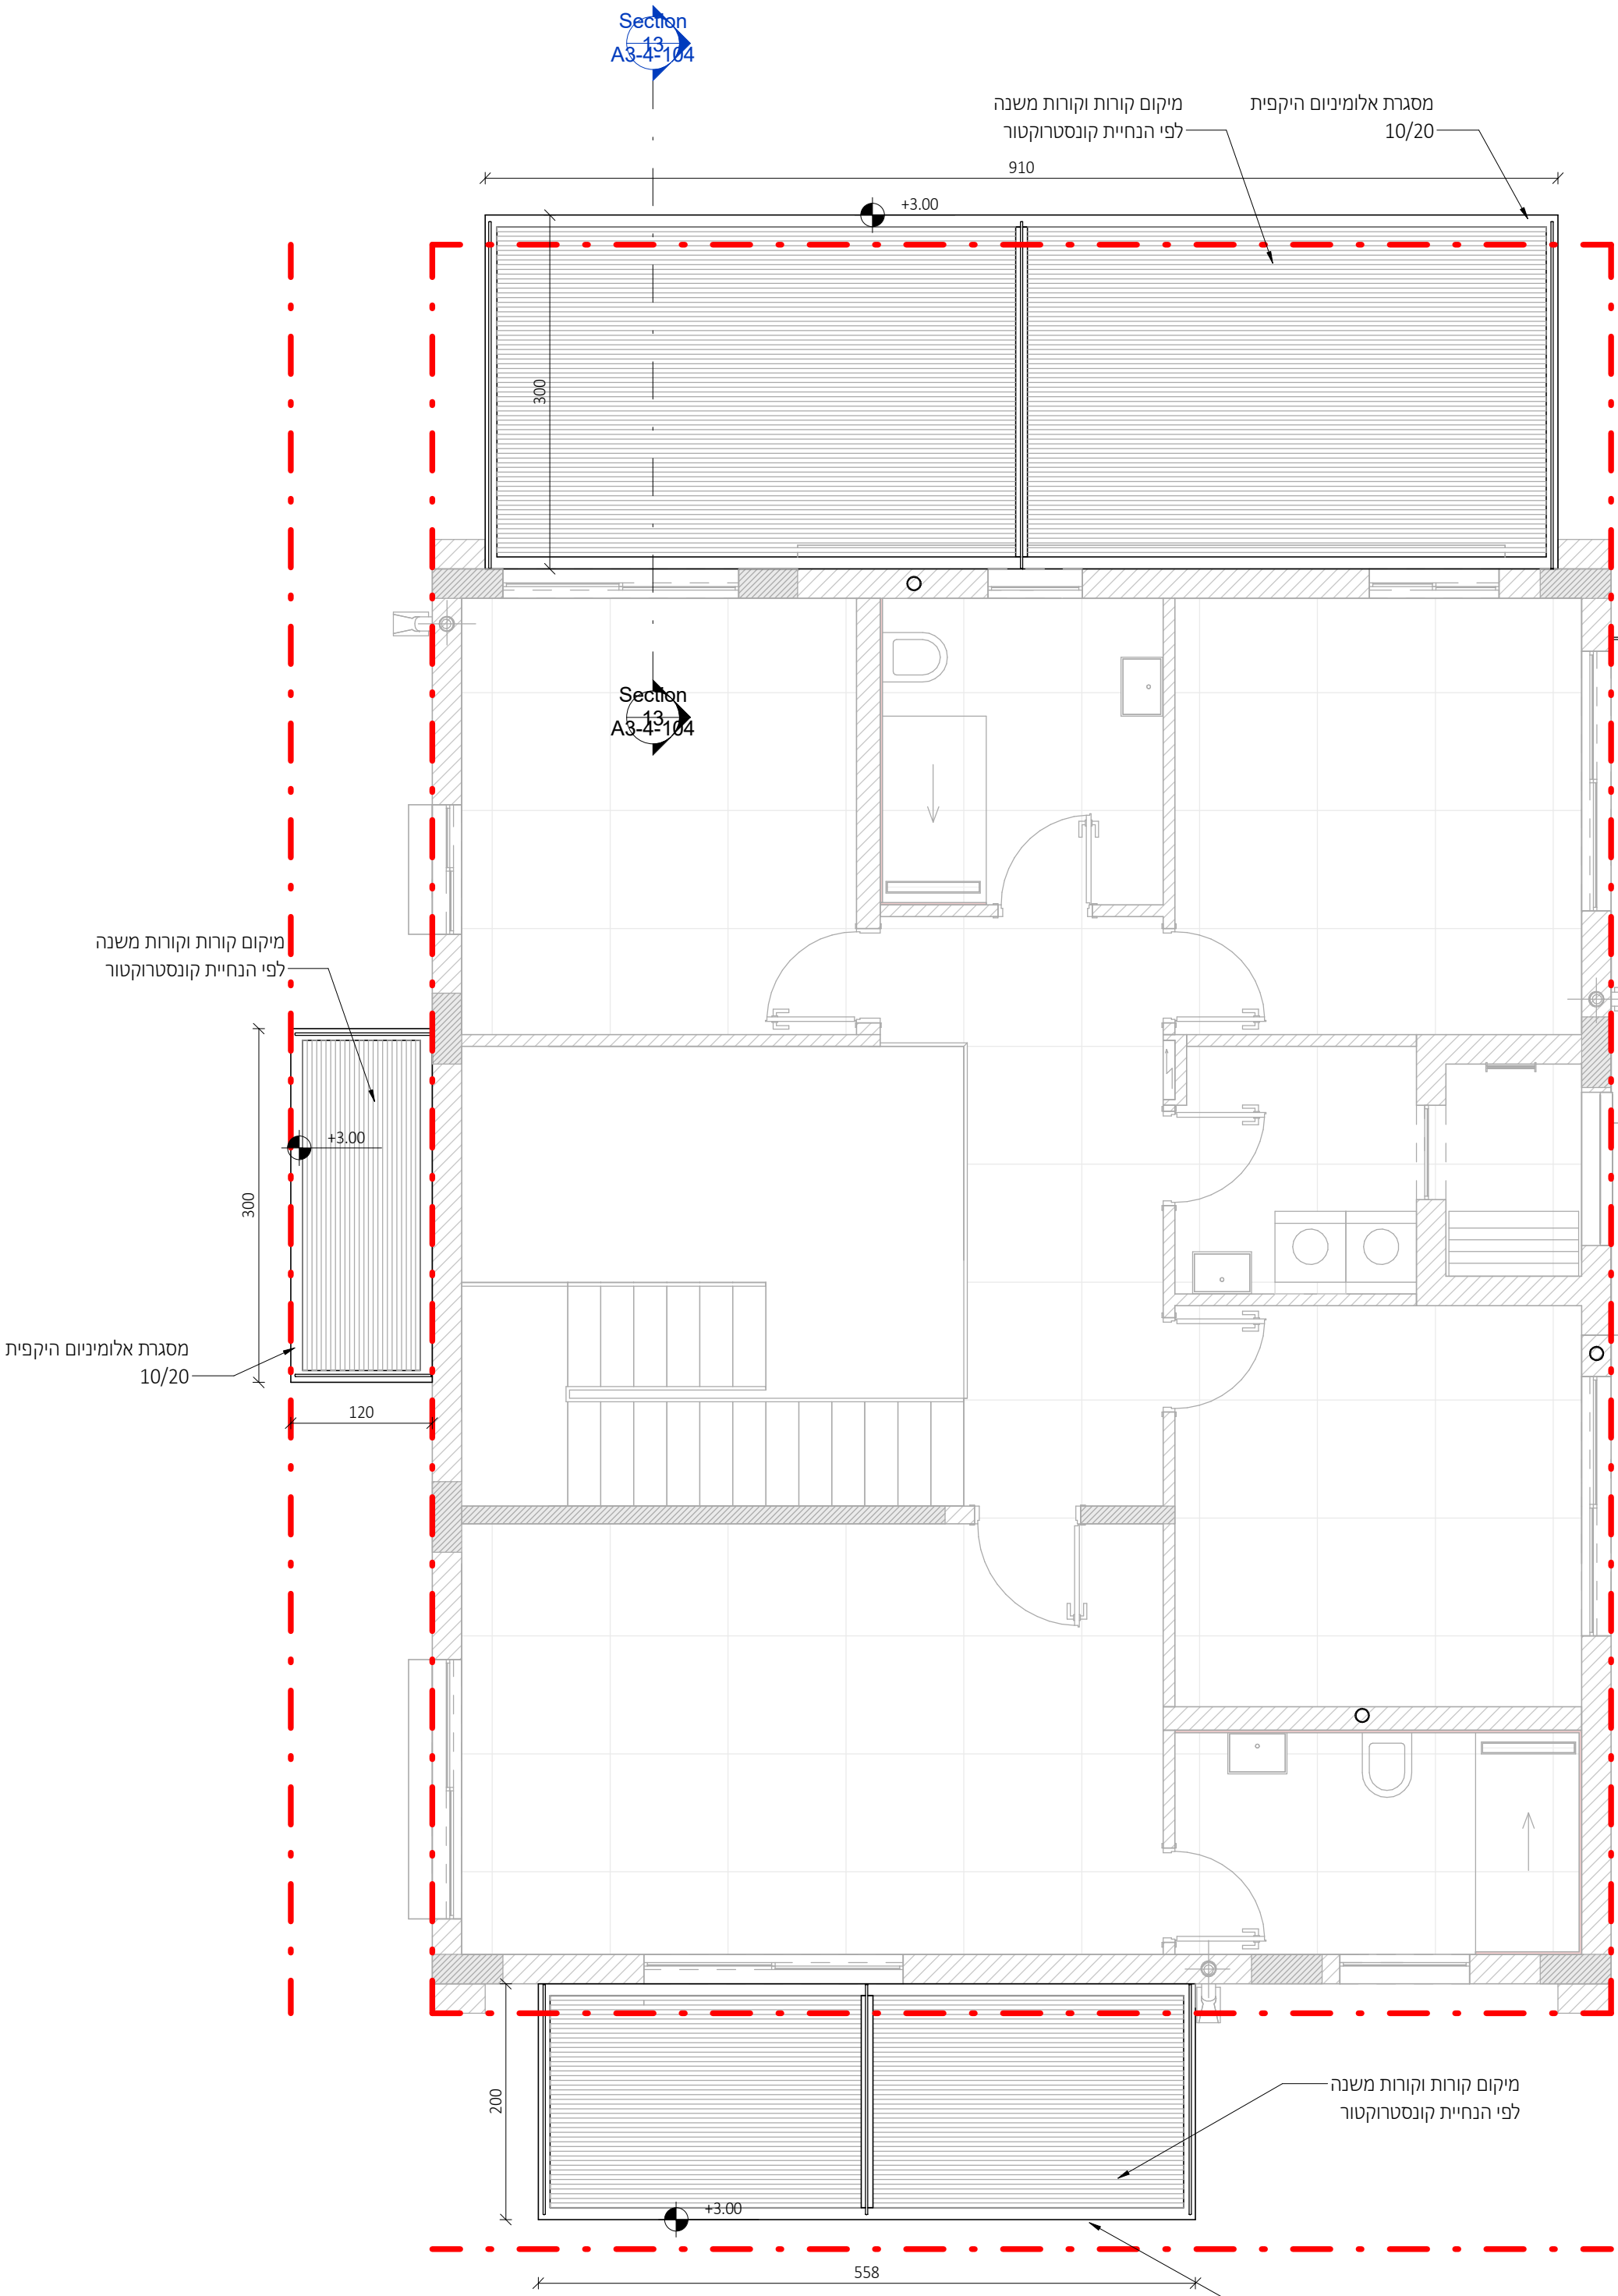

מתכננים:


ניהול פרויקט
מהיסוד - בו סולומון
פיקוח
מהיסוד - בו סולומון
קונסטרוקציה
ערן שילר
מיזוג אוויר
אייל ארז מהנדסים ויועצים בע"מ
אינסטלציה
איתן אלמסי
חשמל
איתן בסיס
אלומיניום
בנף
נתי בלוקא
חשמל חכם
חימום תת רצפתי
איטום
צבי טל
אקוסטיקה
מעליות
קרקע וביסוס
דיה הנדסת קרקע וביסוס
רישוי

± 0.00 = +245.60

הערות:
1. תכנית זו יש לקרוא יחד עם תכנית הרישום.
2. גובה אבטומיסי: ראו תכנית פיתוח.
3. הפירות הן בין קירות הבניה ולא כולל פיתוח.
4. פיתוח השטח סביב הבניה, כולל, מדרגות, גדרות, שבילים, ריצופים, שטחים בגנים, חניה וגן וראו תכנית פיתוח.
5. איסוס קירות ורצפות הבניה כמעט עם הקרקע ובנידוד תרמי לאורך העמודים והקורות של החתך. כלירות או עם סימני גיבוי. ראו תכנית קונסטרוקציה.
6. אף דים יבוצע בכל מישור אופקי הבולם חתך.
7. פיתוח תרמי במסגרת ע"פ מפרט חומרים, מאושר ע"י פיקוח העיר.

המבצע אחראי לסידור: עליו לבקר ולבדוק את כל המידות בתכנית ובמקום המבנה.
במסגרת של שטח או אי התאמה בתכנית /או בבנין, עליו להודיע על כך מיד לאדריכל בסופו המשיך בעבודתו.
המבצע יחזיק את רוב תכניתו שאושר לכניסה.
המבצע יחזיק את כל שטח, של שטחיו של תכנית.
אין לקבוע מידות על ידי חדייה בשר שטח.
התכנית תהיה תכנית האדריכל ואין לשנות כל שימוש בה או ברעיונות הגלומים בה, אלא באישור בכתב מהאדריכל.
המבצע יחזיק את כל תכניתו בתכנית זו, ויש לוודא באחריות על התפקוד והשכלול ליוזא התאמת התכנית האדריכלית "לכניסה" לתכנית זו. המבצע והתכנית האדריכלית של כל העבודות והשימושים.
התכנית כוללת את כל האמצעים והידוע על ליום תחלפת.

משרד קירות:

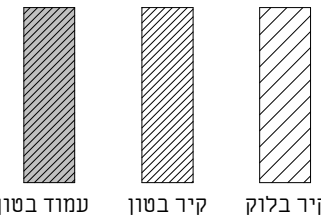

תאריך	תיאור	מהדורה
22.09.2025	מכרז	1

אדריכלות

שם המסמך:	CLIENT NAME:
קבוצת רכישה נופיה	
שם הפרויקט:	PROJECT NAME:
נופיה - מגרש 17	
שם הגיליון:	DRAWING NAME:
פרטי פרגולה	
מספר גיליון:	SHEET NUMBER:
A3-4-104	
תאריך:	SCALE:
29.12.25	קנה מידה: As indicated
תאריך:	EDITION:
29.12.25	1
תאריך:	STATUS:
29.12.25	למכרז
תאריך:	שורש ע"י:
29.12.25	נבדק ע"י:
תאריך:	DATE:
29.12.25	



נוימן חיינר אדריכלים
מנכ"ל: 09-5545642
www.nh-arch.com

זכיתו ייצור / ע"פ הנחיות ע"ד

12/29/2025 3:25:09 PM

רשימת חלונות					
סוג	תיאור	כמות	גובה	רוחב	מס פריט

ק.קרקע

1	450	240	1	צלון רפפה חיצוני חשמלי + ארגז חיצוני	ויטרינה פרופיל 7500 קליל
2	110	240	1	צלון רפפה חיצוני חשמלי + ארגז חיצוני	דלת כנף פרופיל 4350 קליל
2.1	110	240	1	צלון רפפה חיצוני חשמלי + ארגז חיצוני	חלון קבוע פרופיל 7000 קליל
3	180	240	1	צלון רפפה חיצוני חשמלי + ארגז חיצוני	ויטרינה פרופיל 7500 קליל
4	60	110	1	ללא רפפה	חלון קיפ פרופיל 4500 קליל
5	90	110	1	צלון רפפה חיצוני חשמלי + ארגז חיצוני	חלון קיפ פרופיל 4500 קליל
6	220	240	1	צלון רפפה חיצוני חשמלי + ארגז חיצוני	ויטרינה פרופיל 7500 קליל
7	220	110	1	צלון רפפה חיצוני חשמלי + ארגז חיצוני	חלון הזזה פרופיל 7000 קליל

קומה א

8	220	110	4	תריס גלילה חשמלי	חלון הזזה פרופיל 7000 קליל
9	200	110	1	תריס גלילה חשמלי	חלון הזזה פרופיל 7000 קליל
10	80	110	1	תריס גלילה חשמלי	חלון קיפ פרופיל 4500 קליל
11	110	110	2	תריס גלילה חשמלי	חלון הזזה פרופיל 7000 קליל
12	80	210	1	תריס גלילה חשמלי	דלת כנף פרופיל 4350 קליל
13	110	110	1	תריס גלילה חשמלי	חלון קיפ פרופיל 4500 קליל

סוג זכוכית – בהתאם למפורט בדו"ח התרמי (תנאי המינימום בעמוד 9 מתוך המפרט התרמי). כמו כן, הזכוכית תקבע בתיאום עם הקבלן לאחר אישור יועץ התרמי וחברת הניהול

כל פריט יחולק למינימום הכנפיים האפשרי (לתיאום מול ספק האלומיניום ובמסגרת שרטוטי ה shop drawing)

רשימת דלתות					
סוג	הערות	כמות	גובה	רוחב	מספר פריט

דלת חוץ דגם גארה	דלת כניסה	1	240	135	0
דלת פנים "אקוודור" תוצרת חמדיה	דלת פנים	3	210	90	1
דלת פנים "אקוודור" תוצרת חמדיה	דלת פנים	7	210	80	2
דלת פנים "אקוודור" תוצרת חמדיה	דלת נגרות ממ"ד	1	200	80	3

נוימן חיינר אדריכלים בע"מ

כל הזכויות שמורות
ט.ל.ח

NeumanHaynerArchitects



רשימת פתחים		שם התכנית:
גליון מספר: A3-6-1000	מהדורה: 22.09.2025	01
שם הפרויקט: נופיה - מגרש 17	למכרז	
שם המממן: קבוצת רכישה נופיה	קנה מידה:	12/29/2025 3:25:11 PM