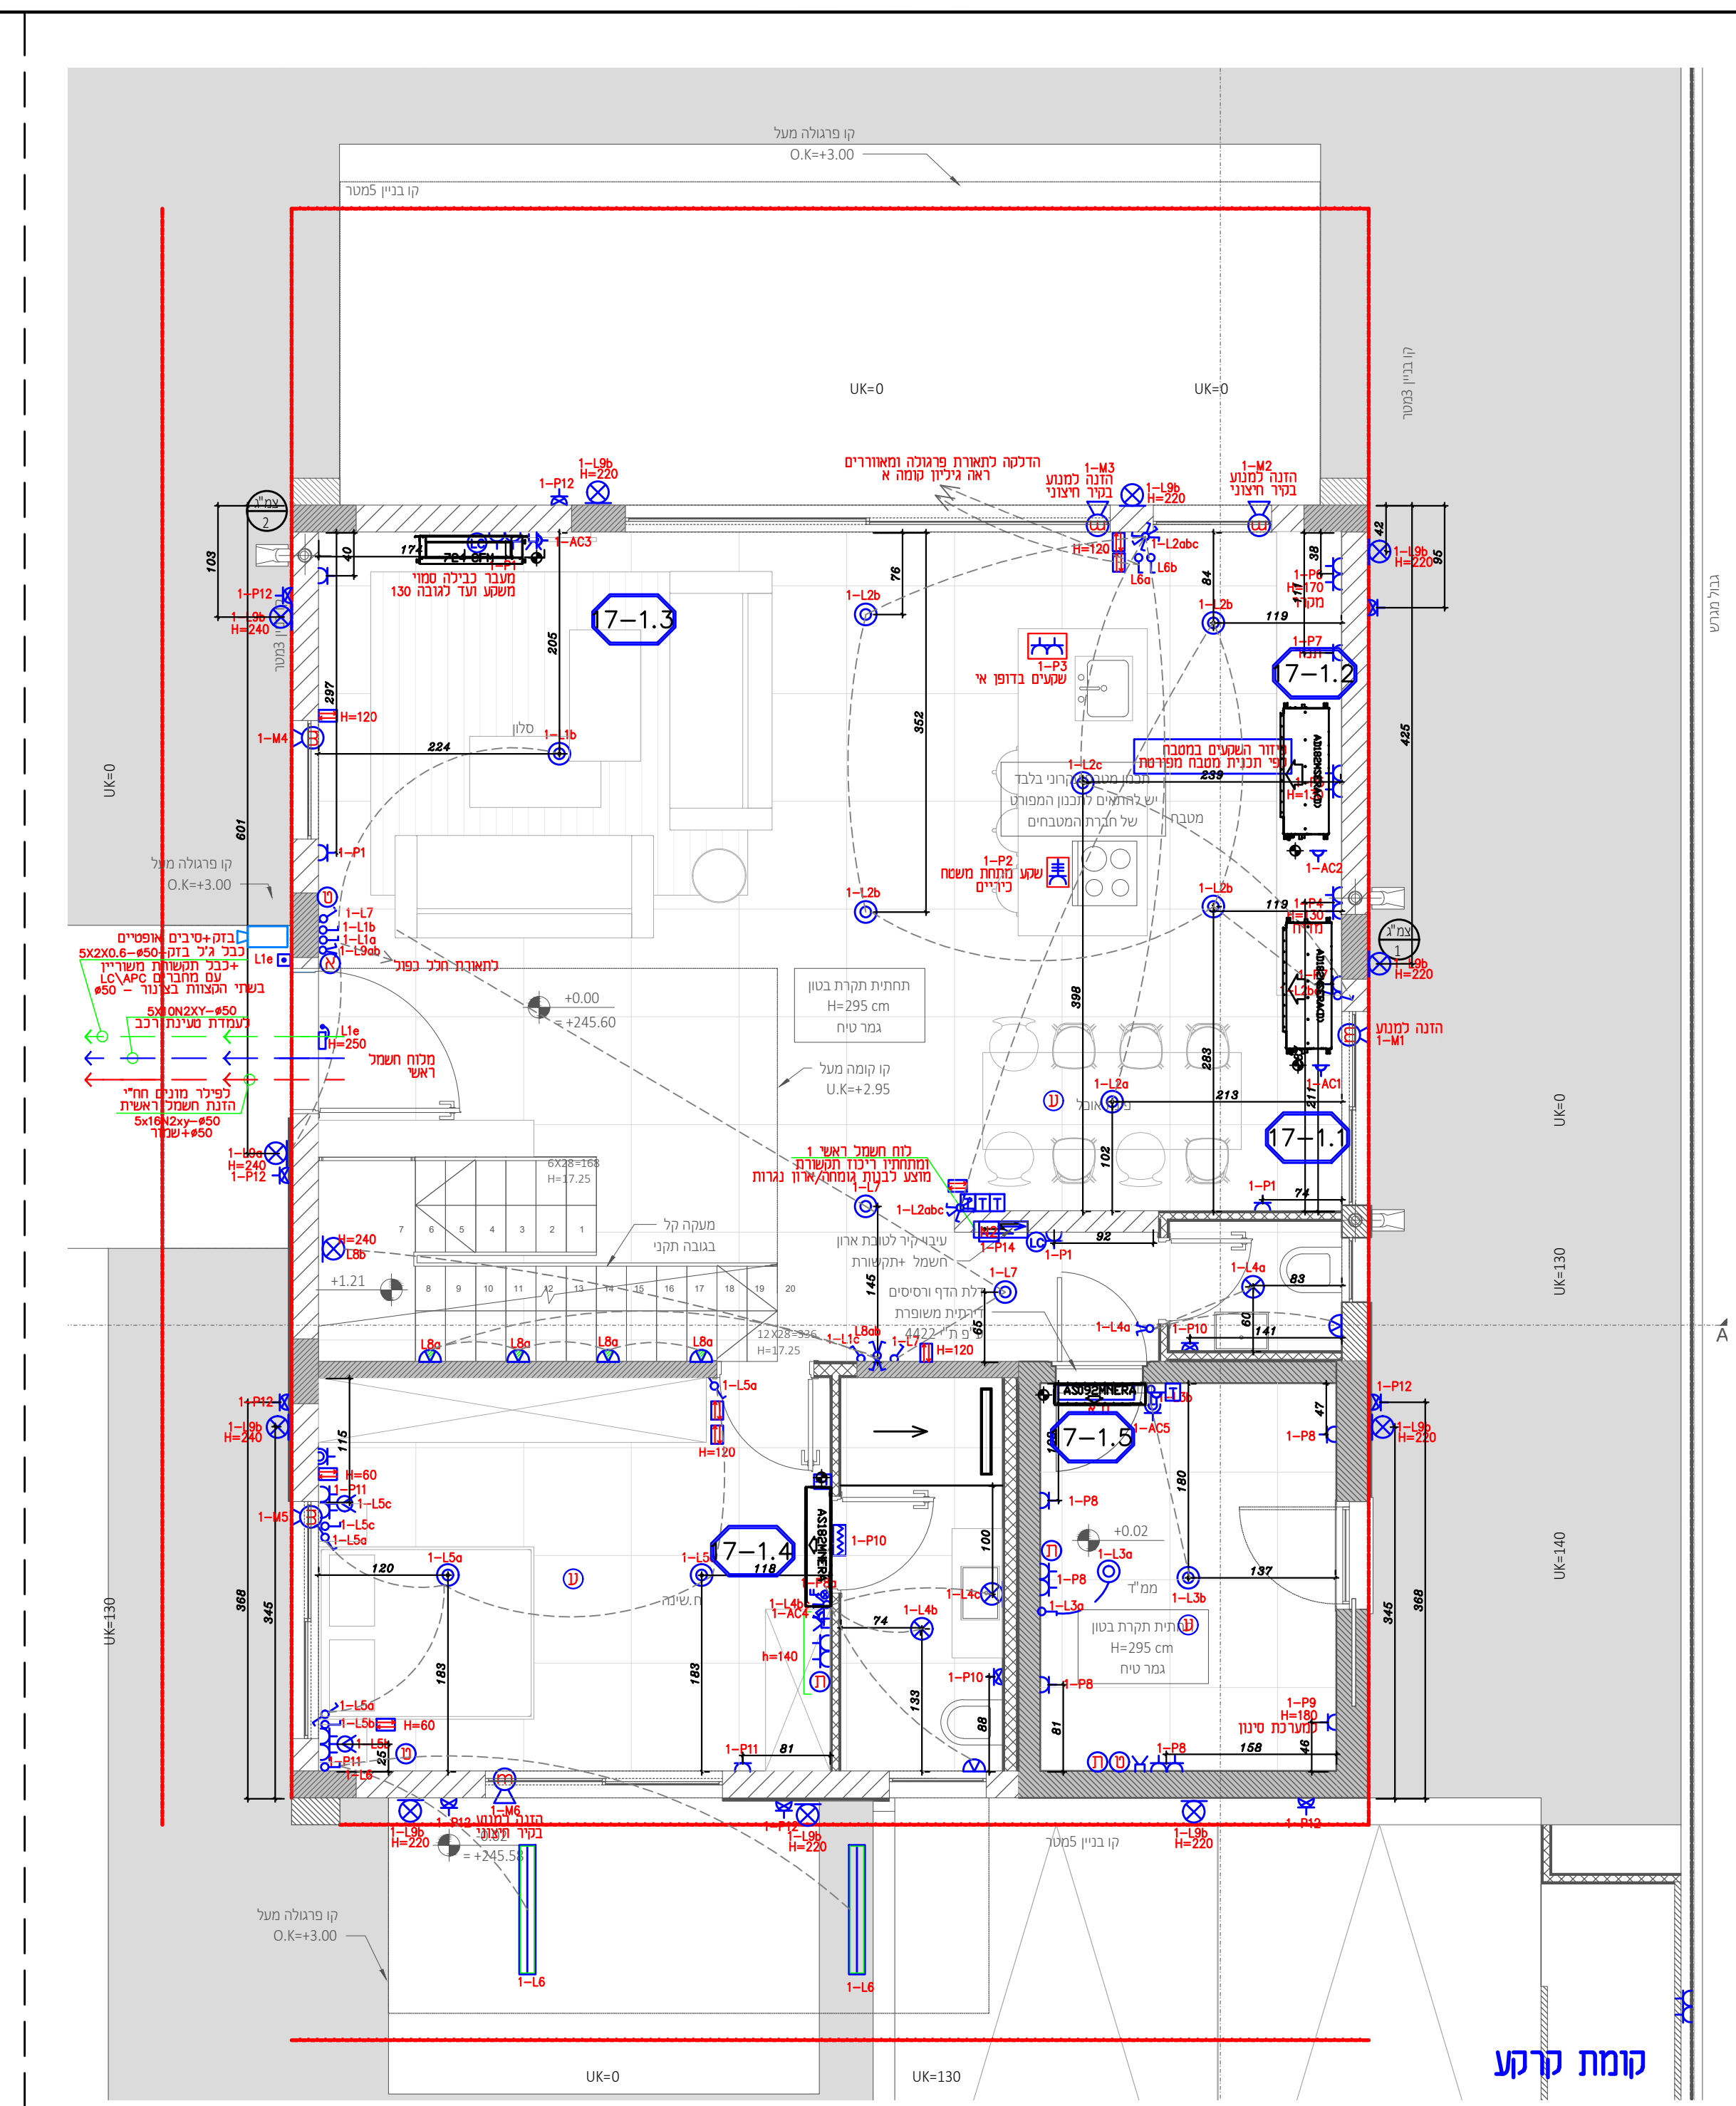
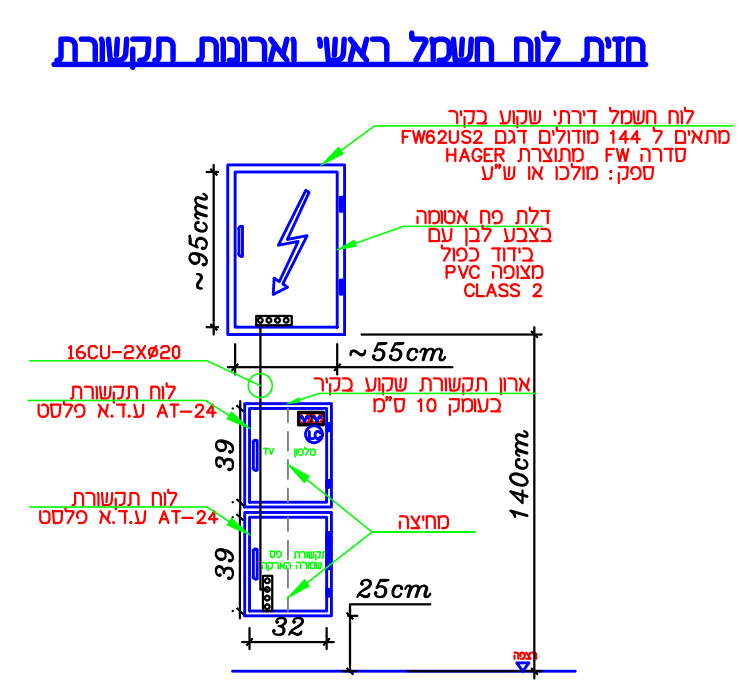
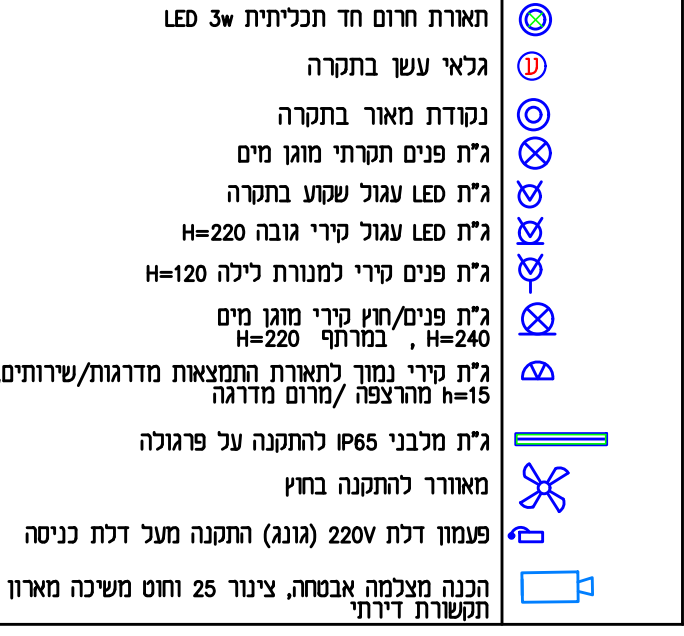


[illegible]

הערות:

- כל ההגברים בתכנית הינם למרכז אביזר
אלא אם ציין במפורש אחרת
- מיקום סופי לנקודות תאורה
ייקבע ע"פ תכנית עיצוב פנים
תאורת חיצ- ע"פ יועץ פיתוח
- מיקום סופי לשקעי מיוג
ע"פ תוכנית יועץ מיוג

עודכן ע"י: _____ יפעת

1

א. בסיס
הנדסת חשמל בע"מ
משרד: יד חרוצים 16, ירושלים 93420
טל: 074-7021015 (י"ד); 050-6550484
פקס: 077-5131015 דוא"ל: office@ebasis.co.il

שם הפרויקט:

נופיה-אלפי מנשה

שם התכנית:

לוח #1 - מגרש 17, נופיה

☒ כביצת	☐ נמכר	☐ לאישור	☐ לעיון	קנה מידה: 1:50
--	----------------------------	------------------------------	-----------------------------	-------------------

File: מס' קובץ: 675W.dwg Date: תאריך: 05.03.2025

תכנן:	שרטט:	אישר:
יפעת	ליאל	איתן

מס' עדכון:	מס' הגליון:	מס' הפרויקט:
------------	-------------	--------------

