

Court 17
1st Floor

Court 17
2nd Floor

[illegible]


חגניות ראשון	02.05.2025	
חגניות ראשון	10.04.2025	
חגניות ראשון	11.03.2025	
חגניות ראשון	04.12.2024	
חגניות כעיון	13.11.2024	
שנייים	חגרים:	סג

✕

- 25 11 2025

סימון מעגלי מיוחד אחד:

אייל ארז | מהנדסים יועצים
ישע ותכנון מערכות מידע ומערכות, פיתוח פרויקט

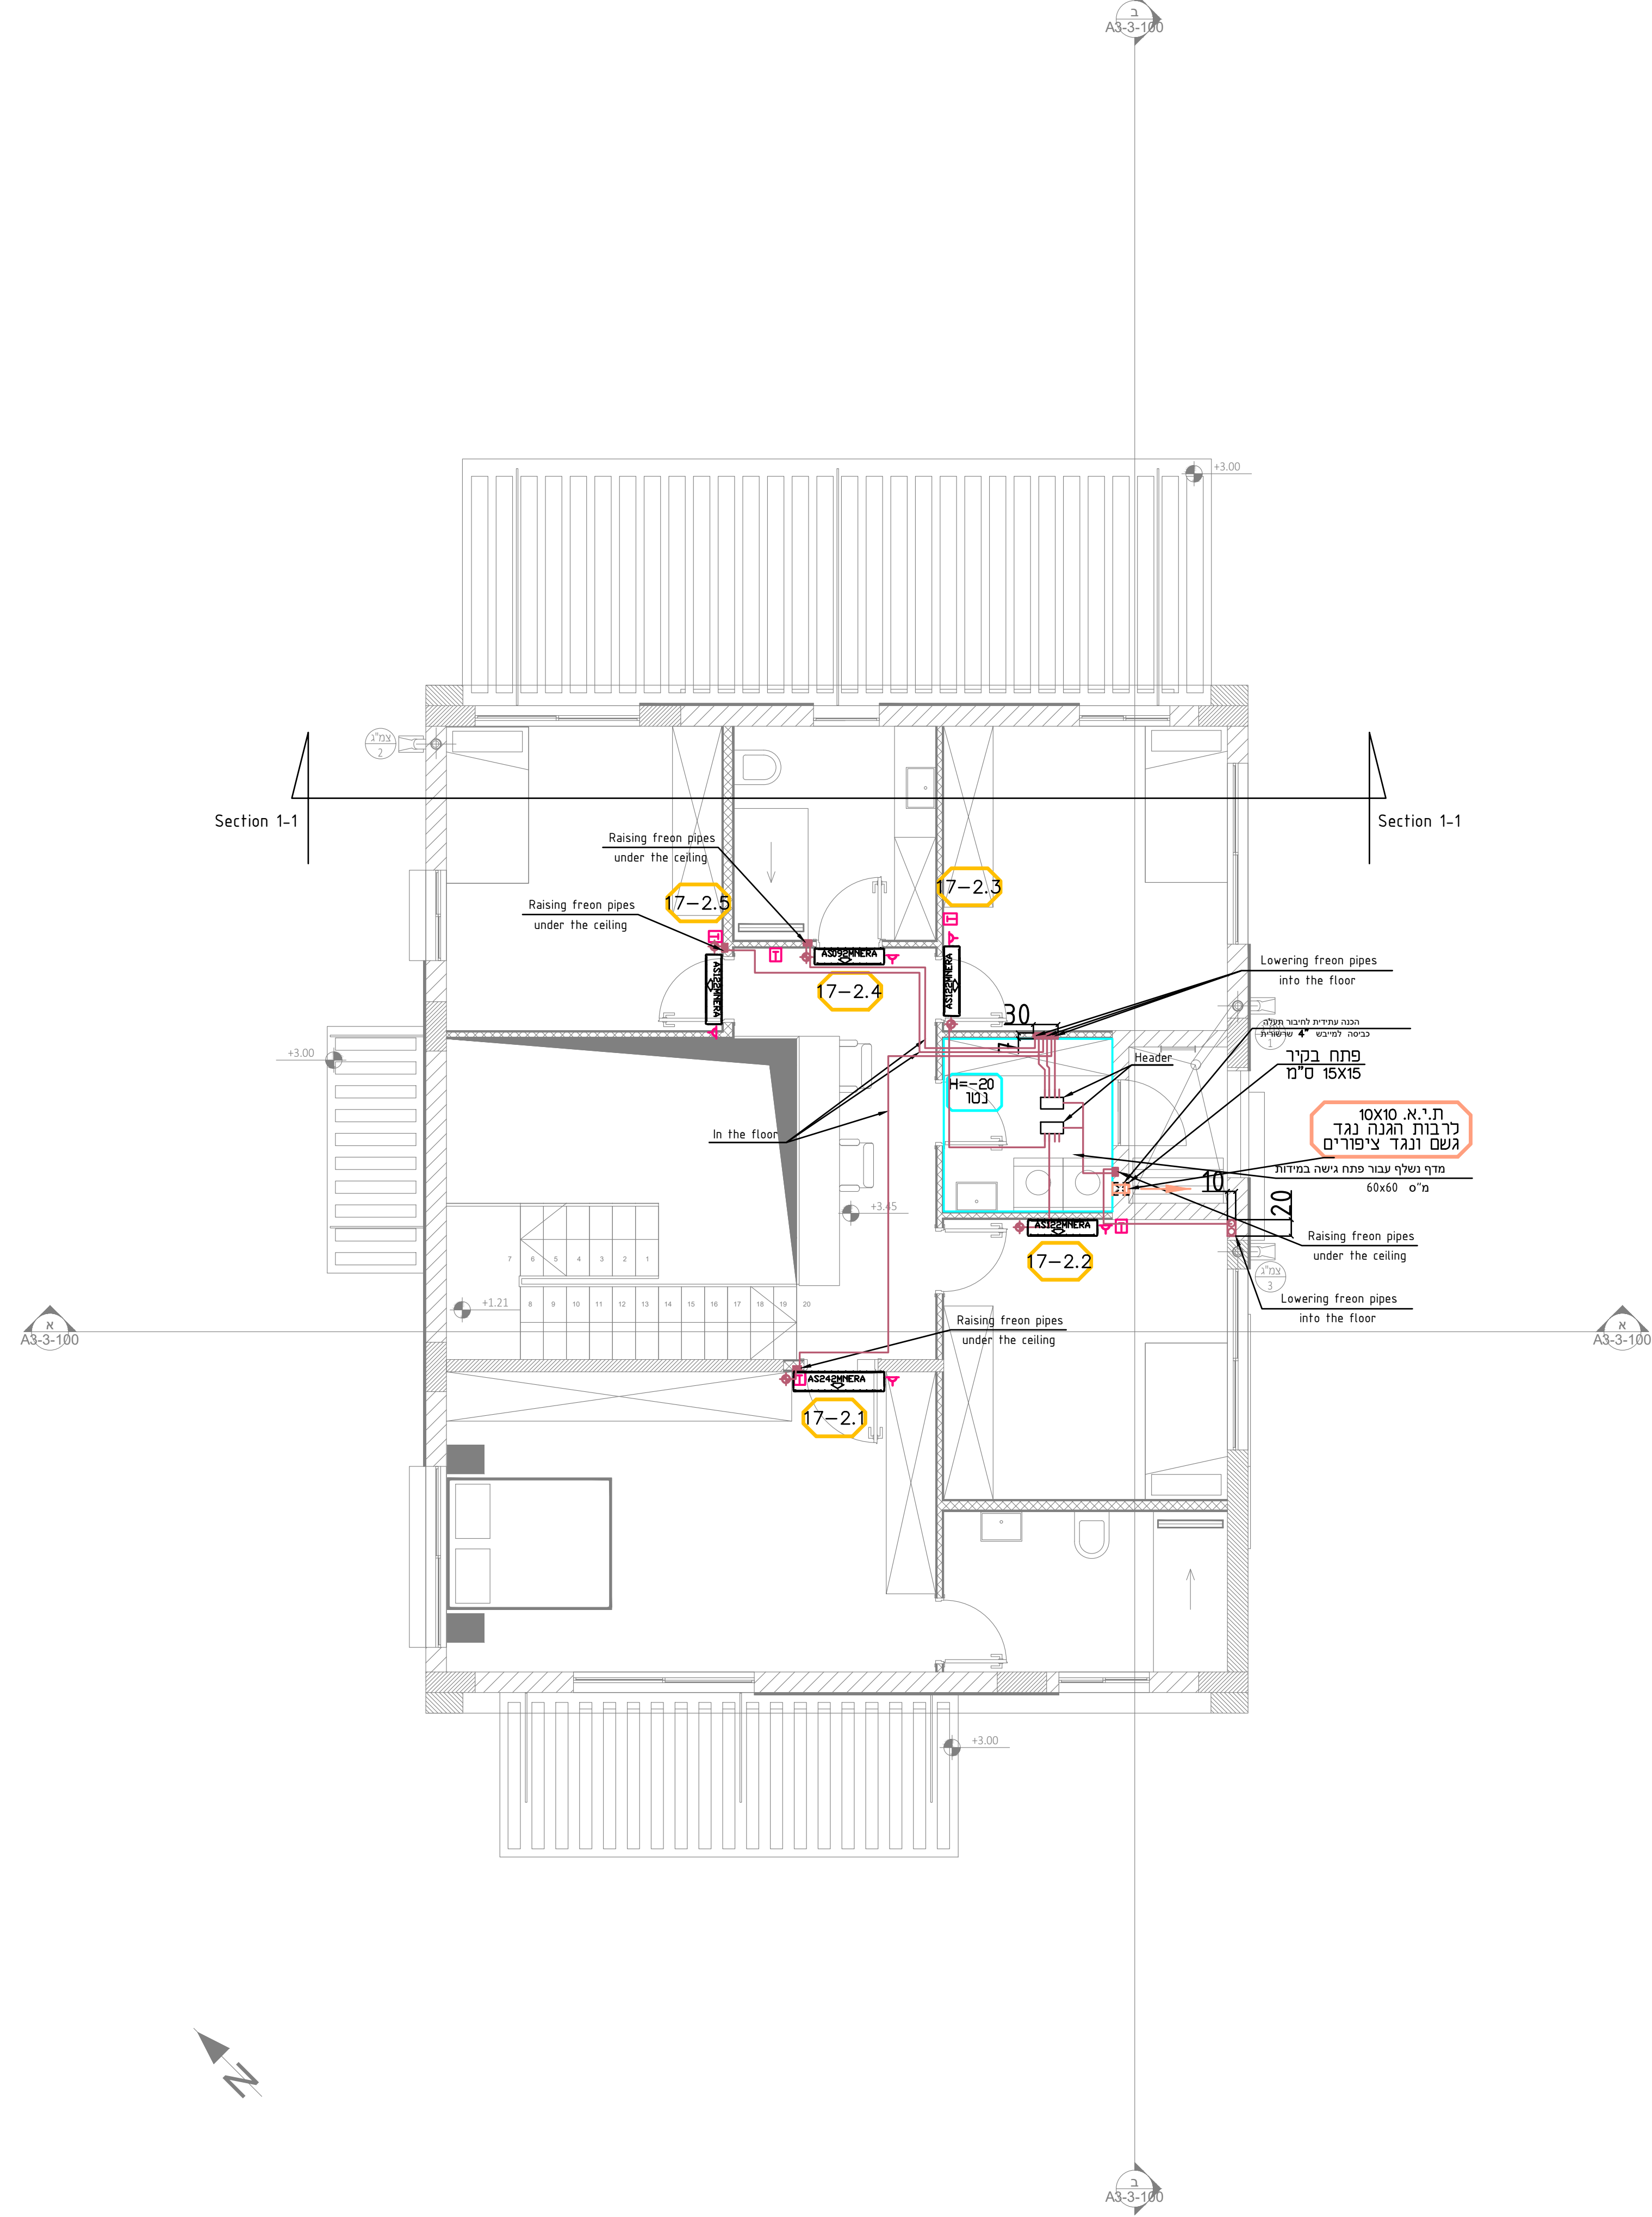


Court 17
Roof
Option No3
VRF duct units

יחידות ספה מעבר 17-1											
מס' יחידה בתכנית	חוצרות	דגם	מאייד	חופית כוור Blu/h	ספיקת אוויר CFM	צבת רעש db(A)	משקל KG	מידות גוף	מידות פני	סמך חזנה V/hz/Ph	הספק נצרך W
17-1.2	Haier	AD182MSERA(D)	Slm Duct Low ESP	19,100	471	33	22.2	171/18.5/42 ס"מ	---	230/50/1	---
17-1.3	Haier	AD242MJERA	Duct Medium ESP	24,200	724	38	33	105/72/72 ס"מ	---	230/50/1	---
17-1.5	Haier	AS092MNERA	מאייד עיני	9,500	352	36	10	115.7/28/20 ס"מ	---	230/50/1	---
17-1.4	Haier	AS182MNERA	מאייד עיני	19,100	541	40	16	111.5/33.6/25 ס"מ	---	230/50/1	---

יחידות כוח מעבר 17-2											
מס' יחידה בבניית	חוצרת	דגם	מאייד	חופית כורר CFM BUH	ספיקת אויר CFM	רמת רעש dB(A)	משקל KG	ידות מזר	סידות פנל	סחה חזנה V/Hz/Ph	הספק צורר W
17-2.1	Haier	AS242MNERA	מאייד עירי	24,200	594	44	16	175/33.6/110.5 ט"מ	---	230/50/1	---
17-2.2 17-2.3 17-2.5	Haier	AS122MNERA	מאייד עירי	12,300	371	37	10	202/28/85.5 ט"מ	---	230/50/1	---
17-2.4	Haier	AS092MNERA	מאייד עירי	9,500	352	36	10	202/28/85.5 ט"מ	---	230/50/1	---

Section 1-1

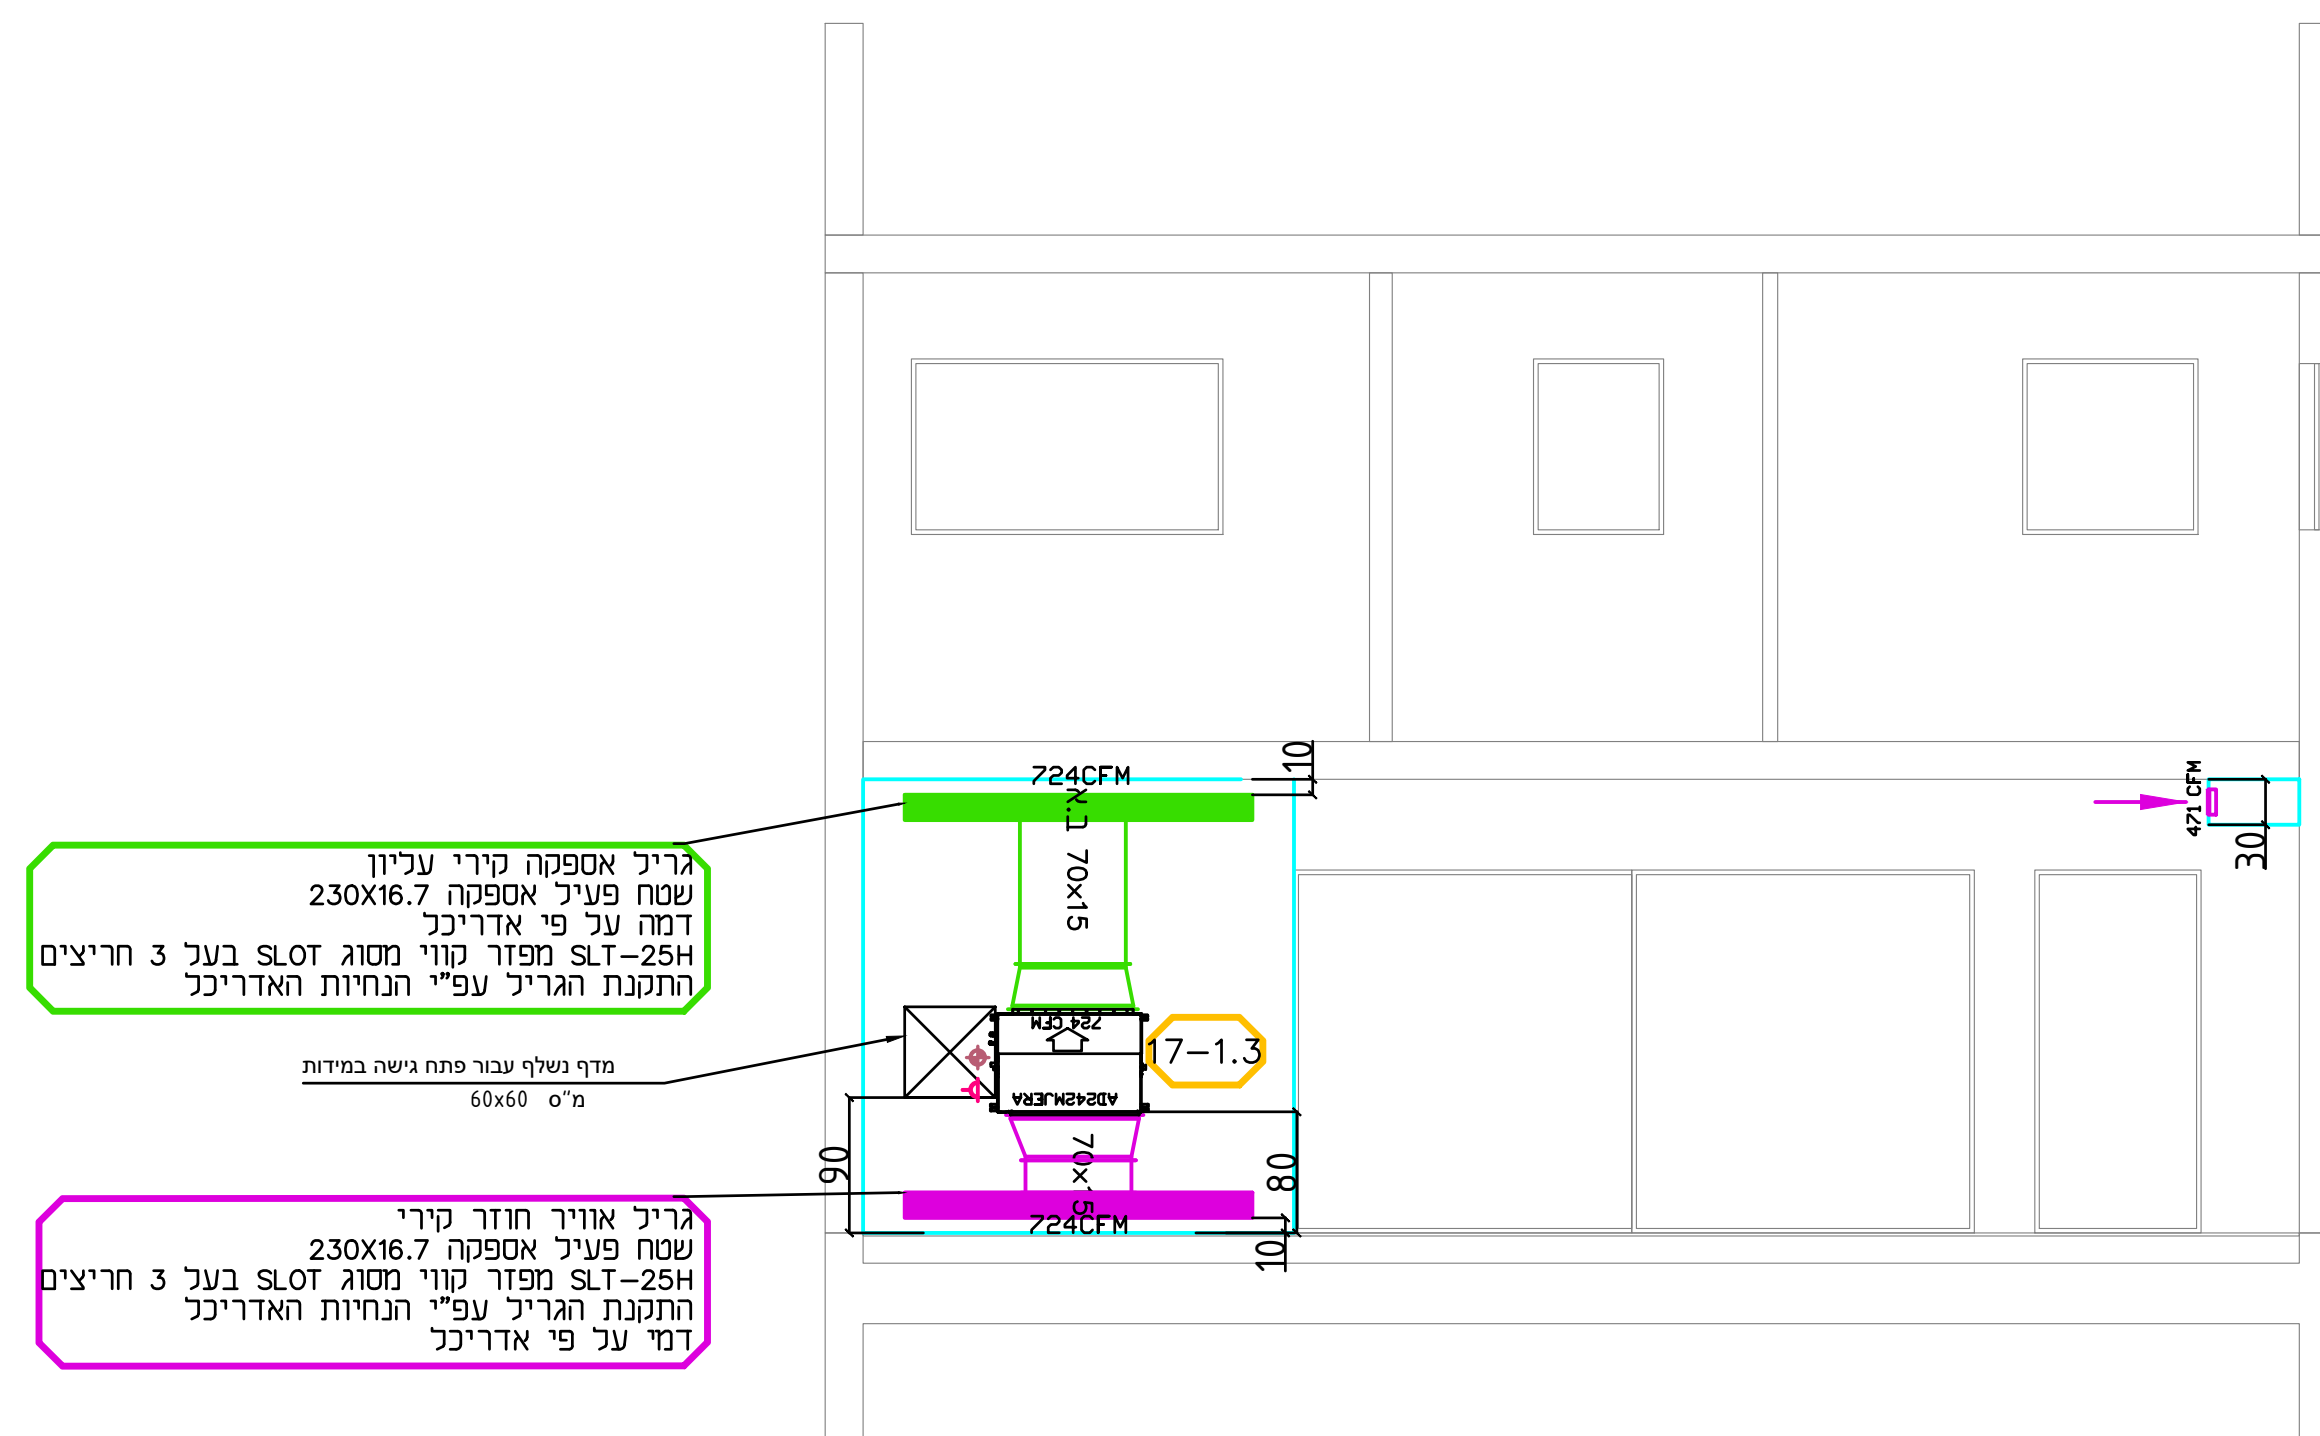

תפוצה

	אוריכל פנים
	אינסטיציה
	בסירת אש
	אקוטסיקה
	חשת ותוארה
	קונסטרוקציה
	קבלו ראש
	ניחול פוריקט
	לכוך
	אדריכל

מהדורה

תחילת לאסור	02.05.2025	
תחילת לאסור	10.04.2025	
תחילת לאסור	11.03.2025	
תחילת לאסור	04.12.2024	
תחילת לעיון	13.11.2024	
שנתיים:	תאריך:	סל:

המבצע אחראי למידות ולהתאמתן למציאות בכל מקרה של אי התאמה, חסירה או טעות עליו להודיע למתכנן לפני התקדמותו בביצועו. אין לקבוע מידות על סמך מדידה בטרנסום. אין לעשות שימוש בחוכנית זו או ברעיונות הגלומים בה ללא אישור בכתב מאת המתכנן.

הערות

1. כל התעלות מחוץ למבנה יבורוד
ביבורד בעוצם 2"
מידות התעלות הן מידות פח
2. תעלות מזוג בתוך המבנה יבורוד
ביבורד אוקטופי פנימי 2"
מידות התעלות הן מידות פח
3. תעלות אוויר צד יבורוד
ביבורד מרז 2"
מידות התעלות הן מידות פח
4. יש לאטום בסליקון את פנית החיבור
יש תעלות מזוג אוויר לפני כיפוף
הפחית המתחברים

מקרא

- [illegible]

מקרא צבעים בתכנית

- | | |
|--------------------------|---|
| תעלות ותריסי אוויר חוזר |  |
| תעלות ותריסי אספקת אוויר |  |
| תעלות ותריסי אוויר צח |  |
| תעלות ותריסי 'ניקת אוויר |  |
| תעלות ותריסי 'שחרור עשן |  |
| צנרת גז וחשמל |  |
| סימון מעגלי מידוג אוויר |  |

191	מבני מוֹרִים צְמוּדֵי קֶרֶק נֹפִיר אֶפְרִי מִנְשֵׁה מִגְדָּשׁ 17
1:50	מִזְדוּג אוֹוִיר ואִיוּרור
02.05.2025	קוֹמַת גִּג וּטְבִילֵאוֹת
5	
דְּבִיעוּ	עָוִי
דְּבִיעוּ	עָוִי
13.11.2024	הַיָּדִי
אִיִּי אִדָּ	תְּבִנָּה וְהַסָּמָ