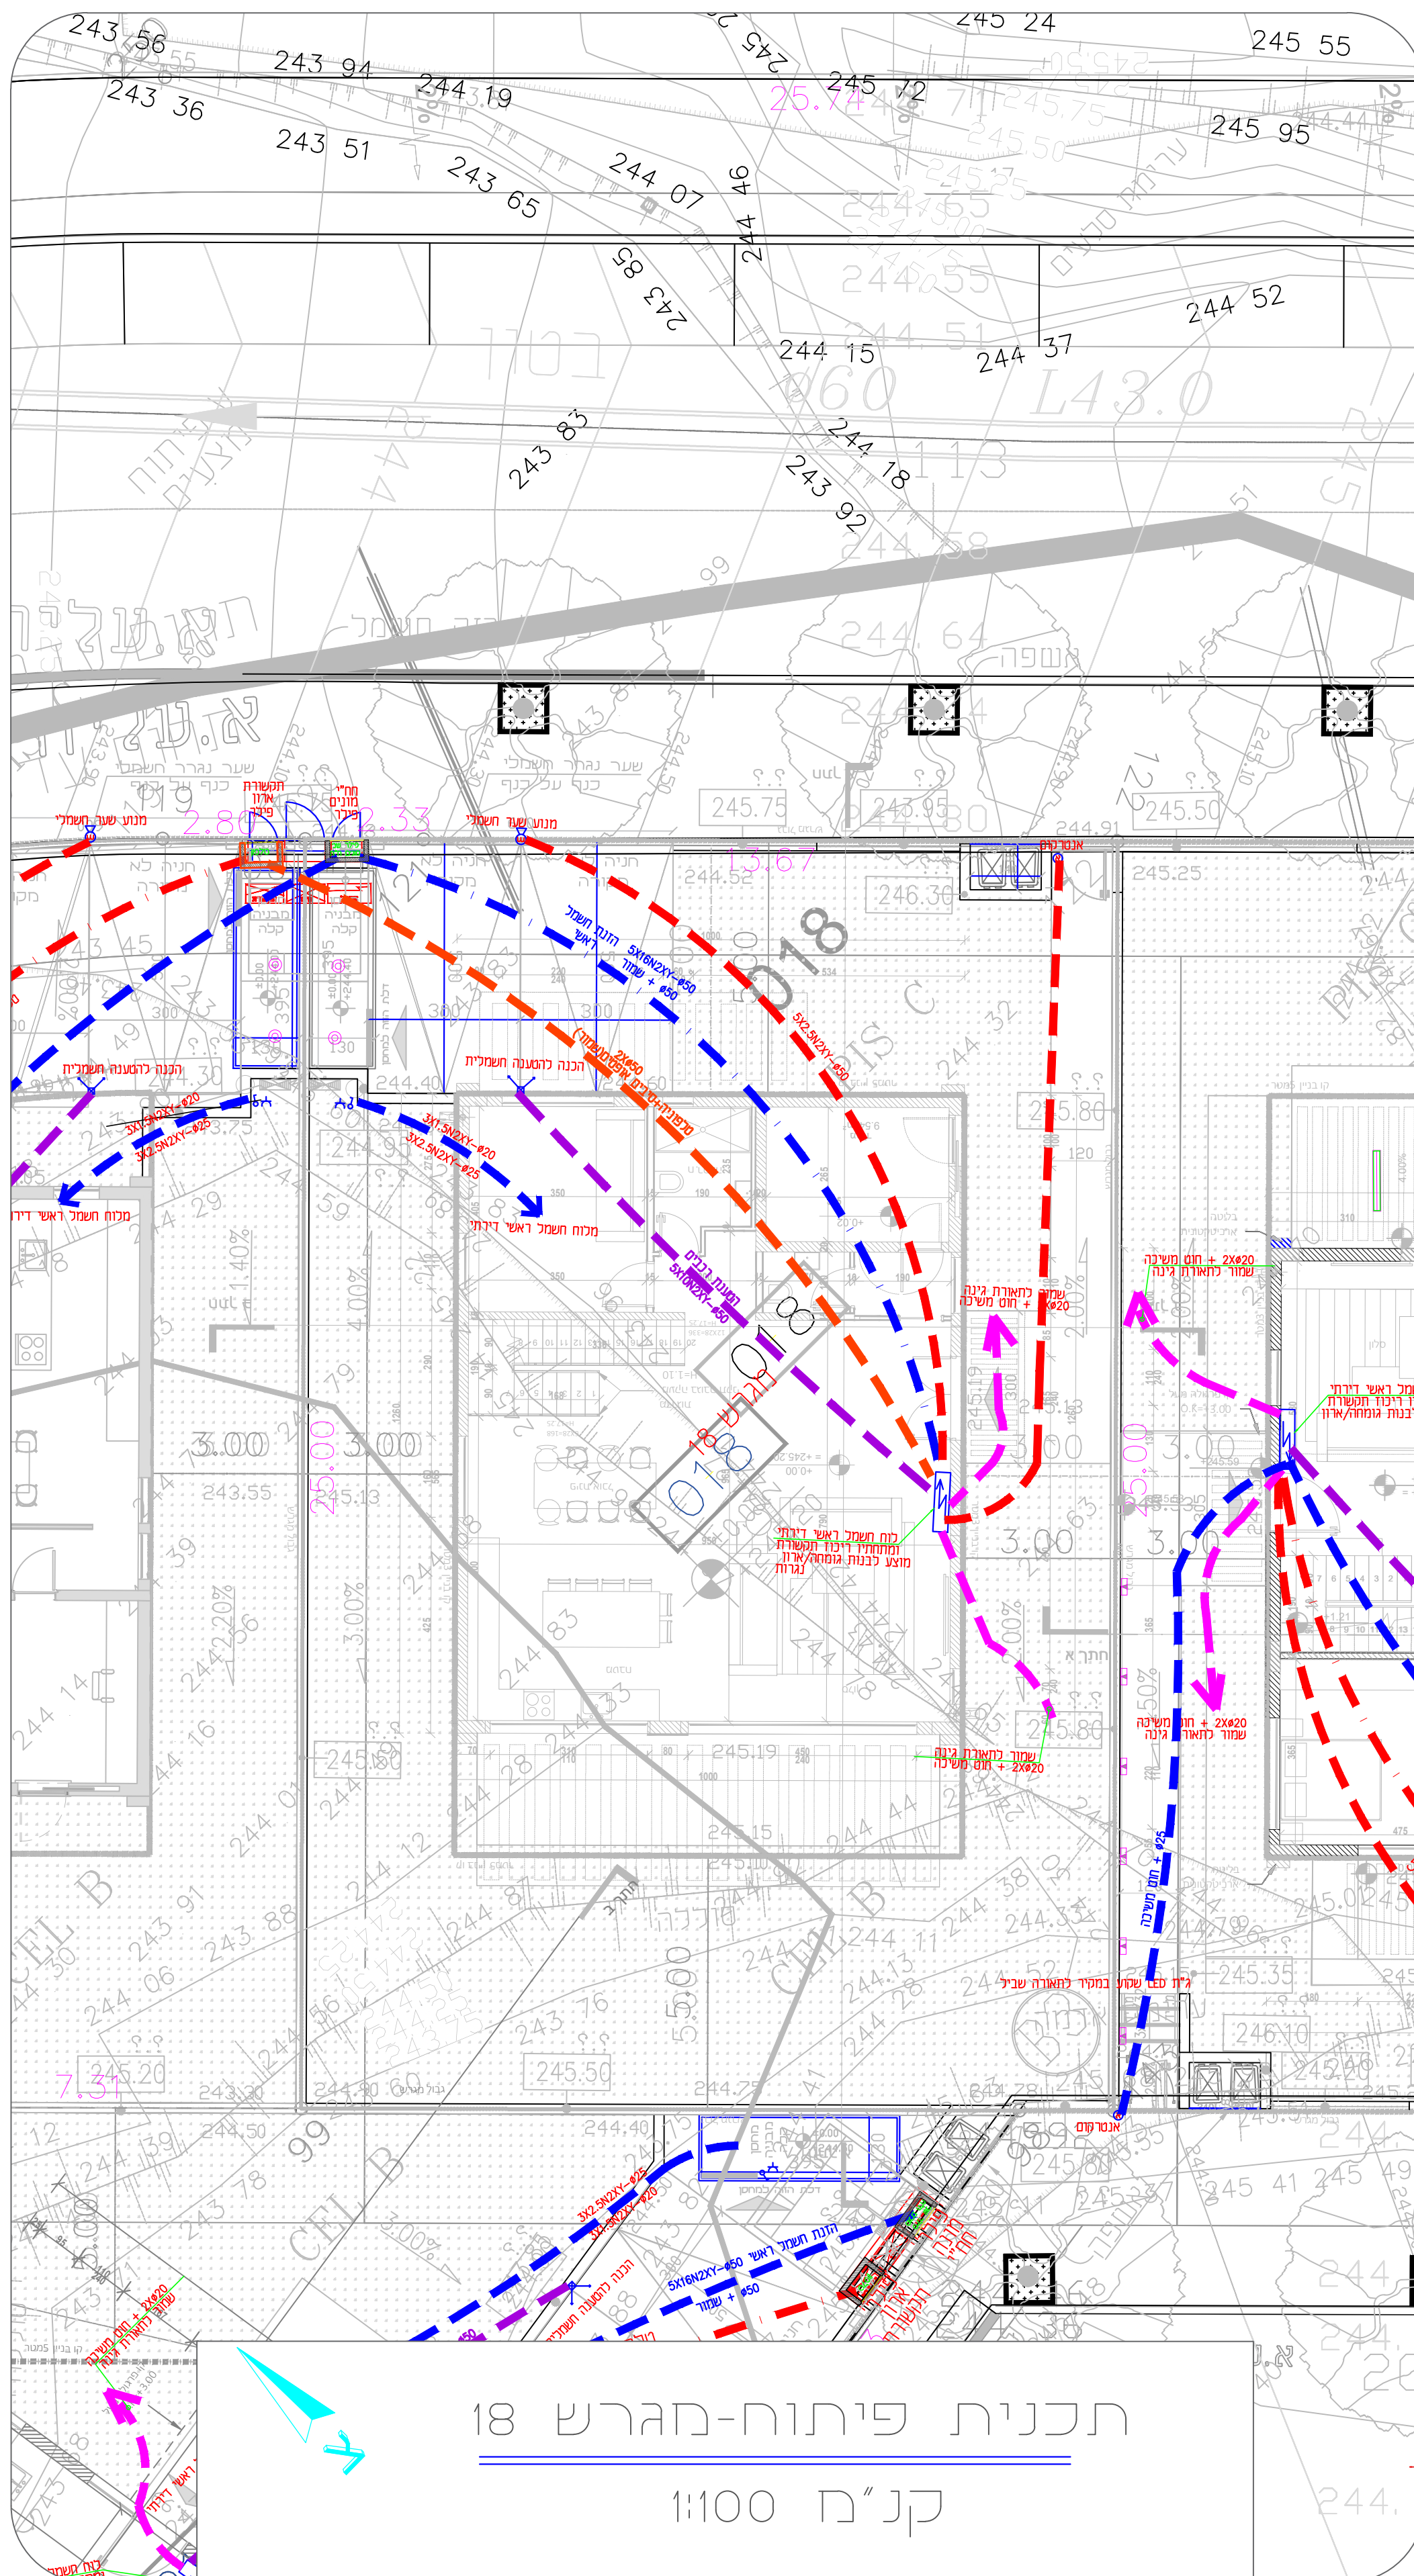


יחידות כפול ומקביל 18-2												
הספק נאמד	מחזור הזנה V/Hz/Ph	מדידות פזל	מדידות זווית	משקל kg	רמת געש dB(A)	מדידות פזל	מדידות זווית	מדידות פזל	מדידות זווית	דגם	חברת	פסי יחידות בתכנית
---	230/50/1	---	ט"מ 204/283/85.5"	10	37	471	12,300	מאייר	מאייר ע"י	AS182MNERA	Haier	18-2.2 18-2.3 18-2.5
---	230/50/1	---	ט"מ 250/33.63/110.5"	16	39	371	15,300	מאייר	מאייר ע"י	AS182MNERA	Haier	18-2.
---	230/50/1	---	ט"מ 250/33.63/110.5"	16	44	594	24,800	מאייר	מאייר ע"י	AS242MNERA	Haier	18-2.

[illegible][illegible]

עודכן ע"י: _____ רחל

א. בסיס
הנדסת חשמל בע"מ
משרד: יד חרוצים 16, ירושלים 93420
טל: 074-7021015 ; נייד: 050-6550484
קדם: 077-5131015 ; דוא"ל: office@ebasis.co.il

שם הפרויקט:

נופיה-אלפי מנשה

שם הגיליון:

תוכנית פיתוח מגרש 18

○ ● ○ ○ לביצוע למשורר לעיון		קנה מידה: 1:100	
File: מס' קובץ: 675P.dwg		Date: תאריך: 17.06.2024	
אישר: איתן		שרטט: אילה	
מס' הפרויקט: 675		מס' הגליון: P18	
		מס' עדכון: 0	

