

[illegible]

		4
		3
		2
חברות בע"מ	02.04.2025	1
שנים:	חאיר:	ס:

הערות

- $\mathbb{N}$


- מקרא צבעים בתכנית

- | | |
|--------------------------|---|
| תעלות ותריסי אוויר חוזר |  |
| תעלות ותריסי אספקת אוויר |  |
| תעלות ותריסי אוויר צח |  |
| תעלות ותריסי ניקת אוויר |  |
| תעלות ותריסי שיחרור עשן |  |
| צנרת גז וחשמל |  |
| סימון מעגלי מידוג אוויר |  |


191	מבני מורים צמודי קרקע נופיה ארפי מנשה מגרש 18	שם המדינה:	חבר מדינה:
1:50	מידוג אוויר ואווורור	שם המדינה:	חבר מדינה:
02.04.2025	קומה ראשונה ושנייה	שם המדינה:	חבר מדינה:
החיר מדינה		שם המדינה:	חבר מדינה:
☐ כביע ☐ מנכר ☒ מנכר ☐ מנכר	☐ מנכר ☒ מנכר ☐ מנכר ☐ מנכר	☐ מנכר ☒ מנכר ☐ מנכר ☐ מנכר	☐ מנכר ☒ מנכר ☐ מנכר ☐ מנכר
02.04.2025	איי ארד	שם המדינה:	חבר מדינה:
החיר מדינה		שם המדינה:	חבר מדינה:

Option **No1**

ככלל יחידות המיזוג אשר נמצאות בתוך נגרות יש לתאם סופית מול אדריכל ונגרות

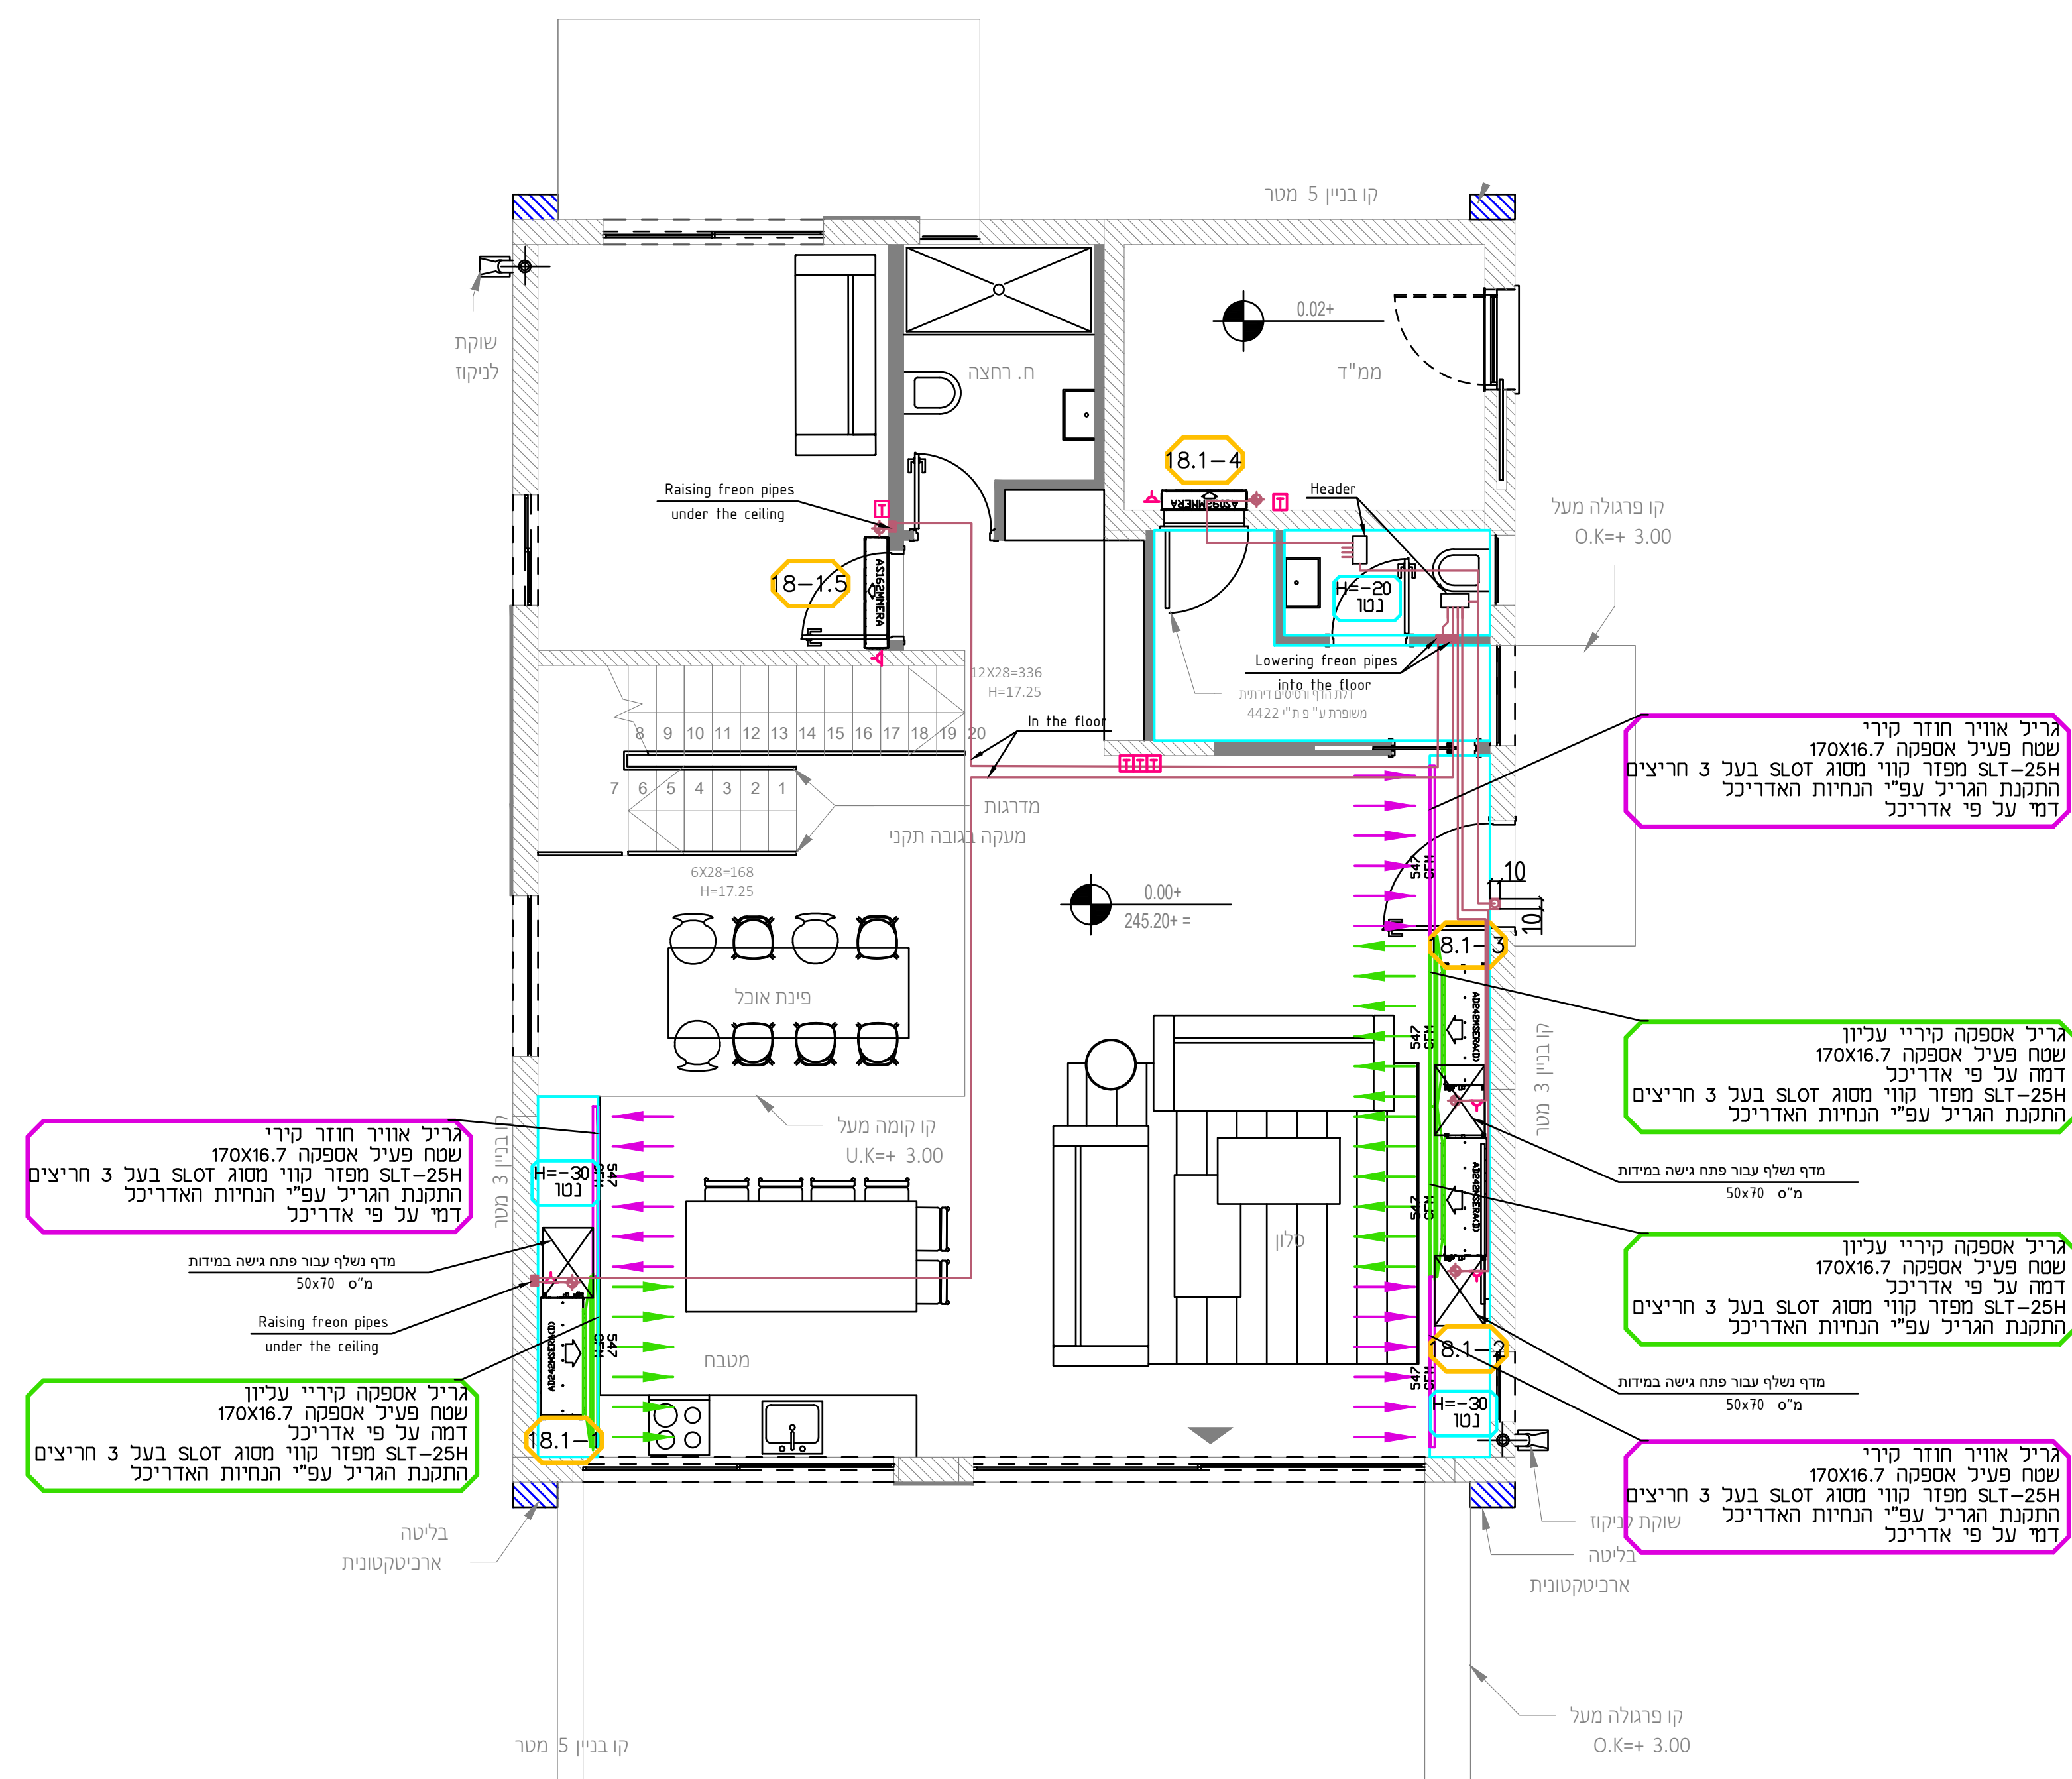Option **No1**

VRF duct unit in living room
and wall mounted in rooms

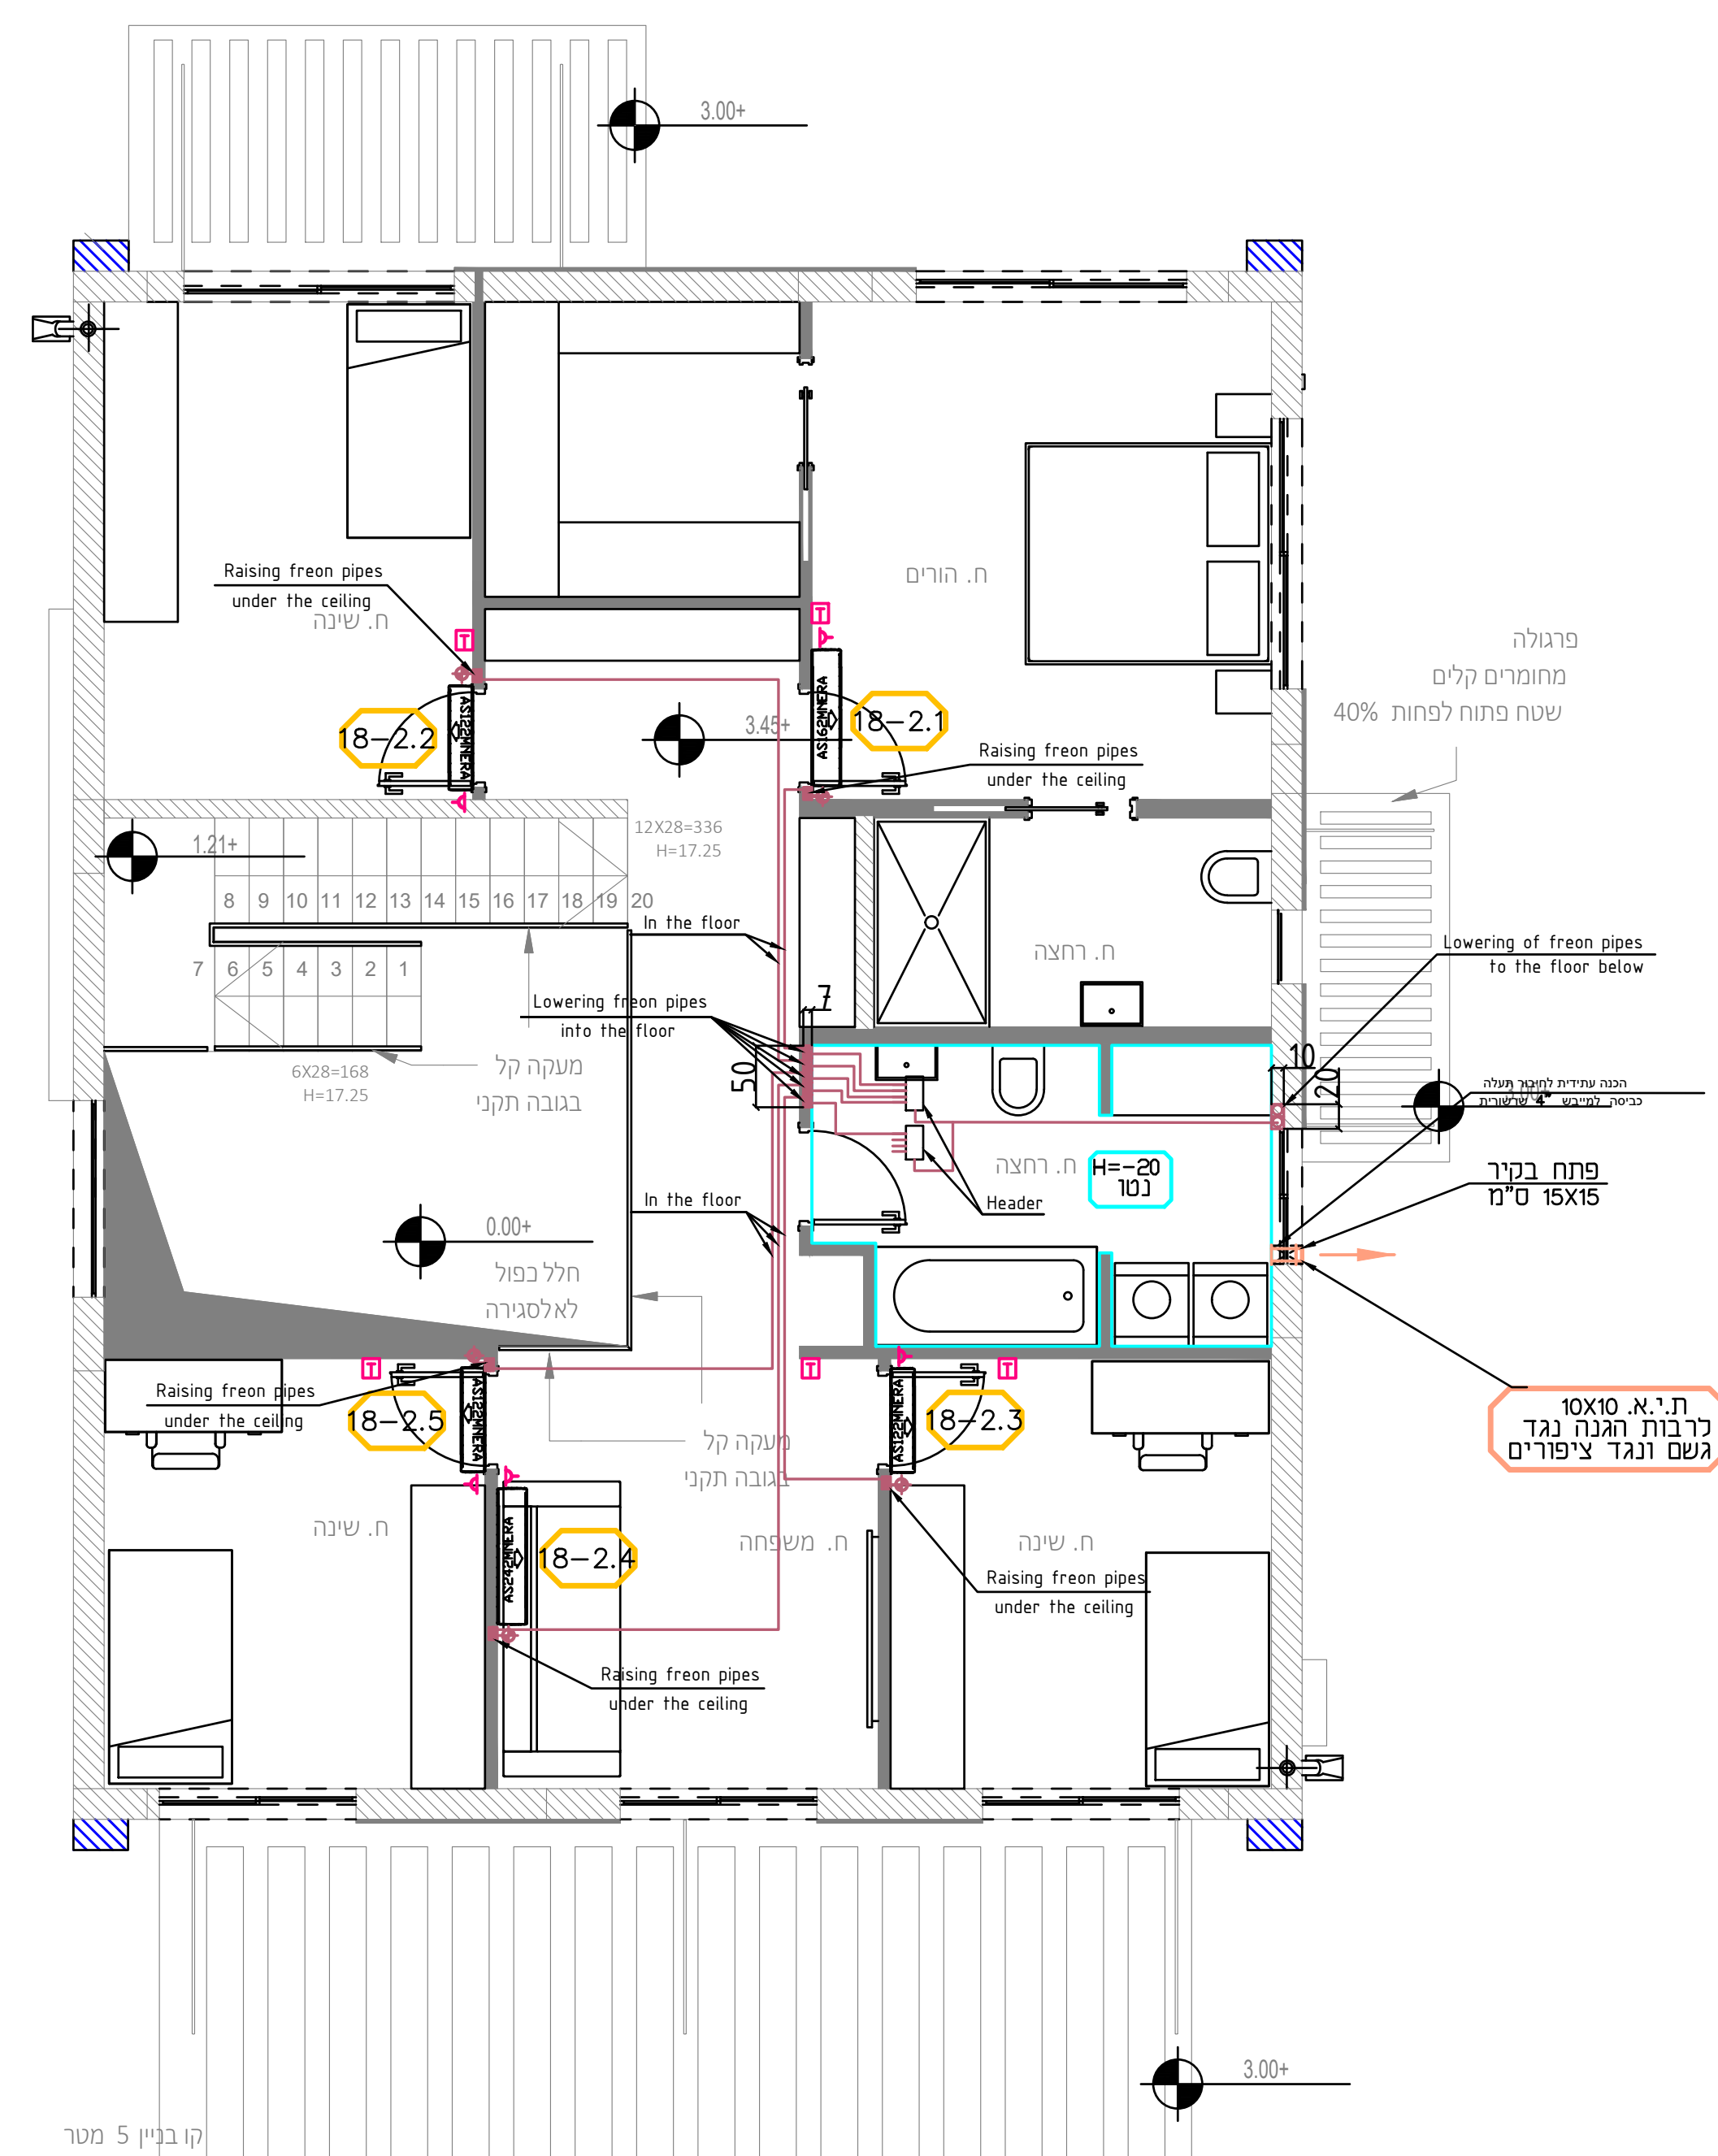

אוריכל פנים	
אינסטיציה	
בסיחת אש	
אקוסטיקה	
חשתי והזרה	
קונסטרוקציה	
קבלו ראש	
ניחול פרויקט	
נמח	
אוריכל	

		⚠
		⚠
תבנית כעיון	02.04.2025	⚠
שנתיים	חאריץ:	ס:

הערות

- N^-


- מקרא צבעים בתכנית

- | | |
|--------------------------|---|
| תעלות ותריסי אוויר חוזר |  |
| תעלות ותריסי אספקת אוויר |  |
| תעלות ותריסי אוויר צח |  |
| תעלות ותריסי יניקת אוויר |  |
| תעלות ותריסי שיחרור עשן |  |
| צנרת גז וחשמל |  |
| סימון מעגלי מזווג אוויר |  |

191	מבני מגורים צמודי קרקע נופיה אפלי מנשה מגרש 18		
הח' הדרום	שם הדרום		
1:50	מיזוג אוויר ואווירודור		
ש"מ			
02.04.2025	קומת גג וטבלאות		
הצד השמאלי	שם הצדדים		
			
החזית			
  	שם הצדדים		
כניסה	מכוד	אשור	עקין
02.04.2025			
חגית			
א"י ארז			
חגית			

Option **No1**

VRF duct unit in living room
and wall mounted in rooms

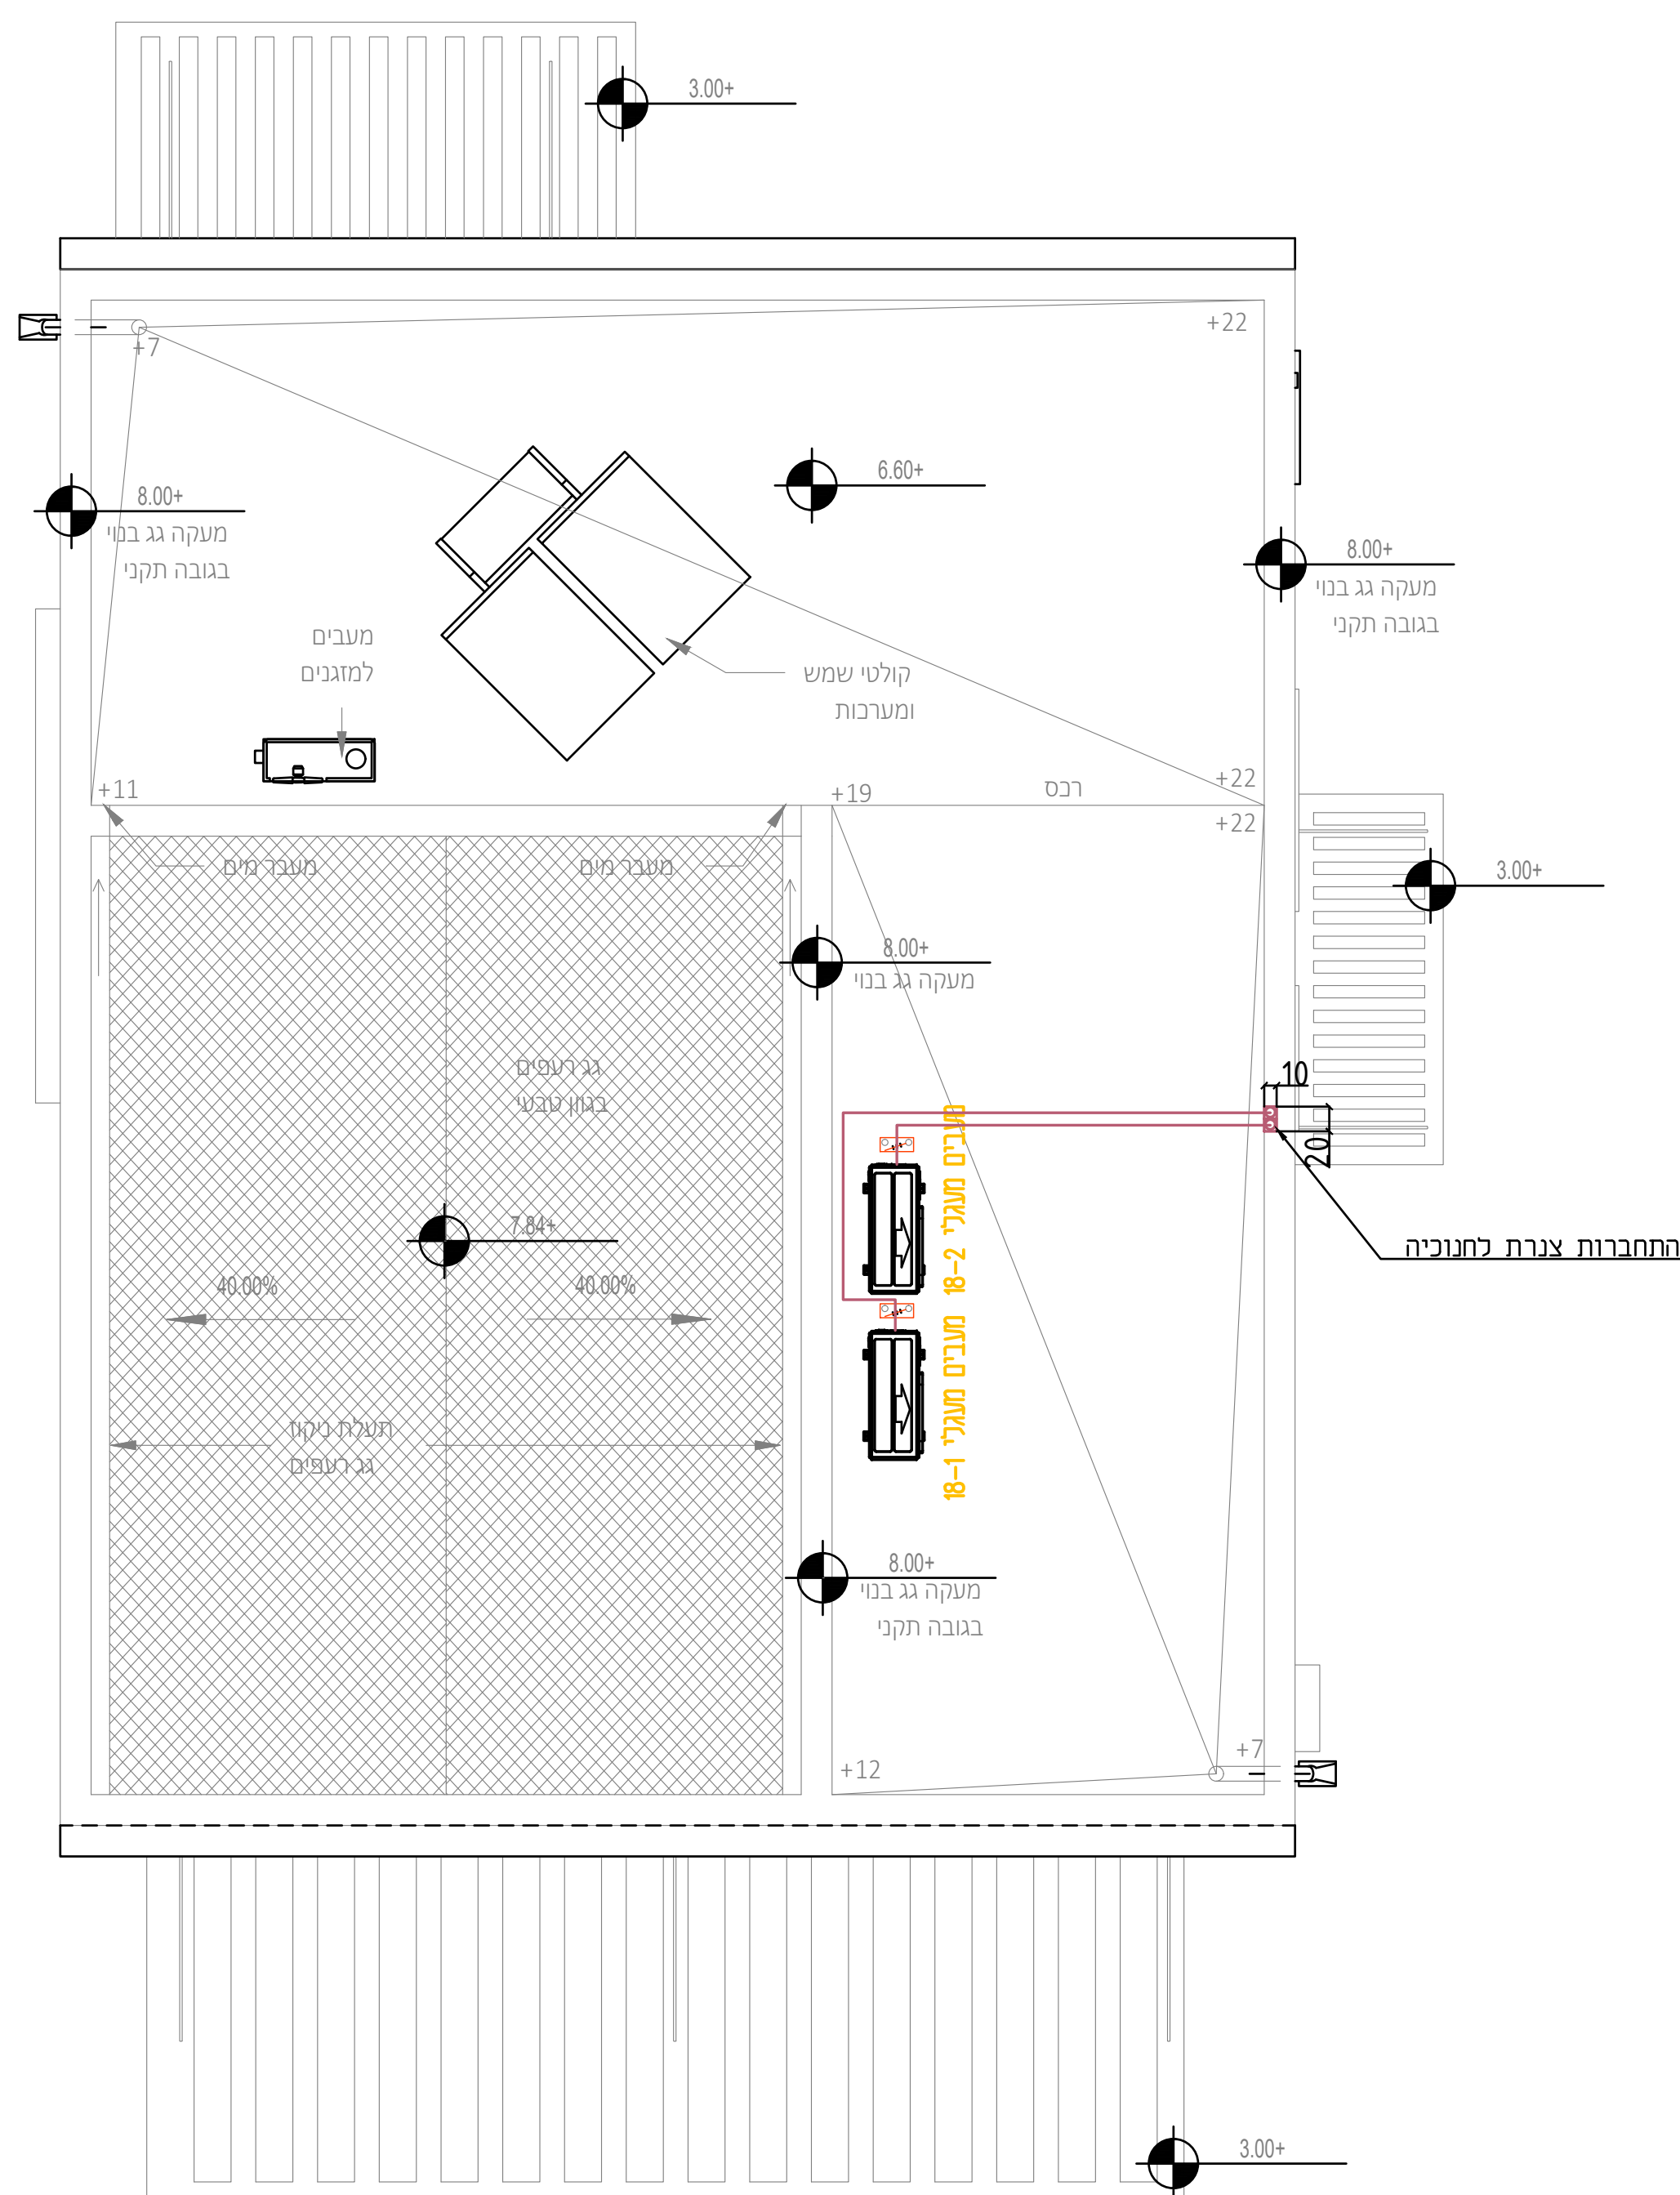

בסיס בטון בגובה מינימלי 10 ס"מ
יחידת עיבוי עומדת ע"ג בולמי רעידות
לטיפול קבלן מיזוג אוויר

מיקום סופי של המעבים
ייקבע בשטח
בתיאום עם האדריכל
יב בליי מזור מזור

מיקום סופי של הניקוזים
ייקבע בשטח בתאום עם האדריכל
יועץ אינסטלציה וקבלן מיזוג אוויר

בסיס בטון בגובה מינימלי 10 ס"מ
יחידת עיבוי עומדת ע"ג בולמי רעידות
לטיפול קברן מזוג אוויר

מיקום סופי של המעבים
ייקבע בשטח
בתיאום עם האדריכל

מיקום סופי של הניקוזים
ייקבע בשטח בתאום עם האדריכל
יועץ אינסטלציה וקבלן מיזוג אוויר

מכשירי מעגלי 18-
AV10NMSETA : דגם
95,500 BTU/Hr : תפוקה
40V/163.6A/105V : מדרה
נתיך חשמלי: (A) 3x25
168 ק"ג : משקל
8 (kW) : הספק נצרך
58 dBS(A) /



מכשירי חשמל 18-2

AV08NMSETA	: דגם
77.100 BTU/Hr	: תפוקה
40W/163.6J/1057	: מידה
3x20 (A)	: נתון חשמלי
168 ק"ג	: משקל
5.79 (KW)	: הספק נצרך
55-100	: טווח



יחידות טפט תמידי 18-1											
סמל יחידה בתכנית	חוצרת	דגם	מאייד	תפוקת קור Btu/h	ספקית אייר CFM	רמת רעש dB(A)	משקל kg	יחידות גוף	יחידות פני	מחם חזנה V/Hz/Ph	הספק צינור w
18-1.1, 18-1.2, 18-1.3	Haier	AD242MS1ERA(D)	Slim Duct Low ESP	24,200	547	36	24	17.1/18.5/42.0 ט"מ	---	230/50/1	---
18-1.4	Haier	AS092MNERA	מאייד עיני	9,500	352	36	10	17.5/28.9/85.5 ט"מ	---	230/50/1	---
18-1.5	Haier	AS162MNERA	מאייד עיני	15,300	471	39	16	17.5/33.6/111.5 ט"מ	---	230/50/1	---

יחידות קצרה מעל 2-18														
מש' יחידה בחכמית	חוצרת	דגם	מאייד	תפוקת קורו Btu/h	ספק אייר CFM	רעש dB(A)	משקל kg	יחידות מ"ר	יחידות מ"ר Vtg/Ph	מחם חזנה W	הספק צינור W			
18-2.5	18-2.3	8-2.2	Haier	AS122MNERA	מאייד עי"ר	12,300	371	37	10	5.7/28.1/85.5	ס"מ			
18-2.1	18-2	8-2.2	Haier	AS162MNERA	מאייד עי"ר	15,300	471	39	16	5.7/33.6/111.5	ס"מ			
18-2.4	18-2	8-2.2	Haier	AS242MNERA	מאייד עי"ר	24,200	594	44	16	5.7/33.6/111.5	ס"מ			