


מתכננים:

ניהול פרויקט
מהיסוד - בן סולומון
פיקוח
מהיסוד - בן סולומון
קונסטרוקציה
ערן שילר
מיזוג אוויר
אייל ארז מהנדסים ויועצים בע"מ
אינסטלציה
איתן אלמסי
חשמל
איתן בסיס
אלומיניום
נוף
נתי בלוקא
חשמל חכם
חימום תת רצפתי
איטום
צבי טל
אקוסטיקה
מעליות
קרקע וביסוס
דיה הנדסת קרקע וביסוס
רישוי

± 0.00 = +243.50
הערות: 1. תכנית זו יש לקרוא יחד עם תכנית הריטשים. 2. גובה אבטמילסי - ראו תכנית פיתוח. 3. המידות הן בין קירות הבניה ולא כולל פיתח. 4. פיתוח השטח סביב הבנוה, כולל, מדרגות, גדרות, שבילים, ריצופים, שיטפים, גדרים, חניה גינה וראו תכנית פיתוח. 5. איסוס קירות ורצפות הבנוה כמנוע עם הקרקע ובידוד תרמי לאורך העמודים והקורות וכל התקנות - כליות או עם סימני (גומן) - ראו תכנית קונסטרוקציה. 6. אף חים יבוצע בכל מישור אופקי הכולס מהגבין. 7. פיתח תרמי במסיד - ע"פ מפרס חומקיר, מאושר ע"י פיקוח העודף.
המבצע אחראי לסידות : עליו לבקר ולבדוק את כל המידות בתכנית ובקשות העבודה. במסור של מנות או אי התאמה בתכנית /או בבנוי, עליו להודיע על כך מיד לאדריכל בסרט המשרד בענבודתו. המבצע ישממש או וקע בתכנית שאושרו לכניצוע. המבצע יחזיק באחר, בכל מה, של מועדכו של תכנית. אל לקבוע מידות על ידי חדייה בשר מוס. התכנית הנה רכוש האדריכל ואין לשנות כל שימוש בה או ברעיונות הגלומים בה, אלא באישור בכתב מהאדריכל. מוהנס /או/ יושע אשר שמו רשום בתכנית זו, נושא לכיד באחריות המקצועית והמקנית לתכנית. על המפעק והמקני לודא התאמת התכנית האדריכלית "לכניצוע" לתכנית ויתר, המכר והתכנית המאושרות ע"י כל הגורמים הרשמיים. התכנית כוללת את כל האחריות והידוע עד ליום תוצאתה.

משרד קירות:

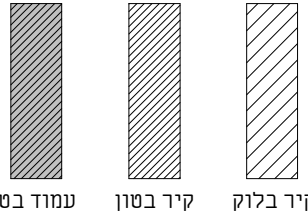

תאריך	תיאור	מהדורה
22.09.2025	מכרז	1

אדריכלות

שם המסמן:	CLIENT NAME:
קבוצת רכישה נופיה	
שם הפרויקט:	PROJECT NAME:
נופיה - מגרש 19	
שם הגליון:	DRAWING NAME:
גליון שער	
מספר גליון:	SHEET NUMBER:
A3-1-099	
מהדורה:	EDITION:
קנה מידה:	SCALE:
סטוס:	STATUS:
למכרז	
שורסס ע"י:	נבדק ע"י:
תאריך:	DATE:
22.09.2025	



נויטן חיינר אדריכלים
מורד החדשים 2, בית חירות
09-954642 78
office@nh-arch.com
www.nh-arch.com

זכיות יימור / ע"פ הנחיות ע"ד

נופיה - מגרש 19			
מס' גליון	שם גליון	מהדורה	תאריך הפצת מהדורה
A3-1-099	גליון שער	1	22.09.2025
A3-1-100	תכנית קומת מרתף	1	22.09.2025
A3-1-101	תכנית קומת קרקע	1	22.09.2025
A3-1-102	תוכנית קומה א	1	22.09.2025
A3-1-103	תכנית גג	1	22.09.2025
A3-2-200	חזיתות 1	1	22.09.2025
A3-2-201	חזיתות 2	1	22.09.2025
A3-3-100	חתכים	1	22.09.2025
A3-4-100	גליון מדרגות	1	22.09.2025
A3-4-103	פרטים	1	22.09.2025
A3-4-104	פרטי פרגולה	1	22.09.2025
A3-6-1000	רשימת פתחים	1	22.09.2025



מתכננים:


ניהול פרויקט
מהיסוד - בן סולמון
פיקוח
מהיסוד - בן סולמון
קונסטרוקציה
ערן שילר
מיזוג אוויר
אייל ארז מהנדסים ויעצים בע"מ
אינסטלציה
איתן אלמסי
חשמל
איתן בסיס
אלומיניום
בופ
נתי בלוקא
חשמל חכם
חימום תת רצפתי
איטום
צבי טל
אקוסטיקה
מעליות
קרקע וביסוס
דיה הנדסת קרקע וביסוס
רישוי

± 0.00 = +243.50

הערות:
1. תכנית זו יש לקרוא יחד עם תכנית הריטשים.
2. גובה אבסולוטי: ראו תכנית פיתוח.
3. המידות הן בין קירות הבניה ולא כולל פחים.
4. פיתוח השטח סביב הבנוה, כולל, מדרגות, גדרות, שבילים, ריצופים, שטחים פתוחים, חניה וגובה רוא תכנית פיתוח.
5. איטום קירות ורצפות הבנוה כמעט עם הקרקע ובנידוד תחרי לאורך העמודים והקירות של המבנה. כליות או עם סימני גיטון- ראו תכנית קונסטרוקציה.
6. אף ימים יבוצע בכל מישור אופקי הבולם חתוכין.
7. סוף תחרי במסיד- ע"פ מפרט תומקיר, מאושר ע"י פיקוח העיר.

הבצע אחראי לסידות : עליו לבקר ולבדוק את כל המידות בתכנית ובקטע המבנה.
במסגרת של מידות או אי התאמה בתכנית /או בבנוי, עליו להודיע על כך מיד לאדריכל בסדר המשיך בעבודתו.
המבצע יישמש או ויק בתכנית המשיך באשר לביצוע.
המבצע יחזיק באחר, בכל מה, של מידות של תכנית.
אין לקבוע מידות על ידי תחריה בשר מוס.
התכנית הנה רשומה האדריכל ואין לשנות כל שימוש בה או ברעיונות הגלומים בה, אלא באישור בכתב מהאדריכל.
המבצע יחזיק בתכנית.
על המבצע והמבצע לודא התאמה התכנית האדריכלית "לביצוע".
למבנית יחיד, המבנה והתכנית המאושרות ע"י כל גורמים הרשמיים.
התכנית כוללת את כל האחריות והידוע עד ליום תחלתה.

משרד קירות:

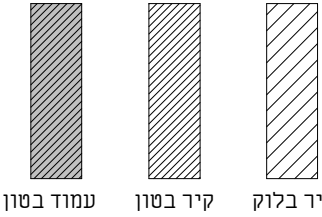

תאריך	תיאור	מהדורה
22.09.2025	מכרז	1

אדריכלות

שם המסין:	CLIENT NAME:
קבוצת רכישה נופיה	
שם הפרויקט:	PROJECT NAME:
נופיה - מגרש 19	
שם הגיליון:	DRAWING NAME:
תוכנית קומה א	
מספר גיליון:	SHEET NUMBER:
A3-1-102	
תחבורה:	EDITION:
SCALE:	קנה מידה:
1 : 50	
STATUS:	סטוס:
למכרז	
שורשם ע"י:	בדוק ע"י:
תאריך:	DATE:
22.09.2025	




נירסן חיינר אדריכלים
מנכ"ל והנדס 2, בית חירות
09-9545642 70
office@nh-arch.com
www.nh-arch.com

זכיות יימור / ע"פ הנחיות ע"ד

הערות:

- יש לעבוד במקביל לתכניות יועצים המאושרות על ידי האדריכל.
- פרטי ספי חלון - עפ"י חוברת אלומיניום של הספק הנבחר ובתיאום מול אדריכל.
- חימום תת רצפתי (במידה ויש במגרש זה) עפ"י פרטי הספק ובתיאום מול אדריכל.
- יש לעבוד במקביל לתכניות עיצוב פנים (במידה ויש מעצב פנים במגרש זה) המאושרות על ידי האדריכל.
- באחריות הקבלן לעדכן את האדריכל על אי התאמה בין התכניות יועצים לאדריכלות.
- כל הדלתות לפי מפרט מצורף.
- כל אלמנטי הבטון יקבלו התייחסות תרמית לפי הנחיות יועץ.
- פרטי איטום,בידוד וניקוז עפ"י תכניות יועצים ובאחריות הקבלן.

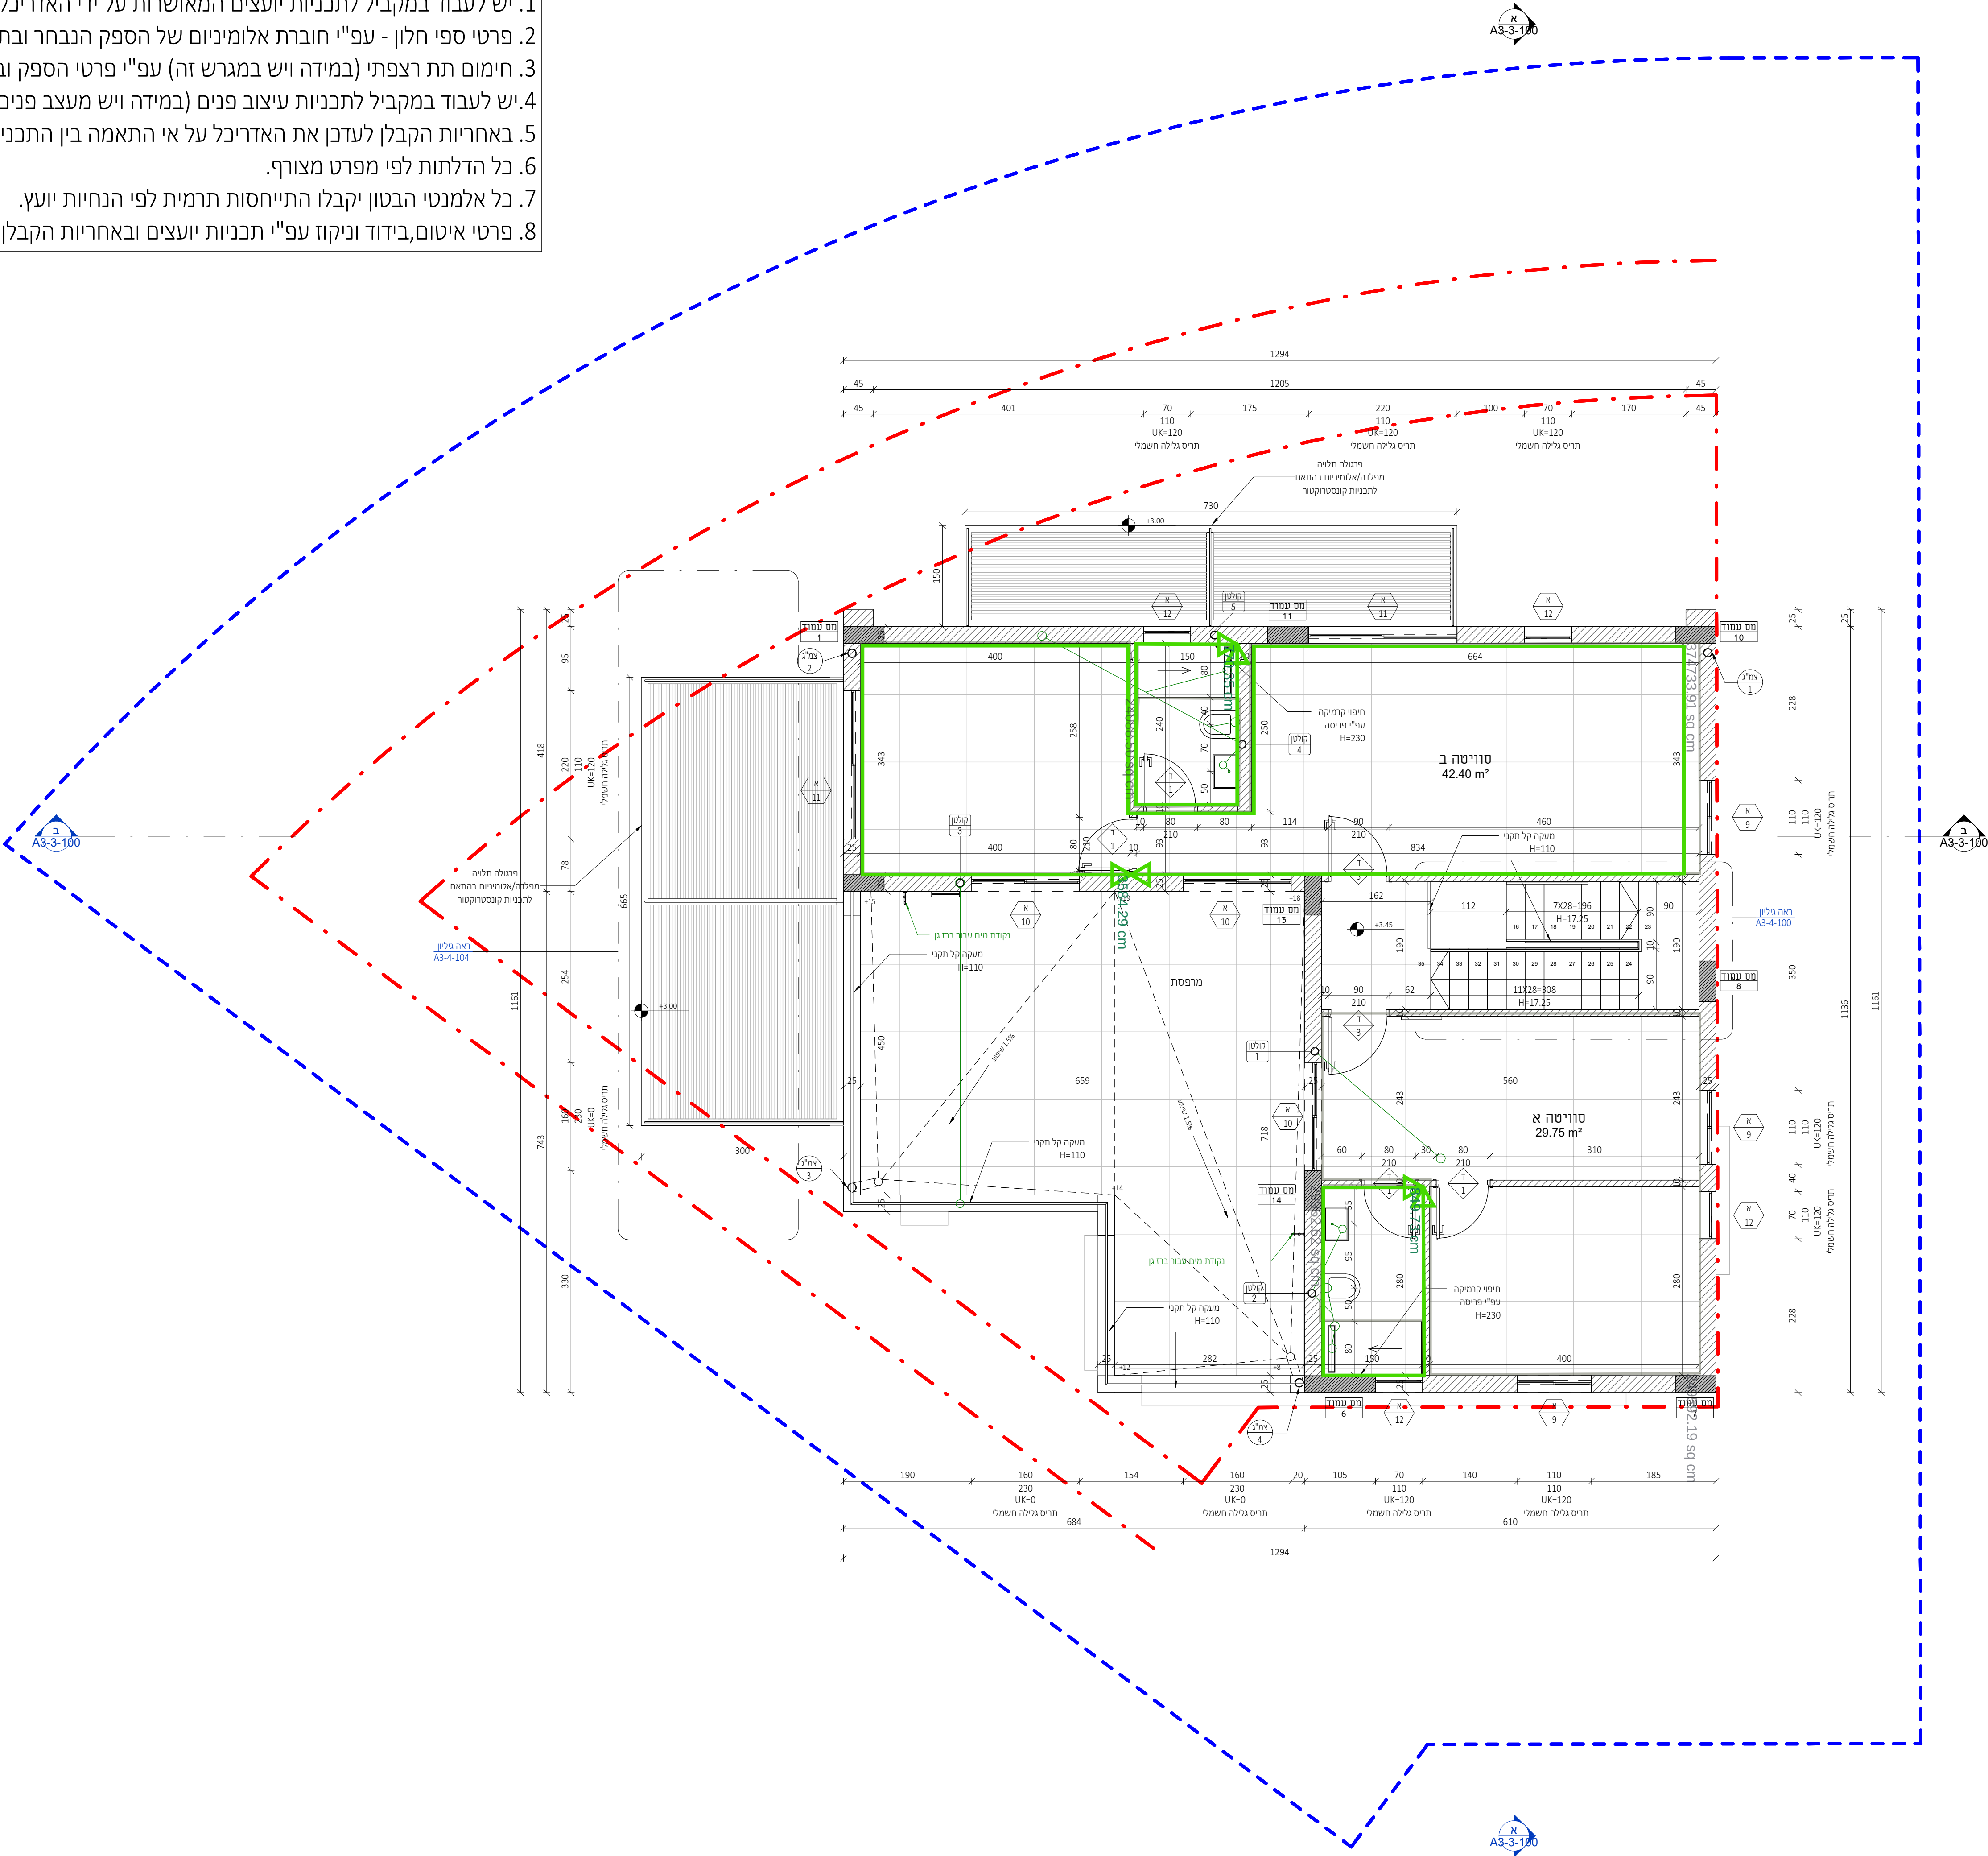

מתכונים:


ניהול פרויקט
מהיסוד - בן סולמון
פיקוח
מהיסוד - בן סולמון
קונסטרוקציה
ערן שילר
מיזוג אוויר
אייל ארז מהנדסים ויועצים בע"מ
אינסטלציה
איתן אלמסי
חשמל
איתן בסיס
אלומיניום
נוף
נתי בלוקא
חשמל חכם
חימום תת רצפתי
איטום
צבי טל
אקוסטיקה
מעליות
קרקע וביסוס
דיה הנדסת קרקע וביסוס
רישוי

$\pm 0.00 = +243.50$

הערות:
 1. תכנית זו יש לקרוא יחד עם תכניות הוועצים.
 2. גובה אבסולוטי – ראו תכנית פיתוח.
 3. המידות הן ב' כ"ר פירות תפוחים (ראו כלל ס' 10).
 4. פיתוח השטח בשטח חניה, קולנוע, כולל, מדרגות, גדרות, שביליים, רציפים,
 5. פסיפגים וכו'.
 6. ראו תכנית יעוץ-ראו תכנית פיתוח.
 7. אסוס. תכנית ורצפות התקנה במגע עם הקרקע ובידוד תרמי לאורך המעברים.
 8. הקורות ועל התקורות – קליטור או עם מיני (יגורן) – ראו תכנית קונסטרוקציה.
 9. א' 40 ס"מ ביצוע כלל מישור אופקי חתכי המבנה.
 10. ראו תרמי ממשל – ראו פרט מורחב, חומרים, חומרים, ע"י פיקוד מורחב.

[illegible]

מקרא קירות:

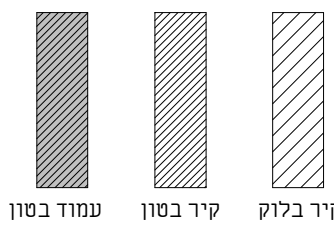[illegible]

אדריכלות

CLIENT NAME: _____ שם המזמין:

קבוצת רכישה נופיה


PROJECT NAME: _____: ס הפרויקט:

נופיה - מגרש 19

DRAWING NAME: ס הגליון:

SHEET NUMBER: 19

A3-1-103

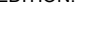SCALE:	קנה מידה:	EDITION:	חזרות:
1 : 50			
STATUS:	סטטוס		
למכר			
	נבדק ע"י:		רדסט ע"י:
DATE:	22.09.2025		מ"ר:




NeumanHaynerArchitects

וימן חיינר אדריכלים
מורד ההדרים 2, בית חירות
טל 09-9545842

זכויות ייצור / ע"פ הנחיות עו"ד

פרטי איטום, בידוד וניקוז הגג עפ"י תכניות יועצים ובאחריות הקבלן

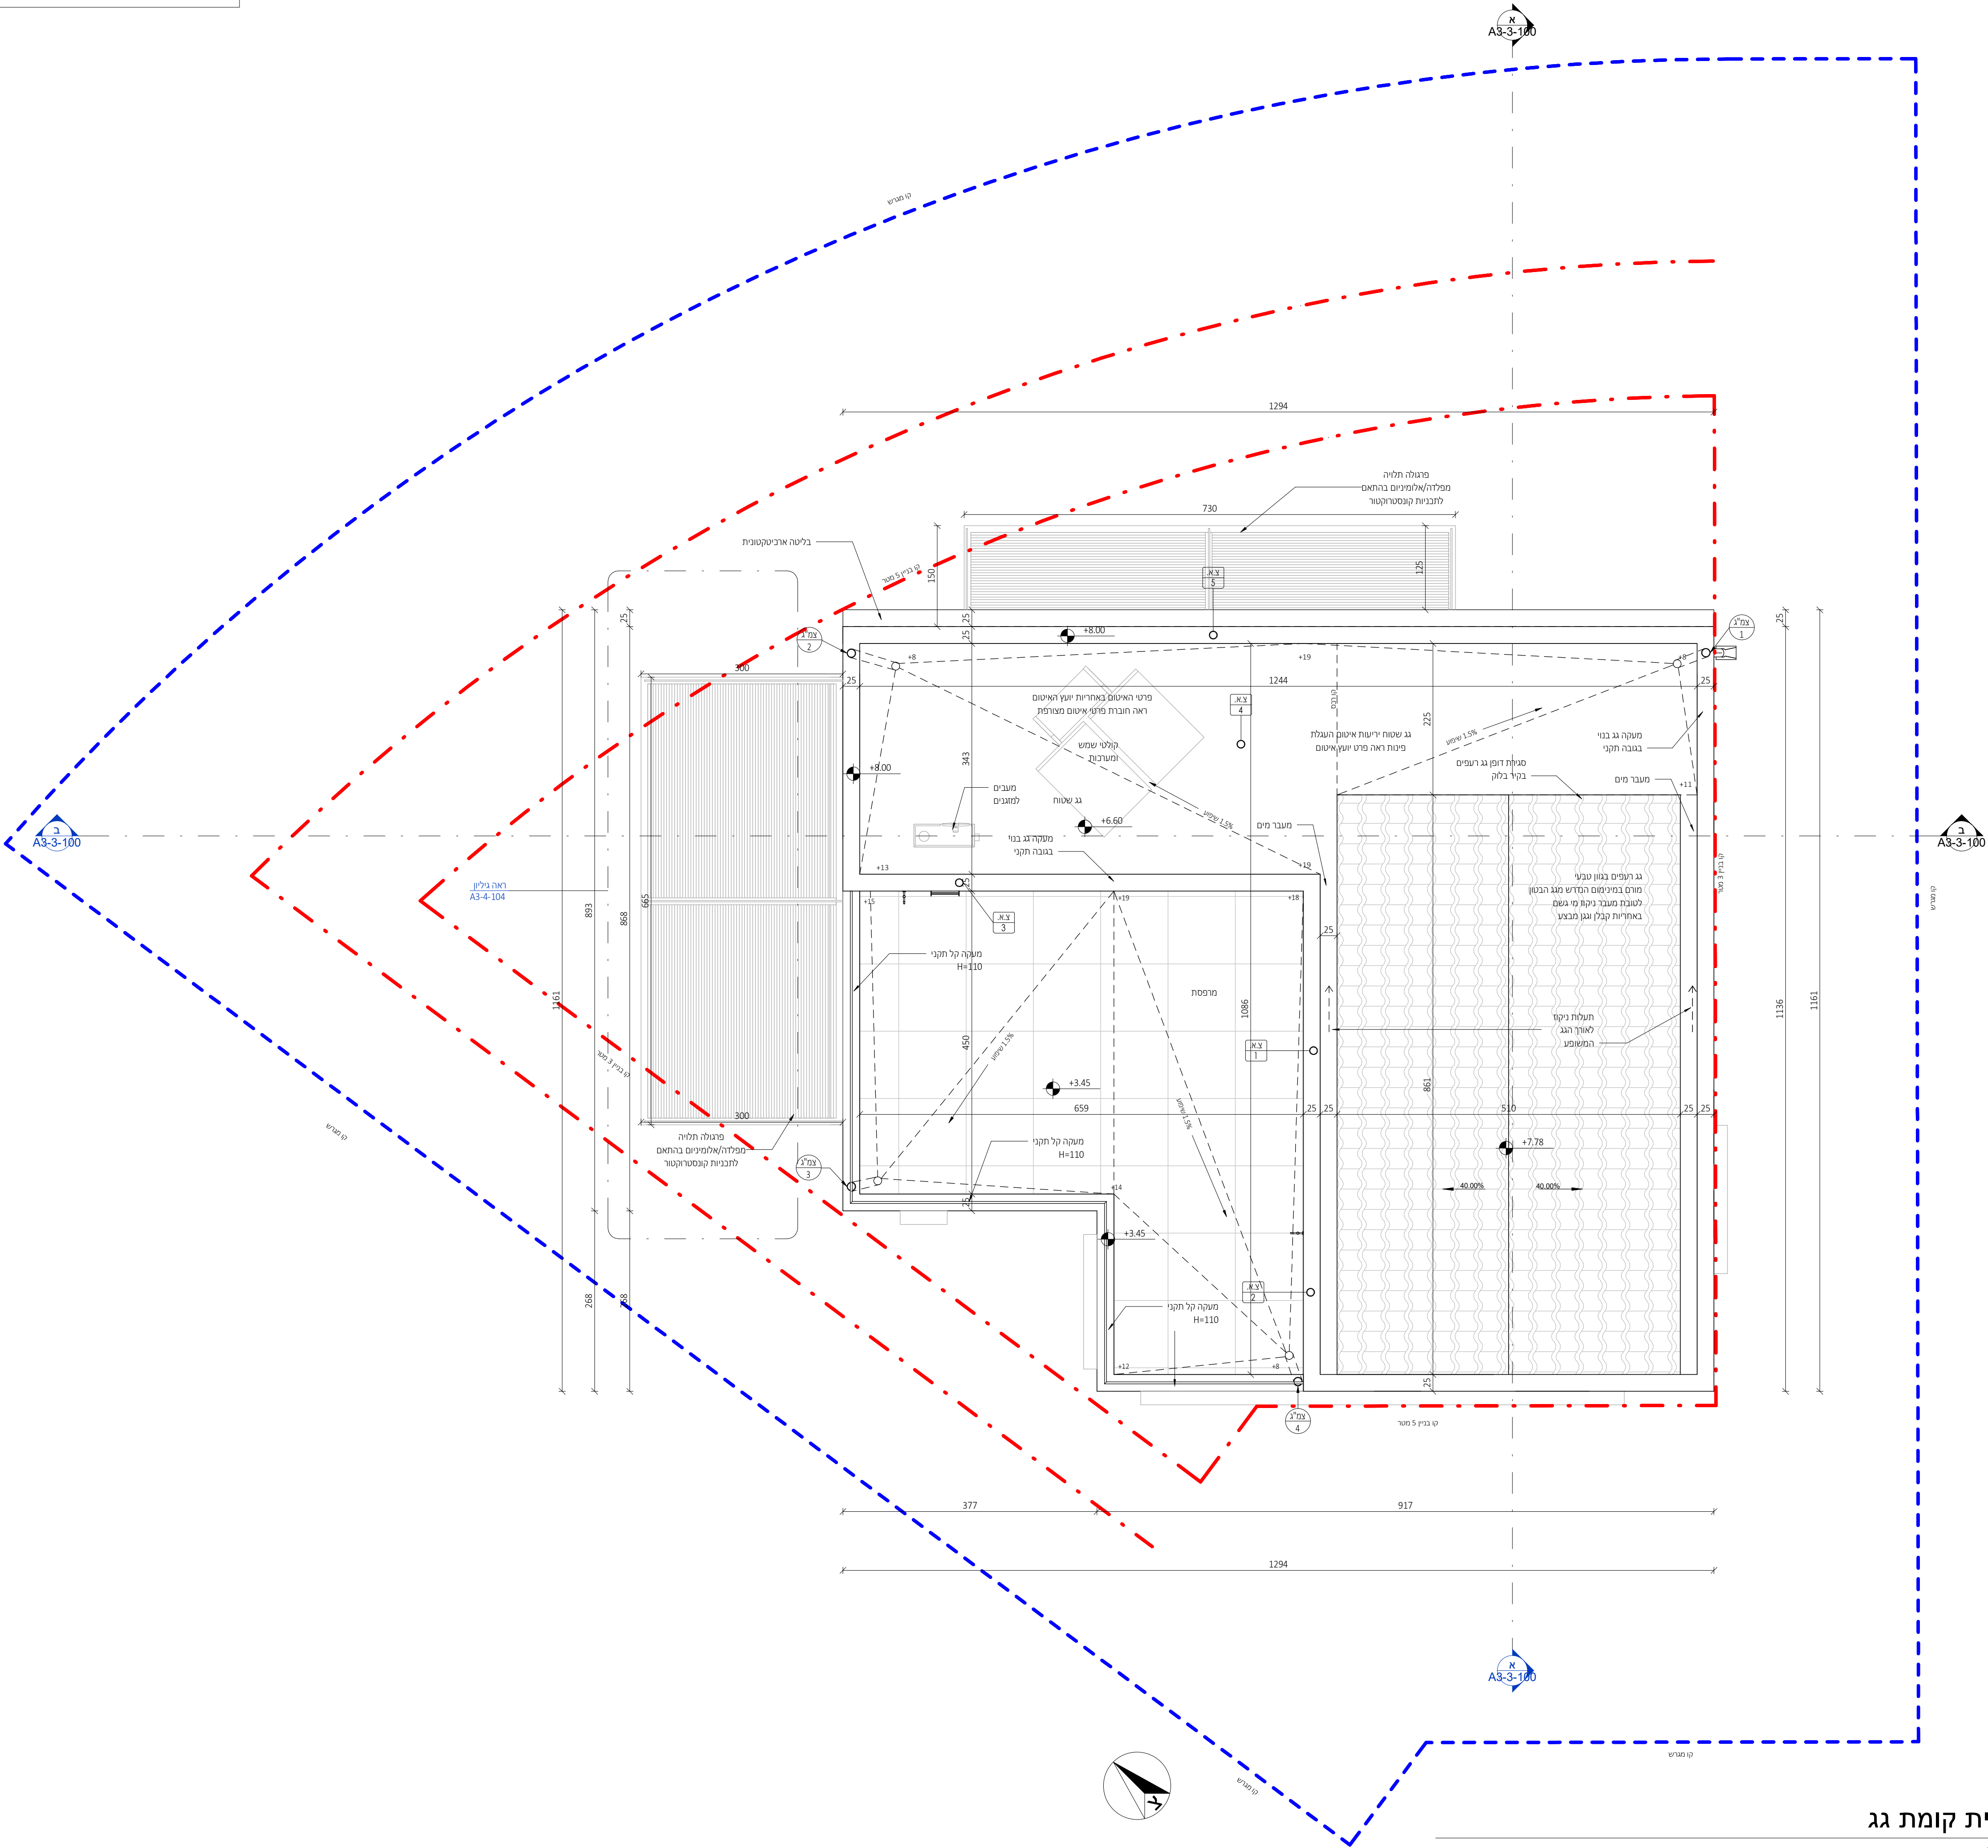

תוכנית קומת גג

מתכונים:


ניהול פרויקט
מהיסוד - בן סולמון
פיקוח
מהיסוד - בן סולמון
קונסטרוקציה
ערן שילר
מיוזג אוויר
איל ארז מהנדסים ויועצים בע"מ
אינסטלציה
איתן אלמסי
חשמל
איתן בסיס
אלומיניום
נוף
נתי בלוקא
חשמל חכם
חימום תת רצפתי
איטום
צבי טל
אקוסטיקה
מעליות
קרקע וביסוס
דיה הנדסת קרקע וביסוס
רישוי

תשובה	אחוז תשובות
כן	~75%
לא	~25%

הערות:

- במסגרת הסקר נשאלו גם מנהלים ובעלי תפקידים אחרים על הצורך בהעסקת מורים נוספים.
- התוצאות של סקרי הבעיות והצרכים שנעשו במסגרת הסקר יועברו לרשות החינוך המקומית לצורך קבלת החלטות.

קרא עירות:

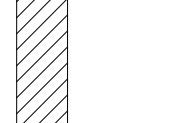


אדריכלות

הפריט:		קבוצת רכישה נופיה	
הפרויקט:		נופיה - מגרש 19	
הגליון:		חזיתות 1	
הפרוטוקול:		A3-2-200	
מספר חזית:	מספר חזית:	מספר חזית:	מספר חזית:
1 : 50	1 : 50	1 : 50	1 : 50
למכור	למכור	למכור	למכור
נכון ע"י:	נכון ע"י:	נכון ע"י:	נכון ע"י:
22.09.2025	22.09.2025	22.09.2025	22.09.2025


NeumanHaynerArchitects

office@nh-arch.com

זכויות ייצור / ע"פ הנחיות עו"ד

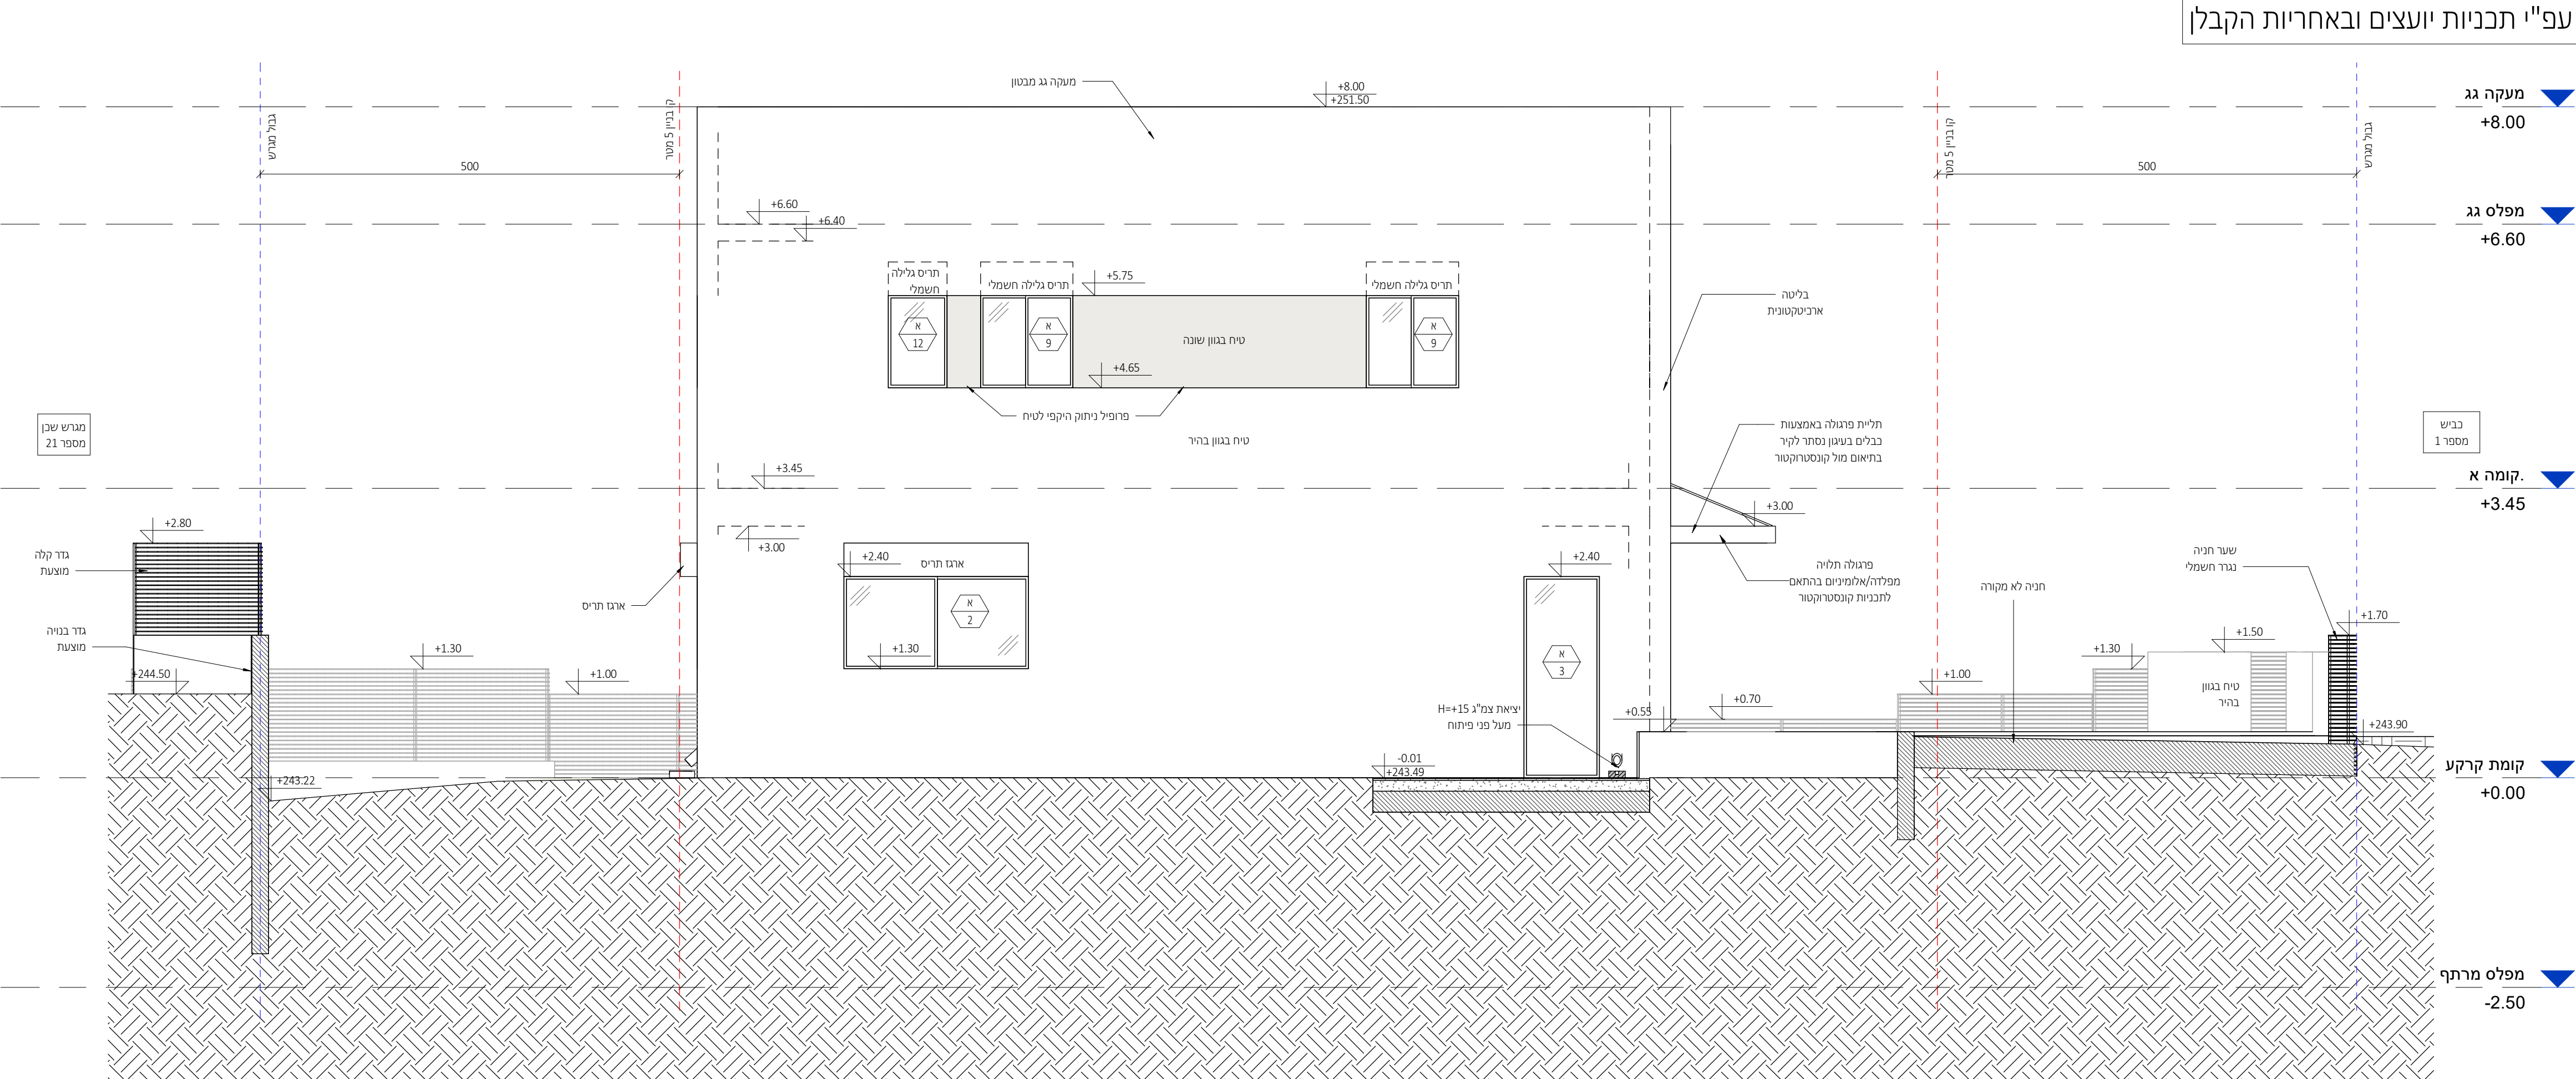

פיתוח נוף עפ"י תוכניות
יועץ נוף ראה פירוט בנפרד

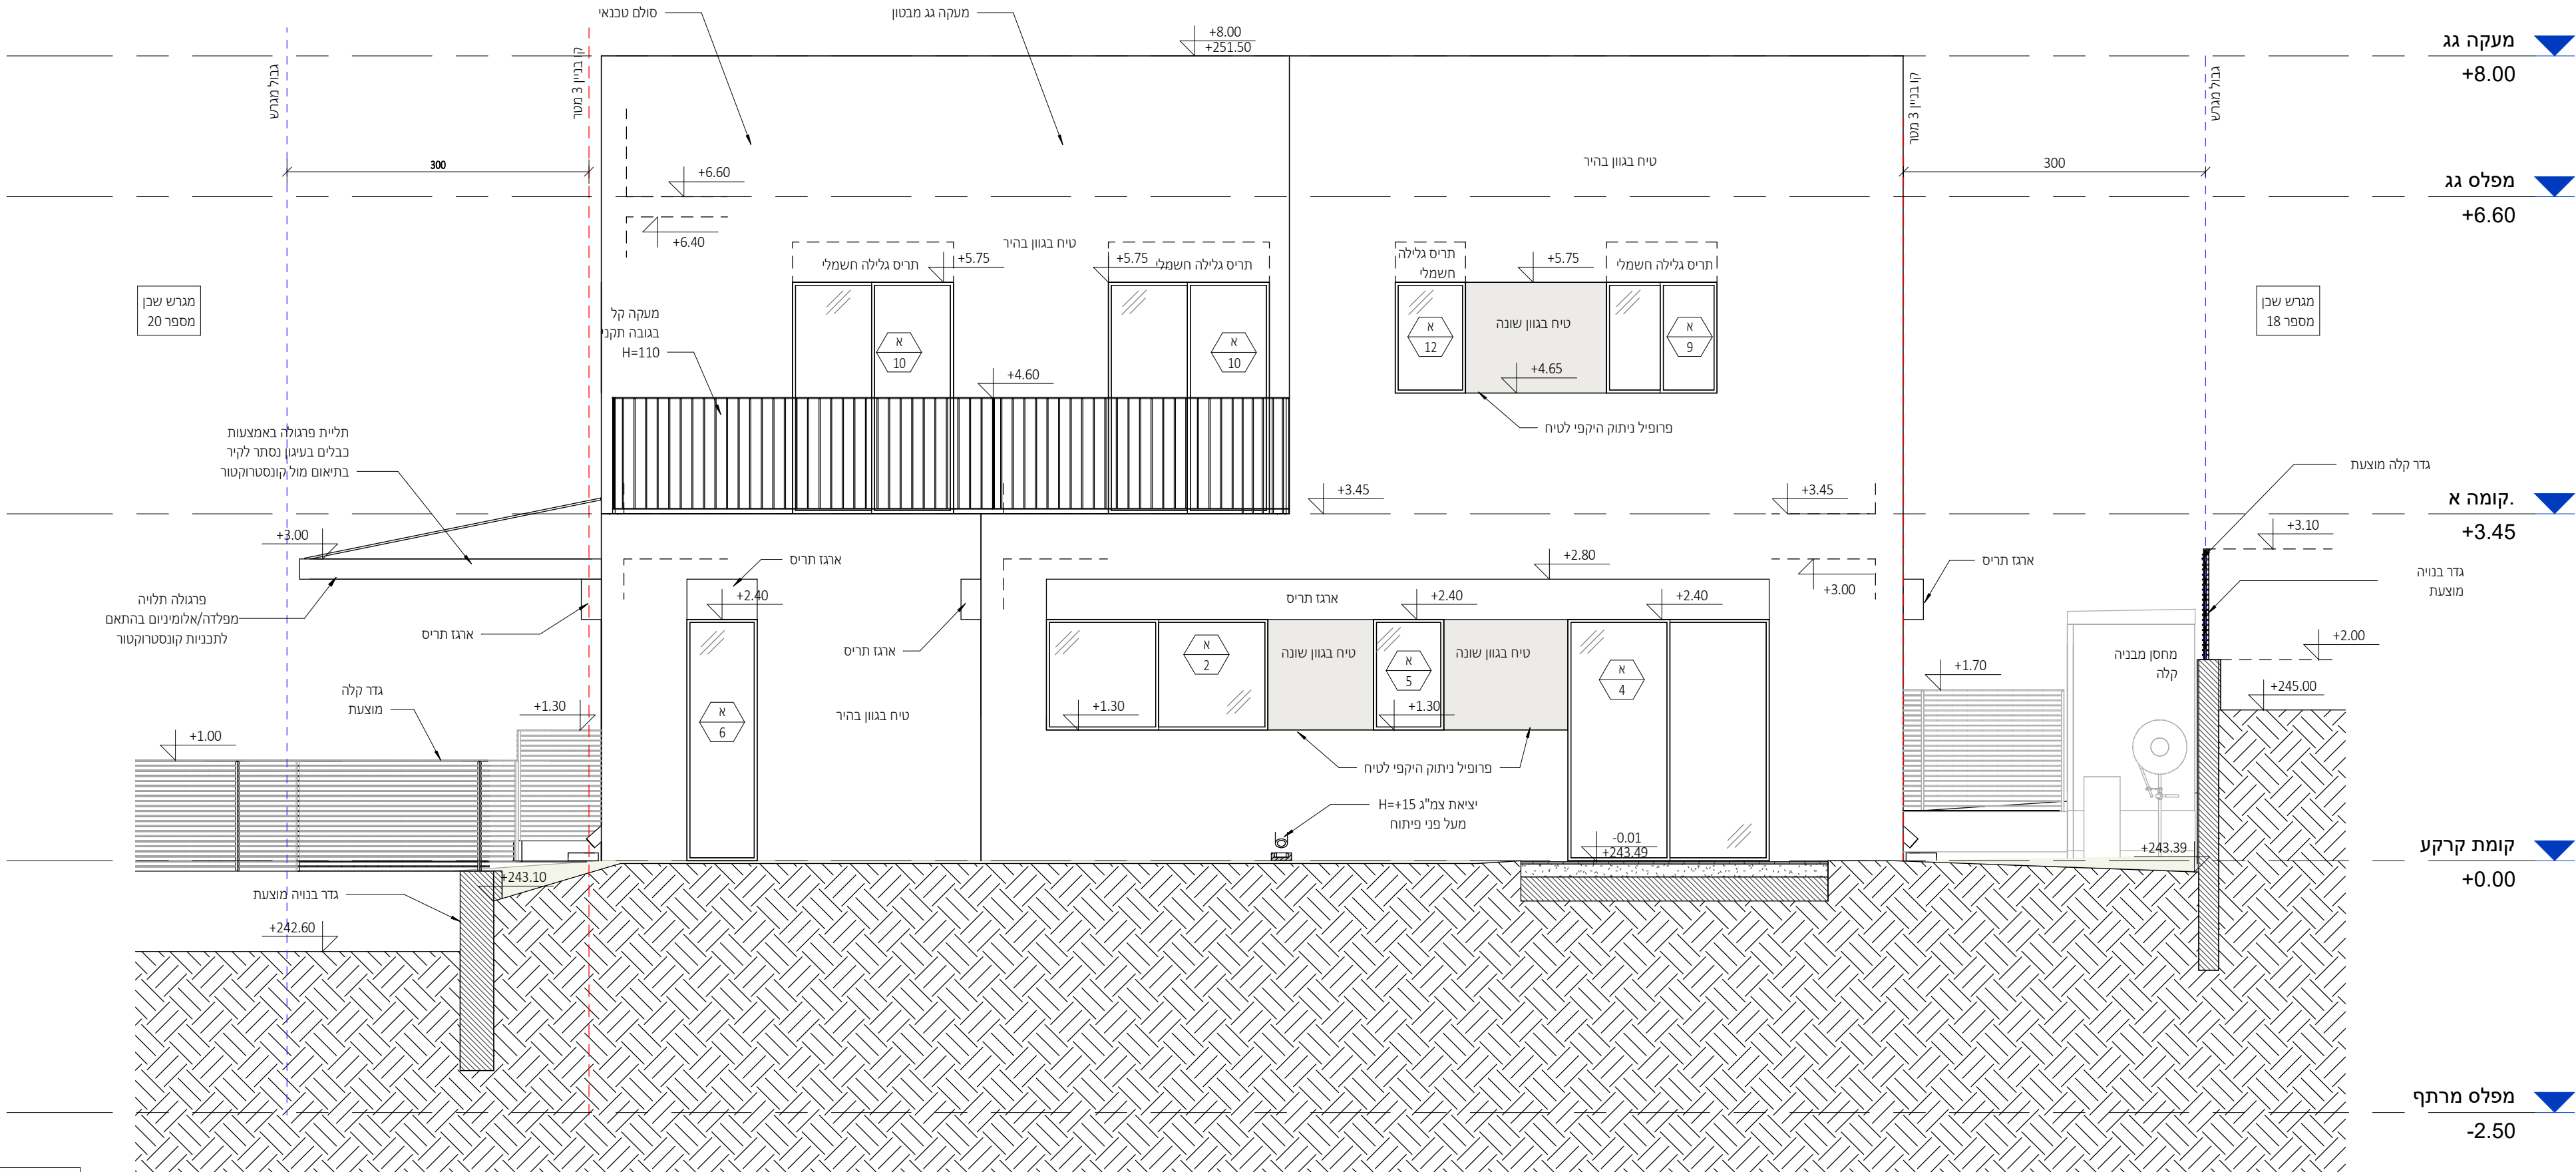


פיתוח נוף עפ"י תוכניות
יועץ נוף ראה פירוט בנפרד

חזית דרום מערבית



1 : 50

פרטי איטום, בידוד וניקוז עפ"י תכניות יועצים ובאחריות הקבלן

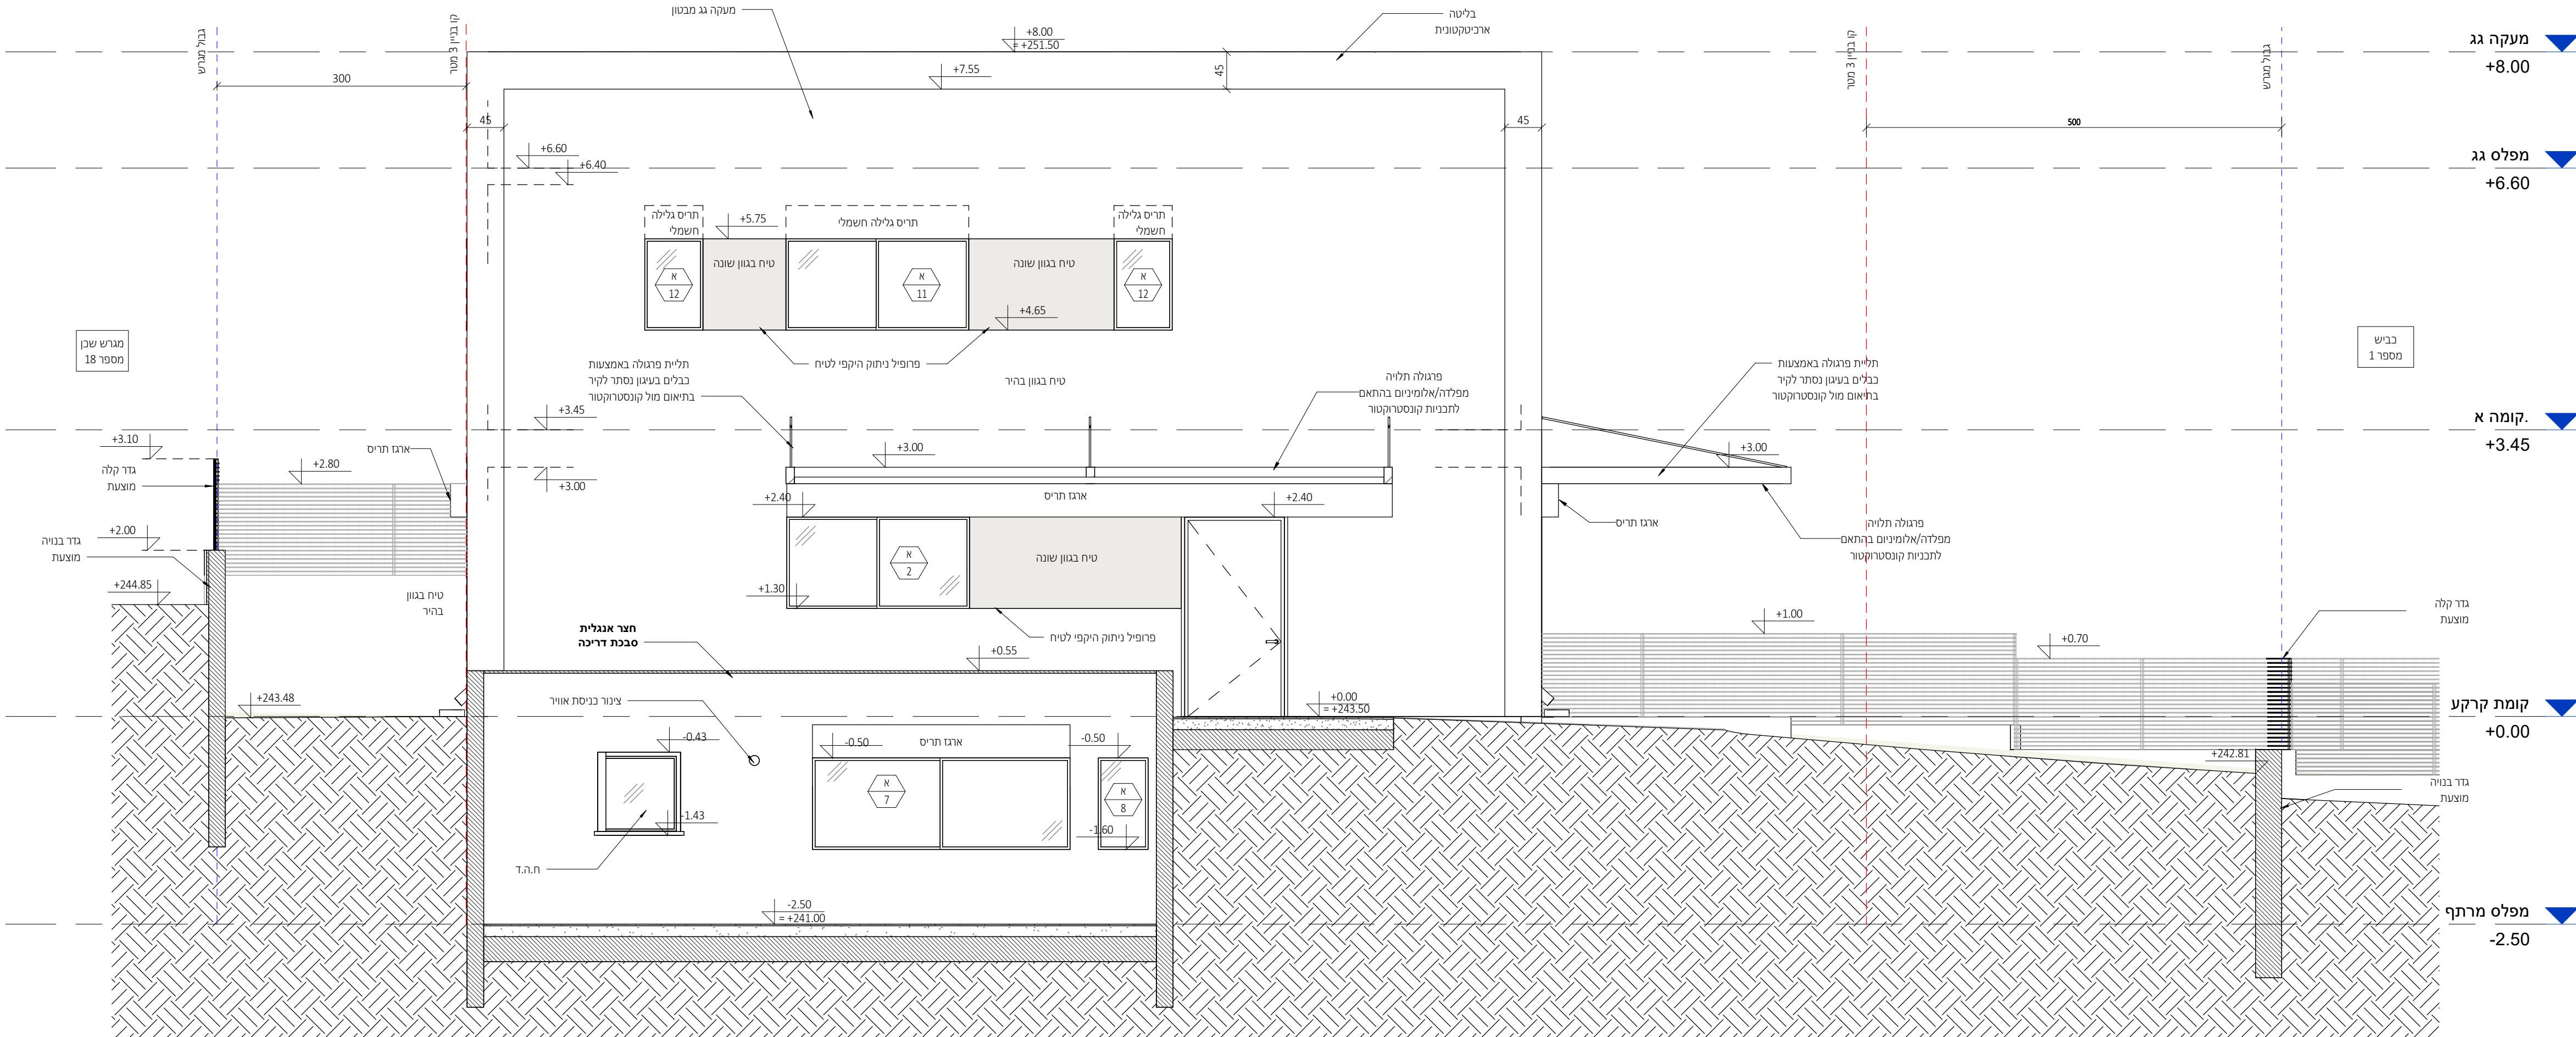

חזית צפון מזרחית

1 : 50

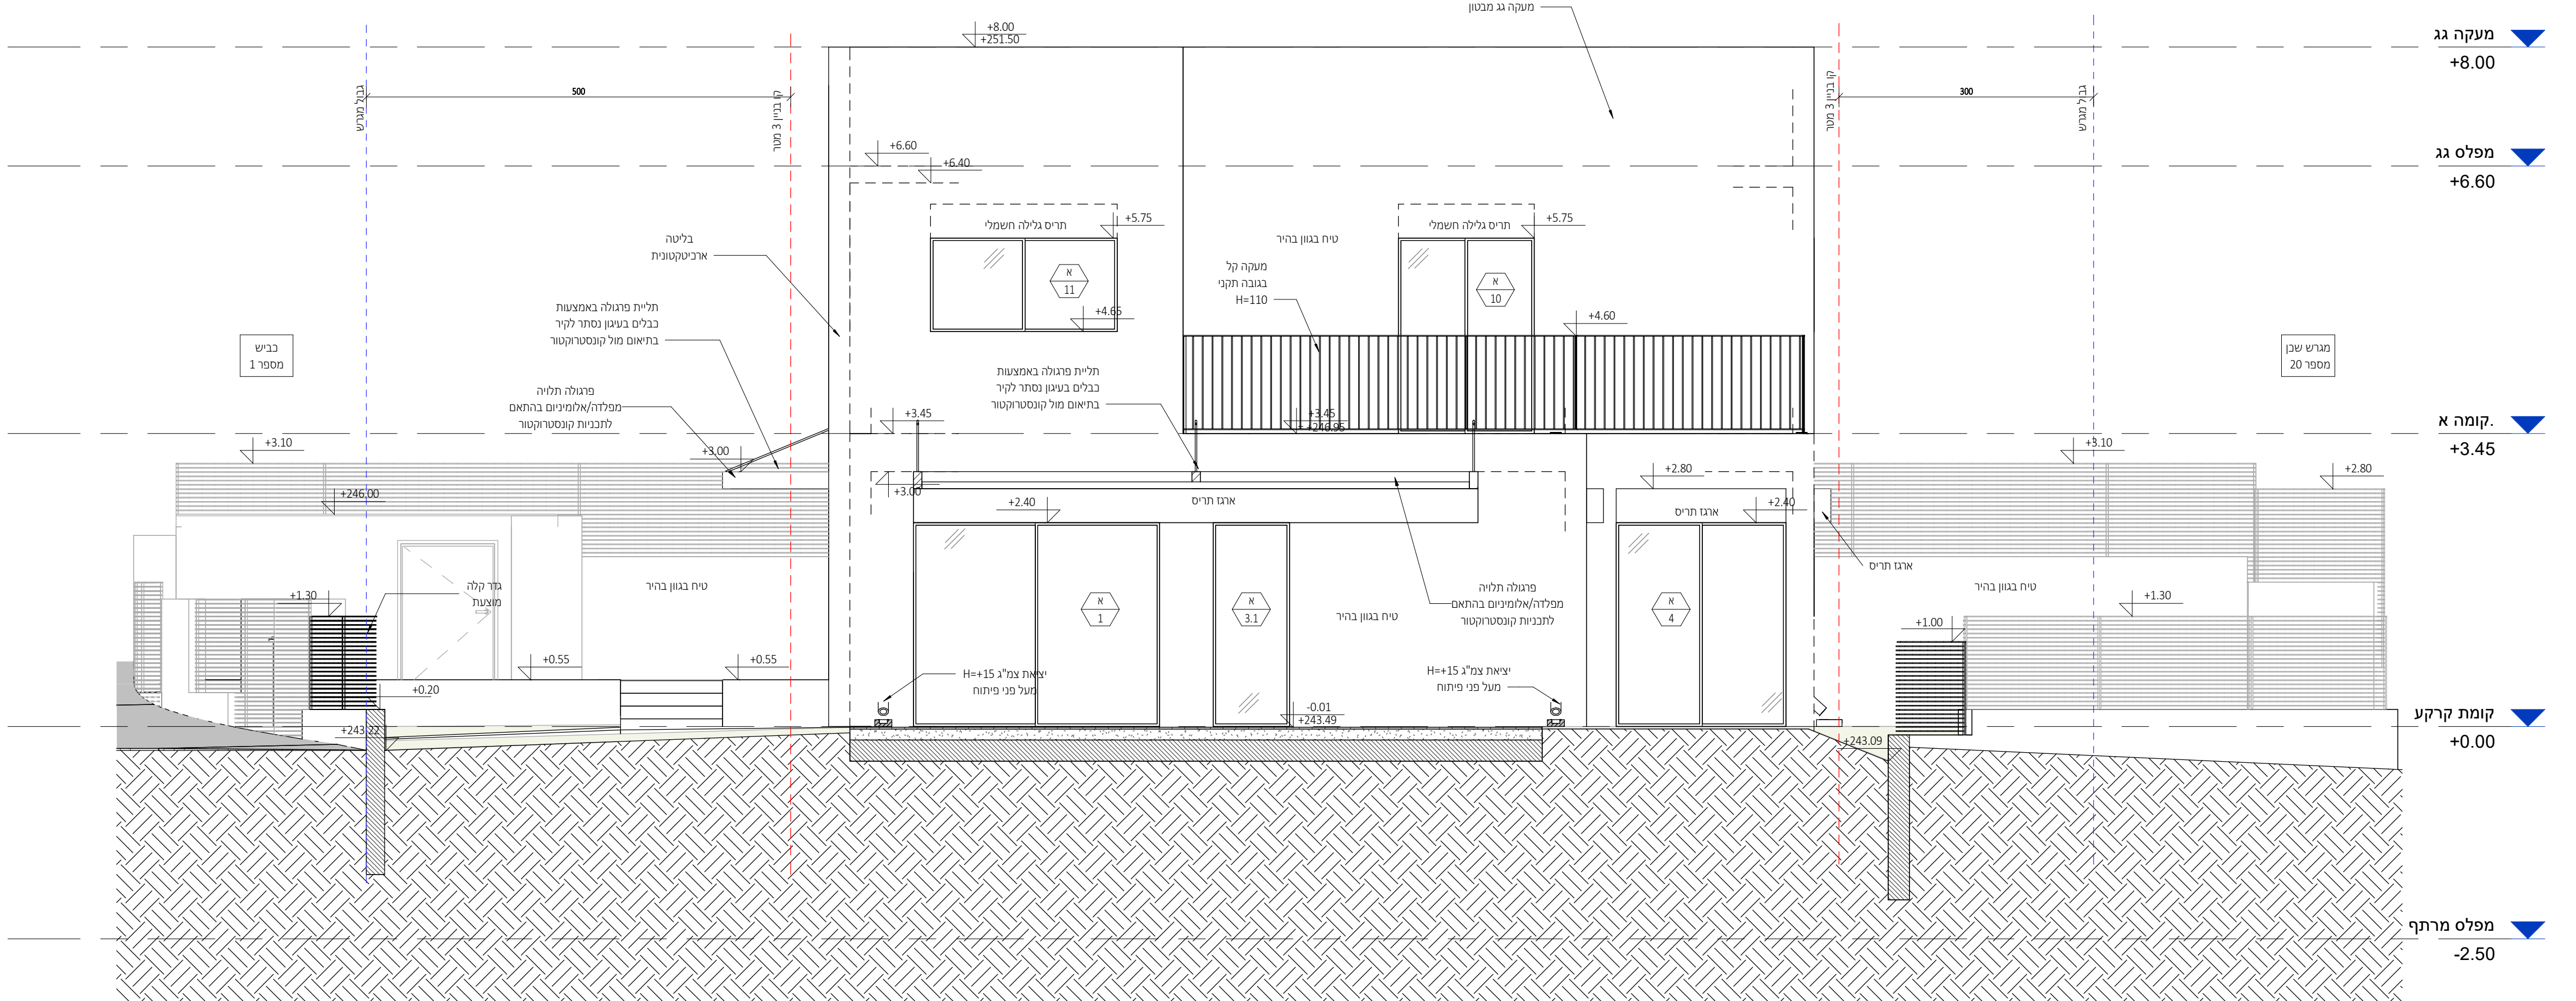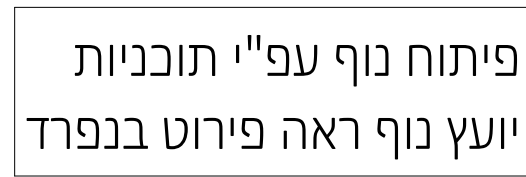

חזית צפון מערבית

1 : 50

מתכונים:

ניהול פרויקט
מהיסוד - בן סולמון
פיקוח
מהיסוד - בן סולמון
קונסטרוקציה
ערן שילר
מיוזג אוויר
איל ארז מהנדסים ויועצים בע"מ
אינסטלציה
איתן אלמסי
חשמל
איתן בסיס
אלומיניום
נוף
נתי בלוקא
חשמל חכם
חימום תת רצפתי
איטום
צבי טל
אקוסטיקה
מעליות
קרקע וביסוס
דיה הנדסת קרקע וביסוס
רישוי

[illegible][illegible]

אדריכלות	
CLIENT NAME:	המסמך
קבוצת רכישה נופיה	
PROJECT NAME:	הפרויקט
נופיה - מגרש 19	
DRAWING NAME:	התכנון
חזיתות 2	
SHEET NUMBER:	פר גליון
A3-2-201	
CALL:	ענה מידור: EDITION:
1 : 50	
TATUS:	סטטוס
למכר	
	1
	סטטוס ע"י:
DATE:	22.09.2025
	יורד

ניהול פרויקט
מהיסוד - בן סולומון
פיקוח
מהיסוד - בן סולומון
קונסטרוקציה
ערן שילר
מיזוג אוויר
אייל ארז מהנדסים ויועצים בע"מ
אינסטלציה
איתן אלמסי
חשמל
איתן בסיס
אלומיניום
בופ
נתי בלוקא
חשמל חכם
חימום תת רצפתי
איטום
צבי טל
אקוסטיקה
מעלות
קרקע וביסוס
דיה הנדסת קרקע וביסוס
רישוי

תשובה	אנשים	מנהלים
אף פעם לא	0.00%	0.00%
לרוב לא	0.00%	0.00%
לרוב כן	0.00%	0.00%
אף פעם כן	0.00%	0.00%

± 0.00 = 2.435.0

הערות:
 הבחין כי קיבלו דוח עם תביעות העוסקים
 במוסדות: ראו תביעות נרחבות
 הודות בהן קיבלו תשובות: כן, לא, חלקית, לא יודע, וכו'.
 שפירושה: סביר להניח שהתשובות הללו הן
 תוצאה של תגובה או תביעות נרחבות
 וקשורות לתהליך התקשורת, ולא של
 חיס חסר: כפי שחשבו אנשי החברה
 חסר: חסר: כפי שחשבו אנשי החברה
 חסר: חסר: כפי שחשבו אנשי החברה

קטגוריית גיל	מספר אנשים
עמוד בסון	8
קיר בסון	6
קיר בלוק	4


PROJECT NAME:		הפרויקט:	
DRAWING NAME:		שם התכנית:	
SHEET NUMBER:		מספר העמוד:	
SCALE:		קנה מידה:	
STATUS:		סטוס	
DATE:		תאריך:	

קבוצת רכישה נופיה	
נופיה - מגרש 19	
חתכים	
A3-3-100	
1:50	
למכר	
בנדק ע"י:	
22.09.2025	דודס ע"י:


NeumanHaynerArchitects

יומן חיינר אדריכלים
משרד האדריכלים 2, בית חירות
09-9545842

זכויות ייצור / ע"פ הנחיות עו"ד

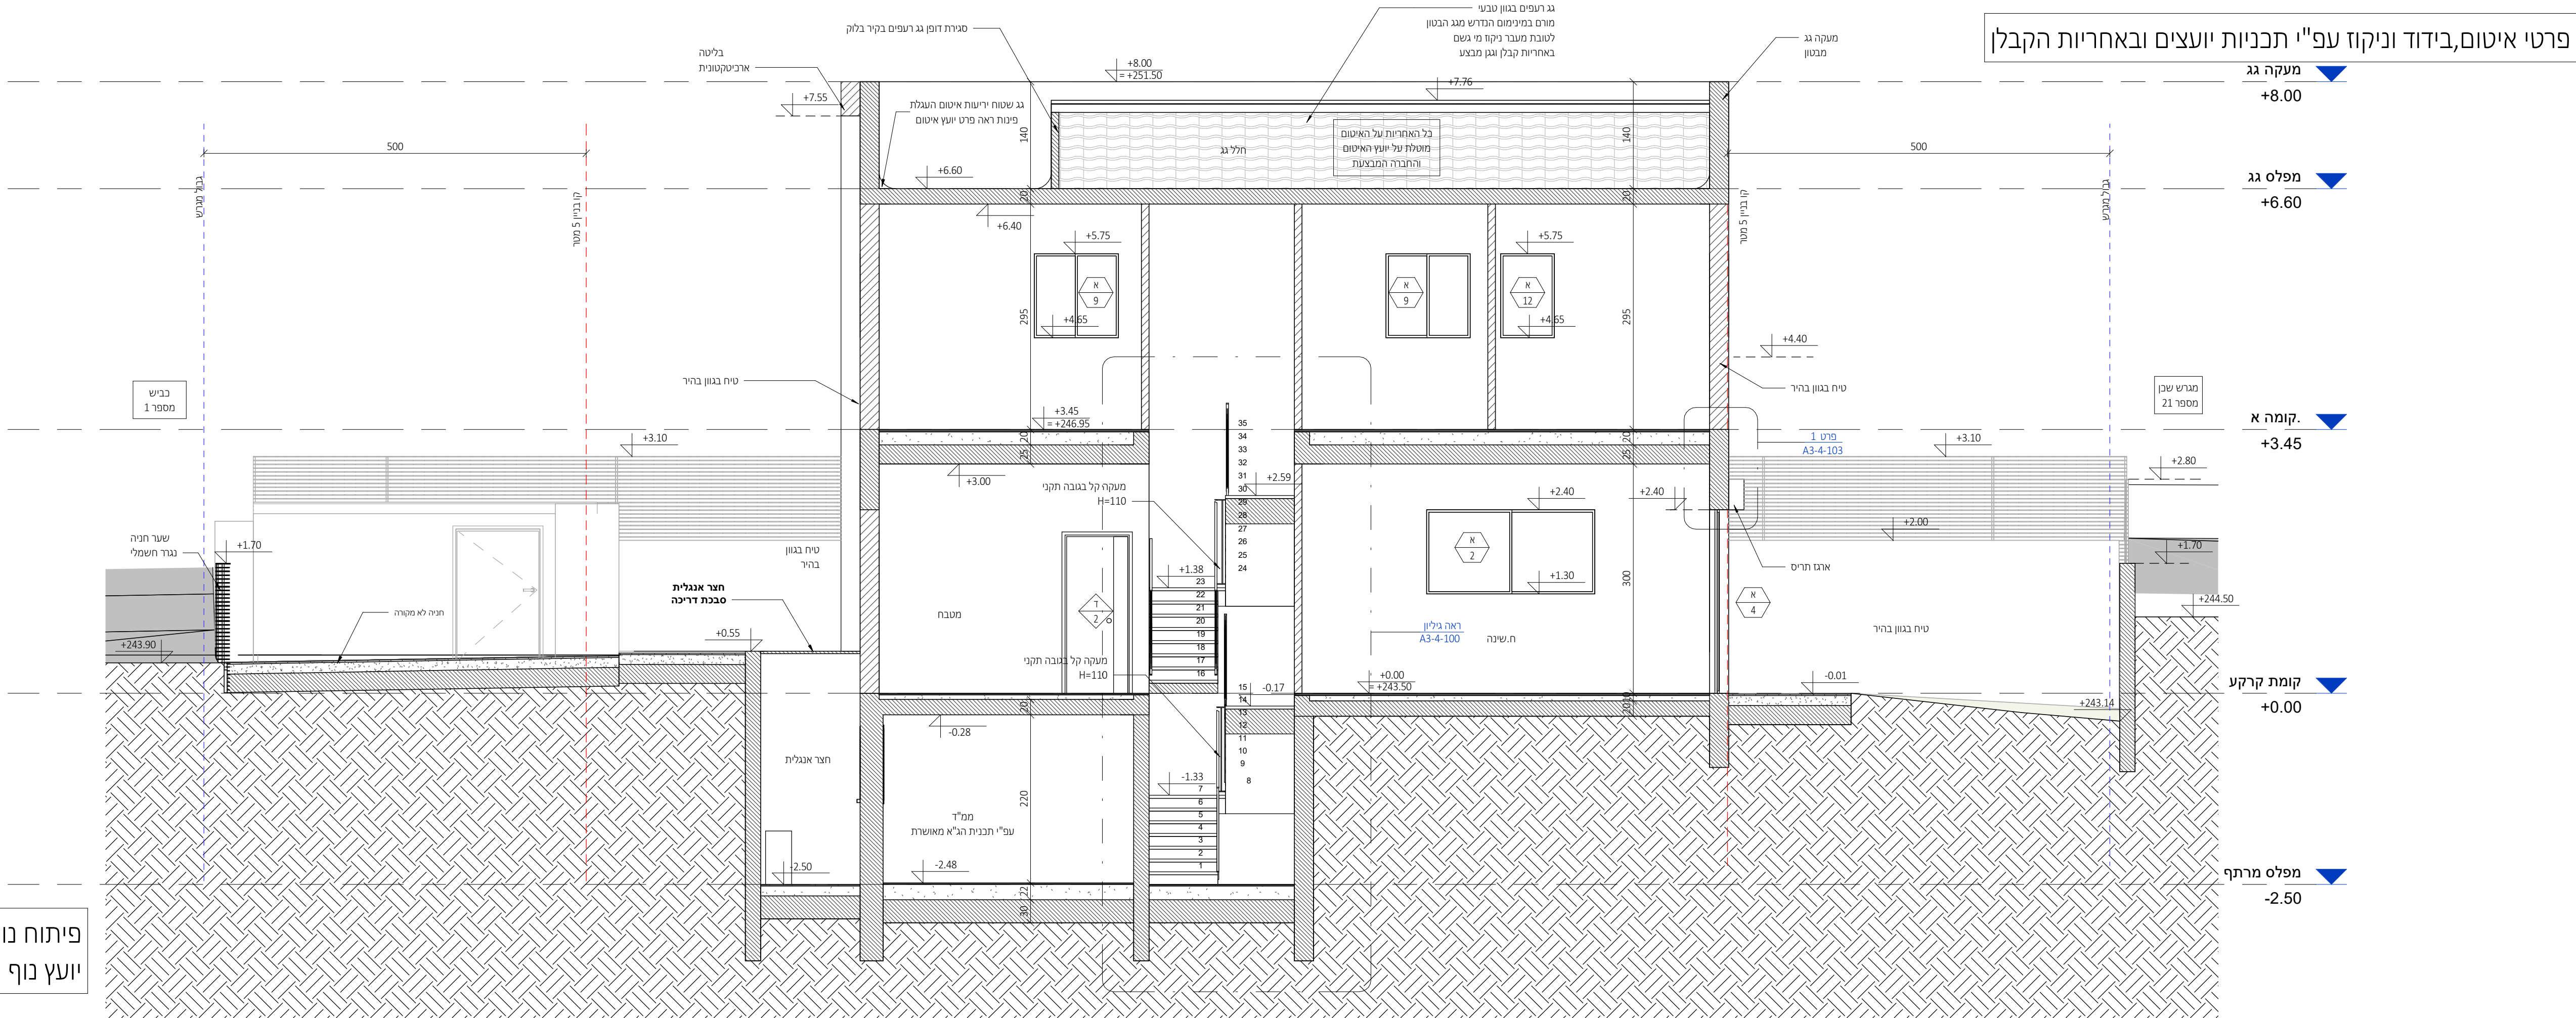

1 : 50

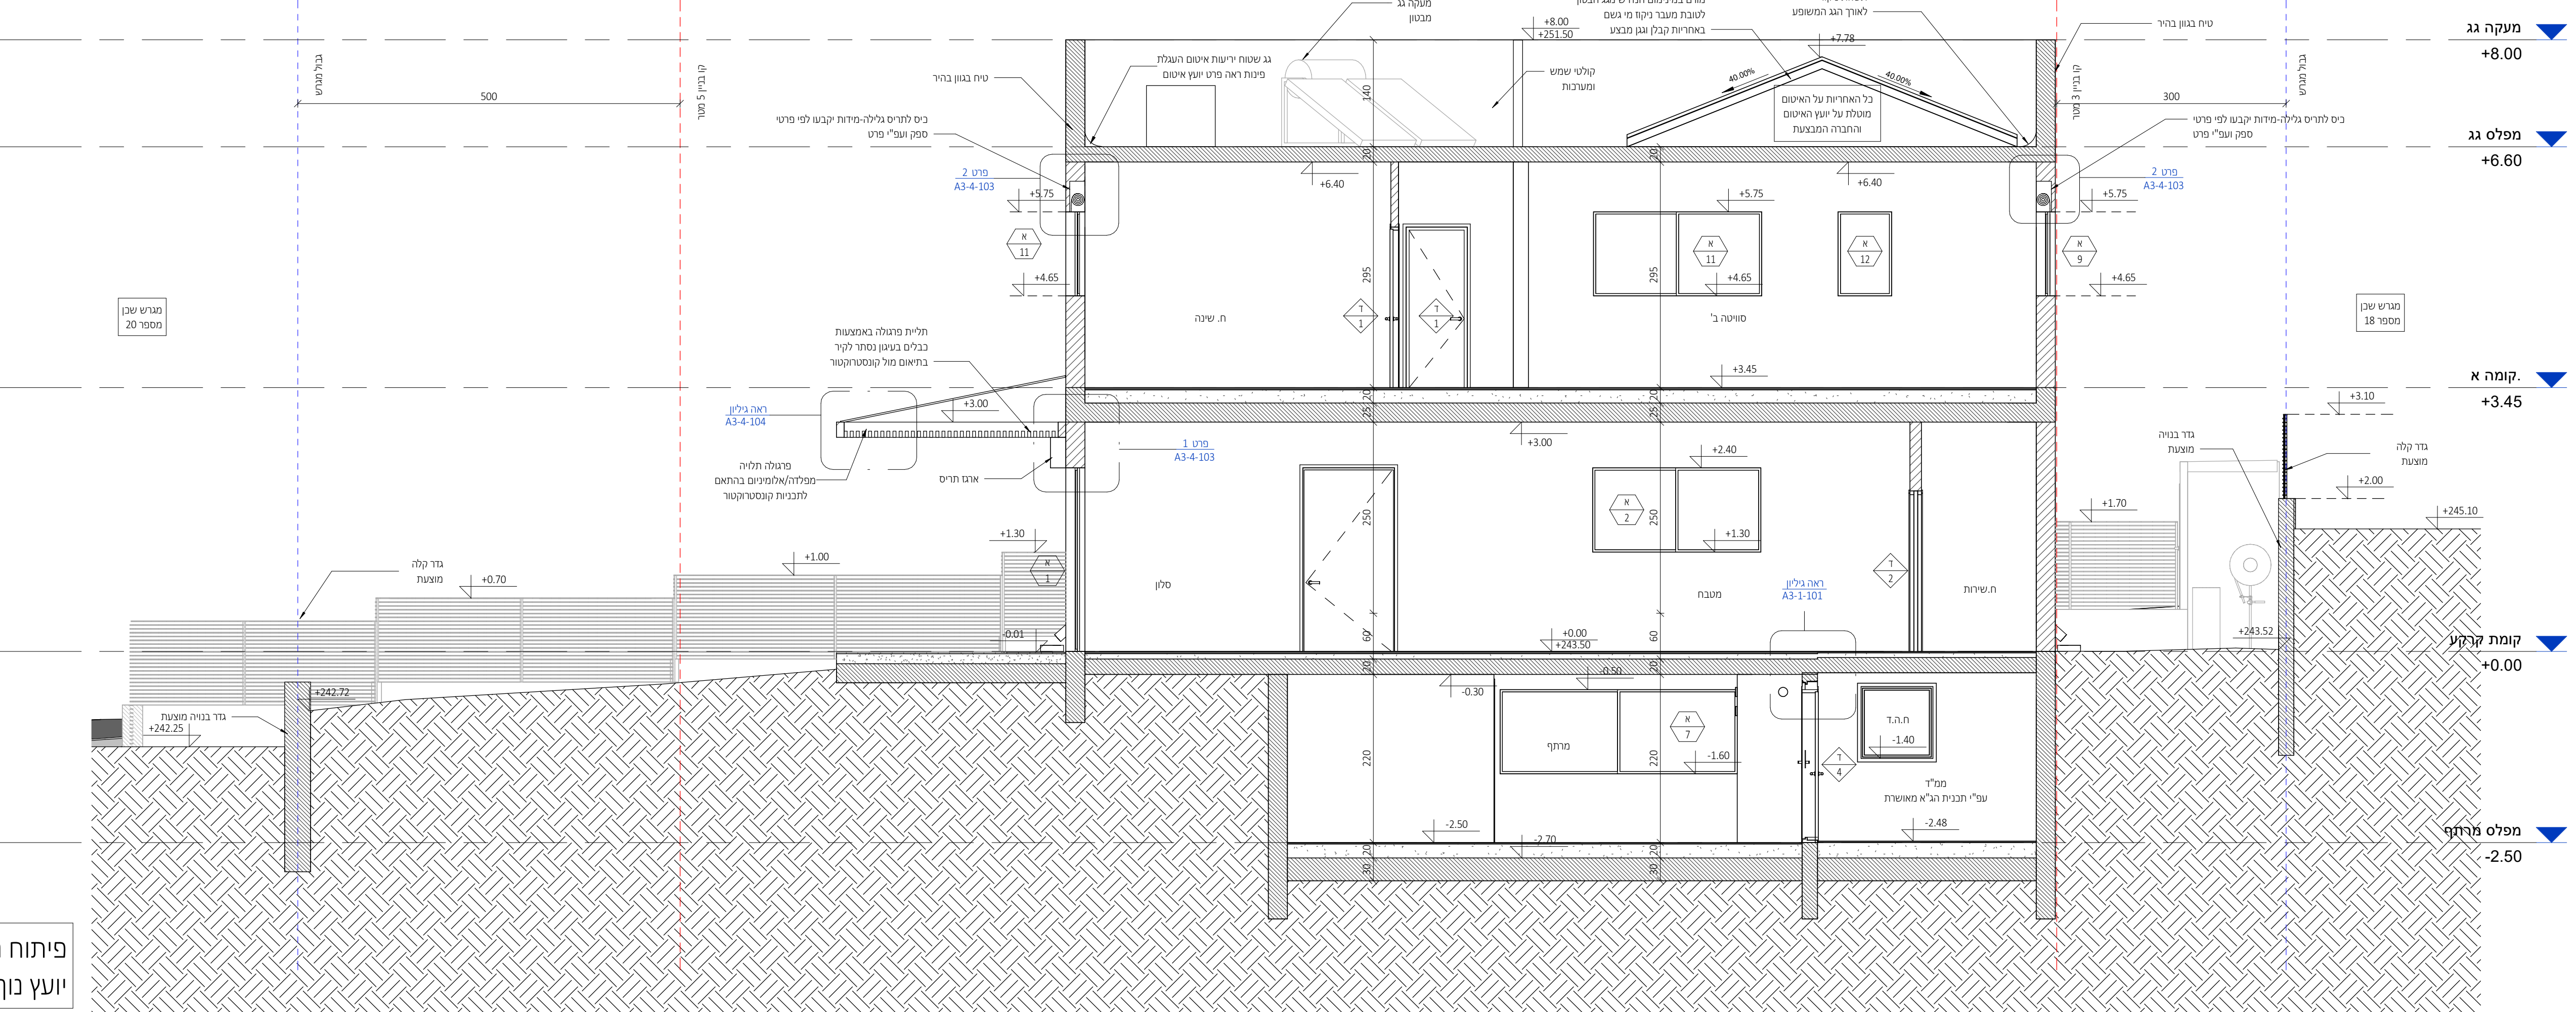

1 : 50

ניהול פרויקט
מהיסוד - בן סולומון
פיקוח
מהיסוד - בן סולומון
קונסטרוקציה
ערן שילר
מזוג אוויר
אייל ארז מהנדסים ויועצים בע"מ
אינסטלציה
איתן אלמסי
חשמל
איתן בסיס
אלומיניום
בנף
נתי בלוקא
חשמל חכם
חימום תת רצפתי
איטום
צבי טל
אקוסטיקה
מעליות
קרקע וביסוס
דיה הנדסת קרקע וביסוס
רישוי

הערות:
 תבנית זו יש לקרוא יחד עם תבנית ההוצעים.
 גובה אבסולוטי – ראו תבנית פיתוח.
 המידות הן בין תבניות (לא כולל סימ).
 פיתוח – שטח סביב המנהרה, כולל, מדורות, שילשים, ריצופים,
 ויטות חשמל כבדים, תהיה ויגורן-ראו תבנית פיתוח.
 איסוס – ראו תרופת המנהרה במגע עם הקרקע בידוד תמימי לאורך העמודים
 וקטרו ושל התקרת- תבנית זו יש פילי (ניגון). ראו תבנית הסמנטיקה
 אף כי ביצוע כלל תרופת אופעי הובילס תחבין.
 סימ תרמי מנהרי – יציפ ספרוס תרופת, מאושר יציפ פיקוד העורפר.

[illegible]

עמוד בטון קיר בטון קיר בלוק

[illegible]

CLIENT NAME: _____: המזמין:

PROJECT NAME: הפרויקט:

DRAWING NAME: תגליון:

SHEET NUMBER: 79 גליון:

SCALE: קנה מידה: EDITION: דורה: Δ

למחרת


דמחמ ע"י:	ובדק ע"י:

DATE: 22.09.2025 י"ד:


NeumanHaynerArchitects

ימן חיינר אדריכלים

09-9545842

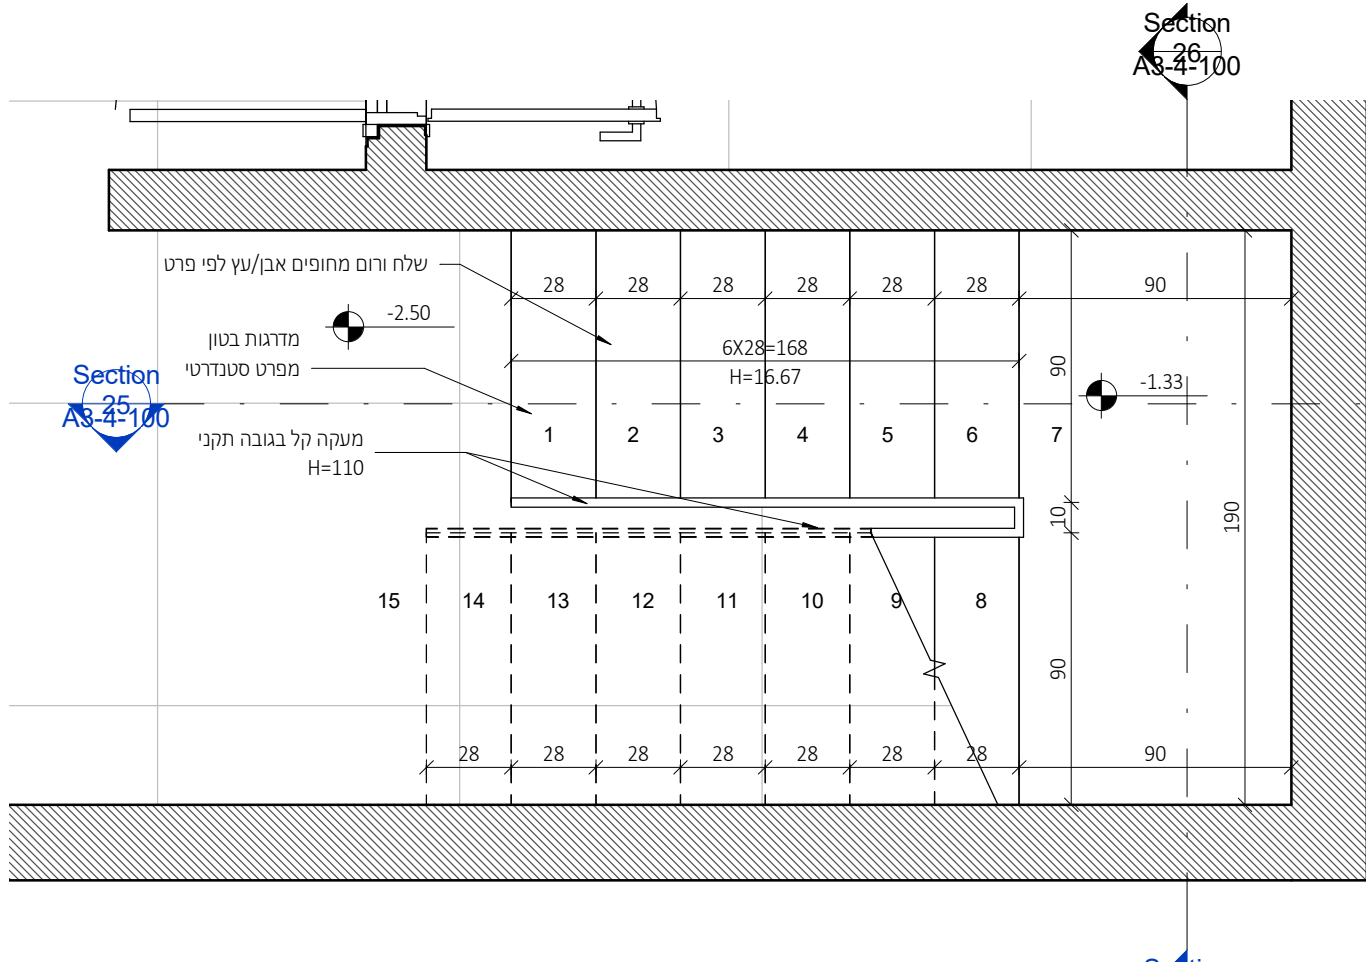


Architectural drawing of a building section showing a grid of columns and beams. The drawing includes dimensions for column spacing (e.g., 28, 18, 17, 19, 20, 21, 22) and beam heights (e.g., H=17.25, H=11.0). It also shows floor levels (+3.45, +1.38) and a section line A-A. The drawing is labeled "Section A-A" and "A6.25.100".



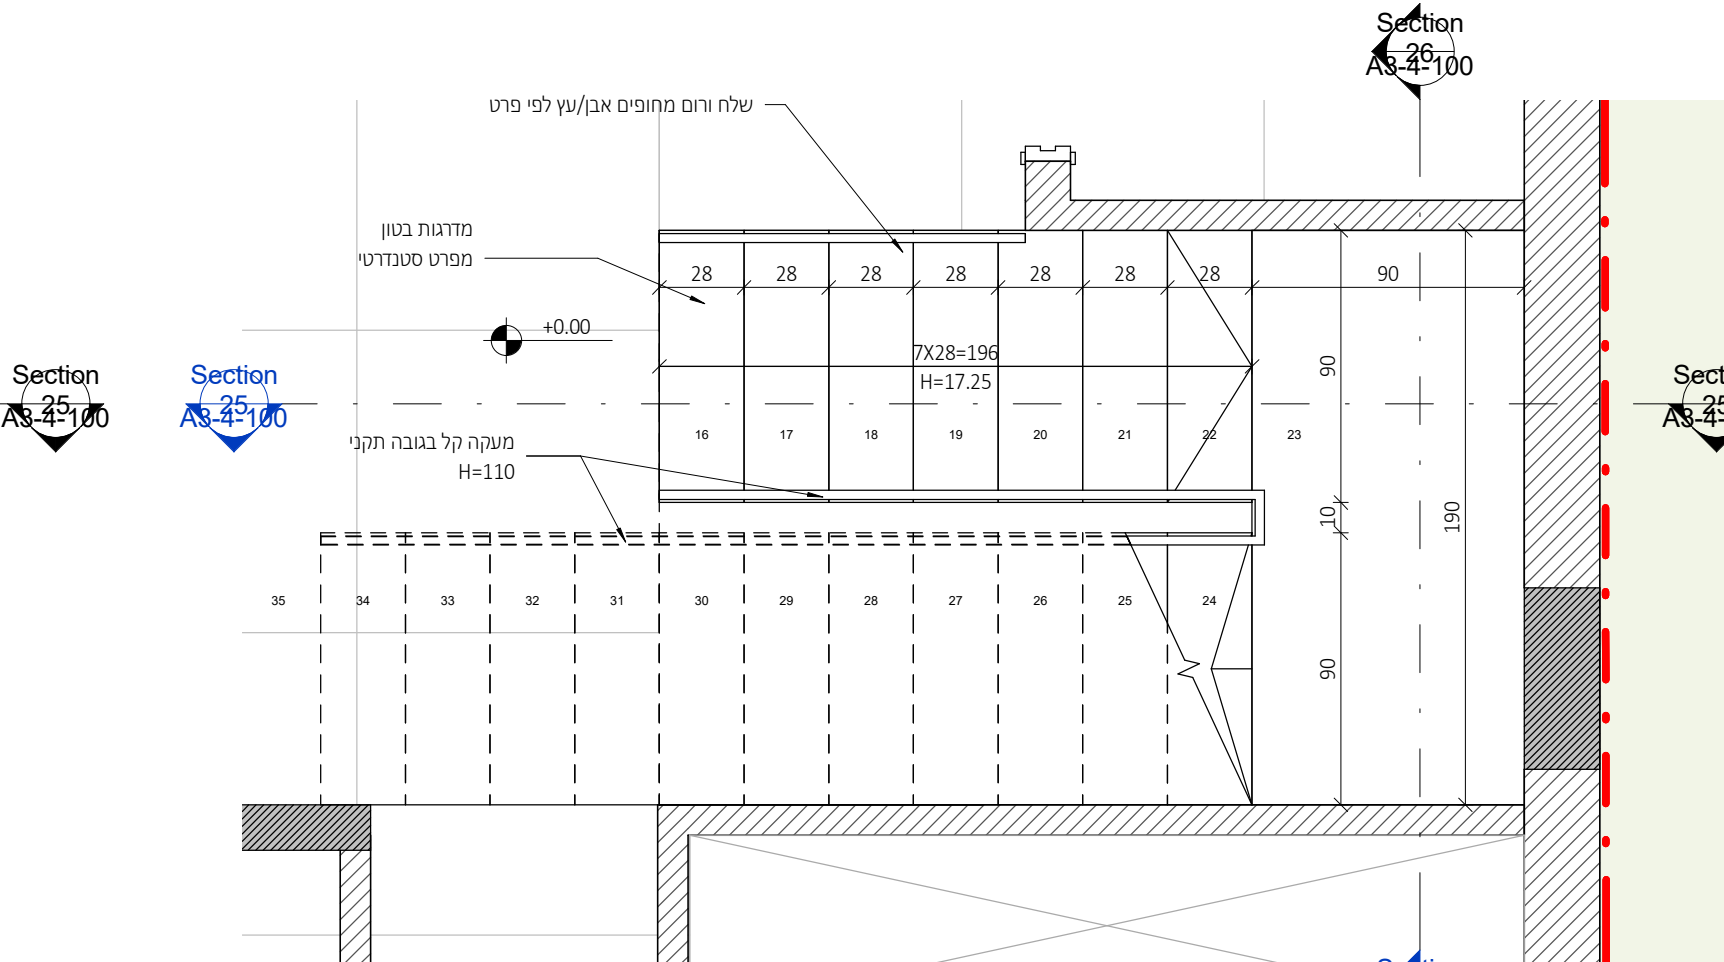


Architectural drawing showing a stepped concrete structure (likely a retaining wall or foundation) with dimensions and labels. The structure is composed of three steps, each with a horizontal width of 28.00 and a vertical height of 16.21. The total width is 84.00 and the total height is 48.63. The structure is labeled with dimensions and notes:

- 28.00 (horizontal dimension for each step)
- 16.21 (vertical dimension for each step)
- 28.00 (horizontal dimension for the top step)
- 16.21 (vertical dimension for the top step)
- 28.00 (horizontal dimension for the bottom step)
- 16.21 (vertical dimension for the bottom step)
- שלה וחזם פרקט אלון 17 מ"מ לאשור אדרכל (Aluminum 17 mm parquet for the floor)
- ריצוף סוג ב (Type B paving)
- חיבור בברזג קצה משופף (Connection with bolt, smooth end)
- בטון עפ"י קונסטרוקטור (Concrete according to the constructor)

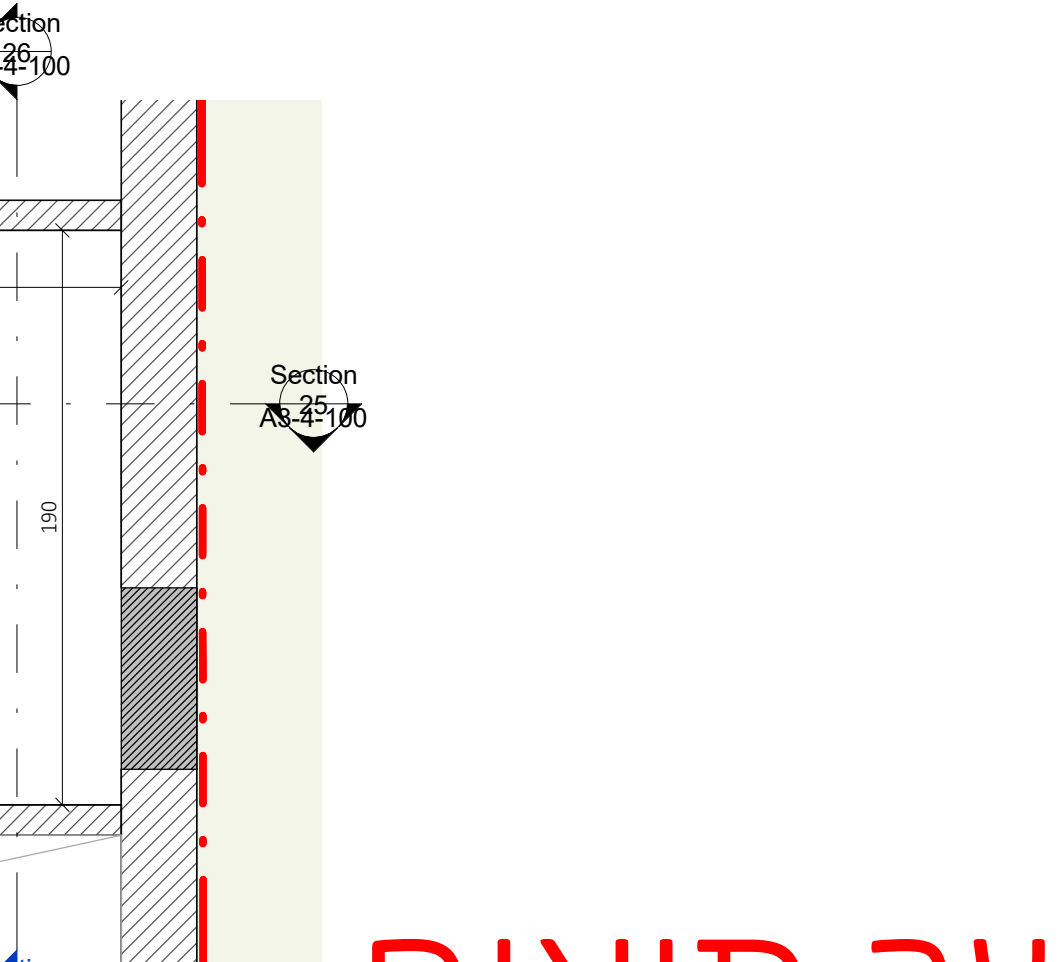

1:

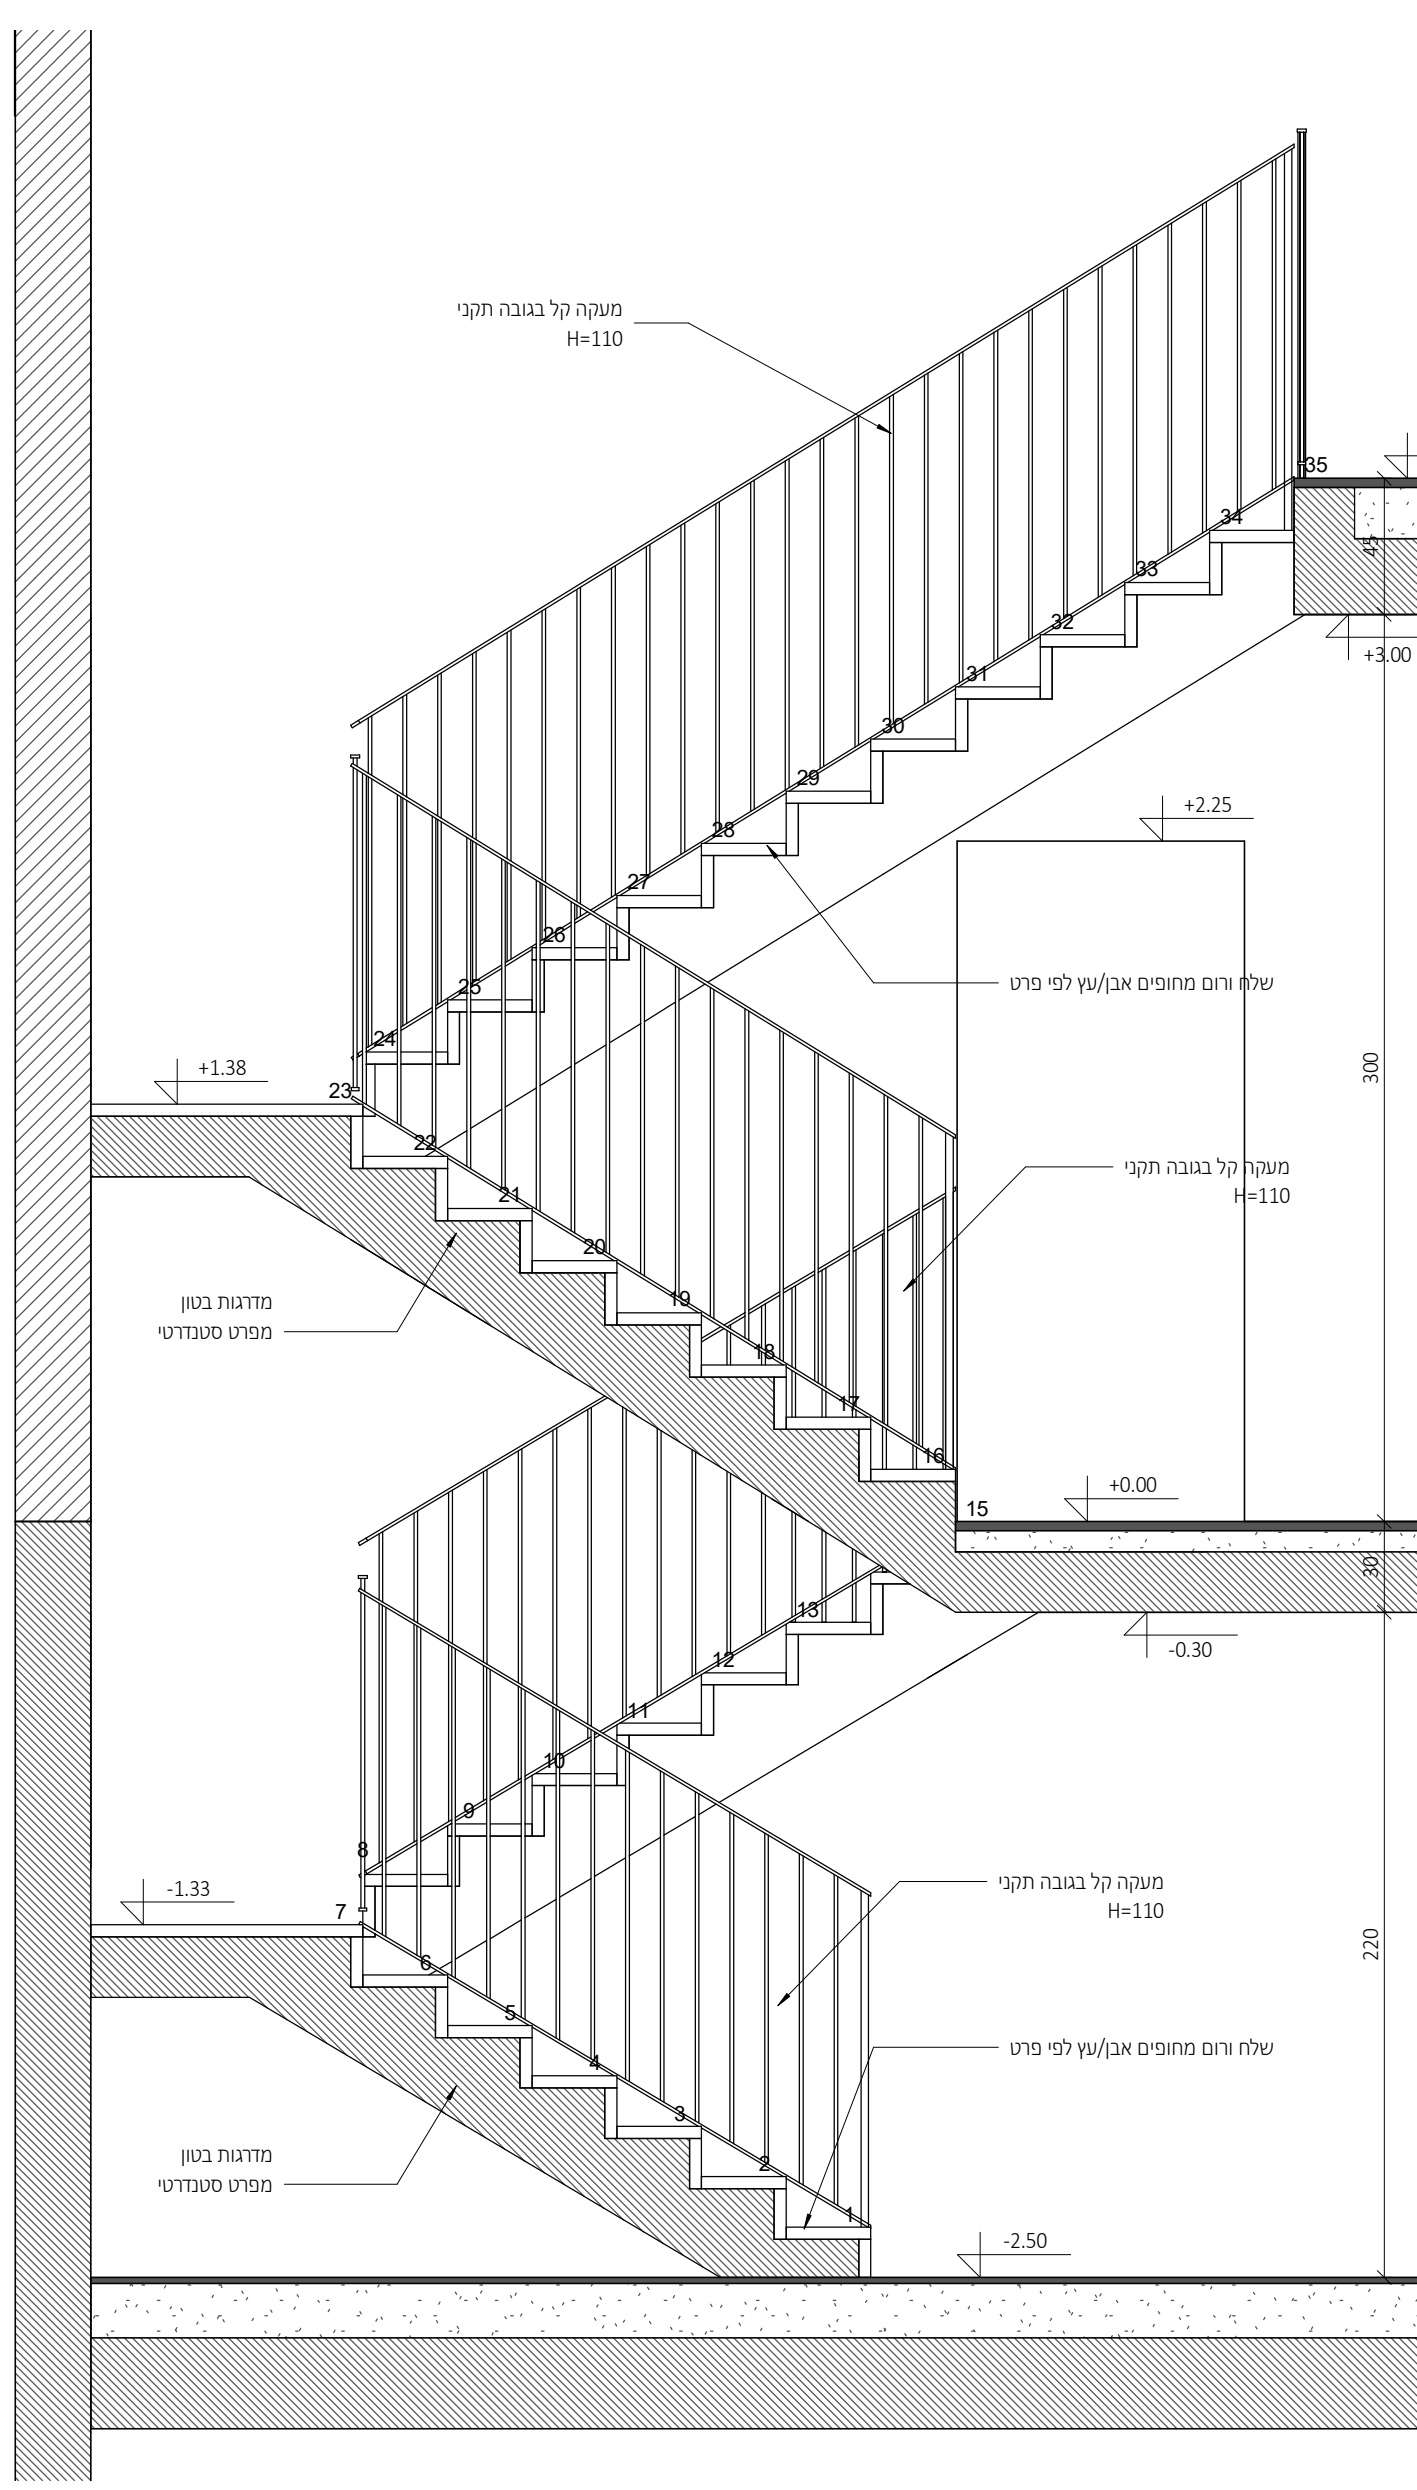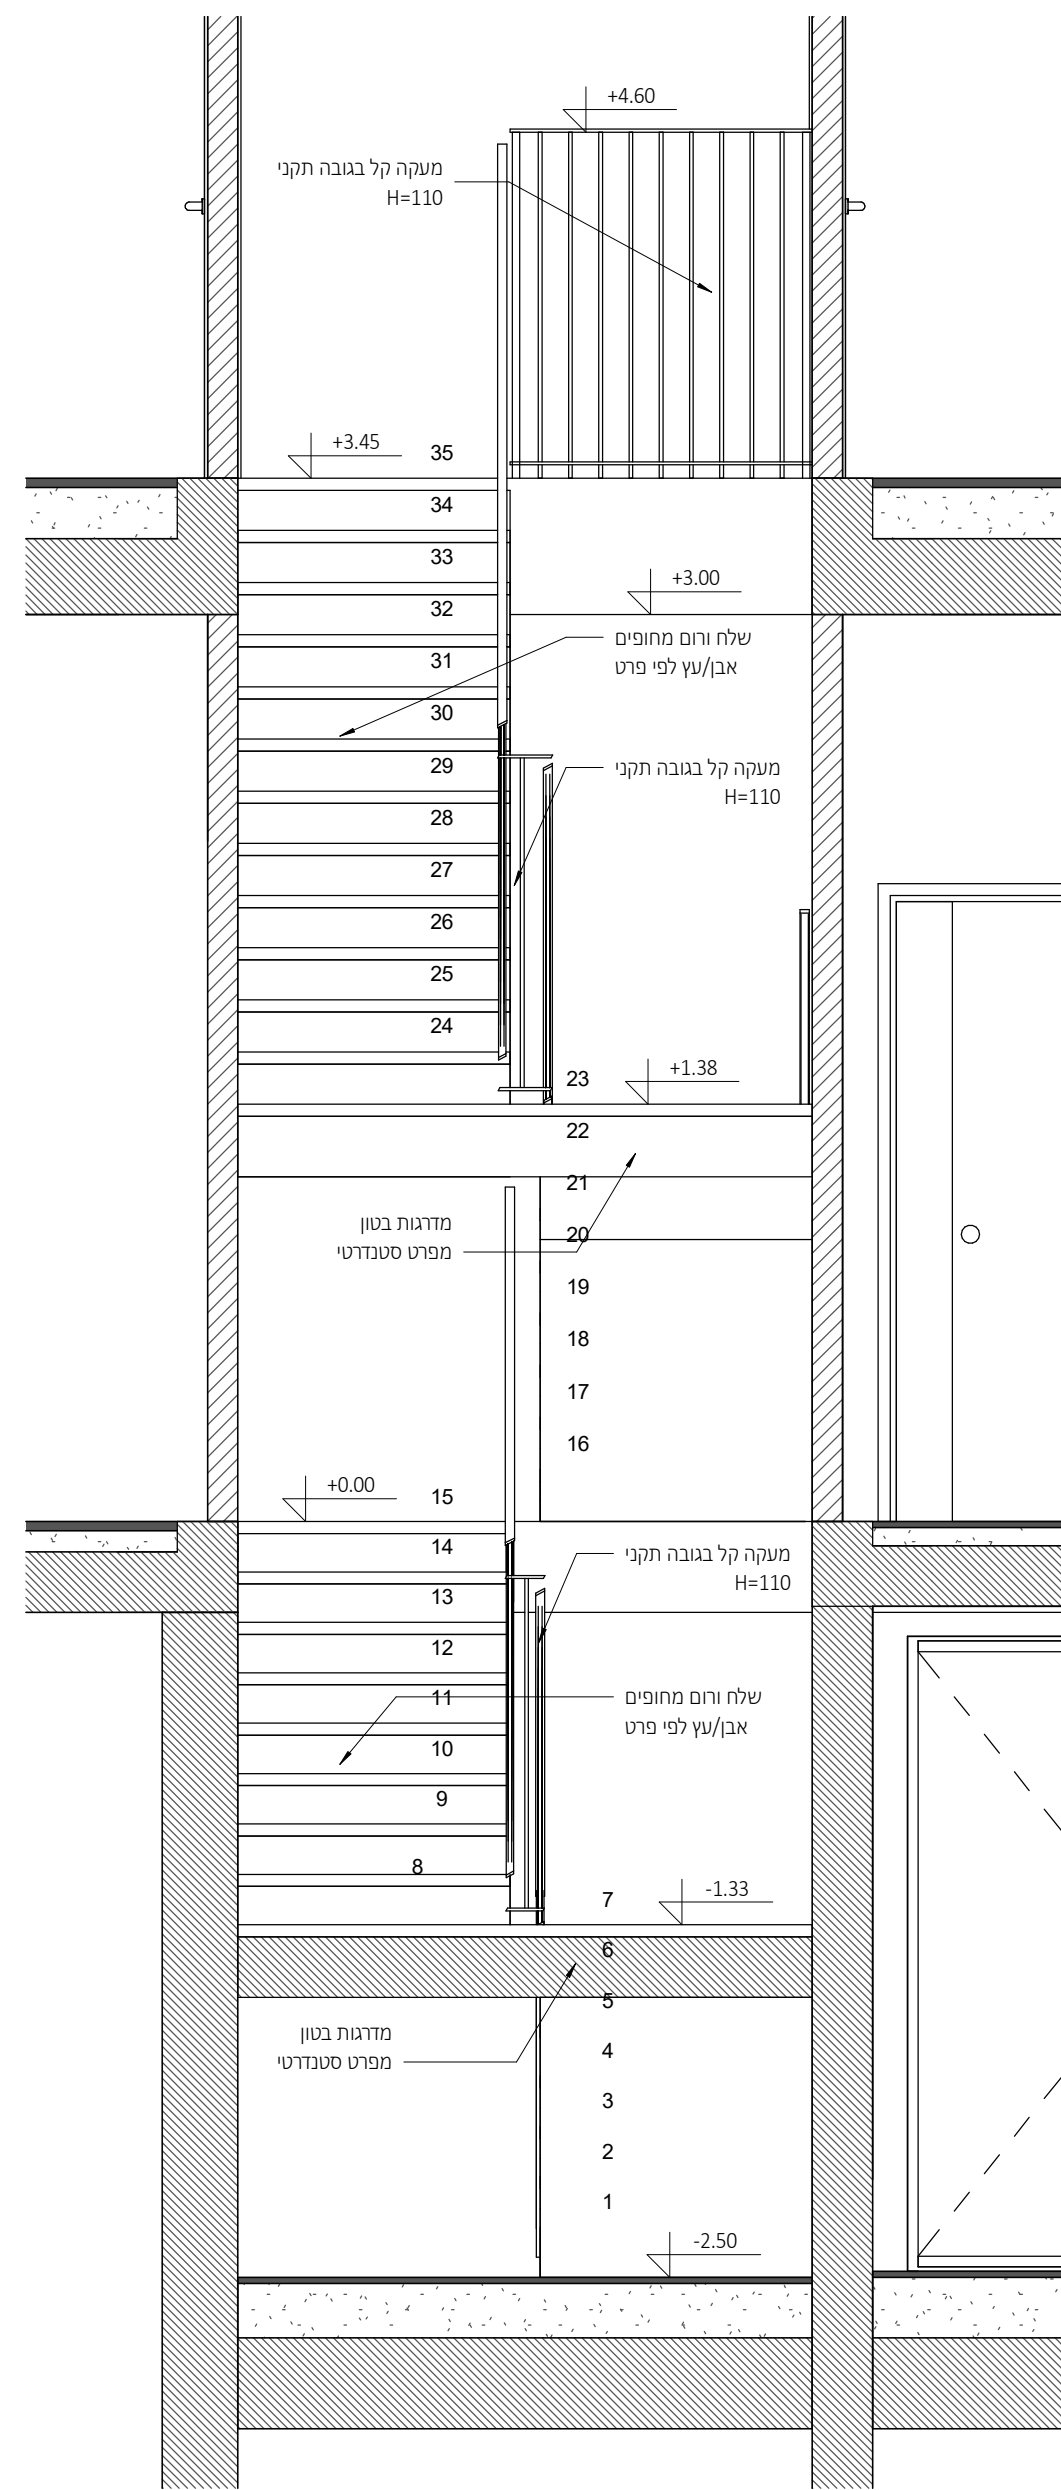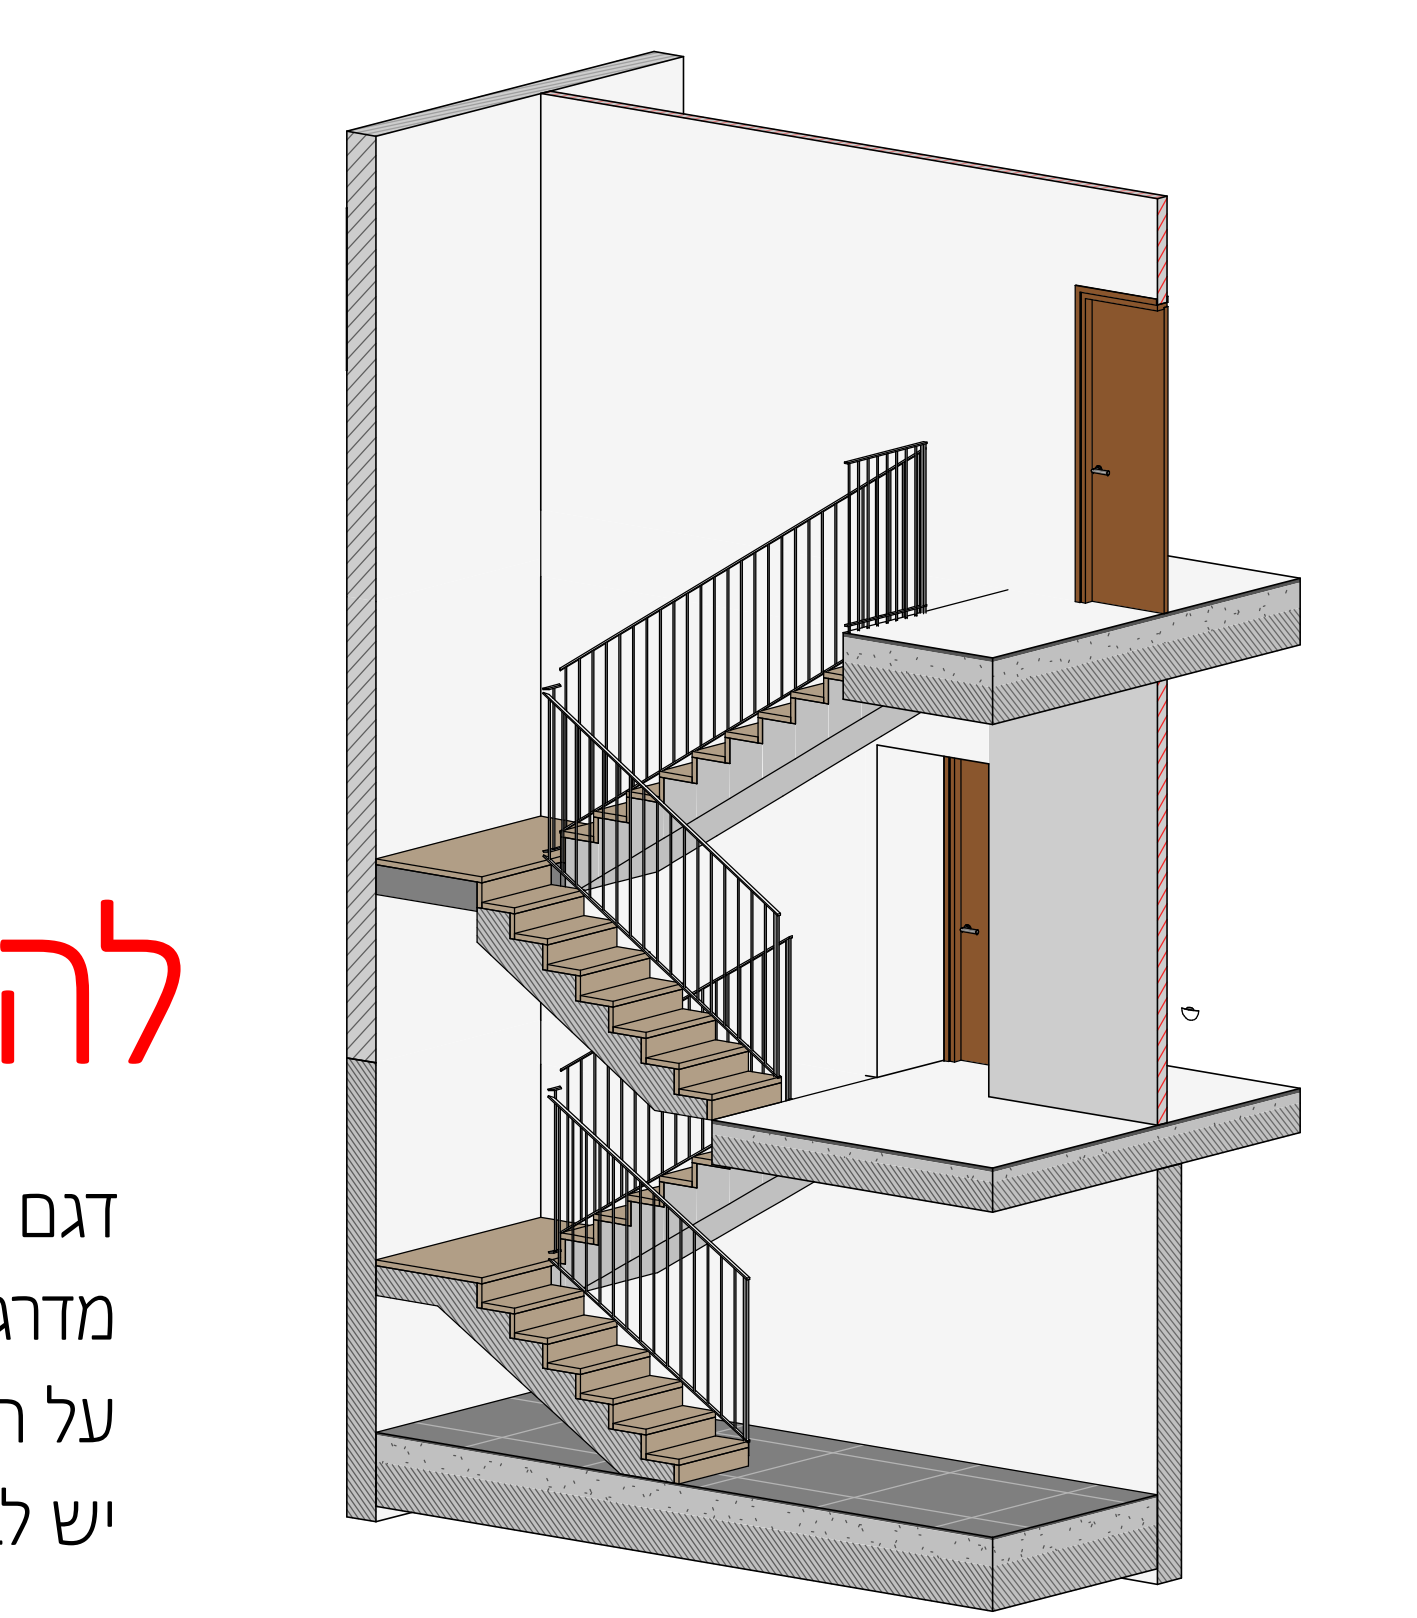

1 : 25

להמשך תיאום

דגם נבחר

מדרגות סטנדרטיות - מפרט סטנדרטי

על הקבלן לשלוח S.D לאישור אדריכל

יש לבצע התאמה לפרט לאחר בחירת חיפוי המדרגות*

ניהול פרויקט
מהיסוד - בן סולומון
פיקוח
מהיסוד - בן סולומון
קונסטרוקציה
ערן שילר
מיזוג אוויר
אייל ארז מהנדסים ויועצים בע"מ
אינסטלציה
איתן אלמסי
חשמל
איתן בסיס
אלומיניום
נוף
נתי בלוקא
חשמל חכם
חימום תת רצפתי
איטום
צבי טל
אקוסטיקה
מעלות
קרקע וביסוס
דיה הנדסת קרקע וביסוס
רישוי

[illegible]

עמוד בטון קיר בטון יד בלוק

[illegible]


CLIENT NAME:		השירותים:	
PROJECT NAME:		הפרויקט:	
קבוצת רכישה נופיה			
נופיה - מגרש 19			
DRAWING NAME:		שם התוכנית:	
פרטים			
SHEET NUMBER:		מספר העמוד:	
A3-4-103			
SCALE:	קנה מידה:	EDITION:	הדורה:
As indicated			
TATUS:	סטטוס		
למכר			
	נבדק ע"י:		ודוס ע"י:
DATE:	22.09.2025		תאריך:




NeumanHaynerArchitects

יומן חיינר אדריכלים
חורר ההדרים 2, בית חירות
09-9545842 גל


office@nh-arch.com
www.nh-arch.com

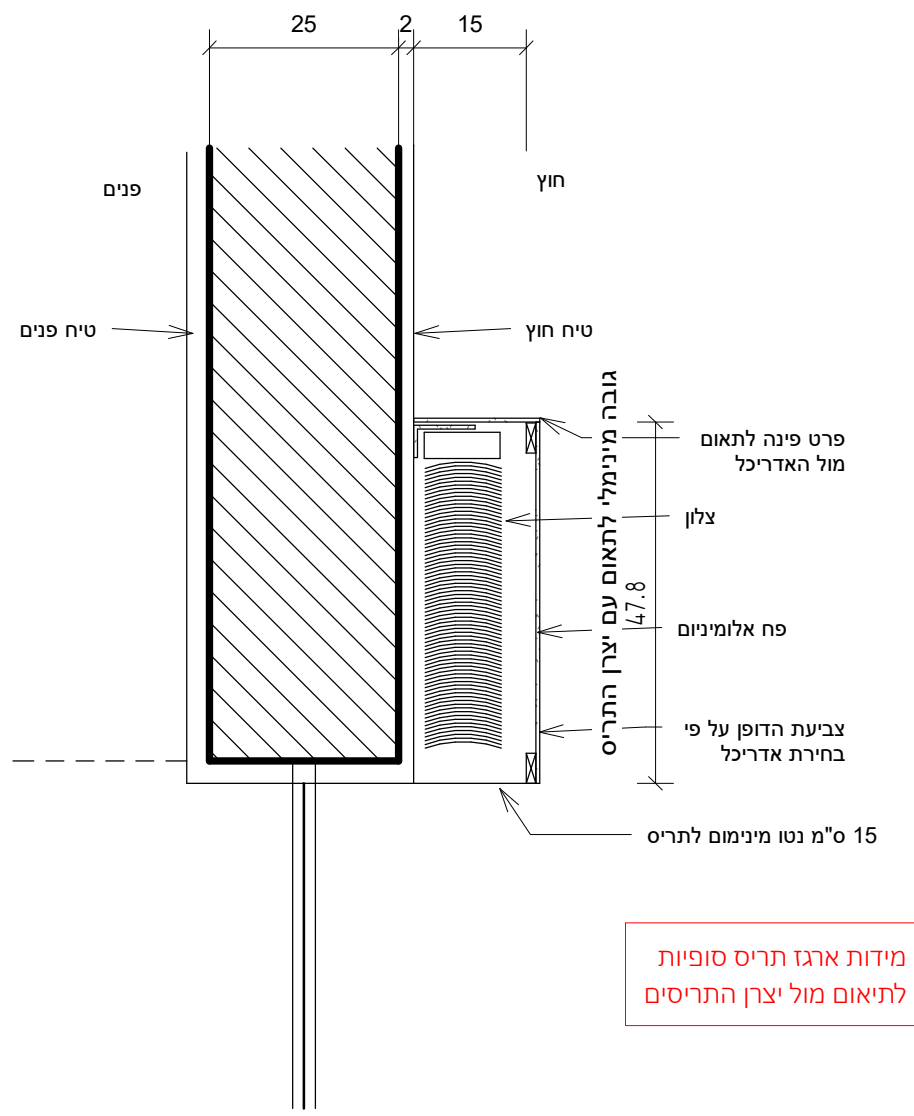

1 : 10

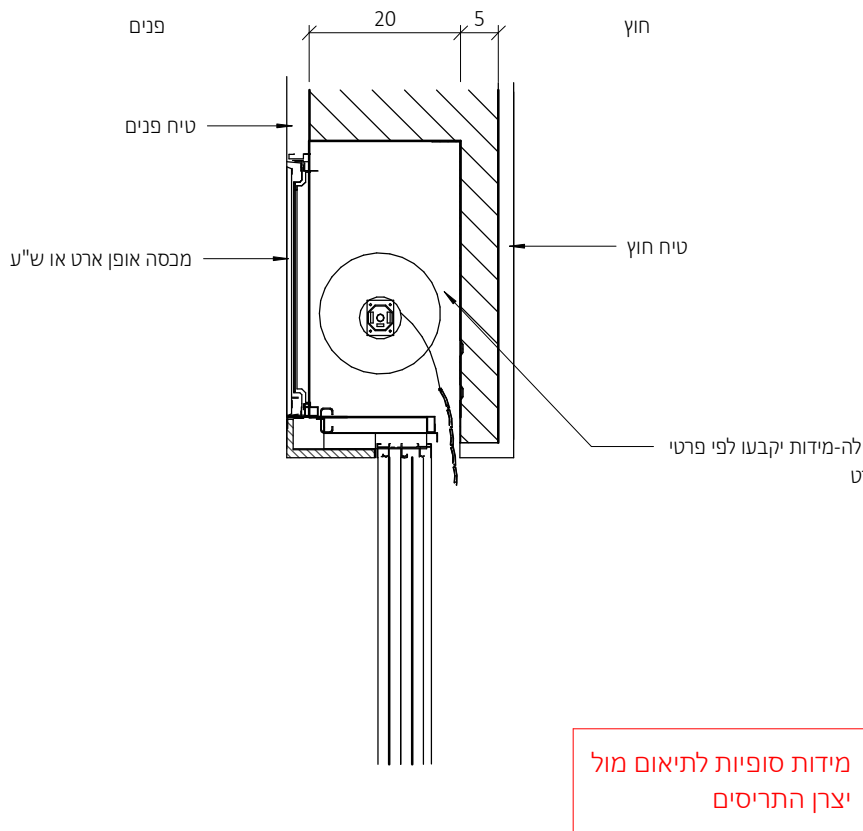


1 : 10

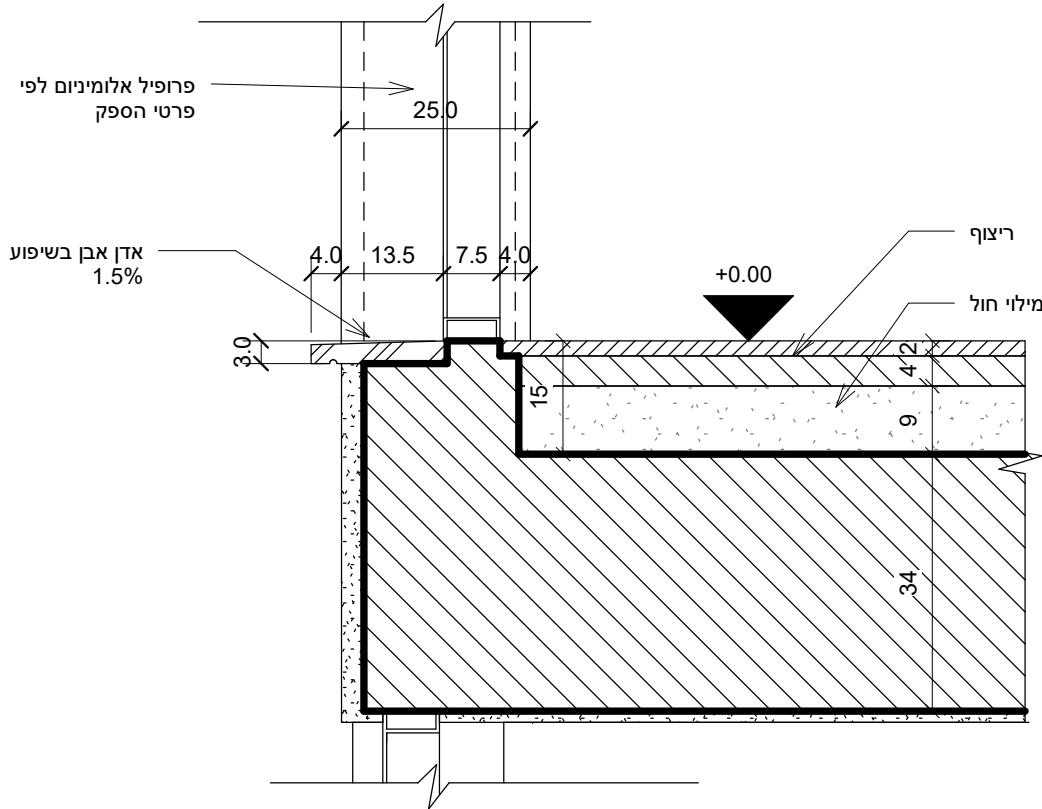

הערה : פרטי האיטום הם עקרוניים בלבד
כל האחריות על האיטום מוטלת על יועץ
האיטום החברה המבצעת
יש לעבוד לפי פרטי האיטום של יועץ הפרויקט.
גובה החלון המופיע בתכניות מצוין את פני סף
האבן. יש להנמיך את הבטון בהתאם

פרט עקרוני בלבד - פרט סופי מספק החלונות


1 : 10

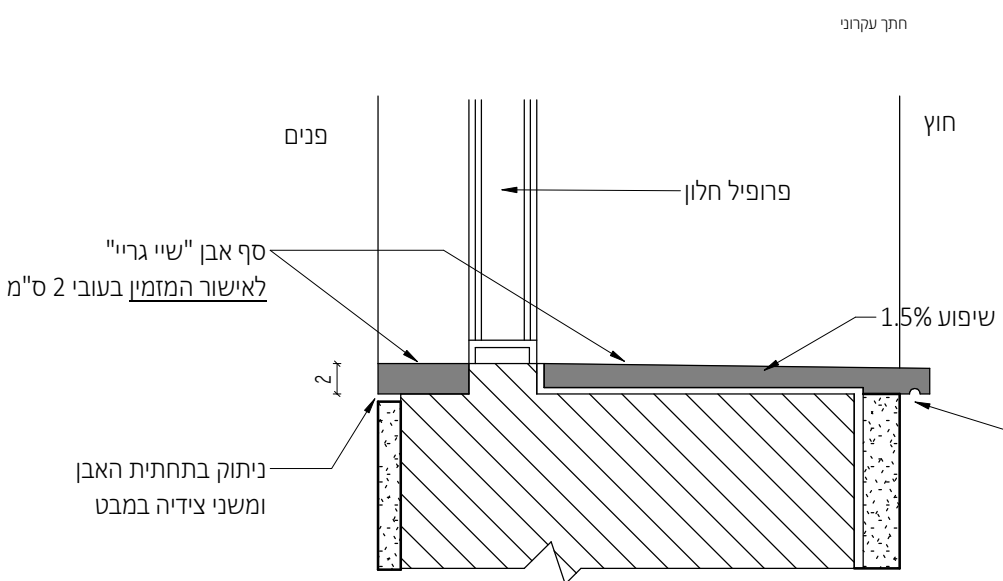


הערה : פרטי האיטום הם עקרוניים בלבד
כל האחריות על האיטום מוטלת על יועץ
האיטום החברה המבצעת
יש לעבוד לפי פרטי האיטום של יועץ הפרו
גובה החלון המופיע בתכניות מצוין את פנ
האבן. יש להנמיך את הבטון בהתאם

פרט עקרוני בלבד - פרט סופי מספק החלונות

1 : 5

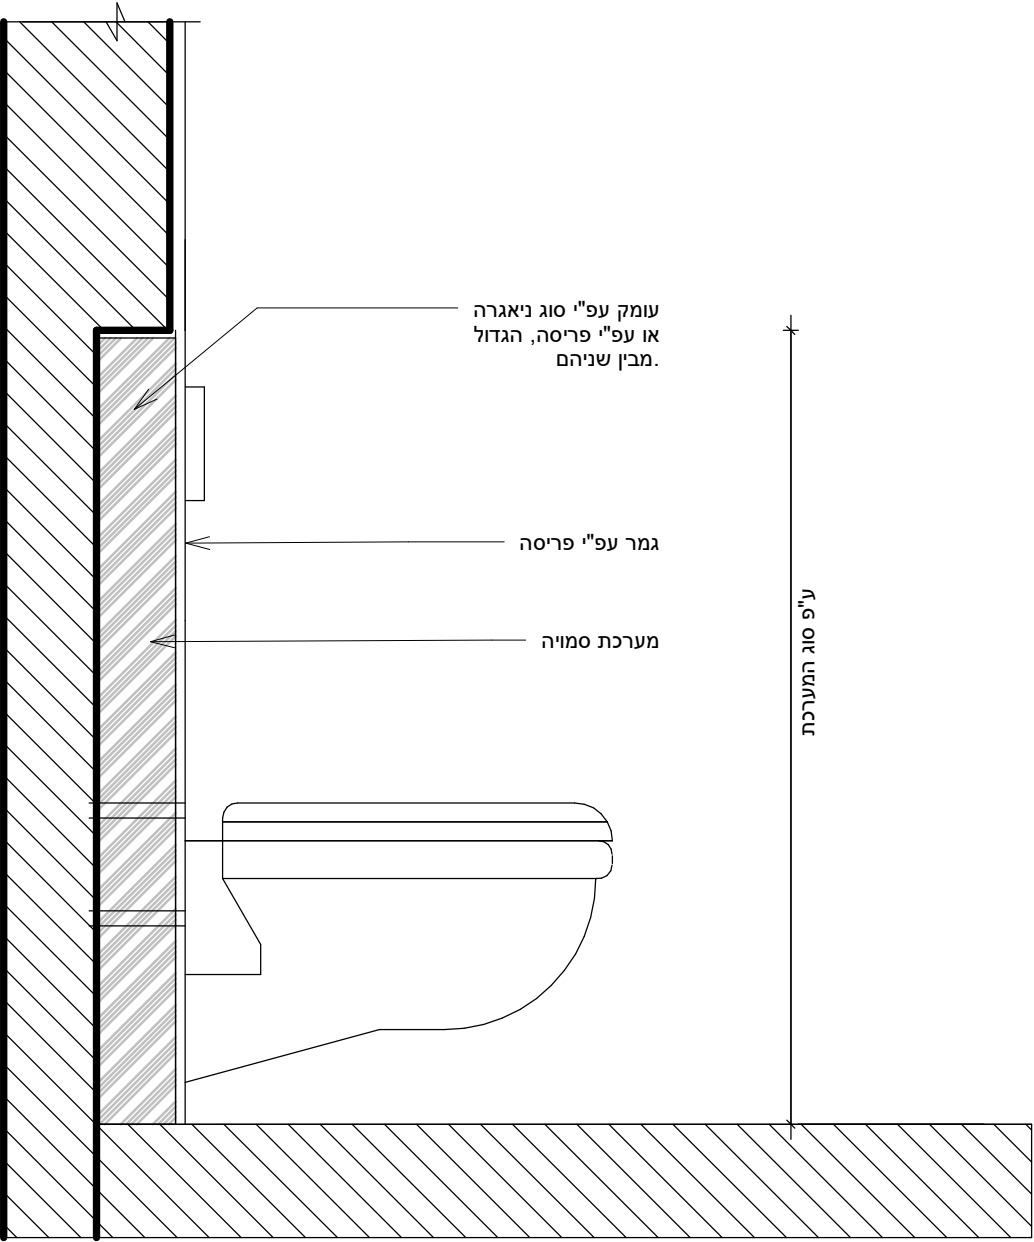

1 : 10

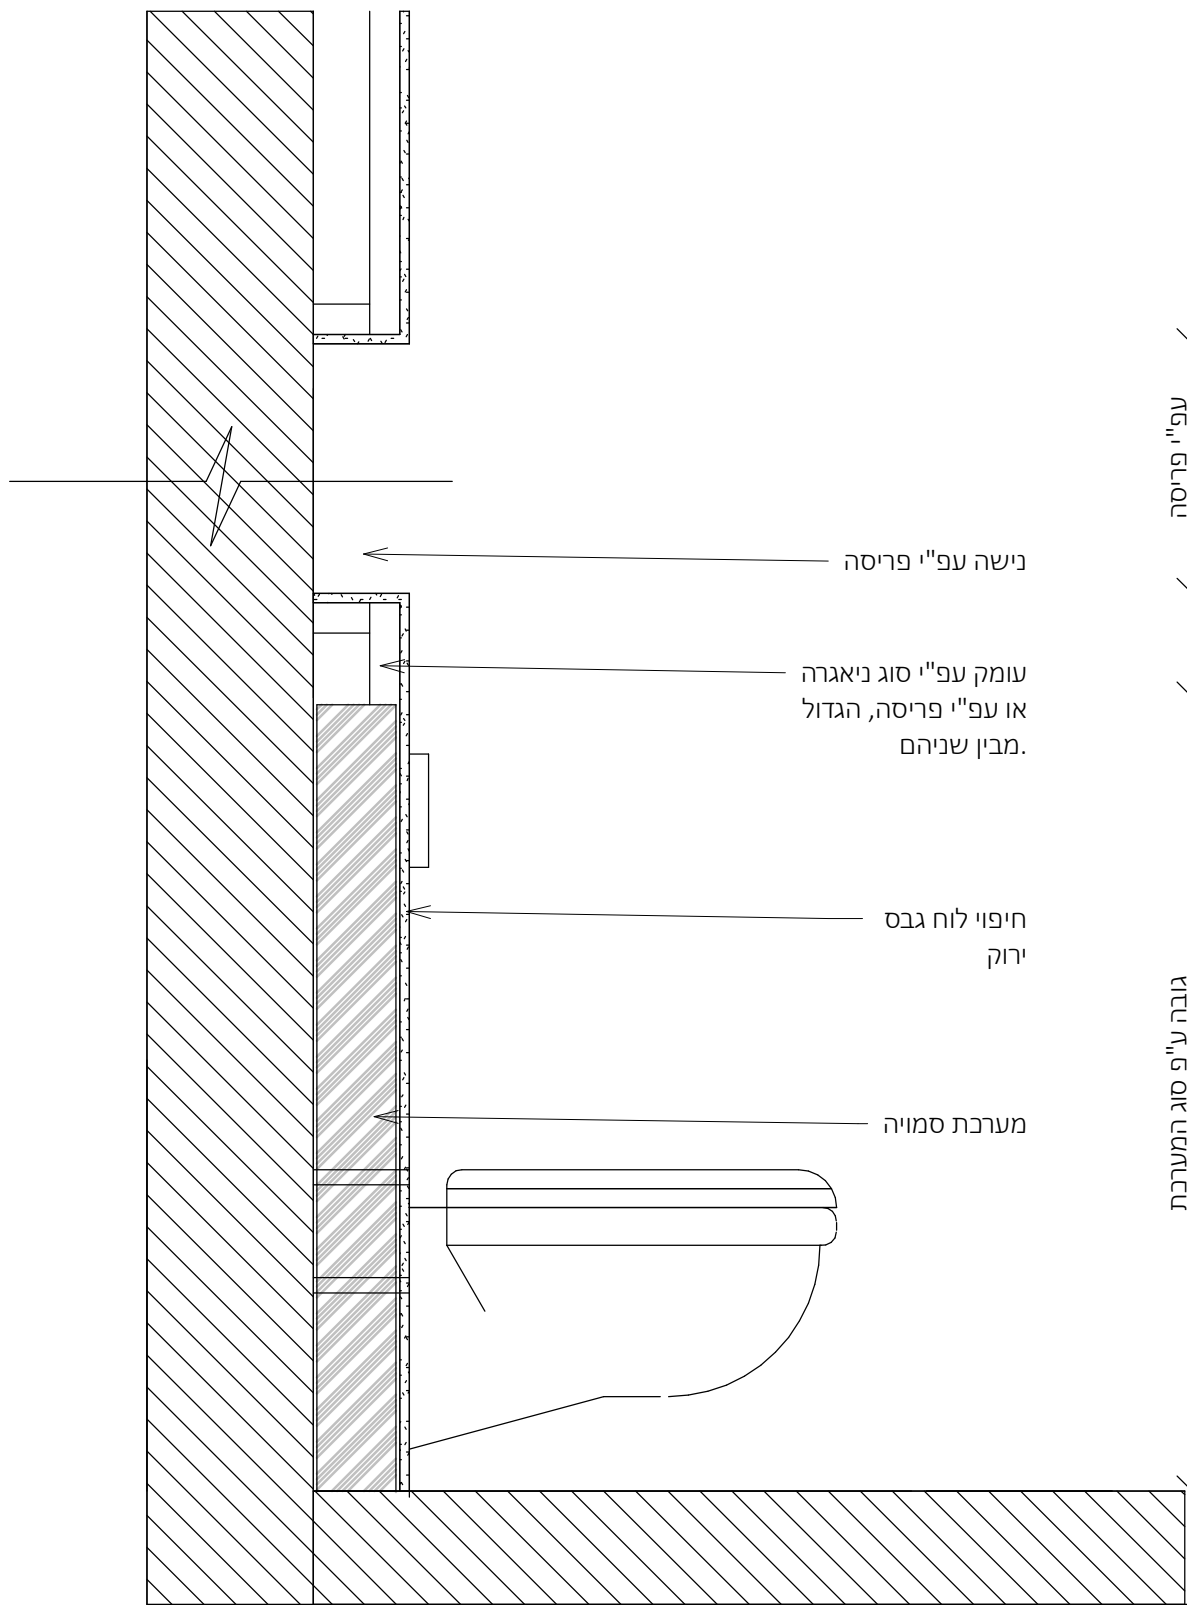

1 : 10

יש לעבוד במקביל לפרטים שיספק
מעצב הפנים (במידה וקיים במגרש זה)
המאושרות על ידי האדריכל.

פרטי האיטום באחריות יועץ האיטום
ראה חוברת פרטי איטום מצורפת


להמשך תיאום

פרגולת אלומיניום




תמונה להמחשה בלבד

להמשך תיאום

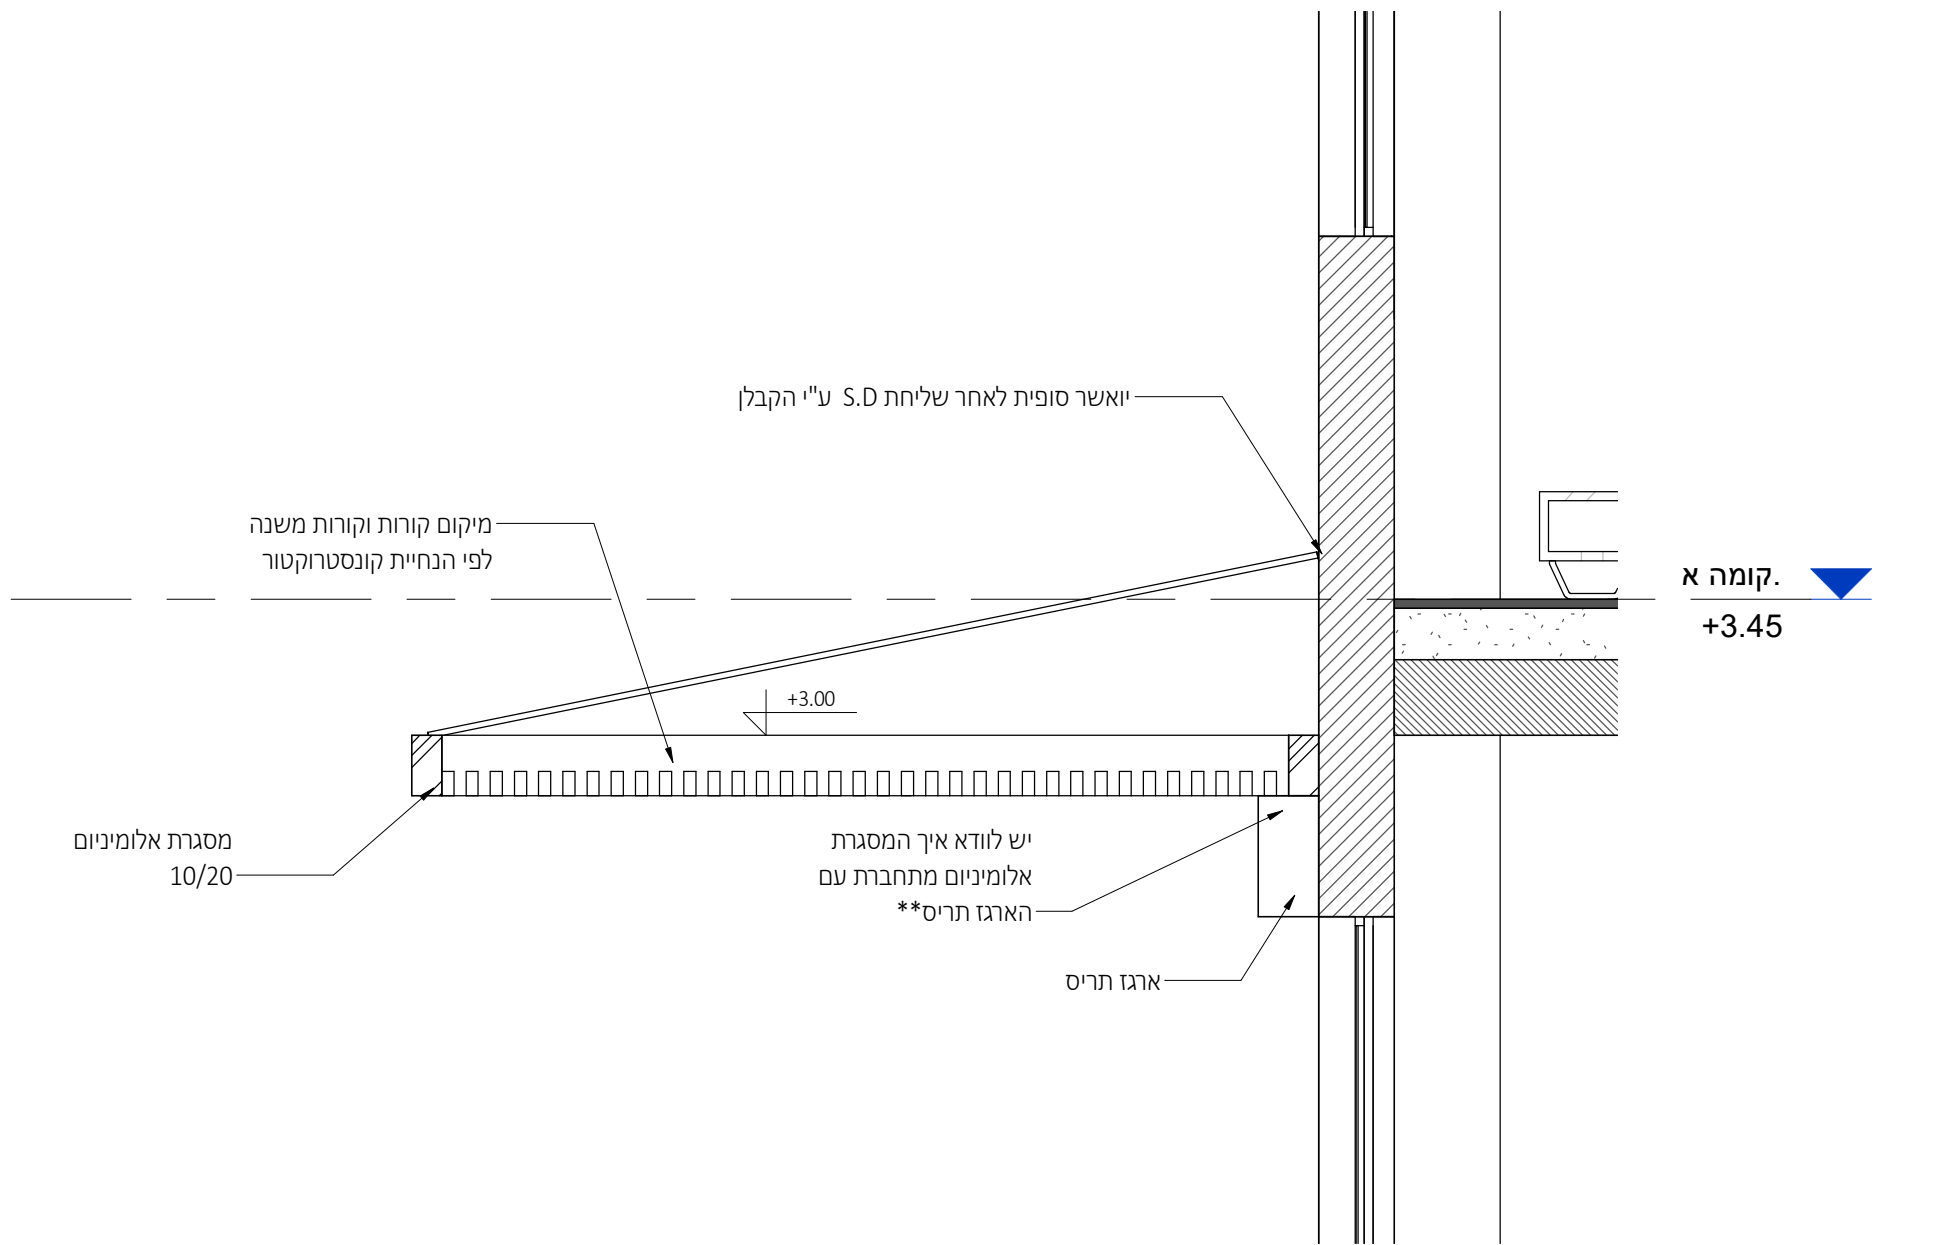


Section 28

1 : 25

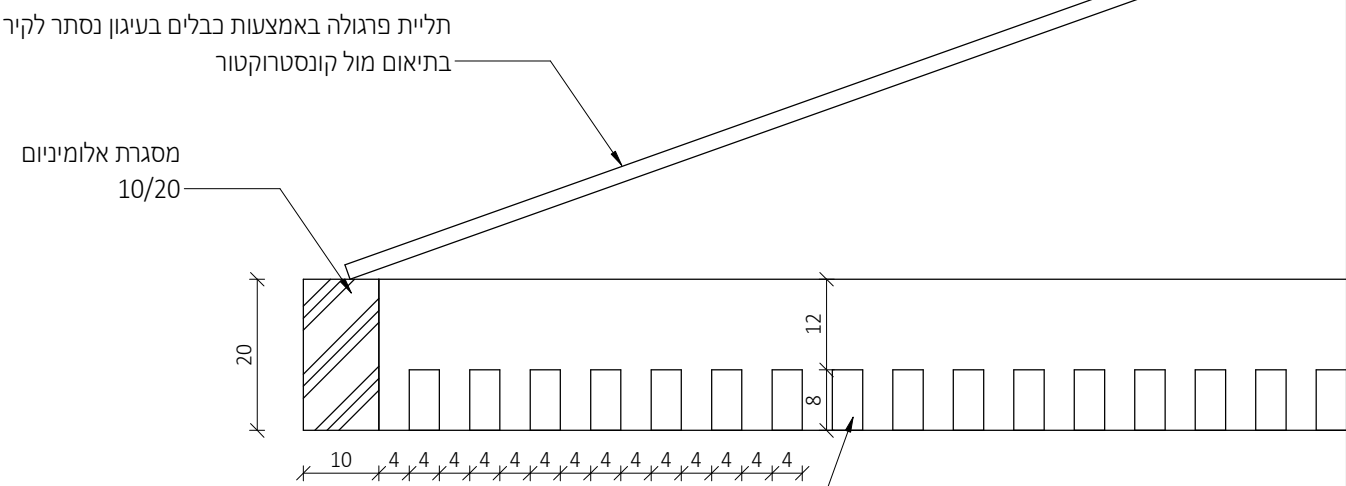

פרגולה - חתך רוחב

1 : 10

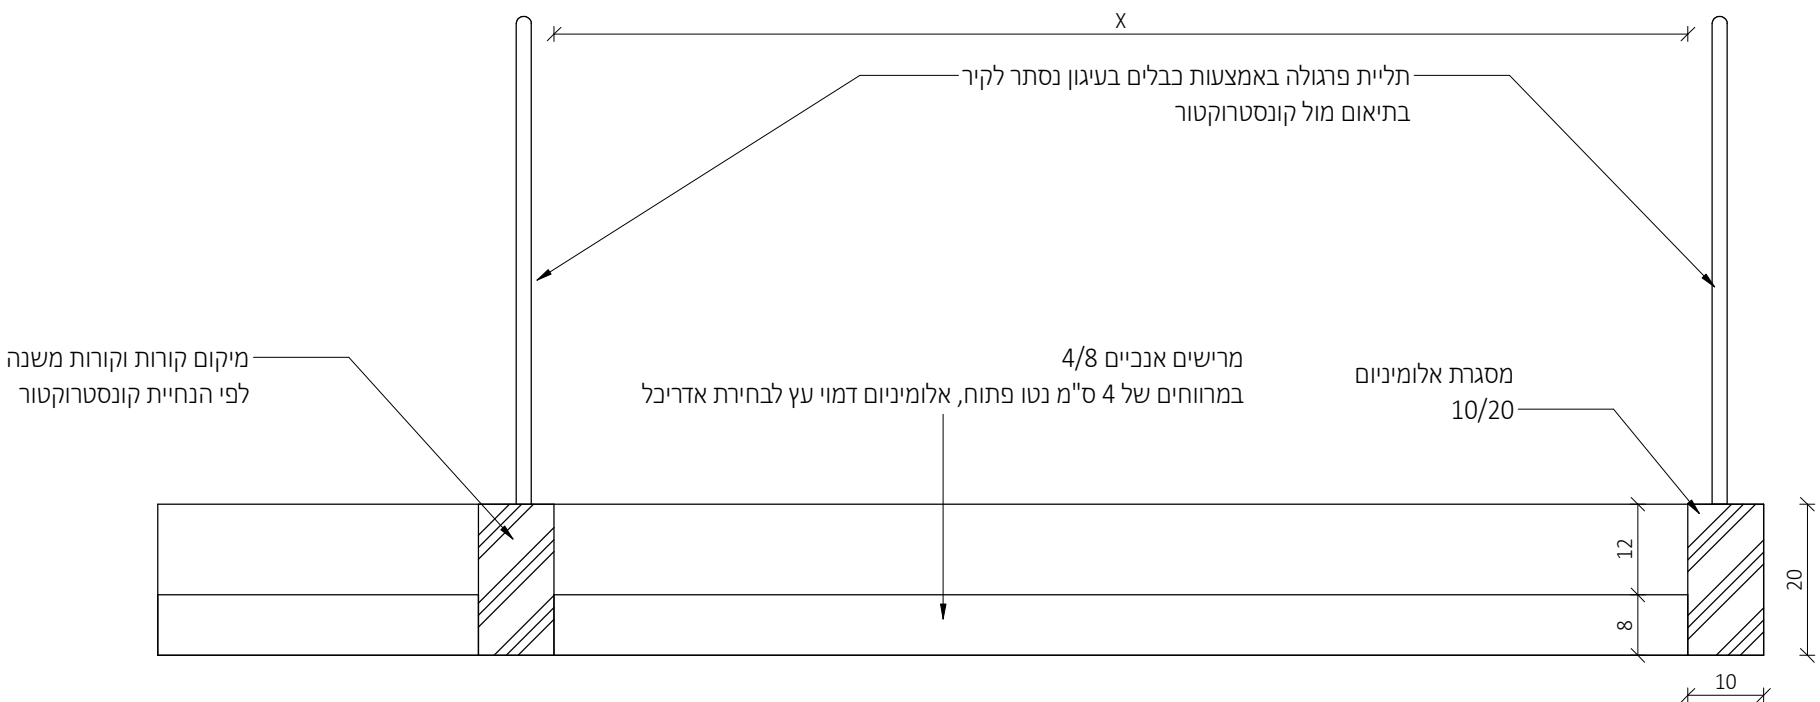

פרגולה - חתך אורך


1 : 10

מתכננים:

ניהול פרויקט
מהיסוד - בן סולומון
פיקוח
מהיסוד - בן סולומון
קונסטרוקציה
ערן שילר
מיזוג אוויר
אייל ארז מהנדסים ויועצים בע"מ
אינסטלציה
איתן אלמסי
חשמל
איתן בסיס
אלומיניום
בופ
נתי בלוקא
חשמל חכם
חימום תת רצפתי
איטום
צבי טל
אקוסטיקה
מעליות
קרקע וביסוס
דיה הנדסת קרקע וביסוס
רישוי

± 0.00 = +243.50
הערות: 1. תכנית זו אינה לקרא יחד עם תכנית הרישוי. 2. גובה אבטומנטים: ראו תכנית פיתוח. 3. הפירות הן בין קירות הבניה ולא כולל פחים. 4. פיתוח השטח סביב המבנה, כולל, מדרגות, גדרות, שבילים, ריצופים, שיפועים, גדרים, חללים וגובה לא תכנית פיתוח. 5. איסוס קירות והפחות המבנה כמעט עם הקרקע ובידוד תרמי לאורך העמודים והקירות וגם על פניהם (גובה) - ראו תכנית קונסטרוקציה. 6. אף דום יבוצע בכל מישור אופקי הכולל מהבניה. 7. סיוח תרמי במסגרת - ע"פ מפרט התמקיר, מאושר ע"י פיקוח העיר.
המבצע והמבוצע: המבצע אחראי לסיווח: עליו לבקר ולבדוק את כל המידות בתכנית ובמקום המבוצע. במסגרת של סיווח או אי התאמה בתכנית /או בבנין, עליו להודיע על כך מיד לאדריכל במסגרת המשך המשרד המבוצע. המבצע יתחשב אך ורק בתכנית שאושרה לכניסה. המבצע יחזיק באחריות, בכל מה, של משרדו של תכנית. אין לקבוע מידות על ידי מדידה בשטח. התכנית היתה רכוש האדריכל ואין לשנות כל שינוש בה או ברעיונות הגלומים בה, אלא באישור בכתב מהאדריכל. מחנכים /או יועץ אשר שמו רשום בתכנית זו, נושא לכיד באחריות המקצועית והתקנית לתכנית. על המפקח והמבצע לודא התאמת התכנית האדריכלית "לכניסה" לתכנית כוללת את כל האחריות והידע עד ליום תחילתה.

משרד קירות:

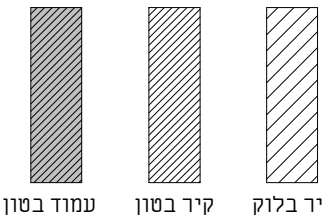

תאריך	תיאור	מהדורה
22.09.2025	מכרז	1

אדריכלות

שם המסמך:	CLIENT NAME:
קבוצת רכישה נופיה	
שם הפרויקט:	PROJECT NAME:
נופיה - מגרש 19	
שם הגיליון:	DRAWING NAME:
פרטי פרגולה	
מספר גיליון:	SHEET NUMBER:
A3-4-104	
תאריך:	DATE:
22.09.2025	

NeumanHaynerArchitects

נירסן חיינר אדריכלים
מנכ"ל התחנה 2, בית חירות
09-9545642 70

office@nh-arch.com
www.nh-arch.com

רשימת חלונות					
מס פריט	רוחב	גובה	כמות	תיאור	סוג

7	310	110	1	צולן רפפה חיצוני חשמלי + ארגז חיצוני	חלון הזזה פרופיל 7000 קליל
8	60	110	1	ללא רפפה	חלון קיפ פרופיל 4500 קליל

1	290	240	1	צלון רפפה חיצוני חשמלי + ארגז חיצוני	ויטרינה פרופיל 7500 קליל
2	220	110	3	צלון רפפה חיצוני חשמלי + ארגז חיצוני	חלון הזזה פרופיל 7000 קליל
3	90	240	1	צלון רפפה חיצוני חשמלי + ארגז חיצוני	דלת כנף פרופיל 4350 קליל
3.1	90	240	1	צלון רפפה חיצוני חשמלי + ארגז חיצוני	חלון קבוע פרופיל 7000 קליל
4	200	240	2	צלון רפפה חיצוני חשמלי + ארגז חיצוני	ויטרינה פרופיל 7500 קליל
5	70	110	1	צלון רפפה חיצוני חשמלי + ארגז חיצוני	חלון קיפ פרופיל 4500 קליל
6	70	240	1	צלון רפפה חיצוני חשמלי + ארגז חיצוני	קבוע עד 130 + חלון קיפ פרופיל 4350

9	110	110	3	תריס גלילה חשמלי	חלון הזזה פרופיל 7000 קליל
10	160	230	3	תריס גלילה חשמלי	ויטרינה פרופיל 7500 קליל
11	220	110	2	תריס גלילה חשמלי	חלון הזזה פרופיל 7000 קליל
12	70	110	4	תריס גלילה חשמלי	חלון קיפ פרופיל 4500 קליל

כל פריט יחולק למינימום הכנפיים האפשרי (לתיאום מול ספק האלומיניום ובמסגרת שרטוטי הshop drawing)

רשימת דלתות					
סוג	הערות	כמות	גובה	רוחב	מספר פריט

0	120	240	1	דלת בניסה	דלת חוץ דגם גארדה
1	80	210	10	דלת פנים	דלת פנים "אקוודור" תוצרת חמדיה
2	80	210	1	דלת הזזה	דלת הזזה "אקוודור" פורמייקה תוצרת חמדיה
3	90	210	2	דלת פנים	דלת פנים "אקוודור" תוצרת חמדיה
4	80	200	1	דלת נגרות ממ"ד	דלת פנים "אקוודור" תוצרת חמדיה

26/10/2025 16:38:09