
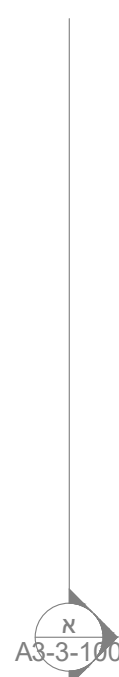


3-195

3-195

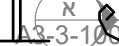

אודינג פנים	
אינסטציה	
ביטחות אש	
אוקסידים	
חשמל ותאורה	
קונסטרוקציה	
קבלו ראשי	
ניווט פרויקט	
נקות	
אודינג	

[illegible][illegible]

1. כל התעלות מחזק למבנה יבדרוד
בבירוד אקוסטי בעובי 2"
2. תעלות מזוג בתור המבנה יבדרוד
בבירוד אקוסטי פנימי 1"
3. תעלות אוויר צד יבדרוד
בבירוד 1" טרמי 1"
4. יש לאמזם במסילקון את פינות החיבור
שי תעלות מזוג אוויר לפני כיפוף
הפחים המתחברים

[illegible]

תעלות ותריסי אוויר חוזר	
תעלות ותריסי סאפנקת אוויר	
תעלות ותריסי אוויר צח	
תעלות ותריסי יניקת אוויר	
תעלות ותריסי שחרור עשן	
צנרת גז וחשמל	
סימון מעגלי מדוזג אוויר	

אייל ארז | מהנדסים יועצים
שפי ותמנן מפרנס חייבו ואימור, פיקוח עליון

אוריכל פנים	
אינסטיציה	
בסיחת אש	
אקוסטיקה	
חשתי והזרה	
קונסטרוקציה	
קבלו ראש	
ניחול פרויקט	
נמח	
אוריכל	

		⚠
		⚠
		⚠
תבנית כעיון	04.05.2025	⚠
שנויים:	חאריץ:	סל:

שלט הפעלה אלחוטי


סימון מעגלי מיזוג אוויר

אייל ארז | מהנדסים יועצים
 יעץ וינגטון העירייה מיוזם ומאמץ, פיתוח ארץ

בסיס בטון בגובה מינימלי 10 ס"מ
יחידת עיבוי עומדת ע"ג בולמי רעידות
לטיפול קבלן מיזוג אוויר

Option No2
inverter duct unit in living
room and wall mounted in
rooms

Option No.2
inverter duct unit in living
room and wall mounted in
rooms

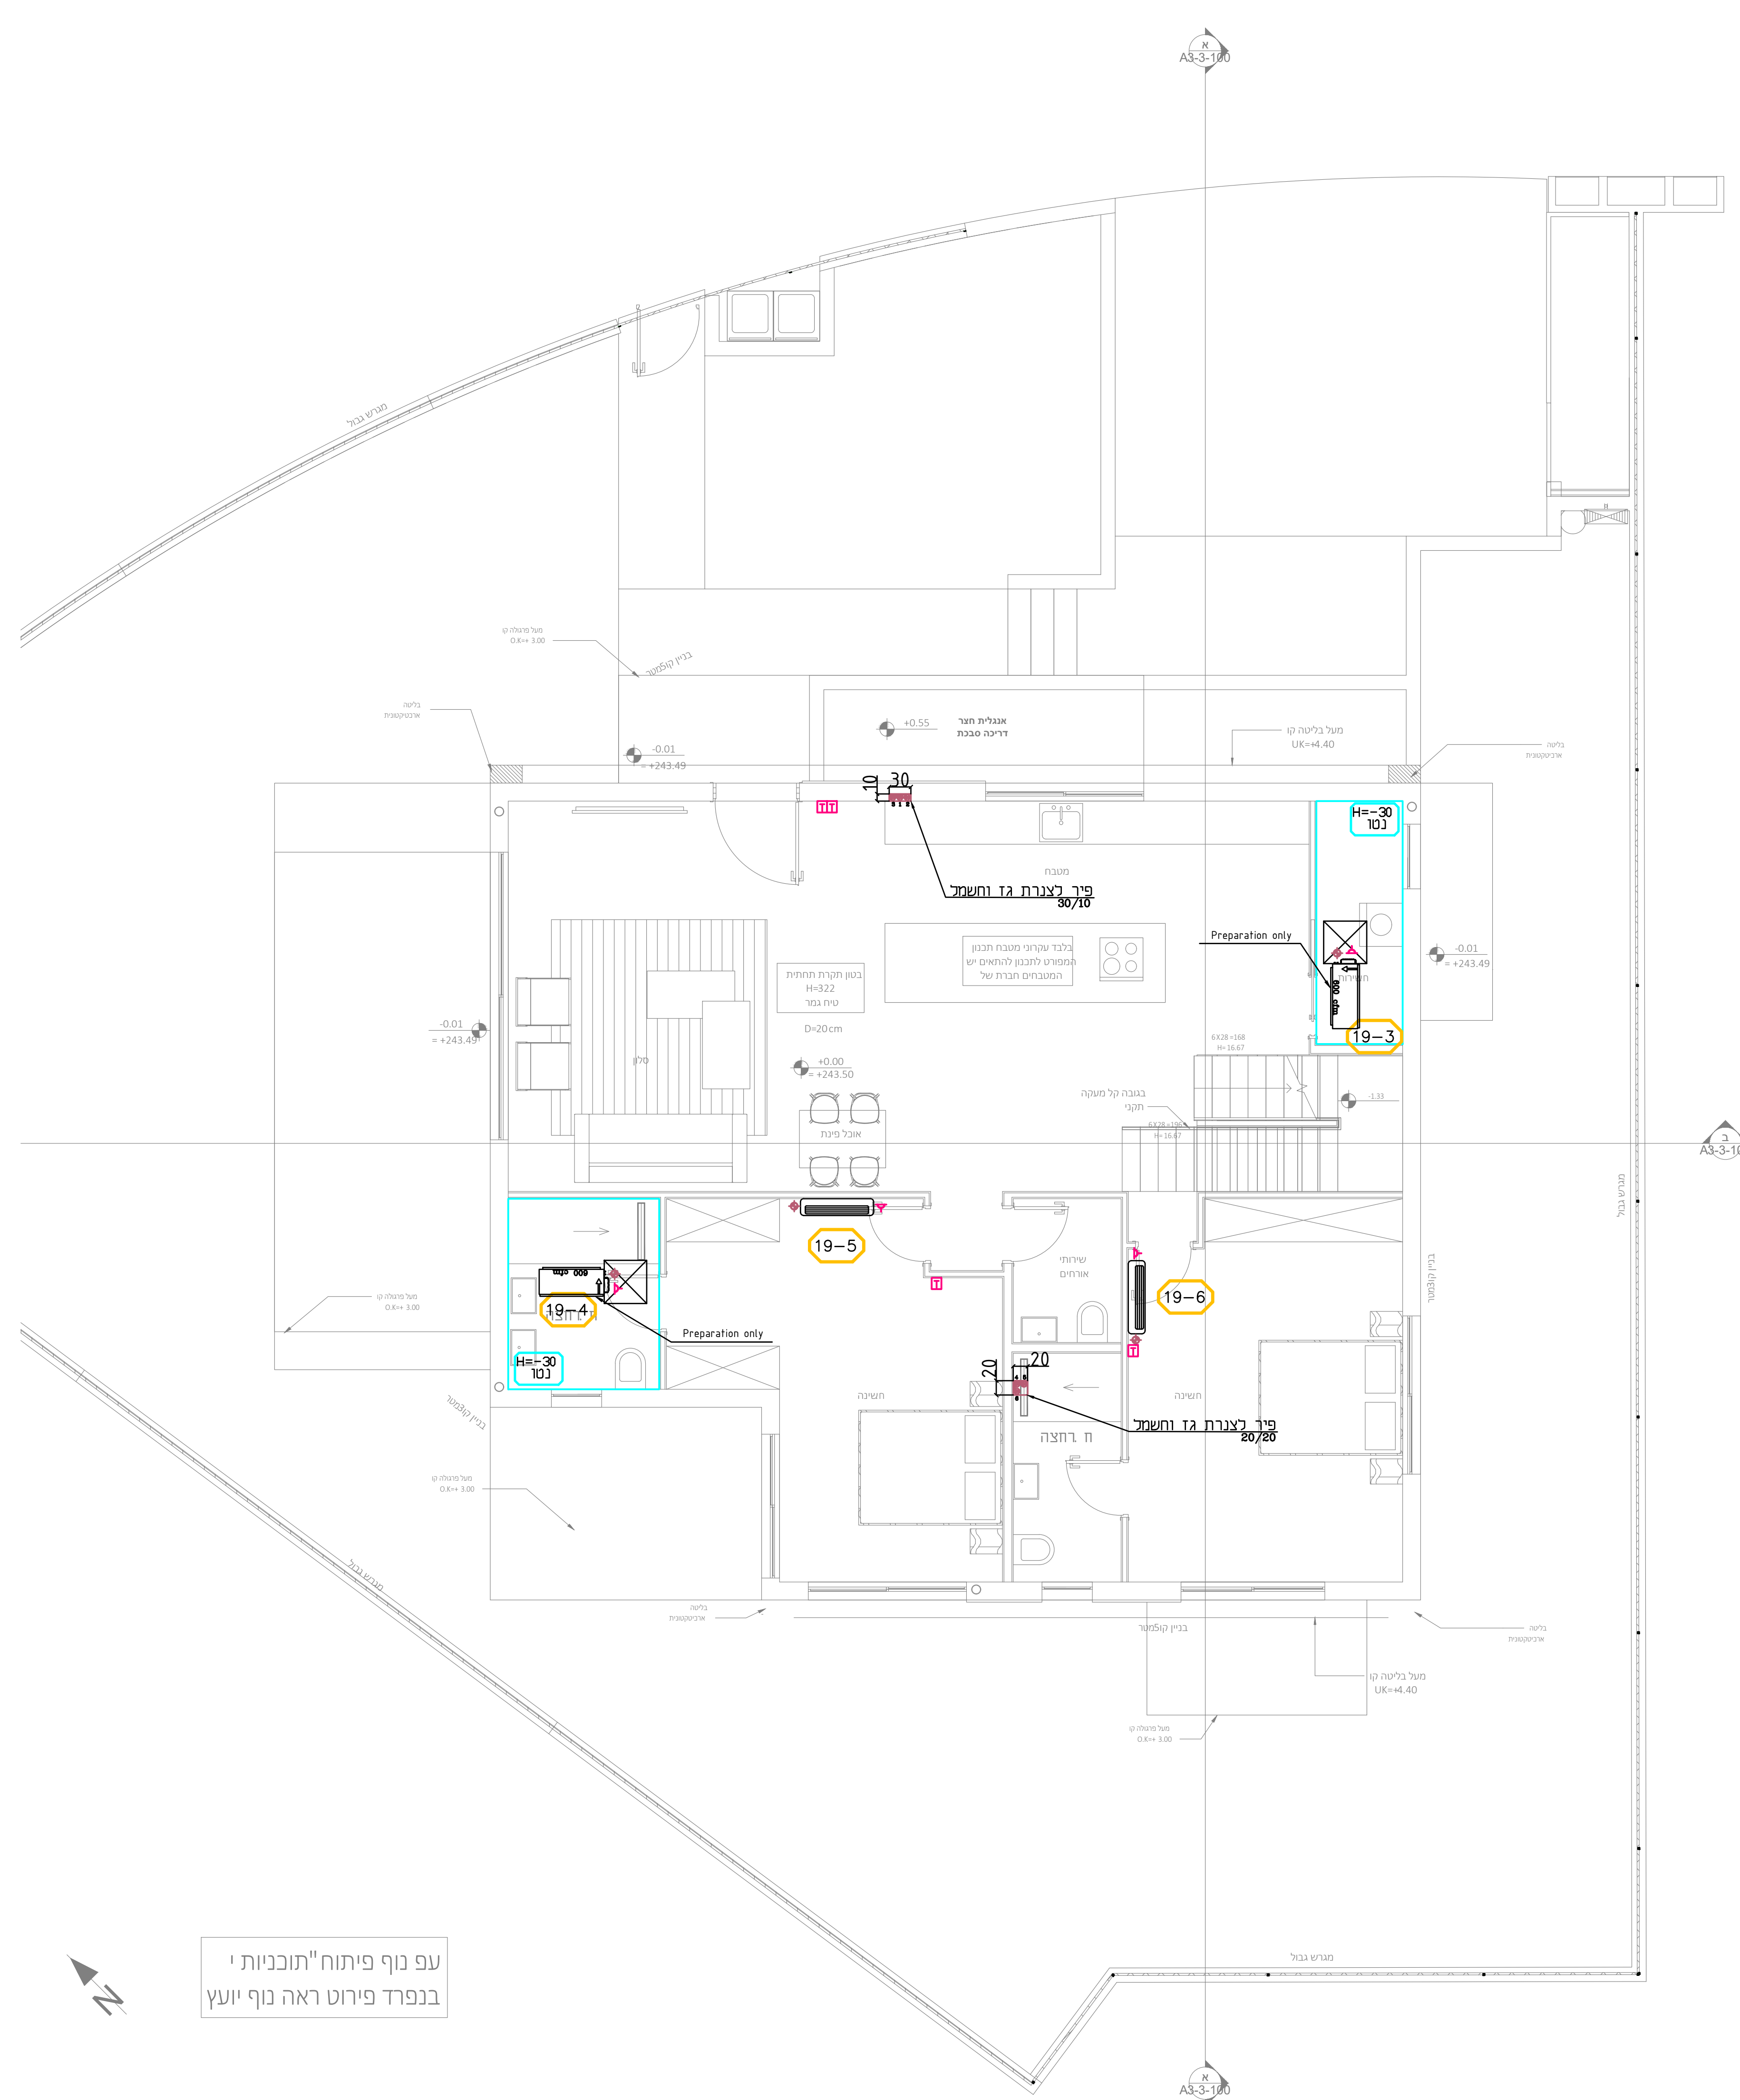

עפ נוק פיתוח "תוכניות י
בנפרד פירוט ראה נוק יועץ

תפוצה	
אדירכל פנים	
אינסטיציה	
ביטחות אש	
אקוסטיקה	
חשש והאזרה	
קונסטרוקציה	
קמבר ראש	
ניחוי פרויקט	
קמח	
מדיניות	

מהדורה

תחנות כעיון	04.05.2025		
שנתיים:		תאריך:	

המבצע אחראי למידות ולהתאמתן למציאות
בבכל מקרה של אי התאמה, סתירה או טעות
עליו להודיע למתכנן לפני התקדמותו בביצוע!
אין לקבוע מידות על סמך מדידה בשרטוט.
אין לעשות כל שימוש בתוכנית זו
או ברעיונות הגלומים בה ללא אישור בכתב
מאת המתכנן.


הערת

1. כל התעלות מחוץ למבנה יבודרו
בבירוד אקוסטי בעובי 2"
מידות התעלות הן מידות פח
2. תעלות מזון בחור המבנה יבודרו
בבירוד אקוסטי פחמי 1"
מידות התעלות הן מידות פח
3. תעלות אוויר צח יבודרו
בבירוד טרמי 1"
מידות התעלות הן מידות פח
4. יש לאטום במסילקון את פינות החיבור
של תעלות מזון אוויר לפני כיפוף
החפים המתחברים

מקרא

- [illegible]

מקרא צבעים בתכנית

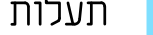- | | |
|--------------------------|---|
| תעלות ותריסי אוויר חוזר |  |
| תעלות ותריסי אספקת אוויר |  |
| תעלות ותריסי אוויר צח |  |
| תעלות ותריסי יניקת אוויר |  |
| תעלות ותריסי שיחרור עשן |  |
| צנרת גז וחשמל |  |
| סימון מעגלי מיזוג אוויר |  |

191	בני מקדושים צמודי קרקע יפיה אפי' ענשה בנה 19
תנ דרומם	הדרומים
1:50	חזו אודי אוזודור-הנעת בלבד
מנח	מנח
04.05.2025	מנח מרתף וקומה
האיר מנח	מנח
1	מנח
מנח	מנח
○	○
מנח	מנח
04.05.2025	04.05.2025
מנח	מנח