
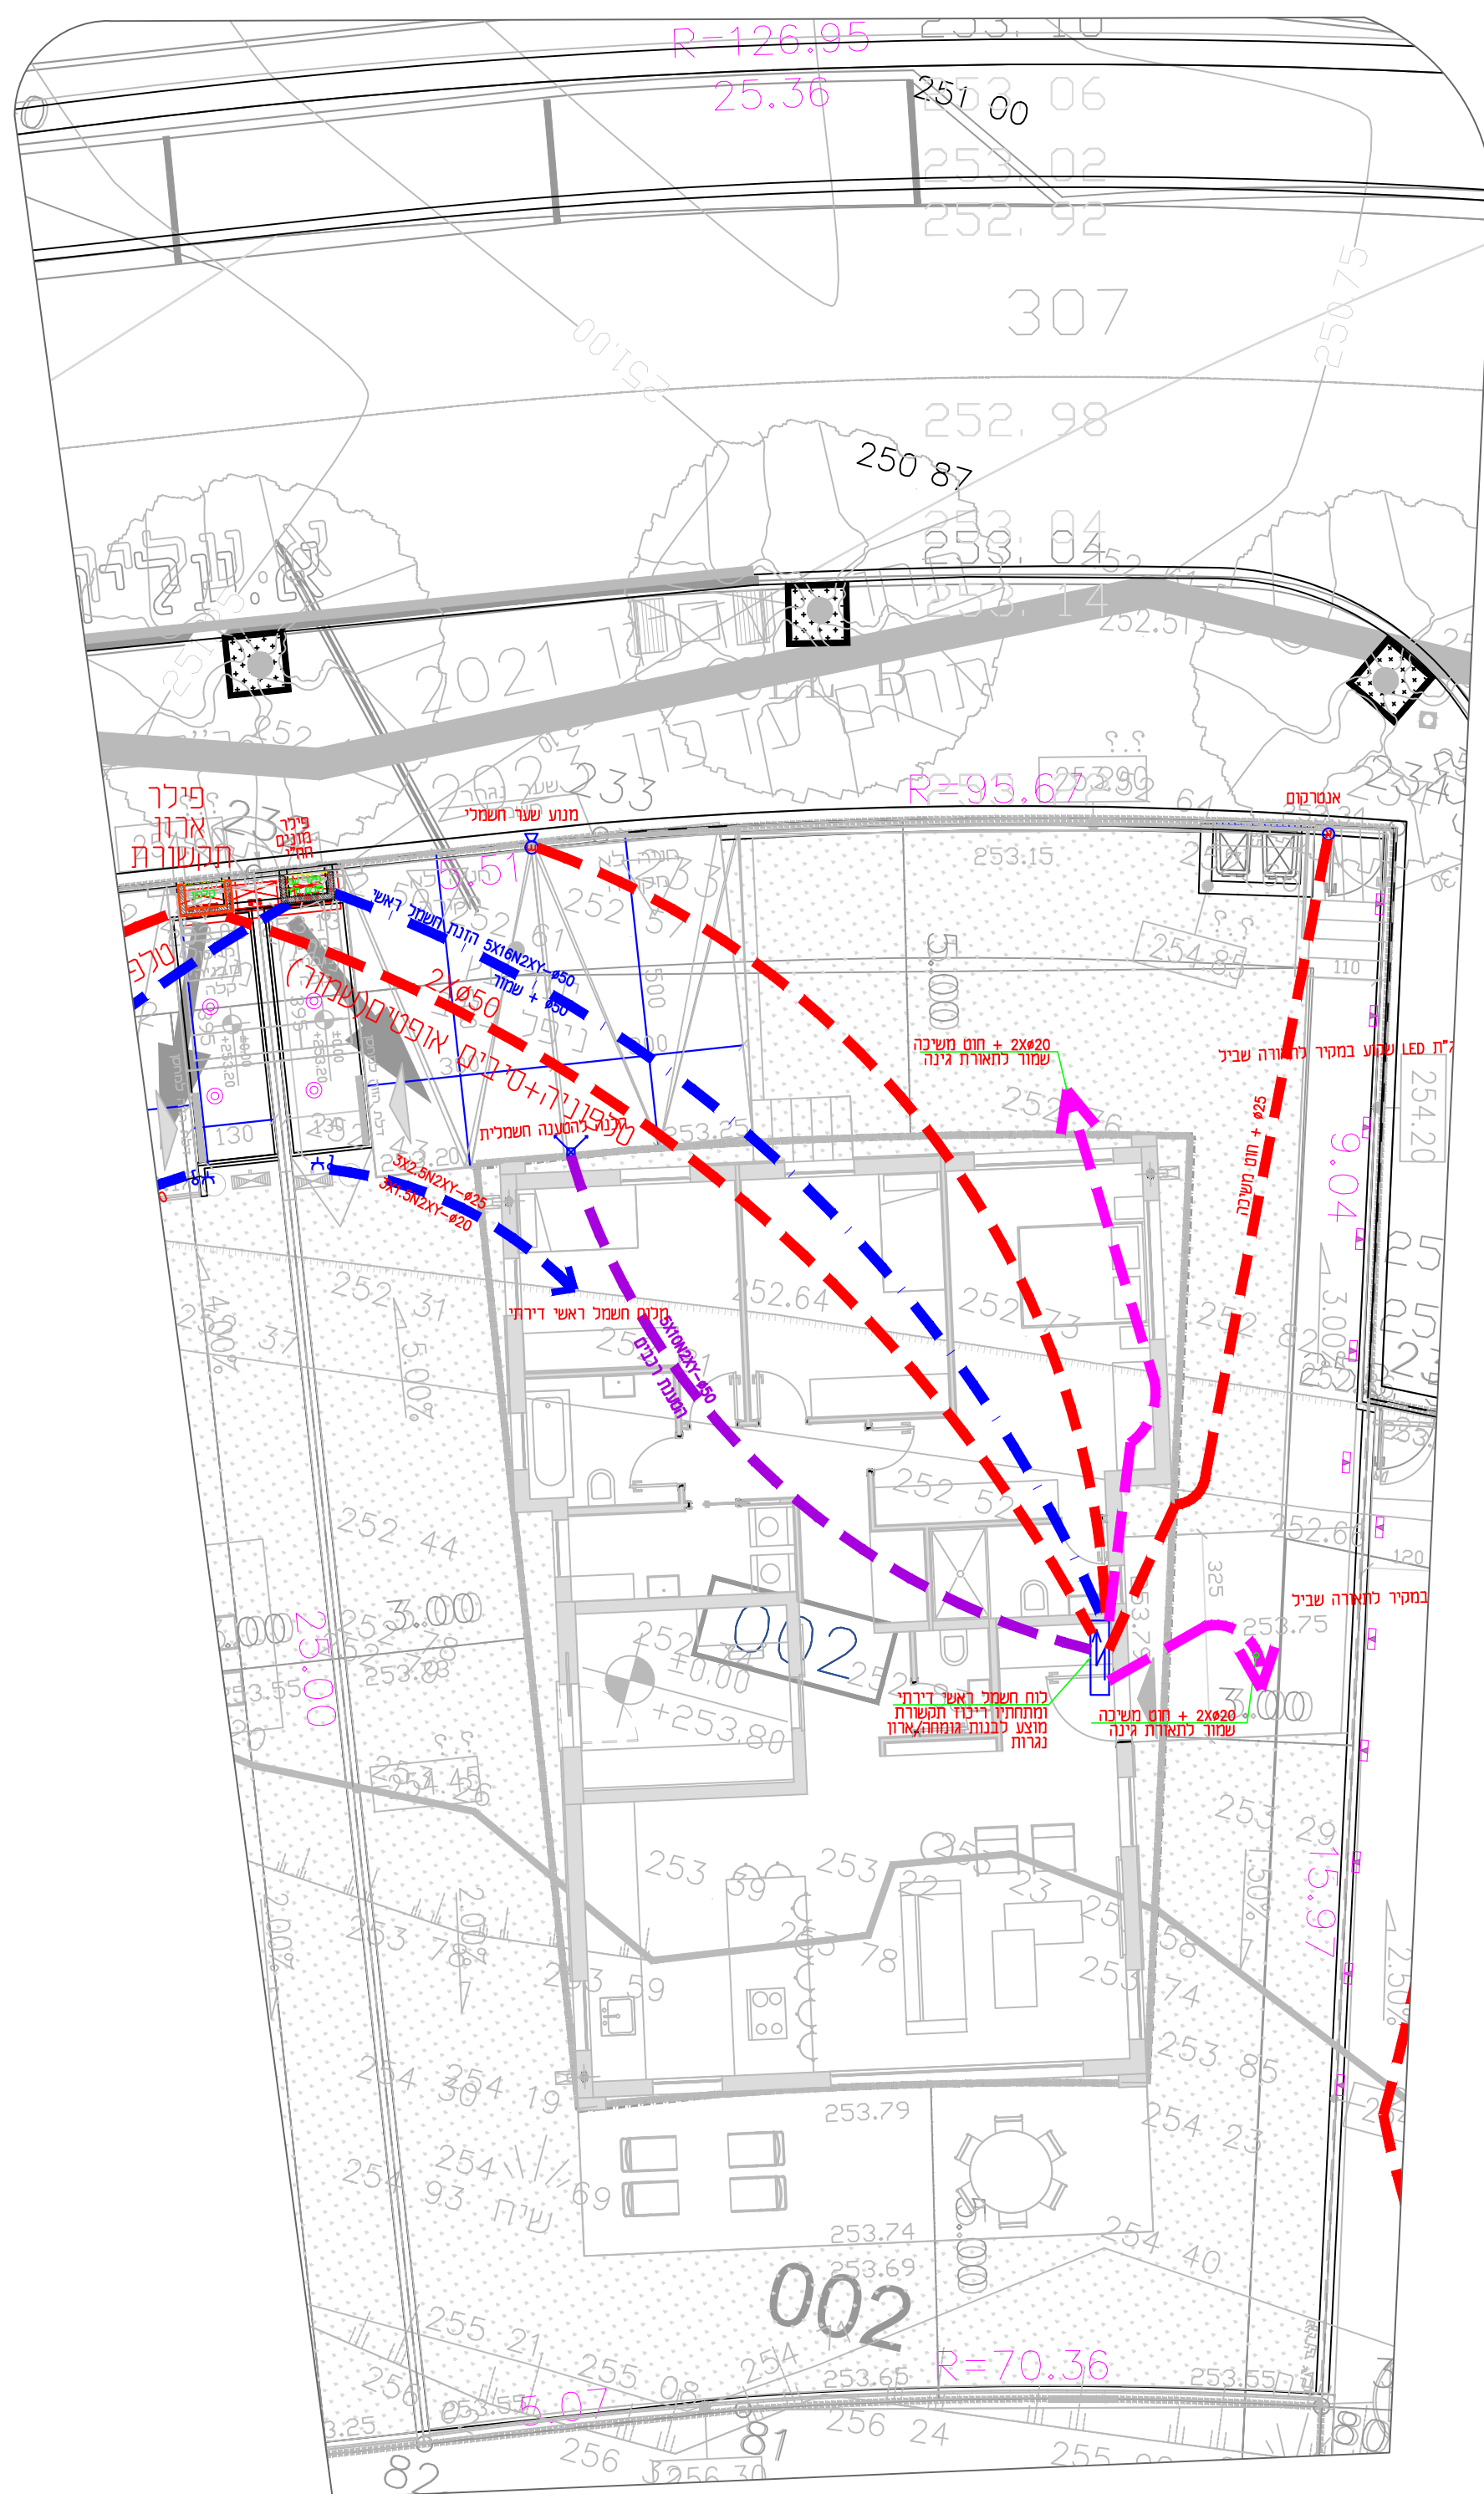


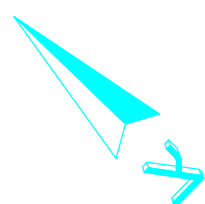

תכנית פיתוח-מגרש 2

קנ"ח 1:100

[illegible][illegible]

עודכן ע"י: _____ רחל

א.בסיס
הנדסת חשמל בע"מ
משרד: יד החוצים 16, ירושלים 93420
טל: 074-7021015 נייד: 050-6550484
קדם: 077-5131015 ר"א: office@ebasis.co.il

שם הפרויקט:

נופיה-אלפי מנשה

שם הגיליון:

תוכנית פיתוח מגרש 2

○ ● ○ ○ לביצוע למכרז לאישור לעיון				קנה מידה: 1:100	
File: מס' קובץ: 675P.dwg				Date: תאריך: 17.06.2024	
אשר: איתן		שרטט: אילה		תכנן: איתן	
מס' הפרויקט: 675		מס' הגליון: P2		מס' עדכון: 0	

תאריך	מס' שינויים	עודכן ע"י: ליאל
19.09.2024	1	עדכון מעגלים
26.11.24	2	עדכון תכנית
8.12.24	3	עדכון תכנית
12.12.24	4	עדכון תכנית
12.2.25	5	עדכון תוכנית לפי שינויי דיירים
8.5.25	6	עדכון תכנית
3.6.25	7	הסמעת מ"א
17.6.25	8	עדכון מעגלים והתאמה כלוח
23.6.25	9	עדכון מעגלים ומפסקים
17.9.25	10	עדכון תכנית

מס'	שינויים	תאריך
1	עדכון מעגלים	19.09.2024
2	עדכון תכנית	26.11.24
3	עדכון תכנית	8.12.24
4	עדכון תכנית	12.12.24
5	עדכון תוכנית לפי שינויי דיירים	12.2.25
6	עדכון תכנית	8.5.25
7	הסמעת מ"א	3.6.25
8	עדכון מעגלים והתאמה כלוח	17.6.25
9	עדכון מעגלים ומפסקים	23.6.25
10	עדכון תכנית	17.9.25

עודכן ע"י: ליאל

תאריך	מס' שינויים	עודכן ע"י: ליאל
19.09.2024	1	עדכון מעגלים
26.11.24	2	עדכון תכנית
8.12.24	3	עדכון תכנית
12.12.24	4	עדכון תכנית
12.2.25	5	עדכון תוכנית לפי שינויי דיירים
8.5.25	6	עדכון תכנית
3.6.25	7	הסמעת מ"א
17.6.25	8	עדכון מעגלים והתאמה כלוח
23.6.25	9	עדכון מעגלים ומפסקים
17.9.25	10	עדכון תכנית

הערות:

- כל הגברים בתכנית הוגם למרכז אביוז אלא אם צוין במפורש אחרת
- מיקום סופי לנקודות תאורה ייקבע ע"פ תכנית עיצוב פנים תאורת חוץ- ע"פ יועץ פיתוח
- מיקום סופי לשקעי מיזוג עפ"י תוכנית יועץ מיזוג


- הערות: מיקום סופי לנקודות תאורה ייקבע ע"פ תכנית עיצוב פנים תאורת חוץ- ע"פ יועץ פיתוח
- במידה והוחלט על הכנות לבית חכם: בהכנה לבית חכם ולדלת חכמה יש להשחיל חוט ס כחול נוסף בכל מפסק הדדקה התכנון עצמו יעשה ע"י ספק בית חכם
- הכנות למיזוג אוויר,חימום תת רצפתי, מערכות באסורה, וחימום מים בחשמל יהיו עפ הנחיות יועץ לכל תחום
- יש לקרוא תכנית זו יחד עם תכנית אדריכלות נמקרא בנזקים אדריכלות

שם הפרויקט:	
נופיה-אלפי מנשה	שם הגיליון:
מגרש 2	תוכנית חשמל
קנה מידה: 1:50	קנה מידה:
תאריך: 15.08.2024	תאריך:
File: 675-2.dwg	מס' קובץ:
תכנון: איתן	שרטט: איתן
מס' עדכון: 9	מס' הגיליון: E
מס' הפרויקט: 675	


לוח	תחשיב ותקשורת	תפוסות	תאורה ותכנון אש
לוח חשמל שטח 16A בודד H=60 זוג שקעי בדפוס 16A אלא אם צוין אחרת זוג שקעים בדפוס 16A אלא אם צוין אחרת מכני שקעים מופסק סיום באביוז 2xN2 "ניסטר" בארץ תמורת תחתית לוח חשמל שטח חד פאזי מוגו מים H=60 אלא אם צוין אחרת שטח יחידת מ"א H=220 16A זוג שקעים בדפוס 16A אלא אם צוין אחרת מיקום סופי לפי תוכנית מיזוג וחבויאם מול אוריינז שטח תחת פאזי לכדיים וחבויאם מול אוריינז נקודת מספון מלאה-צנרת, כבידה ושטח מספון H=60 Box CIMA הכולל: 4 שקעי שרות+2 תמשתורת על חוט משינה מריכוז תמשתורת דירתי נקודת מליידה מושעת+צינור שטוח H=60 נקודת תמשתורת H=60, צינור #25 כלל תמשתורת אופסי תחת חתך מותקן בצינור #25 סיום בית חתך אופסי LC/APC לפי דרישות ח"י 1-1801 עם ראשים מוכנים מראש לוחיתנה בארץ תמשתורת דירתי ובסלול על חוט משינה מריכוז תמשתורת דירתי מונע חשמלי H=200 הכנה לחירמוטטס מוג- צינור 20 כלכל תמרה והמוטטס ויחום תת רצפתי- ביצוע לפי הנחיות ספק שקעי לונגו ויחום חשמלי 10 סמ מעל פתח דלת ביילר הכנה לונגסה סיום בשטח	מפסק מאור בודד H=90 מפסק כפול H=90 מפסק מאור מותקן/מציב H=90 לוחץ פטמון דלת H=90 מנתח מאור 2x16A / 3x16A מפסק דו סטבי מאור לונגו ויחום חשמלי H=160 מפסק מנתח עבוד ויחום מים בגז בגל מפסק ומהר/מהר קורס חשמלי 5 סמ מפל מפסק ואורה לפי פוס H=180 פנל צפיה (מוניטור) +לוחץ פתיחה דלת H=120 חארתת חרום חד תכניתית 3w LED גלאי עשן בתמרה נקודת מאור בתמרה גל"ת פנים תמרת' מוגו מים גל"ת LED עגול שטח בתמרה גל"ת LED עגול קורי גובה H=220 גל"ת פנים קורי לנעורת יכלה H=120 גל"ת פנים/חץ קורי מוגו מים H=240, H=220 במותקן ל"ת קורי נמוך תמרתת התמאצות מדרגות/שירותים, h=15 מרצפה/ ממום מדרגה גל"ת מכני #65 להחנהה על פרגולה מאוריר להחנהה בחוץ פטמון דלת 220v (גוגנ) תמנהה מעל דלת כניסה הכנה מכלקה אבסורה, צינור 25 וחום משינה מאוריר תמשתורת דירתי	מפסק מאור בודד H=90 מפסק כפול H=90 מפסק מאור מותקן/מציב H=90 לוחץ פטמון דלת H=90 מנתח מאור 2x16A / 3x16A מפסק דו סטבי מאור לונגו ויחום חשמלי H=160 מפסק מנתח עבוד ויחום מים בגז בגל מפסק ומהר/מהר קורס חשמלי 5 סמ מפל מפסק ואורה לפי פוס H=180 פנל צפיה (מוניטור) +לוחץ פתיחה דלת H=120 חארתת חרום חד תכניתית 3w LED גלאי עשן בתמרה נקודת מאור בתמרה גל"ת פנים תמרת' מוגו מים גל"ת LED עגול שטח בתמרה גל"ת LED עגול קורי גובה H=220 גל"ת פנים קורי לנעורת יכלה H=120 גל"ת פנים/חץ קורי מוגו מים H=240, H=220 במותקן ל"ת קורי נמוך תמרתת התמאצות מדרגות/שירותים, h=15 מרצפה/ ממום מדרגה גל"ת מכני #65 להחנהה על פרגולה מאוריר להחנהה בחוץ פטמון דלת 220v (גוגנ) תמנהה מעל דלת כניסה הכנה מכלקה אבסורה, צינור 25 וחום משינה מאוריר תמשתורת דירתי	מפסק מאור בודד H=90 מפסק כפול H=90 מפסק מאור מותקן/מציב H=90 לוחץ פטמון דלת H=90 מנתח מאור 2x16A / 3x16A מפסק דו סטבי מאור לונגו ויחום חשמלי H=160 מפסק מנתח עבוד ויחום מים בגז בגל מפסק ומהר/מהר קורס חשמלי 5 סמ מפל מפסק ואורה לפי פוס H=180 פנל צפיה (מוניטור) +לוחץ פתיחה דלת H=120 חארתת חרום חד תכניתית 3w LED גלאי עשן בתמרה נקודת מאור בתמרה גל"ת פנים תמרת' מוגו מים גל"ת LED עגול שטח בתמרה גל"ת LED עגול קורי גובה H=220 גל"ת פנים קורי לנעורת יכלה H=120 גל"ת פנים/חץ קורי מוגו מים H=240, H=220 במותקן ל"ת קורי נמוך תמרתת התמאצות מדרגות/שירותים, h=15 מרצפה/ ממום מדרגה גל"ת מכני #65 להחנהה על פרגולה מאוריר להחנהה בחוץ פטמון דלת 220v (גוגנ) תמנהה מעל דלת כניסה הכנה מכלקה אבסורה, צינור 25 וחום משינה מאוריר תמשתורת דירתי

פרט לגברים של הדדקות, תאורה ותריסים:

מידת לוח חשמל ראשי וארונות תקשורת


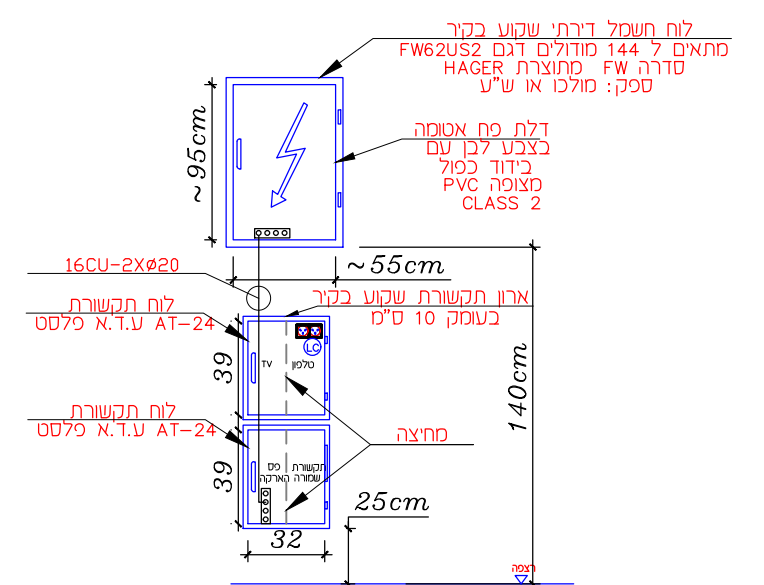


קומת קרקע

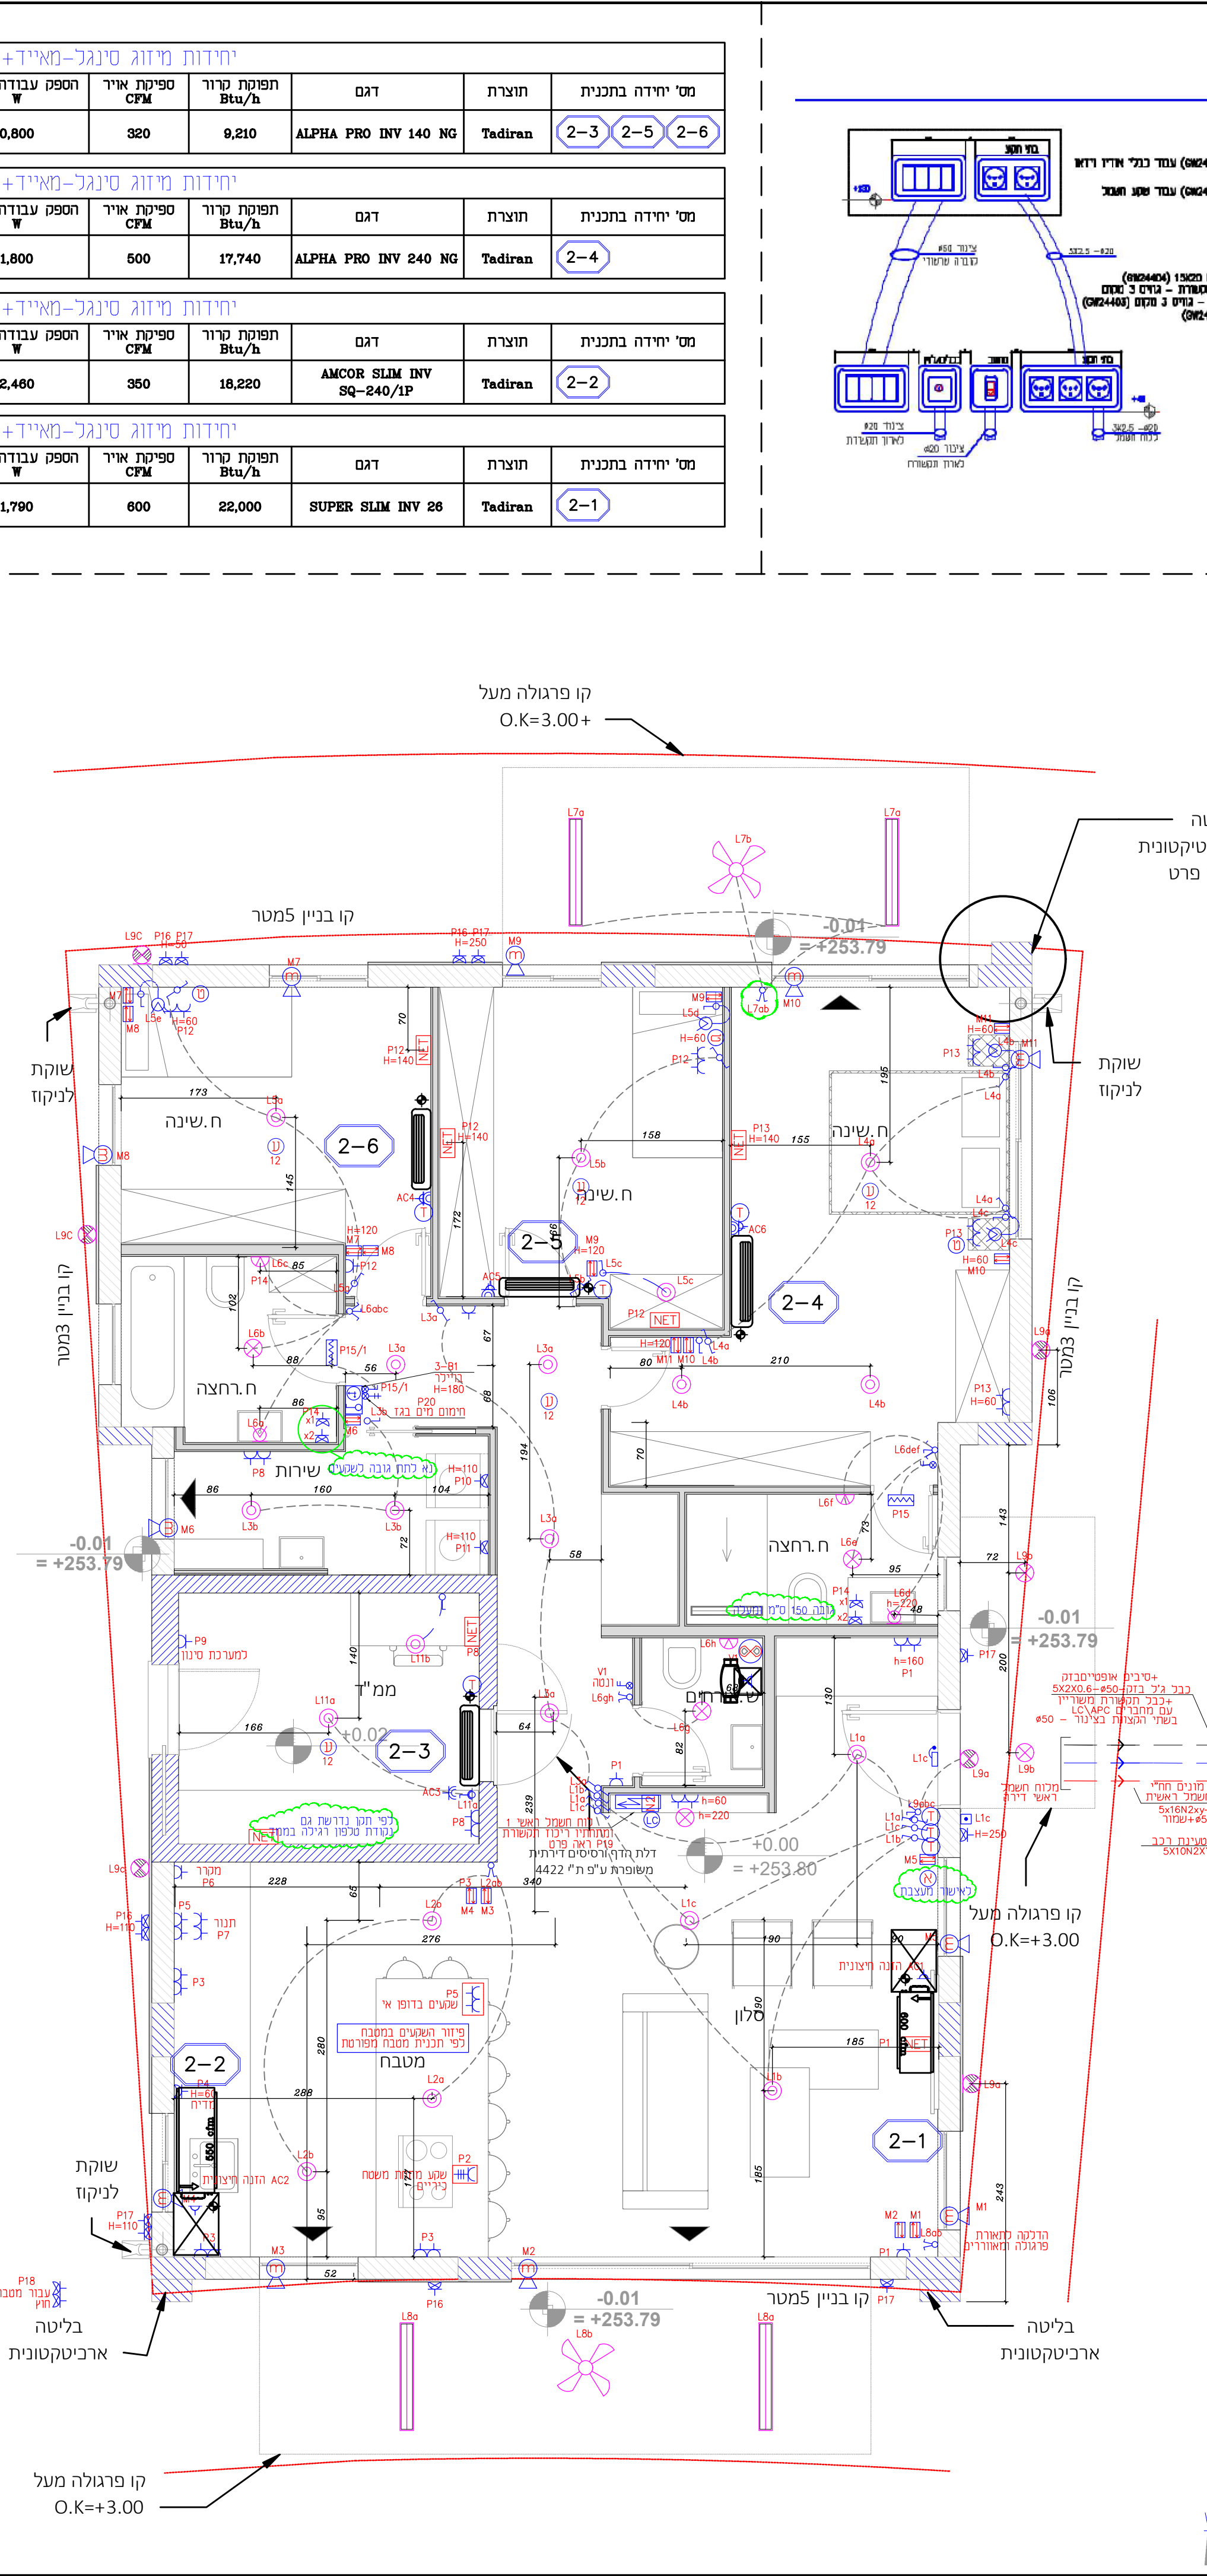


קומה גג

פרט ציאת צנרת חשמל כנגד לכילור וכד

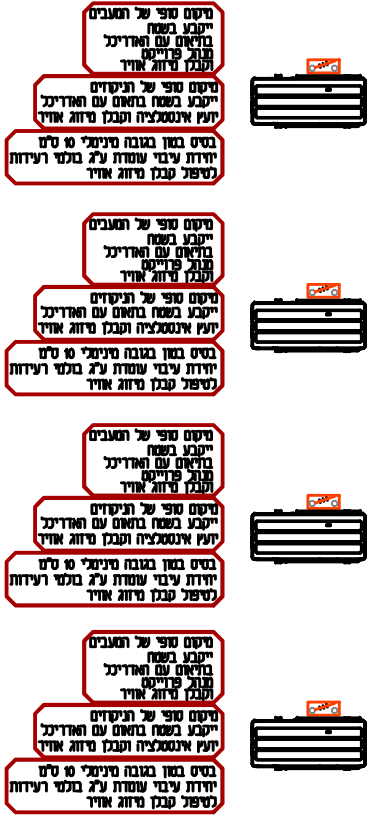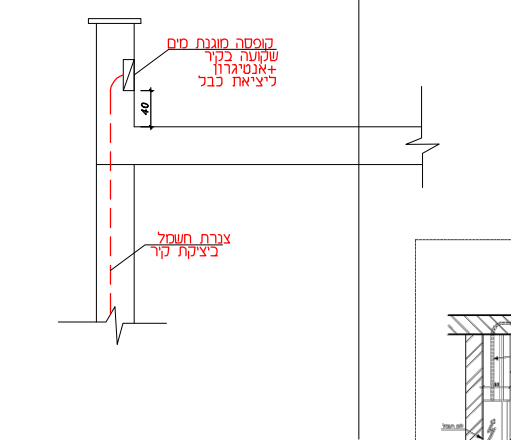

קו גבול פרגולה 40%אל תוך המרווח

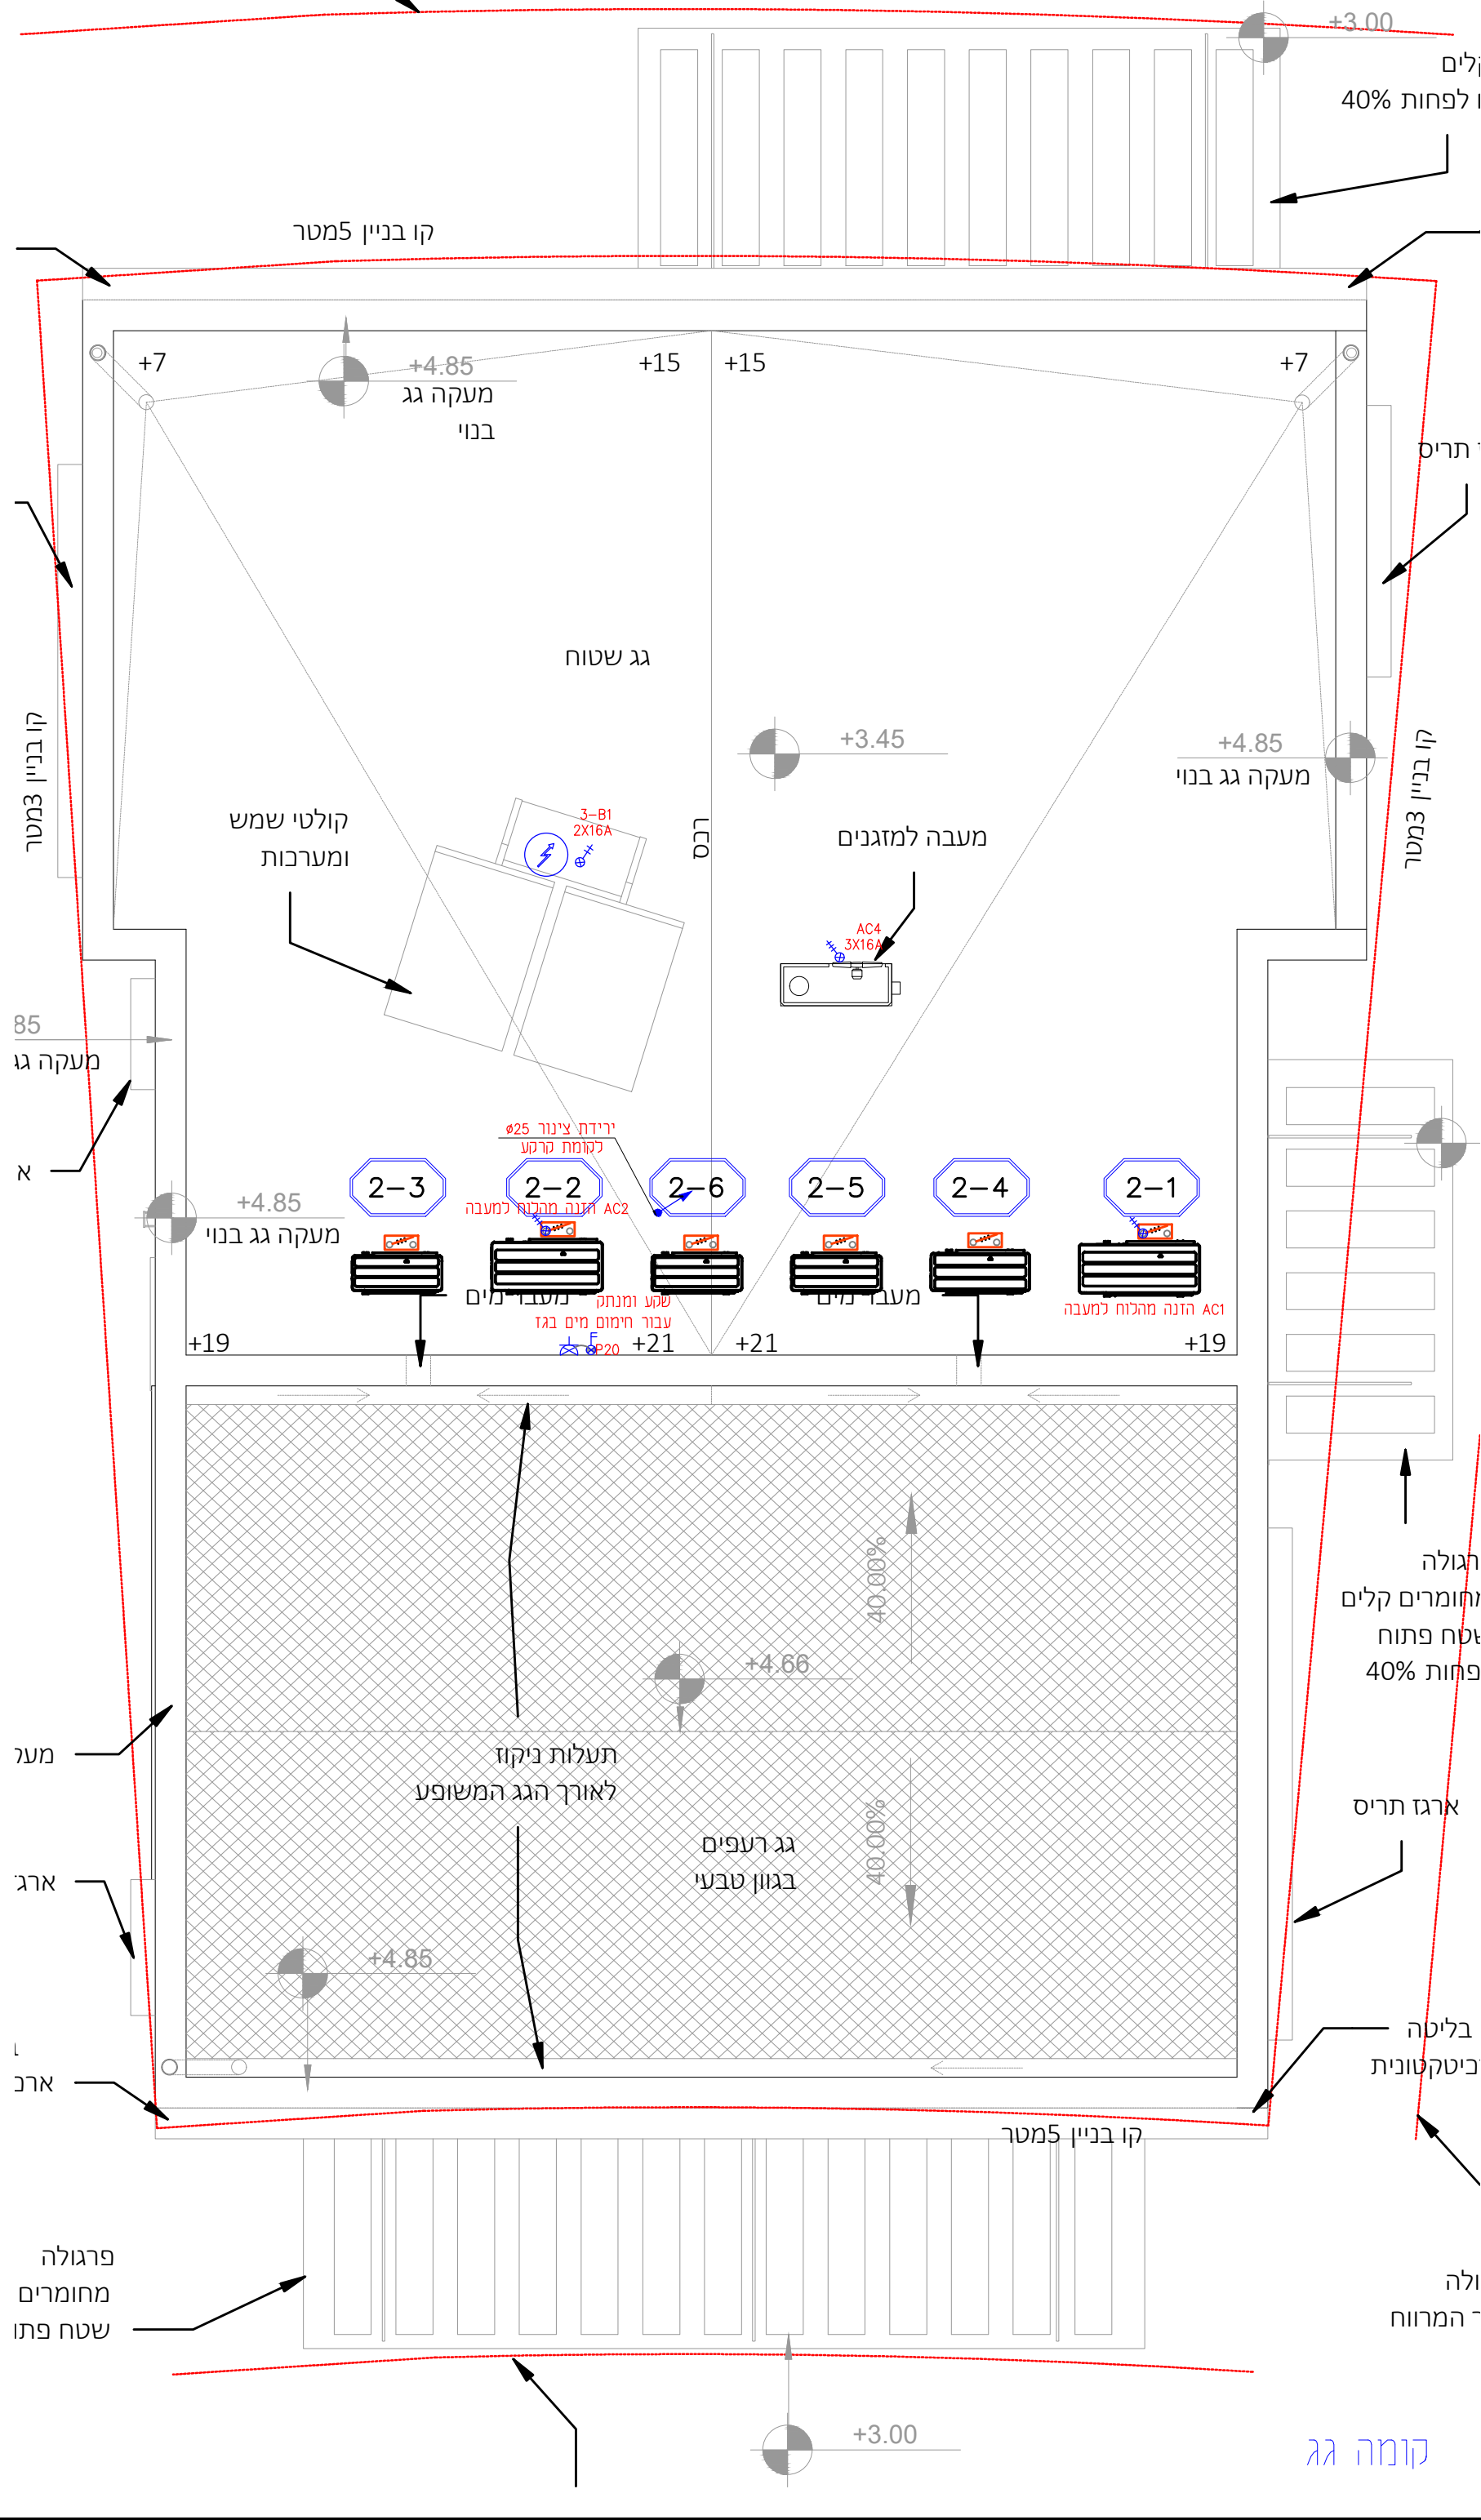

קומה גג