


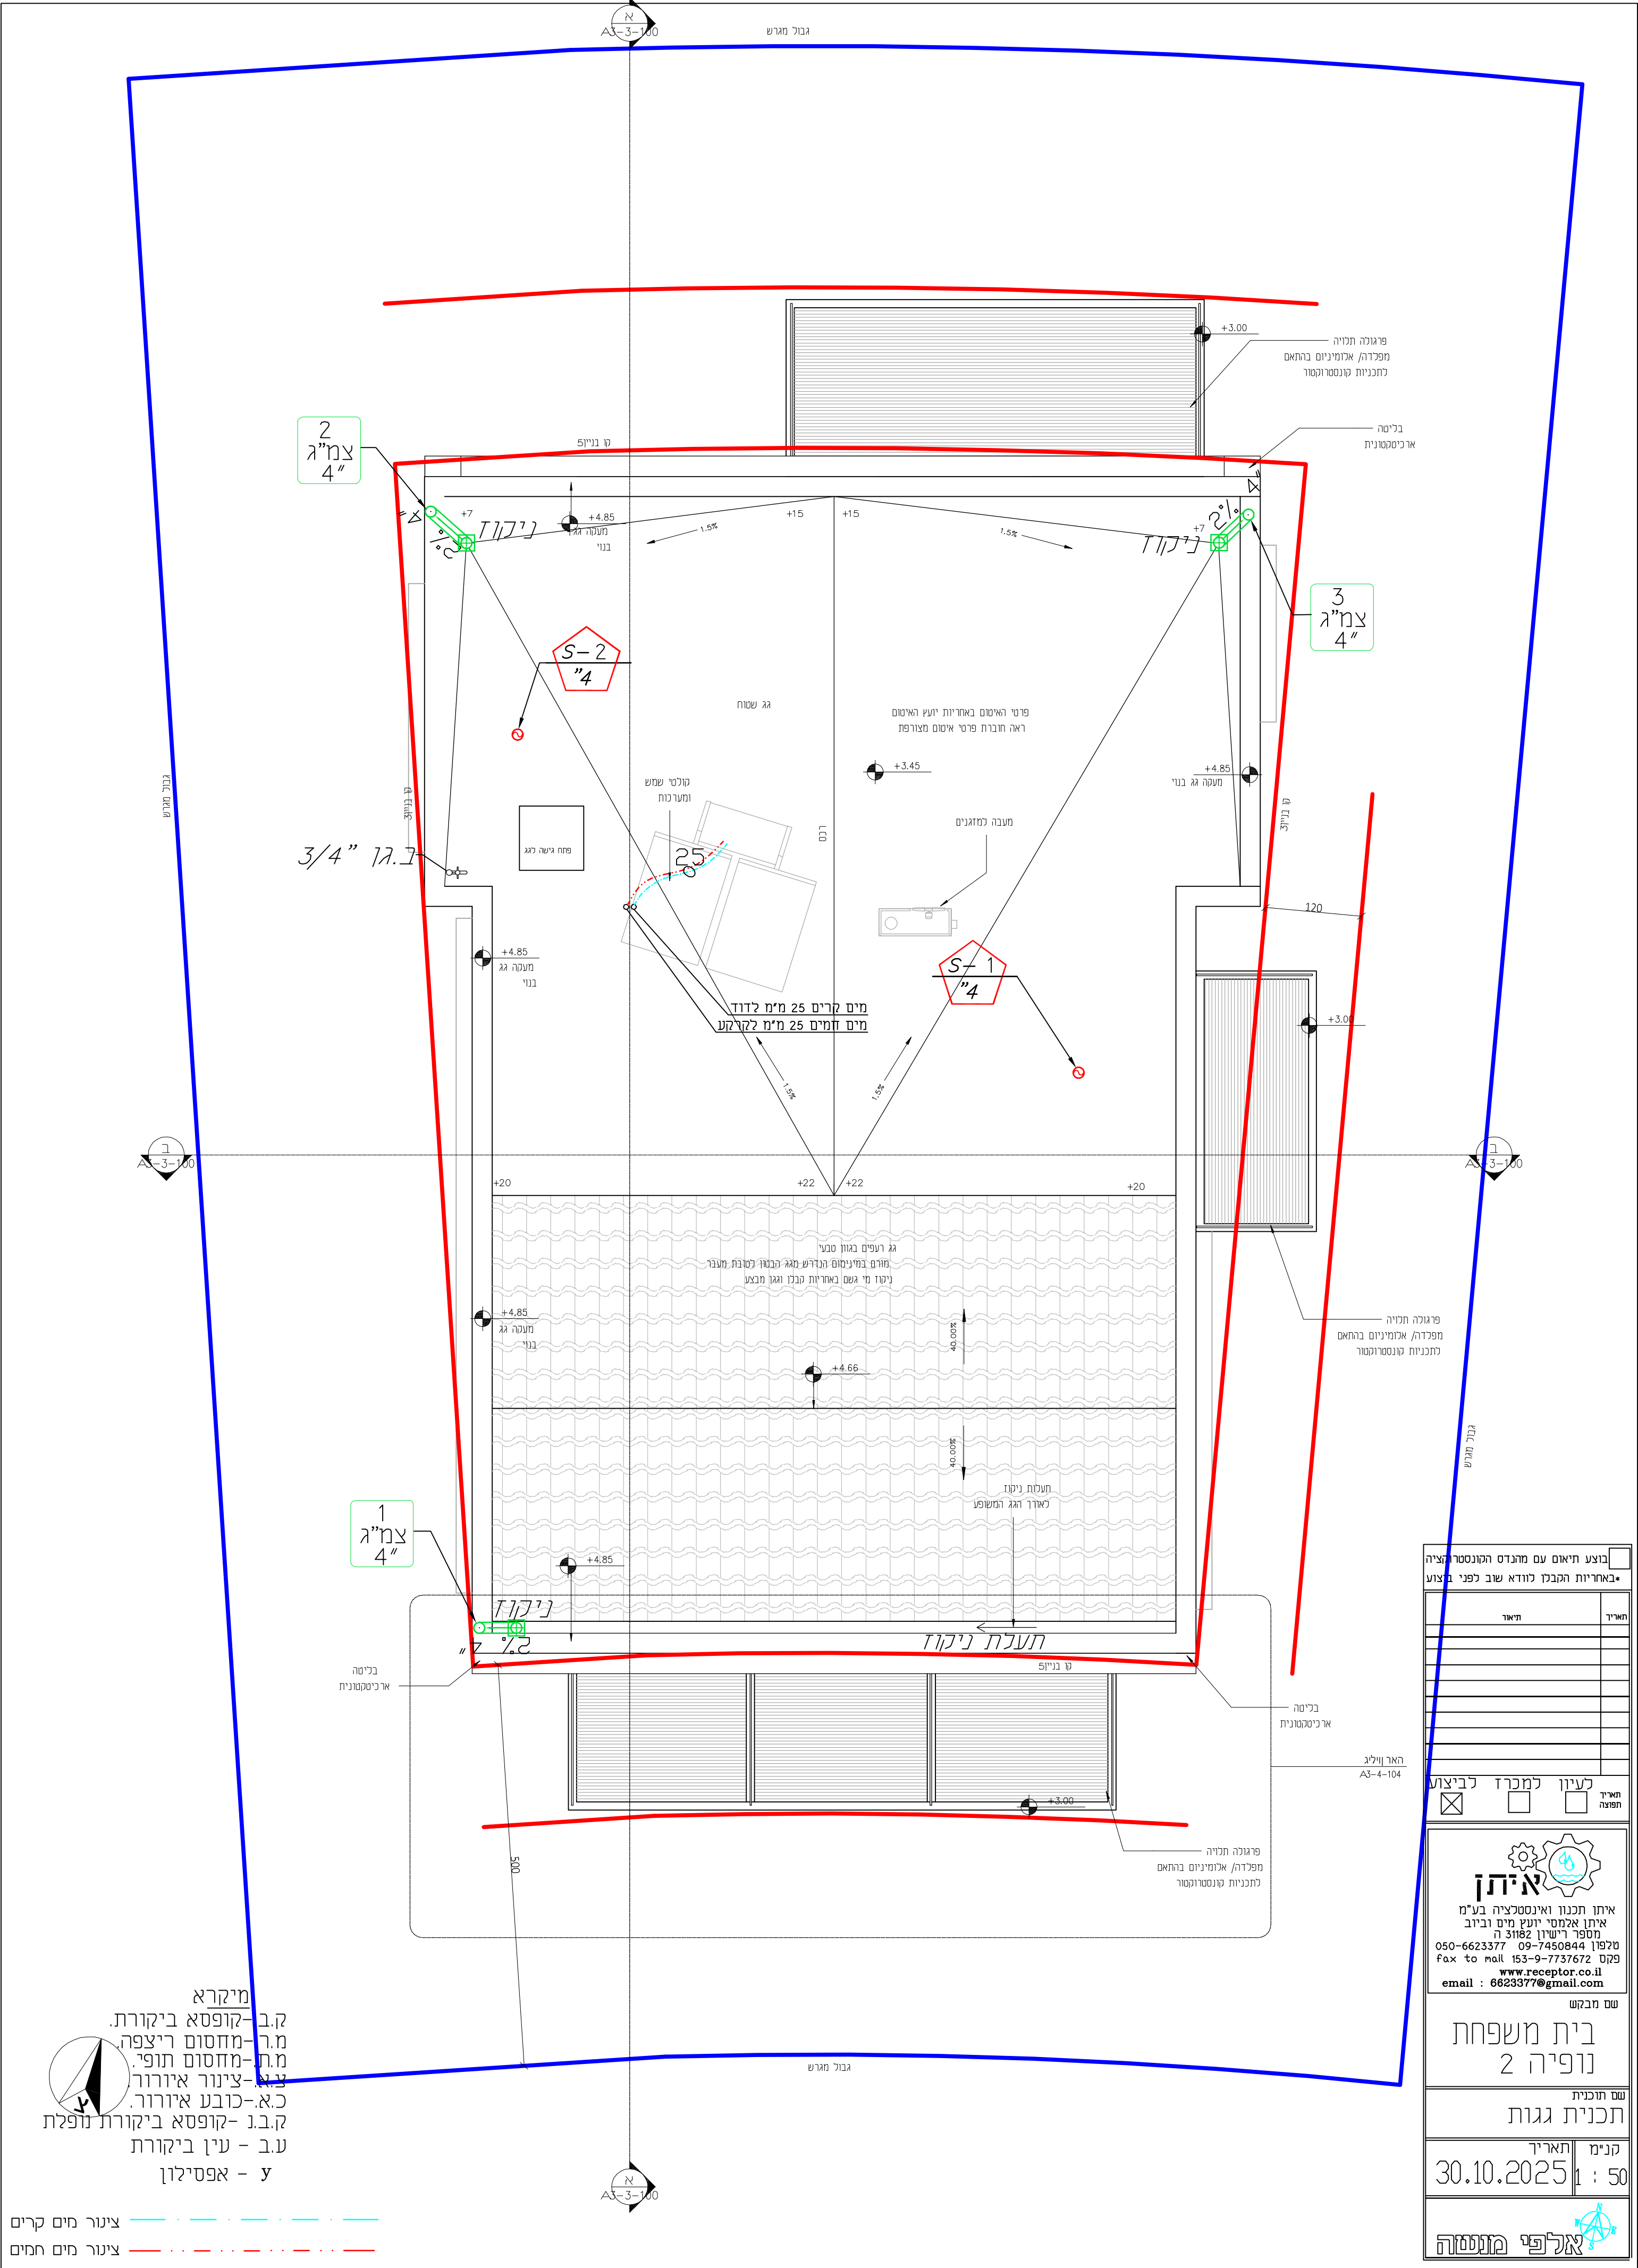

בוצע תיאום עם מהנדס הקונסטרוקציה

באחריות הקבלן לוודא שוב לפני ביצוע

תאריך	תיאור

האר וויליג
A3-4-104

לביצוע

☒

למכרז

☐

לעיון

☐

תאריך תפוצה

איתון
איתון תכנון ואינסטלציה בע"מ
איתון אלמסי יועץ מים וביוב
מספר רישיון 31082 ה
טלפון 09-7450844 050-6623377
Fax to mail 153-9-7737672
www.receptor.co.il
email : 6623377@gmail.com

שם מבקש

בית משפחת
נופיה 2

שם תוכנית

תכנית גגות

קני"מ

תאריך

1 : 50
30.10.2025

אלפי מנשה

מיקרא
ק.ב. - קופסת ביקורת.
מ.ר. - מחסום ריצפה.
מ.ת. - מחסום תופי.
צ.א. - צינור איורור.
כ.א. - כובע איורור.
ק.ב.נ. - קופסת ביקורת נופלת
ע.ב. - עין ביקורת
ע. - אפסילון

צינור מים קרים
צינור מים חמים

