


מתכננים:

ניהול פרויקט
מהיסוד - בן סולומון
פיקוח
מהיסוד - בן סולומון
קונסטרוקציה
ערן שילר
מיזוג אוויר
אייל ארז מהנדסים ויועצים בע"מ
אינסטלציה
איתן אלמסי
חשמל
איתן בסיס
אלומיניום
נוף
נתי בלוקא
חשמל חכם
חימום תת רצפתי
איטום
צבי טל
אקוסטיקה
מעליות
קרקע וביסוס
דיה הנדסת קרקע וביסוס
רישוי

± 0.00 = +242.60
הערות: 1. תכנית זו יש לקרוא יחד עם תכנית הויטמים. 2. גובה אבסולוטי - ראו תכנית פיתוח. 3. המידות הן בין קירות הבניה ולא כולל פחים. 4. פיתוח השטח סביב הבנוה, כולל, מדרגות, נדרות, שנילים, ריצופים, שפעלים, גדרים, חניה וגן וראו תכנית פיתוח. 5. איסוס קירות ורצפות הבנוה כמתע עם הקרקע ובידוד תרמי לאורך העמודים והקורות וכל התקנות. כליות או עם סימני (גובה) - ראו תכנית קונסטרוקציה. 6. אף זמים יבוצע בכל מישור אופקי הבולם מהגבון. 7. ס"ח תרמי בממ"ד - ע"פ מפרט חומקיר, מאושר ע"י פיקוח העיר.
המבצע אחראי למידות : עליו לבקר ולבדוק את כל המידות בתכנית ובקטע הטבורה. במספר של שעות או אי התאמה בתכנית /או בבנוי, עליו להודיע על כך מיד לאדריכל בסרט המשיך בעבודתו. המבצע ישתמש אך ורק בתכנית שאושר לביצוע. המבצע יחזיק באחר, בכל של, של משרדו של תכנית. אין לקבוע מידות על ידי חדיה בשר מוס. התכנית היתה רכוש האדריכל ואין לשנות כל שימוש בה או ברעיונות הגלומים בה, אלא באישור בכתב מהאדריכל. מחדם /או יושע אשר שמו רשום בתכנית זו, נושא לכיד באחריות המקצועית והתקנית לתכנית. על המפקח והמכיל לודא התאמת התכנית האדריכלית "לביצוע" לתכנית ויתר, המכר והתכנית האושרות ע"י כל הגורמים הרשמיים. התכנית כוללת את כל האחריות והדג על ליום תוצאתה.

משרד קירות:

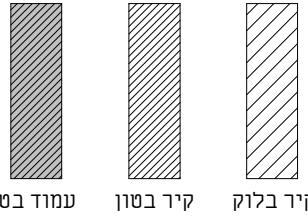

תאריך	תיאור	מהדורה
22.09.2025	מכרז	1

אדריכלות

שם המספר:	CLIENT NAME:
קבוצת רכישה נופיה	
שם הפרויקט:	PROJECT NAME:
נופיה - מגרש 20	
שם הגליון:	DRAWING NAME:
גליון שער	
מספר גליון:	SHEET NUMBER:
A3-1-100	
מהדורה:	EDITION:
SCALE:	קנה מידה:
STATUS:	סטוס
למכרז	
שורטס ע"י:	נבדק ע"י:
תאריך:	DATE:
22.09.25	




נוימן חיינר אדריכלים
מנכ"ל והנדס 2, בית חירות
09-9545642
office@nh-arch.com
www.nh-arch.com

זכיות ייצור / ע"פ הנחיות ע"ד

נופיה - מגרש 20

מס' גליון	שם גליון	מהדורה	תאריך הפצת המהדורה
-----------	----------	--------	--------------------


A3-1-100	גליון שער	1	22.09.2025
A3-1-101	תכנית קומת קרקע	1	22.09.2025
A3-1-102	תכנית גג	1	22.09.2025
A3-2-200	חזיתות 1	1	22.09.2025
A3-2-201	חזיתות 2	1	22.09.2025
A3-3-100	חתכים	1	22.09.2025
A3-4-103	פרטים	1	22.09.2025
A3-4-104	פרטי פרגולה	1	22.09.2025
A3-6-1000	רשימת פתחים	1	22.09.2025

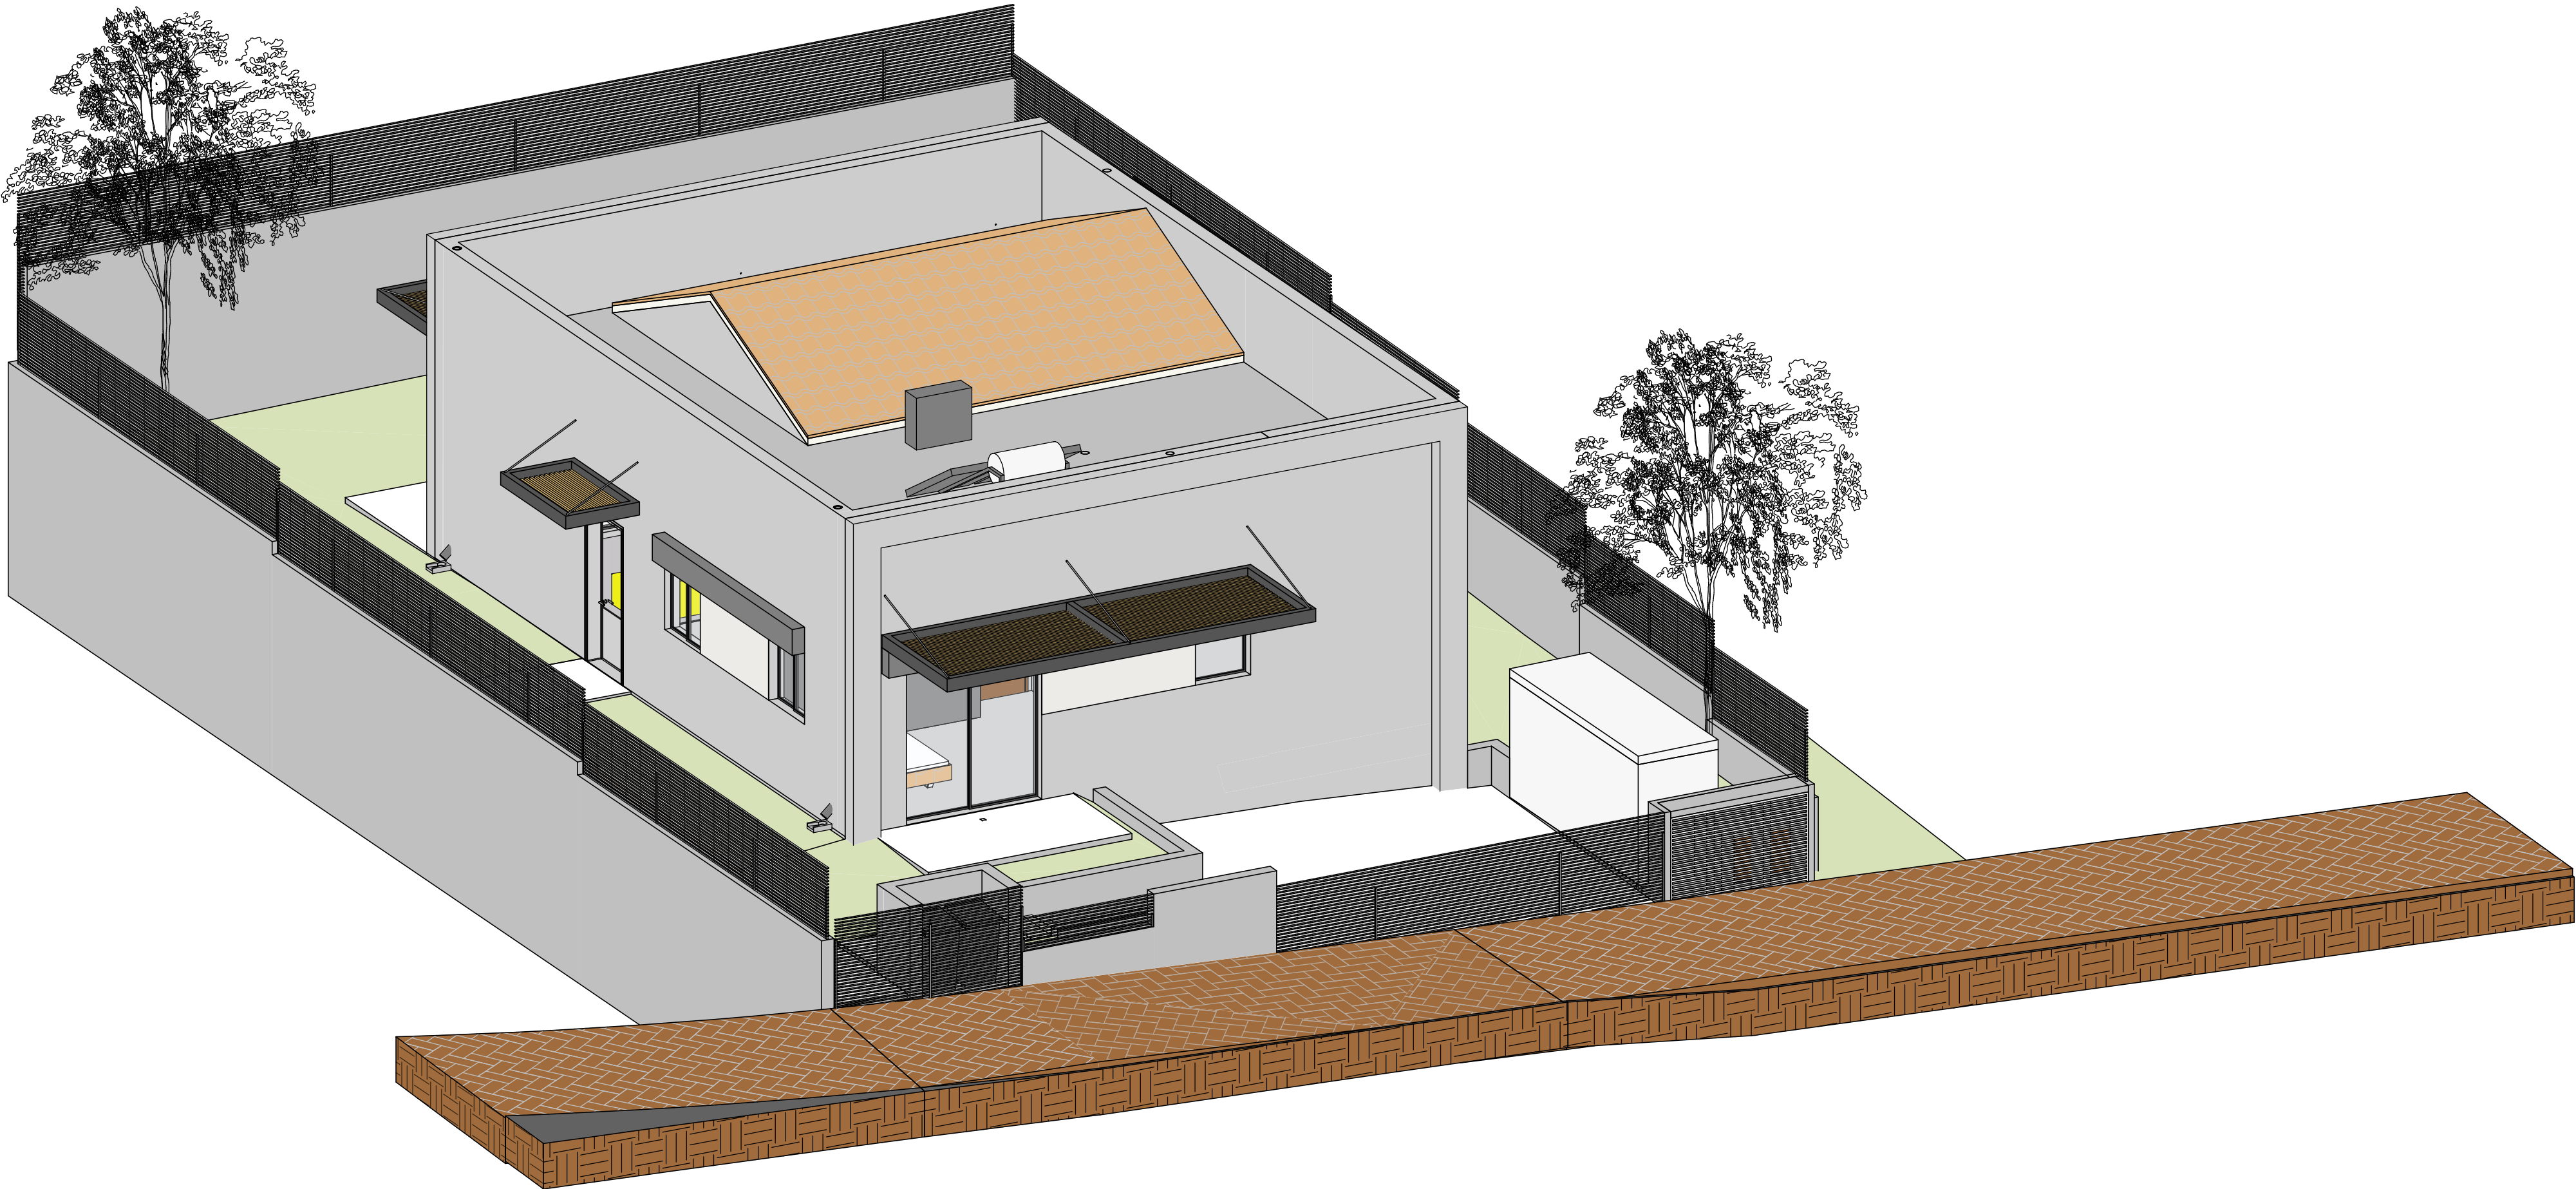

ניהול פרויקט
מהיסוד - בן סולומון
פיקוח
מהיסוד - בן סולומון
קונסטרוקציה
ערן שילר
מיזוג אוויר
אייל ארז מהנדסים ויועצים בע"מ
אינסטלציה
איתן אלמסי
חשמל
איתן בסיס
אלומיניום
בנף
נתי בלוקא
חשמל חכם
חימום תת רצפתי
איטום
צבי טל
אקוסטיקה
מעליות
קרקע וביסוס
דיה הנדסת קרקע וביסוס
רישוי

[illegible][illegible]

CLIENT NAME:	המחלקה הכלכלית
קבוצת רכישה נופיה	
PROJECT NAME:	הפרויקט
נופיה - מגרש 20	
DRAWING NAME:	סוג העיצוב
תכנית קומת קרקע	
SHEET NUMBER:	מספר גיליון
A3-1-101	

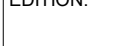SCALE:	קנה מידה:	EDITION:	חזרה:
1 : 50			
STATUS:	סטטוס		
למכר			
	בדוק ע"י:		דפוס ע"י:
DATE:	22.09.25		תאריך:


office@nh-arch.com
www.nh-arch.com

וימן חיינר אדריכלים
אורז הקזרים 2 בית חירות

מס' 08-0646842

09-9545842 70

זכויות ייצור / ע"פ הנחיות עו"ד

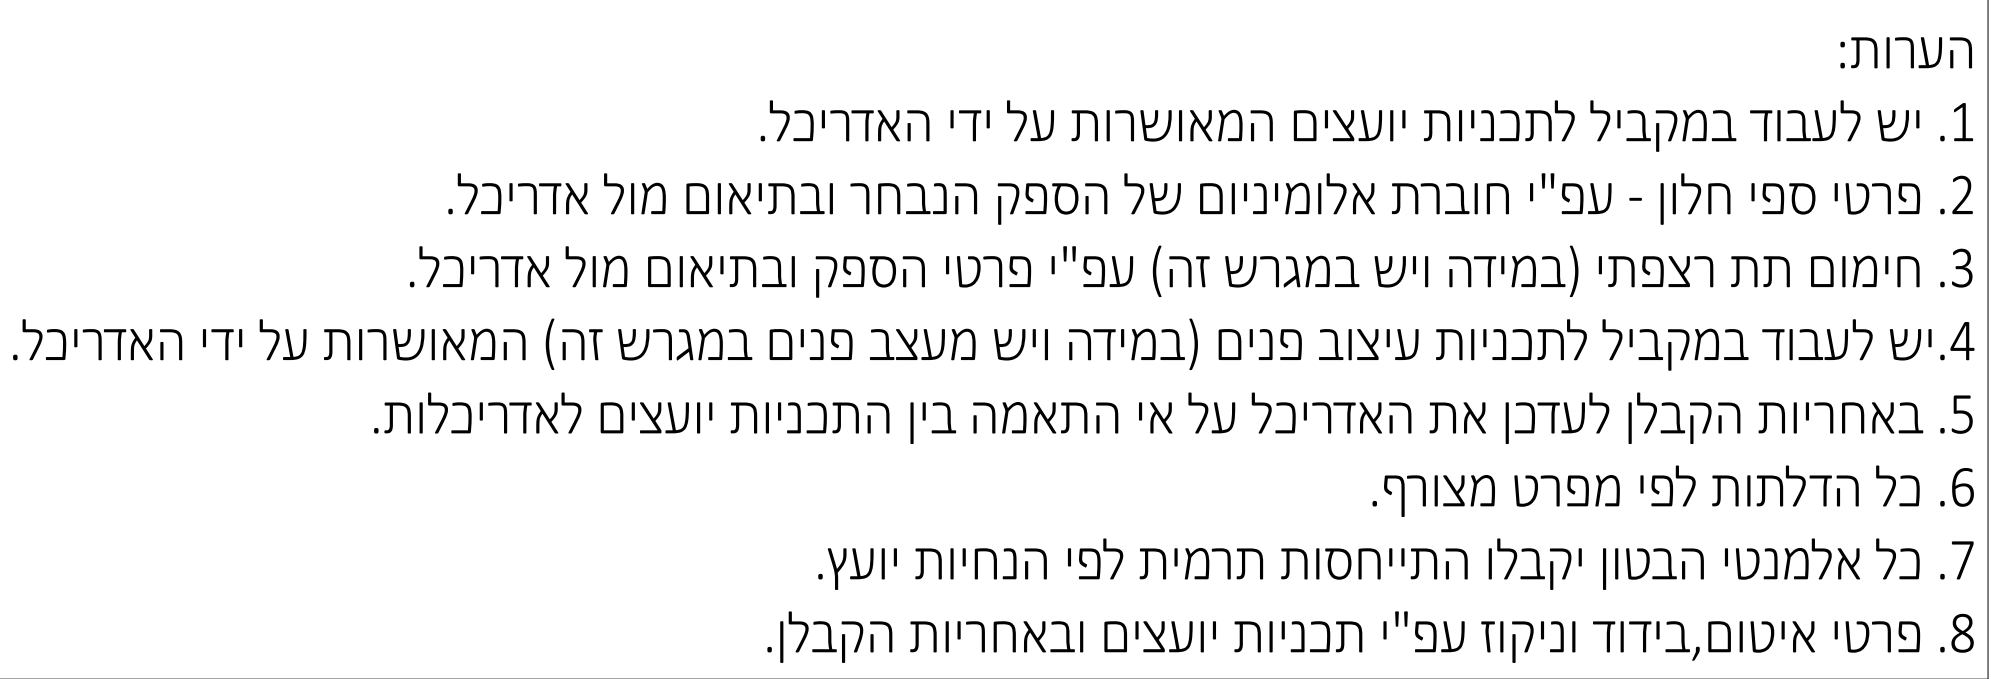

1. יש לעבוד במקביל לתכניות יועצים המאושרות על ידי האדריכל.
2. פרטי ספי חלון - עפ"י חוברת אלומיניום של הספק הנבחר ובתיאום מול אדריכל.
3. חימום תת רצפתי (במידה ויש במגרש זה) עפ"י פרטי הספק ובתיאום מול אדריכל.
4. יש לעבוד במקביל לתכניות עיצוב פנים (במידה ויש מעצב פנים במגרש זה) המאושרות על ידי האדריכל.
5. באחריות הקבלן לעדכן את האדריכל על אי התאמה בין התכניות יועצים לאדריכלות.
6. כל הדלתות לפי מפרט מצורף.
7. כל אלמנטי הבטון יקבלו התייחסות תרמית לפי הנחיות יועץ.
8. פרטי איטום, בידוד וניקוז עפ"י תכניות יועצים ובאחריות הקבלן.

1 : 50

מתכונים:


ניהול פרויקט
מהיסוד - בן סולומון
פיקוח
מהיסוד - בן סולומון
קונסטרוקציה
ערן שילר
מיוזג אוויר
אייל אזר מהנדסים ויועצים בע"מ
אינסטלציה
איתן אלמסי
חשמל
איתן בסיס
אלומיניום
נוף
נתי בלוקא
חשמל חכם
חימום תת רצפתי
איטום
צבי טל
אקוסטיקה
מעליות
קרקע וביסוס
דיה הנדסת קרקע וביסוס
ירשני

$$\pm 0.00 = +242.60$$

הערת:
 תכנית זו איש לקראת ידע תכנית הוועיצים.
 נגבה אבסולוט. ראו תכנית פחות.
 היסודות הן בלא קורות הבית, כולל, מדורות, ירופים, ירופים.
 שופים סביב יחיד-ונון-רא תכנית פחות.
 איסוס תכנית הרפואת הבית במגנטם עקרקע בידוד תמי לאורך העמודים
 תחנות וועל התחרות. בקליות וועל פילי (נינון) ראו תכנית פחות-סנסורקווע
 אדם יבוצע כלל תכנית אופיי הכולם תכנית.
 פחות תכנית. ע"פ פסוס תכנית, תאסוד ע"פ פיקוד העורף.

[illegible]

קרא קירות:

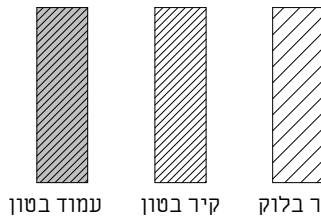[illegible]

אדריכלות

CLIENT NAME: _____: המזמין:

קבוצת רכישה נופיה

PROJECT NAME: הפרויקט:

נופיה - מגרש 20



DRAWING NAME: תגליון:

תכנית גג

SHEET NUMBER: 79 גליון:

A3-1-102

SCALE:	קנה מידה:	EDITION:	דורה:
1 : 50			
STATUS:	סטטוס		
למכור			
	נכדק עיין:		דוטס עיין:
DATE:	22.09.25		יורה:

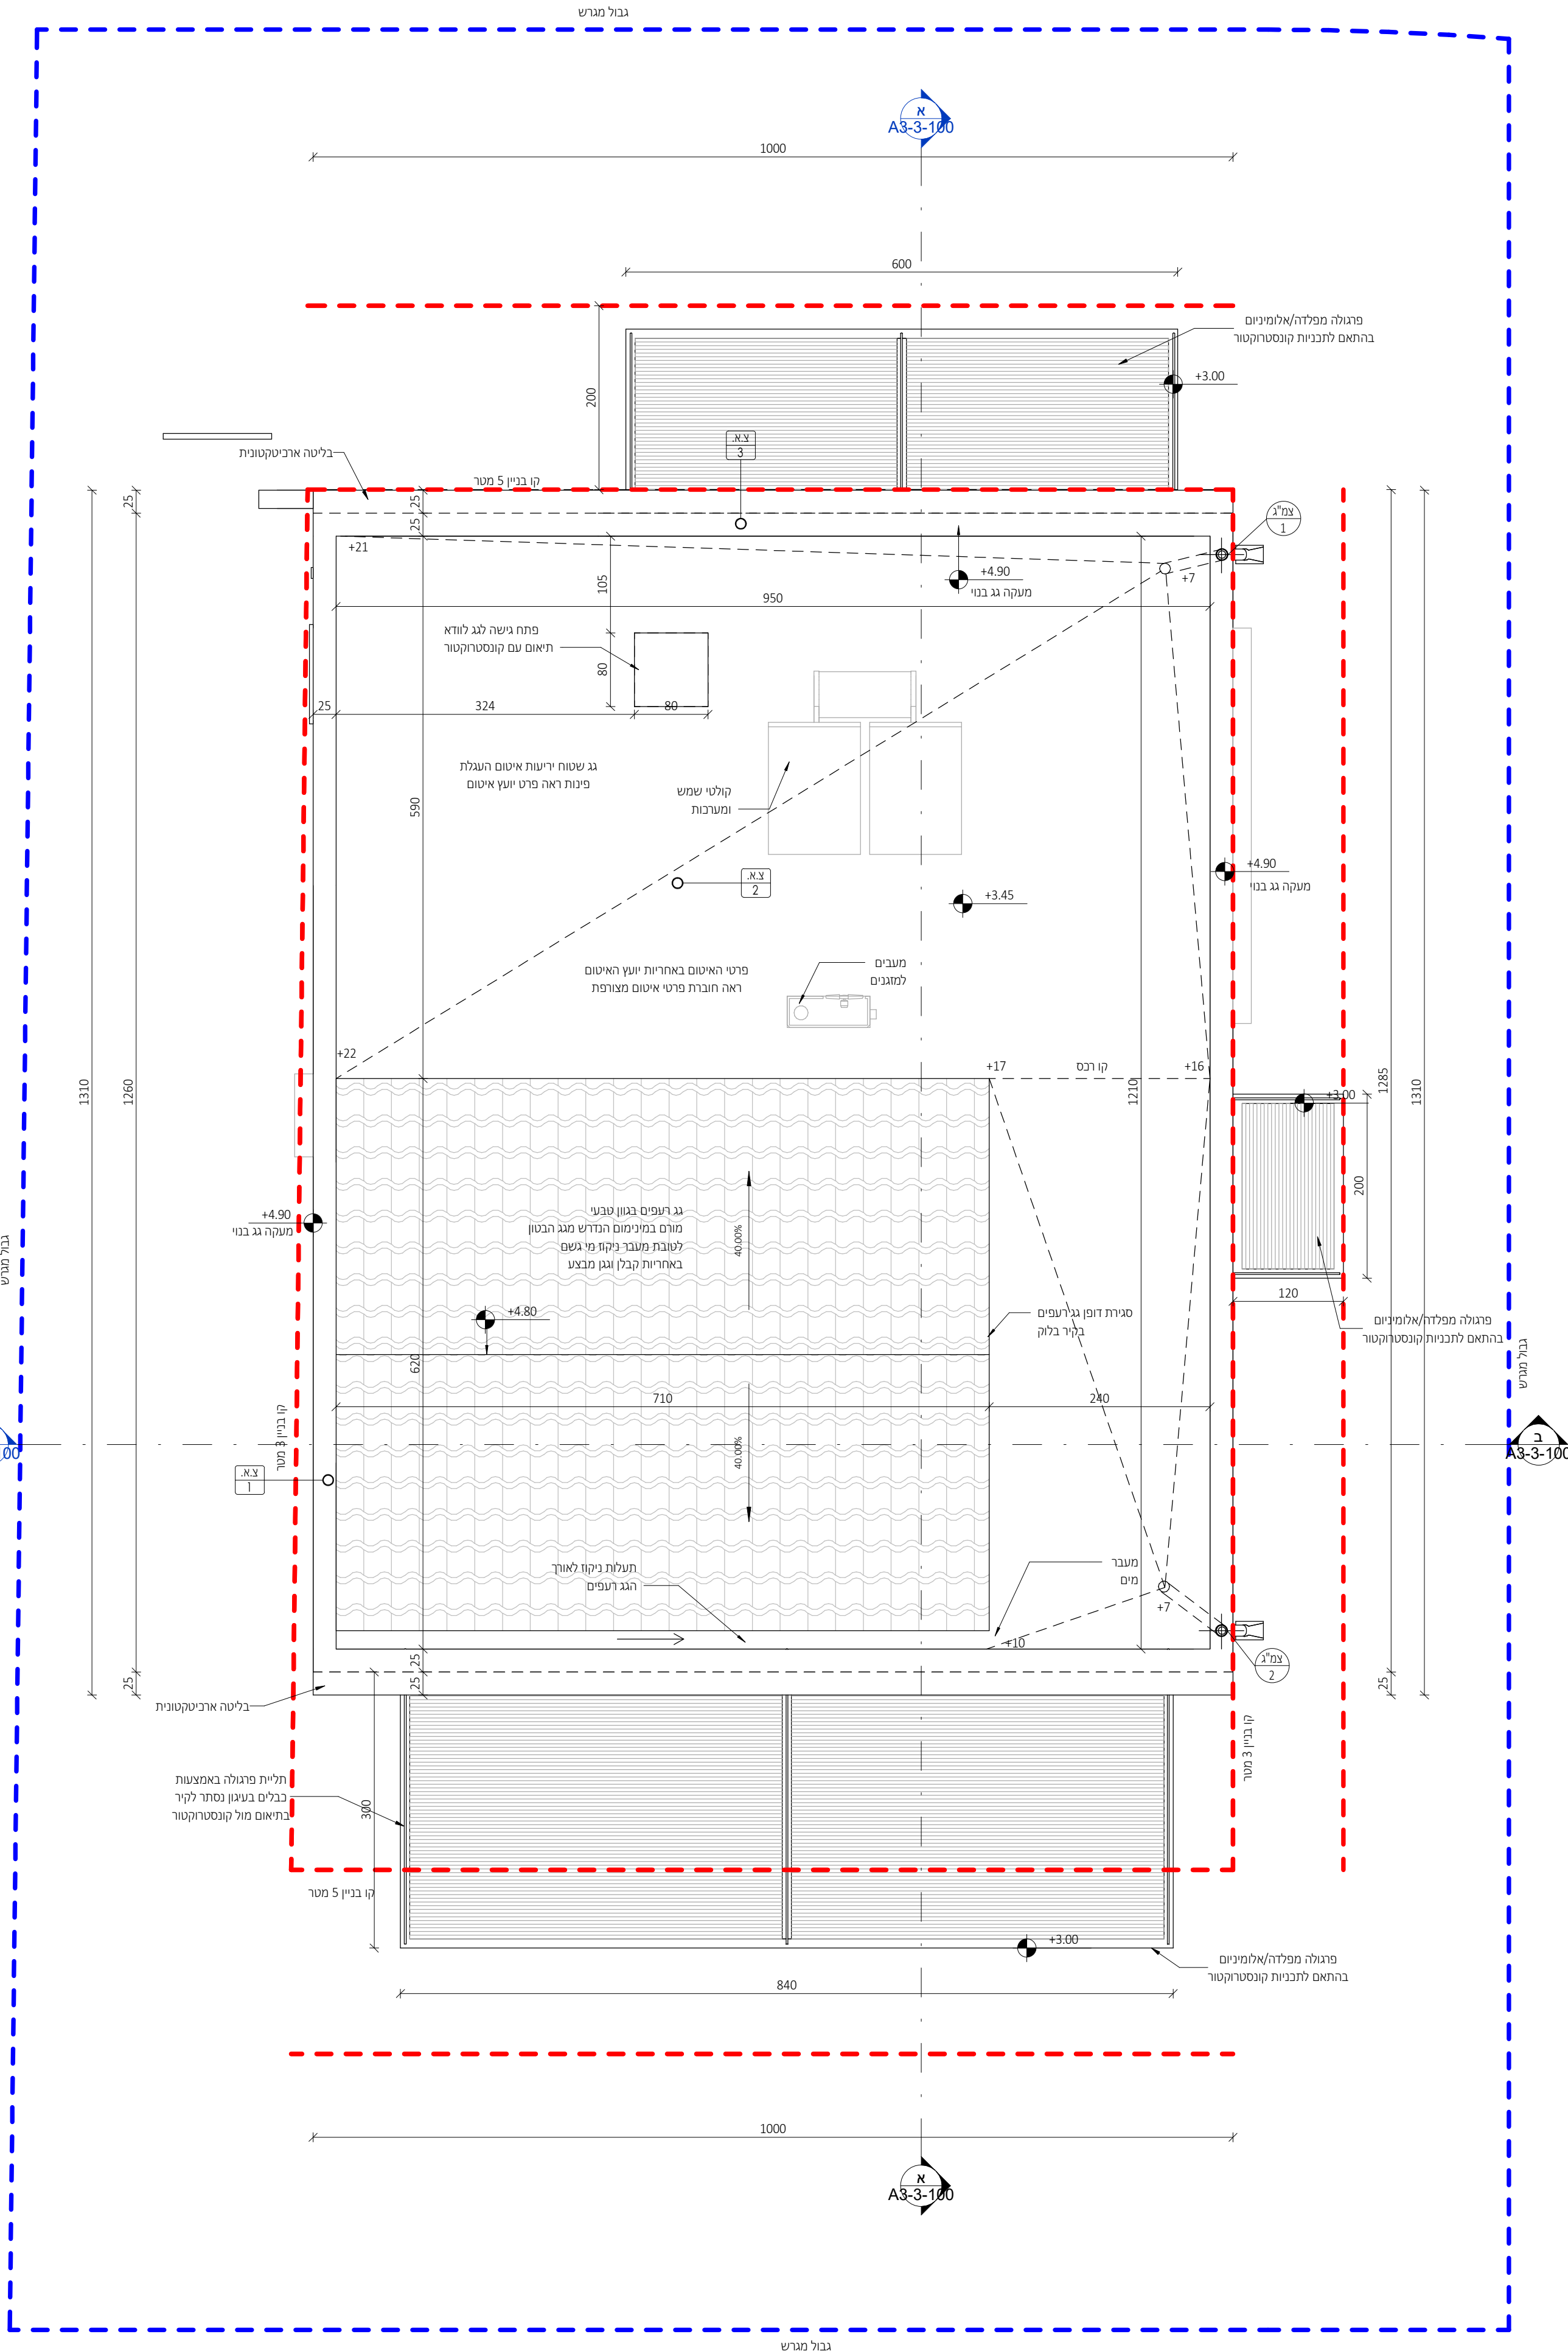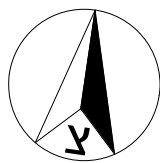

תכנית גג


1 : 50

מתכונים:

ניהול פרויקט
מהיסוד - בן סולמון
פיקוח
מהיסוד - בן סולמון
קונסטרוקציה
ערן שילר
מיזוג אוויר
אייל ארז מהנדסים ויועצים בע"מ
אינסטלציה
איתן אלמסי
חשמל
איתן בסיס
אלומיניום
נוף
נתי בלוקא
חשמל חכם
חימום תת רצפתי
איטום
צבי טל
אקוסטיקה
מעליות
קרקע וביסוס
דיה הנדסת קרקע וביסוס
רישוי

[illegible]

מקרא קירות:

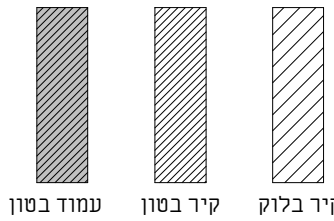[illegible]

אדריכלות

CLIENT NAME: _____ שם המזמין:

קבוצת רכישה נופיה

PROJECT NAME: _____ שם הפרויקט:

נופיה - מגרש 20

DRAWING NAME: ס הגליון:

SHEET NUMBER: 19

SCALE: קנה מידה: EDITION: הדורה:

1:50

STATUS: סמכות 1

למכר	
------	---

DATE: 22.09.25 אר"י:




NeumanHaynerArchitects

office@nh-arch.com
www.nh-arch.com


וימן חיינר אדריכלים

09-9545842 70

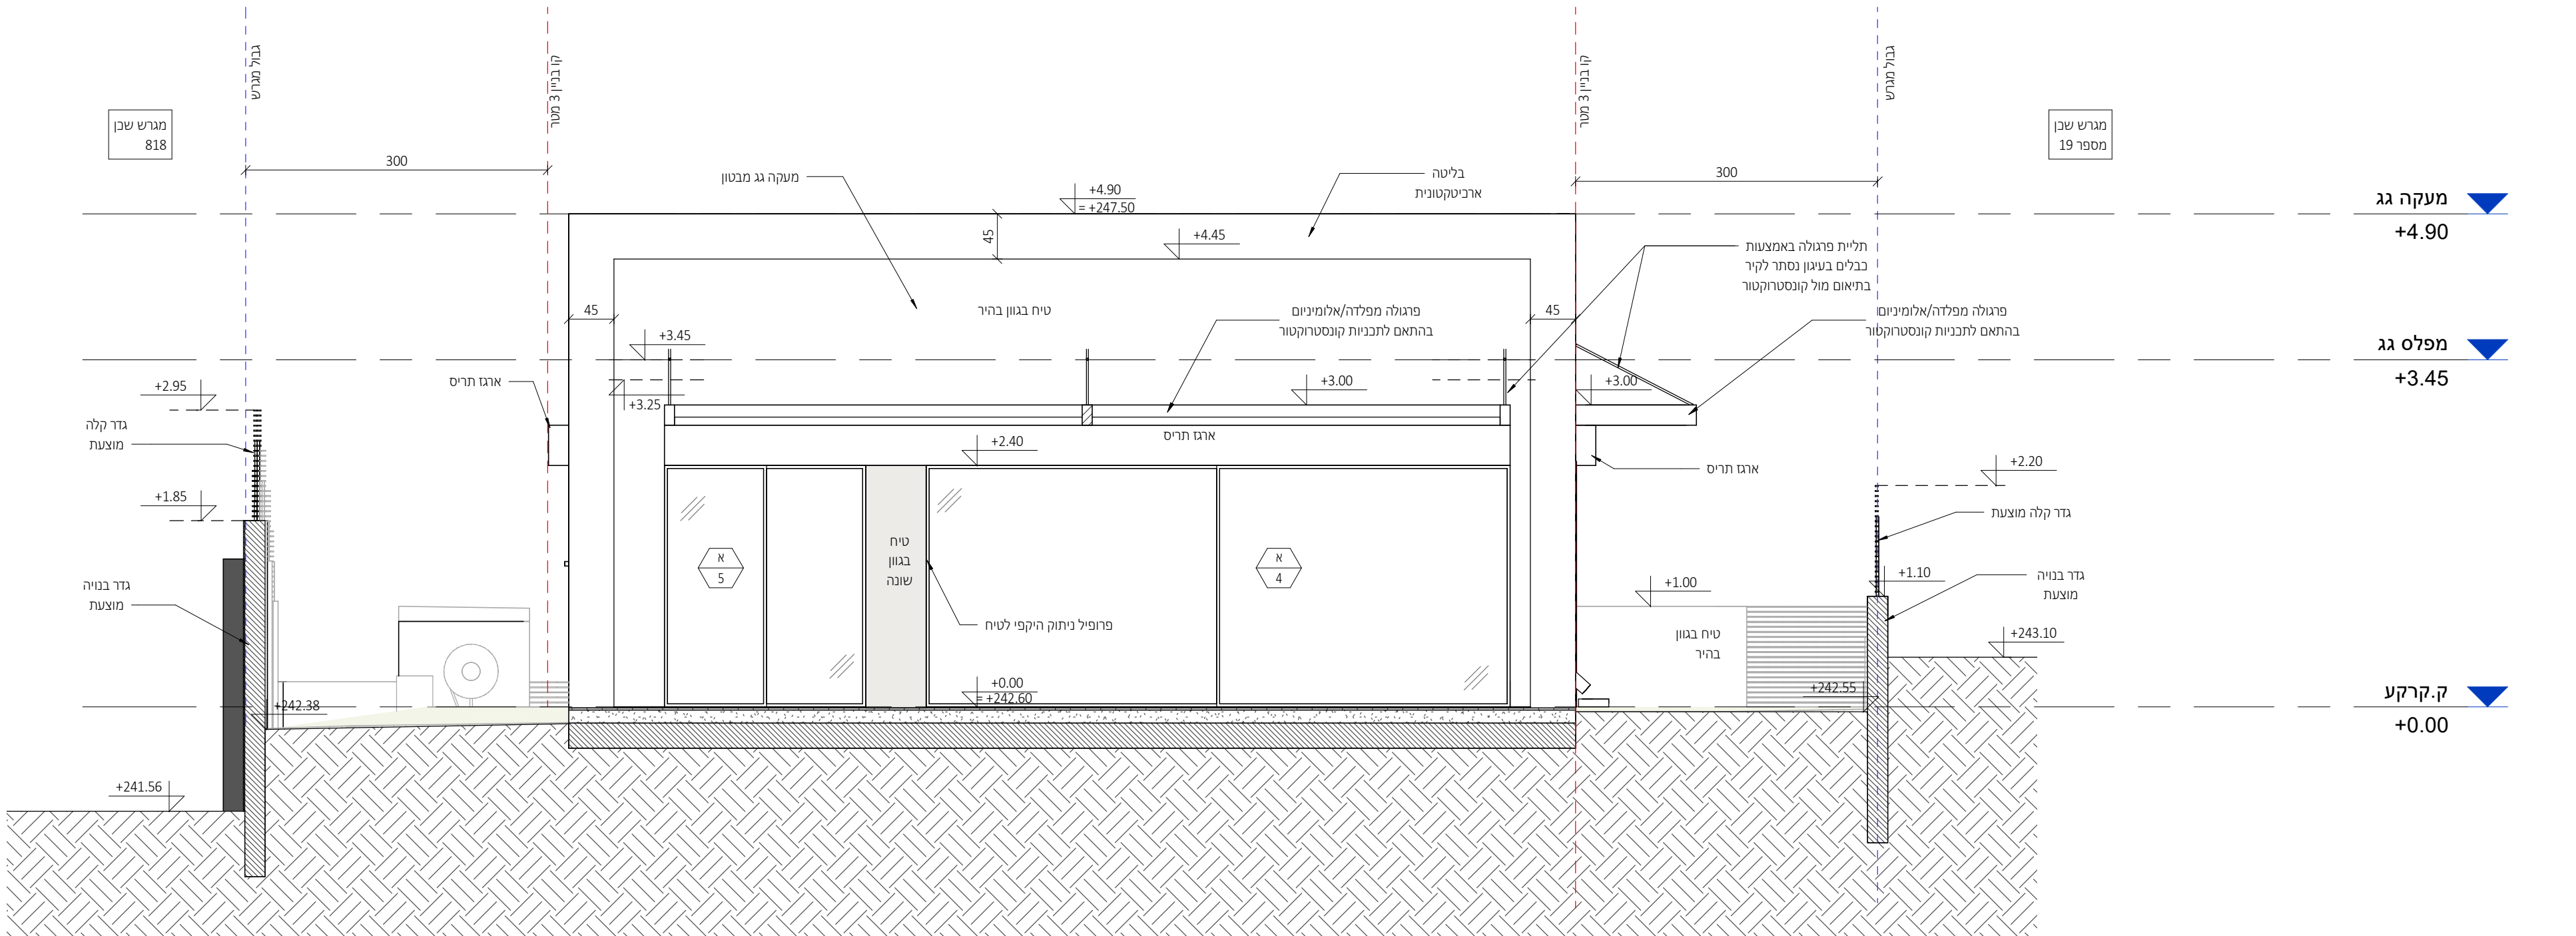

פיתוח נוקף עפ"י תוכניות

יועץ נוף ראה פירוט בנפרד

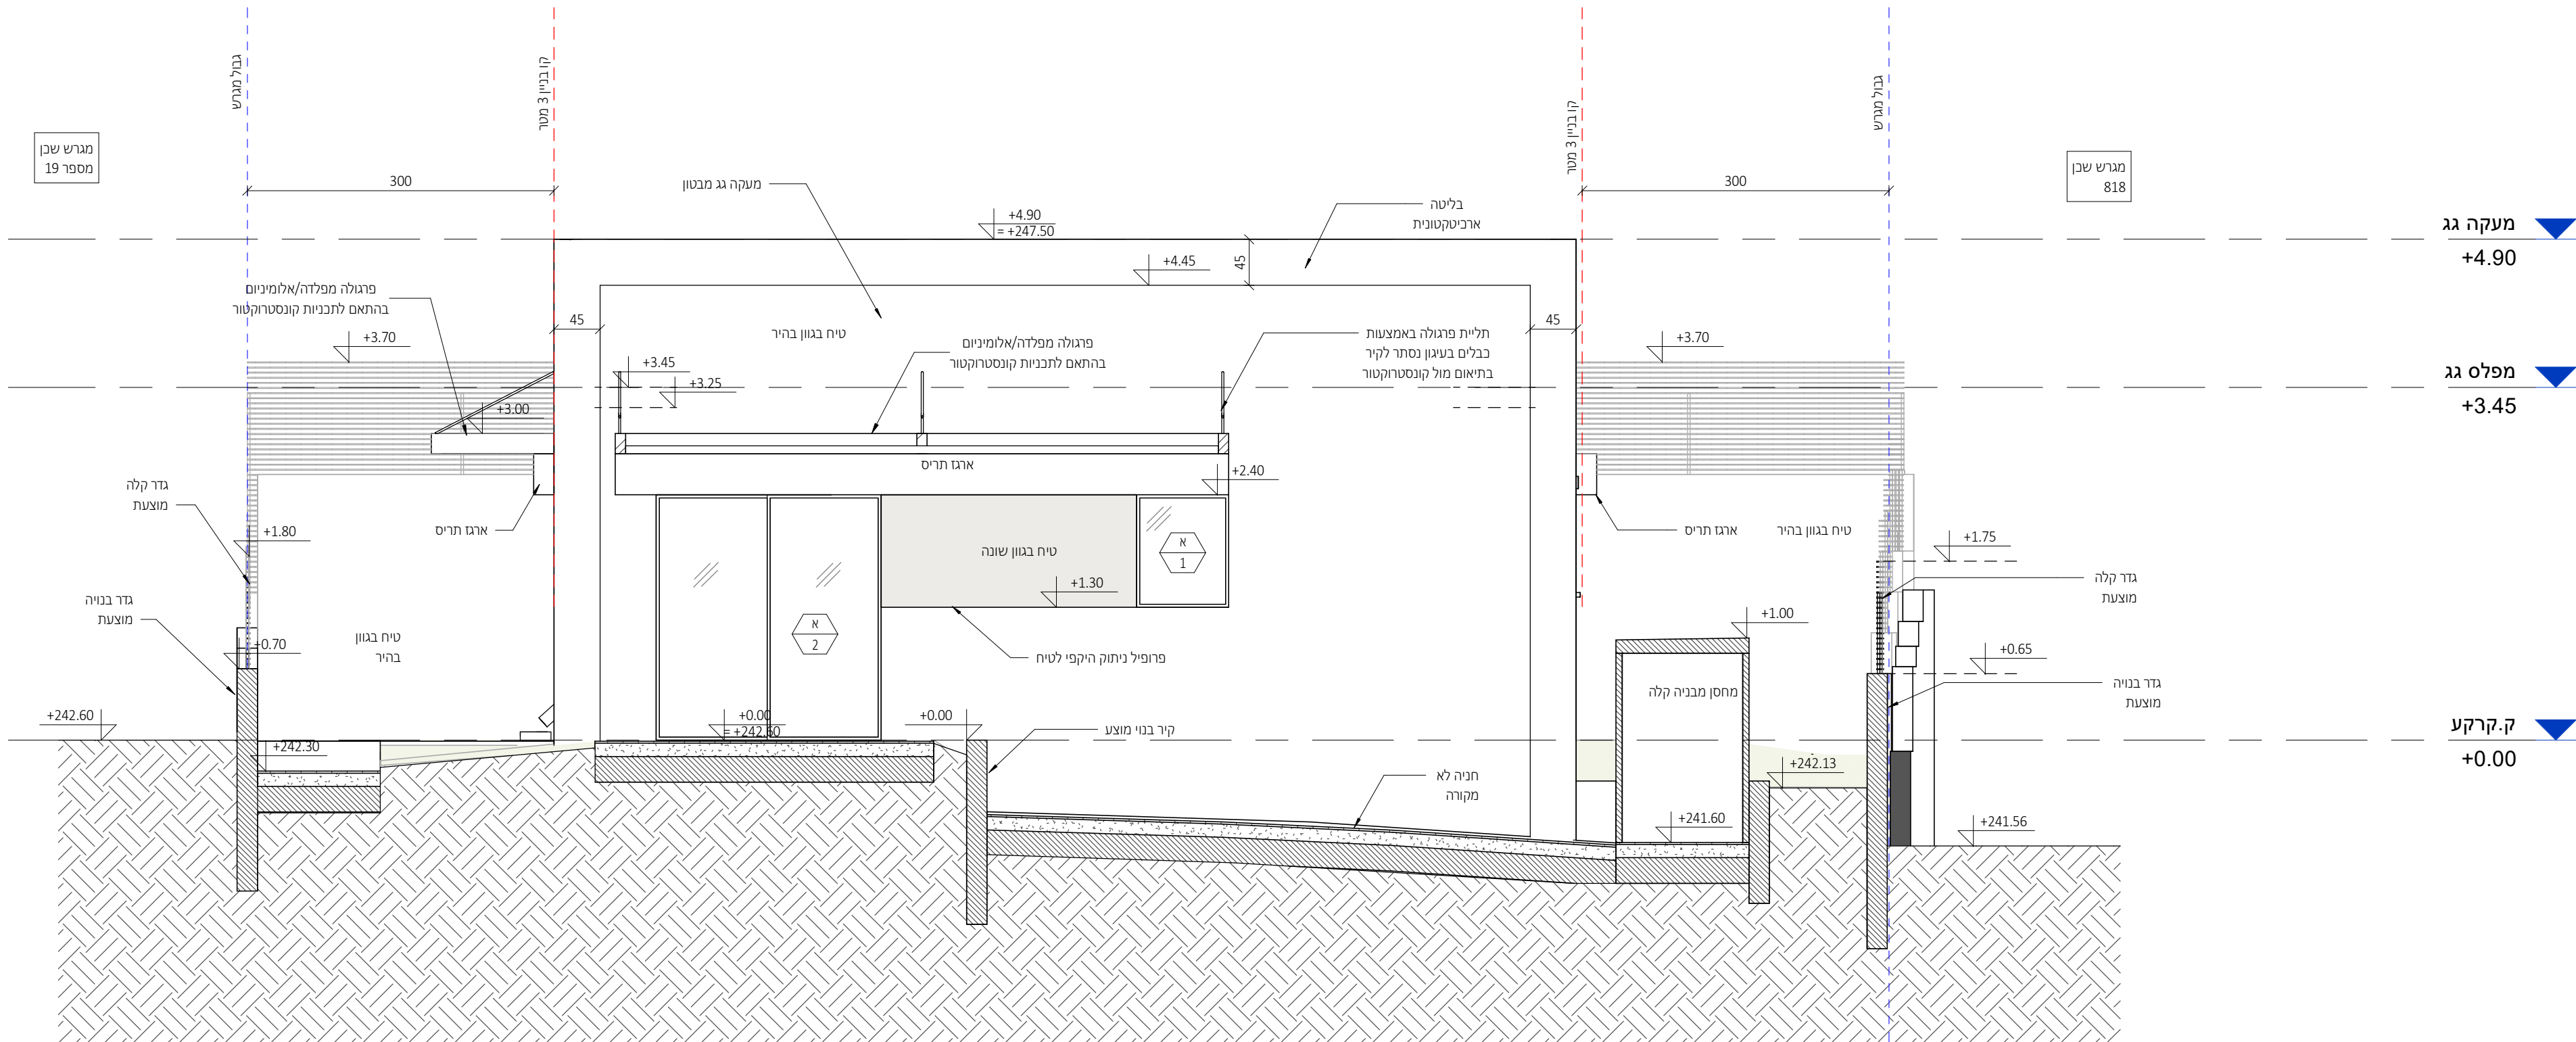

פיתוח נוף עפ"י תוכניות

יועץ נוף ראה פירוט בנפרד


פרטי איטום, בידוד וניקוז עפ"י תכניות יועצים ובאחריות הקבלן

מתכונים:

ניהול פרויקט
מהיסוד - בן סולומון
פיקוח
מהיסוד - בן סולומון
קונסטרוקציה
ערן שילר
מיזוג אוויר
אייל ארז מהנדסים ויועצים בע"מ
אינסטלציה
איתן אלמסי
חשמל
איתן בסיס
אלומיניום
נוף
נתי בלוקא
חשמל חכם
חימום תת רצפתי
איטום
צבי טל
אקוסטיקה
מעליות
קרקע וביסוס
דיה הנדסת קרקע וביסוס
רישוי

[illegible]

מקרא קירות:

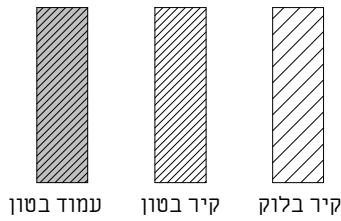[illegible]

אדריכלות

CLIENT NAME: _____ שם המזמין:

קבוצת רכישה נופיה

PROJECT NAME: _____ שם הפרויקט:

נופיה - מגרש 20

DRAWING NAME: ס הגליון:

חזיתות 2

SHEET NUMBER: 190 גליון:

SCALE: קנה מידה: EDITION: הדורה:

1 : 50

למחרת

רשט ע"י:	נבדק ע"י:
----------	-----------


DATE: 22.09.25 חתום:



NeumanHaynerArchitects


office@nh-arch.com
www.nh-arch.com

זכויות ייצור / ע"פ הנחיות עו"ד

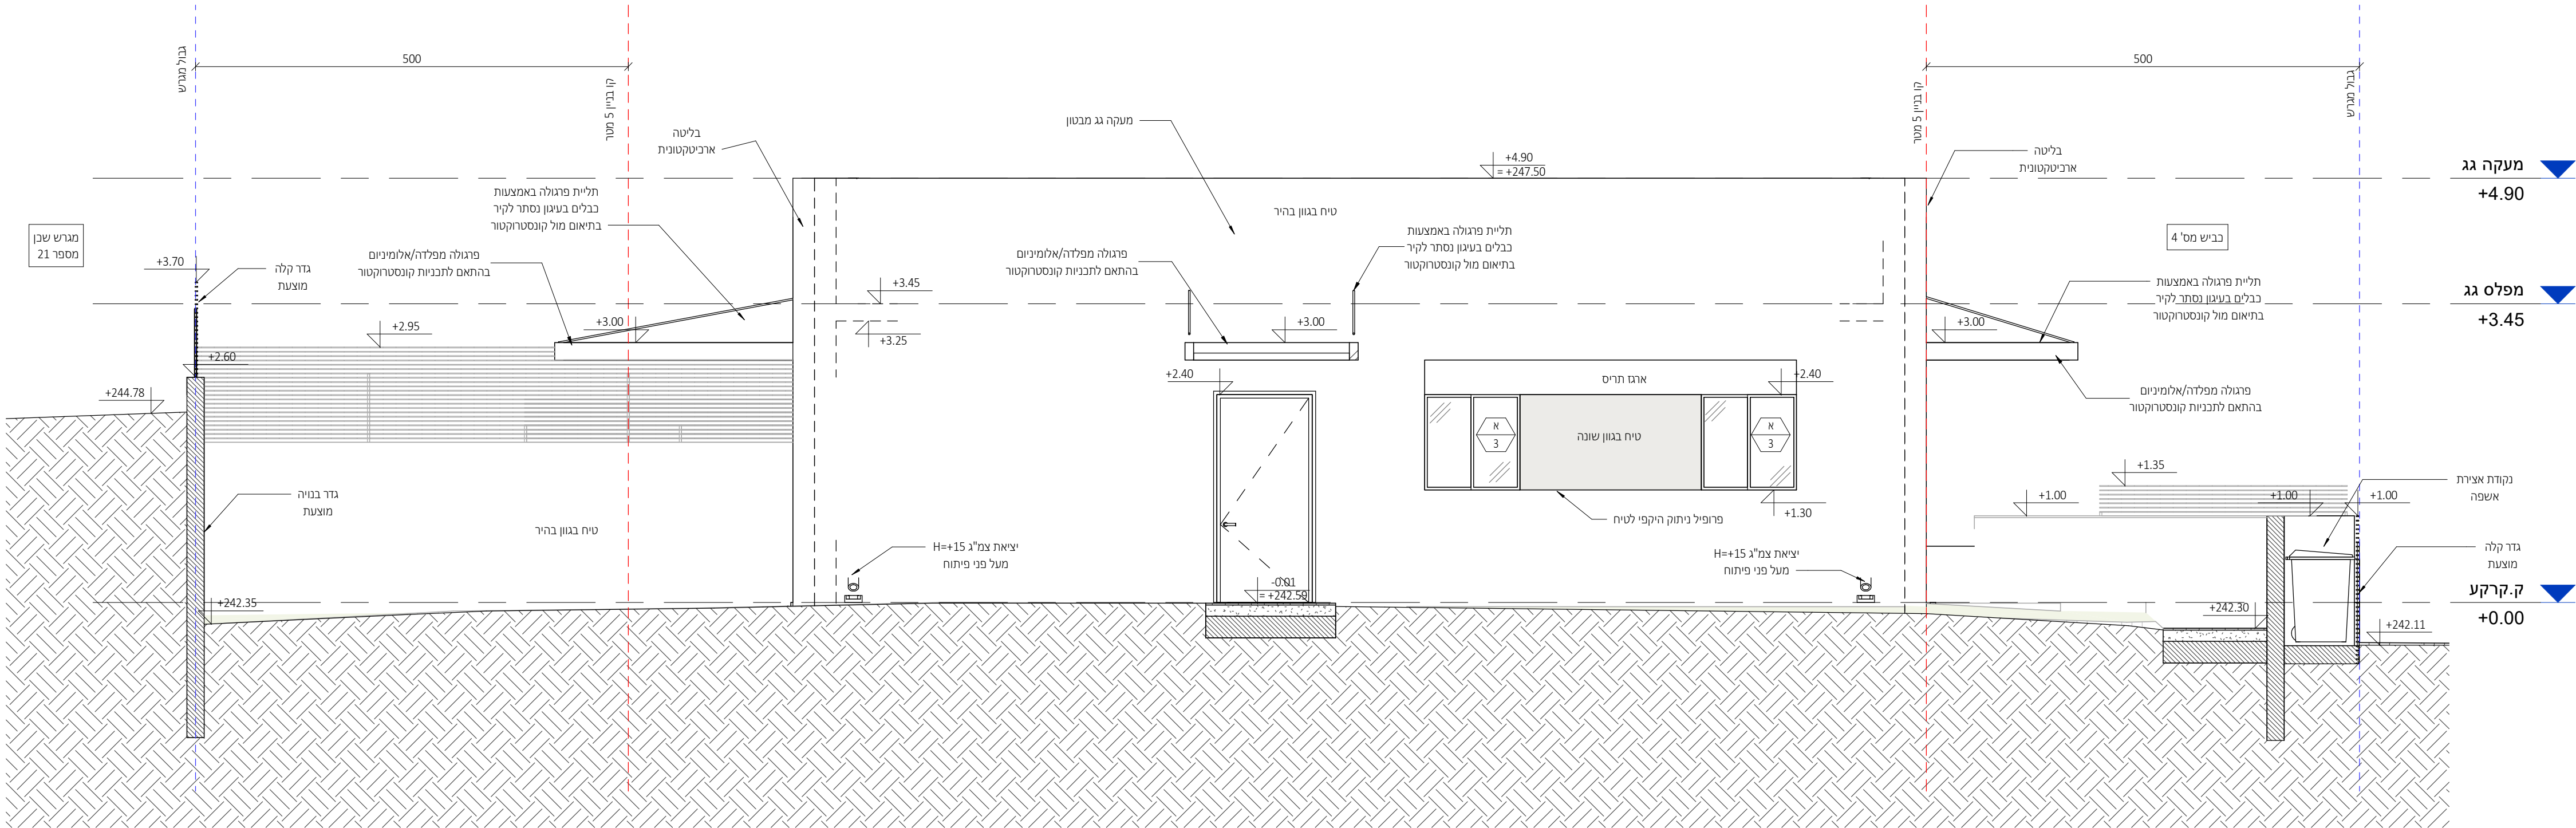

חזית מזרחית

1 : 50

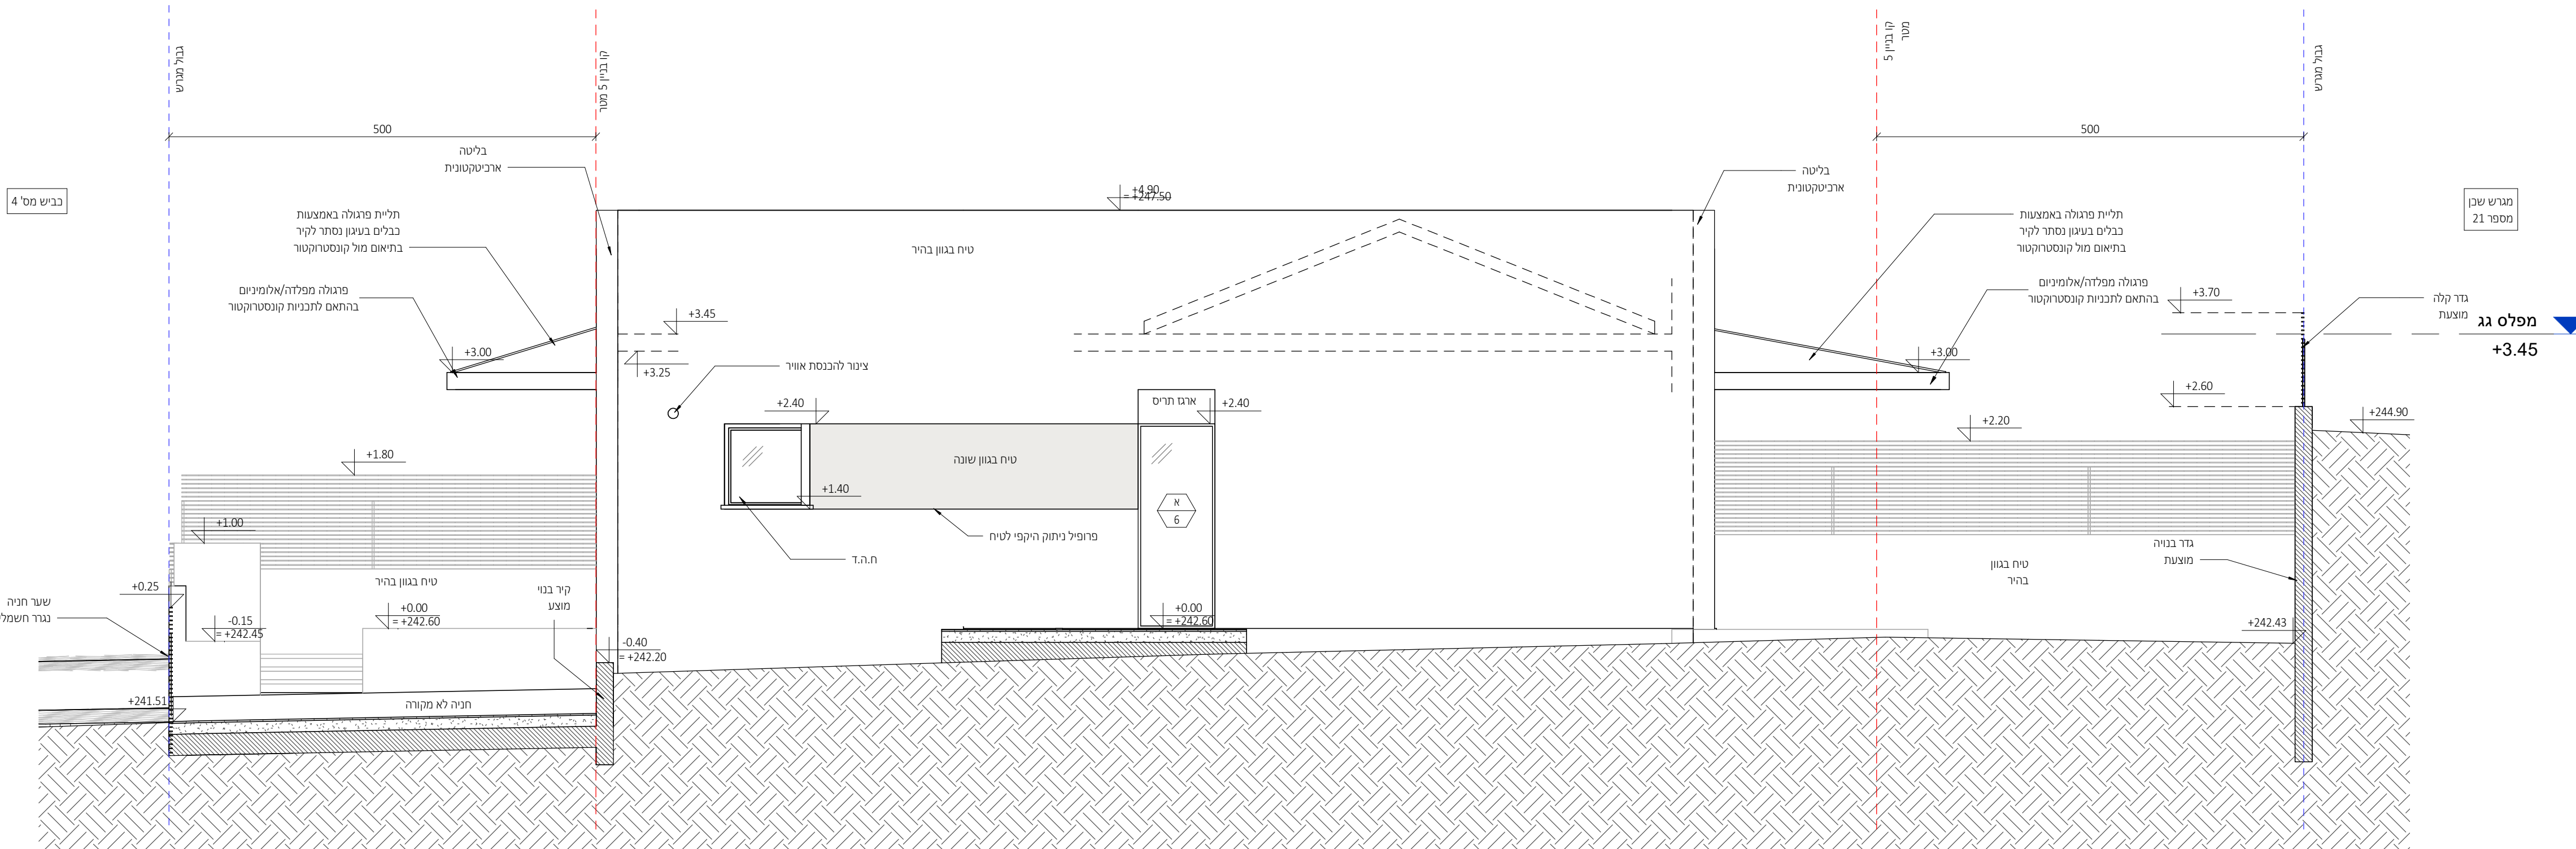

חזית מערבית

1 : 50

פיתוח נוף עפ"י תוכניות

יועץ נוף ראה פירוט בנפרד

פיתוח נוף עפ"י תוכניות

יועץ נוף ראה פירוט בנפרד


פרטי איטום, בידוד וניקוז עפ"י תכניות יועצים ובאחריות הקבלן

מתכונים:

ניהול פרויקט
מהיסוד - בן סולומון
פיקוח
מהיסוד - בן סולומון
קונסטרוקציה
ערן שילר
מיזוג אוויר
אייל ארז מהנדסים ויועצים בע"מ
אינסטלציה
איתן אלמסי
חשמל
איתן בסיס
אלומיניום
נוף
נתי בלוקא
חשמל חכם
חימום תת רצפתי
איטום
צבי טל
אקוסטיקה
מעליות
קרקע וביסוס
דיה הנדסת קרקע וביסוס
רישוי

[illegible]

מקרא קירות:

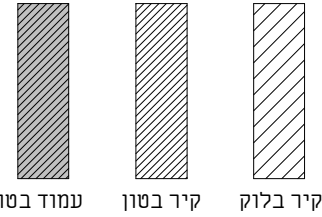[illegible]

אדריכלות

CLIENT NAME:

השם המלא:

קבוצת רכישה נופיה

PROJECT NAME:

שם הפרויקט:

20 מגרש - נופיה

DRAWING NAME:

שם התכנית:

חתכים

SHEET NUMBER:

מספר גיליון:

A3-3-100

SCALE:	קנה מידה:	EDITION:	דפוס:
1 : 50	סטוס:	1	
למכר	נבדק ע"י:		
DATE:		תאריך:	
22.09.25			




NeumanHaynerArchitects

office@nh-arch.com
 www.nh-arch.com


וימן חיינר אדריכלים
מורד ההדריס 2, בית חירות
טל 09-9545842

זכויות ייצור / ע"פ הנחיות עו"ד

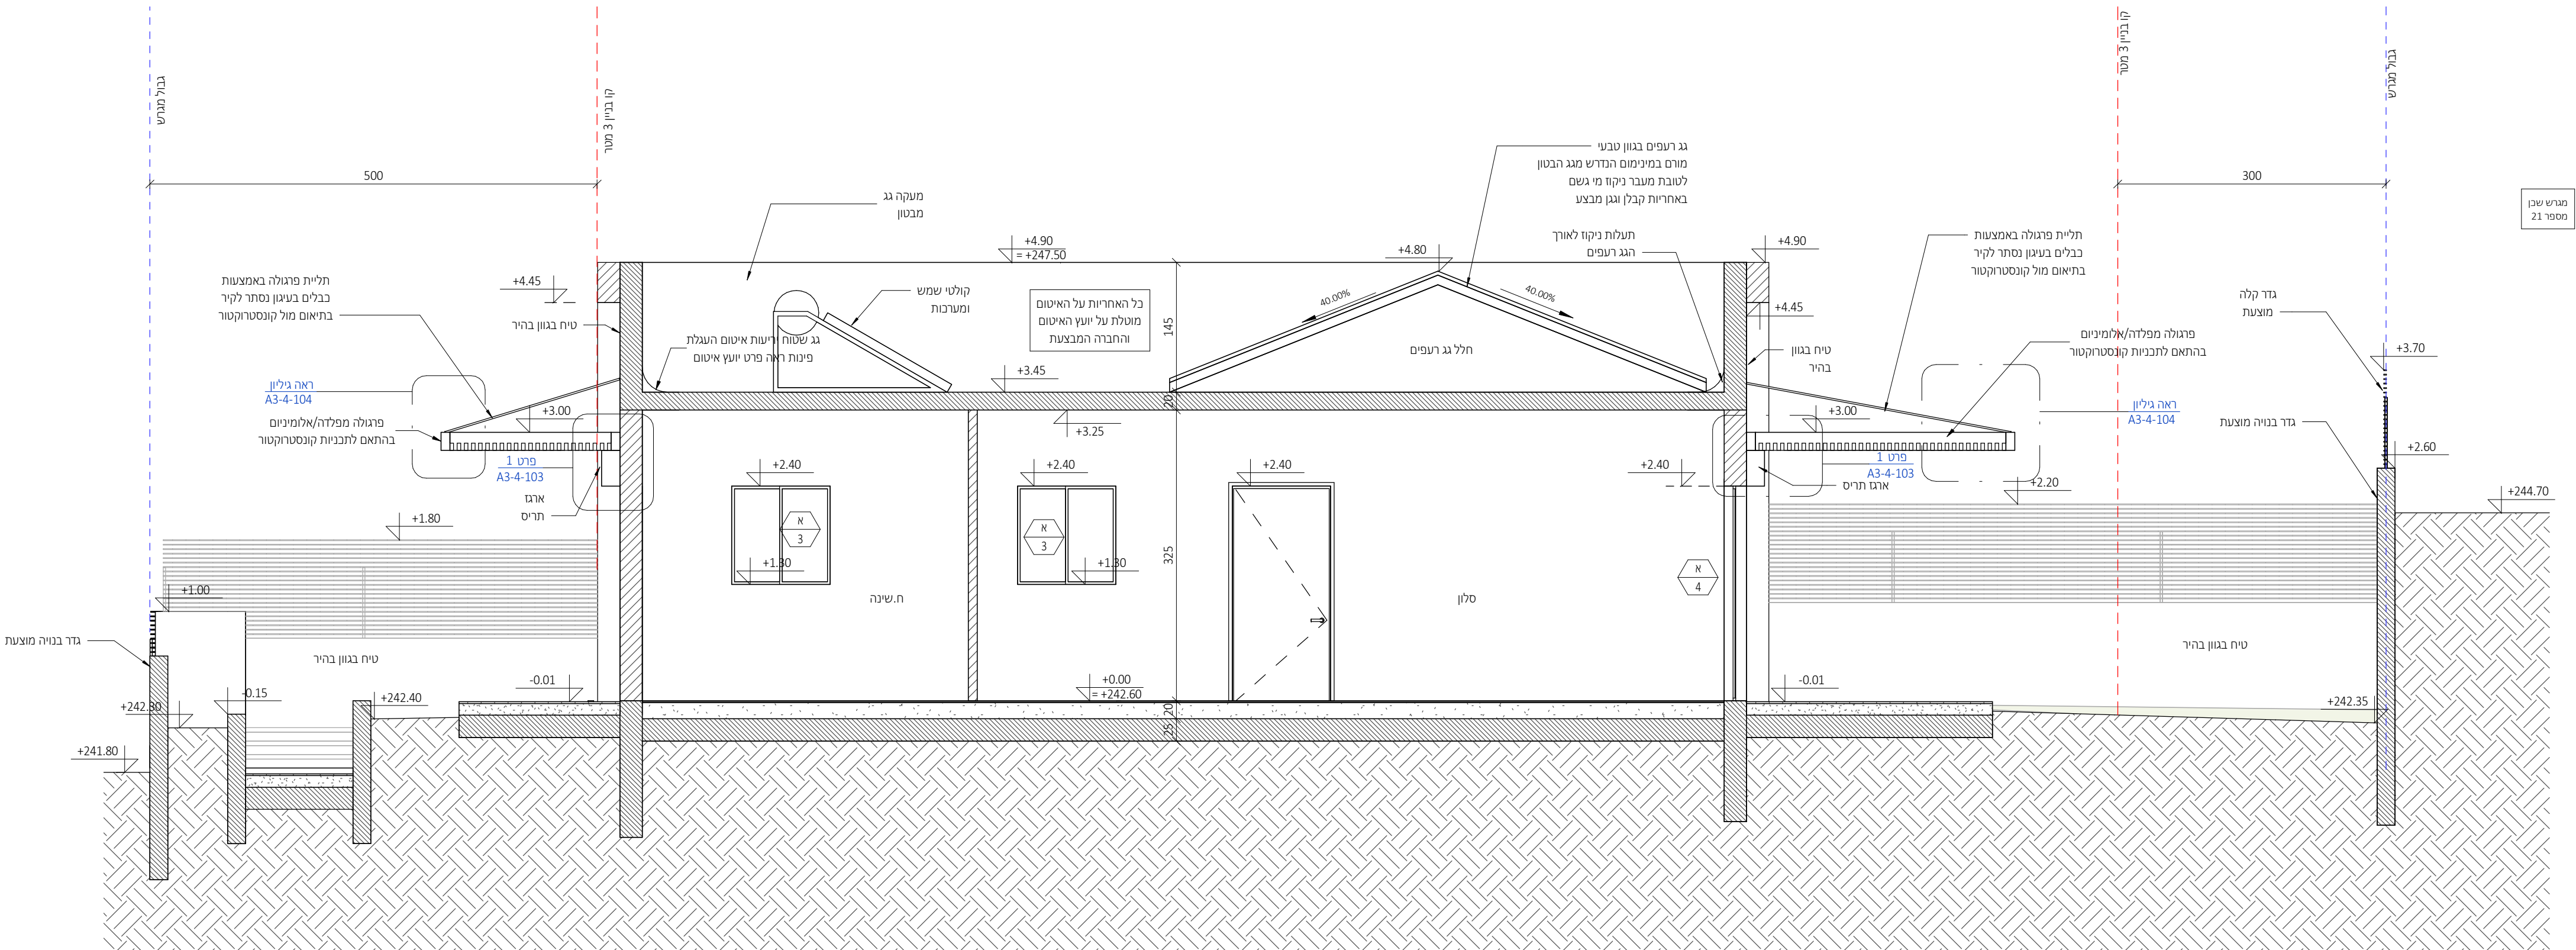

פיתוח נוף עפ"י תוכניות

יועץ נוף ראה פירוט בנפרד

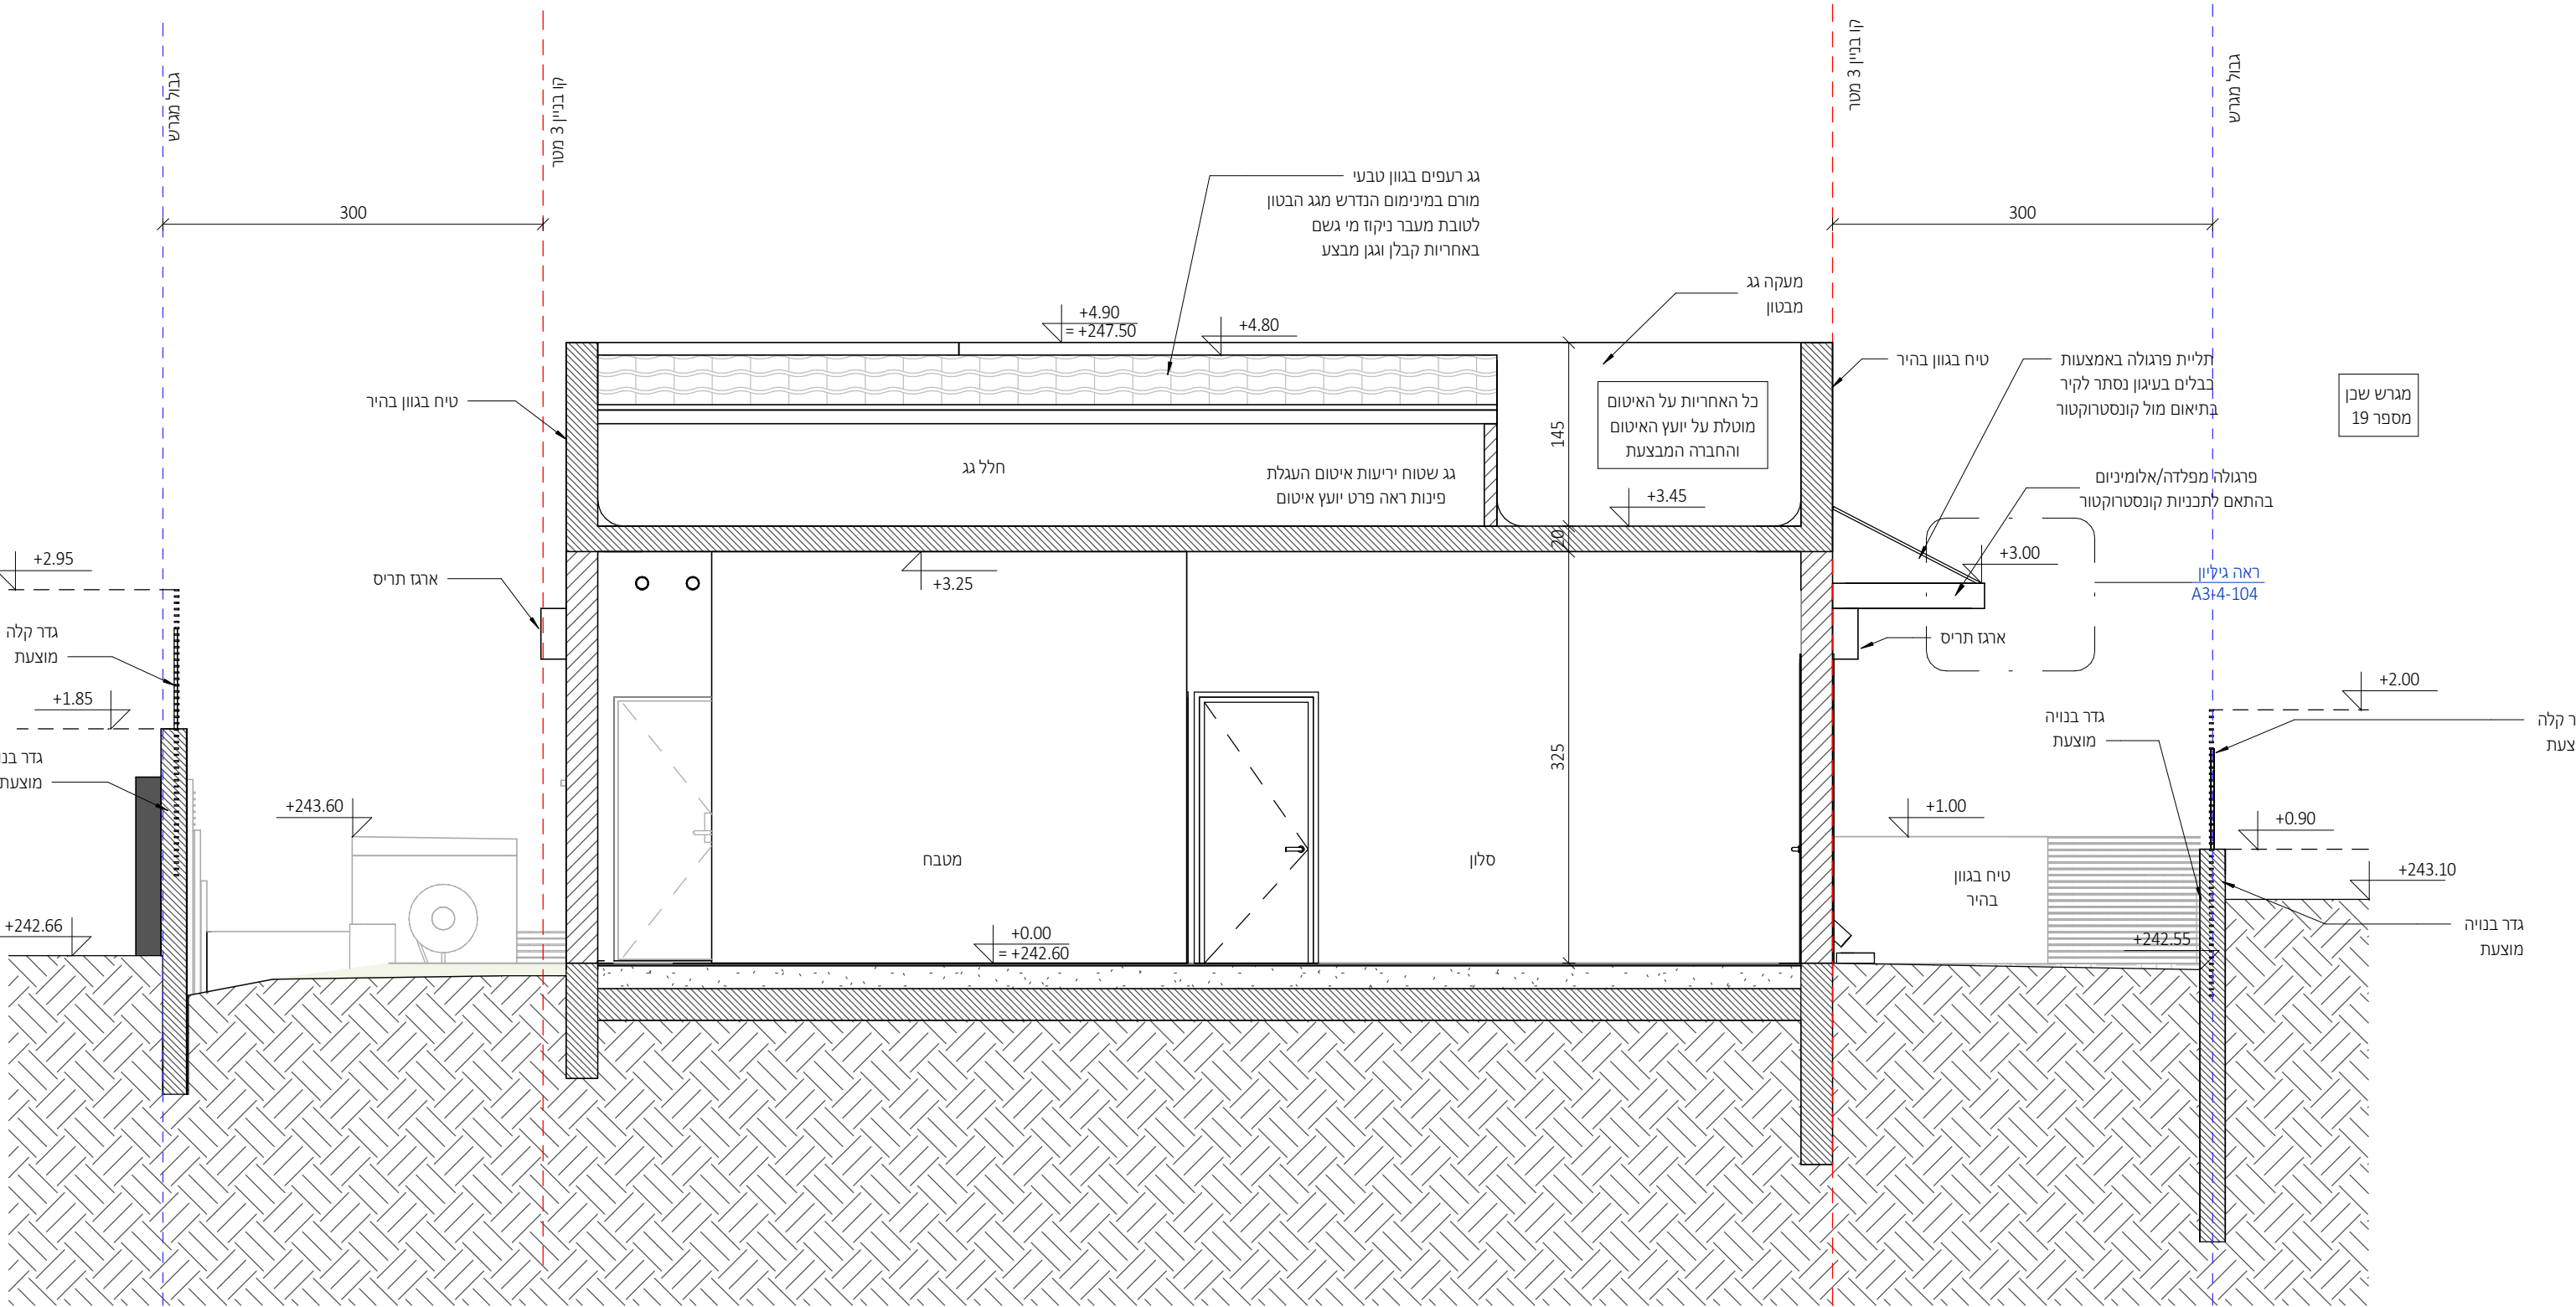

פיתוח נוף עפ"י תוכניות

יועץ נוף ראה פירוט בנפרד


חתך ב-ב

1 : 50


ניהול פרויקט
מהיסוד - בן סולומון
פיקוח
מהיסוד - בן סולומון
קונסטרוקציה
ערן שילר
מיזוג אוויר
אייל ארז מהנדסים ויועצים בע"מ
אינסטלציה
איתן אלמסי
חשמל
איתן בסיס
אלומיניום
נוף
נתי בלוקא
חשמל חכם
חימום תת רצפתי
איטום
צבי טל
אקוסטיקה
מעליות
קרקע וביסוס
דיה הנדסת קרקע וביסוס
רישוי

[illegible]


PROJECT NAME:		ה פרויקט:	
קבוצת רכישה נופיה נופיה - מגרש 20			
DRAWING NAME:		שם הגליון:	
פרטים			
SHEET NUMBER:		מספר הגליון:	
A3-4-103			
SCALE:		מקנה מידה:	
As indicated		EDITION:	
TATUS:		מסמך	
למכר		1	
בדק ע"י:		מסמך ע"י:	
DATE:		תאריך:	
22.09.25			
יוסן היינר אדריכלים הודו המדרים 2, בית חירות 09-9545842			
NeumanHaynerArchitects office@nh-arch.com www.nh-arch.com			

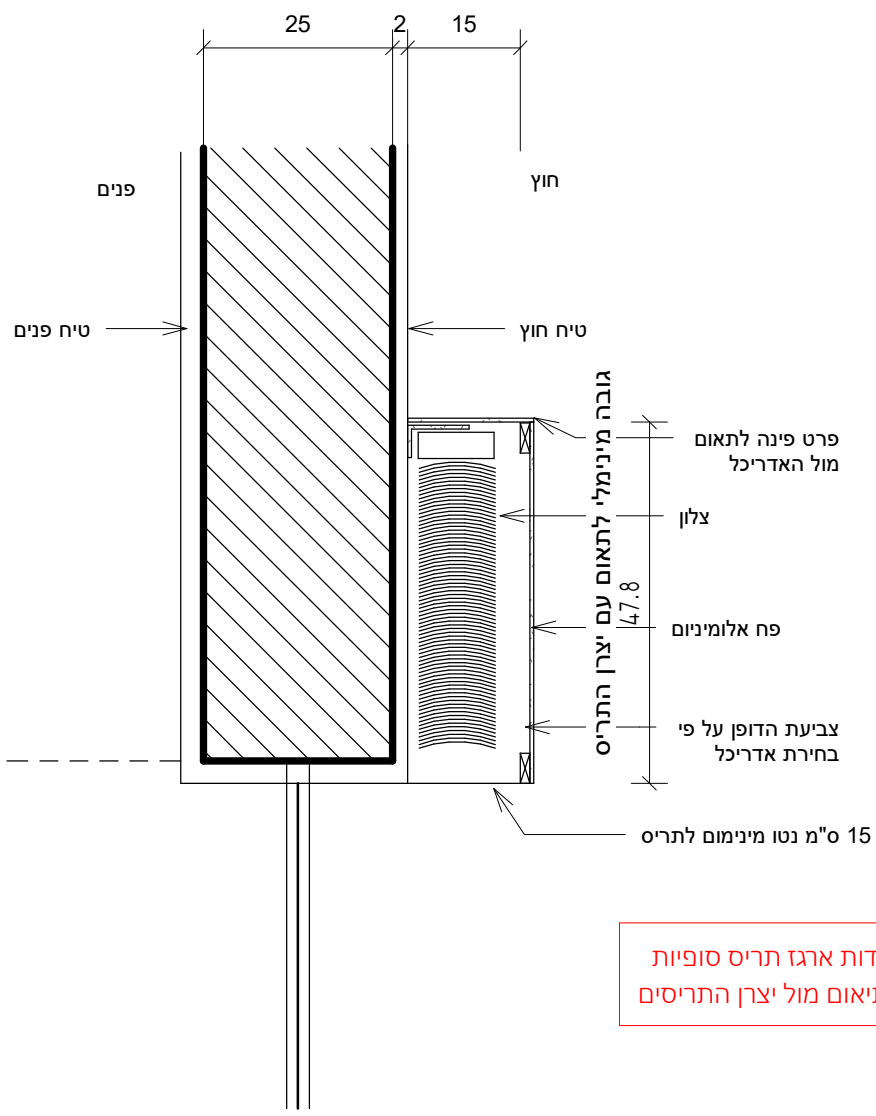


פרט 1 - כיס צלון חיצוני

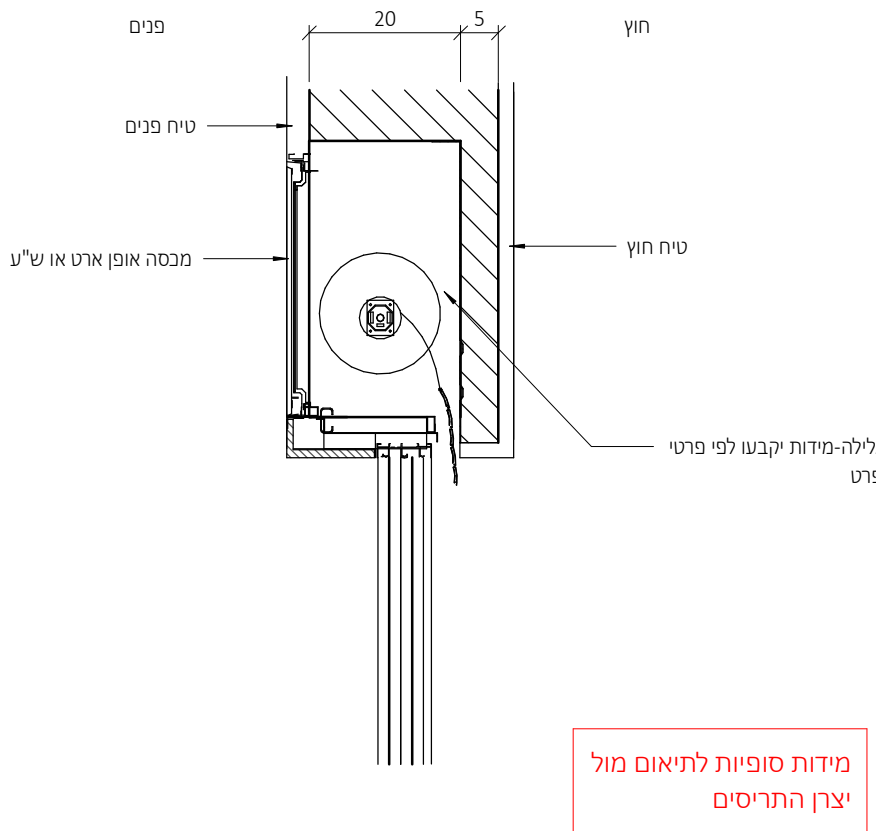

פרט 2 - תריס גלילה
1 : 10

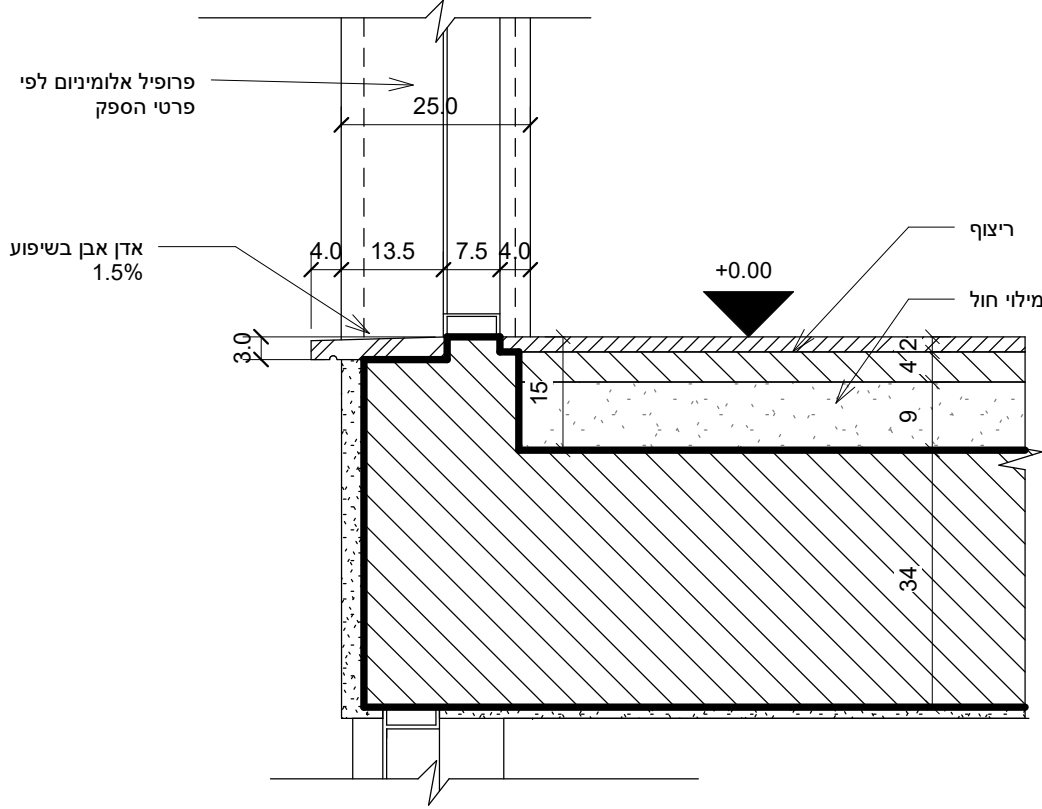


פרט 3 - מפגש חלון ורצפה

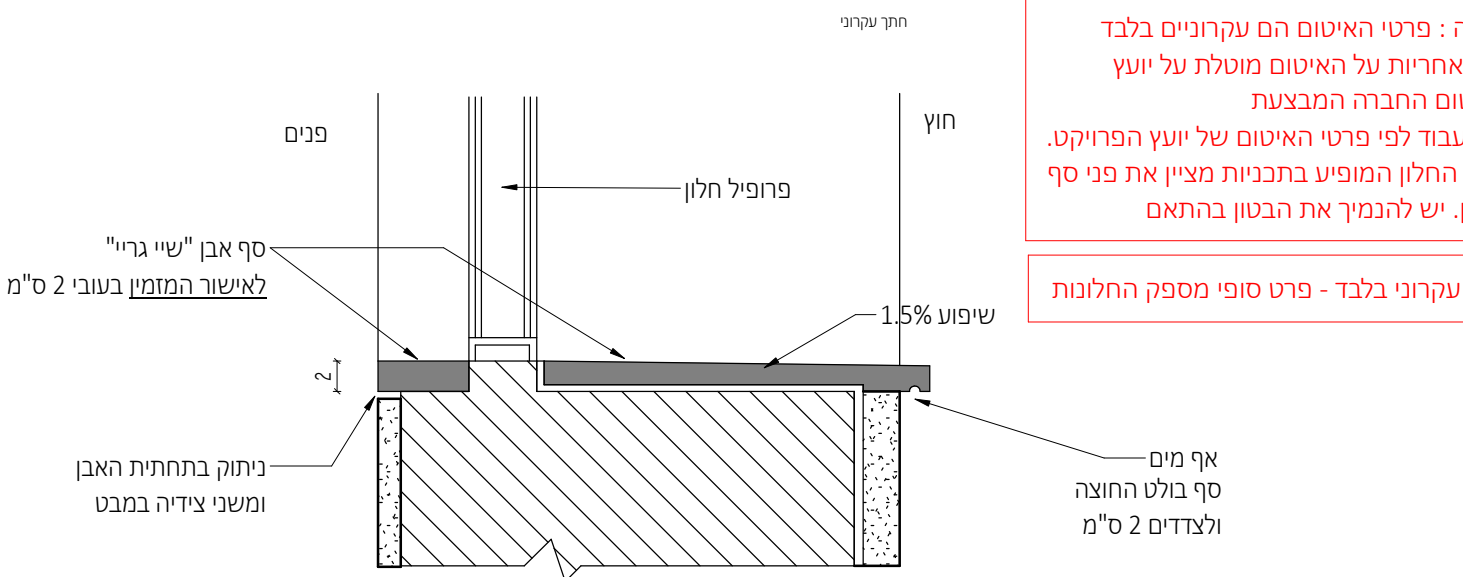


פרט 4 - חלון - פרט טיפוס י - סף חלון

1 : 5

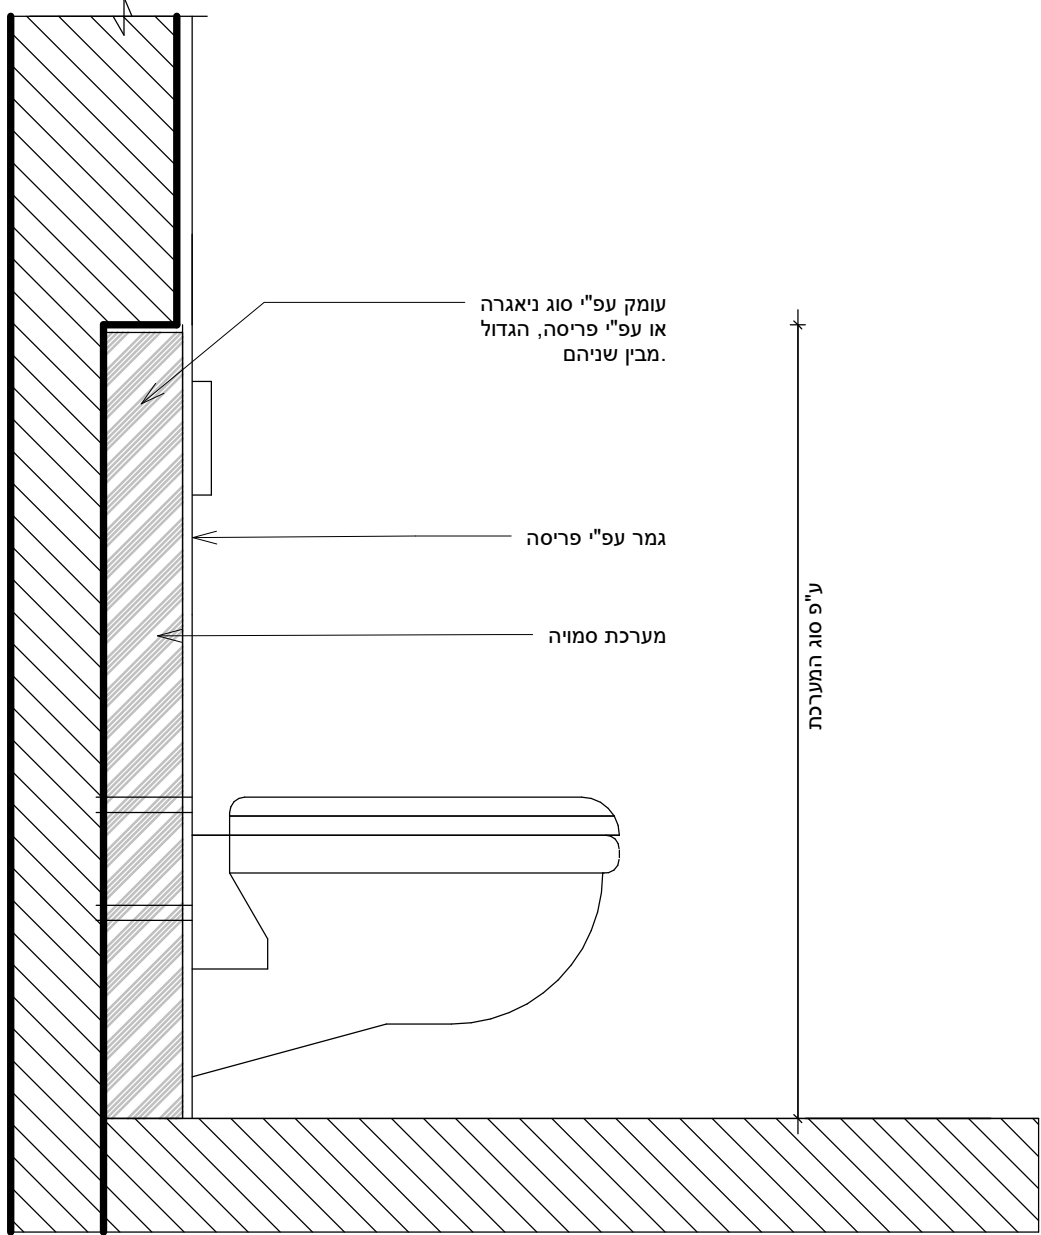

פרט 5 - אסלה תלויה בקיר 20

1 : 10

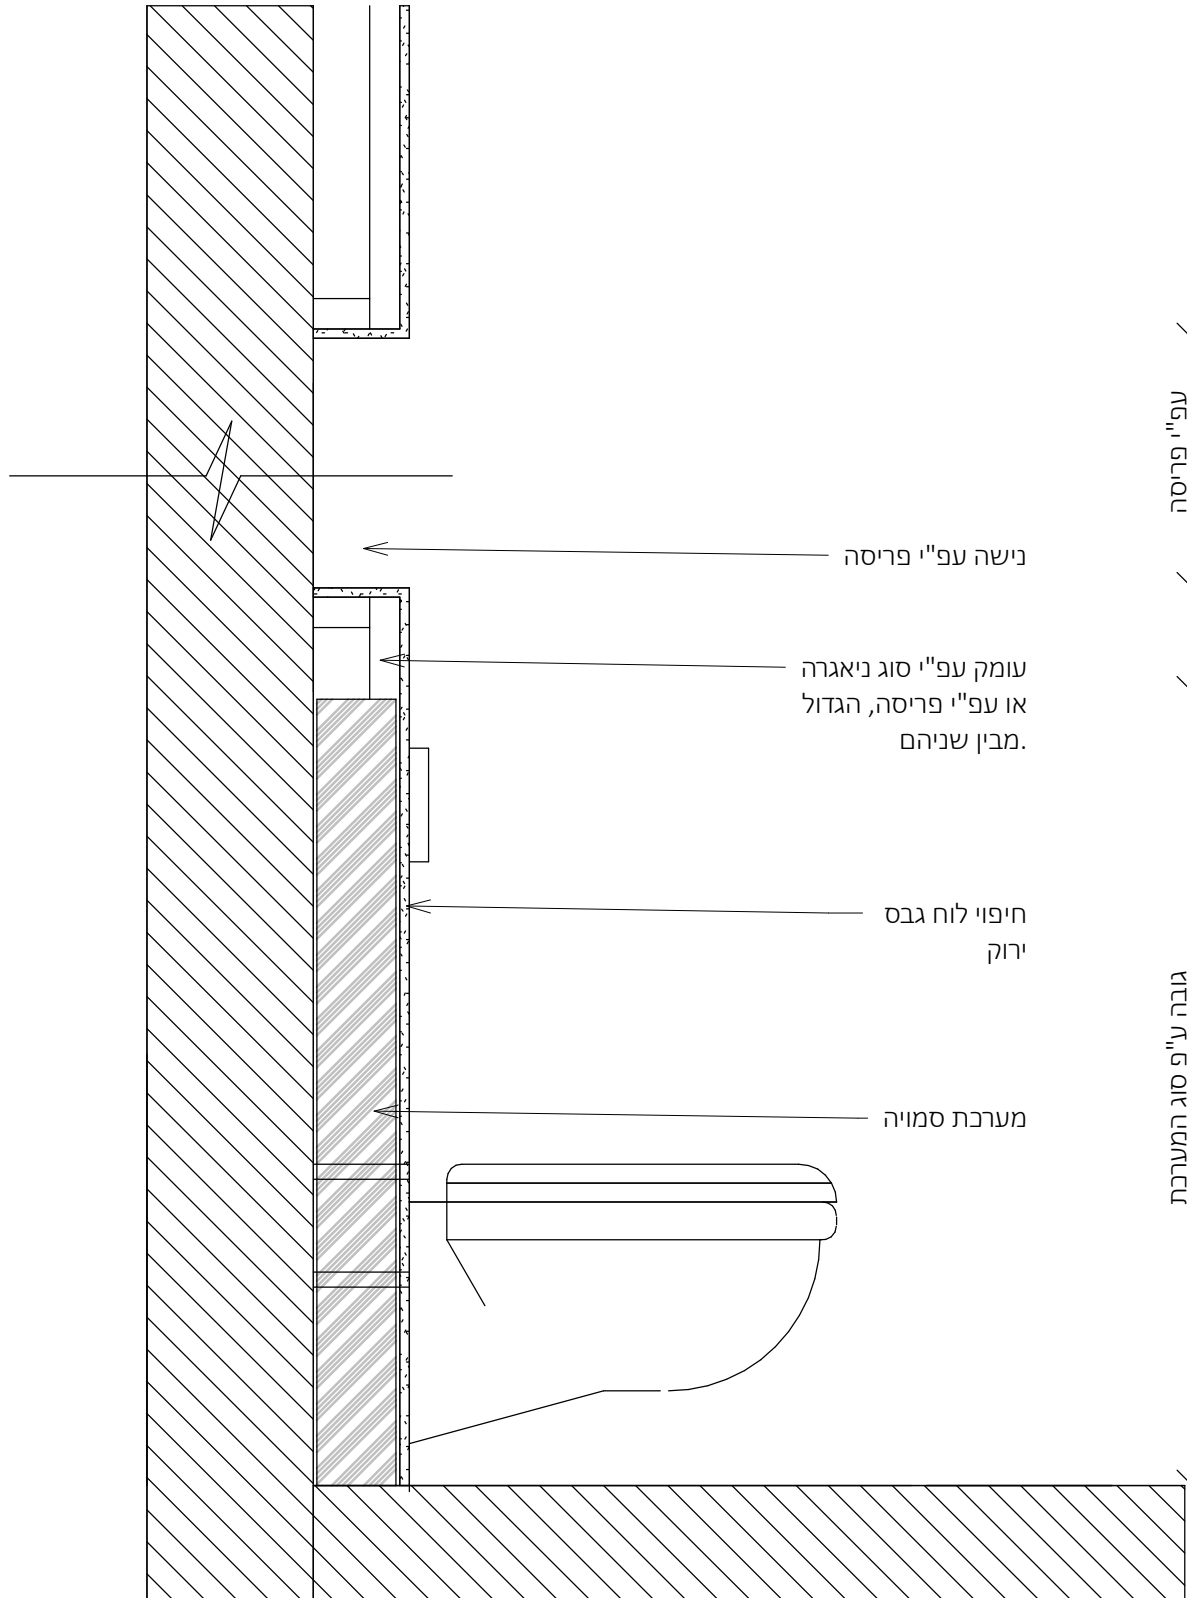

פרט 6 -אסלה תלויה מנגנון סמוי בעיבוי גבס

יש לעבוד במקביל לפרטים שיספק
מעצב הפנים (במידה וקיים במגרש זה)
המאושרות על ידי האדריכל.

פרטי האיטום באחריות יועץ האיטום
ראה חוברת פרטי איטום מצורפת

להמשך תיאום

רשימת חלונות					
סוג	תיאור	כמות	גובה	רוחב	מס פריט

1	90	110	1	צלון רפפה חיצוני חשמלי + ארגז חיצוני	חלון קיפ פרופיל 4500 קליל
2	220	240	1	צלון רפפה חיצוני חשמלי + ארגז חיצוני	ויטרינה פרופיל 7500 קליל
3	110	110	2	צלון רפפה חיצוני חשמלי + ארגז חיצוני	חלון הזזה פרופיל 7000 קליל
4	580	240	1	צלון רפפה חיצוני חשמלי + ארגז חיצוני	ויטרינה פרופיל 7500 קליל
5	200	240	1	צלון רפפה חיצוני חשמלי + ארגז חיצוני	ויטרינה פרופיל 7500 קליל
6	90	240	1	צלון רפפה חיצוני חשמלי + ארגז חיצוני	דלת כנף פרופיל 4350 קליל

כל פריט יחולק למינימום הכנפיים האפשרי (לתיאום מול ספק האלומיניום ובמסגרת שרטוטי shop drawing)

רשימת דלתות					
סוג	הערות	כמות	גובה	רוחב	מספר פריט

נוימן חיינר אדריכלים בע"מ

D:\NH-Arch-Dropbox\NH-Arch-Projects\NH---בתים ודירות
FILE NAME: -----\nofia\טרם - תכנית בסיסית\ריטמודל - 00\20\להיתר\כלל הפרויקטים