


פתחי גישה אופן ארט בתיאום סופי מול אדריכל
כלל יחידות המיזוג אשר נמצאות בתוך נגרות יש לתאם סופית מול אדריכל ונגרות


Court 20 1st Floor

Option No2
inverter duct unit in living
room and wall mounted in
rooms

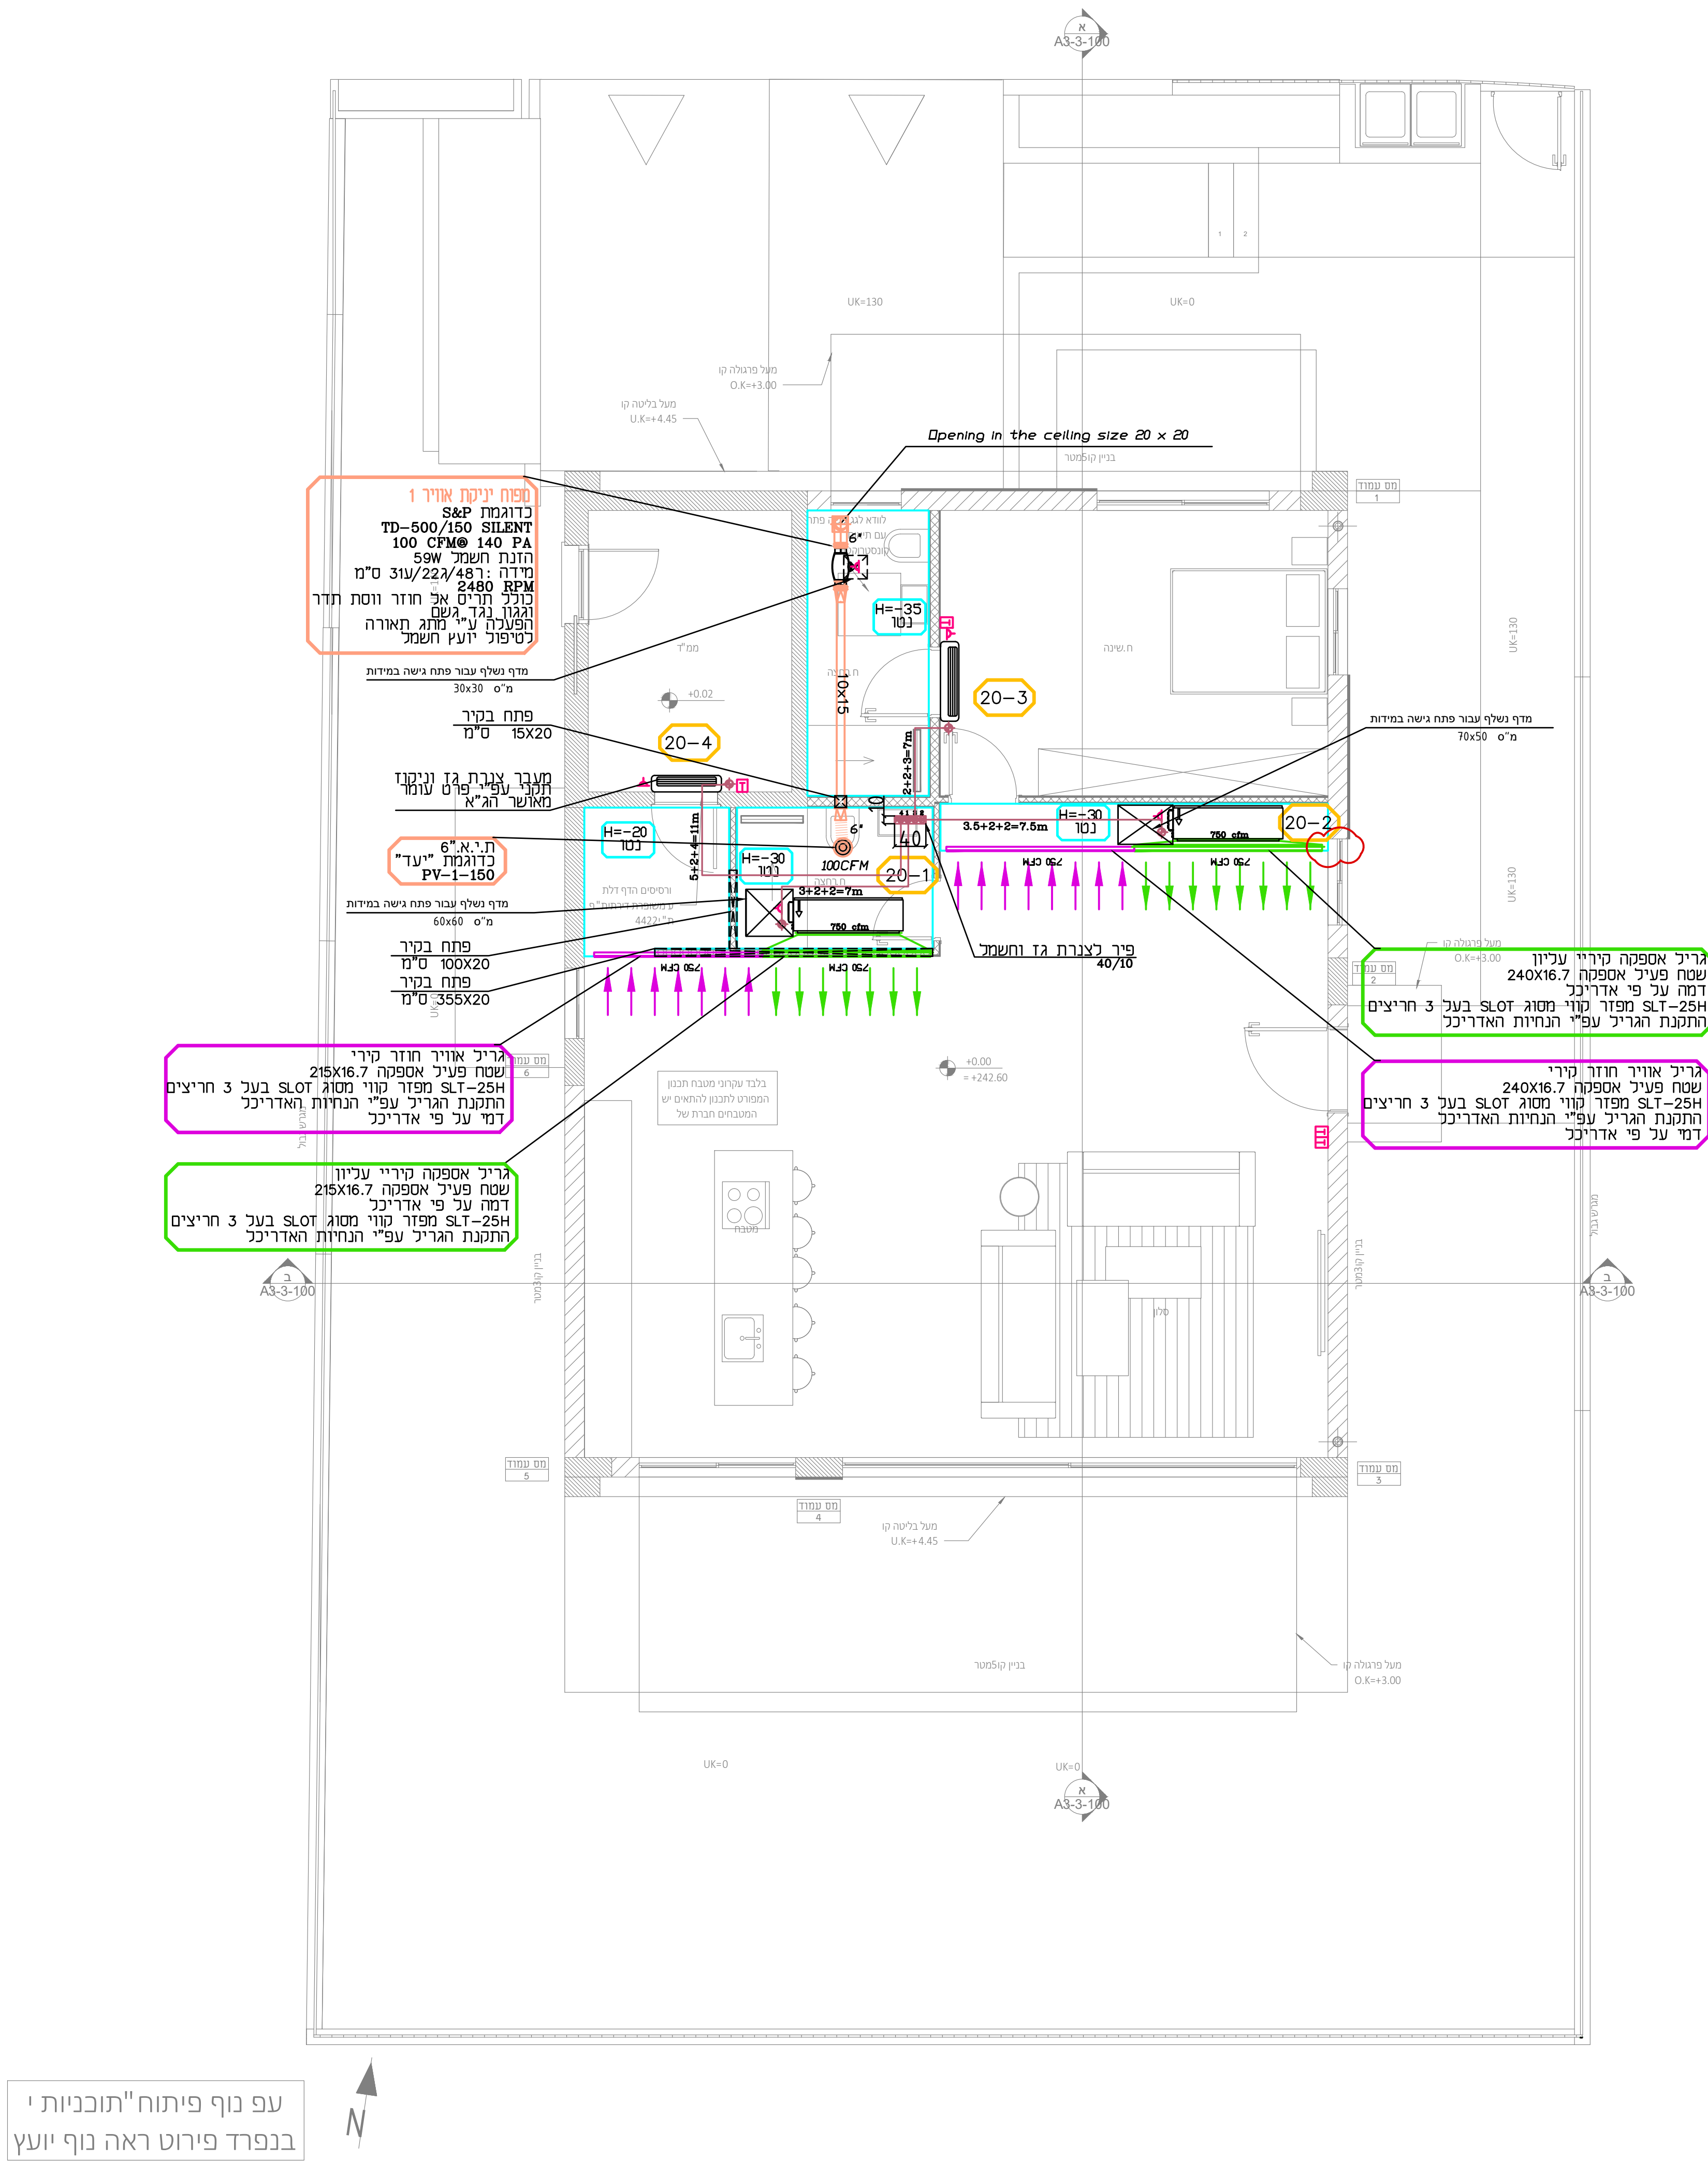

Court 20 Roof

Option No2
inverter duct unit in living
room and wall mounted in
rooms

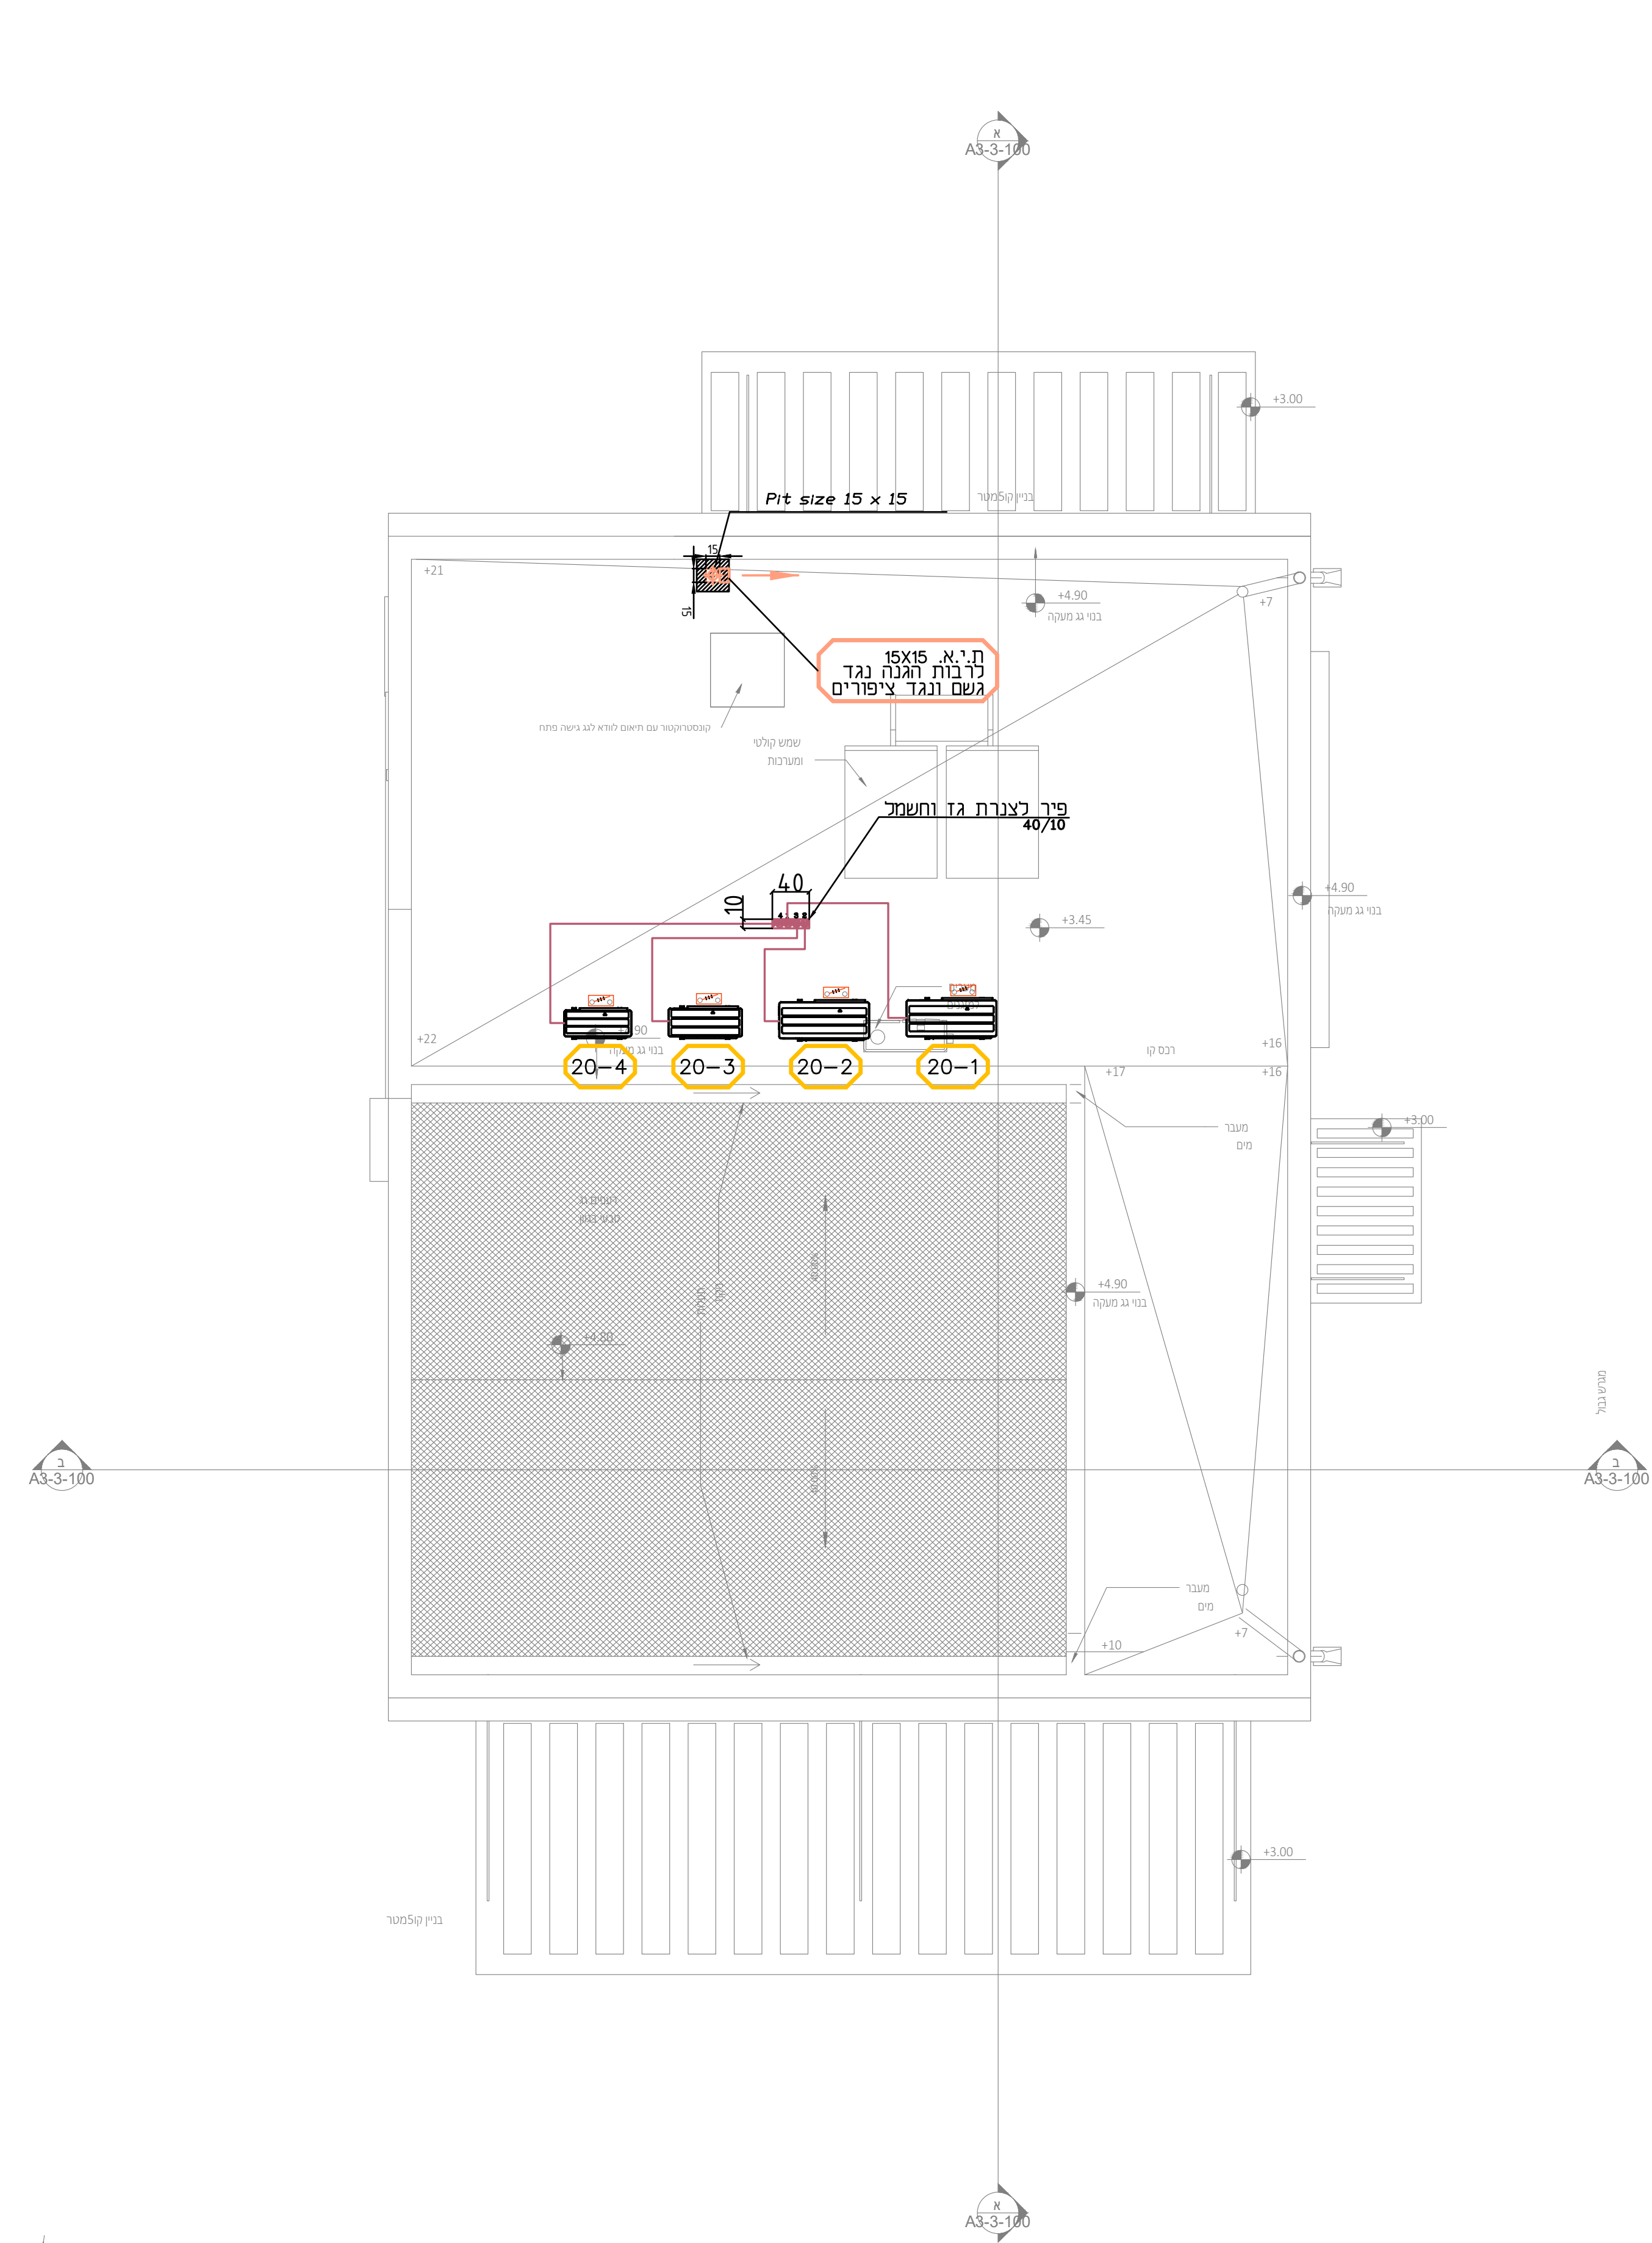

תפוצה						
אדריכל	לוח	תוכן ראשי	תוכן ראשי	תוכן ראשי	תוכן ראשי	תוכן ראשי
אדריכל	לוח	תוכן ראשי	תוכן ראשי	תוכן ראשי	תוכן ראשי	תוכן ראשי
אדריכל	לוח	תוכן ראשי	תוכן ראשי	תוכן ראשי	תוכן ראשי	תוכן ראשי
אדריכל	לוח	תוכן ראשי	תוכן ראשי	תוכן ראשי	תוכן ראשי	תוכן ראשי
אדריכל	לוח	תוכן ראשי	תוכן ראשי	תוכן ראשי	תוכן ראשי	תוכן ראשי
אדריכל	לוח	תוכן ראשי	תוכן ראשי	תוכן ראשי	תוכן ראשי	תוכן ראשי
אדריכל	לוח	תוכן ראשי	תוכן ראשי	תוכן ראשי	תוכן ראשי	תוכן ראשי
אדריכל	לוח	תוכן ראשי	תוכן ראשי	תוכן ראשי	תוכן ראשי	תוכן ראשי
אדריכל	לוח	תוכן ראשי	תוכן ראשי	תוכן ראשי	תוכן ראשי	תוכן ראשי

מהדורה	
08.05.2025	תוכן ראשי
01.04.2025	תוכן ראשי
01.04.2025	תוכן ראשי
01.04.2025	תוכן ראשי
01.04.2025	תוכן ראשי
01.04.2025	תוכן ראשי
01.04.2025	תוכן ראשי
01.04.2025	תוכן ראשי
01.04.2025	תוכן ראשי
01.04.2025	תוכן ראשי

המבצע אחראי למידות ובהתאמתן למציאות
בכל מקרה של אי התאמה, מתירה או טעות
עליו להודיע למחננו לפני התקדמותו בביצוע
אין להבטיח מידות על סמך מדידות בשטח.
אין לעשות כל שימוש בחוכנית זו
או ברעיונות והגומים בה ללא אישור בכתב
מאת המחננו.

הערות

- כל התעלות מחוץ למבנה יבודדו
בידוד אקוסטי בעובי 2"
- תעלות מזוג בתוך המבנה יבודדו
בידוד אקוסטי פנימי 1"
- תעלות אוויר צח יבודדו
בידוד טרמי 1"
- יש לאסום בסיקור את פינות החיבור
של תעלות מיזוג אוויר לפני כיפוף
הפזים המתחברים

מקרא

- מפ- מפוח
- מ.א.ג. - מפזר אוויר קורי
- מ.א.ת. - מפזר אוויר תתקרי
- מ.א.ת. - תריס אוויר חודר
- מ.א.ת. - תריס אוויר צח
- ב.א. - בידוד אקוסטי
- ב.ס. - בידוד טרמי
- כ.ב. - כלא בידוד
- ד.א. - דמפר אש
- טרמסטט לוח הפעלה
- שקע חשמל לספוף יועץ חשמל
- שקע תלת פאזי לספוף יועץ חשמל
- מפסק בסחון חוד פאזי לספוף יועץ חשמל
- מפסק בסחון תלת פאזי לספוף יועץ חשמל
- ניקוז מאיד לספוף יועץ אינסטלציה
- בגובה 25 ס"מ מתחתית גובה המאיד
- שלת הפעלה אלקטרוני

מקרא צבעים בתכנית

- תעלות ותריסי אוויר חודר
- תעלות ותריסי אספקת אוויר
- תעלות ותריסי אוויר צח
- תעלות ותריסי יניקת אוויר
- תעלות ותריסי שיחרור עשן
- צנרת גז וחשמל
- סימון מעגלי מיזוג אוויר

191	מבני מגורים צמודי קרקע נופיה ארפי מנשה מגרש 20
1:50	מיזוג אוויר ואיוורור
08.05.2025	תוכן ראשי
01.04.2025	תוכן ראשי
01.04.2025	תוכן ראשי
