

מתכונים:


ניהול פרויקט
בן סולומון - מהיסוד
פיקוח
מהיסוד - בן סולומון
קונסטרוקציה
ערן שילר
מיזוג אוויר
אייל ארז מהנדסים ויועצים בע"מ
אינסטלציה
איתן אלמסי
חשמל
איתן בסיס
אלומיניום
נוף
נתי בלוקא
חשמל חכם
חימום תת רצפתי
איטום
צבי טל
אקוסטיקה
מעליות
קרקע וביסוס
דיה הנדסת קרקע וביסוס
רישוי

$$+ 0.00 = +245.00$$

הערות:
 1. תביתו ויש לקרוא יחד עם הכביות הוועצים.
 2. גובה אסכולים: ארבע תביות פחות.
 3. המידות הן בין קירות ואלו כולל מים.
 4. פחות השטח שמיני המהרה, כלכל, מדורות, שבילים, רציפות, פשיטות בסיס.
 5. פחות היתר: ארבע תביות במגע עם הקרקע ובידוד תרמי לאורך המעטדים.
 6. הקורות על הקירות: גליות או עם מיני (גילון) – ארבע תביות קונסטרוקציה.
 7. אף אם כיבוע כל מישור אופקי חמור.
 8. שני תרמי במסגרת עם מפרס מומקד, חמור.
 9. שני פידוק מוקד.

[illegible]

מקרא קירות:

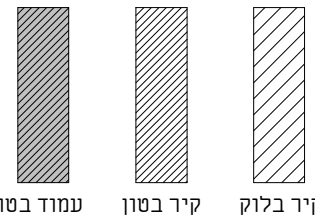[illegible]

אדריכלות

CLIENT NAME: _____ שם המזמין:

קבוצת רכישה נופיה

PROJECT NAME: שם הפרויקט:

נופיה - מגרש 21

DRAWING NAME: ס הגליון:

SHEET NUMBER: 190 גליון:

A3-1-100

SCALE:	קנה מידה:	EDITION:	חזרה:
STATUS:	סטטוס		
למכר	נבדק עין:		דרסט עין:
DATE:	22.09.2025		מיר:



NeumanHaynerArchitects


office@nh-arch.com
www.nh-arch.com

וימן חיינר אדריכלים
מורד ההדרים 2, בית חירות
טל 09-9545842

זכויות ייצור / ע"פ הנחיות עו"ד

נופיה - מגרש 21			
מס' גיליון	שם גיליון	מהדורה	תאריך הפצת מהדורה

22.09.2025	1	גליון שער	A3-1-100
22.09.2025	1	תכנית קומת קרקע	A3-1-101
22.09.2025	1	תכנית מפלס גג	A3-1-102
22.09.2025	1	חזיתות 1	A3-2-200
22.09.2025	1	חזיתות 2	A3-2-201
22.09.2025	1	חתכים	A3-3-100
22.09.2025	1	פרטים	A3-4-103
22.09.2025	1	רשימת פתחים	A3-6-1000

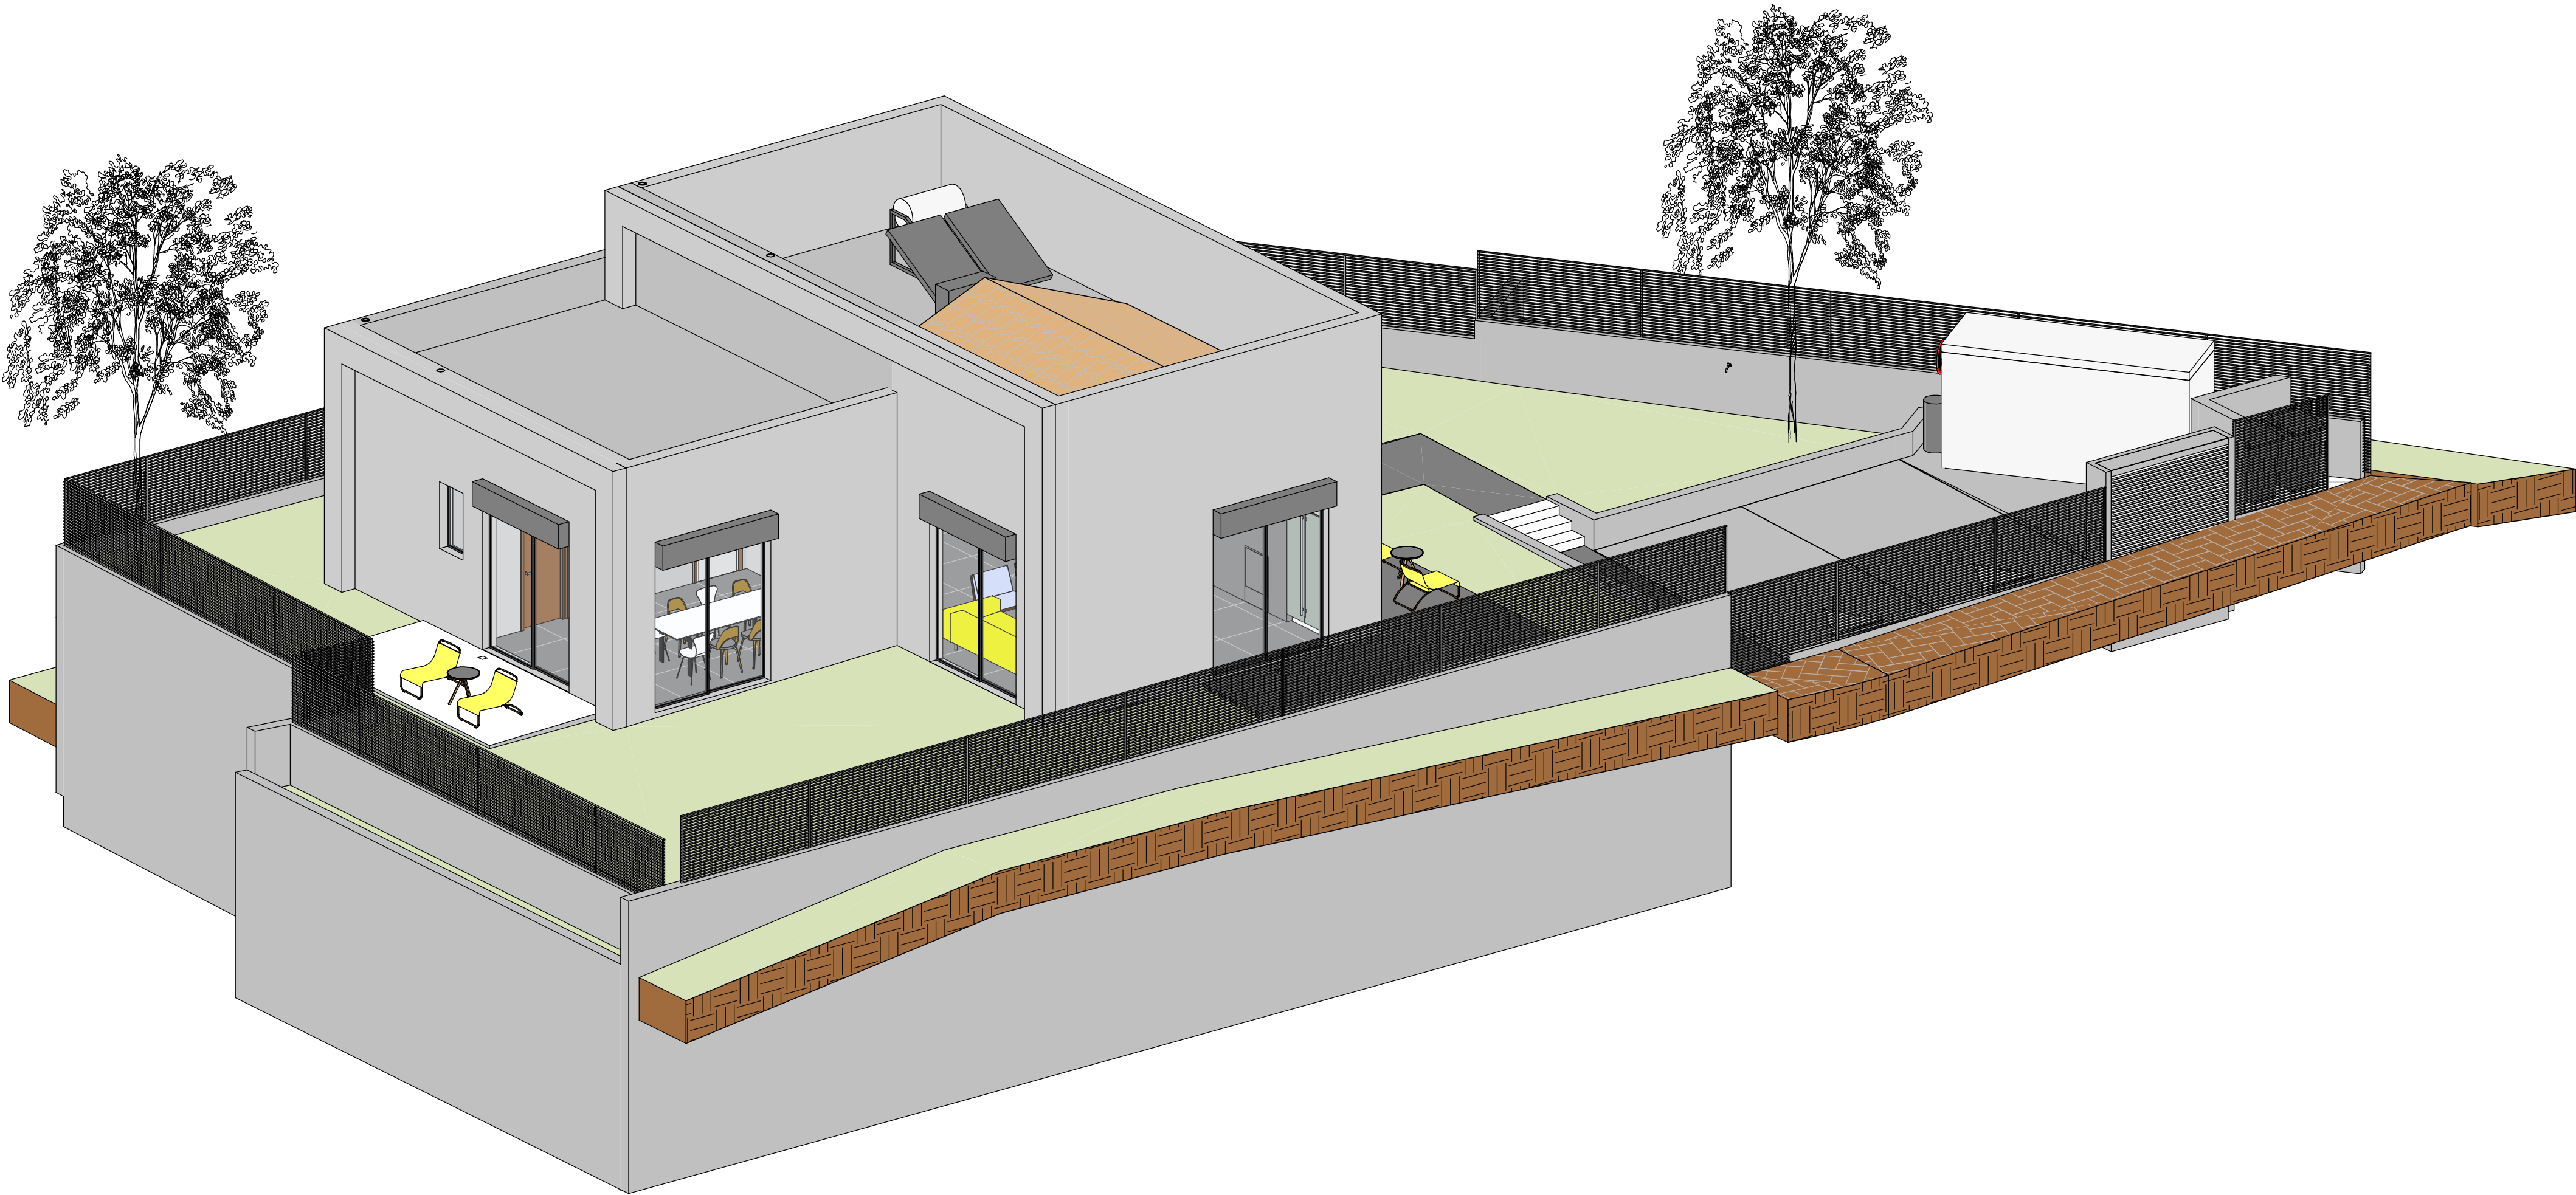

ביהול פרויקט
בן סולומון - מהיסוד
פיקוח
מהיסוד - בן סולומון
קונסטרקציה
ערן שילר
מיזוג אוויר
אייל ארז מהנדסים ויועצים בע"מ
אינסטלציה
איתן אלמסי
חשמל
איתן בסיס
אלומיניום
נרף
נתי בלוקא
חשמל חכם
חימום תת רצפתי
איטום
צבי טל
אקוסטיקה
מעליות
קרקע וביסוס
דיה הנדסת קרקע וביסוס
ירשני

[illegible][illegible]

CLIENT NAME: _____: המזמין:

PROJECT NAME: הפרויקט

DRAWING NAME: 010712.0

NAME	TECHNICAL	EDITION	3335
------	-----------	---------	------

1 : 50 

STATUS: סמטוט **1**

למכרז	
-------	---

100	100
-----	-----


DATE: 22.09.2025 י"ד



רמן פונוב אדריכלות

office@nh-arch.com
www.nh-arch.com

זכויות ייצור / ע"פ הנחיות עו"ד

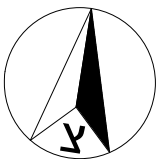

1 : 50

- הערות:
1. יש לעבוד במקביל לתכניות יועצים המאשרות על ידי האדריכל.
 2. פרטי ספי חלון - עפ"י חוברת אלומיניום של הספק הנבחר ובתיאום מול אדריכל.
 3. חימום תת רצפתי (במידה ויש במגרש זה) עפ"י פרטי הספק ובתיאום מול אדריכל.
 4. יש לעבוד במקביל לתכניות עיצוב פנים (במידה ויש מעצב פנים במגרש זה) המאשרות על ידי האדריכל.
 5. באחריות הקבלן לעדכן את האדריכל על אי התאמה בין התכניות יועצים לאדריכלות.
 6. כל הדלתות לפי מפרט מצורף.
 7. כל אלמנטי הבטון יקבלו התייחסות תרמית לפי הנחיות יועץ.
 8. פרטי איטום, בידוד וניקוז עפ"י תכניות יועצים ובאחריות הקבלן.


פרטי איטום, בידוד וניקוז עפ"י תכניות יועצים ובאחריות הקבלן

מתכונים:

ניהול פרויקט
בן סולומון - מהיסוד
פיקוח
מהיסוד - בן סולומון
קונסטרוקציה
ערן שילר
מיזוג אוויר
אייל ארז מהנדסים ויועצים בע"מ
אינסטלציה
איתן אלמסי
חשמל
איתן בסיס
אלומיניום
נוף
נתי בלוקא
חשמל חכם
חימום תת רצפתי
איטום
צבי טל
אקוסטיקה
מעליות
קרקע וביסוס
דיה הנדסת קרקע וביסוס
רישוי

[illegible]

מקרא קירות:

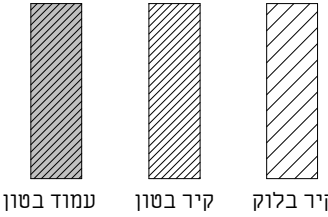[illegible]

אדריכלות

קבוצת רכישה נופיה


בופיה - מגרש 21

חזיתות 1




וימן חיינר אדריכלים
מורד ההדרים 2, בית חירות
טל 09-9545842

מורד ההדרים 2, בית חירות
טל 09-9545842

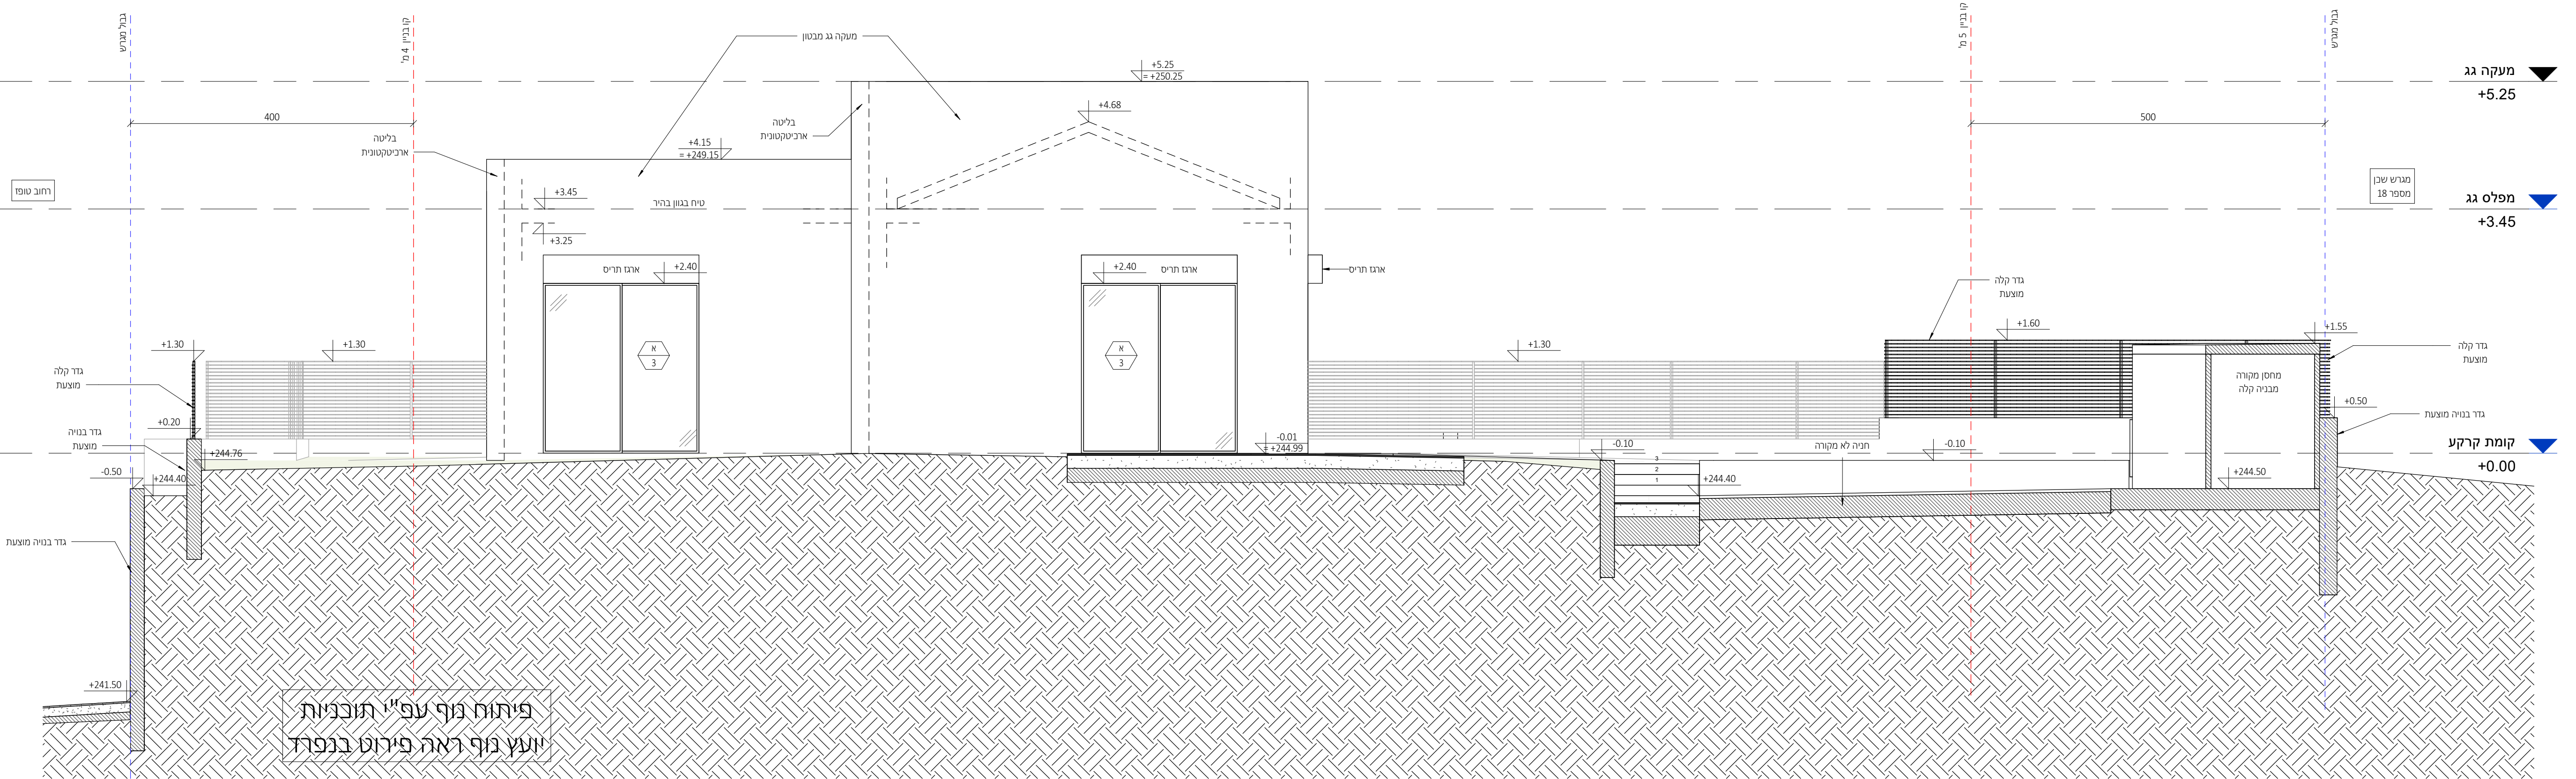

חזית דרומית

1 : 50

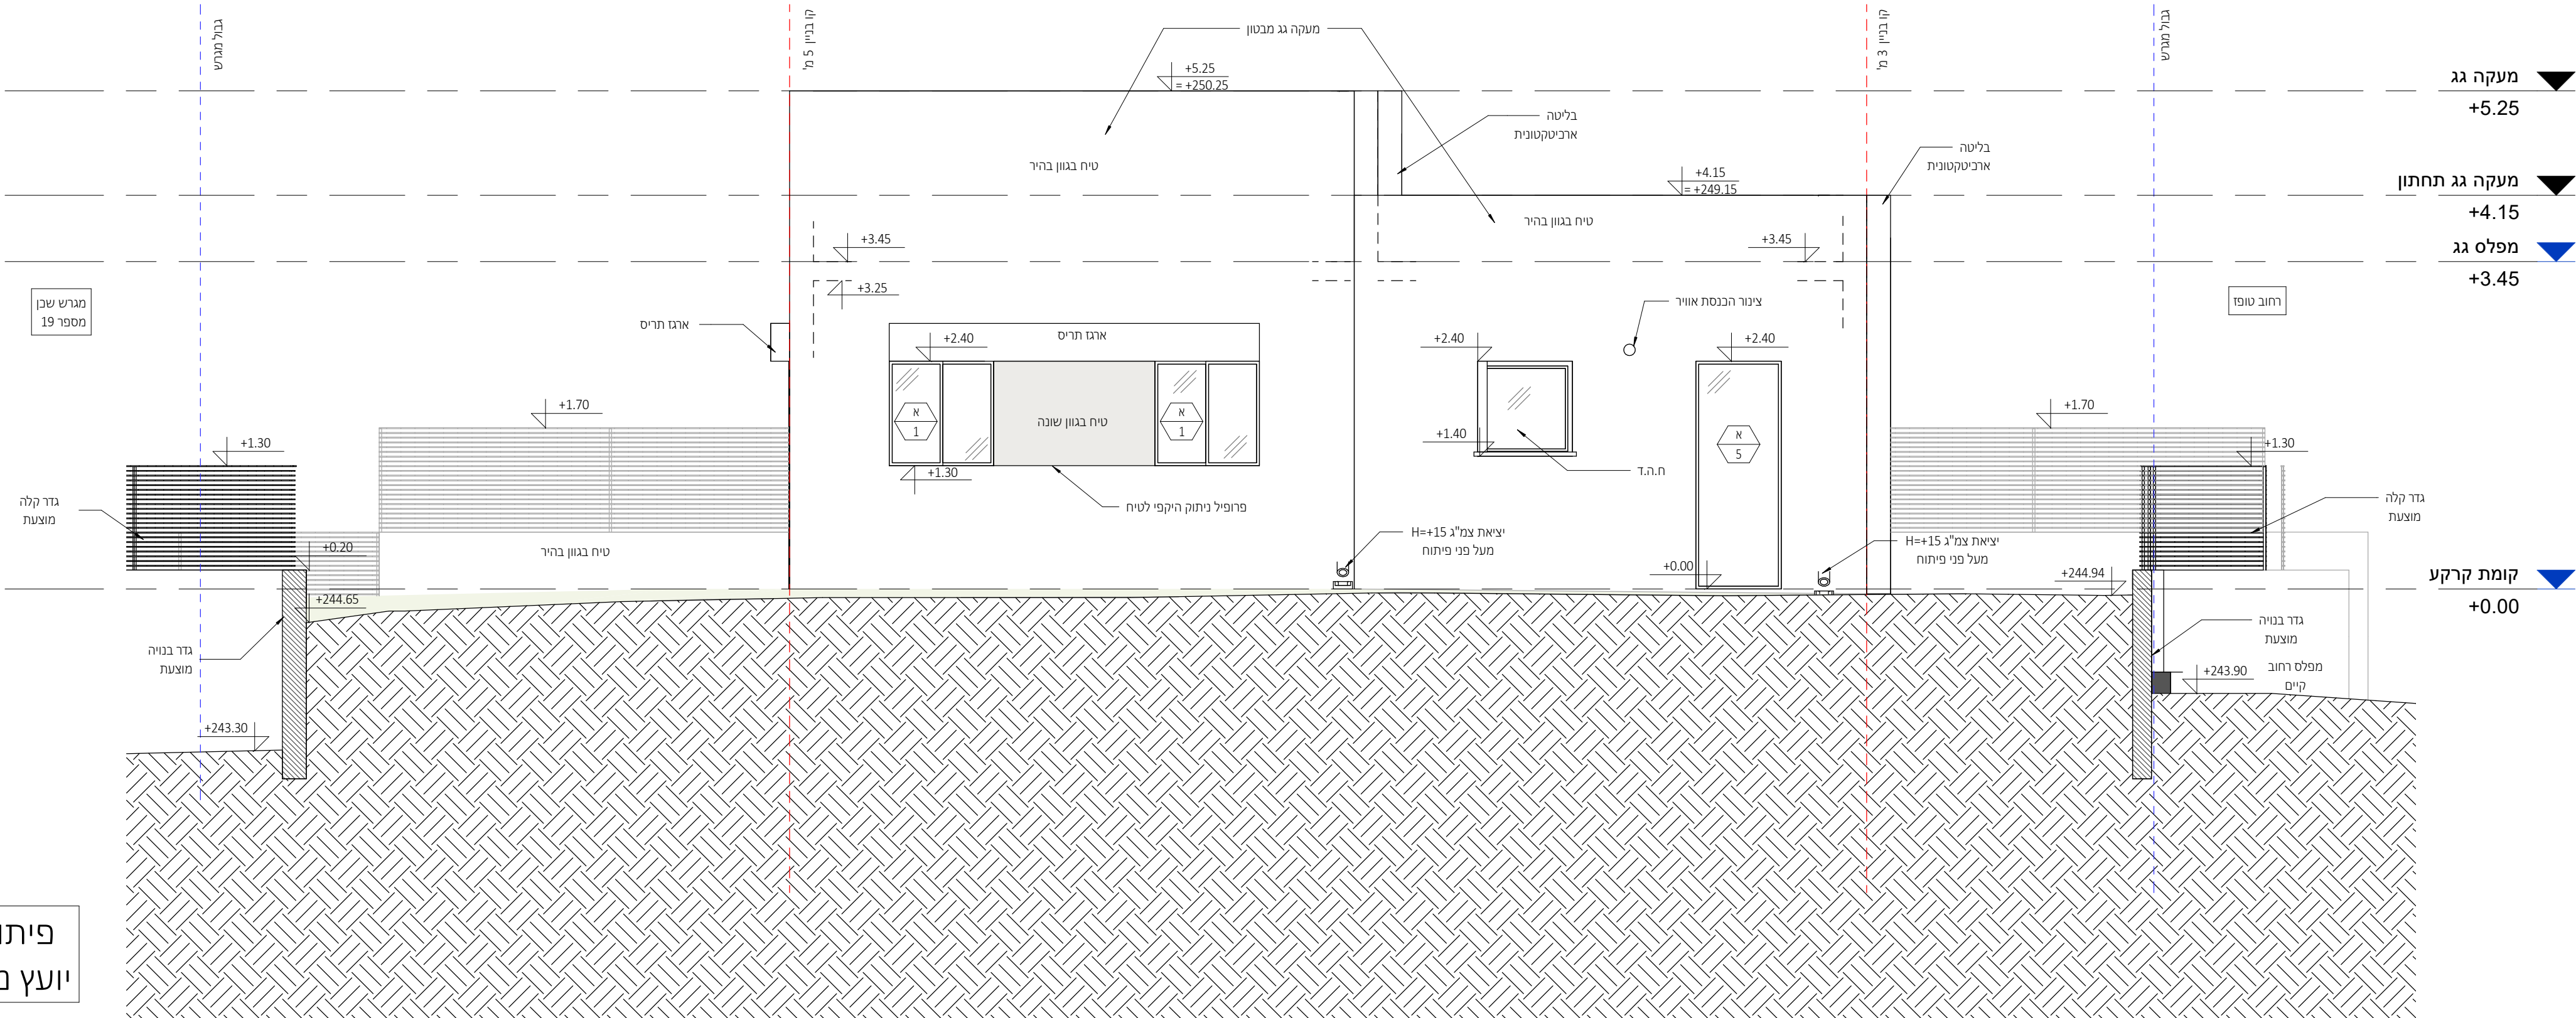

חזית צפונית

1 : 50

פיתוח נוף עפ"י תוכניות
יועץ נוף ראה פירוט בנפרד

מתכננים:

ניהול פרויקט
בן סולומון - מהיסוד
פיקוח
מהיסוד - בן סולומון
קונסטרוקציה
ערן שילר
מיזוג אוויר
אייל ארז מהנדסים ויועצים בע"מ
אינסטלציה
איתן אלמסי
חשמל
איתן בסיס
אלומיניום
נוף
נתי בלוקא
חשמל חכם
חימום תת רצפתי
איטום
צבי טל
אקוסטיקה
מעליות
קרקע וביסוס
דיה הנדסת קרקע וביסוס
רישוי

± 0.00 = +245.00
הערות: 1. תכנית זו יש לקרוא יחד עם תכנית הריטשים. 2. גובה אבטמנטים: ראה תכנית פיתוח. 3. המידות הן בין קירות הבניה ולא כולל פיתוח. 4. פיתוח השטח סביב הבנוה, כולל, מדרגות, נדרות, שנילים, ריצופים, שפופים, גדרים, חניה וגן ראה תכנית פיתוח. 5. איטום קירות ורצפות הבנוה כמנוע עם הקרקע ובידוד תרמי לאורך העמודים והקירות וסל במידת הצורך (גומן)- ראה תכנית קונסטרוקציה. 6. אף דום יבוצע בכל מישור אופקי הכולל מהבנוה. 7. סיוח תרמי במסגרת ע"פ מפרט תרמוקיר, מאושר ע"י פיקוח העודף. המבצע אחראי למידות : עליו לבקר ולבדוק את כל המידות בתכנית ובקטע הטכניקה. במסגרת של מידות או אי התאמה בתכנית /או בבנוה, עליו להודיע על כך מיד לאדריכל בסיום המשיך בעבודותיו. המבצע ישתמש אך ורק בחומרים שאושרו לכניסה. המבצע יחזיק במלא, בכל עת, של משרדו של תכנית. אין לקבוע מידות על ידי חריזה בשר מוס. התכנית הנה רשומה האדריכלי ואין לשנות כל שימוש בה או ברעיונות הגולמים בה, אלא באישור בכתב מהאדריכל. מהנדס /או יועץ אשר שמו רשום בתכנית זו, נושא לכיד באחריות המקצועית והטכנית לתכנית. על המפקח והקבלן לוודא התאמת התכנית האדריכלית "כניסיו" לתכנית זו, והוכר התכנית והאישות ע"י כל הגורמים הרשמיים. התכנית כוללת את כל האמצעים והידוע עד ליום תחפשת.

משרד קירות:
קיר בלוק קיר בסון עמוד בסון

תאריך	תיאור	מהדורה
22.09.2025	מכרז	1

אדריכלות	
המסמך:	CLIENT NAME:
קבוצת רכישה נופיה	
הפרויקט:	PROJECT NAME:
נופיה - מגרש 21	
הגליון:	DRAWING NAME:
חזיתות 2	
מספר גליון:	SHEET NUMBER:
A3-2-201	
הדור:	EDITION:
קנה מידה:	SCALE:
1	1 : 50
סטוס:	TATUS:
למכרז	
נבדק ע"י:	סטוס ע"י:
22.09.2025	DATE:
ירד	


NeumanHaynerArchitects

נירסן חיינר אדריכלים
מודד והנדס 2, בית חירות
09-9545842 78
office@nh-arch.com
www.nh-arch.com

27/10/2025 7:42:12


זכיות ייצור / ע"פ הנחיות ע"ד

פיתוח נוף עפ"י תוכניות
יועץ נוף ראה פירוט בנפרד

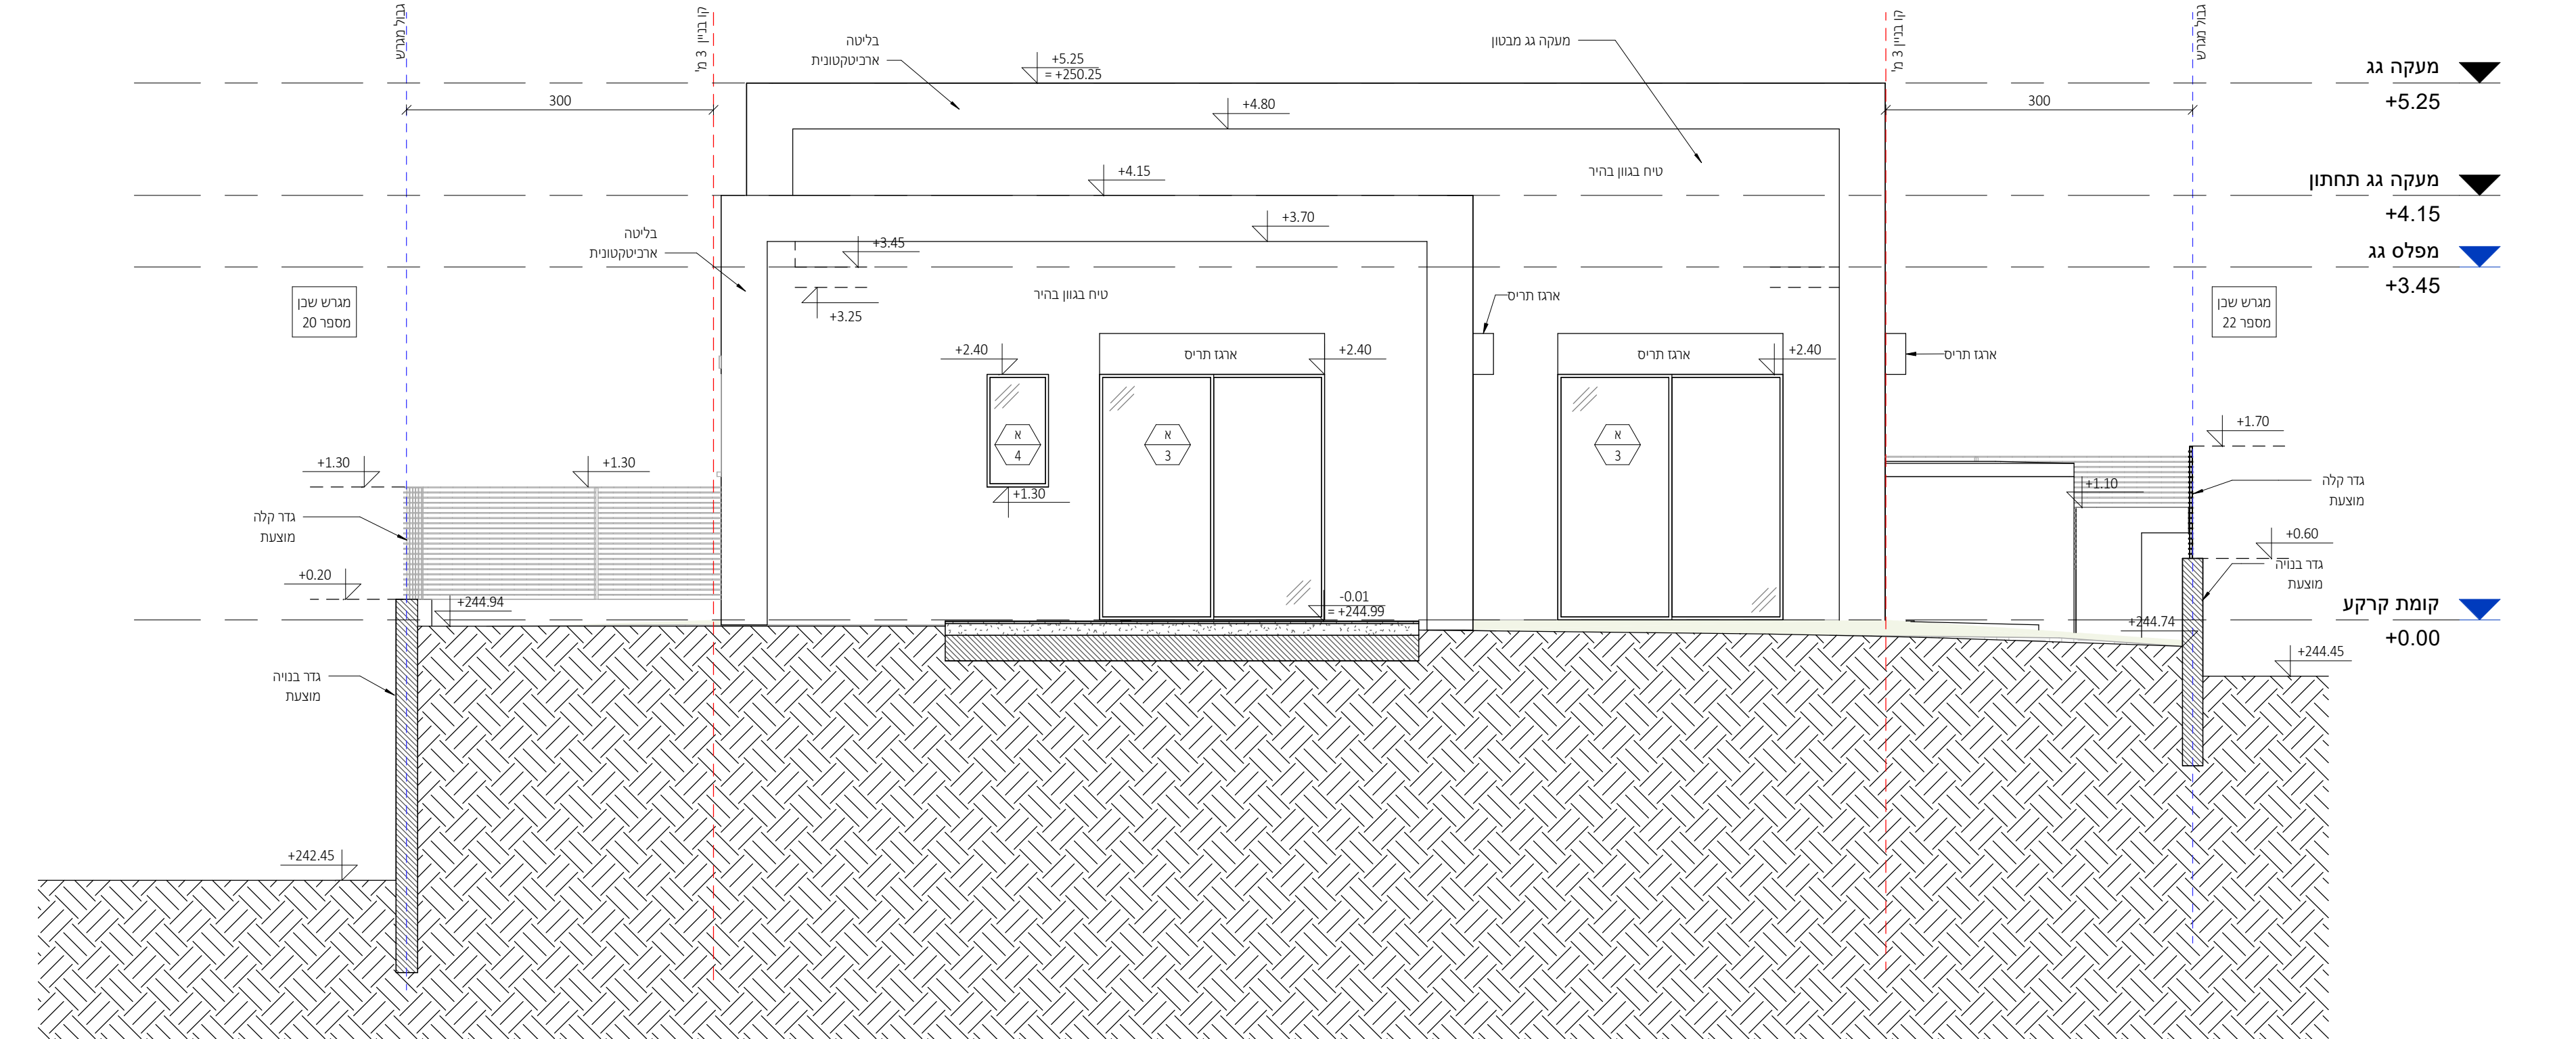

חזית מערבית

1 : 50

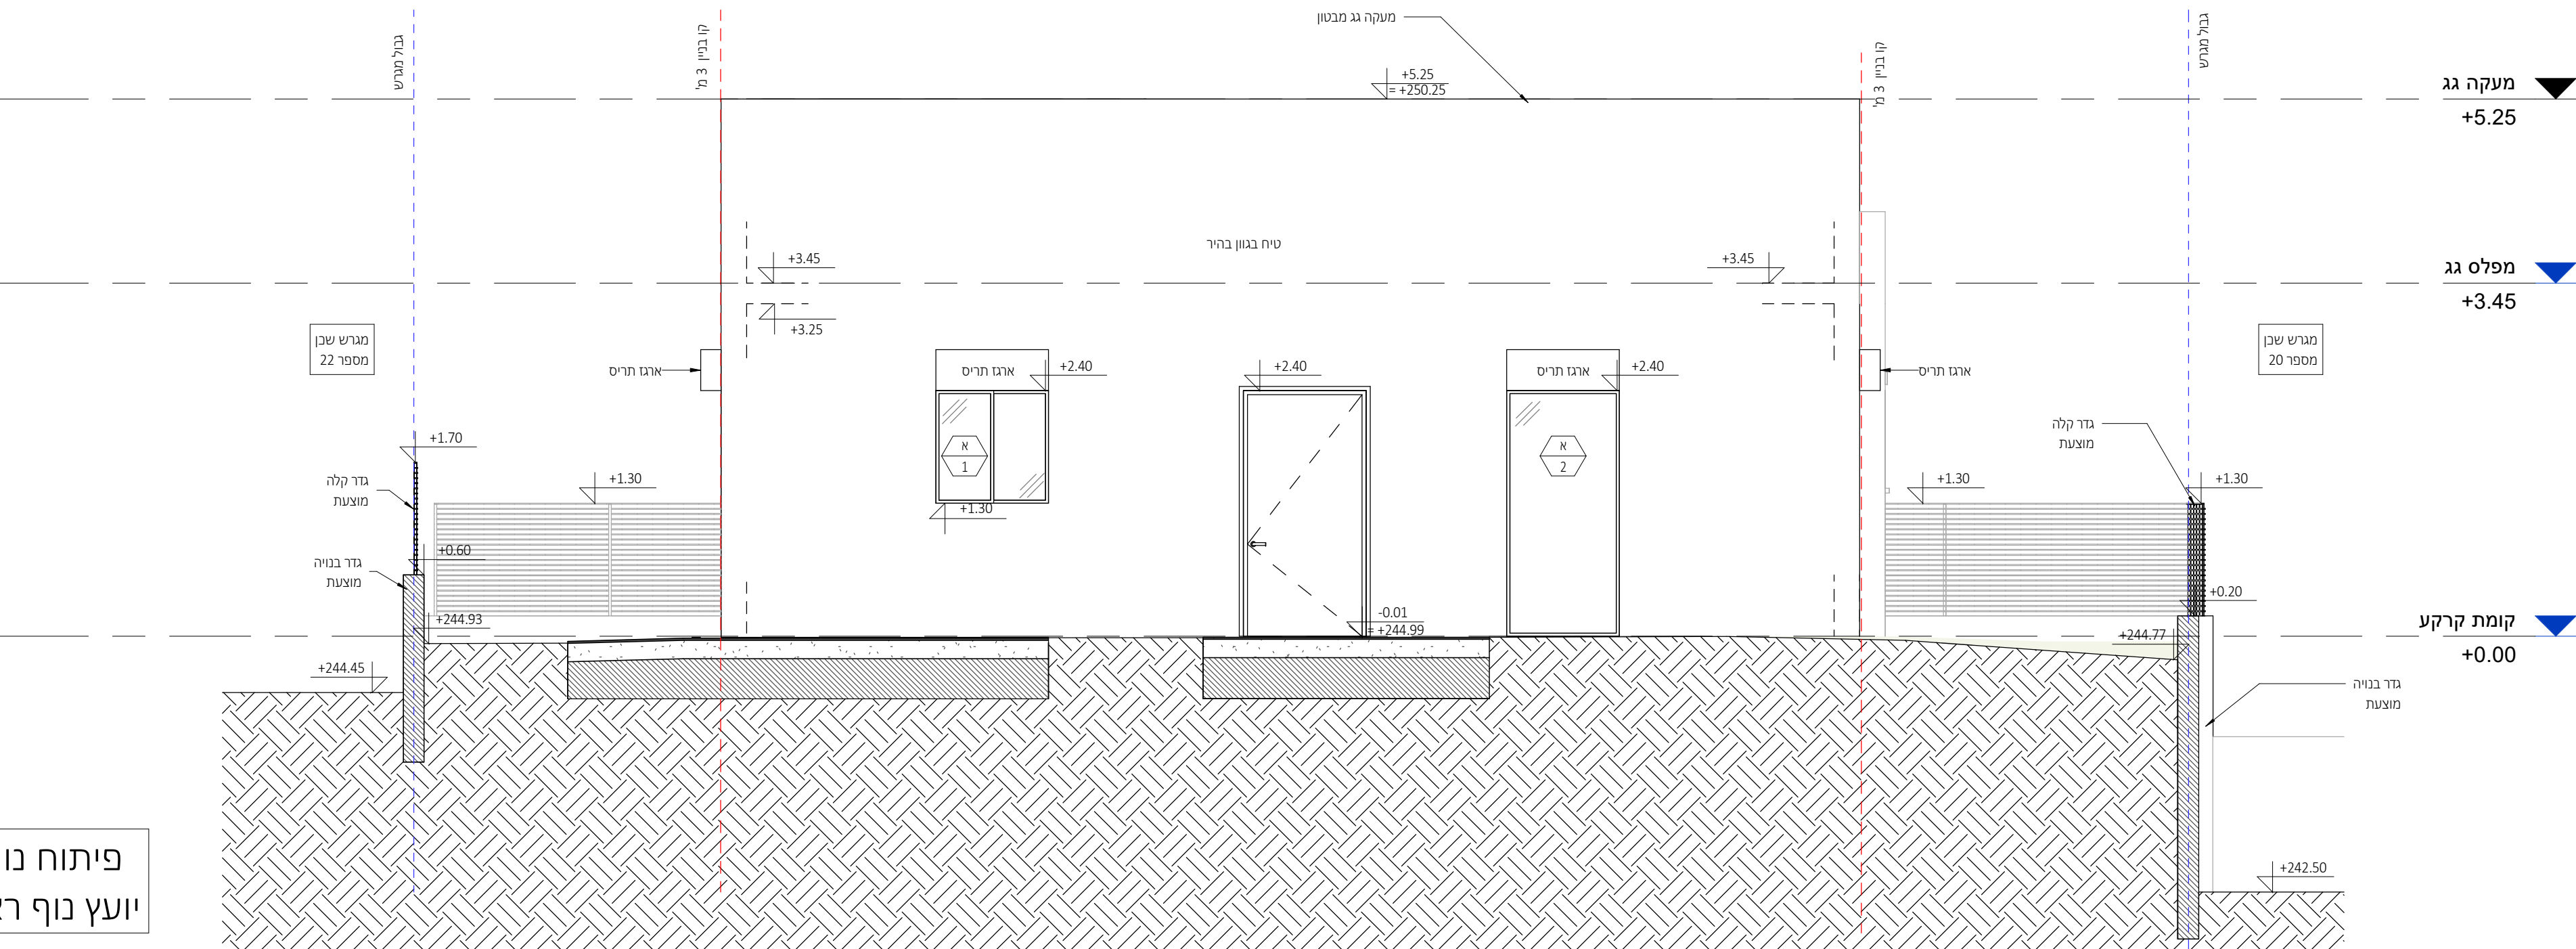

חזית מזרחית

1 : 50

פיתוח נוף עפ"י תוכניות
יועץ נוף ראה פירוט בנפרד

פרטי איטום, בידוד וניקוז עפ"י תכניות יועצים ובאחריות הקבלן

מתכונים:

ניהול פרויקט
בן סולומון - מהיסוד
פיקוח
מהיסוד - בן סולומון
קונסטרוקציה
ערן שילר
מיוזג אוויר
אייל אזר מהנדסים ויועצים בע"מ
אינסטלציה
איתן אלמסי
חשמל
איתן בסיס
אלומיניום
נוף
נתי בלוקא
חשמל חכם
חימום תת רצפתי
איטום
צבי טל
אקוסטיקה
מעליות
קרקע וביסוס
דיה הנדסת קרקע וביסוס
ירשני

± 0.00 = +245.00

הערות:
 1. תכנית זו יש לקרוא יחד עם תכניות היועצים.

הערת:
 תכנית זו איש לקראת ידע תכנית הוועיצים.
 נגבה אבסולוט. ראו תכנית פיתוח.
 הפיתוח הוא בלא קידום תכנית, כולל, מדרגות, תכנית, ריצופים, שופים, תכנית ויגור-ראו תכנית פיתוח.
 איסוס תכנית הרפואת המבנה ממנה עקרקע בידוד תמימ לאורך המעודים
 תחנת וועל התחרות, גלירות וועל פילוי (ניגור). ראו תכנית פנסוסקופיקה
 אדם קיצוע כלל תכנית אופיקי הובלס תכנית.
 פחית תחנת תכנית, טיפ פנסוסקופיקה, תאמור טיפ פיקוד העורפ.

[illegible]

מקרא קירות:

קיר בלוק קיר בטון עמוד בטון

[illegible]

אדריכלות

CLIENT NAME: _____; המזמין:

קבוצת רכישה נופיה

PROJECT NAME: הפרויקט:

בופיה - מגרש 21

DRAWING NAME: תגליון:

חתימים

SHEET NUMBER: 99 גליון:

A3-3-100

SCALE: _____: קנה מידה: EDITION: _____: דורה:

1 : 50

STATUS: סטטוס 1

למכרז


דסט ע"י: _____ נבדק ע"י: _____

DATE: 22.09.2025 17:17

1. The first step is to identify the problem or question that needs to be answered. This involves understanding the context and the specific requirements of the task.


office@nh-arch.com מרכז ההדורים 2, בית חירות

ISSN 0013-788X print; ISSN 1366-5847 online © 2005 Taylor & Francis Ltd.

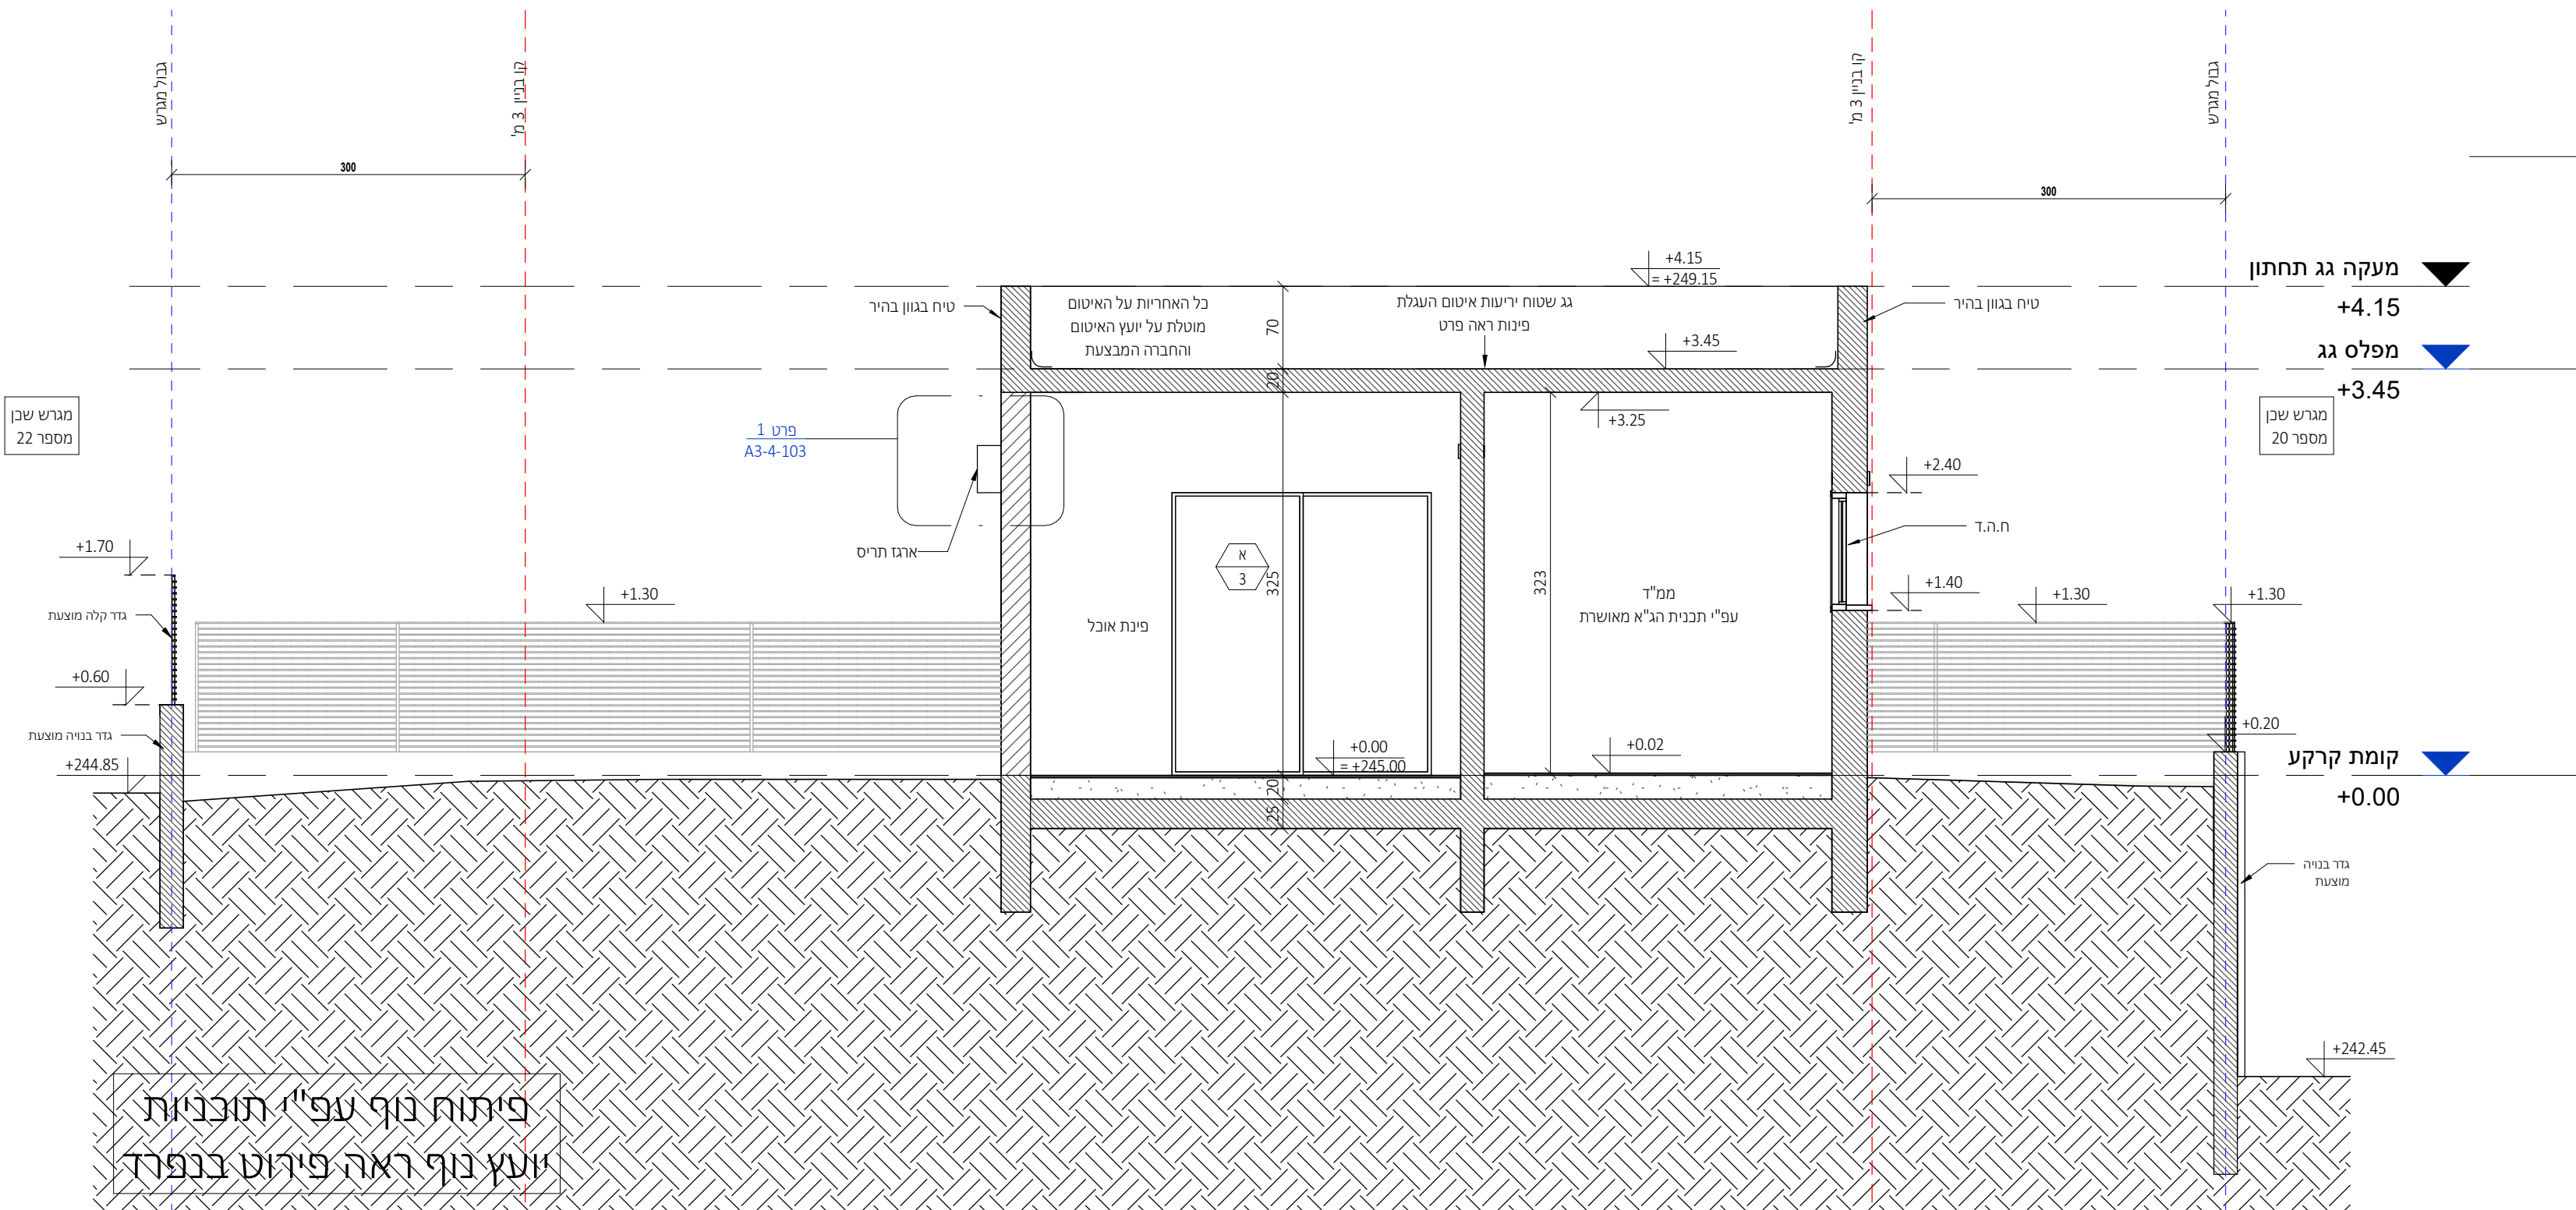


חתך א-א

1 : 50

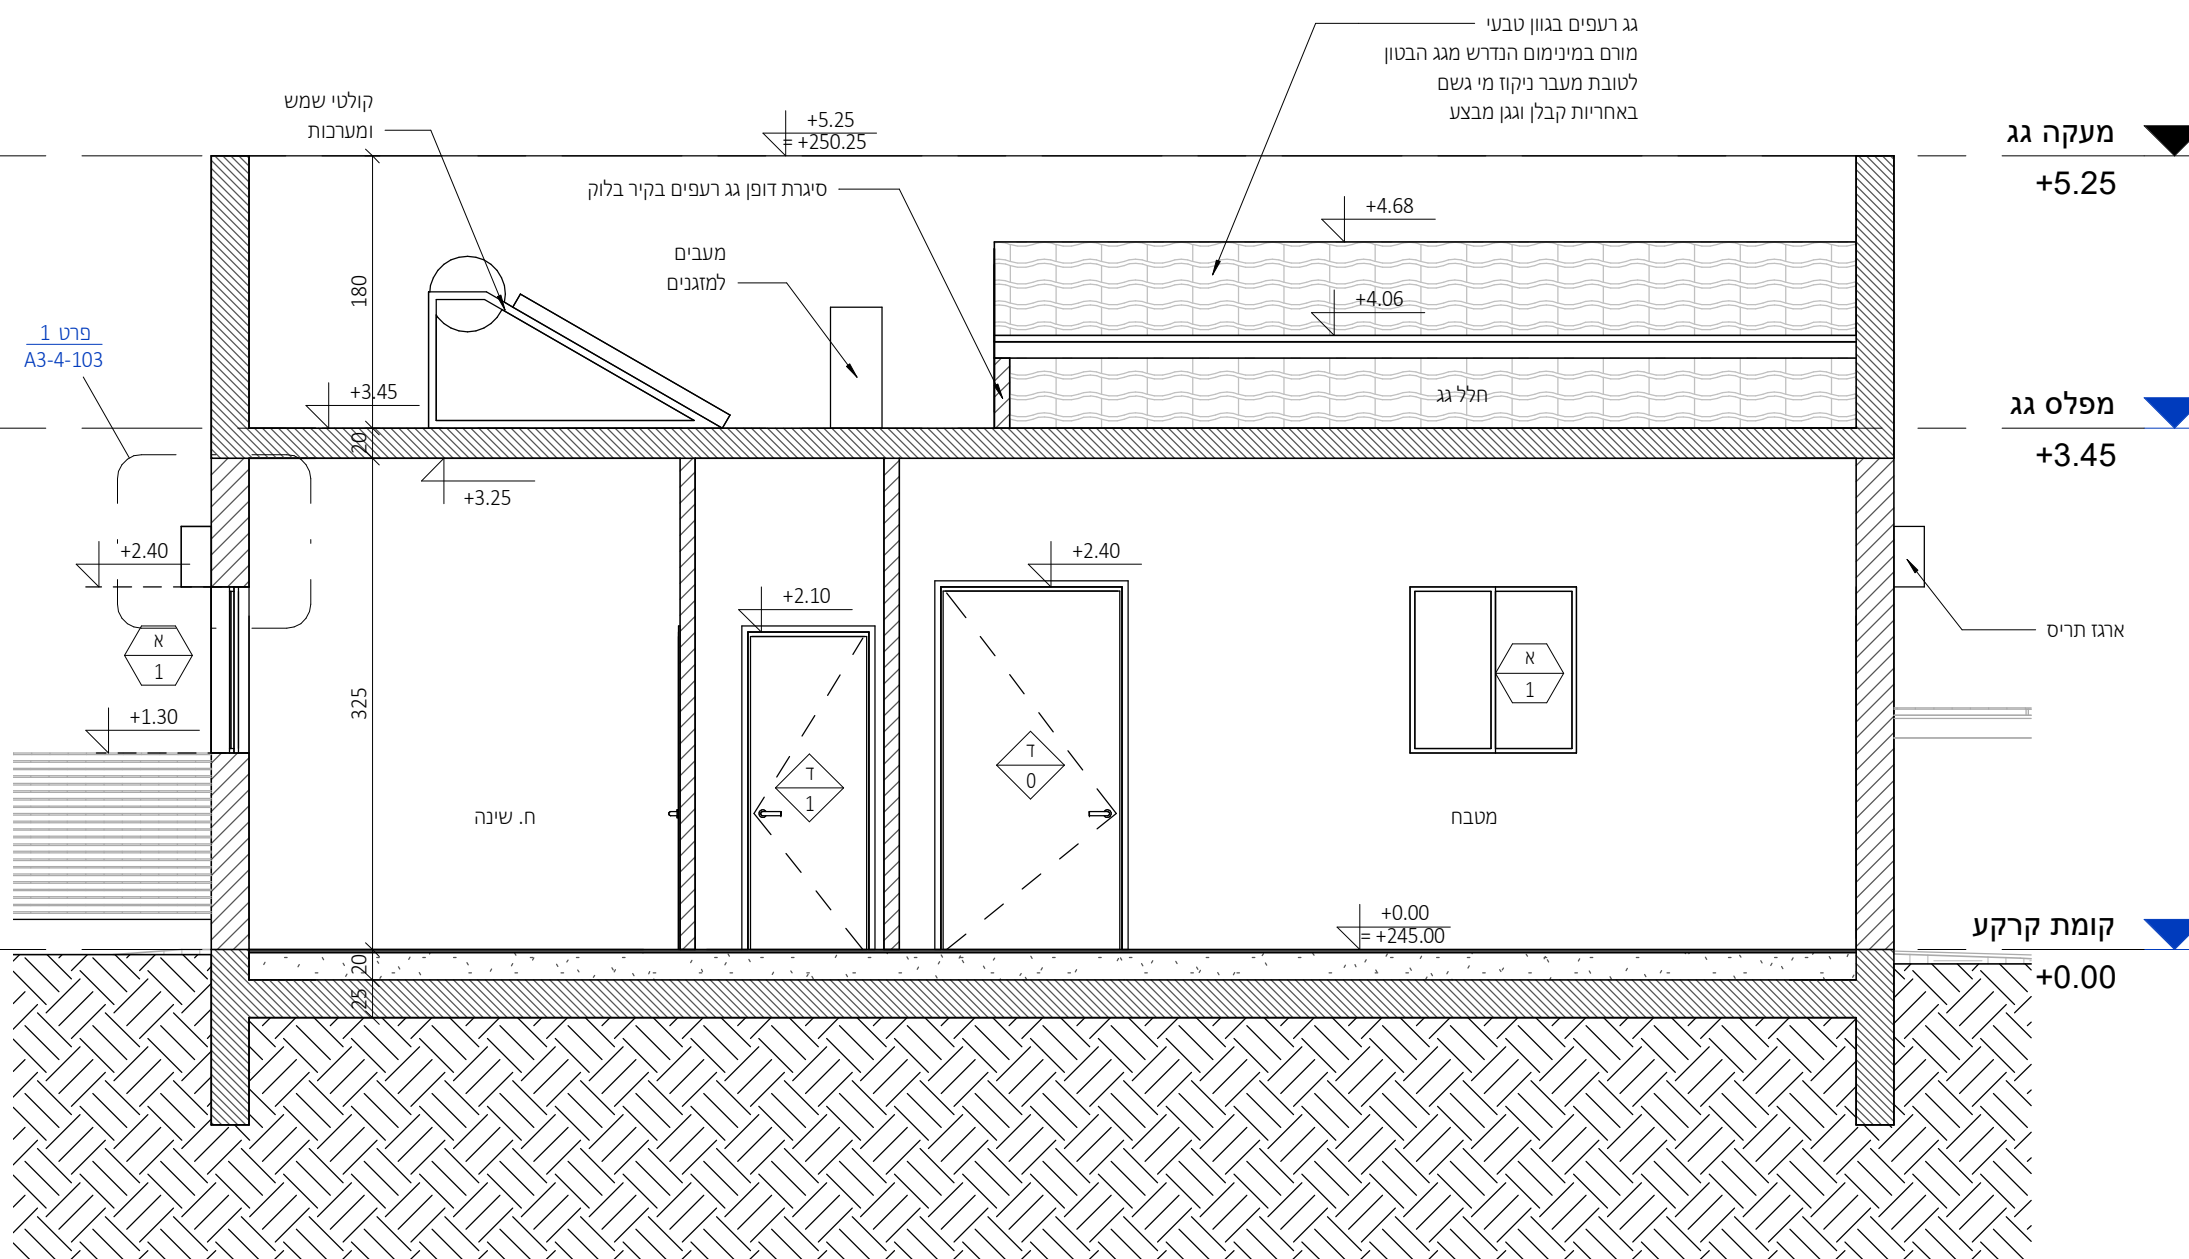

חֶתֶךְ ג-ג

1 : 50

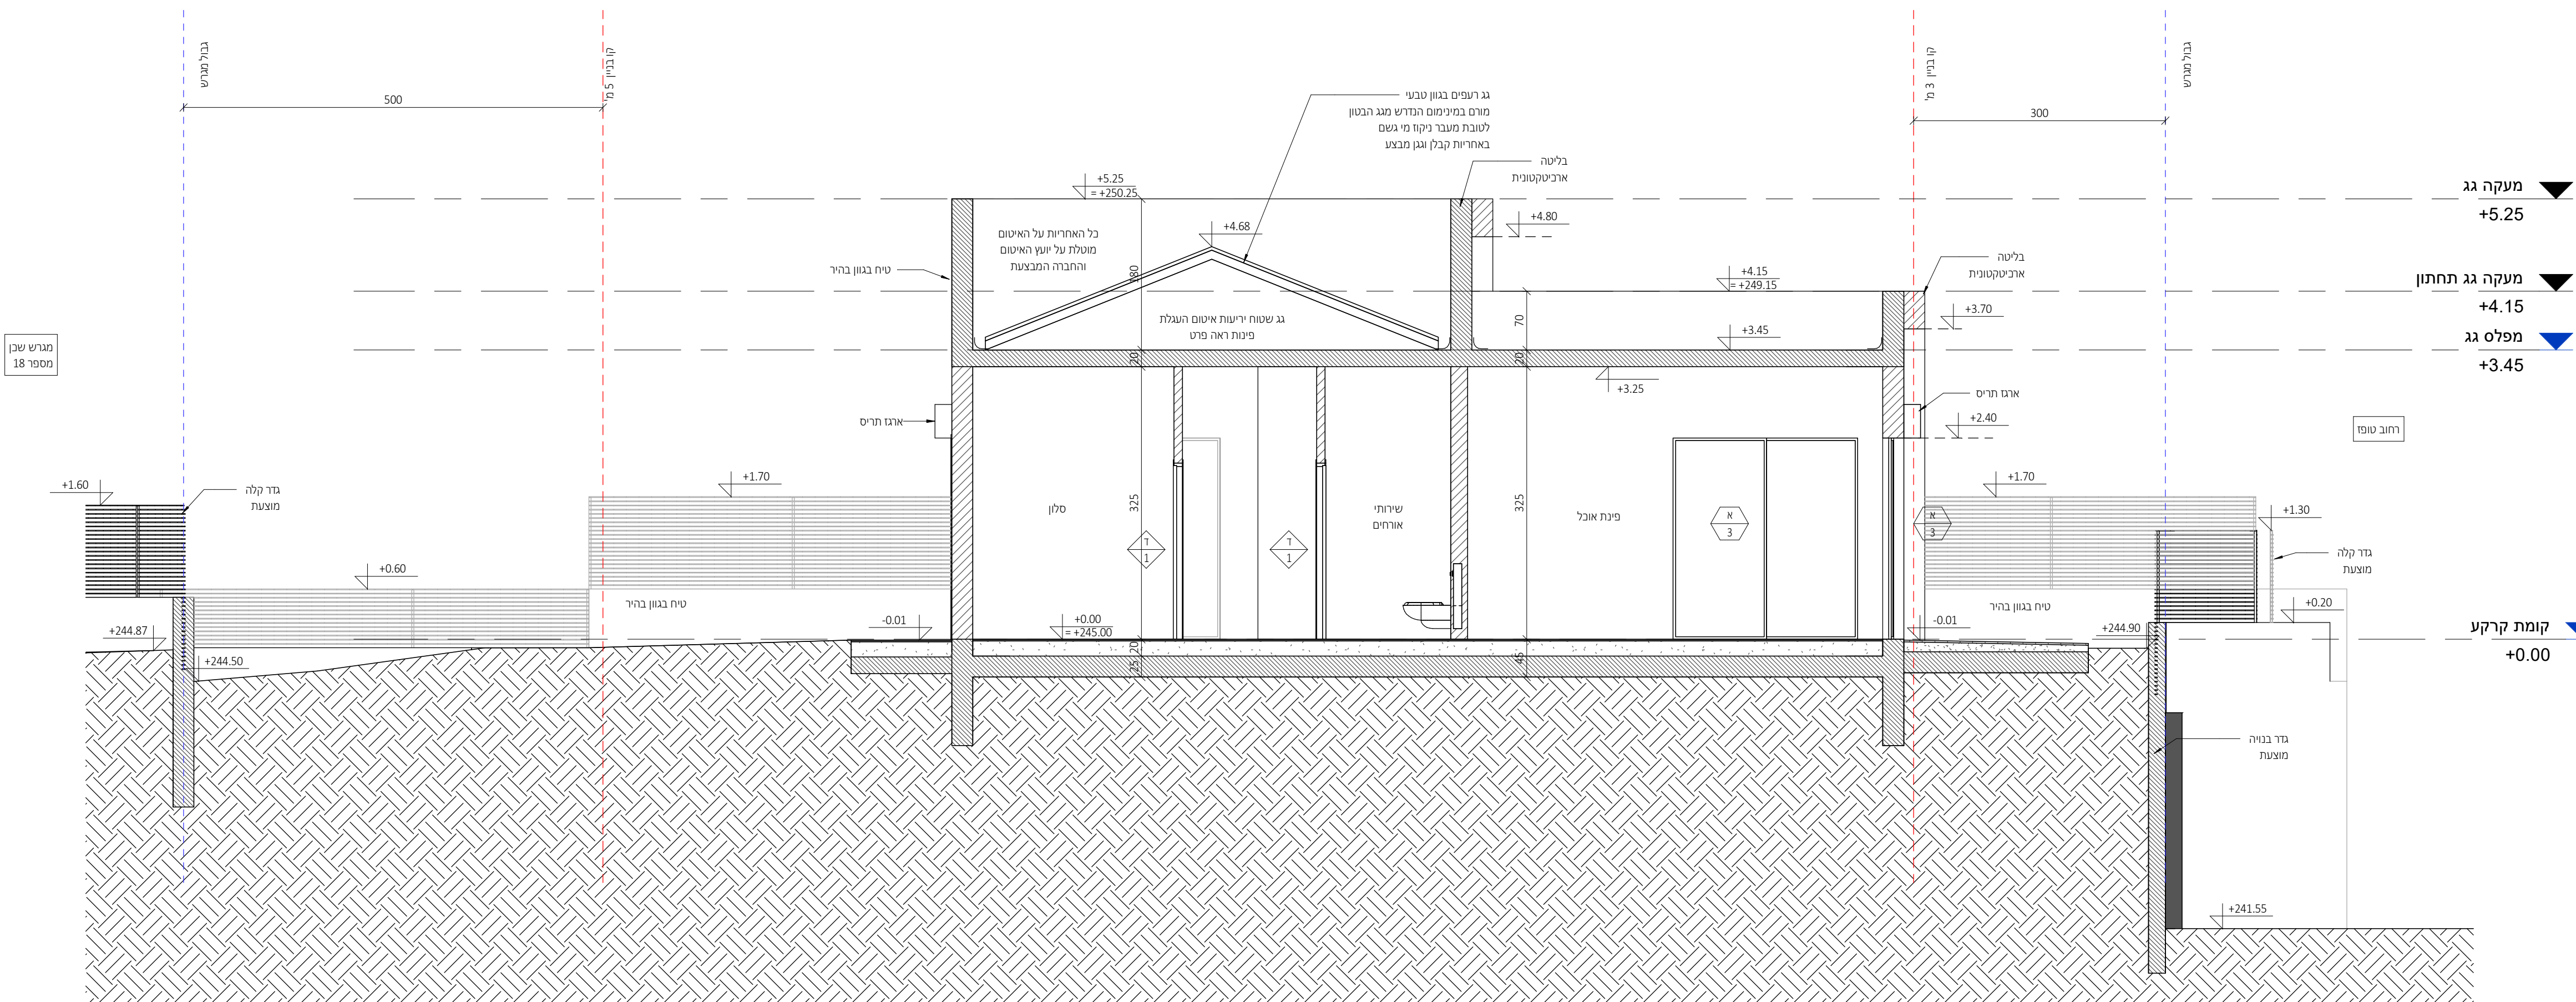

חתך ב-ב

1 : 50

פיתוח נוקף עפ"י תוכניות

יועץ נוף ראה פירוט בנפרד

<u>ניהול פרויקט</u> בן סולומון - מהיסוד
<u>פיקוח</u> מהיסוד - בן סולומון
<u>קונסטרוקציה</u> ערן שילר
<u>מיזוג אוויר</u> אייל ארז מהנדסים ויועצים בע"מ
<u>אינסטלציה</u> איתן אלמסי
<u>חשמל</u> איתן בסיס
<u>אלומיניום</u> נוף
<u>נתי בלוקא</u> חשמל חכם
<u>חימום תת רצפתי</u> איטום
<u>צבי טל</u> אקוסטיקה
<u>מעליות</u> קרקע וביסוס
<u>דיה הנדסת קרקע וביסוס</u> רישוי

[illegible][illegible]

קבוצת רכישה נופיה


PROJECT NAME: ספר הפרויקט:

נרפיה - מגרש 21

RAWING NAME: ס הגליון:

פרטים

SHEET NUMBER: A3-4-103

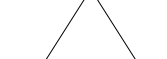
CALE:	קנה מידה:	EDITION:	הדפדה:
As indicated			
TATUS:	סטוס		
למכר			
	ונבד ע"י:	דרסט ע"י:	
ATE:	22.09.2025	מ"ר:	



NeumanHaynerArchitects


office@nh-arch.com
 www.nh-arch.com

זכויות ייצור / ע"פ הנחיות עו"ד

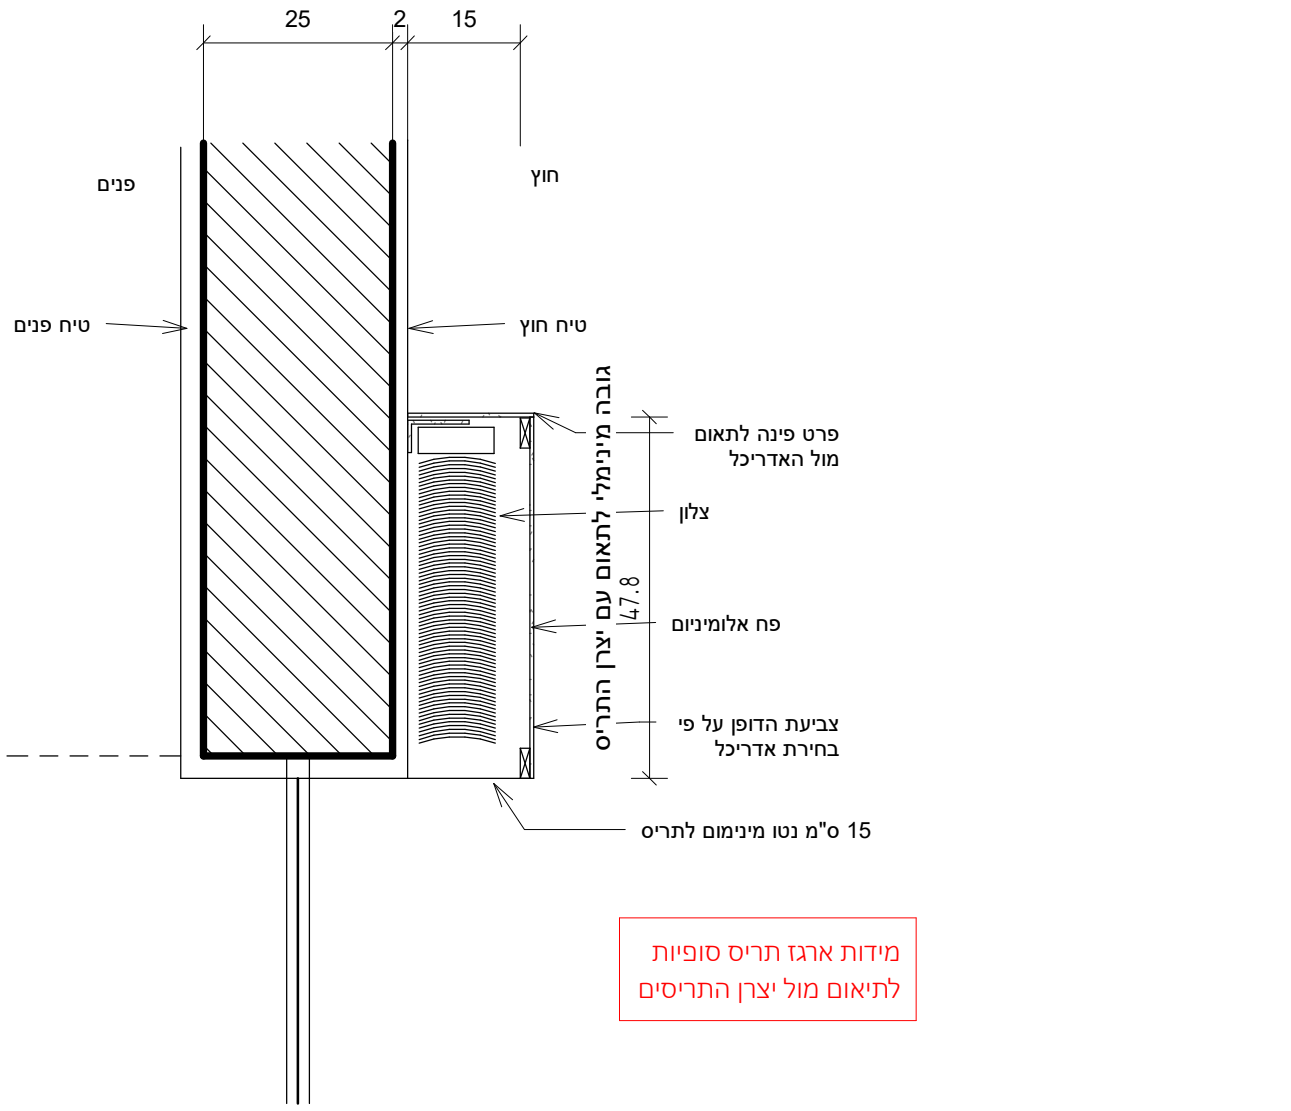

מידות ארגז תריס סופיות
לתיאום מול יצרן התריסים


1 : 10

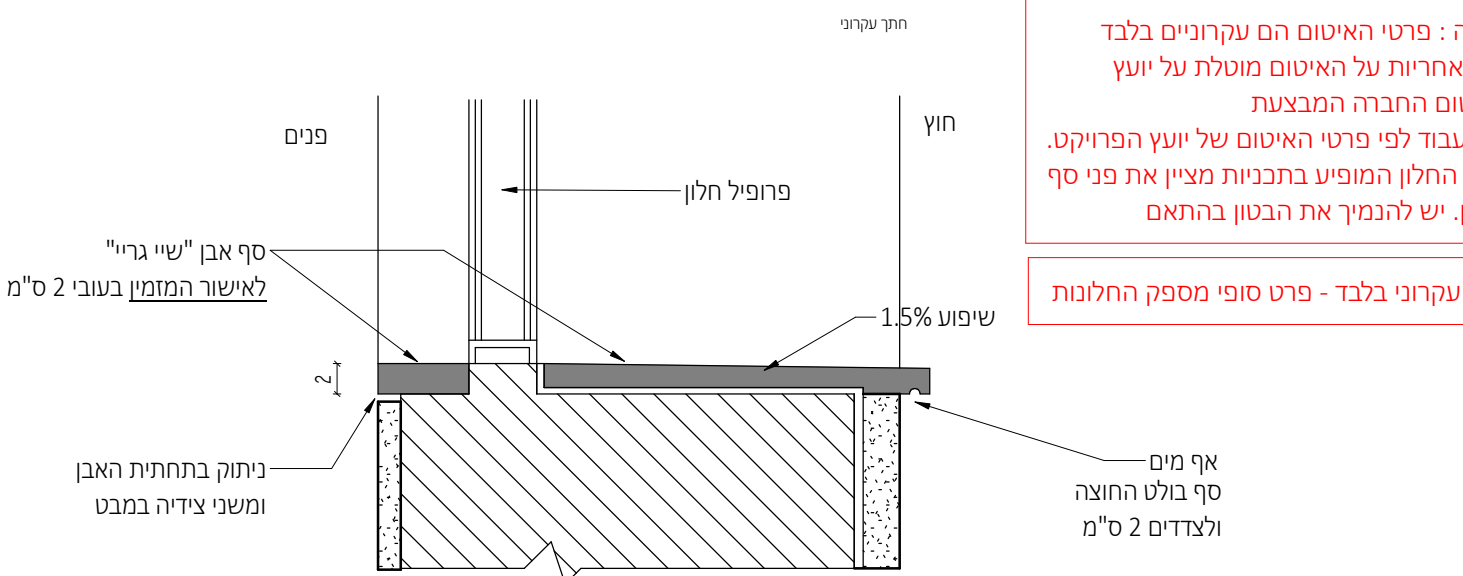

ה: פרטי האיטום הם עקרוניים בלבד
אחריות על האיטום מוטלת על יועץ
זום החברה המבצעת
עבוד לפי פרטי האיטום של יועץ הפרו
החלון המופיע בתכניות מציין את פנ
(יש להנמיך את הבטון בהתאם


עקרוני בלבד - פרט סופי מספק החלונות

1:5

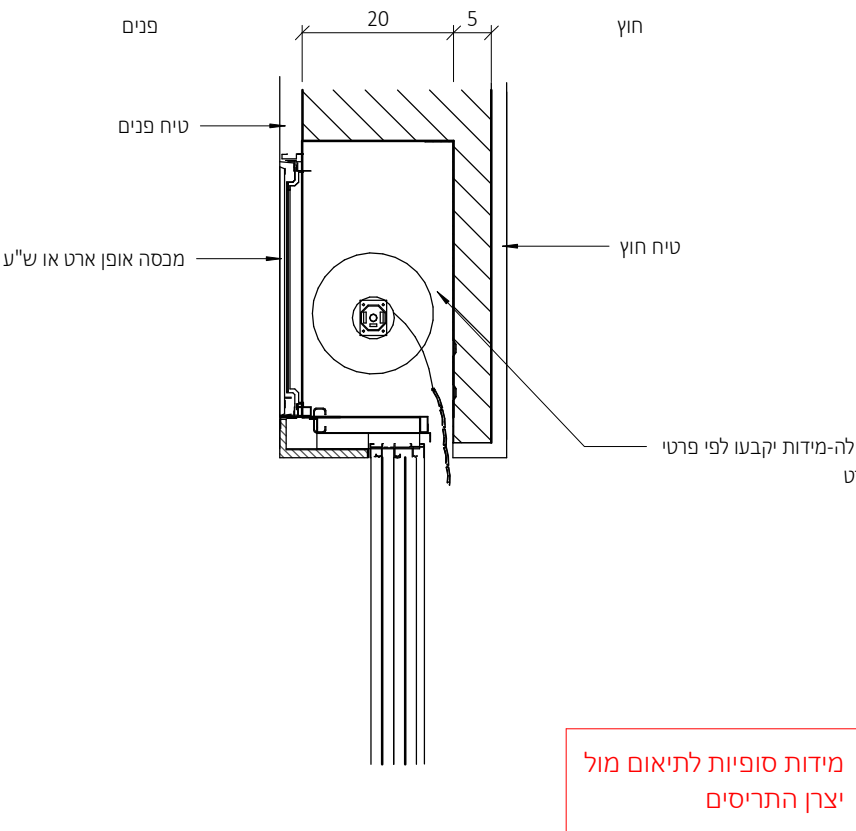


מכירות סופיות לתיאום מול
יצרן התריסים

1 : 10

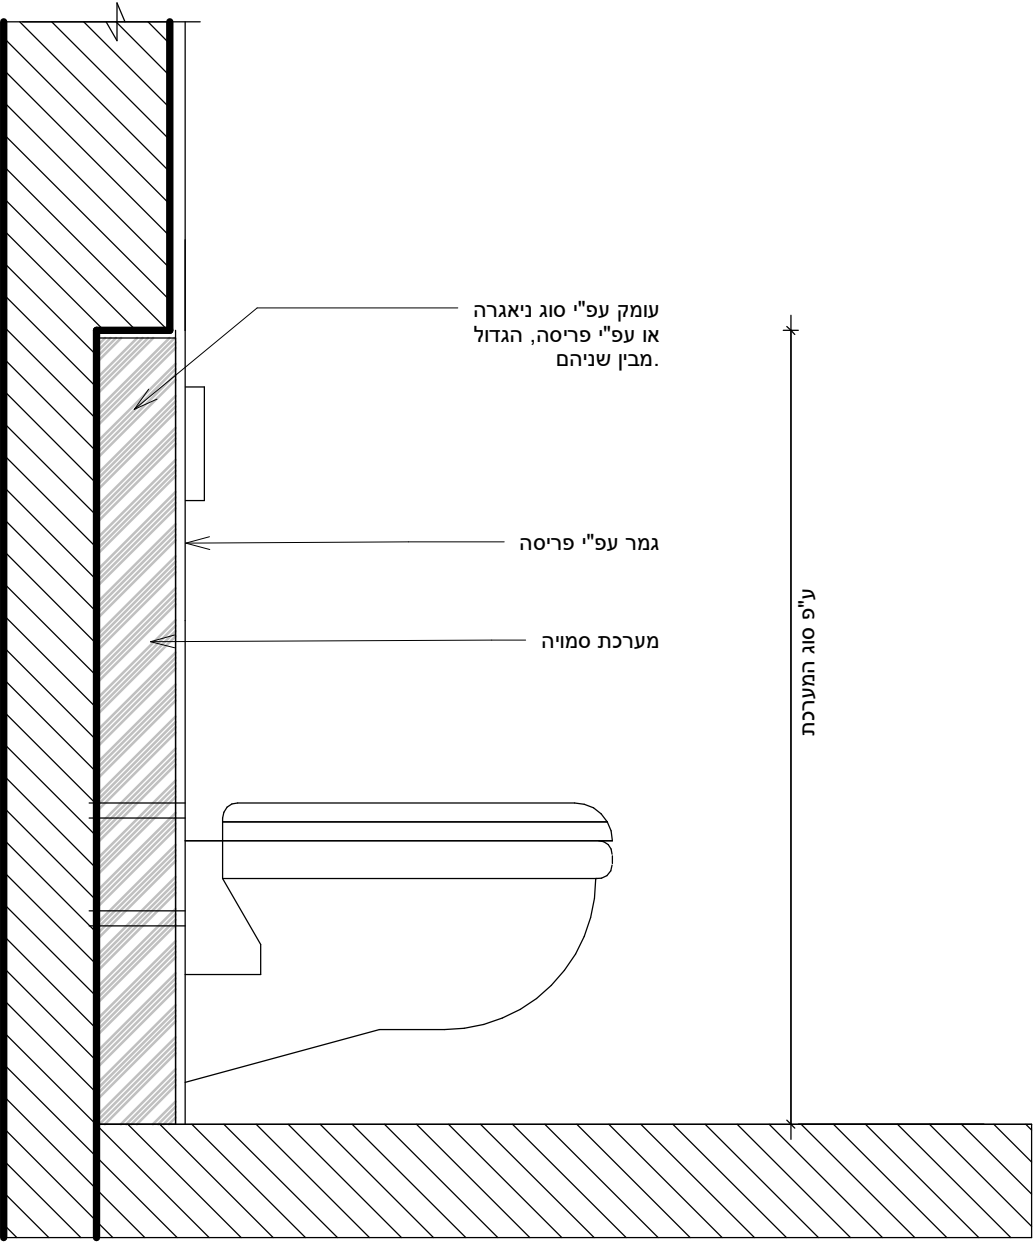


1 : 10

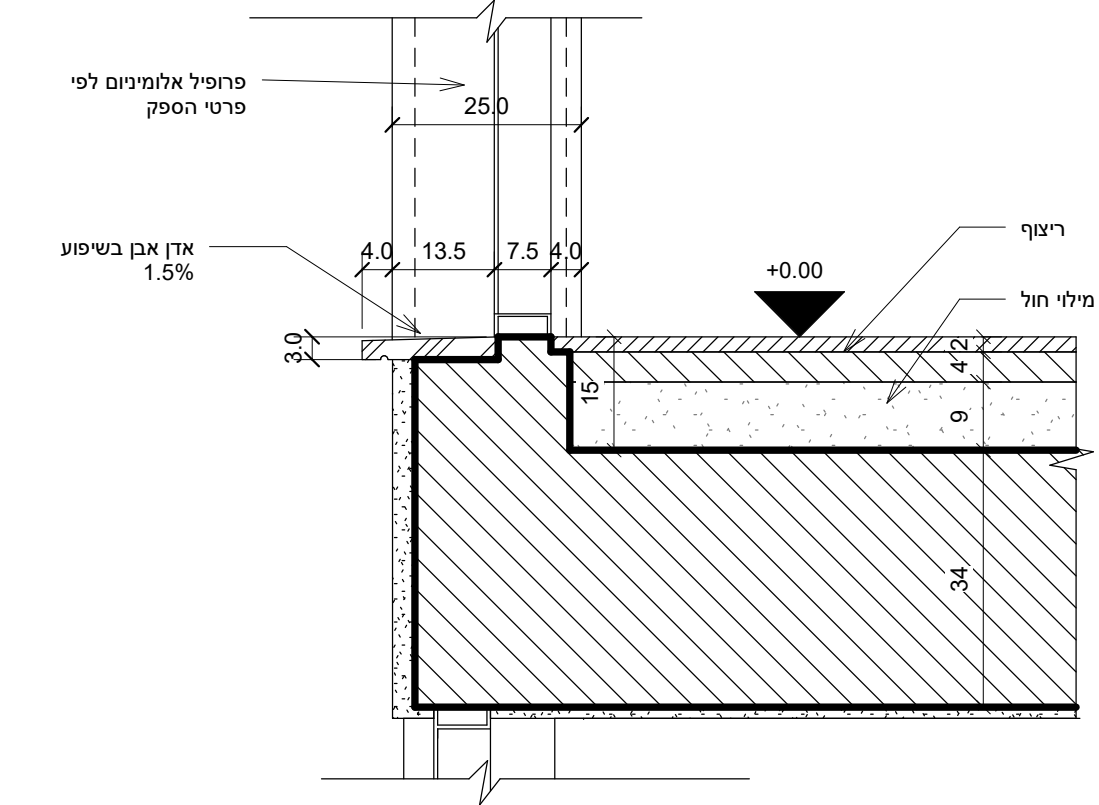

הערה : פרטי האיטום הם עקרוניים בלבד
כל האחריות על האיטום מוטלת על יועץ
האיטום החברה המבצעת
יש לעבוד לפי פרטי האיטום של יועץ הפרויקט.
גובה החלון המופיע בתכניות מציין את פני סף
האבן. יש להנמיך את הבטון בהתאם

פרט עקרוני בלבד - פרט סופי מספק החלונות

1 : 10

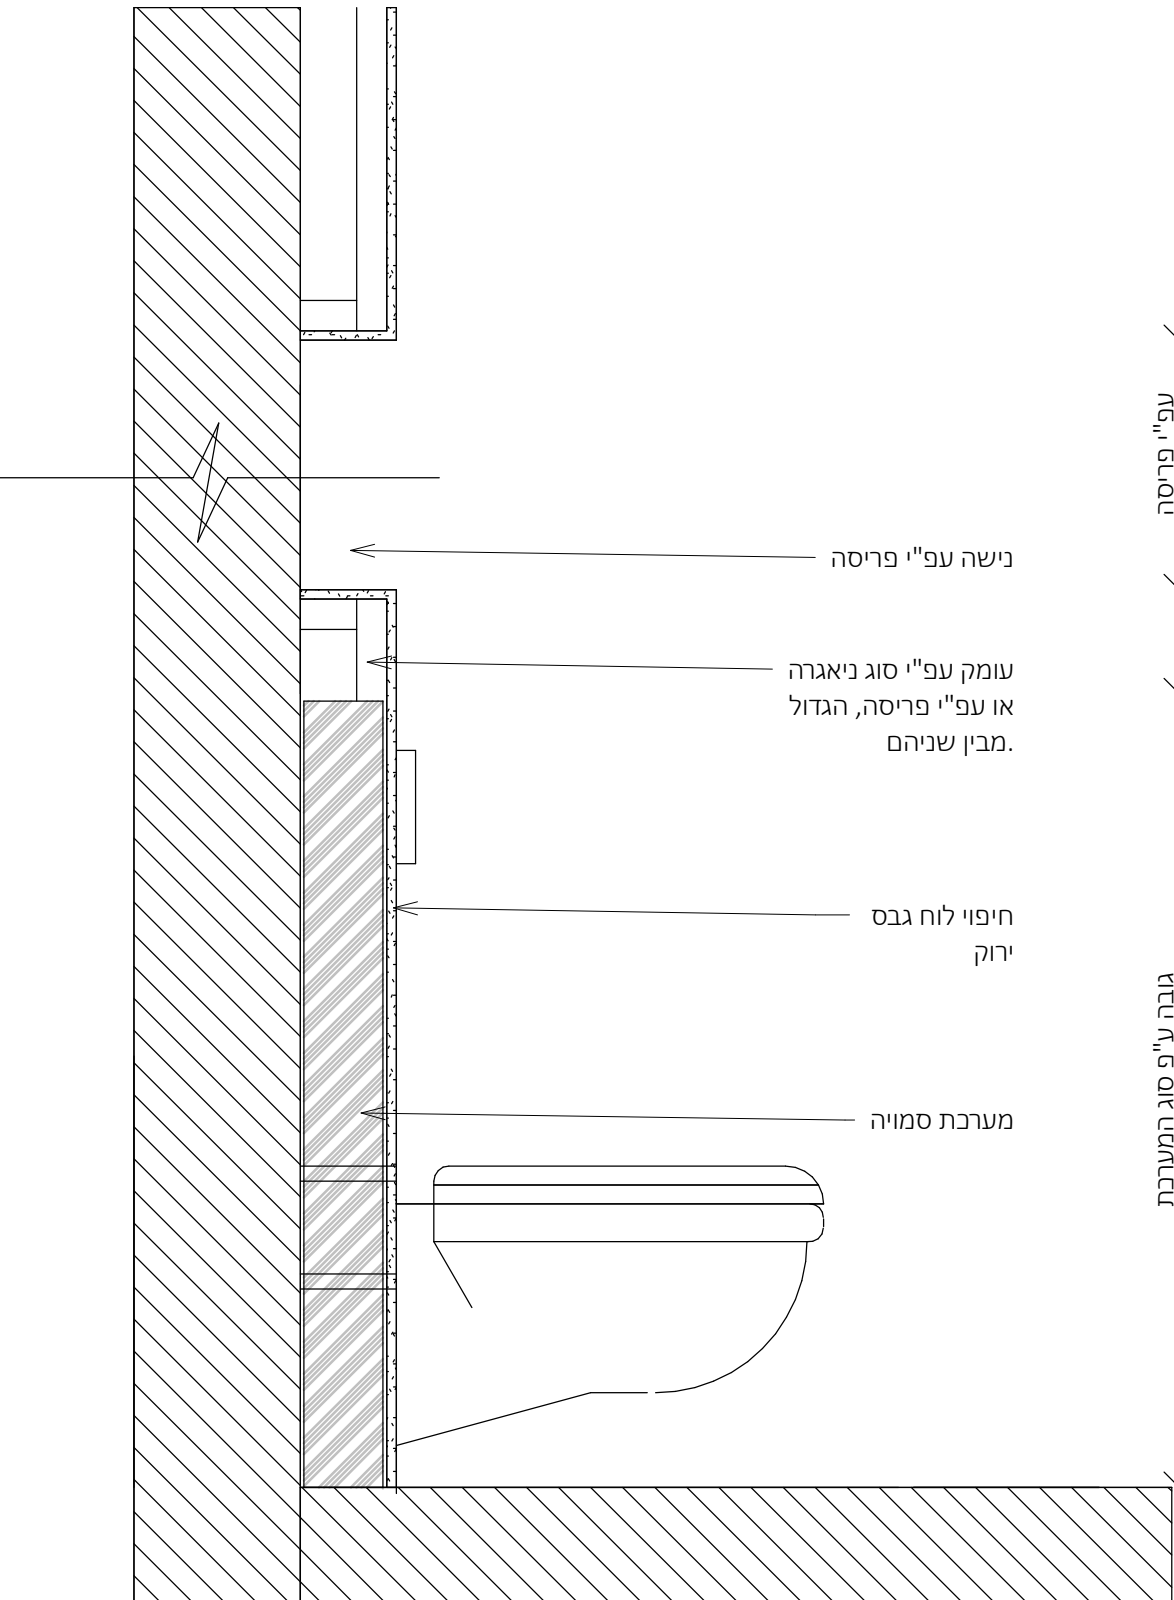

1 : 10

יש לעבוד במקביל לפרטים שיספק
מעצב הפנים (במידה וקיים במגרש זה)
המאושרות על ידי האדריכל.

פרטי האיטום באחריות יועץ האיטום
ראה חוברת פרטי איטום מצורפת

להמשך תיאום

רשימת חלונות					
סוג	תיאור	כמות	גובה	רוחב	מס פריט

1	110	110	3	צלון רפפה חיצוני חשמלי + ארגז חיצוני	חלון הזזה פרופיל 7000 קליל
2	110	240	1	צלון רפפה חיצוני חשמלי + ארגז חיצוני	דלת כנף פרופיל 4350 קליל
3	220	240	4	צלון רפפה חיצוני חשמלי + ארגז חיצוני	ויטרינה פרופיל 7500 קליל
4	60	110	1	ללא רפפה	חלון כיף פרופיל 4500 קליל
5	90	240	1	צלון רפפה חיצוני חשמלי + ארגז חיצוני	דלת כנף פרופיל 4350 קליל

כל פריט יחולק למינימום הכנפיים האפשרי (לתיאום מול ספק האלומיניום ובמסגרת שרטוטי ה shop drawing)

רשימת דלתות					
סוג	הערות	כמות	גובה	רוחב	מספר פריט

0	120	240	1	דלת בניסה	דלת חוץ דגם גארדה
1	80	210	4	דלת פנים	דלת פנים "אקוודור" תוצרת חמדיה
2	80	200	1	דלת נגרות ממ"ד	דלת פנים "אקוודור" תוצרת חמדיה

FILE NAME: -----כלל הפרויקטים להיתר\21\00 תכנית\nofia