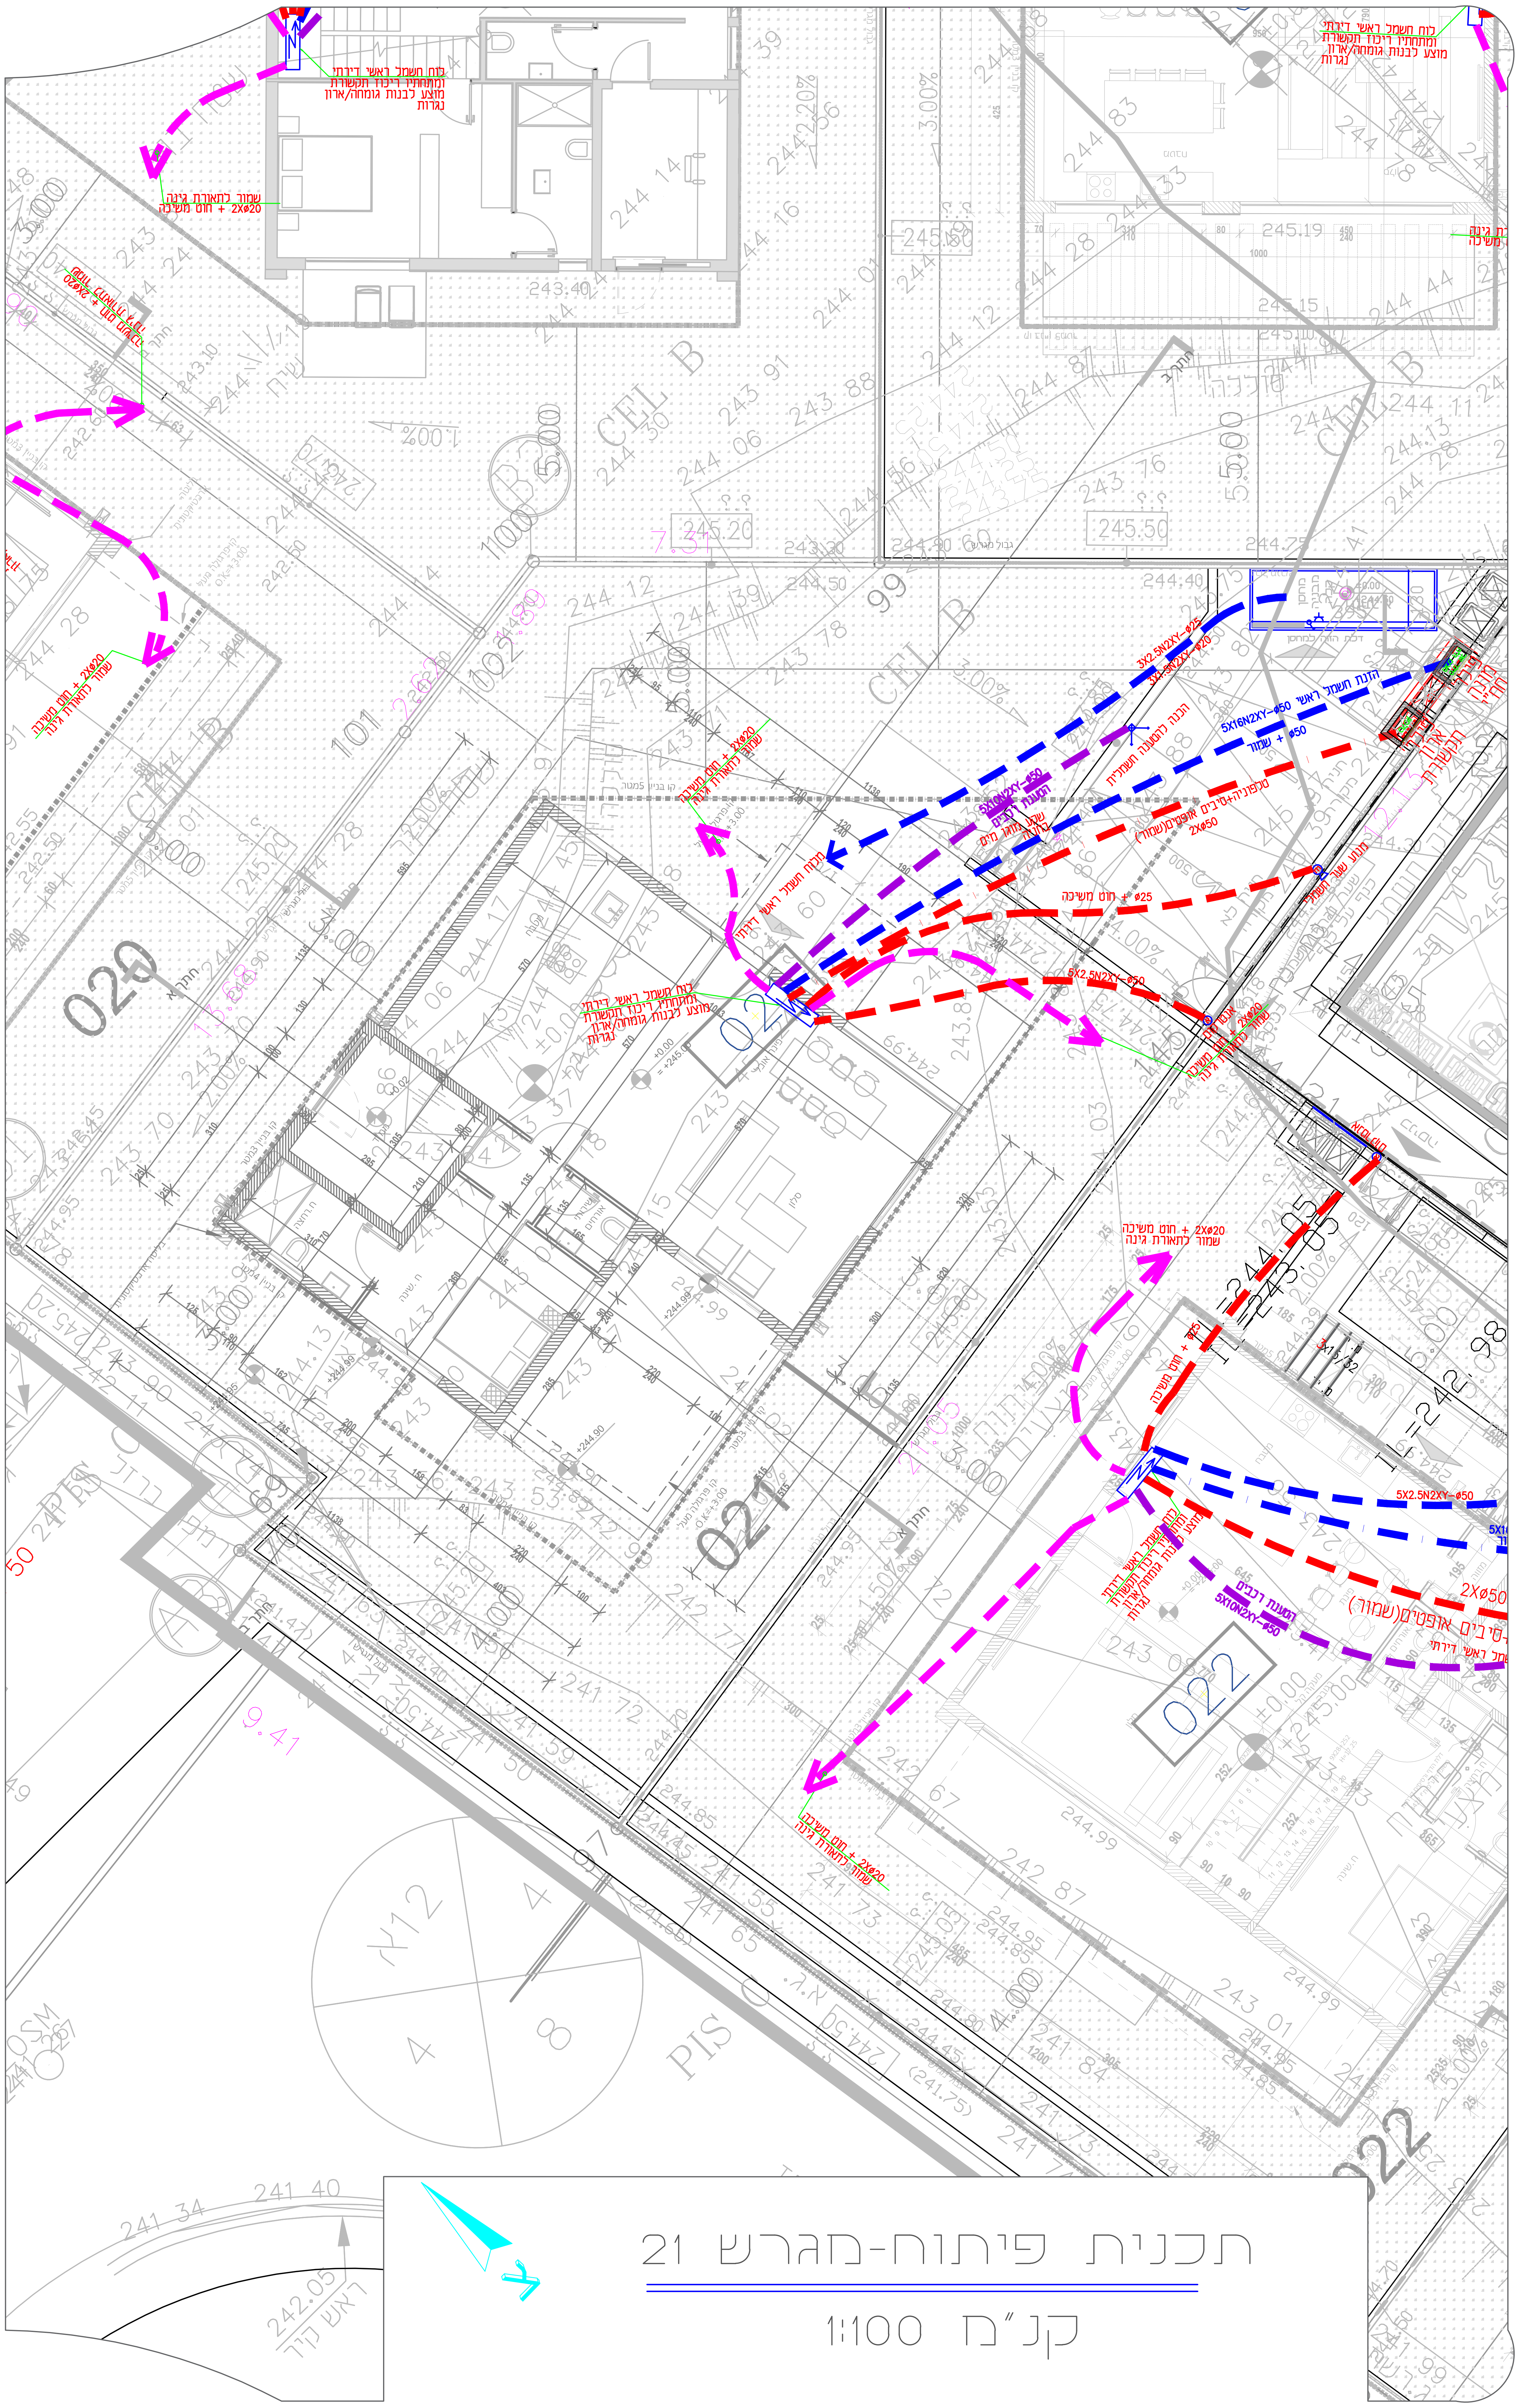

תאריך			חברת בזק	חברת חשמל	מטבחים	אדריכל נוף	קונסטרוקציה	אינסטלציה	אקוסטיקה	בטיחות	קבלן	חשמל	מזמין/יזם	אדריכל	מנהל הפרויקט

מס'	שינויים	תאריך

עודכן ע"י: רחל

א. בסיס
הנדסת חשמל בע"מ
משרד: יד חרוצים 16, ירושלים 93420
טל: 074-7021015 נייד: 050-6550484
פקס: 077-5131015 דוא"ל: office@ebasis.co.il

שם הפרויקט:
נופיה-אלפי מנשה

שם הגיליון:
תוכנית פיתוח מגרש 21

○ לעיון ○ לאישור ● למכרז ○ לביצוע

קנה מידה: 1:100

מס' קובץ: File: 675P.dwg

תאריך: Date: 17.06.2024

תכנן: איתן
שרטט: אילה
אישר: איתן

מס' הפרויקט: 675
מס' הגליון: P21
מס' עדכון: 0

לוח חשמל דירתי ראשי #1
מגרש 21

מוזן ממונה חח"י
5x16N2XY-2XØ50
3x40A C
4X40A 30mA
3x32A C
4X40A 30mA Type B
3x16A C
3X16A
C1 AC3
C2 AC3
3x20A C
C3 AC3
10A C
16A C
3x16A C
0
1 יד
2 שעון
שעון מכני עם רזרבה תוצרת גריזליין דגם 211 תוצרת גרמניה
מאור כללי
שעון שבת לתאורה
תאורת חוץ וחניה
שעון שבת לתאורת חוץ
מיזוג אויר
שעון שבת מיזוג מיני מרכזי
יעודכן לפני תכנית יועץ מיזוג
40
5x10N2XY-Ø50
הכנה למערכת הטענה רכבים חשמליים בחניה
L1 3X1.5N2XY-Ø20 חלל כניסה
L2 3X1.5N2XY-Ø20 סלון מטבח
L3 3X1.5N2XY-Ø20 מסדרון
L4 3X1.5N2XY-Ø20
L5 3X1.5N2XY-Ø20
חדרי שינה
L11 3X1.5N2XY-Ø20 פינת אוכל
L12 3X1.5N2XY-Ø20 מעבר+ ממד
L12/1
L12/2
שמור
L6 3X1.5N2XY-Ø20 שירותים
L7 3X1.5N2XY-Ø20 תאורת פרגולה+ חוץ
L8 3X1.5N2XY-Ø20 תאורת חוץ 1
L9 3X1.5N2XY-Ø20 חניה, מחסן גינה שביל כניסה
10 3X1.5N2XY-Ø20 גלאי עשן
L13 3X1.5N2XY-Ø20 שירותים מקלחת
L14 3X1.5N2XY-Ø20 תאורת חוץ 2
תאורה
P1 3x2.5N2XY-Ø20 סלון
P2 3x2.5N2XY-Ø20
P3 3x2.5N2XY-Ø20
חדרי שינה
P4 3x2.5N2XY-Ø20 מכונת כביסה
P5 3x2.5N2XY-Ø20 מייבש כביסה
P6 3x2.5N2XY-Ø20 תנור
P7 3x2.5N2XY-Ø20 מקרר
P8 3x2.5N2XY-Ø20 מדיח
P9 3x2.5N2XY-Ø20 שירות
P10 3x2.5N2XY-Ø20 שירות
P11 5x2.5N2XY-Ø25 כיריים חשמליות
מטבח
P12
P13
P14
P15
P16
P17
P18
שקעי כח-שמור
P19 3x2.5N2XY-Ø20 בוילר
P21 3x2.5N2XY-Ø20 שקעים חוץ 1
P22 3x2.5N2XY-Ø20 שקעים חוץ 2
P23 3x2.5N2XY-Ø20 חימום מים בגז
P24 3x2.5N2XY-Ø20 תנור ח רחצה
P25 3x2.5N2XY-Ø20 ארון תקשורת
P26 3x2.5N2XY-Ø20 ממד
P27 3x2.5N2XY-Ø20 מערכת סינון ממד
M1 3x2.5N2XY-Ø20 תריס חשמלי
M2 3x2.5N2XY-Ø20 תריס חשמלי
M3 3x2.5N2XY-Ø20 תריס חשמלי
M4 3x2.5N2XY-Ø20 תריס חשמלי
AC1 5x4N2XY-Ø25 הזנה מזגן סלון
AC2 3x2.5N2XY-Ø20 ממ"ד
AC3 3x2.5N2XY-Ø20
מיזוג אויר יחידות עיליות
P20
P21
P22
P23
שמור
שקעים
יעודכן לפני תכנית יועץ מיזוג

הנחיות לבניית לוח חשמל:

- מבנה לוח חשמל פלסטי חסין אש סדרת FW מתוצרת Hager דגם FW62US2 ל-144 מודולים (6x12)2X לפחות
- דלת פח IP30 מתכתית
- בדיד כפול Class-2
- צבע לבן
- מהדקי אפס והארקה עם חיבור מהיר
- ציוד חשמלי יהיה מסוג ABB שניידר הגר או EATON בלבד בעל זרם
- יש לשמור בלוח 30% מקום לתוספת עתידית בלוח

תפוצה	תאריך
מנהל הפרויקט	
אדריכל	
מזמין/יזם	
חשמל	
קבלן	
בטיחות	
אקוסטיקה	
אינסטלציה	
קונסטרוקציה	
אדריכל נוף	
מטבחים	
חברת חשמל	
חברת בזק	

מס'	שינויים	תאריך

עודכן ע"י: יפעת

א. בסיס
הנדסת חשמל בע"מ
משרד: יד חרוצים 16, ירושלים 93420
טל: 074-7021015 נייד: 050-6550484
פקס: 077-5131015 דוא"ל: office@ebasis.co.il

שם הפרויקט:
נופיה-אלפי מנשה

שם התכנית:
לוח #1- מגרש 21, נופיה

קנה מידה: 1:50

○ לעיון ○ לאישור ○ למכרז ● לביצוע

מס' קובץ: File: 675W.dwg
תאריך: Date: 05.03.2025

תכנן: יפעת
שרטט: ליאל
אישר: איתן

מס' עדכון: 0
מס' הגליון: 21
מס' הפרויקט: 675

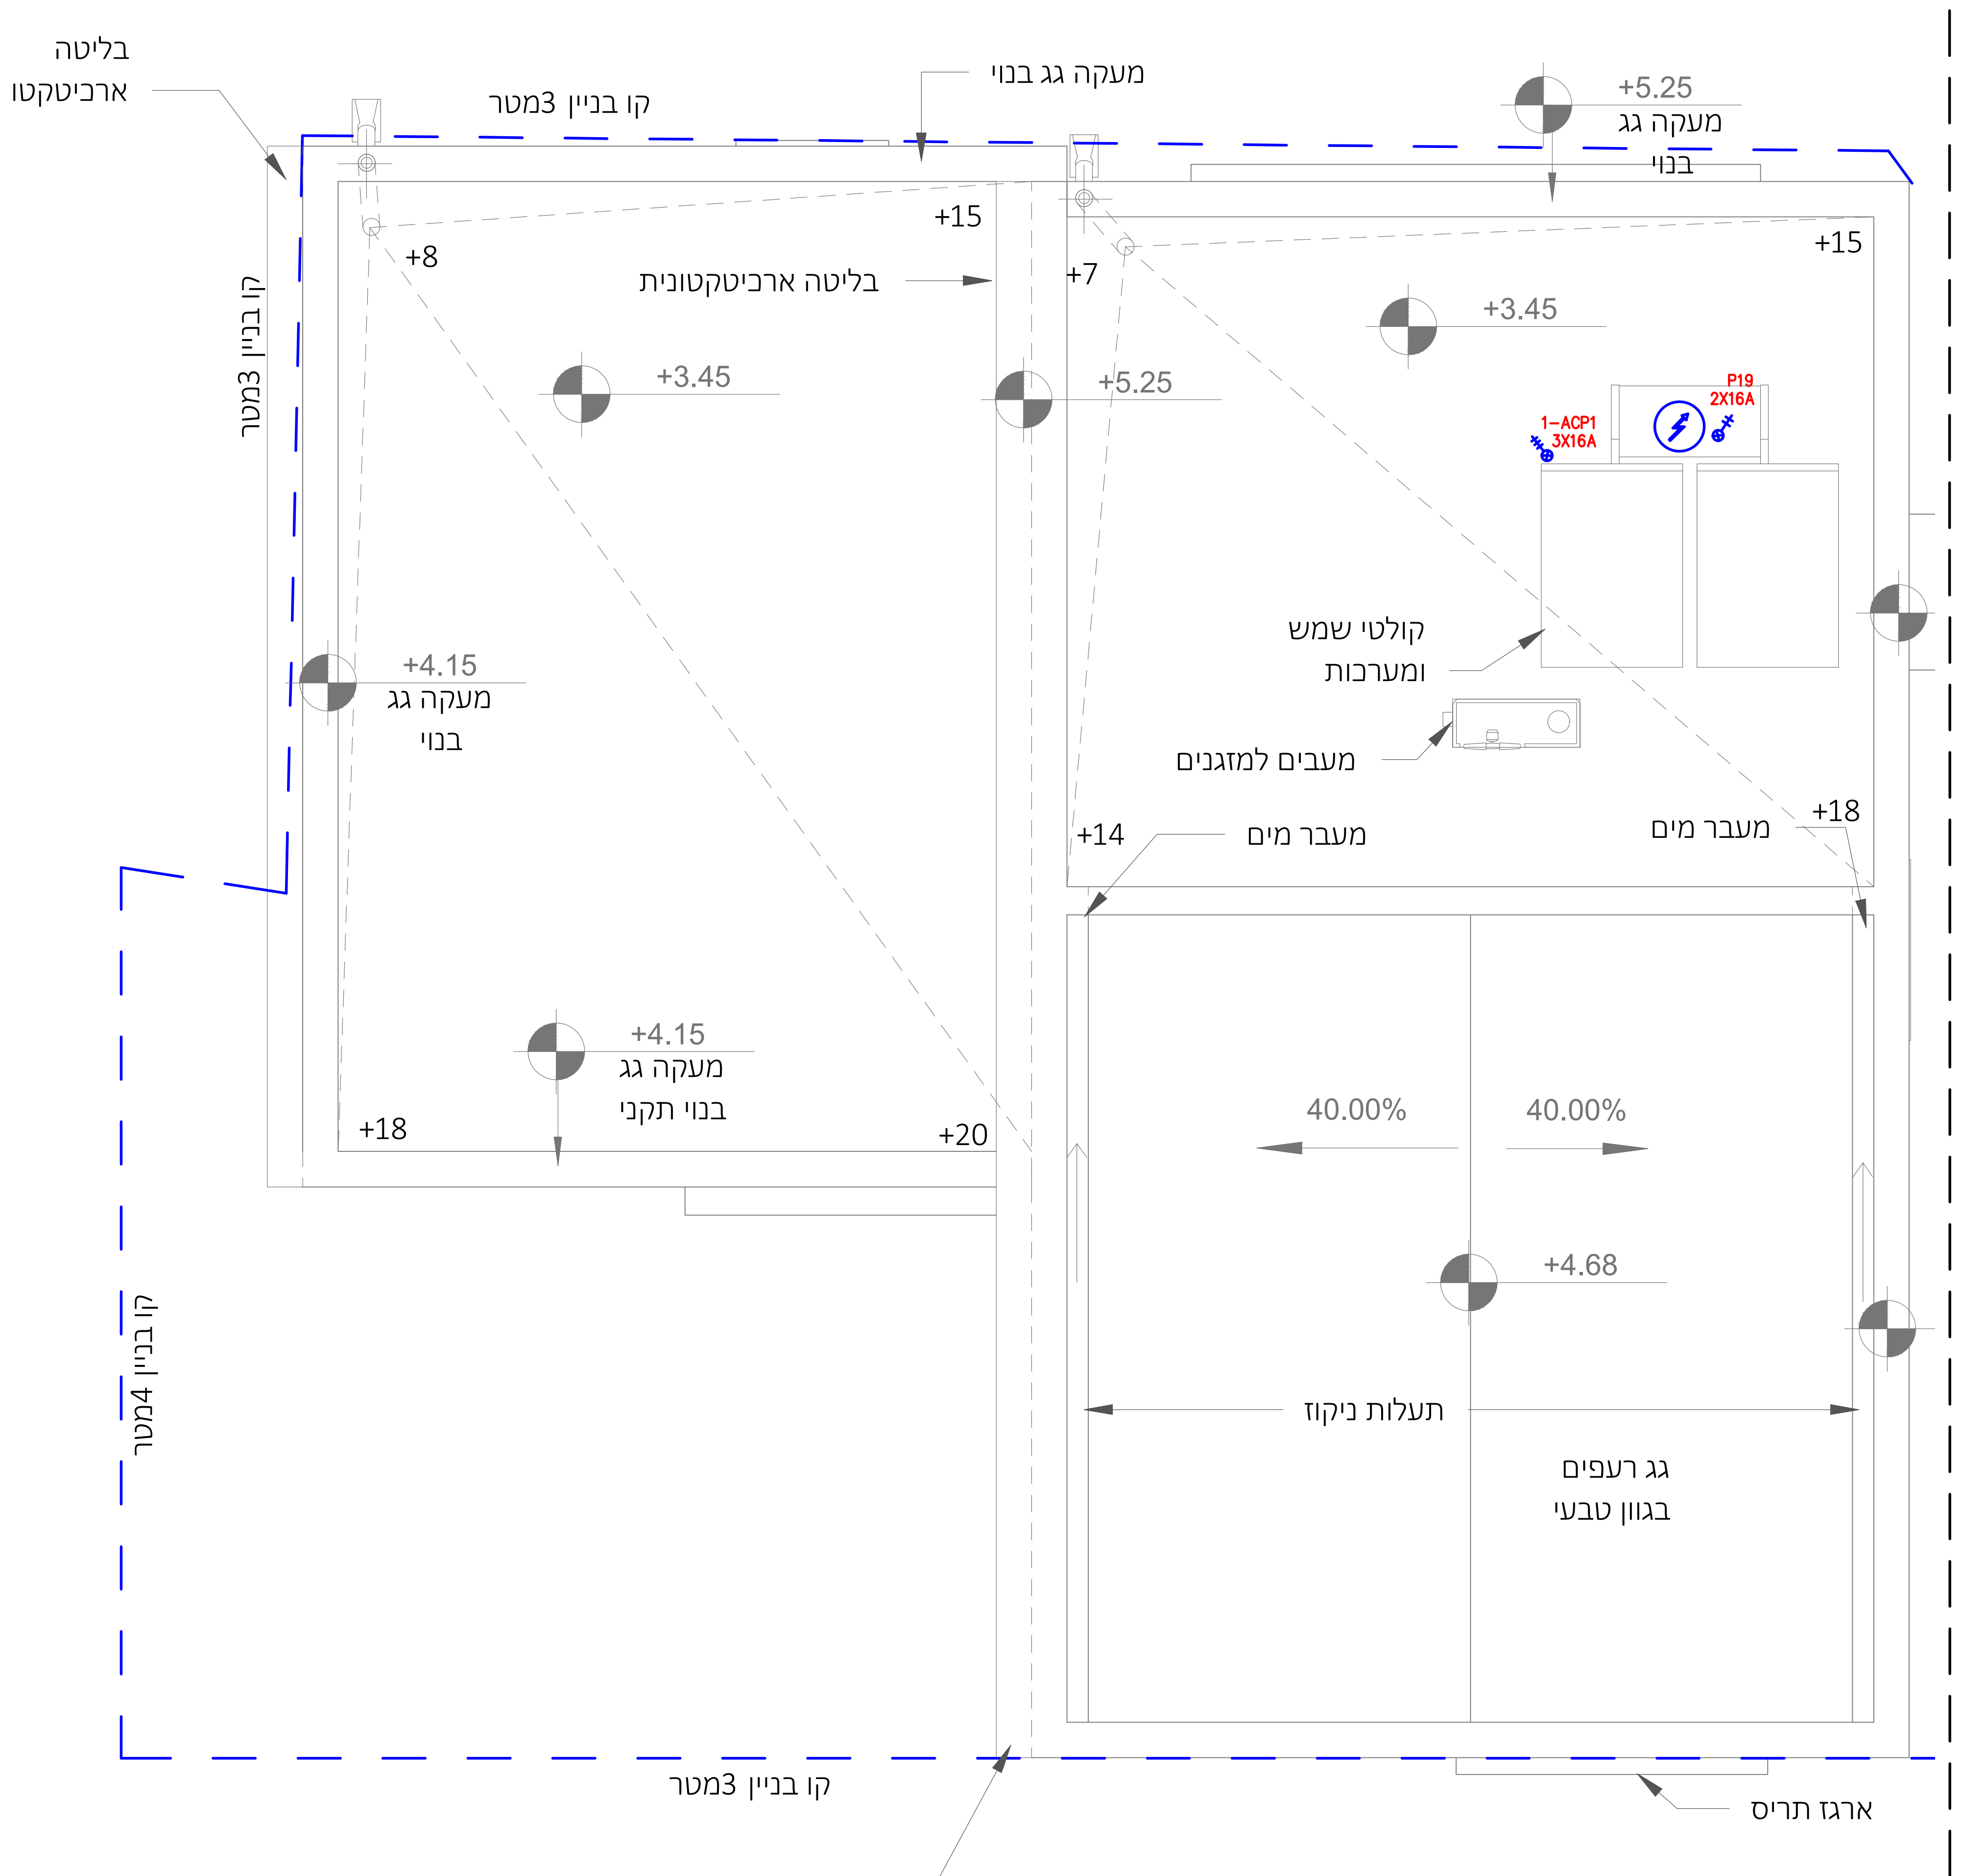

פרט יציאת צנרת חשמל בגג לבוילר וכדו'

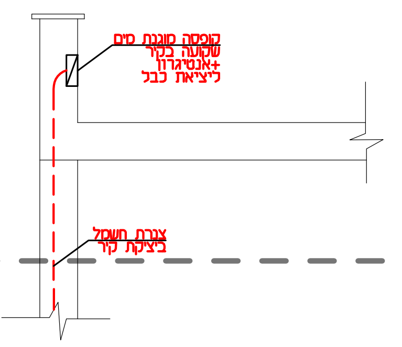

גבול מגרש

קומת גג

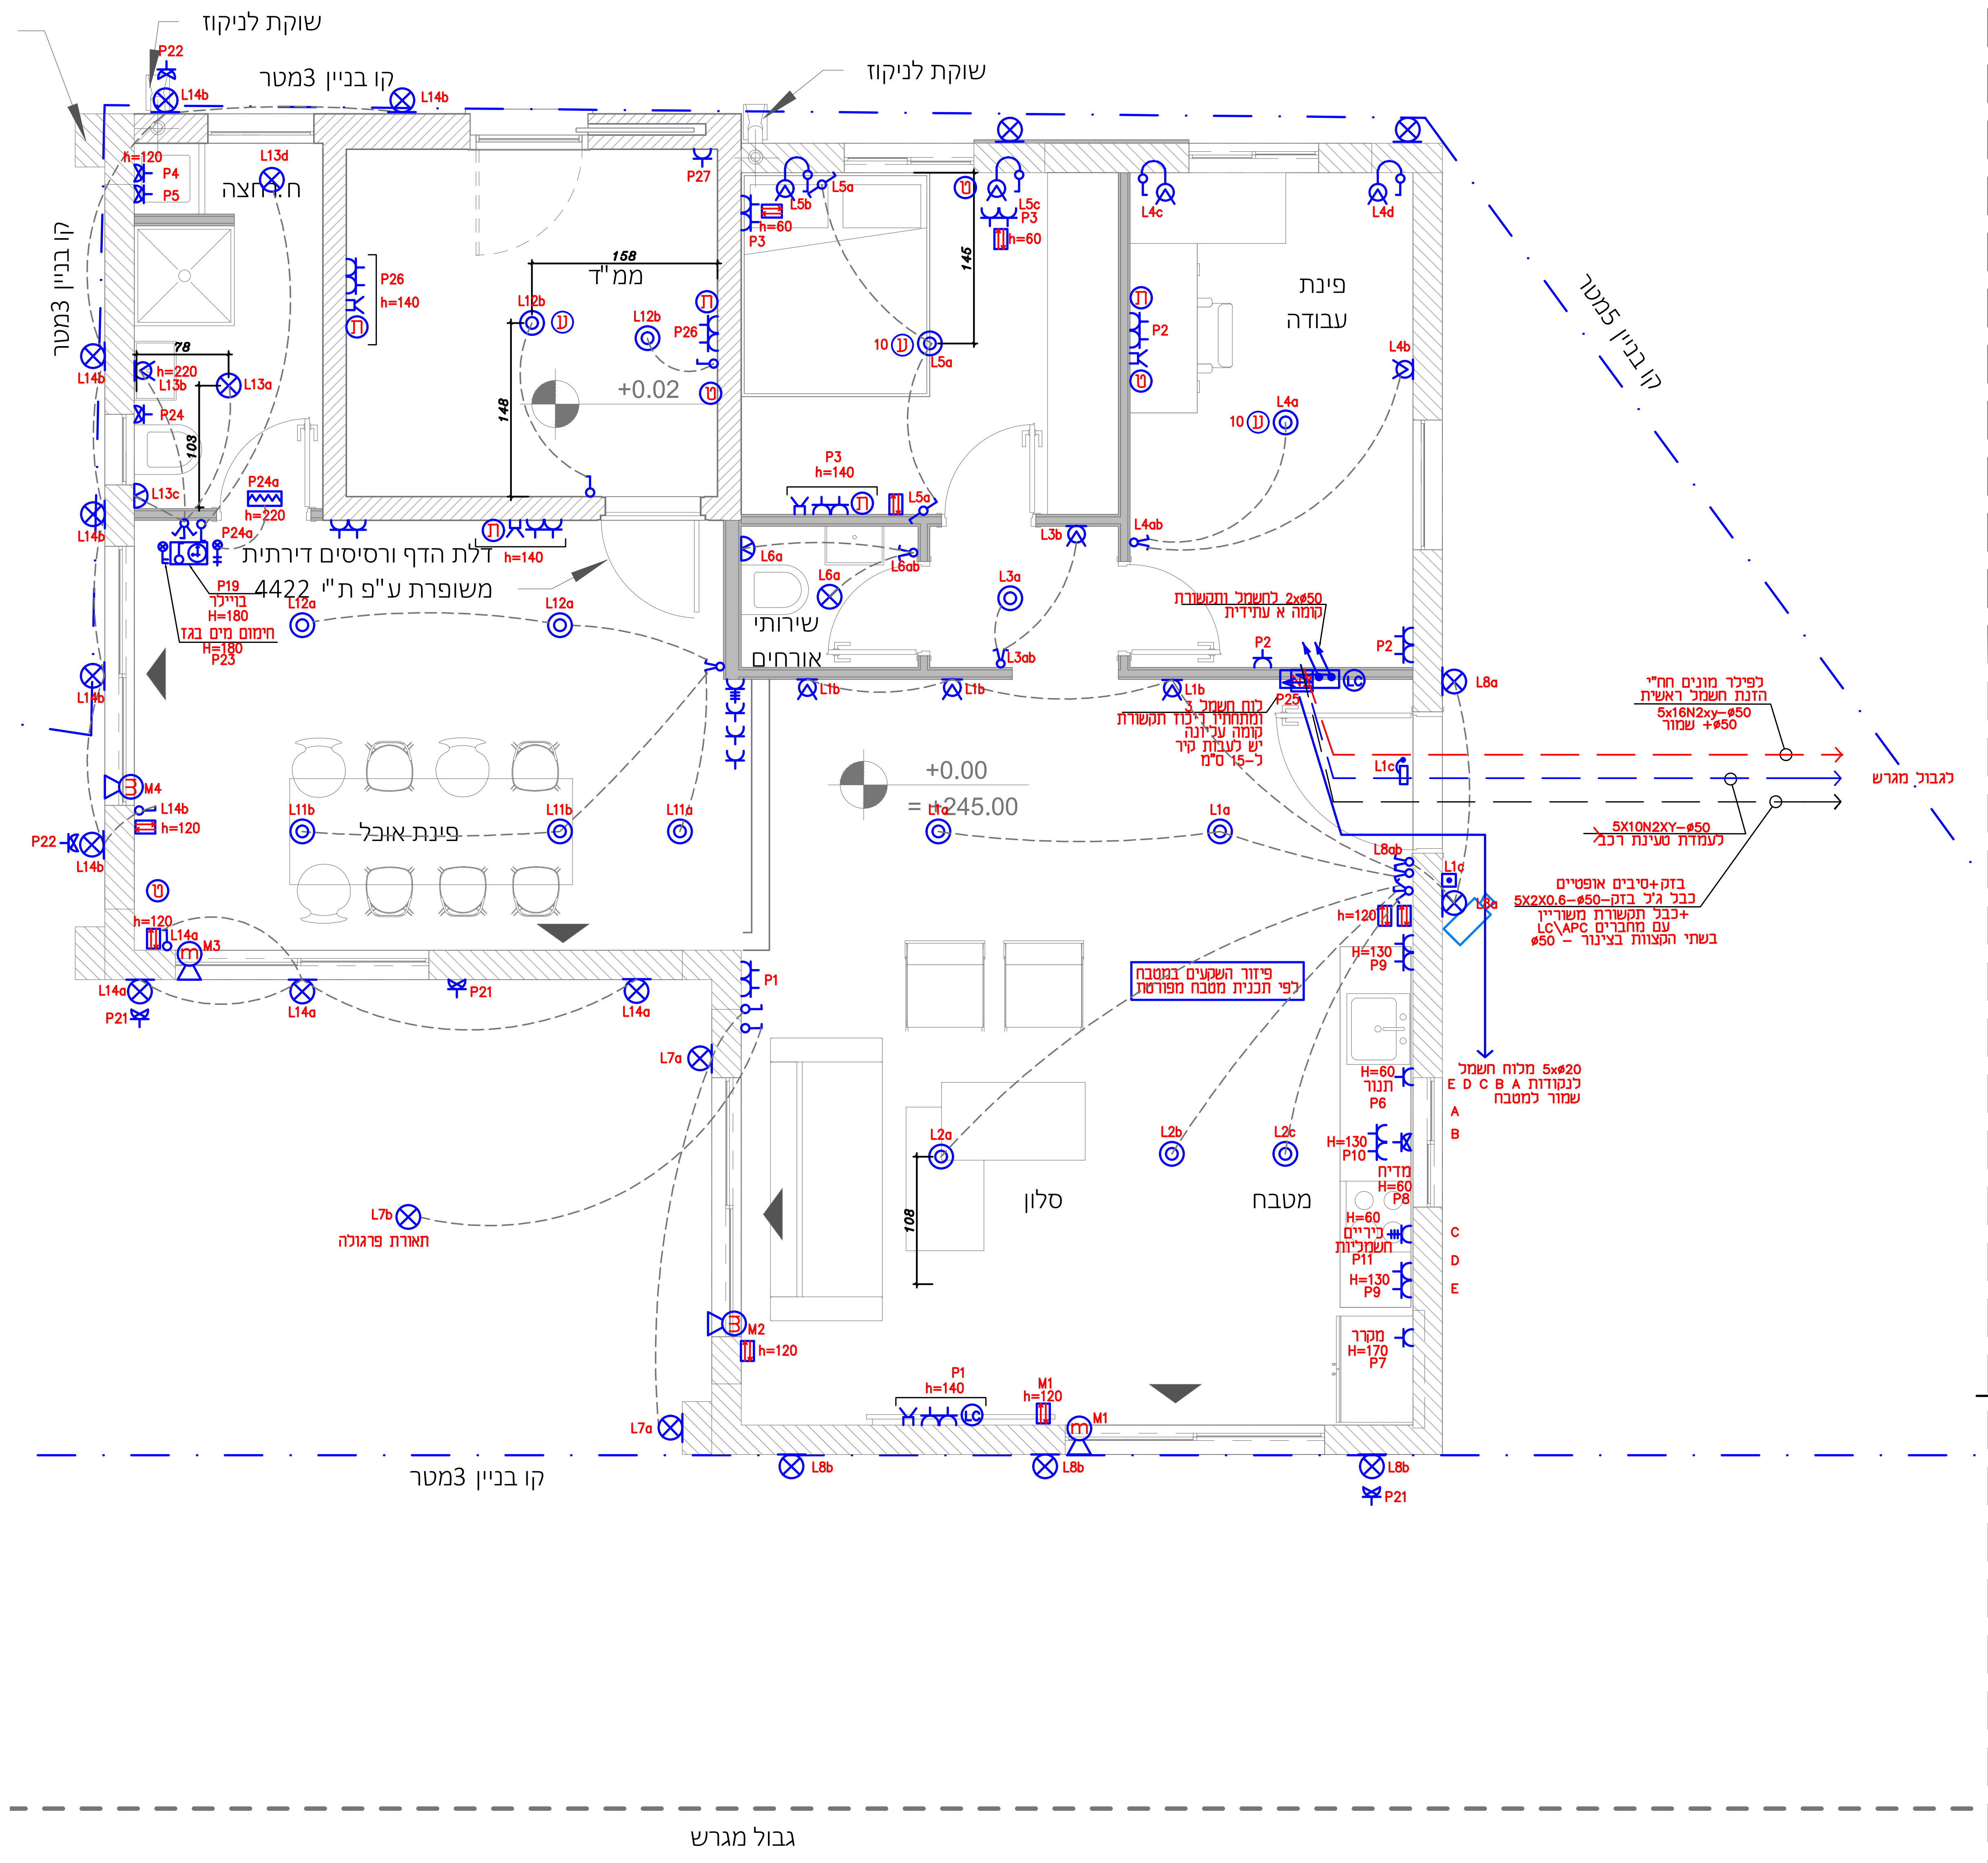
שוקת לניקוז
קו בניין 3מטר
קו בניין 5מטר
מקלחת
ממ"ד
+0.02
פינת עבודה
שירותי אורחים
דלת הדף ורסיס דירתית משופרת ע"פ ת"י 4422
פינת אוכל
+0.00 =±245.00
סלון
מטבח
תאורת פרגולה
2xø50 לחשמל ותקשורת קומה א עתידית
לוח חשמל 3 ומתחתיו ריכוז תקשורת קומה עליונה יש לעבות קיר ל-15 ס"מ
לפילר מונים חח"י הזנת חשמל ראשית 5x16N2xy-ø50 +ø50 שמור
5X10N2XY-ø50 לעמדת טעינת רכב
בזק+סיבים אופטיים כבל ג'ל בזק-5X2X0.6-ø50 +כבל תקשורת משוריין עם מחברים LC\APC בשתי הקצוות בצינור - ø50
לגבול מגרש
פיזור השקעים במטבח לפי תכנית מטבח מפורטת
5xø20 מלוח חשמל לנקודות A B C D E שמור למטבח
H=60 תנור P6
H=130 P9
H=130 P10
מדיח H=60 P8
H=60 כיריים חשמליות P11
גבול מגרש

קומת קרקע

מקרא חשמל ותאורה:

לוח		לוח חשמל
חשמל ותקשורת		שקע 16A בודד H=60 אלא אם צוין אחרת
		זוג שקעי 16A H=60 אלא אם צוין אחרת
	N2	מקבץ שקעים טיפוסי סיום באביזר N2 "ניסקו" בארון תקשורת מתחת לוח חשמל
		שקע חד פאזי מוגן מים H=60 אלא אם צוין אחרת
		שקע ליחידת מ"א 16A H=220 מיקום סופי לפי תכנית מיזוג ובתיאום מול אדריכל
	ט	נקודת טלפון מלאה-צנרת, כבילה ושקע טלפון H=60
		CIMA BOX הכולל: 4 שקעי שרות+2 תקשורת
	ת	נקודת תקשורת H=60, צינור ø25 עם חוט משיכה מריכוז תקשורת דירתי
		נקודת טלויזיה מושלמת+צינור שמור ø20 H=60
	LC	נקודת תקשורת מלאה הכוללת: כבל תקשורת אופטי תקני מותקן בצינור ø25 סיום בית תקע אופטי LC\APD לפי דרישות ת"י 1-11801 עם ראשים מוכנים מראש להתקנה בארון תקשורת דירתי ובסלון עם חוט משיכה מריכוז תקשורת דירתי
	m	מנוע חשמלי H=200
	T	הכנה לתרמוסטט מזגן- צינור 20 לחלל תקרה
	T	תרמוסטט חימום תת רצפתי- יבוצע לפי הנחיות ספק
		שקע לתנור חימום חשמלי 10 סמ מעל פתח דלת
		בוילר
		הכנה לוונטה סיום בשקע
מפסקים		מפסק מאור בודד H=90 אלא אם צוין אחרת במפסקי הדלקה ליד מיטה H=60
		מפסק כפול H=90
		מפסק מאור מחליף H=90
		לחצן פעמון דלת H=90
		מנתק מואר 2X16A / 3X16A
		מפסק דו קוטבי מואר לתנור חימום חשמלי H=160
		מפסק הרמה/הורדה לתריס חשמלי 5 סמ מעל מפסק תאורה ע"פ פרט
		מפסק עם שעון בקיר לבויילר H=180
	א	פנל צפיה (מוניטור) +לחצן פתיחה דלת H=120
תאורה וגילוי אש	⊗	תאורת חרום חד תכליתית LED 3w
	ע	גלאי עשן בתקרה
	◎	נקודת מאור בתקרה
	⊗	ג"ת פנים תקרתי מוגן מים
		ג"ת LED עגול שקוע בתקרה
		ג"ת פנים קירי למנורת לילה H=120
	⊗	ג"ת פנים/חוץ קירי מוגן מים H=240 , במרתף H=220
		ג"ת קירי נמוך לתאורת התמצאות מדרגות/שירותים, h=15 מהרצפה/ מרום מדרגה
		ג"ת מלבני IP65 להתקנה על פרגולה
		מאוורר להתקנה בחוץ
		פעמון דלת 220V (גונג) התקנה מעל דלת כניסה
		הכנה מצלמה אבטחה, צינור 25 וחוט משיכה מארון תקשורת דירתי

פרט לגבהים של הדלקות, תאורה ותריסים:

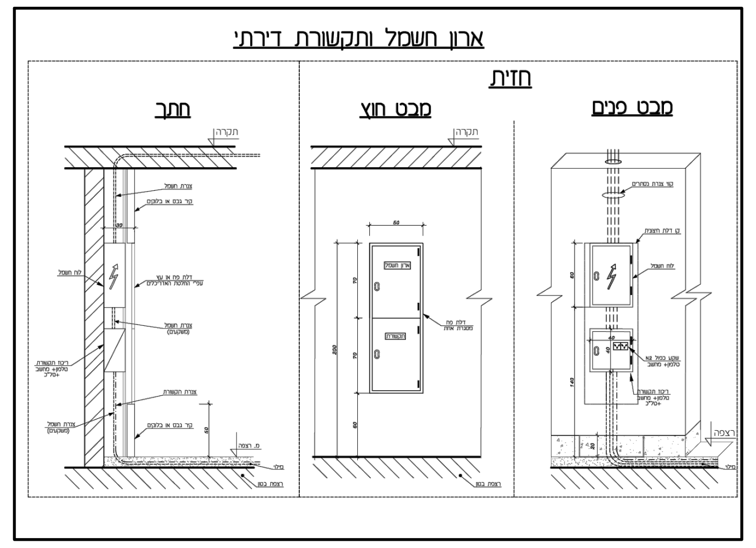

תפוצה	תאריך
מנהל הפרויקט	
אדריכל	
מזמין/יזם	
חשמל	
קבלן	
בטיחות	
אקוסטיקה	
אינסטלציה	
קונסטרוקציה	
אדריכל נוף	
מטבחים	
חברת חשמל	
חברת בזק	

מס'	שינויים	תאריך
1	עידכון תוכנית	10.12.24
2	עידכון תוכנית	15.12.24
3	עידכון תוכנית	24.12.24
4	עידכון לפי שינויי דיירים	9.3.25
5	עידכון לפי שינויי דיירים	16.4.25

עודכן ע"י: יפעת

הערות:
מיזוג אויר- עפ תכנית יועץ מיזוג

א. בסיס
הנדסת חשמל בע"מ
משרד: יד חרוצים 16, ירושלים 93420
טל: 074-7021015 נייד: 050-6550484
פקס: 077-5131015 דוא"ל: office@ebasis.co.il

שם הפרויקט:
נופיה-אלפי מנשה
מגרש 21

שם הגיליון:
תוכנית חשמל טיפוסית

○ לעיון ● לאישור ○ למכרז ○ לביצוע

קנה מידה: 1:50

מס' קובץ: File: 675-21.dwg

תאריך: Date: 30.09.2024

תכנן: איתן

שרטט: שלומית

אישר: איתן

מס' עדכון: 5

מס' הגליון: 1

מס' הפרויקט: 675