

[illegible]

		4
		5
חגניות לאסור	02.05.2025	7
חגניות כעיון	10.04.2025	1
שניניים:	חאריך:	סך:

הערות

- ## מקרא


- מקרא צבעים בתכנית

- | | |
|--------------------------|---|
| תעלות ותריסי אוויר חוזר |  |
| תעלות ותריסי אספקת אוויר |  |
| תעלות ותריסי אוויר צח |  |
| תעלות ותריסי ניקת אוויר |  |
| תעלות ותריסי שיחרור עשן |  |
| צנרת גז וחשמל |  |
| סימון מעגלי מידוג אוויר |  |

191	מבני מגורים צמודי קרקע נופיה אפרי מנשה מגרש 21
רח' דודמנ	שם הפרויקט
1:50	מידוך אוויר ואווירור - הנתון בבכר
02.05.2025	קומה ראשונה וגג
תחילת עבודות	שם העבודה
2	
מחזוריות	שם המחזור
☐ לבדיקה ☐ נכסדור ☒ לאשדור	עיון
	10.04.2025
	האדריכל
	הנבנה והמסר
	אייזר ארז

כלל יחידות המיזוג אשר נמצאות בתוך נגרות יש לתאם סופית מול אדריכל ונגרות

Option No2
inverter duct unit in living
room and wall mounted in
rooms

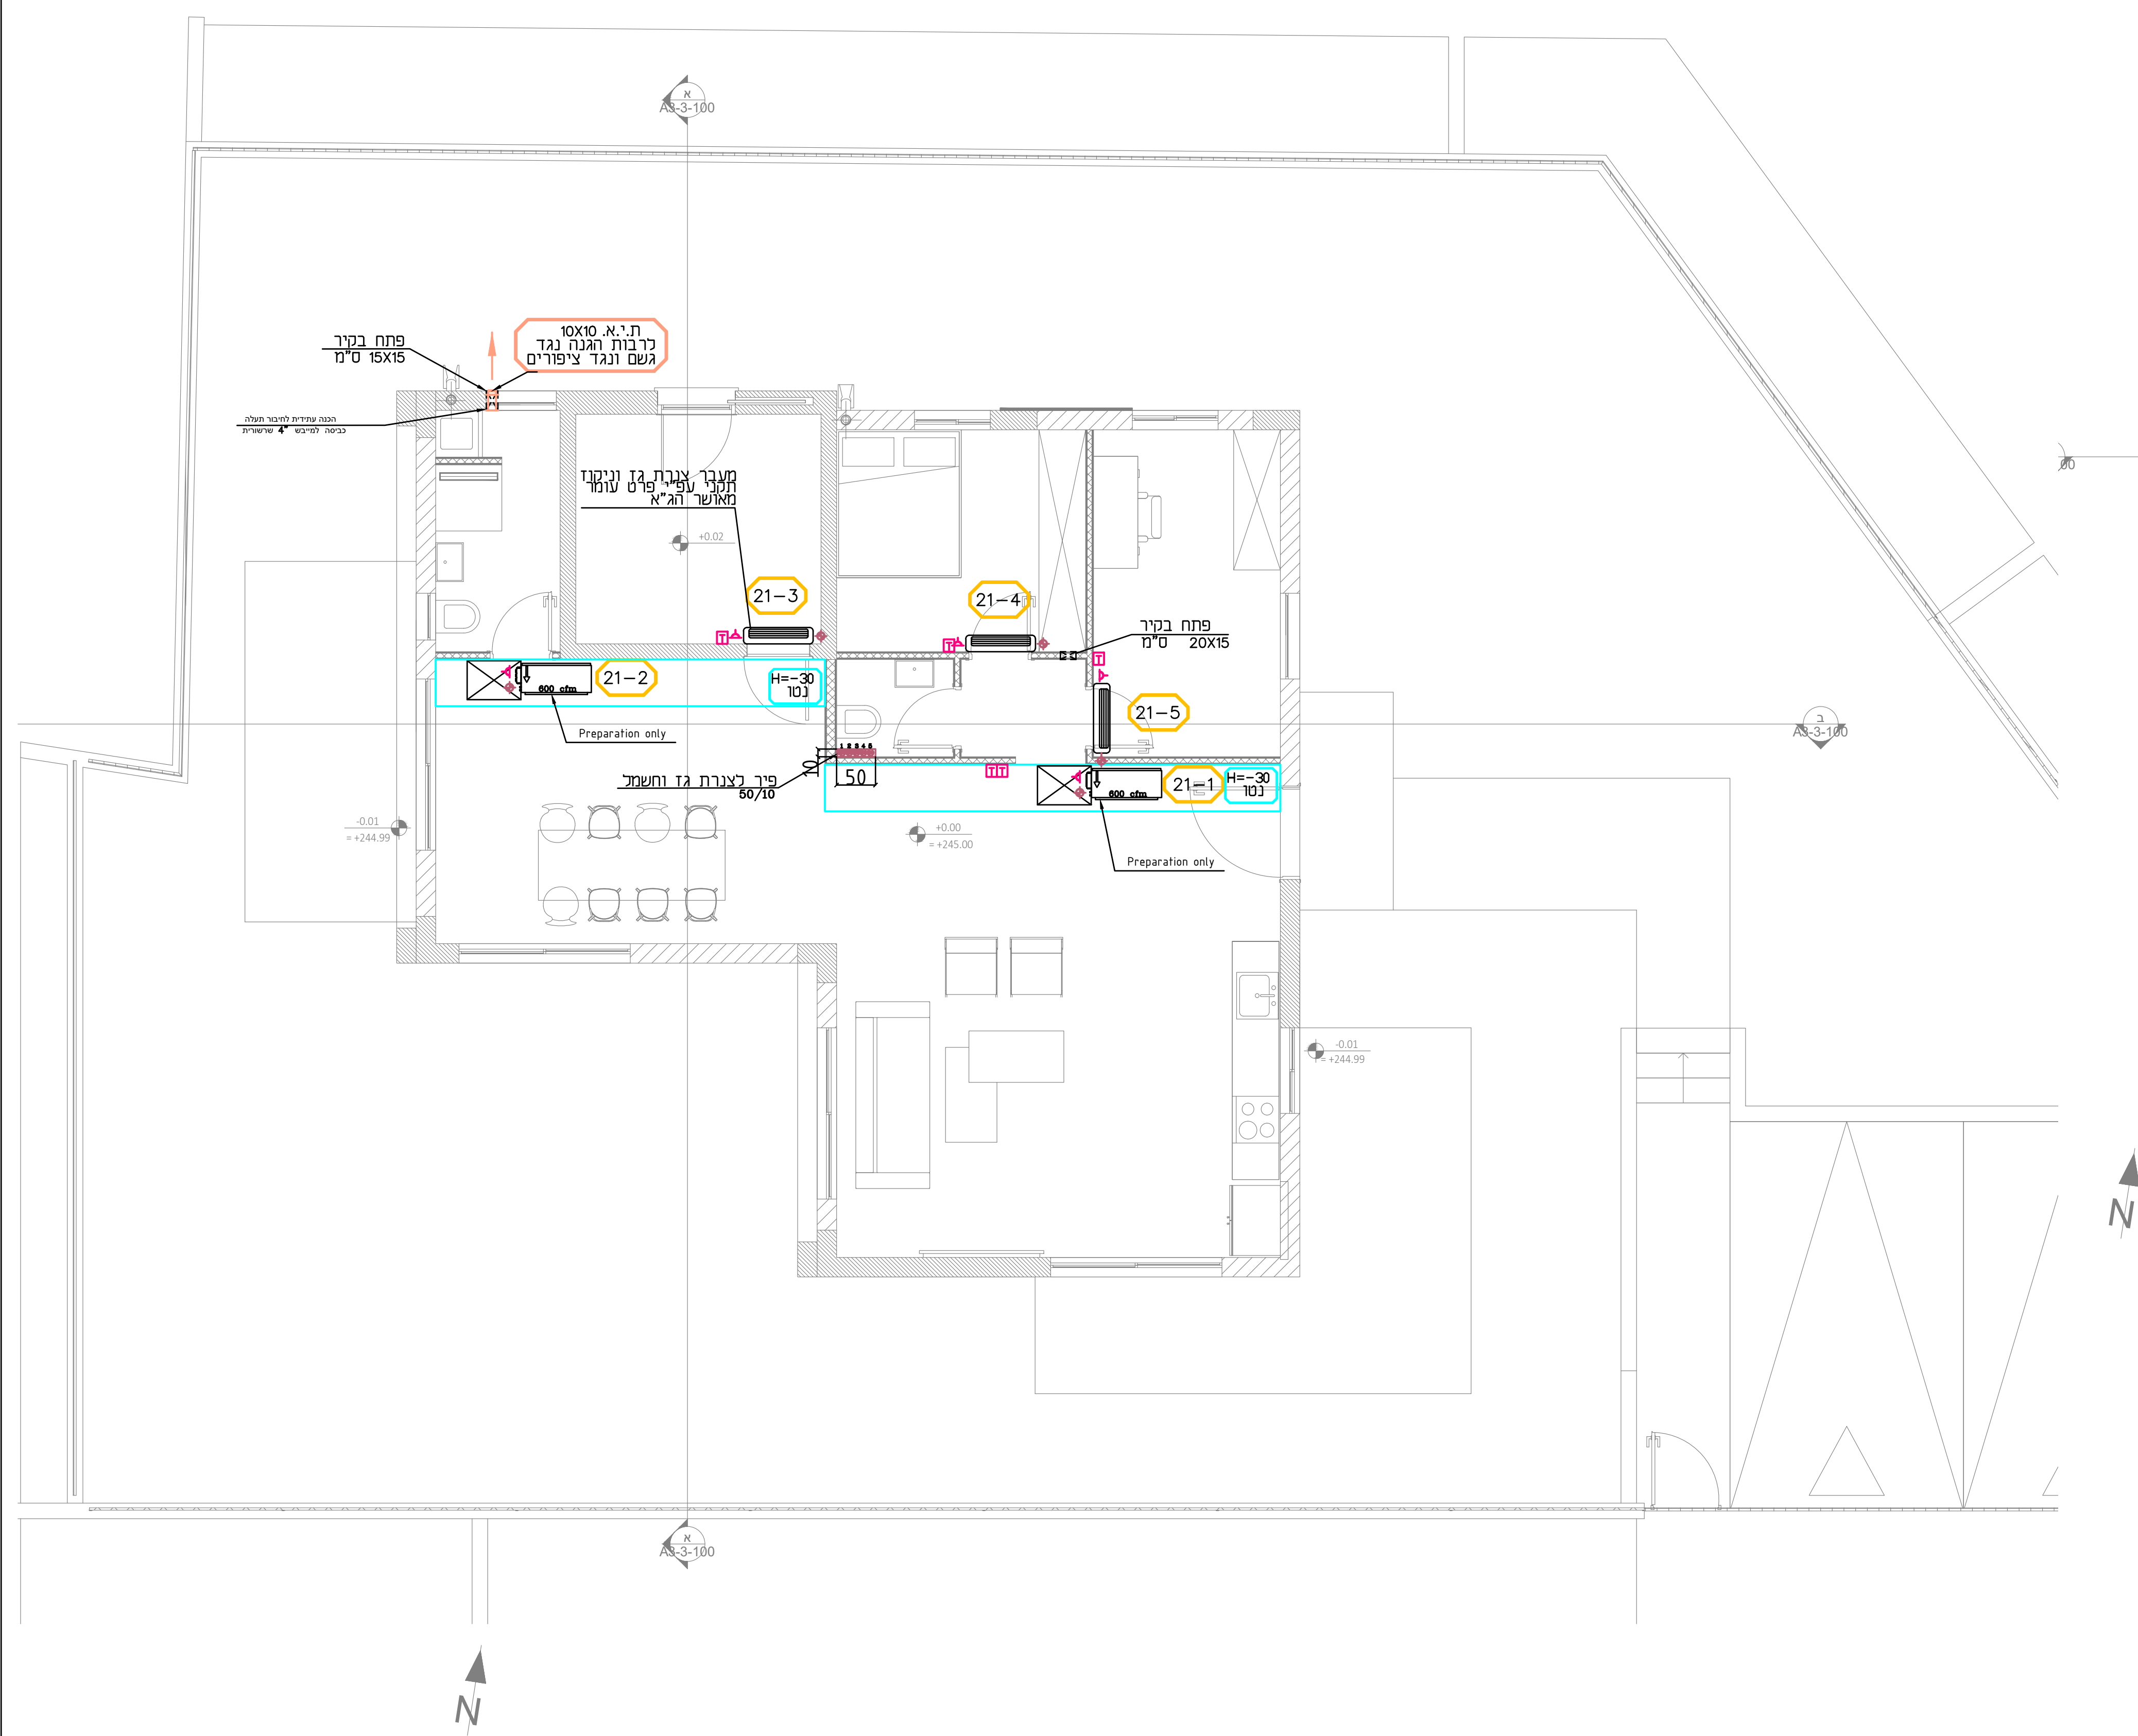

Option No2
inverter duct unit in living
room and wall mounted in
rooms

תפוצה

אוריכל פנים	אונטציע	במיתת אש	אקוטציקה	חשמי התארה	קונסטרוקציע	קבלו ראש	ניחול פרויקט	נמח	אוריכל
-------------	---------	----------	----------	------------	-------------	----------	--------------	-----	--------

מהדורה

		⚠
		⚠
חבנית כאשר	02.05.2025	⚠
חבנית רעיון	10.04.2025	⚠
שנתיים:	חאריץ:	ס:

המבצע אחראי למידות ולהתאמתן למציאות בכל מקרה של אי התאמה, סתירה או טעות עליו להודיע למתכנן לפני התקדמותו בביצועו אין לקבוע מידות על סמך מדיניות בשרטוט. אין לעשות כל שימוש בתוכנית זו ברעיונות הגלומים בה ללא אישור בכתב מאת המתכנן.

הערות

1. כל הבנידוד מחוץ למכתבה יבדודו
ברבידוד אקוסט' בעבור "2"
מידות העלעות ה מידות פח
2. תעלות מידות בתוך המכתבה יבדודו
ברבידוד אקוסט' פנים "1"
מידות העלעות ה מידות פח
3. תעלות אוויר צה יבדודו
ברבידוד טומ "1"
מידות העלעות ה מידות פח
4. יש לאסום בסטיליקון פנות החיבור
ש תעלות מידות אוויר לפני כיפוף
הפנים המתחברים

מקרא

פס- פסוח	
מ.א.ב. - מפדו אוויר קורי	
מ.א.ת. - מפדו אוויר הכרתי	
ת.א.ת. - חרירי אוויר חודר	
ת.א.צ. - חרירי אוויר צח	
ב.א. - בידוד אקוסטי	
ב.ס. - בידוד טרמי	
כ.ב. - כלא בידוד	
ד.ד. - דפדף אש	
מורמסנט	
חשחרת חשחרת	
חשחרת חשחרת	
מקרא צבעים בתכנית

- | | |
|--------------------------|---|
| תעלות ותריסי אוויר חוזר |  |
| תעלות ותריסי אספקת אוויר |  |
| תעלות ותריסי אוויר צח |  |
| תעלות ותריסי יניקת אוויר |  |
| תעלות ותריסי שיחרור עשן |  |
| צנרת גז וחשמל |  |
| סימון מעגלי מיוזג אוויר |  |

[illegible]