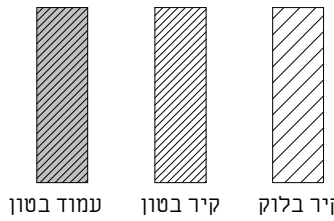


## מתכונים:

|                               |
|-------------------------------|
| ניהול פרויקט                  |
| מהיסוד - בן סולומון           |
| פיקוח                         |
| מהיסוד - בן סולומון           |
| קונסטרוקציה                   |
| ערן שילר                      |
| מיזוג אוויר                   |
| אייל ארז מהנדסים ויועצים בע"מ |
| אינסטלציה                     |
| איתן אלמסי                    |
| חשמל                          |
| איתן בסיס                     |
| אלומיניום                     |
| נוף                           |
| נתי בלוקא                     |
| חשמל חכם                      |
| חימום תת רצפתי                |
| איטום                         |
| צבי טל                        |
| אקוסטיקה                      |
| מעליות                        |
| קרקע וביסוס                   |
| דיה הנדסת קרקע וביסוס         |
| רישוי                         |

[illegible]

מקרא קירות:

[illegible]

## אדריכלות

CLIENT NAME: \_\_\_\_\_ שם המזמין:

## קבוצת רכישה נופיה


PROJECT NAME: שם הפרויקט:

נופיה - מגרש 22

DRAWING NAME: ס הגליון:

SHEET NUMBER: 190 גליון:

A3-1-100
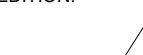
|         |           |                                                                                     |           |
|---------|-----------|-------------------------------------------------------------------------------------|-----------|
| SCALE:  | קנה מידה: | EDITION:                                                                            | דפוס:     |
| STATUS: | סטוס      |  |           |
| למכר    |           |                                                                                     |           |
|         | נבדק ע"י: | אלמוג אור                                                                           | דפוס ע"י: |
| DATE:   | 22.09.25  |                                                                                     | מ"ר:      |




NeumanHaynerArchitects

office@nh-arch.com  
www.nh-arch.com

וימן חיינר אדריכלים  
מורד ההדרים 2, בית חירות  
טל 09-9545842

| נופיה - מגרש 22 |           |        |                   |
|-----------------|-----------|--------|-------------------|
| מס' גיליון      | שם גיליון | מהדורה | תאריך הפצת מהדורה |
|                 |           |        |                   |

|          |   |                 |           |
|----------|---|-----------------|-----------|
| 22.09.25 | 1 | גליון שער       | A3-1-100  |
| 22.09.25 | 1 | תכנית קומת קרקע | A3-1-101  |
| 22.09.25 | 1 | תכנית קומה א    | A3-1-102  |
| 22.09.25 | 1 | תכנית מפלס גג   | A3-1-103  |
| 22.09.25 | 1 | חזיתות 1        | A3-2-200  |
| 22.09.25 | 1 | חזיתות 2        | A3-2-201  |
| 22.09.25 | 1 | חתכים           | A3-3-100  |
| 22.09.25 | 1 | גליון מדגות     | A3-4-100  |
| 22.09.25 | 1 | פרטים           | A3-4-103  |
| 22.09.25 | 1 | פרטי פרגולה     | A3-4-104  |
| 22.09.25 | 1 | רשימת פתחים     | A3-6-1000 |

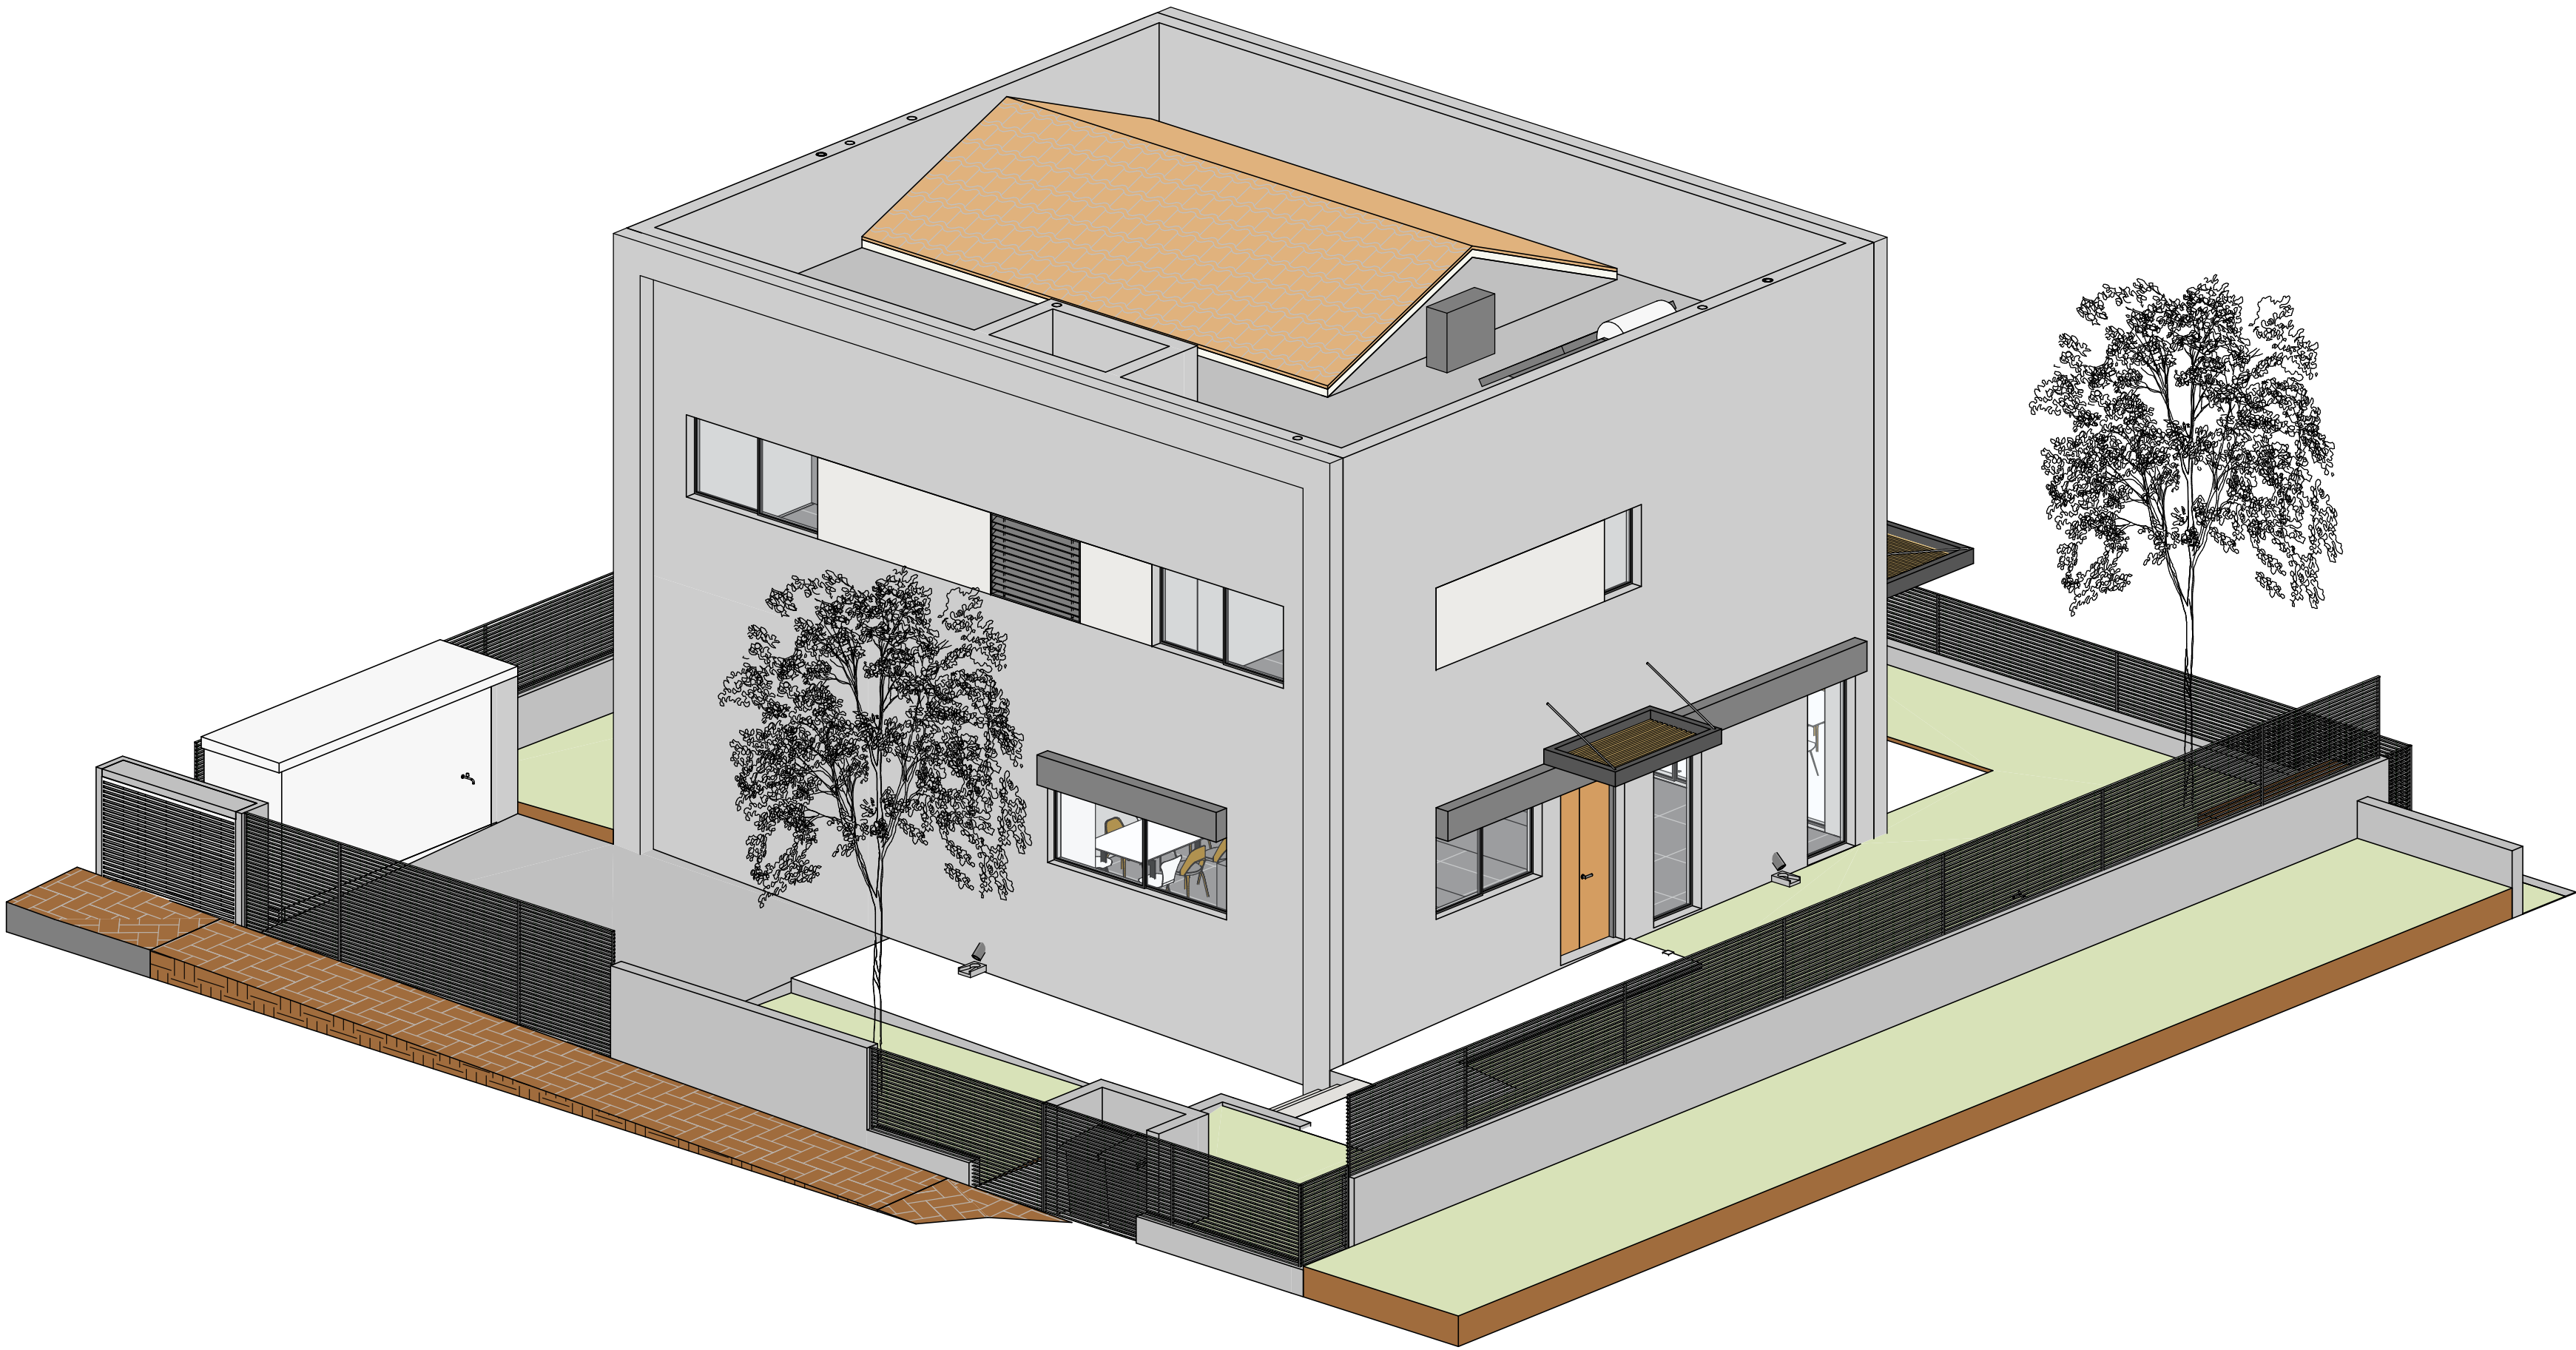

זכויות ייצור / ע"פ הנחיות עו"ד



|                               |
|-------------------------------|
| ניהול פרויקט                  |
| מהיסוד - בן סולומון           |
| פיקוח                         |
| מהיסוד - בן סולומון           |
| קונסטרוקציה                   |
| ערן שילר                      |
| מיזוג אוויר                   |
| אייל ארז מהנדסים ויועצים בע"מ |
| אינסטלציה                     |
| איתן אלמסי                    |
| חשמל                          |
| איתן בסיס                     |
| אלומיניום                     |
|                               |
| נוף                           |
| נתי בלוקא                     |
| חשמל חכם                      |
|                               |
| חימום תת רצפתי                |
|                               |
| איטום                         |
| צבי טל                        |
| אקוסטיקה                      |
|                               |
| מעליות                        |
|                               |
| קרקע וביסוס                   |
| דיה הנדסת קרקע וביסוס         |
| רישוי                         |

[illegible]

 עמוד בטון  
 קיר בטון  
 ירי בלוק

[illegible]

|                   |            |
|-------------------|------------|
| CLIENT NAME:      | המחיר      |
| קבוצת רכישה נופיה |            |
| PROJECT NAME:     | הפרויקט    |
| נופיה - מגרש 22   |            |
| DRAWING NAME:     | התכנון     |
| תכנית קומת קרקע   |            |
| SHEET NUMBER:     | מפרט גליון |
| A3-1-101          |            |


|            |           |                                                                                     |           |
|------------|-----------|-------------------------------------------------------------------------------------|-----------|
| SCALE:     | קנה מידה: | EDITION:                                                                            | חזרה:     |
| 1 : 50     |           |  |           |
| STATUS:    | סטטוס     |                                                                                     |           |
| למברז      |           |                                                                                     |           |
| שרון בוימן | נבדק ע"י: | אלמוג אור                                                                           | רדסט ע"י: |
| DATE:      | 22.09.25  |                                                                                     | חזיר:     |

office@nh-arch.com  
www.nh-arch.com

מורד ההדרים 2, בית חירות  
טל 09-9545842

זכויות ייצור / ע"פ הנחיות עו"ד

1. יש לעבוד במקביל לתכניות יועצים המאושרות על ידי האדריכל.
2. פרטי ספי חלון - עפ"י חוברת אלומיניום של הספק הנבחר ובתיאום מול אדריכל.
3. חימום תת רצפתי (במידה ויש במגרש זה) עפ"י פרטי הספק ובתיאום מול אדריכל.
4. יש לעבוד במקביל לתכניות עיצוב פנים (במידה ויש מעצב פנים במגרש זה) המאושרות על ידי האדריכל.
5. באחריות הקבלן לעדכן את האדריכל על אי התאמה בין התכניות יועצים לאדריכלות.
6. כל הדלתות לפי מפרט מצורף.
7. כל אלמנטי הבטון יקבלו התייחסות תרמית לפי הנחיות יועץ.
8. פרטי איטום, בידוד וניקוז עפ"י תכניות יועצים ובאחריות הקבלן.

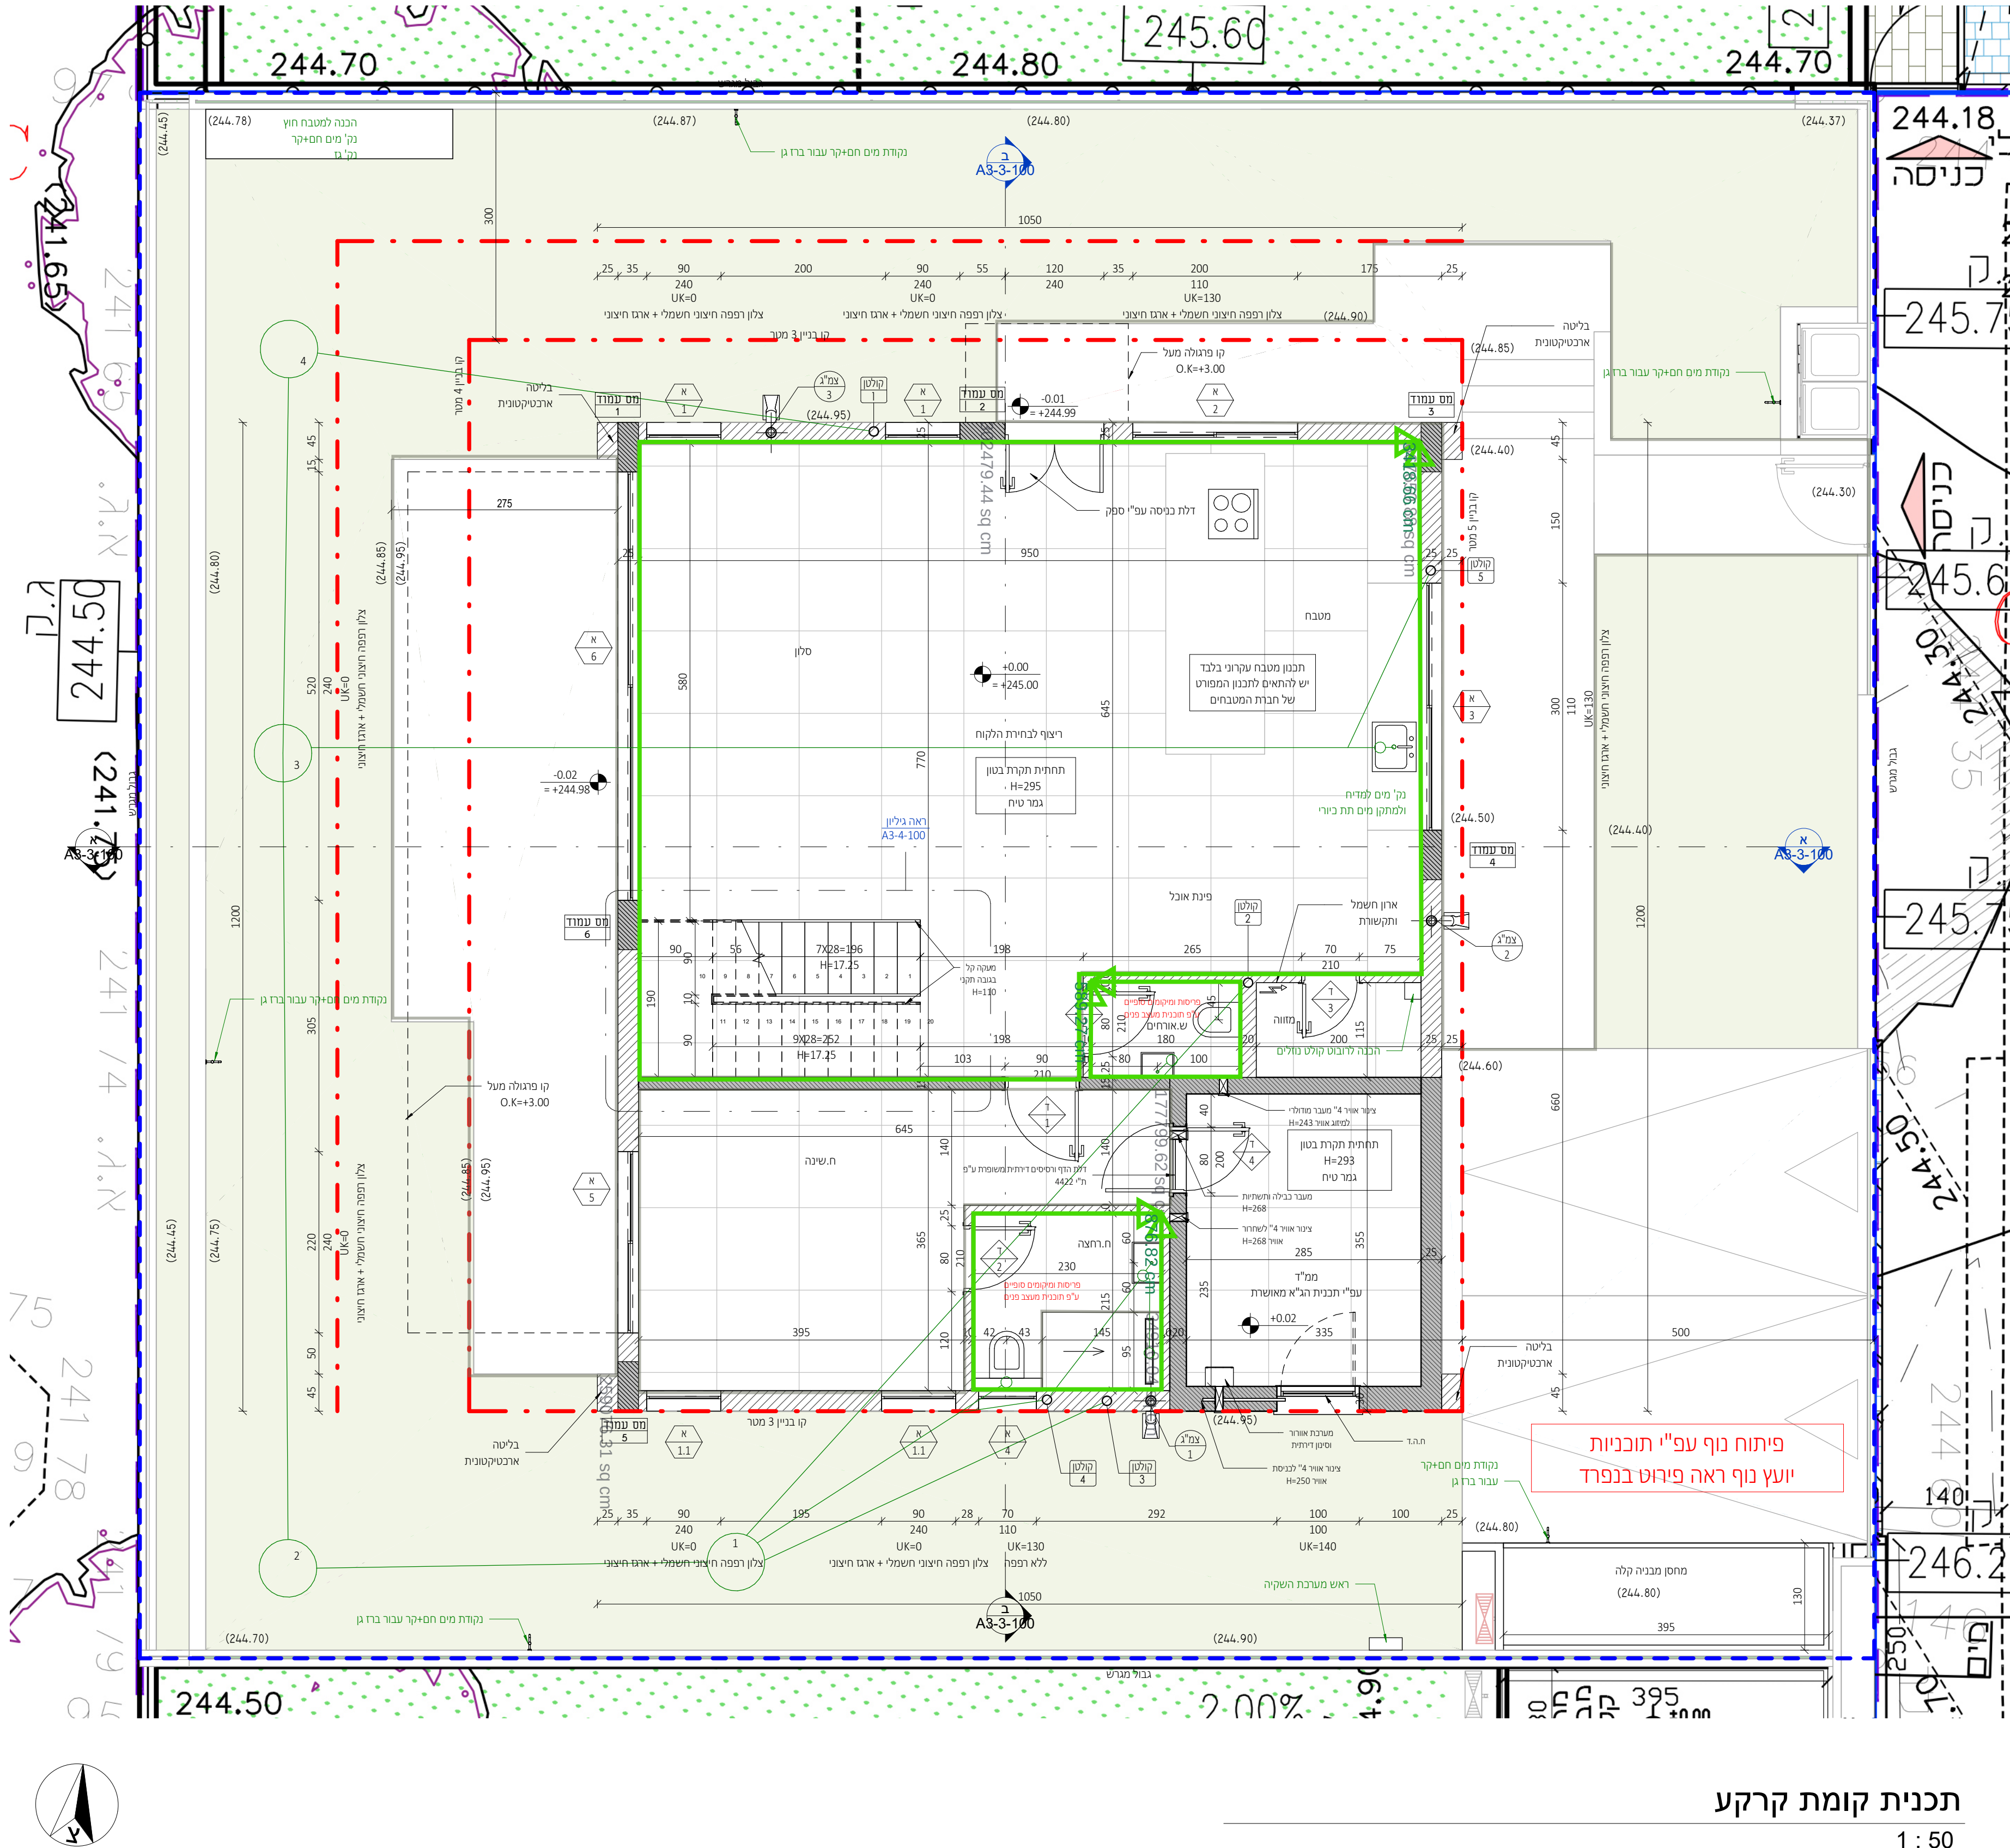

1 : 50



|                               |
|-------------------------------|
| ניהול פרויקט                  |
| מהיסוד - בן סולומון           |
| פיקוח                         |
| מהיסוד - בן סולומון           |
| קונסטרוקציה                   |
| ערן שילר                      |
| מיזוג אוויר                   |
| אייל ארז מהנדסים ויועצים בע"מ |
| אינסטלציה                     |
| איתן אלמסי                    |
| חשמל                          |
| איתן בסיס                     |
| אלומיניום                     |
| נוף                           |
| נתי בלוקא                     |
| חשמל חכם                      |
| חימום תת רצפתי                |
| איטום                         |
| צבי טל                        |
| אקוסטיקה                      |
| מעליות                        |
| קרקע וביסוס                   |
| דיה הנדסת קרקע וביסוס         |
| רישוי                         |

[illegible]

קיר בלוק   קיר בטון   עמוד בטון


|                   |            |
|-------------------|------------|
| אדריכלות          |            |
| CLIENT NAME:      | ה'תשס"ח    |
| קבוצת רכישה נופיה |            |
| PROJECT NAME:     | הפרויקט    |
| נופיה - מגרש 22   |            |
| DRAWING NAME:     | התכנית     |
| תכנית קומה א      |            |
| SHEET NUMBER:     | 190 גליון: |
| A3-1-102          |            |

NeumanHaynerArchitects

יומן חיינר אדריכלים  
יורד ההדריס 2, בית חירות  
09-9545842 טל

office@nh-arch.com  
www.nh-arch.com

1. יש לעבוד במקביל לתכניות יועצים המאושרות על ידי האדריכל.
2. פרטי ספי חלון - עפ"י חוברת אלומיניום של הספק הנבחר ובתיאום מול אדריכל.
3. חימום תת רצפתי (במידה ויש במגרש זה) עפ"י פרטי הספק ובתיאום מול אדריכל.
4. יש לעבוד במקביל לתכניות עיצוב פנים (במידה ויש מעצב פנים במגרש זה) המאושרות על ידי האדריכל.
5. באחריות הקבלן לעדכן את האדריכל על אי התאמה בין התכניות יועצים לאדריכלות.
6. כל הדלתות לפי מפרט מצורף.
7. כל אלמנטי הבטון יקבלו התייחסות תרמית לפי הנחיות יועץ.
8. פרטי איטום, בידוד וניקוז עפ"י תכניות יועצים ובאחריות הקבלן.

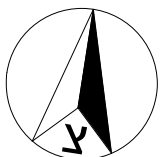

## 1 : 50




## מתכונים:

|                               |
|-------------------------------|
| ניהול פרויקט                  |
| מהיסוד - בן סולומון           |
| פיקוח                         |
| מהיסוד - בן סולומון           |
| קונסטרוקציה                   |
| ערן שילר                      |
| מיזוג אוויר                   |
| אייל ארז מהנדסים ויועצים בע"מ |
| אינסטלציה                     |
| איתן אלמסי                    |
| חשמל                          |
| איתן בסיס                     |
| אלומיניום                     |
| נוף                           |
| נתי בלוקא                     |
| חשמל חכם                      |
| חימום תת רצפתי                |
| איטום                         |
| צבי טל                        |
| אקוסטיקה                      |
| מעליות                        |
| קרקע וביסוס                   |
| דיה הנדסת קרקע וביסוס         |
| רישוי                         |

[illegible]

זקרא קירות:

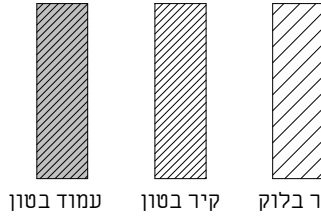[illegible]

## אדריכלות


|               |  |                                                                                     |  |
|---------------|--|-------------------------------------------------------------------------------------|--|
| PROJECT NAME: |  | קבוצת רכישה נופיה                                                                   |  |
| DRAWING NAME: |  | נופיה - מגרש 22                                                                     |  |
| SHEET NUMBER: |  | תכנית מפלס גג                                                                       |  |
| SCALE:        |  | EDITION:                                                                            |  |
| 1 : 50        |  |  |  |
| TATUS:        |  | מסמך                                                                                |  |
| למכרז         |  | נבדק ע"י:                                                                           |  |
| שרון בינמן    |  | אלמוג אור                                                                           |  |
| DATE:         |  | 22.09.25                                                                            |  |



NeumanHaynerArchitects

וימן חיינר אדריכלים  
מורד ההדרים 2, בית חירות  
טל' 09-9545842

זכויות ייצור / ע"פ הנחיות עו"ד

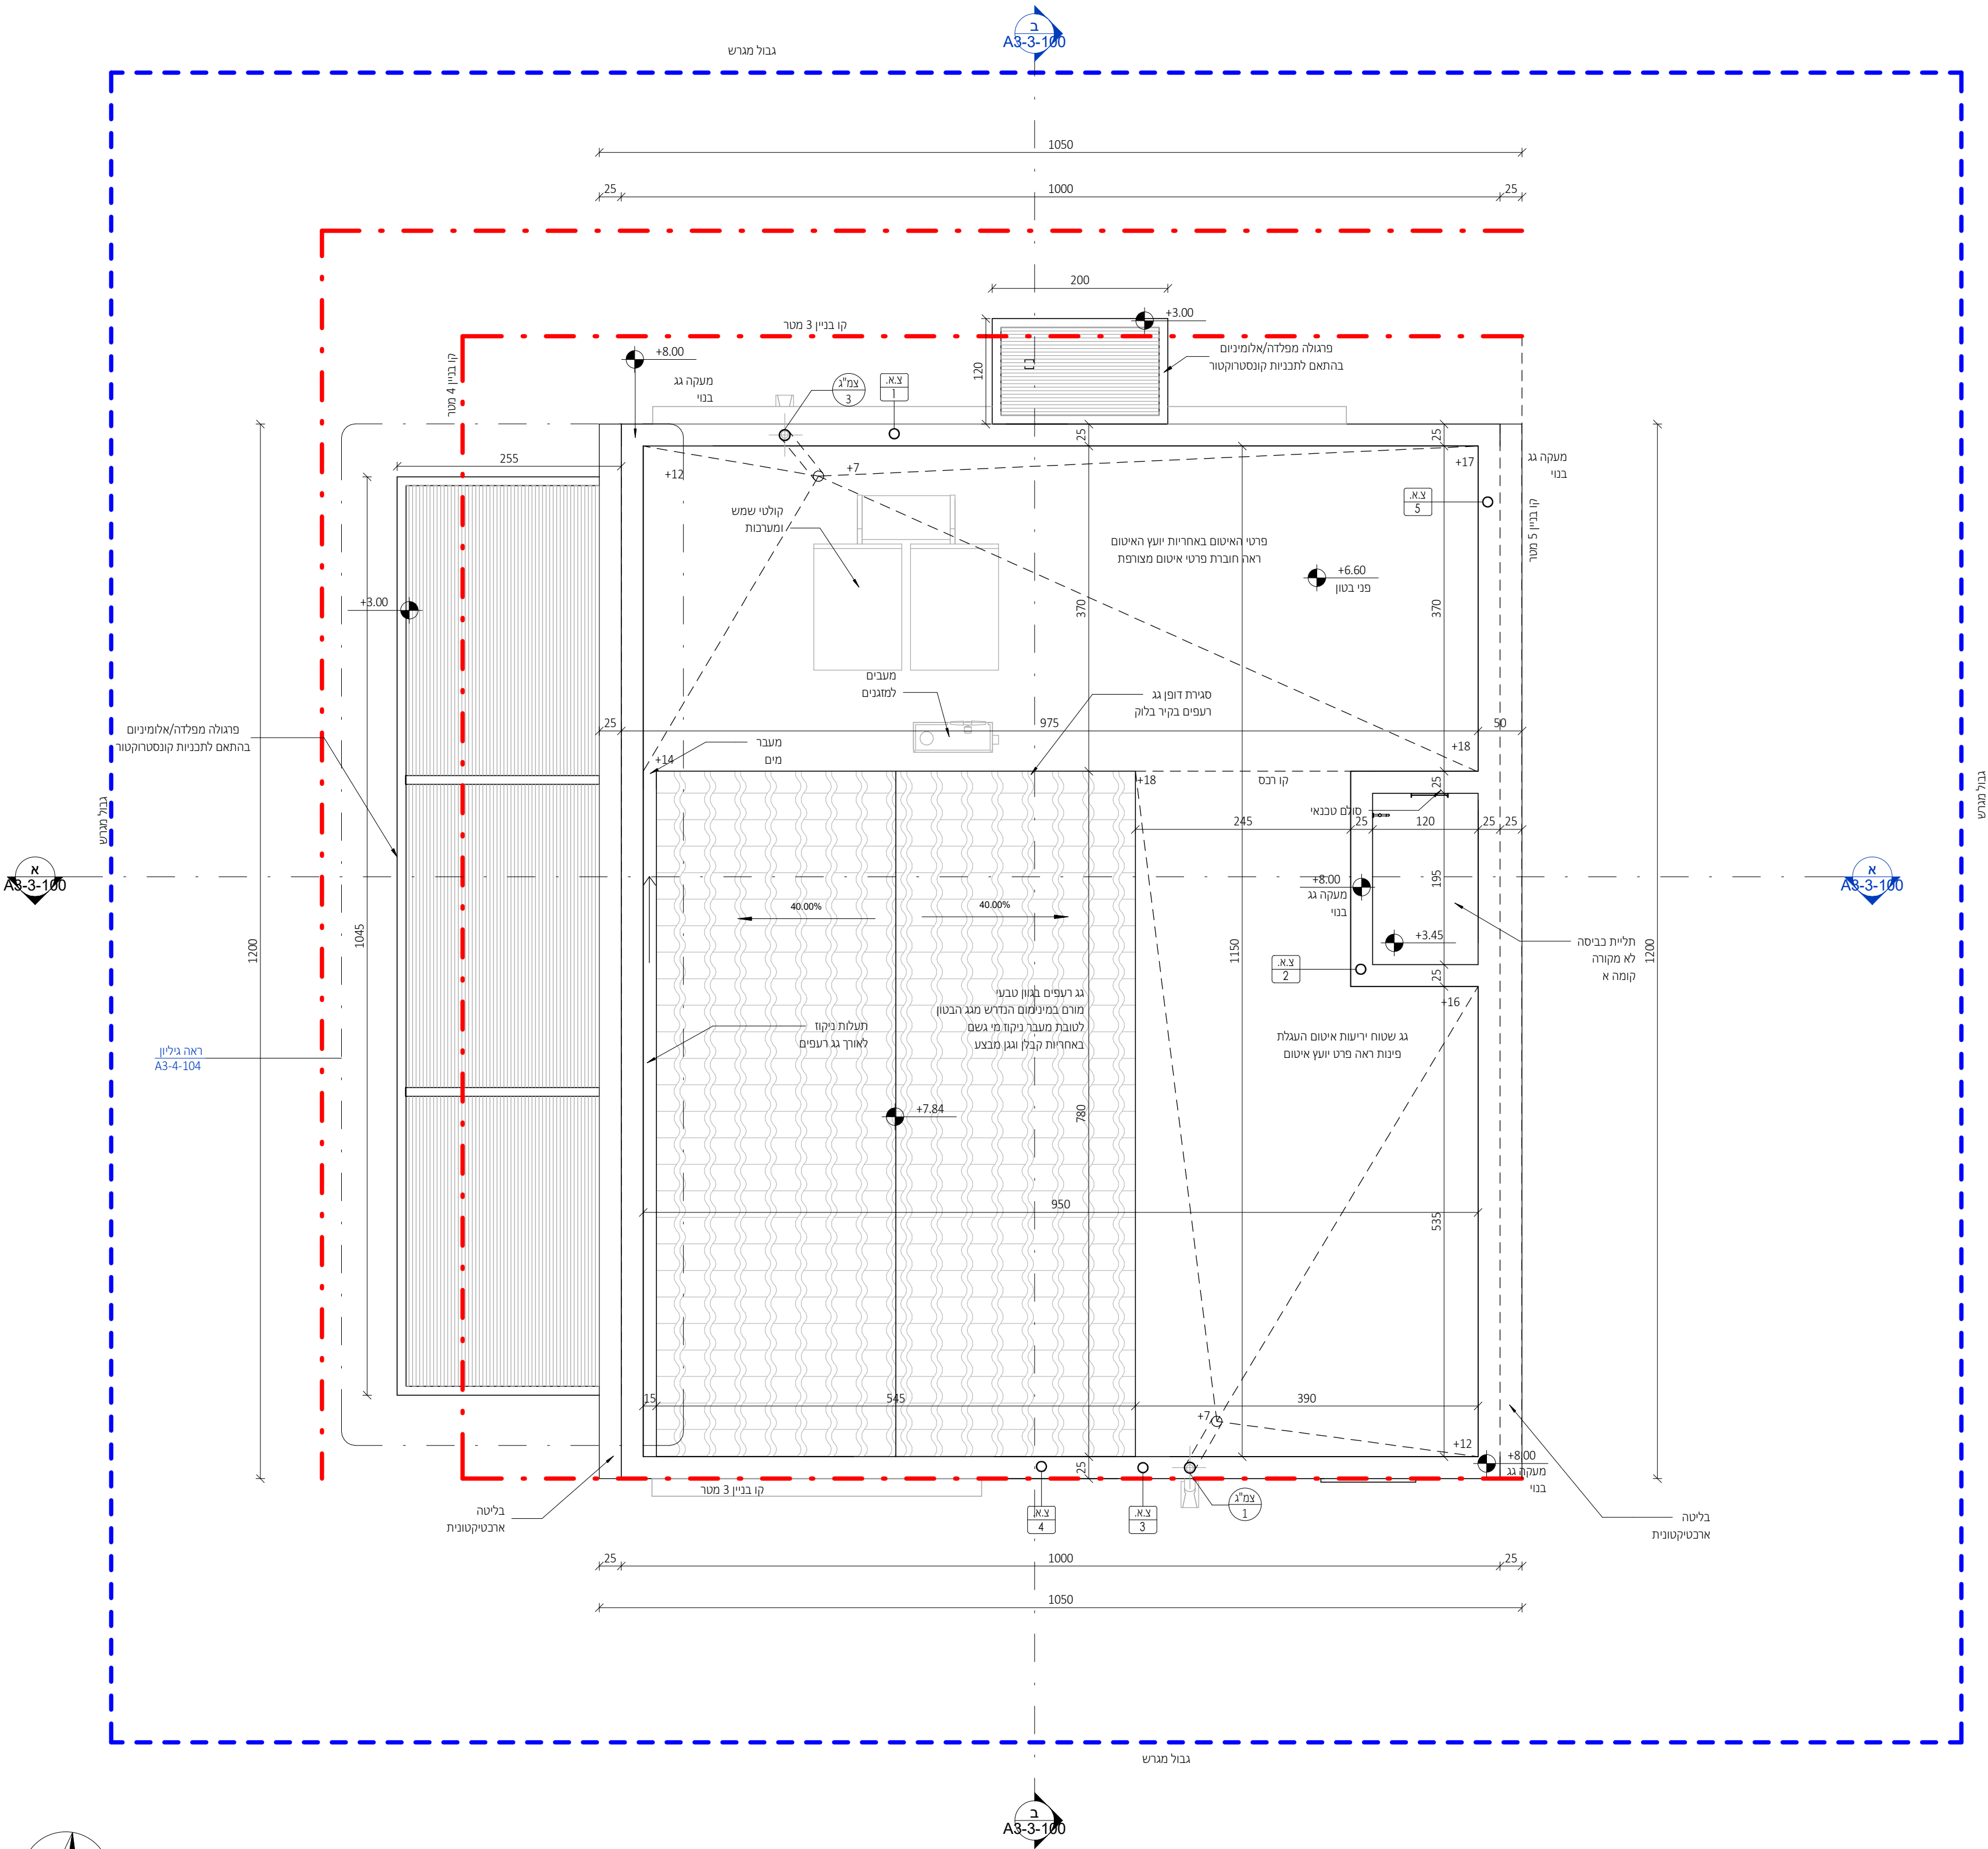

## תכנית גג

1 : 50




|                               |
|-------------------------------|
| ניהול פרויקט                  |
| מהיסוד - בן סולומון           |
| פיקוח                         |
| מהיסוד - בן סולומון           |
| קונסטרוקציה                   |
| ערן שילר                      |
| מיזוג אוויר                   |
| אילל ארז מהנדסים ויועצים בע"מ |
| אינסטלציה                     |
| איתן אלמסי                    |
| חשמל                          |
| איתן בסיס                     |
| אלומיניום                     |
| נוף                           |
| נתי בלוקא                     |
| חשמל חכם                      |
| חימום תת רצפתי                |
|                               |
| איטום                         |
| צבי טל                        |
| אקוסטיקה                      |
|                               |
| מעליות                        |
|                               |
| קרקע וביסוס                   |
| דיה הנדסת קרקע וביסוס         |
| רישוי                         |

|   |
|---|
| ± 0.00 = +245.00   |
| הערות:<br>1. תכנית זו הי לקרא יחד עם תכנית הרושפים.<br>2. גובה אבסולוטי - ראו תכנית פיתוח.<br>3. הפירות הן בין קירות הבניה ולא כולל פיתח.<br>4. פיתוח השטח סביב הבנוה, כולל, מדרגות, גדרות, שבילים, ריצופים, שטחים גזרים, חניה גג ורא תכנית פיתוח.<br>5. איטום קירות ורצפות הבנוה כמעט עם הקרקע ובידוד תרמי לאורך העמודים והקורות נגד התקררות - כליות או עם סימני גימון- ראו תכנית קונסטרוקציה<br>6. אף דום יבוצע בכל מישור אופקי הכולל חתוכי.<br>7. סיוח תרמי בממד"ד - ע"פ מפרט דוממקור, מאושר ע"י פיקוד העורף.<br><br>המבצע אחראי לסידור : עליו לבקר ולבדוק את כל המידוח בתכנית ובקשות הטוברה.<br>במסגרת של מומחש או אי התאמה בתכנית /או בבנין, עליו להודיע על כך מיד לאדריכל בסופו המשיך בעבודתו.<br>המבצע יחשמש או ויק בתכנית שאושרו לכניסיו.<br>המבצע יחזיק באחר, בכל עת, של מחדש של תכנית.<br>אח לקבוע מידוח על ידי חדיה בשו מוס.<br>התכנית רהנה רכוש האדריכל ואין לשנות כל שימוש בה או ברעיונות הגלומים בה, אלא באישור בכתב מהאדריכל.<br>מומנם /או יושע אשר שמו רשום בתכנית זו, נושא לכיד באחריות המקצועית והתקנית לתכנית.<br>על המפקח והמכיל לודא התאמת התכנית האדריכלית לכניסיו לתכנית ויתר, המכר והתכנית המאושרות ע"י כל הגורמים הרשמיים. התכנית כוללת את כל התאמותיה הדרוש עד ליום תחלתה. |


|                                              |
|----------------------------------------------|
| משרד קירות:                                  |
| <div><div></div><div></div><div></div></div> |
| קיר בלוק קיר בסון עמוד בסון                  |

| תאריך    | תיאור | מהדורה |
|----------|-------|--------|
| 22.09.25 | מכר   | 1      |
|          |       |        |
|          |       |        |
|                                                                  |               |           |            |
|------------------------------------------------------------------|---------------|-----------|------------|
| אדריכלות                                                         |               |           |            |
| המסמך:                                                           | CLIENT NAME:  |           |            |
| קבוצת רכישה נופיה                                                |               |           |            |
| הפרויקט:                                                         | PROJECT NAME: |           |            |
| נופיה - מגרש 22                                                  |               |           |            |
| הגליון:                                                          | DRAWING NAME: |           |            |
| חזיתות 1                                                         |               |           |            |
| מספר גליון:                                                      | SHEET NUMBER: |           |            |
| A3-2-200                                                         |               |           |            |
| מחזוריה:                                                         | EDITION:      | קנה מידה: | SCALE:     |
| 1                                                                | 1             | 1 : 50    | 1 : 50     |
| שורסם ע"י:                                                       | אלמוג אור     | נבדק ע"י: | שרון בוימן |
| תאריך:                                                           | 22.09.25      | DATE:     | 22.09.25   |
| NeumanHaynerArchitects                                           |               |           |            |
| נויון חיינר אדריכלים<br>מורד ההדרים 2, בית חירות<br>09-954642 78 |               |           |            |
| office@nh-arch.com<br>www.nh-arch.com                            |               |           |            |
| זכיות ייצור / ע"פ הנחיות ע"ד                                     |               |           |            |

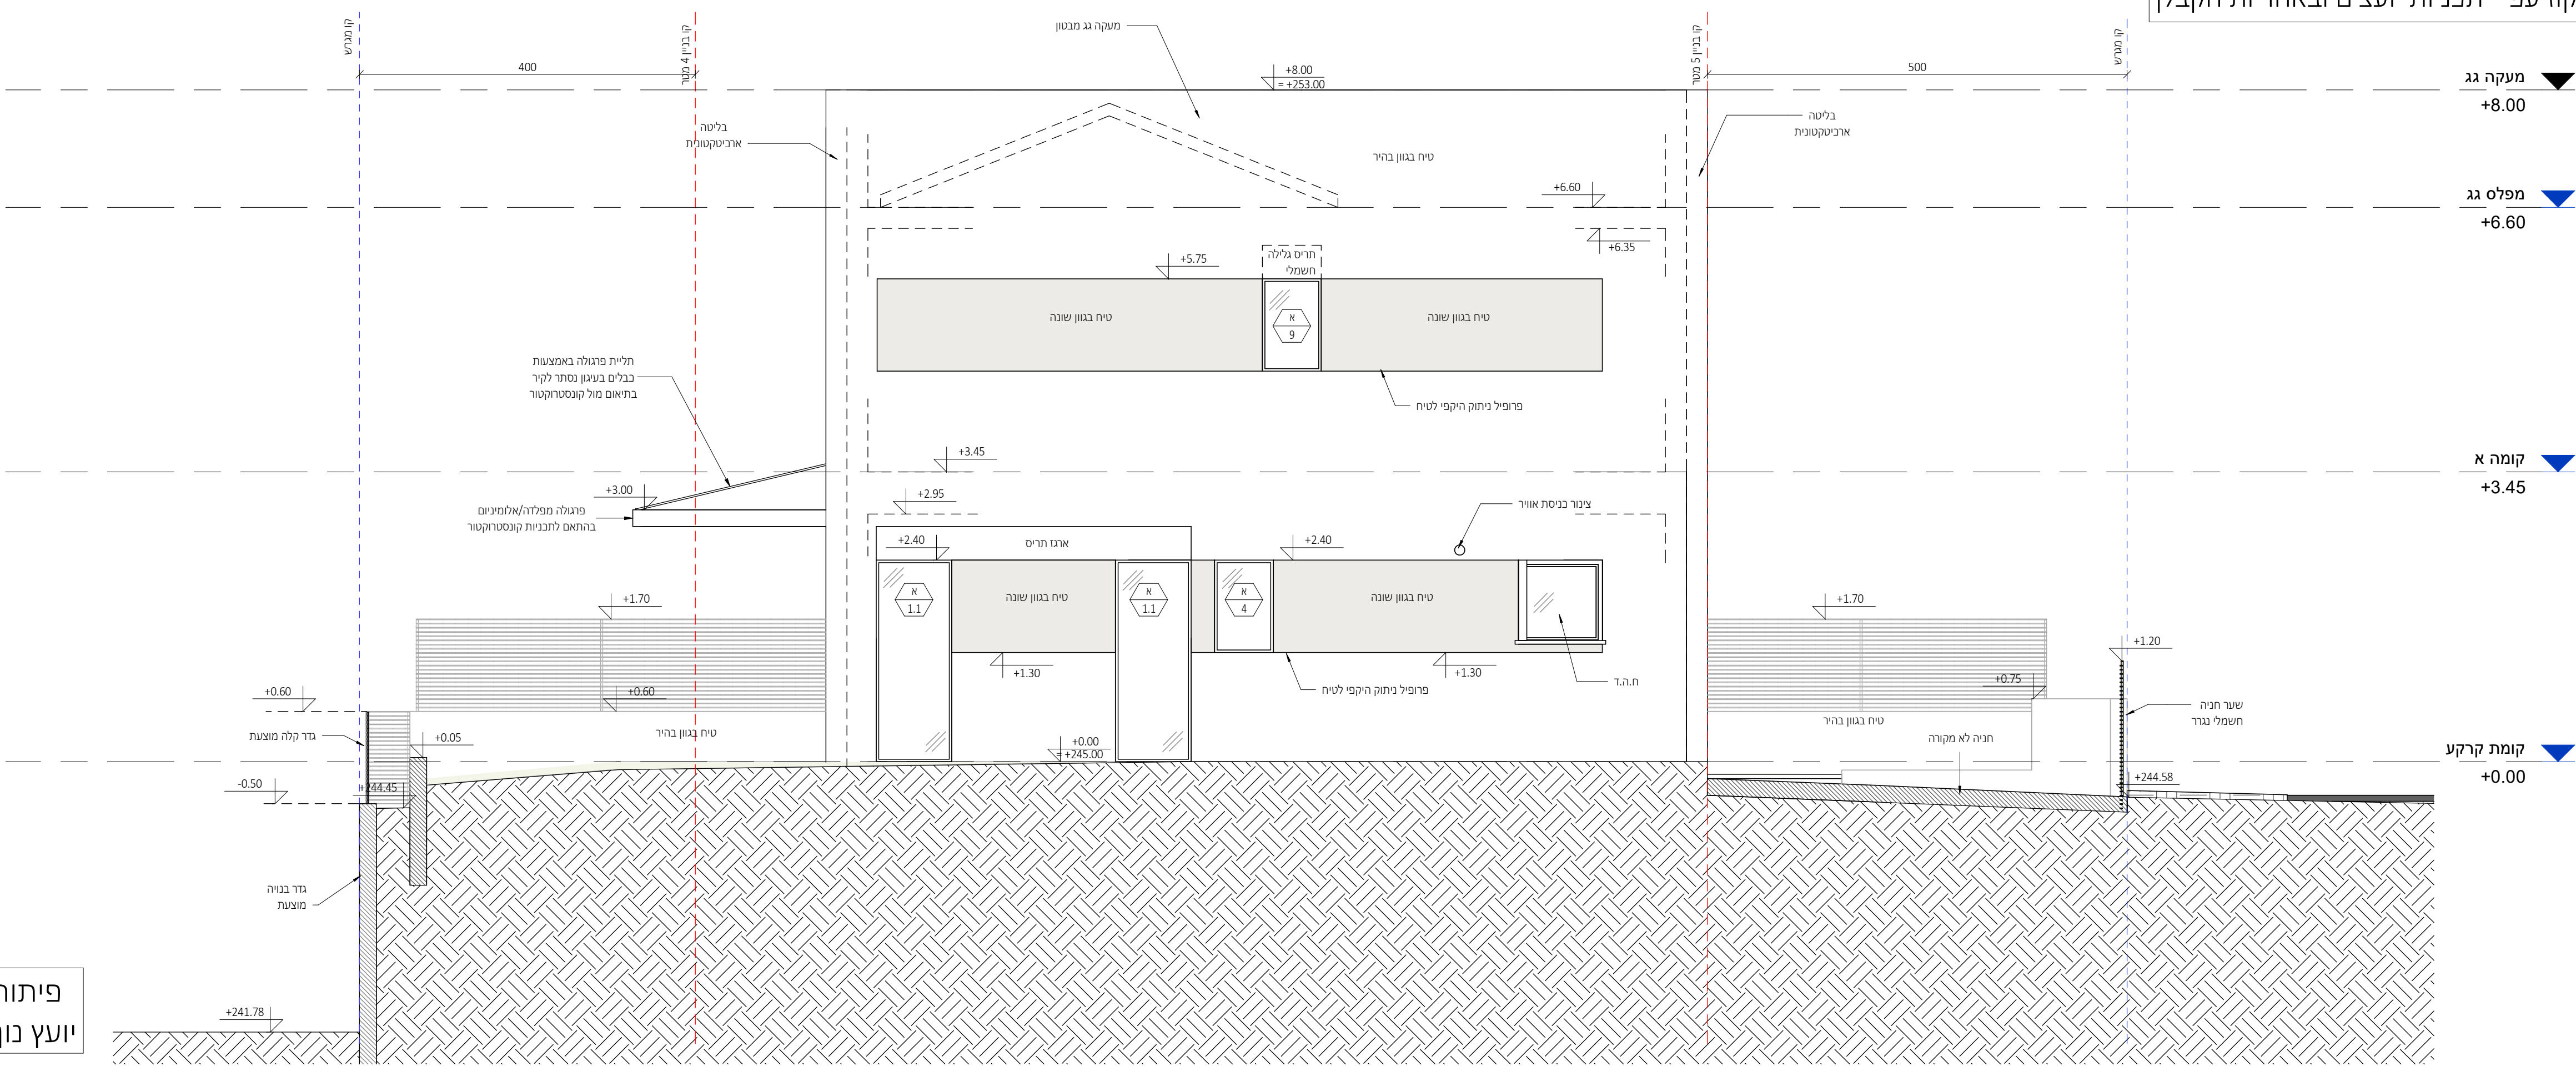

פיתוח נוף עפ"י תוכניות  
יועץ נוף ראה פירוט בנפרד

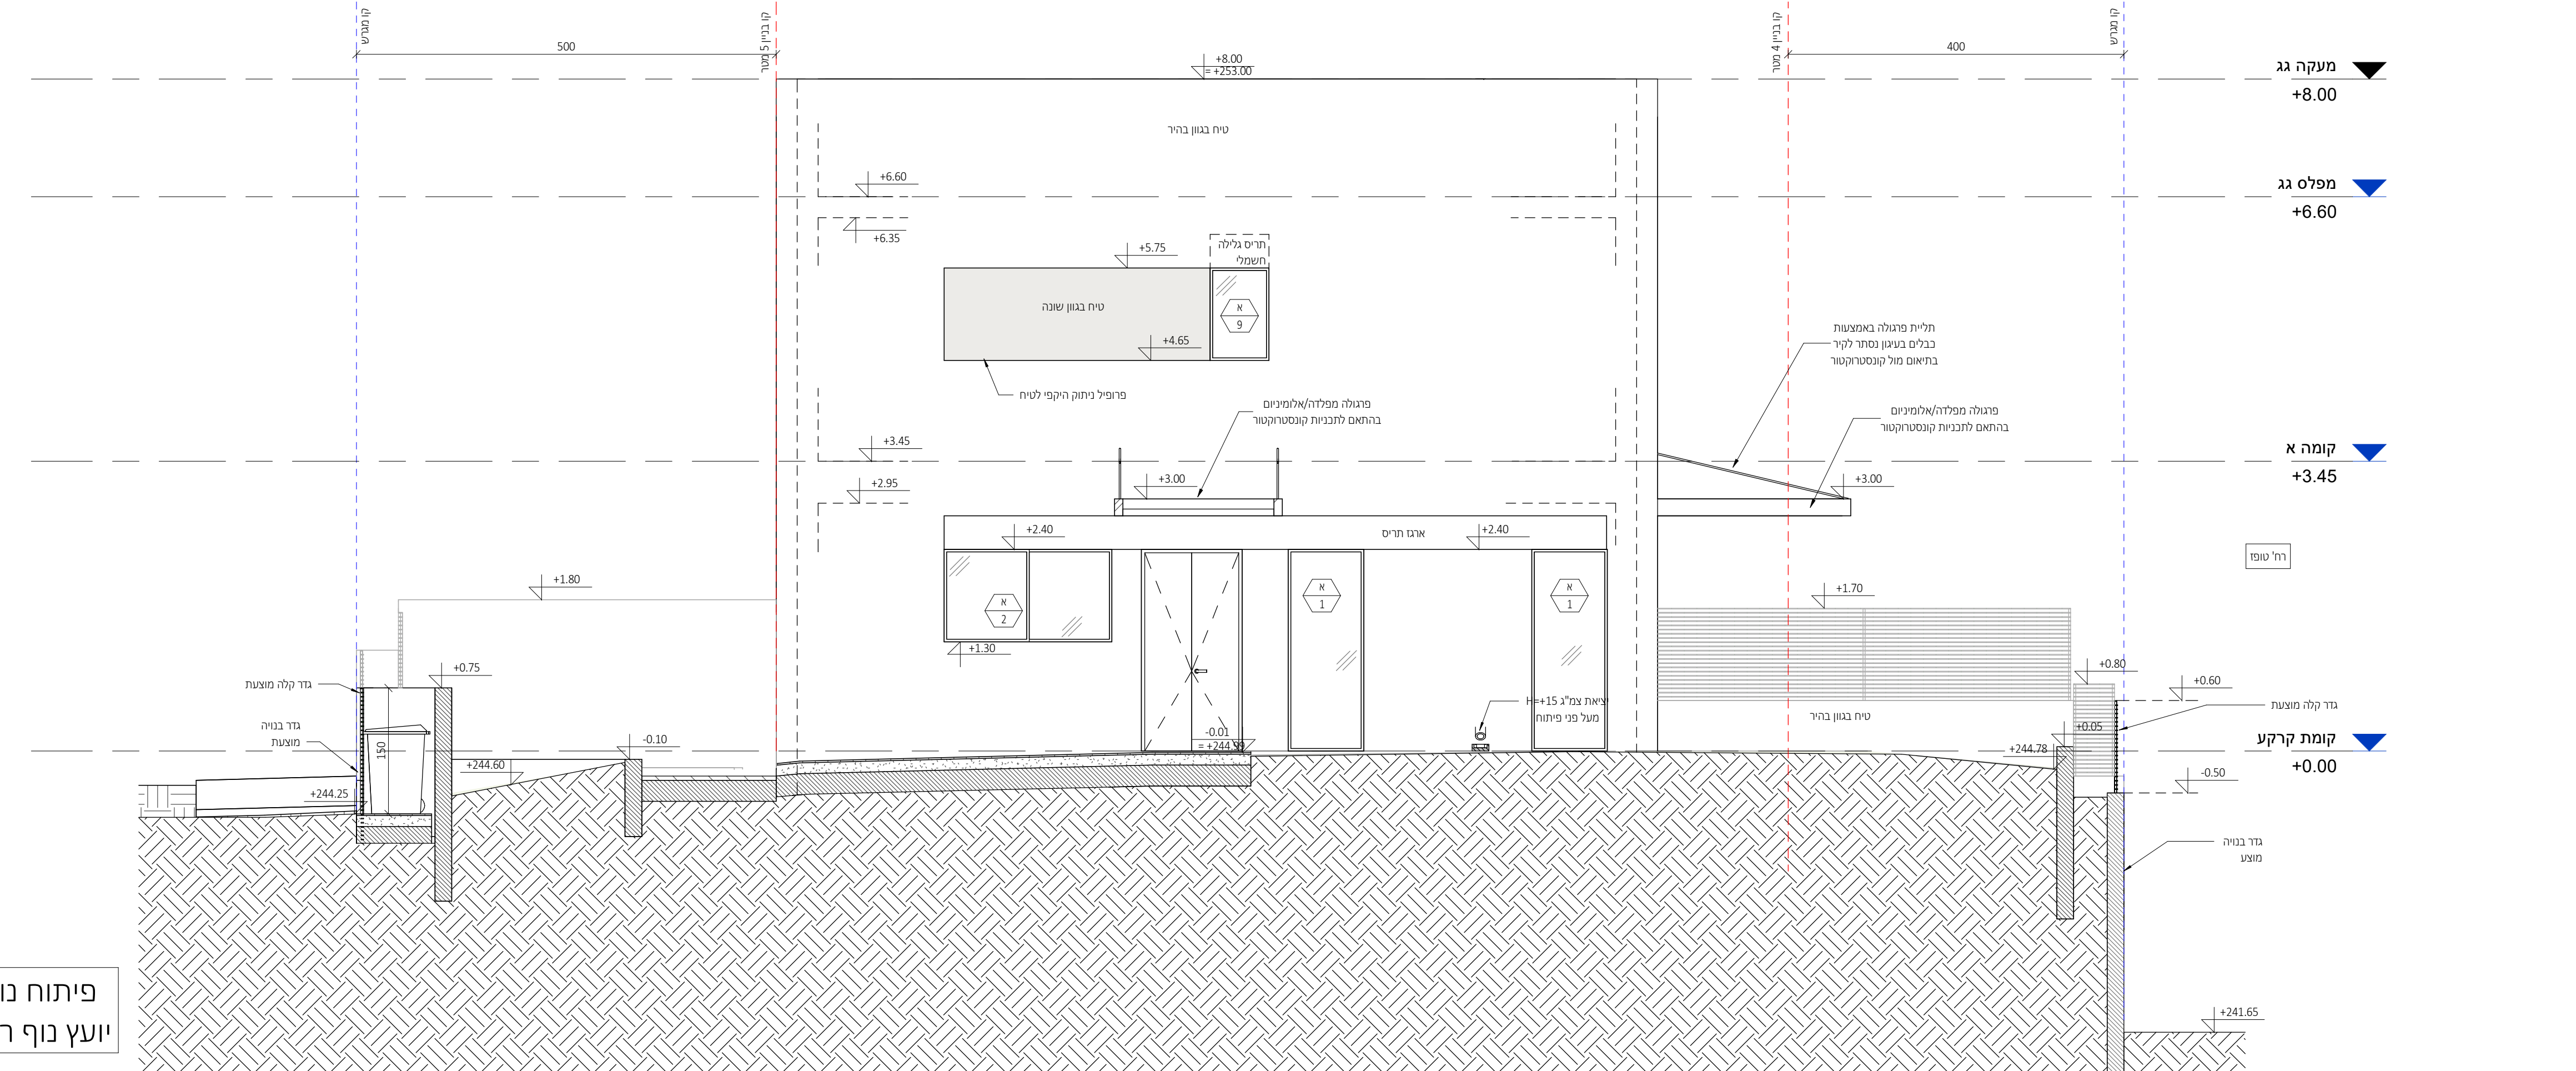


פיתוח נוף עפ"י תוכניות  
יועץ נוף ראה פירוט בנפרד

## חזית צפונית

1 : 50




פרטי איטום, בידוד וניקוז עפ"י תכניות יועצים ובאחריות הקבלן

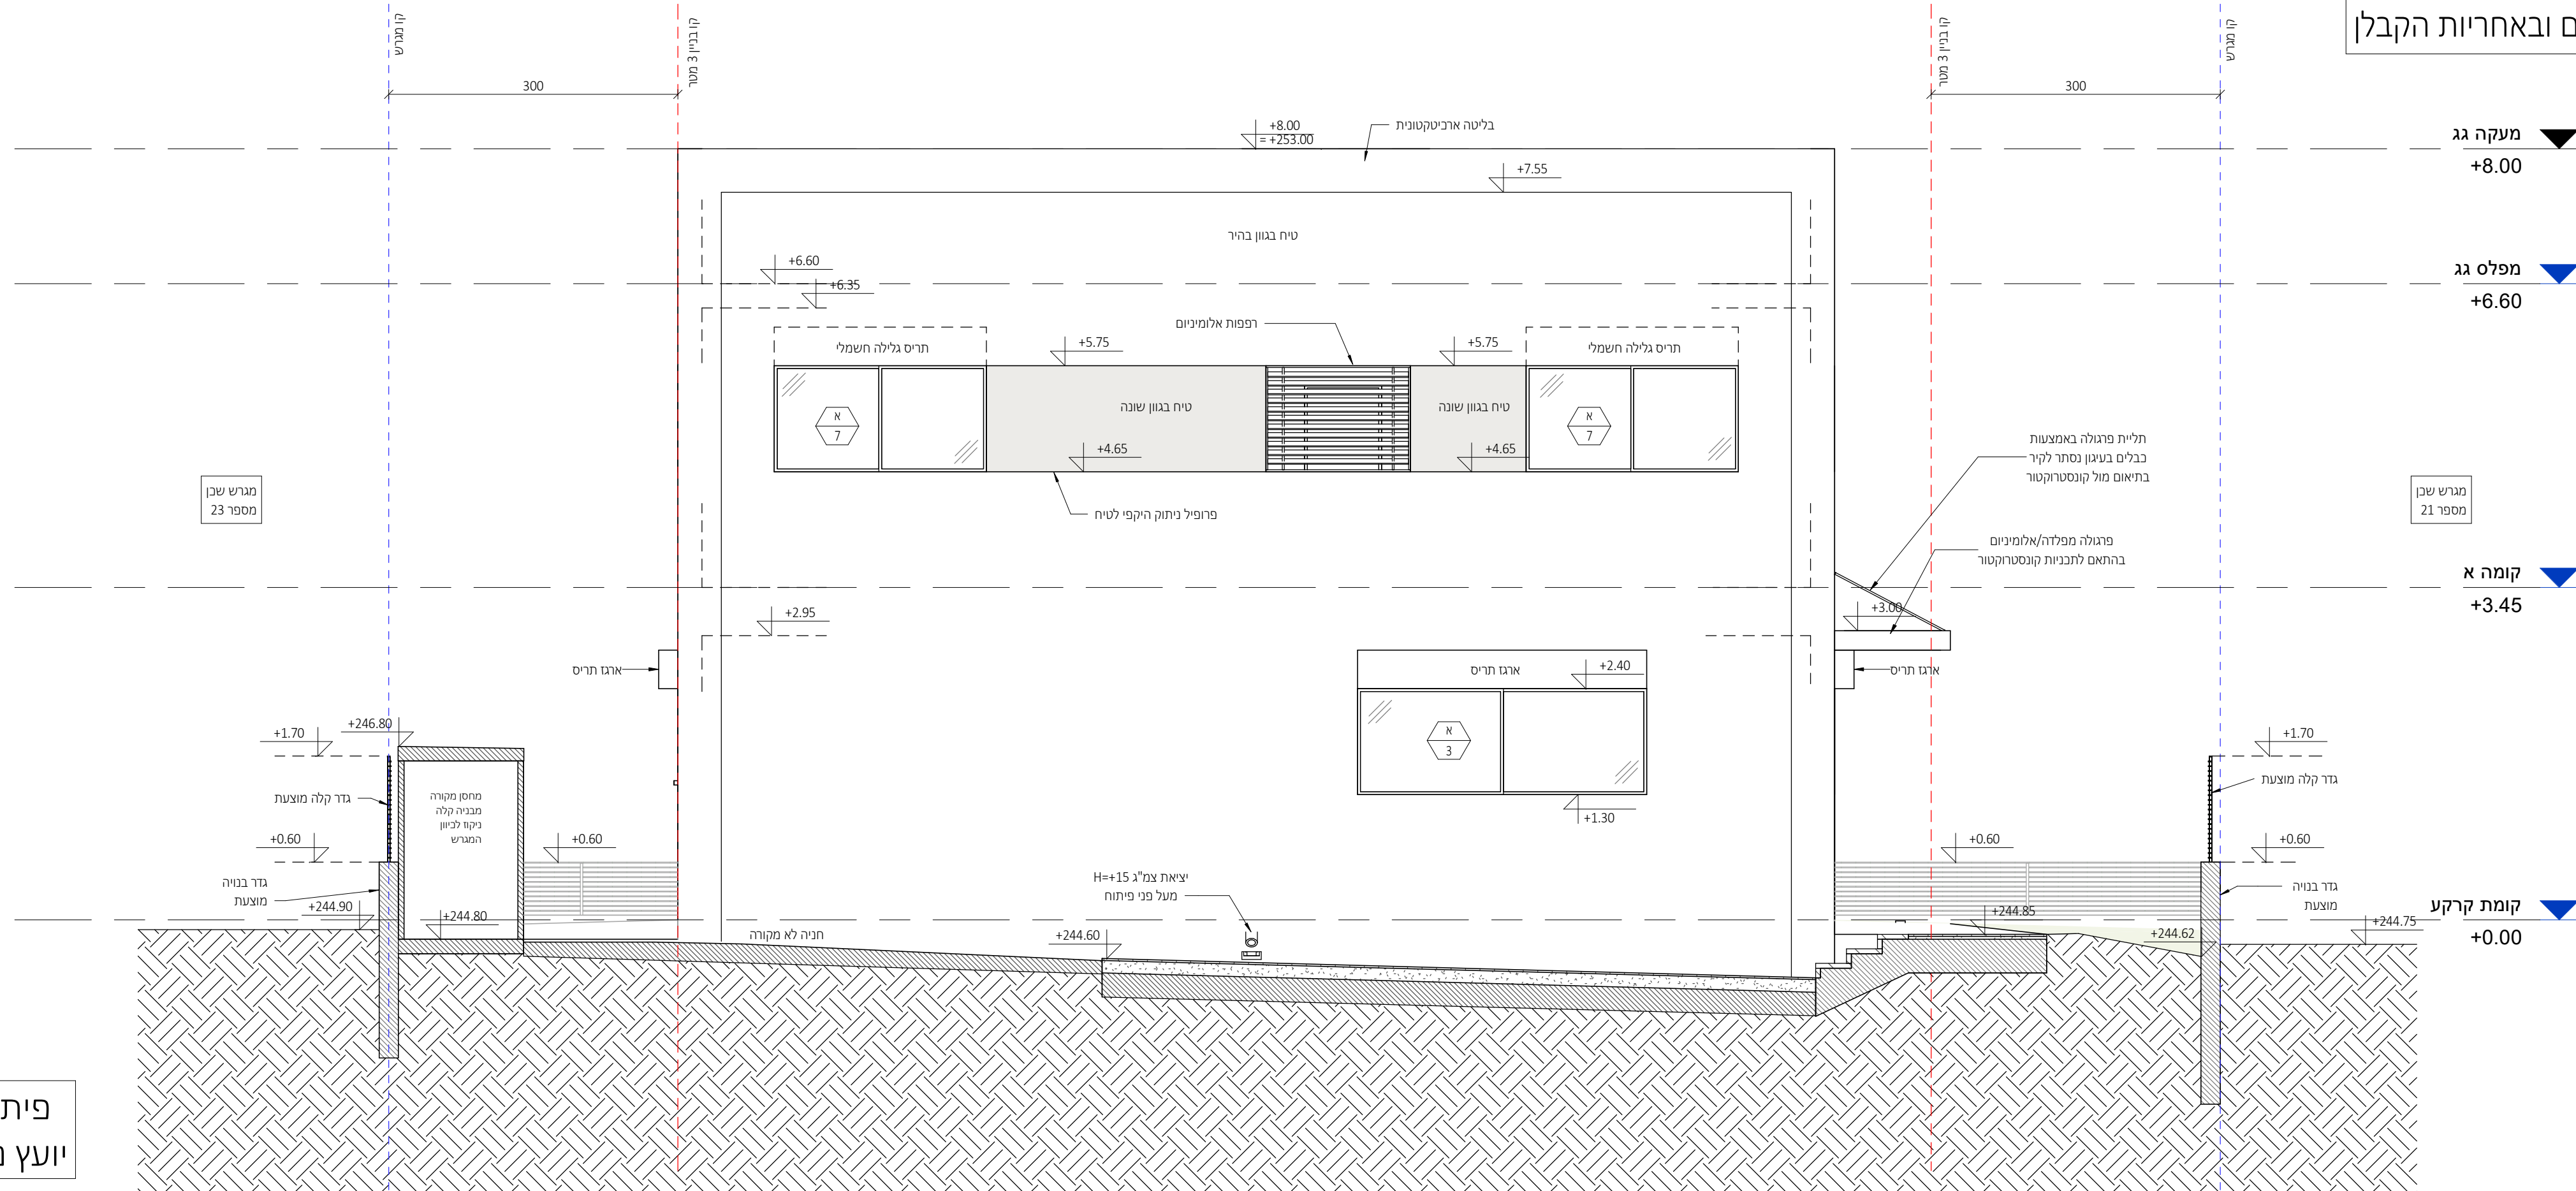

## חזית מזרחית

1 : 50

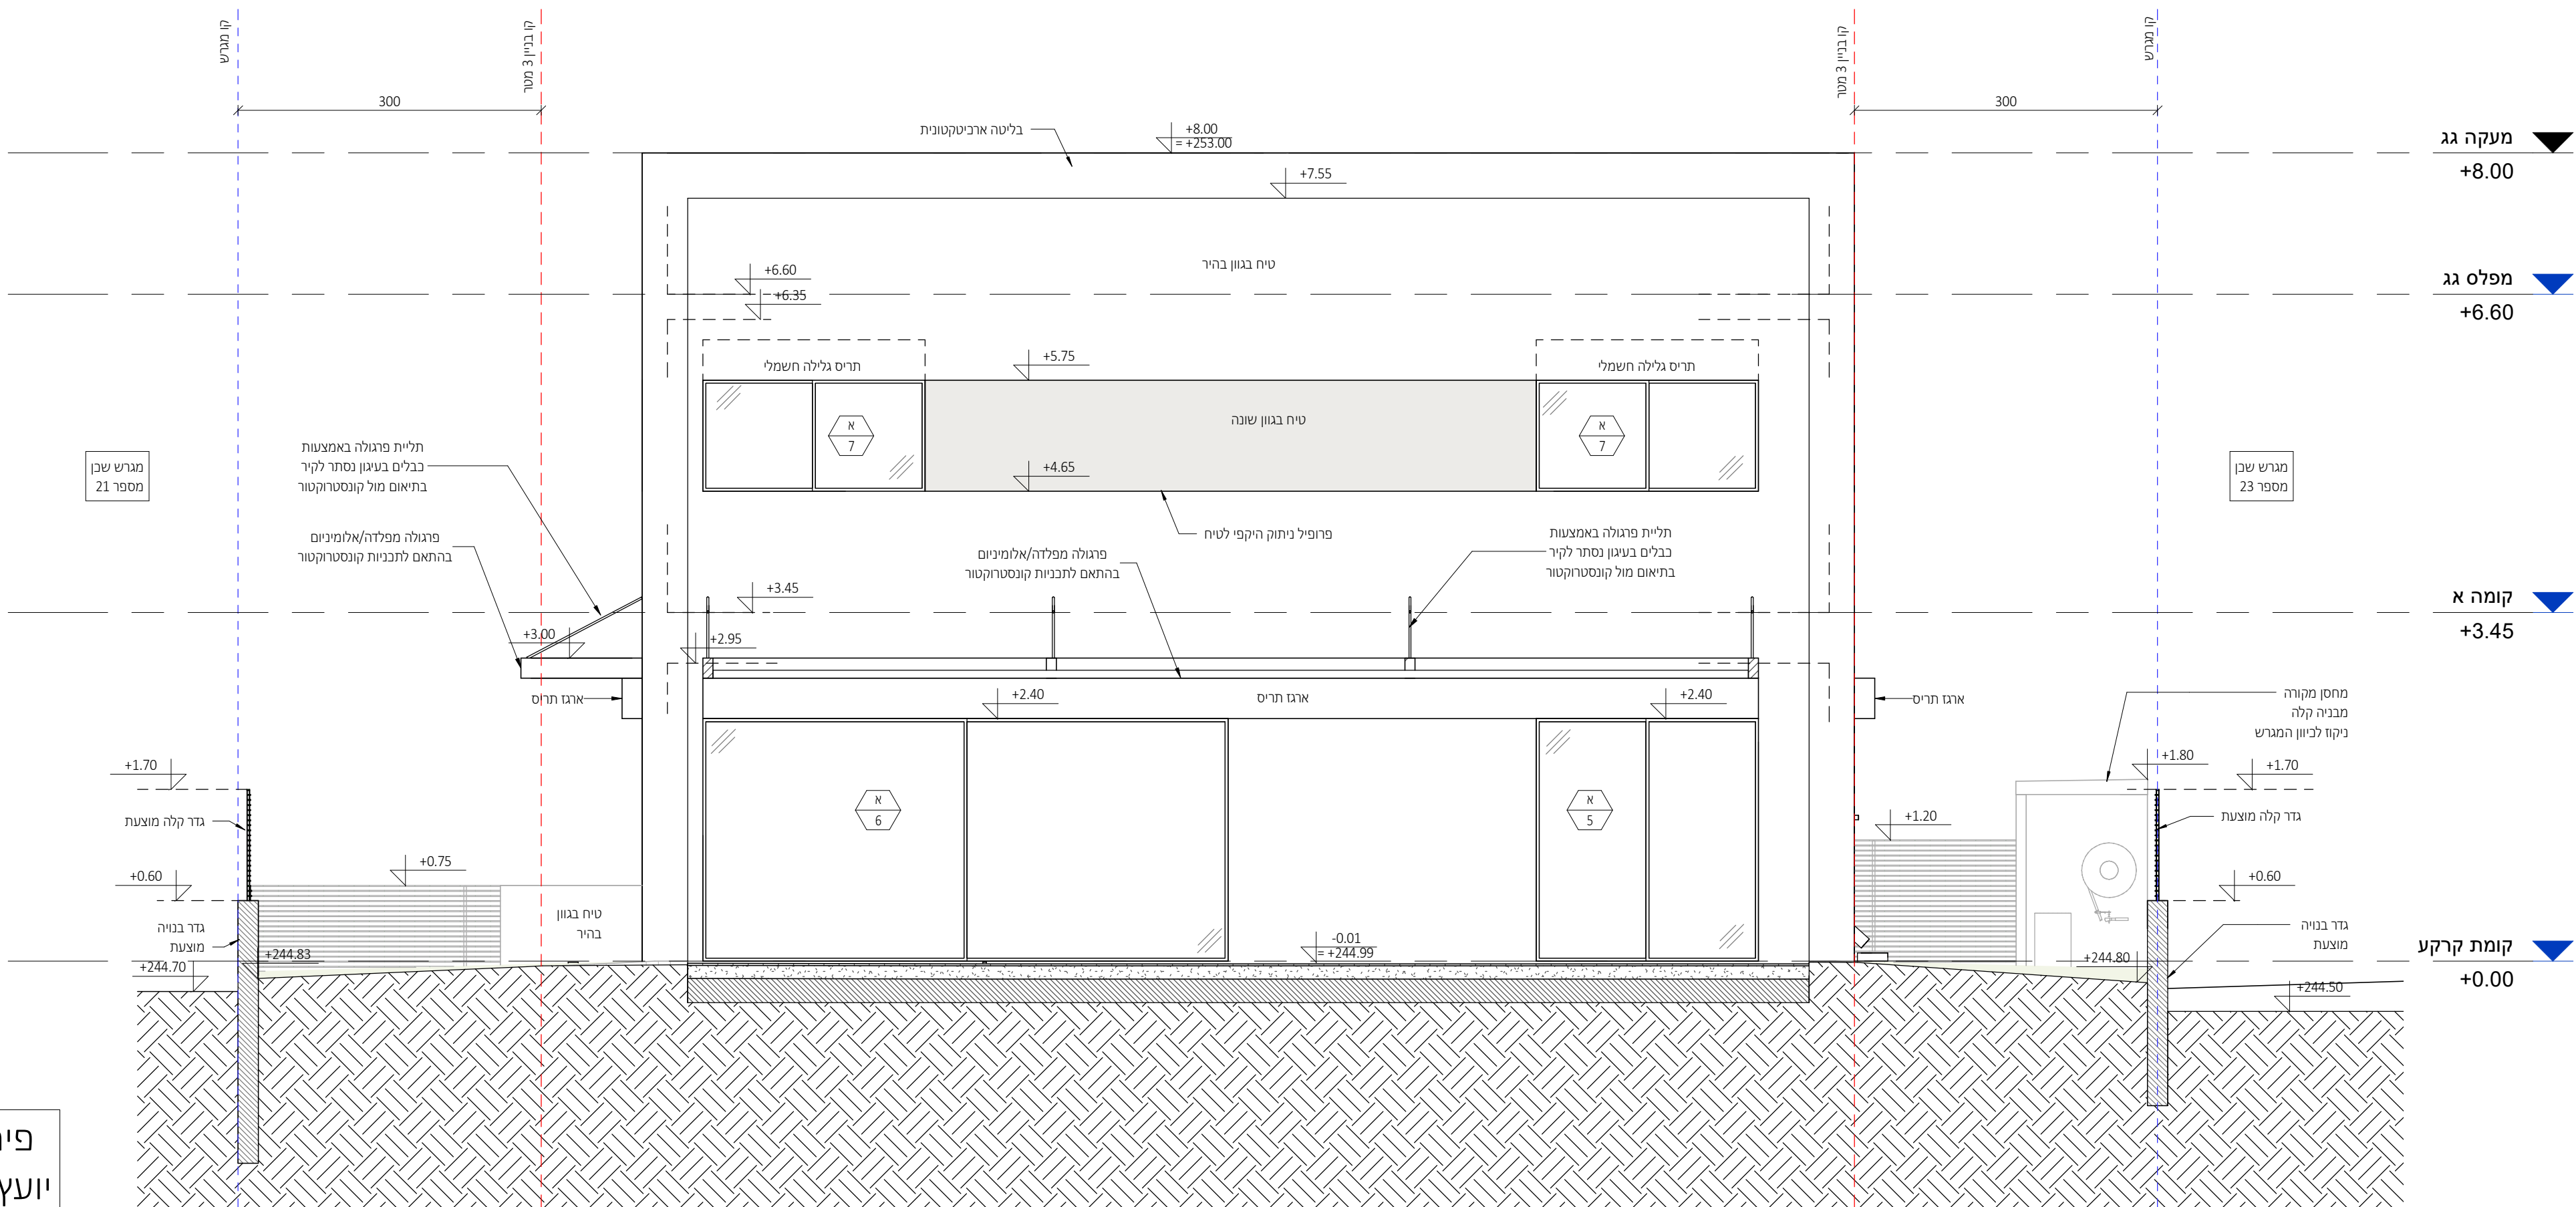

## חזית מערבית


1 : 50

## מתכונים:

|                               |
|-------------------------------|
| ניהול פרויקט                  |
| מהיסוד - בן סולומון           |
| פיקוח                         |
| מהיסוד - בן סולומון           |
| קונסטרוקציה                   |
| ערן שילר                      |
| מיוזג אוויר                   |
| אייל אזר מהנדסים ויועצים בע"מ |
| אינסטלציה                     |
| איתן אלמסי                    |
| חשמל                          |
| איתן בסיס                     |
| אלומיניום                     |
|                               |
| נוף                           |
| נתי בלוקא                     |
| חשמל חכם                      |
|                               |
| חימום תת רצפתי                |
|                               |
| איטום                         |
| צבי טל                        |
| אקוסטיקה                      |
|                               |
| מעליות                        |
|                               |
| קרקע וביסוס                   |
| דיה הנדסת קרקע וביסוס         |
| ירשני                         |

[illegible]

מקרא קירות:

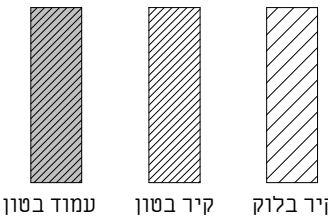[illegible]

## אדריכלות

|                   |             |
|-------------------|-------------|
| CLIENT NAME:      | המסין:      |
| קבוצת רכישה נופיה |             |
| PROJECT NAME:     | הפרויקט:    |
| נופיה - מגרש 22   |             |
| DRAWING NAME:     | שם הנליין:  |
| חזיתות 2          |             |
| SHEET NUMBER:     | פרט הנליין: |
| A3-2-201          |             |

|         |           |                                                                                     |          |
|---------|-----------|-------------------------------------------------------------------------------------|----------|
| SCALE:  | קנה מידה: | EDITION:                                                                            | דורה:    |
| 1 : 50  |           |  |          |
| STATUS: | סטוס      |                                                                                     |          |
| למכר    |           |                                                                                     |          |
|         | (בכד ע"י) | אמלוג אור                                                                           | סטוס ע"י |
| DATE:   | 22.09.25  |                                                                                     | י"ר:     |



NeumanHaynerArchitects

ימון חיינר אדריכלים  
ורד הקדרים 2, בית חירות

www.nh-arch.com 09-9545842 7

פיתוח נוף עפ"י תוכניות  
יועץ נוף ראה פירוט בנפרד

פיתוח נוף עפ"י תוכניות  
יועץ נוף ראה פירוט בנפרד




מתכננים:

|                               |
|-------------------------------|
| ניהול פרויקט                  |
| מהיסוד - בן סולמון            |
| פיקוח                         |
| מהיסוד - בן סולמון            |
| קונסטרוקציה                   |
| ערן שילר                      |
| מיזוג אוויר                   |
| אייל ארז מהנדסים ויועצים בע"מ |
| אינסטלציה                     |
| איתן אלמסי                    |
| חשמל                          |
| איתן בסיס                     |
| אלומיניום                     |
| נוף                           |
| נתי בלוקא                     |
| חשמל חכם                      |
| חימום תת רצפתי                |
|                               |
| איטום                         |
| צבי טל                        |
| אקוסטיקה                      |
| מעליות                        |
| קרקע וביסוס                   |
| ד"ה הנדסת קרקע וביסוס         |
| רישוי                         |

|   |
|---|
| <div>± 0.00 = +245.00</div>   |
| הערות:<br>1. תכנית זו יש לקרוא יחד עם תכנית הריטשים.<br>2. גובה אבטמנטים: ראה תכנית סיווח.<br>3. הפירות הן בין קירות הבניה ולא כולל פיתח.<br>4. פיתוח השטח סביב הבנוה, כולל, מדרגות, גדרות, שבילים, ריצופים, שטחים גזרים, חניה וכו' ראה תכנית פיתוח.<br>5. איטום קירות ורצפות הבנוה כמנוע עם הקרקע ובידוד תרמי לאורך העמודים והקורות ופני היתדות. כליות או עם סימני גימון. ראה תכנית קונסטרוקציה.<br>6. אף חים יבוצע בכל מישור אופקי הכולל חתוכים.<br>7. פיתח תרמי במסד- ע"פ מפרט תרמוקיר, מאושר ע"י פיקוד העורף.<br><br>המבצע אחראי לסיווח: עליו לבקר ולבדוק את כל המידוח בתכנית ובקשות הבנוה.<br>במסדו של שטח או אי התאמה בתכנית /או בבנוי, עליו להודיע על כך מיד לאדריכל בסופו המשיך בעבודתו.<br>המבצע יוועטש או ויק בתכנית שאושרו לכניסו.<br>המבצע יחזיק אחרא, לכל מה, של מחדש של תכנית.<br>אין לקבוע מידוח על ידי חזירה בשו שום.<br>התכנית הנה רכוש האדריכל ואין לשנות כל שימוש בה או ברעיונות הגלומים בה, אלא באישור בכתב מהאדריכל.<br>מהנדס /או יועץ אשר שמו רשום בתכנית זו, נושא לכיד באחריות המקצועית והתקנית לתכנית.<br>על המפקח והקבלן לוודא התאמת התכנית האדריכלית "כניסו" לתכנית יחיד, הפוך והתכנית הואשמות ע"י כל גורמים הרשמיים.<br>התכנית כוללת את כל האמצעים והידוע עד ליום תחלתה. |

משרד קירות:

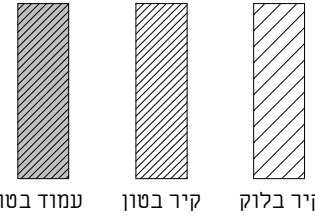

| תאריך    | תיאור | מהדורה |
|----------|-------|--------|
| 22.09.25 | מכרז  | 1      |
|          |       |        |
|          |       |        |
אדריכלות



|                   |               |
|-------------------|---------------|
| שם המוסד:         | CLIENT NAME:  |
| קבוצת רכישה נופיה |               |
| שם הפרויקט:       | PROJECT NAME: |
| נופיה - מגרש 22   |               |
| שם הגיליון:       | DRAWING NAME: |
| חתכים             |               |
| מספר גיליון:      | SHEET NUMBER: |
| A3-3-100          |               |
| חזרה:             | EDITION:      |
| קנה מידה:         | SCALE:        |
| 1 : 50            |               |
| סטוס:             | STATUS:       |
| למכרז             |               |
| שורסס ע"י:        | ע"י:          |
| אלמוג אור         | שרון בימן     |
| תאריך:            | DATE:         |
| 22.09.25          |               |



נרסן חיינר אדריכלים  
מודד והנדס 2, בית חירות  
09-9546842 78  
office@nh-arch.com  
www.nh-arch.com

זכיות ייצור / ע"פ הנחיות ע"ד

פיתוח נוף עפ"י תוכניות יועץ נוף ראה פירוט בנפרד

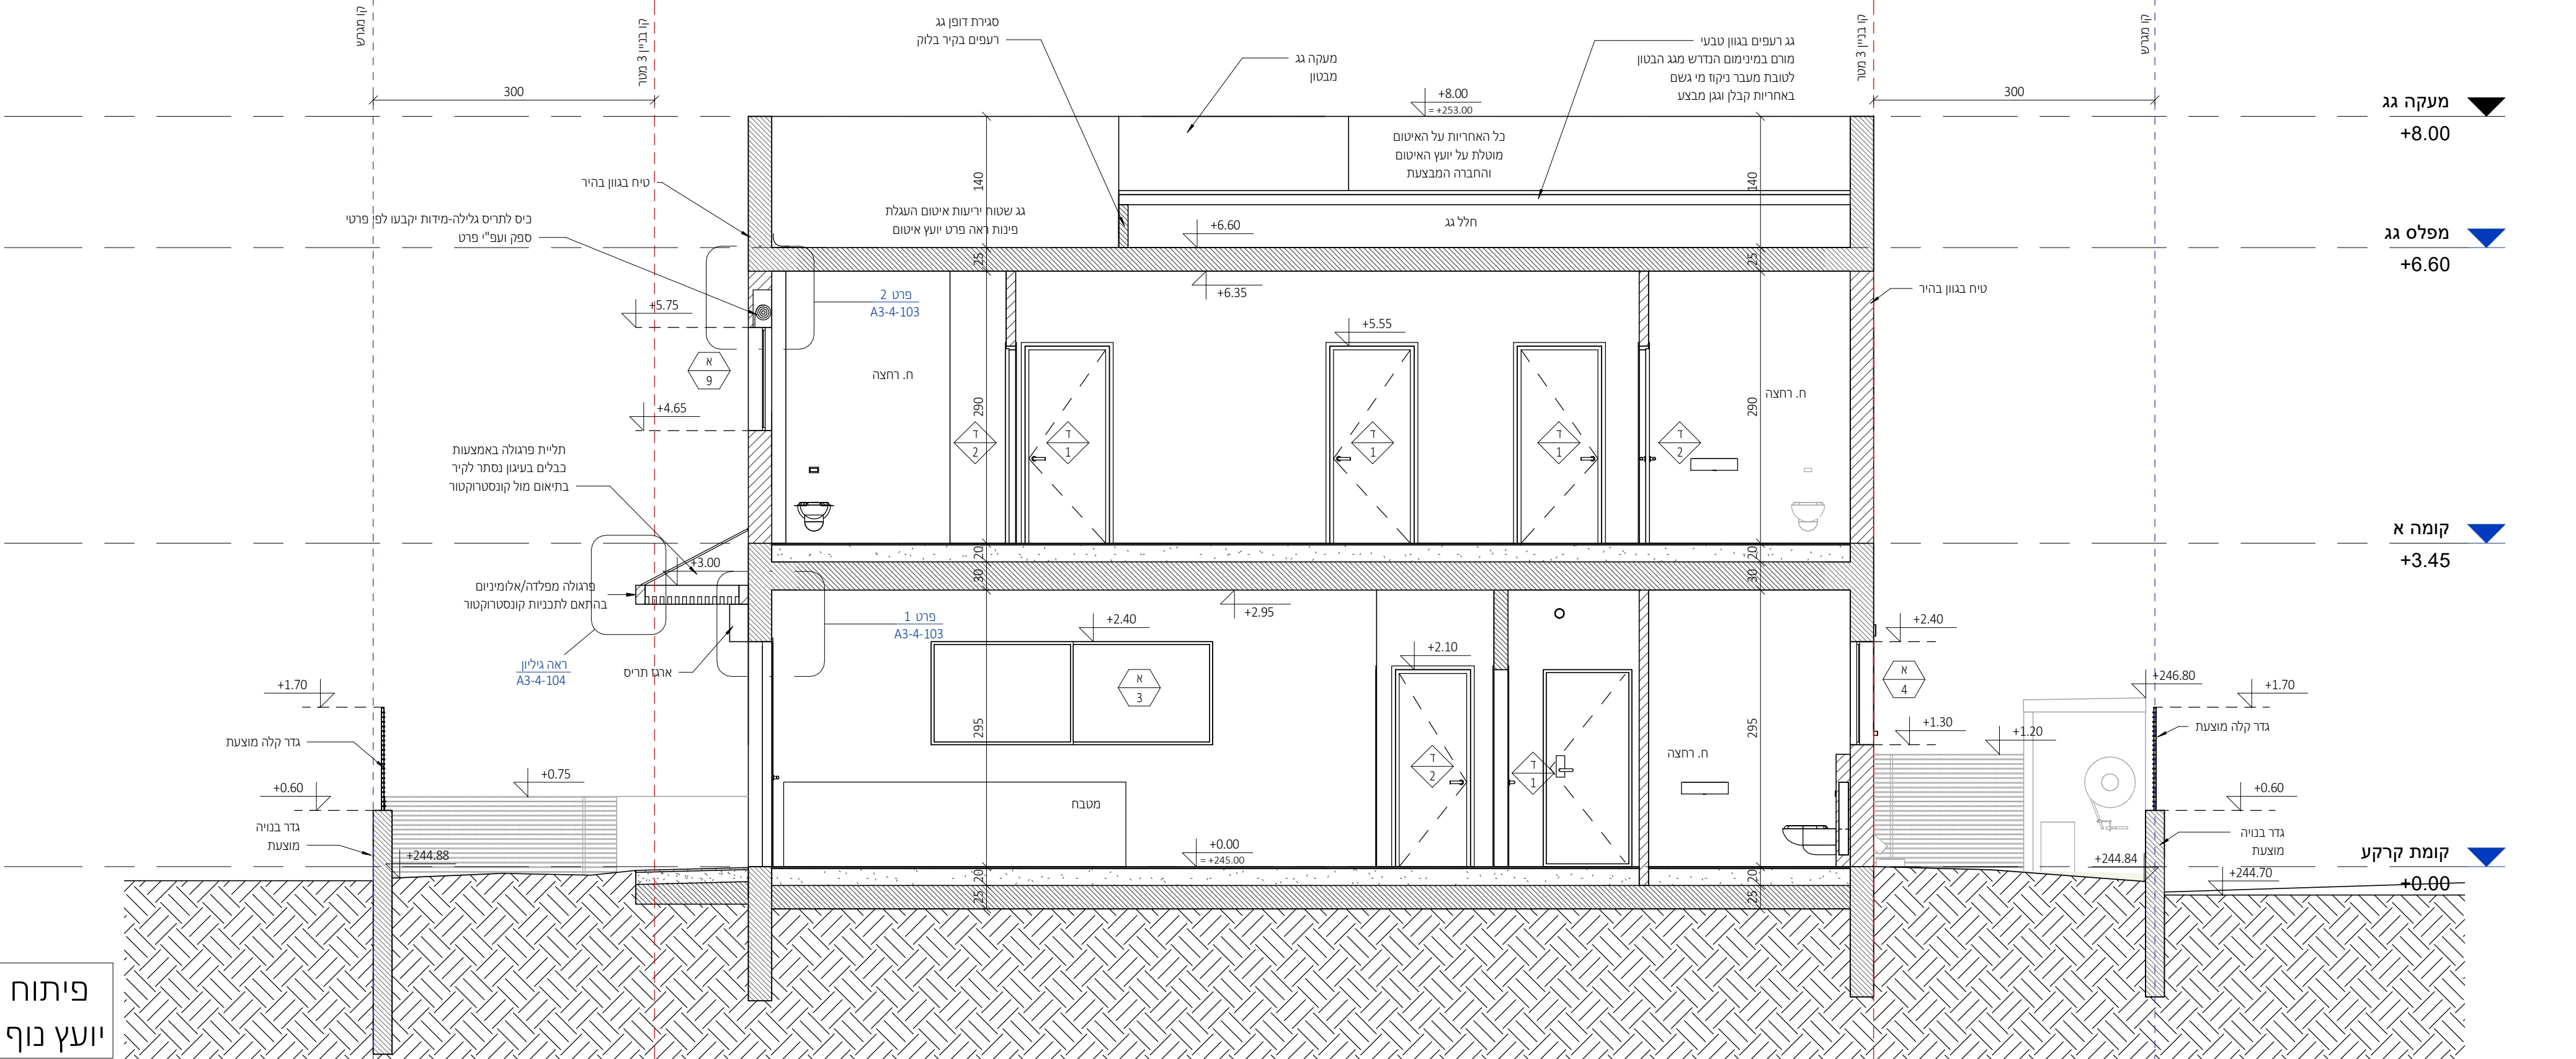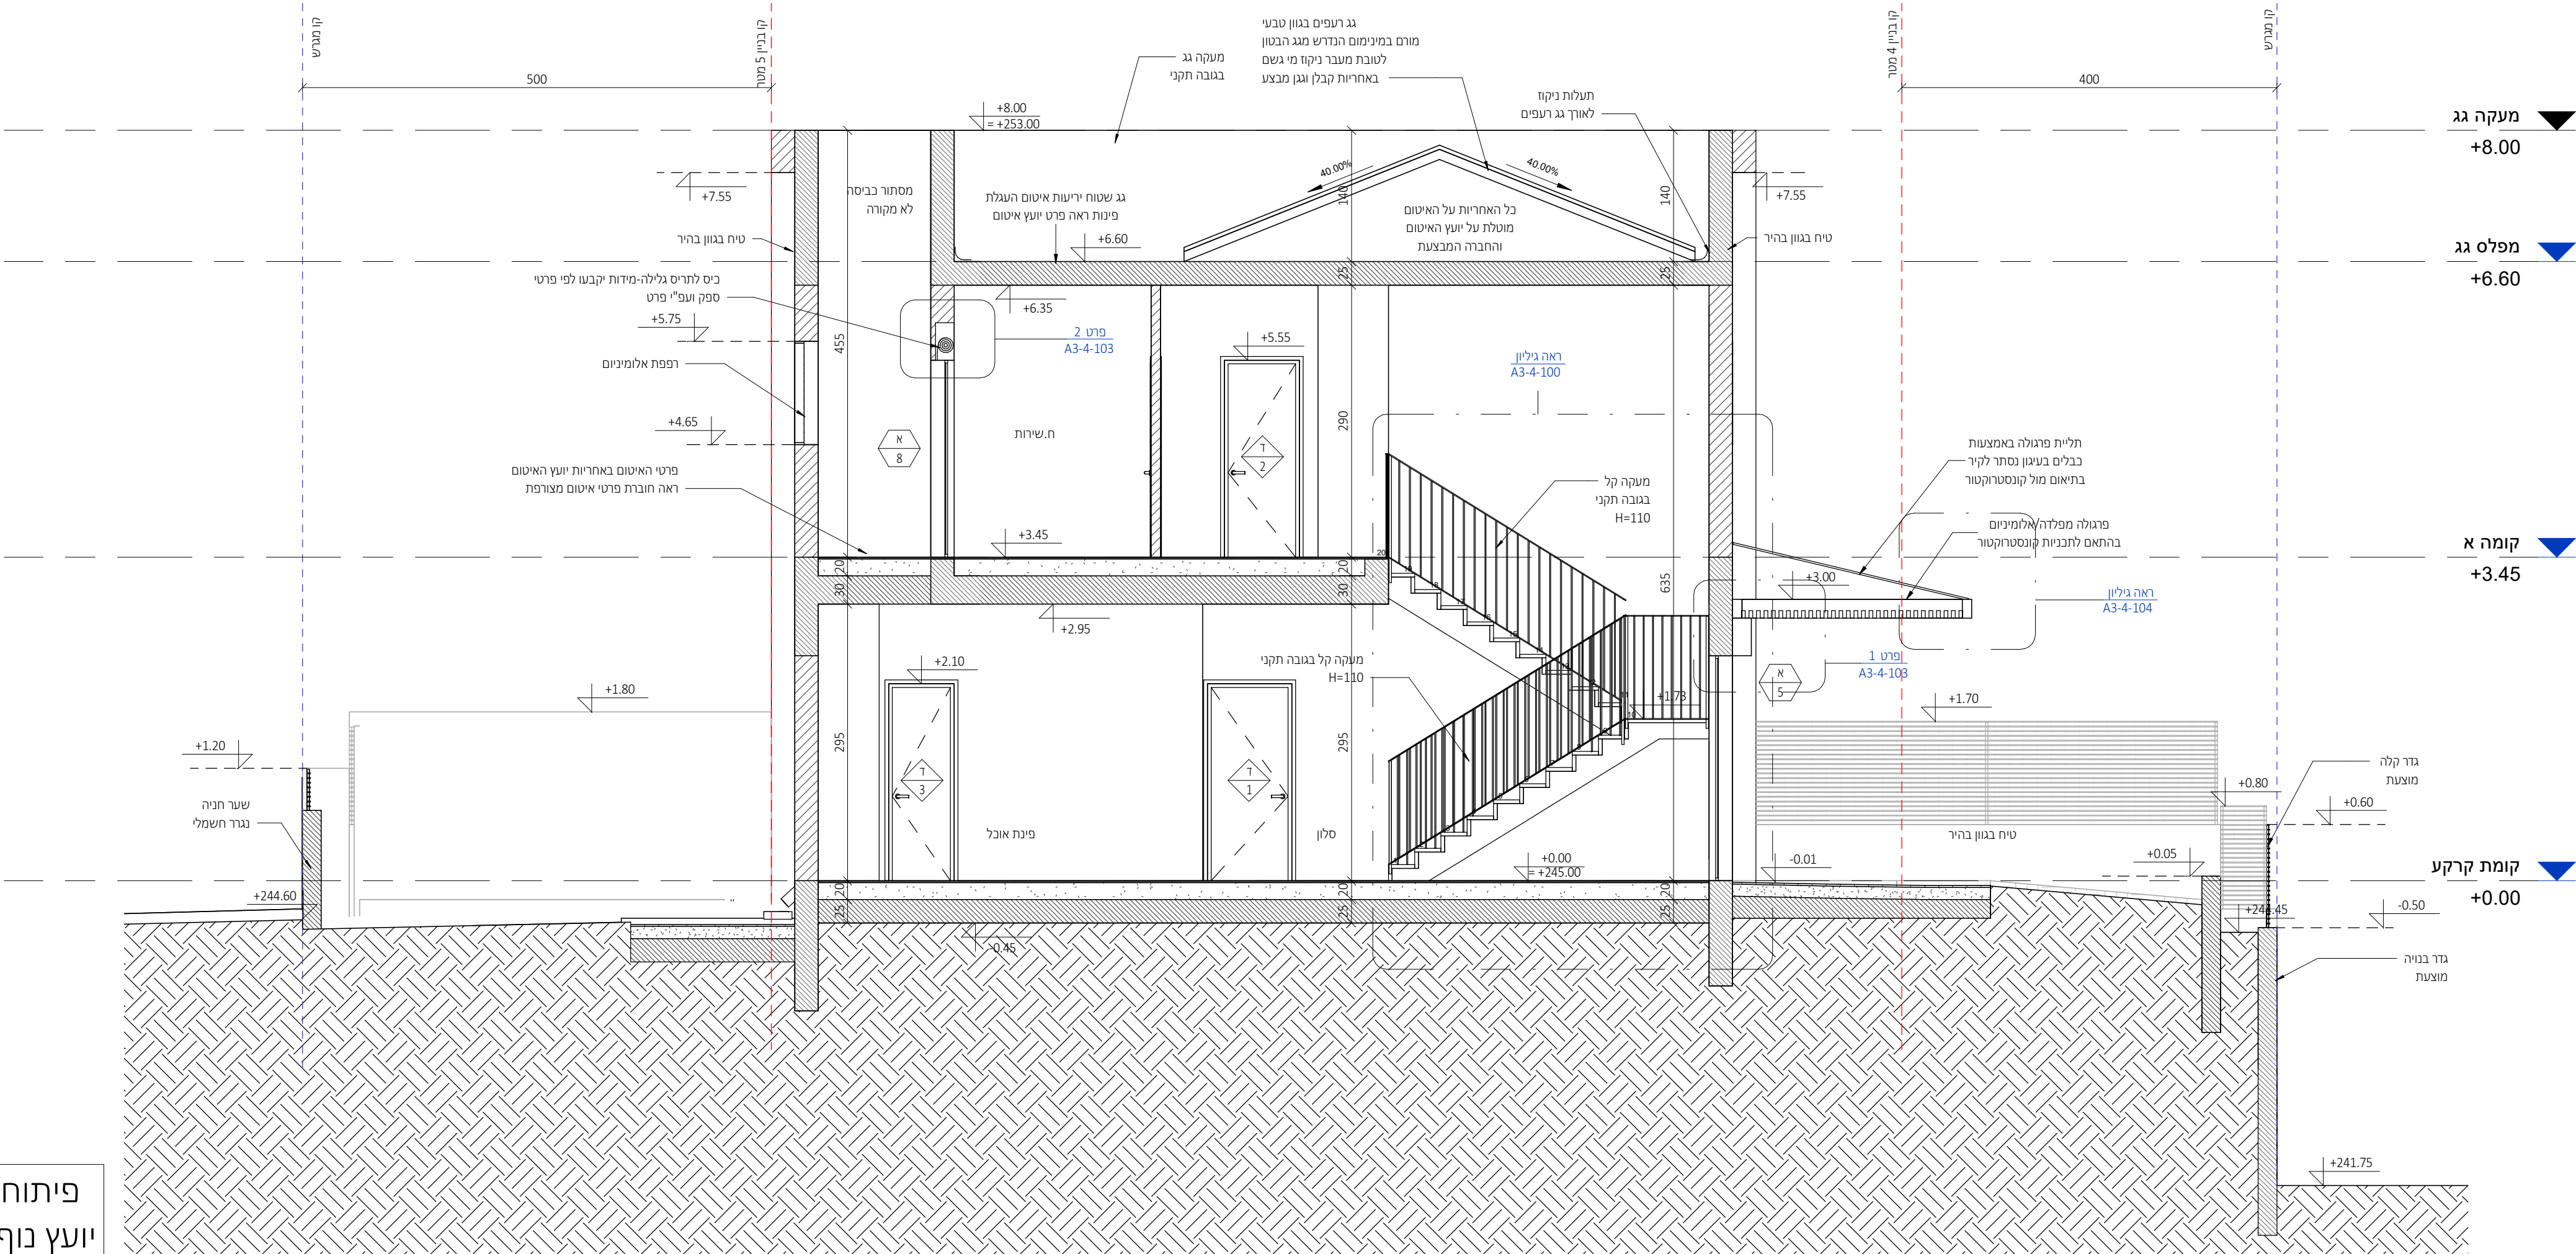

פיתוח נוף עפ"י תוכניות יועץ נוף ראה פירוט בנפרד

חתך ב-ב

1 : 50



|                               |
|-------------------------------|
| ניהול פרויקט                  |
| מהיסוד - בן סולומון           |
| פיקוח                         |
| מהיסוד - בן סולומון           |
| קונסטרוקציה                   |
| ערן שילר                      |
| מיזוג אוויר                   |
| אייל ארז מהנדסים ויועצים בע"מ |
| אינסטלציה                     |
| איתן אלמסי                    |
| חשמל                          |
| איתן בסיס                     |
| אלומיניום                     |
| נוף                           |
| נתי בלוקא                     |
| חשמל חכם                      |
| חימום תת רצפתי                |
| איטום                         |
| צבי טל                        |
| אקוסטיקה                      |
| מעליות                        |
| קרקע וביסוס                   |
| דיה הנדסת קרקע וביסוס         |
| רישוי                         |




[illegible][illegible]

|                                                                                                 |                                                         |
|-------------------------------------------------------------------------------------------------|---------------------------------------------------------|
| <div> <div>אדריכלות</div> <div> <div>שם המסמך:</div> <div>קבוצת רכישה נופיה</div> </div> </div> |                                                         |
| <div> <div>PROJECT NAME:</div> <div>הפרויקט:</div> </div>                                       |                                                         |
| <div> <div>נופיה - מגרש 22</div> </div>                                                         |                                                         |
| <div> <div>DRAWING NAME:</div> <div>שם הגליון:</div> </div>                                     |                                                         |
| <div> <div>גליון מדרגות</div> </div>                                                            |                                                         |
| <div> <div>SHEET NUMBER:</div> <div>מספר גליון:</div> </div>                                    |                                                         |
| <div> <div>A3-4-100</div> </div>                                                                |                                                         |
| <div> <div>CALC:</div> <div>קנה מידה:</div> </div>                                              | <div> <div>EDITION:</div> <div>דור:</div> </div>        |
| <div> <div>As indicated</div> </div>                                                            | <div> <div> <div>1</div> </div> </div>                  |
| <div> <div>TATUS:</div> <div>סטוס</div> </div>                                                  | <div> <div>סטוס ע"י:</div> <div>אלמוג אור</div> </div>  |
| <div> <div>למכר</div> </div>                                                                    | <div> <div>בדוק ע"י:</div> <div>שרון חיימן</div> </div> |
| <div> <div>DATE:</div> <div>תאריך:</div> </div>                                                 | <div> <div>22.09.25</div> </div>                        |

NeumanHaynerArchitects

יומן חיינר אדריכלים  
חורר ההדריס 2, בית חורר  
09-9545842

office@nh-arch.com  
www.nh-arch.com

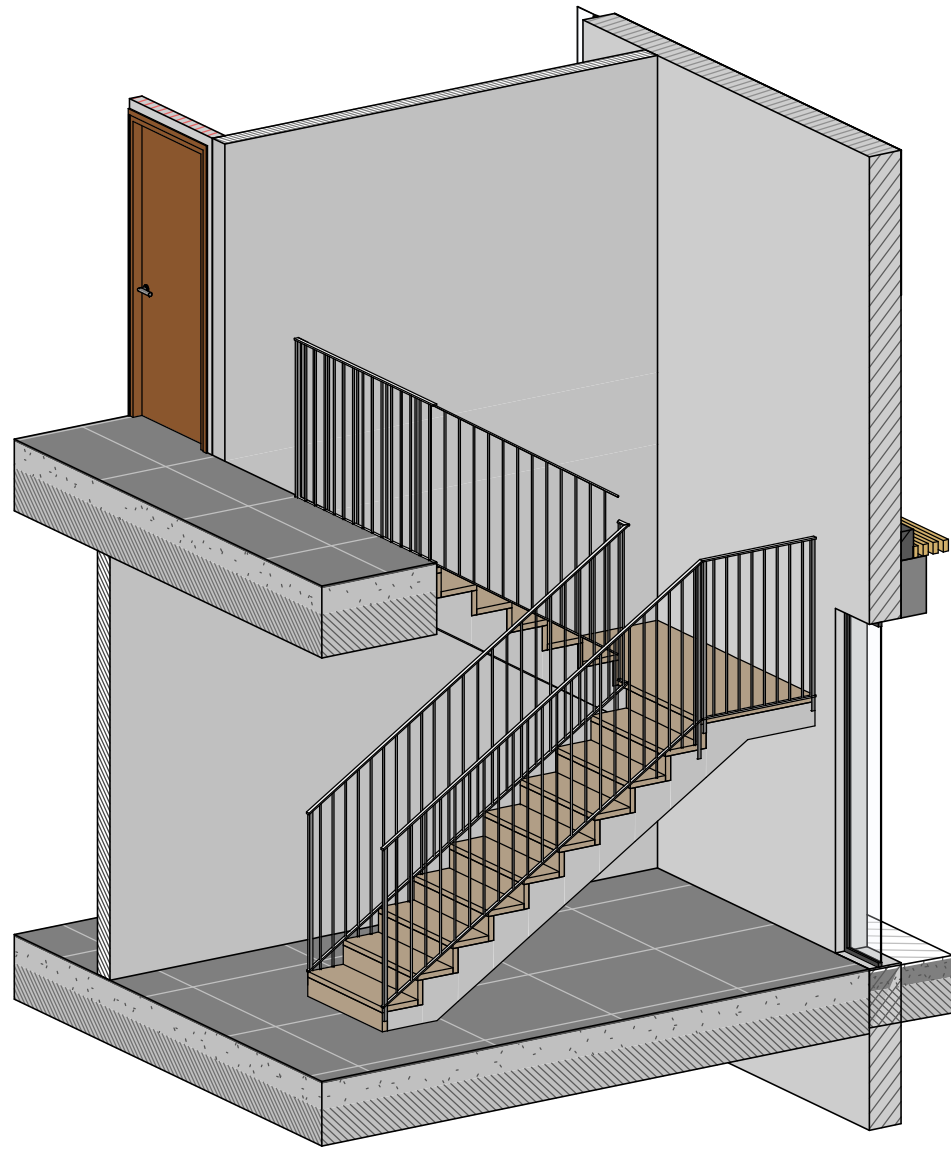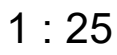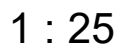


## דגם נבחר


## מדרגות סטנדרטיות - מפרט סטנדרטי

על הקבלן לשלוח S.D לאישור אדריכל

יש לבצע התאמה לפרט לאחר בחירת חיפוי המדרגות\*

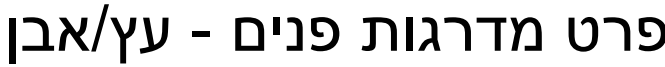

1 : 10

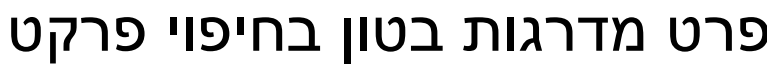


1 : 10



## תמונה להמחשה בלבד




1 : 10

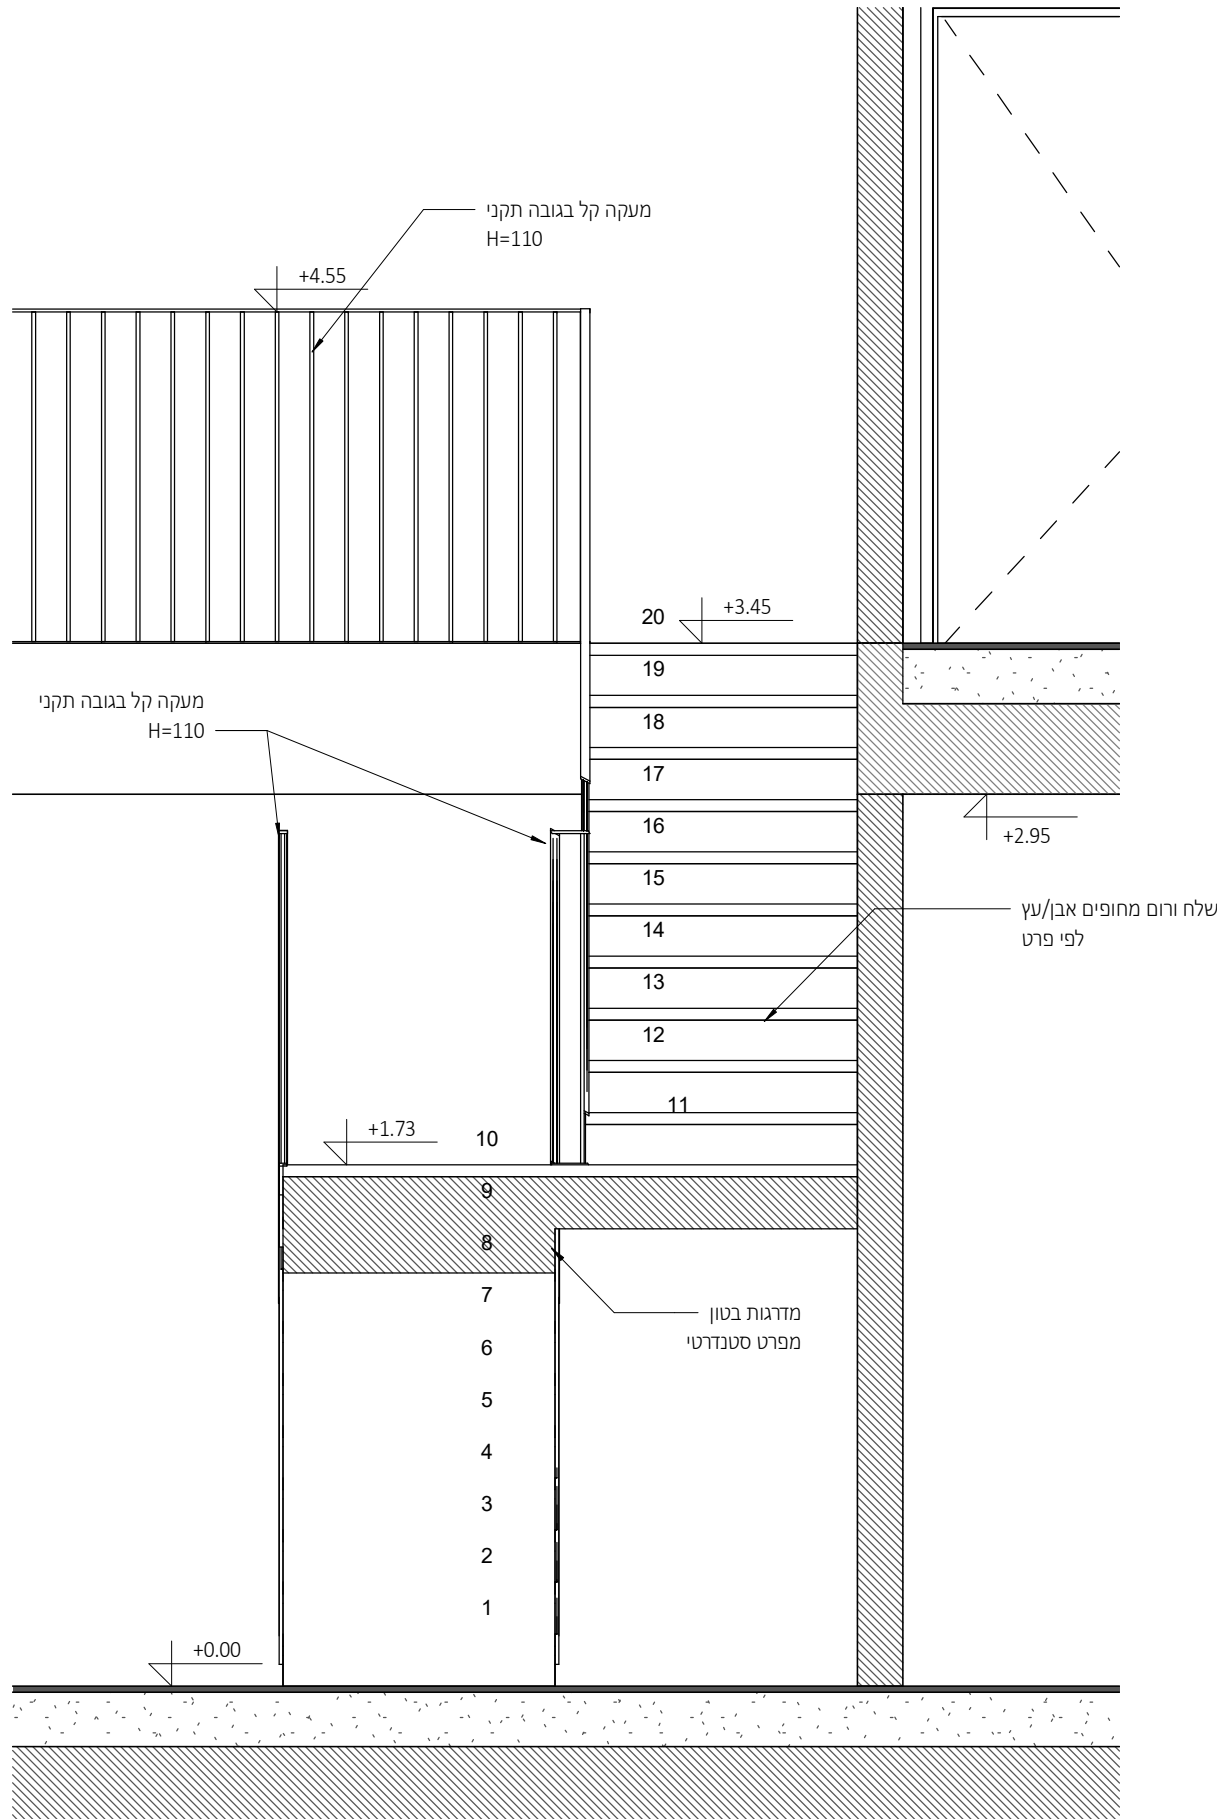

24

1 : 25

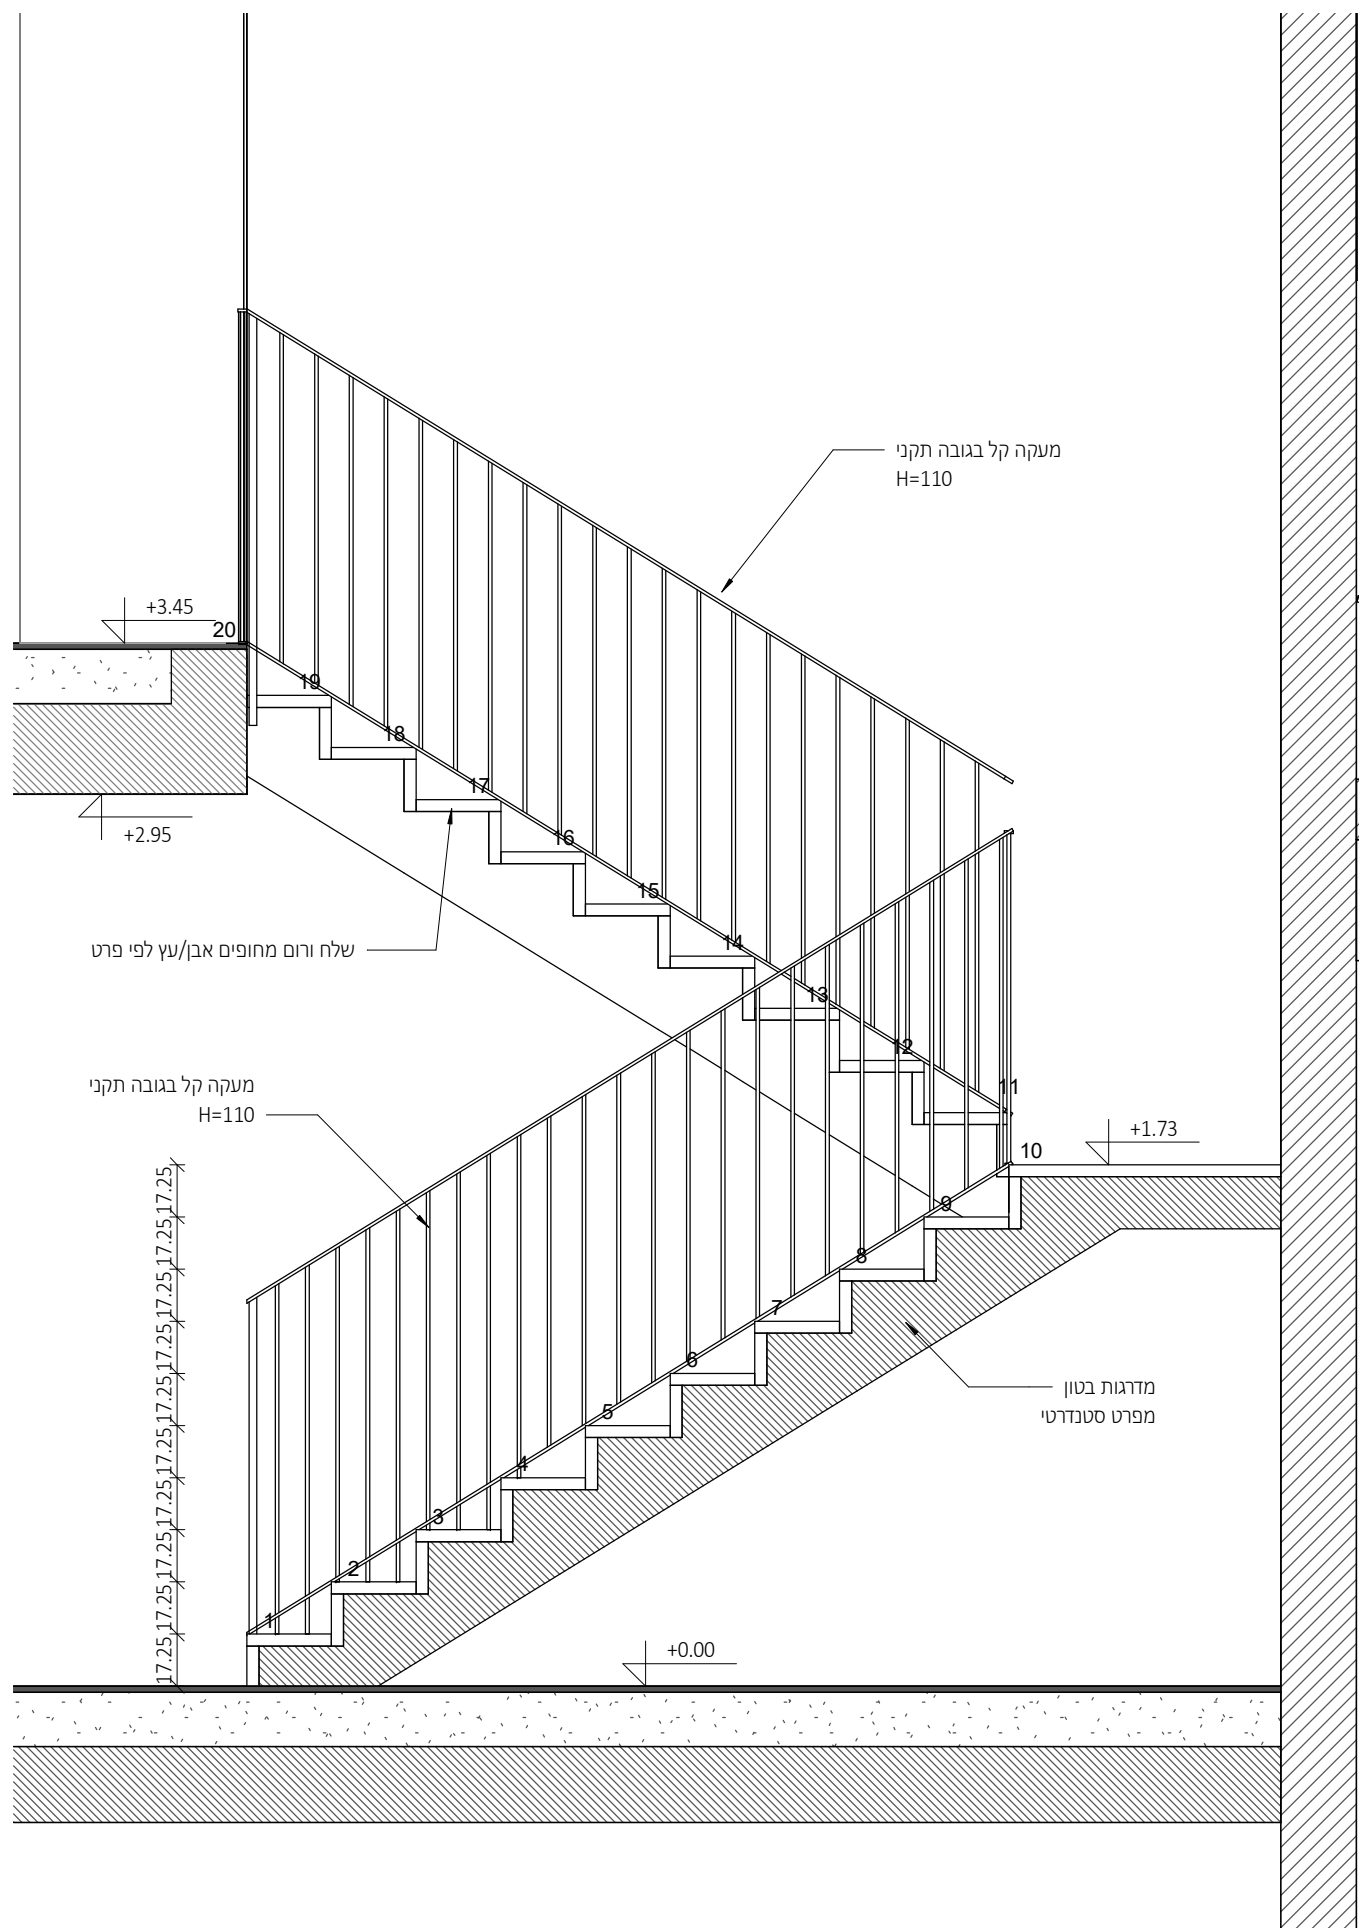

23


1 : 25




|                               |
|-------------------------------|
| ניהול פרויקט                  |
| מהיסוד - בן סולומון           |
| פיקוח                         |
| מהיסוד - בן סולומון           |
| קונסטרוקציה                   |
| ערן שילר                      |
| מיזוג אוויר                   |
| אייל ארז מהנדסים ויועצים בע"מ |
| אינסטלציה                     |
| איתן אלמסי                    |
| חשמל                          |
| איתן בסיס                     |
| אלומיניום                     |
| נוף                           |
| נתי בלוקא                     |
| חשמל חכם                      |
| חימום תת רצפתי                |
| איטום                         |
| צבי טל                        |
| אקוסטיקה                      |
| מעליות                        |
| קרקע וביסוס                   |
| דיה הנדסת קרקע וביסוס         |
| רישוי                         |

[illegible]


|                                       |           |                                                                                     |        |
|---------------------------------------|-----------|-------------------------------------------------------------------------------------|--------|
| CLIENT NAME:                          |           | העמותה                                                                              |        |
| קבוצת רכישה נופיה                     |           |                                                                                     |        |
| PROJECT NAME:                         |           | הפרויקט:                                                                            |        |
| נופיה - מגרש 22                       |           |                                                                                     |        |
| DRAWING NAME:                         |           | התכנון:                                                                             |        |
| פרטים                                 |           |                                                                                     |        |
| SHEET NUMBER:                         |           | הפרט:                                                                               |        |
| A3-4-103                              |           |                                                                                     |        |
| SCALE:                                | קנה מידה: | EDITION:                                                                            | הדורה: |
| As indicated                          |           |  |        |
| STATUS:                               | סטוס      |                                                                                     |        |
| למכר                                  |           |                                                                                     |        |
| DATE:                                 | 22.09.25  | האריך:                                                                              |        |
| NeumanHaymanArchitects                |           |  |        |
| office@nh-arch.com<br>www.nh-arch.com |           | יוזמן ויינר אדריכלים<br>התורה והתודות 2, בית תריות<br>09-9546042 70                 |        |

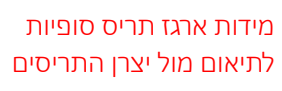

1 : 10

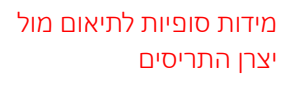


1 : 10


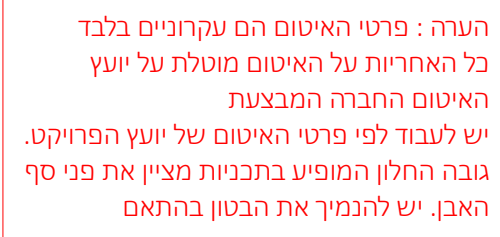


**פרט עקרוני בלבד - פרט סופי מספק החלונות**

1 : 10

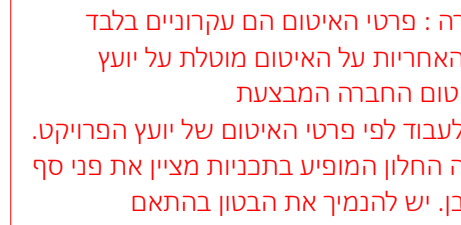

1 : 5

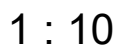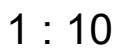

פרטי האיטום באחריות יועץ האיטום  
ראה חוברת פרטי איטום מצורפת

# להמשך תיאום







| רשימת חלונות |       |      |      |      |         |
|--------------|-------|------|------|------|---------|
| סוג          | תיאור | כמות | גובה | רוחב | מס פריט |

קומת קרקע

|     |     |     |   |                                      |                                             |
|-----|-----|-----|---|--------------------------------------|---------------------------------------------|
| 1   | 90  | 240 | 2 | צלון רפפה חיצוני חשמלי + ארגז חיצוני | חלון קבוע פרופיל 7000 קליל                  |
| 1.1 | 90  | 240 | 2 | צלון רפפה חיצוני חשמלי + ארגז חיצוני | חלון קבוע עד 130 + חלון דרייפקי פרופיל 4350 |
| 2   | 200 | 110 | 1 | צלון רפפה חיצוני חשמלי + ארגז חיצוני | חלון הזזה פרופיל 7000 קליל                  |
| 3   | 300 | 110 | 1 | צלון רפפה חיצוני חשמלי + ארגז חיצוני | חלון הזזה פרופיל 7000 קליל                  |
| 4   | 70  | 110 | 1 | ללא רפפה                             | חלון קיפ פרופיל 4500 קליל                   |
| 5   | 220 | 240 | 1 | צלון רפפה חיצוני חשמלי + ארגז חיצוני | ויטרינה פרופיל 7500 קליל                    |
| 6   | 520 | 240 | 1 | צלון רפפה חיצוני חשמלי + ארגז חיצוני | ויטרינה פרופיל 7500 קליל                    |

קומה א

|   |     |     |   |                  |                            |
|---|-----|-----|---|------------------|----------------------------|
| 7 | 220 | 110 | 4 | תריס גלילה חשמלי | חלון הזזה פרופיל 7000 קליל |
| 8 | 80  | 210 | 1 | תריס גלילה חשמלי | דלת כנף פרופיל 4350 קליל   |
| 9 | 70  | 110 | 2 | תריס גלילה חשמלי | חלון קיפ פרופיל 4500 קליל  |

סוג זכוכית – בהתאם למפורט בדו"ח התרמי (תנאי המינימום בעמוד 9 מתוך המפרט התרמי). כמו כן, הזכוכית תקבע בתיאום עם הקבלן לאחר אישור יועץ התרמי וחברת הניהול

כל פריט יחולק למינימום הכנפיים האפשרי (לתיאום מול ספק האלומיניום ובמסגרת שרטוטי הshop drawing)

| רשימת דלתות |                                |      |      |      |           |
|-------------|--------------------------------|------|------|------|-----------|
| סוג         | הערות                          | כמות | גובה | רוחב | מספר פריט |
| 0           | דלת חוץ דגם גארדה              | 1    | 240  | 120  | 0         |
| 1           | דלת פנים "אקוודור" תוצרת חמדיה | 6    | 210  | 90   | 1         |
| 2           | דלת פנים "אקוודור" תוצרת חמדיה | 4    | 210  | 80   | 2         |
| 3           | דלת פנים "אקוודור" תוצרת חמדיה | 1    | 210  | 70   | 3         |
| 4           | דלת פנים "אקוודור" תוצרת חמדיה | 1    | 210  | 80   | 4         |

נוימן חיינר אדריכלים בע"מ

כל הזכויות שמורות  
ט.ל.ח.

NeumanHaynerArchitects

רשימת פתחים

שם התכנית:

|                             |  |                  |               |
|-----------------------------|--|------------------|---------------|
| גליון מספר: A3-6-1000       |  | מהדורה: 22.09.25 | <div>01</div> |
| שם הפרויקט: נופיה - מגרש 22 |  | סטטוס: למכרז     |               |
| שם המממן: קבוצת רכישה נופיה |  | קנה מידה:        |               |
| 30/11/2025 15:55:38         |  |                  |               |