


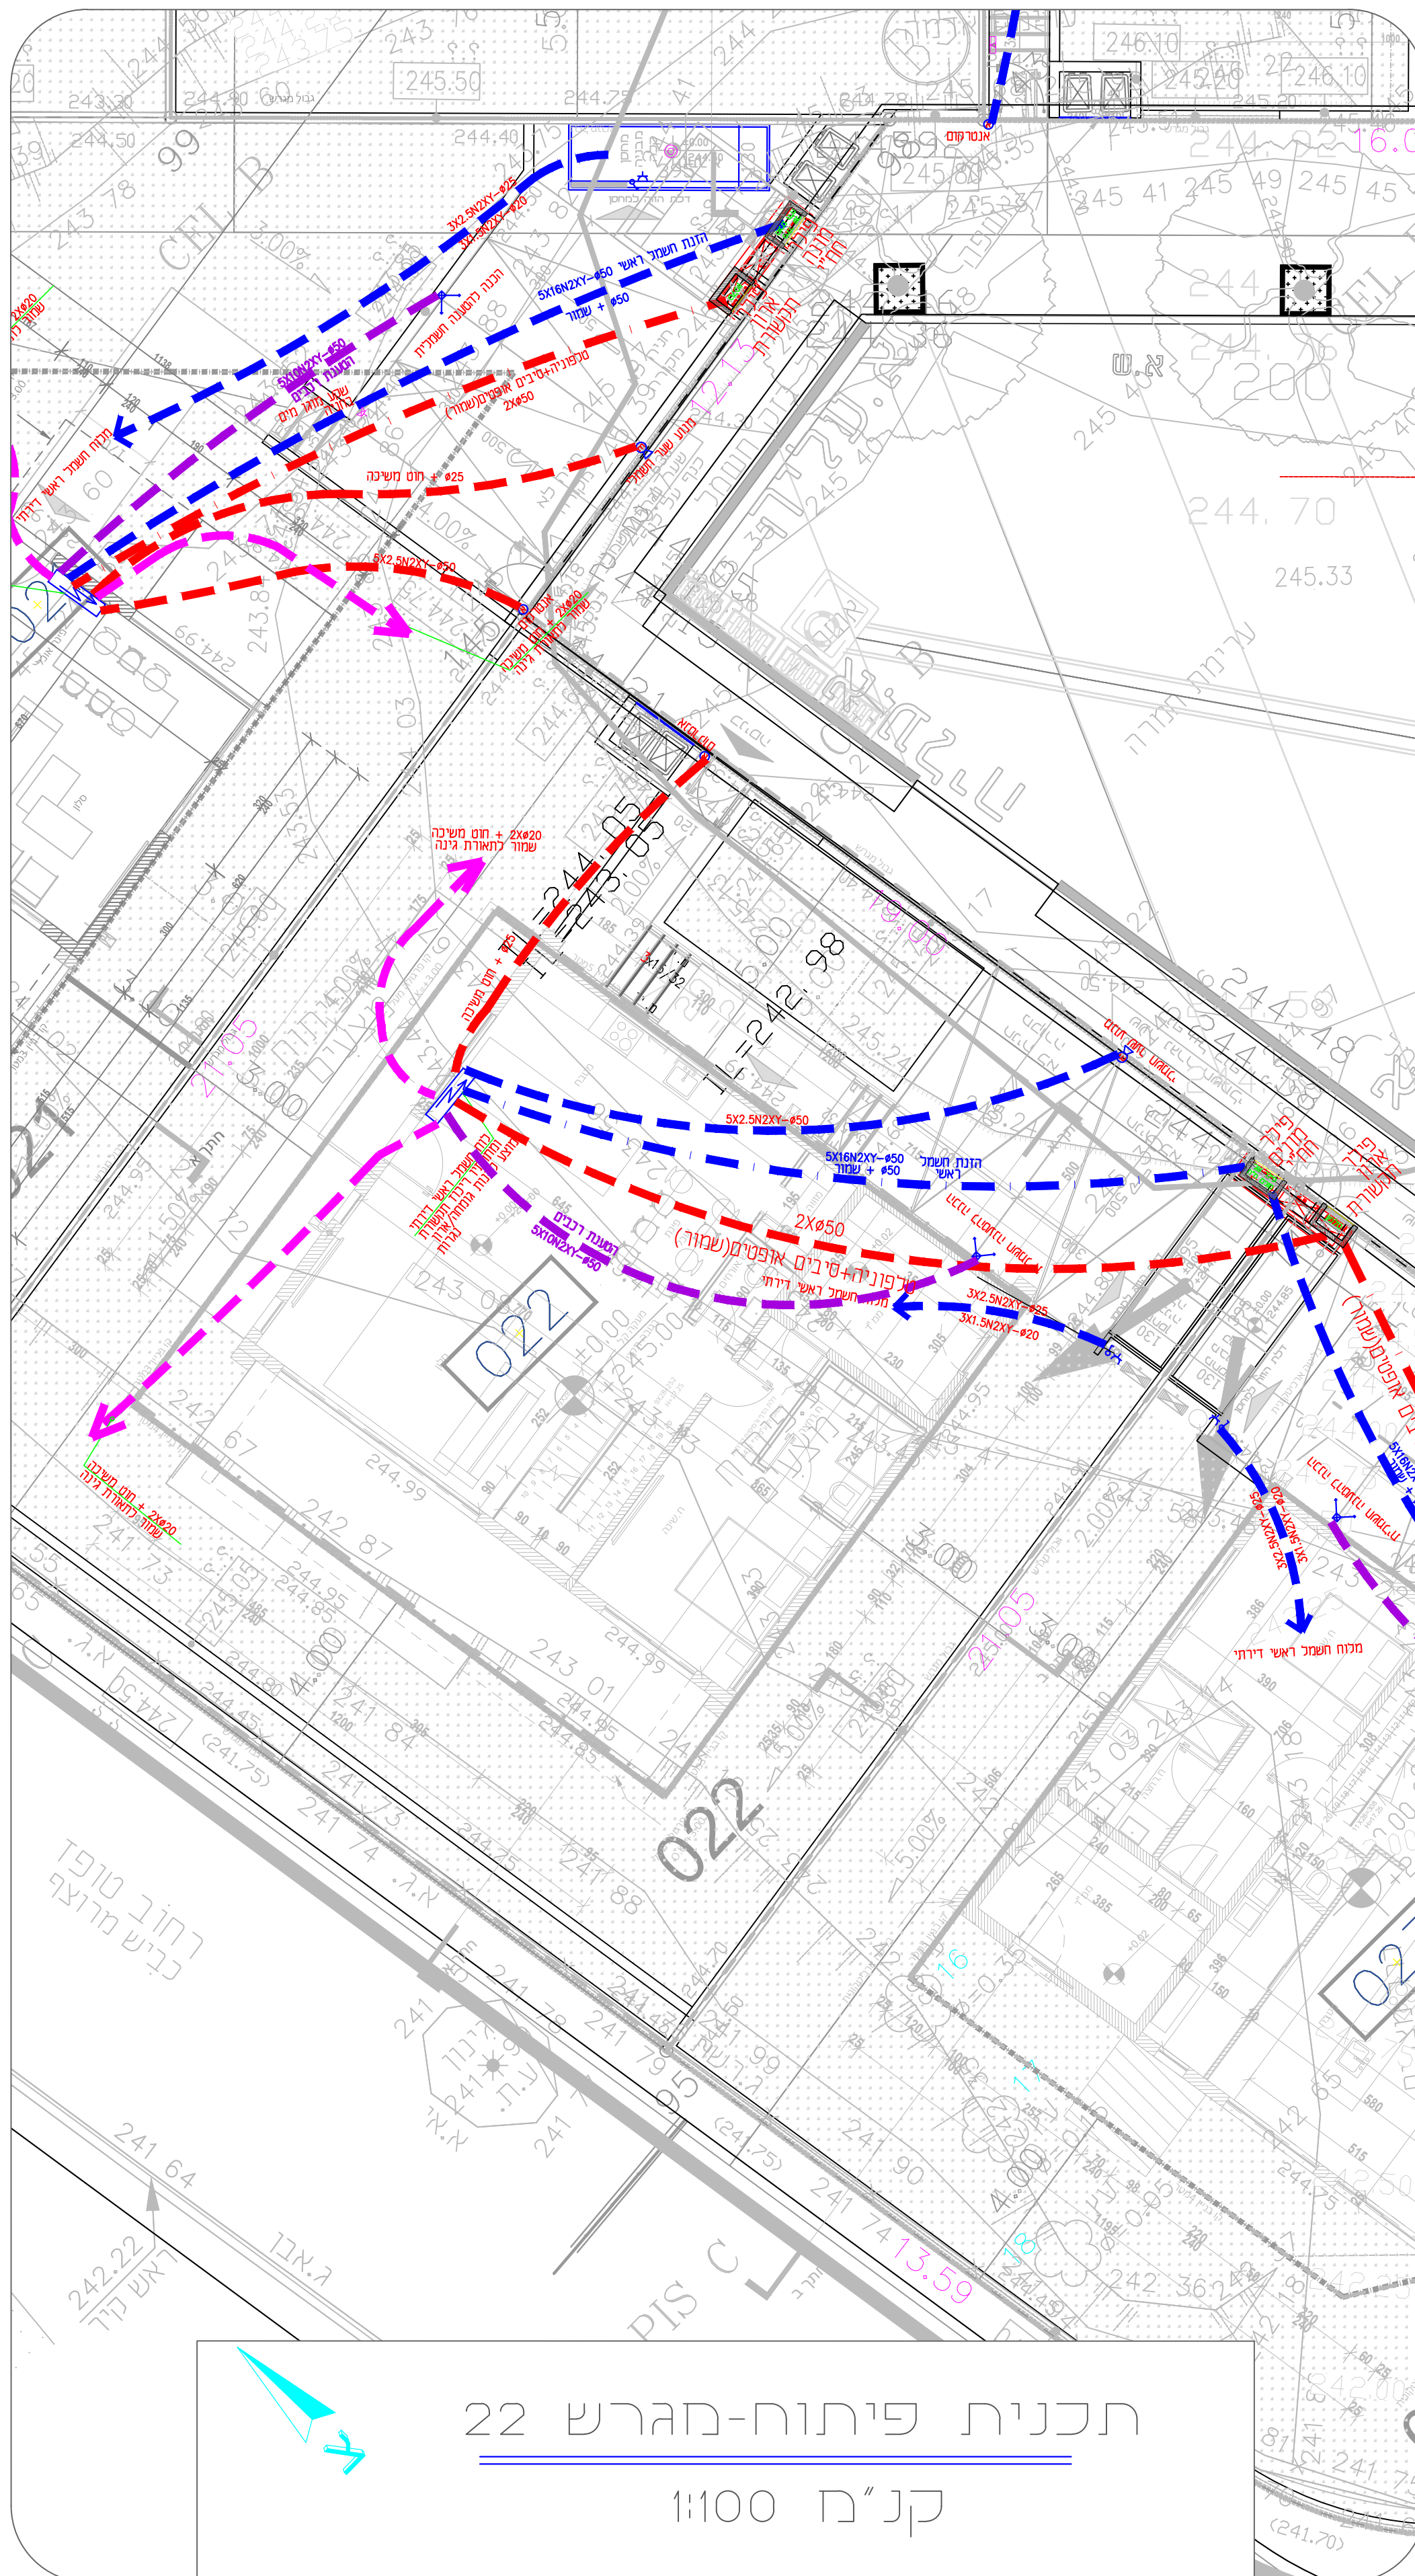

[illegible][illegible]

עודכן ע"י: \_\_\_\_\_ רחל

א. בסיס  
הנדסת חשמל בע"מ

משרד: יד חרוצים 16, ירושלים 93420  
טל: 074-7021015 נייד: 050-6550484  
פקס: 077-5131015 רשת: office@ebasis.co.il



# שם הפרויקט: נופיה-אלפי מנשה

שם הגיליון:
תוכנית פיתוח מגרש 22

|   |  |                                                          |  |
|---|--|----------------------------------------------------------|--|
| <div> <div>○</div> <div>●</div> <div>○</div> <div>○</div> </div> <div> <div>כביצוץ</div> <div>נמכרז</div> <div>לאישור</div> <div>לעיון</div> </div> |  | <div>קנה מידה:</div> <div>1:100</div>                    |  |
| <div>File:</div> <div>מס' קובץ:</div> <div>675P.dwg</div>                                                                                           |  | <div>Date:</div> <div>תאריך:</div> <div>17.06.2024</div> |  |
| <div>אישר:</div> <div>איתן</div>   |  | <div>שרטט:</div> <div>אילה</div>                         |  |
| <div>מס' הפרויקט:</div> <div>675</div>   |  | <div>מס' הגליון:</div> <div>P22</div>                    |  |
|   |  | <div>מס' עדכון:</div> <div>0</div>                       |  |

|              |             |            |
|--------------|-------------|------------|
| מס' הפרויקט: | מס' הגליון: | מס' עדכון: |
| 675          | 22          | 0          |

