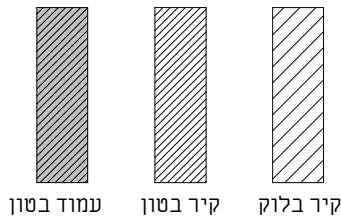


מתכונים:

ניהול פרויקט
מהיסוד - בן סולמון
פיקוח
מהיסוד - בן סולמון
קונסטרוקציה
ערן שילר
מיזוג אוויר
אייל ארז מהנדסים ויועצים בע"מ
אינסטלציה
איתן אלמסי
חשמל
איתן בסיס
אלומיניום
נוף
נתי בלוקא
חשמל חכם
חימום תת רצפתי
איטום
צבי טל
אקוסטיקה
מעליות
קרקע וביסוס
דיה הנדסת קרקע וביסוס
רישוי

[illegible]

מקרא קירות:

[illegible]

אדריכלות

CLIENT NAME: _____ שם המזמין:

קבוצת רכישה נופיה

PROJECT NAME: שם הפרויקט:

נופיה - מגרש 23

DRAWING NAME: ס הגליון:

גליון שער

SHEET NUMBER: 190 גליון:

A3-1-100

SCALE: קנה מידה: EDITION: הדורה: ^

STATUS: סמטוט 1

רשט ע"י:	נבדק ע"י:
----------	-----------

DATE: 22.09.25 :877



NeumanHaynerArchitects


וימן חיינר אדריכלים
 וורד ההדסים 2, בית חירות
 טל 09-9545842
 office@nh-arch.com
 www.nh-arch.com

וימן חיינר אדריכלים
מורד ההדריס 2, בית חירות
טל 09-9545842

זכויות ייצור / ע"פ הנחיות עו"ד

נופיה - מגרש 23			
מס' גיליון	שם גיליון	מהדורה	תאריך הפצת מהדורה

22.09.2025	1	גליון שער	A3-1-100
22.09.2025	1	קרקע	A3-1-101
22.09.2025	1	קומה א	A3-1-102
22.09.2025	1	גג	A3-1-103
22.09.2025	1	חזיתות 1	A3-2-200
22.09.2025	1	חזיתות 2	A3-2-201
22.09.2025	1	חתכים	A3-3-100
22.09.2025	1	גליון מדדגות	A3-4-100
22.09.2025	1	פרטים	A3-4-103
22.09.2025	1	פרטי פרגולה	A3-4-104
22.09.2025	1	רשימת פתחים	A3-6-1000

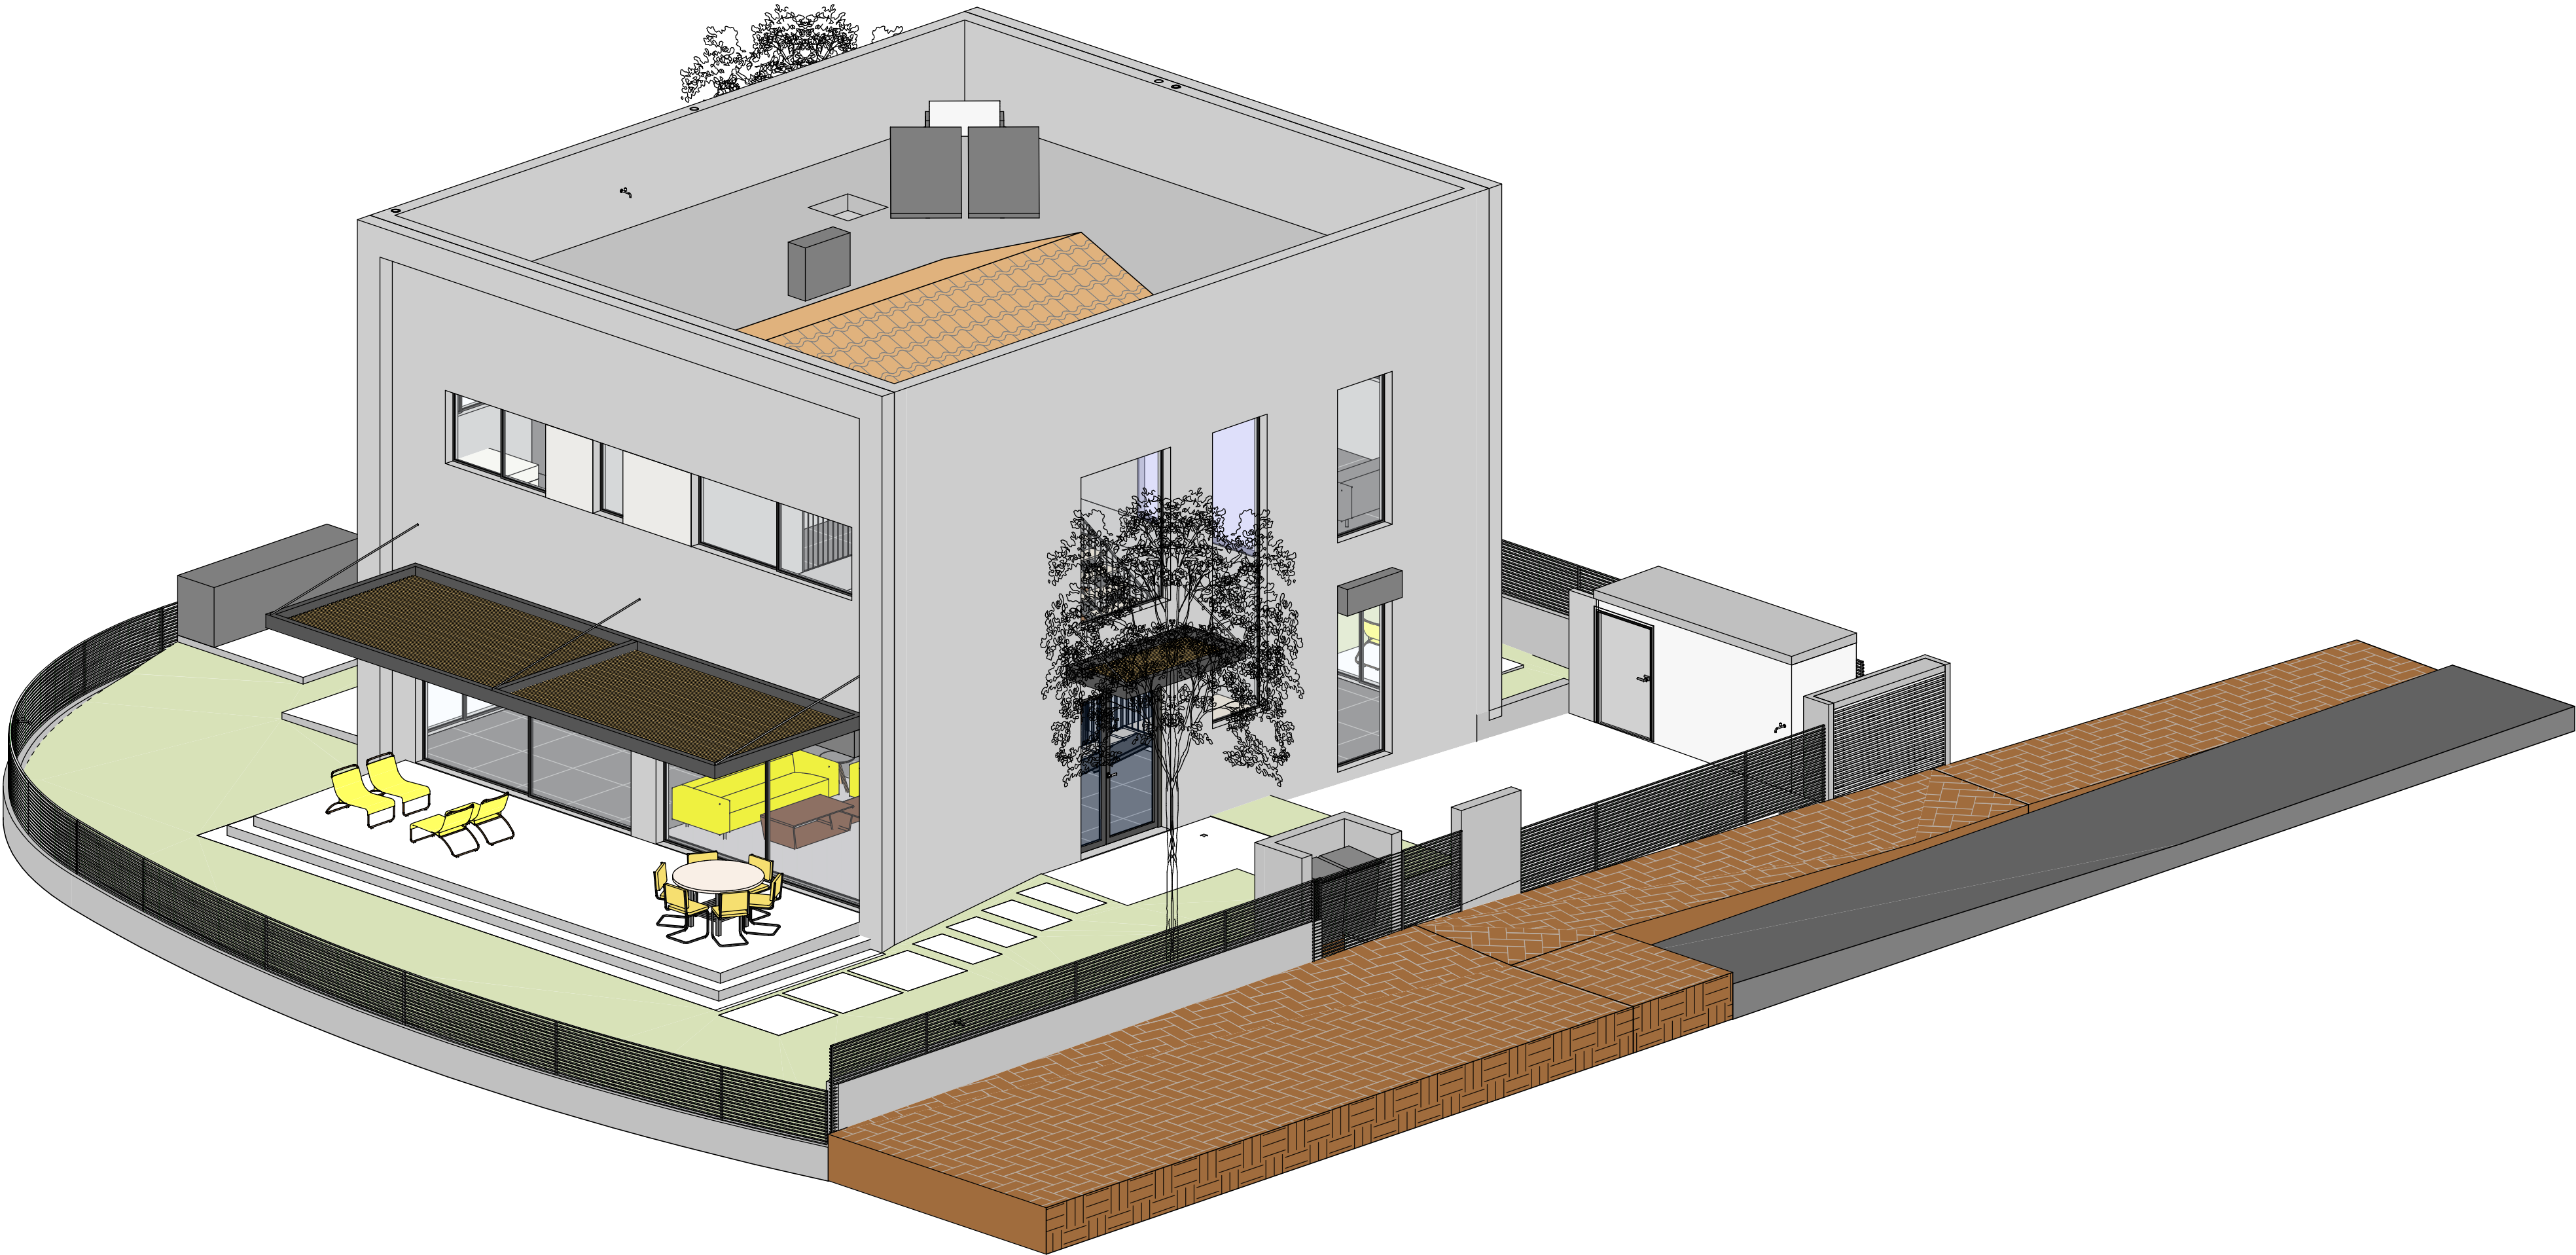

ניהול פרויקט
מהיסוד - בן סולומון
פיקוח
מהיסוד - בן סולומון
קונסטרוקציה
ערן שילר
מיזוג אוויר
אייל ארז מהנדסים ויועצים בע"מ
אינסטלציה
איתן אלמסי
חשמל
איתן בסיס
אלומיניום
נוף
נתי בלוקא
חשמל חכם
חימום תת רצפתי
איטום
צבי טל
אקוסטיקה
מעליות
קרקע וביסוס
דיה הנדסת קרקע וביסוס
רישוי

הצהרה	כן (%)
התכנית הזאת תורמת להגדלת היעילות העסקית	65
התכנית הזאת תורמת להפחתת עלויות	75
התכנית הזאת תורמת להפחתת הסיכונים	60
התכנית הזאת תורמת להפחתת הריבוי	55
התכנית הזאת תורמת להפחתת הבעיות	60

[illegible]


CLIENT NAME:	המחירון
קבוצת רכישה נופיה	
PROJECT NAME:	הפרויקט
נופיה - מגרש 23	
DRAWING NAME:	התגלית
קרקע	
SHEET NUMBER:	פרט גליון:
A3-1-101	

SCALE:	קנה מידה:	EDITION:	דורות:
1 : 50			
STATUS:	סטטוס		
למבר			
	נבדק ע"י:		דרסט ע"י:
DATE:	22.09.25		אריך:

NeumanHaynerArchitects

יומן חיינר אדריכלים
בית חירות 2, החדרים
09-9545842

office@nh-arch.com
www.nh-arch.com

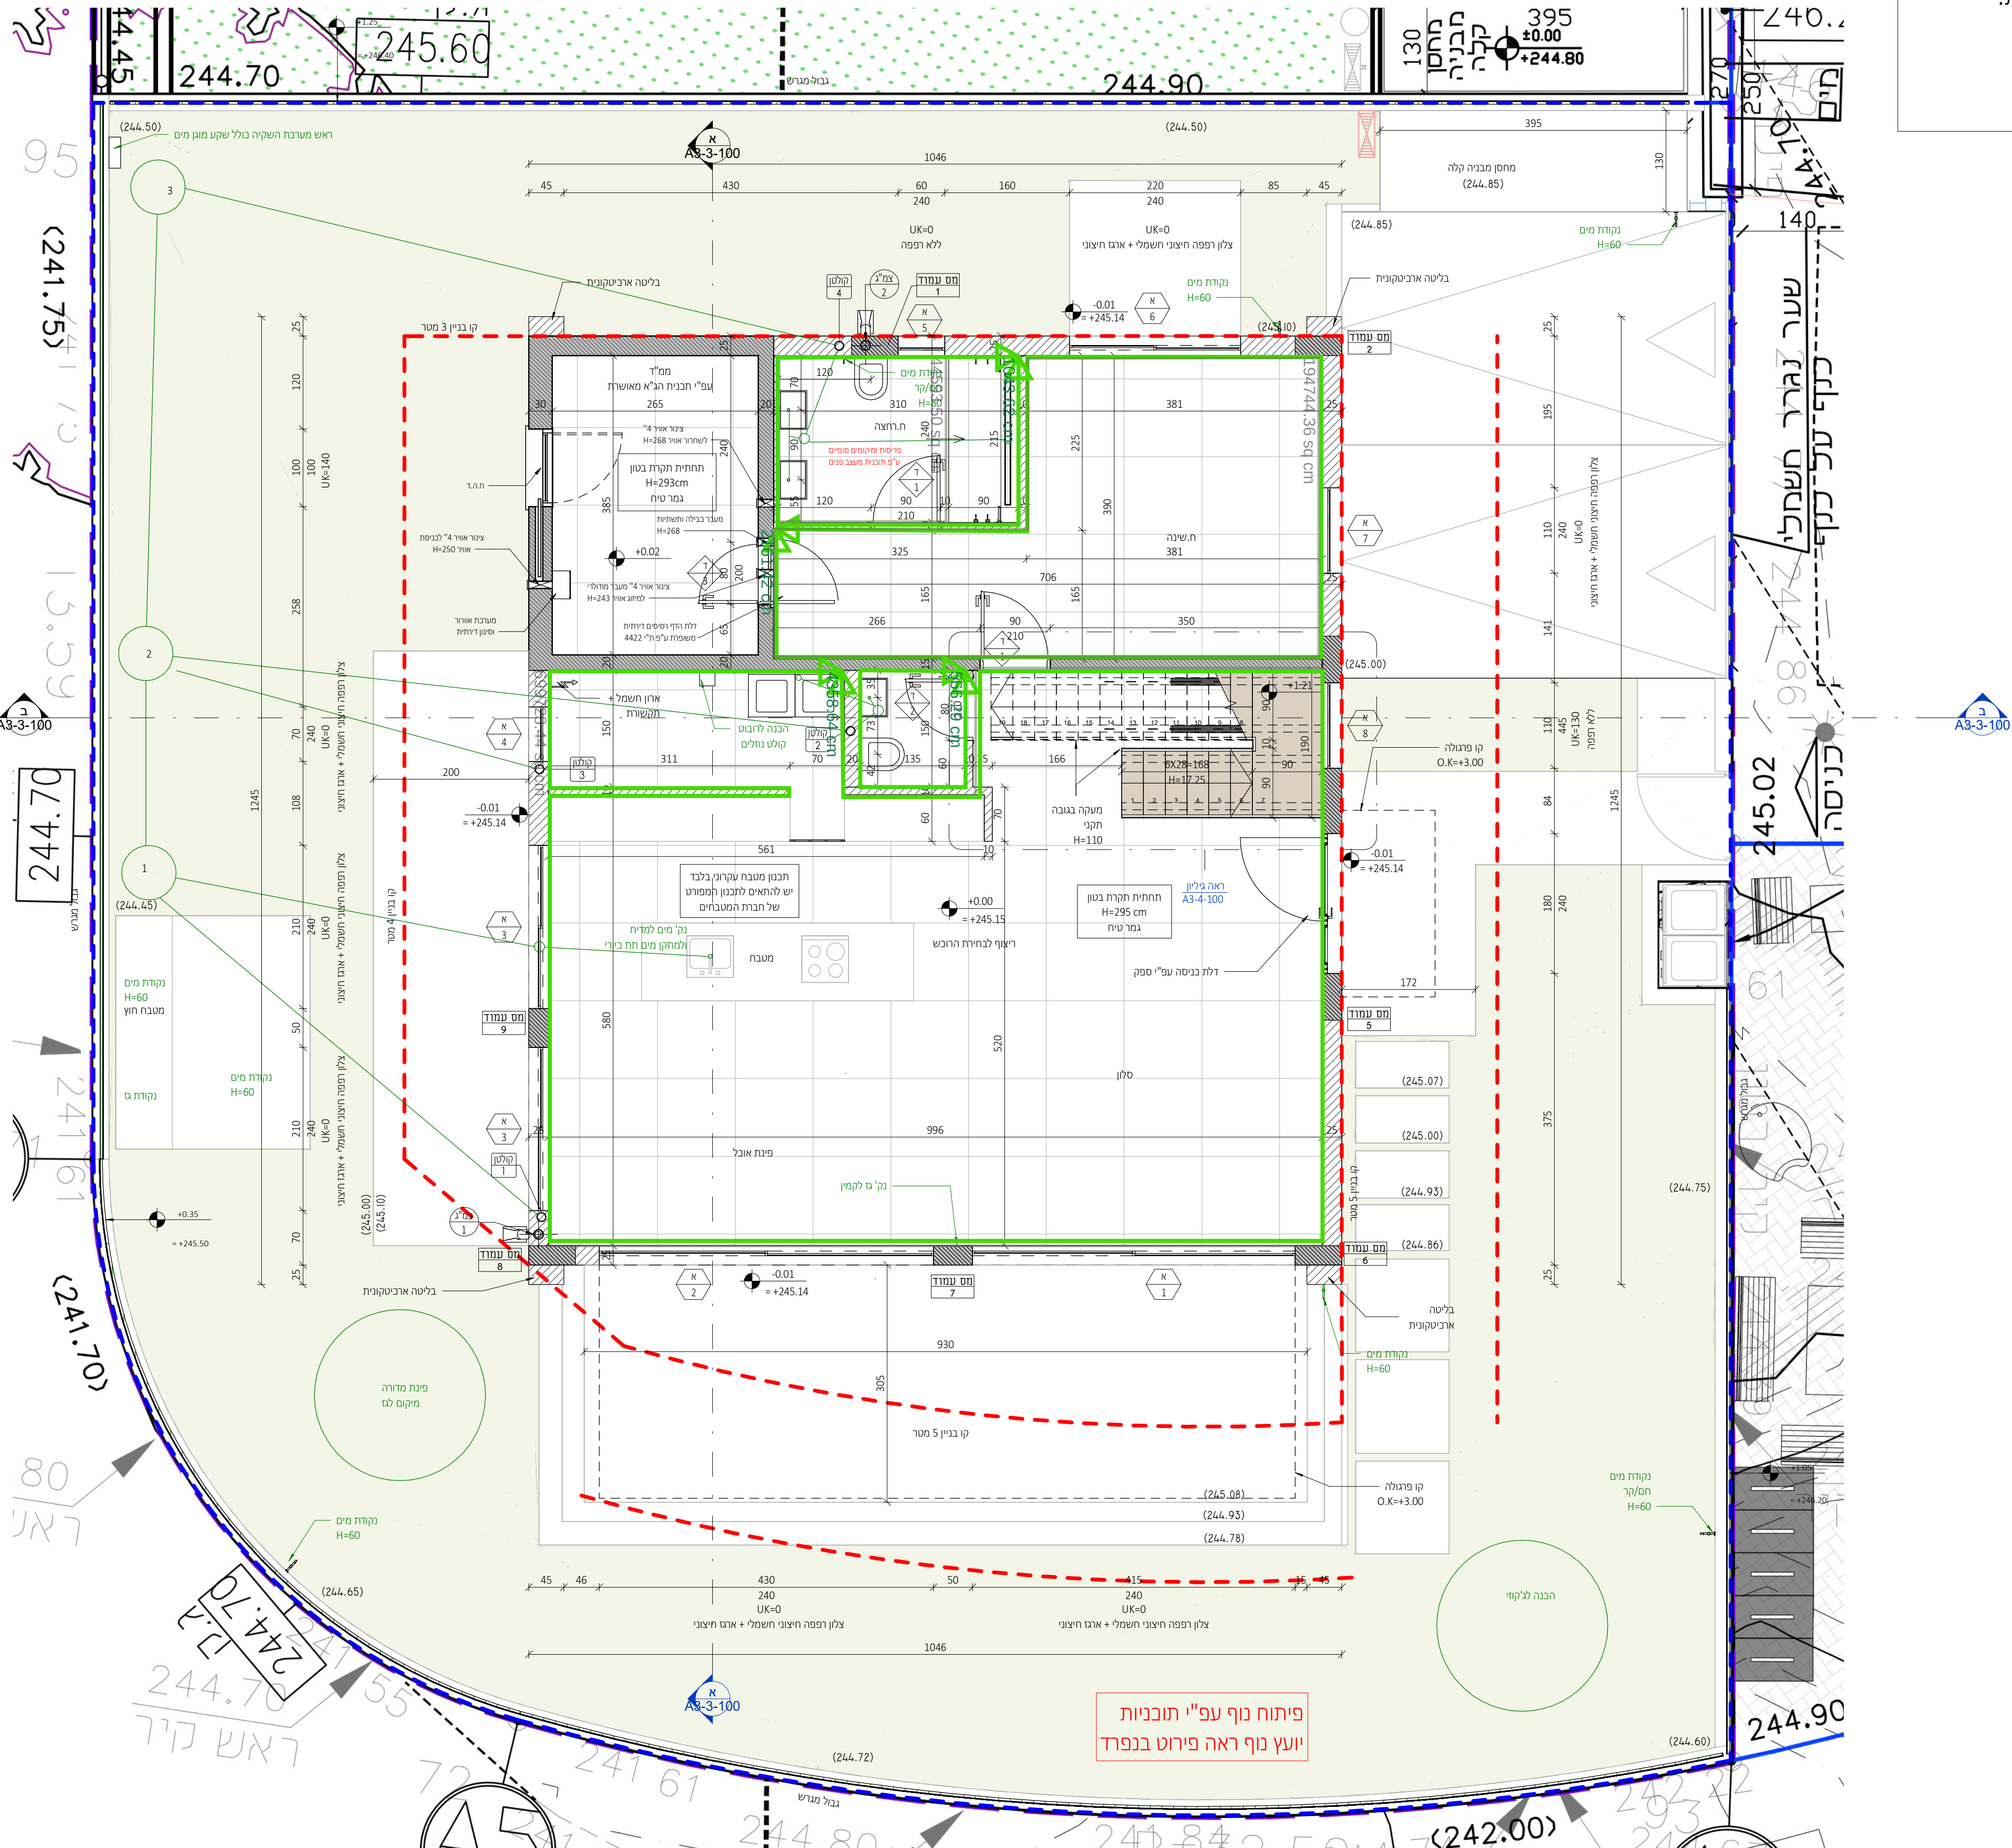

1 : 50

1. יש לעבוד במקביל לתכניות יועצים המאושרות על ידי האדריכל.
2. פרטי ספי חלון - עפ"י חוברת אלומיניום של הספק הנבחר ובתיאום מול אדריכל.
3. חימום תת רצפתי (במידה ויש במגרש זה) עפ"י פרטי הספק ובתיאום מול אדריכל.
4. יש לעבוד במקביל לתכניות עיצוב פנים (במידה ויש מעצב פנים במגרש זה) המאושרות על ידי האדריכל.
5. באחריות הקבלן לעדכן את האדריכל על אי התאמה בין התכניות יועצים לאדריכלות.
6. כל הדלתות לפי מפרט מצורף.
7. כל אלמנטי הבטון יקבלו התייחסות תרמית לפי הנחיות יועץ.
8. פרטי איטום, בידוד וניקוז עפ"י תכניות יועצים ובאחריות הקבלן.

- הערות:
- יש לעבוד במקביל לתכניות יועצים המאושרות על ידי האדריכל.
 - פרטי ספי חלון - עפ"י חוברת אלומיניום של הספק הנבחר ובתיאום מול אדריכל.
 - חימום תת רצפתי (במידה ויש במגרש זה) עפ"י פרטי הספק ובתיאום מול אדריכל.
 - יש לעבוד במקביל לתכניות עיצוב פנים (במידה ויש מעצב פנים במגרש זה) המאושרות על ידי האדריכל.
 - באחריות הקבלן לעדכן את האדריכל על אי התאמה בין התכניות יועצים לאדריכלות.
 - כל הדלתות לפי מפרט מצורף.
 - כל אלמנטי הבטון יקבלו התייחסות תרמית לפי הנחיות יועץ.
 - פרטי איטום,בידוד וניקוז עפ"י תכניות יועצים ובאחריות הקבלן.

ניהול פרויקט
מהיסוד - בן סולומון
פיקוח
מהיסוד - בן סולומון
קונסטרוקציה
ערן שילר
מיזוג אוויר
אייל ארז מהנדסים ויועצים בע"מ
אינסטלציה
איתן אלמסי
חשמל
איתן בסיס
אלומיניום
נוף
נתי בלוקא
חשמל חכם
חימום תת רצפתי
איטום
צבי טל
אקוסטיקה
מעליות
קרקע וביסוס
דיה הנדסת קרקע וביסוס
רישוי


± 0.00 = +245.15
הערות: 1. תכנית זו איננה לקרא יחד עם תכנית הריטשים. 2. גובה אבסולוטי - ראו תכנית פיתוח. 3. המידות הן בין קירות הבניה ולא כולל פחים. 4. פיתוח השטח סביב הבניה, כולל, מדרגות, גדרות, שבילים, ריצופים, שטחים בגנים, חניה וגן ראו תכנית פיתוח. 5. איטום קירות הרצפת הבניה כמעט עם הקרקע ובידוד תרמי לאורך העמודים והקירות וכל תכנית - לפרט או עם סימני גימון - ראו תכנית קונסטרוקציה. 6. אין מים יבוצע בכל מישור אופקי הכולל מחבנין. 7. סוף תרמי במסלול - ע"פ מפרט ותומקור, מאושר ע"י פיקוח העיר.
המבצע אחראי לסידור: עליו לבקר ולבדוק את כל המידות בתכנית ובמקום הבניה. במסלול של מסלול או אי התאמה בתכנית /או בבנין, עליו להודיע על כך מיד לאדריכל בסיום המשיך בעבודות. המבצע ישתמש או ויקי בתכנית שאושר לכניסה. המבצע יחזיק תוכנית, בכל עת, של משרדו של תכנית. אין לקבוע מידות על ידי מדידה בשטח. התכנית היתה רכוש האדריכל ואין לשנות כל שימוש בה או ברעיונות הגלומים בה, אלא באישור בכתב מאדריכל. מומנם /או יושם אשר ממנו רשום בתכנית זו, נושא לכיד באחריות המקצועית והתקנית לתכנית. על המפקח והמבצע לודא התאמת התכנית האדריכלית "כניסיו" לתכנית זו, ויתר, המוכר והתכנית המאושרות ע"י כל גורמים הרשמיים. התכנית כוללת את כל האמצעים והידוע עד ליום תחלתה.
משרד קירות:
קיר בלוק קיר בסוס עמוד בסוסן

תאריך	תיאור	מהדורה
22.09.2025	מכרז	1

אדריכלות
שם המסלול:
קבוצת רכישה נופיה
שם הפרויקט:
נופיה - מגרש 23
שם הגליון:
קומה א
מספר גליון:
A3-1-102
תחזורה:
EDITION: קנה מידה:
SCALE: 1 : 50
STATUS: סטוס
למכרז
שורשים ע"י:
נבדק ע"י:
תאריך:
22.09.25

NeumanHaynerArchitects נירסן חיינו אדריכלים מודד והנדס 2, בית חירות 09-954642 78	נירסן חיינו אדריכלים מודד והנדס 2, בית חירות 09-954642 78
--	--

זכויות יוצר / ע"פ הנחיות ע"ד

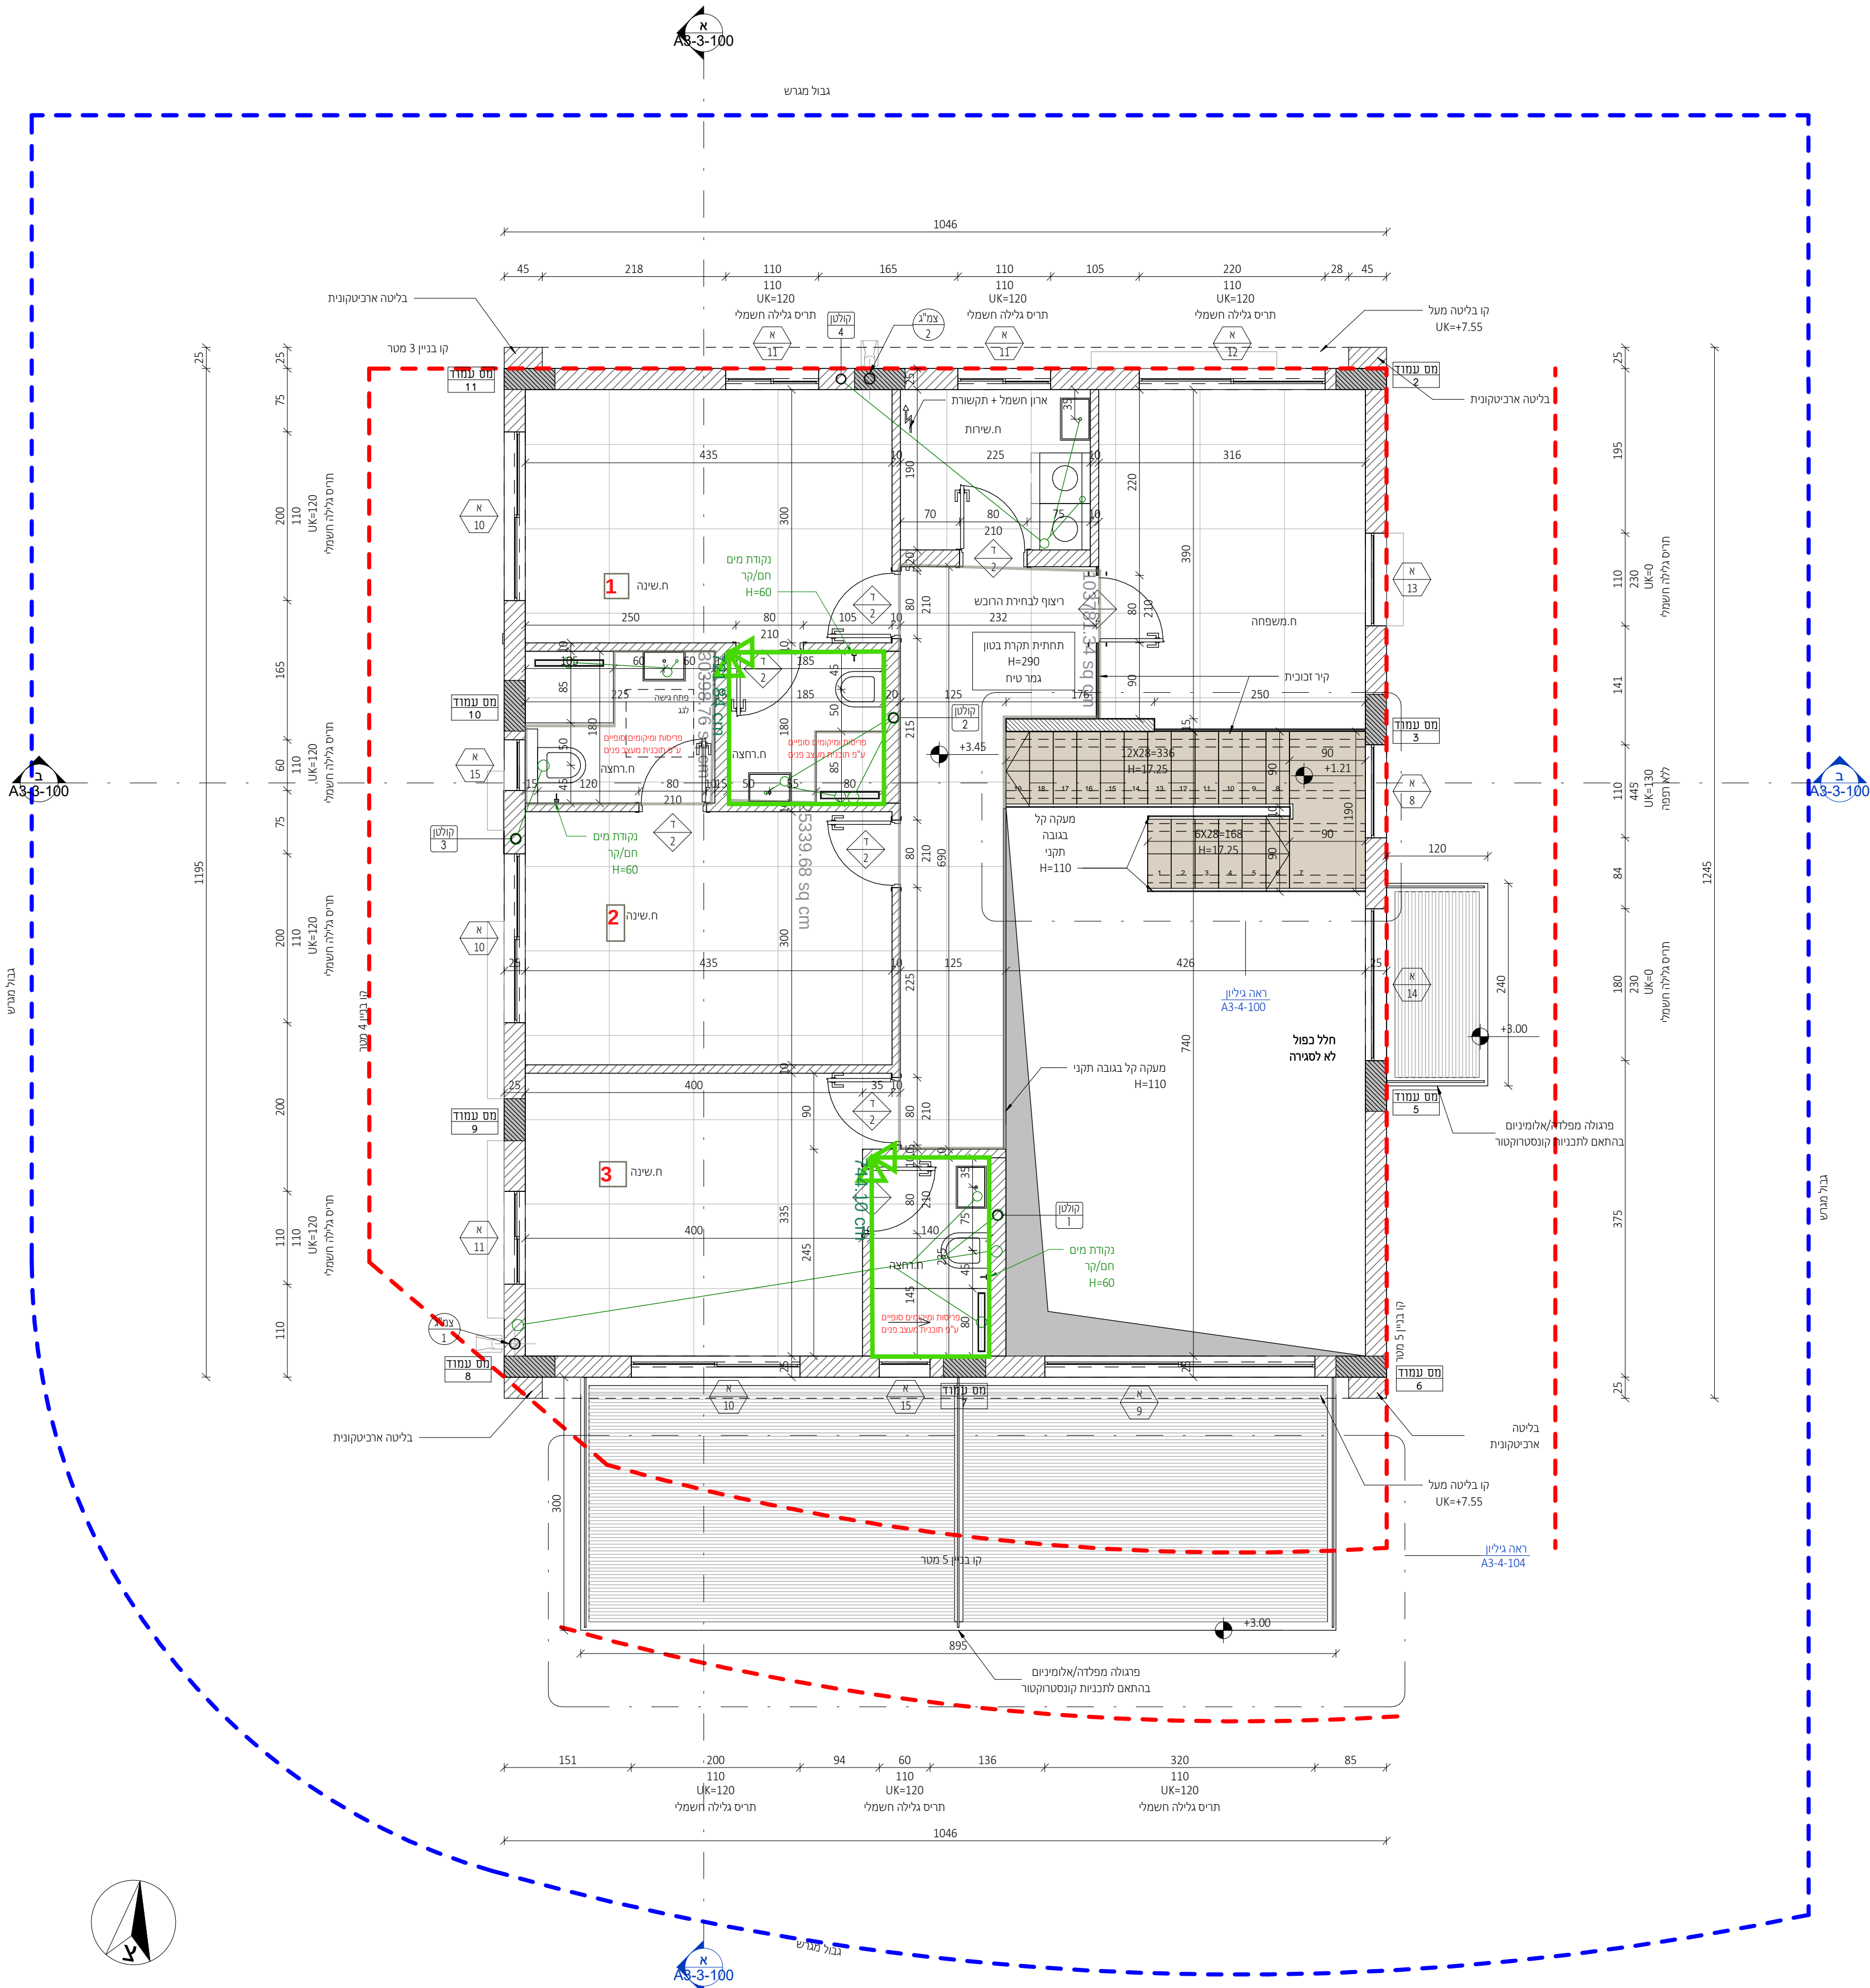

תכנית קומה א

1 : 50

מתכונים:


ניהול פרויקט
מהיסוד - בן סולומון
פיקוח
מהיסוד - בן סולומון
קונסטרוקציה
ערן שילר
מיזוג אוויר
אייל ארז מהנדסים ויועצים בע"מ
אינסטלציה
איתן אלמסי
חשמל
איתן בסיס
אלומיניום
נוף
נתי בלוקא
חשמל חכם
חימום תת רצפתי
איטום
צבי טל
אקוסטיקה
מעליות
קרקע וביסוס
דיה הנדסת קרקע וביסוס
רישוי

$$\pm 0.00 = +245.15$$

הערות:
 1. תכנית זו יש לקרוא יחד עם תכניות הוועצים.
 2. גובה אבסולוטים – ראו תכנית פיתוח.
 3. המידות הן ב'ין פירות תחנה, (ראו כלול ס'ח).
 4. פיתוח השטח בשטח חניה, כולל, מדרגות, גדרות, שביליים, רציפים,
 5. פסיפוגים וכו'.
 6. אסוס. תכנית ורצפות התנהג במגע עם הקרקע ובידוד תרמי לאורך המעטרים
 7. הוקורות ועל התקורות – כליות או עם מיני (גירון) – ראו תכניות קונסטרוקציה
 8. א' ח' כיבוע כלל מישור אופקי חתוכי החתוכי.
 9. ראו תרמי מבטבי – ראו פרט מורחב, מחבר.

[illegible]

זקרא קירות:

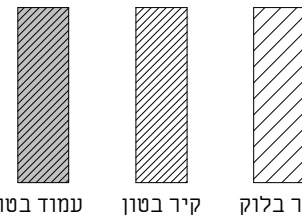[illegible]

אדריכלות

CLIENT NAME: _____ שם המזמין:

קבוצת רכישה נופיה

PROJECT NAME: שם הפרויקט:

נופיה - מגרש 23

DRAWING NAME: ס הגליון:

גג

SHEET NUMBER: 190 גליון:

A3-1-103

SCALE: _____: קנה מידה: EDITION: _____: הדורה:

1 : 50

STATUS: סמכות 1

למכרז	
-------	---

רשטע ע"י: _____ נבדק ע"י: _____


DATE: 22.09.25 אר"י:

NeumanHaynerArchitects

נומני פנויב אצדוקליות

office@nh-arch.com
www.nh-arch.com


צביה / א"פ בנסים א"י

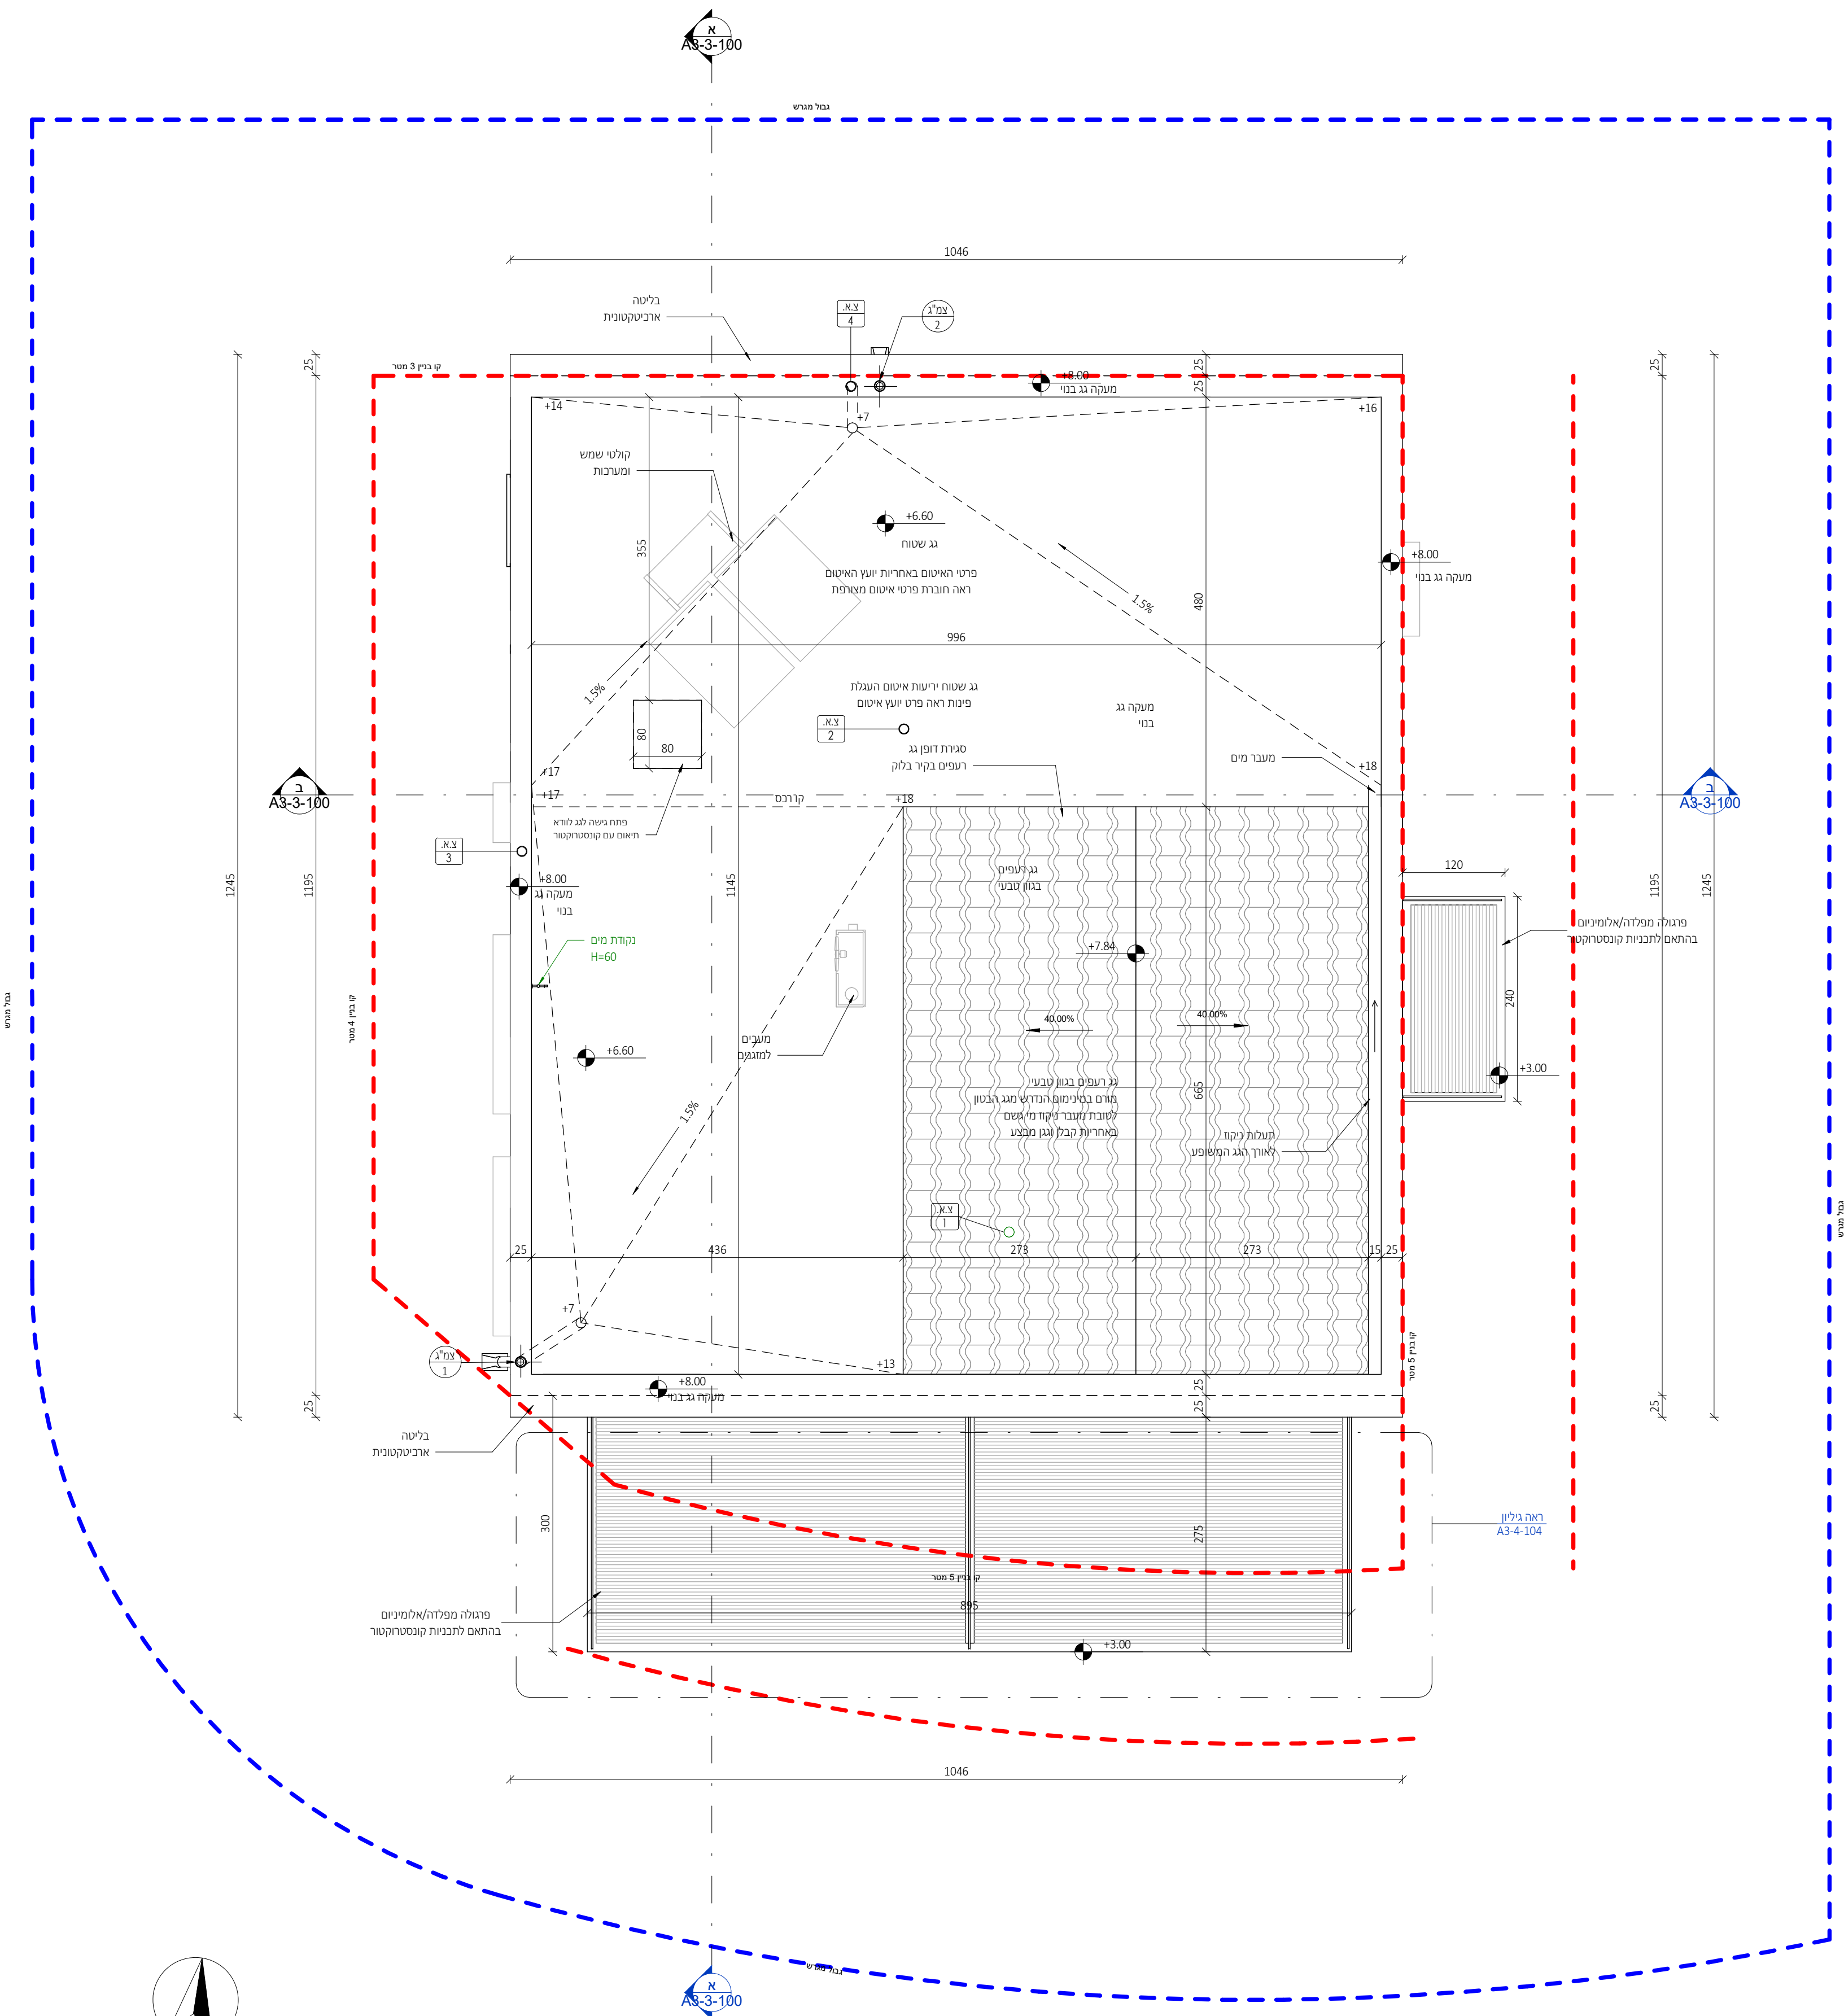


תכנית גג

1 : 50

פרטי איטום, בידוד וניקוז עפ"י תכניות יועצים ובאחריות הקבלן

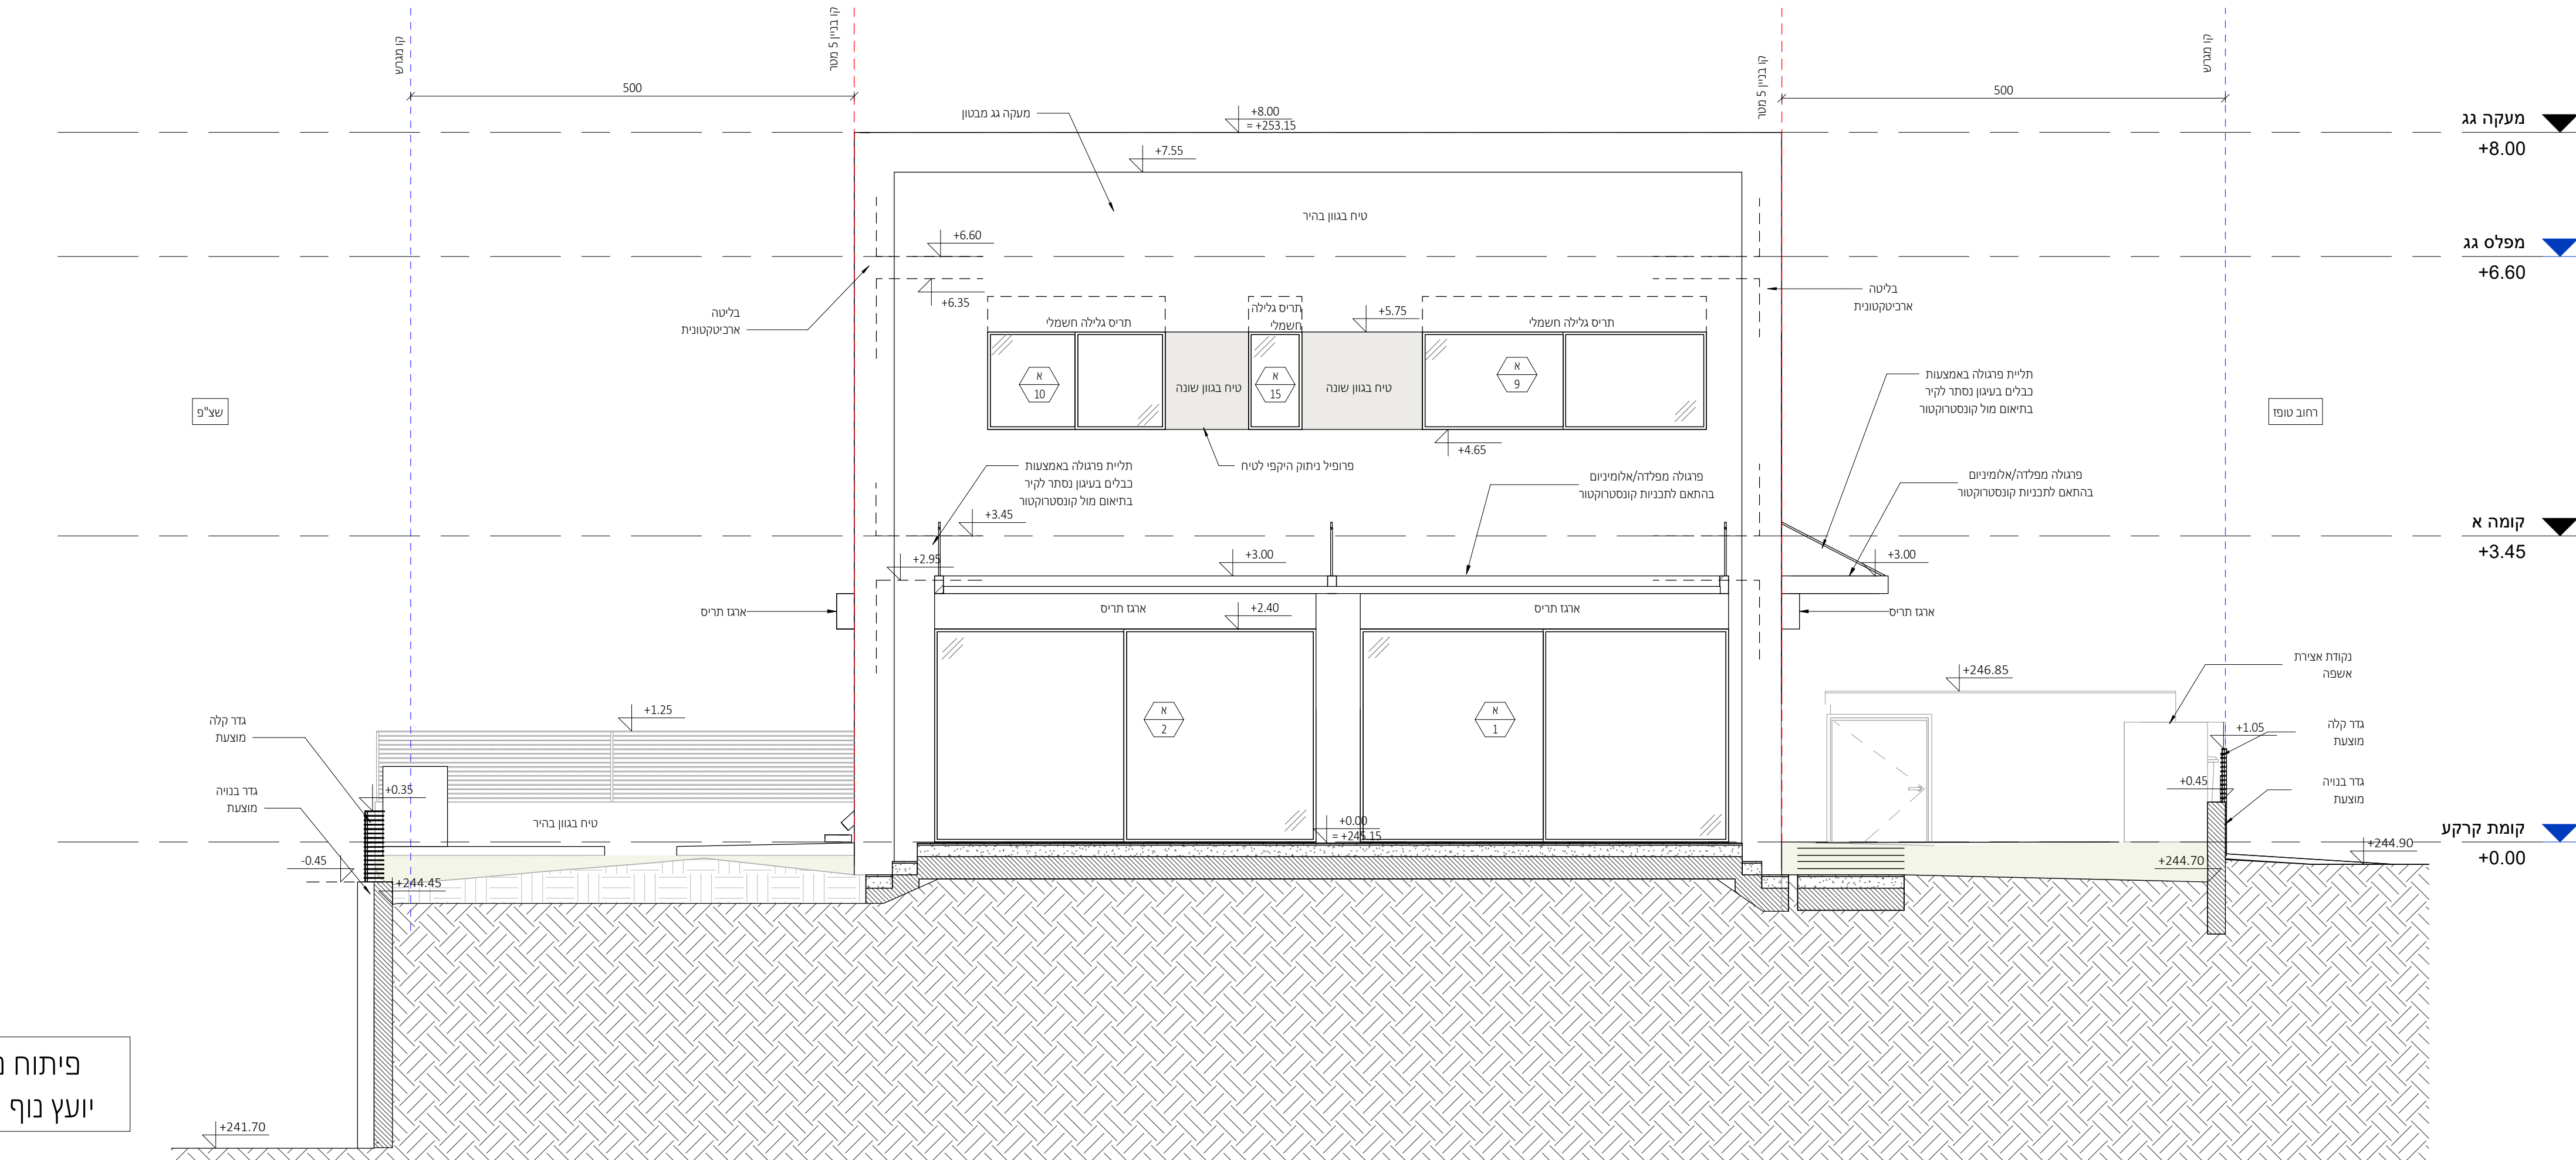

פיתוח נוף עפ"י תוכניות
ועץ נוף ראה פירוט בנפרד

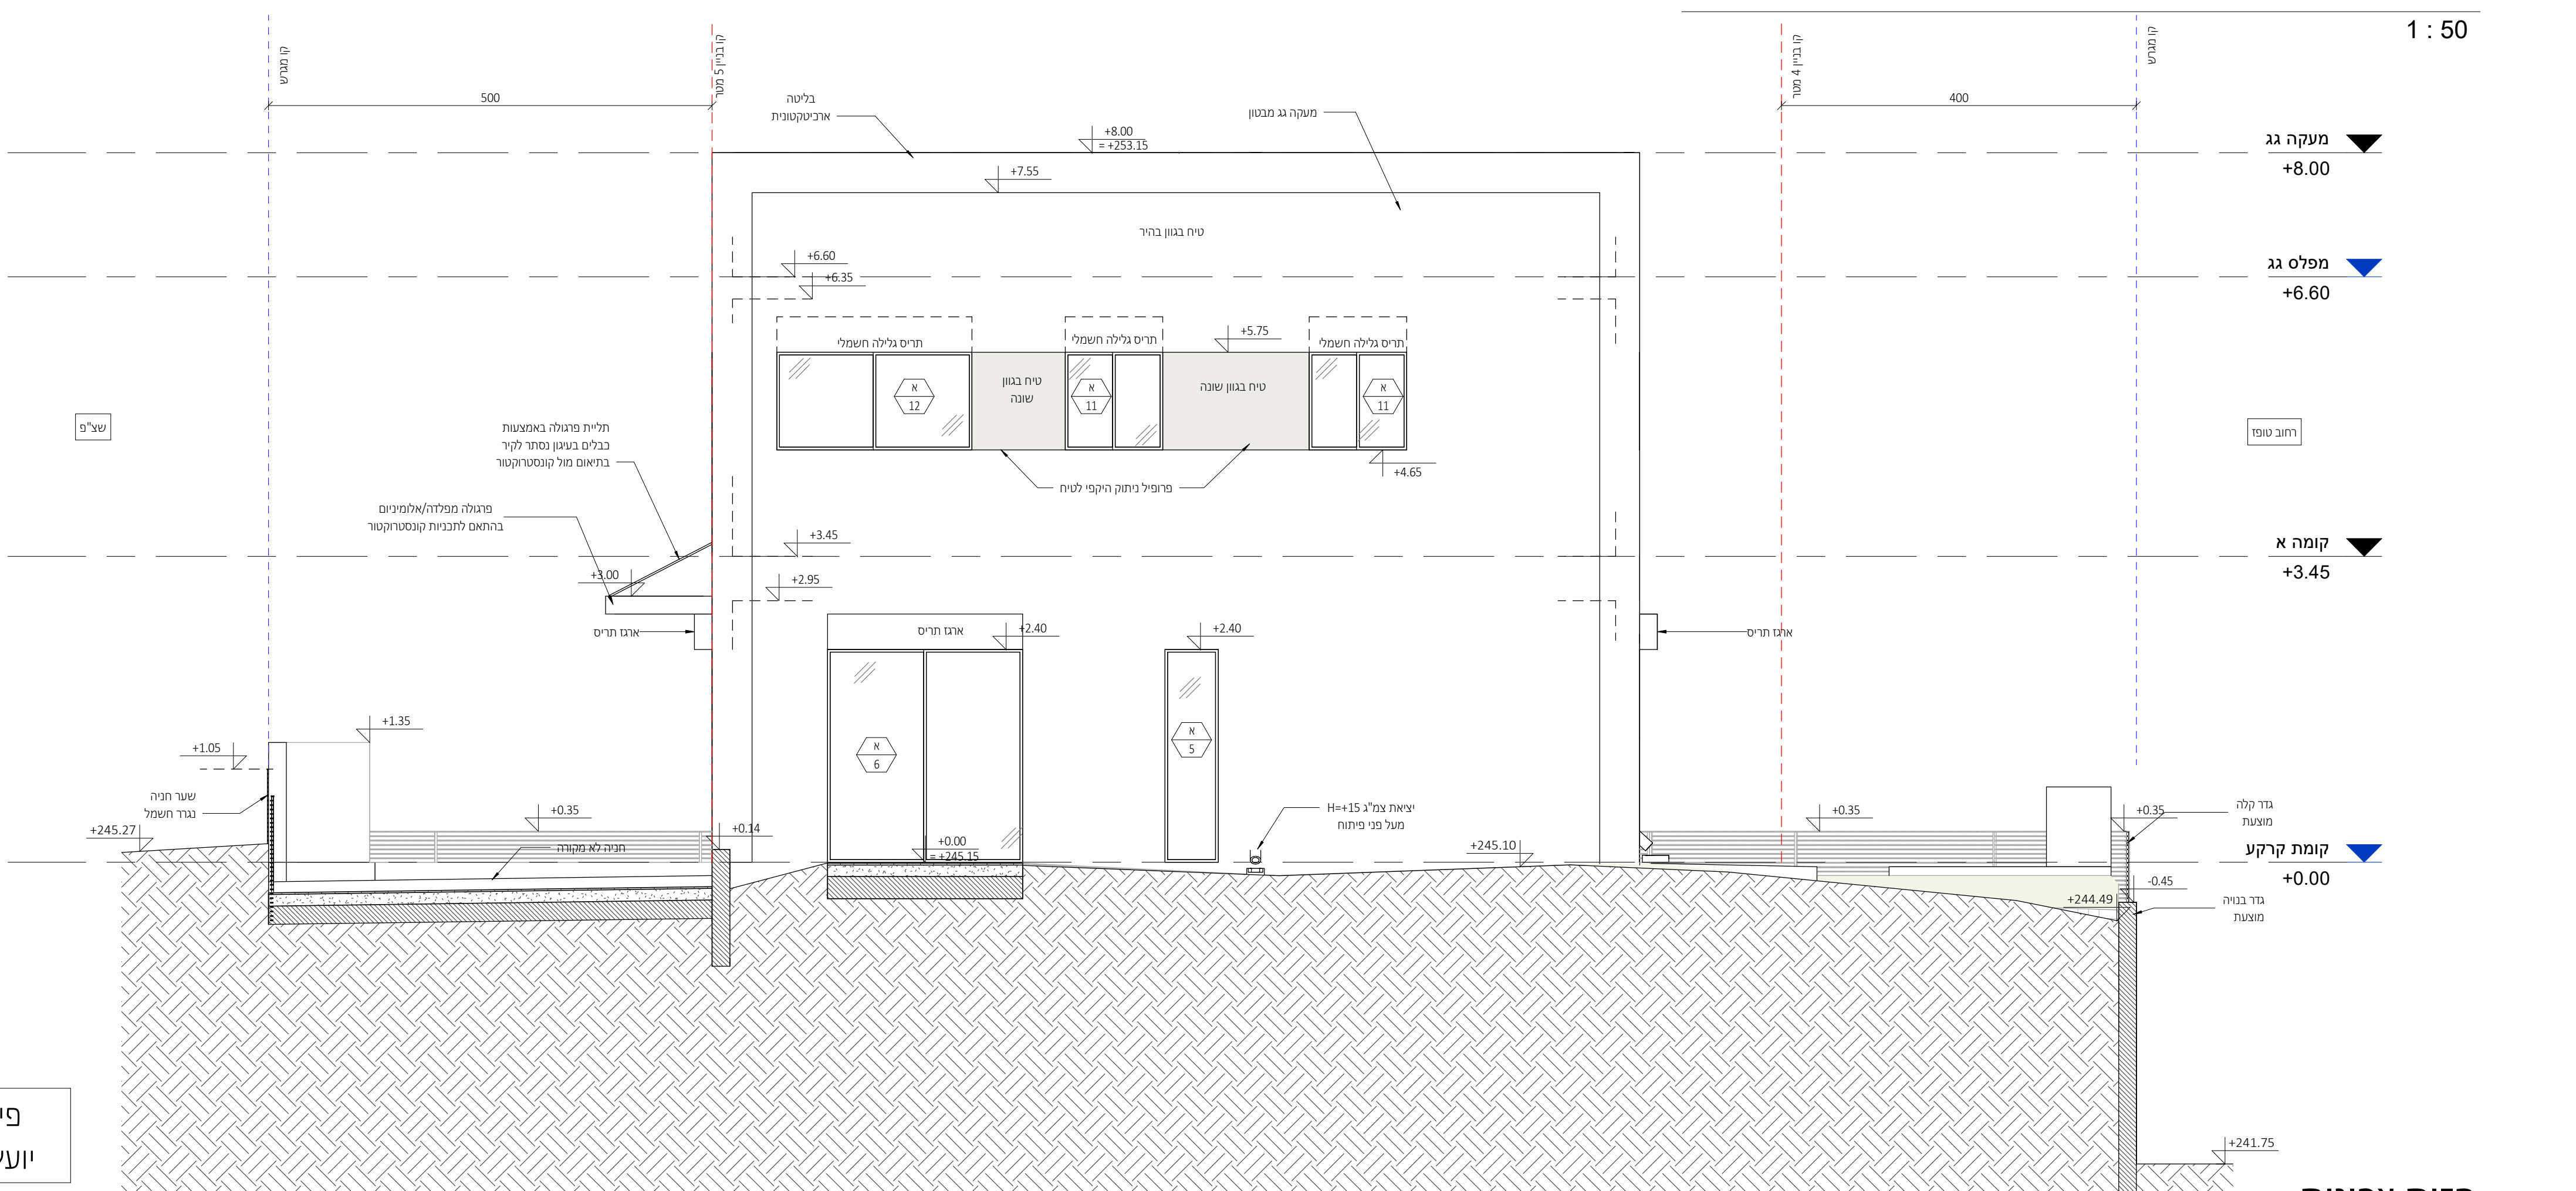

פיתוח נוף עפ"י תוכניות
יועץ נוף ראה פירוט בנפרד

חזית צפונית

1 : 50

מִתְכַּנְנִים:	
בִּיהוּל פְּרוּקִיט	
מֵהִיסוּד - בֶּן סוֹלוֹמוֹן	
פִּיקוּחַ	
מֵהִיסוּד - בֶּן סוֹלוֹמוֹן	
קוֹנְסֵטְרוֹקְצִיָּה	
עֶרֶן שִׁילֵר	
מִזִּיג אוֹוִיר	
אִיל אֶדֶר מֵהֵנְדָסִים וְיוֹעֲצִים בַּע"מ	
אִינְסְטֵלְצִיָּה	
אִיתָן אֶלְמָסִי	
חֲשֶׁמֶל	
אִיתָן בָּסִיס	
אַלְמִינִיּוֹם	
נוֹף	
נְתִי בְלוּקָא	
חֲשֶׁמֶל חֶכֶם	
חִימוֹם רֶצֶת רַפְּתִי	
אִטּוֹם	
צִבִּי טֵל	
אֶקוֹסְטִיקָה	
מַעֲלִיּוֹת	
קֶרְקֶע וְבִיסוֹס	
דִּיה הֵנְדָסֶת קֶרְקֶע וְבִיסוֹס	
רִשּׁוֹן	

הרעות
 הרעות היא קלרועה של עובדות והוצגתן
 כהוכחה להכחשה של עובדות אחרות.
 ההרעות היא כלי בידור המיועד לציבור
 רחב, ולכן היא נעזרת בשימוש במונחים
 מדעיים, אך לרוב היא איננה מדעית.
 ההרעות היא כלי בידור המיועד לציבור
 רחב, ולכן היא נעזרת בשימוש במונחים
 מדעיים, אך לרוב היא איננה מדעית.
 ההרעות היא כלי בידור המיועד לציבור
 רחב, ולכן היא נעזרת בשימוש במונחים
 מדעיים, אך לרוב היא איננה מדעית.

[illegible]


אדריכלות	
CLIENT NAME:	המסרן
קבוצת רכישה נופיה	
PROJECT NAME:	הפרויקט
נופיה - מגרש 23	
DRAWING NAME:	התקציר
חזיתות 1	
SHEET NUMBER:	פרגליון
A3-2-200	
CALL:	ענה מידון:
1 : 50	EDITION:
TATUS:	מסמס
למכר	
נבדק עיני:	יורד:
DATE:	22.09.25
	יורד:

מתכונים:

ניהול פרויקט
מהיסוד - בן סולמון
פיקוח
מהיסוד - בן סולמון
קונסטרוקציה
ערן שילר
מיזוג אוויר
אייל ארז מהנדסים ויועצים בע"מ
אינסטלציה
איתן אלמסי
חשמל
איתן בסיס
אלומיניום
נוף
נתי בלוקא
חשמל חכם
חימום תת רצפתי
איטום
צבי טל
אקוסטיקה
מעליות
קרקע וביסוס
דיה הנדסת קרקע וביסוס
רישוי

[illegible][illegible]

אדריכלות

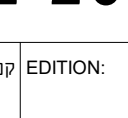
CLIENT NAME:		הפרויקט:	
PROJECT NAME:		הפרויקט:	
23 מגרש -		סמל הקרקע:	
DRAWING NAME:		סמל הקרקע:	
2 חזיתות		הפרויקט:	
SHEET NUMBER:		הפרויקט:	
A3-2-201		הפרויקט:	
SCALE:	קנה מידה:	EDITION:	הדורה:
1 : 50	סטטוס		1
STATUS:	למכר		
נבדק ע"י:		דפוס ע"י:	
DATE:	22.09.25	היום:	

NeumanHaynerArchitects


יומן חיינר אדריכלים
בית חירות 2, החדרים 209-9545842

office@nh-arch.com
www.nh-arch.com

פיתוח נוף עפ"י תוכניות
יועץ נוף ראה פירוט בנפרד

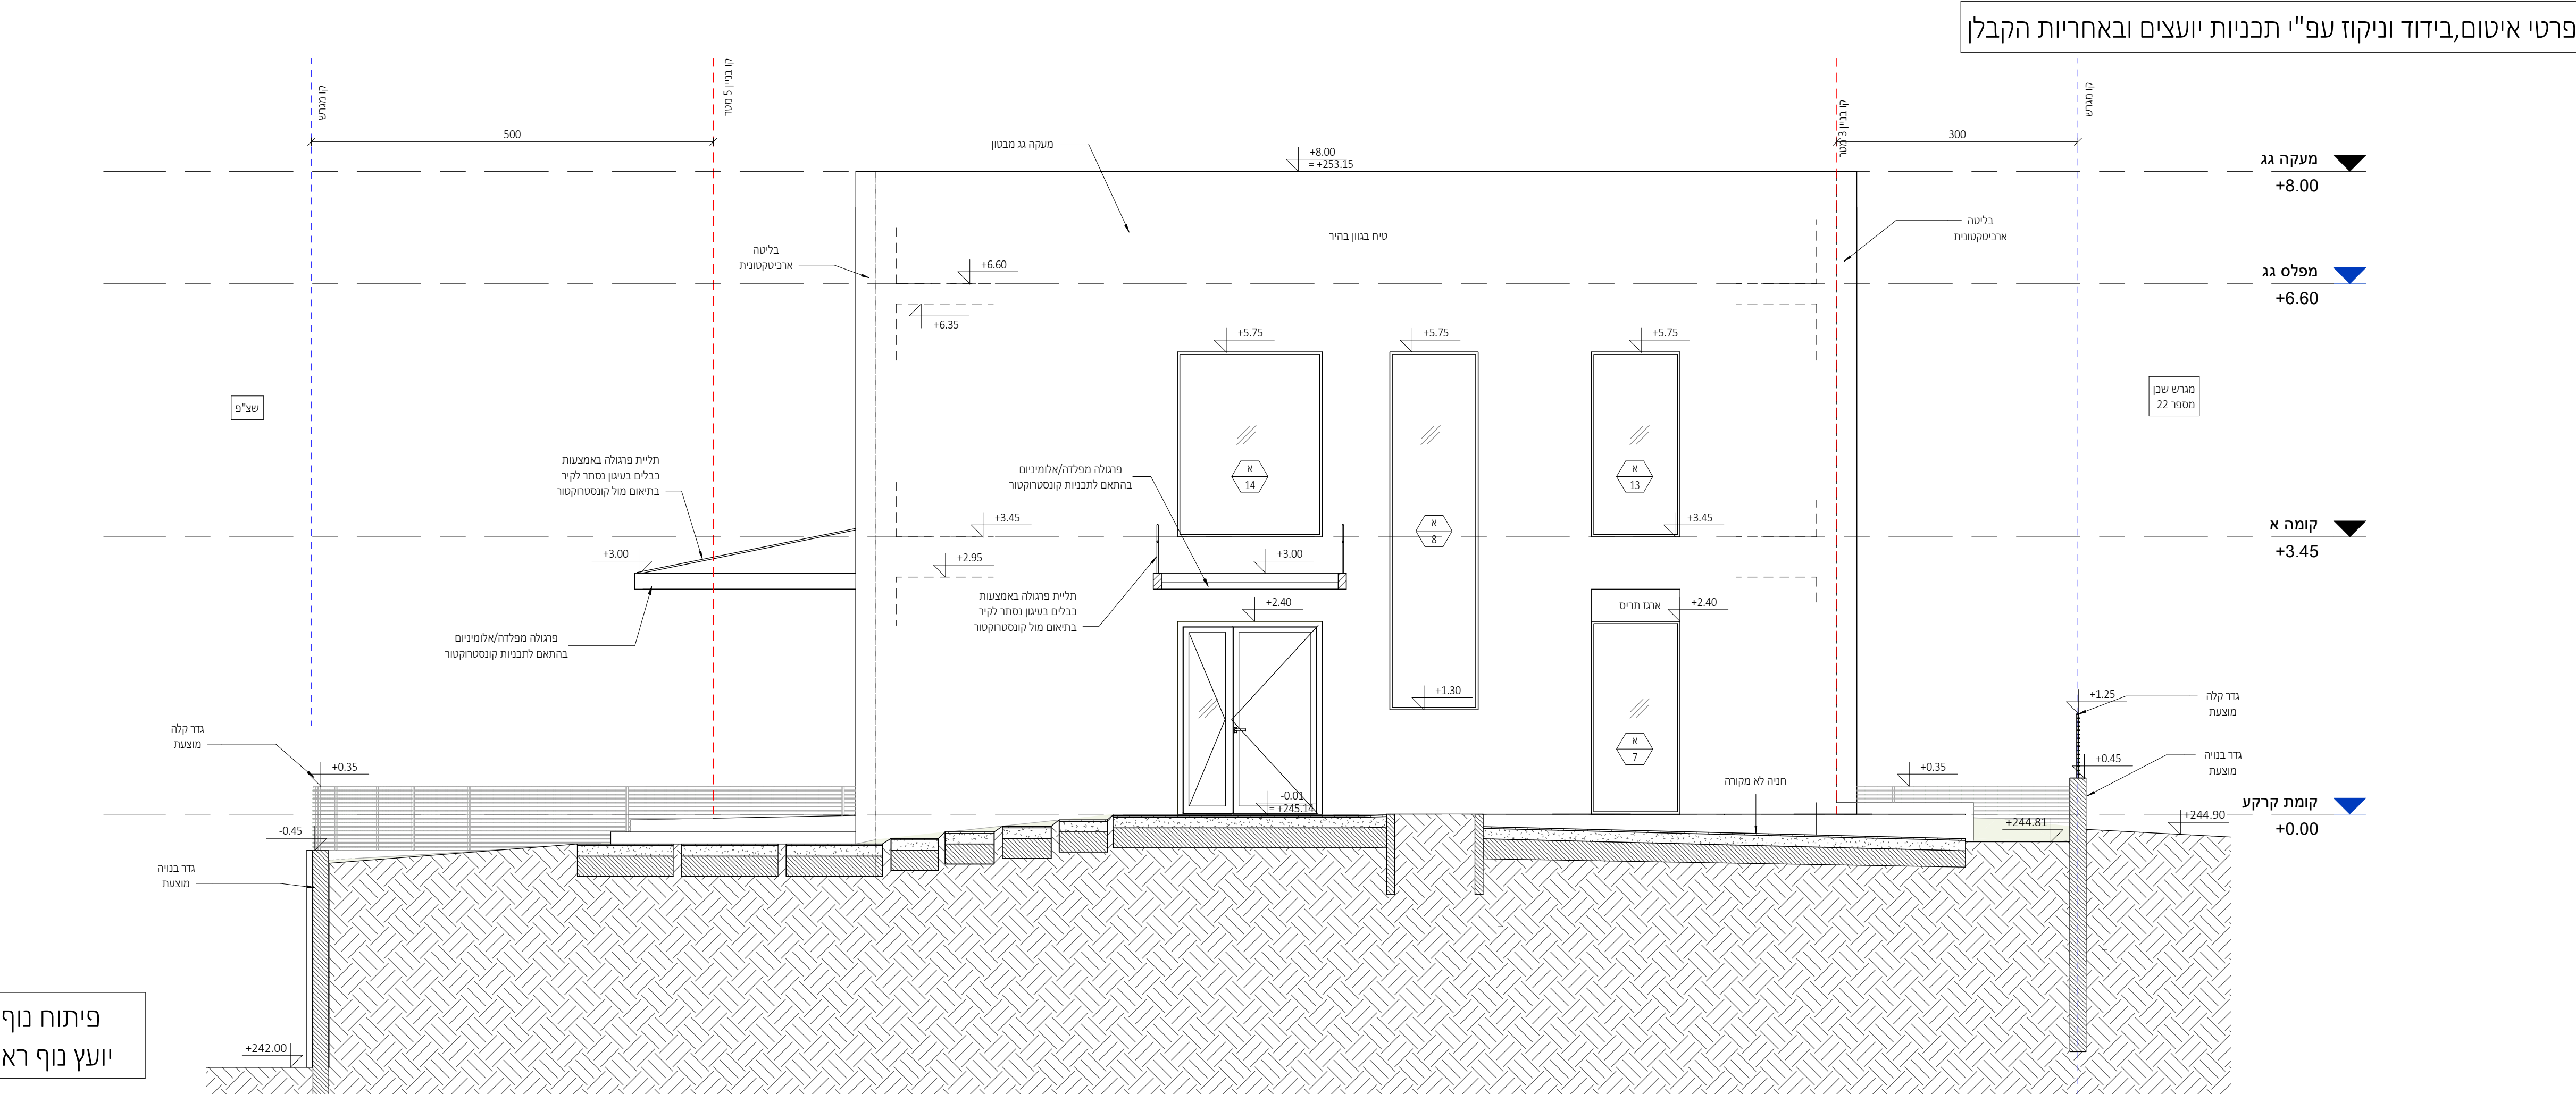

חזית מזרחית

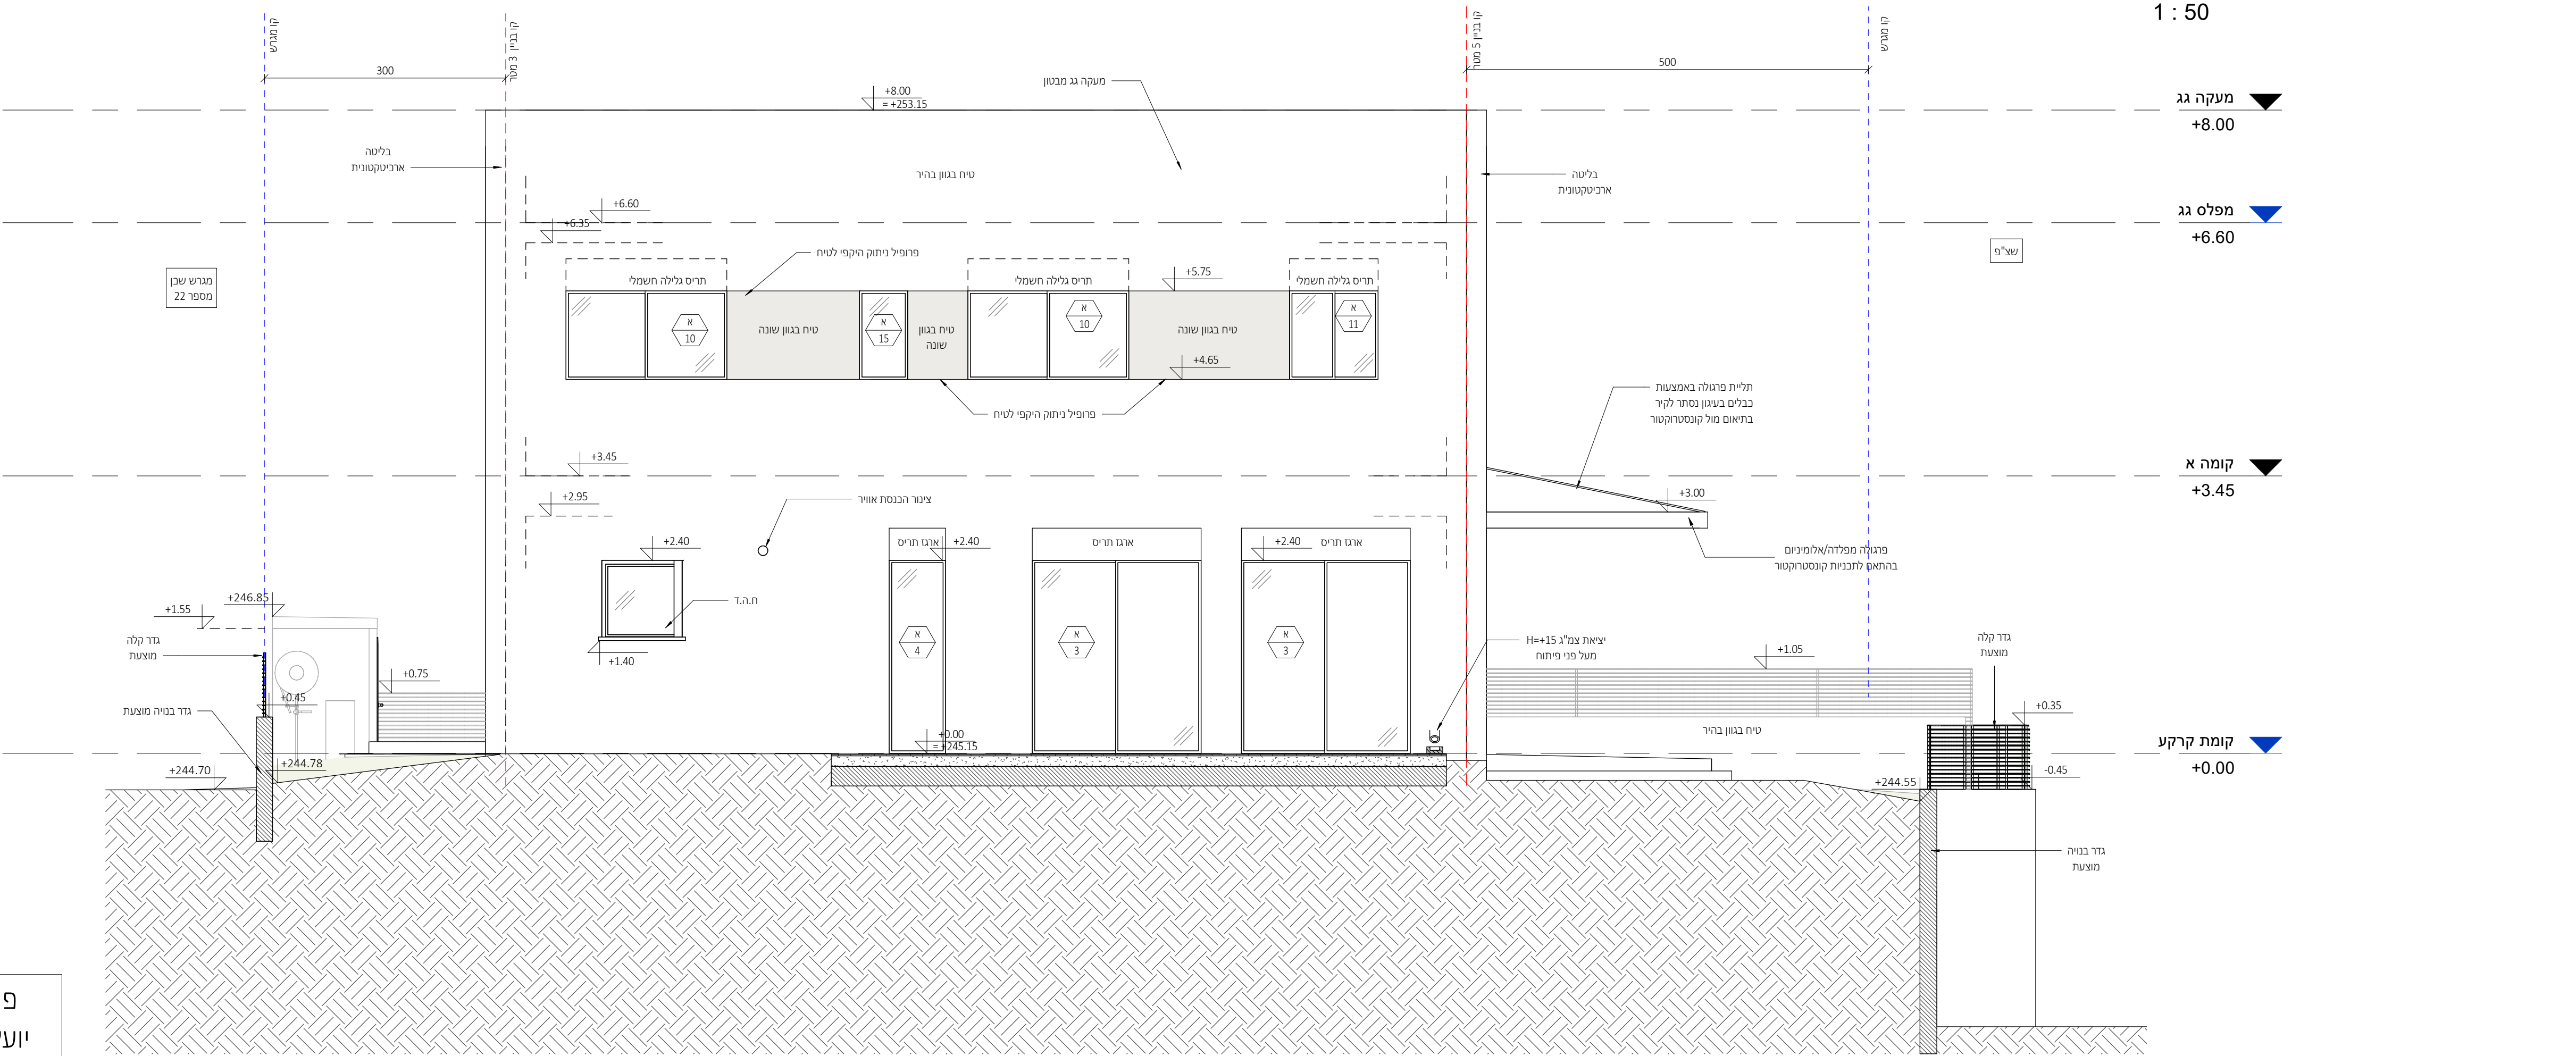

חזית מערבית

מתכונים:

ניהול פרויקט
מהיסוד - בן סולומון
פיקוח
מהיסוד - בן סולומון
קונסטרוקציה
ערן שילר
מיזוג אוויר
אייל ארז מהנדסים ויועצים בע"מ
אינסטלציה
איתן אלמסי
חשמל
איתן בסיס
אלומיניום
נוף
נתי בלוקא
חשמל חכם
חימום תת רצפתי
איטום
צבי טל
אקוסטיקה
מעליות
קרקע וביסוס
דיה הנדסת קרקע וביסוס
רישוי

[illegible]

מקרא קירות:

		
עמוד בסון	קיר בסון	קיר בלוק

[illegible]


אדריכלות

CLIENT NAME:		הפיקס: 054-5555555	
PROJECT NAME:		הפרויקט: 054-5555555	
קבוצת רכישה נופיה			
נופיה - מגרש 23			
DRAWING NAME:		שם התכנון: 054-5555555	
חתיכים			
SHEET NUMBER:		מספר גליון: 054-5555555	
A3-3-100			
SCALE:	קנה מידה:	EDITION:	חזרה:
1:50			
STATUS:	סטטוס:		
למכר			
	נבדק ע"י:		דפוס ע"י:
DATE:	22.09.25		תאריך:


NeumanHaynerArchitects

office@nh-arch.com
www.nh-arch.com

זכויות ייצור / ע"פ הנחיות עו"ד

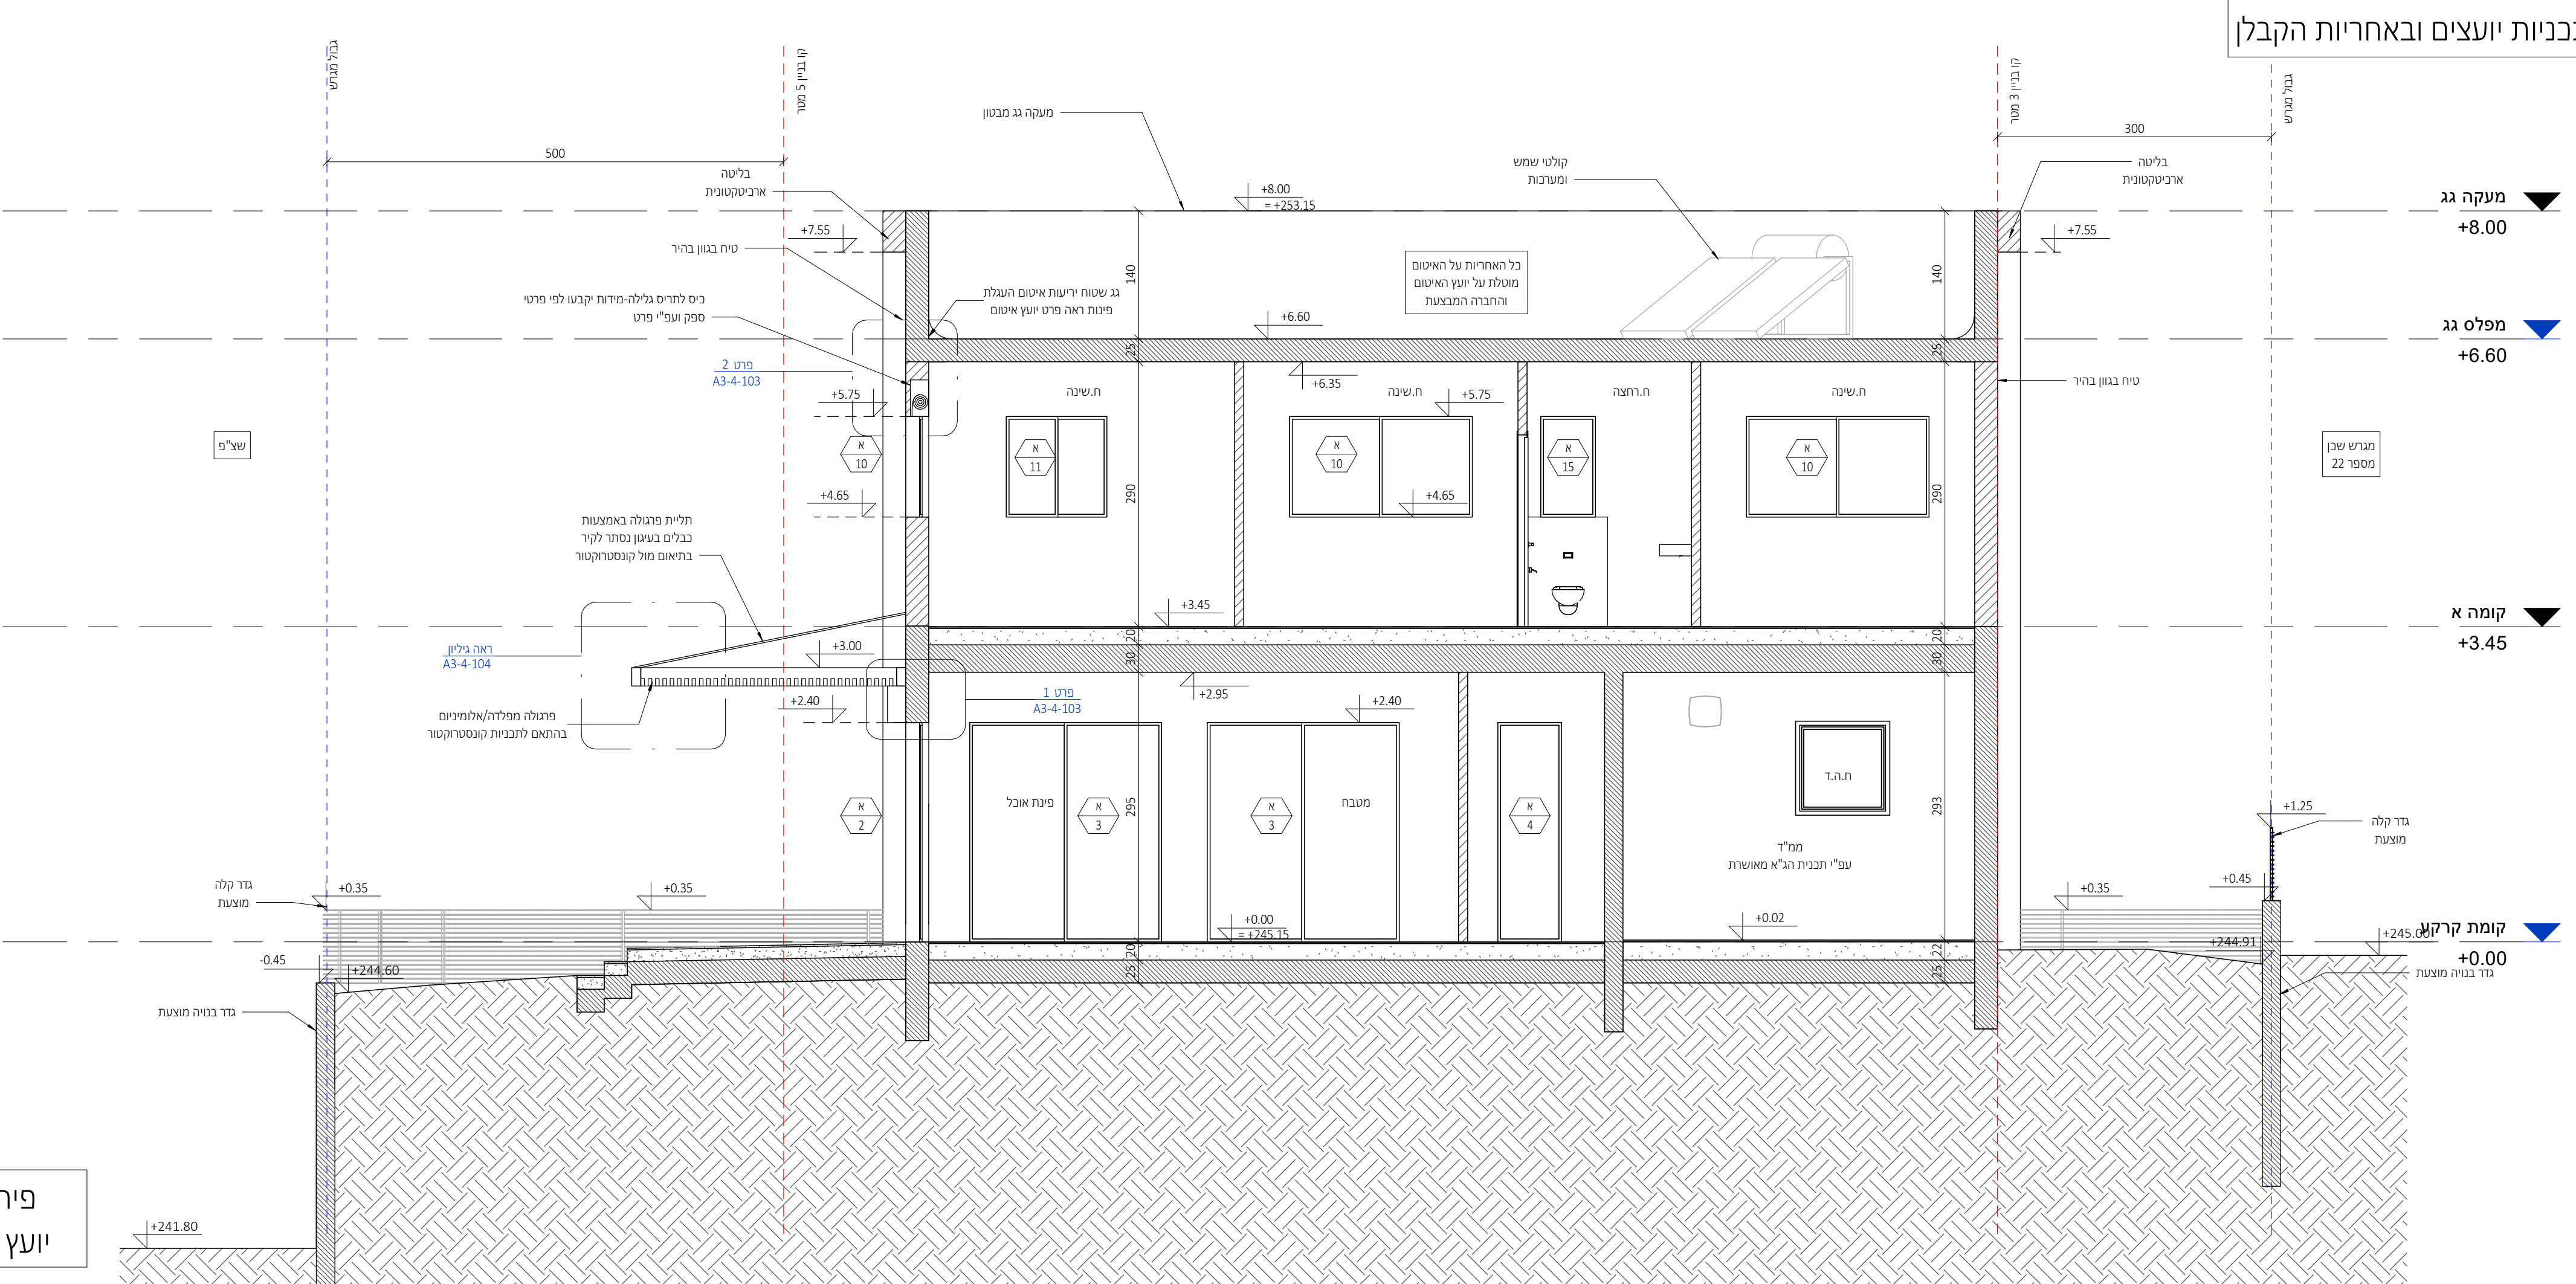

פיתוח נוף עפ"י תוכניות
יועץ נוף ראה פירוט בנפרד

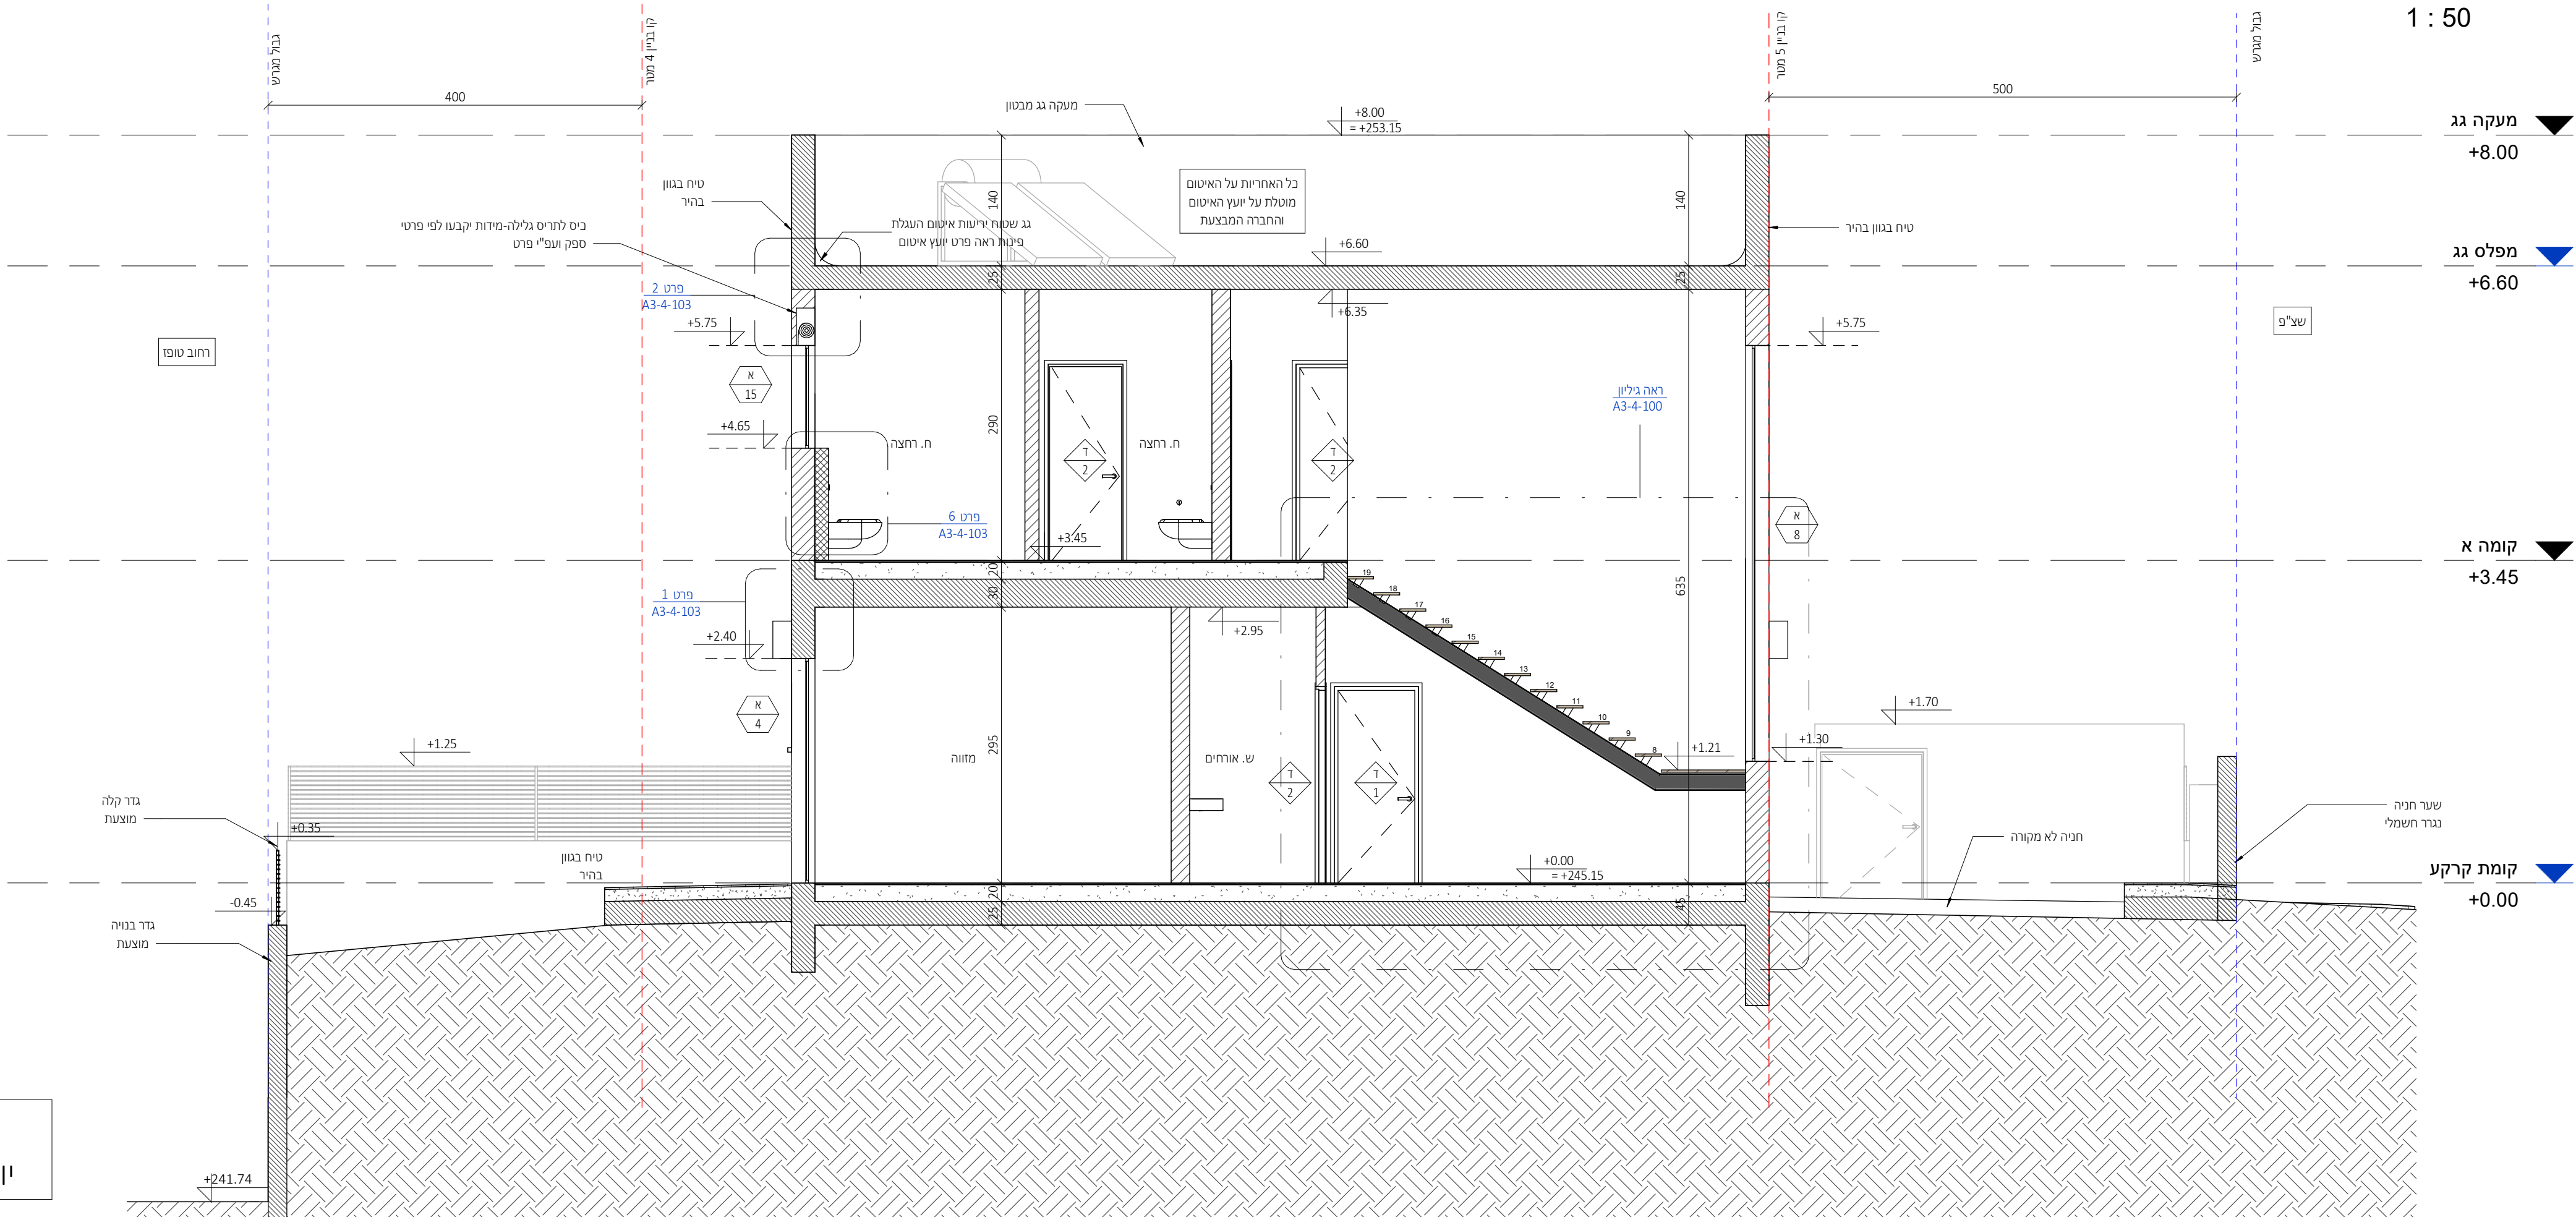

פיתוח נוף עפ"י תוכניות
יועץ נוף ראה פירוט בנפרד

חֵתֶּךָ א-א

1 : 50

מעקה גג 
+8.00

מפלוס גג
+6.60

קומה א 
+3.45

קומת קרקע 
+0.00

חתך ב-ב

1 : 50

ניהול פרויקט
מהיסוד - בן סולומון
פיקוח
מהיסוד - בן סולומון
קונסטרוקציה
ערן שילר
מיזוג אוויר
אייל ארז מהנדסים ויועצים בע"מ
אינסטלציה
איתן אלמסי
חשמל
איתן בסיס
אלומיניום
נוף
נתי בלוקא
חשמל חכם
חימום תת רצפתי
איטום
צבי טל
אקוסטיקה
מעליות
קרקע וביסוס
דיה הנדסת קרקע וביסוס
רישוי

[illegible][illegible]


CLIENT NAME:		המחיר: 0	
PROJECT NAME:		הפרויקט: 0	
קבוצת רכישה נופיה			
נופיה - מגרש 23			
DRAWING NAME:		השם: 0	
גליון מדרגות			
SHEET NUMBER:		המספר: 0	
A3-4-100			
SCALE:	קנה מידה:	EDITION:	הדורה:
As indicated			
STATUS:	סטוס:		
למכר		הדפוס: 0	
בדק עיין:			
DATE:	22.09.25		תאריך:




NeumanHaynerArchitects

office@nh-arch.com
www.nh-arch.com


זכויות ייצור / ע"פ הנחיות עו"ד

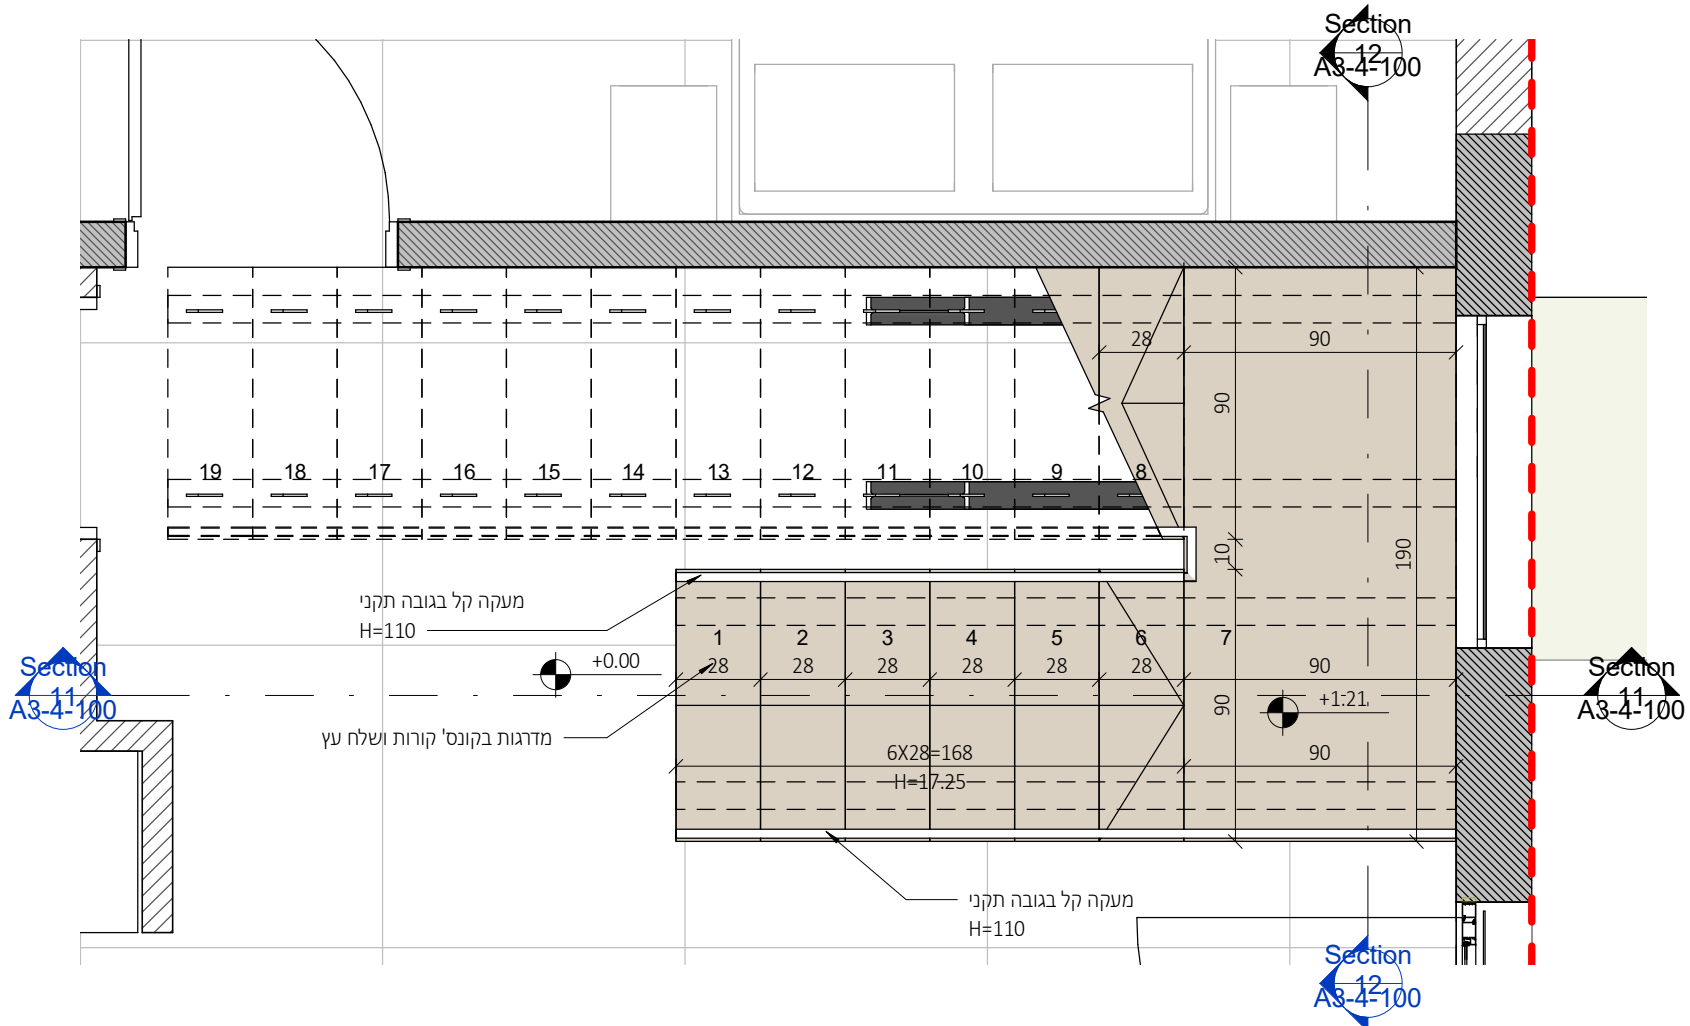


1 : 25

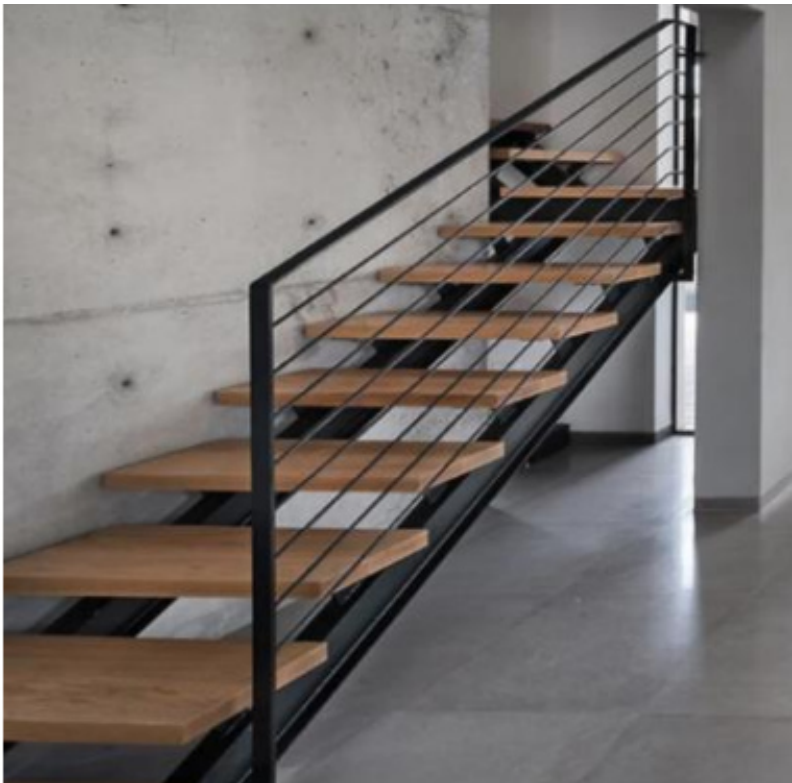

תמונה להמחשה בלבד

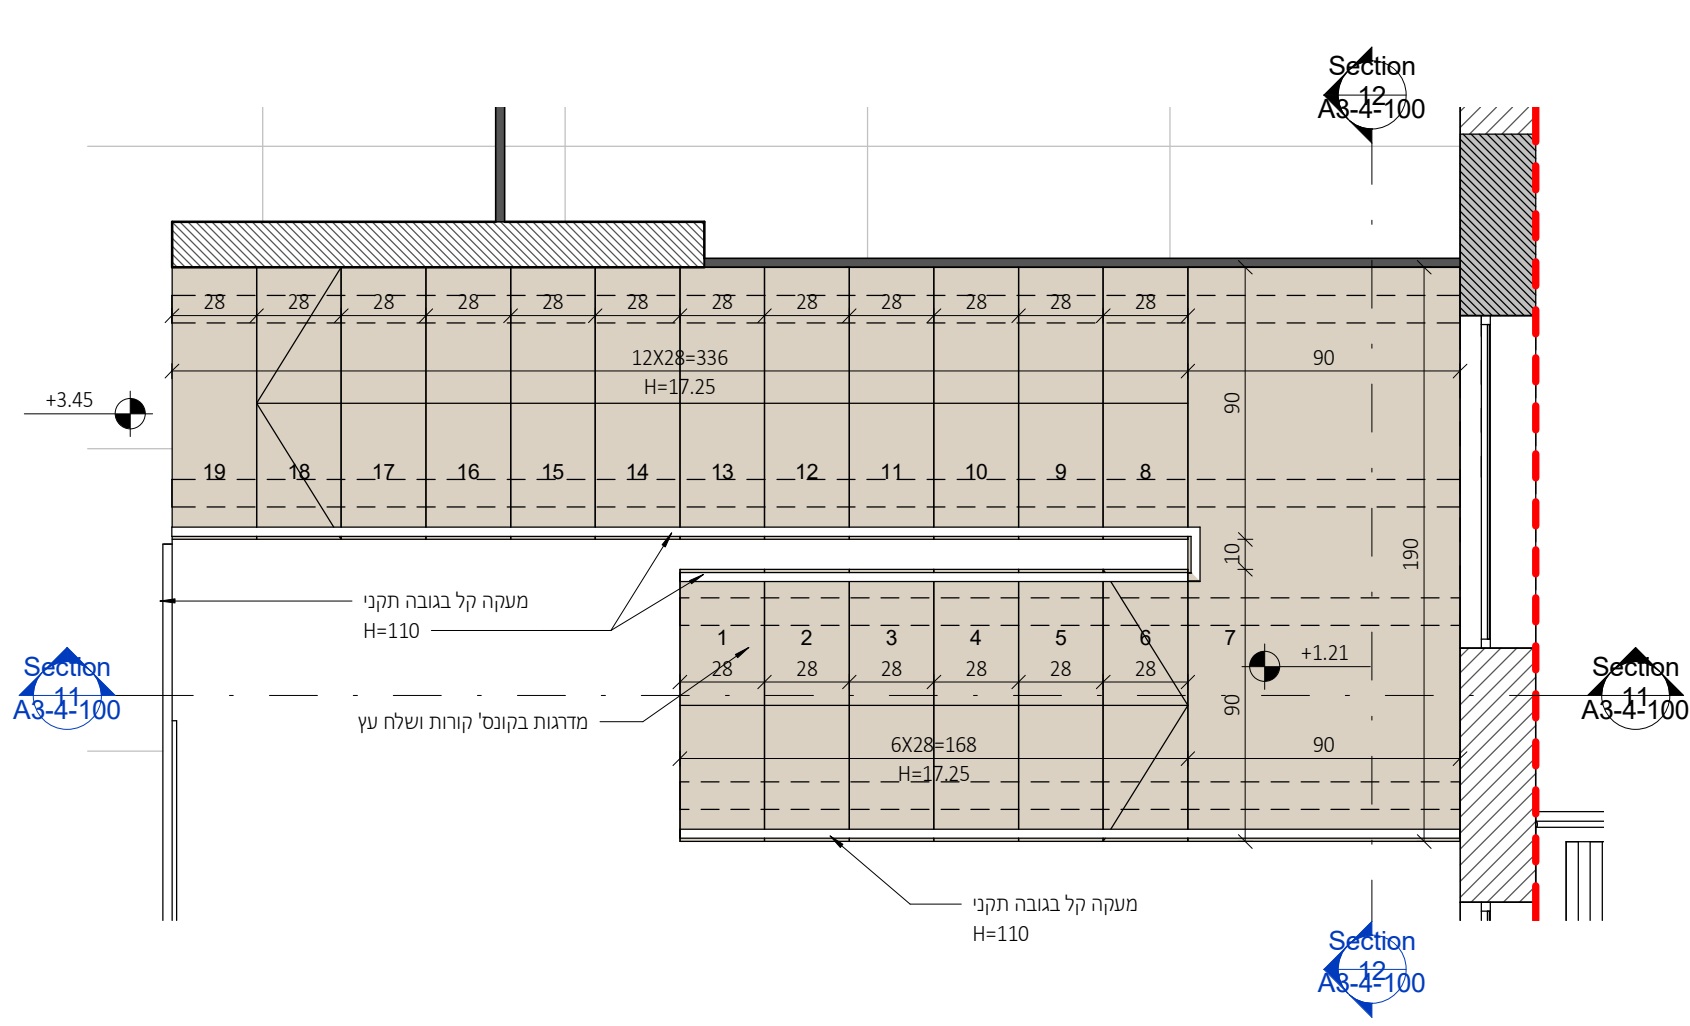

1 : 25

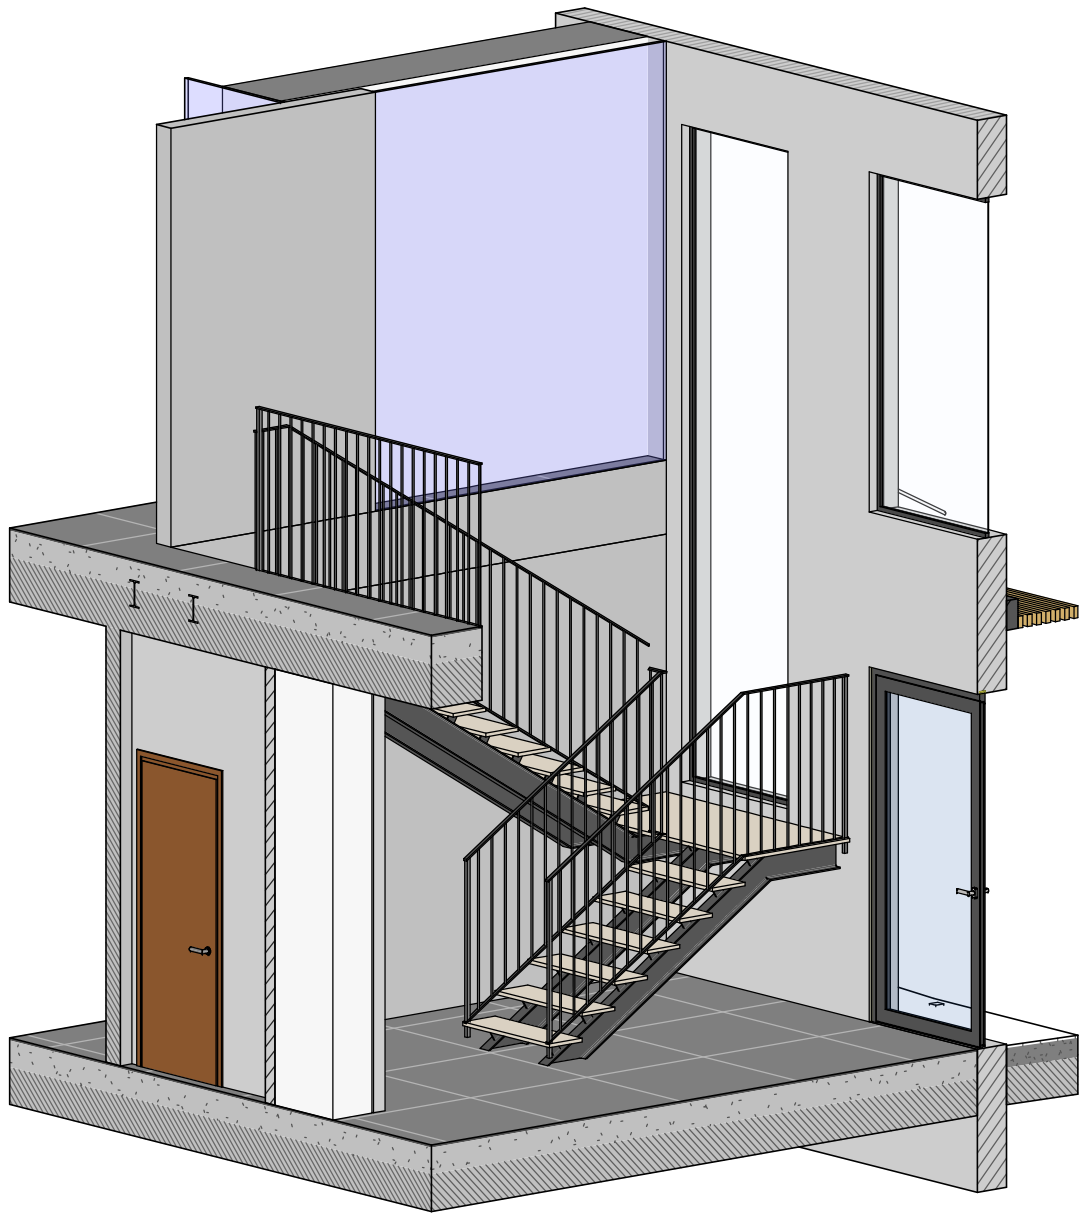


דגם נבחר


מדרגות קלות - מפרט פרימיום

על הקבלן לשלוח S.D לאישור אדריכל


יש לבצע התאמה לפרט לאחר בחירת חיפוי המדרגות*

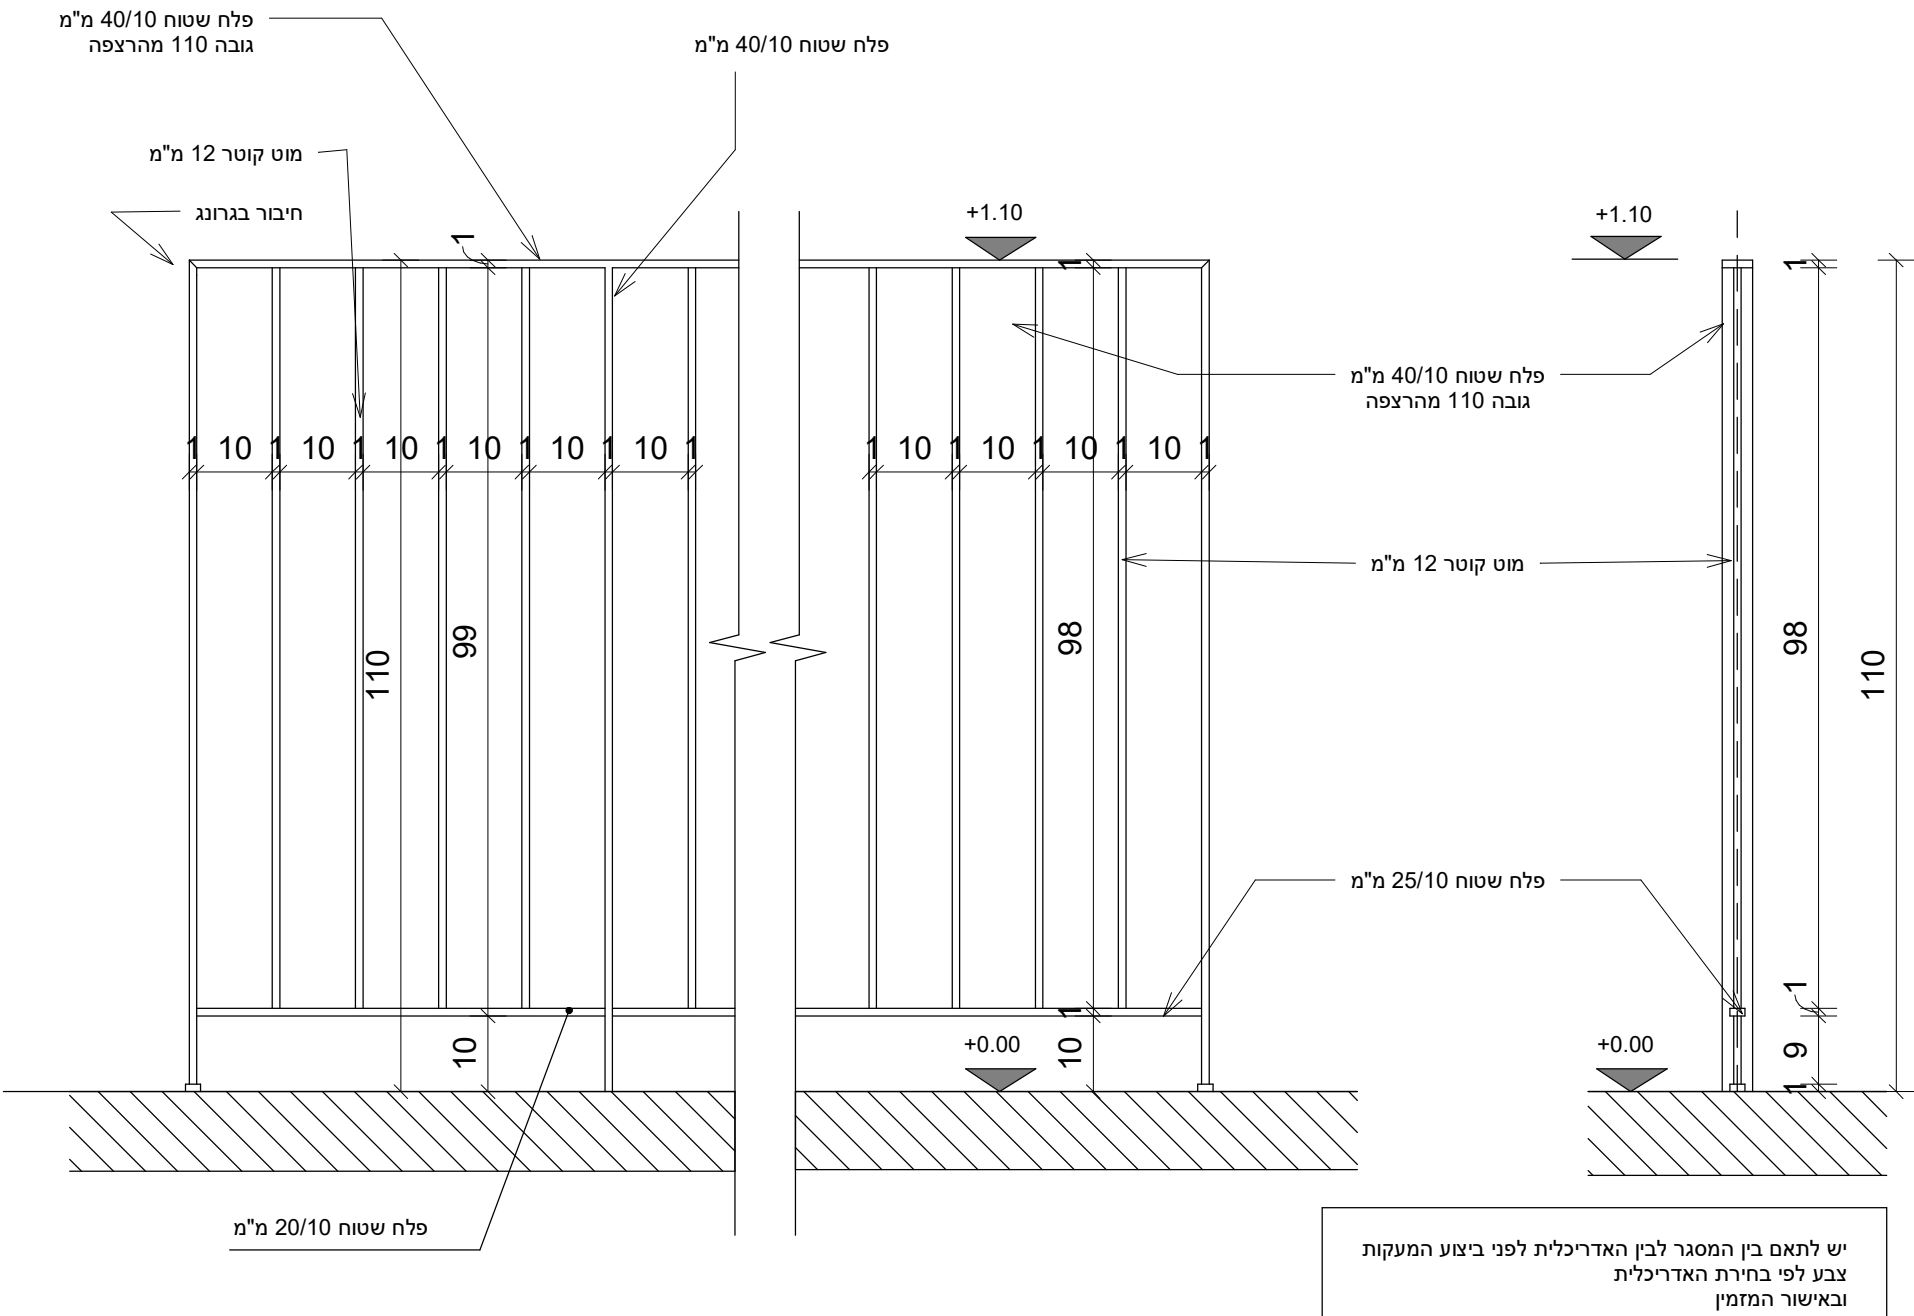

1 : 10

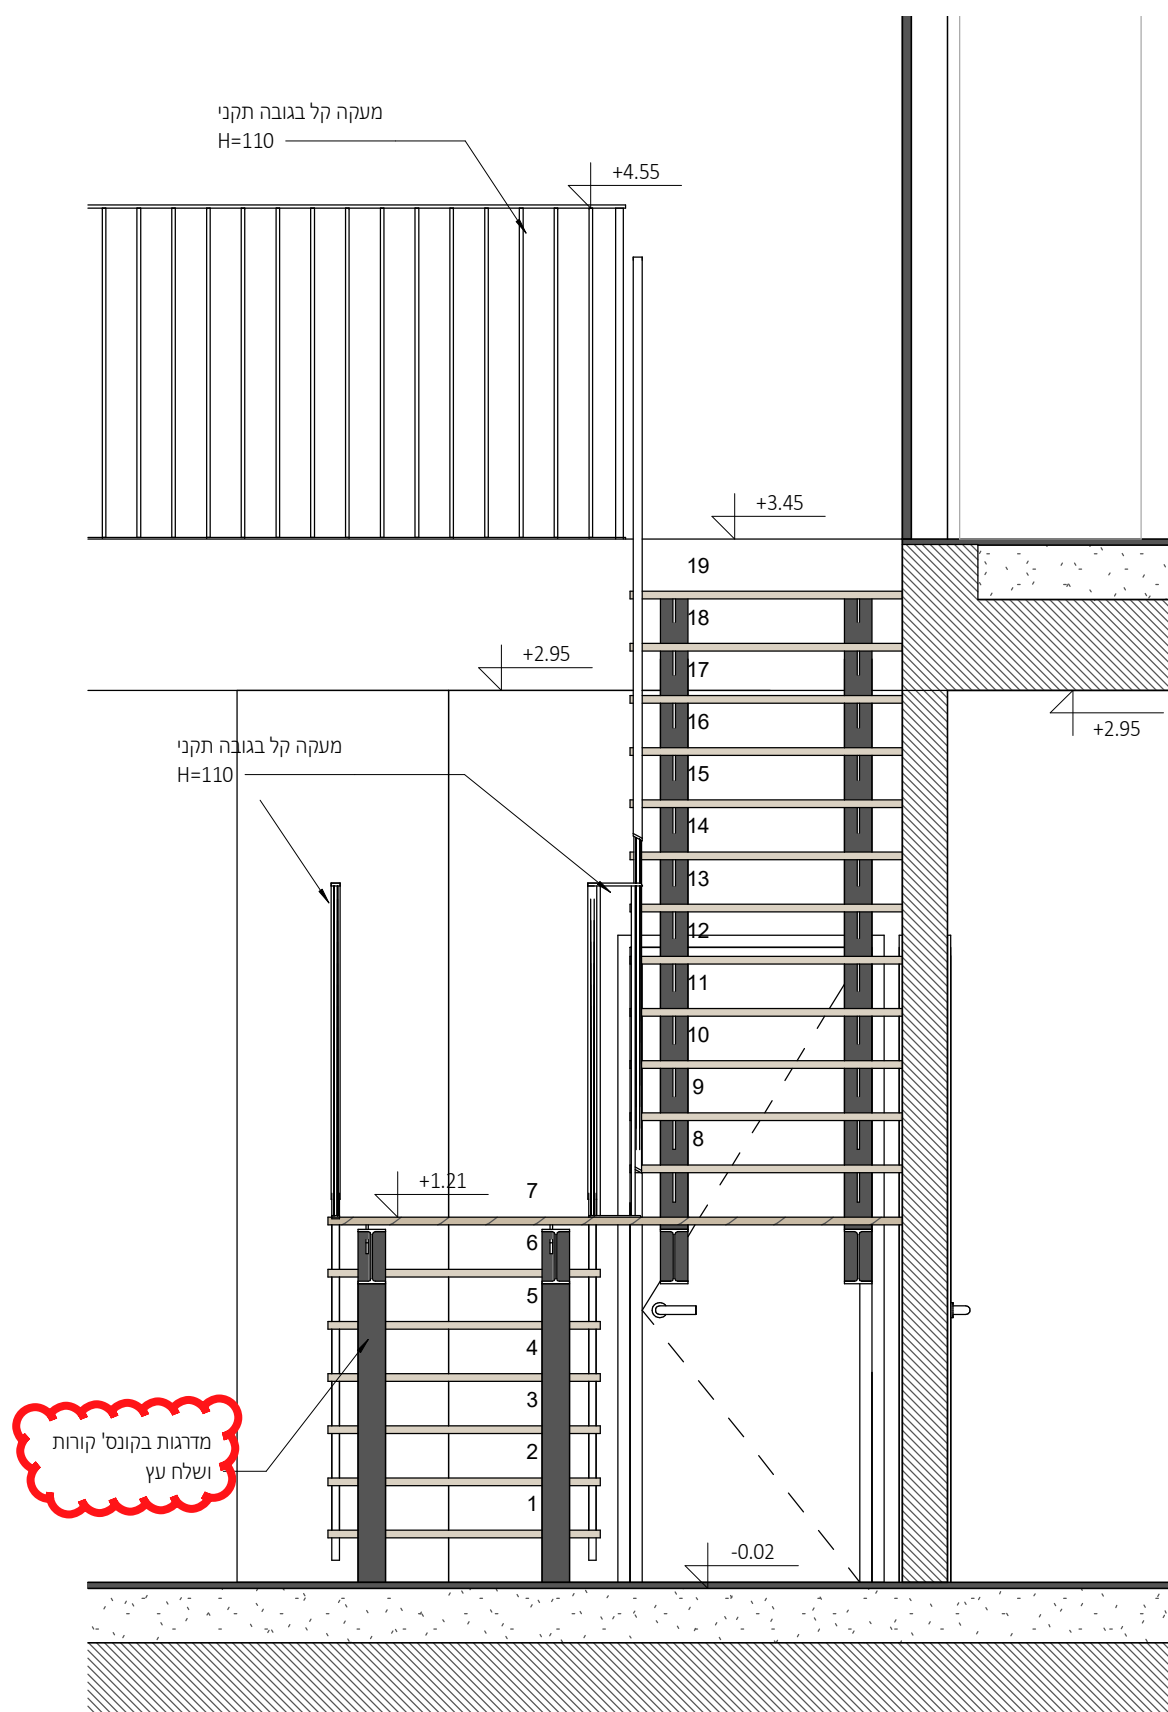

1 : 25

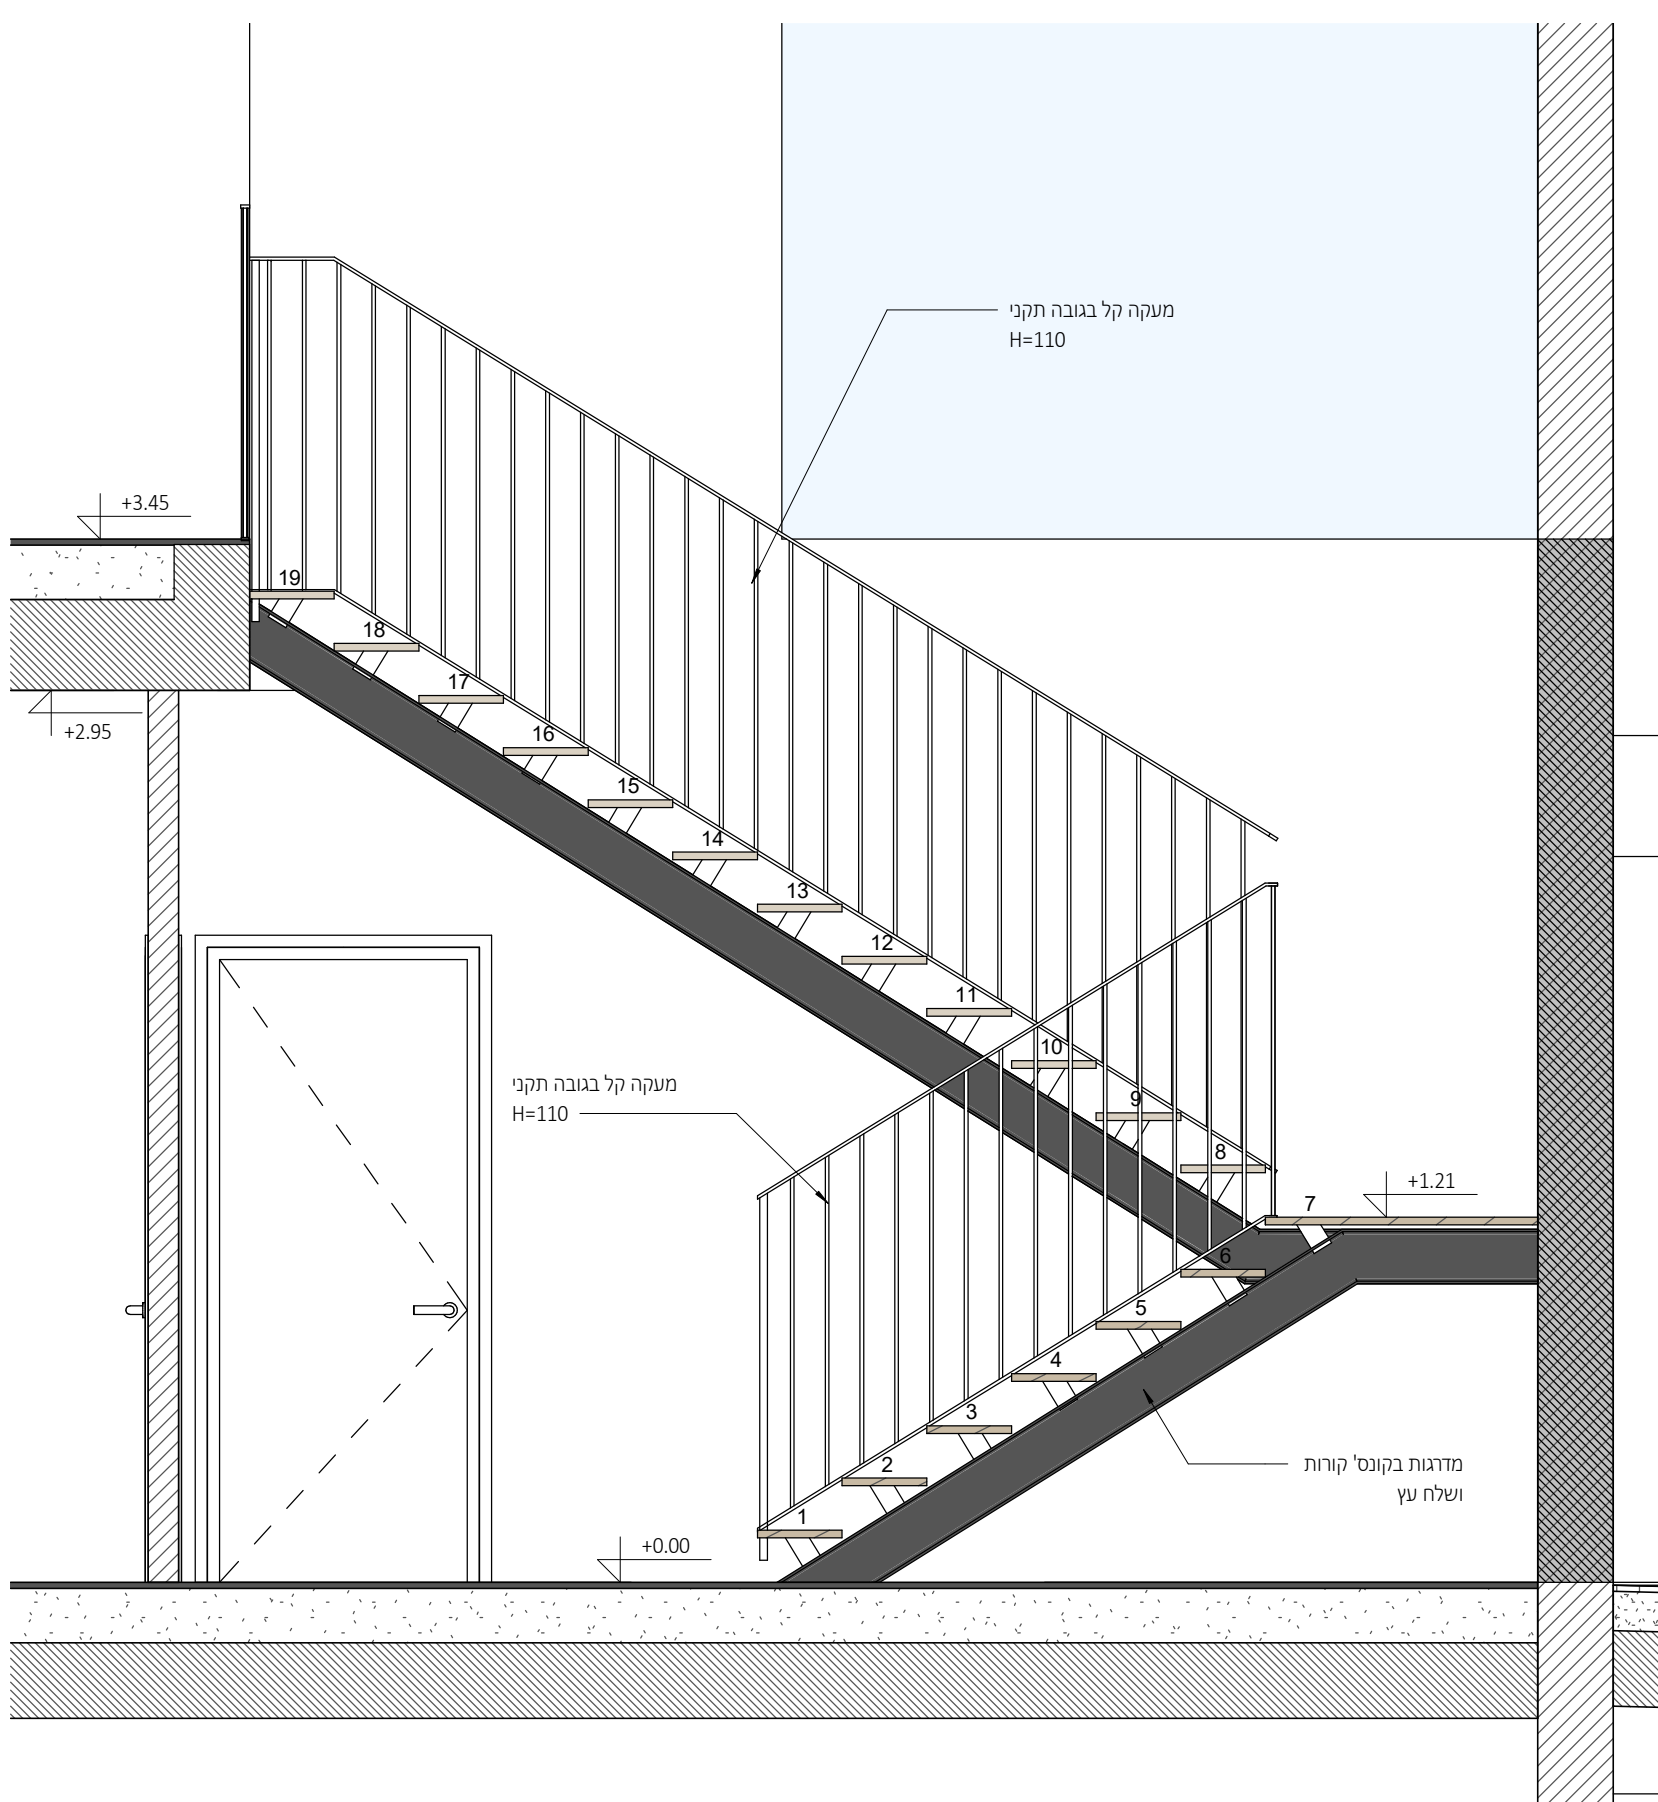


1 : 25


ניהל פרויקט
מהיסוד - בן סולומון
פיקוח
מהיסוד - בן סולומון
קונסטרוקציה
ערן שילר
מיזוג אוויר
אייל ארז מהנדסים ויועצים בע"מ
אינסטלציה
איתן אלמסי
חשמל
איתן בסיס
אלומיניום
נוף
נתי בלוקא
חשמל חכם
חימום תת רצפתי
איטום
צבי טל
אקוסטיקה
מעליות
קרקע וביסוס
דיה הנדסת קרקע וביסוס
רישיון

[illegible]

PROJECT NAME:		ה פרויקט:	
23 מגרש -		נופיה -	
DRAWING NAME:		שם הנדסה:	
פרטים			
SHEET NUMBER:		מספר העמוד:	
A3-4-103			
SCALE:	קנה מידה:	EDITION:	הדורה:
As indicated			
STATUS:	סטוס:		
למכר			
DATE:		תאריך:	
22.09.25			
Neuman-HaynerArchitects			
יוסוף חיינר אדריכלים חורד חמדס 2, בית חירות 09-9545842			
office@nh-arch.com www.nh-arch.com			

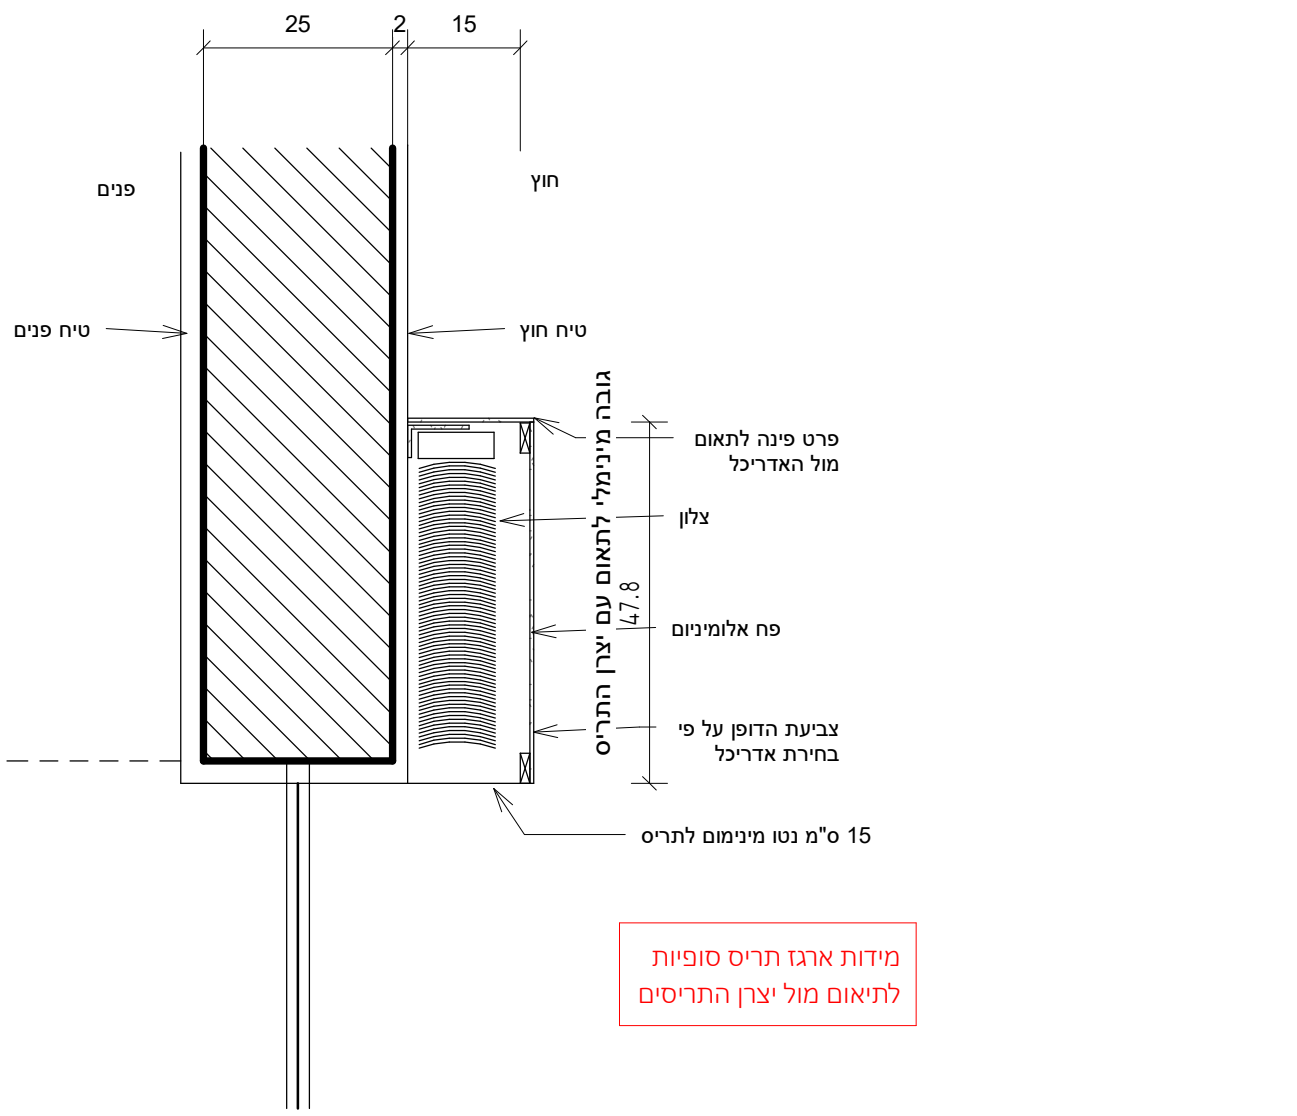


פרט 1 - כיס צלון חיצוני

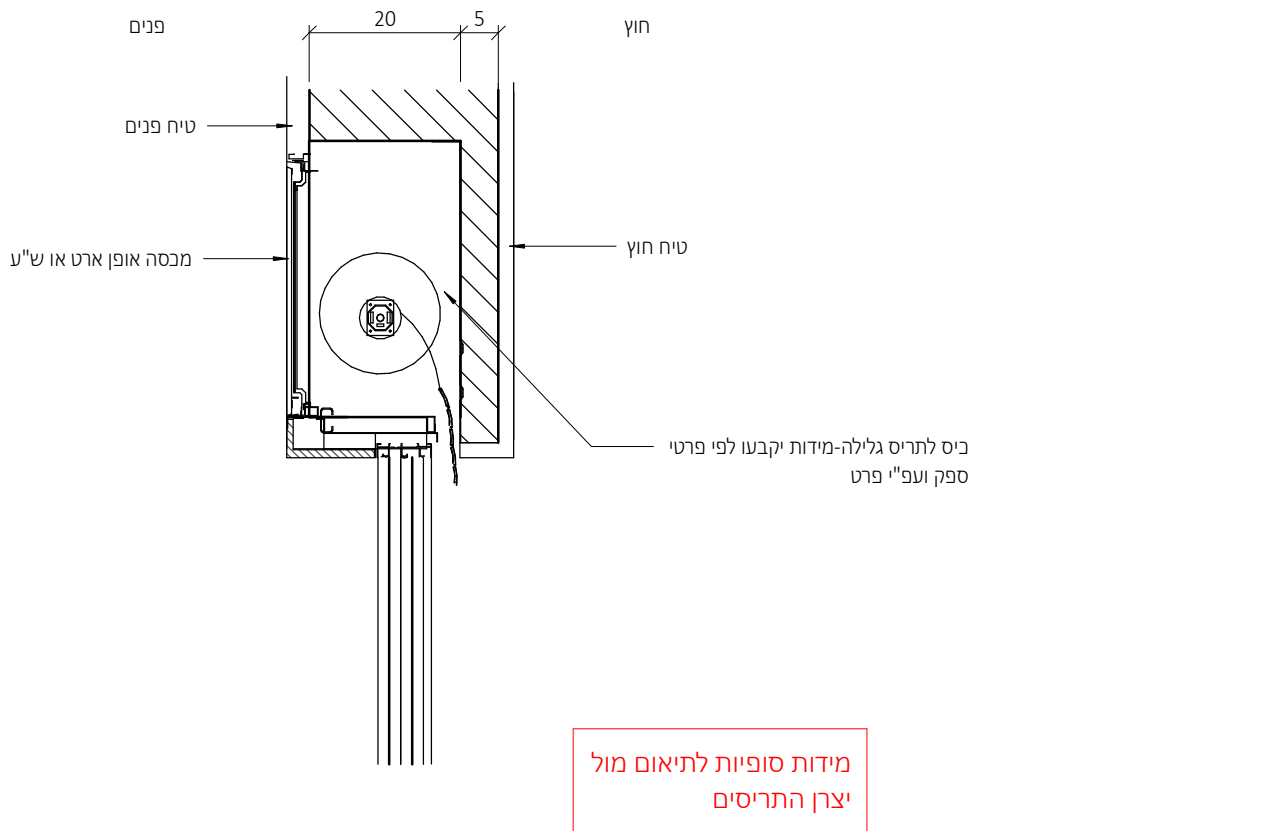


פרט 2 - תריס גלילה


1 : 10

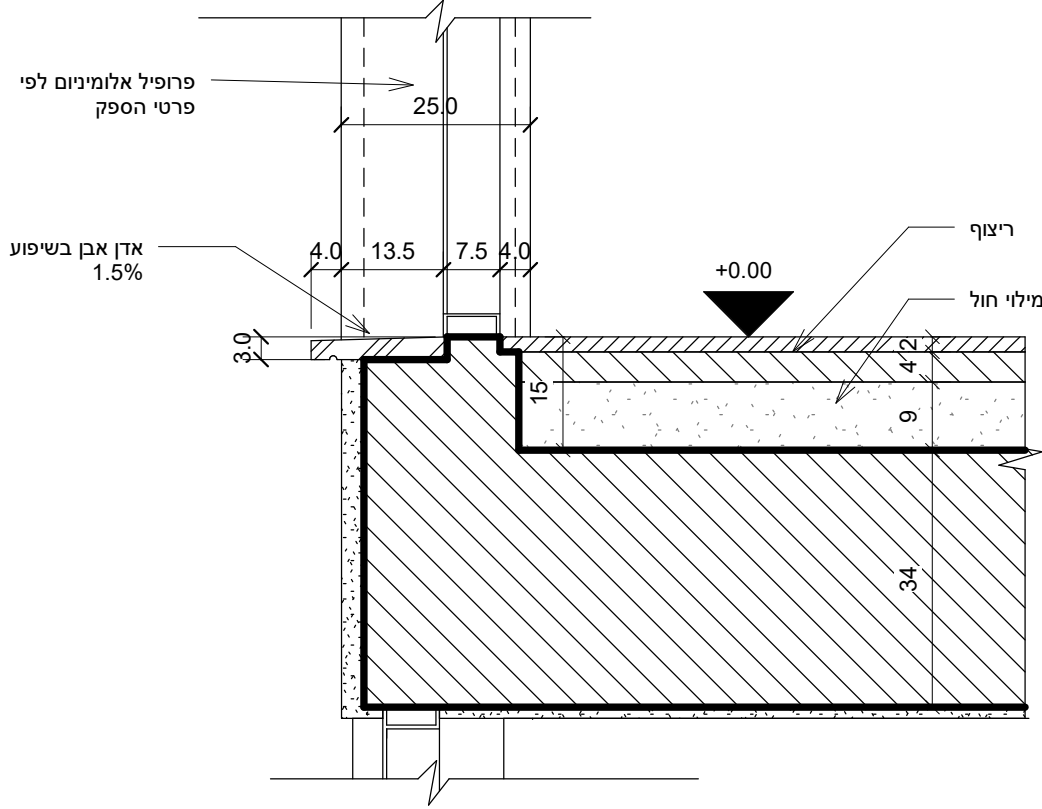

פרט ערני בלבד - פרט סופי מספק החלונות

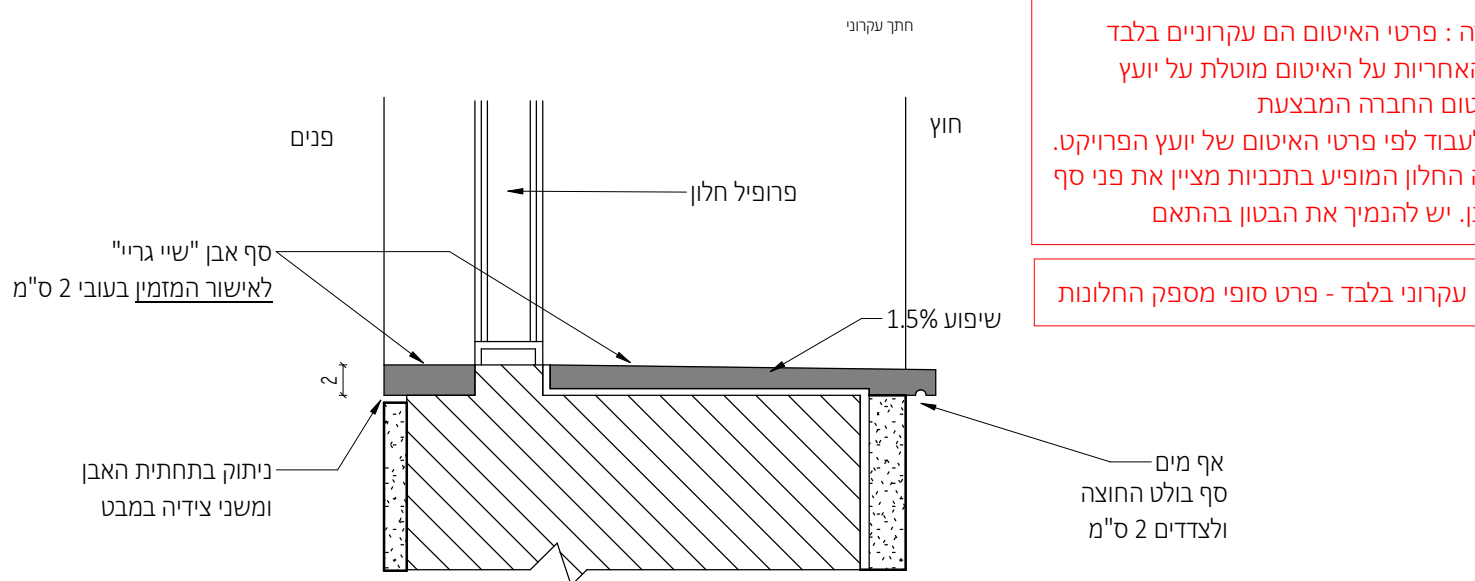
פרט 3 - מפגש חלון ורצפה
1 : 10

פרט 4 - חלון - פרט טיפוס י - סף חלון

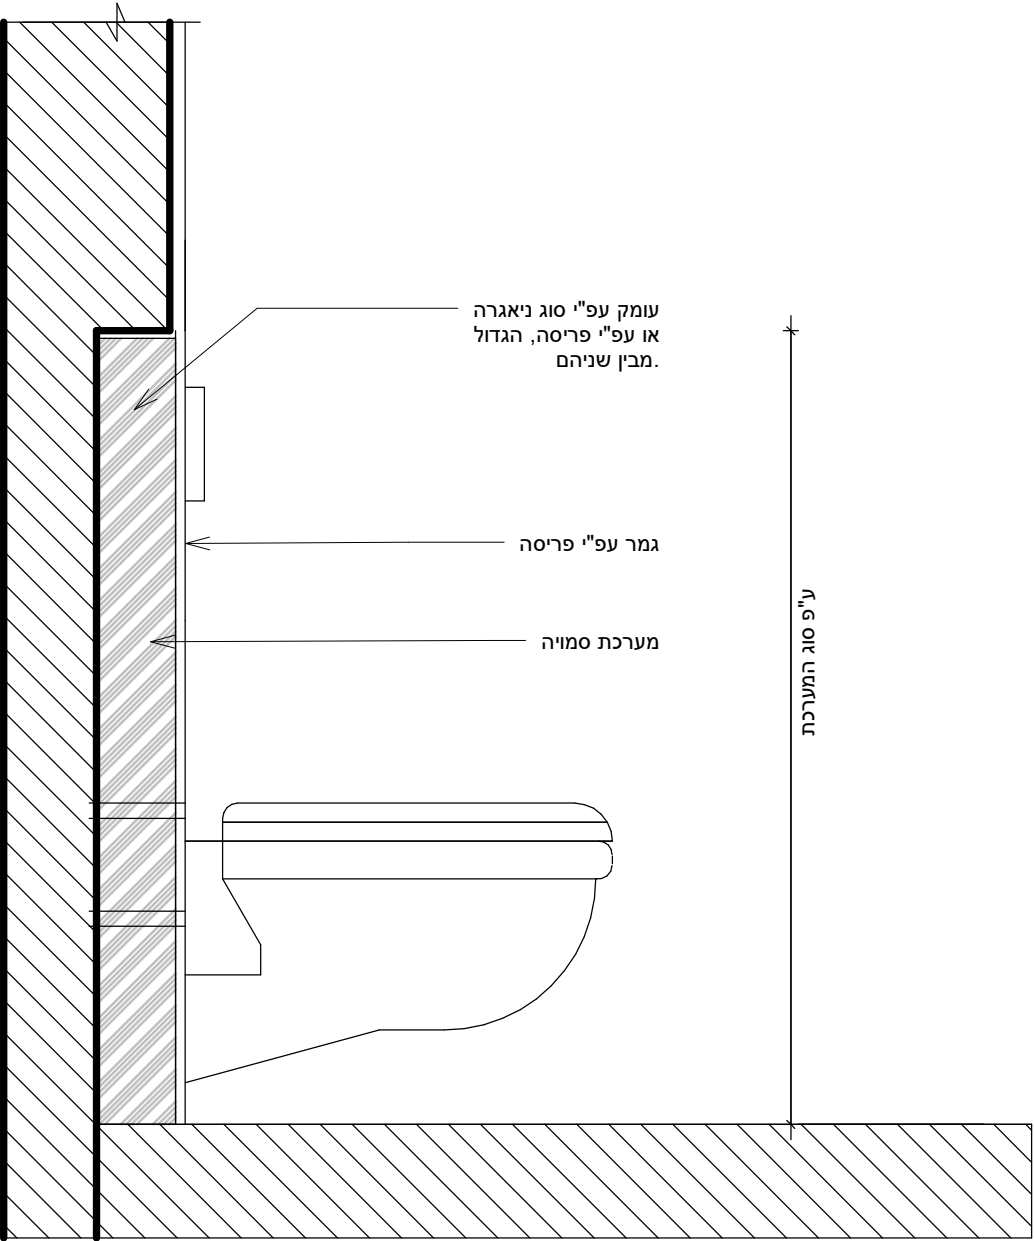

פרט 5 - אסלה תלויה בקיר 20

1 : 10

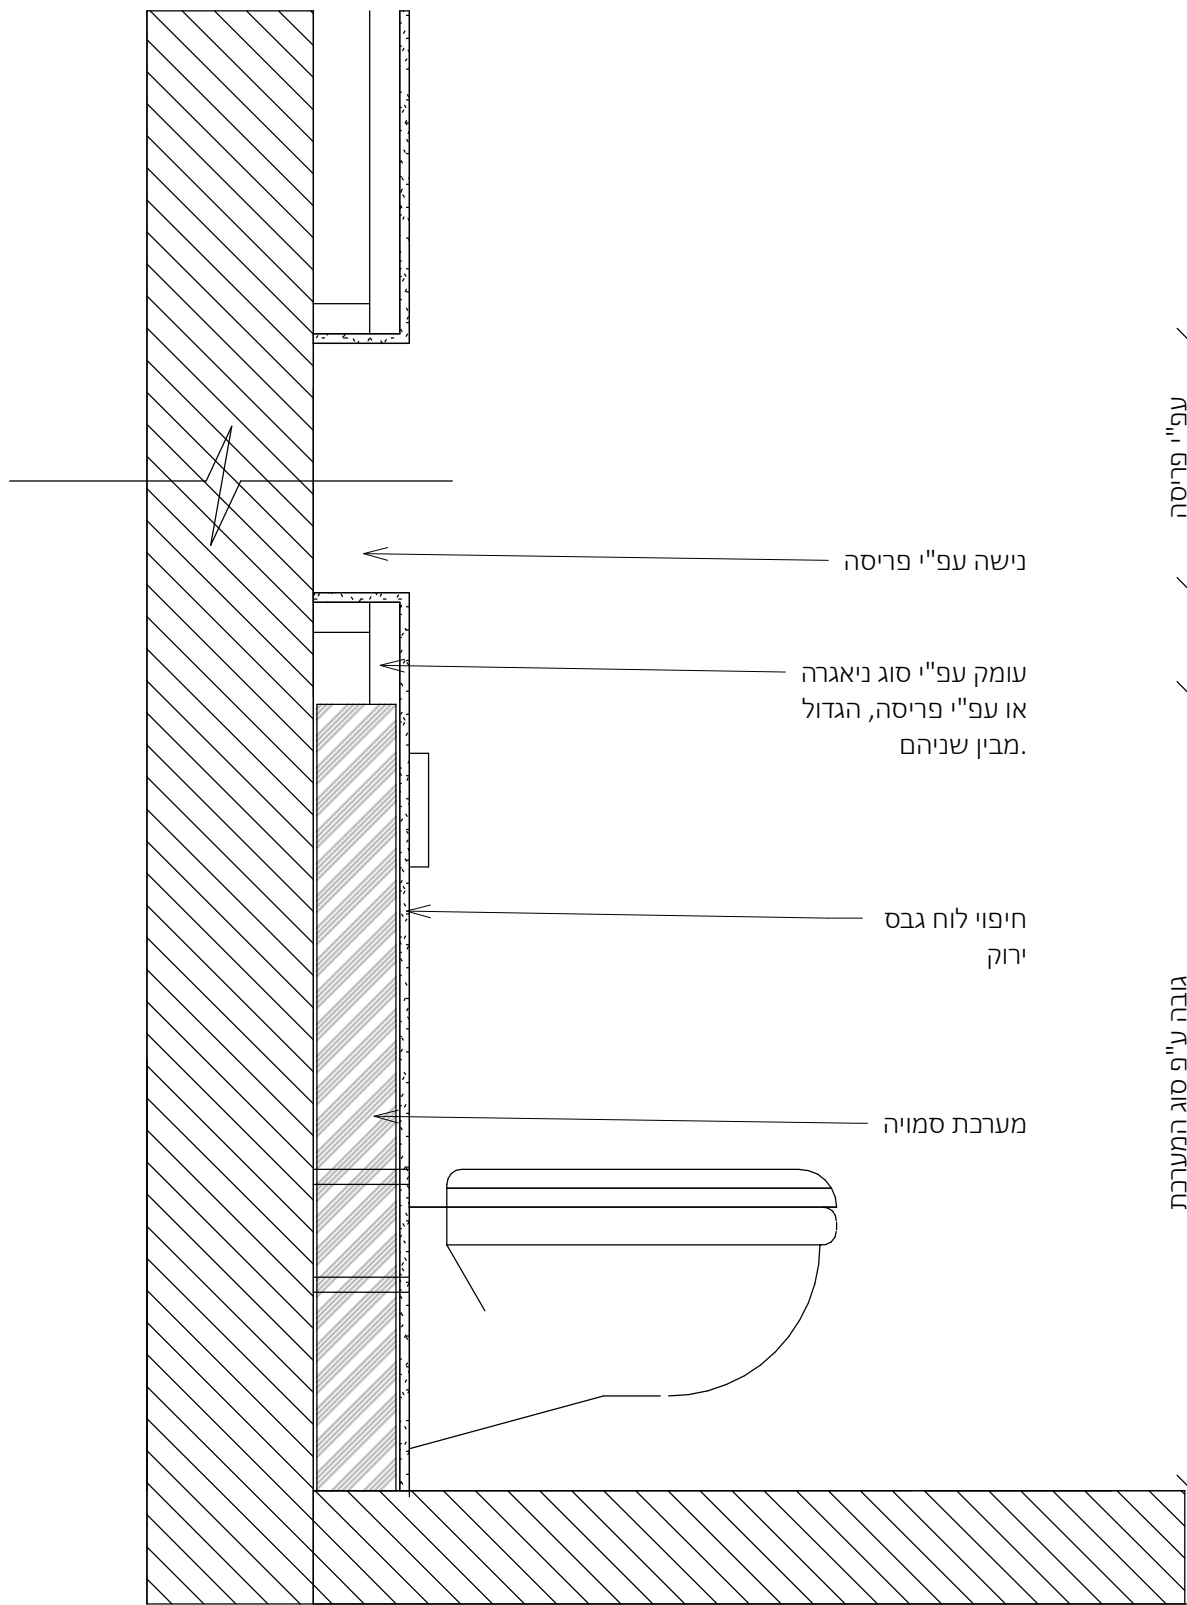

פרט 6 -אסלה תלויה מנגנון סמוי בעיבוי גבס

יש לעבוד במקביל לפרטים שיספק
מעצב הפנים (במידה וקיים במגרש זה)
המאושרות על ידי האדריכל.

פרטי האיטום באחריות יועץ האיטום
ראה חוברת פרטי איטום מצורפת

להמשך תיאום

FILE NAME: -----כלל הפרויקטים להיתר\00\23\תכנית\nofia