

אוריכל פנים	
אינסטיציה	
בסיחת אש	
אקוסטיקה	
חשתי והזרה	
קונסטרוקציה	
קבלו ראש	
ניחול פזיונס	
נמח	
אוריכל	

חברות לאשור	08.05.2025	⚠️
חברות לאשור	31.03.2025	⚠️
חברות כעיון	11.03.2025	⚠️
שנתיים:	חאריץ:	100:

הערות


- מקרא

- מקרא צבעים בתכנית

- | | |
|--------------------------|---|
| תעלות ותריסי אוויר חוזר |  |
| תעלות ותריסי אספקת אוויר |  |
| תעלות ותריסי אוויר צח |  |
| תעלות ותריסי יניקת אוויר |  |
| תעלות ותריסי שיחרור עשן |  |
| צנרת גז וחשמל |  |
| סימון מעגלי מזווג אוויר |  |

191	מבני מקורים צמודי קרקע נופיה אפי' מנשה 23 מרש	שם המרחק
1:50	מיוזג אוויר ואווורור	שם המרחק
08.05.2025	קומה ראשונה ושנייה	שם המרחק
תאריך תחילת		שם המרחק
		שם המרחק
מרחקים		שם המרחק
   	נכסור	עיון
בנימין		שם המרחק
	10.03.2025	שם המרחק
	אילן ארז	שם המרחק

Court 23
1st Floor
Option ~~No~~3
VRF duct units

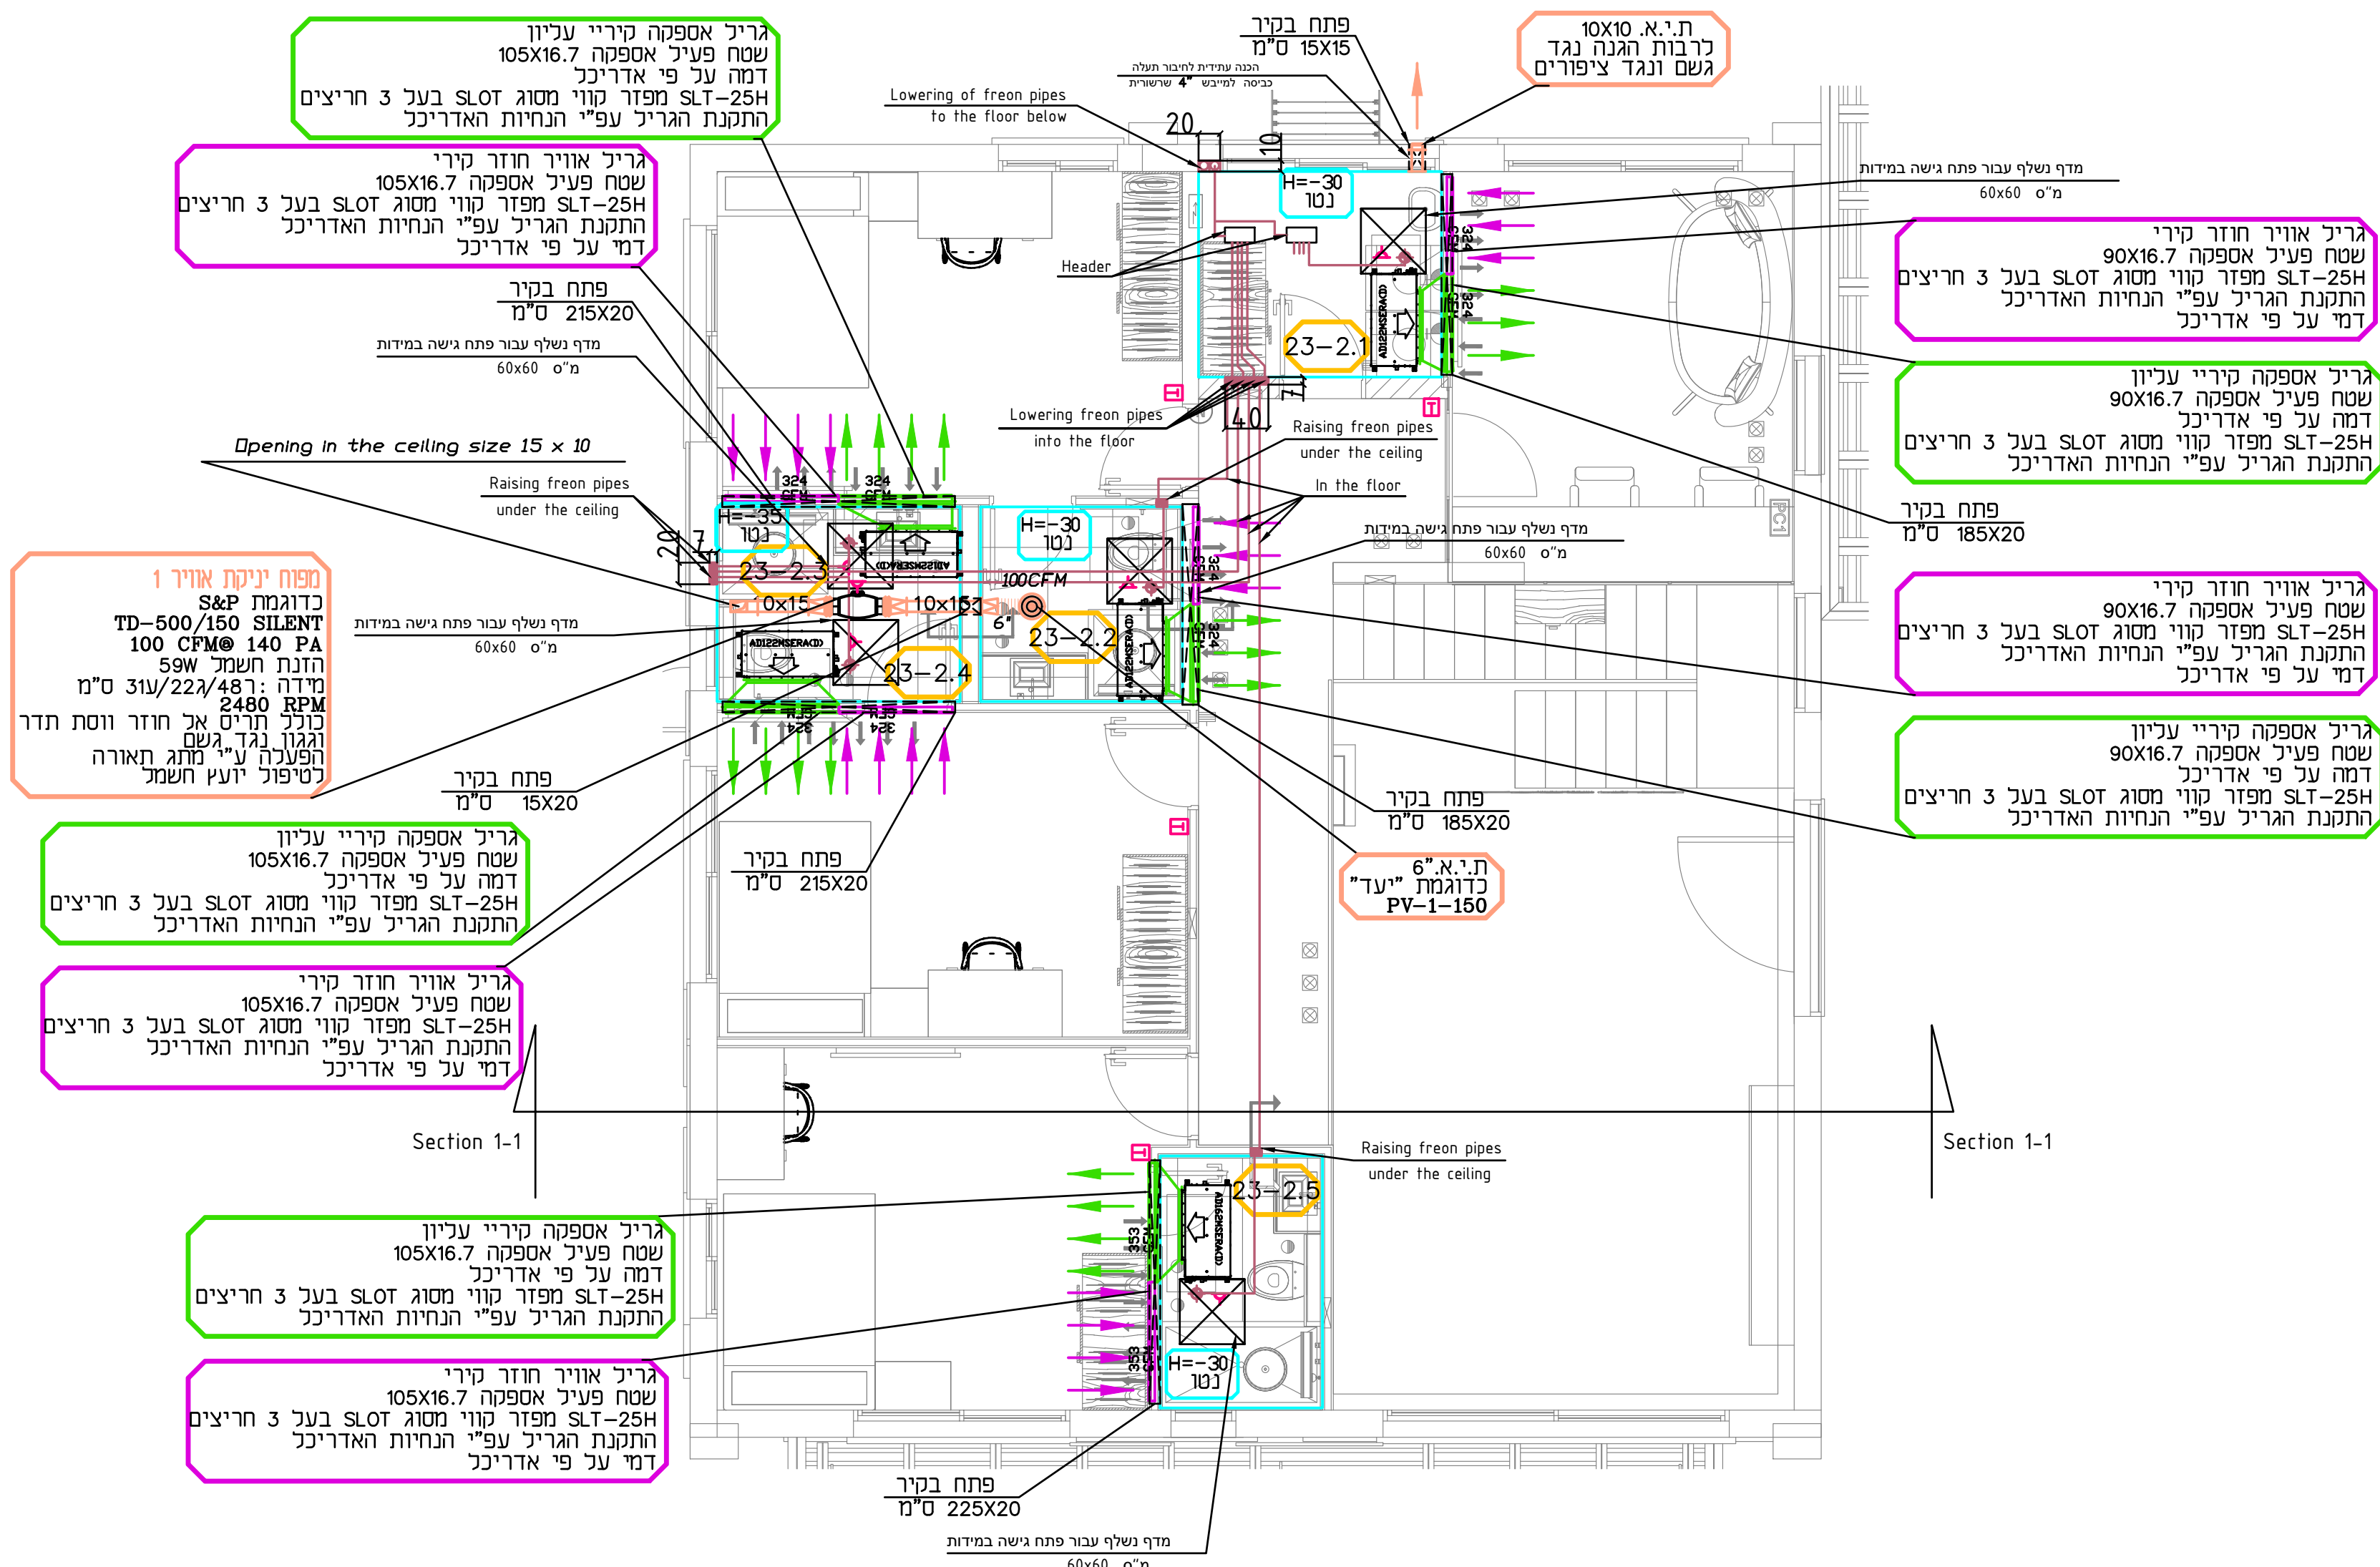

אוריכל פנים	
אינסטיציה	
בסיחת אש	
אקוסטיקה	
חשתי והזרה	
קונסטרוקציה	
קבלו ראש	
ניחול פרויקט	
נמח	
אוריכל	

חברות לאשור	08.05.2025	⚠️
חברות לאשור	31.03.2025	⚠️
חברות כעיון	11.03.2025	⚠️
שנתיים:	חאריץ:	100:

מפ- מפוח
מ.א.ג. מפדור אוויר קירי
מ.מ.א. מפדור אוויר תקררת
ת.א.ה. תריס אוויר חוזר
ת.צ.צ. תריס אוויר צח
ב.א. בידוד אקוסטי
ב.ט. בידוד טרמי
ד.ב. נלא בידוד
ג.ב. דמפר אש
ט.ט. טרמוסטט לוח הפעלה
שקע חשמל נדפסור יו
שקע תלת פאזי נדפסור
מפסק בטחון חד פאזי
מפסק בטחון תלת פאזי
ניקוז מאייד טריפול יו
גובה 25 ס"מ מחותני
שלט עכירה אכרוסי

תעלות ותריסי אוויר חוזר	
תעלות ותריסי אספקת אוויר	
תעלות ותריסי צח	
תעלות ותריסי יניקת אוויר	
תעלות ותריסי שיחרור עשן	
צנרת גז וחשמל	
סימון מעגלי מיזוג אוויר	

אייל ארז | מהנדסים יועצים
ייעוץ ותכנון מערכות חימום ואימוץ, פיקוח עליון

Section 1-1

Section 1-1

יחידות קצה מעל 2-23											
חסי יחידה בנחנית	חוצרת	דגם	מאייד	חפסות קורר Cooling	ספיקת אויר CFM	רמת רעש dB(A)	משקל kg	מידות מרו	מידות פני	מחם חונה V/Hz/Ph	חפסן ניצור W
2.3-2.1 2.5-2.2 2.3-2.3	Haier	AS122MNERA	מאייד עיני	12,300	371	37	10	205/283/85.5 מ"מ	---	230/50/1	---
2.3-2.4											
2.3-2.5	Haier	AD162MSERA(D)	Slim Duct Low ESP	15,400	363	32	18.5	425/18.5/85.5 מ"מ	---	230/50/1	---

[illegible]