פרט יציאת צנרת חשמל בגג לבוילר וכדו'

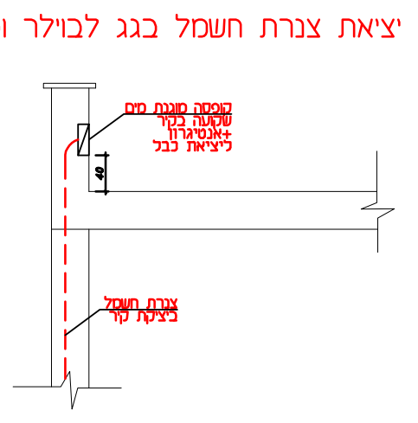

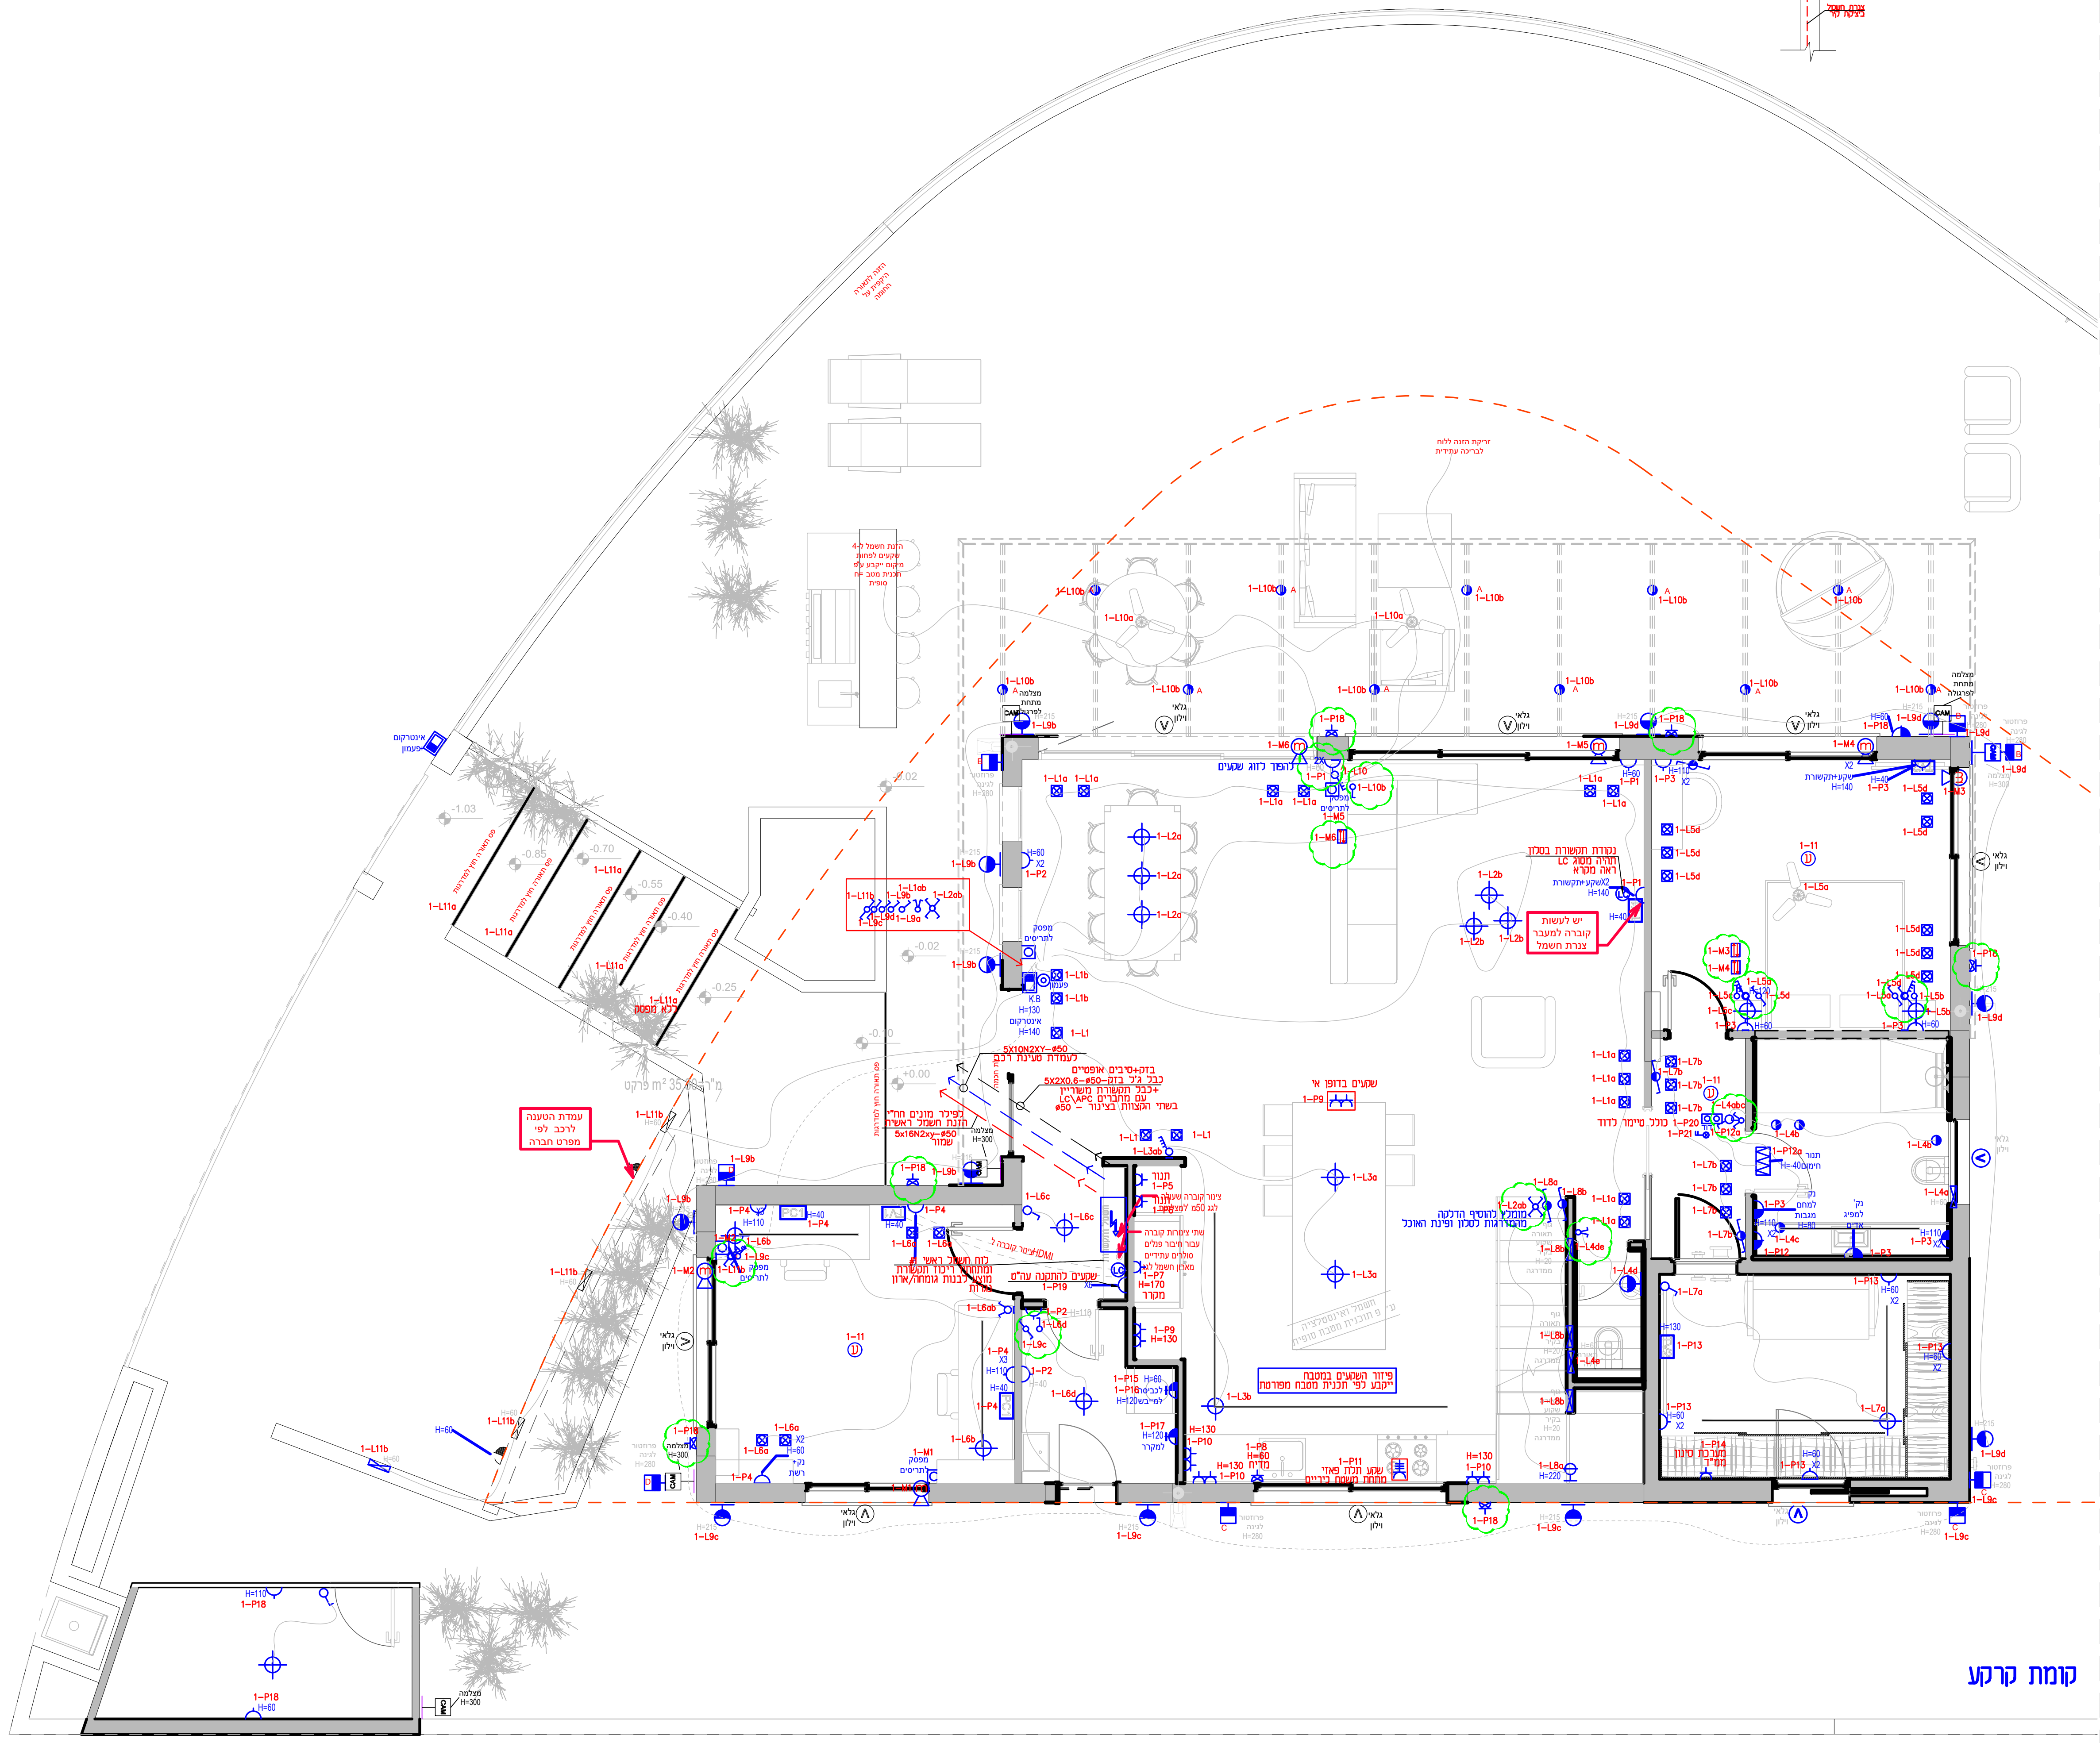

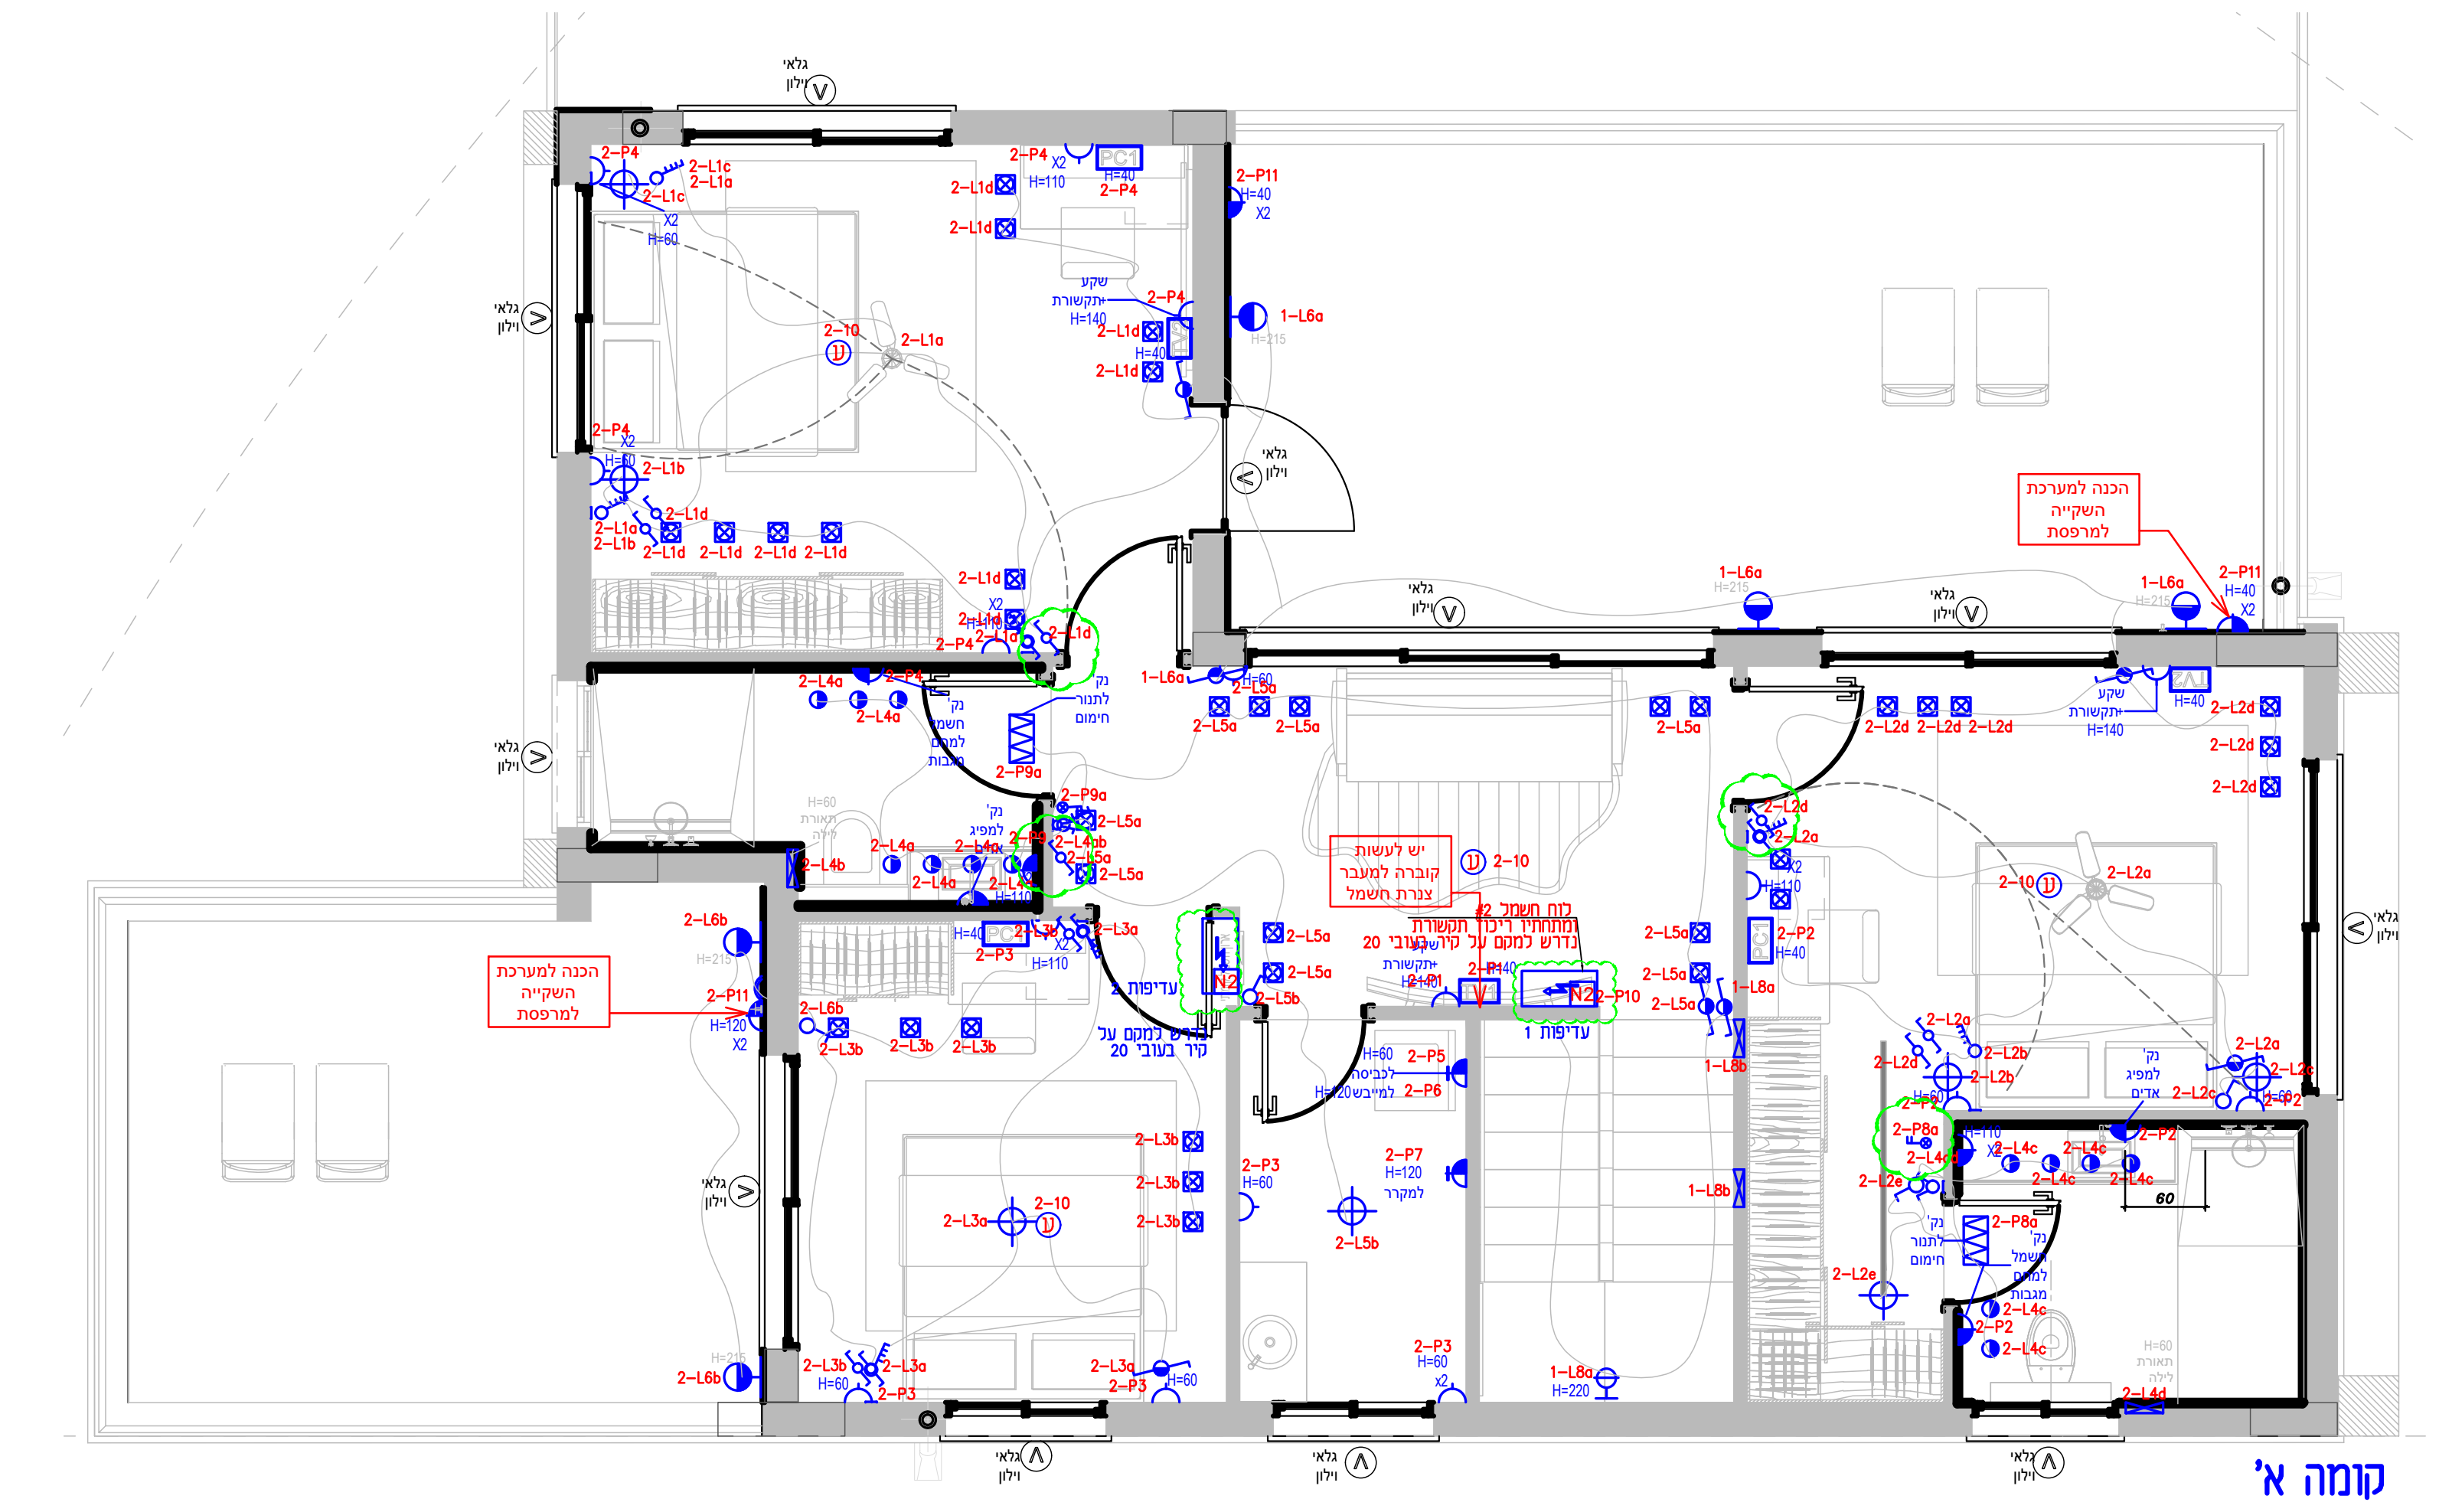

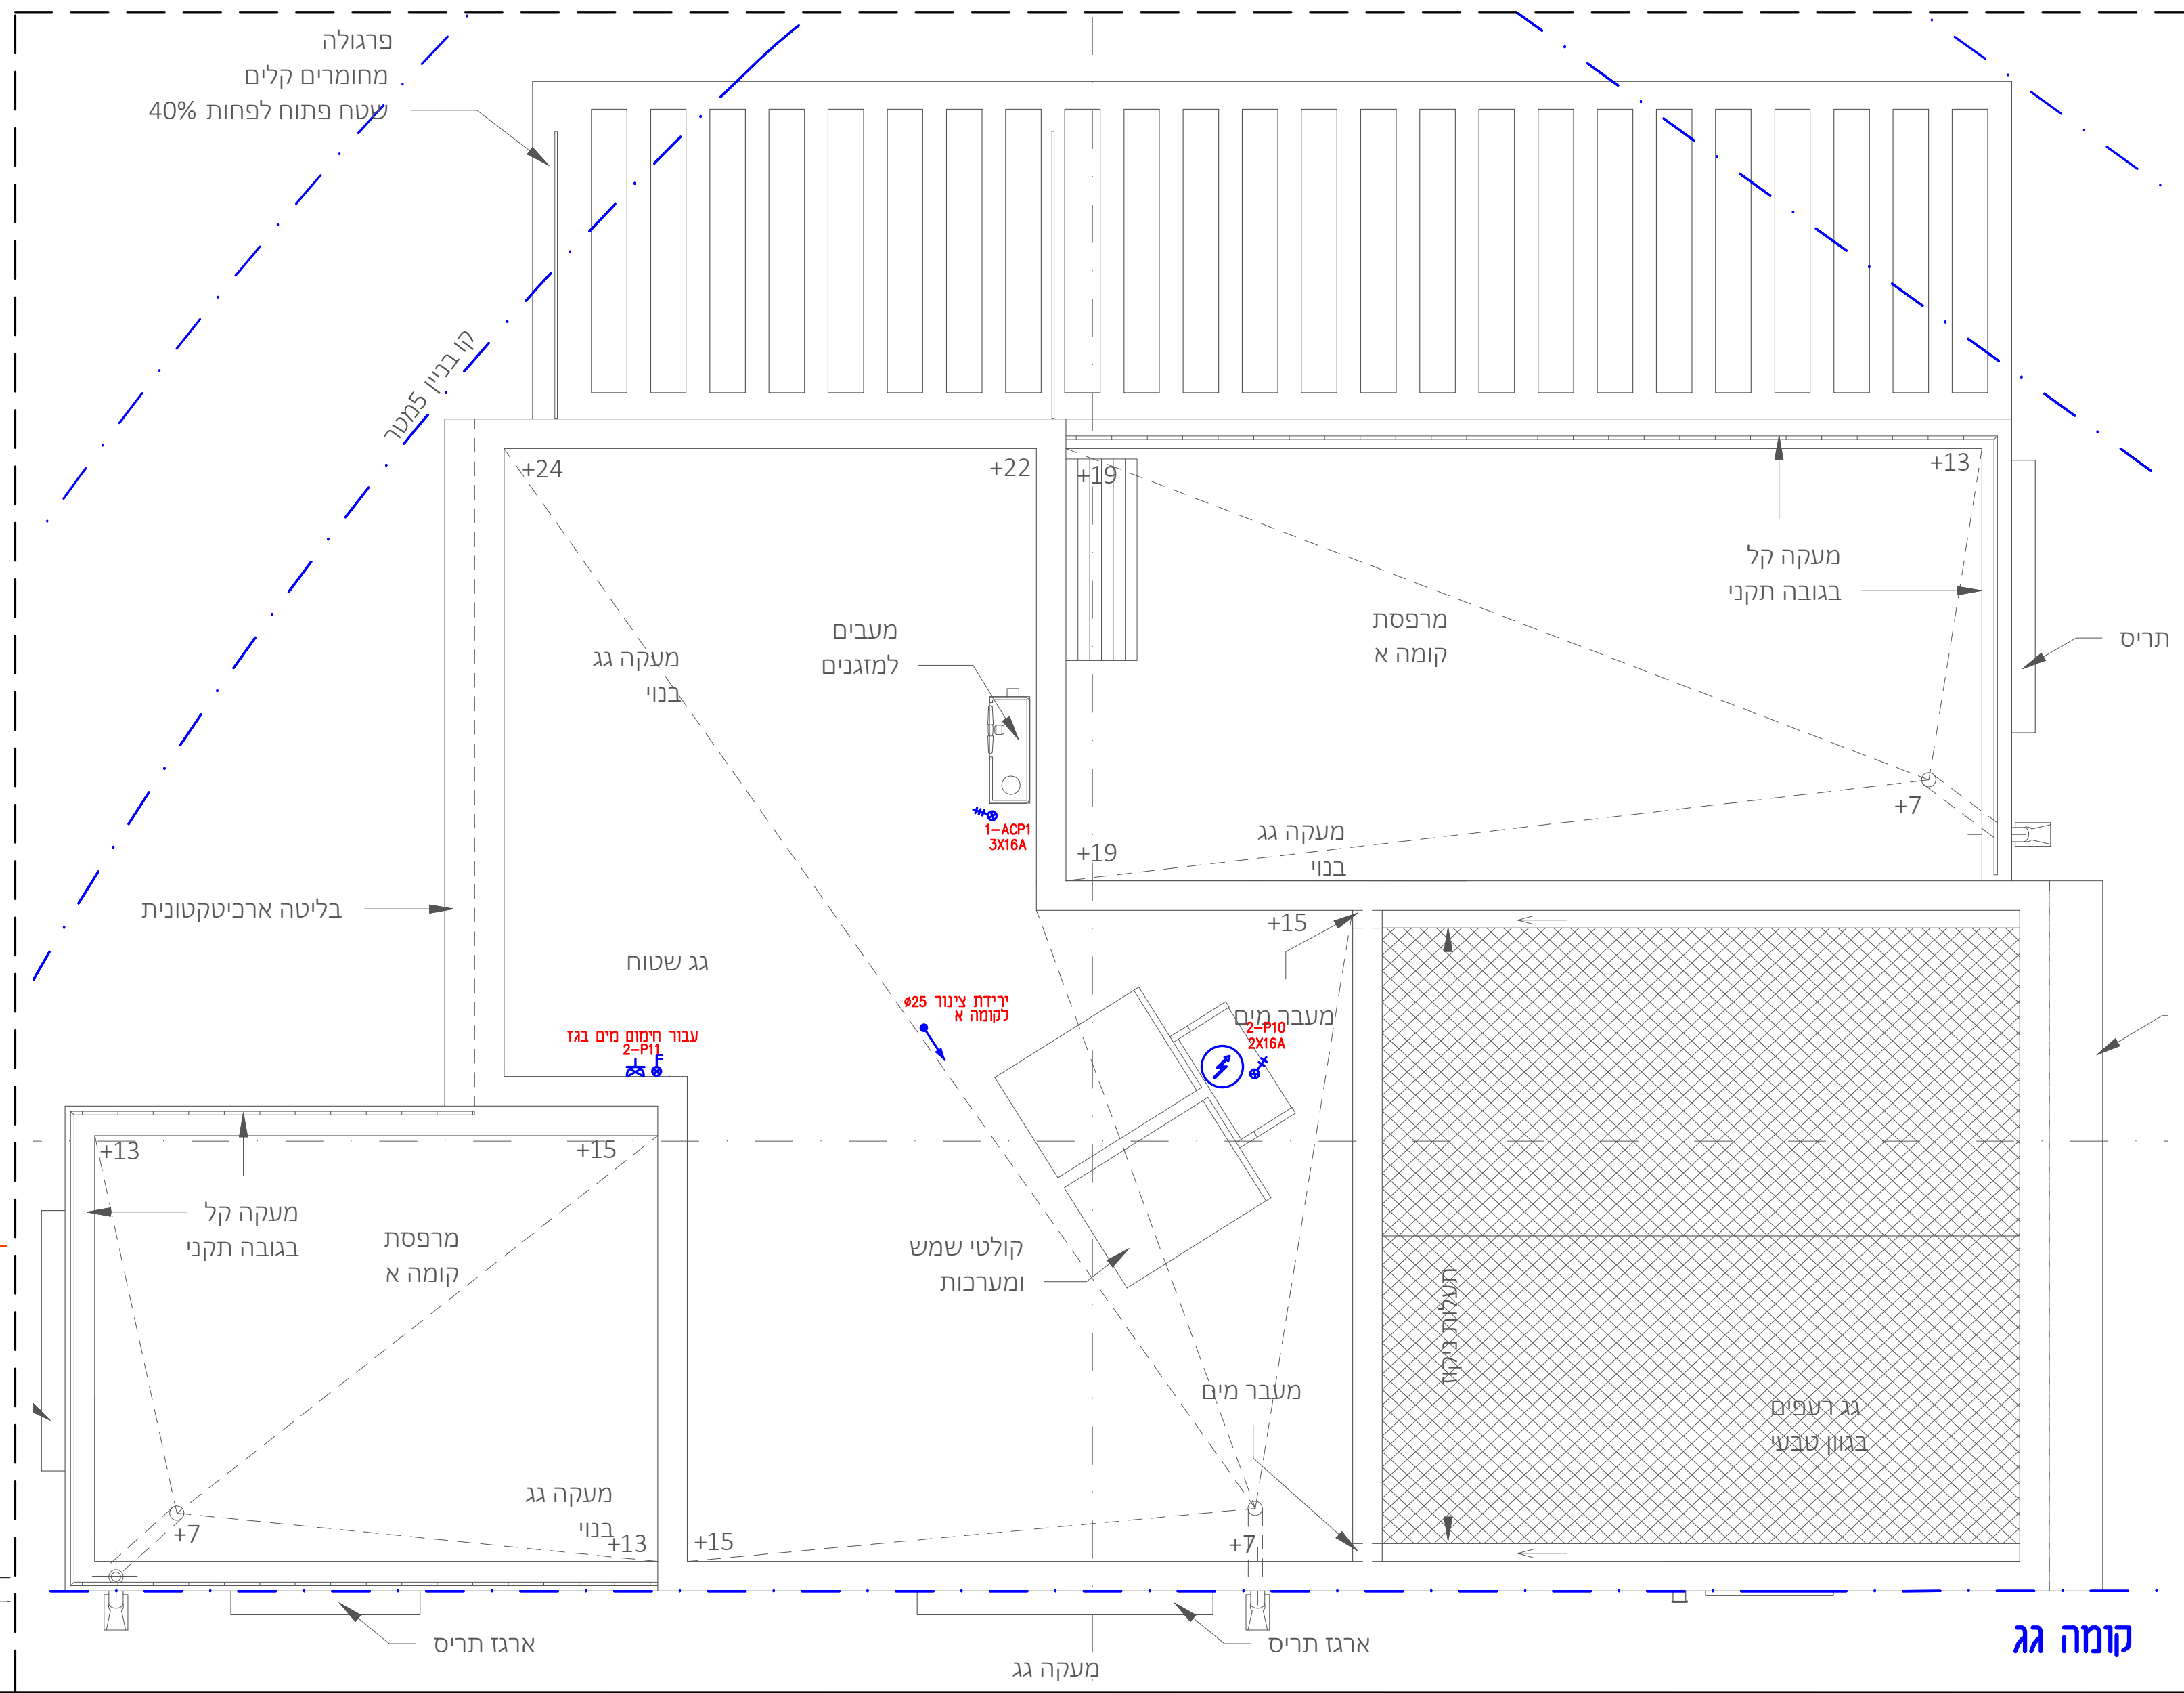

מקרא חשמל ותאורה:

לוח		לוח חשמל
חשמל ותקשורת		שקע 16A בודד H=60 אלא אם צוין אחרת
		זוג שקעי 16A H=60 אלא אם צוין אחרת
	N2	מקבץ שקעים טיפוסי סיום באביזר N2 "ניסקו" בארון תקשורת מתחת לוח חשמל
		שקע חד פאזי מוגן מים H=60 אלא אם צוין אחרת
		שקע ליחידת מ"א 16A H=220 מיקום סופי לפי תכנית מיזוג ובתיאום מול אדריכל
	ט	נקודת טלפון מלאה-צנרת, כבילה ושקע טלפון H=60
		CIMA BOX הכולל: 4 שקעי שרות+2 תקשורת
	ת	נקודת תקשורת H=60, צינור ø25 עם חוט משיכה מריכוז תקשורת דירתי
		נקודת טלויזיה מושלמת+צינור שמור ø20 H=60
	LC	נקודת תקשורת מלאה הכוללת: כבל תקשורת אופטי תקני מותקן בצינור ø25 סיום בית תקע אופטי LC\APD לפי דרישות ת"י 1-11801 עם ראשים מוכנים מראש להתקנה בארון תקשורת דירתי ובסלון עם חוט משיכה מריכוז תקשורת דירתי
	m	מנוע חשמלי H=200
	T	הכנה לתרמוסטט מזגן- צינור 20 לחלל תקרה
	T	תרמוסטט חימום תת רצפתי- יבוצע לפי הנחיות ספק
		שקע לתנור חימום חשמלי 10 סמ מעל פתח דלת
		בויילר
		הכנה לוונטה סיום בשקע
מפסקים		מפסק מאור בודד H=90 אלא אם צוין אחרת במפסקי הדלקה ליד מיטה H=60
		מפסק כפול H=90
		מפסק מאור מחליף H=90
		לחצן פעמון דלת H=90
		מנתק מואר 3X16A / 2X16A
	F	מפסק דו קוטבי מואר לתנור חימום חשמלי H=160
		מפסק הרמה/הורדה לתריס חשמלי 5 סמ מעל מפסק תאורה ע"פ פרט
		מפסק עם שעון בקיר לבויילר H=180
	א	פנל צפיה (מוניטור) +לחצן פתיחה דלת H=120
תאורה וגלאי אש		תאורת חרום חד תכליתית LED 3w
	ע	גלאי עשן בתקרה
		נקודת מאור בתקרה
		ג"ת פנים תקרתי מוגן מים
		ג"ת LED עגול שקוע בתקרה
		ג"ת LED עגול קירי גובה H=220
		ג"ת פנים קירי למנורת לילה H=120
		ג"ת פנים/חוץ קירי מוגן מים H=240 , במרתף H=220
		ג"ת קירי נמוך לתאורת התמצאות מדרגות/שירותים, h=15 מהרצפה/ מרום מדרגה
		ג"ת מלבני IP65 להתקנה על פרגולה
		מאוורר להתקנה בחוץ
		פעמון דלת 220V (גונג) התקנה מעל דלת כניסה
		הכנה מצלמה אבטחה, צינור 25 וחוט משיכה מארון תקשורת דירתי

פרט לגבהים של הדלקות, תאורה ותריסים:

חזית לוח חשמל ראשי וארונות תקשורת

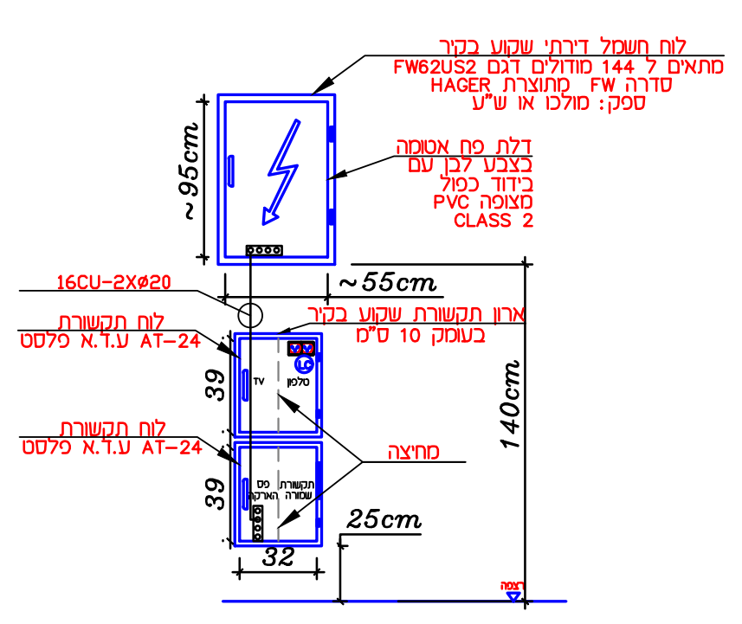

תפוצה	תאריך
מנהל הפרויקט	
אדריכל	
מזמין/יזם	
חשמל	
קבלן	
בטיחות	
אקוסטיקה	
אינסטלציה	
קונסטרוקציה	
אדריכל נוף	
מטבחים	
חברת חשמל	
חברת בזק	

מס'	שינויים	תאריך
1	עדכון תוכנית	10.12.24
2	עדכון תוכנית	15.12.24
3	עדכון תוכנית	24.12.24
4	עדכון תוכנית	23.4.25

עודכן ע"י: יפעת

הערות:

-כהכנה לבית חכם ולדלת חכמה יש להשחיל חוט 0 כחול נוסף בכל מפסק הדלקה התכנון עצמו יעשה ע"י ספק בית חכם

-הכנות למיזוג אויר,חימום תת רצפתי, מערכות אבטחה, וחימום מים בחשמל יהיו עפ הנחיות יועץ לכל תחום

- יש לקרוא תכנית זו יחד עם תכנית אדריכלות למקרא בלוקים אדריכלות

א. בסיס
הנדסת חשמל בע"מ
משרד: יד חרוצים 16, ירושלים 93420
טל: 074-7021015 נייד: 050-6550484
פקס: 077-5131015 דוא"ל: office@ebasis.co.il

שם הפרויקט:
נופיה-אלפי מנשה
מגרש 24

שם הגיליון:
תוכנית חשמל טיפוסית

○ לעיון	○ לאישור	● למכרז	○ לביצוע	קנה מידה: 1:50
מס' קובץ: File: 675-24.dwg				תאריך: Date: 11.08.2024
תכנן: איתן	שרטט: אביבה	אישר: איתן		
מס' עדכון: 4	מס' הגליון: E	מס' הפרויקט: 675		

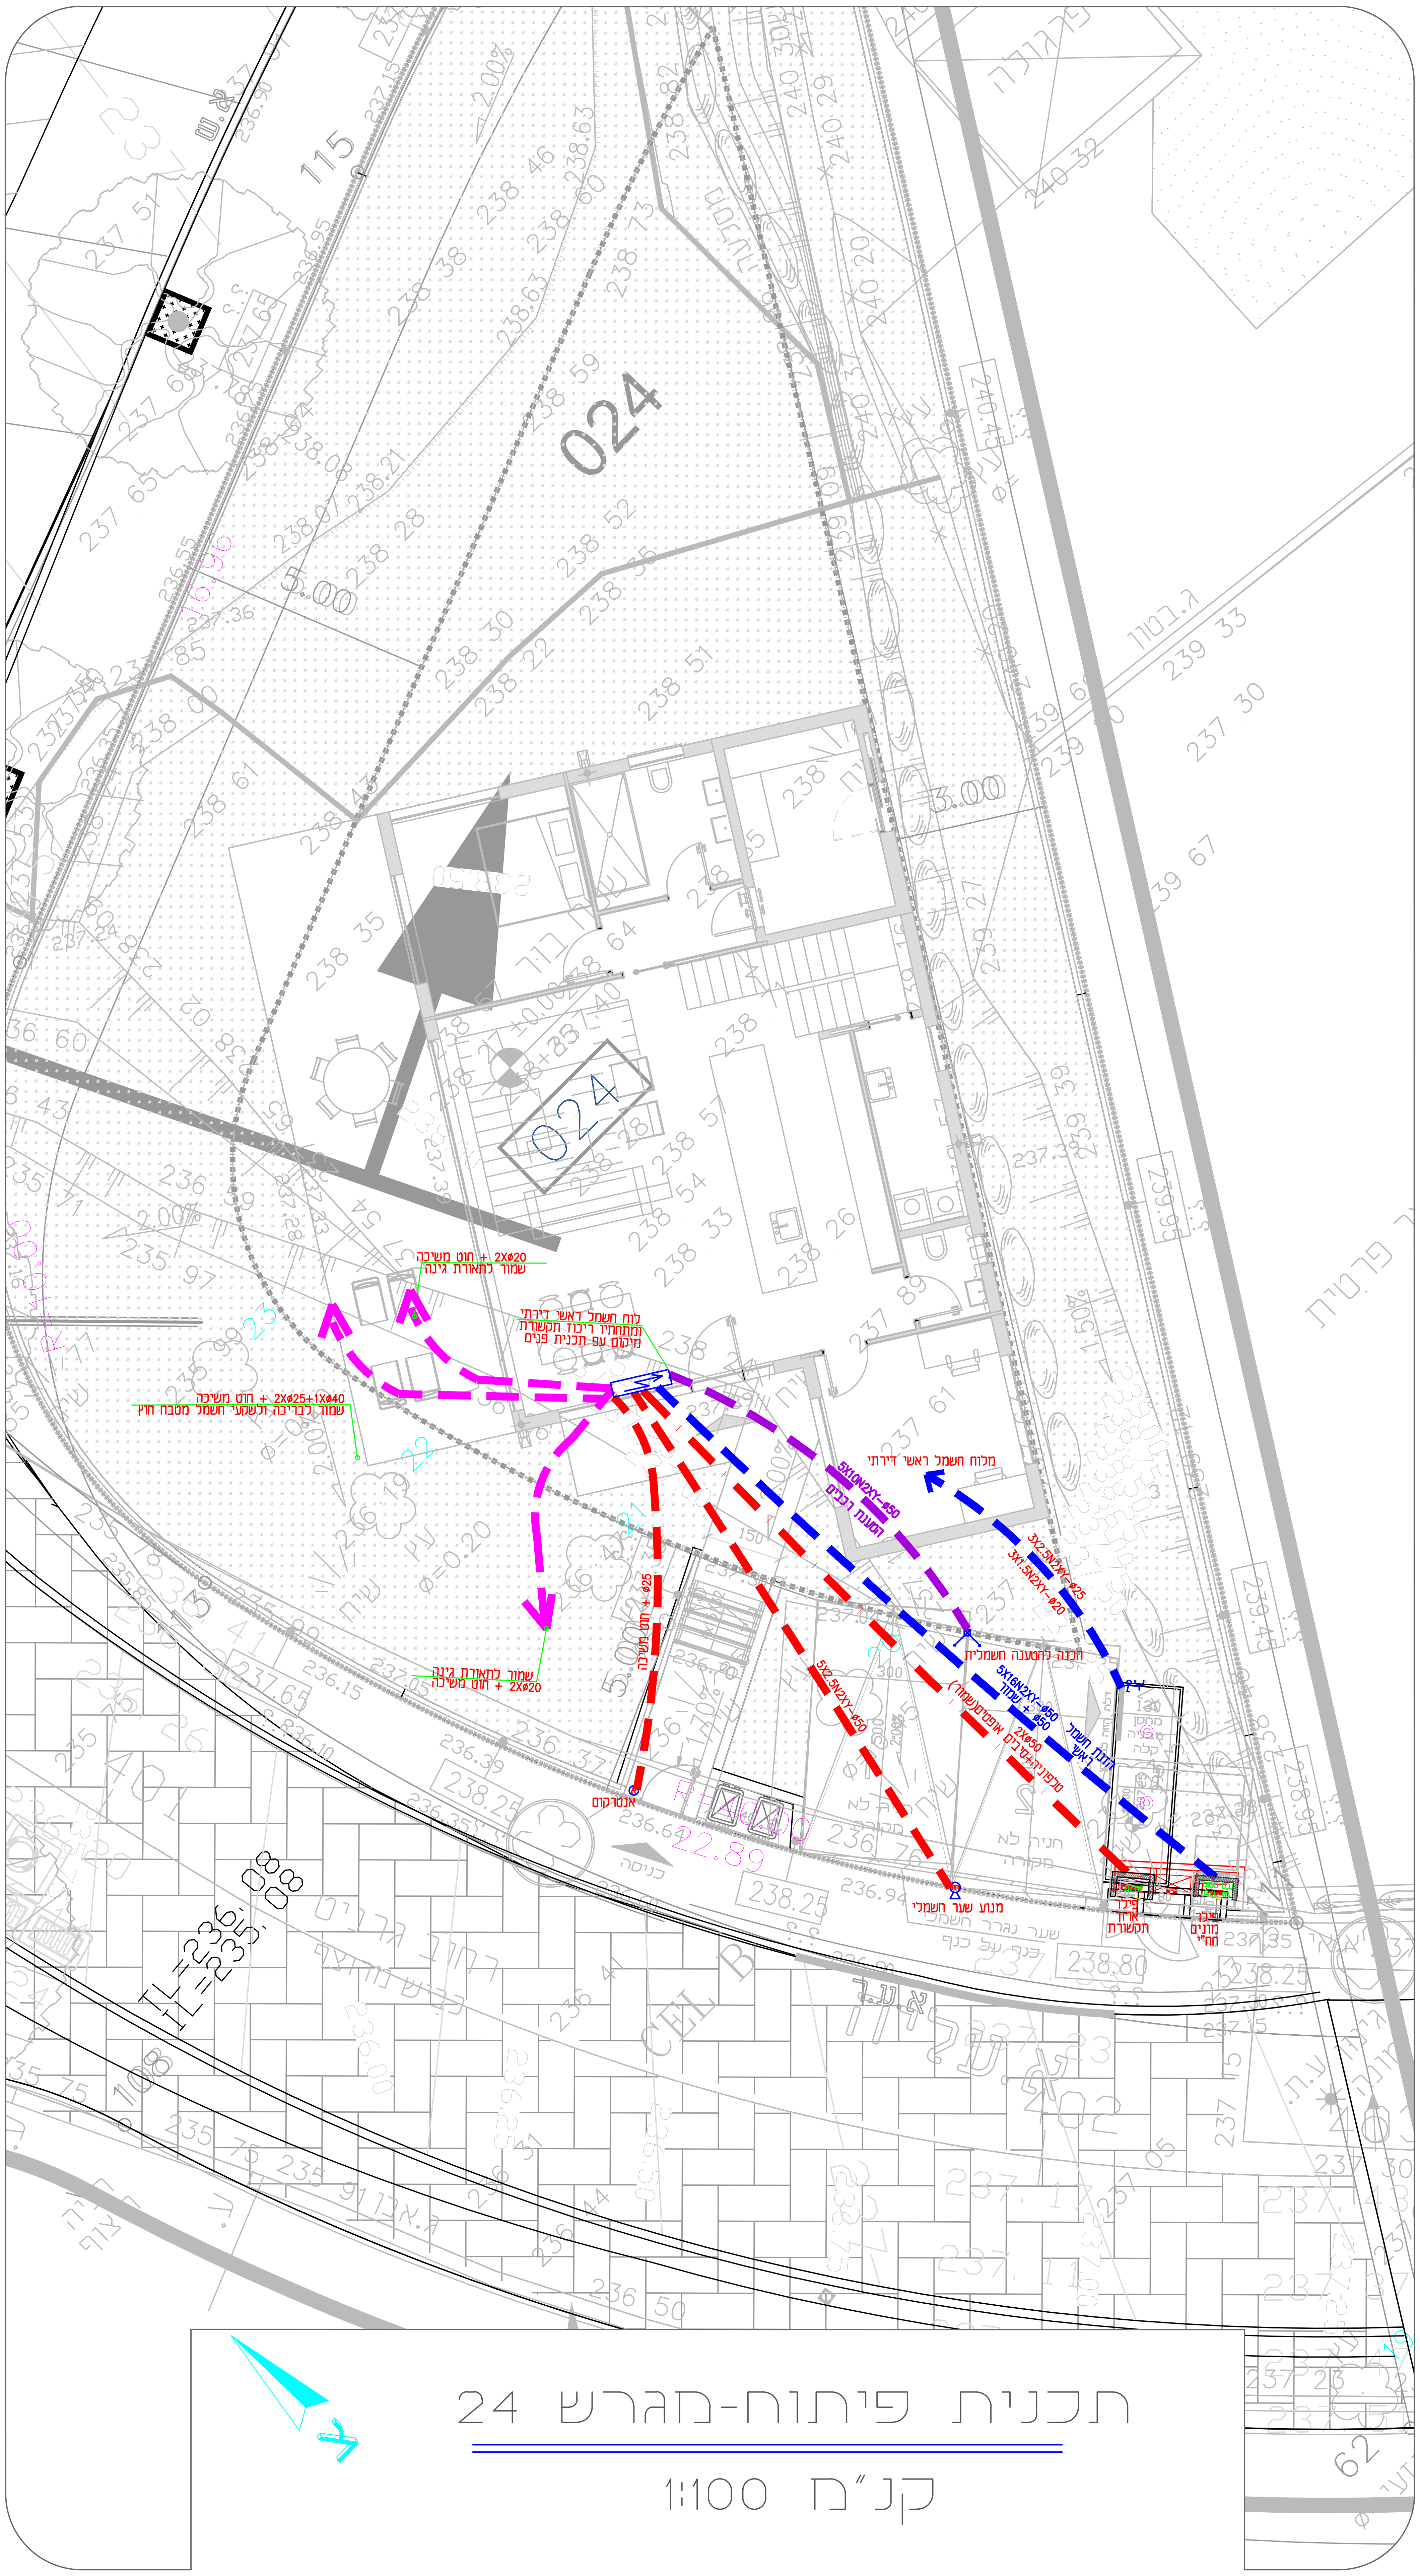

תכנית פיתוח-מגרש 24

קנ"מ 1:100

תאריך			חברת בזק	חברת חשמל	מטבחים	אדריכל נוף	קונסטרוקציה	אינסטלציה	אקוסטיקה	בטיחות	קבלן	חשמל	מזמין/יזם	אדריכל	מנהל הפרויקט

תפוצה

מס'	שינויים	תאריך

עודכן ע"י: רחל

א. בסיס
הנדסת חשמל בע"מ
משרד: יד חרוצים 16, ירושלים 93420
טל: 074-7021015 נייד: 050-6550484
פקס: 077-5131015 דוא"ל: office@ebasis.co.il

שם הפרויקט:
נופיה-אלפי מנשה

שם הגיליון:
תוכנית פיתוח מגרש 24

○ לעיון	○ לאישור	● למכרז	○ לביצוע

קנה מידה: 1:100

תאריך: Date: 17.06.2024

מס' קובץ: File: 675P.dwg

תכנן: איתן

שרטט: אילה

אישר: איתן

מס' עדכון: 0

מס' הגליון: P24

מס' הפרויקט: 675

לוח חשמל דירתי ראשי #1
מגרש 24

הנחיות לבניית לוח חשמל:

- מבנה לוח חשמל פלסטי חסין אש סדרת FW מתוצרת Hager דגם FW62US2 ל-144 מודולים 2X(6x12) לפחות
- דלת פח IP30 מתכתית
- בדיד כפול Class-2
- צבע לבן
- מהדקי אפס והארקה עם חיבור מהיר
- ציוד חשמלי יהיה מסוג ABB שניידר הגר או EATON בלבד בעל זרם
- יש לשמור בלוח 30% מקום לתוספת עתידית בלוח

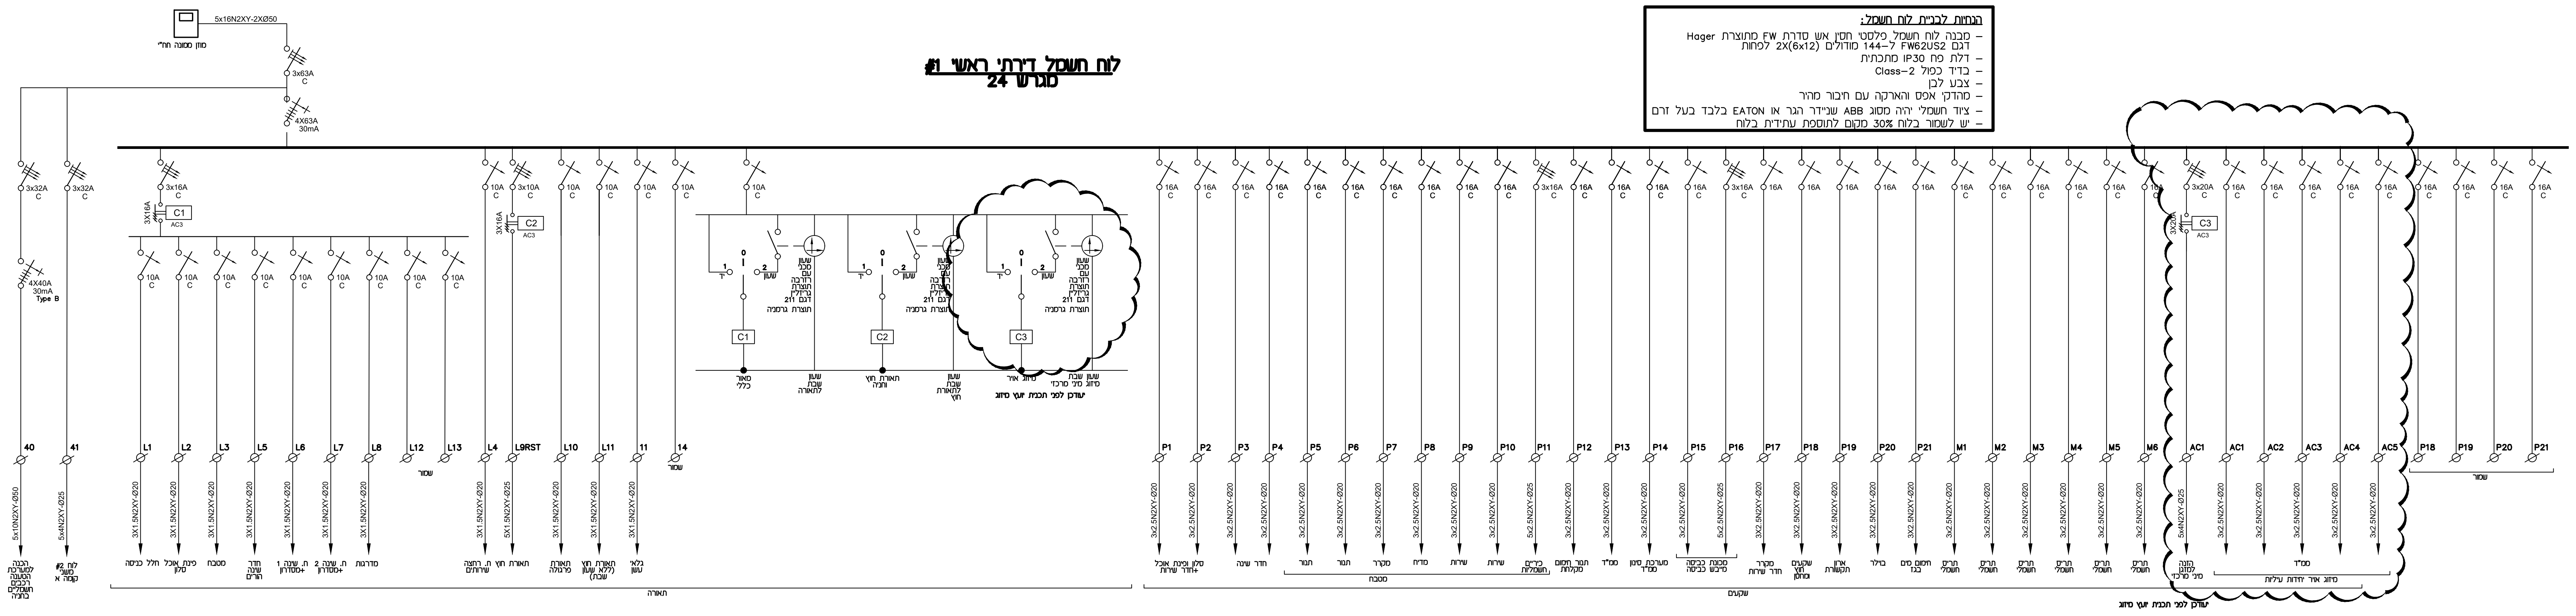
מוזן ממונה חח"י
5x16N2XY-2XØ50
3x63A C
4X63A 30mA
40 3x32A C 4X40A 30mA Type B 5x10N2XY-Ø50 הכנה למערכת הטענה רכבים חשמליים בחניה
41 3x32A C 5x4N2XY-Ø25 לוח #2 משני קומה א
3x16A C 3X16A C1 AC3
L1 10A C 3X1.5N2XY-Ø20 חלל כניסה
L2 10A C 3X1.5N2XY-Ø20 פינת אוכל סלון
L3 10A C 3X1.5N2XY-Ø20 מטבח
L5 10A C 3X1.5N2XY-Ø20 חדר שינה הורים
L6 10A C 3X1.5N2XY-Ø20 ח. שינה 1 +מסדרון
L7 10A C 3X1.5N2XY-Ø20 ח. שינה 2 +מסדרון
L8 10A C 3X1.5N2XY-Ø20 מדרגות
L12 10A C
L13 10A C
שמור
L4 10A C 3X1.5N2XY-Ø20 ח. רחצה שירותים
L9RST 3x10A C 3X16A C2 AC3 5X1.5N2XY-Ø25 תאורת חוץ
L10 10A C 3X1.5N2XY-Ø20 תאורת פרגולה
L11 10A C 3X1.5N2XY-Ø20 תאורת חוץ (ללא שעון שבת)
11 10A C 3X1.5N2XY-Ø20 גלאי עשן
14 10A C שמור
10A C
0 I 1 יד 2 שעון
שעון מכני עם רזרבה תוצרת גריזלין דגם 211 תוצרת גרמניה
C1 מאור כללי
שעון שבת לתאורה
C2 תאורת חוץ וחניה
שעון שבת לתאורת חוץ
C3 מיזוג אויר
שעון שבת מיזוג מיני מרכזי
יעודכן לפני תכנית יועץ מיזוג
תאורה
P1 16A C 3x2.5N2XY-Ø20
P2 16A C 3x2.5N2XY-Ø20
סלון ופינת אוכל +חדר שירות
P3 16A C 3x2.5N2XY-Ø20
P4 16A C 3x2.5N2XY-Ø20
חדר שינה
P5 16A C 3x2.5N2XY-Ø20 תנור
P6 16A C 3x2.5N2XY-Ø20 תנור
P7 16A C 3x2.5N2XY-Ø20 מקרר
P8 16A C 3x2.5N2XY-Ø20 מדיח
P9 16A C 3x2.5N2XY-Ø20 שירות
P10 16A C 3x2.5N2XY-Ø20 שירות
P11 3x16A C 5x2.5N2XY-Ø25 כיריים חשמליות
מטבח
P12 16A C 3x2.5N2XY-Ø20 תנור חימום מקלחת
P13 16A C 3x2.5N2XY-Ø20 ממ"ד
P14 16A C 3x2.5N2XY-Ø20 מערכת סינון ממ"ד
P15 16A C 3x2.5N2XY-Ø20 מכונת כביסה
P16 3x16A C 5x2.5N2XY-Ø25 מייבש כביסה
P17 16A 3X2.5N2XY-Ø20 מקרר חדר שירות
P18 16A 3X2.5N2XY-Ø20 שקעים חוץ ומחסן
P19 16A 3X2.5N2XY-Ø20 ארון תקשורת
P20 16A 3X2.5N2XY-Ø20 בוילר
P21 16A 3X2.5N2XY-Ø20 חימום מים בגז
M1 16A C 3x2.5N2XY-Ø20 תריס חשמלי
M2 16A C 3x2.5N2XY-Ø20 תריס חשמלי
M3 16A C 3x2.5N2XY-Ø20 תריס חשמלי
M4 16A C 3x2.5N2XY-Ø20 תריס חשמלי
M5 16A C 3x2.5N2XY-Ø20 תריס חשמלי
M6 16A C 3x2.5N2XY-Ø20 תריס חשמלי
שקעים
AC1 3x20A C 3X20A C3 AC3 5x4N2XY-Ø25 הזנה למזגן מיני מרכזי
AC1 16A C 3x2.5N2XY-Ø20
AC2 16A C 3x2.5N2XY-Ø20
AC3 16A C 3x2.5N2XY-Ø20
AC4 16A C 3x2.5N2XY-Ø20
AC5 16A C 3x2.5N2XY-Ø20
ממ"ד
מיזוג אויר יחידות עיליות
יעודכן לפני תכנית יועץ מיזוג
P18 16A C
P19 16A C
P20 16A C
P21 16A C
שמור

לוח חשמל משני #2
מגרש 24

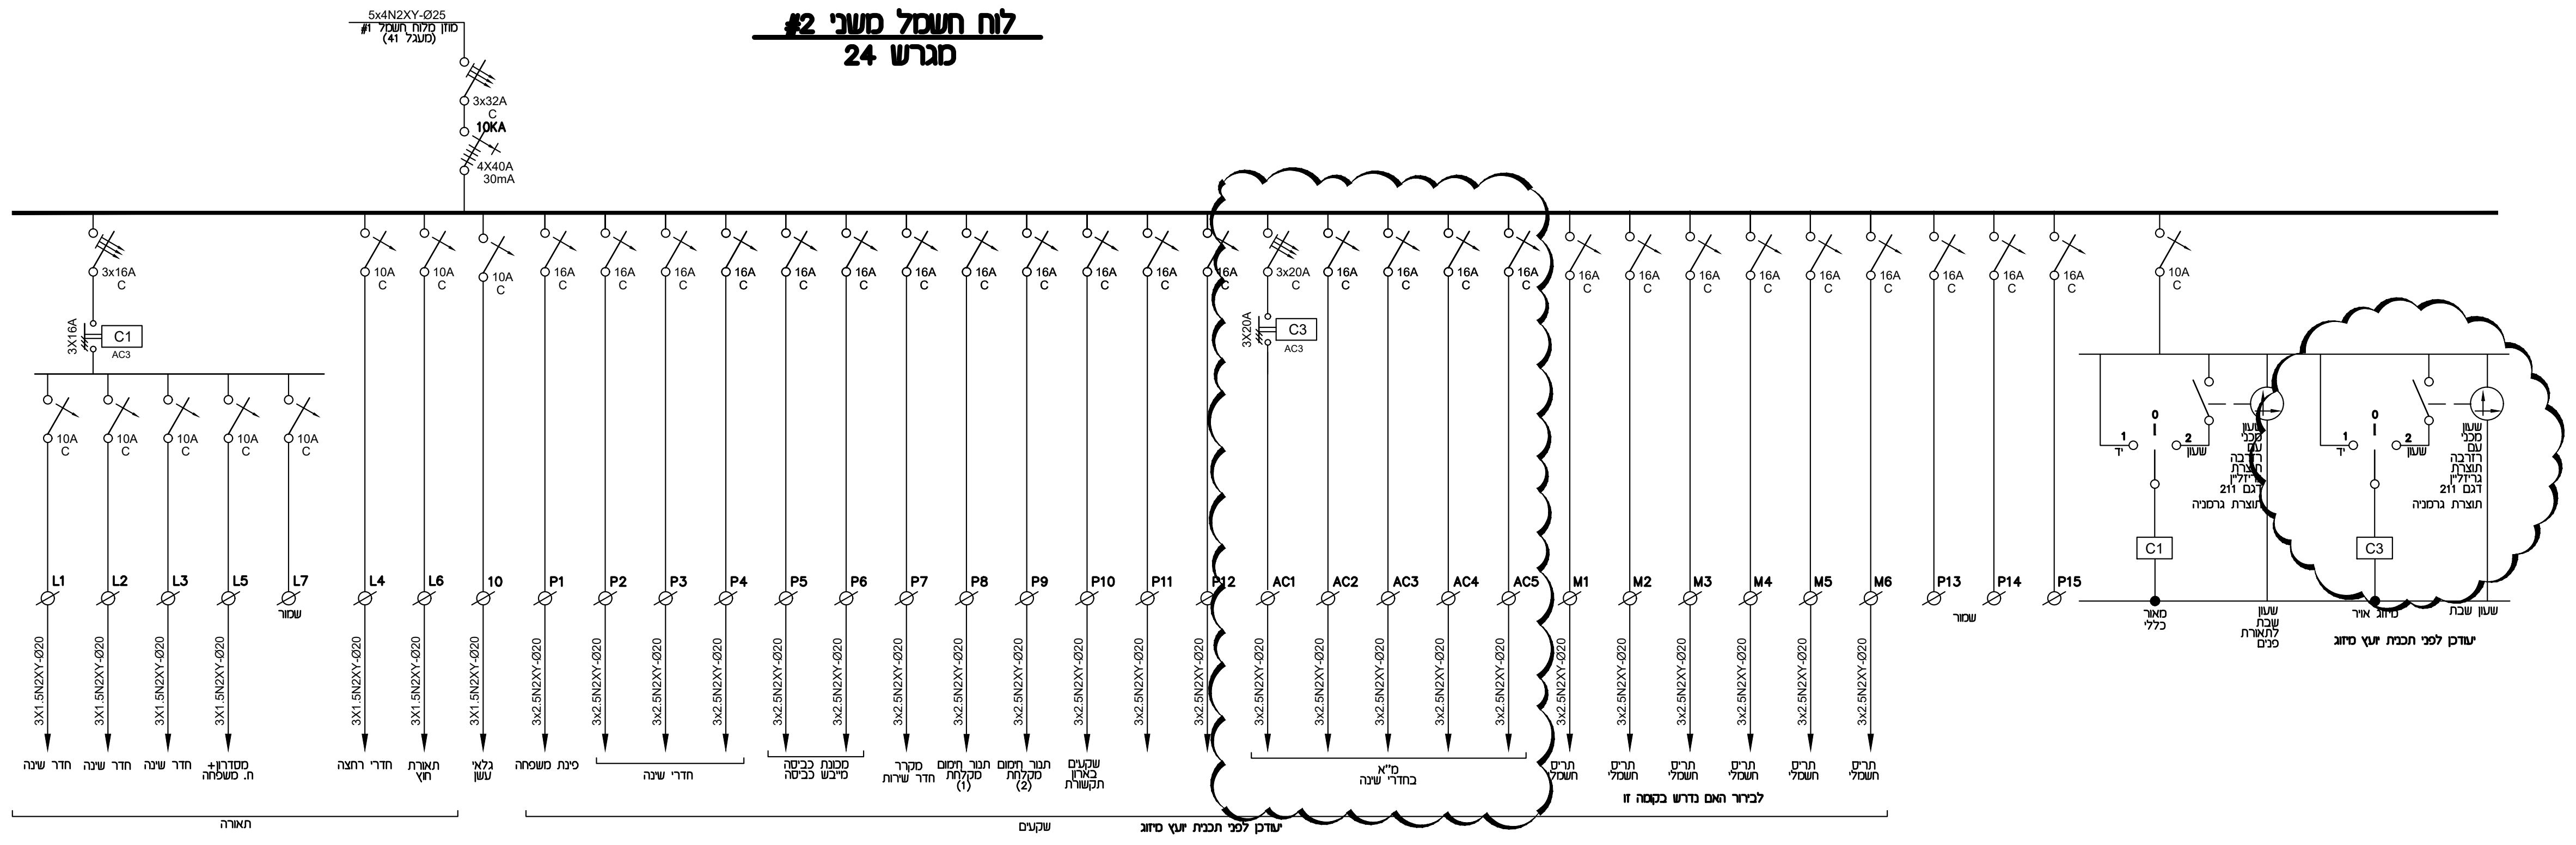
5x4N2XY-Ø25
מוזן מלוח חשמל #1 (מעגל 41)
3x32A C
10KA
4X40A 30mA
3x16A C 3X16A C1 AC3
L1 10A C 3X1.5N2XY-Ø20 חדר שינה
L2 10A C 3X1.5N2XY-Ø20 חדר שינה
L3 10A C 3X1.5N2XY-Ø20 חדר שינה
L5 10A C 3X1.5N2XY-Ø20 מסדרון+ ח. משפחה
L7 10A C שמור
L4 10A C 3X1.5N2XY-Ø20 חדרי רחצה
L6 10A C 3X1.5N2XY-Ø20 תאורת חוץ
10 10A C 3X1.5N2XY-Ø20 גלאי עשן
תאורה
P1 16A C 3x2.5N2XY-Ø20 פינת משפחה
P2 16A C 3x2.5N2XY-Ø20
P3 16A C 3x2.5N2XY-Ø20
P4 16A C 3x2.5N2XY-Ø20
חדרי שינה
P5 16A C 3x2.5N2XY-Ø20 מכונת כביסה
P6 16A C 3x2.5N2XY-Ø20 מייבש כביסה
P7 16A C 3x2.5N2XY-Ø20 מקרר חדר שירות
P8 16A C 3x2.5N2XY-Ø20 תנור חימום מקלחת (1)
P9 16A C 3x2.5N2XY-Ø20 תנור חימום מקלחת (2)
P10 16A C 3x2.5N2XY-Ø20 שקעים בארון תקשורת
P11 16A C 3x2.5N2XY-Ø20
P12 16A C 3x2.5N2XY-Ø20
שקעים
AC1 3x20A C 3X20A C3 AC3 3x2.5N2XY-Ø20
AC2 16A C 3x2.5N2XY-Ø20
AC3 16A C 3x2.5N2XY-Ø20
AC4 16A C 3x2.5N2XY-Ø20
AC5 16A C 3x2.5N2XY-Ø20
מ"א בחדרי שינה
יעודכן לפני תכנית יועץ מיזוג
M1 16A C 3x2.5N2XY-Ø20 תריס חשמלי
M2 16A C 3x2.5N2XY-Ø20 תריס חשמלי
M3 16A C 3x2.5N2XY-Ø20 תריס חשמלי
M4 16A C 3x2.5N2XY-Ø20 תריס חשמלי
M5 16A C 3x2.5N2XY-Ø20 תריס חשמלי
M6 16A C 3x2.5N2XY-Ø20 תריס חשמלי
לבירור האם נדרש בקומה זו
P13 16A C
P14 16A C
P15 16A C
שמור
10A C
0 I 1 יד 2 שעון
שעון מכני עם רזרבה תוצרת גריזלין דגם 211 תוצרת גרמניה
C1 מאור כללי
שעון שבת לתאורת פנים
C3 מיזוג אויר
שעון שבת
יעודכן לפני תכנית יועץ מיזוג

תפוצה														תאריך
מנהל הפרויקט	אדריכל	מזמין/יזם	חשמל	קבלן	בטיחות	אקוסטיקה	אינסטלציה	קונסטרוקציה	אדריכל נוף	מטבחים	חברת חשמל	חברת בזק		

מס'	שינויים	תאריך

עודכן ע"י: יפעת

א. בסיס
הנדסת חשמל בע"מ
משרד: יד חרוצים 16, ירושלים 93420
טל: 074-7021015 נייד: 050-6550484
פקס: 077-5131015 דוא"ל: office@ebasis.co.il

שם הפרויקט:
נופיה-אלפי מנשה

שם התכנית:
לוח #1- מגרש 24, נופיה

קנה מידה: 1:50	○ לעיון ○ לאישור ○ למכרז ● לביצוע
תאריך: Date: 05.03.2025	מס' קובץ: File: 675W.dwg
תכנן: יפעת	שרטט: ליאל
אישר: איתן	
מס' עדכון: 0	מס' הגליון: 24
מס' הפרויקט: 675	