

אוריכל פנים	
אינסטיציה	
בסיחת אש	
אקוסטיקה	
חשתי והזרה	
קונסטרוקציה	
קבלו ראש	
ניחול פרויקט	
נמח	
אוריכל	

תחילת כרשור	14.06.2025	
תחילת כרשור	10.04.2025	
תחילת כרשור	31.03.2025	
תחילת כרשור	11.03.2025	
שנתיים	תאריך:	100

הערות

- מזקורא

- מקרא צבעים בתכנית

- | | |
|--------------------------|---|
| תעלות ותריסי אוויר חוזר |  |
| תעלות ותריסי אספקת אוויר |  |
| תעלות ותריסי אוויר צח |  |
| תעלות ותריסי יניקת אוויר |  |
| תעלות ותריסי שיחרור עשן |  |
| צנרת גז וחשמל |  |
| סימון מעגלי מזווג אוויר |  |

191	מבני מגורים צמודי קרקע נופיה אפי' מנשה מגרש 24	שם המזכיר
1:50	מיזוג אוויר ואווירור	שם המזכיר
14.06.2025	קומת גג וטבלאות	שם המזכיר
הצדד מחזורי	4	שם המזכיר
☐ כניסוע ☐ מכוני ☒ אשור ☐ עקני	11.03.2025 יא"ב ארז חנוי	שם המזכיר


Section 1-1

מסדרון מסדרון

5.0 4.0 1.0 2.0

Section 1-1

Section 1-1

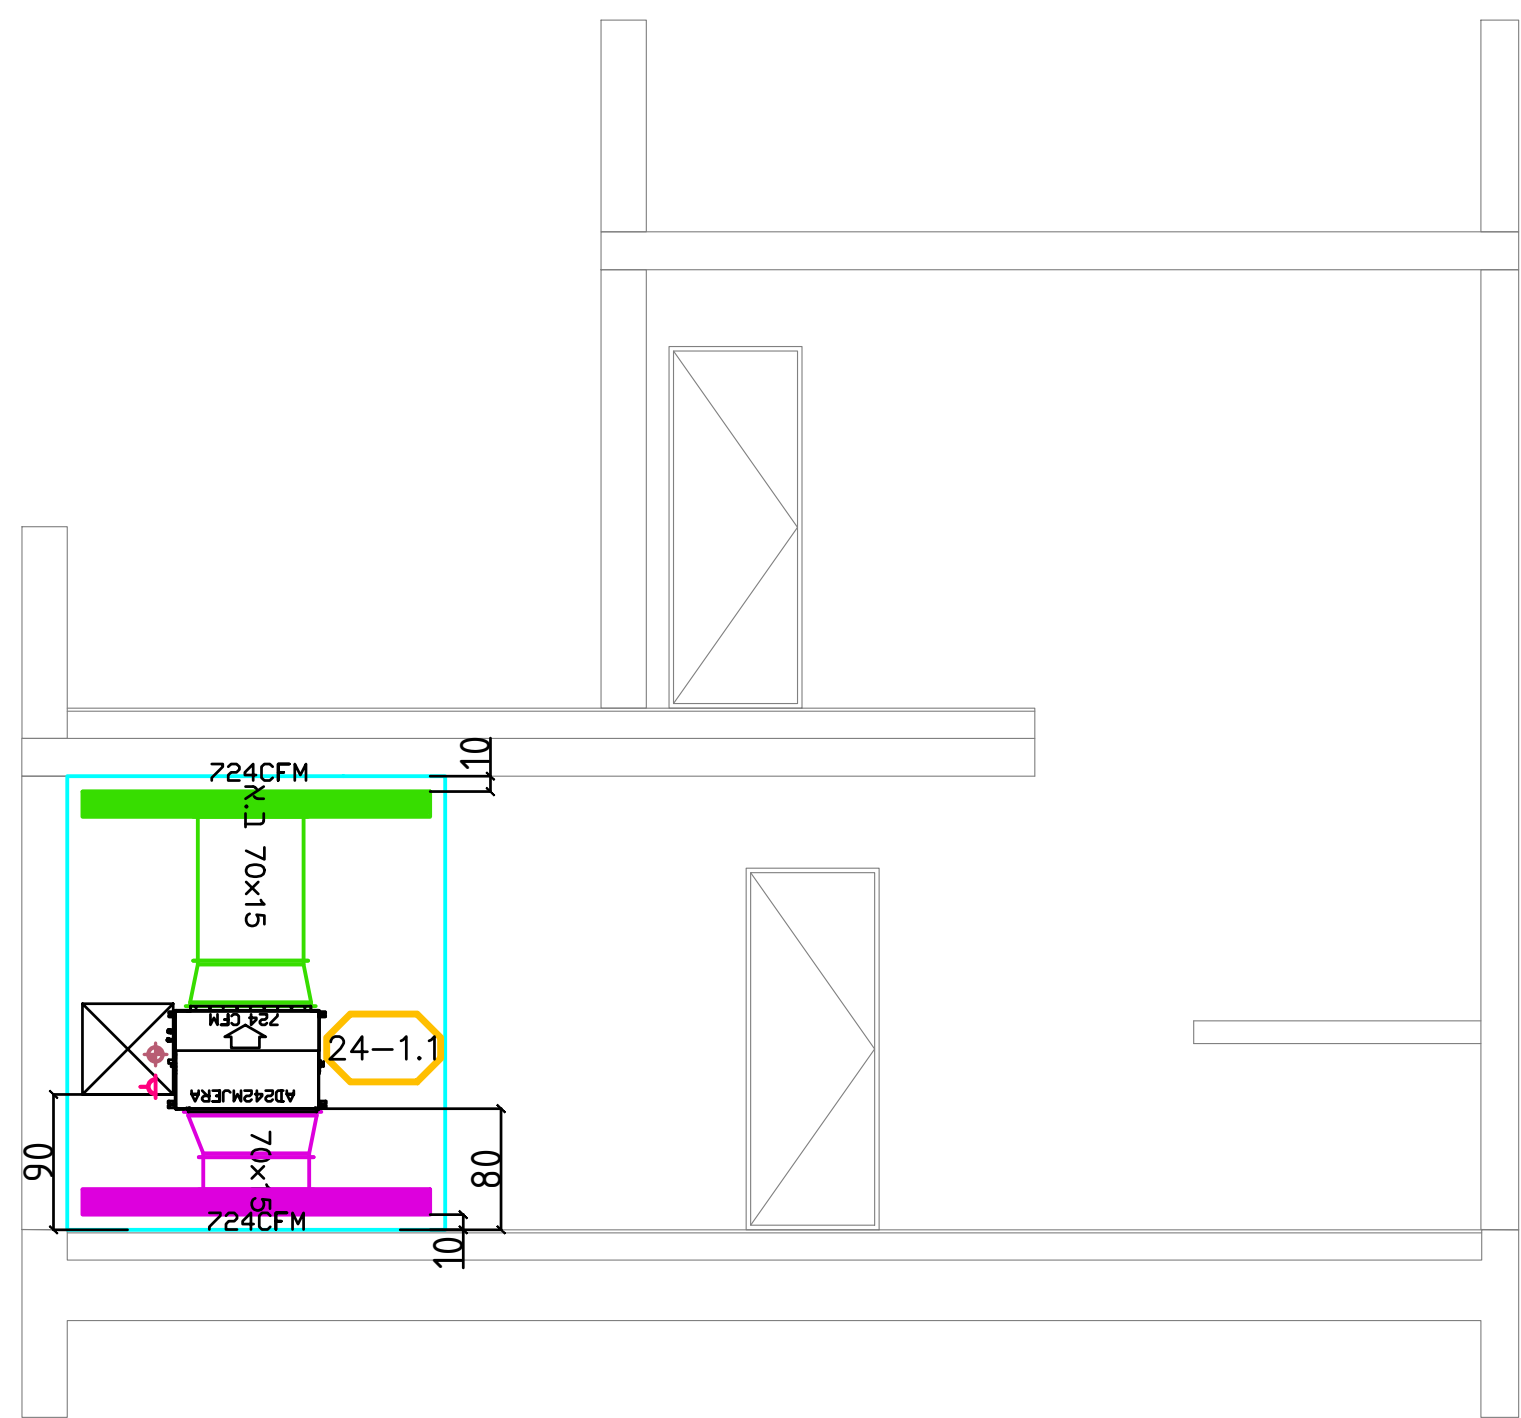

יחידות קצה שמעל 24-1											
חשבוני ציוד	מחזור חום W/Hz/Ph	מידות פני	מידות גוף	משקל KG	רמת רעש dB(A)	ספיקת אוויר CFM	תופסת כוור Btu/h	מאייד	דגם	תוצרת	מס' יחידה בתכנית
---	230/50/1	---	ר"ס 42x18.5/85"	18.5	32	353	15,400	Slim Duct Low ESP	AD162MSERA(D)	Haier	24-1.3 24-1.4 24-1.5 24-1.6
---	230/50/1	---	ר"ס 72x253/105"	33	38	724	24,800	Duct Medium ESP	AD242MJERA	Haier	24-1.1
---	230/50/1	---	ר"ס 20x283/85.5"	10	36	352	9,500	ומאייד עויני	AS092MNERA	Haier	24-1.7

ידידות כסה מעל 2-24											
סנן יעידה בחבנית	חוצרת	גדג	מאייד	תפוקת כוור Blw/h	ספיקת אויר CPM	רמח רעש dB(A)	משקל kg	מידות ממ	מידות פנל	מתח חזנה V/Hz/Ph	חפסן צנר W
24-2, 24-2.2, 24-1.2	Haier	AD182MSER(D)	Slm Duct Low ESP	12,300	324	30	18.5	421x18.5/85	---	230/50/1	---
24-2, 24-2.4	Haier	AD182MSER(D)	Slm Duct Low ESP	19,100	471	33	22.2	421x18.5/117	---	230/50/1	---

מכשירי טלפון 24

AU10NFKERA	: דגם
95,500 BTU/Hr	: תפוקה
40W/163.6A/105V	: מידה
3A25 (A)	: נתון חשמלי
149 ק"ג	: משקל
8.75 [KW]	: הספק נצרך
66 dB(A)	



בסיס בטון בגובה מינימלי 10 ס"מ
יחידת עיבוי עומדת ע"ג בולמי רעידות
לטיפול קבלן מיזוג אוויר

מיקום סופי של המעבים
ייקבע בשטח
בתיאום עם האדריכל
וקבלן מיזוג אוויר

מיקום סופי של הניקוזים
ייקבע בשטח בתאום עם האדריכל
יועץ אינסטלציה וקבלן מיזוג אוויר

מפרט טכני
 AU08NFKERA : דגם
 77.100 BTU/hr : תפוקה
 40W/1633/1057 : מידה
 3x20 (A) : נתיב השמירה
 149 ק"ג : משקל
 6.45 (KW) : צריכת חשמל
 65 dB(A) : רעש



בסיס בטון בגובה מינימלי 10 ס"מ
יחידת עיבוי עומדת ע"ג בולמי רעידות
לטיפול קבלן מיזוג אוויר

מיקום סופי של המעבים
ייקבע בשטח
בתיאום עם האדריכל
וקבלו מיזוג אוויר

מיקום סופי של הניקוזים
ייתבצע בשטח בתאום עם האדריכל
יועץ אינסטלציה וקבלן מיזוג אוויר

אוריג' פנים	אונטסציע	במיתות אש	אקוטסיקה	חשמי ותוארה	קונסטרוקציע	קבלו ראש	ניחול פווינטס	נעמוח	אוריג'י
-------------	----------	-----------	----------	-------------	-------------	----------	---------------	-------	---------

חבנית ראשון	14.06.2025	4
חבנית ראשון	10.04.2025	5
חבנית ראשון	31.03.2025	7
חבנית כעיון	11.03.2025	7
שנתיים	חאריך:	100

הערות

- קרא

- מקרא צבעים בתכנית

- | | |
|--------------------------|---|
| תעלות ותריסי אוויר חוזר |  |
| תעלות ותריסי אספקת אוויר |  |
| תעלות ותריסי אוויר צח |  |
| תעלות ותריסי יניקת אוויר |  |
| תעלות ותריסי שיחרור עשן |  |
| צנרת גז וחשמל |  |
| סימון מעגלי מיוזג אוויר |  |

191	מבני מגורים צמודי קרקע נופיה אפי' מנשה 24 מגרש
1:50	מזיג אוויר ואווירור ש"מ
14.06.2025	קומה ראשונה ושנייה ש"מ
4	ש"מ
מחירים	ש"מ
☐ בלעז ☐ נכסור ☒ לאשור ☐ עיון	14.03.2025 חגית יאיר ארז חנוכה

כלל יחידות המיזוג אשר נמצאות בתוך נגרות יש לתאם סופית מול אדריכל ונגרות

Court 24
1st Floor
Option **No3**
VRF duct units

