


Option No4
VRF duct and wall mounted
units on the 1st floor.
And inverter wall mounted
units on th 2nd floor.



Option No4
VRF duct and wall mounted
units on the 1st floor.
And inverter wall mounted
units on th 2nd floor.

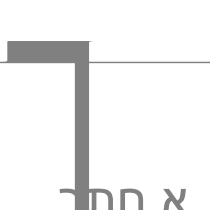

אודינג	קטח
נהוי פרוינט	קבן ואש
קונסטרוקציע	חשתי וחוארה
אוקסידה	בטירוח אש
אינסטיצה	אודינג פנים

תחילת העיון	25.06.2025	
שניות:	חזרתי:	סך:

הערות

- מקרא

- ## מקרא צבעים


- 
- X-X

191	מבני מגורים צמודי קרקע נופיה אפי' מנשה מגרש 3
סל דריסה	סל דריסה
1:50	מיזוג אוויר ואווירורר
סל	קומה ראשונה ושנייה
25.06.2025	סל מדידה
תציר מדידה	
	
סל מדידה	סל מדידה
   	לעון
לביצע	אישור
	מסמך
	25.06.2025
	אחיה
	גנני מדידה אייל ארז

Court 3 1st Floor

Option №4

VRF duct and wall mounted
units on the 1st floor.
And inverter wall mounted
units on th 2nd floor.

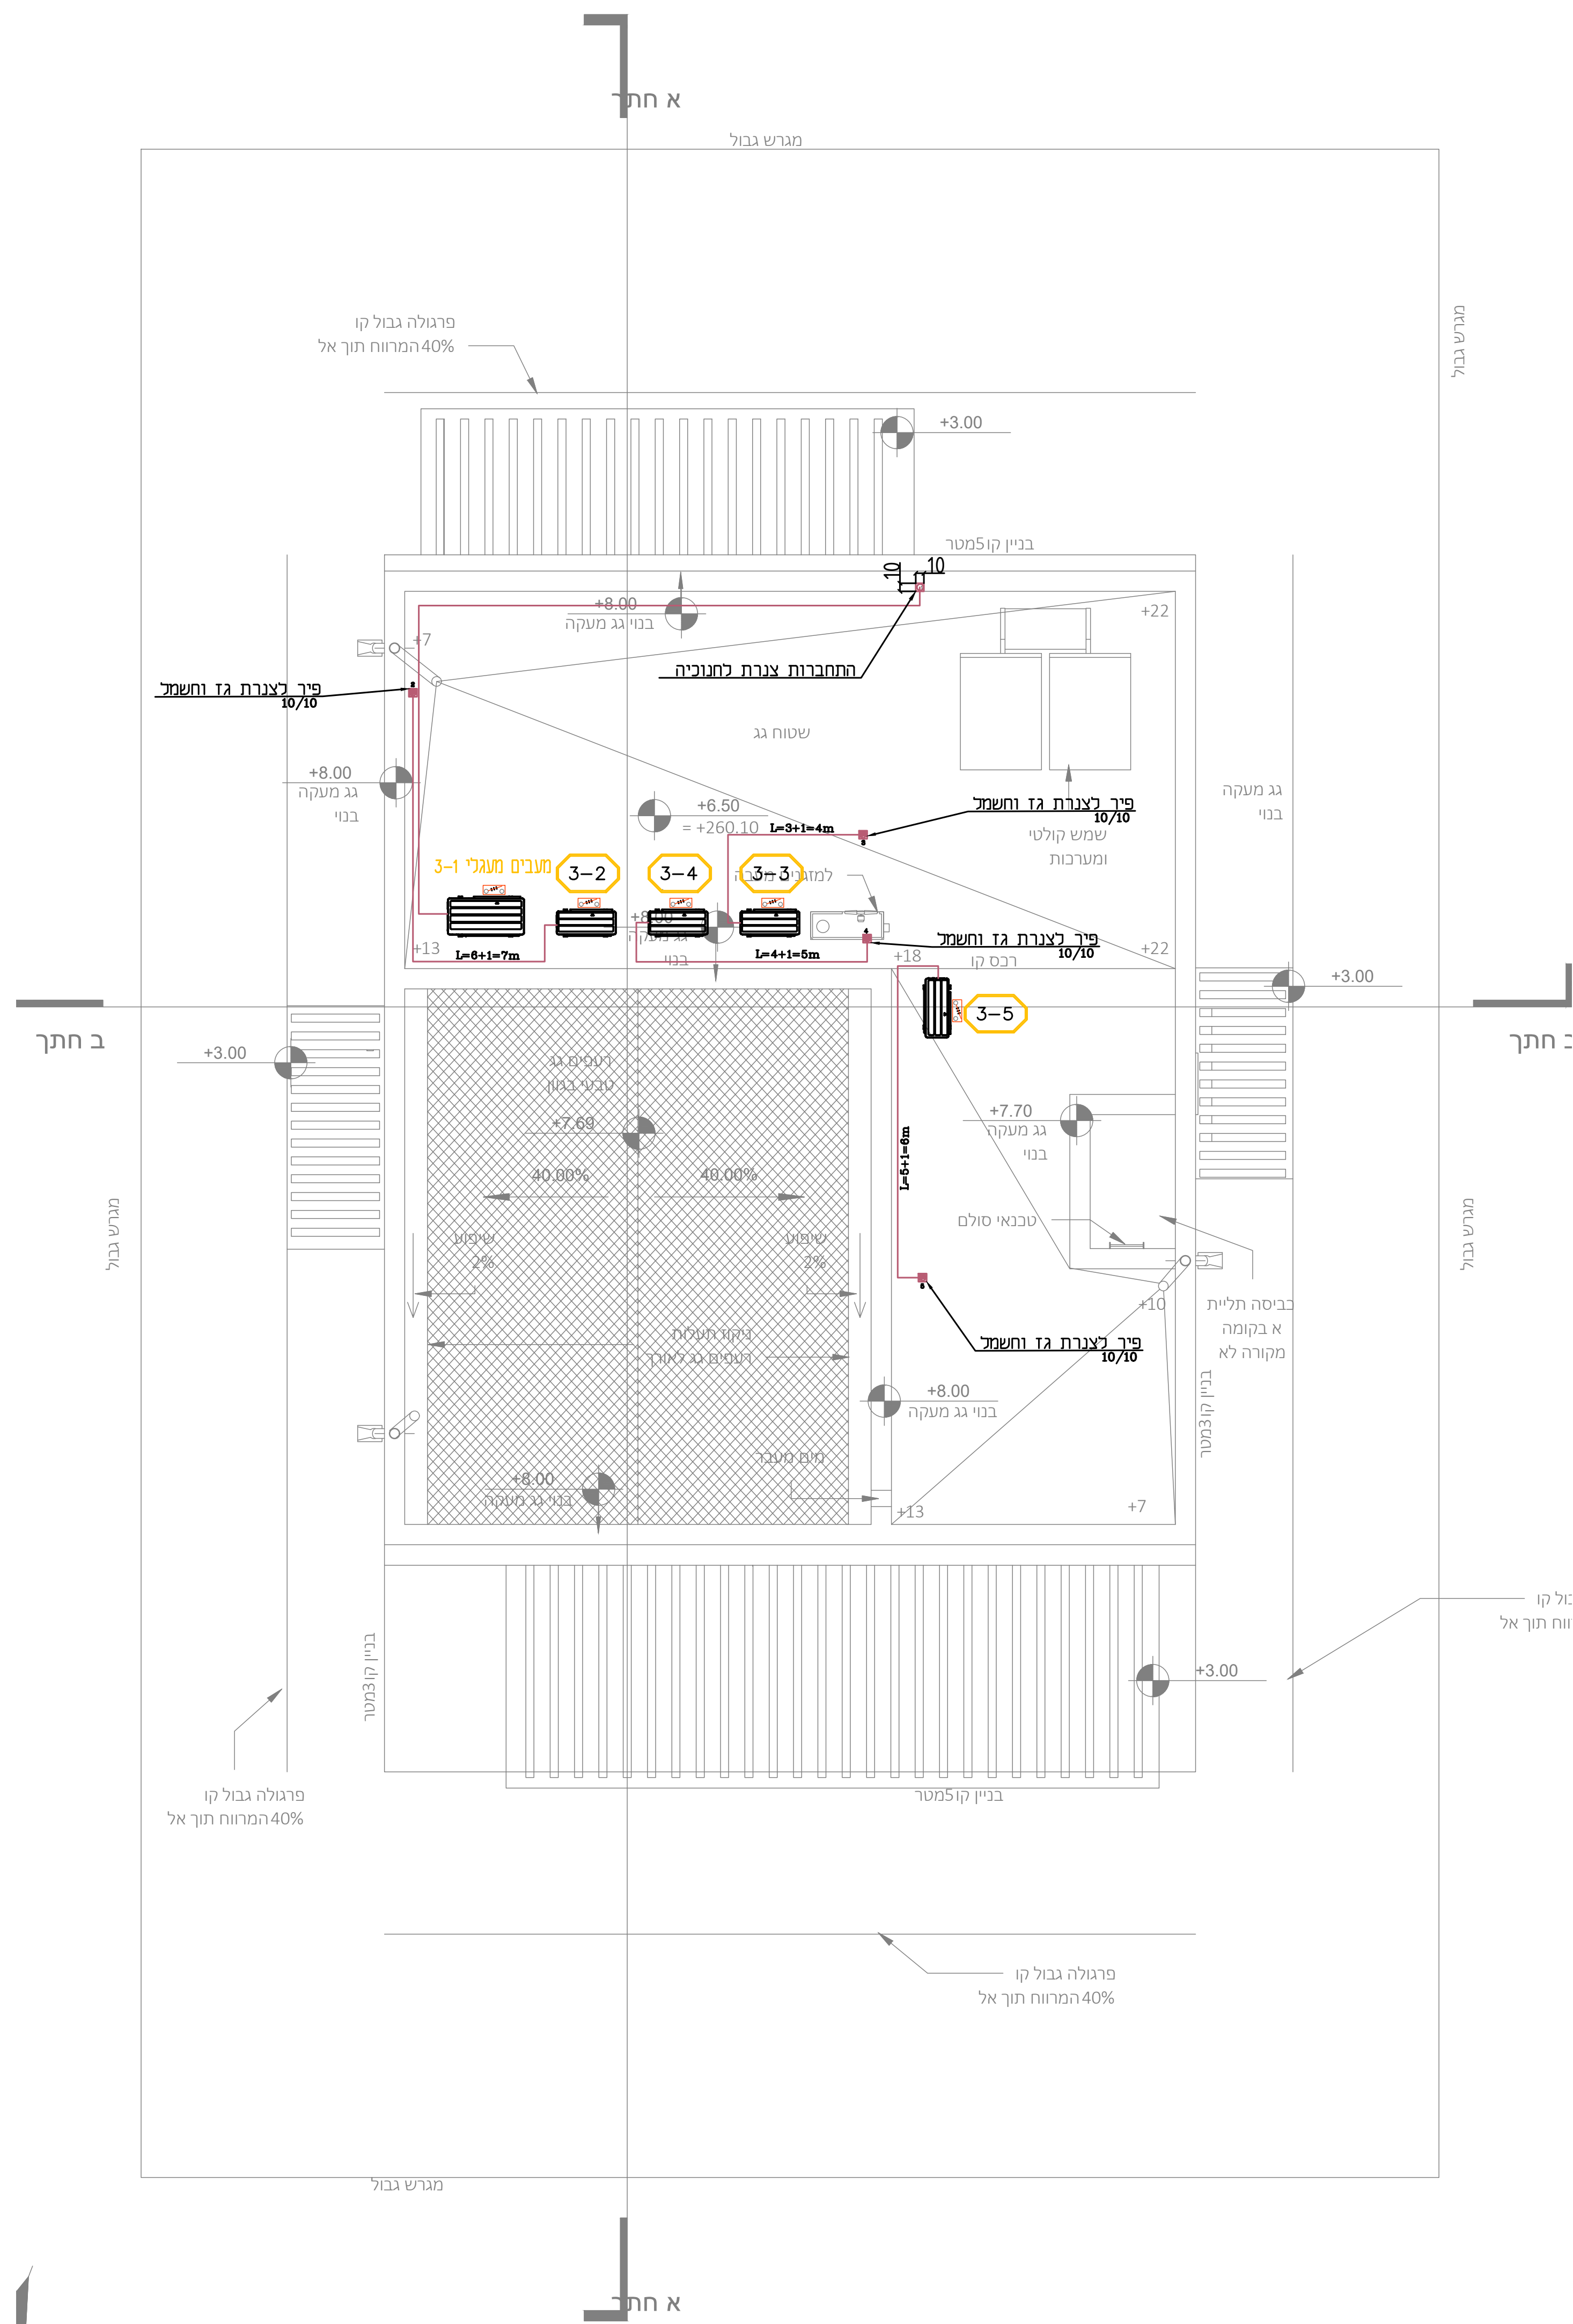

דגם : X-280UL/C1-2
תפוקה : 28000 Btu/h
מחזור : 46.2W/161.5/94.7
רמת רעש : 32dB(A)
ספיקת אוויר : 324 CFM
מסתקת קירור : 12,300 Btu/h
מאייד : Slim Duct Low ESP
תוצרת : Tadiran
דגם : GMV-ND38PLS/C1-T
מס' יחידה בתכנית : 3-1.3

דגם : X-280UL/C1-2
תפוקה : 28000 Btu/h
מחזור : 46.2W/161.5/94.7
רמת רעש : 32dB(A)
ספיקת אוויר : 324 CFM
מסתקת קירור : 12,300 Btu/h
מאייד : Slim Duct Low ESP
תוצרת : Tadiran
דגם : GMV-ND38PLS/C1-T
מס' יחידה בתכנית : 3-1.3

דגם : X-280UL/C1-2
תפוקה : 28000 Btu/h
מחזור : 46.2W/161.5/94.7
רמת רעש : 32dB(A)
ספיקת אוויר : 324 CFM
מסתקת קירור : 12,300 Btu/h
מאייד : Slim Duct Low ESP
תוצרת : Tadiran
דגם : GMV-ND38PLS/C1-T
מס' יחידה בתכנית : 3-1.3

דגם : X-280UL/C1-2
תפוקה : 28000 Btu/h
מחזור : 46.2W/161.5/94.7
רמת רעש : 32dB(A)
ספיקת אוויר : 324 CFM
מסתקת קירור : 12,300 Btu/h
מאייד : Slim Duct Low ESP
תוצרת : Tadiran
דגם : GMV-ND38PLS/C1-T
מס' יחידה בתכנית : 3-1.3


דגם : X-280UL/C1-2
תפוקה : 28000 Btu/h
מחזור : 46.2W/161.5/94.7
רמת רעש : 32dB(A)
ספיקת אוויר : 324 CFM
מסתקת קירור : 12,300 Btu/h
מאייד : Slim Duct Low ESP
תוצרת : Tadiran
דגם : GMV-ND38PLS/C1-T
מס' יחידה בתכנית : 3-1.3

יחידות מיזוג סניגל-מאייד+מעבה										
מס' יחידה בתכנית	תוצרת	דגם	מאייד	תפוקת קירור Btu/h	ספיקת אוויר CFM	רמת רעש db(A)	משקל KG	מידות גובה	מידות פני	מחזור V/Hz/Ph
3-1.3	Tadiran	GMV-ND38PLS/C1-T	Slim Duct Low ESP	12,300	324	31	19	46.2W/203/101	---	230/50/1
3-1.4	Tadiran	GMV-ND56PLS/C1-T	Slim Duct Low ESP	19,100	441	35	25	46.2W/203/101	---	230/50/1
3-1.2	Tadiran	GMV-ND71PLS/C1-T	Slim Duct Low ESP	24,200	647	37	31	46.2W/203/101	---	230/50/1
3-1.5	Tadiran	AS092MNERA	מאייד עיני	9,500	352	36	10	20W/283/85.5	---	230/50/1

יחידות מיזוג סינגל-מאייד+מעבה									
מס' יחידה בתכנית	תוצרת	דגם	תפוקת קירור Btu/h	ספיקת אוויר CFM	הספק עבודה למנוע W	מידות מאייד	מידות מעבה	נחיר דגם C	הערות
3-4 3-5	Tadiran	ALPHA PRO INV 140 NG	9,210	320	0,800	21.1W/29.12/89.4	33W/55.52/73.2	1x100	חזנה במאייד

יחידות מיזוג סינגל-מאייד+מעבה									
מס' יחידה בתכנית	תוצרת	דגם	תפוקת קירור Btu/h	ספיקת אוויר CFM	הספק עבודה למנוע W	מידות מאייד	מידות מעבה	נחיר דגם C	הערות
3-23-3	Tadiran	ALPHA PRO INV 180 NG	11,940	380	1,100	21.1W/29.12/89.4	33W/55.52/73.2	1x100	חזנה במאייד

#	Model name	length in project	factory length
3-4	ALFA PRO INV 140 NG	4.0	15
3-5	ALFA PRO INV 140 NG	6.0	15
3-2	ALFA PRO INV 180 NG	7.0	15
3-3	ALFA PRO INV 180 NG	5.0	15

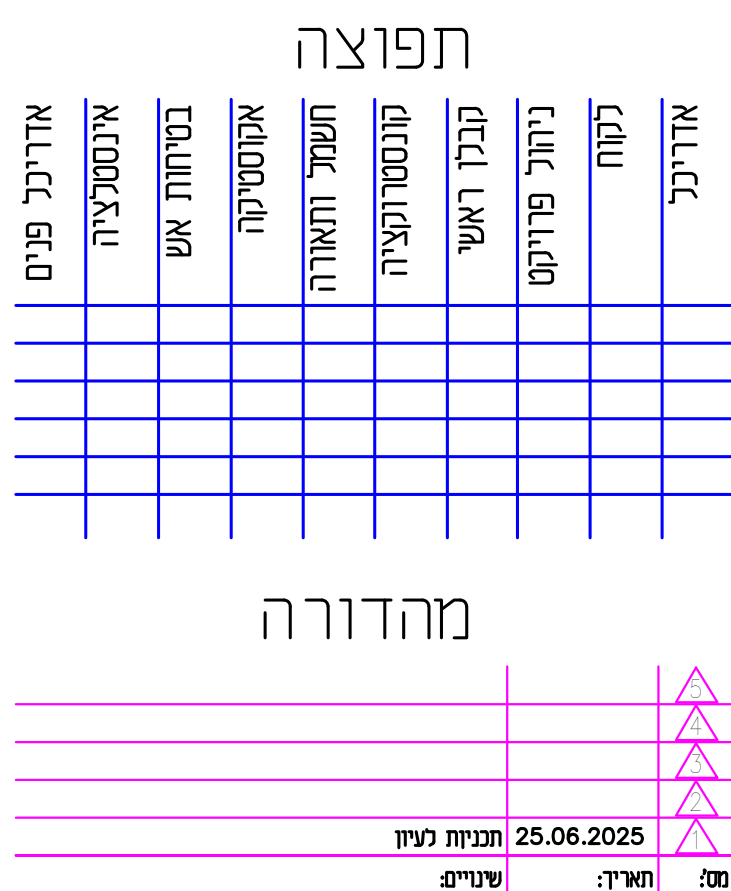

המבצע אחראי למידות ובהתאמתן למציאות בכל מקרה של אי התאמה, סתירה או טעות עליו להודיע למתכנן לפני התקדמותו בביצועו. אין לנהוג מידות על סמך מדידה בשרטוט. אין לעשות כל שימוש בתוכנית זו או ברעיונות והגומים בה ללא אישור בכתב מאת המתכנן.

הערות

- כל תעלות מחוץ למבנה יבודדו בבידוד אקוסטי בעובי 2" מידות התעלות הן מידות פח
- תעלות מזוג בתוך המבנה יבודדו בבידוד אקוסטי פנימי 1" מידות התעלות הן מידות פח
- תעלות אוויר צח יבודדו בבידוד סרמי 1" מידות התעלות הן מידות פח
- יש לאסום בסיקורן את פינות החיבור של תעלות מיזוג אוויר לפני כיפוף הפורום המתחברים

מקרא

- מפ- מפוח
- מ.א.ג. - מפוח אוויר קירי
- מ.א.ת. - מפוח אוויר תתקרי
- ת.א.ת. - תריס אוויר חוזר
- ת.א.צ. - תריס אוויר צח
- ב.א. - בידוד אקוסטי
- ב.ס. - בידוד סרמי
- כ.ב. - כלא בידוד
- ד.א. - דמפר אש
- סרמסטט לח הפעלה
- שקע חשמל לספוק יועץ חשמל
- שקע תלת פאזי לספוק יועץ חשמל
- מפסק בסנחון חד פאזי לספוק יועץ חשמל
- מפסק בסנחון תלת פאזי לספוק יועץ חשמל
- ניקוז מאייד לספוק יועץ אינסטלציה
- גובה 25 ס"מ מתחתית גובה המאייד
- שלט הפעלה אלחוטי

מקרא צבעים בתכנית

- תעלות ותריסי אוויר חוזר
- תעלות ותריסי אספקת אוויר
- תעלות ותריסי אוויר צח
- תעלות ותריסי יניקת אוויר
- תעלות ותריסי שיחרור עשן
- צנרת גז וחשמל
- סימון מעגלי מיזוג אוויר

191	מבני מגורים צמודי קרקע נופיה אפרי מנשה מגרש 3
1:50	מיזוג אוויר ואיוורור
25.06.2025	קומת גג וטבלאות
25.06.2025	תאריך פתיחה
25.06.2025	תאריך סיום
25.06.2025	תאריך סיום
25.06.2025	תאריך סיום
25.06.2025	תאריך סיום
25.06.2025	תאריך סיום
25.06.2025	תאריך סיום

