


מתכננים:

ניהול פרויקט
מהיסוד - בן סולומון
פיקוח
מהיסוד - בן סולומון
קונסטרוקציה
ערן שילר
מיזוג אוויר
אייל ארז מהנדסים ויועצים בע"מ
אינסטלציה
איתן אלמסי
חשמל
איתן בסיס
אלומיניום
נוף
נתי בלוקא
חשמל חכם
חימום תת רצפתי
איטום
צבי טל
אקוסטיקה
מעליות
קרקע וביסוס
דיה הנדסת קרקע וביסוס
רישוי

± 0.00 = +253.50
הערות: 1. תכנית זו יש לקרוא יחד עם תכנית הריטשים. 2. גובה אבסולוטי: ראו תכנית פיתוח. 3. המידות הן בין קירות הבניה ולא כולל פחים. 4. פיתוח השטח סביב הבנוה, כולל, מדרגות, גדרות, שבילים, ריצופים, שיפועים וכו'. 5. איסוס קירות ורצפות הבנוה כמתע עם הקרקע ובידוד תרמי לאורך העמודים והקורות וכל התפריה. כליות או עם סימני גיבסון. ראו תכנית קונסטרוקציה. 6. אף חים יבוצע בכל מישור אופקי הבולם מהגבון. 7. פוח תרמי בממד"ד ע"פ מפרט חומקיר, מאושר ט"י פיקוד העורף. המבצע אחראי לסידות : עליו לבקר ולבדוק את כל המידות בתכנית ובמקום המבנוה. במסגרת של מנות או אי התאמה בתכנית /או בבנוי, עליו להודיע על כך מיד לאדריכל בסדר המשיך בעבודתו. המבצע יתחשב או וקע בתכנית שאושר לכניצוע. המבצע יחזיק באחר, לכל שטח, של מועדכו של תכנית. אל לקבוע מידות על ידי חדייה בשר מוס. התכנית הינה רכוש האדריכל ואין לשנותה כל שימוש בה או ברעיונות הגלומים בה, אלא באישור בכתב מהאדריכל. מוהנס /או' יושע אשר שמו רשום בתכנית זו, נושא לכיד באחריות המקצועית והטקטית לתכנית. על המפעק והמכניז לודא התאמת התכנית האדריכלית "לכניצוע" לתכנית ויתר, המכר והתכנית המאושרות ע"י כל הגורמים הרשמיים. התכנית כוללת את כל האמצעים והידוע עד ליום תחמשת.

משרד קירות:

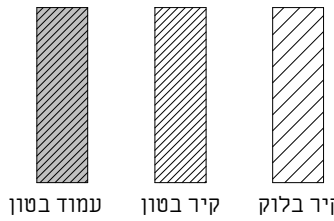

תאריך	תיאור	מהדורה
22.09.2025	מכרז	1

אדריכלות


שם המסין:	CLIENT NAME:
נופיה קבוצת רכישה	
שם הפרויקט:	PROJECT NAME:
נופיה - מגרש 4	
שם הגליון:	DRAWING NAME:
גליון שער	
מספר גליון:	SHEET NUMBER:
A3-1-100	
מהדורה:	EDITION:
SCALE:	קנה מידה:
STATUS:	סטוס
למכרז	
שורס ע"י:	נבדק ע"י:
תאריך:	DATE:
22.09.25	



נויסן חיינו אדריכלים
מודד והדורס 2, בית חירות
09-9545642
office@nh-arch.com
www.nh-arch.com

נופיה - מגרש 4

מס' גליון	שם גליון	מהדורה	תאריך הפצת מהדורה
A3-1-100	גליון שער	1	22.09.2025
A3-1-101	קומת קרקע	1	22.09.2025
A3-1-102	קומת גג	1	22.09.2025
A3-2-200	חזיתות 1	1	22.09.2025
A3-2-201	חזיתות 2	1	22.09.2025
A3-3-100	חתכים	1	22.09.2025
A3-4-103	פרטים	1	22.09.2025
A3-4-104	פרטי פרגולה	1	22.09.2025
A3-6-1000	רשימת פתחים	1	22.09.2025

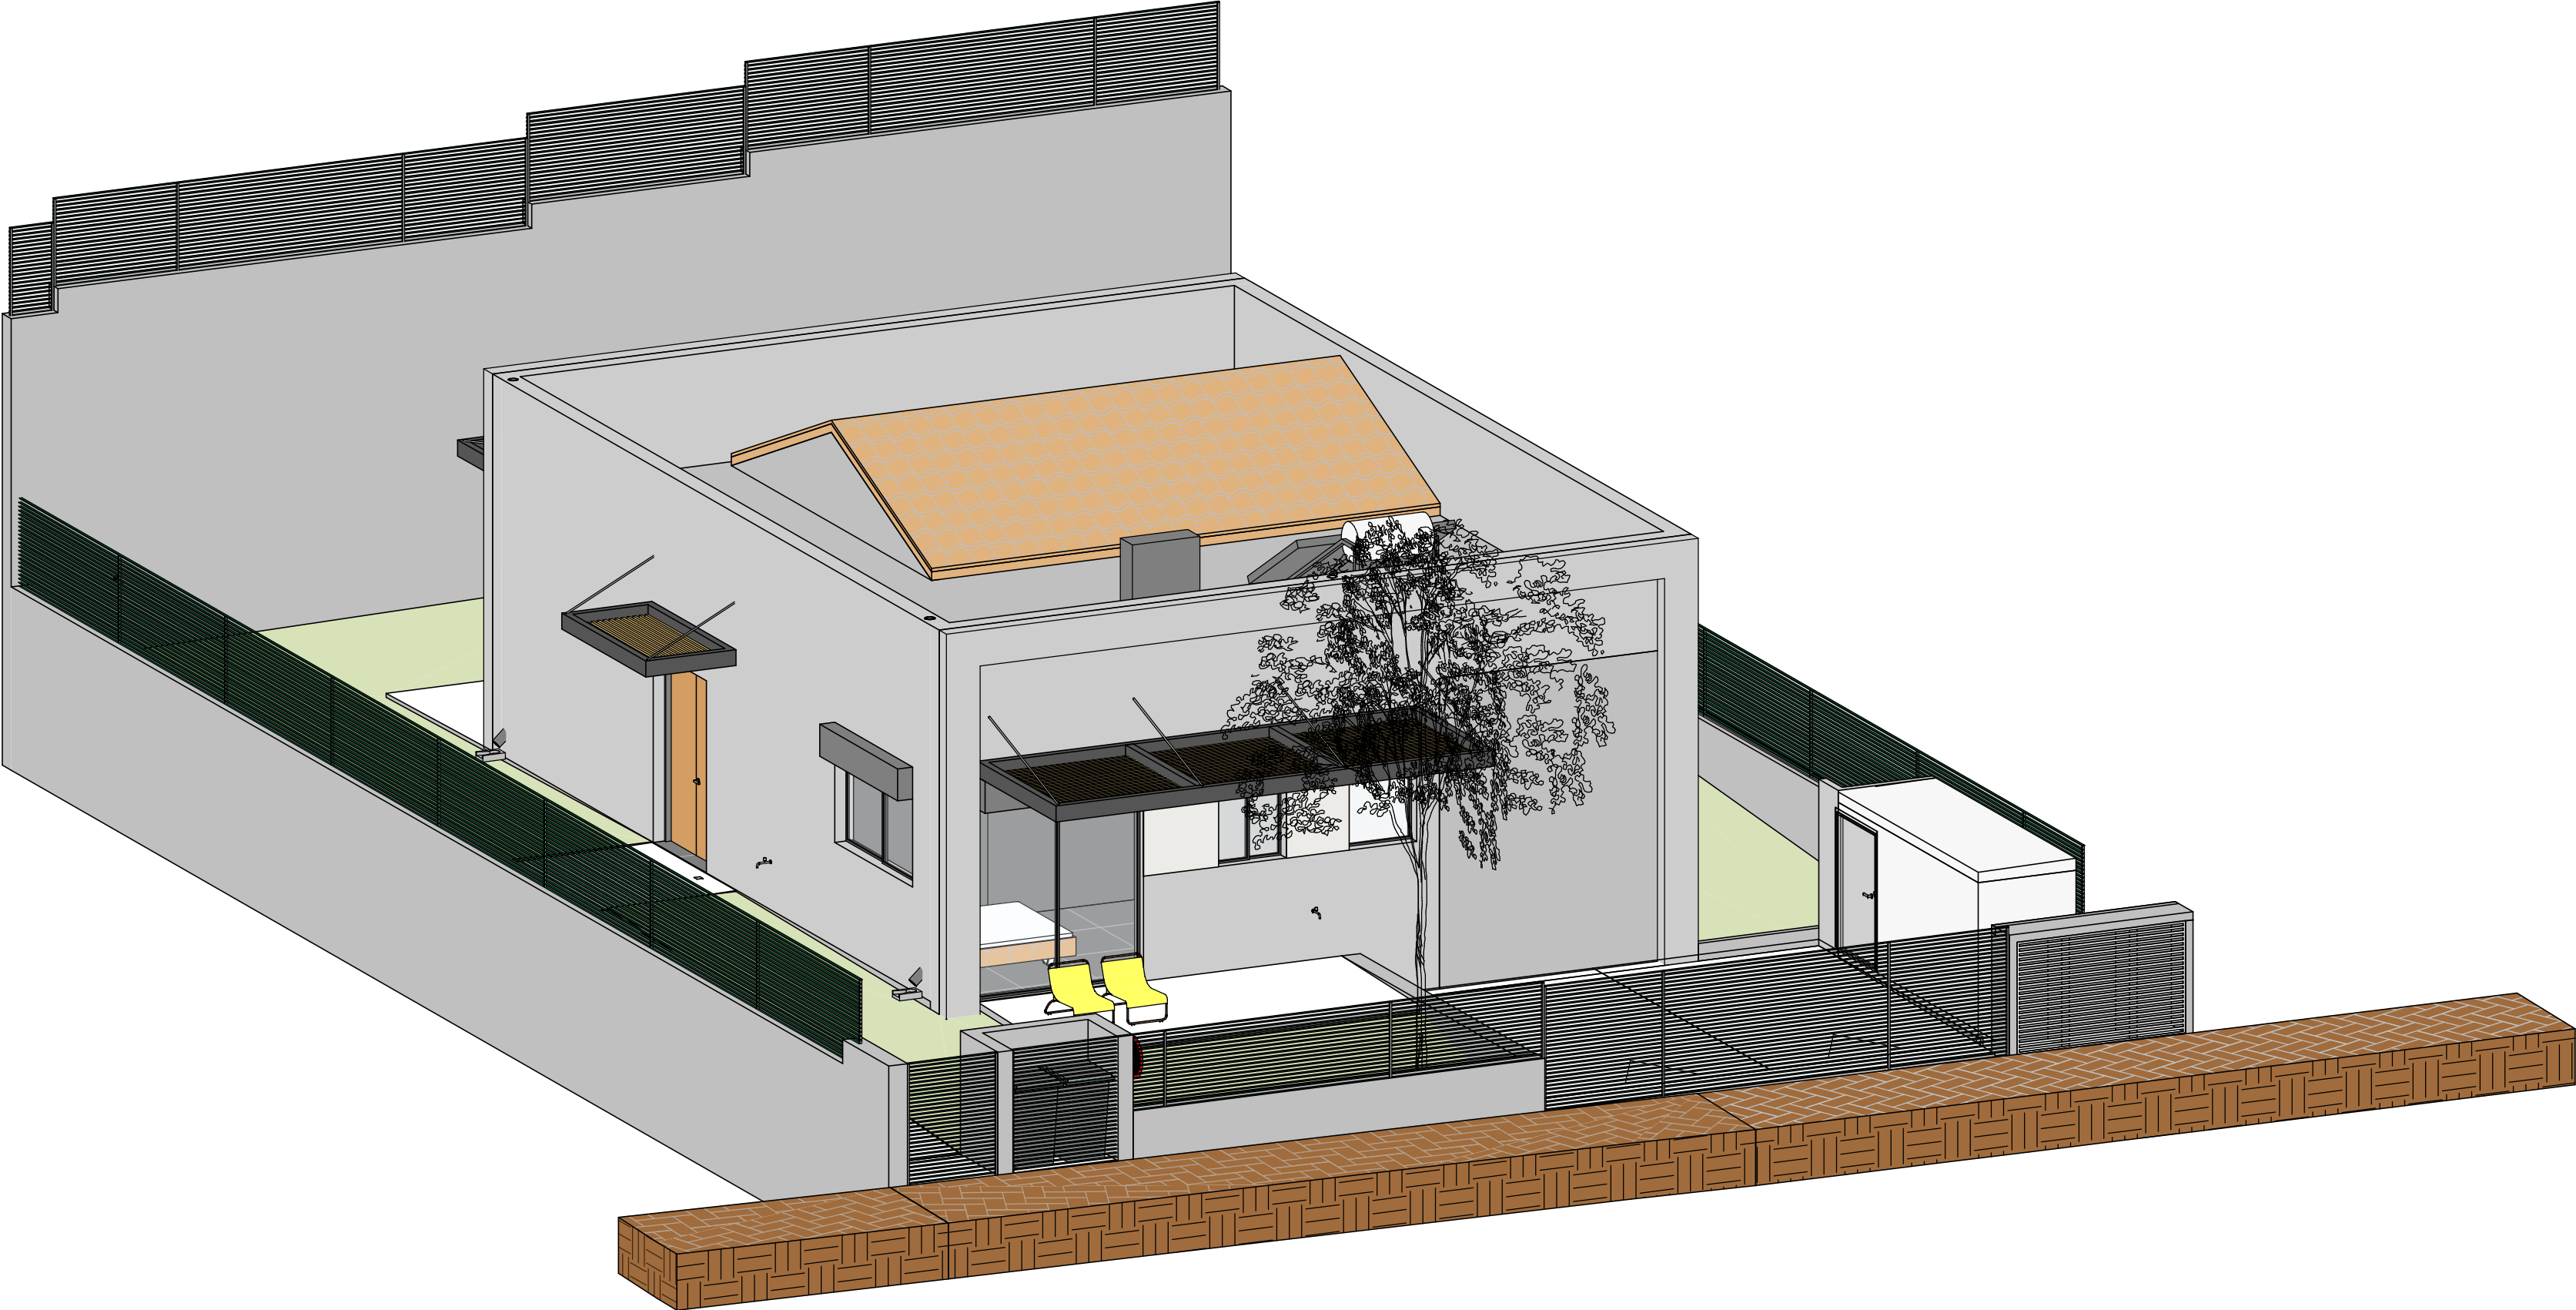

ניהול פרויקט
מהיסוד - בן סולומון
פיקוח
מהיסוד - בן סולומון
קונסטרוקציה
ערן שילר
מיזוג אוויר
אייל ארז מהנדסים ויועצים בע"מ
אינסטלציה
איתן אלמסי
חשמל
איתן בסיס
אלומיניום
נוף
נתי בלוקא
חשמל חכם
חימום תת רצפתי
איטום
צבי טל
אקוסטיקה
מעליות
קרקע וביסוס
דיה הנדסת קרקע וביסוס
רישוי

הערה:
הנתונים אינם מייצגים את תוצאות המבחן. המבחן נעשה באמצעות מערכת אוטומטית, ולכן ישנן טעויות אפשריות. 


[illegible]

CLIENT NAME:		המחלקה	
נופיה קבוצת רכישה			
PROJECT NAME:		סדרת הפרויקט	
נופיה - מגרש 4			
DRAWING NAME:		סדרת הגיליון	
קומת קרקע			
SHEET NUMBER:		מספר הגיליון	
A3-1-101			
SCALE:	קנה מידה:	EDITION:	דפוס:
1 : 50			
STATUS:	סטוס		
למכור			
	[בין ע"י]	דפוס ע"י:	
DATE:	22.09.25	אריך:	

NeumanHaynerArchitects

יומן חיינר אדריכלים
רודר ההדרים 2, בית חירות
99-9545842 טל

office@nh-arch.com
www.nh-arch.com

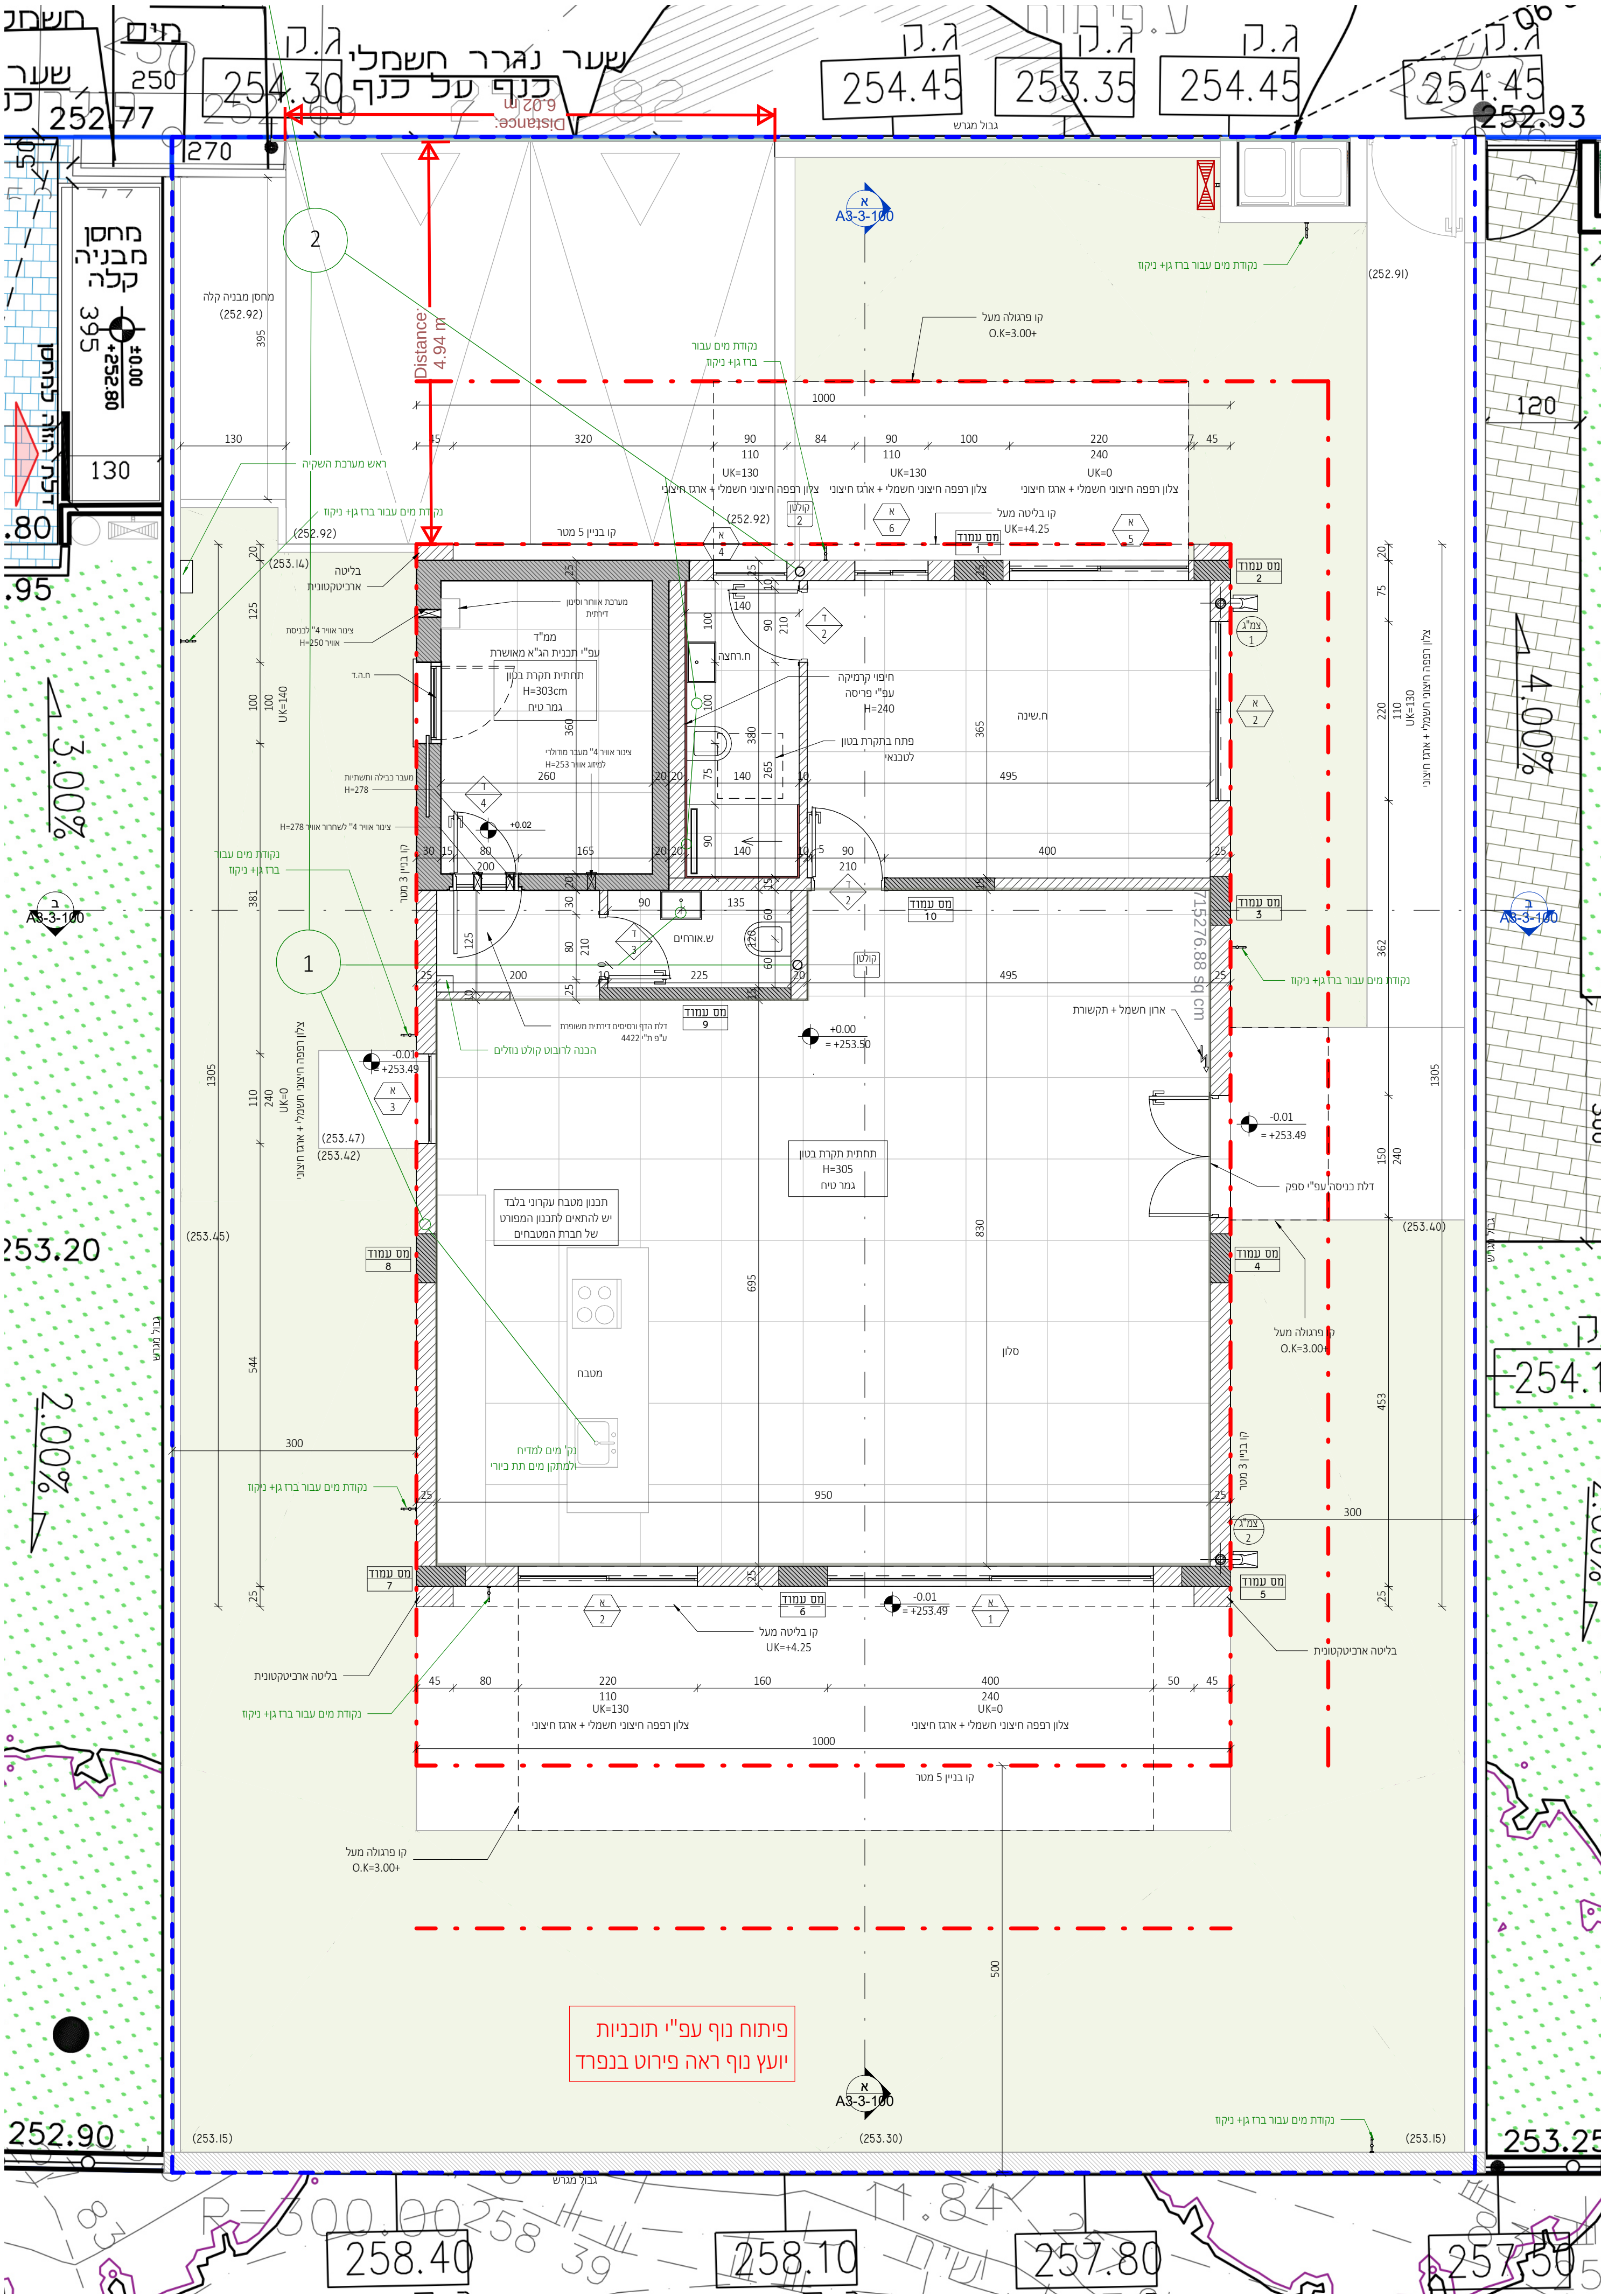

1. יש לעבוד במקביל לתכניות יועצים המאושרות על ידי האדריכל.
2. פרטי ספי חלון - עפ"י חוברת אלומיניום של הספק הנבחר ובתיאום מול אדריכל.
3. חימום תת רצפתי (במידה ויש במגרש זה) עפ"י פרטי הספק ובתיאום מול אדריכל.
4. יש לעבוד במקביל לתכניות עיצוב פנים (במידה ויש מעצב פנים במגרש זה) המאושרות על ידי האדריכל.
5. באחריות הקבלן לעדכן את האדריכל על אי התאמה בין התכניות יועצים לאדריכלות.
6. כל הדלתות לפי מפרט מצורף.
7. כל אלמנטי הבטון יקבלו התייחסות תרמית לפי הנחיות יועץ.
8. פרטי איטום, בידוד וניקוז עפ"י תכניות יועצים ובאחריות הקבלן.


1 : 50

מתכנים:

ניהול פרויקט
מהיסוד - בן סולמון
פיקוח
מהיסוד - בן סולמון
קונסטרוקציה
ערן שילר
מיזוג אוויר
אייל ארז מהנדסים ויועצים בע"מ
אינסטלציה
איתן אלמסי
חשמל
איתן בסיס
אלומיניום
נוף
נתי בלוקא
חשמל חכם
חימום תת רצפתי
איטום
צבי טל
אקוסטיקה
מעליות
קרקע וביסוס
דיה הנדסת קרקע וביסוס
רישוי

± 0.00 = +253.50
הערות: 1. תכנית זו יש לקרוא יחד עם תכניות הריטשים. 2. גובה אבטמנטיס: ראו תכנית פיתוח. 3. הפרדות הן בין קירות הבניה ולא כולל פיתח. 4. פיתוח השטח סביב הבנוה, כולל, מדרגות, גדרות, שבילים, ריצופים, שטחים גברהם, חניה וגן ראו תכנית פיתוח. 5. איטום קירות ורצפות הבנוה כמנוע עם הקרקע ובידוד תרמי לאורך העמודים והקירות מכל הצדדים. כלירות או עם סימני (גובה) - ראו תכנית קונסטרוקציה 6. אף דום יבוצע בכל מישור אופקי הכולל מהבנוה. 7. פיתח תרמי במסד - ע"פ מפרט תרמוקיר, מאושר ע"י פיקוח העודף.
המבצע אחראי למידות: עלי לברר ולבדוק את כל המידות בתכנית ובקטעם הנבונה. במסגרת של מידות או אי התאמה בתכנית /או בבנוה, עלי להודיע על כך מיד לאדריכל בסרט המשיך הנבונה. המבצע יישמש את ויק בתכנית שאושר לכניס. המבצע יחזיק באחר, בכל עת, של מידות של תכנית. אין לקבוע מידות של ידי מדידה בשטח. התכנית רחבה רחבה האדריכל יאין לשטח כל שימוש בה או ברעיונות הגולמים בה, אלא באישור כותב מהאדריכל. מחנדים /או יועץ אשר שמו רשום בתכנית זו, נושא לכך באחריות המקצועית והתקנית לתכנית. על המפקח והמבצע לודא התאמת התכנית האדריכלית "כניס" לתכנית יחידה, המכר והתכנית האושרות ע"י כל גורמים הרשמיים. התכנית כוללת את כל האמצעים והידוע על ליום תחלפת.

משרד קירות:

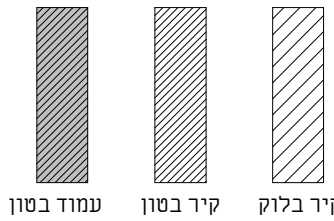

תאריך	תיאור	מהדורה
22.09.2025	מכר	1


אדריכלות

שם המסין:	CLIENT NAME:
נופיה קבוצת רכישה	
שם הפרויקט:	PROJECT NAME:
נופיה - מגרש 4	
שם הגליון:	DRAWING NAME:
חזיתות 1	
מספר גליון:	SHEET NUMBER:
A3-2-200	
תחלודה:	EDITION:
קנה מידה:	SCALE:
1 : 50	
סטוס:	STATUS:
למכר	
שורטס עיי:	נבדק עיי:
תאריך:	DATE:
22.09.25	

NeumanHaynerArchitects

נויטן חיינר אדריכלים
מודד והנדס 2, בית חירות
09-9546842 78
office@nh-arch.com
www.nh-arch.com


22/09/2025 10:27:59

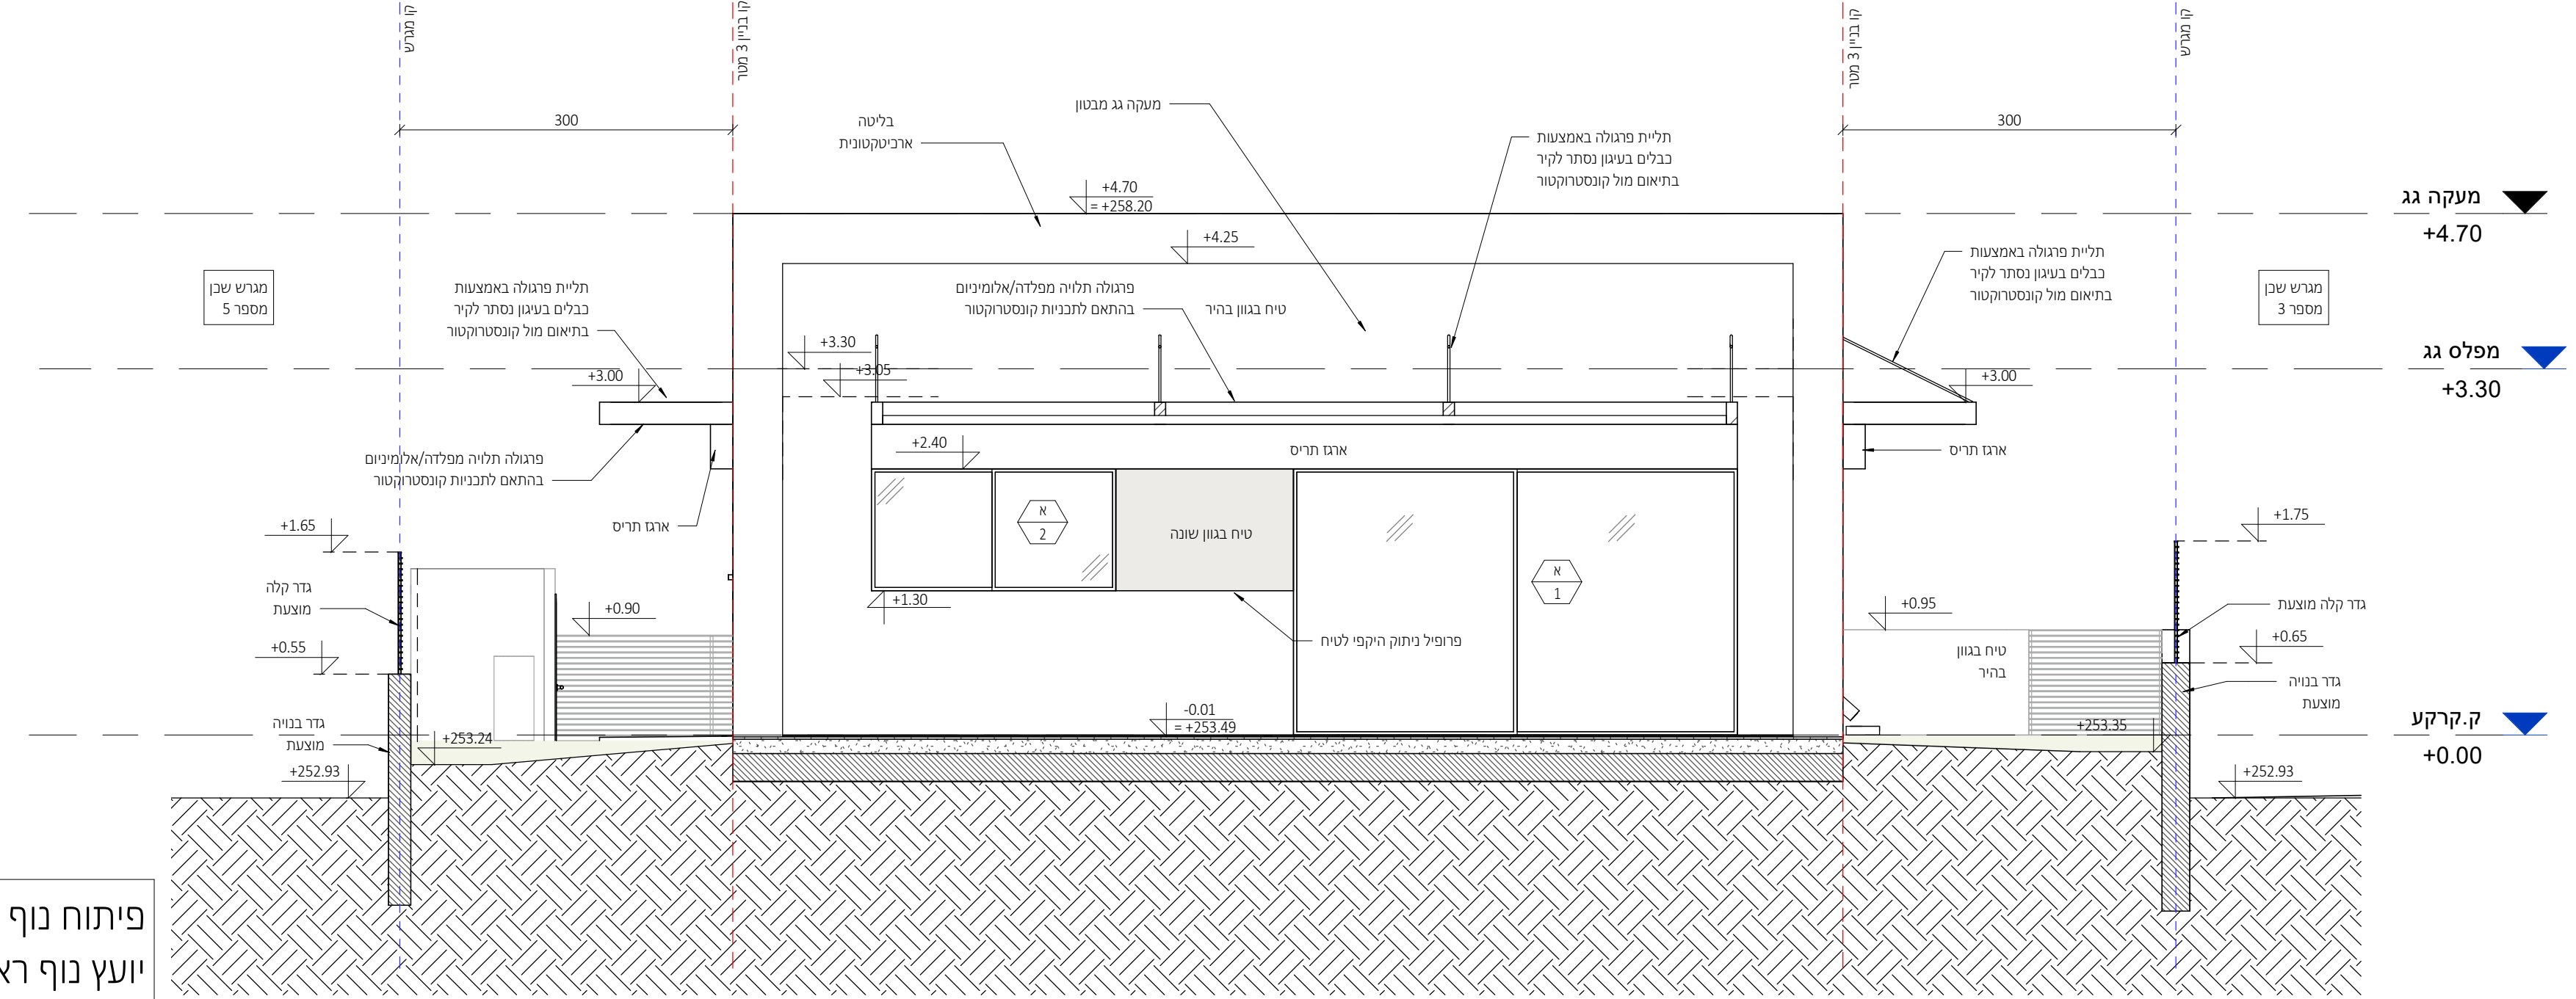

פיתוח נוף עפ"י תוכניות
יועץ נוף ראה פירוט בנפרד

חזית דרומית

1 : 50

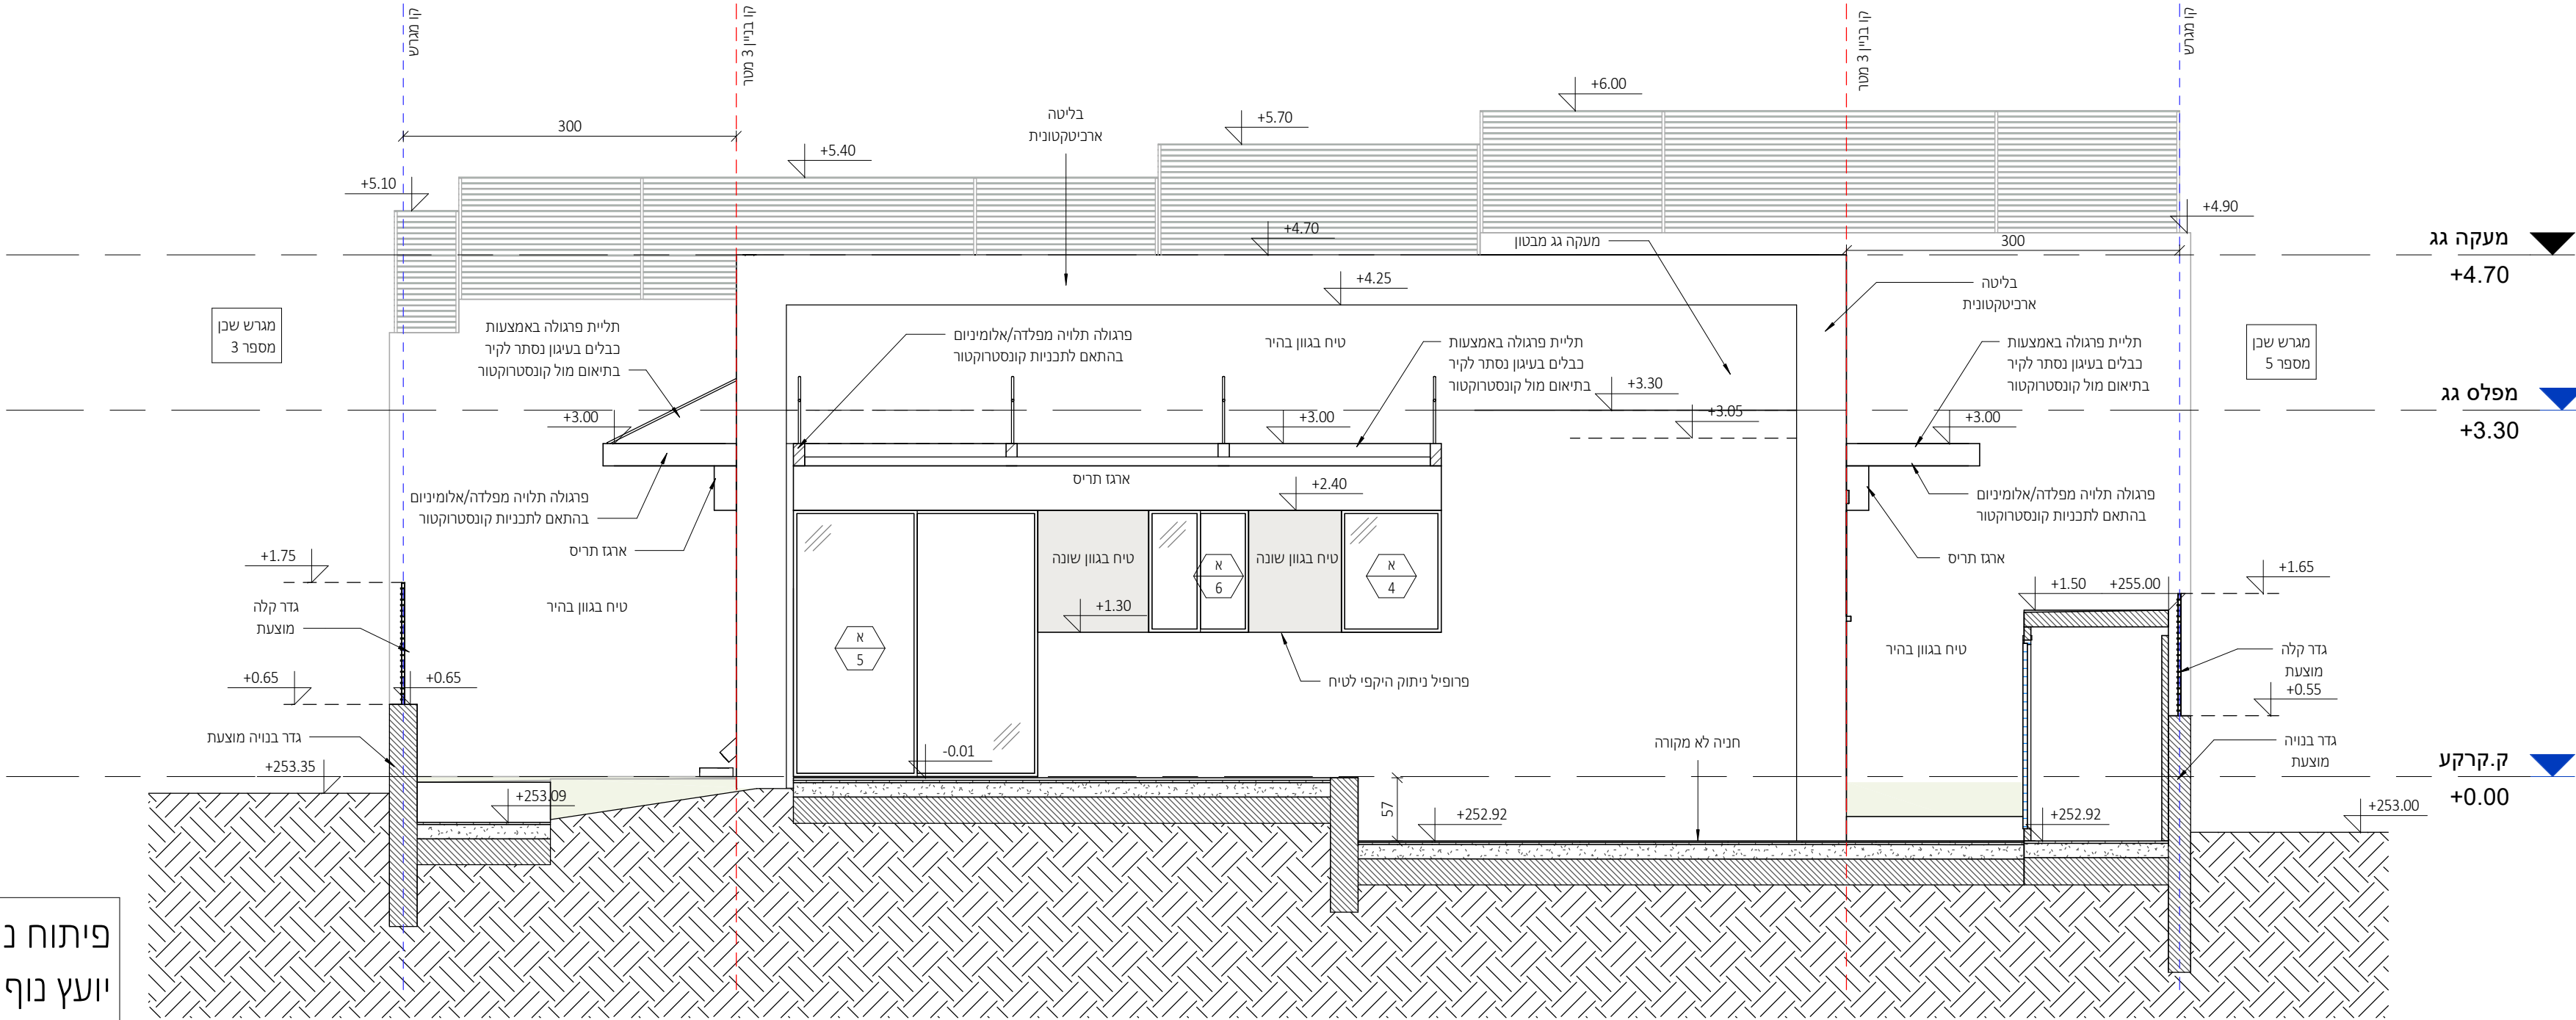

פיתוח נוף עפ"י תוכניות
יועץ נוף ראה פירוט בנפרד

חזית צפונית

1 : 50


פרטי איטום, בידוד וניקוז עפ"י תכניות יועצים ובאחריות הקבלן

מתכונים:

ניהול פרויקט
מהיסוד - בן סולמון
פיקוח
מהיסוד - בן סולמון
קונסטרוקציה
ערן שילר
מיזוג אוויר
אייל ארז מהנדסים ויועצים בע"מ
אינסטלציה
איתן אלמסי
חשמל
איתן בסיס
אלומיניום
נוף
נתי בלוקא
חשמל חכם
חימום תת רצפתי
איטום
צבי טל
אקוסטיקה
מעליות
קרקע וביסוס
דיה הנדסת קרקע וביסוס
רישוי

[illegible]

מקרא קירות:

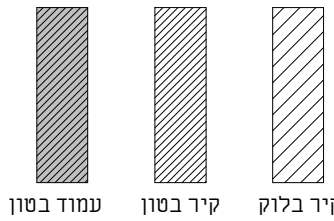[illegible]

אדריכלות

CLIENT NAME: _____ שם המזמין:

נופיה קבוצת רכישה

PROJECT NAME: שם הפרויקט:

נופיה - מגרש 4

DRAWING NAME: ס הגליון:

חתימים

SHEET NUMBER: 190 גליון:

A3-3-100


SCALE: _____ קנה מידה: _____ EDITION: _____ הדורה:

1:50

STATUS: 01000 1

רמטט ע"י:	נבדק ע"י:
-----------	-----------


DATE: 22.09.25 חתום:

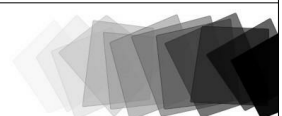

NeumanHaynerArchitects


office@nh-arch.com
www.nh-arch.com

זכויות ייצור / ע"פ הנחיות עו"ד

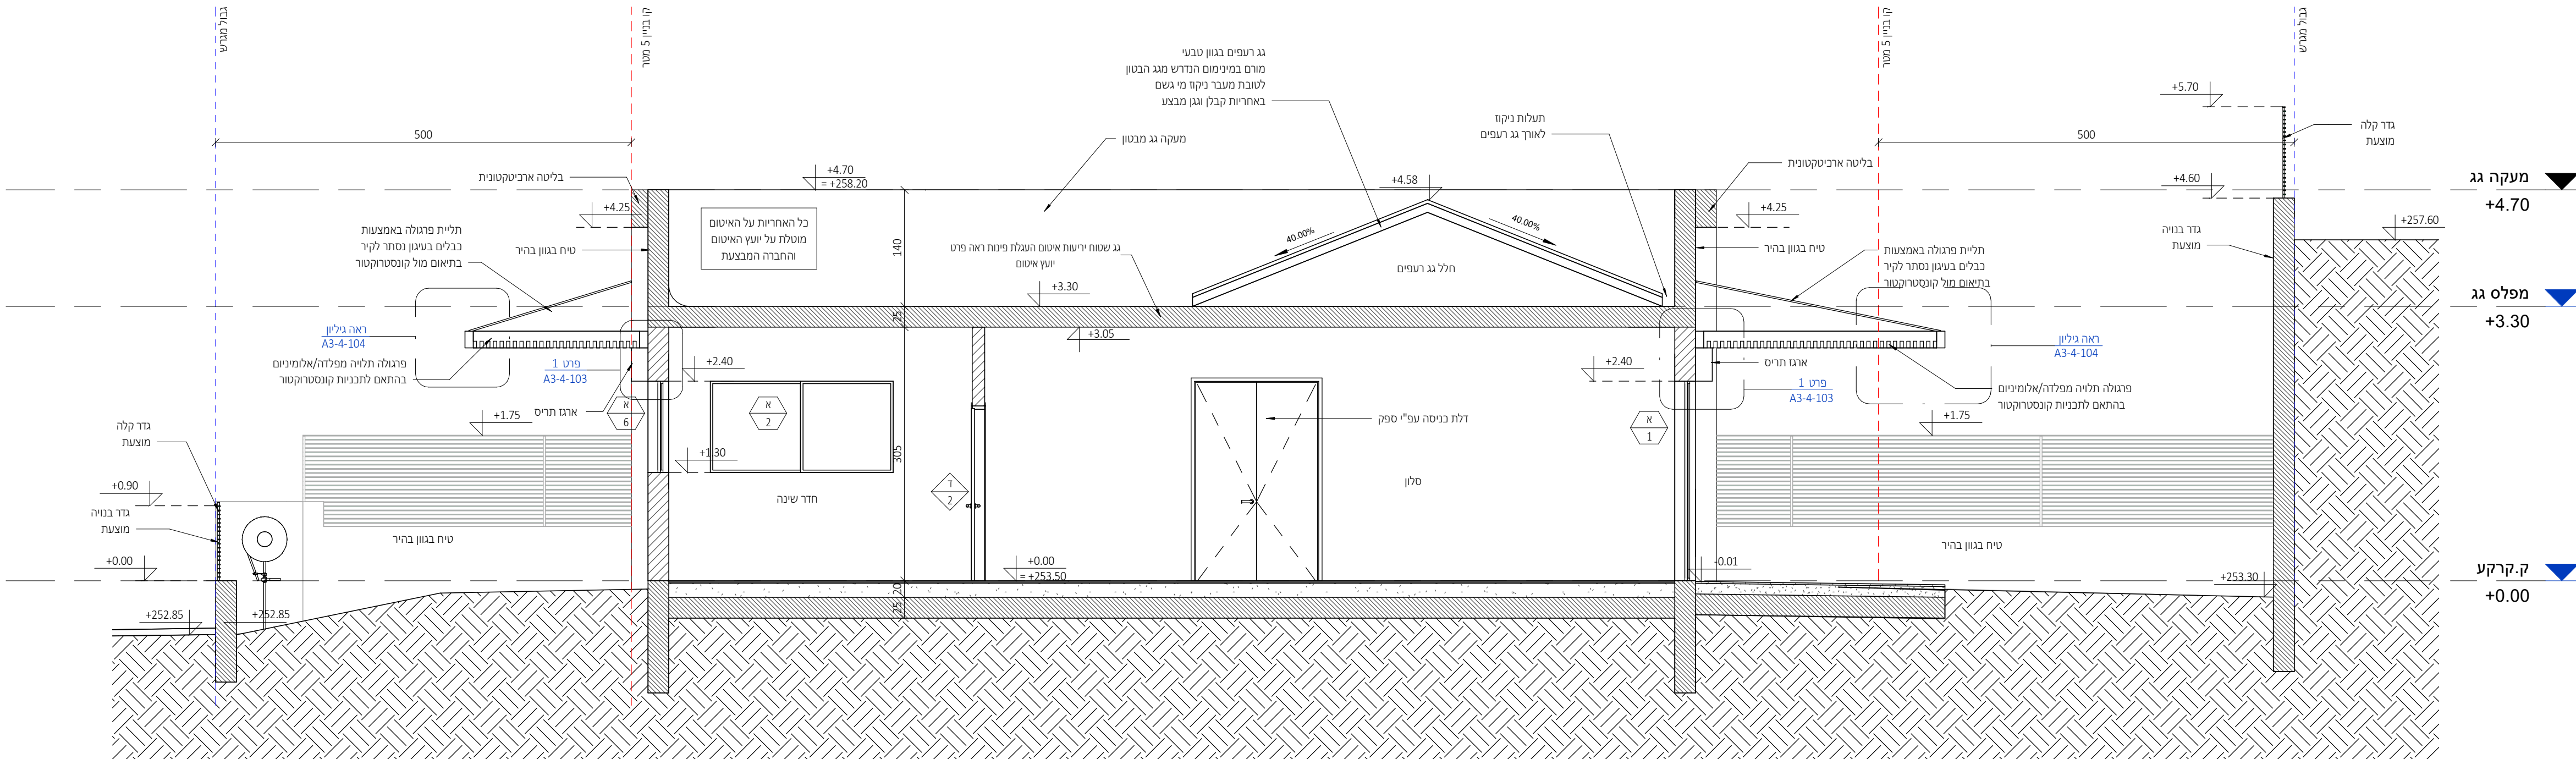

חתך א-א

1 : 50

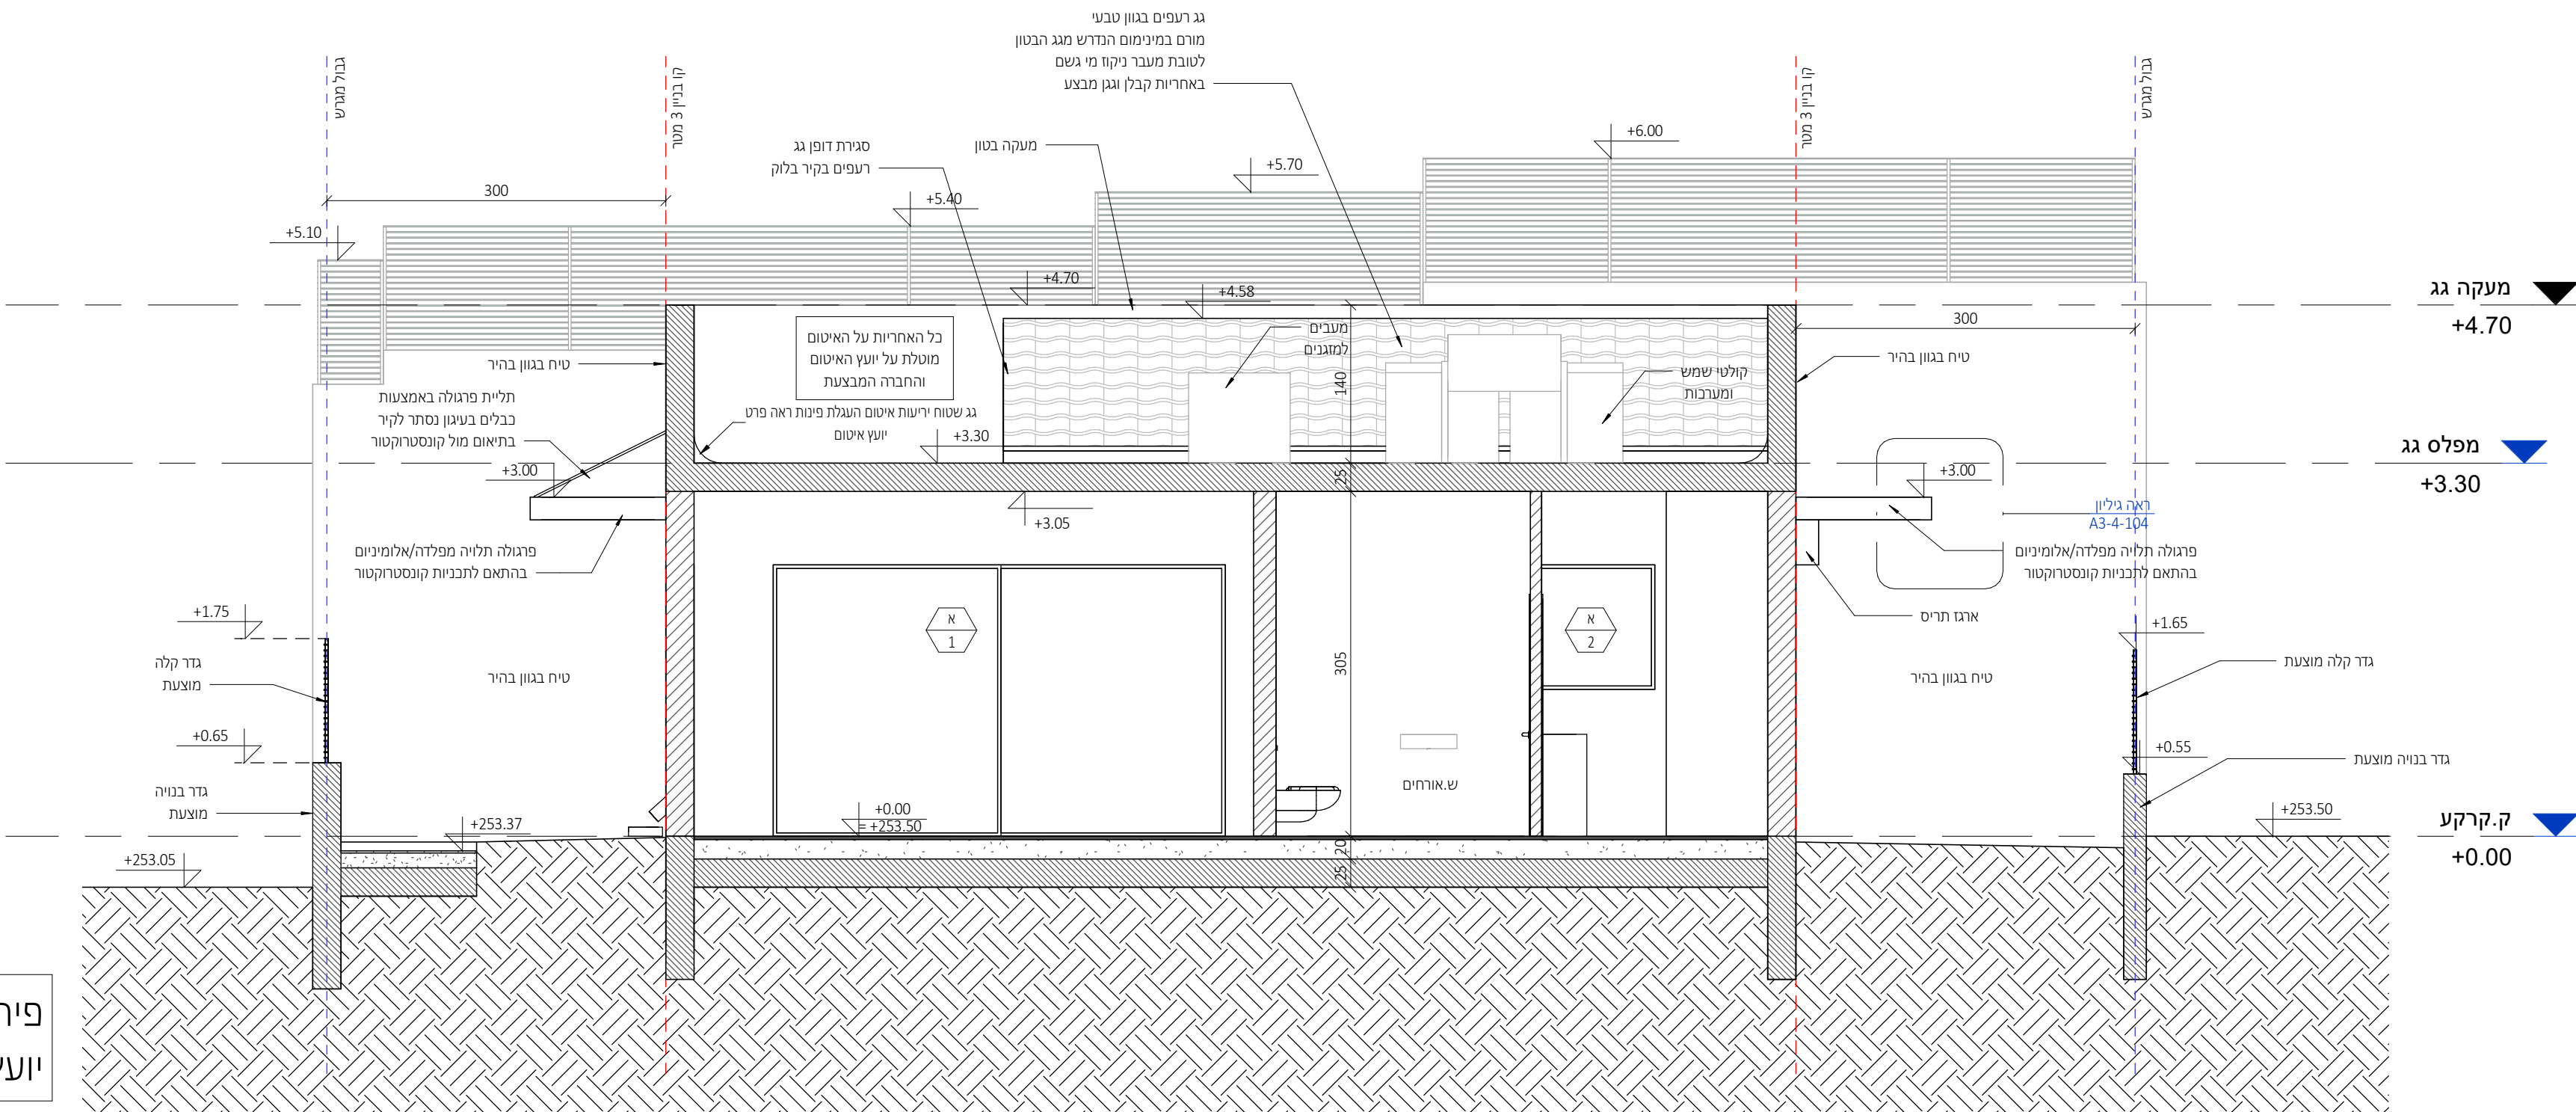

חתך ב-ב

1 : 50

ניהול פרויקט
מהיסוד - בן סולומון
פיקוח
מהיסוד - בן סולומון
קונסטרוקציה
ערן שילר
מיזוג אוויר
אייל ארז מהנדסים ויועצים בע"מ
אינסטלציה
איתן אלמסי
חשמל
איתן בסיס
אלומיניום
נוף
נתי בלוקא
חשמל חכם
חימום תת רצפתי
איטום
צבי טל
אקוסטיקה
מעליות
קרקע וביסוס
דיה הנדסת קרקע וביסוס
רישוי

[illegible]

עמוד בטון קיר בטון יד בלוק

[illegible]


CLIENT NAME:		המוקדם:	
PROJECT NAME:		הפרויקט:	
נופיה קבוצת רכישה			
4 מגרש -			
DRAWING NAME:		שם התכנון:	
פרטים			
SHEET NUMBER:		מספר העליון:	
A3-4-103			
SCALE:	קנה מידה:	EDITION:	הדורה:
As indicated			
STATUS:	סטטוס		
למכר			
	נבדק ע"י:		מוסר ע"י:
DATE:	22.09.25		תאריך:




NeumanHaynerArchitects

יומן חייגר אדריכלים
 חורר ההדרים 2, בית חירות
 09-9545842 זל


office@nh-arch.com
 www.nh-arch.com

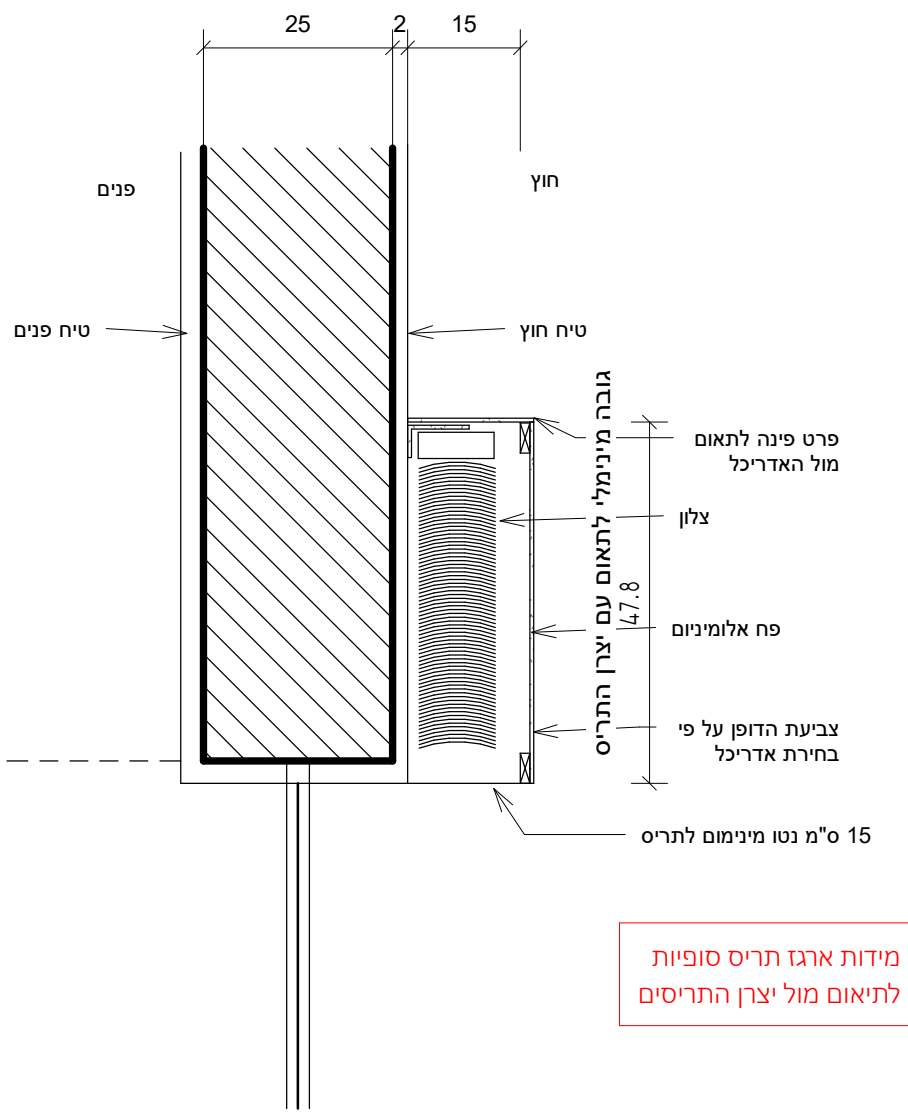

1 : 10

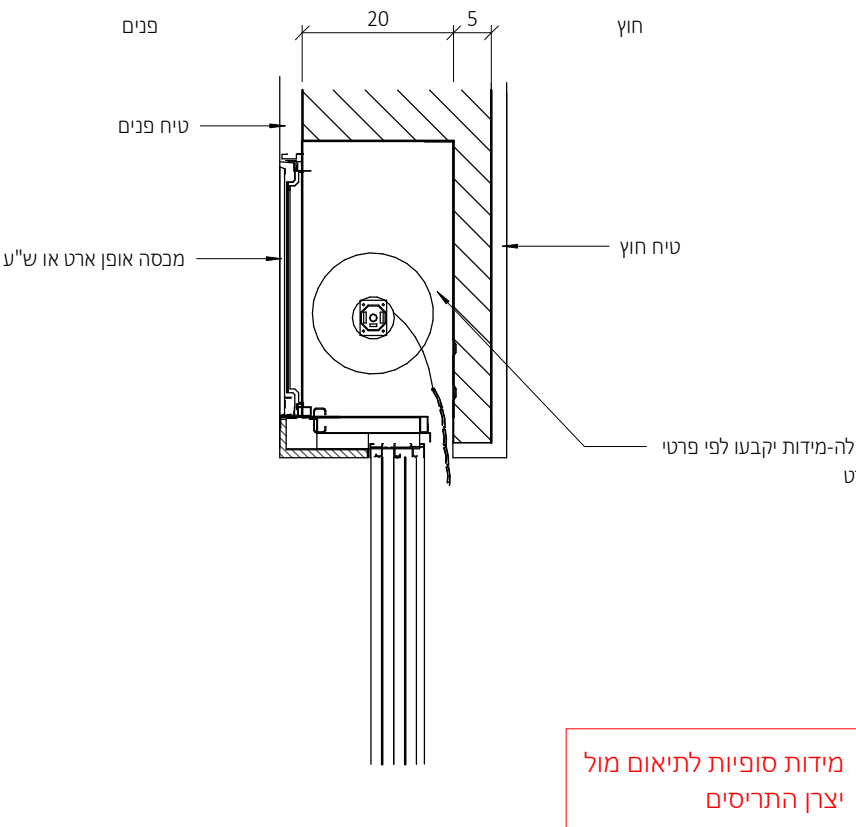


1 : 10

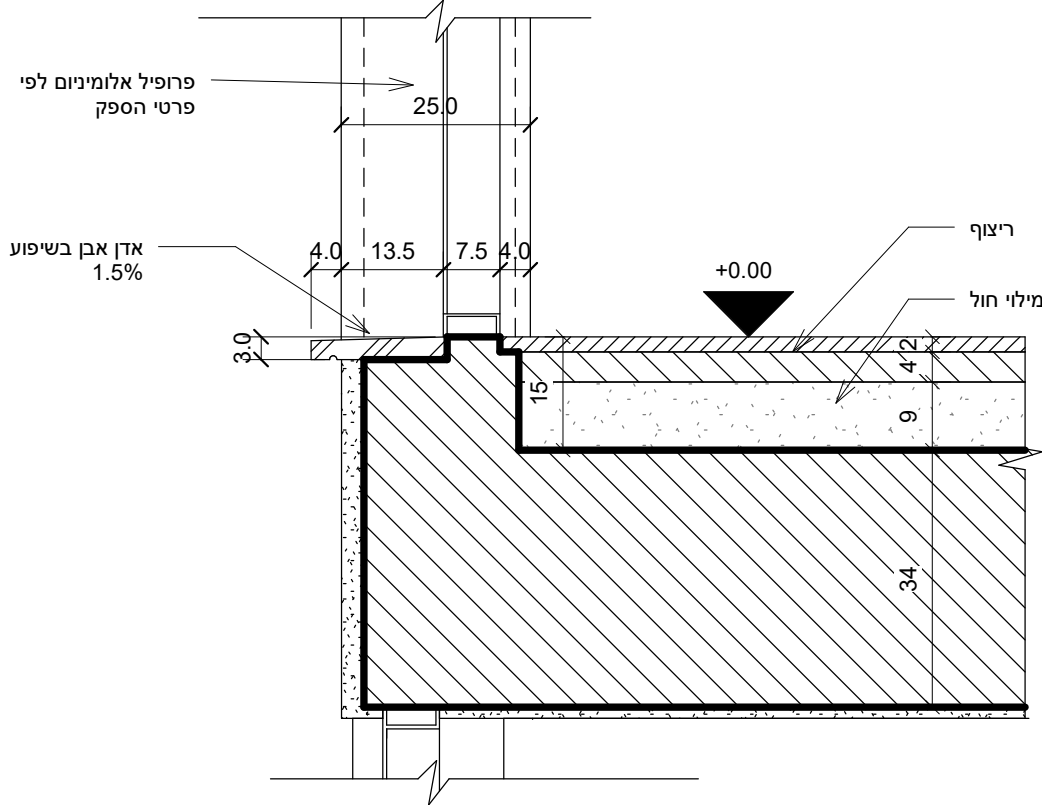


הערה : פרטי האיטום הם עקרוניים בלבד
כל האחריות על האיטום מוטלת על יועץ
האיטום החברה המבצעת
יש לעבוד לפי פרטי האיטום של יועץ הפרק
גובה החלון המופיע בתכניות מצוין את פ
האבן. יש להנמיך את הבטון בהתאם

פרט עקרוני בלבד - פרט סופי מספק החלונות


1 : 10

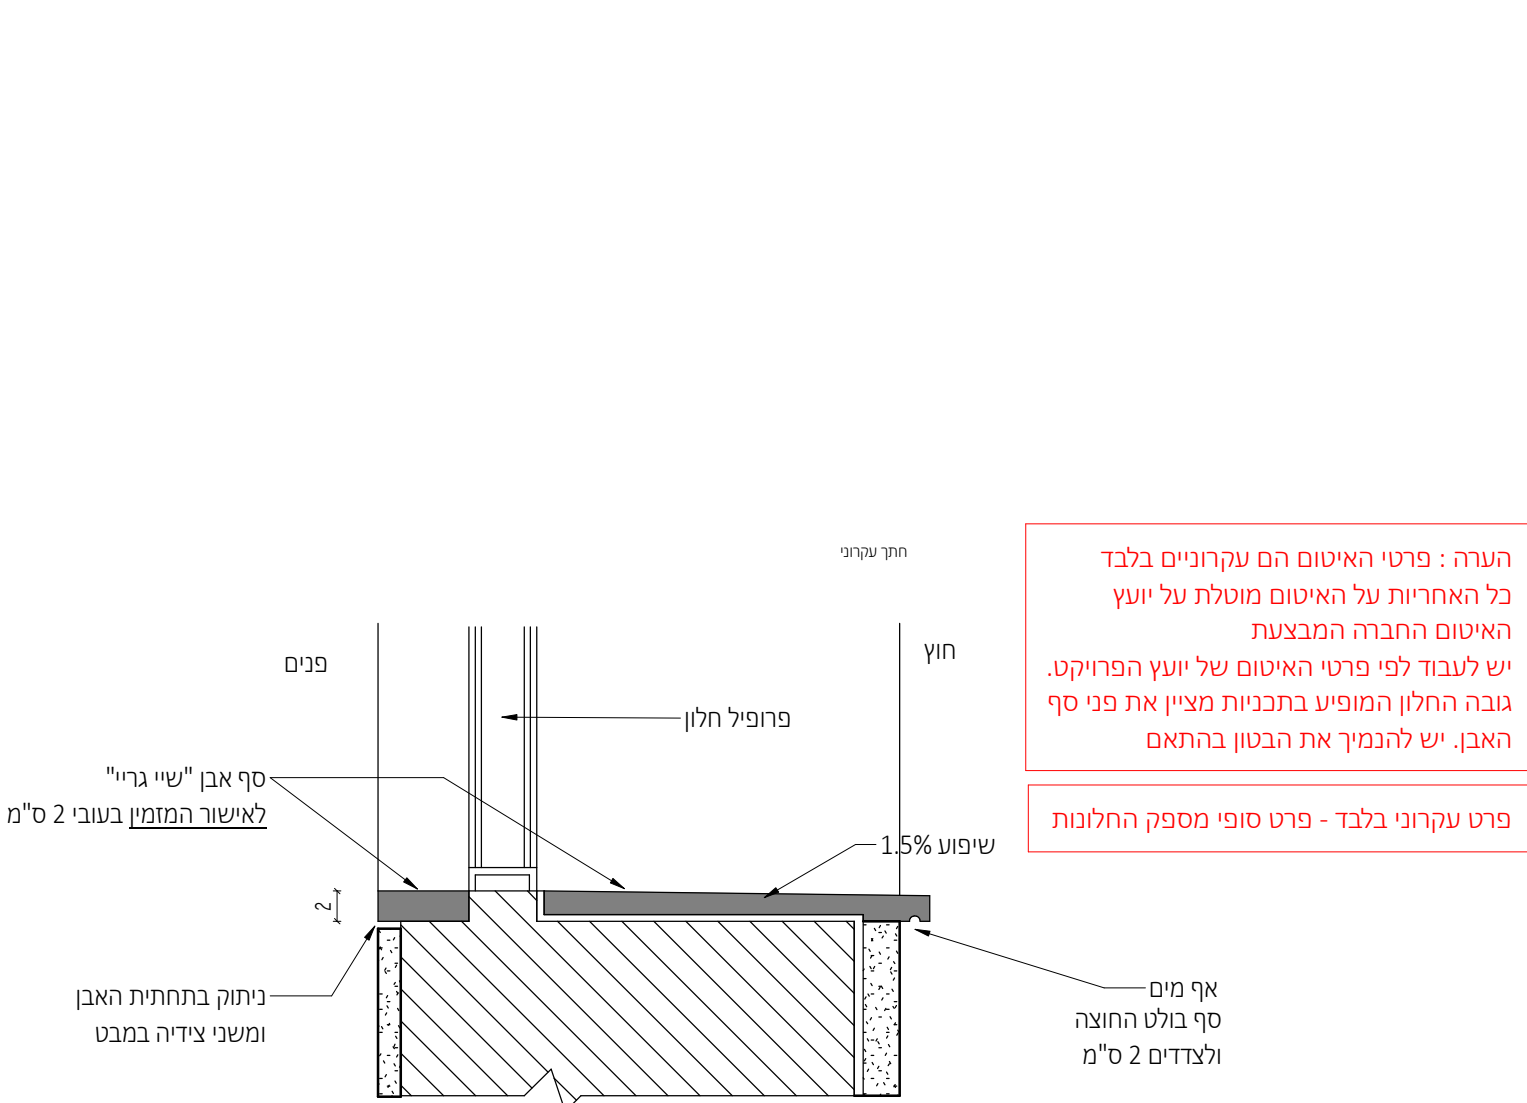

1:5

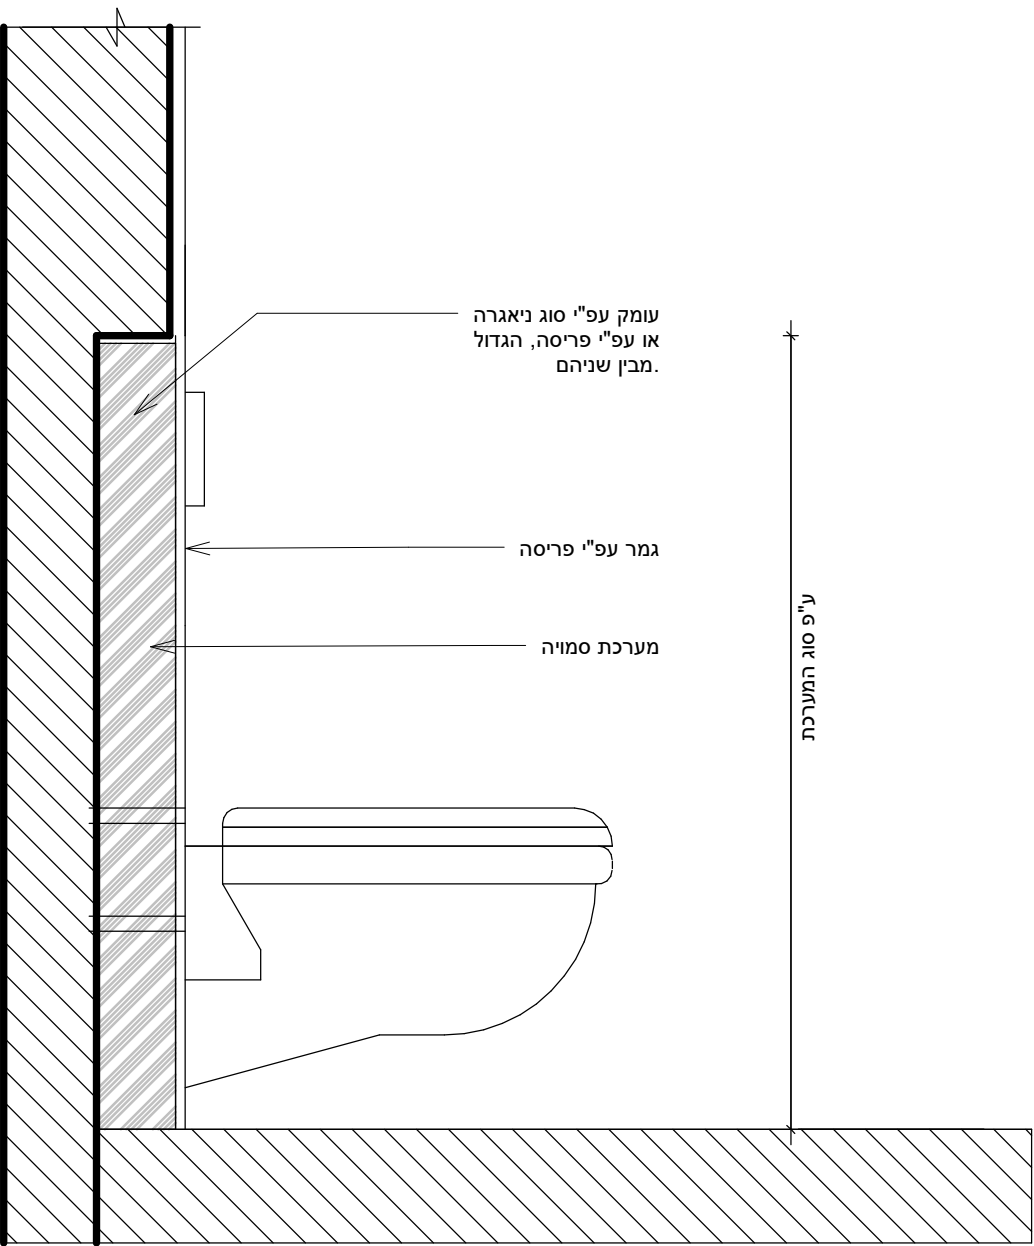

1 : 10

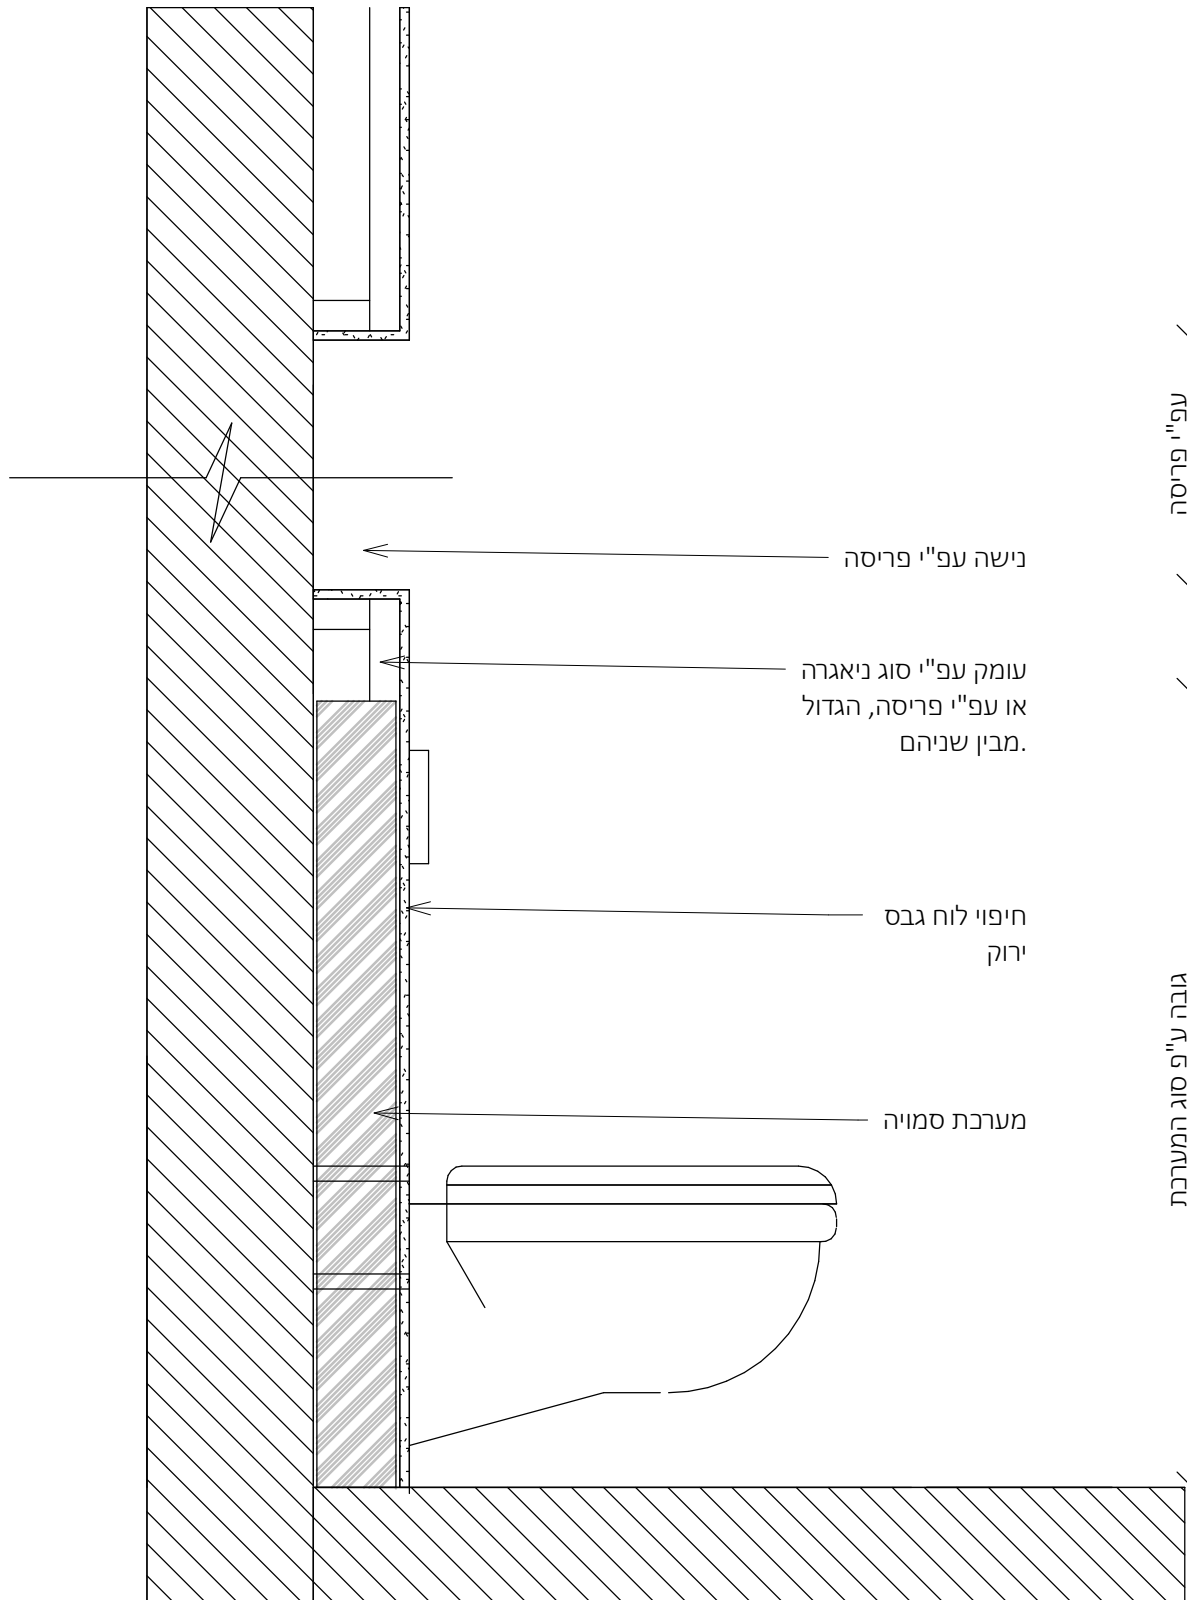

1 : 10

יש לעבוד במקביל לפרטים שיספק
מעצב הפנים (במידה וקיים במגרש זה)
המאושרות על ידי האדריכל.

פרטי האיטום באחריות יועץ האיטום
ראה חוברת פרטי איטום מצורפת



להמשך תיאום

פרגולת אלומיניום




תמונה להמחשה בלבד

להמשך תיאום

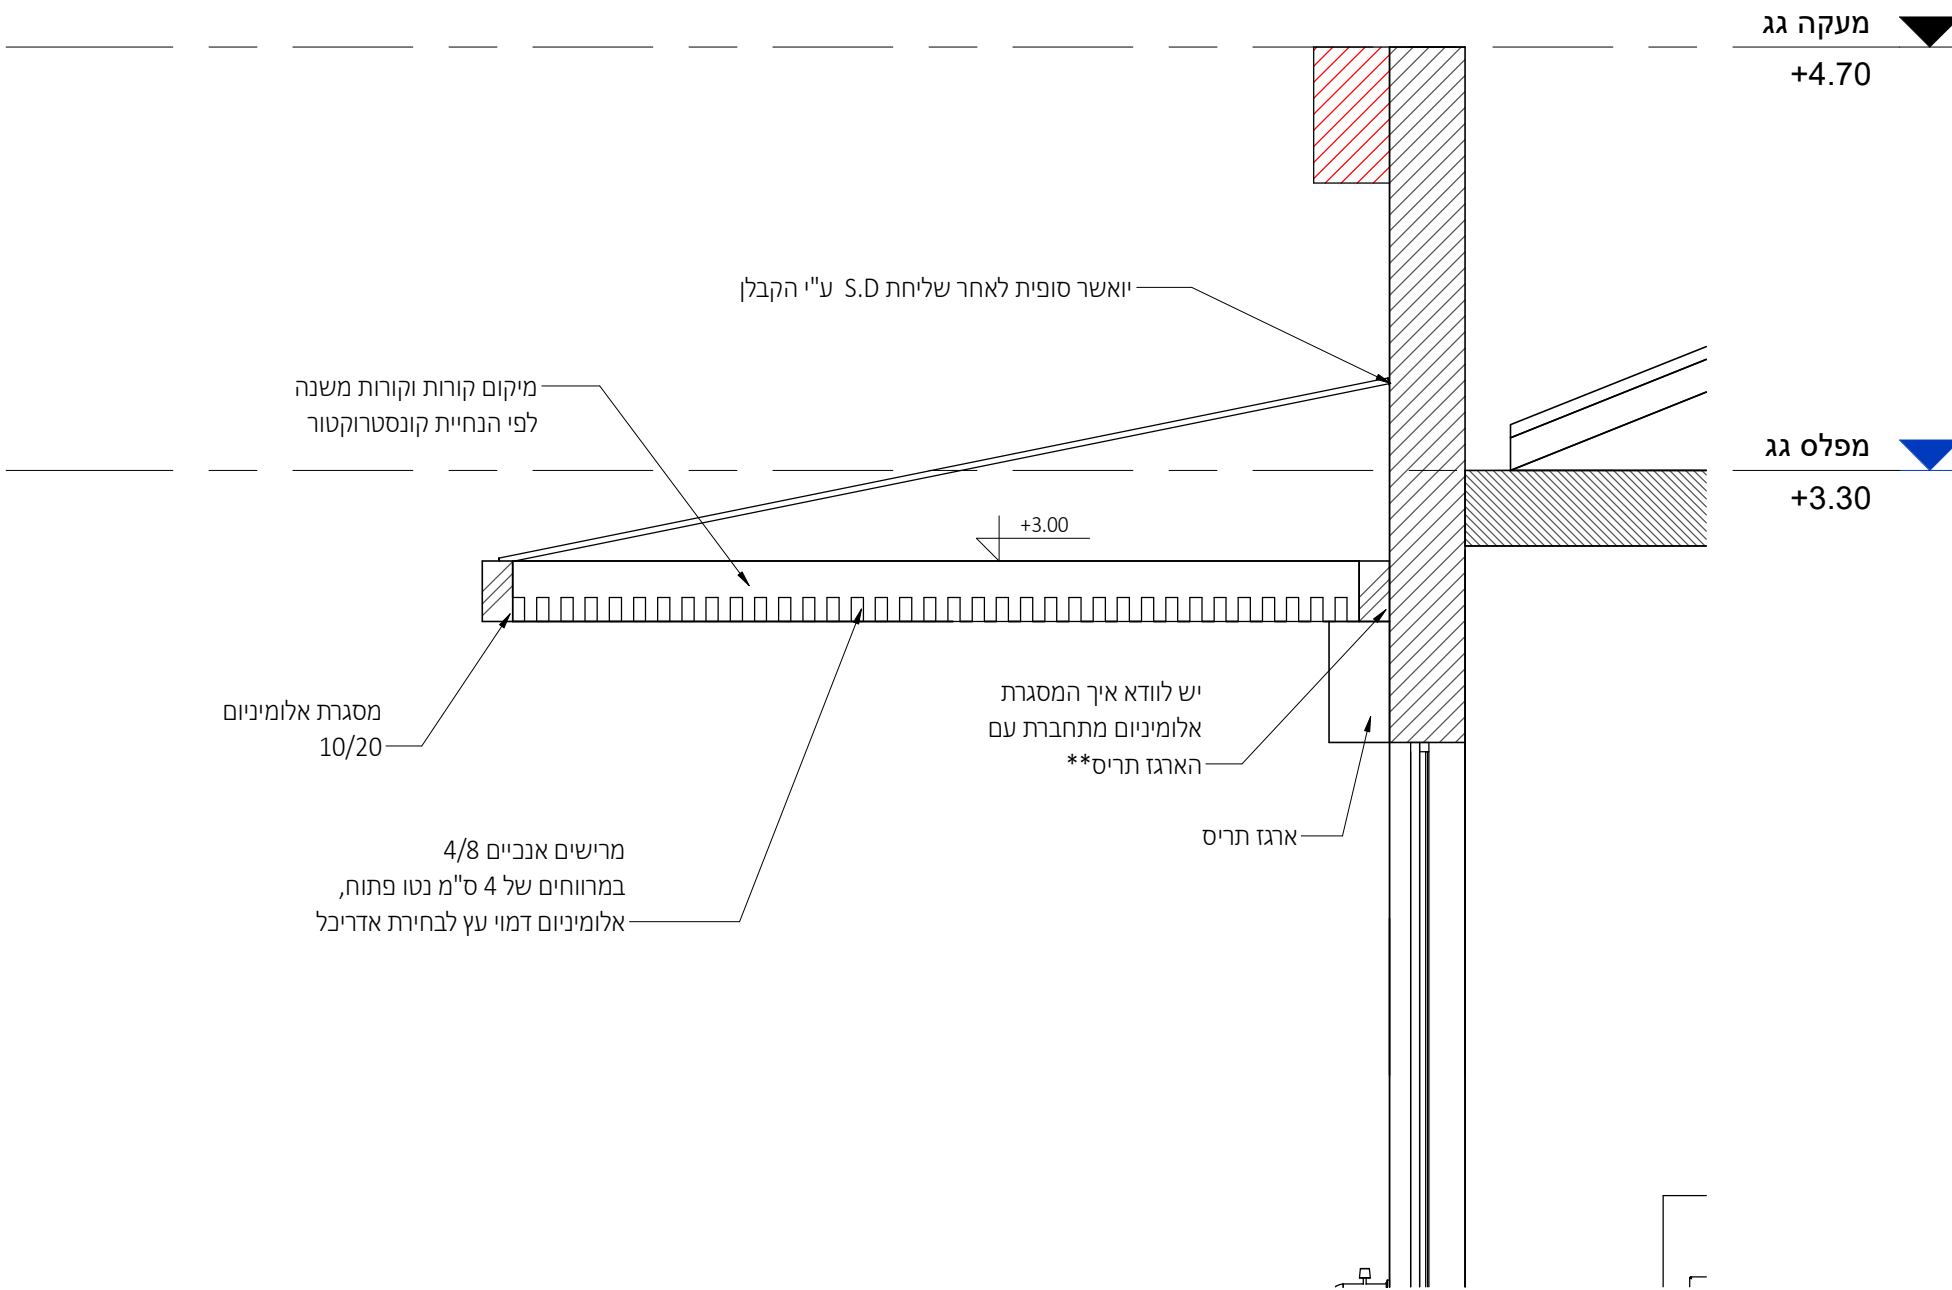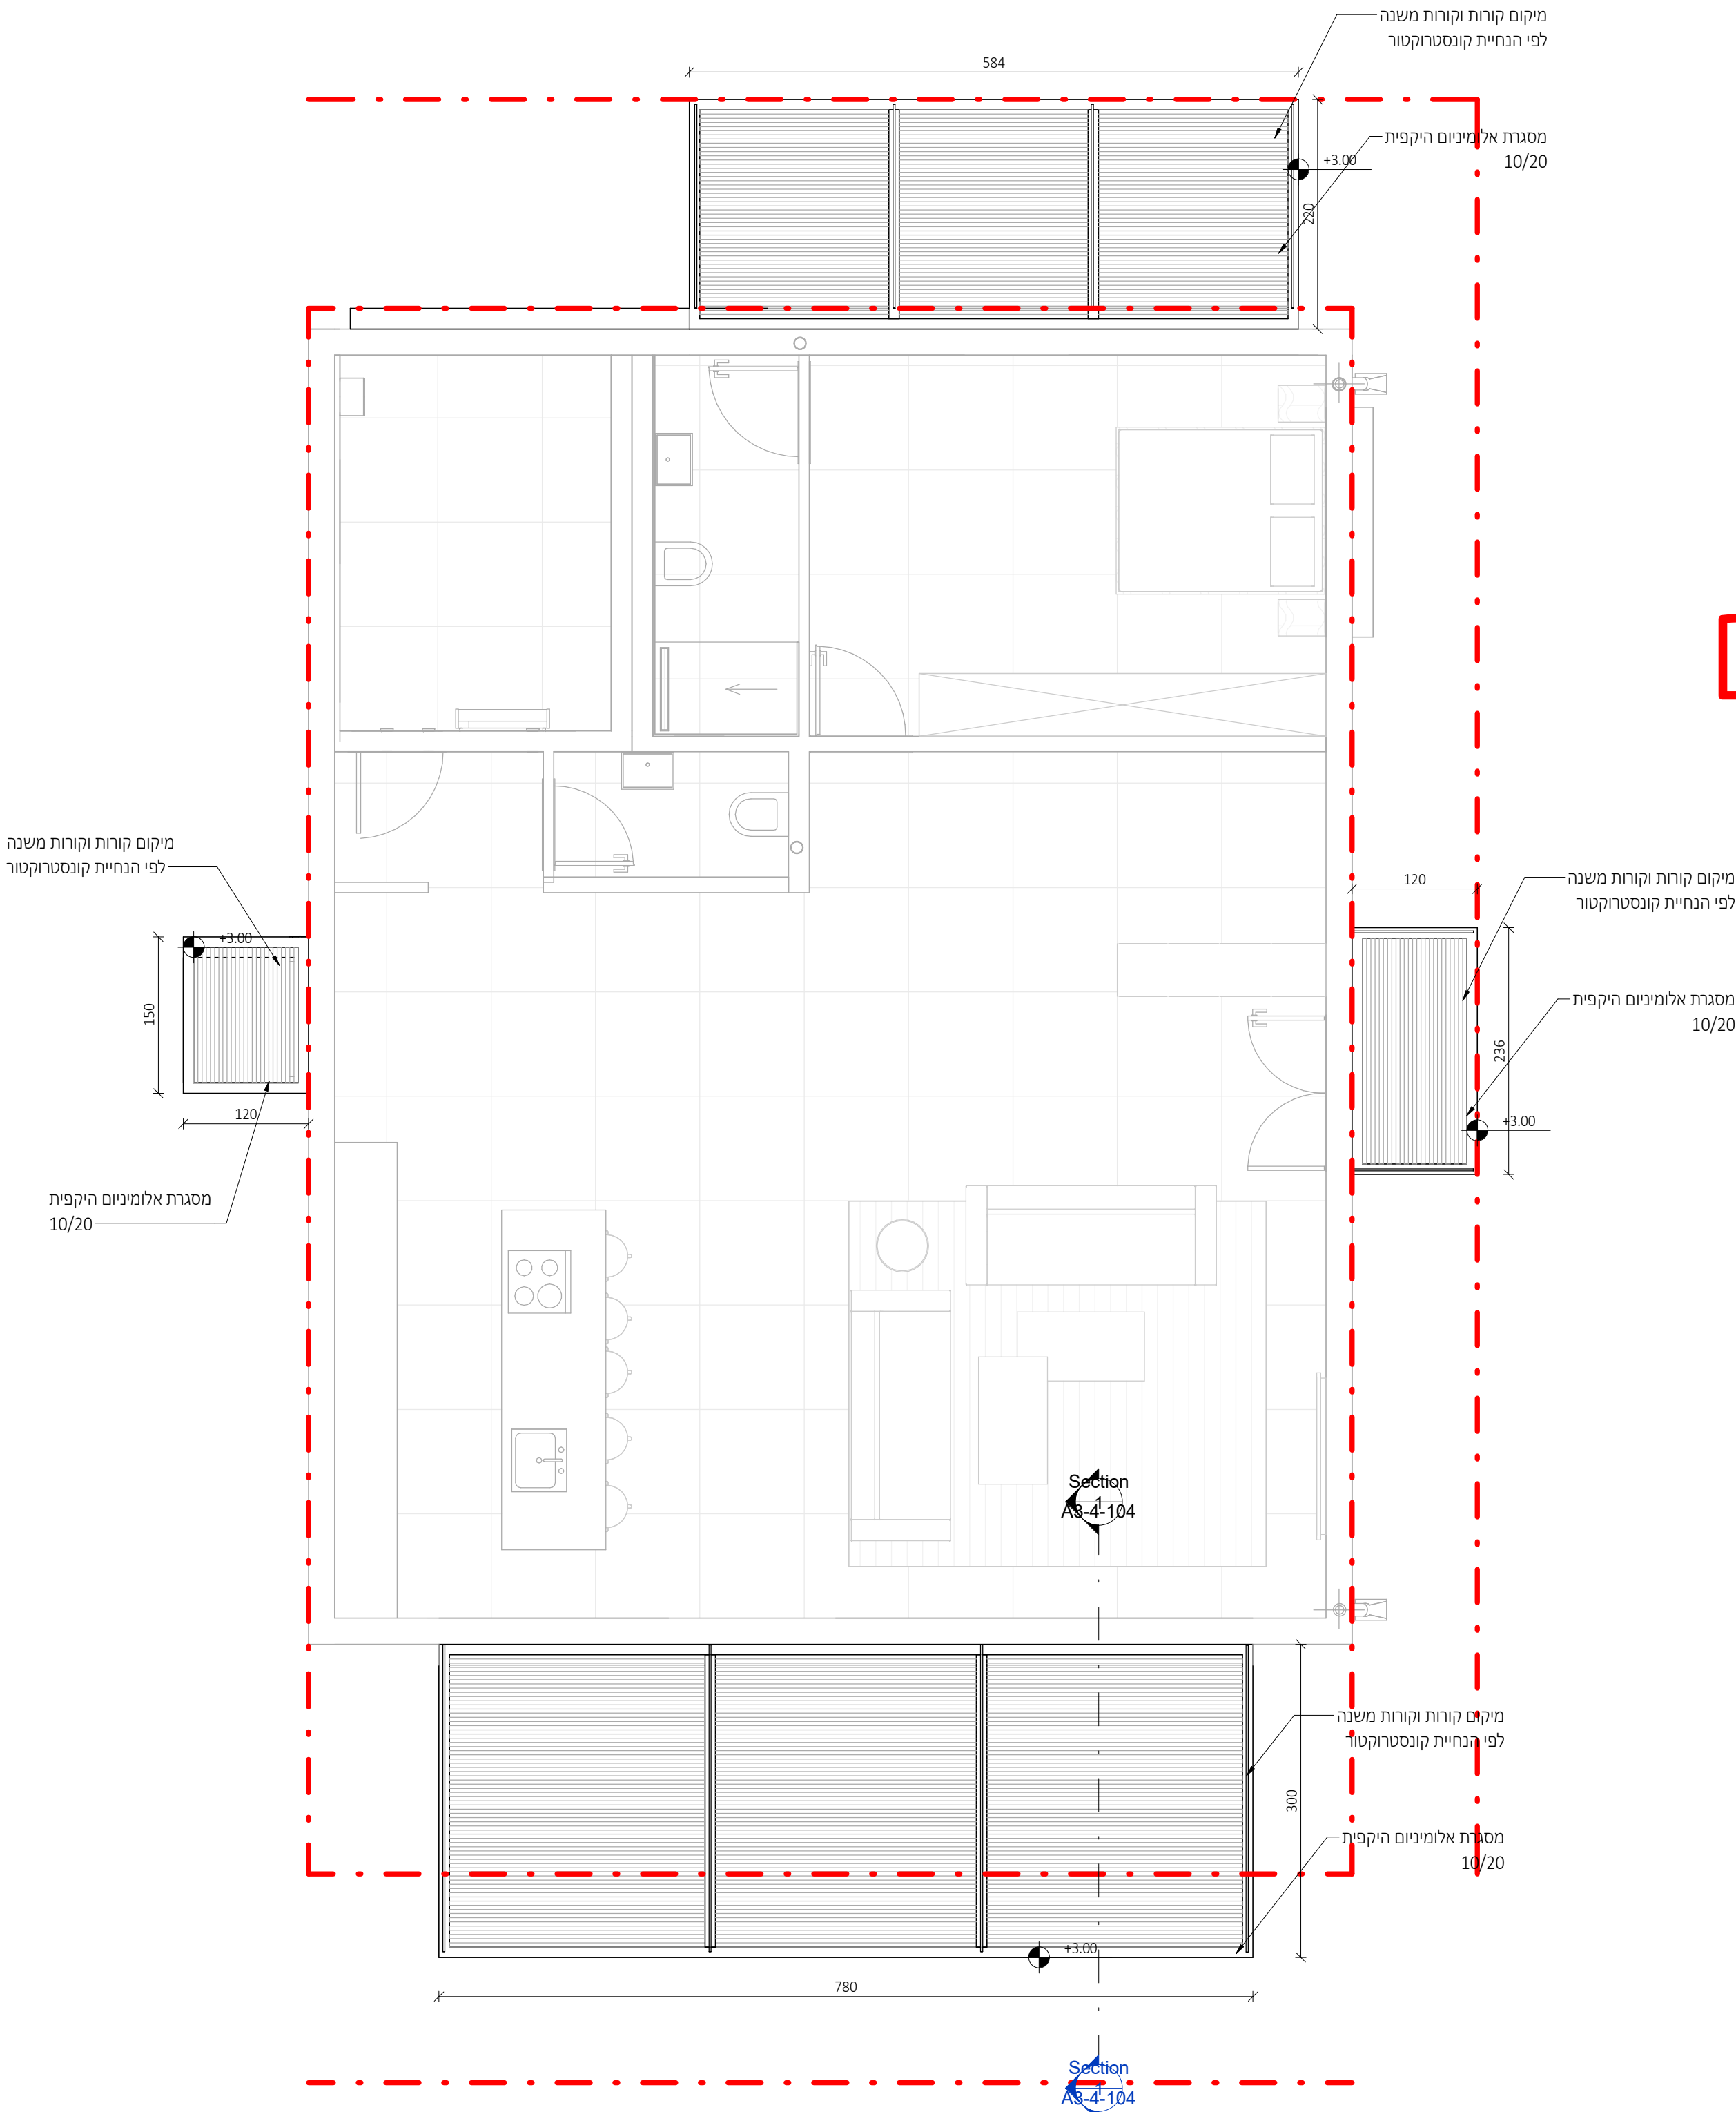


Section 1

1 : 25

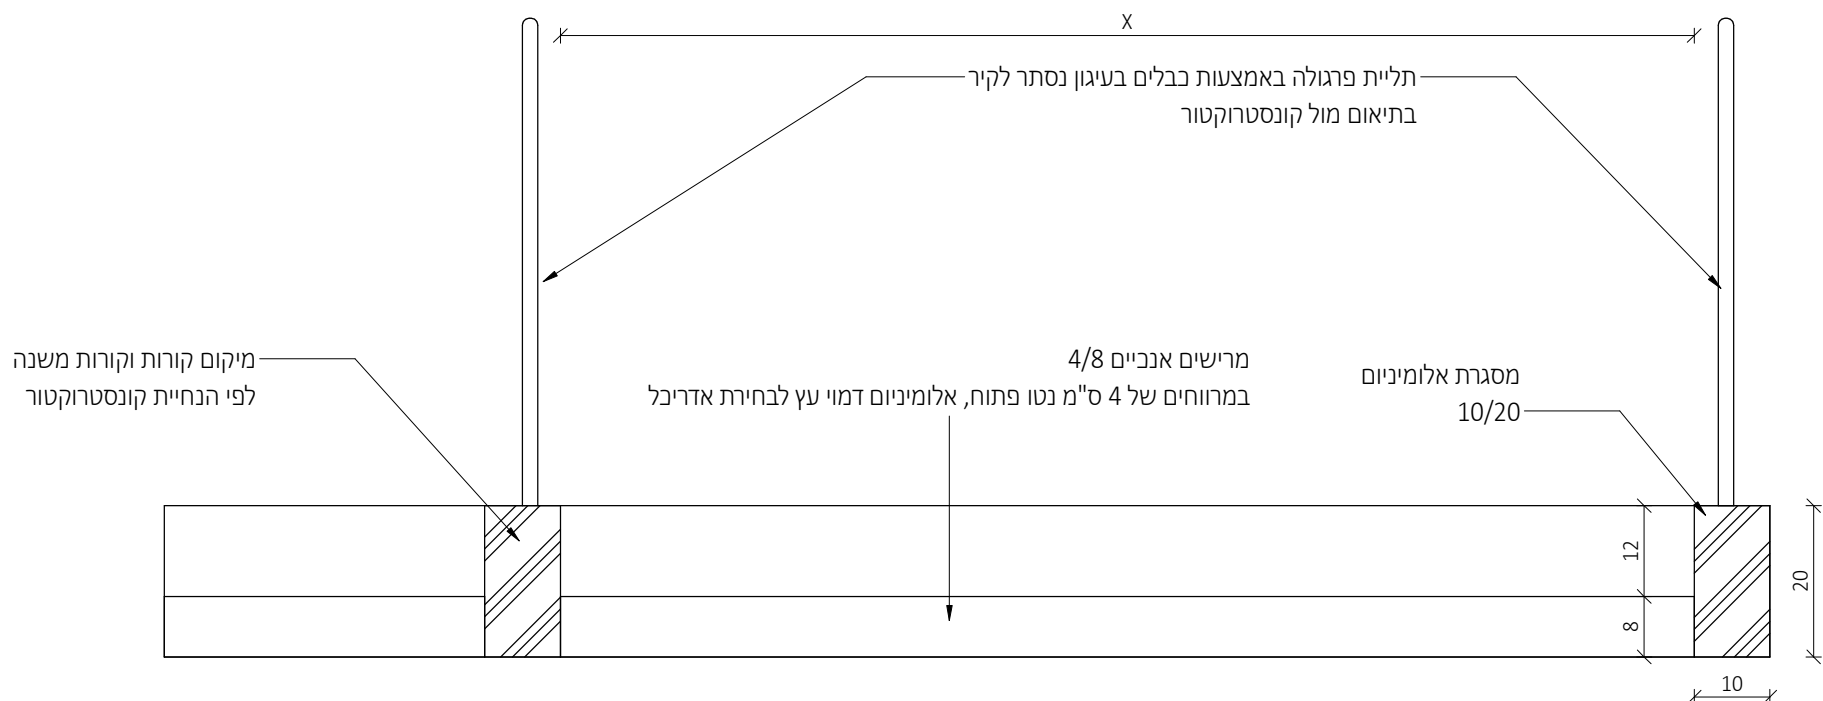

פרגולה - חתך אורך

1 : 10

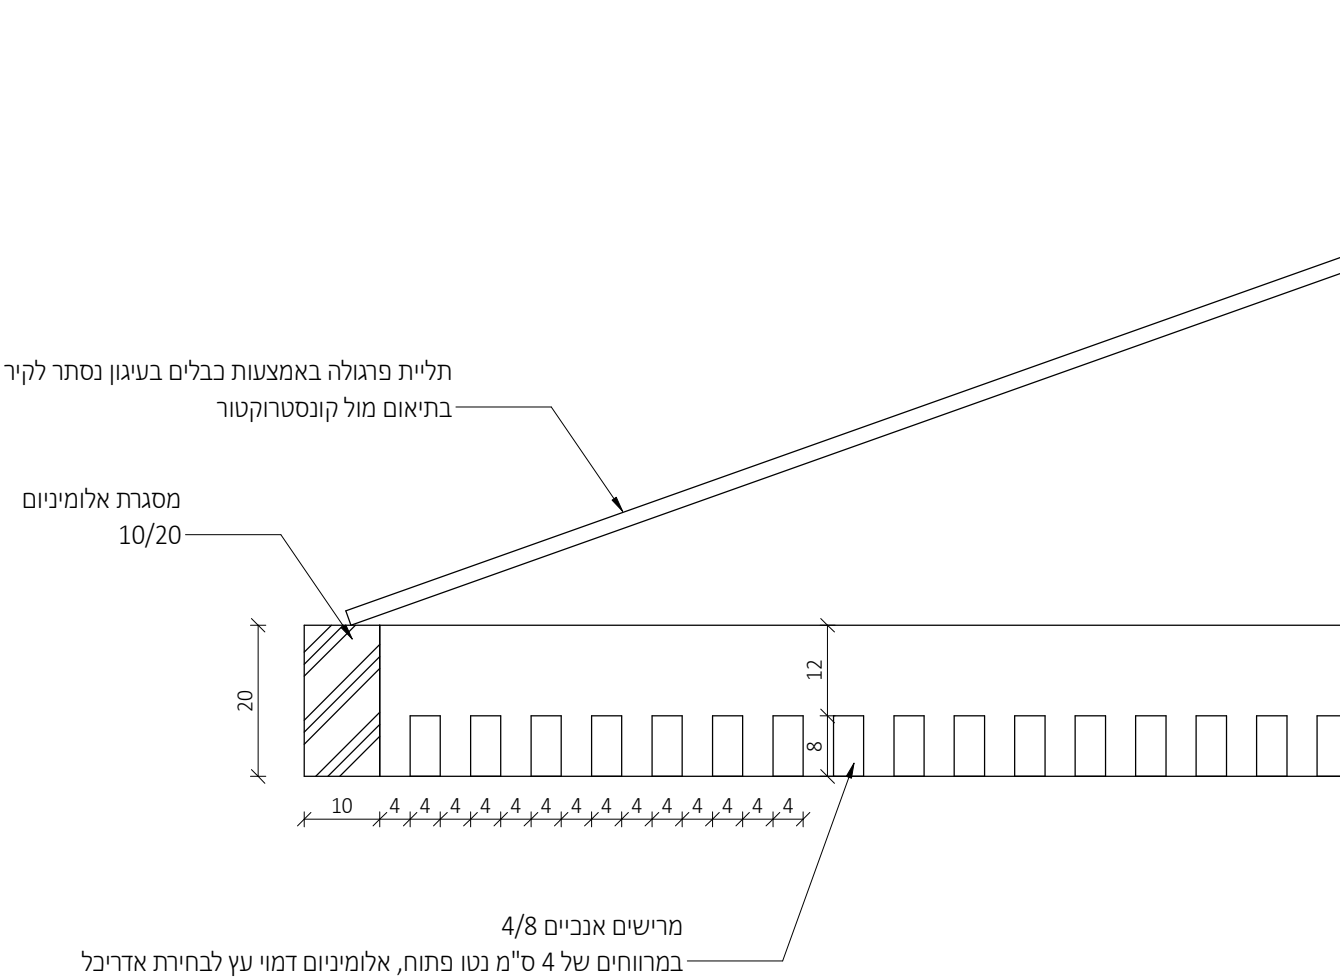

פרגולה - חתך רוחב


1 : 10

מתכננים:

ניהול פרויקט
מהיסוד - בן סולומון
פיקוח
מהיסוד - בן סולומון
קונסטרוקציה
ערן שילר
מיזוג אוויר
אייל ארז מהנדסים ויועצים בע"מ
אינסטלציה
איתן אלמסי
חשמל
איתן בסיס
אלומיניום
נוף
נתי בלוקא
חשמל חכם
חימום תת רצפתי
איטום
צבי טל
אקוסטיקה
מעליות
קרקע וביסוס
דיה הנדסת קרקע וביסוס
רישוי

± 0.00 = +253.50 הערות: 1. תכנית זו יש לקרוא יחד עם תכנית הרישום. 2. גובה אבטמנטים: ראו תכנית פיתוח. 3. המידות הן בין קירות הבניה ולא כולל פיתוח. 4. פיתוח השטח סביב הבניה, כולל, מדרגות, גדרות, שבילים, ריצופים, שיפופים, גדרים, חניה וגן ואו תכנית פיתוח. 5. איסוס קירות הצפת הבניה כמעט עם הקרקע ובנידוד תחרי לאור העמודים והקורות ועל התקרות. כלירות או עם סימני (גובה) - ראו תכנית קונסטרוקציה. 6. אף מים יבוצע בכל מישור אופקי הכולל מתבנית. 7. סיוח תחרי במסגרת ע"פ מפרט חומרים, מאושר ט"י פיקוד העורף. המבצע אחראי לסידור: עליו לבקר ולבדוק את כל המידות בתכנית ובמקום התבונה. במסגרת של מידות או אי התאמה בתכנית /או בבנין, עליו להודיע על כך מיד לאדריכל במסגרת המשך העבודה. המבצע יישמש או ויקי בתכנית שאושרו לכניסיו. המבצע יחזיק באחר, בכל מה, של מידות של תכנית. אין לקבוע מידות על ידי מדידה בשטח. התכנית היתה רכוש האדריכל ואין לשנות כל שימוש בה או ברעיונות הגלומים בה, אלא באישור בכתב מהאדריכל. מתקדם /או יושע אשר שמו רשום בתכנית זו, נושא לכיד באחריות הנדסאית והנדסאית לתכנית. על התקפת והשקלן ליוזא התאמת התכנית האדריכלית "כניסיו" לתכנית זוהי, הופך והתכנית המאושרות ע"י כל גורמים רשמיים. התכנית כוללת את כל האמצעים והידוע על ליום תוצאתה.

משך קירות:

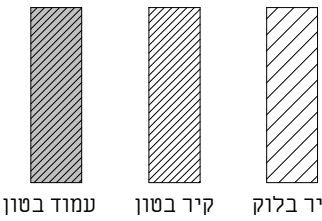

תאריך	תיאור	מהדורה
22.09.2025	מכרז	1

אדריכלות

שם המסמך:	CLIENT NAME:
נופיה קבוצת רכישה	
שם הפרויקט:	PROJECT NAME:
נופיה - מגרש 4	
שם הגיליון:	DRAWING NAME:
פרטי פרגולה	
מספר גליון:	SHEET NUMBER:
A3-4-104	
תאריך:	DATE:
22.09.25	

רשימת חלונות					
סוג	תיאור	כמות	גובה	רוחב	מס פריט

1	400	240	1	צלון רפפה חיצוני חשמלי + ארגז חיצוני	יטרינה פרופיל 7500 קליל
2	220	110	2	צלון רפפה חיצוני חשמלי + ארגז חיצוני	חלון הזזה פרופיל 7000 קליל
3	110	240	1	צלון רפפה חיצוני חשמלי + ארגז חיצוני	דלת בנף פרופיל 4350 קליל
4	90	110	1	צלון רפפה חיצוני חשמלי + ארגז חיצוני	חלון קיפ פרופיל 4500 קליל
5	220	240	1	צלון רפפה חיצוני חשמלי + ארגז חיצוני	יטרינה פרופיל 7500 קליל
6	90	110	1	צלון רפפה חיצוני חשמלי + ארגז חיצוני	חלון הזזה פרופיל 7000 קליל

כל פריט יחולק למינימום הכנפיים האפשרי (לתיאום מול ספק האלומיניום ובמסגרת שרטוטי הshop drawing)

רשימת דלתות					
מספר פריט	רוחב	גובה	כמות	הערות	סוג

0	150	240	1	דלת כניסה	דלת חוץ דגם גארדה
2	90	210	2	דלת פנים	דלת פנים "אקוודור" תוצרת חמדיה
3	80	210	1	דלת פנים	דלת פנים "אקוודור" תוצרת חמדיה
4	80	200	1	דלת נגרות ממ"ד	דלת פנים "אקוודור" תוצרת חמדיה

FILE NAME: -----כלל הפריקטים להיתר\004\תכנית\nofia\-----