


פתחי גישה אופן ארט בתיאום סופי מול אדריכל
כלל יחידות המיזוג אשר נמצאות בתוך נגרות יש לתאם סופית מול אדריכל ונגרות

Court 4

1st Floor

Option №2

inverter duct unit in living
room and wall mounted in
rooms

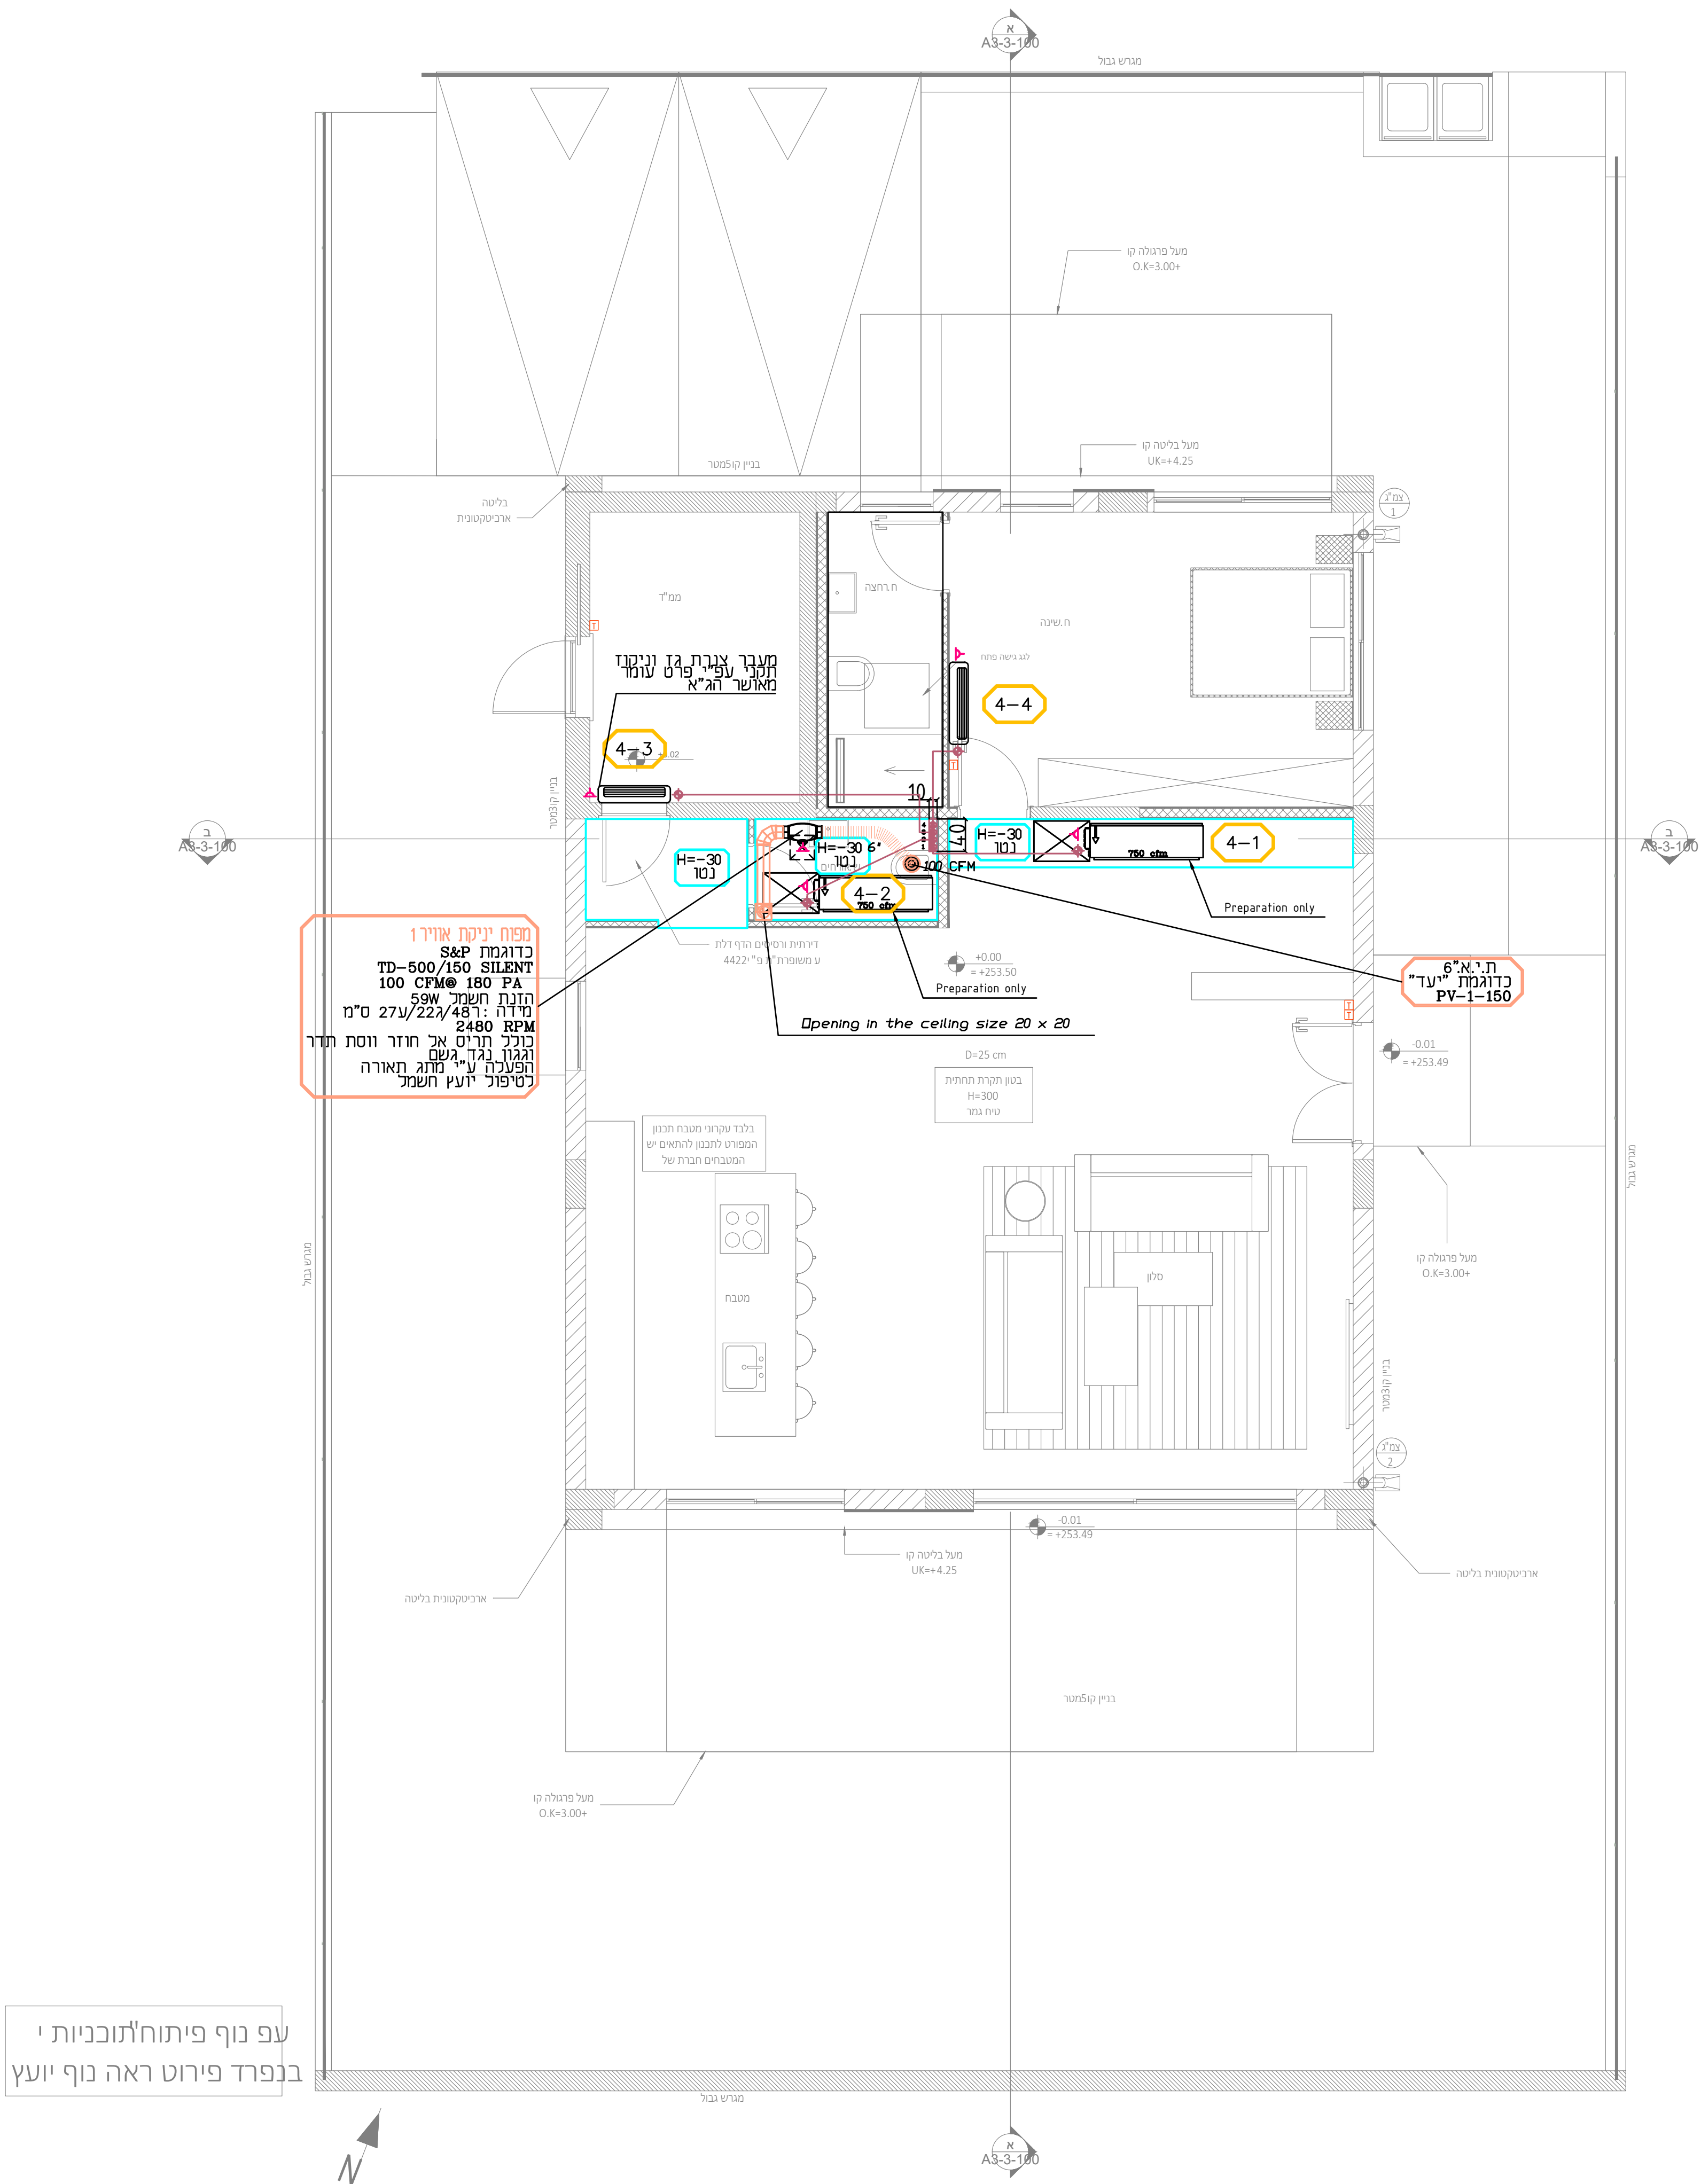


Court 4

Roof

Option №2

inverter duct unit in living
room and wall mounted in
rooms

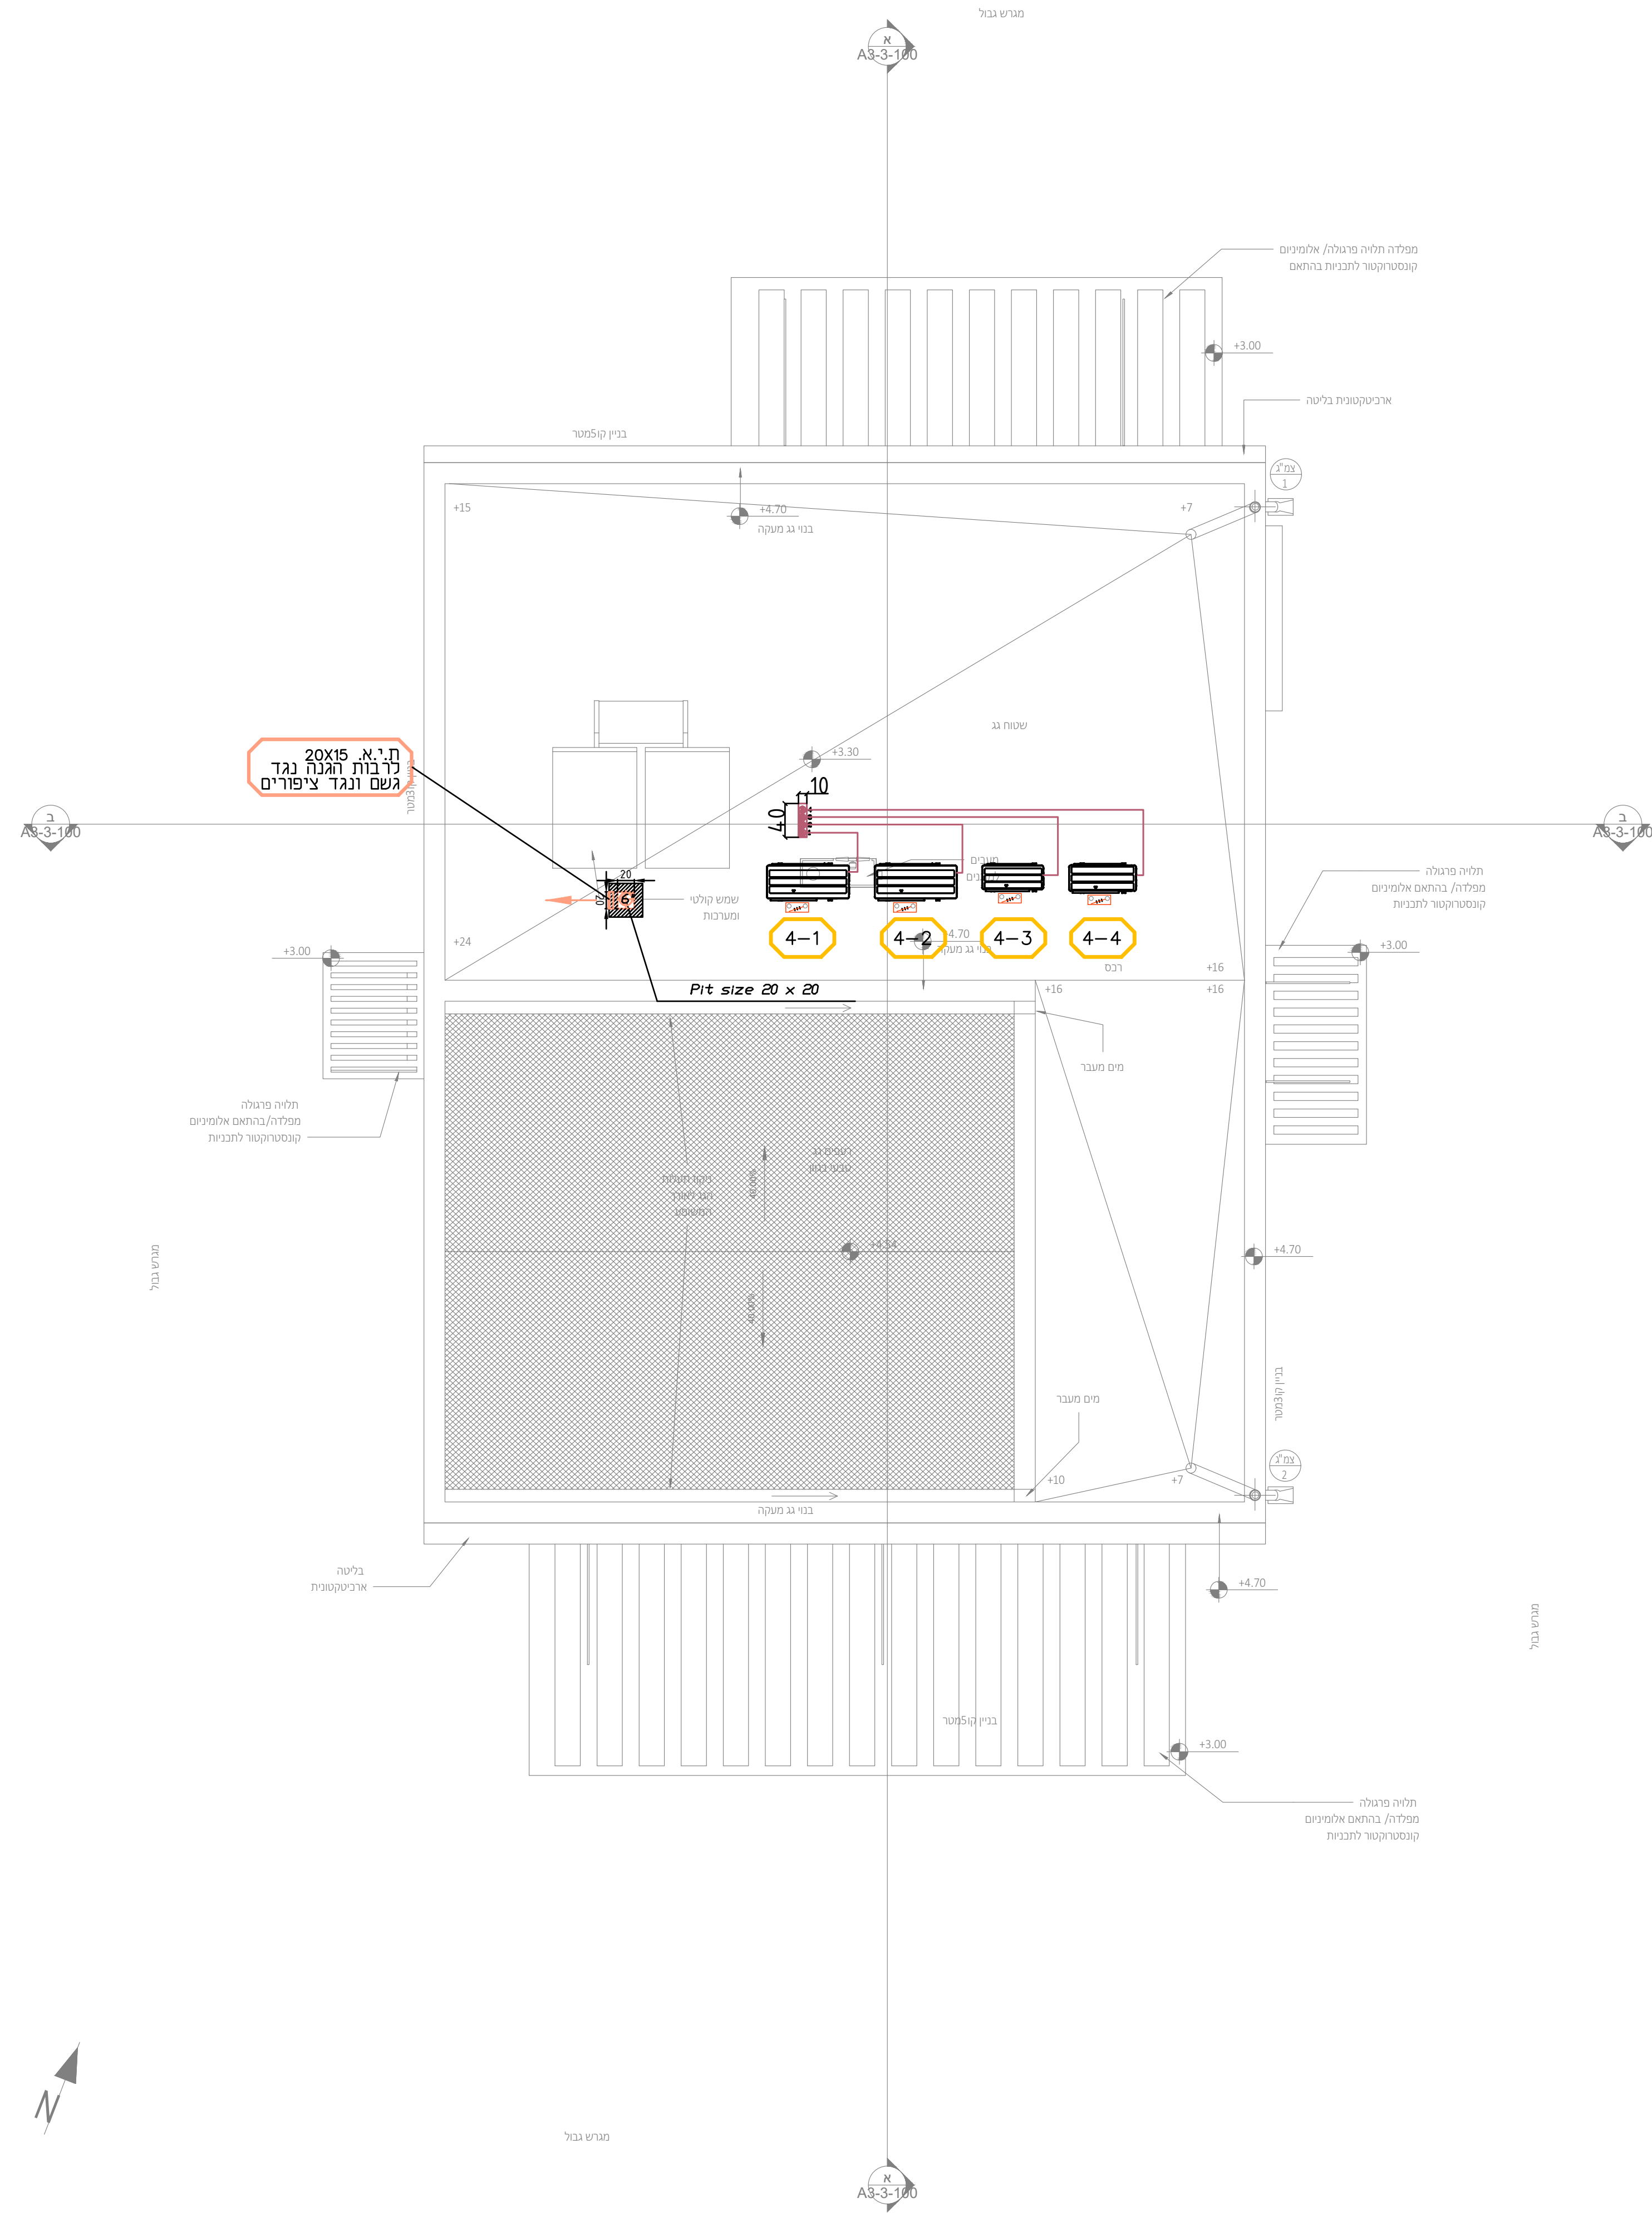

אדריכל	לוח	כותר פורט	טבל ראשי	טבלת הצעה	חשבוני	אקסטריה	בטוחות	אקסטריה	אדריכל פנים

מהדורה	תאריך	גרסה
1	18.09.2025	גרסה ראשונה
2	01.05.2025	גרסה שנייה
3	01.05.2025	גרסה שלישית

המבצע אחראי למידות ובהתאמתן למציאות
בכל מידה של אי התאמה, סתירה או טעות
עליו להודיע למתכנן לפני התקדמותו בביצוע
אין לנכות מידות על סמך מדידה בשרטוט.
אין לעשות כל שימוש בחוכנית זו
או ברעיונות והנחיות בה לא אישר בכתב
מתא המתכנן.

הערות

- כל התעלות מחוץ למבנה יבודדו
בידוד אקוסטי בעובי 2"
- תעלות מזוג בתוך המבנה יבודדו
בידוד אקוסטי פנימי 1"
- תעלות אוויר צח יבודדו
בידוד טרמי 1"
- יש לאסום בסיקור את פינות החיבור
של תעלות מזוג אוויר כפני כיפוף
הפורם המתחברים

מקרא

- מפ- מפוח
- מ.א.ג. - מפוח אוויר קורי
- מ.א.ת. - מפוח אוויר תחריט
- ת.א.ת. - תריס אוויר חודר
- ת.א.צ. - תריס אוויר צח
- ב.א. - בידוד אקוסטי
- ב.ס. - בידוד טרמי
- כ.ב. - כלא בידוד
- ד.א. - דמפר אש
- טרנססטט לוח הפעלה
- שקע חשמל לספול יועץ חשמל
- שקע תלת פאזי לספול יועץ חשמל
- מפסק בטחון חד פאזי לספול יועץ חשמל
- מפסק בטחון תלת פאזי לספול יועץ חשמל
- ניקוז מאייד לספול יועץ אינסטלציה
בגובה 25 ס"מ מתחתית גובה המאייד
- שלט הפעלה אלקטרוני

מקרא צבעים בתכנית

- תעלות ותריסי אוויר חודר
- תעלות ותריסי אספקת אוויר
- תעלות ותריסי אוויר צח
- תעלות ותריסי 'ניקת אוויר
- תעלות ותריסי שיחורר עשן
- צנרת גז וחשמל
- סימון מעגלי מיזוג אוויר

מבני מגורים צמודי קרקע	191
נופיה אפרי מנשה	
מגרש 4	
שם הפרויקט	מיזוג אוויר ואיוורור
מספר	1:50
תאריך פיתוח	18.09.2025
שם המעצב	מ.א.ג.
שם המעצב	מ.א.ג.
	אוריכל פנים
	אינסטיציה
	בסירת אש
	אקוטסיקה
	חשתי וחזורה
	קונסטרוקציה
	קברו ראש
	ניחול פוריקט
	לכוך
	אדריכל

		⚠
		⚠
חבניות רעיון	18.09.2025	⚠
חבניות רעיון	01.05.2025	⚠
שננים:	חאריד:	סל:

הערות

4. יש לאטום בסיליקון את פינות החיבור של תעלות מיזוג אויר לפני כיפוף הפחים המתחברים

מפוח

- T** **טרמוסטט** לוח הפעלה

- שקע חשמל לטפול יועץ חשמל
- שקע תלת פאזי לטפול יועץ חשמל
- מפסק בטחון חד פאזי לטפול יועץ חשמל
- מפסק בטחון תלת פאזי לטפול יועץ חשמל
- ניקוז מאיד לטפול יועץ אינסטלציה
בגובה 25 ס"מ מתחתית גובה המאייד
- שלט הפעלה אלווסי

תעלות ותריסי אוויר חוזר

- | | |
|--------------------------|---|
| תעלות ותריסי אספקת אוויר |  |
| תעלות ותריסי אוויר צח |  |
| תעלות ותריסי יניקת אוויר |  |
| תעלות ותריסי שיחרור עשן |  |
| צנרת גז וחשמל |  |
| סימון מעגלי מידוג אוויר |  |

191	מבני מוריס צמודי קרקע נפיה אלפי מנשה מגרש 4
1:50	על תרשים
18.09.2025	מיוזג אוויר ואווירור
תב"ד מוריס	קומת גג וטבלאות
2	על תרשים
מוריס	ענני
○	●
לבנים	לשור
01.05.2025	חור
תב"ד מוריס	איי אר