

מתכננים:

ניהול פרויקט
מהיסוד - בן סולומון
פיקוח
מהיסוד - בן סולומון
קונסטרוקציה
ערן שילר
מיזוג אוויר
אייל ארז מהנדסים ויועצים בע"מ
אינסטלציה
איתן אלמסי
חשמל
איתן בסיס
אלומיניום
נוף
נתי בלוקא
חשמל חכם
חימום תת רצפתי
איטום
צבי טל
אקוסטיקה
מעליות
קרקע וביסוס
דיה הנדסת קרקע וביסוס
רישוי

± 0.00 = +253.30
הערות: 1. תכנית זו יש לקרוא יחד עם תכנית הריטשים. 2. גובה אבסולוטי - ראו תכנית פיתוח. 3. המידות הן בין קירות הבניה ולא כולל פיתח. 4. פיתוח השטח סביב המבנה, כולל, מדרגות, גדרות, שבילים, ריצופים, שיפופים וכו'. 5. איטום קירות והצפות המבנה כמעט עם הקרקע ובידוד תרמי לאורך העמודים והקירות וכל המפרקים. כליות או עם סימני גיבס - ראו תכנית קונסטרוקציה. 6. אף דום יבוצע בכל מישור אופקי הכולל מהגבן. 7. סיוח תרמי בממד' ע"פ מפרט תומקיר, מאושר ט"י פיקוד העורף.
המבצע אחראי לסידות : עליו לבקר ולבדוק את כל המידות בתכנית ובנקטת הטובה. במסגרת של סמכות או אי התאמה בתכנית /או בבנוי, עליו להודיע על כך מיד לאדריכל בסרט המשיך בעבודתו. המבצע ישתמש או וקל בתכניתו שאושר לכניסו. המבצע יחזיק באחר, לכל שטח, של מודנו של תכנית. את לקבוע מידות על ידי חזירה בשטח. התכנית הינה רכוש האדריכל ואין לשנות כל שימוש בה או ברעיונות הגלומים בה, אלא באישור בכתב מהאדריכל. מהנדס /או יועץ אשר שמו רשום בתכנית זו, נושא לכיד באחריות המקצועית והסנדית לתכנית. על המפקח והמכיל לודא התאמת התכנית האדריכלית "כניסו" לתכנית ויתר, המכר והתכנית המאושרות ע"י כל הגורמים הרשמיים. התכנית כוללת את כל האמצעים והידע עד ליום תחלתה.

מקרא קירות:
קיר בלוקקיר בסוסעמוד בסוסן

תאריך	תיאור	מהדורה
22/09/2025	מכרז	1

אדריכלות

שם המסין:	CLIENT NAME:
קבוצת רכישה נופיה	
שם הפרויקט:	PROJECT NAME:
נופיה - מגרש 5	
שם הגליון:	DRAWING NAME:
גליון שער	
מספר גליון:	SHEET NUMBER:
A3-1-099	
מהדורה:	EDITION:
קנה מידה:	SCALE:
סטוס:	STATUS:
למכרז	
שורס ע"י:	נבדק ע"י:
תאריך:	DATE:
22.09.25	



NeumanHaynerArchitects


נוימן חיינר אדריכלים
מודד והנדס 2, בית חירות
09-9546842

office@nh-arch.com
www.nh-arch.com

22/09/2025 11:32:43

זכיות יימור / ע"פ הנחיות ע"ד

נופיה - מגרש 5			
מס' גליון	שם גליון	מהדורה	תאריך הפצת מהדורה
A3-1-099	גליון שער	1	22/09/2025
A3-1-100	קומת מרתף	1	22/09/2025
A3-1-101	קומת קרקע	1	22/09/2025
A3-1-102	גג	1	22/09/2025
A3-2-200	חזיתות 1	1	22/09/2025
A3-2-201	חזיתות 2	1	22/09/2025
A3-3-100	חתכים	1	22/09/2025
A3-4-100	גליון מדרגות	1	22/09/2025
A3-4-103	פרטים	1	22/09/2025
A3-4-104	פרטי פרגולה	1	22/09/2025
A3-6-1000	רשימת פתחים	1	22/09/2025

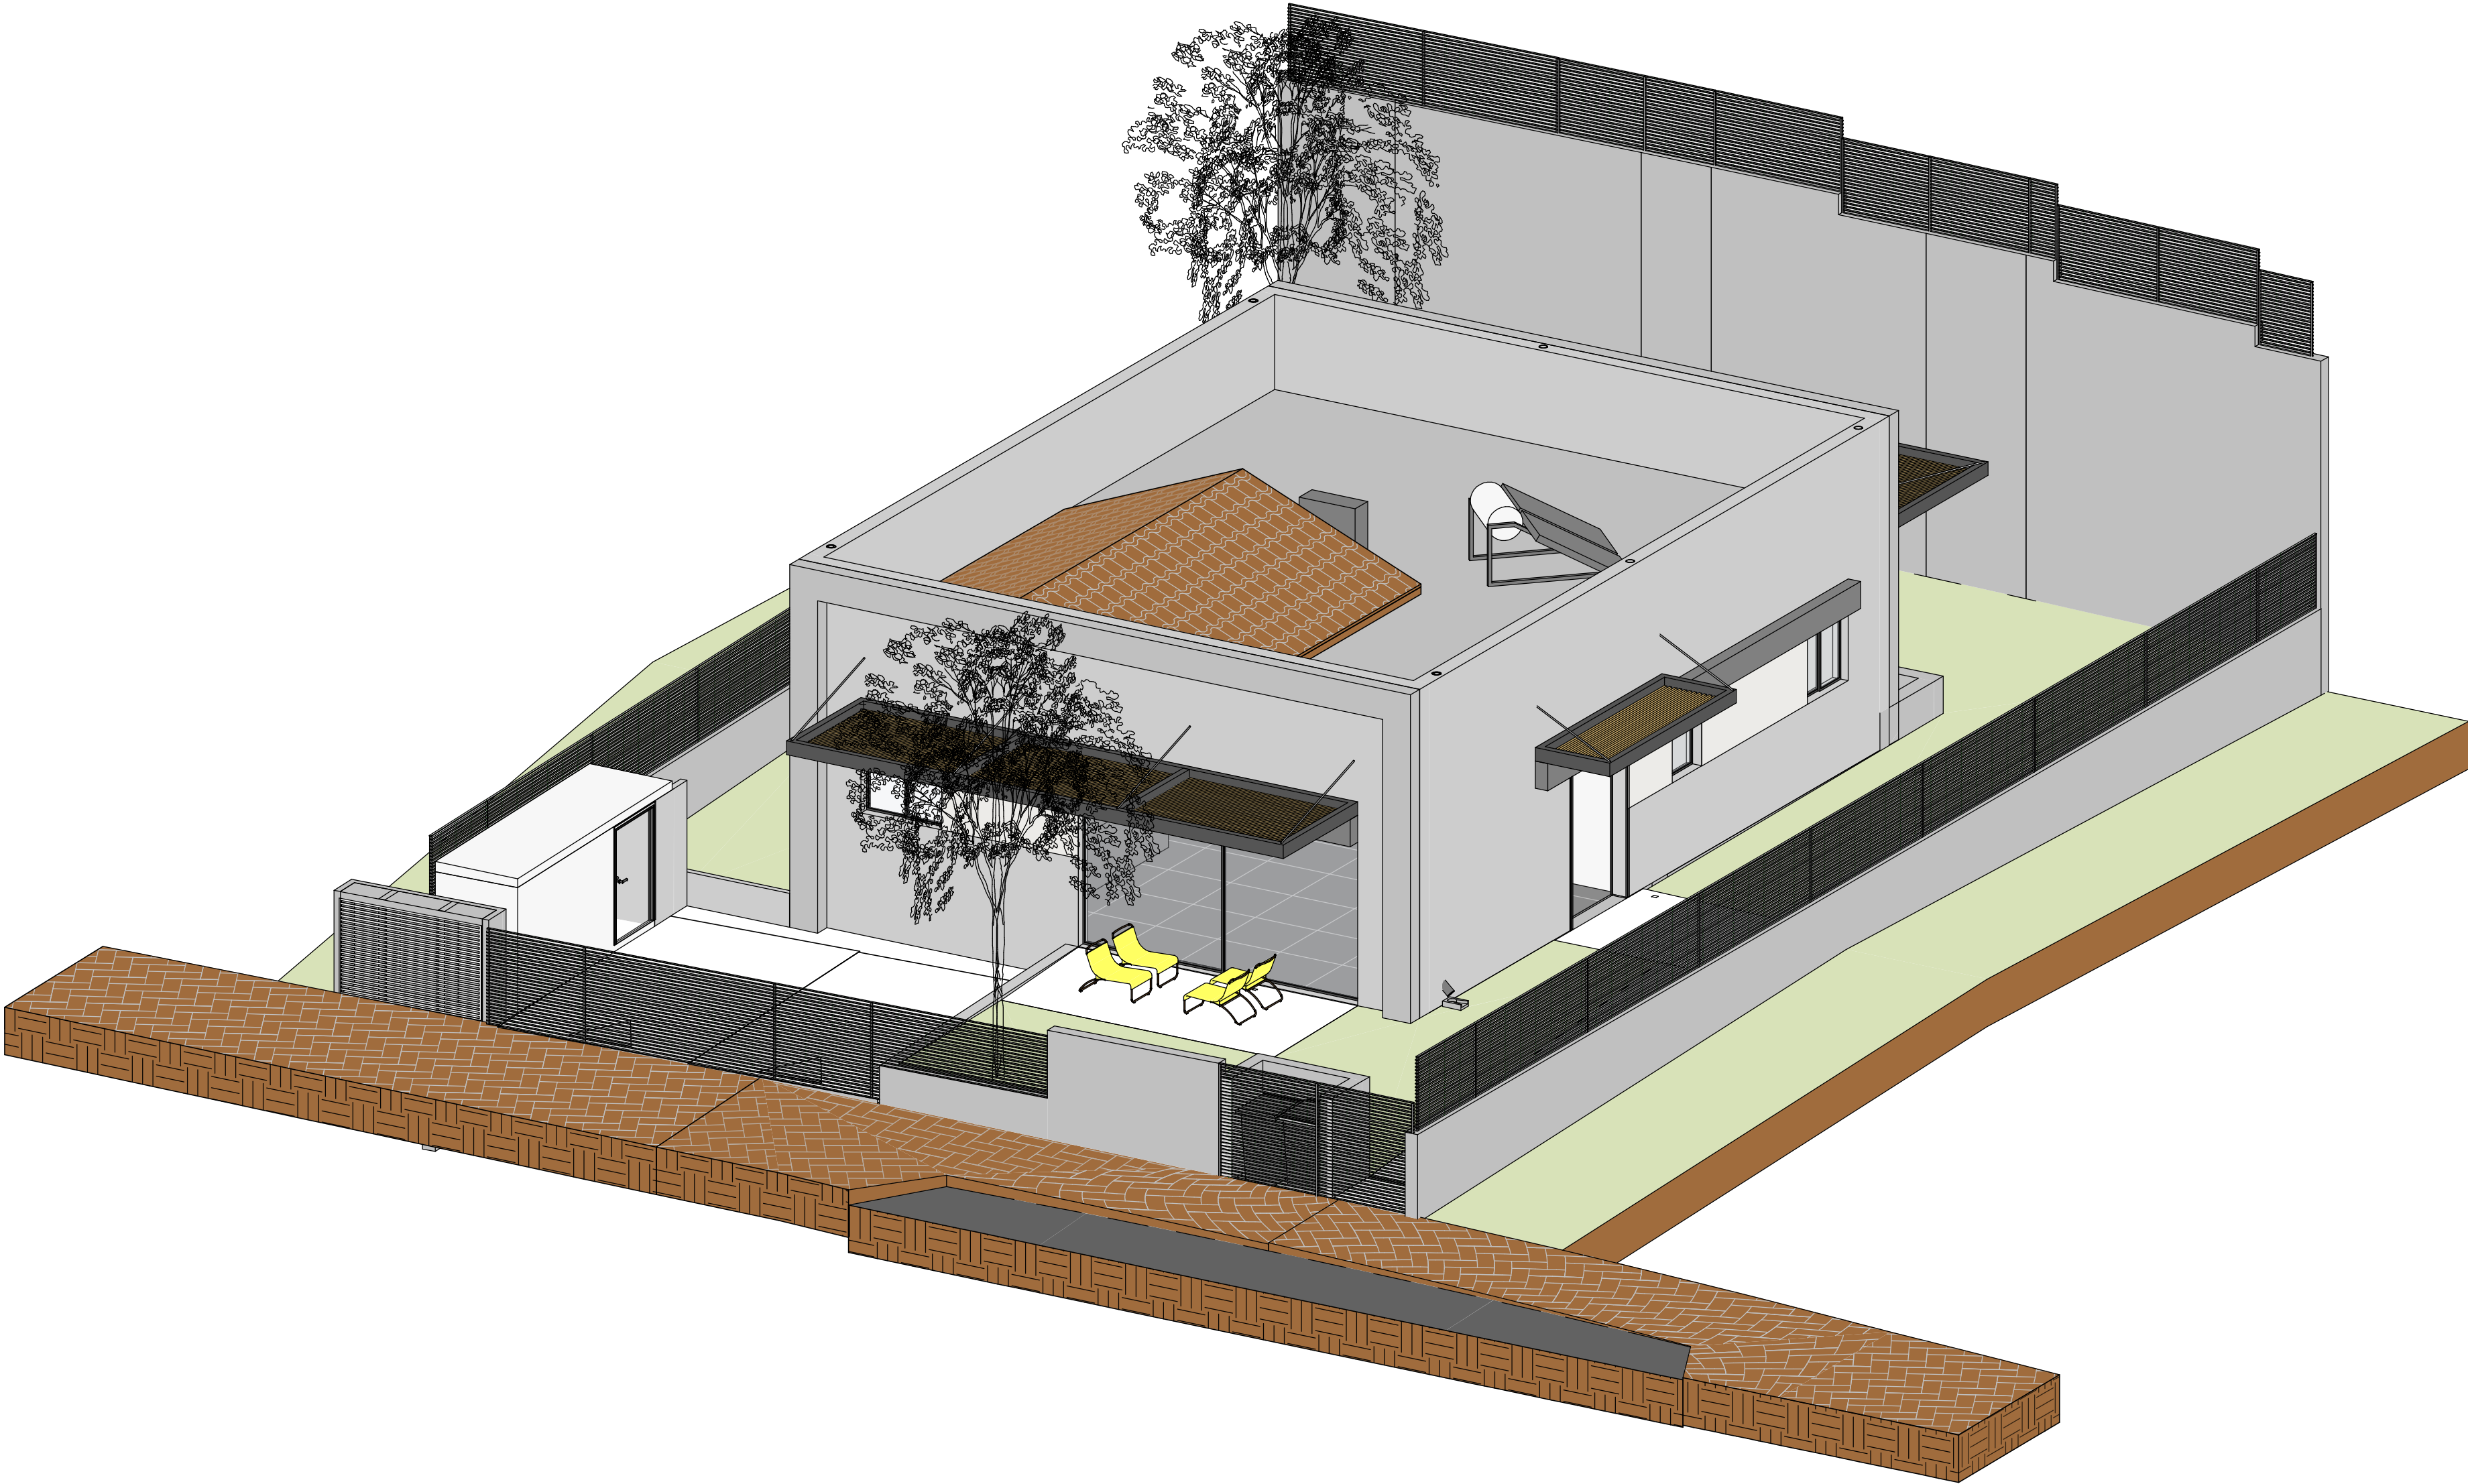

מתכונים:


ניהול פרויקט
מהיסוד - בן סולומון
פיקוח
מהיסוד - בן סולומון
קונסטרוקציה
ערן שילר
מיזוג אוויר
אייל ארז מהנדסים ויועצים בע"מ
אינסטלציה
איתן אלמסי
חשמל
איתן בסיס
אלומיניום
נוף
נתי בלוקא
חשמל חכם
חימום תת רצפתי
איטום
צבי טל
אקוסטיקה
מעליות
קרקע וביסוס
דיה הנדסת קרקע וביסוס
רישוי

$$\pm 0.00 = +253.30$$

הערות:
 1. תכנית זו יש לקרוא יחד עם תכניות הוועצים.
 2. גובה אבסולוטי – ראו תכנית פיתוח.
 3. המידות הן ב' ביורות תחתית' (ראו כלול 1.10).
 4. פיתוח השטח בשטח חניה, הנהגה, כלכלי, מדרגות, גדרות, שביליים, רציפים,
 5. פסיפגים וכו'.
 6. ראו תכנית פיתוח.
 7. ראו תכנית פיתוח.
 8. אסוס. תכנית ורצפות התקנה במגע עם הקרקע ובידוד תרמי לאורך המעטרים
 9. הקורות ועל התקורות – כליות או עם מיני (גירון) – ראו תכנית קונסטרוקציה
 10. א.4 ו.4.1 כיבוע כלבי מישור אופקי חתוכי החתך.
 11. ראו תרמי ממשל – ראו פרט מפורט, מומלץ, חתך ע"י פיקוד מרחק.

[illegible]

מקרא קירות:

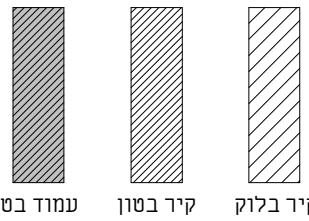[illegible]

אדריכלות

CLIENT NAME: _____ שם המזמין:

קבוצת רכישה נופיה

PROJECT NAME: _____ שם הפרויקט:

נופיה - מגרש 5

DRAWING NAME: ס הגליון:

SHEET NUMBER: 19

A3-1-100

SCALE: _____: קנה מידה: EDITION: _____: הדורה:

1:50

STATUS: 01000 1

רמטט ע"י:	נבדק ע"י:
-----------	-----------

DATE: 22.09.25 חתום:




NeumanHaynerArchitects

office@nh-arch.com
www.nh-arch.com

וימן חיינר אדריכלים
מורד ההדרים 2, בית חירות
טל 09-9545842

זכויות ייצור / ע"פ הנחיות עו"ד

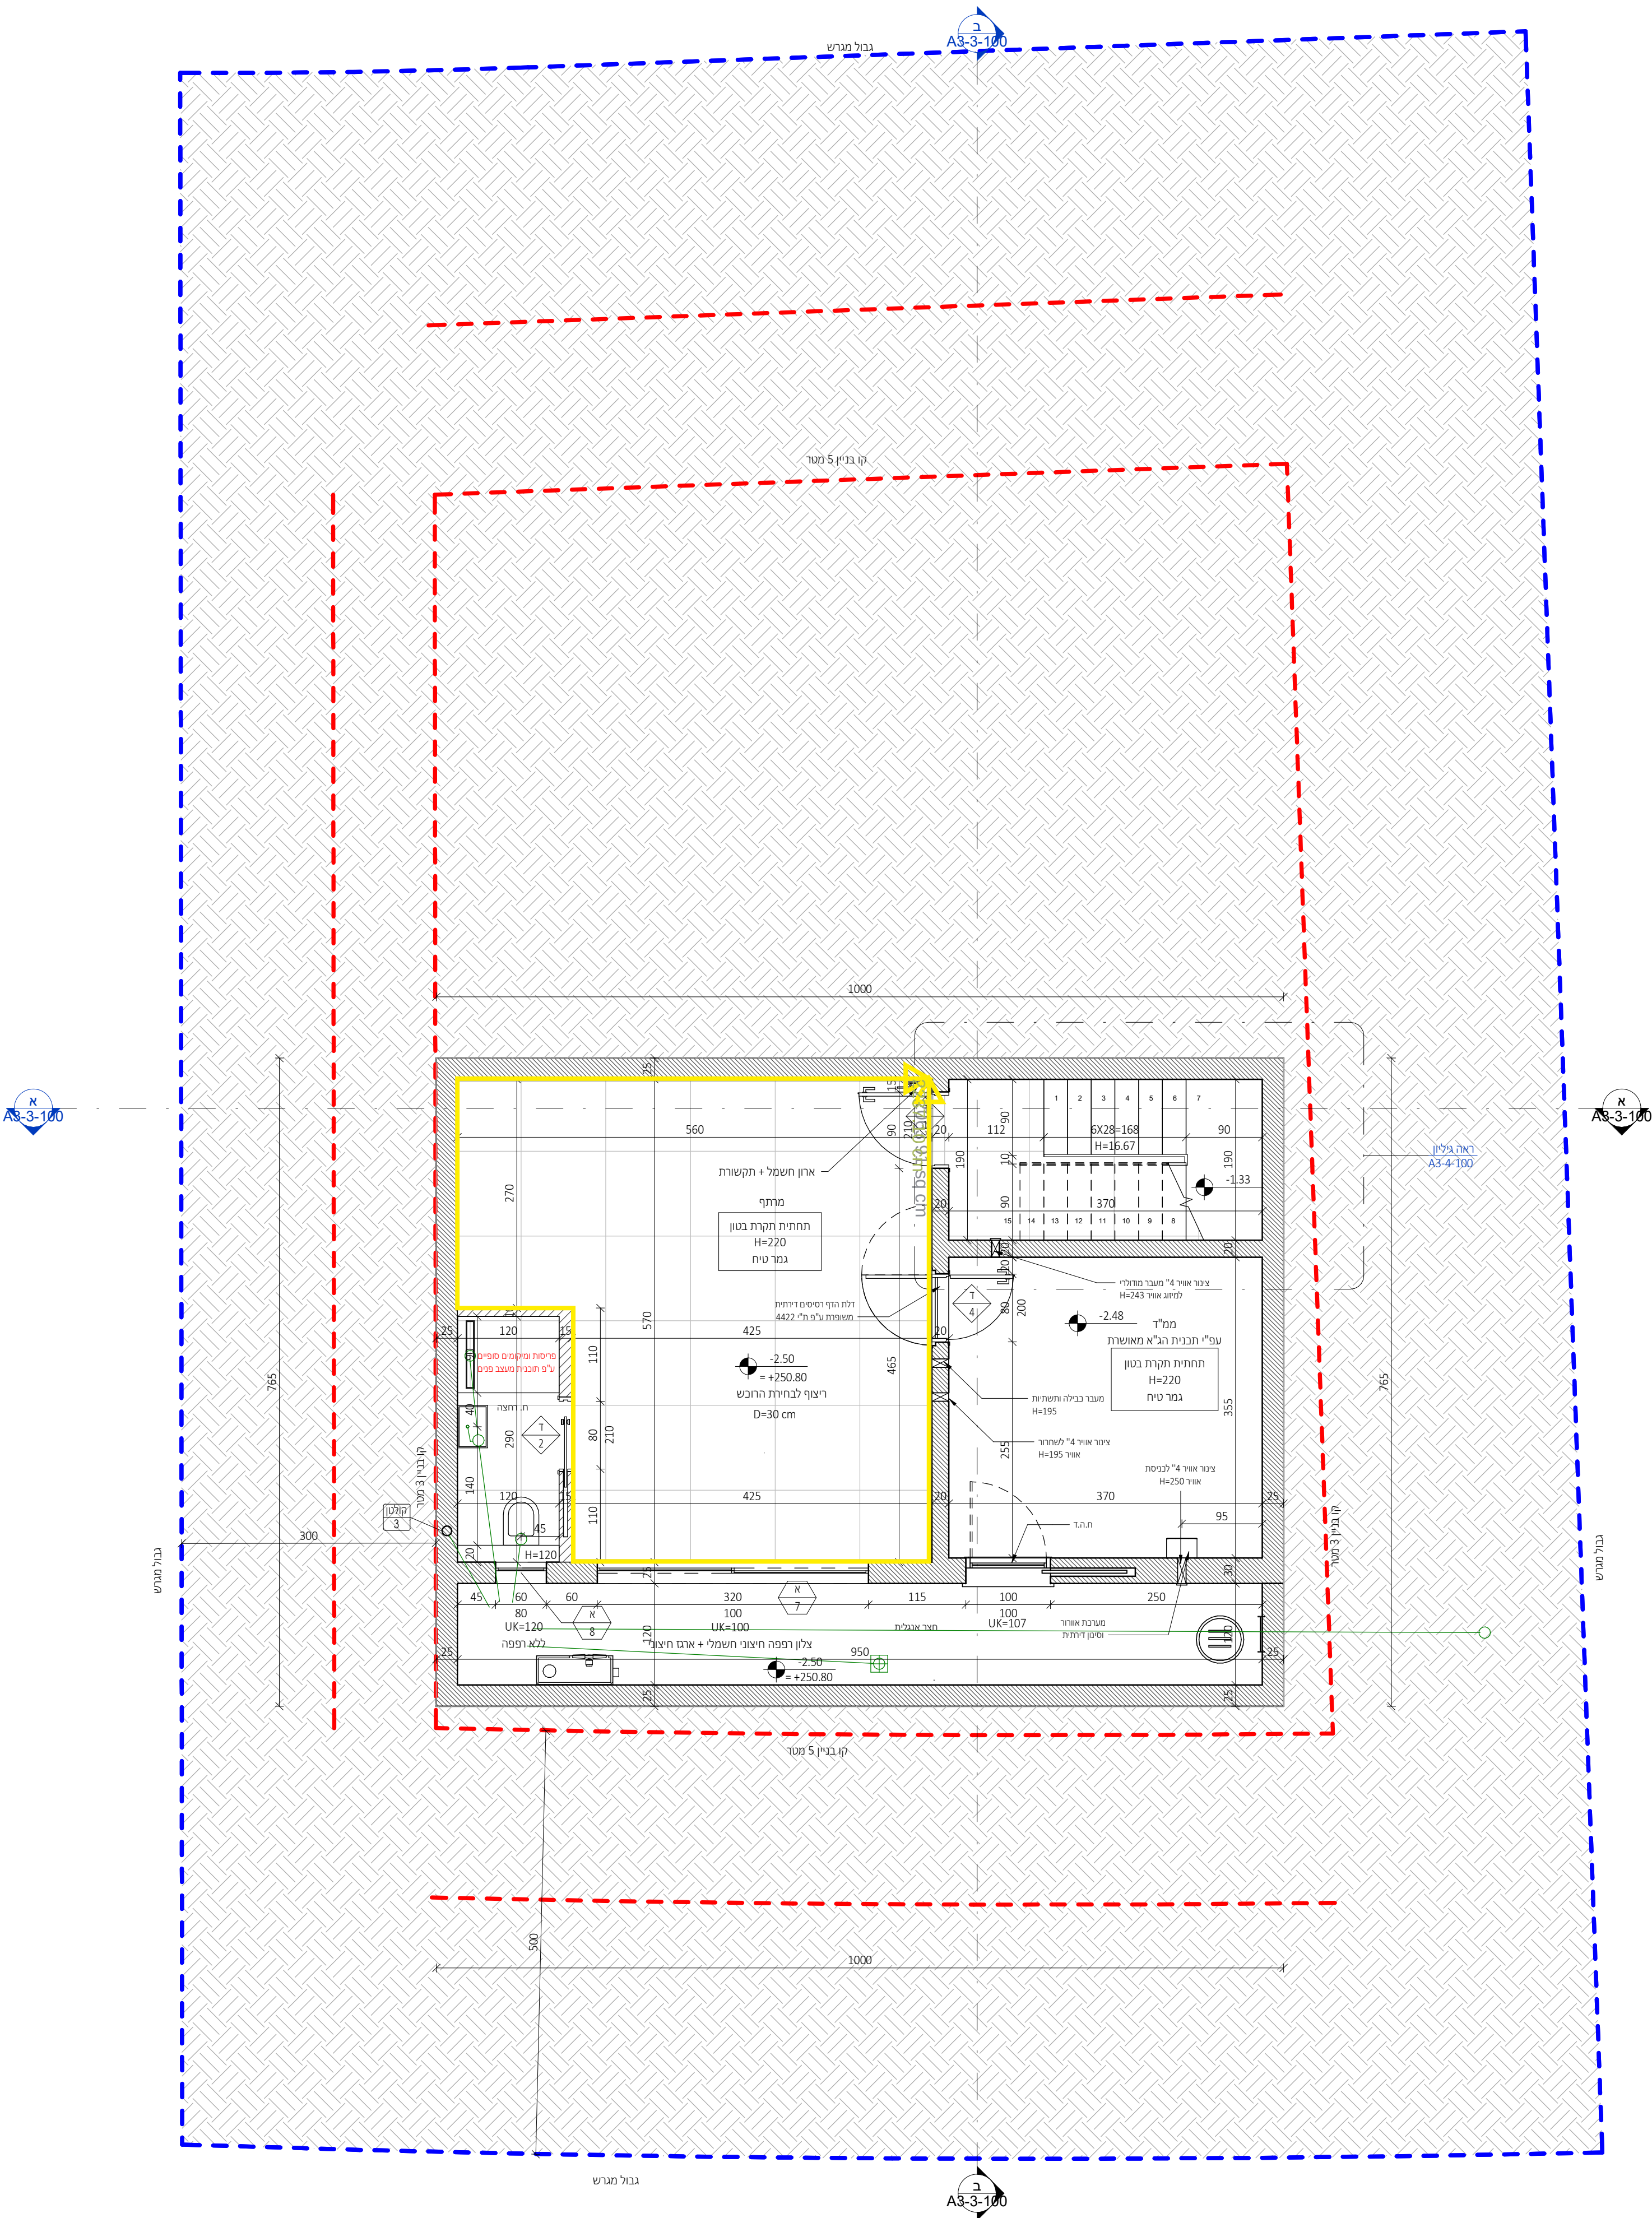

תכנית קומת מרתף

1 : 50

הערות:

1. יש לעבוד במקביל לתכניות יועצים המאושרות על ידי האדריכל.
2. פרטי ספי חלון - עפ"י חוברת אלומיניום של הספק הנבחר ובתיאום מול אדריכל.
3. חימום תת רצפתי (במידה ויש במגרש זה) עפ"י פרטי הספק ובתיאום מול אדריכל.
4. יש לעבוד במקביל לתכניות עיצוב פנים (במידה ויש מעצב פנים במגרש זה) המאושרות על ידי האדריכל.
5. באחריות הקבלן לעדכן את האדריכל על אי התאמה בין התכניות יועצים לאדריכלות.
6. כל הדלתות לפי מפרט מצורף.
7. כל אלמנטי הבטון יקבלו התייחסות תרמית לפי הנחיות יועץ.
8. פרטי איטום, בידוד וניקוז עפ"י תכניות יועצים ובאחריות הקבלן.

ניהול פרויקט
מהיסוד - בן סולומון
פיקוח
מהיסוד - בן סולומון
קונסטרוקציה
ערן שילר
מיזוג אוויר
אייל ארז מהנדסים ויועצים בע"מ
אינסטלציה
איתן אלמסי
חשמל
איתן בסיס
אלומיניום
נוף
נתי בלוקא
חשמל חכם
חימום תת רצפתי
איטום
צבי טל
אקוסטיקה
מעליות
קרקע וביסוס
דיה הנדסת קרקע וביסוס
רישוי


[illegible][illegible]

CLIENT NAME:		המספר 10	
קבוצת רכישה נופיה			
PROJECT NAME:		הפרויקט 10	
נופיה - מגרש 5			
DRAWING NAME:		התוכנית 10	
קומת קרקע			
SHEET NUMBER:		הפרויקט 10	
A3-1-101			
SCALE:	קנה מידה:	EDITION:	דורסה:
1 : 50			
STATUS:	סטוס:		
למכר			
	(101 ע"י):	דורסה ע"י:	
DATE:	22.09.25		איר:

NeumanHaynerArchitects

יומן חיינר אדריכלים
רודר והדרים 2, בית חירות
09-9545842 טל

office@nh-arch.com
www.nh-arch.com

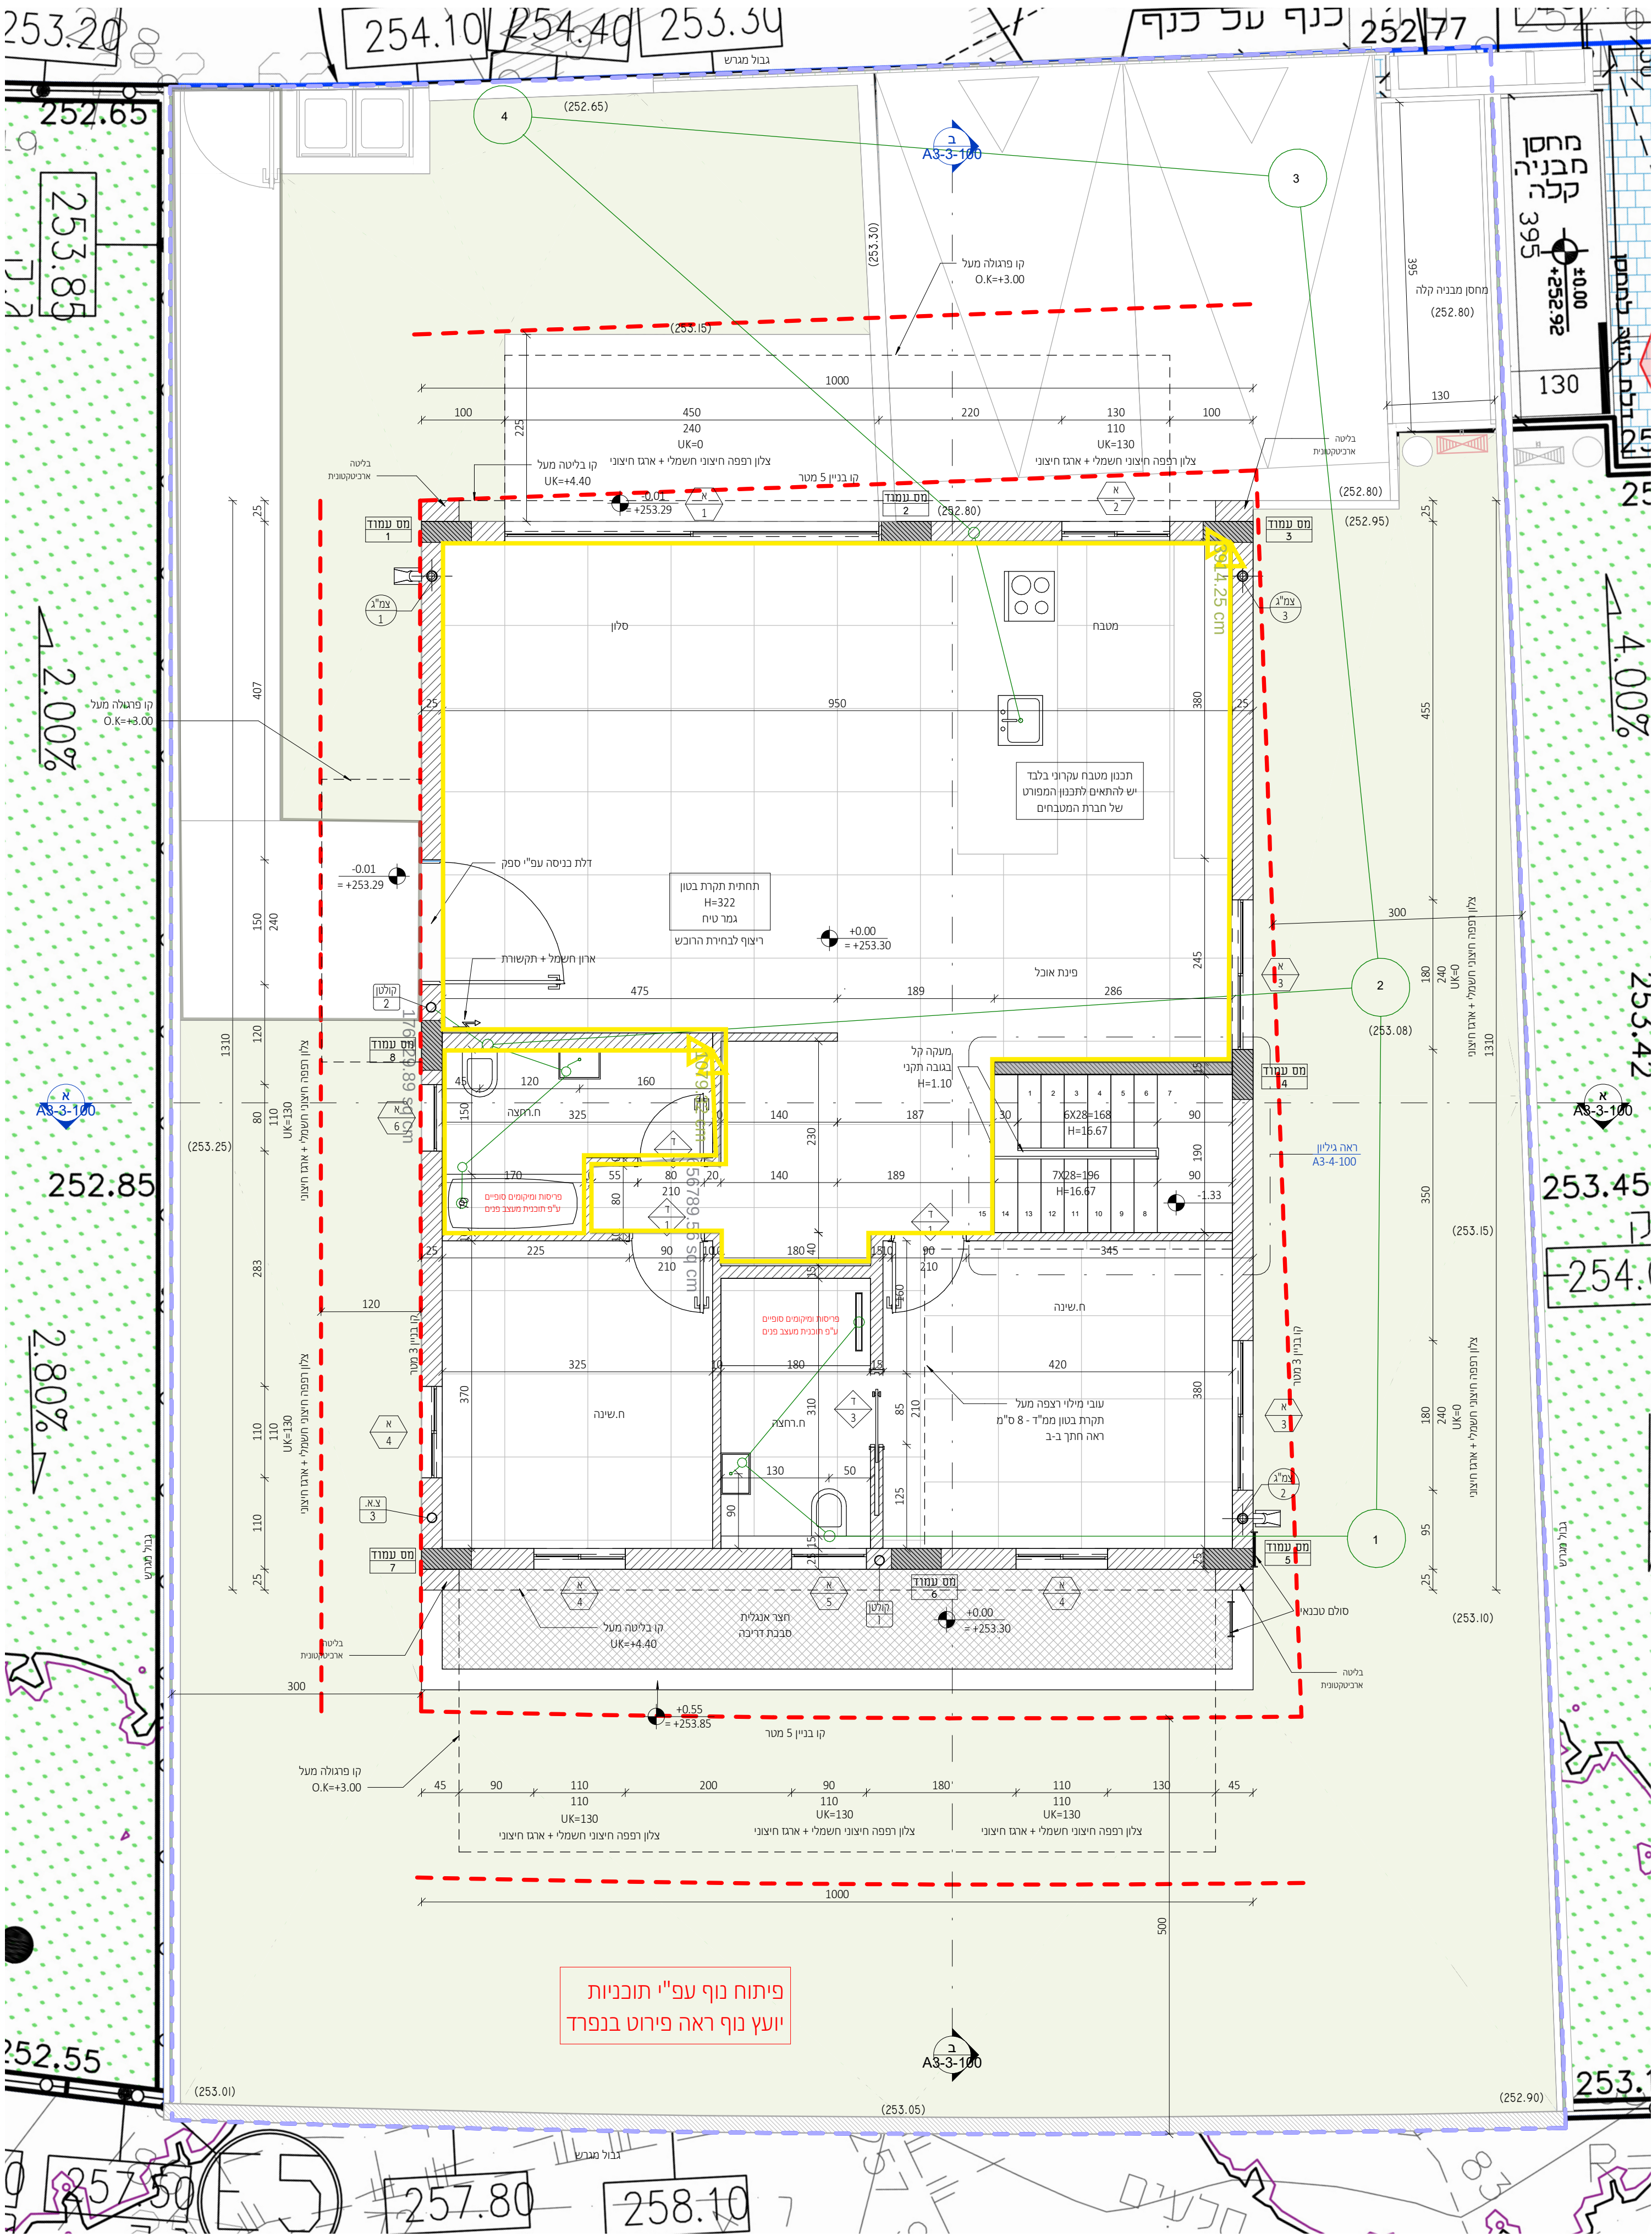

1 : 50


1. יש לעבוד במקביל לתכניות יועצים המאושרות על ידי האדריכל.
2. פרטי ספי חלון - עפ"י חוברת אלומיניום של הספק הנבחר ובתיאום מול אדריכל.
3. חימום תת רצפתי (במידה ויש במגרש זה) עפ"י פרטי הספק ובתיאום מול אדריכל.
4. יש לעבוד במקביל לתכניות עיצוב פנים (במידה ויש מעצב פנים במגרש זה) המאושרות על ידי האדריכל.
5. באחריות הקבלן לעדכן את האדריכל על אי התאמה בין התכניות יועצים לאדריכלות.
6. כל הדלתות לפי מפרט מצורף.
7. כל אלמנטי הבטון יקבלו התייחסות תרמית לפי הנחיות יועץ.
8. פרטי איטום, בידוד וניקוז עפ"י תכניות יועצים ובאחריות הקבלן.

מתכננים:

ניהול פרויקט
מהיסוד - בן סולומון
פיקוח
מהיסוד - בן סולומון
קונסטרוקציה
ערן שילר
מיזוג אוויר
אייל ארז מהנדסים ויועצים בע"מ
אינסטלציה
איתן אלמסי
חשמל
איתן בסיס
אלומיניום
בופ
נתי בלוקא
חשמל חכם
חימום תת רצפתי
איטום
צבי טל
אקוסטיקה
מעליות
קרקע וביסוס
דיה הנדסת קרקע וביסוס
רישוי

± 0.00 = +253.30
הערות: 1. תכנית זו אינה לקרא יחד עם תכנית הרישום. 2. גובה אבסולוטי: ראו תכנית פיתוח. 3. המידות הן בין קירות הבניה ולא כולל פחים. 4. פיתוח השטח סביב המבנה, כולל, מדרגות, גדרות, שבילים, ריצופים, שטחים בגובה, חניה וגן ראו תכנית פיתוח. 5. איטום קירות ורצפות המבנה כמתנע עם הקרקע ובידוד תרמי לאורך העמודים והקירות על מנת למנוע חדירת אוויר וסימני גרעין- ראו תכנית קונסטרוקציה. 6. איך דים יבוצע בכל מישור אופקי הכולל חתוכיו. 7. סוף תחמי במסלול- ע"פ מפרט חומרים, מאושר ע"י פיקוח העורך. המבצע אחראי לסידור: עליו לבקר ולבדוק את כל המידות בתכנית ובקטע המבנה. במסלול של שטח או אי התאמה בתכנית /או בבנין, עליו להודיע על כך מיד לאדריכל בסיום המשרד בעבודתו. המבצע יחזיק את רוב תכניות שאושרו לכניסה. המבצע יחזיק את כל המידות, כלל, נט, של שטחו של תכנית. אין לקבוע מידות על ידי מדידה בשטח. התכנית הינה רישום האדריכל ואין לטעון כל שימוש בה או ברעיונות הגלומים בה, אלא באישור בכתב מהאדריכל. חומרים /או יושם אשר שמו רשום בתכנית זו, נושא לכיד באחריות המעצבים והמקצועית לתכנית. על המפעל והמקבל לודא התאמת התכנית האדריכלית "כביצוע" לתכנית זו, תוכן התכנית והאחריות המוטלות על כל הגורמים הרשומים. התכנית כוללת את כל האחריות והידוע עד ליום תחלתה.


מקרא קירות:

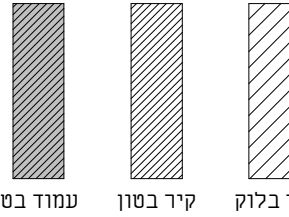

תאריך	תיאור	מהדורה
22/09/2025	מכרז	1

אדריכלות

שם המסמך:	CLIENT NAME:
קבוצת רכישה נופיה	
שם הפרויקט:	PROJECT NAME:
נופיה - מגרש 5	
שם הגליון:	DRAWING NAME:
גג	
מספר גליון:	SHEET NUMBER:
A3-1-102	
תאריך:	DATE:
22.09.25	

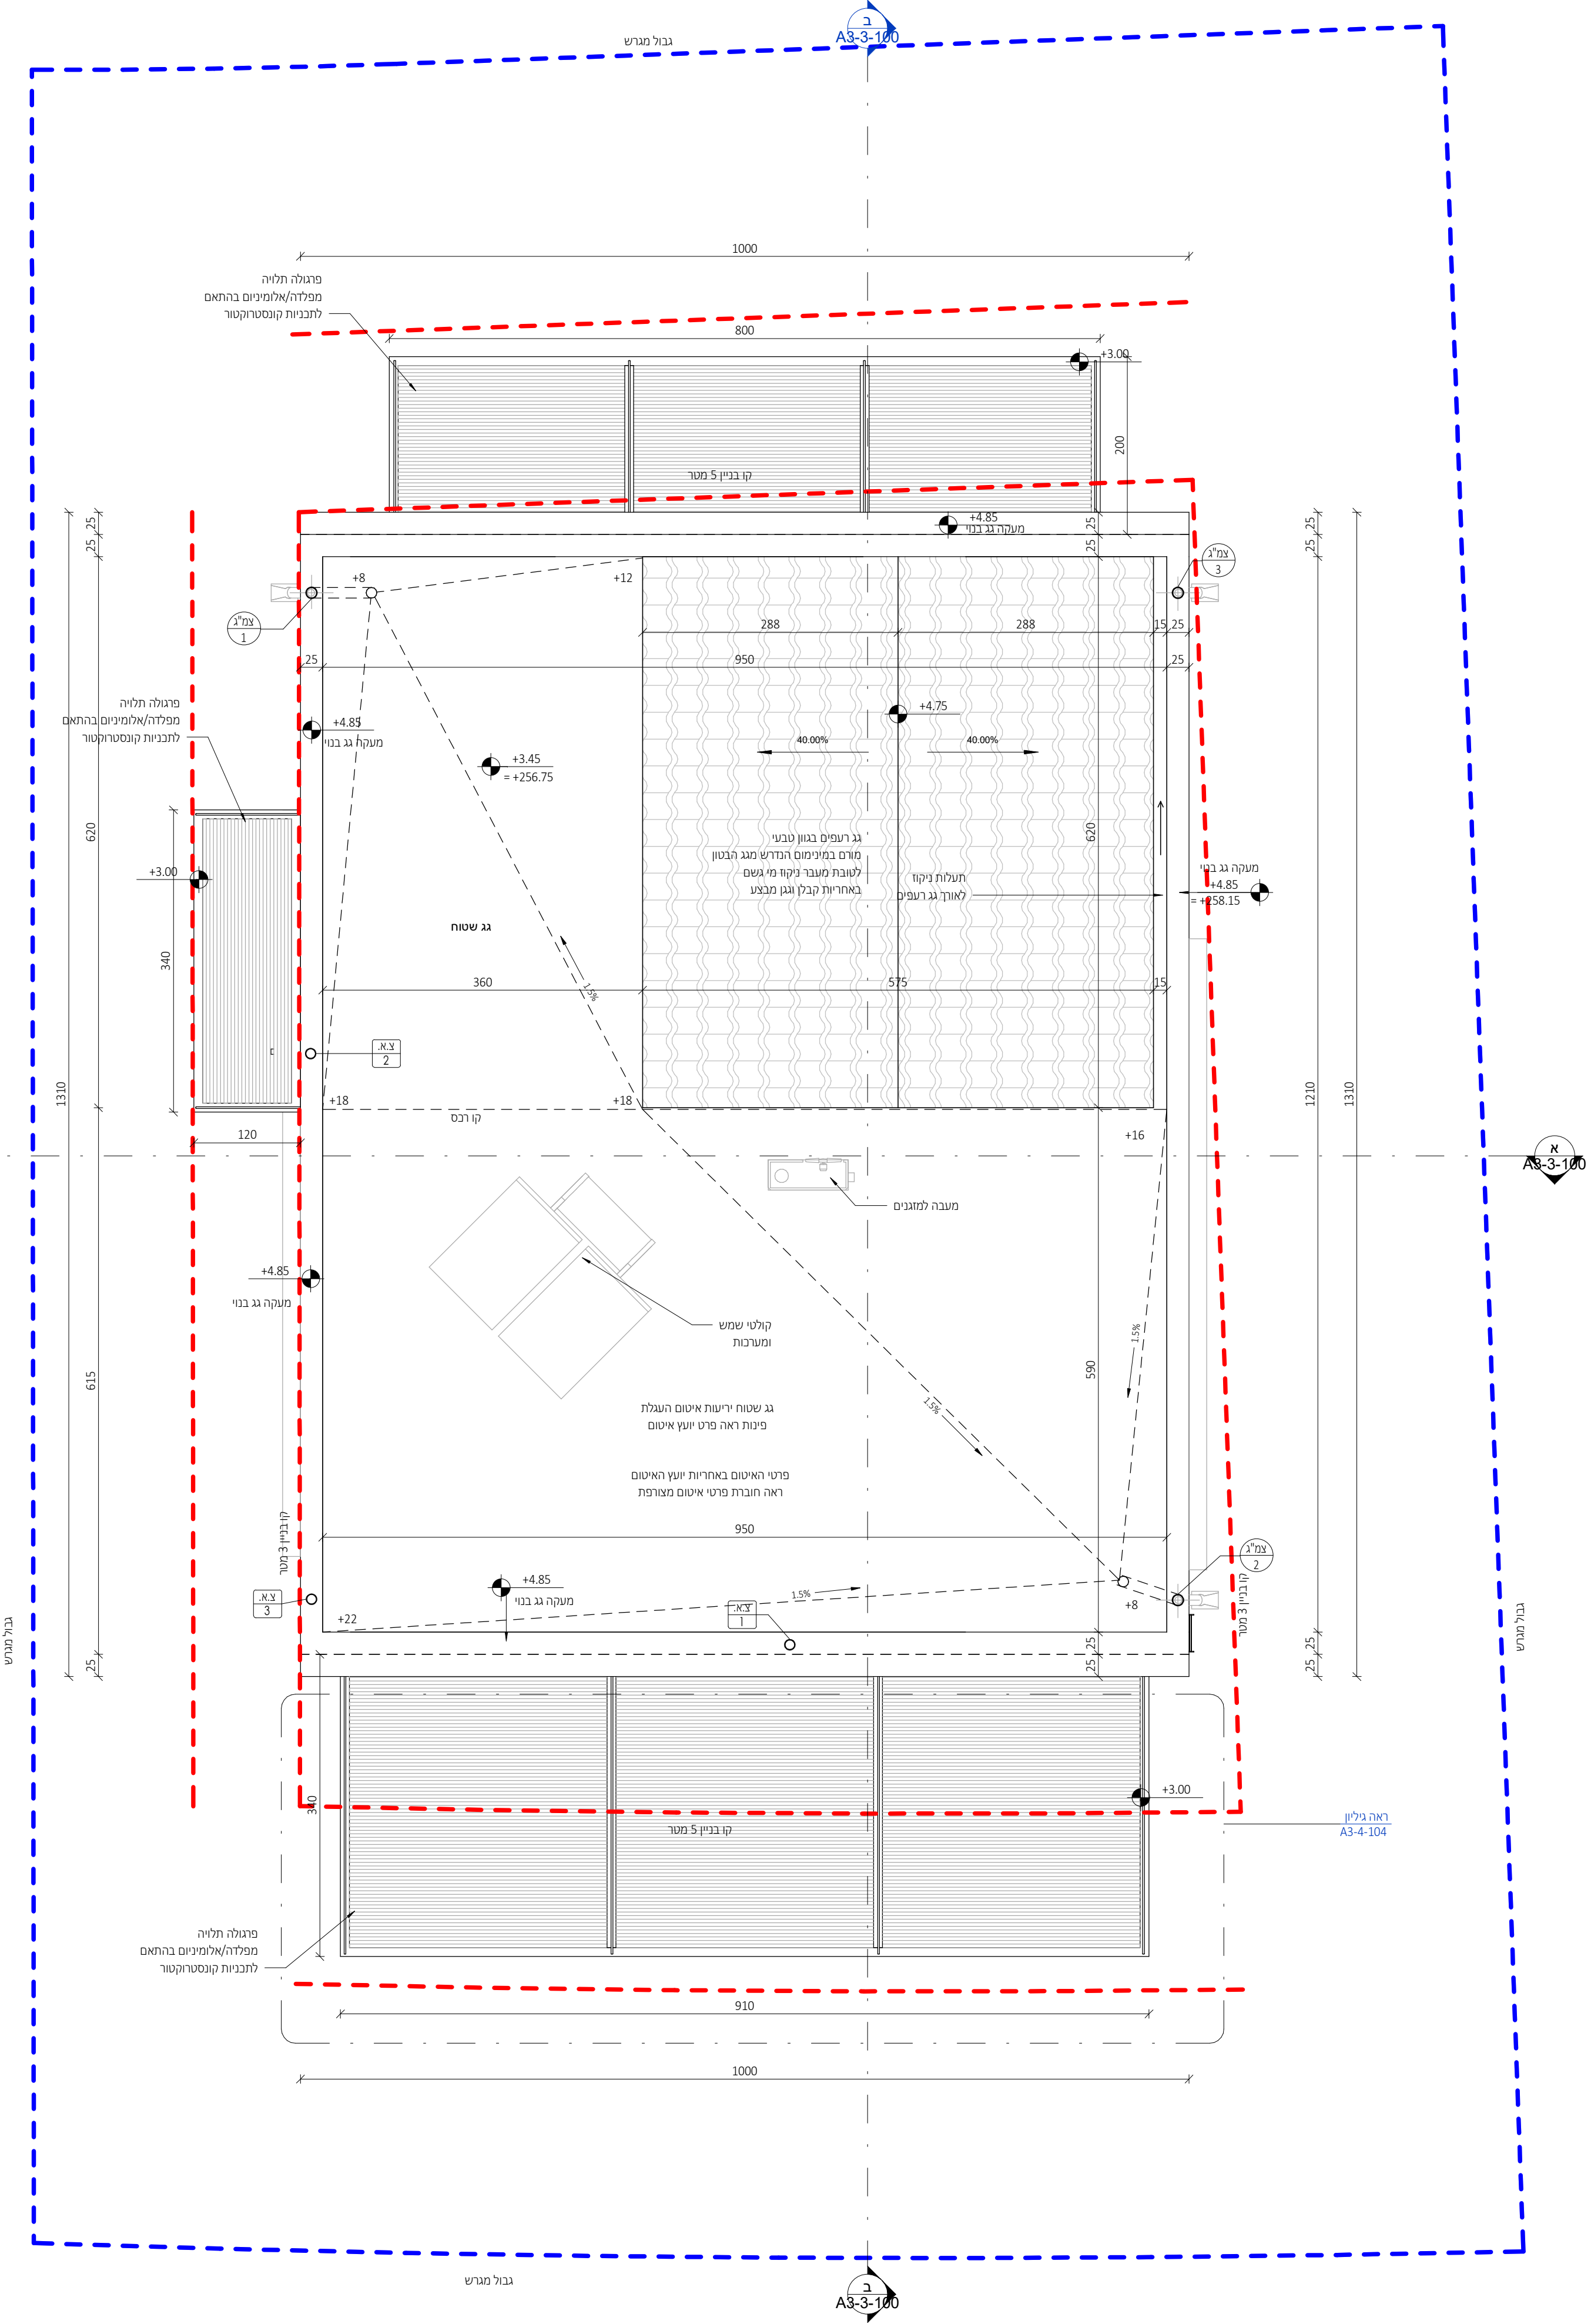

תכנית קומת גג

1 : 50

מתכננים:

ניהול פרויקט
מהיסוד - בן סולמון
פיקוח
מהיסוד - בן סולמון
קונסטרוקציה
ערן שילר
מיזוג אוויר
אייל ארז מהנדסים ויועצים בע"מ
אינסטלציה
איתן אלמסי
חשמל
איתן בסיס
אלומיניום
נוף
נתי בלוקא
חשמל חכם
חימום תת רצפתי
איטום
צבי טל
אקוסטיקה
מעליות
קרקע וביסוס
דיה הנדסת קרקע וביסוס
רישוי

± 0.00 = +253.30
הערות: 1. תכנית זו הי לקרא יחד עם תכנית הריטשים. 2. גובה איטום: ראו תכנית סיטוח. 3. המידות הן בין קירות הבניה ולא כולל סיח. 4. פיתוח השטח סביב המבנה, כולל, מדרגות, גדרות, שבילים, ריצופים, שטחים גרויים, חניה וגן ראו תכנית פיתוח. 5. איטום קירות ורצפות המבנה כמעט עם הקרקע ובידוד תרמי לאורך העמודים והקורות נפרד מהקירות. כליות או עם סימני גימון- ראו תכנית קונסטרוקציה. 6. אף חים יבוצע בכל מישור אופקי הכולל מחבנין. 7. סיח תרמי במסיד- ע"פ מפרט דוממקיר, מאושר ע"י פיקוח העיר.
המבצע אחראי לסידות: עליו לבקר ולבדוק את כל המידות בתכנית ובקטום המבוצה. במסגרת של מידות או אי התאמה בתכנית /או בבנין, עליו להודיע על כך מיד לאדריכל כנסד המשיך בעבודותיו. המבצע יישמש או ויק בתכנית שאושר לכניסיו. המבצע יחזיק באחר, בכל מות, של מחדש של תכנית. אז לקבוע מידות על ידי חזירה בשו שום. התכנית רחבה רחבה האדריכל יאזן לשווח כל שימוש בה או ברעיונות הגולמים בה, אלא באישור בכתב מהאדריכל. מחדס /או יושע אשר שמו רשום בתכנית זו, נושא לכז באחריות המקצועית והמקצועית לתכנית. על התפקד והשכלן ליוזא התאמת התכנית האדריכלית "לכניסיו" לתכנית. ויתר, המכר והתכנית האושרות ע"י כל גורמים ורשמיים. התכנית כוללת את כל האחריות והידוע על ליום תוצאתה.
מקרא קירות:
קיר בלוק קיר בסון עמוד בסון

תאריך	תיאור	מהדורה
22/09/2025	מכרז	1

אדריכלות


שם המסין:	CLIENT NAME:
קבוצת רכישה נופיה	
שם הפרויקט:	PROJECT NAME:
נופיה - מגרש 5	
שם הגליון:	DRAWING NAME:
חזיתות 1	
מספר גליון:	SHEET NUMBER:
A3-2-200	
תאריך:	DATE:
22.09.25	

22/09/2025 11:32:50

NeumanHaynerArchitects

נירסן חיינר אדריכלים
מודד תהדירס 2, בית חירות
09-954642 78
office@nh-arch.com
www.nh-arch.com


זכיות יימר / ע"פ הנחיות ע"ד

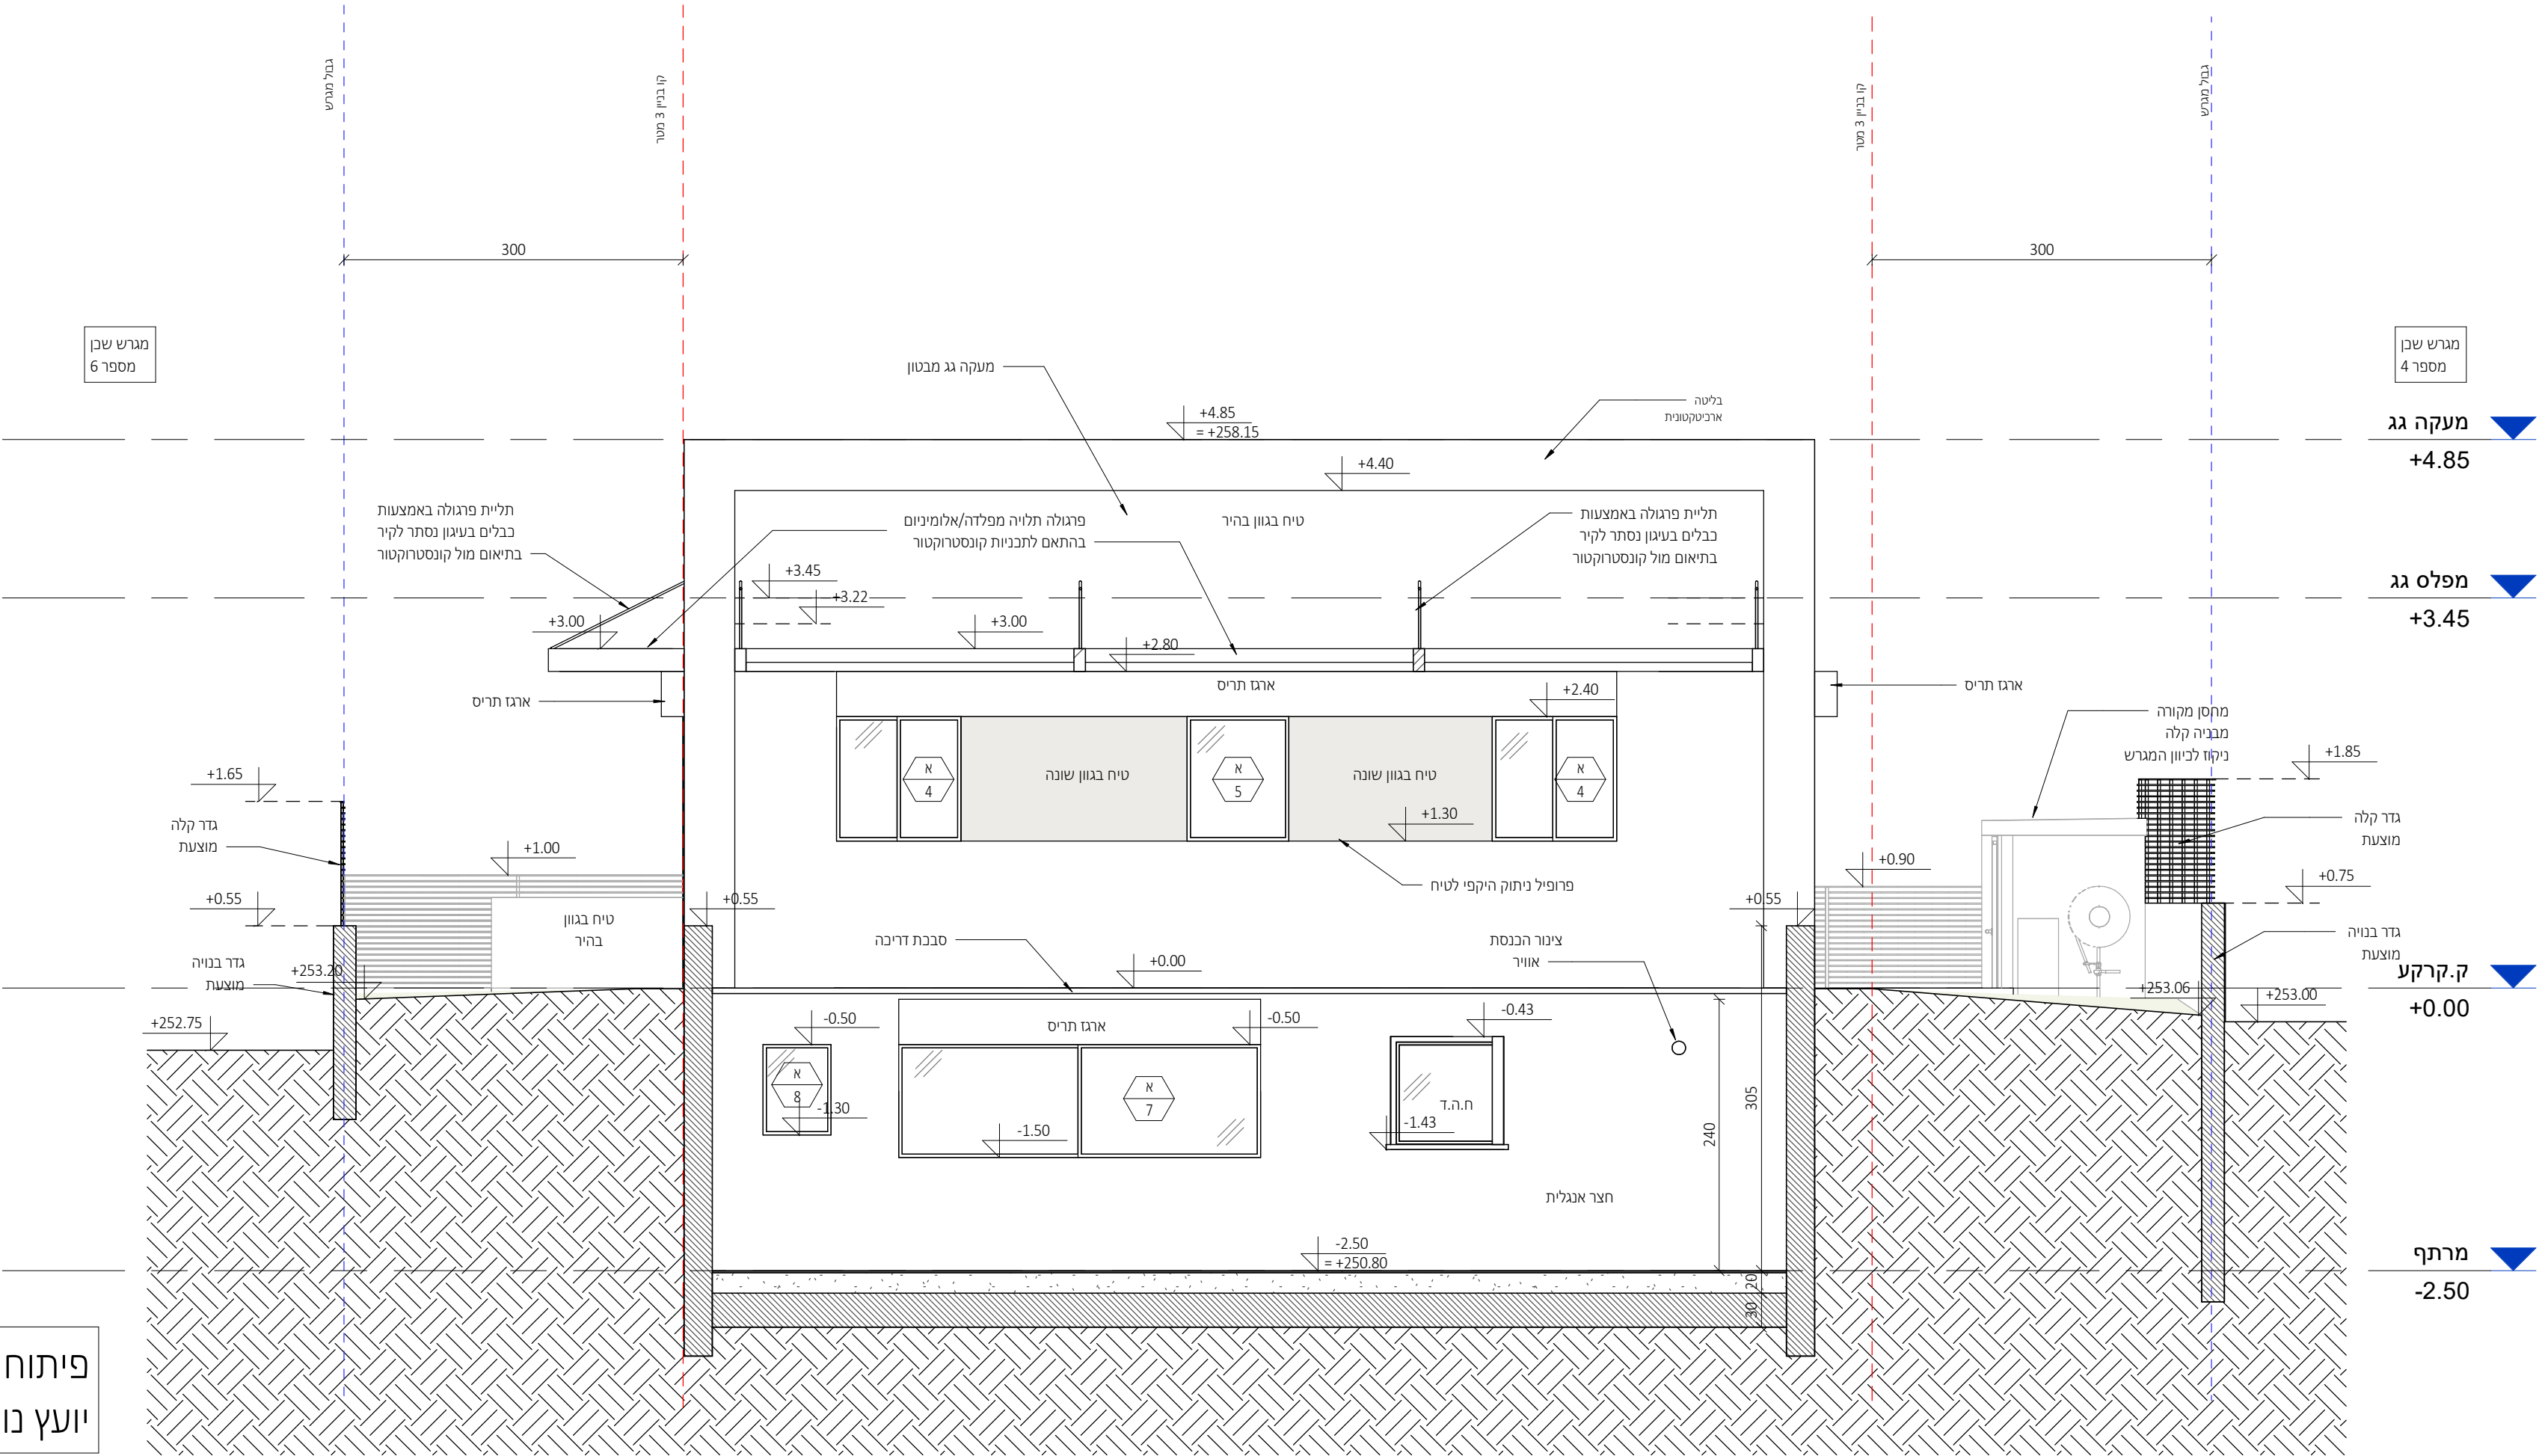

פיתוח נוף עפ"י תוכניות
יועץ נוף ראה פירוט בנפרד

חזית דרומית

1 : 50

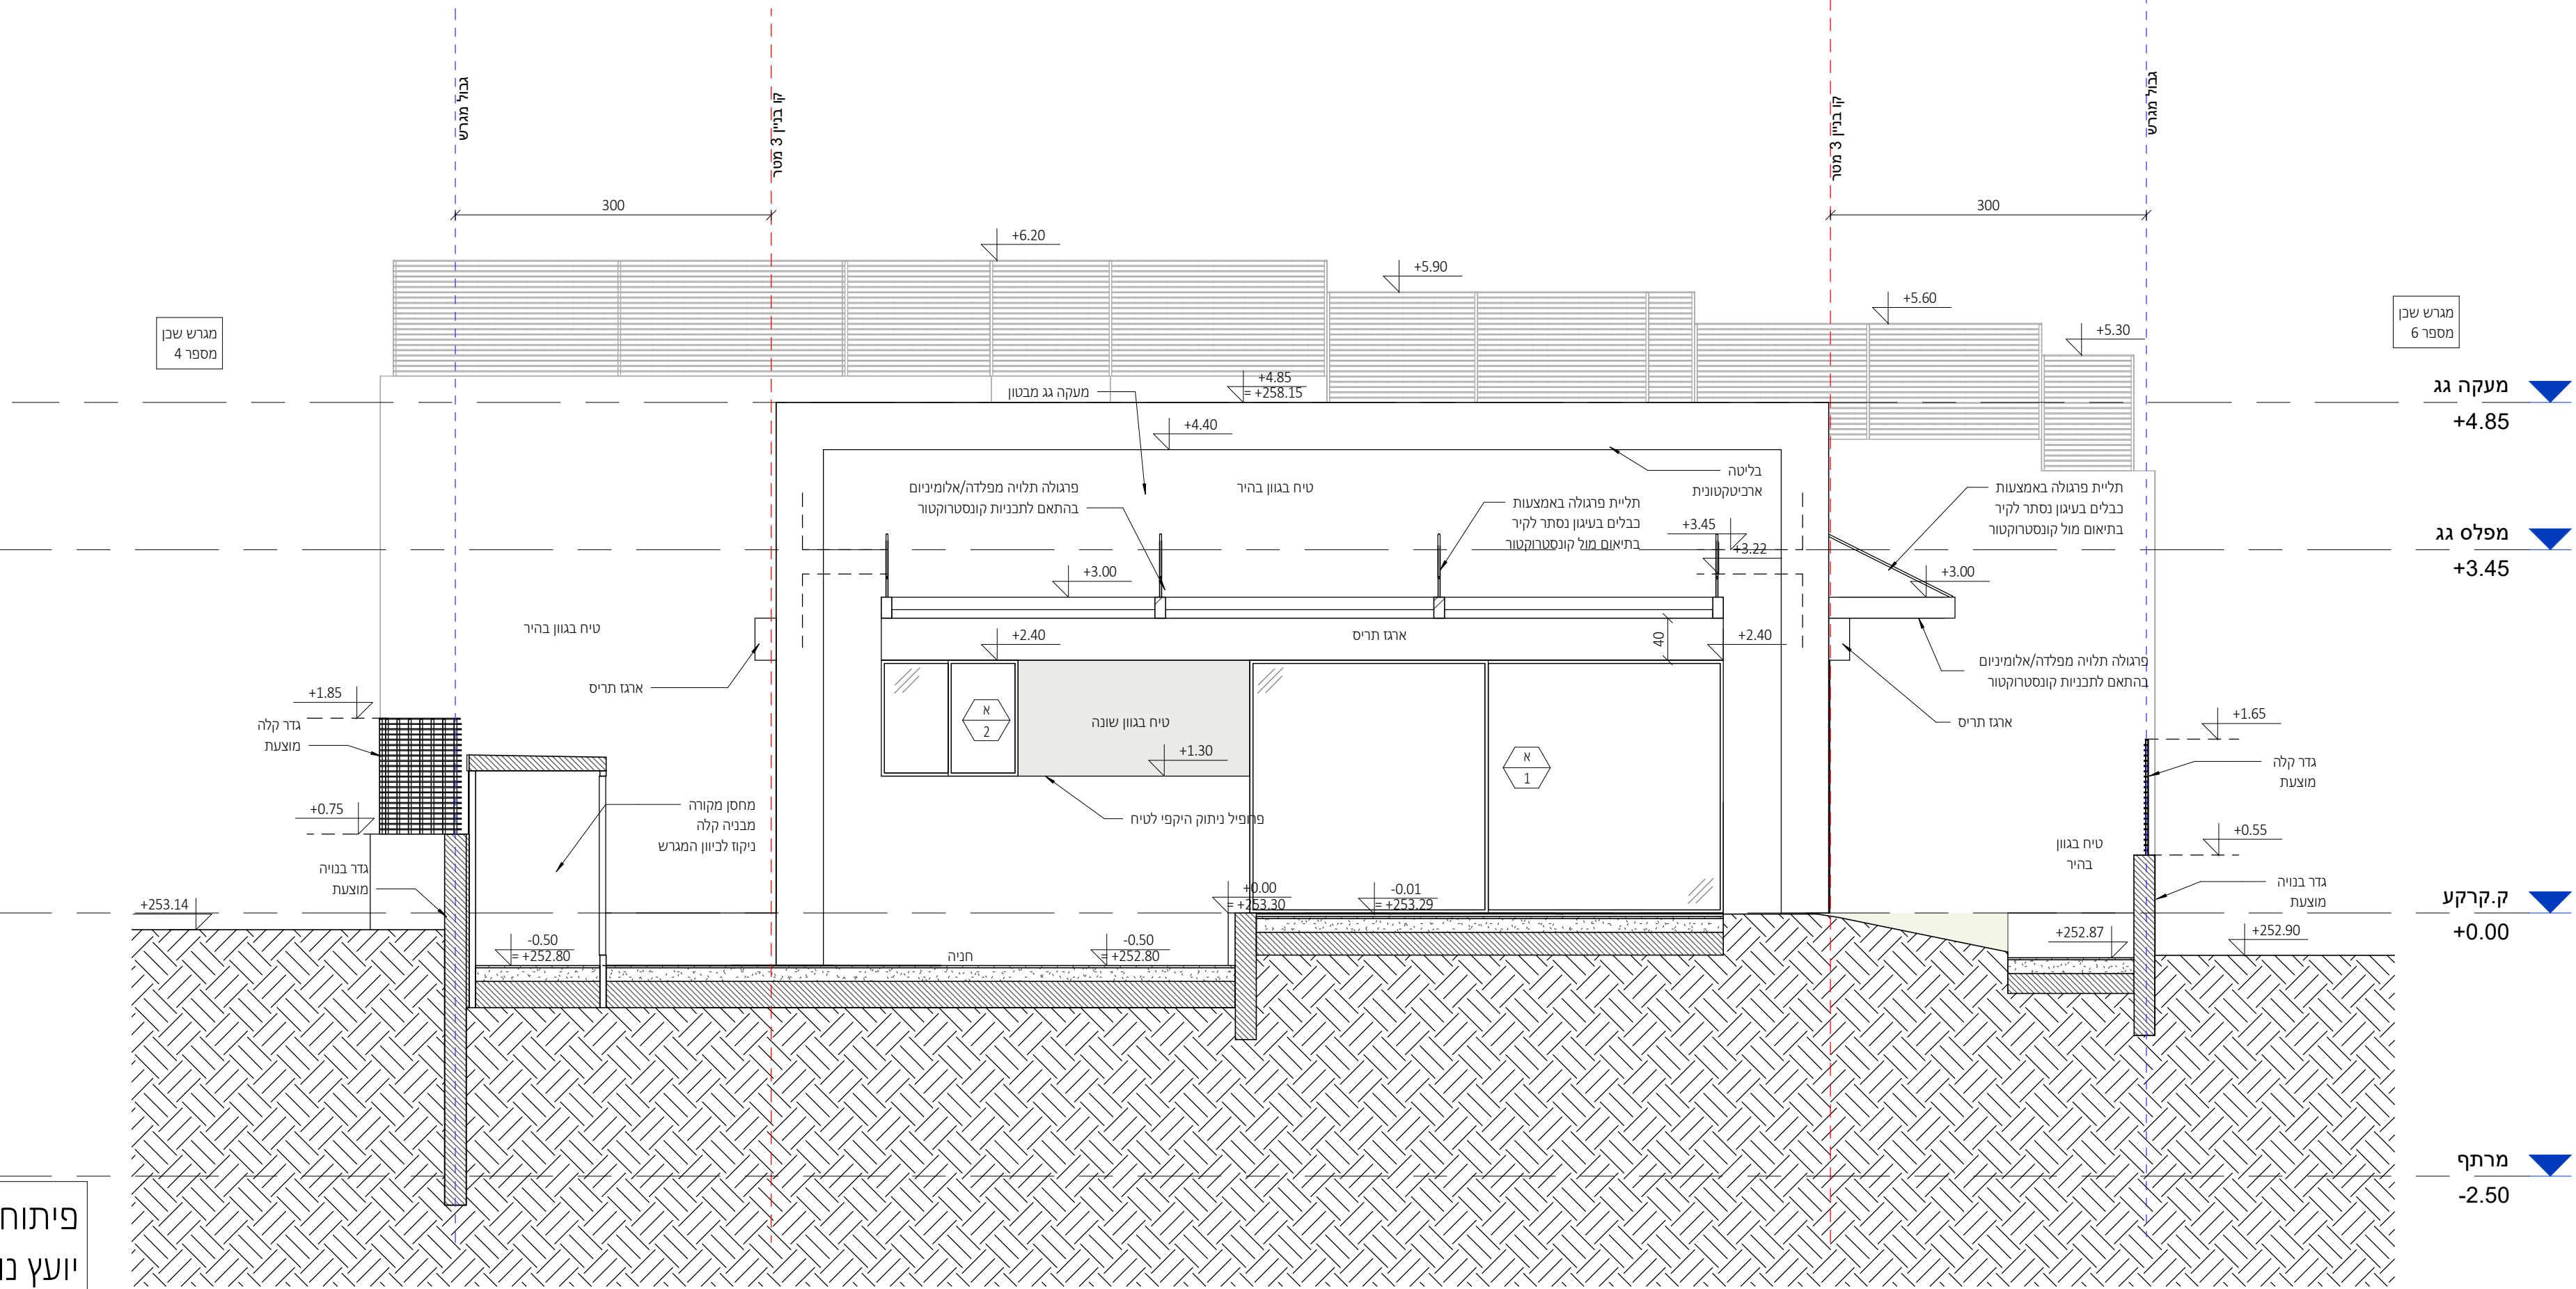

פיתוח נוף עפ"י תוכניות
יועץ נוף ראה פירוט בנפרד

חזית צפונית

1 : 50

פרטי איטום, בידוד וניקוז עפ"י תכניות יועצים ובאחריות הקבלן

מתכונים:

ניהול פרויקט
מהיסוד - בן סולומון
פיקוח
מהיסוד - בן סולומון
קונסטרוקציה
ערן שילר
מיזוג אוויר
אייל ארז מהנדסים ויועצים בע"מ
אינסטלציה
איתן אלמסי
חשמל
איתן בסיס
אלומיניום
בופ
נתי בלוקא
חשמל חכם
חימום תת רצפתי
איטום
צבי טל
אקוסטיקה
מעלות
קרקע וביסוס
דיה הנדסת קרקע וביסוס
רישוי

הערות:
 1. תבנית זו נלקחה יחד עם תוכנית העיונים
 2. כל מילוסלסוף אחרי תבנית נכתב
 3. המידות הן ב"ר קודמת תחת כל
 4. תבנית זו, כולל מידות, הן
 5. שטחים, גורמים, יחידות וכו' וכו'
 6. שטחים, גורמים, יחידות וכו' וכו'
[illegible]


אדריכלות

PROJECT NAME:		המחיר: 1000 ש"ח	
DRAWING NAME:		המחיר: 1000 ש"ח	
SHEET NUMBER:		המחיר: 1000 ש"ח	
SCALE:		EDITION:	
1 : 50		1	
TATUS:		המחיר: 1000 ש"ח	
למכר		המחיר: 1000 ש"ח	
DATE:		המחיר: 1000 ש"ח	
22.09.25		המחיר: 1000 ש"ח	


NeumanHaynerArchitects

office@nh-arch.com
www.nh-arch.com

זכויות ייצור / ע"פ הנחיות עו"ד

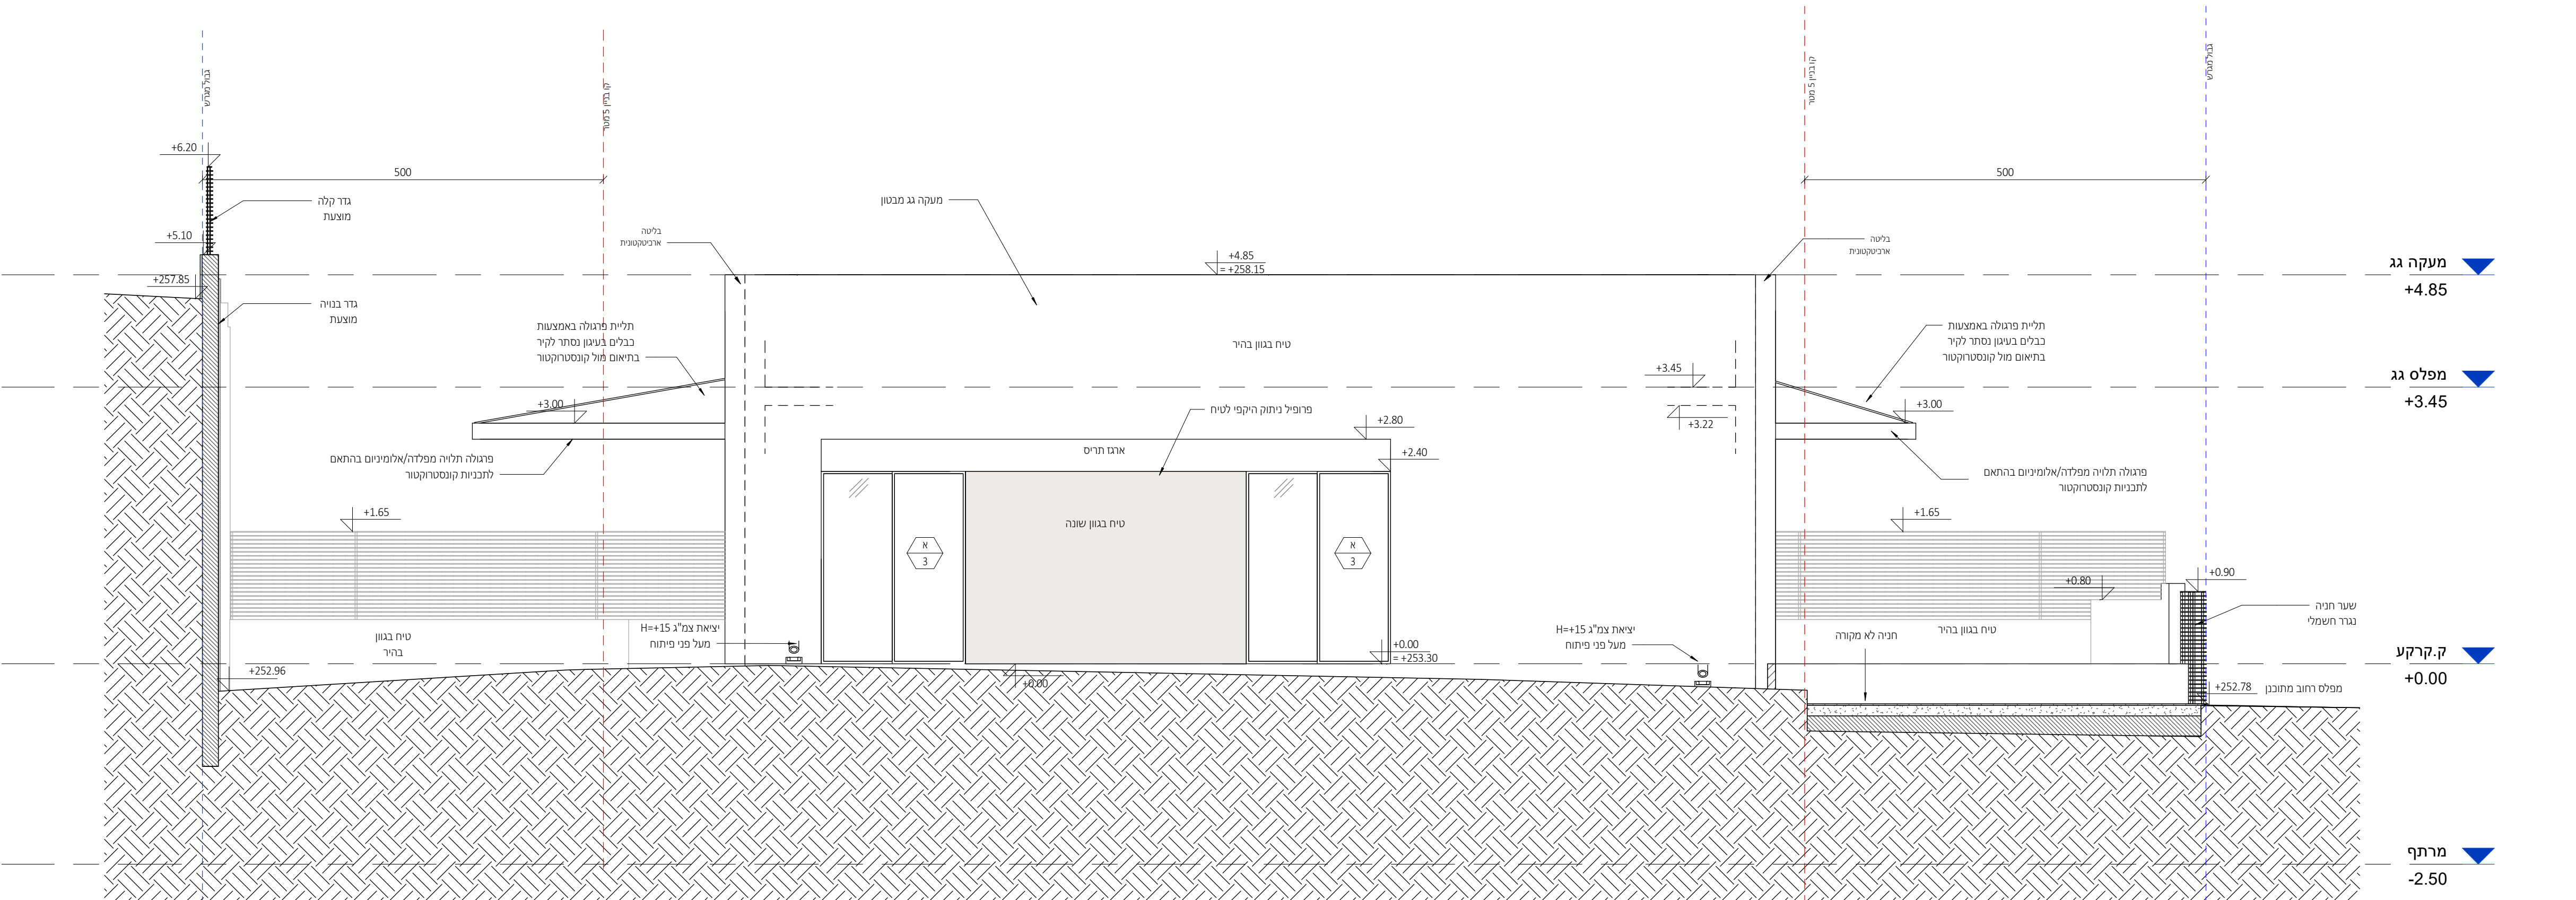

פיתוח נוף עפ"י תוכניות
יועץ נוף ראה פירוט בנפרד

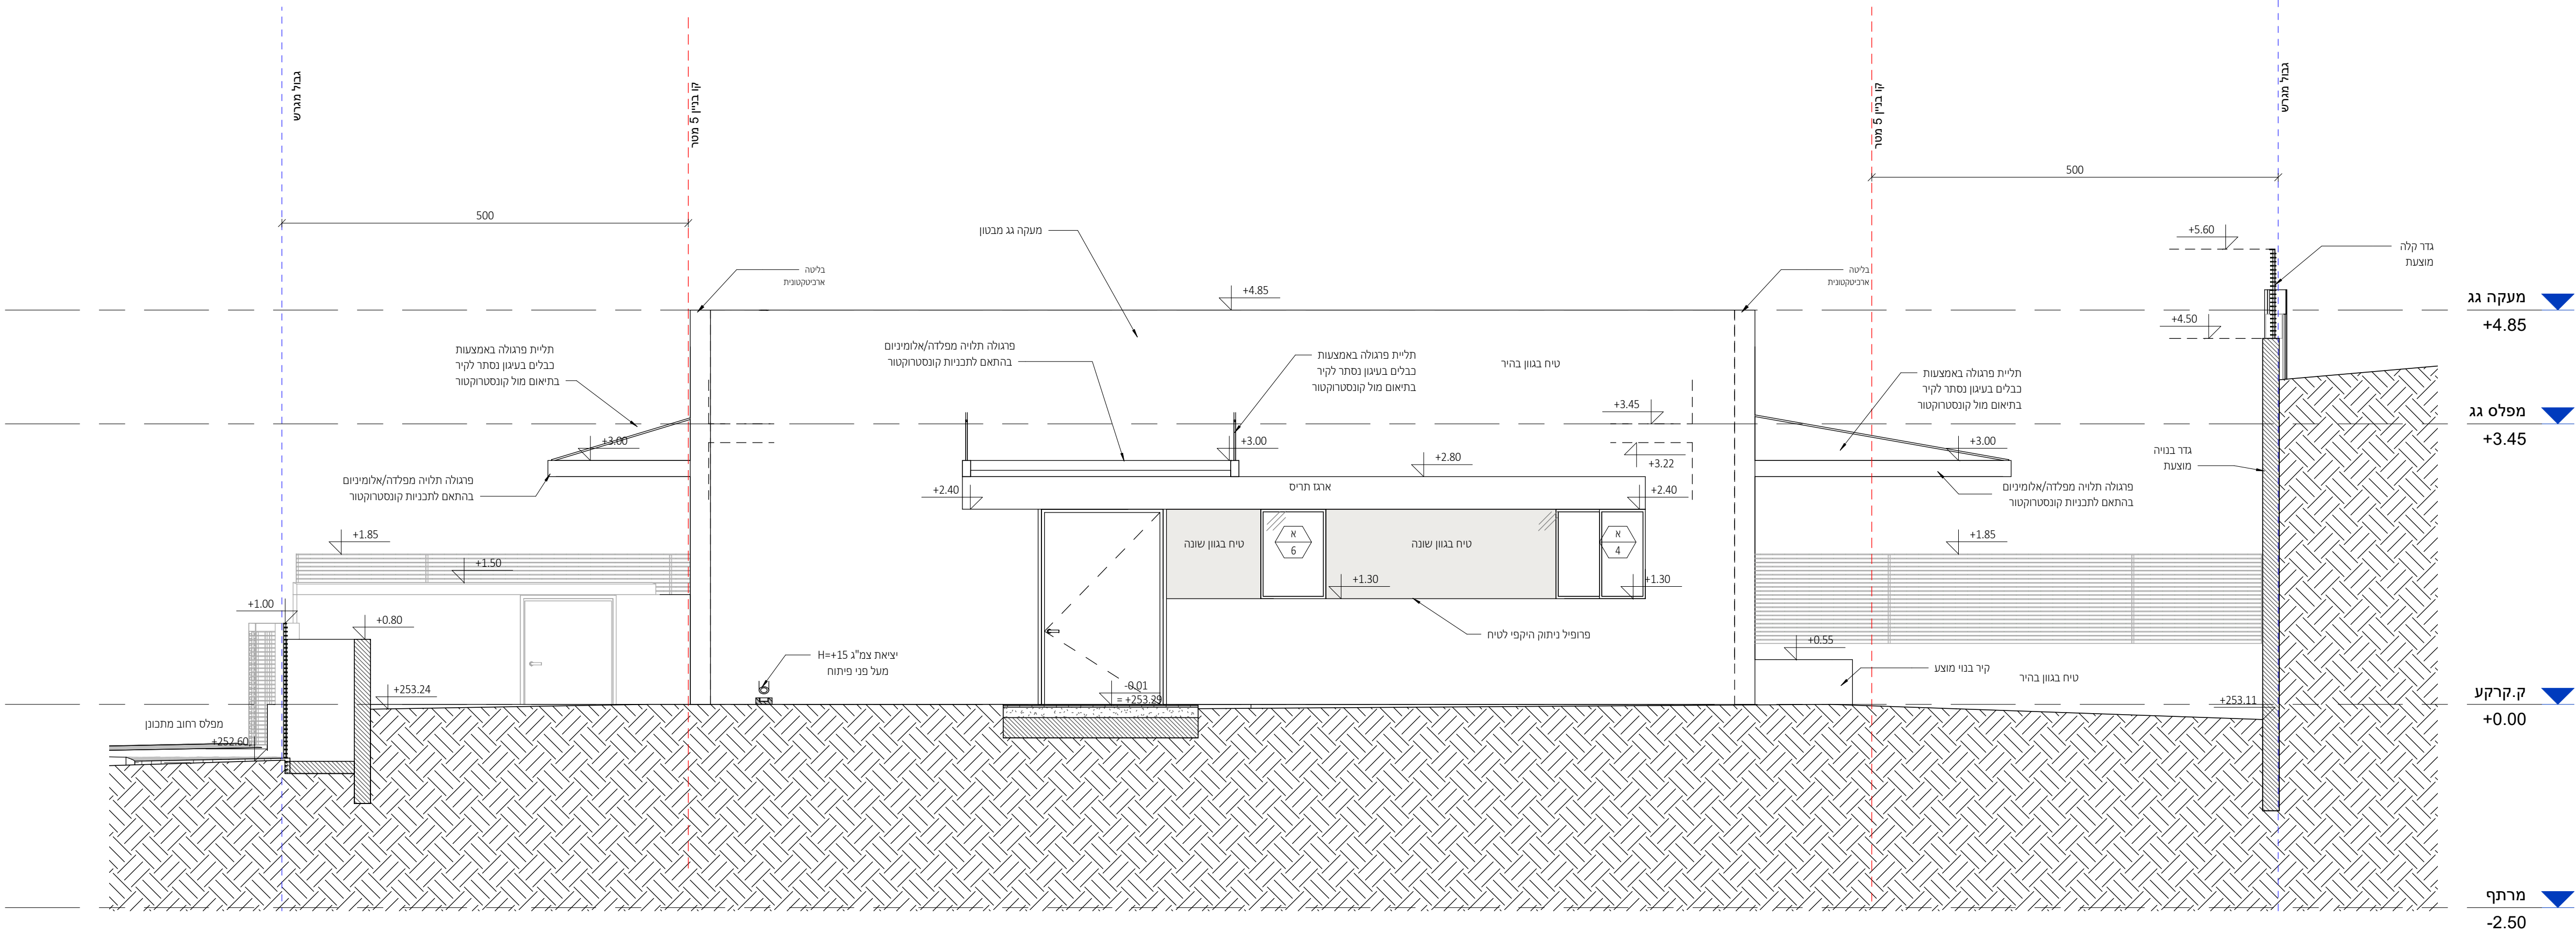

פיתוח נוף עפ"י תוכניות
יועץ נוף ראה פירוט בנפרד

חזית מערבית

1 : 50

פרטי איטום, בידוד וניקוז עפ"י תכניות יועצים ובאחריות הקבלן

מתכונים:

ניהול פרויקט
מהיסוד - בן סולמון
פיקוח
מהיסוד - בן סולמון
קונסטרוקציה
ערן שילר
מיזוג אוויר
אייל ארז מהנדסים ויועצים בע"מ
אינסטלציה
איתן אלמסי
חשמל
איתן בסיס
אלומיניום
נוף
נתי בלוקא
חשמל חכם
חימום תת רצפתי
איטום
צבי טל
אקוסטיקה
מעליות
קרקע וביסוס
דיה הנדסת קרקע וביסוס
רישוי

[illegible][illegible]

אדריכלות

CLIENT NAME:		ה' המסמך:	
PROJECT NAME:		ה' הפרויקט:	
DRAWING NAME:		ה' הגרסה:	
SHEET NUMBER:		ה' מספר גיליון:	
SCALE: As indicated STATUS: למכור		EDITION:  תוספת: 1	
DATE: 22.09.25		תאריך: 22.09.25	

NeumanHaynerArchitects

office@nh-arch.com
www.nh-arch.com


זכויות ייצור / ע"פ הנחיות עו"ד

שינוי עובי מילוי ריצוף מעל תקרת בטון ממ"ד

1 : 10


קרקע +0.00

פיתוח נוף עפ"י תוכניות
יועץ נוף ראה פירוט בנפ

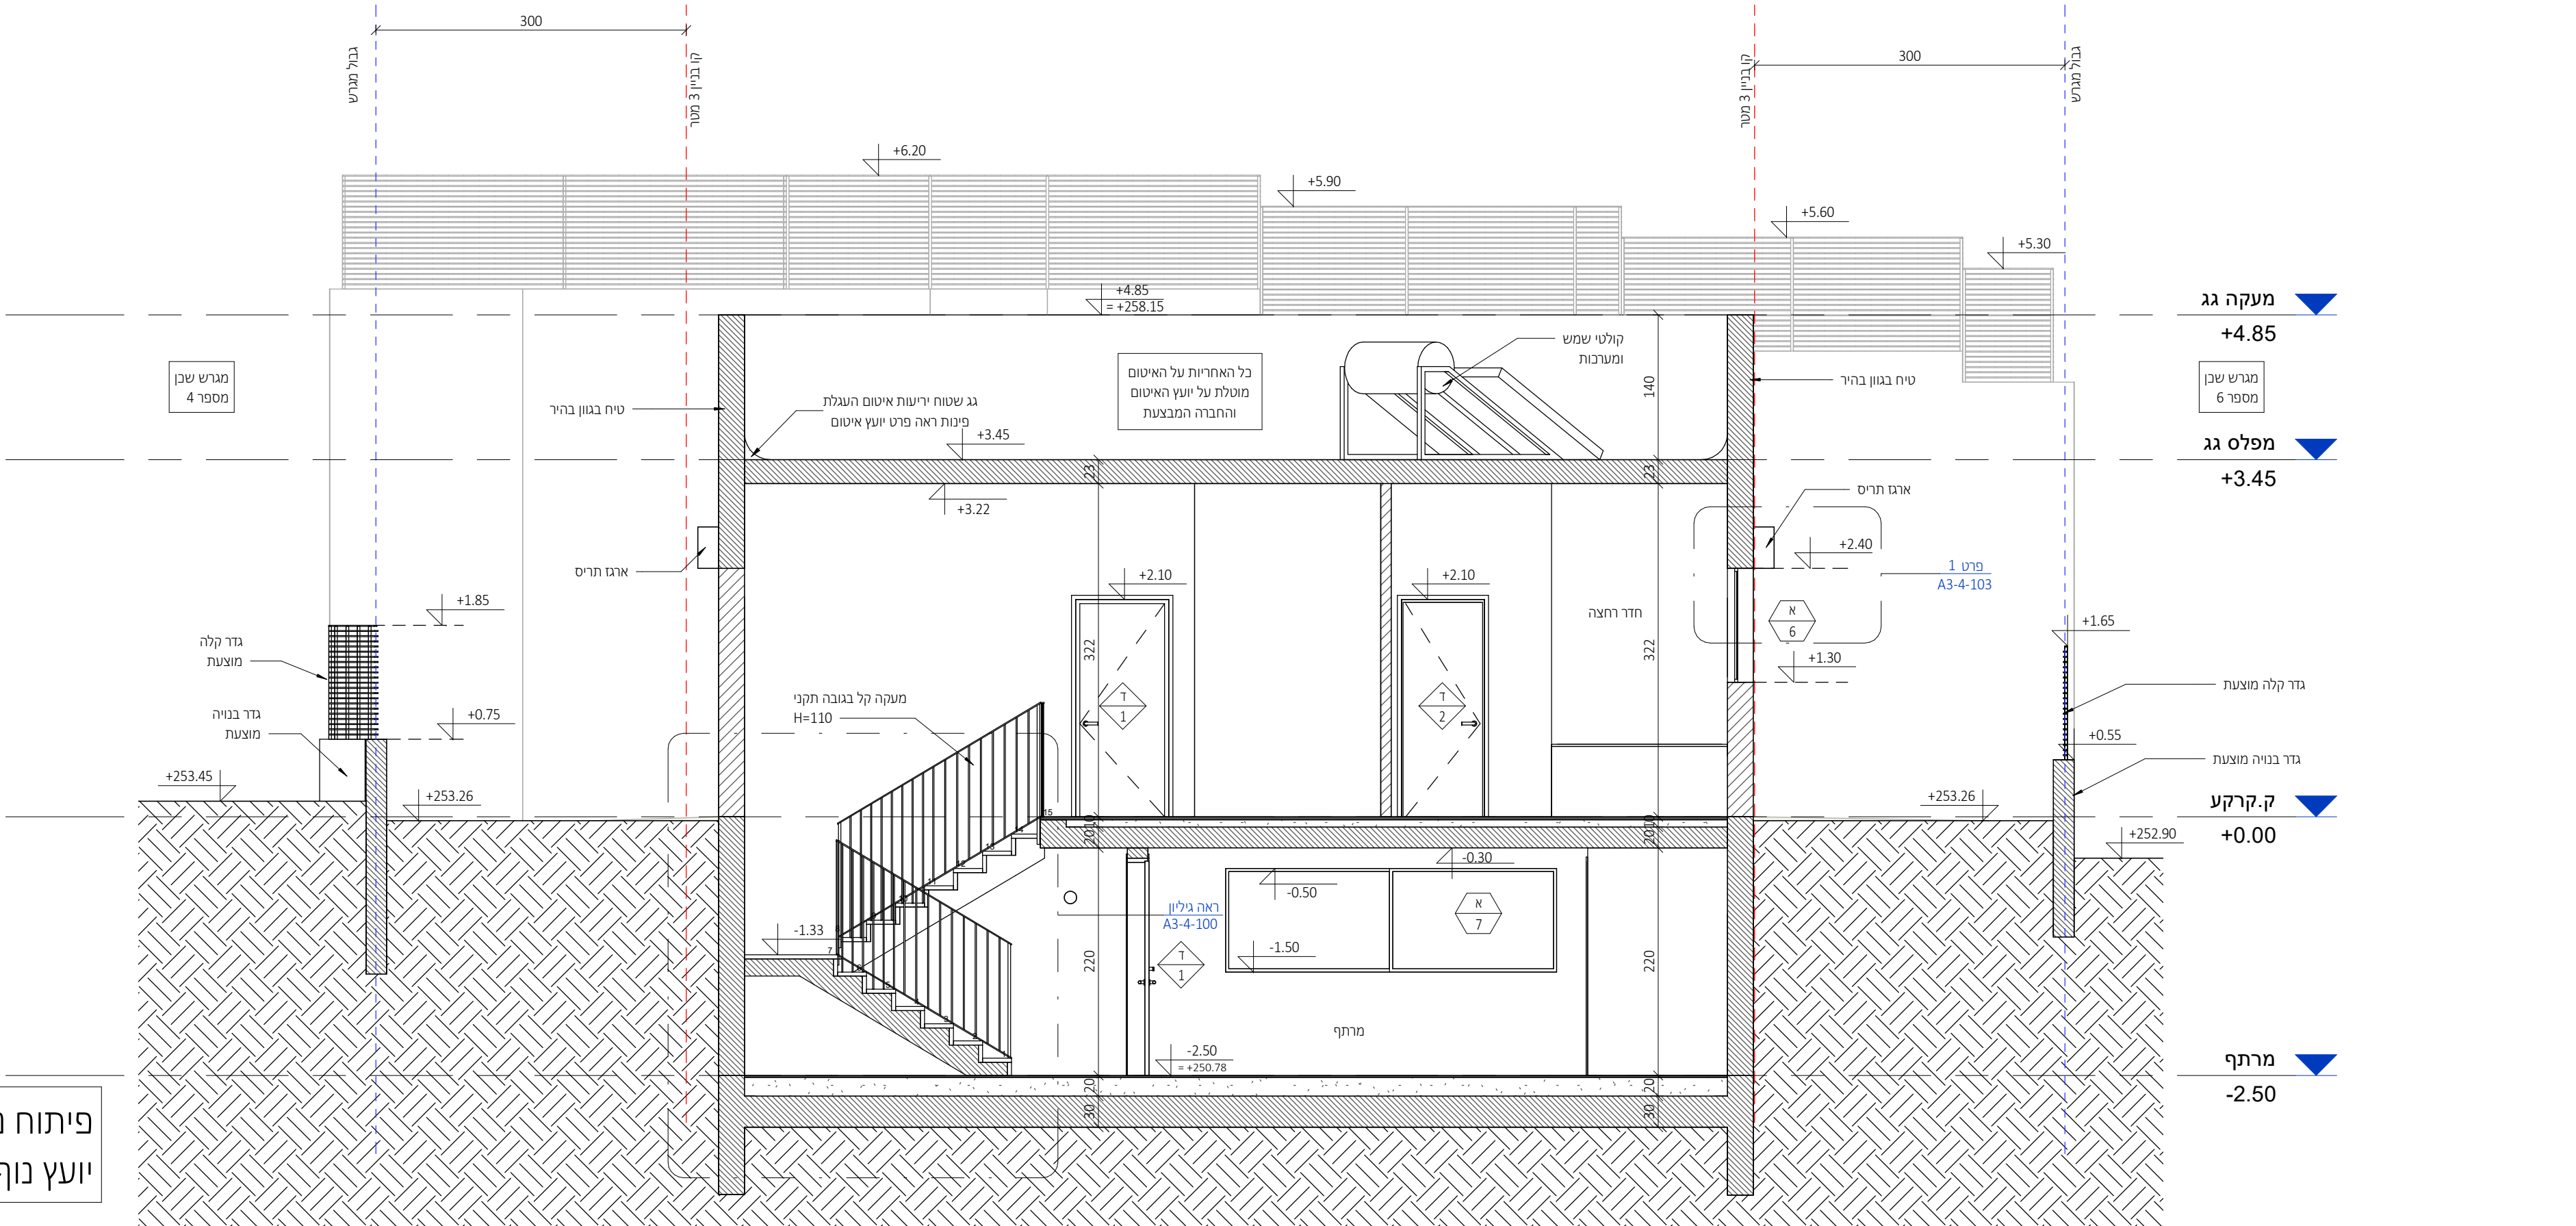

חֲתָךְ א-א

1 : 50

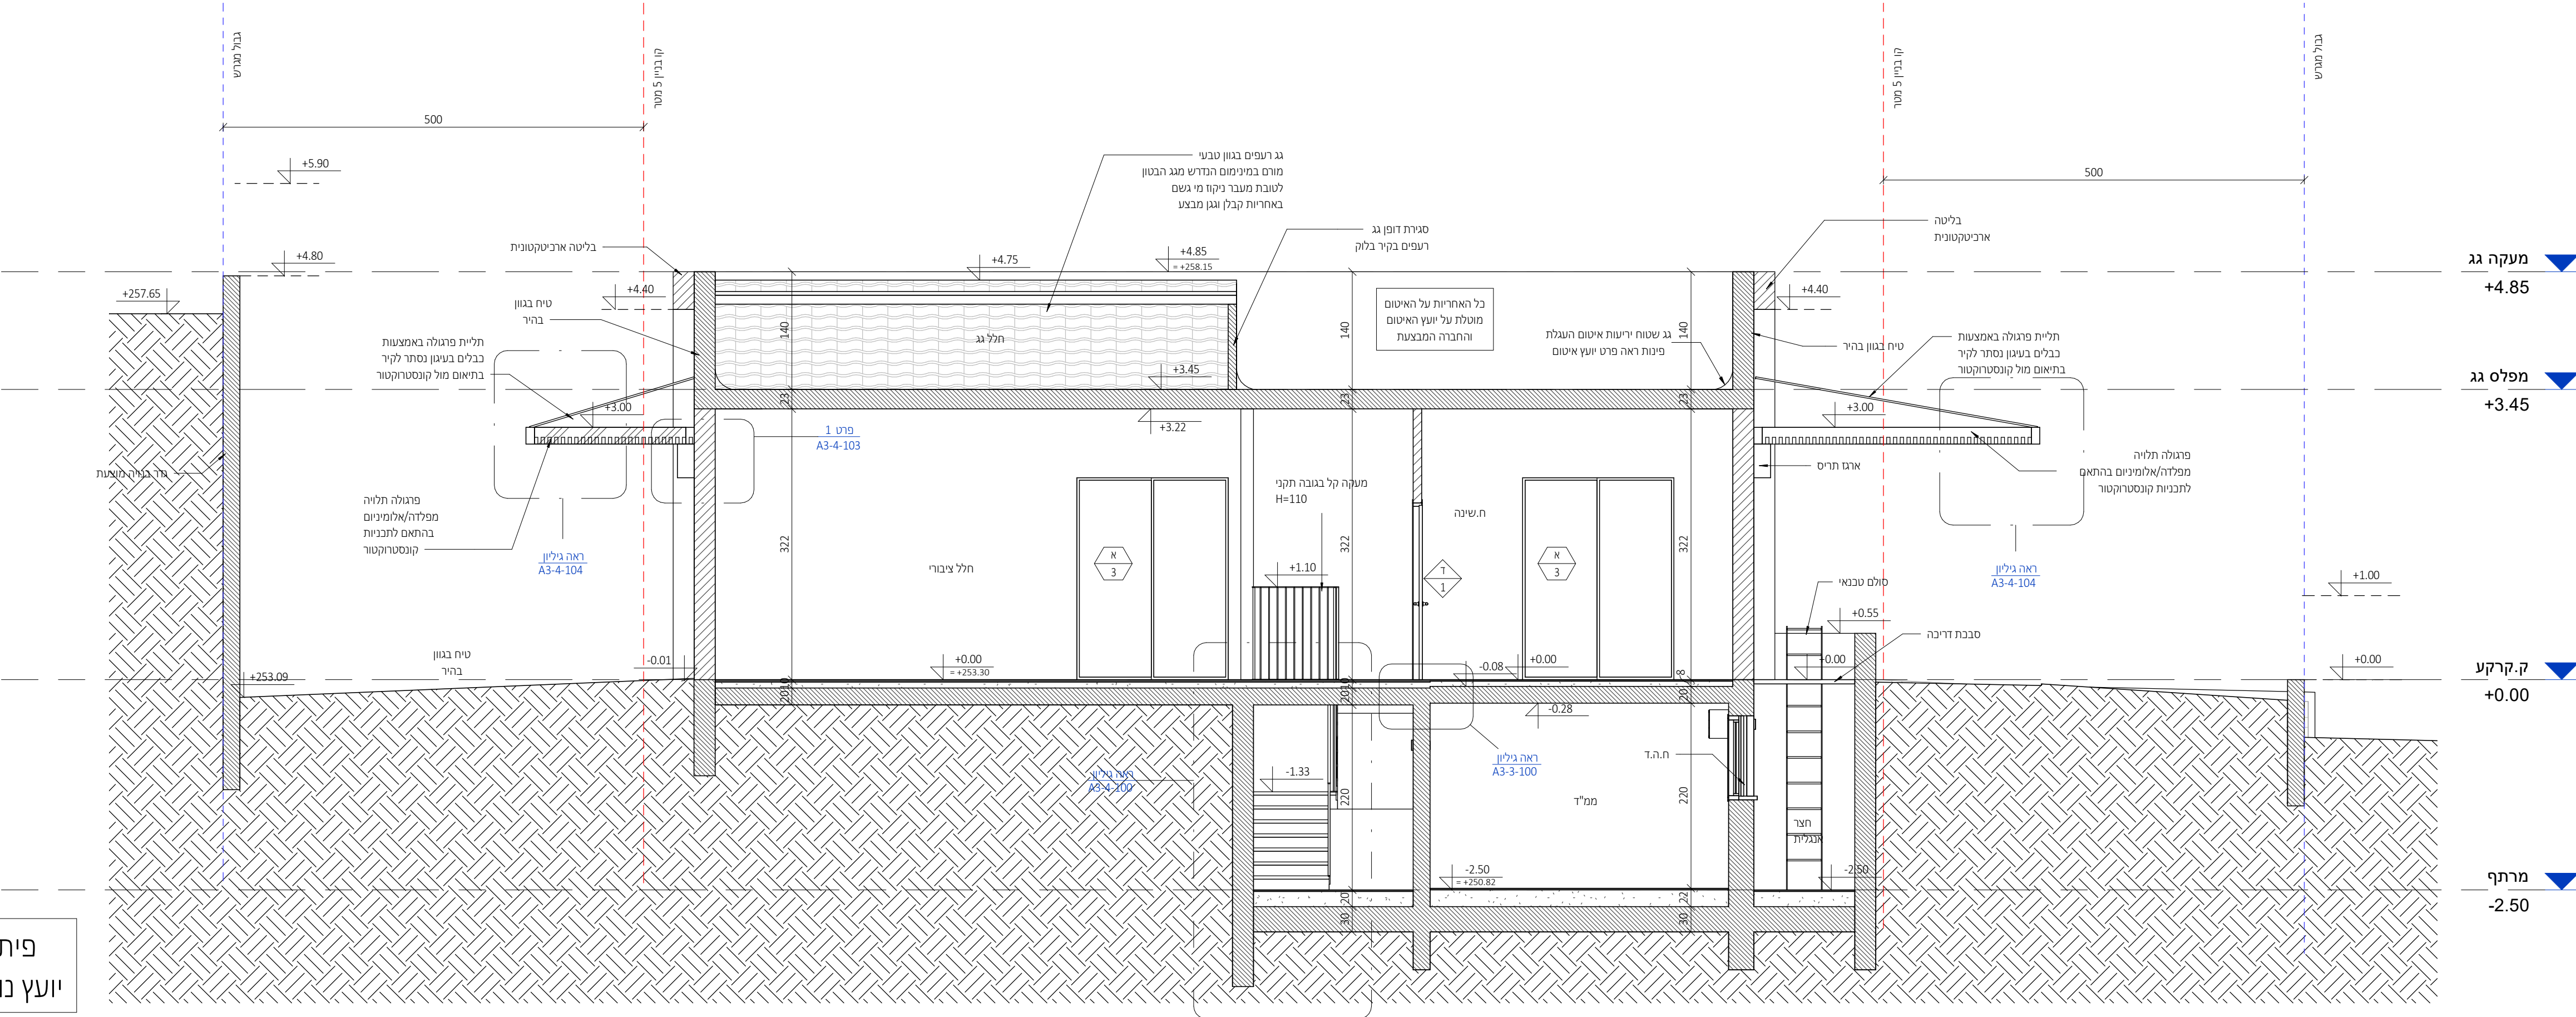

פיתוח נוף עפ"י תוכניות
יועץ נוף ראה פירוט בנפרד

חתך ב-ב

1 : 50

ניהול פרויקט
מהיסוד - בן סולומון
פיקוח
מהיסוד - בן סולומון
קונסטרקציה
ערן שילר
מיזוג אוויר
אייל ארז מהנדסים ויועצים בע"מ
אינסטלציה
איתן אלמסי
חשמל
איתן בסיס
אלומיניום
נוף
נתי בלוקא
חשמל חכם
חימום תת רצפתי
איטום
צבי טל
אקוסטיקה
מעליות
קרקע וביסוס
דיה הנדסת קרקע וביסוס
רישוי

[illegible]

עמוד בסור קיר בסור בלוק

[illegible]

CLIENT NAME:		המחיר:	
PROJECT NAME:		הפרויקט:	
DRAWING NAME:		שם התוכנית:	
SHEET NUMBER:		מספר העמוד:	
SCALE:		מקנה מידה:	
STATUS:		סטוס:	
DATE:		תאריך:	

קבוצת רכישה נופיה

נופיה - מגרש 5

גליון מדרגות

A3-4-100


As indicated

למכר


22.09.25

מדרגה:


דריס ע"י:

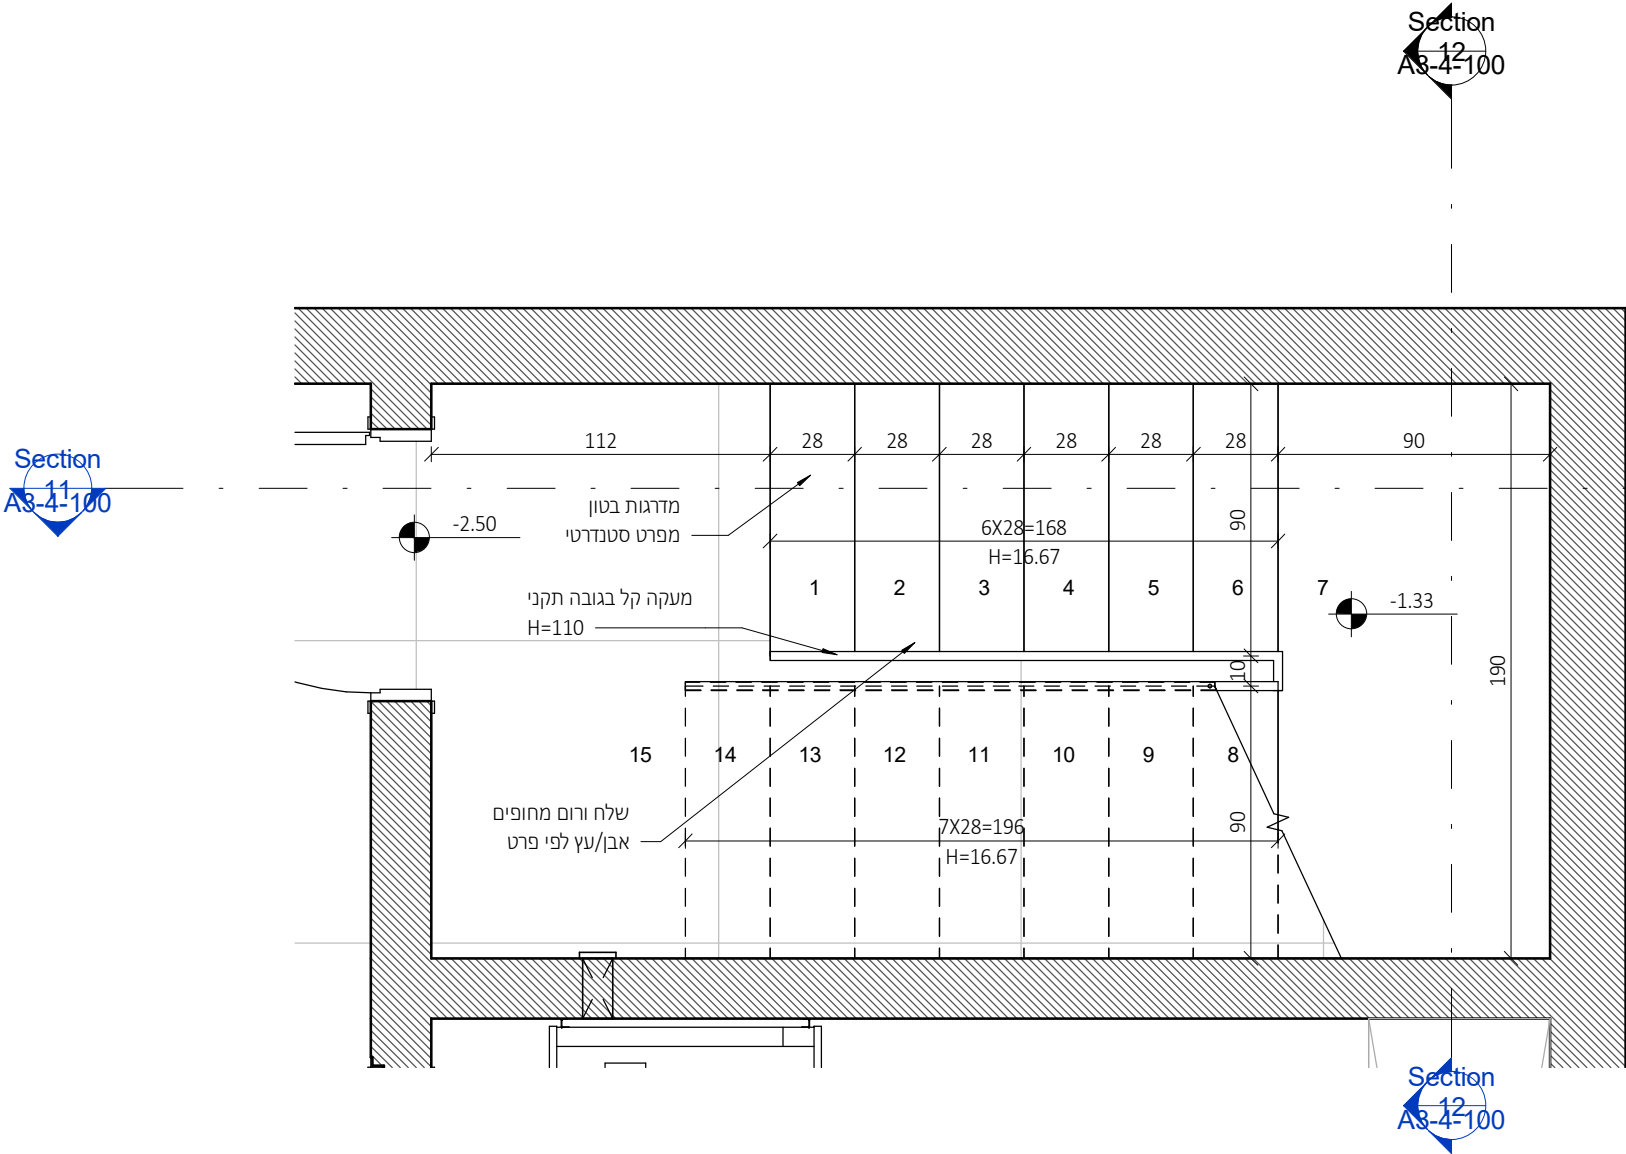

1 : 25

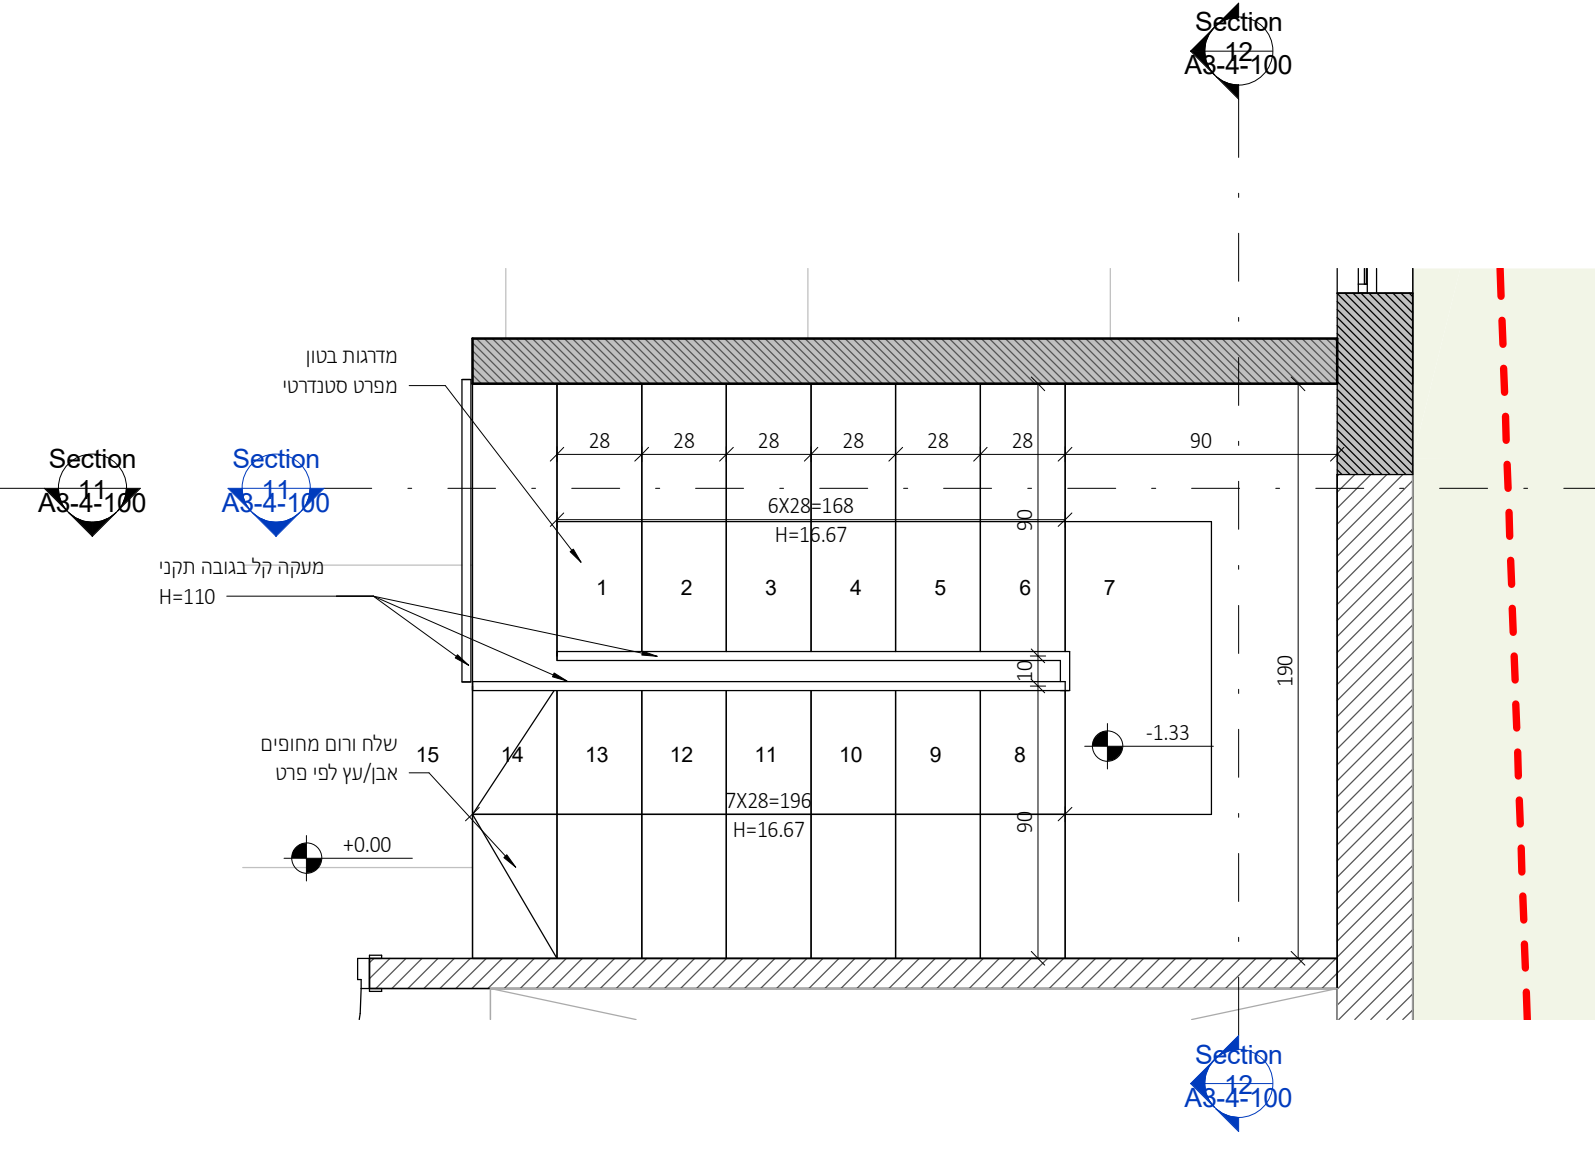

1 : 25

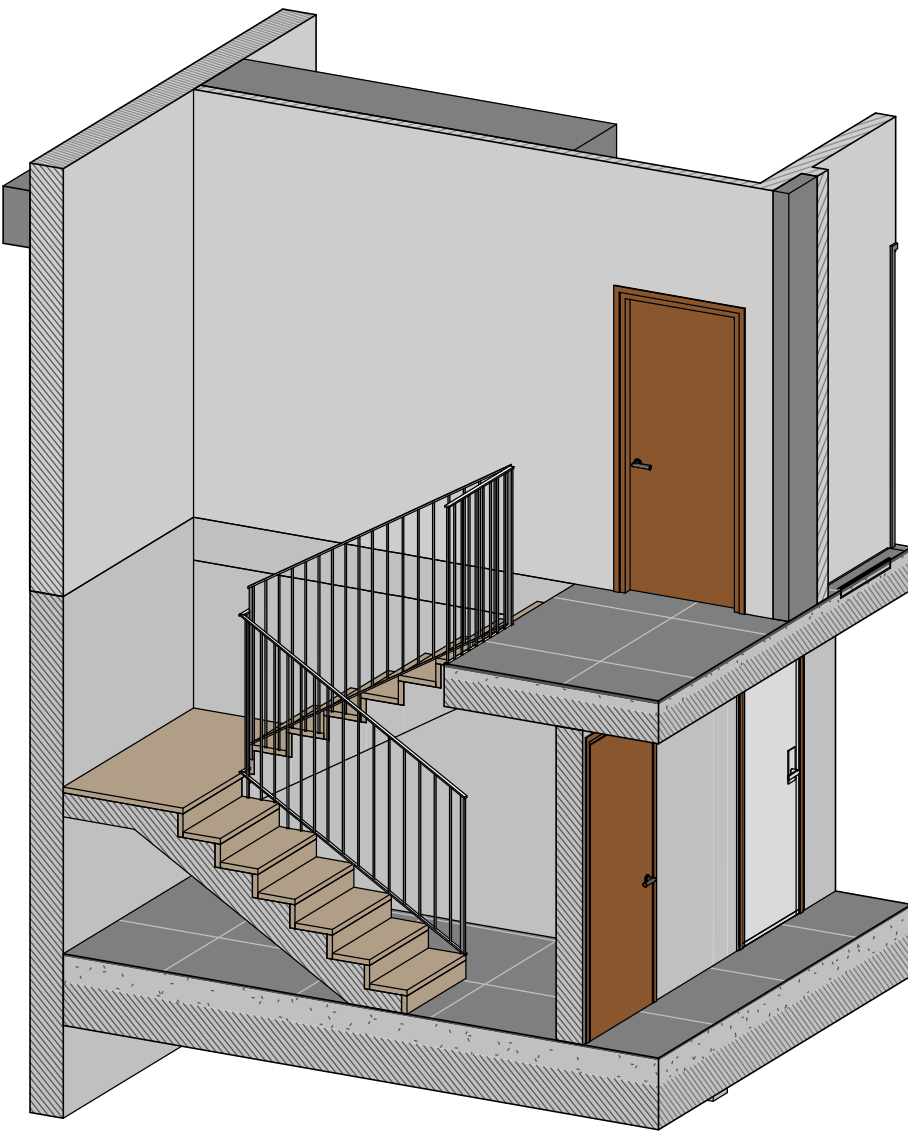


דגם נבחר

מדרגות סטנדרטיות - מפרט סטנדרטי


על הקבלן לשלוח S.D לאישור אדריכל

יש לבצע התאמה לפרט לאחר בחירת חיפוי המדרגות*

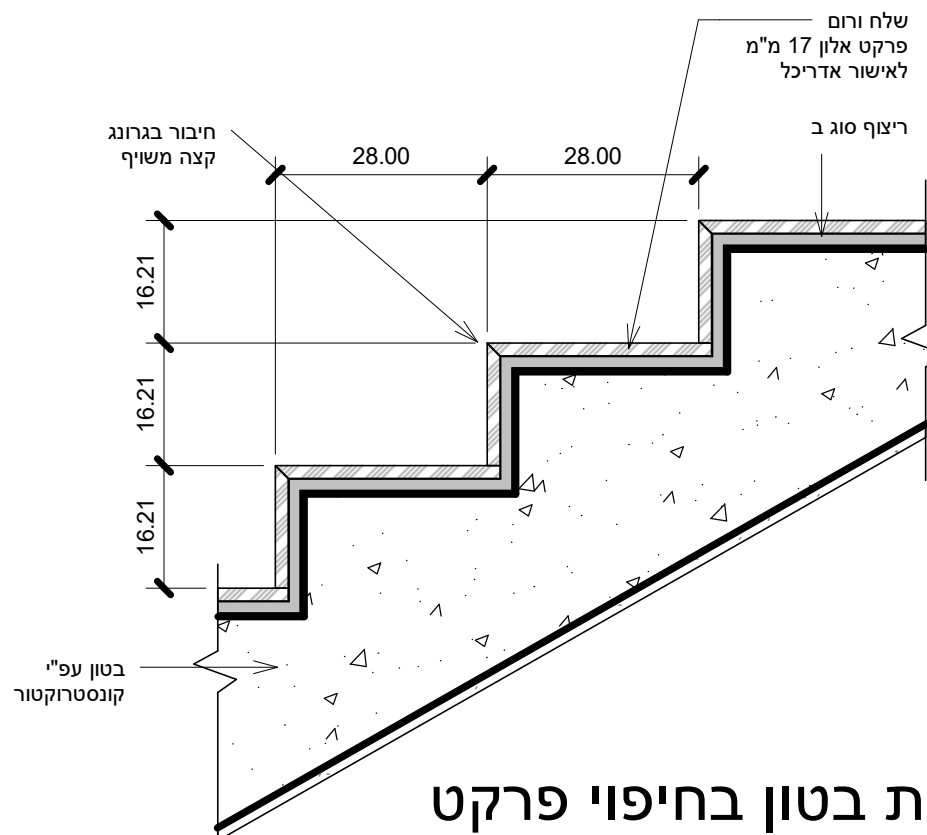

פרט מדרגות בטון בחיפוי פרקט

1 : 10

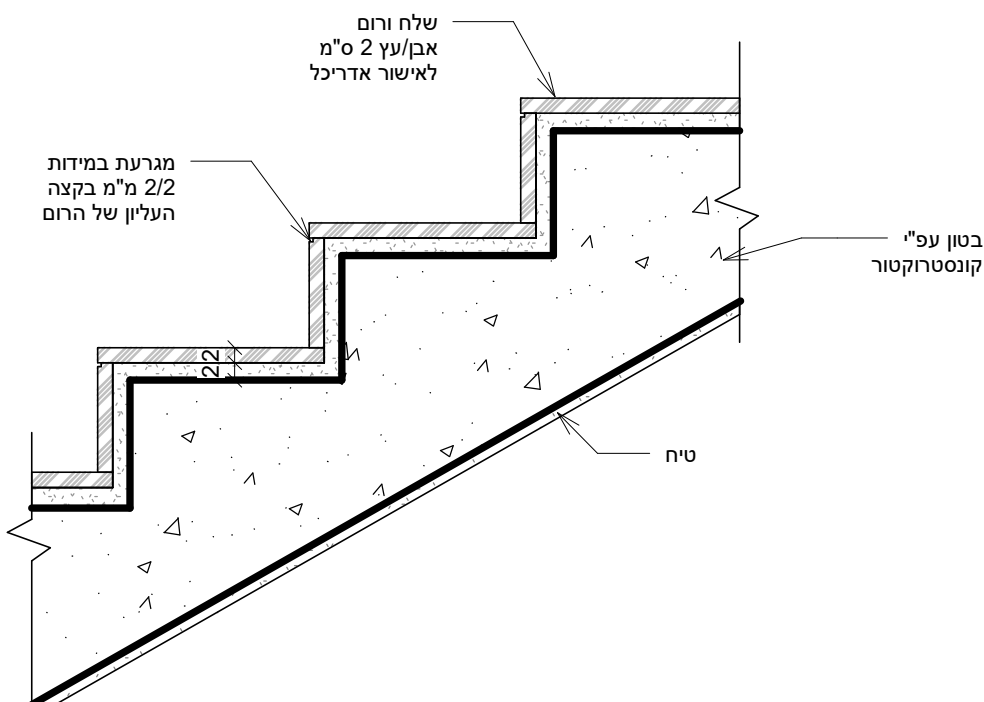


פרט מדרגות פנים - עץ/אבן


1 : 10




תמונה להמחשה בלבד

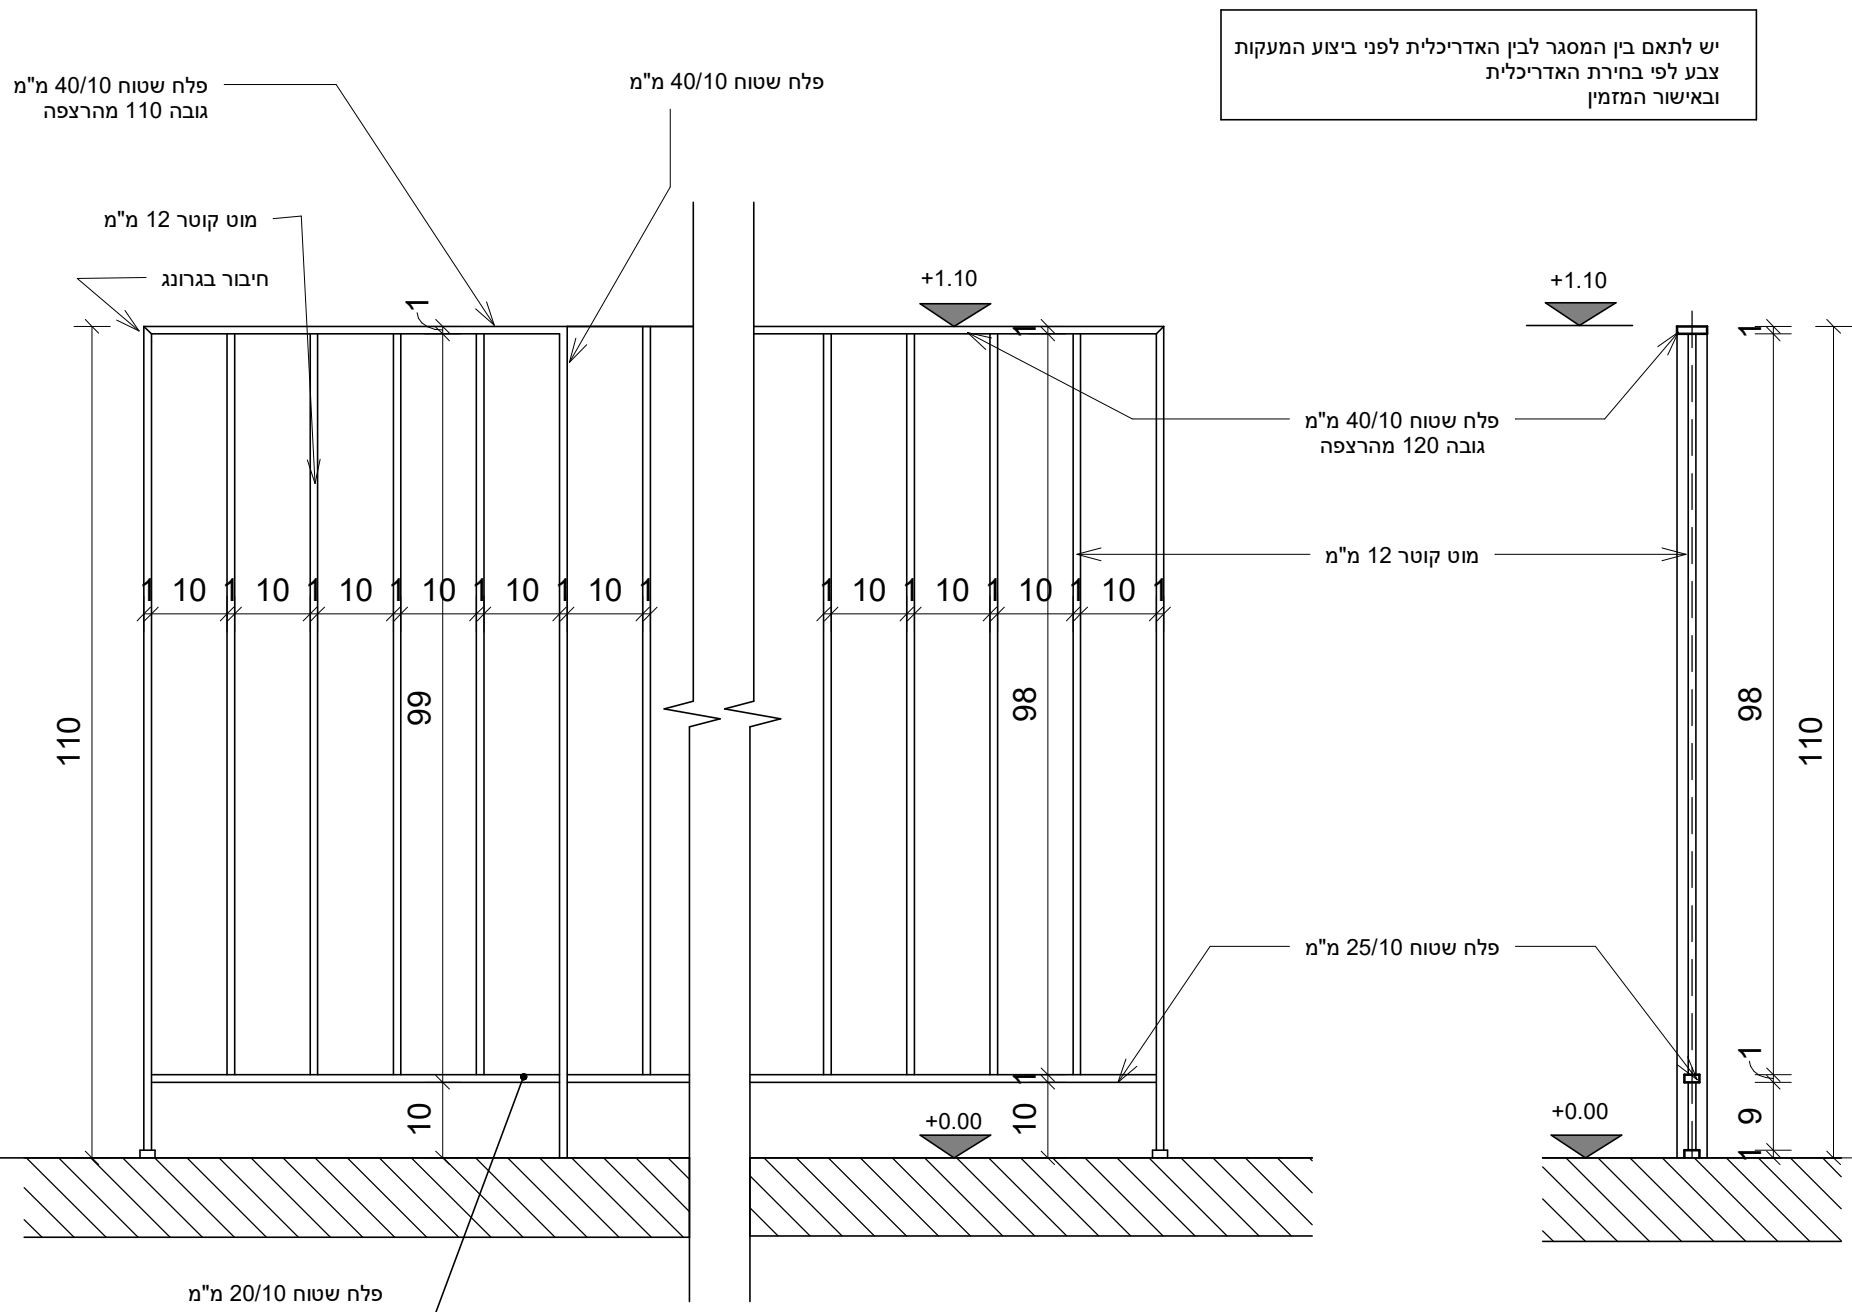

1 : 10

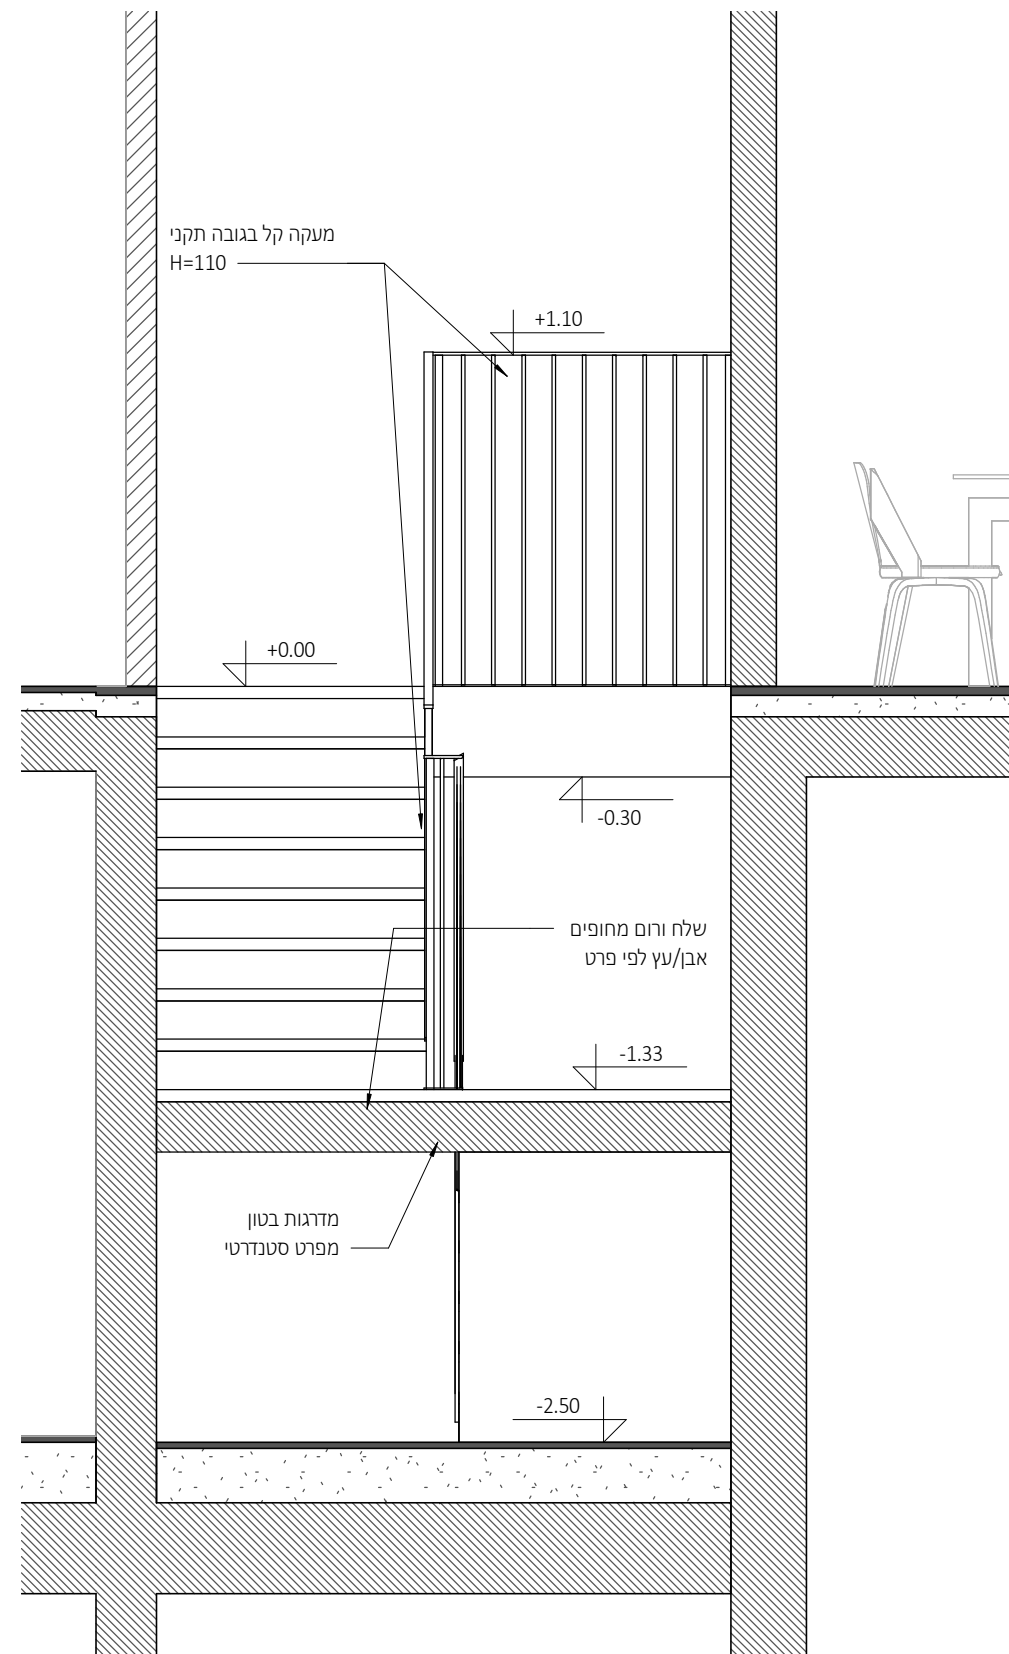

1 : 25

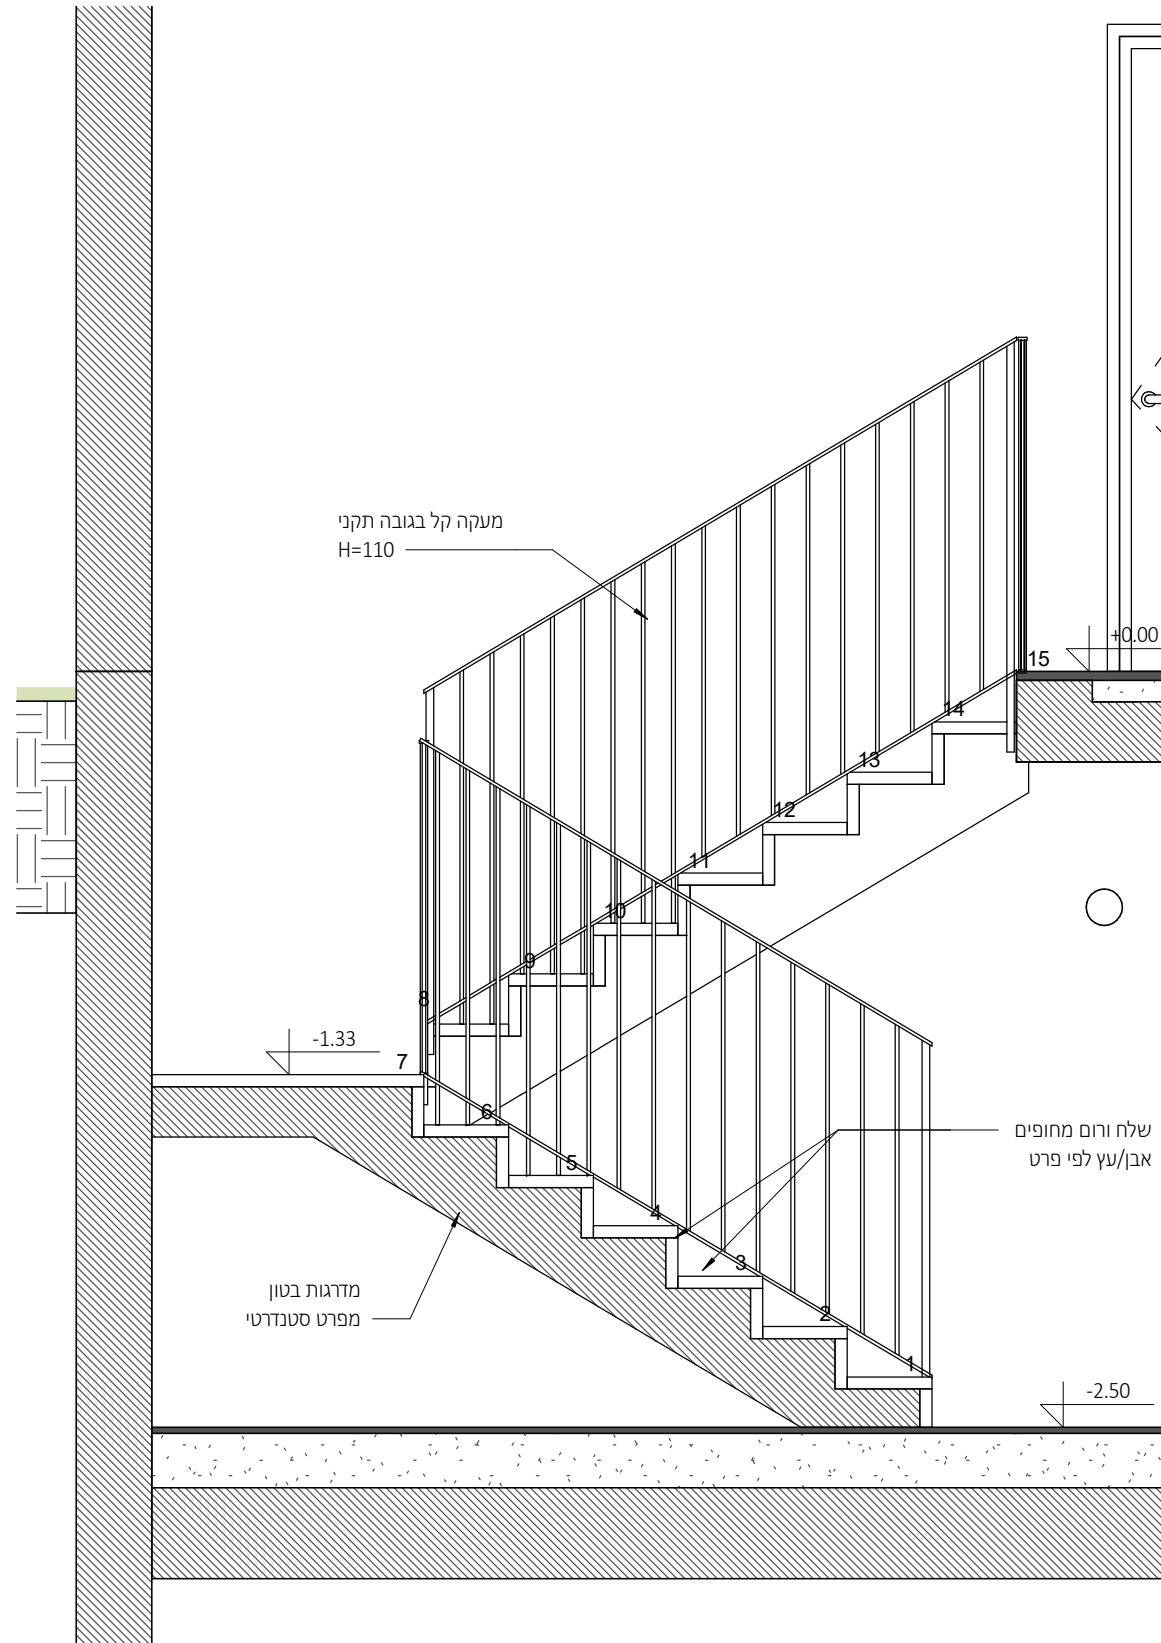

1 : 25

ניהול פרויקט
מהיסוד - בן סולומון
פיקוח
מהיסוד - בן סולומון
קונסטרוקציה
ערן שילר
מיזוג אוויר
אייל ארז מהנדסים ויועצים בע"מ
אינסטלציה
איתן אלמסי
חשמל
איתן בסיס
אלומיניום
נוף
נתי בלוקא
חשמל חכם
חימום תת רצפתי
איטום
צבי טל
אקוסטיקה
מעליות
קרקע וביסוס
דיה הנדסת קרקע וביסוס
רישוי

[illegible]

עמוד בטון קיר בטון דבלוק

[illegible]


CLIENT NAME:		ה' המסמך:	
PROJECT NAME:		ה' הפרויקט:	
קבוצת רכישה נופיה			
נופיה - מגרש 5			
DRAWING NAME:		ה' הגליון:	
פרטים			
SHEET NUMBER:		ה' הפורמט:	
A3-4-103			
CALCULATION:	ה' קנה מידה:	EDITION:	ה' הדפוס:
As indicated	סטטוס		ה' הדפוס:
TATUS:	למכר		ה' הדפוס:
DATE:	22.09.25	ה' הדפוס:	




NeumanHaynerArchitects

יומן חייגר אדריכלים
 חורר ההדריס 2, בית חירות
 09-9545842 זל

office@nh-arch.com
 www.nh-arch.com


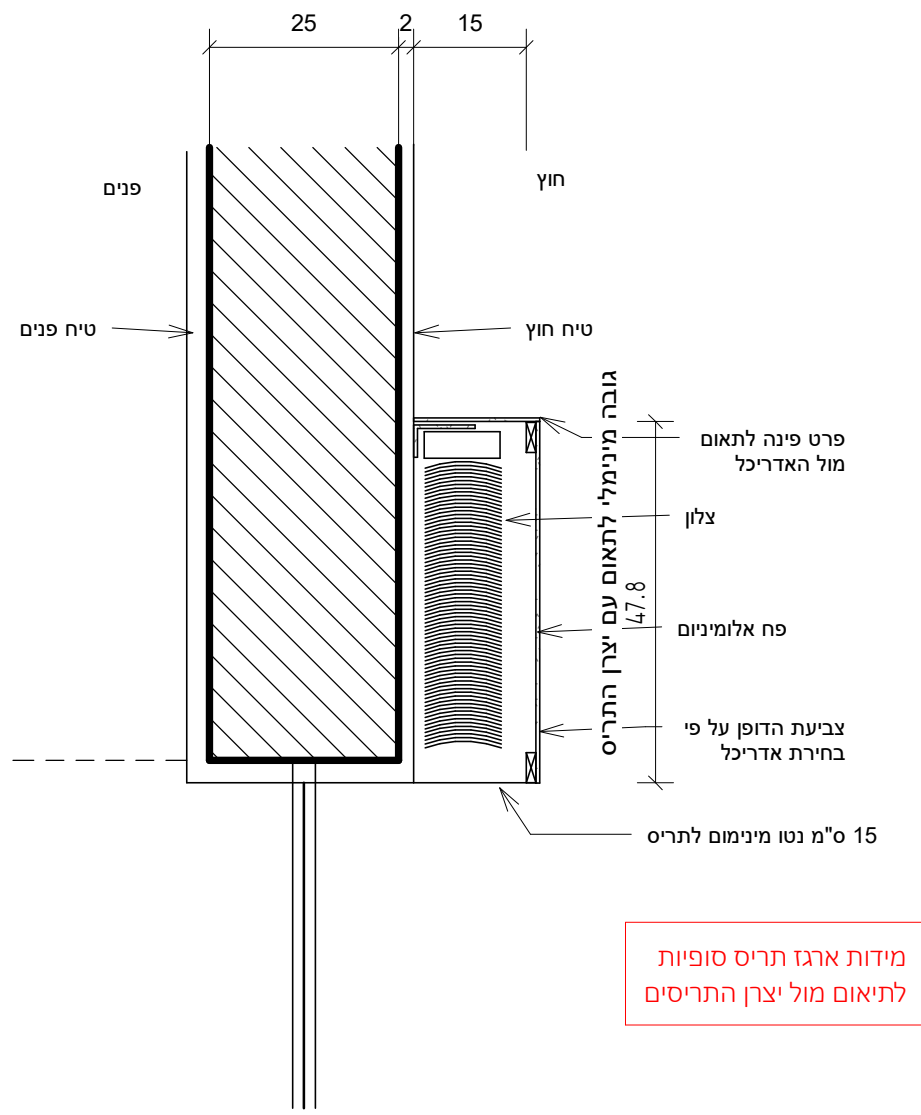


פרט 1 - כיס צלון חיצוני

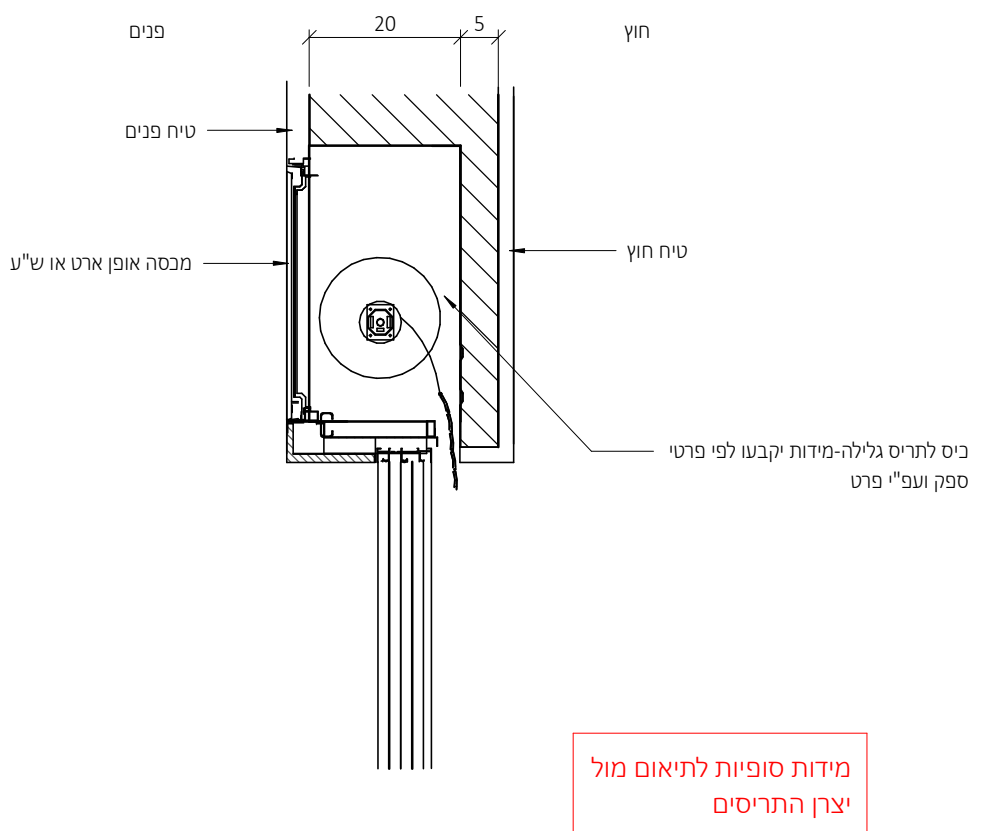


פרט 2 - תריס גלילה

1 : 10

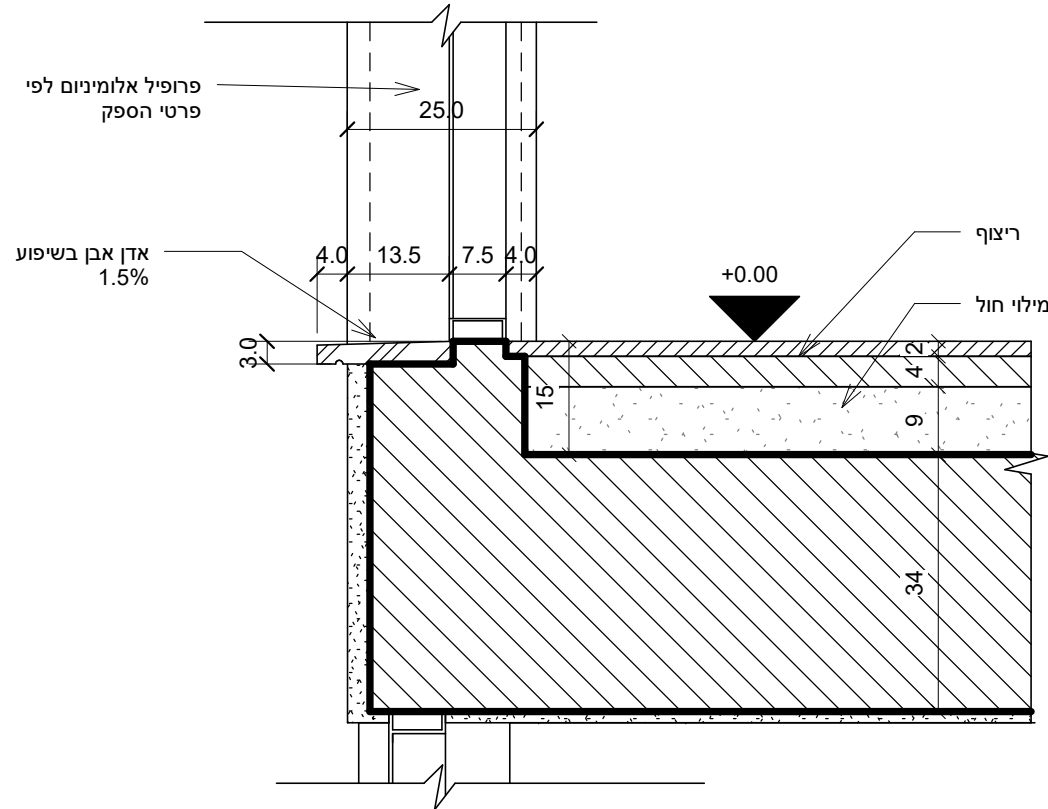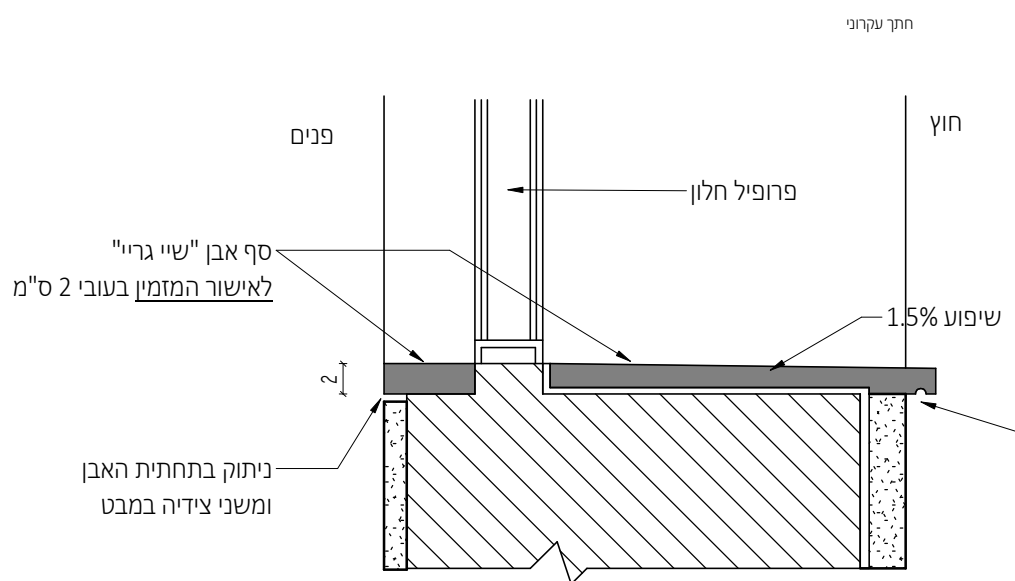
פרט 3 - מפגש חלון ורצפה
1 : 10

פרט 4 - חלון - פרט טיפוס י - סף חלון

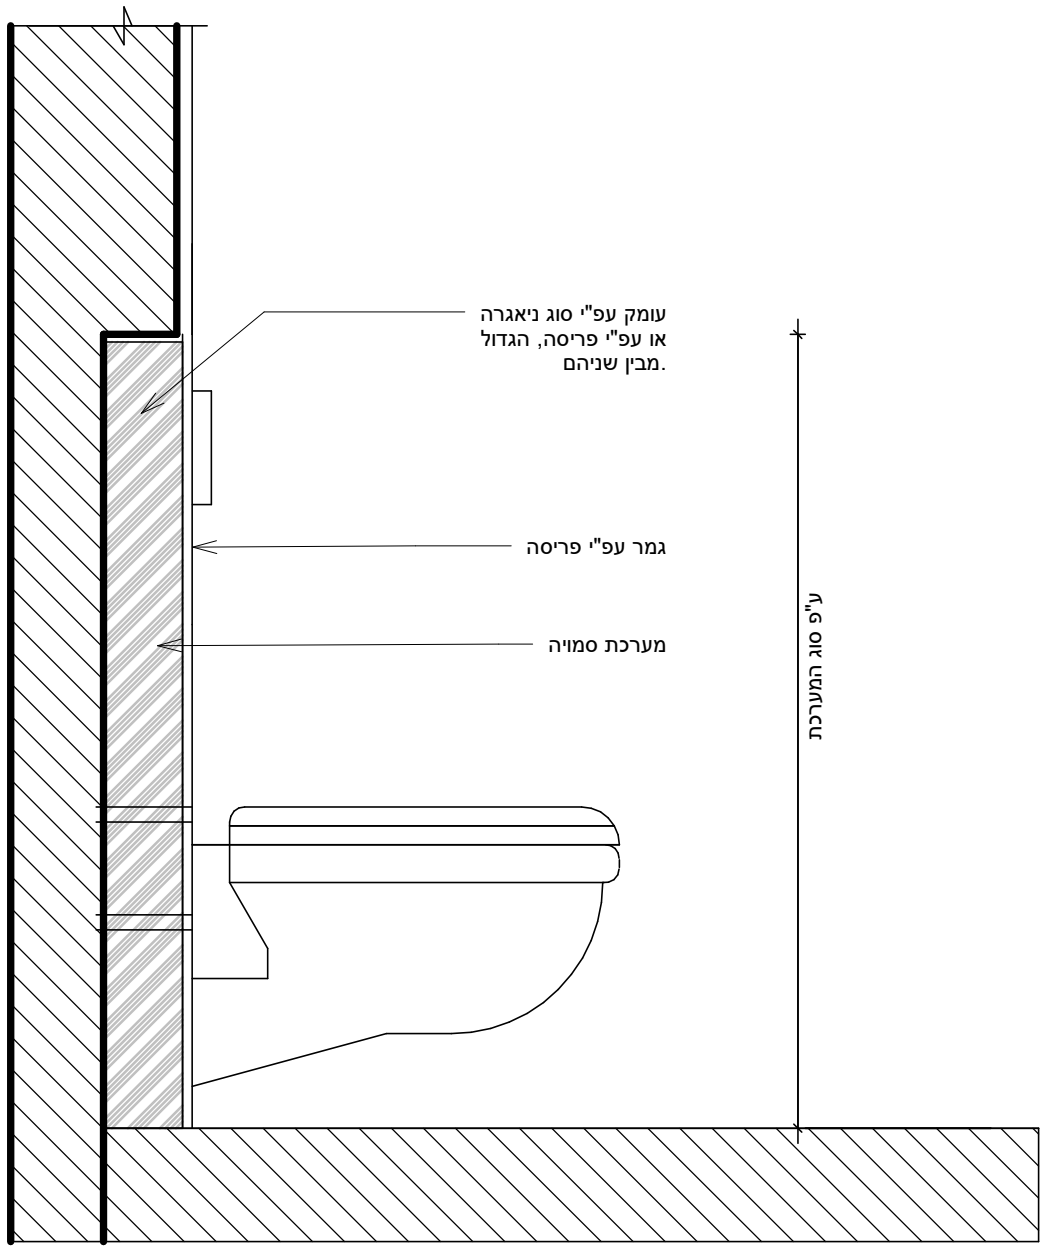

פרט 5 - אסלה תלויה בקיר 20

1 : 10

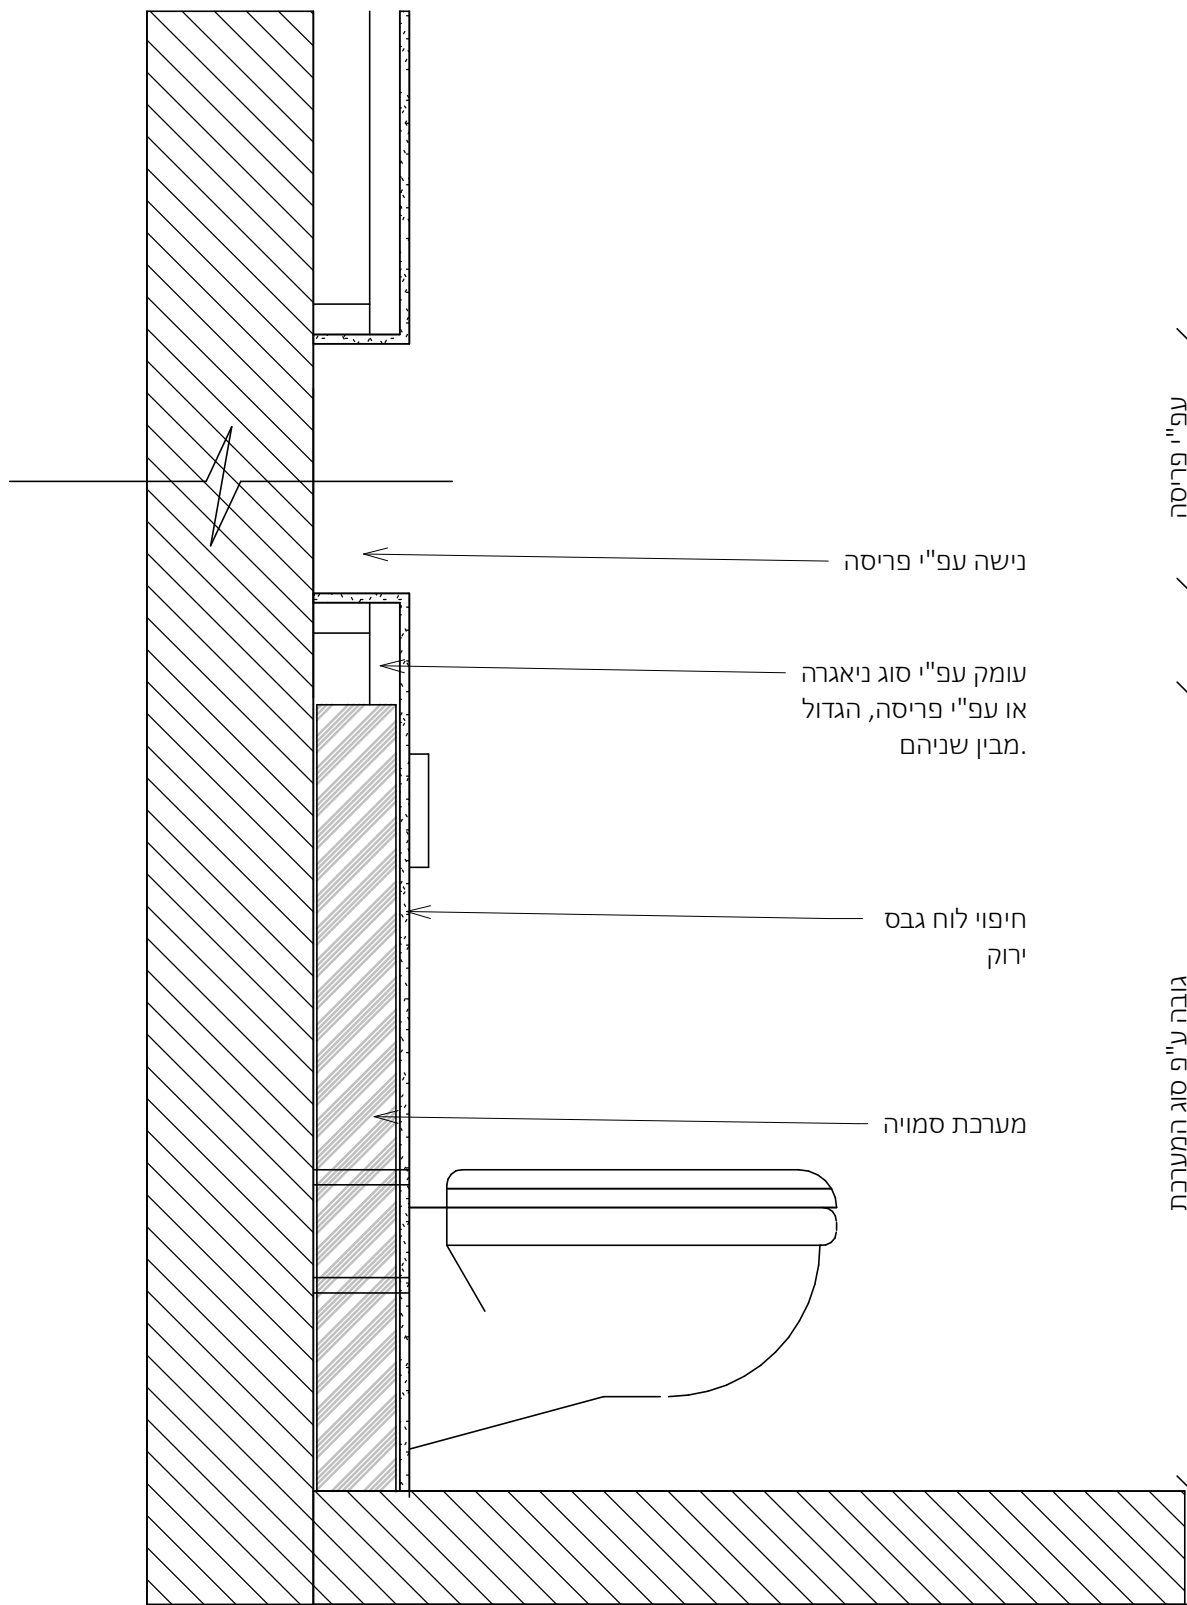

פרט 6 -אסלה תלויה מנגנון סמוי בעיבוי גבס

יש לעבוד במקביל לפרטים שיספק
מעצב הפנים (במידה וקיים במגרש זה)
המאושרות על ידי האדריכל.

פרטי האיטום באחריות יועץ האיטום
ראה חוברת פרטי איטום מצורפת



להמשך תיאום

פרגולת אלומיניום




תמונה להמחשה בלבד

להמשך תיאום

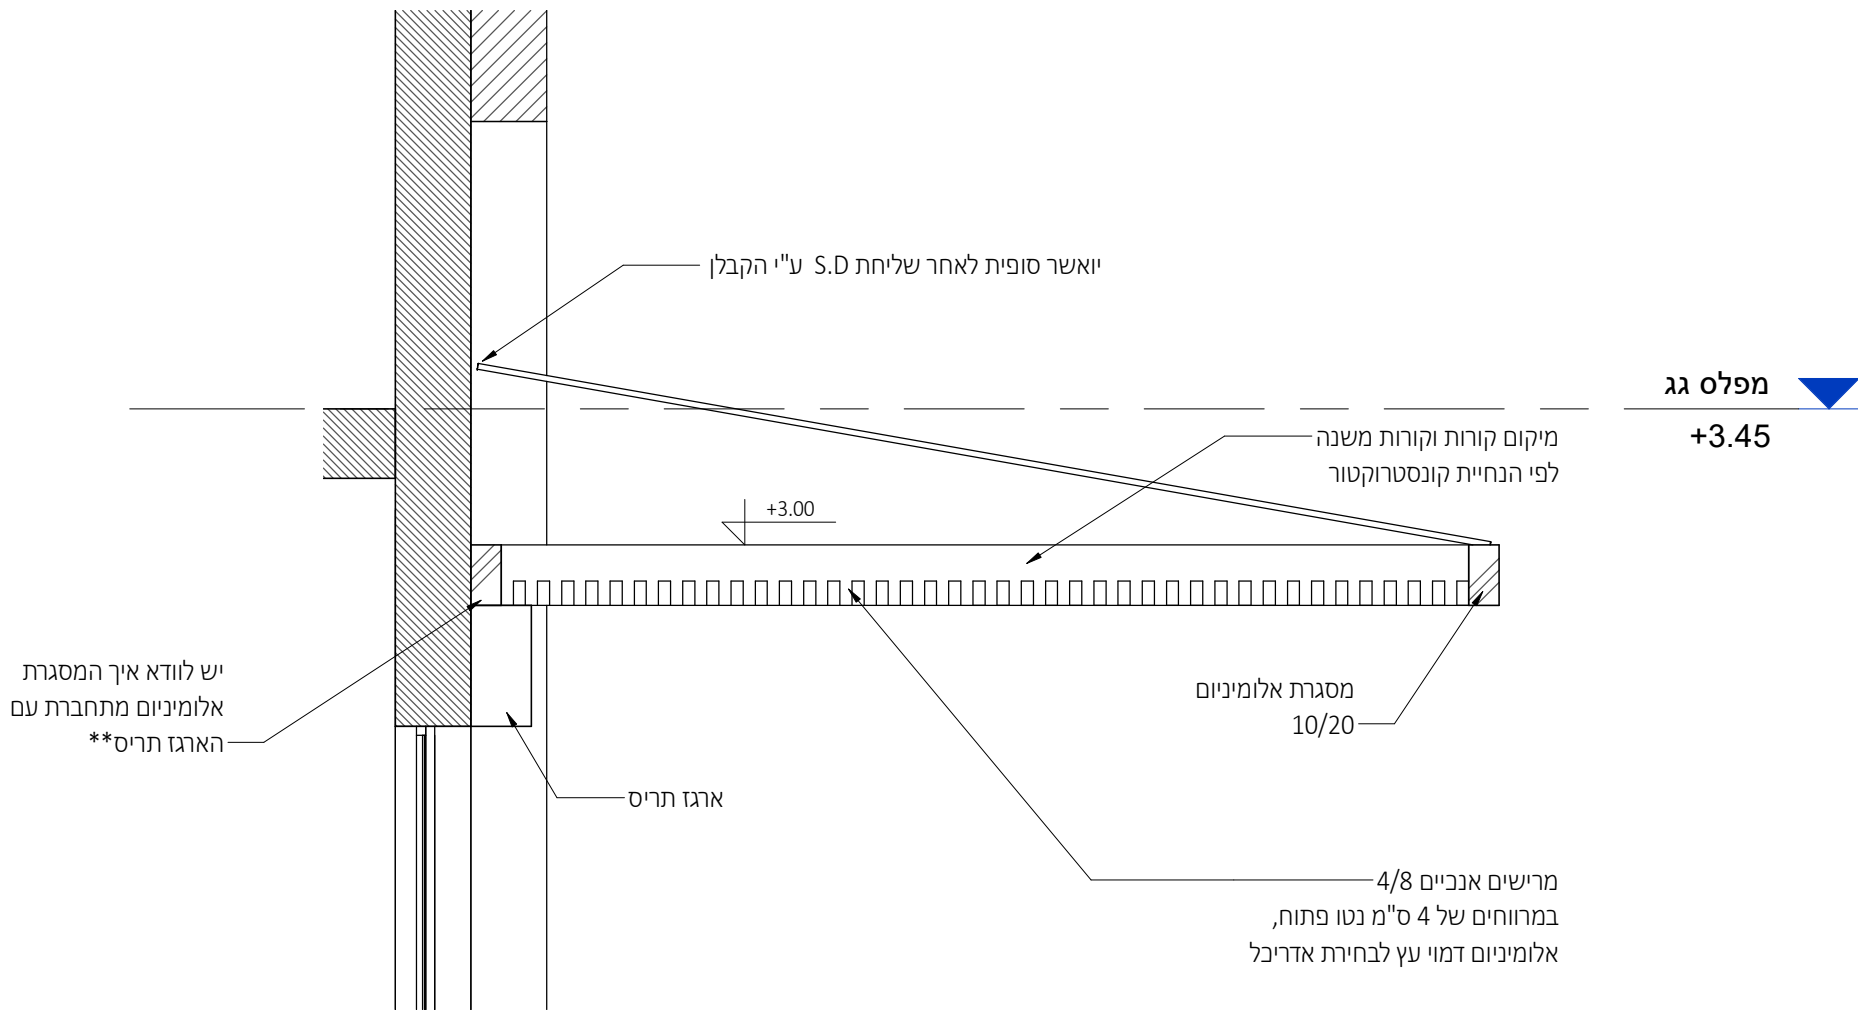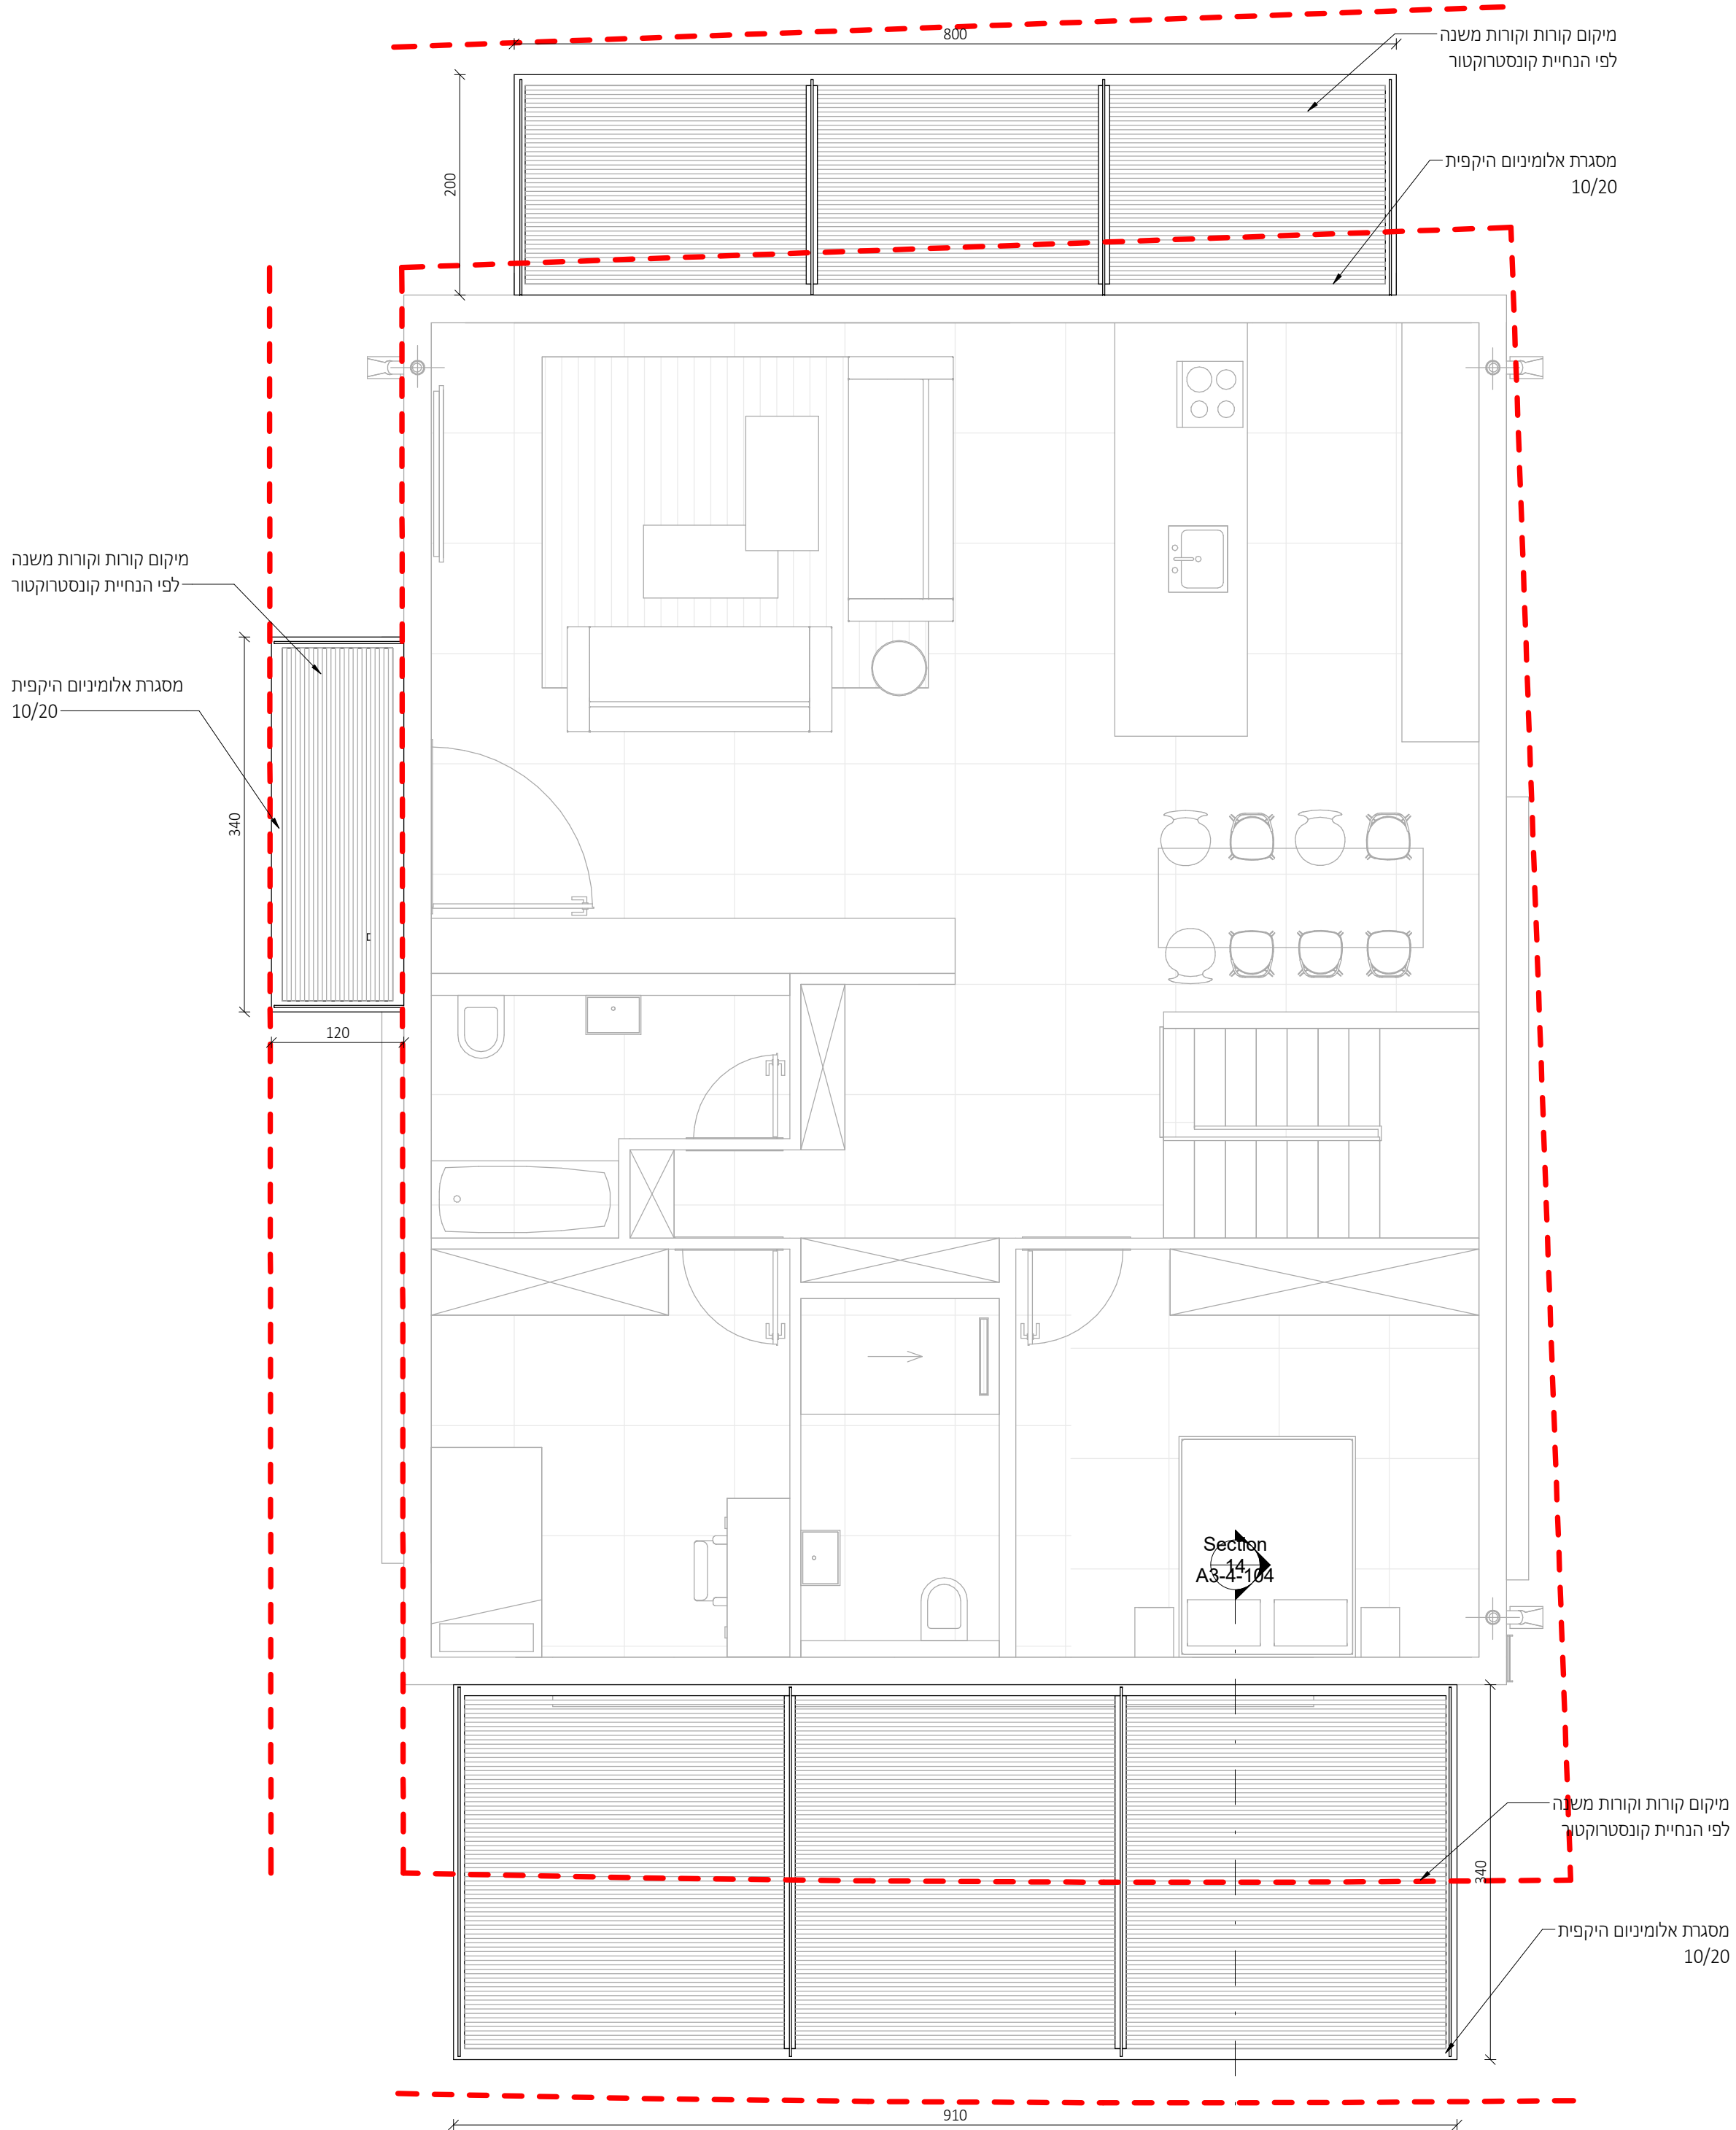


Section 14

1 : 25

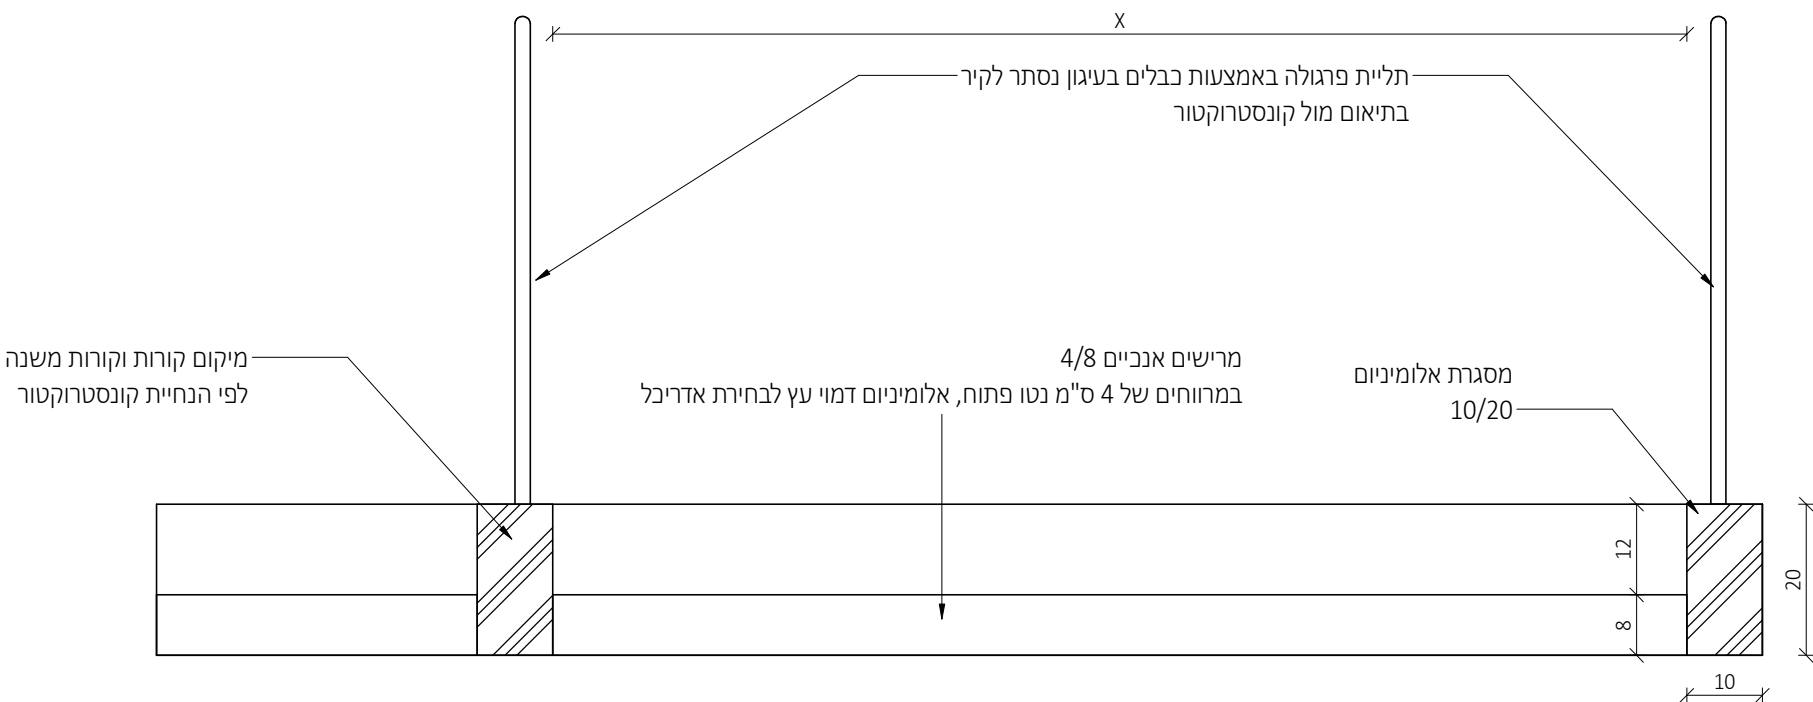

פרגולה - חתך אורך

1 : 10

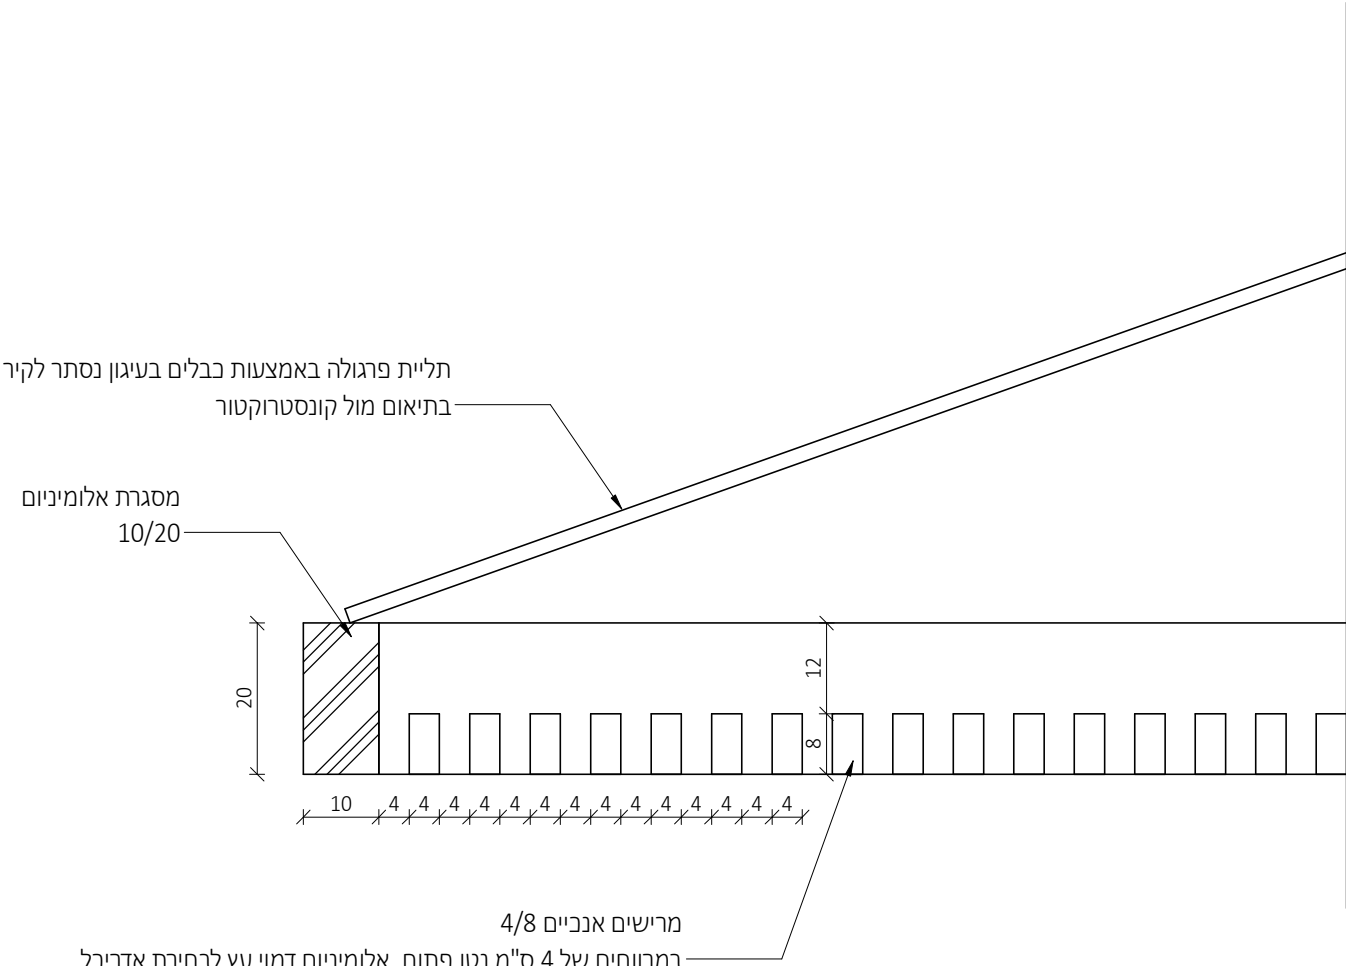

פרגולה - חתך רוחב

1 : 10

מתכננים:


ניהול פרויקט
מהיסוד - בן סולומון
פיקוח
מהיסוד - בן סולומון
קונסטרוקציה
ערן שילר
מיזוג אוויר
אייל ארז מהנדסים ויועצים בע"מ
אינסטלציה
איתן אלמסי
חשמל
איתן בסיס
אלומיניום
נוף
נתי בלוקא
חשמל חכם
חימום תת רצפתי
איטום
צבי טל
אקוסטיקה
מעליות
קרקע וביסוס
דיה הנדסת קרקע וביסוס
רישוי

± 0.00 = +253.30

- הערות:
1. תכנית זו יש לקרוא יחד עם תכנית הרישום.
 2. גובה אבטומיטי: ראו תכנית פיתוח.
 3. הפרדות הן בין קירות הבניה ולא כולל פיתוח.
 4. פיתוח השטח סביב הבניה, כולל, מדרגות, גדרות, שבילים, ריצופים, שטחים בגנים, חניה וגן וא תכנית פיתוח.
 5. איטום קירות הצפת הבניה כמעט עם הקרקע ובנידוד תחסי לאורך העמודים והקירות וכל המפרקים. כלירות או עם סימני גיבס. ראו תכנית קונסטרוקציה.
 6. אף דים יבוצע בכל מישור אופקי הבולם מהגבול.
 7. סוף תחסי במסיד- ע"פ מפרס תדמיקר. מאושר ט"י פיקוד העורף.

המבצע אחראי לסידות : עליו לבקר ולבדוק את כל המידות בתכנית ובקשות הטבחה.
במסגרת של מידות או אי התאמה בתכנית /או בבנוי, עליו להודיע על כך מיד לאדריכל בסדר המשיך בעבודתו.
המבצע ישתמש או ויק בתכנית שאושרו לכניסיו.
המבצע יחזיק באחר, לכל שטח, של משרדו של תכנית.
את לקבוע מידות על ידי חזירה בשו שום.
התכנית היתה הכושה האדריכל ואין לשנות כל שימוש בה או ברעיונות המלומים בה, אלא באישור בכתב מהאדריכל.
המבצע /או יועץ אשר שמו רשום בתכנית זו, נושא לכיד באחריות המקצועית והטכנית לתכנית.
על המפקח והמבצע לזרוא התאמת התכנית האדריכלית "כניסיו" לתכנית ויתר, המכר והתכנית המאושרות ע"י כל גורמים הרשמיים.
התכנית כוללת את כל האחריות והידוע עד ליום תחלתה.

מקרא קירות:

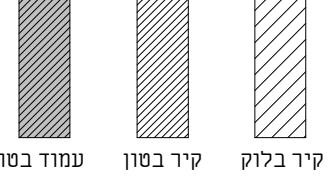

תאריך	תיאור	מהדורה
22/09/2025	מכרז	1

אדריכלות

שם המסין:	CLIENT NAME:
קבוצת רכישה נופיה	
שם הפרויקט:	PROJECT NAME:
נופיה - מגרש 5	
שם הגיליון:	DRAWING NAME:
פרטי פרגולה	
מספר גיליון:	SHEET NUMBER:
A3-4-104	
מחזוריה:	EDITION:
קנה מידה:	SCALE:
As indicated	
סטוס:	STATUS:
למכרז	
שורסס ע"י:	נבדק ע"י:
תאריך:	DATE:
22.09.25	



נירסן חיינר אדריכלים
מורד החדר 2, בית חירות
09-5545642 78
office@nh-arch.com
www.nh-arch.com

רשימת חלונות					
סוג	תיאור	כמות	גובה	רוחב	מס פריט

מרתף

חלון הזזה פרופיל 7000 קליל	צלון רפפה חיצוני חשמלי + ארגז חיצוני	1	100	320	7
חלון קיפ פרופיל 4500 קליל	ללא רפפה	1	80	60	8

קרקע

ויטרינה פרופיל 7500 קליל	צלון רפפה חיצוני חשמלי + ארגז חיצוני	1	240	450	1
חלון הזזה פרופיל 7000 קליל	צלון רפפה חיצוני חשמלי + ארגז חיצוני	1	110	130	2
ויטרינה פרופיל 7500 קליל	צלון רפפה חיצוני חשמלי + ארגז חיצוני	2	240	180	3
חלון הזזה פרופיל 7000 קליל	צלון רפפה חיצוני חשמלי + ארגז חיצוני	3	110	110	4
חלון קיפ פרופיל 4500 קליל	צלון רפפה חיצוני חשמלי + ארגז חיצוני	1	110	90	5
חלון קיפ פרופיל 4500 קליל	צלון רפפה חיצוני חשמלי + ארגז חיצוני	1	110	80	6

סוג זכוכית – בהתאם למפורט בדו"ח התרמי (תנאי המינימום בעמוד 9 מתוך המפרט התרמי). כמו כן, הזכוכית תקבע בתיאום עם הקבלן לאחר אישור יועץ התרמי וחברת הניהול

כל פריט יחולק למינימום הכנפיים האפשרי (לתיאום מול ספק האלומיניום ובמסגרת שרטוטי הshop drawing)

רשימת דלתות					
סוג	הערות	כמות	גובה	רוחב	מספר פריט

דלת חוץ דגם גארדה	דלת כניסה	1	240	150	0
דלת פנים "אקוודור" תוצרת חמדיה	דלת פנים	3	210	90	1
דלת הזזה "אקוודור" פורמייקה תוצרת חמדיה	דלת הזזה	2	210	80	2
דלת הזזה "אקוודור" פורמייקה תוצרת חמדיה	דלת הזזה	1	210	85	3
דלת פנים "אקוודור" תוצרת חמדיה	דלת נגרות ממ"ד	1	200	80	4

נוימן חיינר אדריכלים בע"מ

כל הזכויות שמורות
ח.ל.ח

NeumanHaynerArchitects

רשימת פתחים

שם התכנית:

A3-6-1000

גליון מספר:

מהדורה:

22/09/2025



נופיה - מגרש 5

שם הפרויקט:

סטטוס:

למכרז

שם המממן:

קנה מידה:

קבוצת רכישה נופיה

22/09/2025 11:33:01

D:\NH-Arch-Dropbox\NH-Arch-Projects\NH-בתים ודירות\00\5\תכנית\nofia\

FILE NAME: כלל הפרויקטים להיתר\00\5\תכנית\nofia\