


אסור לכסות תאי ביוֹב ו בורות חלחול רק אחרי טופס 4

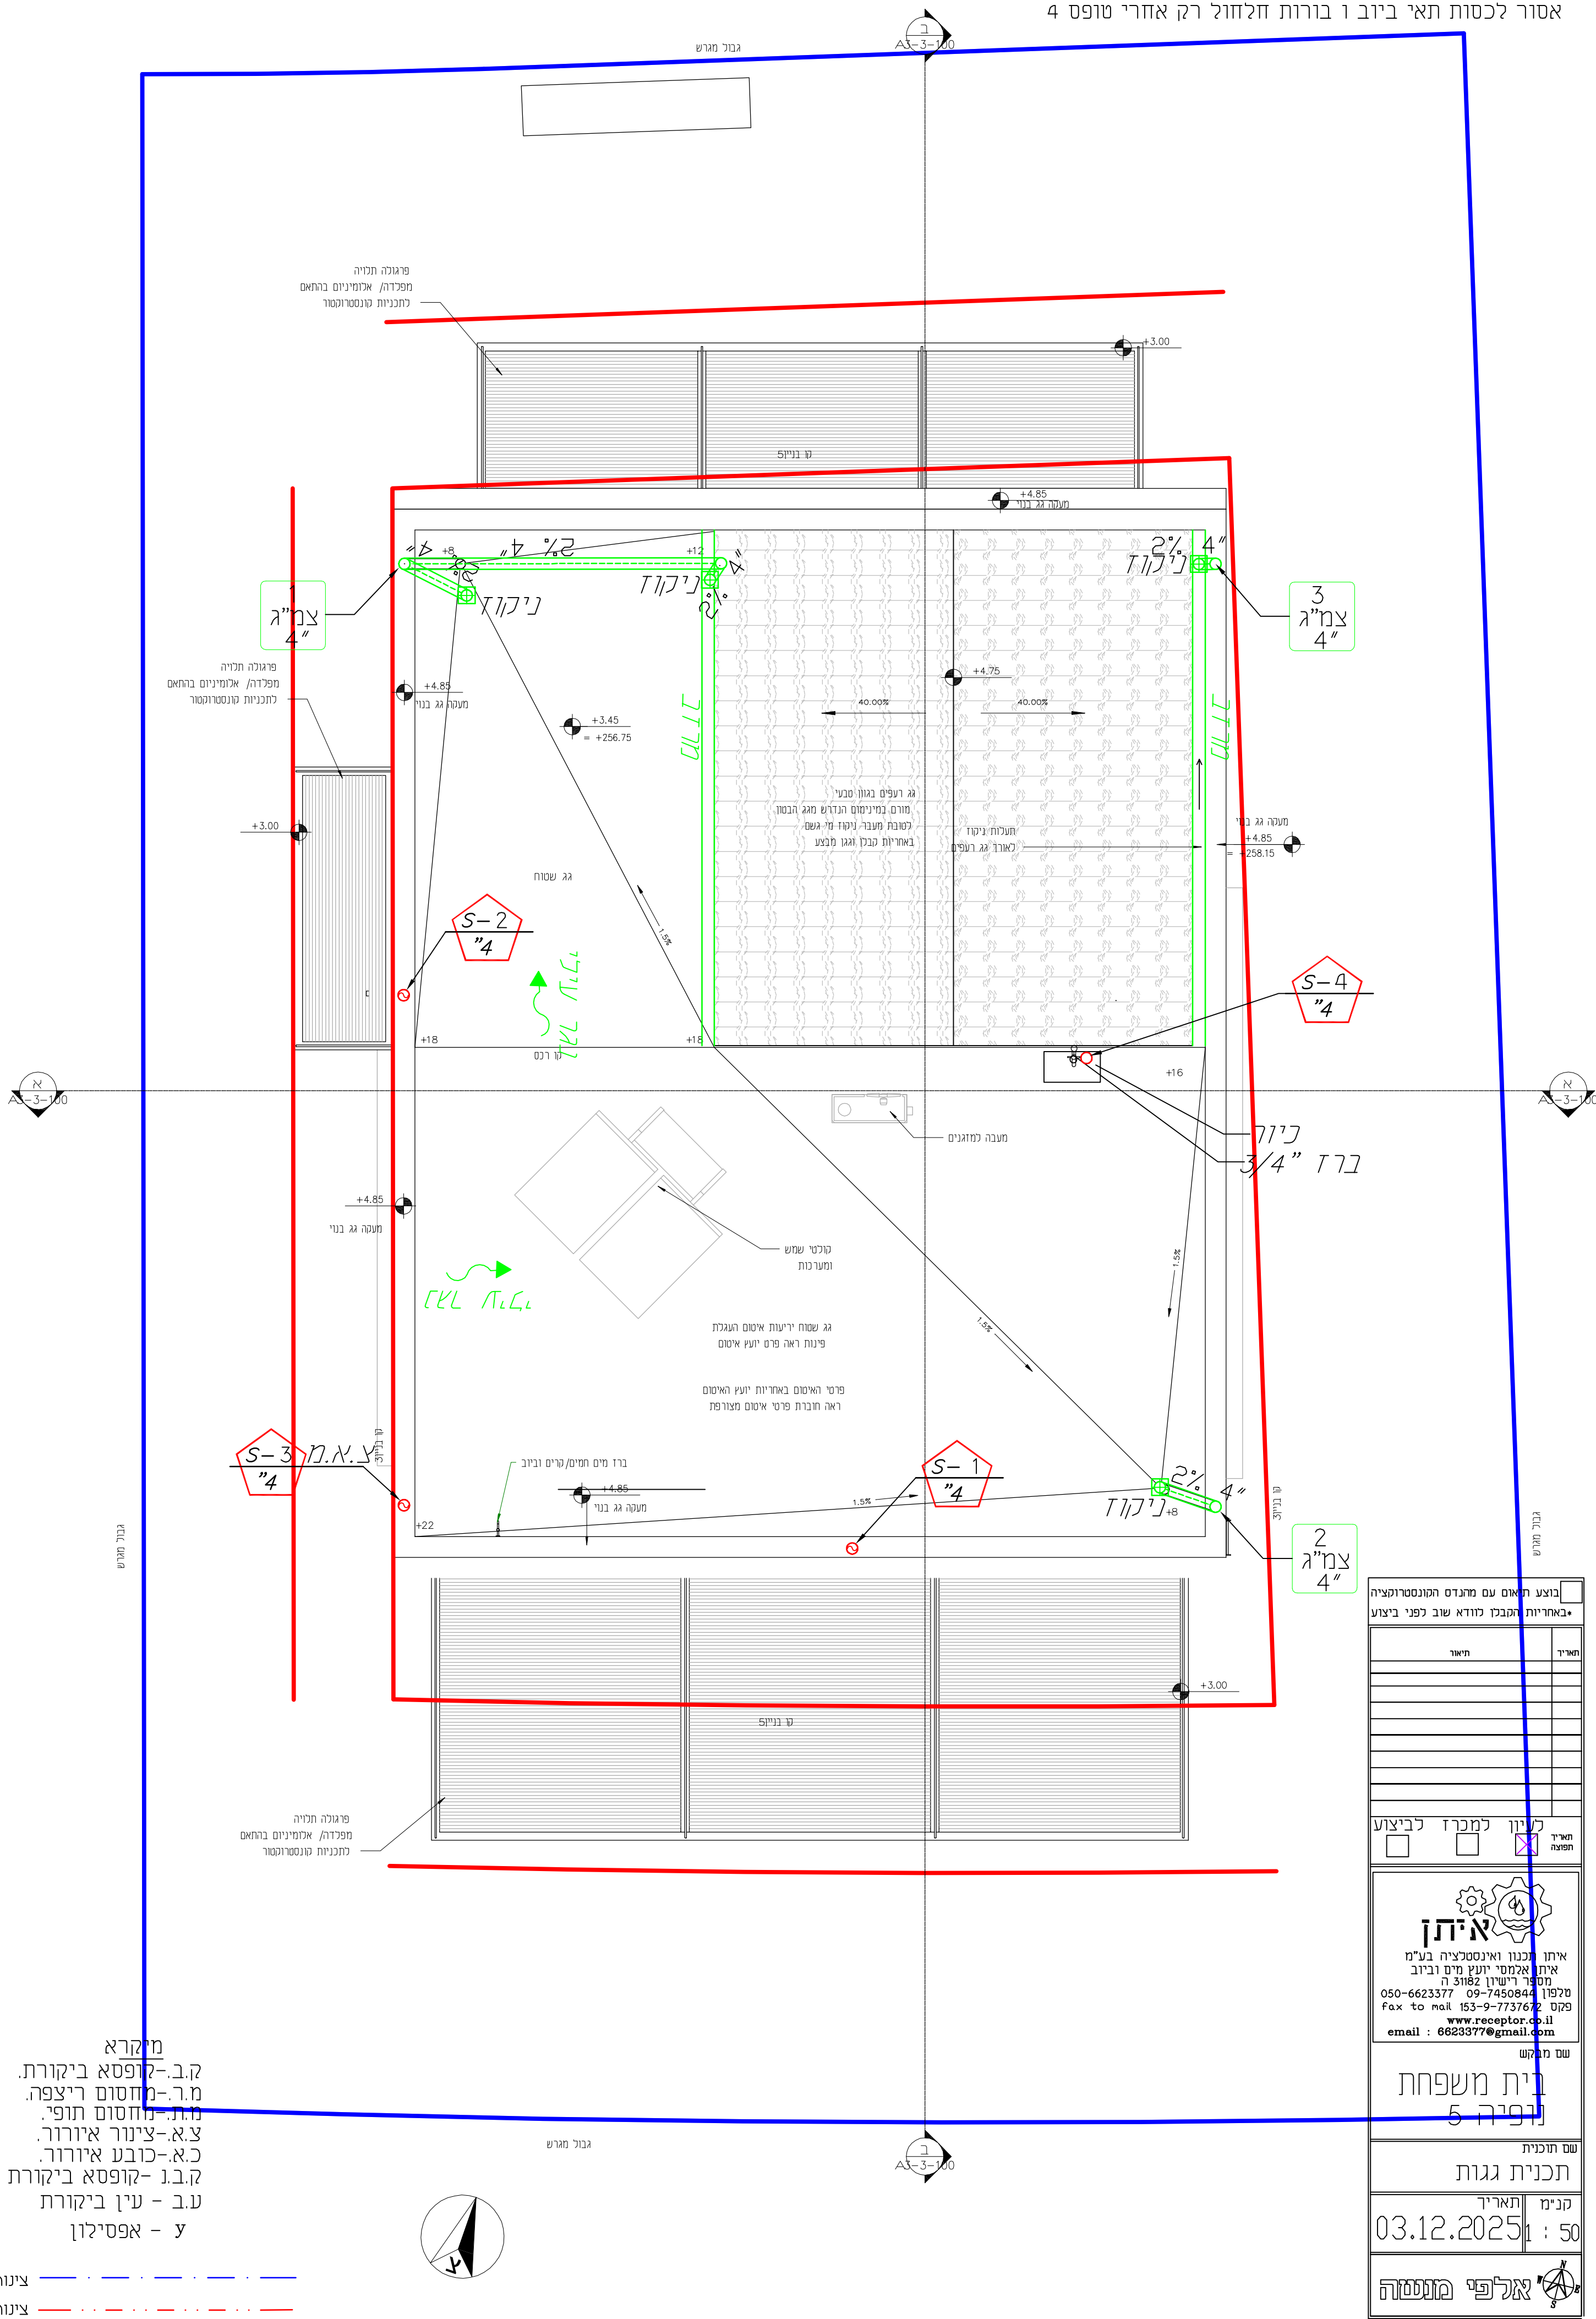

ביצוע תיאום עם מנהלס הקונסטרוקציה •באחריות המבקד כוודא שוב לפני ביצוע	
חזיר	תיאר
לעיון ☒	למכרז ☐
תאריך חפצה	לביצוע ☐
 איטן איתן הננו ואינסטליצי בע"מ איתן האמיני יועץ מיס וביוב מספר רישון 31082 ה טלפון 050-6623377 09-7450844 פקס 09-7737672 www.receptor.co.il email : 6623377@gmail.com	
שם מחלק	
בית משפחת נריה 5	
שם חוכנית	
תכנית גגות	
תאריך	קנימ
03.12.2025	1 : 50
אלפי מענטזה	
	

