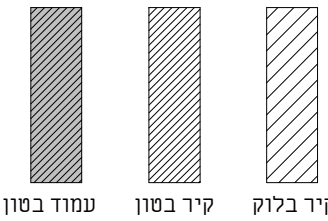


מתכונים:


ניהול פרויקט
מהיסוד - בן סולומון
פיקוח
מהיסוד - בן סולומון
קונסטרוקציה
ערן שילר
מיזוג אוויר
אייל ארז מהנדסים ויועצים בע"מ
אינסטלציה
איתן אלמסי
חשמל
איתן בסיס
אלומיניום
נוף
נתי בלוקא
חשמל חכם
חימום תת רצפתי
איטום
צבי טל
אקוסטיקה
מעליות
קרקע וביסוס
דיה הנדסת קרקע וביסוס
רישוי

[illegible]

מקרא קירות:

[illegible]

אדריכלות

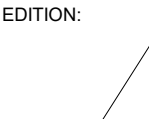PROJECT NAME:		קבוצת רכישה נופיה	
DRAWING NAME:		נופיה - מגרש 6	
SHEET NUMBER:		גליון שער	
SCALE:		EDITION:	
TATUS:			
DATE:		22.09.2025	



NeumanHaynerArchitects

נוימן חיינר אדריכלים
מורד ההדריס 2, בית חירות
של 09-9545842

office@nh-arch.com
www.nh-arch.com

נופיה - מגרש 6			
מס' גיליון	שם גיליון	מהדורה	תאריך הפצת מהדורה
A3-1-100	גיליון שער	1	22.09.2025
A3-1-101	תכנית קומת קרקע	1	22.09.2025
A3-1-102	תכנית קומה א	1	22.09.2025
A3-1-103	תכנית גג	1	22.09.2025
A3-2-200	חזיתות 1	1	22.09.2025
A3-2-201	חזיתות 2	1	22.09.2025
A3-3-100	חתכים	1	22.09.2025
A3-4-100	גליון מדרגות	1	22.09.2025
A3-4-103	פרטים	1	22.09.2025
A3-4-104	פרטי פרגולה	1	22.09.2025
A3-6-1000	רשימת פתחים	1	22.09.2025



ניהול פרויקט
מהיסוד - בן סולומון
פיקוח
מהיסוד - בן סולומון
קונסטרוקציה
ערן שילר
מיזוג אוויר
אייל ארז מהנדסים ויועצים בע"מ
אינסטלציה
איתן אלמסי
חשמל
איתן בסיס
אלומיניום
נוף
נתי בלוקא
חשמל חכם
חימום תת רצפתי
איטום
צבי טל
אקוסטיקה
מעליות
קרקע וביסוס
דיה הנדסת קרקע וביסוס
רישוי

[illegible][illegible]


CLIENT NAME:		ה מסיק	
קבוצת רכישה נופיה			
PROJECT NAME:		ה מסיק	
נופיה - מגרש 6			
DRAWING NAME:		ה מסיק	
תכנית קומת קרקע			
SHEET NUMBER:		ה מסיק	
A3-1-101			
SCALE:	קנה מידה:	EDITION:	הדורה:
1 : 50			
STATUS:	סטוס		
למכר			
	נבדק ע"י:		רשם ע"י:
DATE:	22.09.2025		איר:

NeumanHaynerArchitects

יומן חיינר אדריכלים
רודר ההדורים 2, בית חירות
09-9545842 טל

office@nh-arch.com
www.nh-arch.com

1. יש לעבוד במקביל לתכניות יועצים המאשרות על ידי האדריכל.
2. פרטי ספי חלון - עפ"י חוברת אלומיניום של הספק הנבחר ובתיאום מול אדריכל.
3. חימום תת רצפתי (במידה ויש במגרש זה) עפ"י פרטי הספק ובתיאום מול אדריכל.
4. יש לעבוד במקביל לתכניות עיצוב פנים (במידה ויש מעצב פנים במגרש זה) המאושר.
5. באחריות הקבלן לעדכן את האדריכל על אי התאמה בין התכניות יועצים לאדריכלות.
6. כל הדלתות לפי מפרט מצורף.
7. כל אלמנטי הבטון יקבלו התייחסות תרמית לפי הנחיות יועץ.
8. פרטי איטום, בידוד וניקוז עפ"י תכניות יועצים ובאחריות הקבלן.

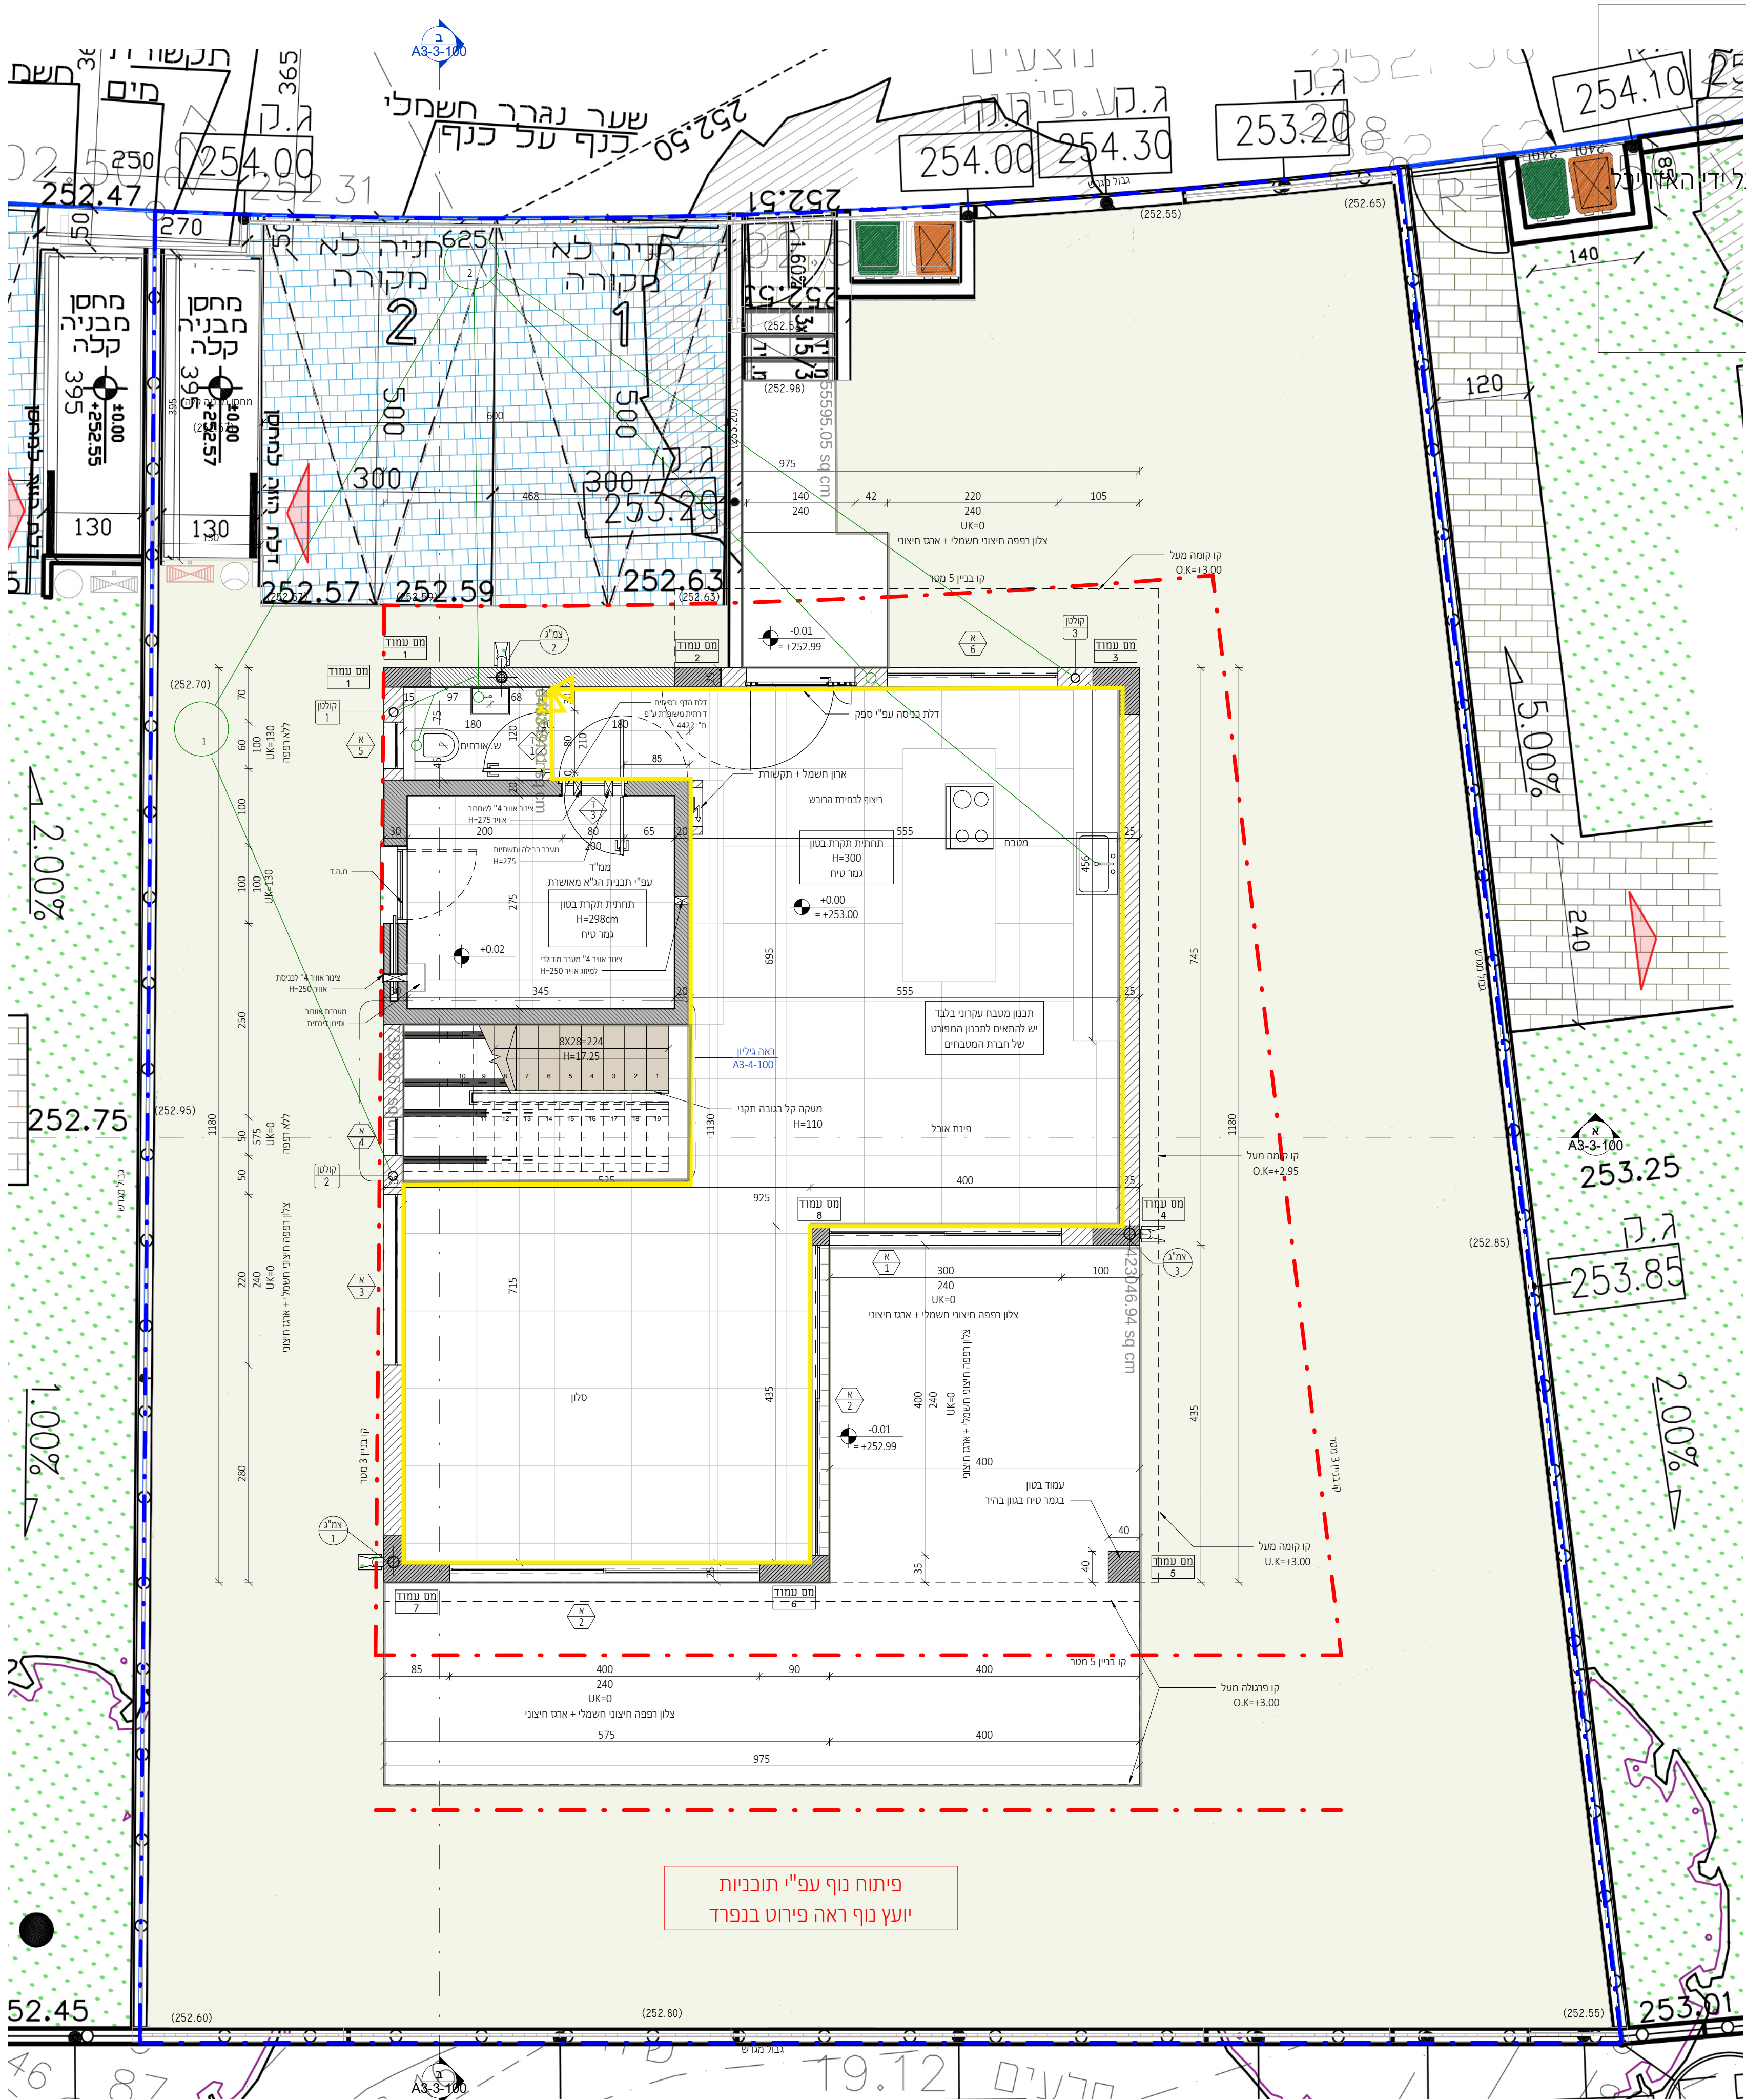


1 : 50

הערות:

1. יש לעבוד במקביל לתכניות יועצים המאושרות על ידי האדריכל.
2. פרטי ספי חלון - עפ"י חוברת אלומיניום של הספק הנבחר ובתיאום מול אדריכל.
3. חימום תת רצפתי (במידה ויש במגרש זה) עפ"י פרטי הספק ובתיאום מול אדריכל.
4. יש לעבוד במקביל לתכניות עיצוב פנים (במידה ויש מעצב פנים במגרש זה) המאושרות על ידי האדריכל.
5. באחריות הקבלן לעדכן את האדריכל על אי התאמה בין התכניות יועצים לאדריכלות.
6. כל הדלתות לפי מפרט מצורף.
7. כל אלמנטי הבטון יקבלו התייחסות תרמית לפי הנחיות יועץ.
8. פרטי איטום, בידוד וניקוז עפ"י תכניות יועצים ובאחריות הקבלן.

- 1 : 50

www.elsevier.com/locate/jmb

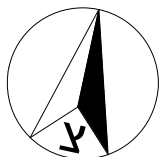




פרטי איטום, בידוד וניקוז עפ"י תכניות יועצים ובאחריות הקבלן

מתכונים:

ניהול פרויקט
מהיסוד - בן סולומון
פיקוח
מהיסוד - בן סולומון
קונסטרוקציה
ערן שילר
מיזוג אוויר
אייל ארז מהנדסים ויועצים בע"מ
אינסטלציה
איתן אלמסי
חשמל
איתן בסיס
אלומיניום
בופ
נתי בלוקא
חשמל חכם
חימום תת רצפתי
איטום
צבי טל
אקוסטיקה
מעלות
קרקע וביסוס
דיה הנדסת קרקע וביסוס
רישוי

[illegible][illegible]

אדריכלות

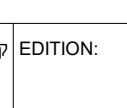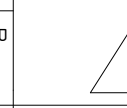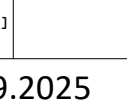
PROJECT NAME:		קבוצת רכישה נופיה	
DRAWING NAME:		נופיה - מגרש 6	
SHEET NUMBER:		חזיתות 1	
SCALE:		EDITION:	
1 : 50			
TATUS:		דמרה:	
למכר			
DATE:		דפוס ע"י:	
22.09.2025			



NeumanHaynerArchitects


וימן חיינר אדריכלים
מורד ההדרים 2, בית חירות
טל 09-9545842

זכויות ייצור / ע"פ הנחיות עו"ד

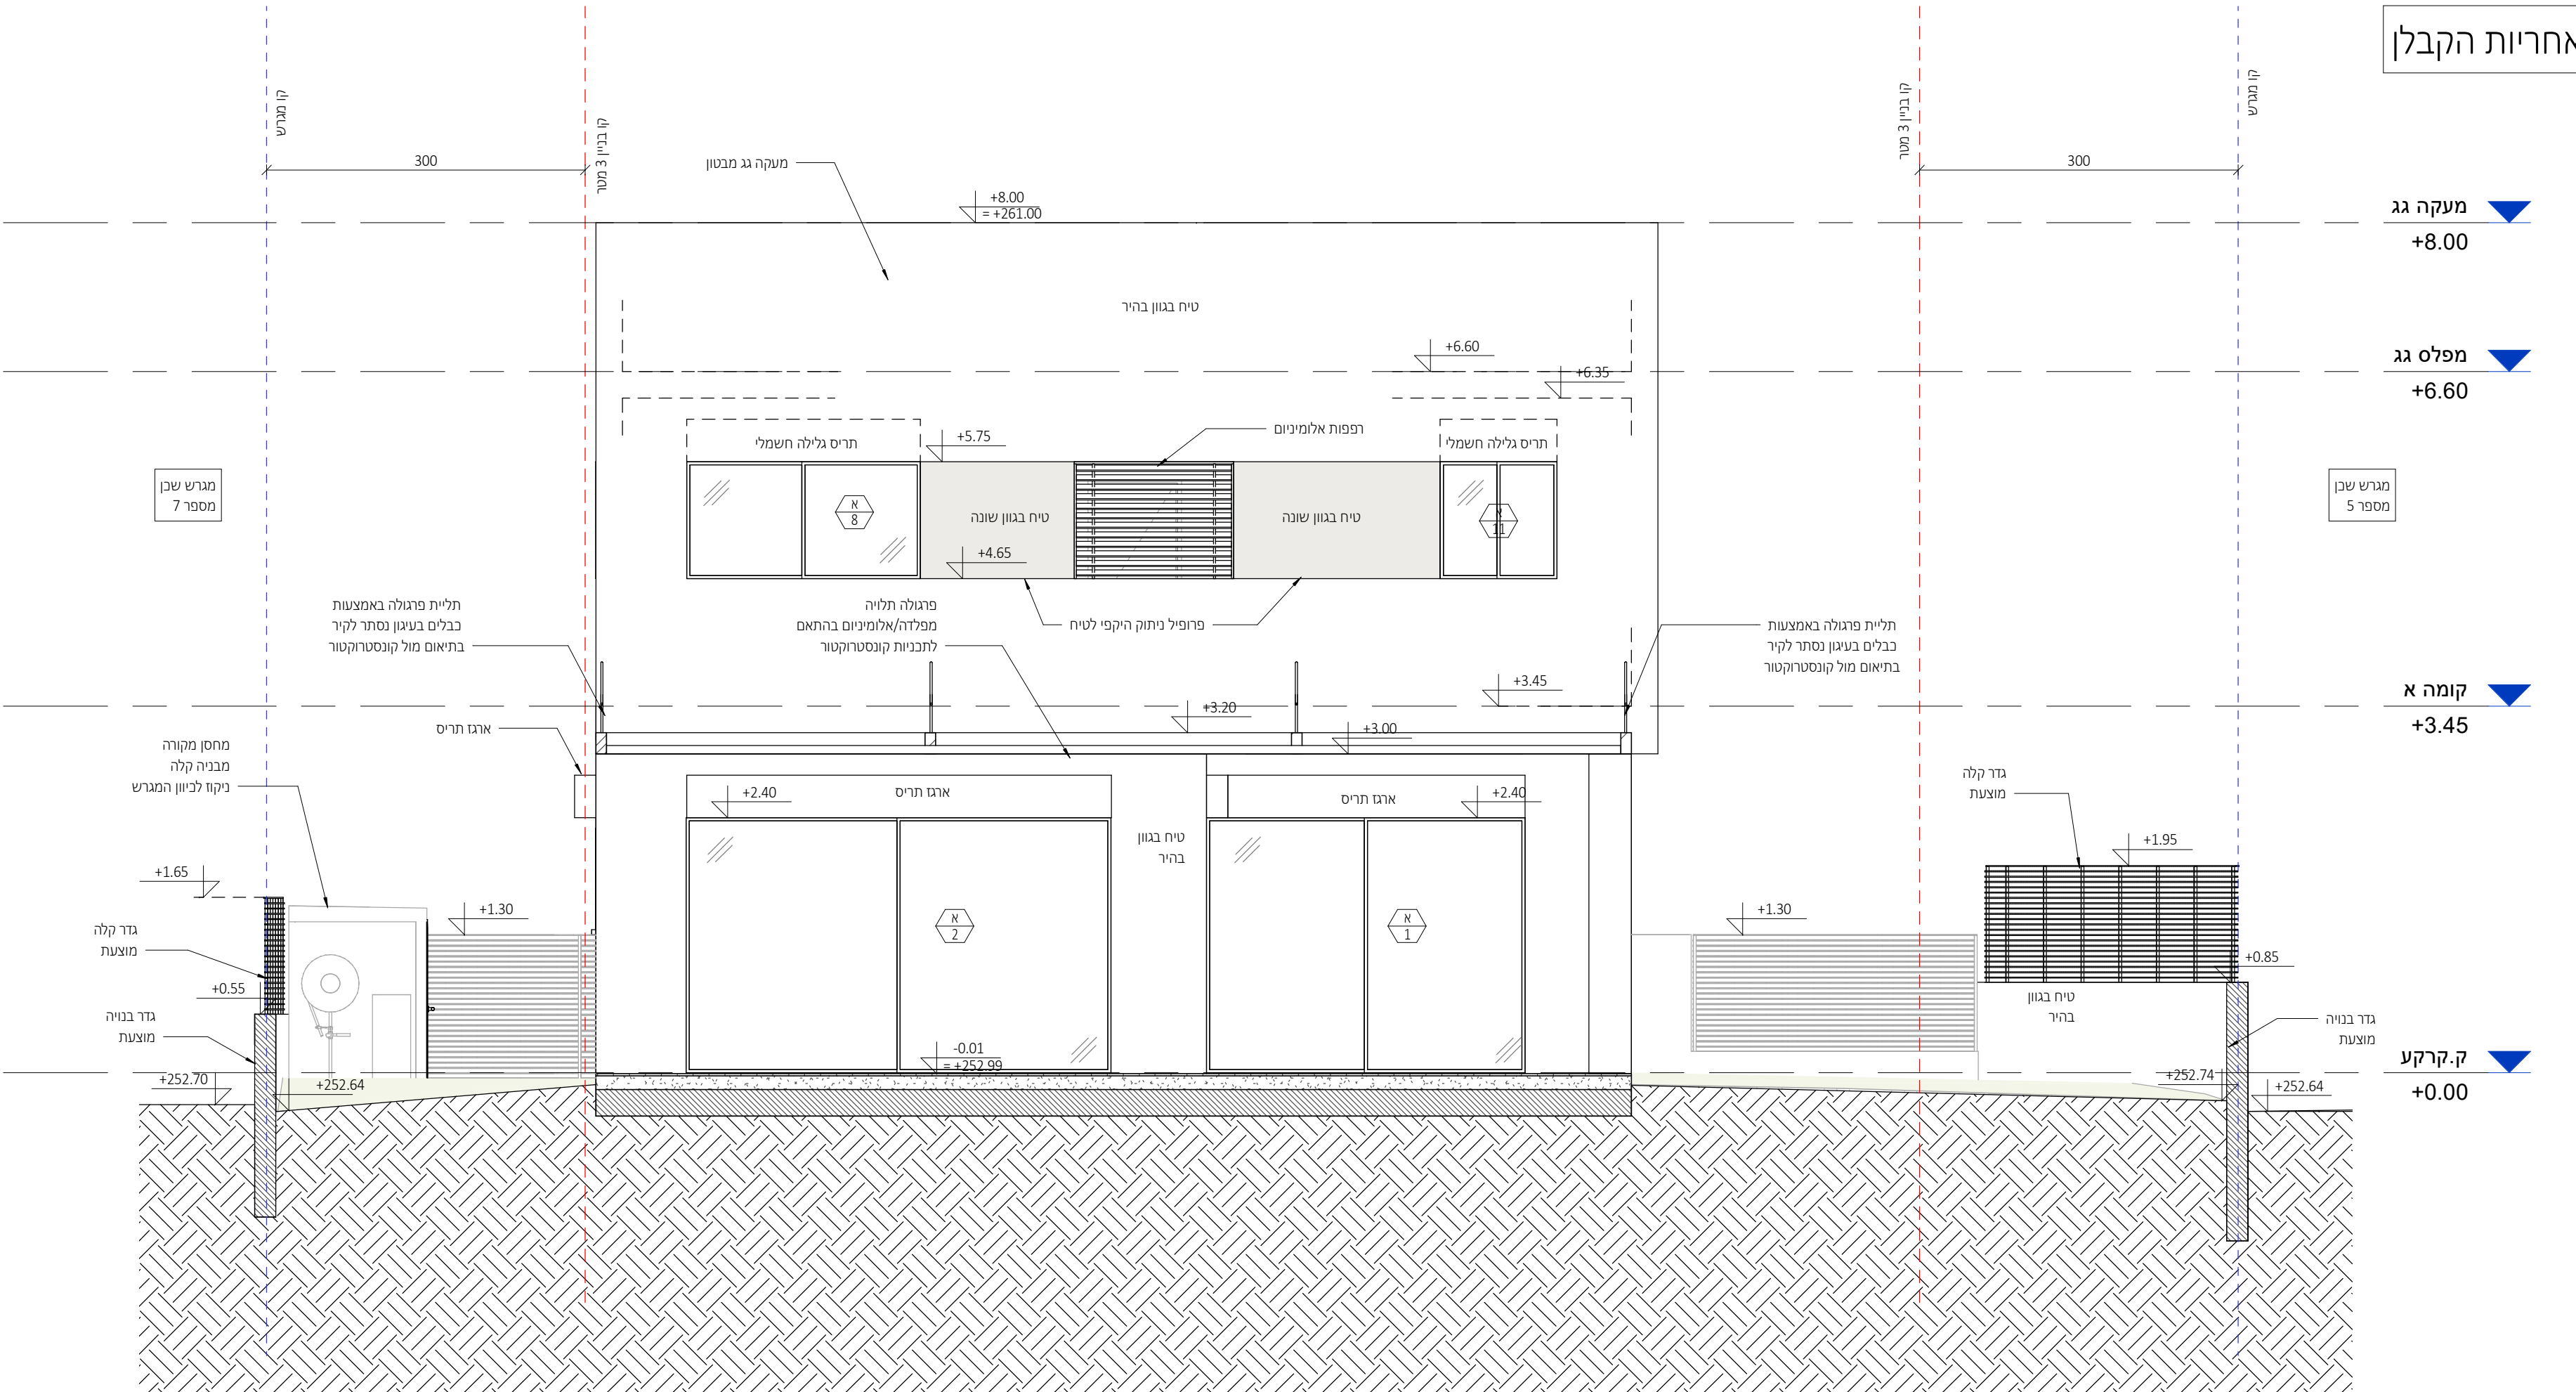

חזית דרומית

1 : 50

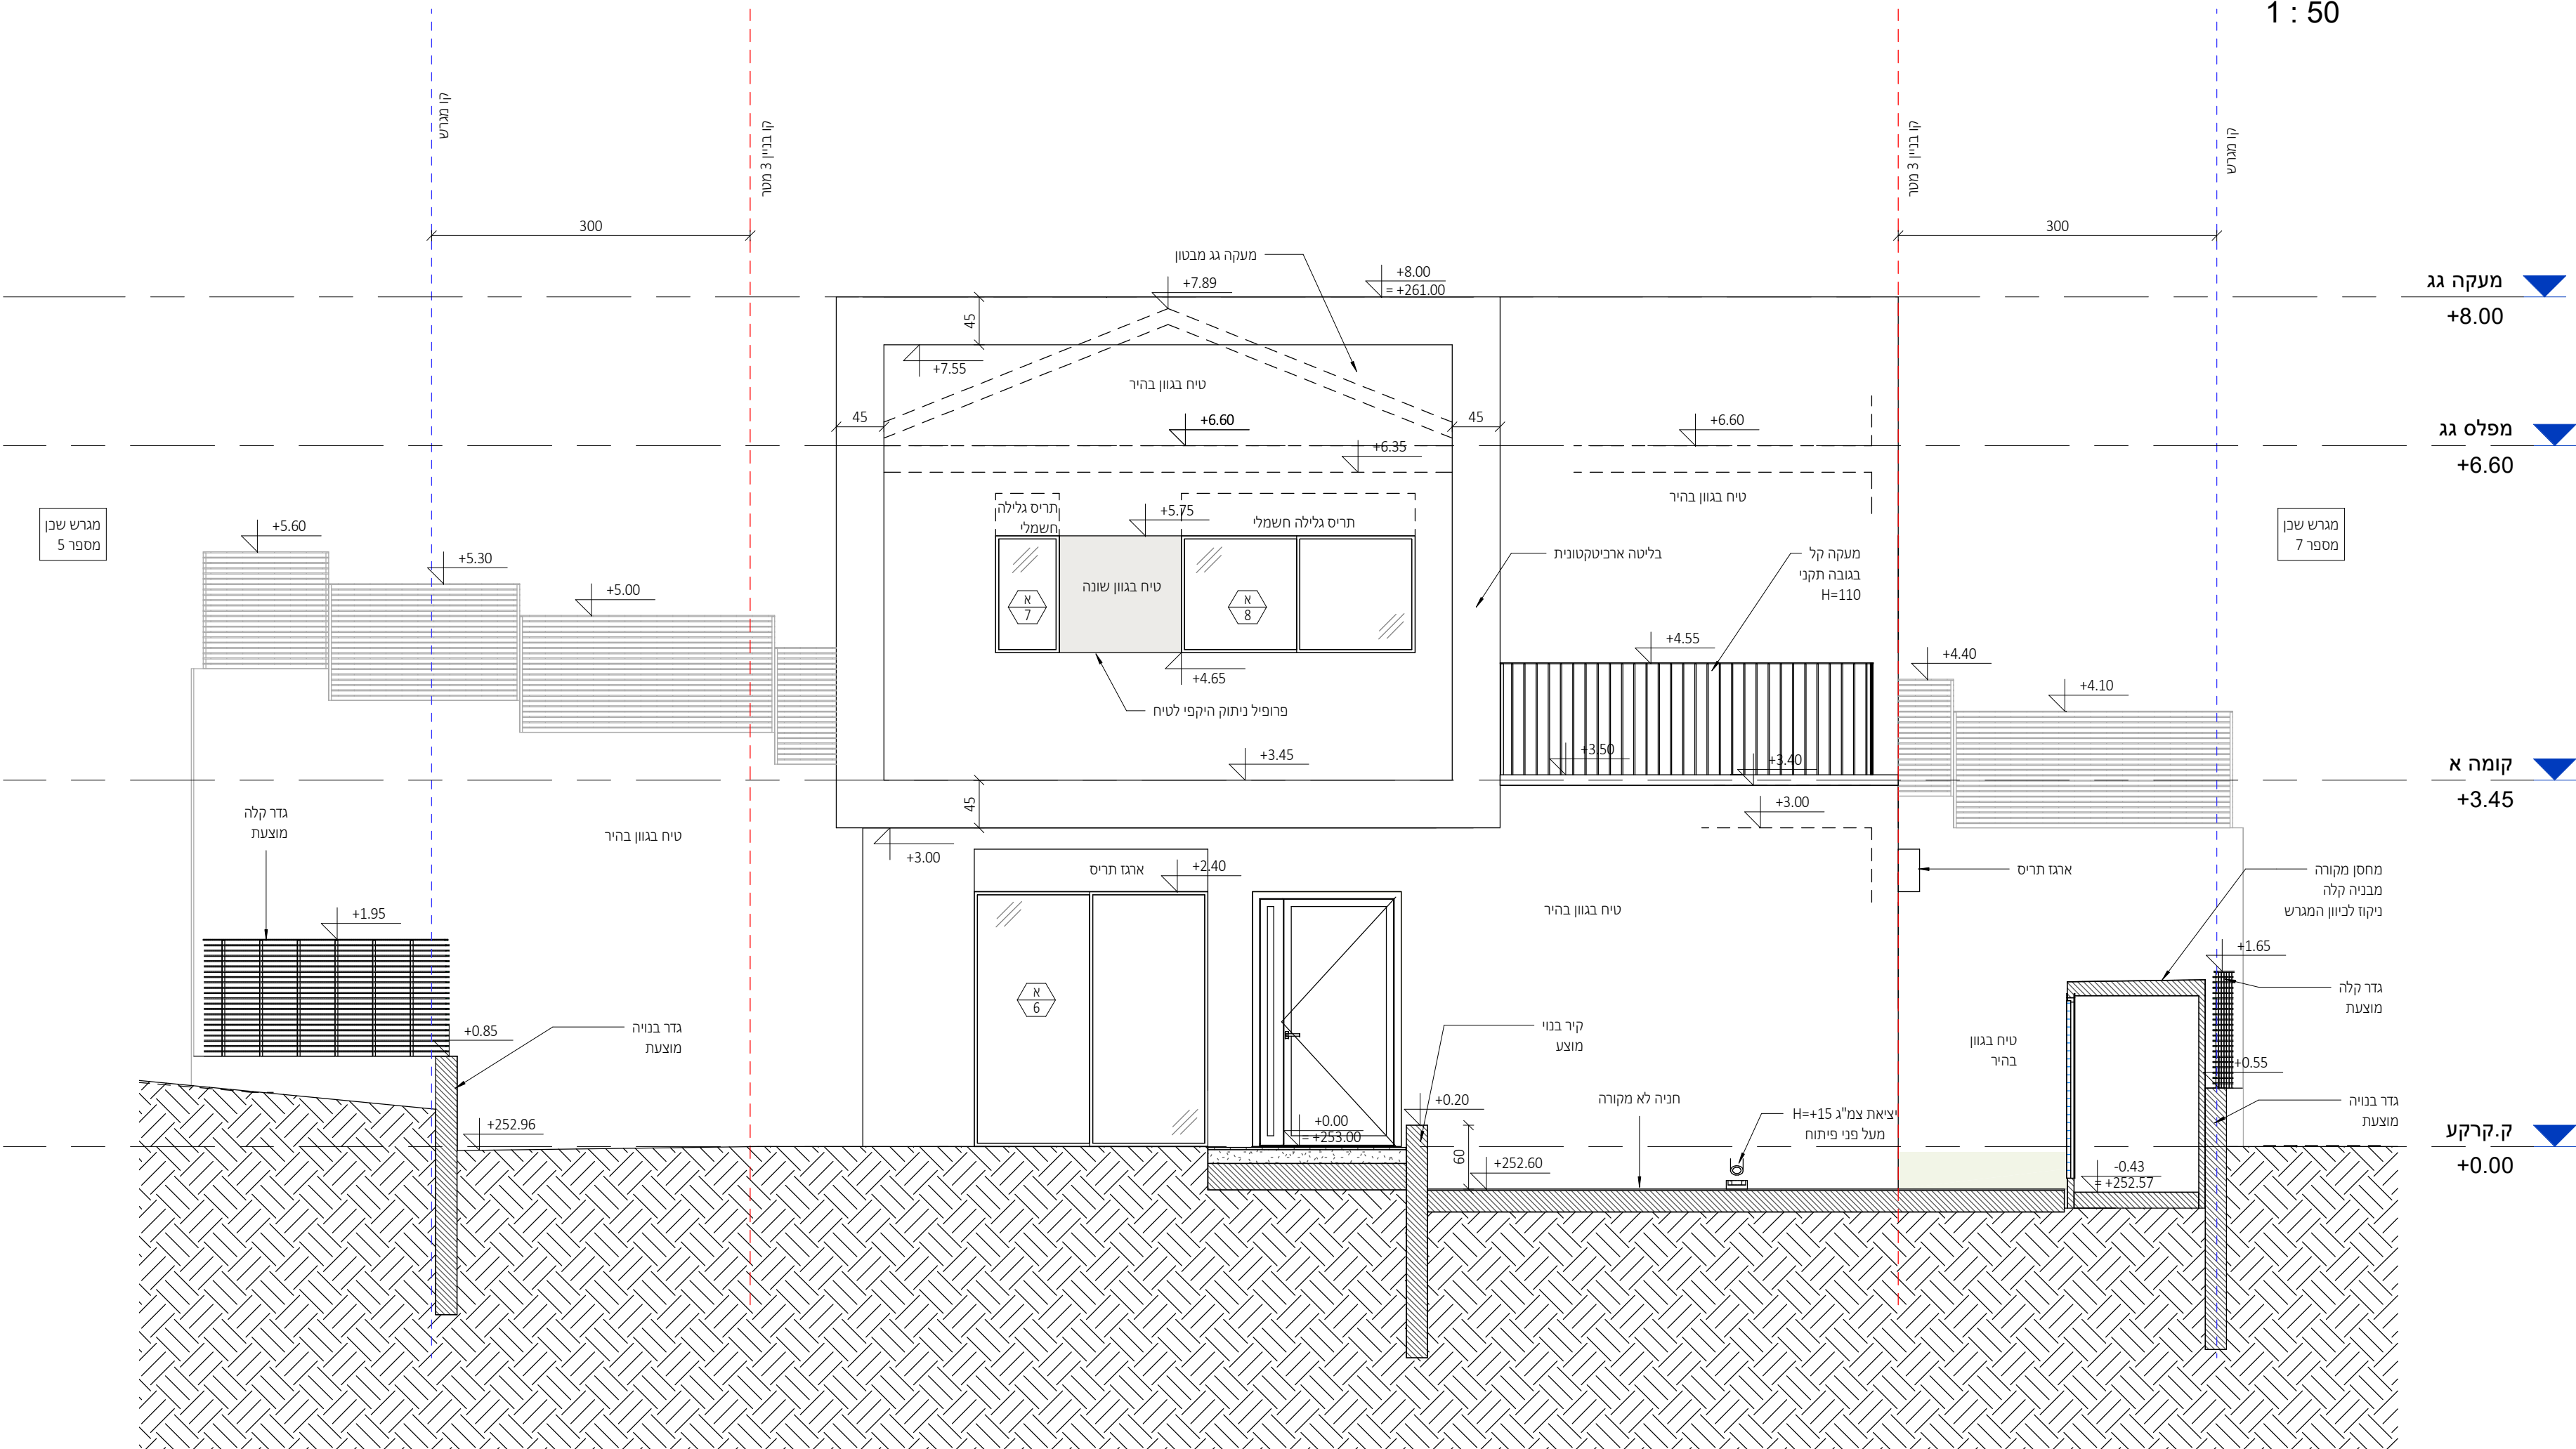

חזית צפונית


1 : 50

ניהול פרויקט
מהיסוד - בן סולומון
פיקוח
מהיסוד - בן סולומון
קונסטרוקציה
ערן שילר
מיזוג אוויר
אייל ארז מהנדסים ויועצים בע"מ
אינסטלציה
איתן אלמסי
חשמל
איתן בסיס
אלומיניום
נוף
נתי בלוקא
חשמל חכם
חימום תת רצפתי
איטום
צבי טל
אקוסטיקה
מעליות
קרקע וביסוס
דיה הנדסת קרקע וביסוס
רישוי

[illegible][illegible]

אדריכלות	
CLIENT NAME:	המסחר
קבוצת רכישה נופיה	
PROJECT NAME:	הפרויקט
נופיה - מגרש 6	
DRAWING NAME:	התוכנית
חזיתות 2	
SHEET NUMBER:	הפרויקט גיליון
A3-2-201	
SCALE:	קנה מידה:
1 : 50	
STATUS:	סטטוס
למכר	
	נבדק ע"י:
DATE:	אריך:
22.09.2025	

office@nh-arch.com
www.nh-arch.com

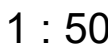

פרטי איטום, בידוד וניקוז עפ"י תכניות יועצים ובאחריות הקבלן

מתכונים:

ניהול פרויקט
מהיסוד - בן סולומון
פיקוח
מהיסוד - בן סולומון
קונסטרוקציה
ערן שילר
מיוזג אוויר
אייל ארז מהנדסים ויועצים בע"מ
אינסטלציה
איתן אלמסי
חשמל
איתן בסיס
אלומיניום
נוף
נתי בלוקא
חשמל חכם
חימום תת רצפתי
איטום
צבי טל
אקוסטיקה
מעליות
קרקע וביסוס
דיה הנדסת קרקע וביסוס
ירשני

[illegible][illegible]

אדריכלות


CLIENT NAME:	המספר		
קבוצת רכישה נופיה			
PROJECT NAME:	הפרויקט		
נופיה - מגרש 6			
DRAWING NAME:	התכנית		
חתכים			
SHEET NUMBER:	פר גליון		
A3-3-100			
SCALE:	קנה מידה:	EDITION:	דור:
1 : 50			
STATUS:	סטוס		
למכר			
	נבדק ע"י:	סטוס ע"י:	
DATE:	22.09.2025		יור:

NeumanHaynerArchitects

ימון חיינר אדריכלים
ורד ההדרים 2, בית חירות
ל 09-9545842

office@nh-arch.com
www.nh-arch.com

זכויות ייצור / ע"פ הנחיות עו"ד

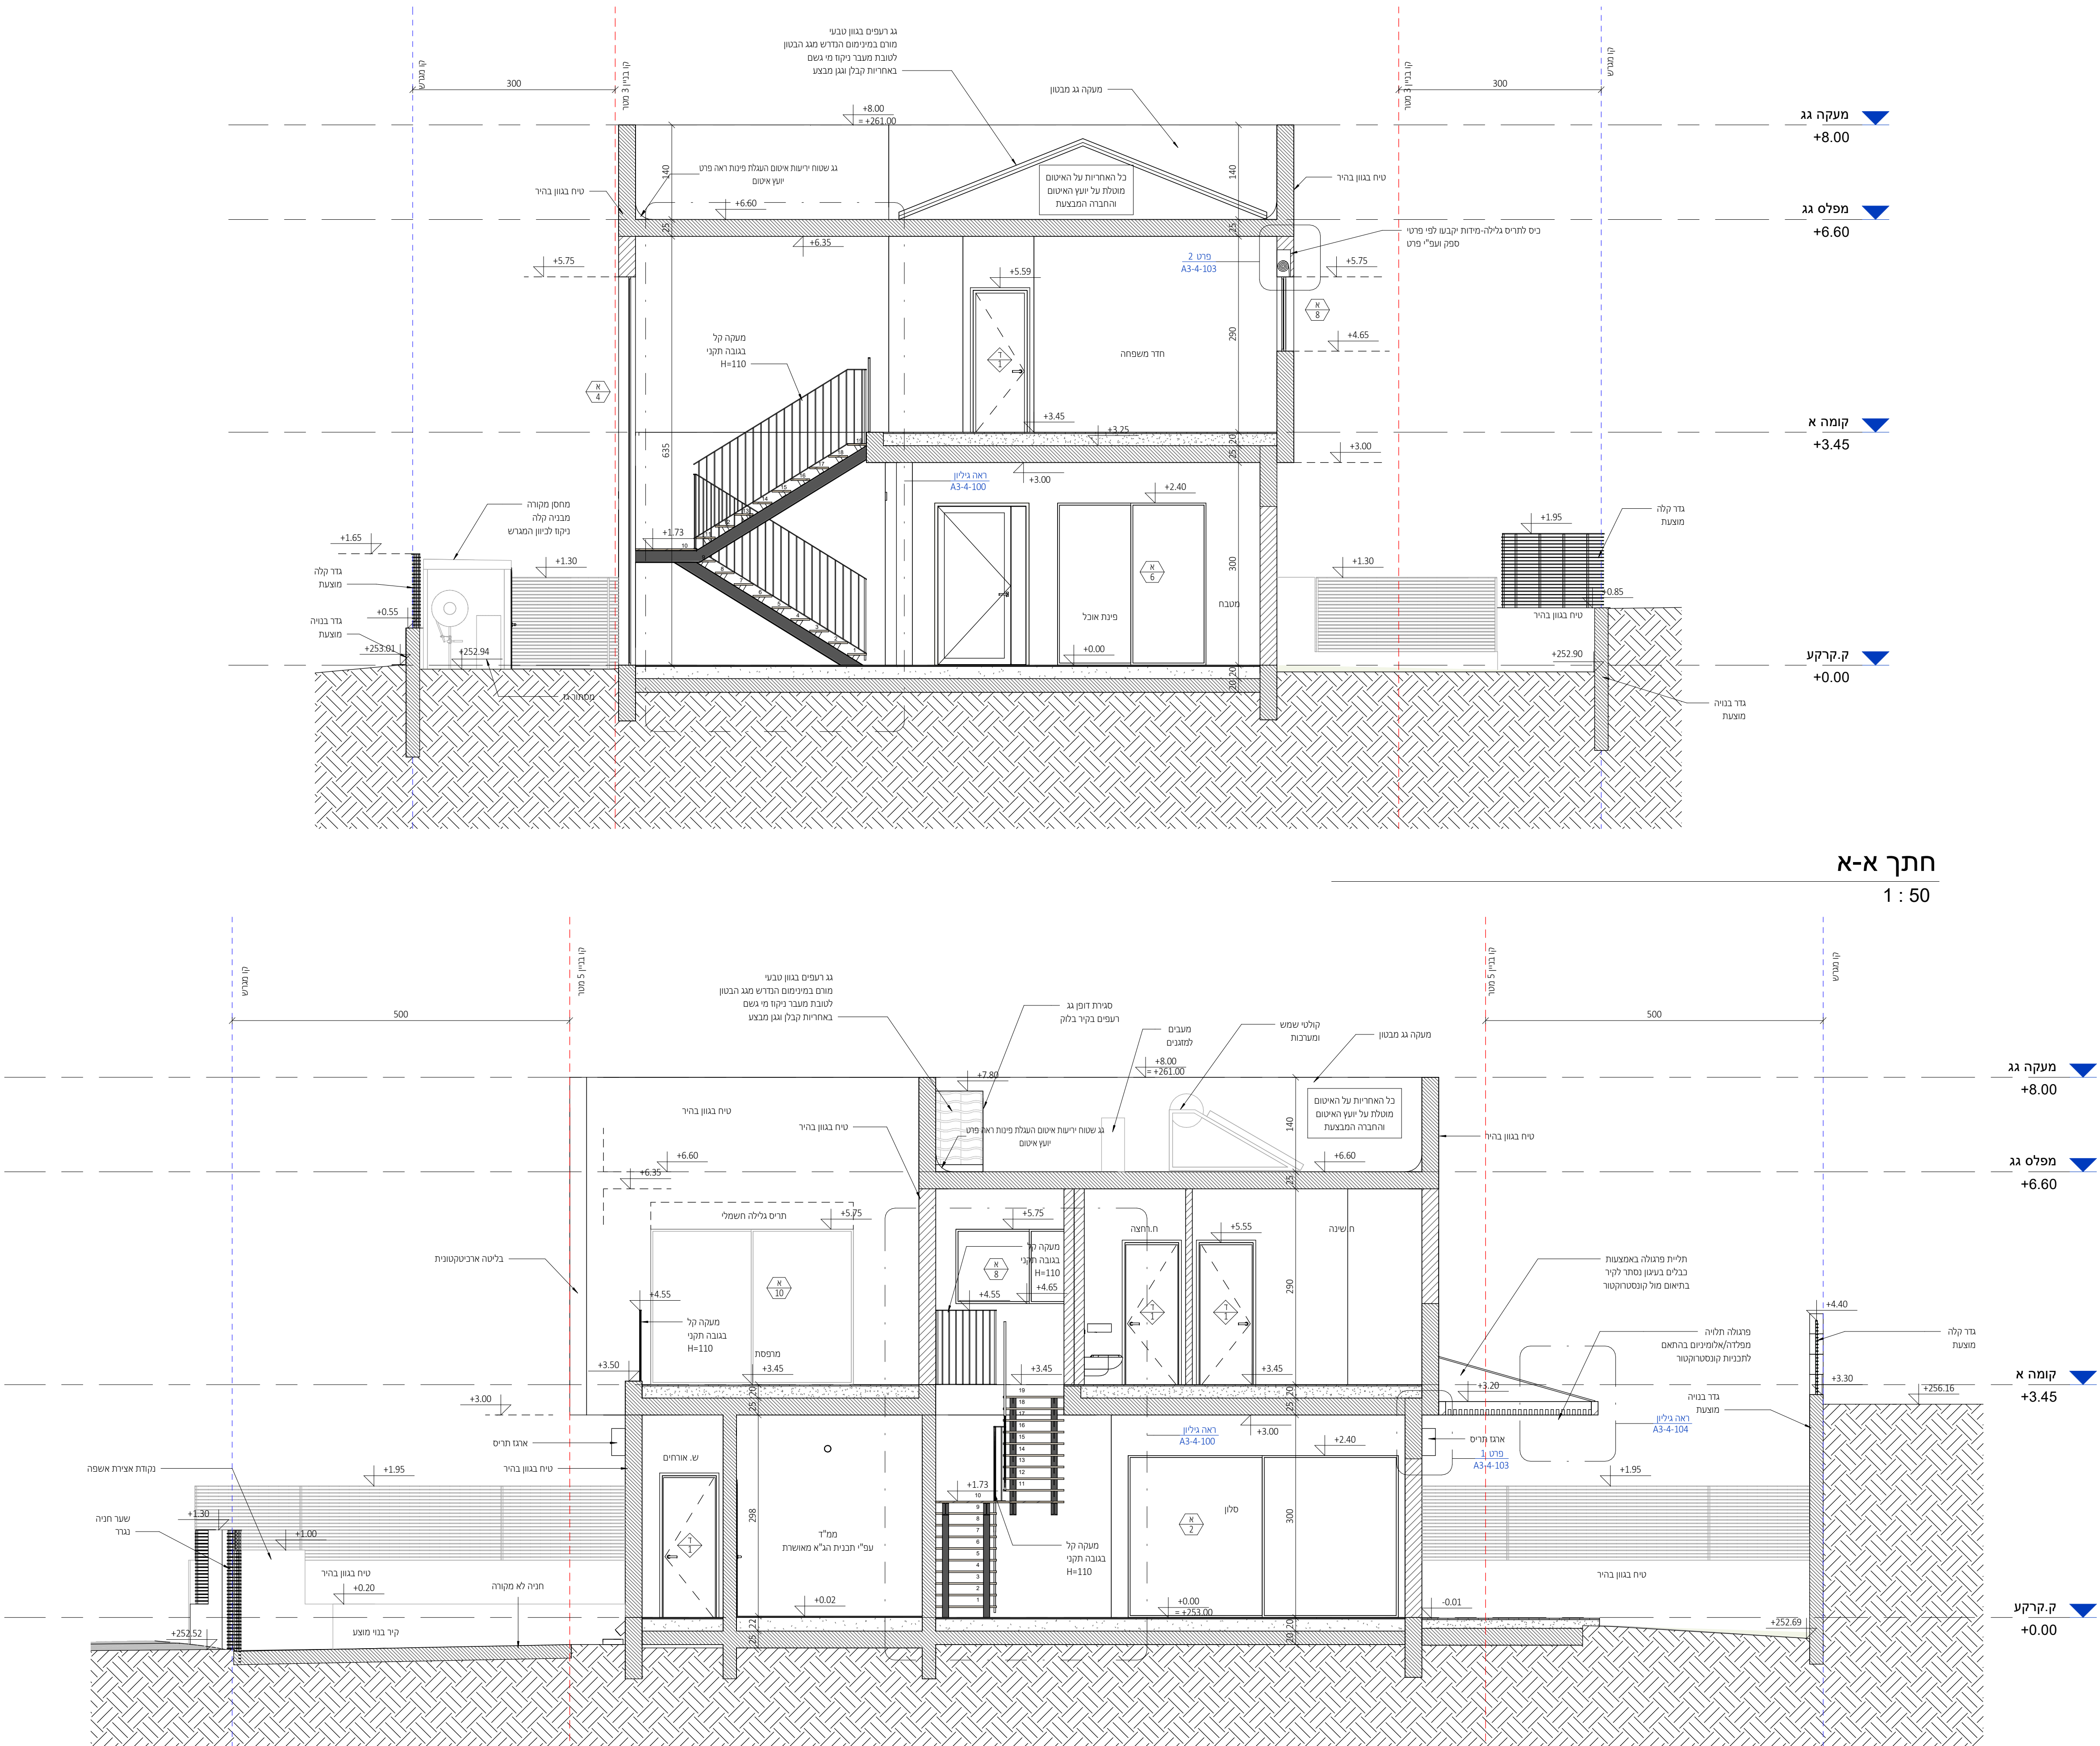

חֲתָךְ ב-ב

1 : 50









ניהל פרויקט
מהיסוד - בן סולומון
פיקוח
מהיסוד - בן סולומון
קונסטרוקציה
ערן שילר
מיזוג אוויר
אייל ארז מהנדסים ויועצים בע"מ
אינסטלציה
איתן אלמסי
חשמל
איתן בסיס
אלומיניום
נוף
נתי בלוקא
חשמל חכם
חימום תת רצפתי
איטום
צבי טל
אקוסטיקה
מעליות
קרקע וביסוס
דיה הנדסת קרקע וביסוס
רישיון

שקרא קירות:



עמוד בטון קיר בטון קיר בלוק

אדריכלות		שם הפרויקט:
קבוצת רכישה נופיה		חומר:
נופיה - מגרש 6		סלולר:
גליון מדרגות		מספר גליון:
A3-4-100		ענף מינה:
SCALE:	EDITION:	דור:
As indicated		סטוסים
STATUS:		סטוס ע"י:
למכר		תאריך:
DATE:	22.09.2025	

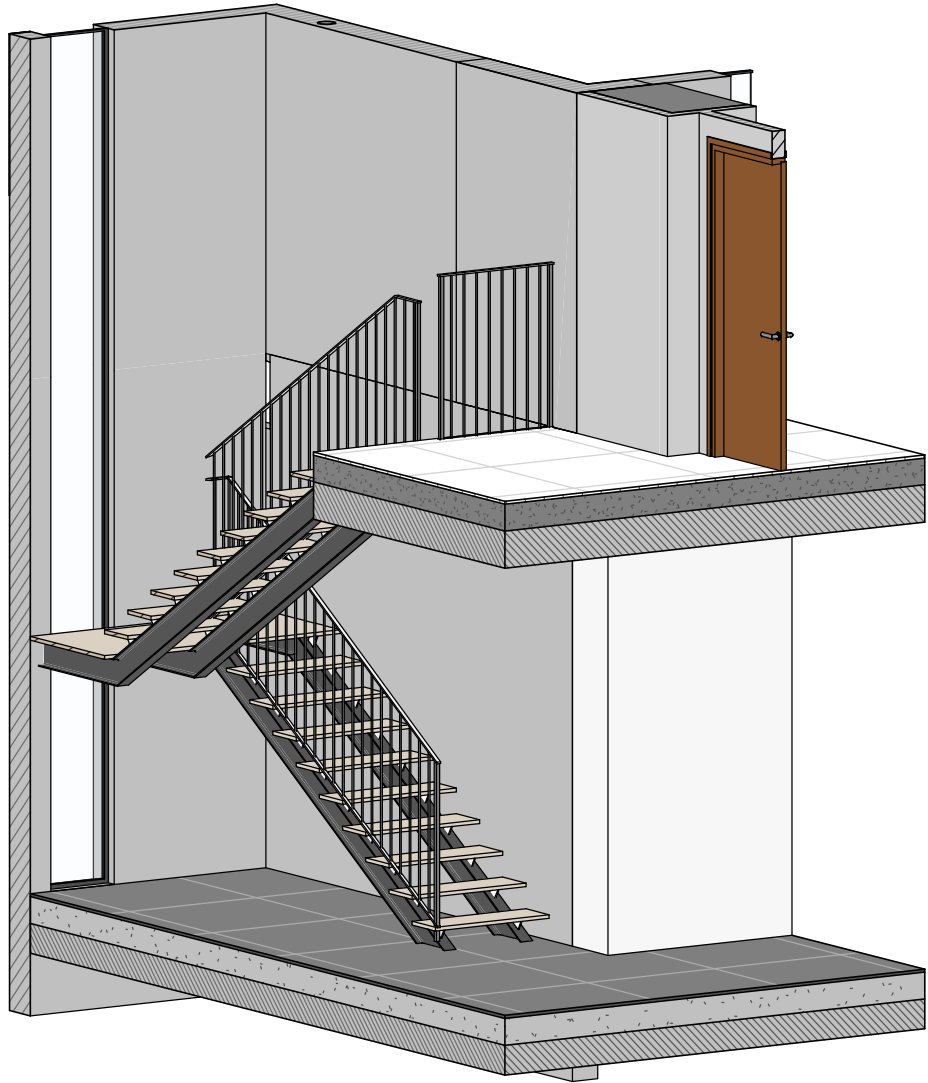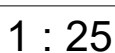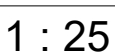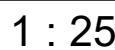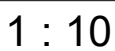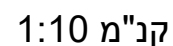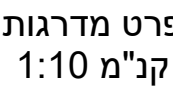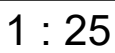

יש לבצע התאמה לפרט לאחר בחירת חיפוי המדרגות*

להמשך תיאום

ניהול פרויקט
מהיסוד - בן סולומון
פיקוח
מהיסוד - בן סולומון
קונסטרוקציה
ערן שילר
מיזוג אוויר
אייל ארז מהנדסים ויועצים בע"מ
אינסטלציה
איתן אלמסי
חשמל
איתן בסיס
אלומיניום
נוף
נתי בלוקא
חשמל חכם
חימום תת רצפתי
איטום
צבי טל
אקוסטיקה
מעליות
קרקע וביסוס
דיה הנדסת קרקע וביסוס
רישוי

[illegible][illegible]

CLIENT NAME: _____ שם המזמין:

PROJECT NAME: _____ שם הפרויקט: _____

DRAWING NAME: ס הגליון:

SHEET NUMBER: 190 גליון:

קנה מידה:	EDITION:	דפוס:	▲
-----------	----------	-------	---

STATUS: סמכות 1


רמז ע"י:	ובדק ע"י:

DATE: 22.09.2025




יומן חיינר אדריכלים
אוצד הכצרות 4 בוס חכום


www.nh-arch.com 09-9545842 70

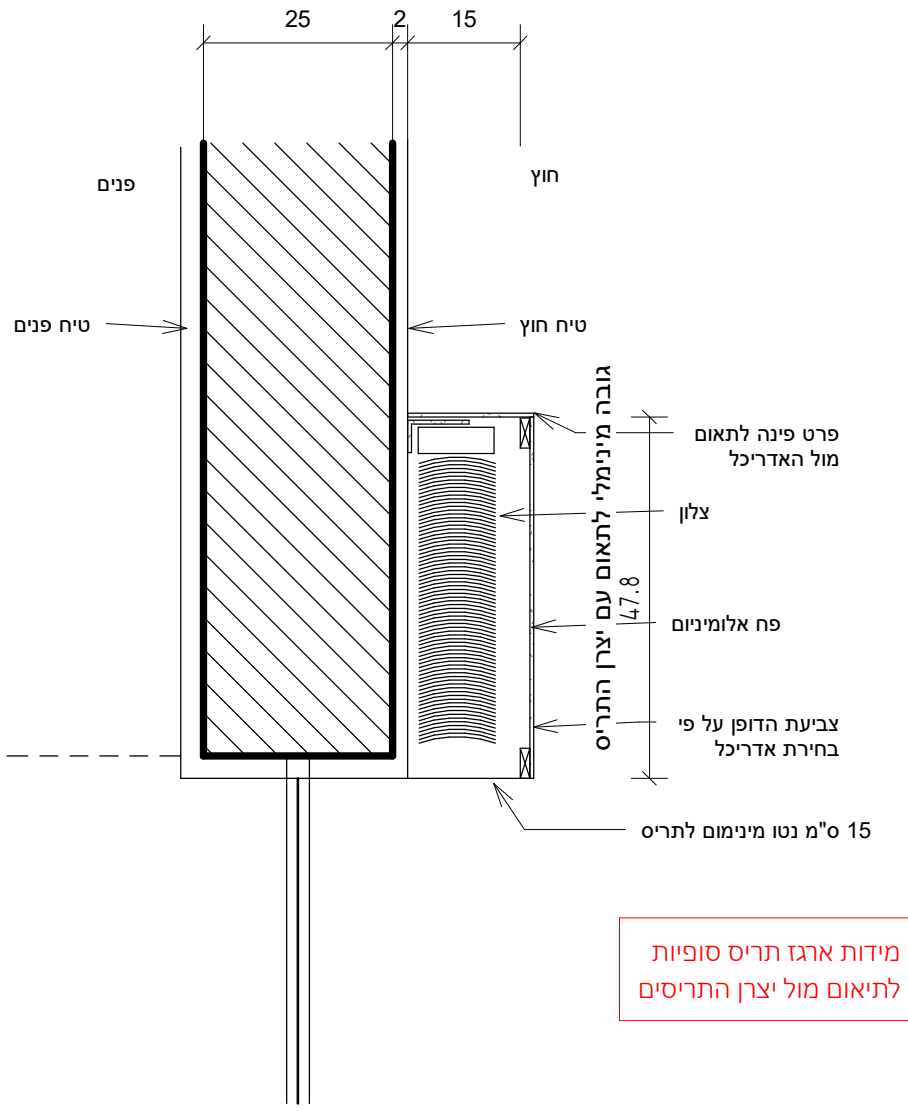


1 : 10

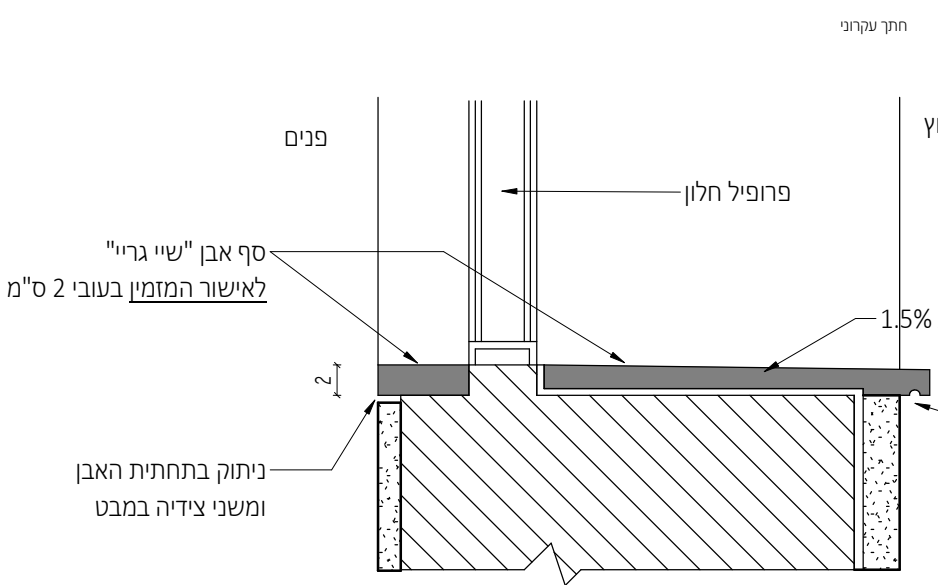


1 : 5

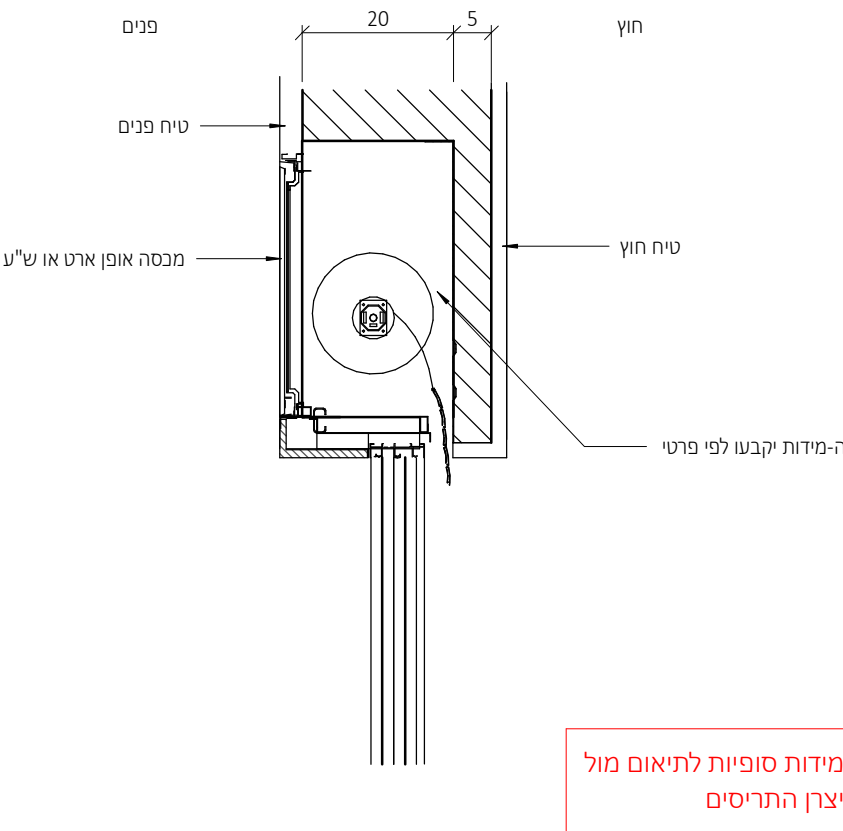


1 : 10

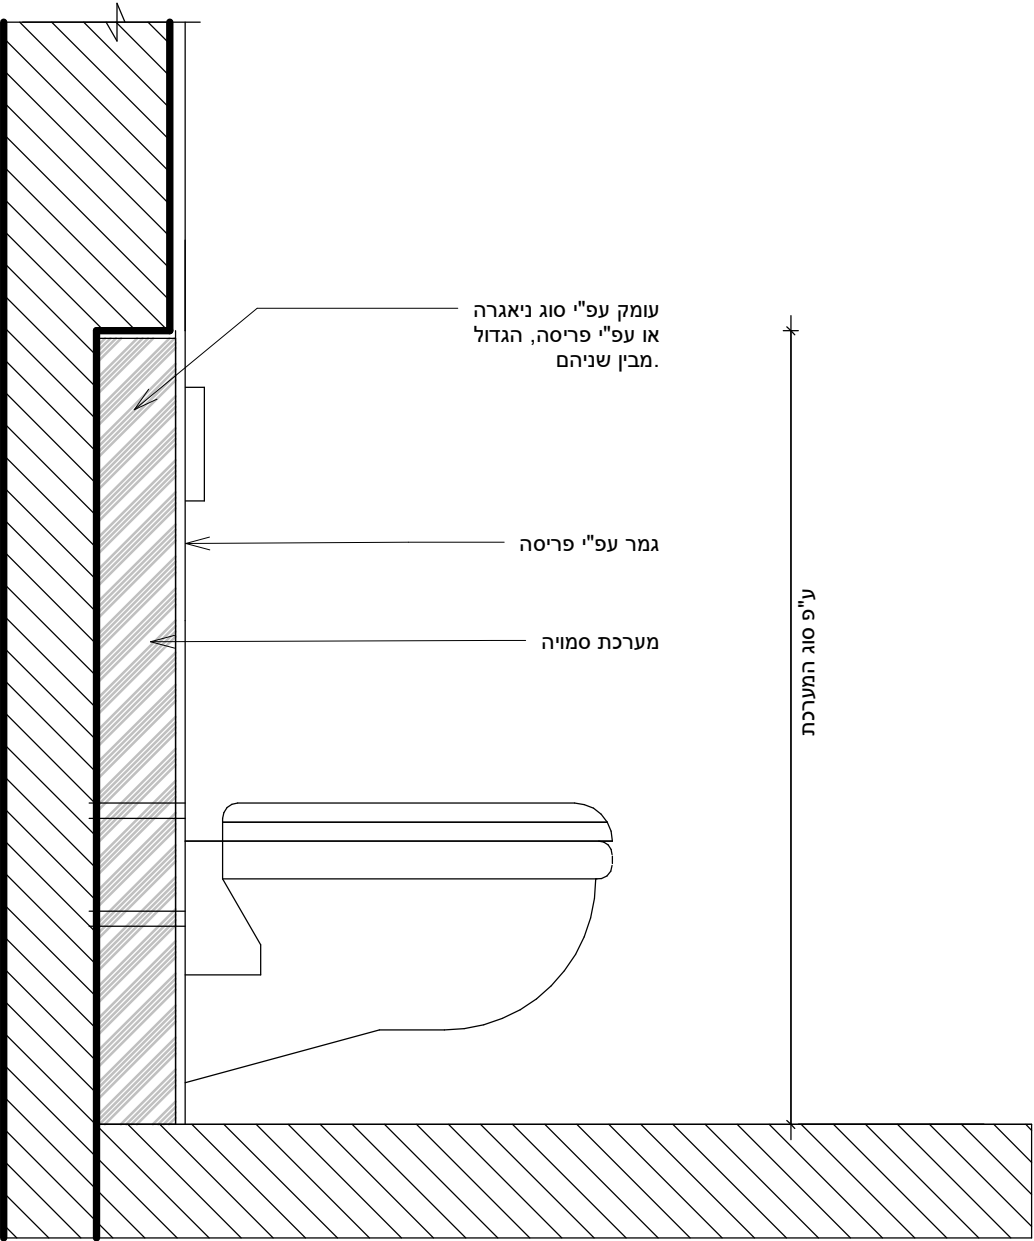

1 : 10

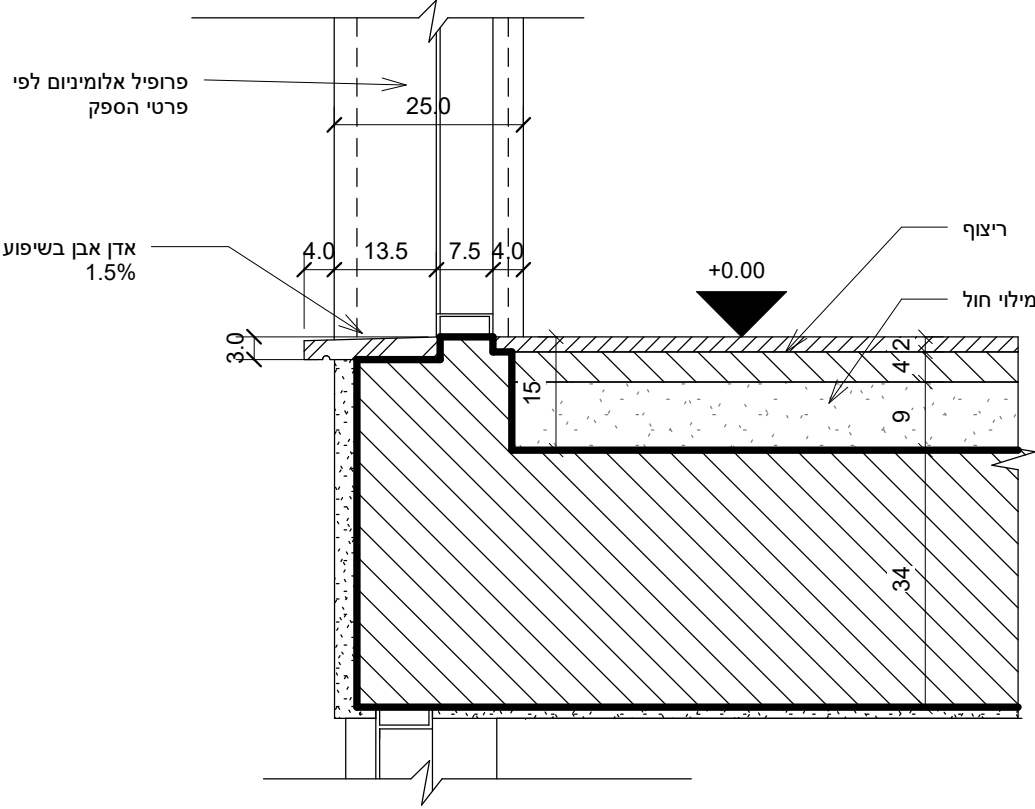

1 : 10

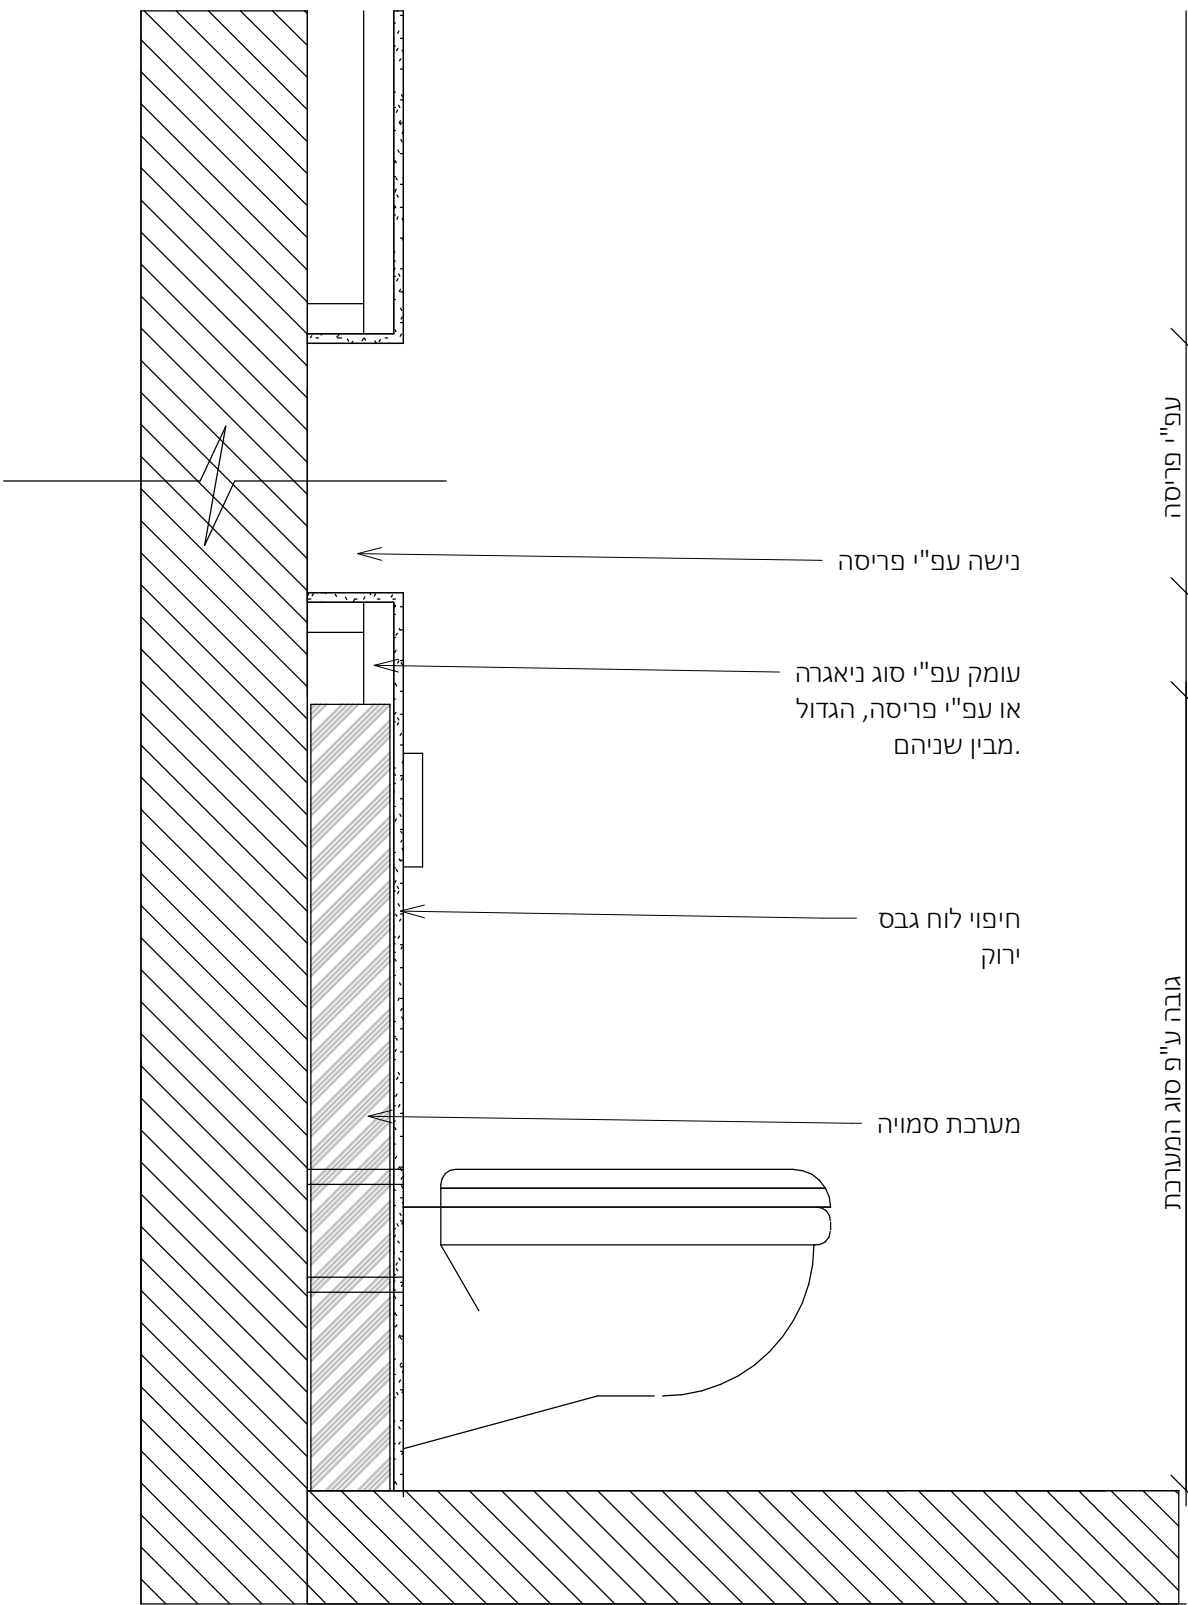

1 : 10

פרטי האיטום באחריות יועץ האיטום
ראה חוברת פרטי איטום מצורפת


להמשך תיאום

פרגולת אלומיניום




תמונה להמחשה בלבד

להמשך תיאום

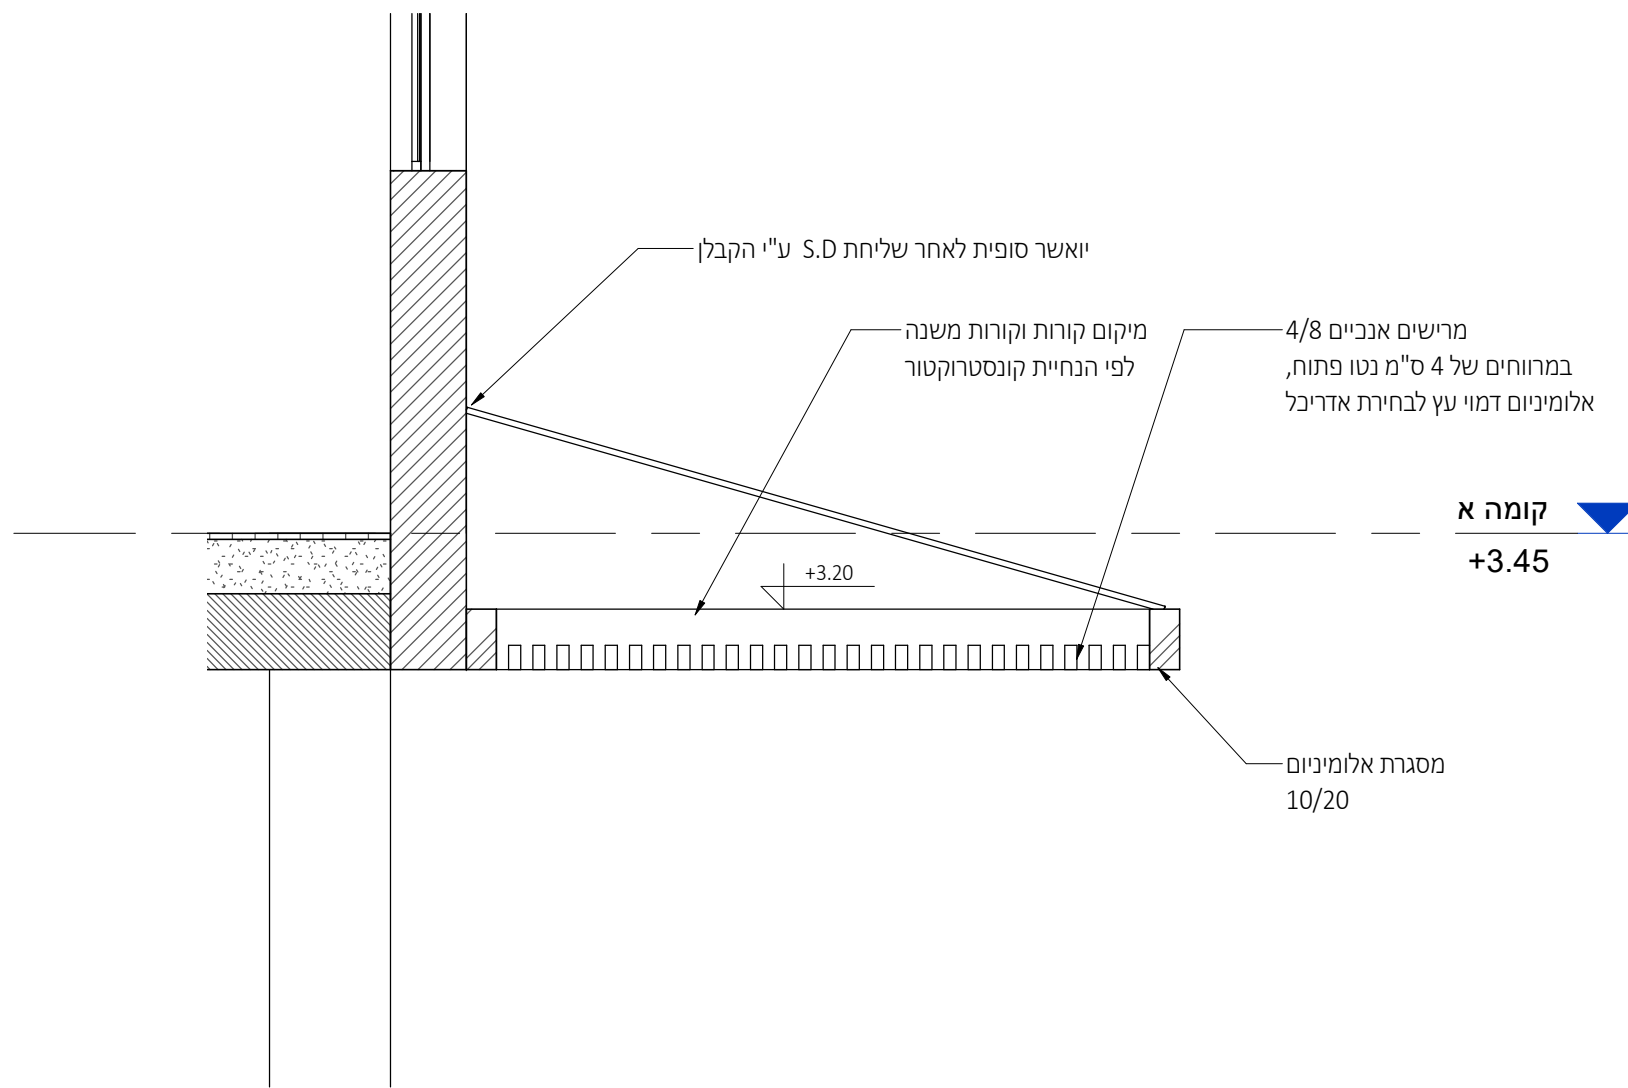


Section 11

1 : 25

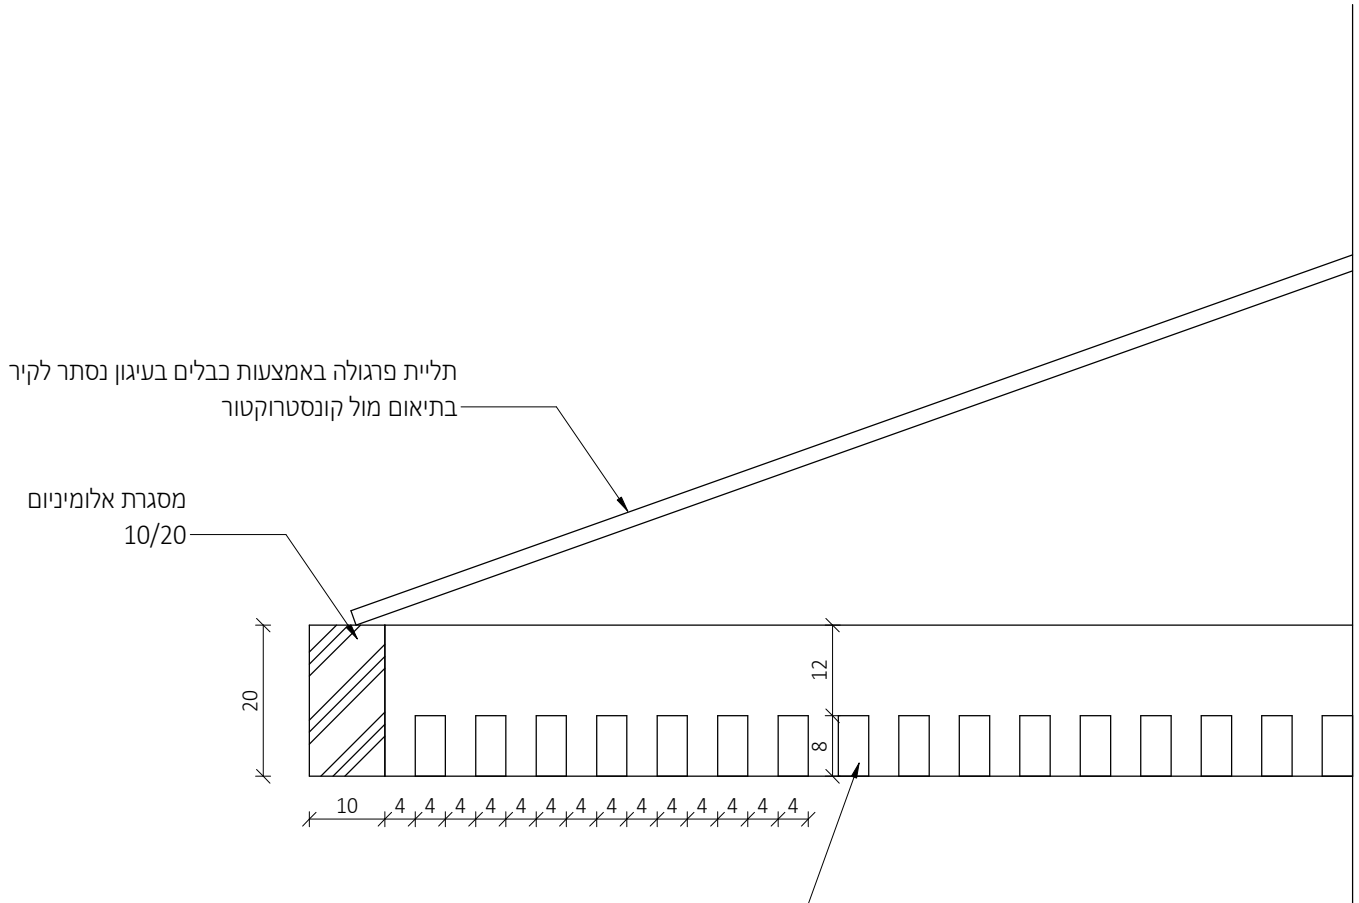


פרגולה - חתך רוחב

1 : 10

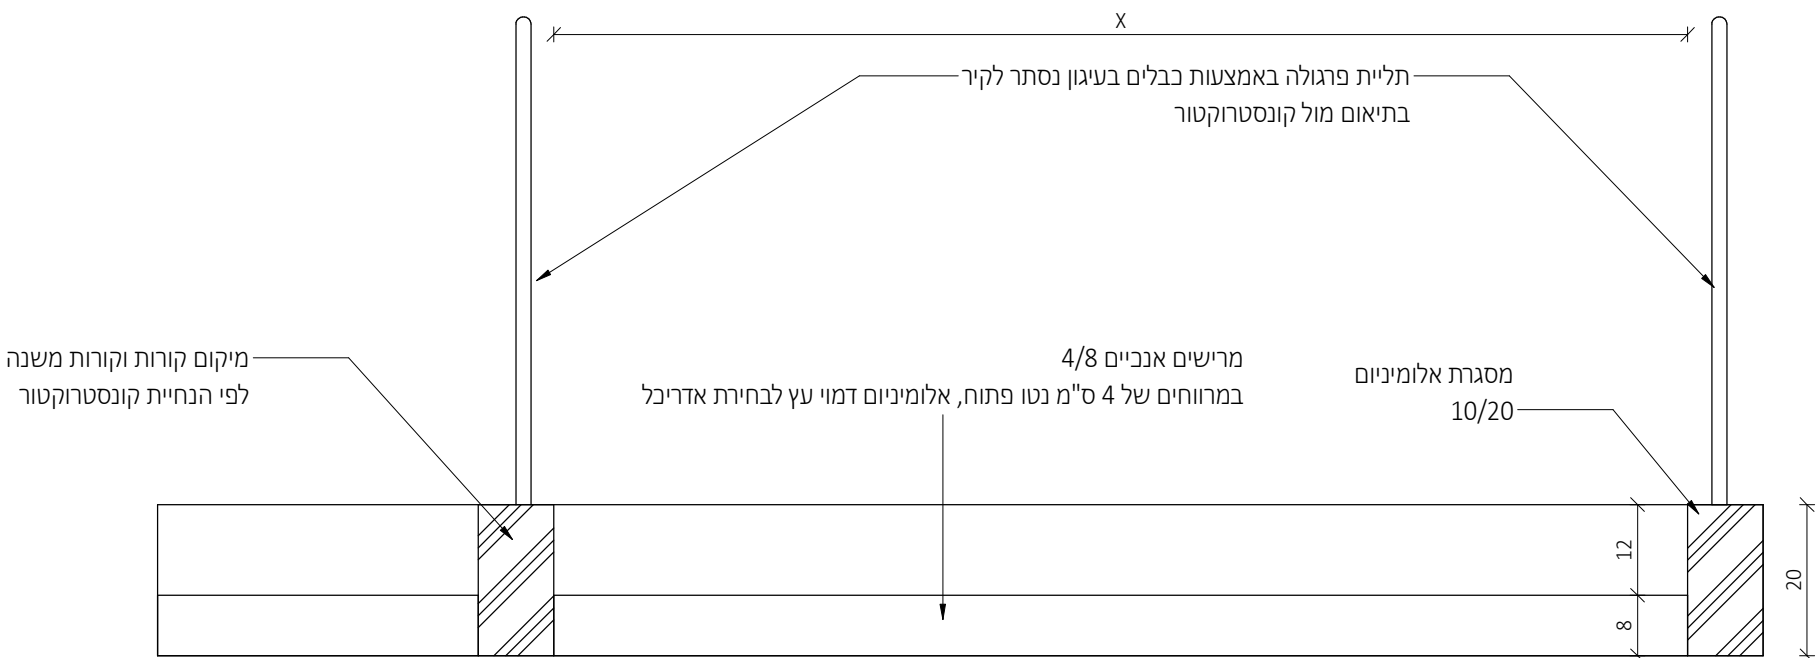


פרגולה - חתך אורך

1 : 10

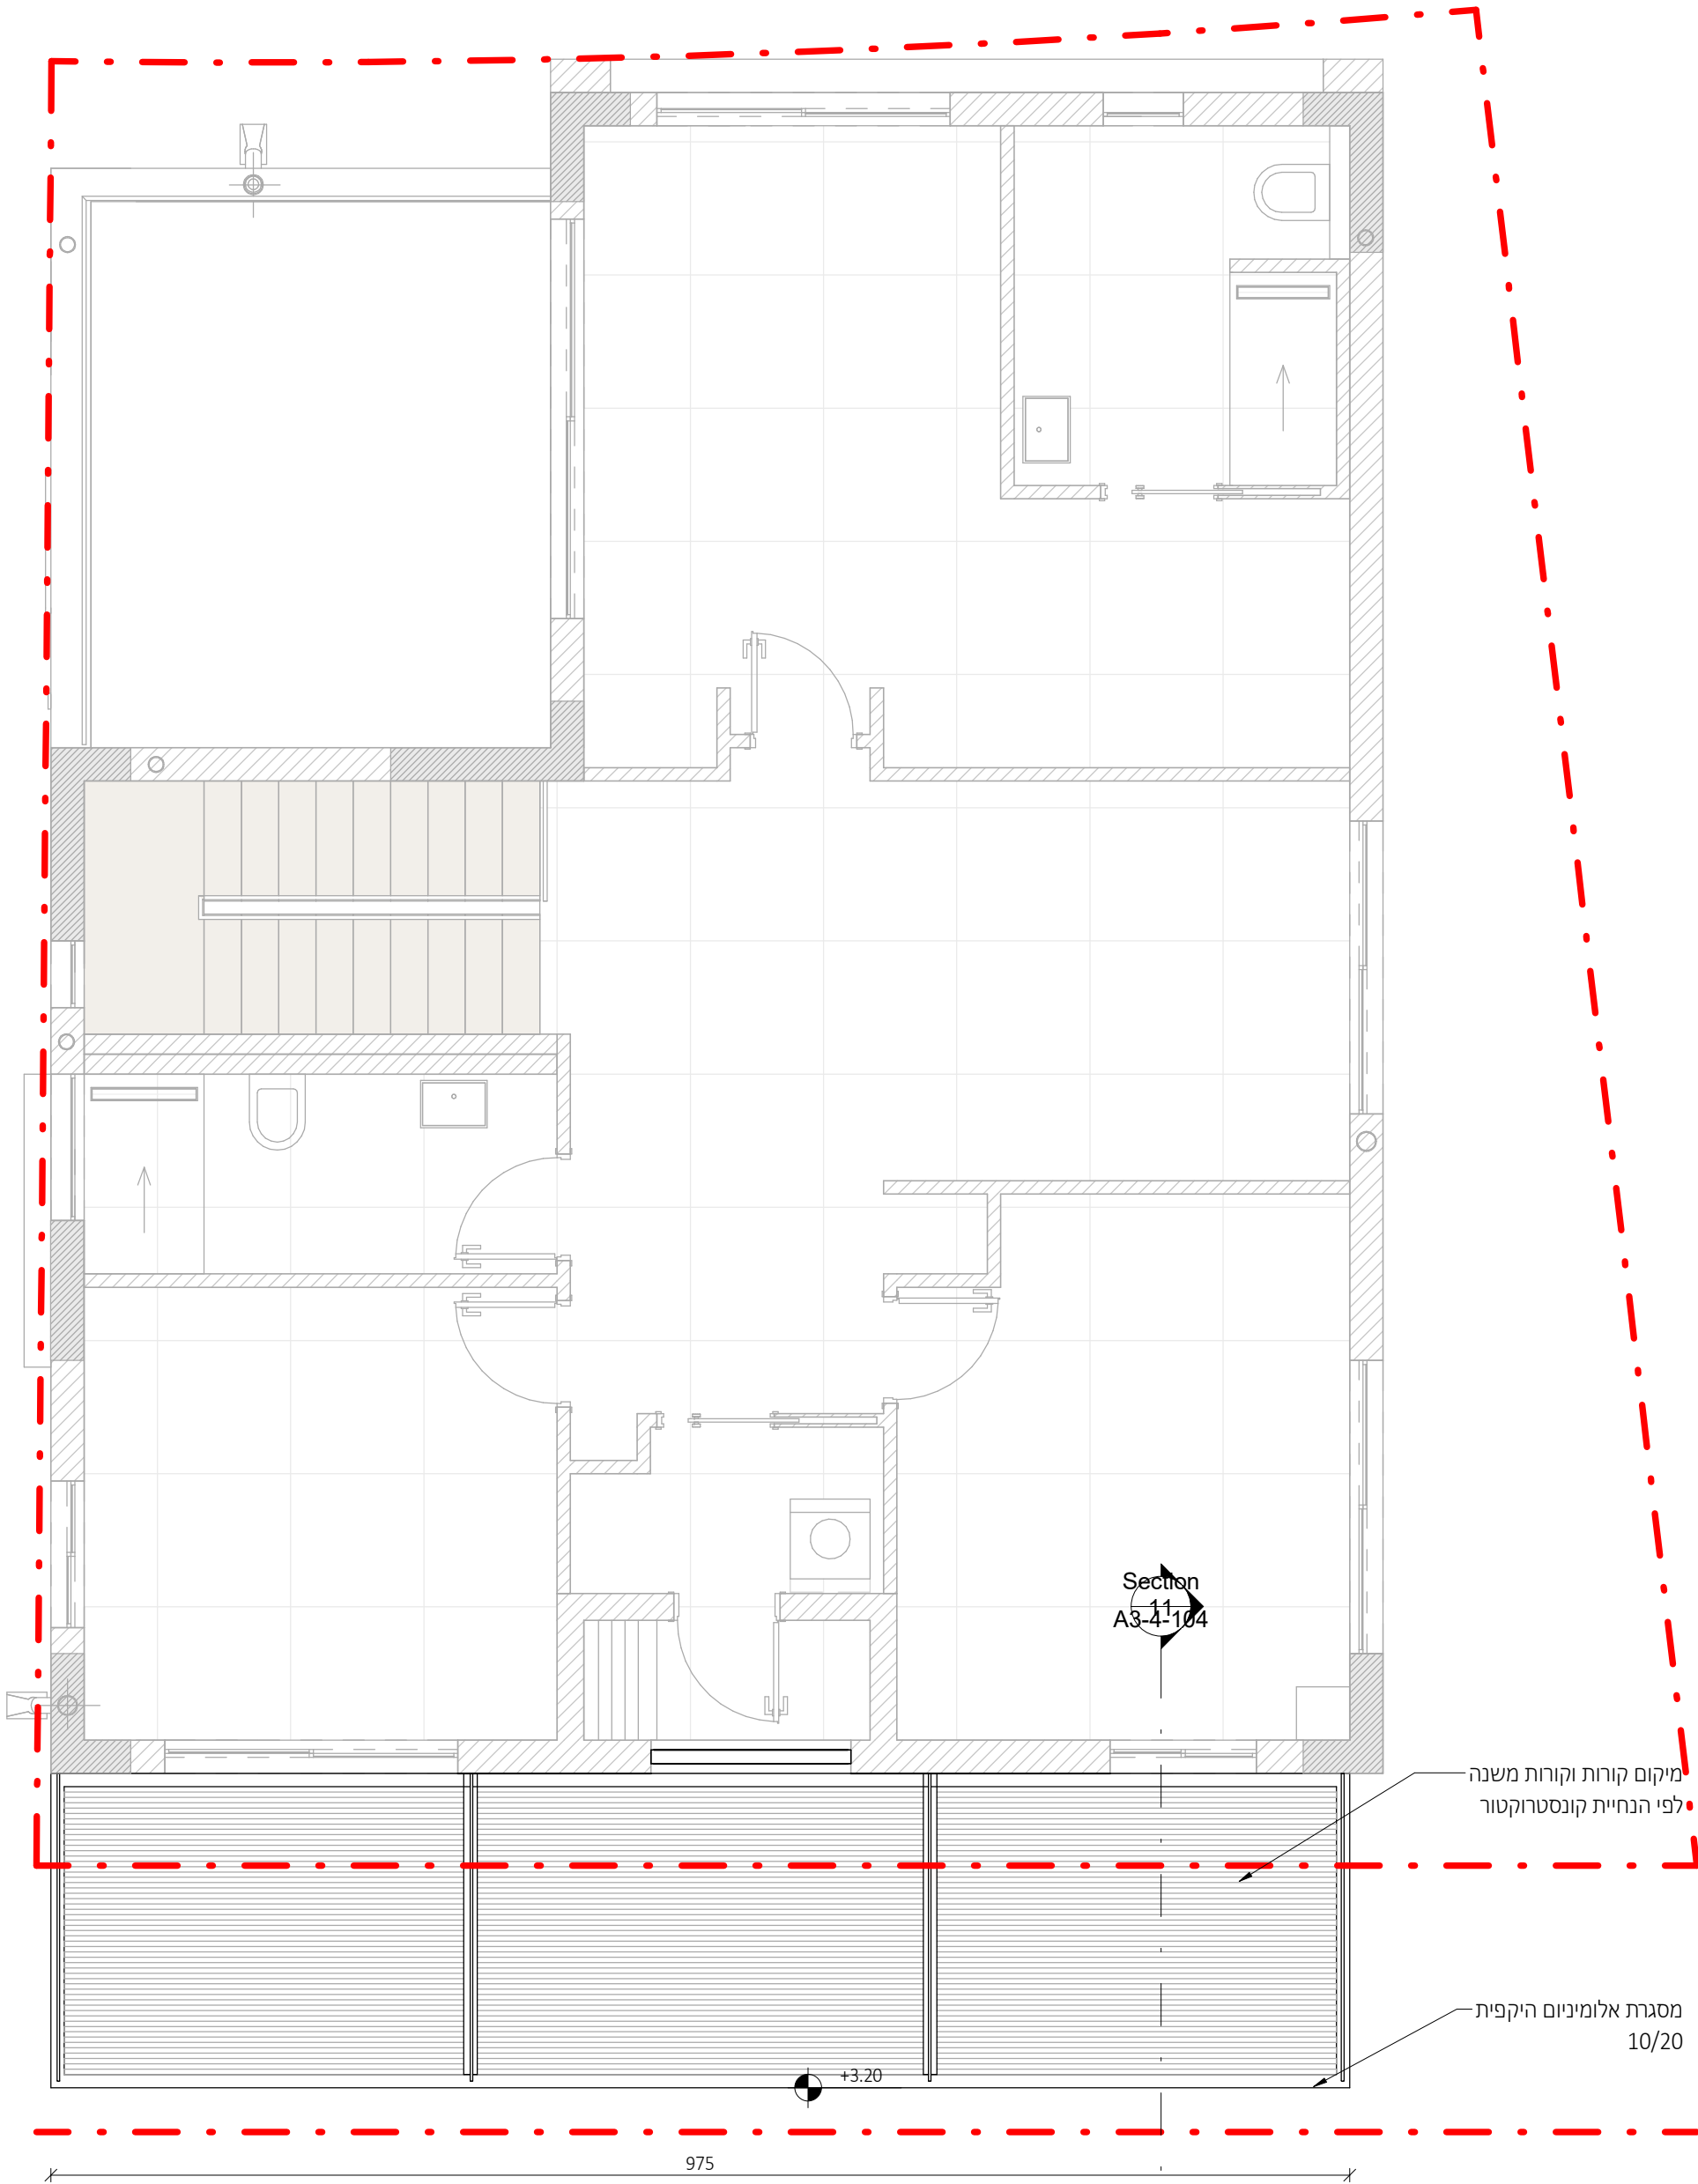

Section A3-4-104

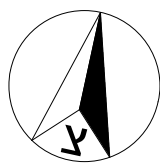


מתכננים:

ניהול פרויקט
מהיסוד - בן סולומון
פיקוח
מהיסוד - בן סולומון
קונסטרוקציה
ערן שילר
מיזוג אוויר
אייל ארז מהנדסים ויועצים בע"מ
אינסטלציה
איתן אלמסי
חשמל
איתן בסיס
אלומיניום
נוף
נתי בלוקא
חשמל חכם
חימום תת רצפתי
איטום
צבי טל
אקוסטיקה
מעליות
קרקע וביסוס
דיה הנדסת קרקע וביסוס
רישוי

± 0.00 = +253.00
הערות: 1. תכנית זו הי לקרא יחד עם תכנית הרישויים. 2. גובה אבטמילר: ראו תכנית פיתוח. 3. הפירות הן בין קירות הבניה ולא כולל פיתח. 4. פיתוח השטח סביב הבנה, כולל, מדרגות, גדרות, שבילים, ריצופים, שפכים, גדרים, חניה וגנין לא תכנית פיתוח. 5. איסוס קירות ורצפות הבנה כמעט עם הקרקע ובידוד תרמי לאורך העמודים והקירות וכל התפרות. כלירות או עם סימני (גניון)- ראו תכנית קונסטרוקציה. 6. אף דים יבוצע בכל מישור אופקי הבולם חתונן. 7. ס"ח תרמי במיד"ד- ע"פ מפרס חומקיר, מאפשר ט"י פיקוד העודף. המבצע התכנית: הבקשת התכנית: במסגרת של מסגרת או אי התאמה בתכנית /או בבנין, טעני להודיע על כך מיד לאדריכל בסופו המשיך בעבודתו. המבצע יחסינא, יחסינא, כלל, עת, של משרדו של תכנית. התכנית תהיה תכנית האדריכל ואין לשנות כל שימוש בה או ברעיונות הגלומים בה, אלא באישור בכתב מהאדריכל. המבצע יחסינא, יחסינא, כלל, עת, של משרדו של תכנית. על המפקח והמבצע לודא התאמת התכנית האדריכלית "לביצוע" לתכנית כוללת את כל האפשרויות הרצוה עד ליום תחלתה.

משרד קירות:

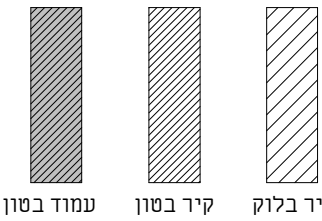

תאריך	תיאור	מהדורה
22.09.2025	מכרז	1

אדריכלות

שם המשיין:	CLIENT NAME:
קבוצת רכישה נופיה	
שם הפרויקט:	PROJECT NAME:
נופיה - מגרש 6	
שם הגליון:	DRAWING NAME:
פרטי פרגולה	
מספר גליון:	SHEET NUMBER:
A3-4-104	
תחבורה:	EDITION:
קנה מידה:	SCALE:
As indicated	
סטוס:	STATUS:
למכרז	
שורסס ע"י:	נבדק ע"י:
תאריך:	DATE:
22.09.2025	



נירסן חיינר אדריכלים
מודד והדריס 2, בית חירות
09-9545642
www.nh-arch.com
office@nh-arch.com

22/09/2025 11:56:24

זכיות יימור / ע"פ הנחיות ע"ד

רשימת חלונות					
סוג	תיאור	כמות	גובה	רוחב	מס פריט

ק.קרקע

1	300	240	1	צלון רפפה חיצוני חשמלי + ארגז חיצוני	ויטרינה פרופיל 7500 קליל
2	400	240	2	צלון רפפה חיצוני חשמלי + ארגז חיצוני	ויטרינה פרופיל 7500 קליל
3	220	240	1	צלון רפפה חיצוני חשמלי + ארגז חיצוני	חלון קבוע פרופיל 7000 קליל
4	50	575	1	ללא רפפה	חלון קבוע פרופיל 7000 קליל
5	60	100	1	ללא רפפה	חלון קיפ פרופיל 4500 קליל
6	220	240	1	צלון רפפה חיצוני חשמלי + ארגז חיצוני	ויטרינה פרופיל 7500 קליל

קומה א

7	60	110	1	תריס גלילה חשמלי	חלון קיפ פרופיל 4500 קליל
8	220	110	4	תריס גלילה חשמלי	חלון הזזה פרופיל 7000 קליל
9	110	110	1	תריס גלילה חשמלי	חלון קיפ פרופיל 4500 קליל
10	300	230	1	תריס גלילה חשמלי	ויטרינה פרופיל 7500 קליל
11	110	110	2	תריס גלילה חשמלי	חלון הזזה פרופיל 7000 קליל

סוג זכוכית – בהתאם למפורט בדו"ח התרמי (תנאי המינימום בעמוד 9 מתוך המפרט התרמי). כמו כן, הזכוכית תקבע בתיאום עם הקבלן לאחר אישור יועץ התרמי וחברת הניהול

כל פריט יחולק למינימום הכנפיים האפשרי (לתיאום מול ספק האלומיניום ובמסגרת שרטוטי shop drawing)

רשימת דלתות					
סוג	הערות	כמות	גובה	רוחב	מספר דלת

דלת חוץ דגם גארדה	דלת כניסה	1	240	140	0
דלת פנים "אקוודור" תוצרת חמדיה	דלת פנים	6	210	80	1
דלת הזזה "אקוודור" פורמייקה תוצרת חמדיה	דלת הזזה	2	210	80	2
דלת פנים "אקוודור" תוצרת חמדיה	דלת נגרות ממ"ד	1	200	80	3

נוימן חיינר אדריכלים בע"מ

כל הזכויות שמורות
ט.ל.ח

NeumanHaynerArchitects



רשימת פתחים			שם התכנית:
גליון מספר:	A3-6-1000	מהדורה:	22.09.2025
שם הפרויקט:	נופיה - מגרש 6	סטטוס:	למכרז
שם המחמיר:	קבוצת רכישה נופיה	קנה מידה:	
22/09/2025 11:56:25			