
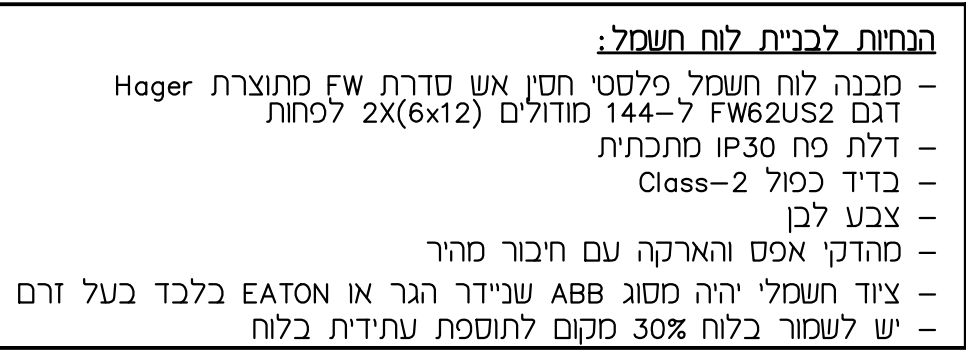
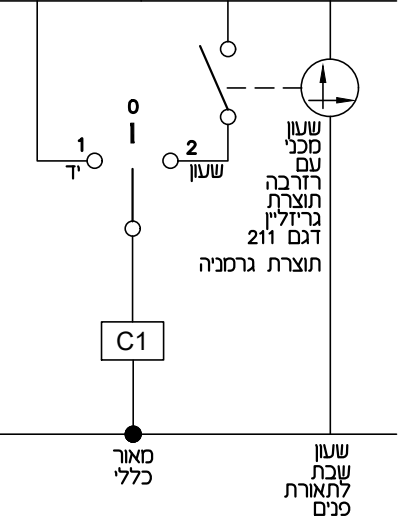


[illegible][illegible]

עודכן ע"י: אילה

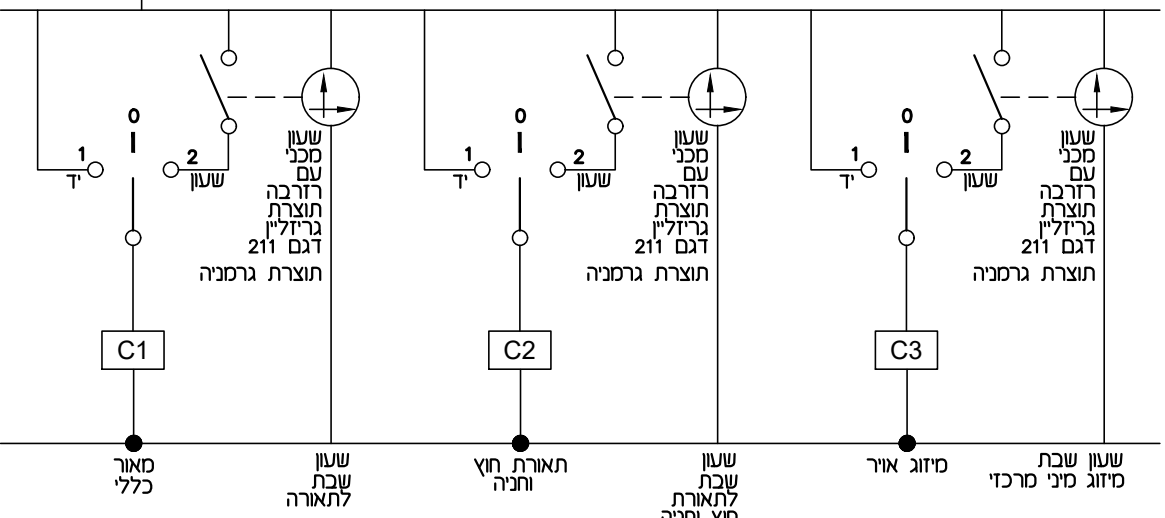

א. בסיס
הנדסת חשמל בע"מ
מגור: די חורזים 16, ירושלים 93420
070-7021015 :טל 050-6550484 :פיקס
077-5131015 :טלפקס office@ebasis.co.il :אימייל

פירוק:

נופיה-אלפי מנשה

תכנית:

לוח #1 - מגרש 6, נופיה

☒	☐	☐	☐
לביצוע	למכרז	לאישור	לעיון

File: מס' קובץ :
675W.dwg

אשר:	גל
אונד	

מס' הפרויקט:	אדוארד
שם:	אדוארד

675	6
-----	---

--	--

[illegible]

מס'	שניים	תאריך
1	ערכו תכנית	10.12.24
2	ערכו תכנית	15.12.24
3	ערכו תכנית	25.2.25
4	ערכו תכנית	5.3.25
5	ערכו תכנית	15.5.25
6	ערכו תכנית	19.6.25
7	ערכו תכנית	19.10.25

עודכן ע"י: _____ יפעת

יות:

– כהכנה לבית חכם ולדלת חכמה יש להשחיל חוט 0 כחול נוסף בכל מפסק הדלקה התכנון עצמו יעשה ע"י ספק בית חכם

–הכנות למיזוג אויר, חימום תת רצפתי,
מערכות אבטחה, וחימום מים בחשמל
יורו עפ הנחיות יועץ לכל תחום

– יש לקרוא תכנית זו יחד עם תכנית אדריכלות

א. בסיס
הנדסת חשמל בע"מ

משרד: יד חרוצים 16, ירושלים 93420
טל: 074-7021015 פקס: 050-6550484
קדם: 077-5131015 א"ת: office@ebasis.co.il



שם הפרויקט:

נופיה-אלפי מנשה
מגרש 6



שם הגיליון:

תוכנית תאורה

○ ● ○ ○ כריכות מכרז לאשר נעיון				קנה מידה: 1:50	
File: מס' קובץ: 675-6.dwg				Date: תאריך: 15.08.2024	
איש: איתן		שרטט: אביבה		תכנן: איתן	
מס' הפרויקט: 675		מס' הגיוון: L		מס' ערכון: 7	

לוח השנה            	           
לוח השנה            	           

פרט לגבהים של הדלקות,
תאורה ותריסים:

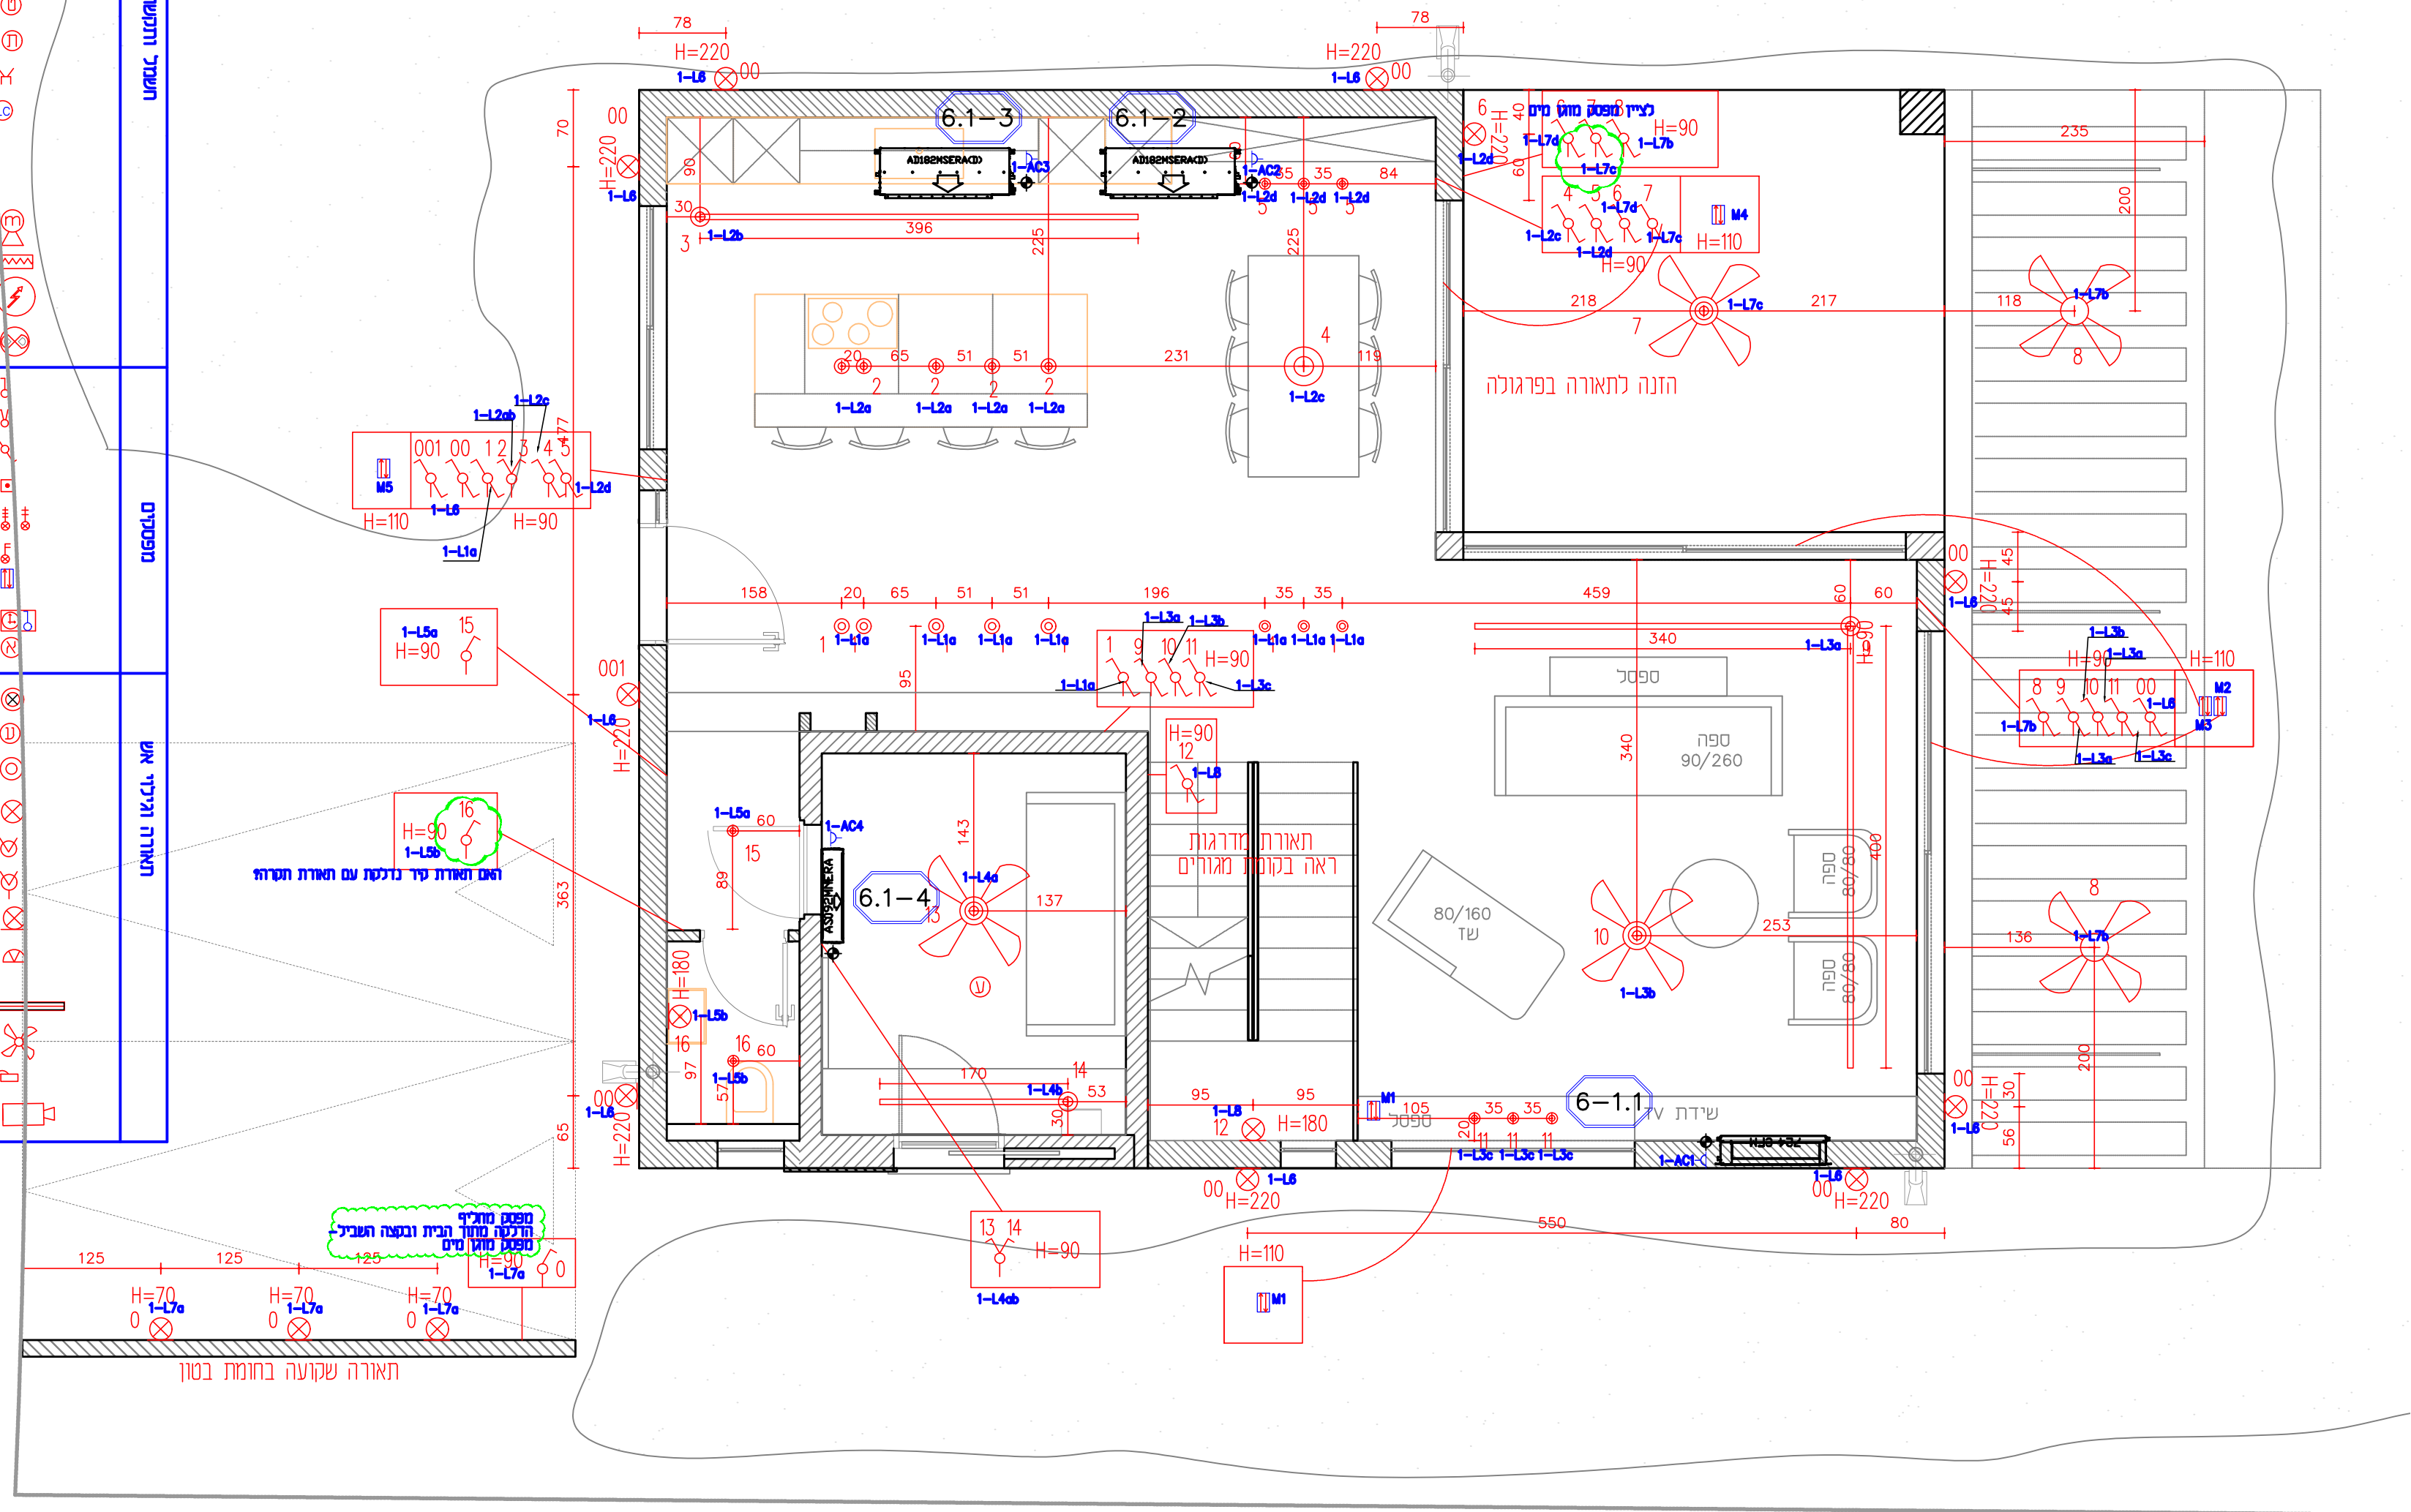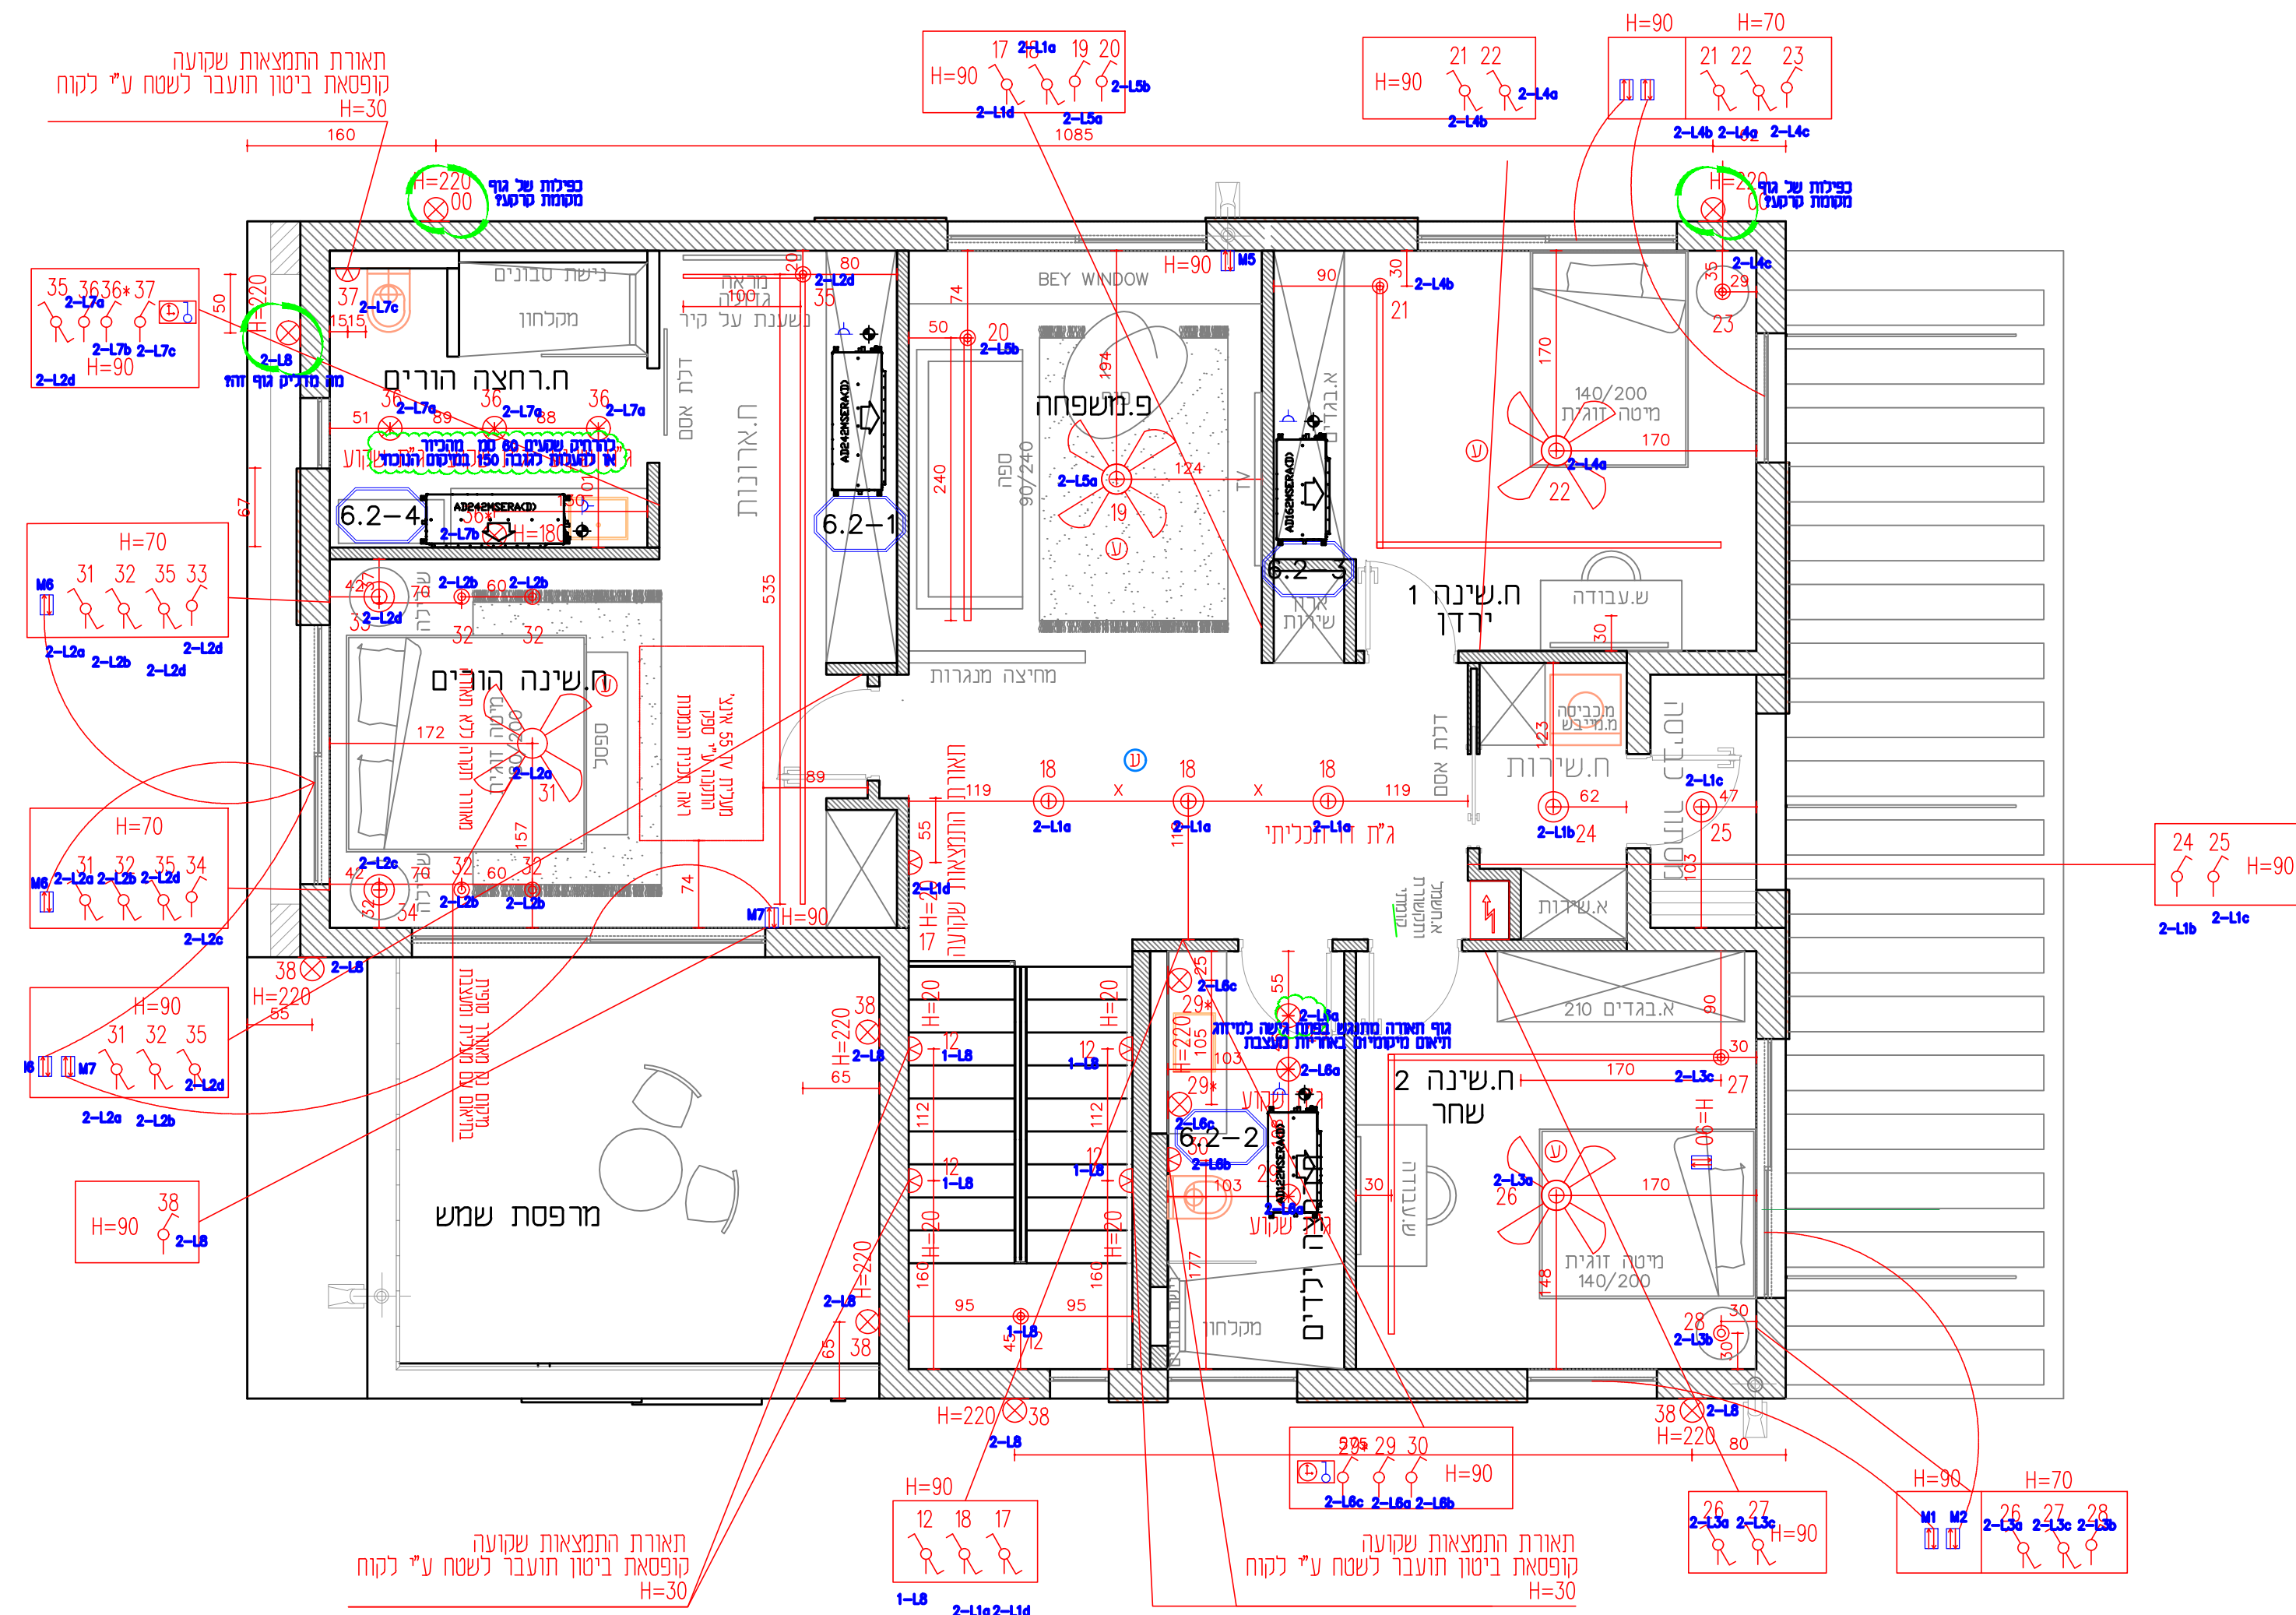[illegible]

קומה א'

קומת קרקע